

SHEET 1 OF 4 SHEETS

TRACT NO. 15618

ACCEPTED AND FILED AT THE REQUEST OF

ALL OF VESTING TENTATIVE
TRACT NO. 15618

BLOCK MODULE
5157 39

DATE OF SURVEY:
NOVEMBER 1997

IN UNINCORPORATED TERRITORY OF ORANGE COUNTY, CALIFORNIA
BEING A SUBDIVISION OF LOTS 3 AND 4 OF TRACT NO. 15615 FILED IN BOOK 777 PAGES
14 THROUGH 31 OF MISCELLANEOUS MAPS, RECORD OF ORANGE COUNTY, CALIFORNIA.

NOVEMBER 1998

JAMES F. GILLEN, L.S. 5557

HUITT-ZOLLARS, INC.

43 LOTS AND LOTS A AND B

8.574 ACRES

FIRST AMERICAN TITLE CO.

DATE MAY 28, 1999

TIME 2:07pm FEE \$13.00

INSTRUMENT NO. 19990398292

BOOK 786 PAGE 44-47

GARY L. GRANVILLE
COUNTY CLERK-RECORDER

BY Matthew Huf
DEPUTY

OWNERSHIP CERTIFICATE:

WE, THE UNDERSIGNED, BEING ALL PARTIES HAVING ANY RECORD TITLE INTEREST IN THE LAND COVERED BY THIS MAP, DO HEREBY CONSENT TO THE PREPARATION AND RECORDATION OF SAID MAP, AS SHOWN WITHIN THE DISTINCTIVE BORDER LINE. WE ALSO HEREBY DEDICATE TO THE PUBLIC FOR STREET PURPOSES: BLAKEMORE DRIVE, AND KEMPTON LANE.

SURVEYOR'S STATEMENT:

I HEREBY STATE THAT THIS MAP CONSISTING OF 4 SHEETS CORRECTLY REPRESENTS TRUE AND COMPLETE SURVEY AS SHOWN MADE IN NOVEMBER 1997; WAS MADE BY ME OR UNDER MY DIRECTION; THAT THE MONUMENTS ARE OF THE CHARACTER AND OCCUPY OR WILL OCCUPY THE POSITIONS INDICATED BY SAID MAP; AND THAT SAID MONUMENTS WILL BE SUFFICIENT TO ENABLE THE SURVEY TO BE RETRACED.



James F. Gillen
JAMES F. GILLEN, L.S. 5557
REGISTRATION DATE: 9/30/01

TAYLOR WOODROW HOMES, INC., A CALIFORNIA CORPORATION,

BY: Thomas O. Redwitz BY: Robert C. Lerner
PRINT NAME: Thomas O. Redwitz PRINT NAME: ROBERT C. LERNER
PRINT TITLE: Vice President PRINT TITLE: VICE PRESIDENT
Regional Manager

DMB LADERA, L.L.C., A DELAWARE LIMITED LIABILITY COMPANY, BENEFICIARY UNDER A DEED OF TRUST RECORDED MAY 5, 1999 AS INSTRUMENT NO. 1999032822 OF OFFICIAL RECORDS.

BY: RANCHO MISSION VIEJO, L.L.C., A DELAWARE LIMITED LIABILITY COMPANY,
AS AGENT AND OR MANAGER.

BY: Paul Johnson
PRINT NAME: PAUL JOHNSON
PRINT TITLE: V.P.-COMMUNITY DEVELOPMENT

~~DMB CONSOLIDATED HOLDINGS, L.L.C., AN ARIZONA LIMITED LIABILITY COMPANY, BENEFICIARY UNDER A DEED OF TRUST RECORDED DECEMBER 10, 1996 AS INSTRUMENT NO. 19960624030 OF OFFICIAL RECORDS.~~

~~BY: DMB ASSOCIATES, INC. AN ARIZONA CORPORATION,
AS MANAGER.~~

~~BY: Terry D. Randall
PRINT NAME: TERRY D. RANDALL
PRINT TITLE: VICE PRESIDENT~~


COUNTY SURVEYOR'S STATEMENT:

I HEREBY STATE THAT I HAVE EXAMINED THIS MAP AND HAVE FOUND IT TO BE SUBSTANTIALLY IN CONFORMANCE WITH THE TENTATIVE MAP AS FILED WITH, AMENDED AND APPROVED BY THE ORANGE COUNTY SUBDIVISION COMMITTEE; THAT ALL PROVISIONS OF THE SUBDIVISION MAP ACT AND COUNTY SUBDIVISION REGULATIONS HAVE BEEN COMPLIED WITH AND I AM SATISFIED SAID MAP IS TECHNICALLY CORRECT.

DATED THIS 14TH DAY OF MAY, 1999.

Michael K. Sullivan
JOHN CANAS, COUNTY SURVEYOR

BY: MICHAEL K. SULLIVAN, DEPUTY
L.S. 6254 EXPIRES 6-30-02

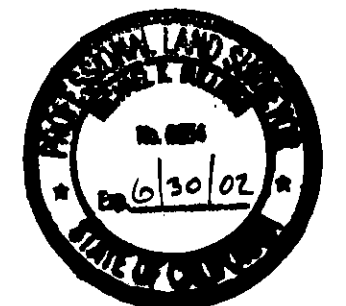

COUNTY TREASURER-TAX COLLECTOR'S CERTIFICATE:

STATE OF CALIFORNIA)
COUNTY OF ORANGE)SS

I HEREBY CERTIFY THAT ACCORDING TO THE RECORDS OF MY OFFICE THERE ARE NO LIENS AGAINST THE LAND COVERED BY THIS MAP OR ANY PART THEREOF FOR UNPAID STATE, COUNTY, MUNICIPAL OR LOCAL TAXES OR SPECIAL ASSESSMENTS COLLECTED AS TAXES, EXCEPT TAXES OR SPECIAL ASSESSMENTS COLLECTED AS TAXES NOT YET PAYABLE.

AND DO ALSO HEREBY CERTIFY TO THE RECORDER OF ORANGE COUNTY THAT THE PROVISIONS OF THE SUBDIVISION MAP ACT HAVE BEEN COMPLIED WITH REGARDING DEPOSITS TO SECURE THE PAYMENT OF TAXES OR SPECIAL ASSESSMENTS COLLECTED AS TAXES ON THE LAND COVERED BY THIS MAP.

DATED THIS 14 DAY OF April, 1999.

JOHN M.W. MOORLACH
COUNTY TREASURER-TAX COLLECTOR

BY: Darlene J. Bloom
DEPUTY TREASURER-TAX COLLECTOR


CLERK OF THE BOARD OF SUPERVISORS' CERTIFICATE:

STATE OF CALIFORNIA)
COUNTY OF ORANGE)SS

I HEREBY CERTIFY THAT THIS MAP WAS PRESENTED FOR APPROVAL TO THE BOARD OF SUPERVISORS OF ORANGE COUNTY AT A REGULAR MEETING THEREOF HELD ON THE 25th DAY OF May, 1999, AND THAT THEREUPON SAID BOARD DID, BY AN ORDER DULY PASSED AND ENTERED, APPROVE SAID MAP AND DID ACCEPT ON BEHALF OF THE PUBLIC, SUBJECT TO IMPROVEMENTS: THE DEDICATION FOR STREET PURPOSES OF: BLAKEMORE DRIVE, AND KEMPTON LANE.

DATED THIS 25th DAY OF May, 1999.

Darlene J. Bloom
DARLENE J. BLOOM
CLERK OF THE BOARD OF SUPERVISORS

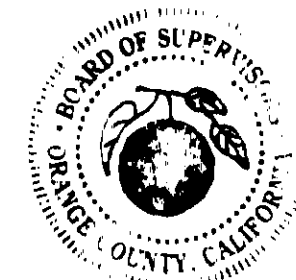

AUTOMATIC FIRE SPRINKLER NOTE:

ALL COMMERCIAL STRUCTURES OVER 6,000 SQUARE FEET; ALL MULTI FAMILY RESIDENTIAL STRUCTURES; ALL DETACHED, SINGLE FAMILY STRUCTURES EXCEEDING 5,500 SQUARE FEET, AND ALL STRUCTURES EXCEEDING FIRE AUTHORITY ACCESS REQUIREMENTS SHALL BE PROTECTED BY AN AUTOMATIC SPRINKLER SYSTEM.

HIGH FIRE HAZARD AREA NOTE:

THE LOTS SHOWN ON THIS MAP ARE IN A HIGH FIRE HAZARD AREA DUE TO WLD LAND EXPOSURE BASED ON STATE SRA MAPS.

NOTES:

PROPERTY MAY BE SUBJECT TO IMPACTS FROM THE FOOTHILL/EASTERN TRANSPORTATION CORRIDOR.

THE PROPERTY SHOWN ON THIS MAP IS "CONDITIONALLY EXCLUDED" FROM A "SPECIAL FIRE PROTECTION AREA." THERE ARE NO LOTS IN THIS TRACT THAT ARE SUBJECT TO CONSTRUCTION FEATURES OF THE ORANGE COUNTY ORDINANCE 3960.

SEE SHEET 2 FOR NOTARY ACKNOWLEDGMENTS AND SIGNATURE OMISSIONS.

SHEET 2 OF 4 SHEETS

TRACT NO. 15618

IN UNINCORPORATED TERRITORY OF ORANGE COUNTY, CALIFORNIA

ALL OF VESTING TENTATIVE
TRACT NO. 15618DATE OF SURVEY:
NOVEMBER 1997

NOVEMBER 1998

JAMES F. GILLEN, L.S. 5557

HUITT-ZOLLARS, INC.

43 LOTS AND LOTS A AND B


8.574 ACRES

TAYLOR WOODROW HOMES, INC.

STATE OF CALIFORNIA)
COUNTY OF ORANGE)SS

ON THIS 26TH DAY OF FEBRUARY, 1999, BEFORE ME,
MICHAEL R. LEONDIS, A NOTARY PUBLIC IN AND FOR SAID STATE,
PERSONALLY APPEARED THOMAS D. REDWITZ AND
ROBERT C. LIEWER, PERSONALLY KNOWN TO ME OR PROVED TO ME
ON THE BASIS OF SATISFACTORY EVIDENCE TO BE THE PERSONS WHOSE NAMES
ARE SUBSCRIBED TO THE WITHIN INSTRUMENT AND ACKNOWLEDGED TO ME THAT
THEY EXECUTED THE SAME IN THEIR AUTHORIZED CAPACITIES, AND THAT BY THEIR
SIGNATURES ON THE INSTRUMENT THE PERSONS, OR THE ENTITY UPON BEHALF
OF WHICH THE PERSONS ACTED, EXECUTED THE INSTRUMENT.

WITNESS MY HAND:

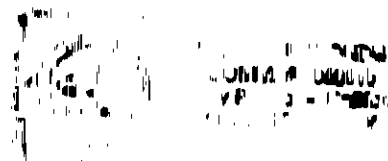MY COMMISSION EXPIRES 6/99NOTARY PUBLIC IN AND FOR SAID STATE IS IN ORANGE COUNTY.MICHAEL R. LEONDIS
PRINT NAME

DMB LADERA, L.L.C.

STATE OF CALIFORNIA)
COUNTY OF ORANGE)SS

ON THIS 1st DAY OF MARCH, 1999, BEFORE ME, M. Kristin King
A NOTARY PUBLIC IN AND FOR SAID STATE, PERSONALLY APPEARED Paul Johnson
PERSONALLY KNOWN TO ME OR PROVED TO ME ON THE BASIS OF SATISFACTORY EVIDENCE TO
BE THE PERSON WHOSE NAME IS SUBSCRIBED TO THE WITHIN INSTRUMENT AND ACKNOWLEDGED
TO ME THAT HE EXECUTED THE SAME IN HIS AUTHORIZED CAPACITY, AND THAT BY HIS SIGNATURE
ON THE INSTRUMENT THE PERSON, OR THE ENTITY UPON BEHALF OF WHICH THE PERSON ACTED,
EXECUTED THE INSTRUMENT, AS BENEFICIARY.

WITNESS MY HAND:

MY COMMISSION EXPIRES 7/29/00

NOTARY PUBLIC IN AND FOR SAID STATE

MY PRINCIPAL PLACE OF BUSINESS
IS IN Orange COUNTY.M. Kristin King
PRINT NAME

DMB CONSOLIDATED HOLDINGS, L.L.C.

STATE OF CALIFORNIA)
COUNTY OF ORANGE)SS

ON THIS 4th DAY OF MARCH, 1999, BEFORE ME, M. Kristin King
A NOTARY PUBLIC IN AND FOR SAID STATE, PERSONALLY APPEARED Terry D. Randall
PERSONALLY KNOWN TO ME OR PROVED TO ME ON THE BASIS OF SATISFACTORY EVIDENCE TO
BE THE PERSON WHOSE NAME IS SUBSCRIBED TO THE WITHIN INSTRUMENT AND ACKNOWLEDGED
TO ME THAT HE EXECUTED THE SAME IN HIS AUTHORIZED CAPACITY, AND THAT BY HIS SIGNATURE
ON THE INSTRUMENT THE PERSON, OR THE ENTITY UPON BEHALF OF WHICH THE PERSON ACTED,
EXECUTED THE INSTRUMENT, AS BENEFICIARY.

WITNESS MY HAND:

MY COMMISSION EXPIRES 9/29/00

NOTARY PUBLIC IN AND FOR SAID STATE

MY PRINCIPAL PLACE OF BUSINESS
IS IN Orange COUNTY.M. Kristin King
PRINT NAME

SIGNATURE OMISSIONS:

IN ACCORDANCE WITH THE PROVISIONS OF SECTION 66436(a) (3) OF THE SUBDIVISION
MAP ACT, THE FOLLOWING SIGNATURES HAVE BEEN OMITTED:

1. LADERA DEVELOPMENT COMPANY, L.L.C., HOLDER OF OIL, GAS, MINERAL, AND WATER RIGHTS
RECORDED DECEMBER 10, 1996 AS INSTRUMENT NO. 19960624029 OF OFFICIAL RECORDS.
2. DMB LADERA, L.L.C., A DELAWARE LIMITED LIABILITY COMPANY, HOLDER OF EASEMENTS
RESERVED IN A DEED RECORDED MAY 5, 1999 AS INSTRUMENT NO. 19990328621 OF
OFFICIAL RECORDS.

MONUMENT NOTES:

▲ INDICATES FOUND 2" I.P. TAGGED "L.S. 5557" PER TRACT NO. 15615,
M.M. 777 / 14-31.● INDICATES LOCATION OF OCS WELL MONUMENT WITH A 2" BRASS CAP STAMPED
"L.S. 5557" TO BE SET PER TRACT NO. 15615, M.M. 777 / 14-31.△ INDICATES LOCATION OF 2" I.P. TAGGED "L.S. 5557" OR SPIKE & WASHER
STAMPED "L.S. 5557" OR LEAD, TACK & TAG "L.S. 5557" TO BE SET PER
TRACT NO. 15615, M.M. 777 / 14-31.□ INDICATES LOCATION OF 1" I.P. TAGGED "L.S. 5557" OR SPIKE & WASHER
STAMPED "L.S. 5557" OR LEAD, TACK & TAG "L.S. 5557" TO BE SET PER
TRACT NO. 15615, M.M. 777 / 14-31.○ INDICATES LOCATION OF 1" I.P. TAGGED "L.S. 5557" OR SPIKE & WASHER
STAMPED "L.S. 5557" OR LEAD, TACK & TAG "L.S. 5557" TO BE SET WITHIN
90 DAYS AFTER ACCEPTANCE OF IMPROVEMENTS.2" I.P. TAGGED "L.S. 5557" OR SPIKE & WASHER STAMPED "L.S. 5557" OR LEAD,
TACK AND TAG "L.S. 5557" TO BE SET AT ALL TRACT BOUNDARY CORNERS, EXCEPT
FOR TRACT BOUNDARY CORNERS ON STREET CENTERLINES, WITHIN 90 DAYS AFTER
ACCEPTANCE OF IMPROVEMENTS, UNLESS OTHERWISE NOTED.1" I.P. TAGGED "L.S. 5557" OR SPIKE & WASHER STAMPED "L.S. 5557" OR LEAD,
TACK AND TAG "L.S. 5557" TO BE SET AT ALL INTERIOR LOT CORNERS, EXCEPT LOT
CORNERS ABUTTING STREETS; LEAD, TACK & TAG "L.S. 5557" TO BE SET IN TOP OF
CURB OR SIDEWALK ON 9.75' OFFSET ON SIDE LOT LINES PRODUCED FOR LOT CORNERS
ABUTTING KEMPTON LANE, AND ON A 10.75' OFFSET ON SIDE LOT LINES PRODUCED FOR
LOT CORNERS ABUTTING BLAKEMORE DRIVE, WITHIN 90 DAYS AFTER ACCEPTANCE OF
IMPROVEMENTS, UNLESS OTHERWISE NOTED.NO MONUMENTATION TO BE SET AT BC'S AND EC'S OF STREET RIGHT OF WAY LINES,
UNLESS OTHERWISE NOTED.

BASIS OF BEARINGS:

BEARINGS SHOWN HEREON ARE BASED ON THE WESTERLY LINE OF LOT 3 BEING
N18°39'21"E AS SHOWN ON TRACT NO. 15615, FILED IN BOOK 777, PAGES 14
THROUGH 31 OF MISCELLANEOUS MAPS, RECORDS OF ORANGE COUNTY ALIF #114

SHEET 3 OF 4 SHEETS

TRACT NO. 15618

ALL OF VESTING TENTATIVE
TRACT NO. 15618

IN UNINCORPORATED TERRITORY OF ORANGE COUNTY, CALIFORNIA

NOVEMBER 1998


JAMES F. GILLEN, L.S. 5557

DATE OF SURVEY:
NOVEMBER 1997


HUITT-ZOLLARS, INC.

43 LOTS AND LOTS A AND B

8.574 ACRES

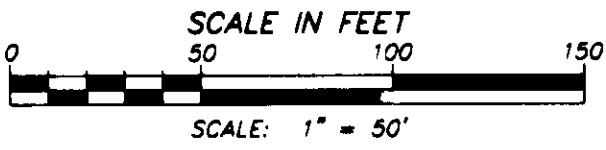

SEE SHEET 4

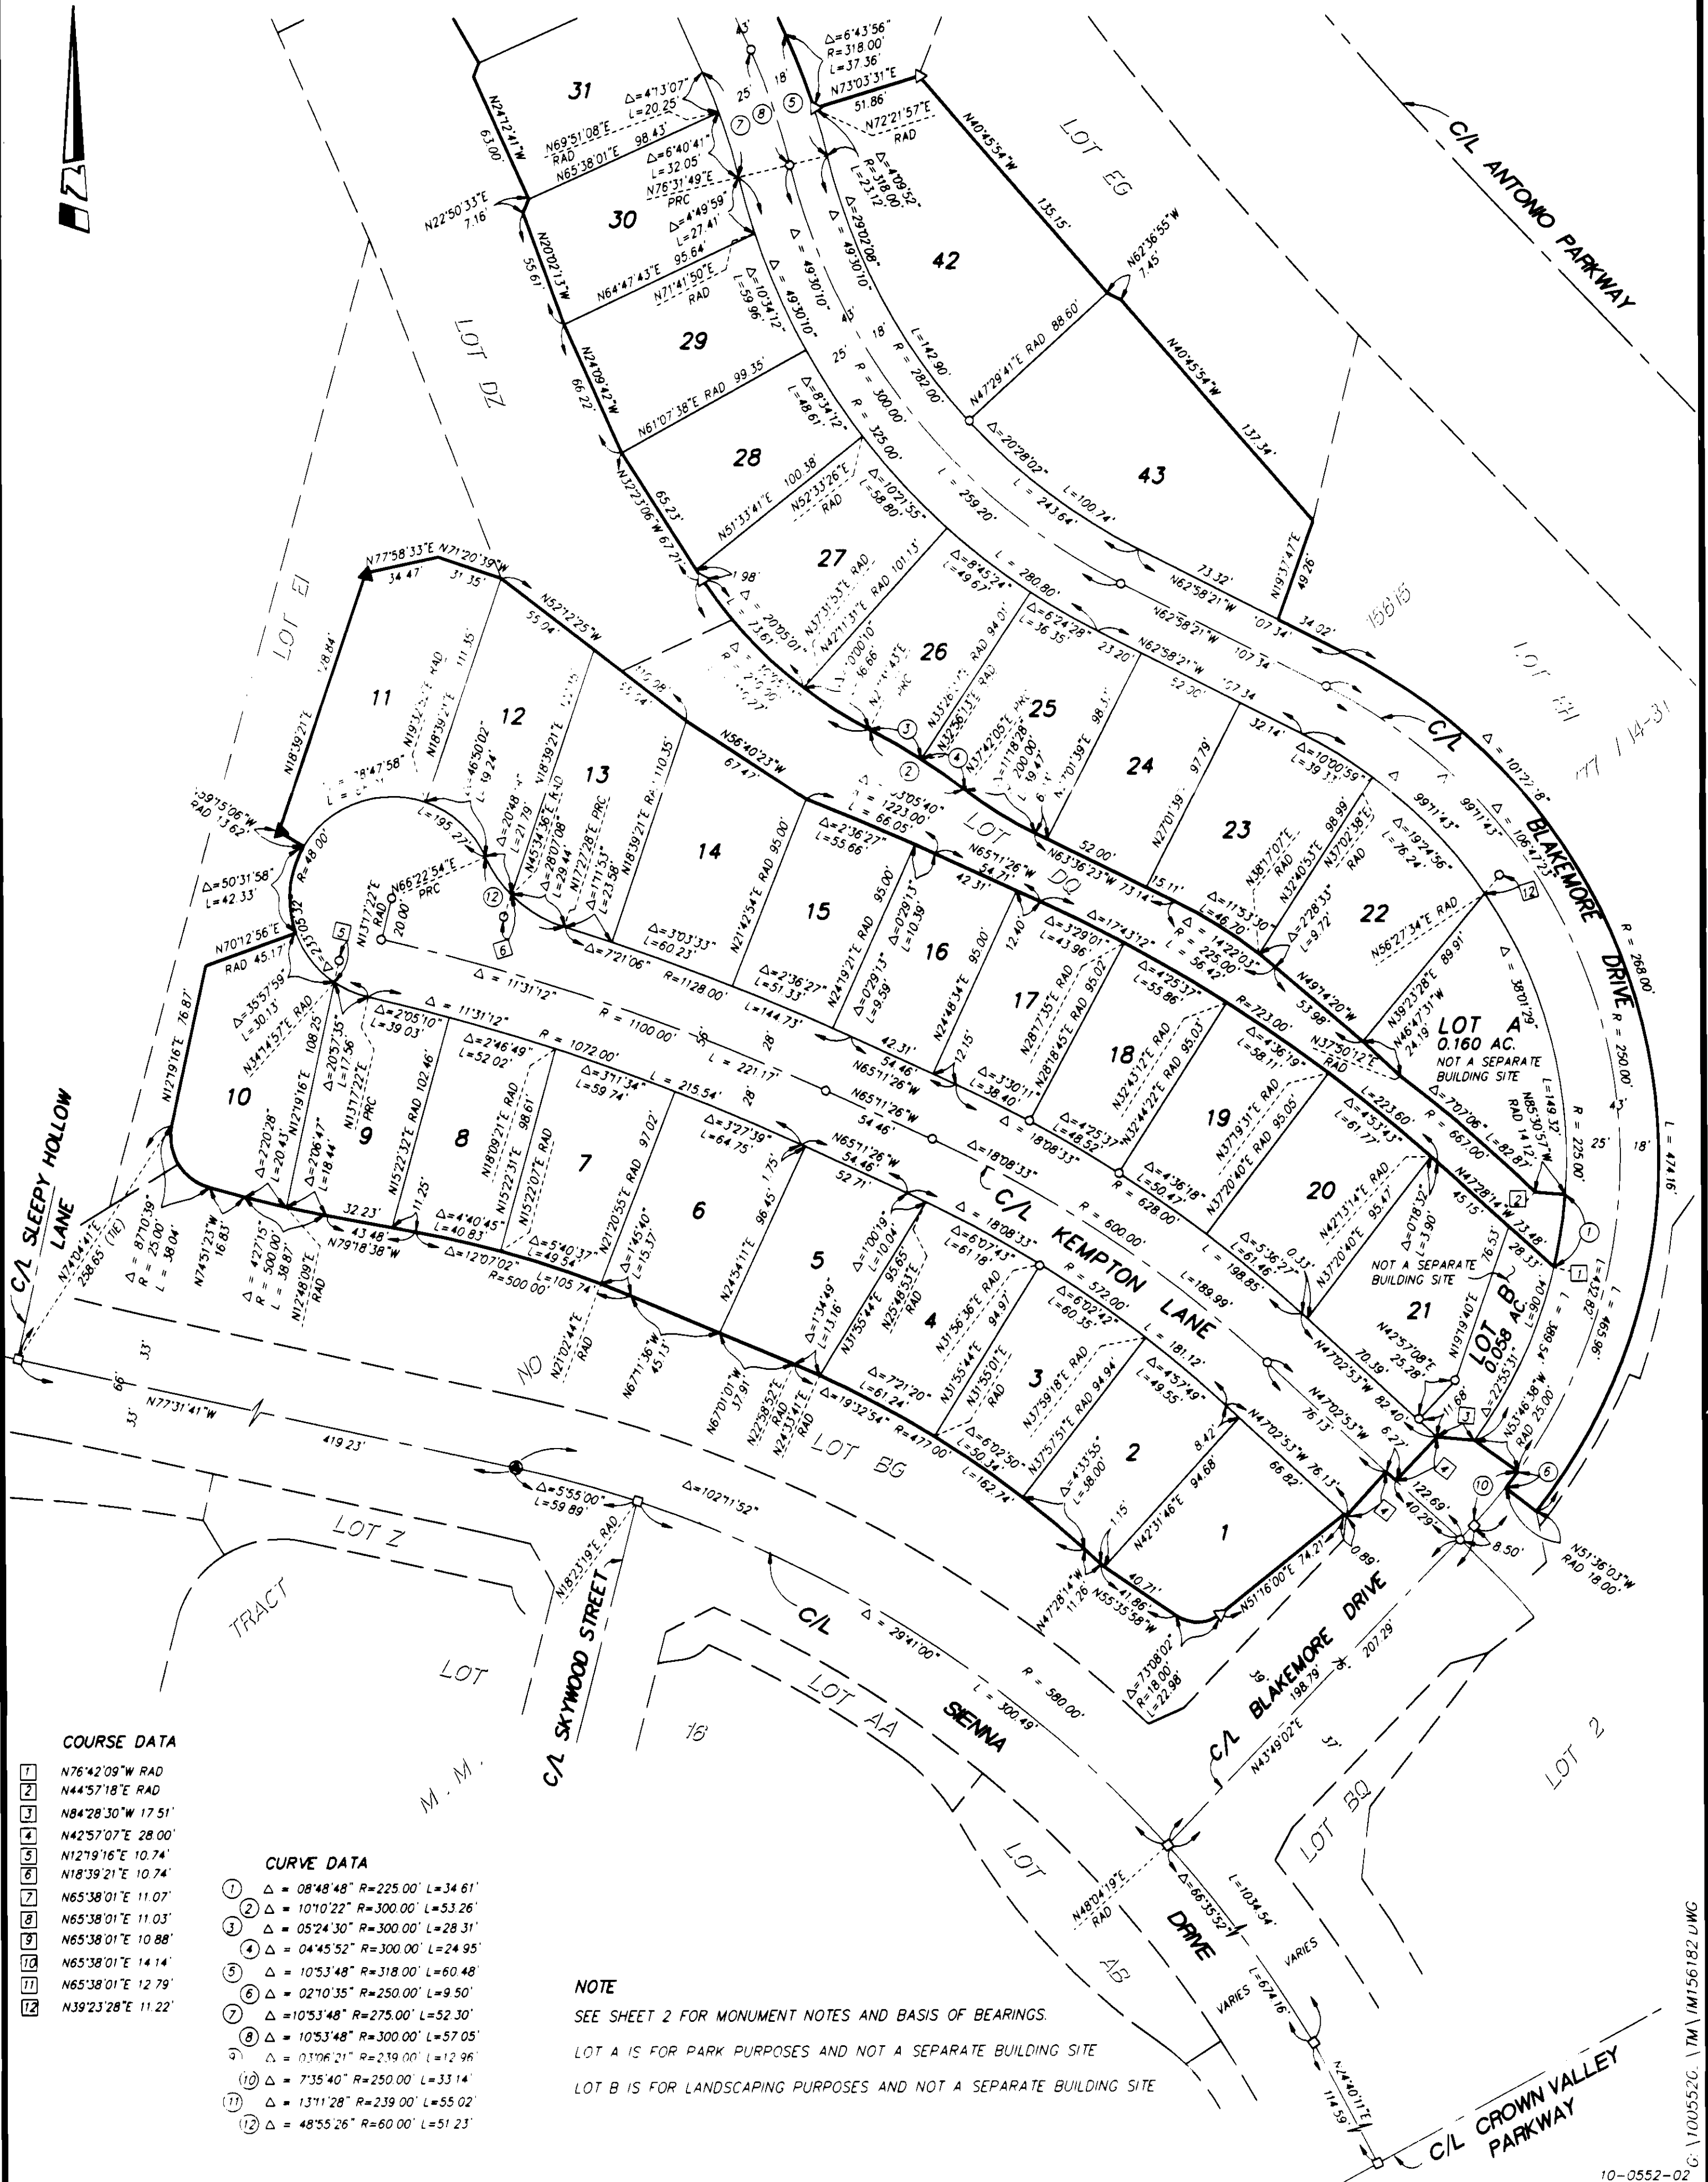

SHEET 4 OF 4 SHEETS

TRACT NO. 15618

IN UNINCORPORATED TERRITORY OF ORANGE COUNTY, CALIFORNIA

NOVEMBER 1998

JAMES F. GILLEN, L.S. 5557



HUITT-ZOLLARS, INC.

43 LOTS AND LOTS A AND B

8.574 ACRES

ALL OF VESTING TENTATIVE
TRACT NO. 15618

DATE OF SURVEY:
NOVEMBER 1997

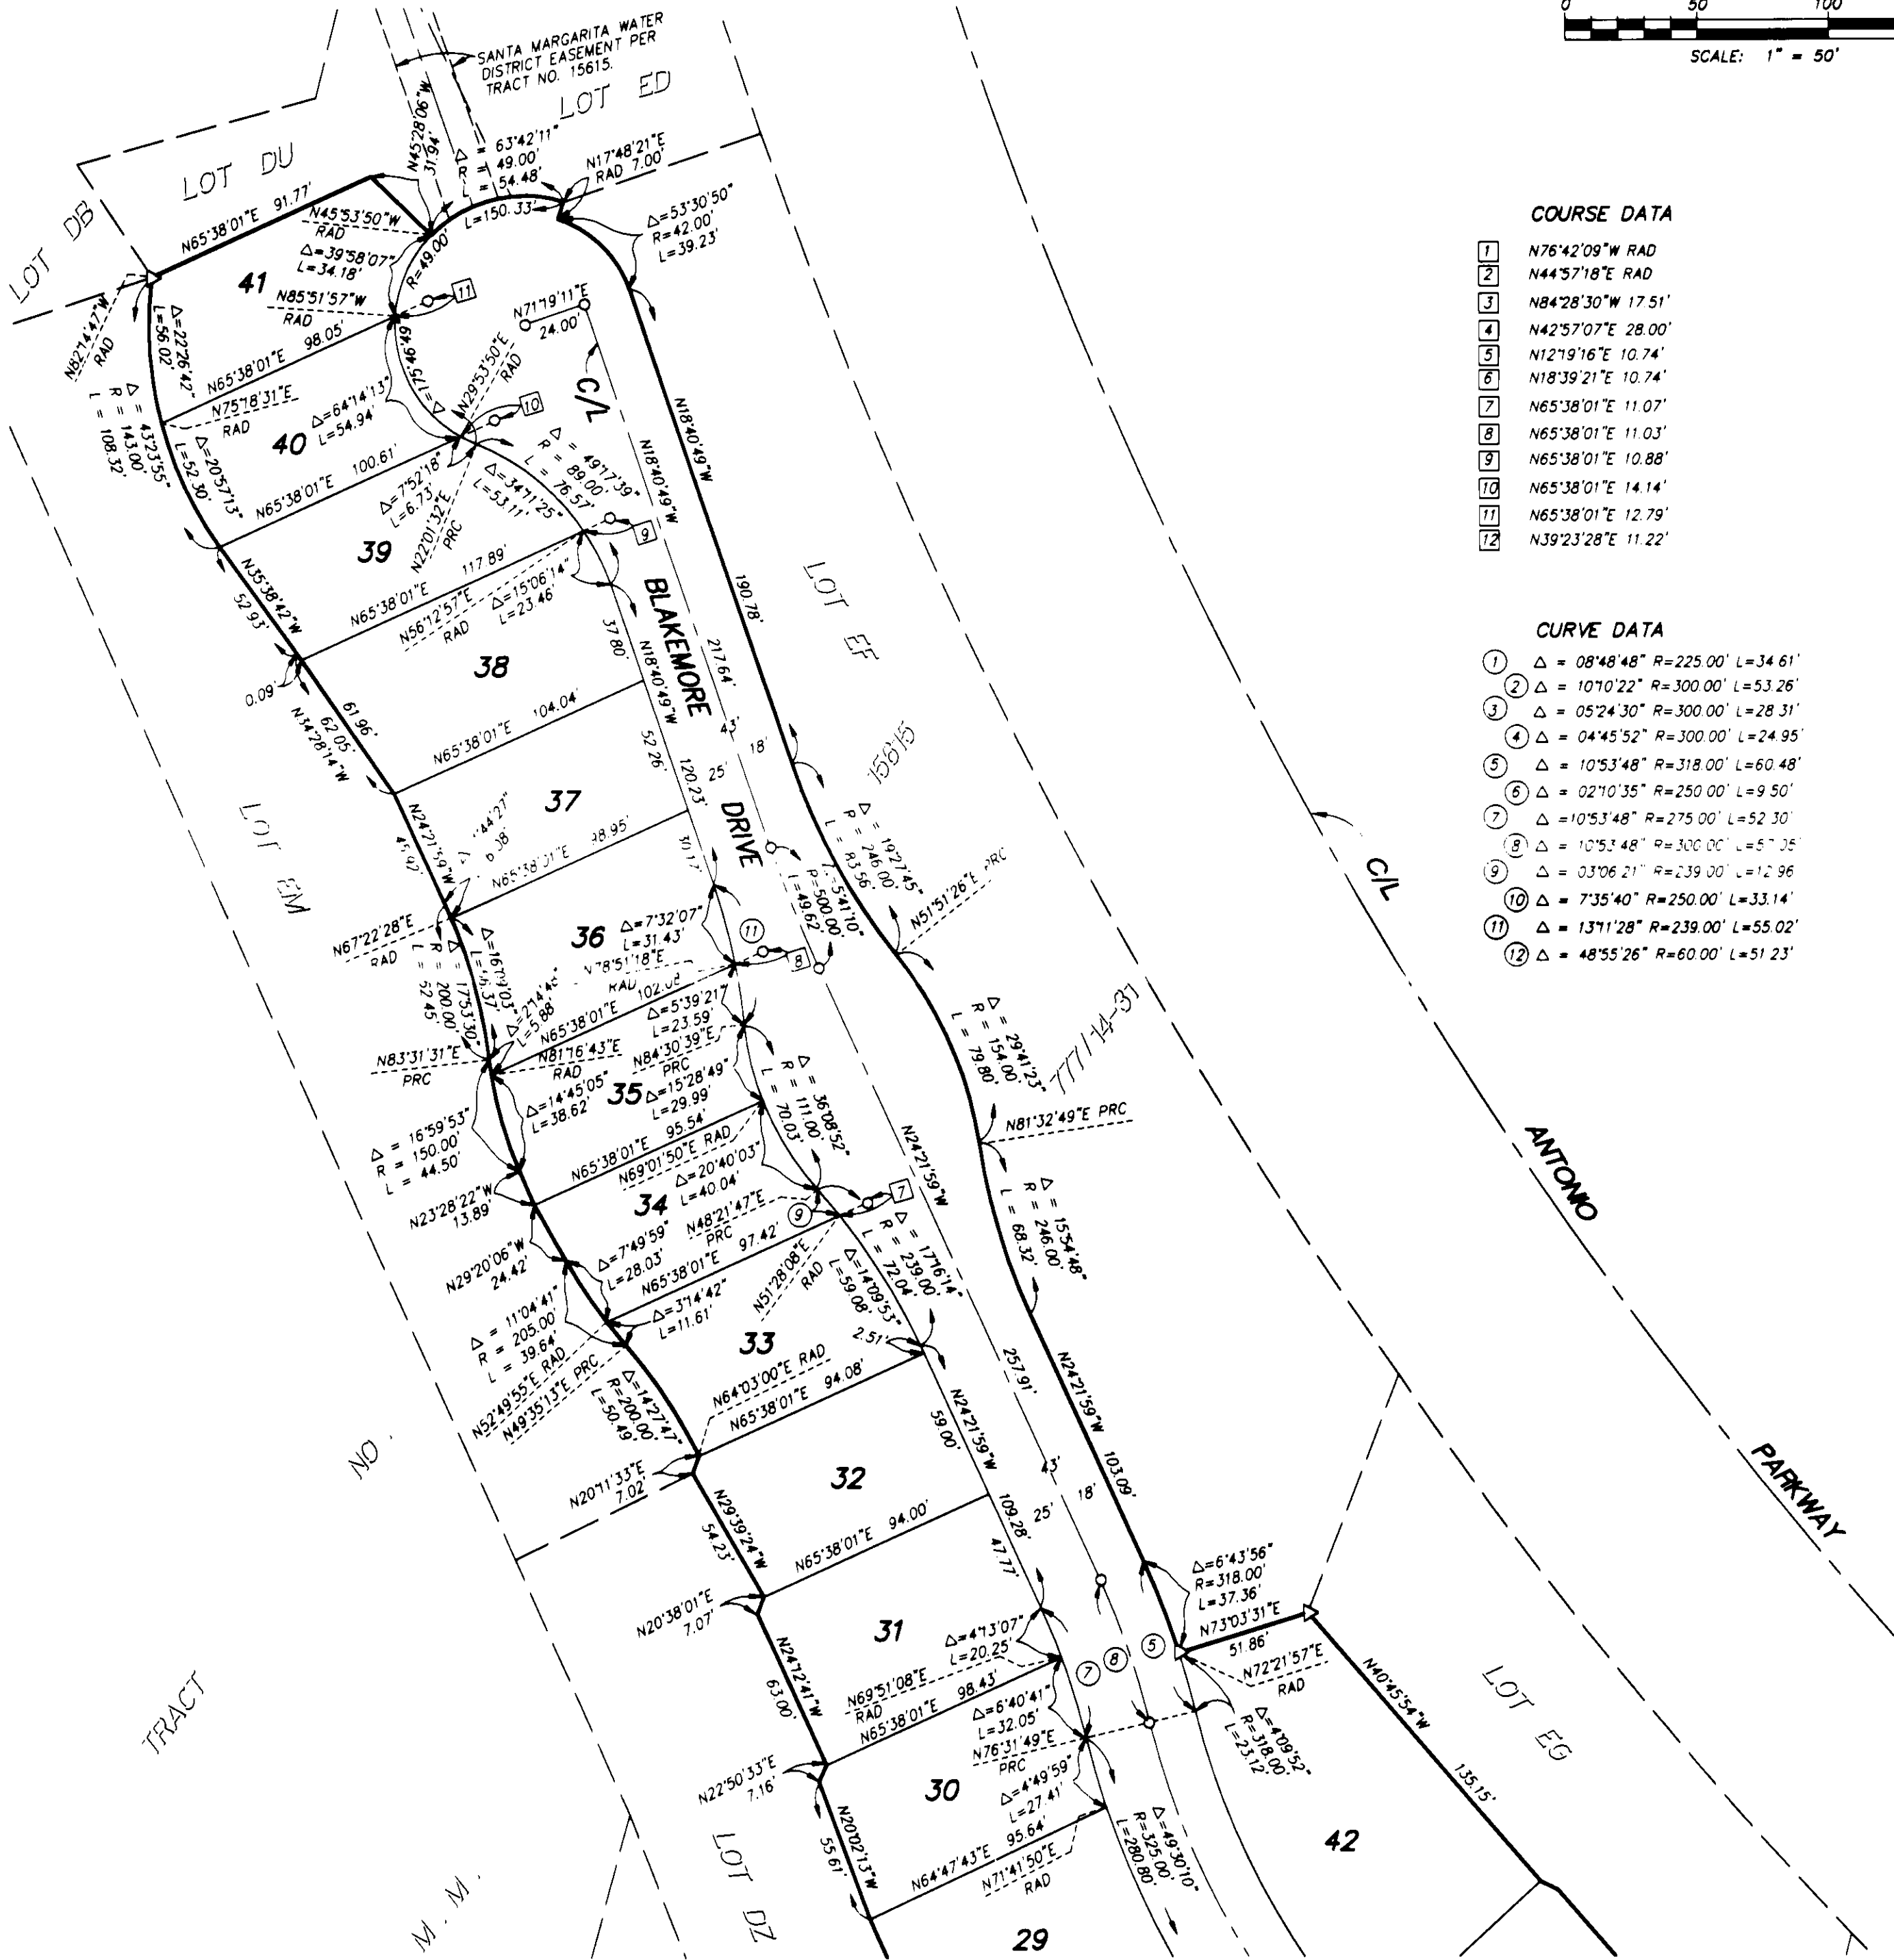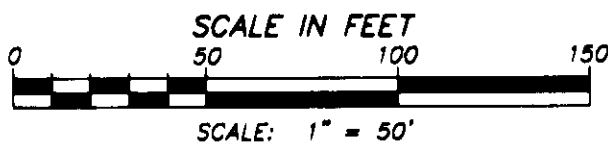

COURSE DATA

- | | |
|----|--------------------|
| 1 | N76°42'09"W RAD |
| 2 | N44°57'18"E RAD |
| 3 | N84°28'30"W 17.51' |
| 4 | N42°57'07"E 28.00' |
| 5 | N12°19'16"E 10.74' |
| 6 | N18°39'21"E 10.74' |
| 7 | N65°38'01"E 11.07' |
| 8 | N65°38'01"E 11.03' |
| 9 | N65°38'01"E 10.88' |
| 10 | N65°38'01"E 14.14' |
| 11 | N65°38'01"E 12.79' |
| 12 | N39°23'28"E 11.22' |

CURVE DATA

- | | |
|----|----------------------------------|
| 1 | Δ = 08°48'48" R=225.00' L=34.61' |
| 2 | Δ = 10°10'22" R=300.00' L=53.26' |
| 3 | Δ = 05°24'30" R=300.00' L=28.31' |
| 4 | Δ = 04°45'52" R=300.00' L=24.95' |
| 5 | Δ = 10°53'48" R=318.00' L=60.48' |
| 6 | Δ = 02°10'35" R=250.00' L=9.50' |
| 7 | Δ = 10°53'48" R=275.00' L=52.30' |
| 8 | Δ = 10°53'48" R=300.00' L=57.35' |
| 9 | Δ = 03°06'21" R=239.00' L=12.96' |
| 10 | Δ = 7°35'40" R=250.00' L=33.14' |
| 11 | Δ = 13°11'28" R=239.00' L=55.02' |
| 12 | Δ = 48°55'26" R=60.00' L=51.23' |

SEE SHEET 3

NOTE

SEE SHEET 2 FOR MONUMENT NOTES AND BASIS OF BEARINGS.

LOT A IS FOR PARK PURPOSES AND NOT A SEPARATE BUILDING SITE.

LOT B IS FOR LANDSCAPING PURPOSES AND NOT A SEPARATE BUILDING SITE.