

SHEET 1 OF 5 SHEETS

(ALL OF VESTING TENTATIVE
TRACT NO. 15629)TOTAL ACRES: 6.551 AC.
NUMBERED LOTS: 43
LETTERED LOTS: 5
DATE OF SURVEY: NOVEMBER 1997.

BLOCK: 5157 MODULE: 19,09,18,08

TRACT NO. 15629

IN THE UNINCORPORATED TERRITORY OF ORANGE COUNTY, STATE OF CALIFORNIA

BEING LOT 14 OF TRACT NO. 15615 IN THE UNINCORPORATED TERRITORY OF THE
COUNTY OF ORANGE, STATE OF CALIFORNIA, AS SHOWN ON A MAP FILED IN BOOK
777, PAGES 14 THROUGH 31 OF MISCELLANEOUS MAPS, RECORDS IN THE OFFICE
OF THE COUNTY RECORDER OF ORANGE COUNTY, CALIFORNIA.

DOUGLAS BENDER AND ASSOCIATES DOUGLAS W. BENDER R.C.E. 28946

SEPTEMBER, 1998

ACCEPTED AND FILED AT THE

REQUEST OF
FIRST AMERICAN TITLE INSURANCE COMPANYDATE June 30, 1999TIME 1:57 PM FEE \$15.00INSTRUMENT # 99-487365BOOK 787 PAGE 43-47GARY L. GRANVILLE
COUNTY CLERK-RECORDERBY Kathryn Watson
DEPUTYOWNERSHIP CERTIFICATE:WE, THE UNDERSIGNED, BEING ALL PARTIES HAVING ANY RECORD TITLE
INTEREST IN THE LAND COVERED BY THIS MAP, DO HEREBY CONSENT TO
THE PREPARATION AND RECORDATION OF SAID MAP, AS SHOWN WITHIN
THE DISTINCTIVE BORDER LINE.WE ALSO HEREBY DEDICATE TO THE PUBLIC FOR STREET PURPOSES
WALDEN STREET, BANCROFT STREET, AND BRAMFORD STREET.

WE ALSO HEREBY DEDICATE TO THE COUNTY OF ORANGE:



1. AN EASEMENT FOR STORM DRAIN PURPOSES AS SHOWN ON THIS
MAP.

WE ALSO HEREBY DEDICATE TO SANTA MARGARITA WATER DISTRICT, THE EASEMENTS FOR WATER AND
SEWER PIPELINES AND ACCESS PURPOSES AS SHOWN ON SAID MAP, SAID EASEMENTS SHALL BE
SUBJECT TO THE SAME TERMS AND CONDITIONS AS ARE SHOWN IN THAT CERTAIN EASEMENT RECORDED
OCTOBER 6, 1980 IN BOOK 13776, PAGE 341 OF OFFICIAL RECORDS, COUNTY OF ORANGE.THE SANTA MARGARITA WATER DISTRICT SHALL RESTORE OTHER IMPROVEMENTS OR FACILITIES LOCATED
WITHIN EASEMENT, IF IT HAS CONSENTED TO THE LOCATION OF SUCH IMPROVEMENTS OR FACILITIES TO
THE EXTENT THAT THE EXERCISE OF ITS RIGHTS IN CONNECTION WITH THE EASEMENT IMPACTS OTHER
IMPROVEMENTS OR FACILITIES LOCATED WITHIN THE EASEMENT, HOWEVER, IN NO EVENT SHALL SANTA
MARGARITA WATER DISTRICT BE RESPONSIBLE FOR THE COST OF RELOCATING ITS FACILITIES IN THE
EVENT OF CONFLICTS WITH SUCH THE IMPROVEMENTS OR FACILITIES.

BROOKFIELD SARASOTA INC., A CALIFORNIA CORPORATION, OWNER


JEFFREY PROSTOR
PRESIDENTDANIEL J. PEDLEY
CHIEF FINANCIAL OFFICERDMB LADERA, L.L.C., A DELAWARE LIMITED LIABILITY COMPANY, BENEFICIARY
UNDER A DEED OF TRUST RECORDED AS INST. NO. 19990203797 O.R.
BY: RANCHO MISSION VIEJO, LLC, A DELAWARE LIMITED LIABILITY COMPANY,
AS AGENT AND OR MANAGER.BY: Stephen C. Schrank
PRINT NAME: Stephen C. Schrank
PRINT TITLE: Exec. V.P.BY: Paul Johnson
PRINT NAME: PAUL JOHNSON
PRINT TITLE: V.P. - COMM. DEVEL

CERTIFICATE OF ACCEPTANCE - SANTA MARGARITA WATER DISTRICT

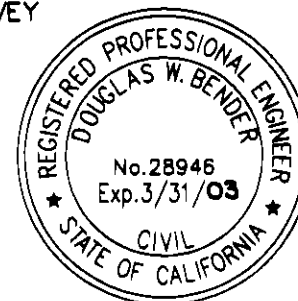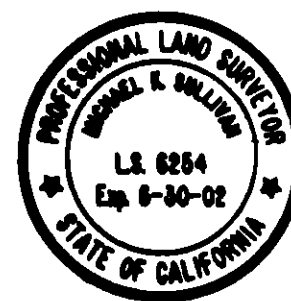THE UNDERSIGNED, BEING THE DULY APPOINTED AGENT OF THE SANTA MARGARITA WATER
DISTRICT, A PUBLIC CORPORATION OF ORANGE COUNTY, CALIFORNIA, PURSUANT TO ITS
RESOLUTION NO. 88-10-2 DOES HEREBY ACCEPT ON BEHALF OF SAID DISTRICT, THE EASEMENTS
FOR WATER AND SEWER PIPELINES AND ACCESS PURPOSES, AS DEDICATED AND SHOWN ON THIS
TRACT MAP BY AND BETWEEN THE SANTA MARGARITA WATER DISTRICT AND BROOKFIELD SARASOTA INC.
AND DOES HEREBY CERTIFY THAT THE GRANTEE CONSENTS TO THE RECORDATION OF SAID MAP.BY: Daniel R. Ferons
DANIEL R. FERONS, CHIEF ENGINEER
SANTA MARGARITA WATER DISTRICTENGINEER'S STATEMENT:I HEREBY STATE THAT THIS MAP CONSISTING OF 5 SHEETS, CORRECTLY REPRESENTS
A TRUE AND COMPLETE SURVEY AS SHOWN MADE IN NOVEMBER, 1997; WAS MADE BY
ME OR UNDER MY DIRECTION; THAT THE MONUMENTS ARE OF THE CHARACTER AND
OCCUPY (OR WILL OCCUPY) THE POSITIONS INDICATED BY SAID MAP; AND THAT
SAID MONUMENTS ARE (OR WILL BE) SUFFICIENT TO ENABLE THE SURVEY
TO BE RETRACED.DOUGLAS W. BENDER, R.C.E. 28946
MY REGISTRATION EXPIRES MARCH 31, 2003.COUNTY SURVEYOR'S STATEMENT:I HEREBY STATE THAT I HAVE EXAMINED THIS MAP AND HAVE FOUND IT TO BE
SUBSTANTIALLY IN CONFORMANCE WITH THE TENTATIVE MAP AS FILED WITH, AMENDED
AND APPROVED BY THE ORANGE COUNTY SUBDIVISION COMMITTEE; THAT ALL
PROVISIONS OF THE SUBDIVISION MAP ACT AND COUNTY SUBDIVISION REGULATIONS
HAVE BEEN COMPLIED WITH AND I AM SATISFIED SAID MAP IS TECHNICALLY CORRECT.DATED THIS 11TH DAY OF JUNE, 1999Michael K. Sullivan
JOHN CANAS, COUNTY SURVEYORBY: MICHAEL K. SULLIVAN, DEPUTY
L.S. 6254 EXPIRES 6-30-02CLERK OF THE BOARD OF SUPERVISOR'S CERTIFICATE:STATE OF CALIFORNIA)
COUNTY OF ORANGE)I HEREBY CERTIFY THAT THIS MAP WAS PRESENTED FOR APPROVAL TO THE BOARD OF
SUPERVISORS OF ORANGE COUNTY AT A REGULAR MEETING THEREOF HELD ON THE 22ND
DAY OF JUNE, 1999, AND THAT THEREUPON SAID BOARD DID, BY AN ORDER
DULY PASSED AND ENTERED, APPROVE SAID MAP AND DID ACCEPT ON BEHALF OF THE
PUBLIC, SUBJECT TO IMPROVEMENTS, THE DEDICATION FOR STREET PURPOSES:
WALDEN STREET, BANCROFT STREET, AND BRAMFORD STREET.

AND DID ALSO ACCEPT ON BEHALF OF THE COUNTY OF ORANGE:

1. AN EASEMENT FOR STORM DRAIN PURPOSES AS SHOWN ON THIS
MAP.

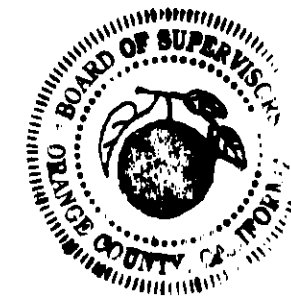DATED THIS 22ND DAY OF JUNE, 1999Darlene J. Bloom
CLERK OF THE BOARD OF SUPERVISORSCOUNTY TREASURER-TAX COLLECTOR'S CERTIFICATE:STATE OF CALIFORNIA)
COUNTY OF ORANGE)I HEREBY CERTIFY THAT ACCORDING TO THE RECORDS OF MY OFFICE THERE ARE NO
LIENS AGAINST THE LAND COVERED BY THIS MAP OR ANY PART THEREOF FOR UNPAID
STATE, COUNTY, MUNICIPAL OR LOCAL TAXES OR SPECIAL ASSESSMENTS COLLECTED
AS TAXES, EXCEPT TAXES OR SPECIAL ASSESSMENTS COLLECTED AS TAXES NOT YET
PAYABLE.AND DO ALSO CERTIFY TO THE RECORDER OF ORANGE COUNTY THAT THE PROVISIONS OF
THE SUBDIVISION MAP ACT HAVE BEEN COMPLIED WITH REGARDING DEPOSITS TO
SECURE THE PAYMENT OF TAXES OR SPECIAL ASSESSMENTS COLLECTED AS TAXES ON
THE LAND COVERED BY THIS MAP.DATED THIS 3 DAY OF MAY, 1999.JOHN M.W. MOORLACH
COUNTY TREASURER-TAX COLLECTOR

BY: DEPUTY TREASURER-TAX COLLECTOR

Darlene J. Bloom

SIGNATURE OMISSIONS:

PURSUANT TO SECTION 66436 (a) (3) OF THE SUBDIVISION MAP ACT, THE FOLLOWING
SIGNATURES HAVE BEEN OMITTED:

1. LADERA DEVELOPMENT COMPANY, L.L.C., HOLDER OF OIL, GAS AND MINERAL RIGHTS
RECORDED DECEMBER 10, 1996 AS INSTRUMENT NO. 19960624029 OF OFFICIAL RECORDS.
2. DMB LADERA, L.L.C. HOLDER OF EASEMENT RESERVED IN A DEED RECORDED APRIL 16, 1999
1999 AS INSTRUMENT NO. 990203797 OFFICIAL RECORDS.

AUTOMATIC FIRE SPRINKLER NOTE:

ALL COMMERCIAL STRUCTURES OVER 6,000 SQUARE FEET; ALL MULTIFAMILY RESIDENTIAL
STRUCTURES; ALL DETACHED, SINGLE-FAMILY STRUCTURES EXCEEDING 5,500 SQUARE FEET,
AND ALL STRUCTURES EXCEEDING FIRE AUTHORITY ACCESS REQUIREMENTS SHALL BE
PROTECTED BY AN AUTOMATIC SPRINKLER SYSTEM, IN A MANNER MEETING THE APPROVAL
OF THE FIRE CHIEF.

SPECIAL FIRE PROTECTION NOTE:

PROPERTY IS IN A SPECIAL FIRE PROTECTION AREA AND MUST MEET ALL REQUIREMENTS
FOR DEVELOPMENT WITHIN THE AREA.

HIGH FIRE HAZARD AREA NOTE:

THE LOTS SHOWN ON THIS MAP ARE IN A HIGH FIRE HAZARD AREA DUE TO
WILD LAND EXPOSURE.

NOTES:

PROPERTY MAY BE SUBJECT TO IMPACTS FROM THE FOOTHILL/EASTERN
TRANSPORTATION CORRIDOR.787
43

SHEET 2 OF 5 SHEETS

(ALL OF VESTING TENTATIVE
TRACT NO. 15629)TOTAL ACRES: 6.551 AC.
NUMBERED LOTS: 43
LETTERED LOTS: 5
DATE OF SURVEY: NOVEMBER 1997.

TRACT NO. 15629

IN THE UNINCORPORATED TERRITORY OF ORANGE COUNTY, STATE OF CALIFORNIA

DOUGLAS BENDER AND ASSOCIATES DOUGLAS W. BENDER R.C.E. 28946

SEPTEMBER, 1998

BROOKFIELD SARASOTA INC.STATE OF CALIFORNIA)
) SS
COUNTY OF ORANGE)

ON THIS 20th day of April, 1999, BEFORE ME, JULIE McNATT,
A NOTARY PUBLIC IN AND FOR SAID STATE, PERSONALLY APPEARED
JEFFREY PROSTOR AND DANIEL J. PEDLEY
PERSONALLY KNOWN TO ME (OR ~~PROVED TO ME ON THE BASIS OF SATISFACTORY EVIDENCE~~)
TO BE THE PERSON (S) WHOSE NAME (S) IS/ARE SUBSCRIBED TO THE WITHIN INSTRUMENT
AND ACKNOWLEDGED TO ME THAT HE/SHE/THEY EXECUTED THE SAME IN HIS/HER/THEIR
AUTHORIZED CAPACITY (IES), AND THAT BY HIS/HER/THEIR SIGNATURE (S) ON THE
INSTRUMENT THE PERSON (S), OR THE ENTITY UPON BEHALF OF WHICH THE PERSON (S)
ACTED, EXECUTED THE INSTRUMENT.

WITNESS MY HAND:

SIGNATURE *Julie McNatt*
NOTARY PUBLIC IN AND FOR SAID STATEMY PRINCIPAL PLACE OF BUSINESS IS
IN Orange COUNTY.JULIE McNATT
(NAME PRINTED)MY COMMISSION EXPIRES 5/22/2002SANTA MARGARITA WATER DISTRICTSTATE OF CALIFORNIA)
COUNTY OF ORANGE) SS

ON THIS 23rd of April, 1999, BEFORE ME, ANDREA M. EVANS,
A NOTARY PUBLIC IN AND FOR SAID STATE, PERSONALLY APPEARED
DANIEL R. FERONS
PERSONALLY KNOWN TO ME (OR ~~PROVED TO ME ON THE BASIS OF SATISFACTORY EVIDENCE~~)
TO BE THE PERSON (S) WHOSE NAME (S) IS/ARE SUBSCRIBED TO THE WITHIN INSTRUMENT
AND ACKNOWLEDGED TO ME THAT HE/SHE/THEY EXECUTED THE SAME IN HIS/HER/THEIR
AUTHORIZED CAPACITY (IES), AND THAT BY HIS/HER/THEIR SIGNATURE (S) ON THE
INSTRUMENT THE PERSON (S), OR THE ENTITY UPON BEHALF OF WHICH THE PERSON (S)
ACTED, EXECUTED THE INSTRUMENT.

WITNESS MY HAND:

SIGNATURE *Andrea M. Evans*
NOTARY PUBLIC IN AND FOR SAID STATEMY PRINCIPAL PLACE OF BUSINESS IS
IN ORANGE COUNTY.ANDREA M. EVANS
(NAME PRINTED)MY COMMISSION EXPIRES 3-17-00DMB LADERA, L.L.C.STATE OF CALIFORNIA)
COUNTY OF ORANGE) SS

ON THIS 22nd of April 1999, BEFORE ME, M. Kristin King,
A NOTARY PUBLIC IN AND FOR SAID STATE, PERSONALLY APPEARED
Stephen C. Schrank and Paul Johnson
PERSONALLY KNOWN TO ME (OR ~~PROVED TO ME ON THE BASIS OF SATISFACTORY EVIDENCE~~)
TO BE THE PERSON (S) WHOSE NAME (S) IS/ARE SUBSCRIBED TO THE WITHIN INSTRUMENT
AND ACKNOWLEDGED TO ME THAT HE/SHE/THEY EXECUTED THE SAME IN HIS/HER/THEIR
AUTHORIZED CAPACITY (IES), AND THAT BY HIS/HER/THEIR SIGNATURE (S) ON THE
INSTRUMENT THE PERSON (S), OR THE ENTITY UPON BEHALF OF WHICH THE PERSON (S)
ACTED, EXECUTED THE INSTRUMENT.

WITNESS MY HAND:

SIGNATURE *M. Kristin King*
NOTARY PUBLIC IN AND FOR SAID STATEMY PRINCIPAL PLACE OF BUSINESS IS
IN Orange COUNTY.M. Kristin King
(NAME PRINTED)MY COMMISSION EXPIRES 9-29-00

SHEET 3 OF 5 SHEETS

(VESTING TENTATIVE
TRACT NO. 15629)
TOTAL ACRES: 6.551 AC.
NUMBERED LOTS: 43
LETTERED LOTS: 5
DATE OF SURVEY: NOVEMBER, 1997.

TRACT NO. 15629

IN THE UNINCORPORATED TERRITORY OF ORANGE COUNTY, STATE OF CALIFORNIA
DOUGLAS BENDER AND ASSOCIATES DOUGLAS W. BENDER R.C.E. 28946

MONUMENT NOTES:

- 2" I.P. TAGGED RCE 28946 OR A LEAD & TAG RCE 28946 IN CONCRETE OR AN 8" SPIKE & WASHER STAMPED RCE 28946 IN ASPHALT PAVING TO BE SET AT ALL TRACT CORNERS, WITHIN 90 DAYS AFTER ACCEPTANCE OF IMPROVEMENTS, UNLESS OTHERWISE NOTED.
- 1" I.P. TAGGED RCE 28946 OR A LEAD & TAG RCE 28946 IN CONCRETE TO BE SET AT ALL LOT CORNERS EXCEPT LOT CORNERS THAT ABUTS A STREET WHICH WILL BE MARKED ON A 4.25" OFFSET OUTSIDE THE TRUE LOT CORNER IN CONCRETE BY A LEAD AND TAG "RCE 28946" ON SIDELINES PRODUCED, UNLESS OTHERWISE NOTED. (NO MONUMENTS WILL BE SET FOR ANGLE POINTS, CORNER CUT-OFFS, B.C.'S, E.C.'S, P.C.C.'S OR P.R.C.'S THAT ABUT STREET WHICH ARE NOT LOT CORNERS MARKING SIDELINES, UNLESS OTHERWISE NOTED.)
- 8" SPIKE & WASHER STAMPED RCE 28946 IN ASPHALT PAVING OR LEAD & TAG RCE 28946 IN CONCRETE TO BE SET AT ALL CENTERLINE INTERSECTIONS, B.C.'S, E.C.'S AND ALL OTHER CENTERLINE POINTS OF CONTROL, UNLESS OTHERWISE NOTED, WITHIN 90 DAYS AFTER ACCEPTANCE OF IMPROVEMENTS.
- INDICATES 1" I.P. TAGGED "L.S. 5557" OR SPIKE & WASHER STAMPED "L.S. 5557" OR LEAD, TACK & TAG "L.S. 5557" TO BE SET PER TRACT NO. 15615 M.M. 777/14-31.
- INDICATES 2" I.P. TAGGED "L.S. 5557" OR SPIKE & WASHER STAMPED "L.S. 5557" OR LEAD, TACK & TAG "L.S. 5557" TO BE SET PER TRACT NO. 15615 M.M. 777/14-31.
- △ INDICATES FOUND ORANGE COUNTY GPS MONUMENT AS NOTED.
- INDICATES SET 2" I.P. TAGGED R.C.E. 28946 PRIOR TO RECORDATION.

EASEMENT NOTES:

- (A) INDICATES AN EASEMENT FOR STORM DRAIN PURPOSES DEDICATED TO THE COUNTY OF ORANGE.
- (B) INDICATES AN EASEMENT FOR SEWER AND WATER PURPOSES DEDICATED TO THE SANTA MARGARITA WATER DISTRICT.
- (C) INDICATES AN EASEMENT FOR SEWER PURPOSES DEDICATED TO THE SANTA MARGARITA WATER DISTRICT.

SCALE: 1" = 80'

BASIS OF BEARINGS:


BEARINGS SHOWN HEREON ARE BASED ON THE LINE BETWEEN O.C.S. HORIZONTAL CONTROL STATION GPS NO. 9009 AND STATION NO. 1426 BEARING N81°10'47"E PER RECORDS ON FILE IN THE OFFICE OF THE ORANGE COUNTY SURVEYOR.

DATUM STATEMENT:

COORDINATES SHOWN HEREON ARE BASED UPON THE CALIFORNIA COORDINATE SYSTEM (CCCS83) ZONE VI 1983 NAD (1981.35 EPOCH O.C.S. GPS ADJUSTMENT). ALL DISTANCES SHOWN ARE GROUND DISTANCES UNLESS OTHERWISE NOTED. TO OBTAIN GRID DISTANCE, MULTIPLY GROUND DISTANCE BY .99993923.

NOTE:

LOTS A THROUGH E ARE LANDSCAPE LOTS AND ARE NOT SEPARATE BUILDING SITES.

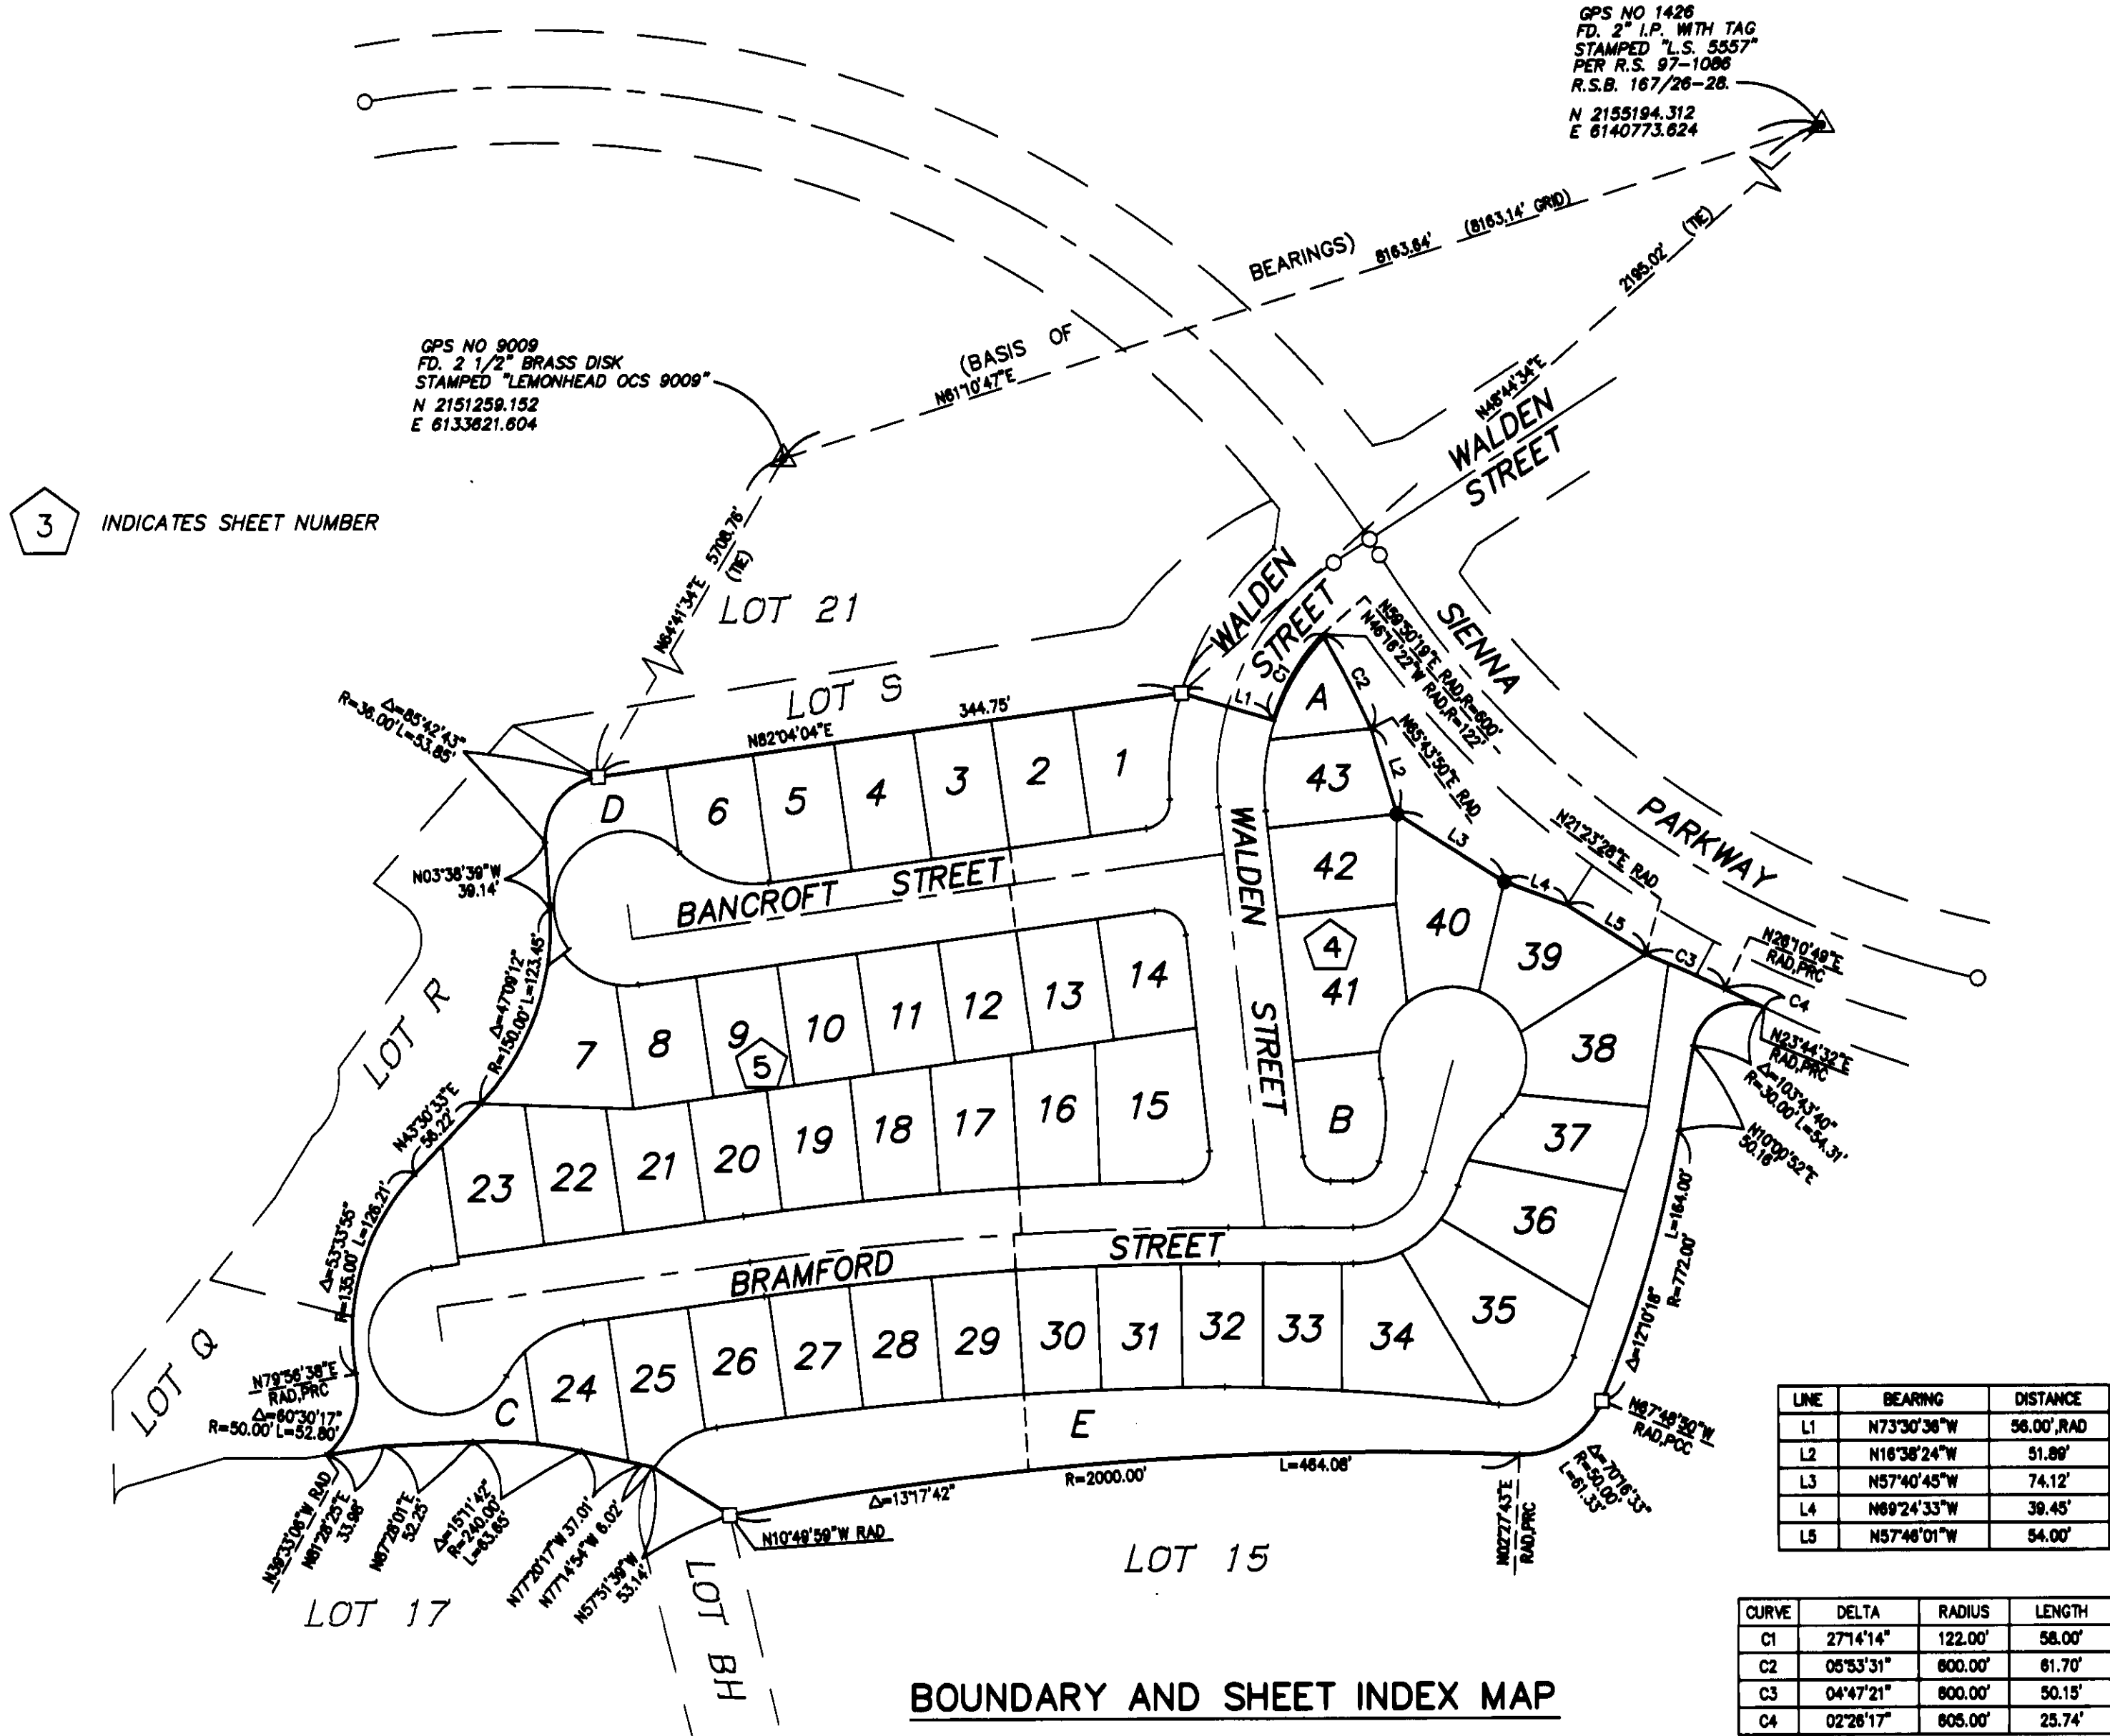

SHEET 4 OF 5 SHEETS

(VESTING TENTATIVE
TRACT NO. 15629)

TOTAL ACRES: 6.551 AC.
NUMBERED LOTS: 43
LETTERED LOTS: 5
DATE OF SURVEY: NOVEMBER, 1997.

TRACT NO. 15629

IN THE UNINCORPORATED TERRITORY OF ORANGE COUNTY, STATE OF CALIFORNIA


DOUGLAS BENDER AND ASSOCIATES DOUGLAS W. BENDER R.C.E. 28946

SEE SHEET 3 FOR BASIS OF BEARINGS, DATUM STATEMENT, MONUMENT
NOTES, EASEMENT NOTES AND BOUNDARY AND SHEET INDEX MAP.

SCALE: 1" = 40'

LINE	BEARING	DISTANCE
L1	N73°30'36"W	56.00' RAD
L3	N89°53'24"W	13.21'

CURVE	DELTA	RADIUS	LENGTH
C1	83°58'37"	18.00'	23.44'
C2	91°54'56"	18.00'	25.67'
C3	82°12'31"	18.00'	22.96'
C4	95°22'05"	18.00'	26.63'
C5	00°23'56"	2030.00'	14.13'
C6	27°14'14"	122.00'	58.00'
C7	02°26'17"	605.000'	25.74'
C8	83°48'12"	17.00'	24.86'
C9	251°7'48"	92.00'	40.82'
C10	23°27'56"	48.00'	18.84'

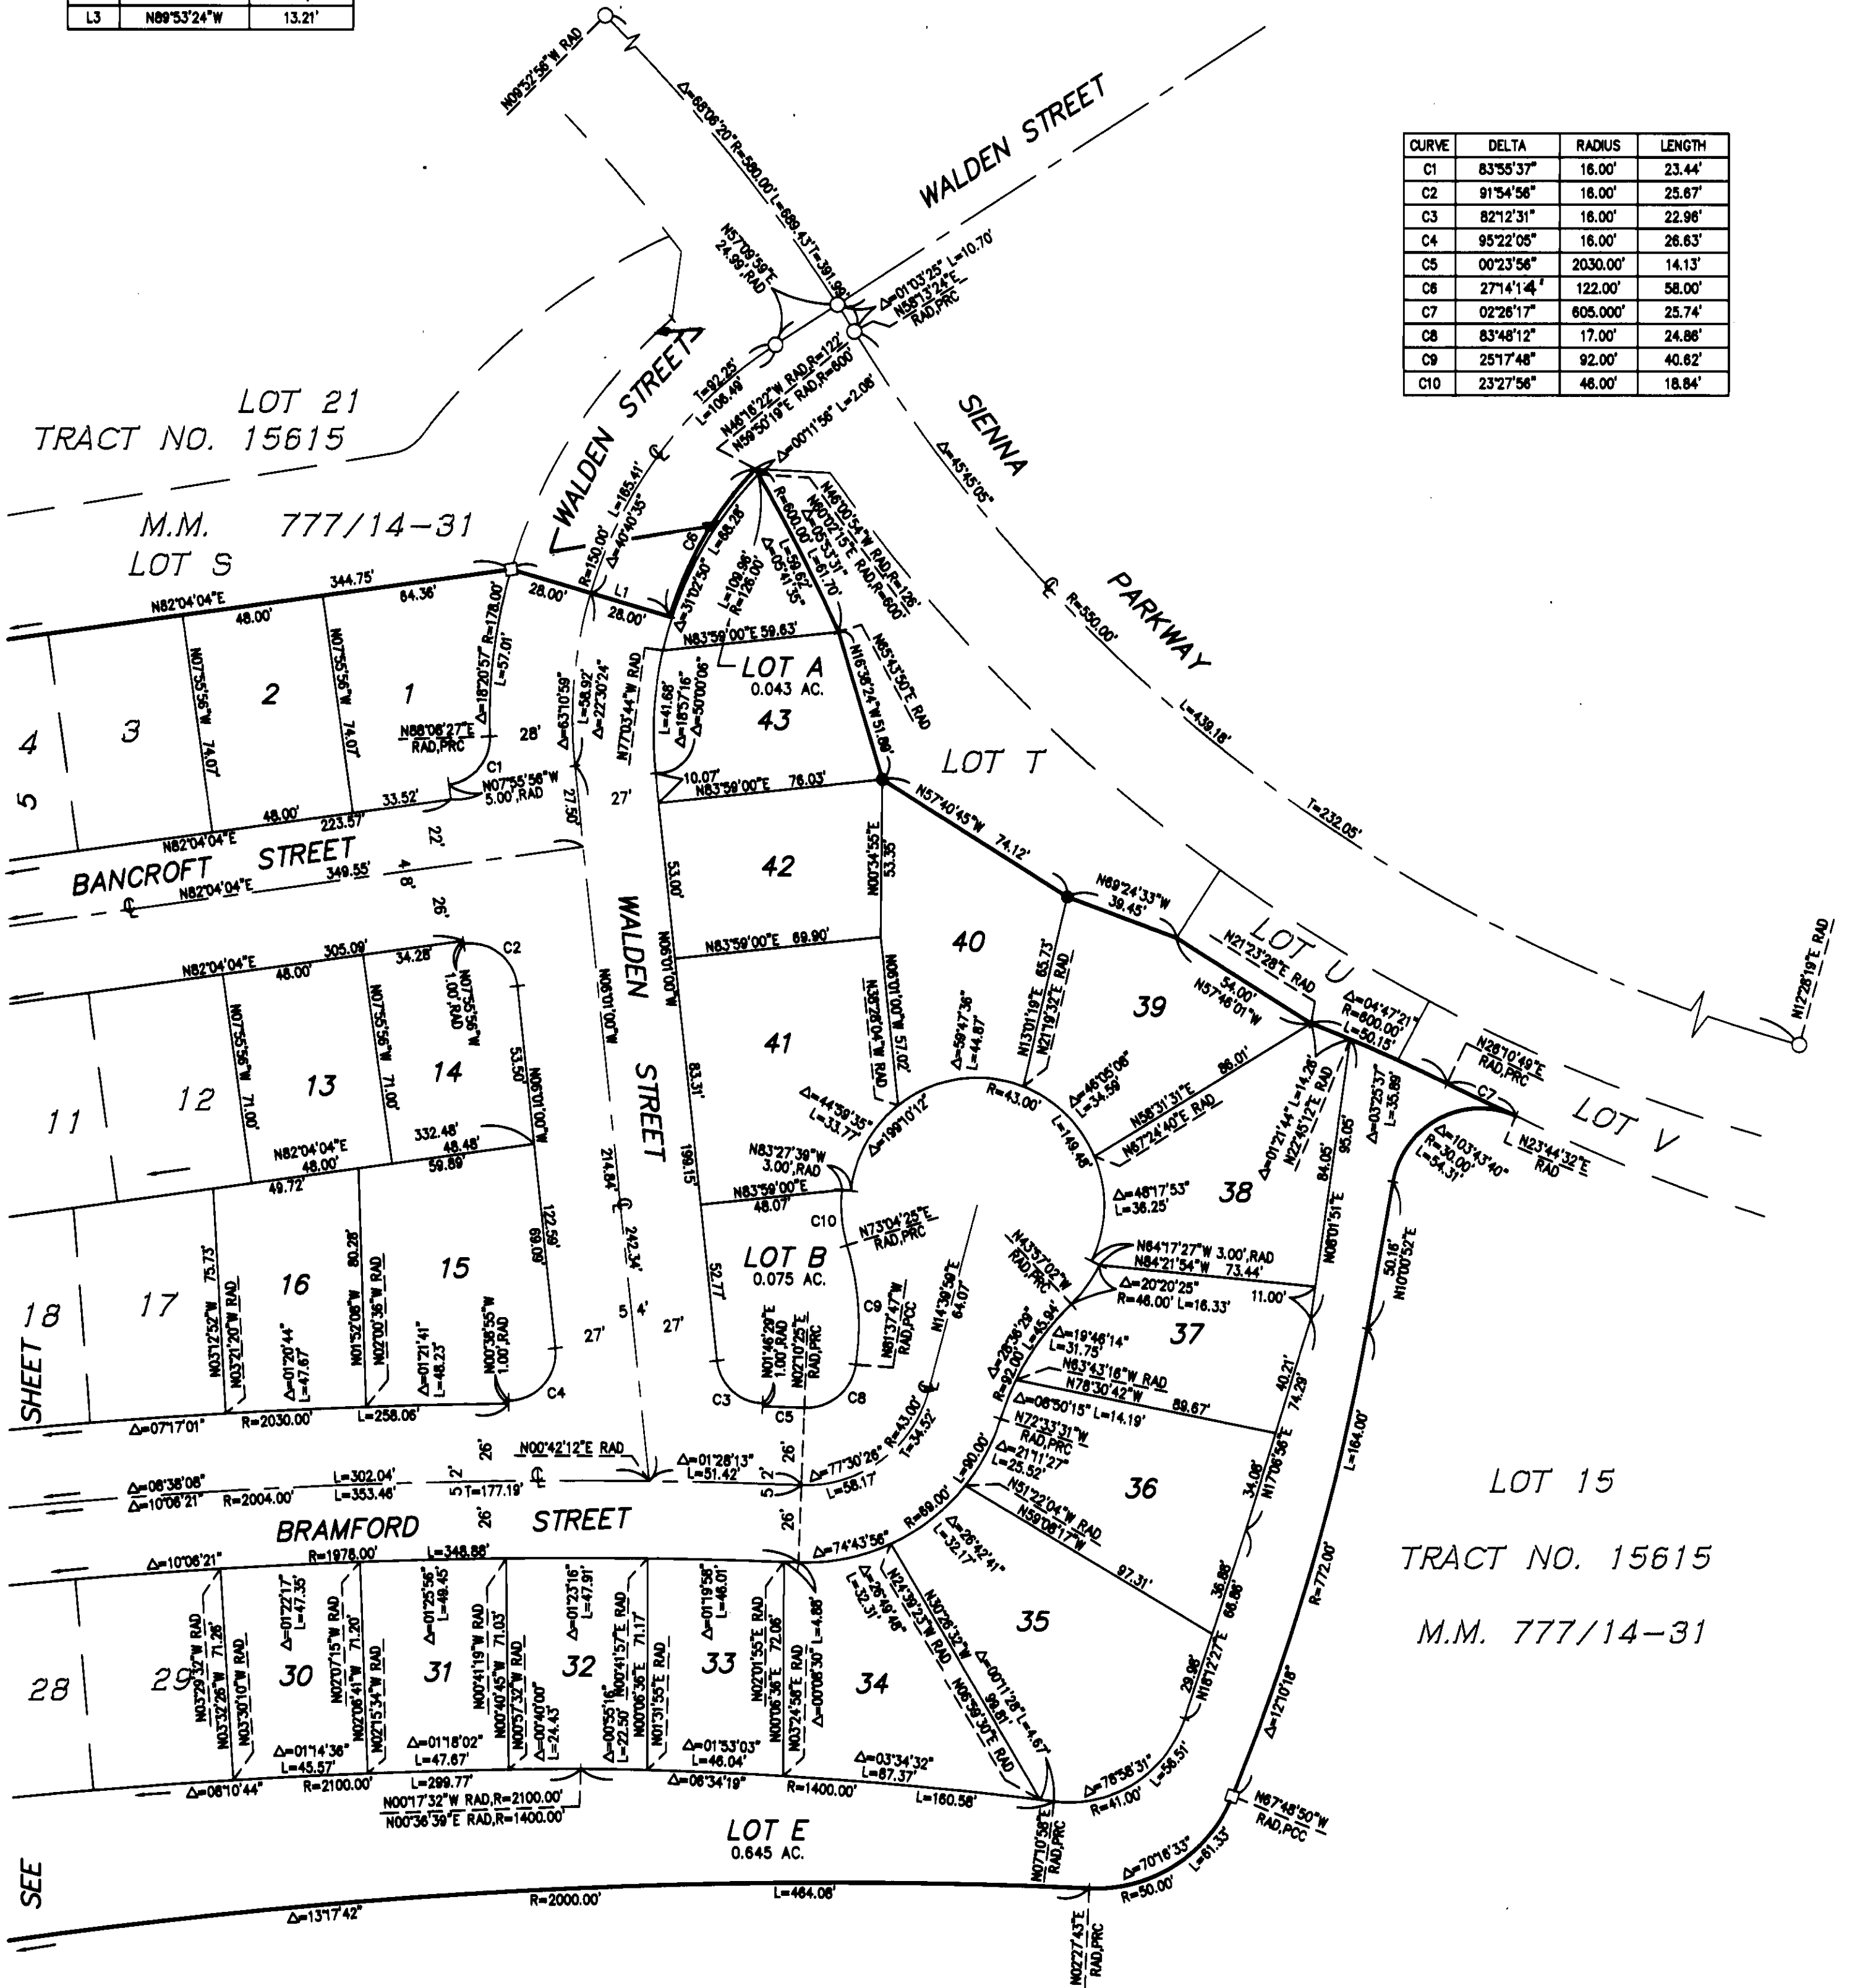

EASEMENT NOTES:

- (A) INDICATES AN EASEMENT FOR STORM DRAIN PURPOSES DEDICATED TO THE COUNTY OF ORANGE.
- (B) INDICATES AN EASEMENT FOR SEWER AND WATER PURPOSES DEDICATED TO THE SANTA MARGARITA WATER DISTRICT.
- (C) INDICATES AN EASEMENT FOR SEWER PURPOSES DEDICATED TO THE SANTA MARGARITA WATER DISTRICT.

SHEET 5 OF 5 SHEETS

(VESTING TENTATIVE
TRACT NO. 15629)

TOTAL ACRES: 6.551 AC.
NUMBERED LOTS: 43
LETTERED LOTS: 5
DATE OF SURVEY: NOVEMBER, 1997.

TRACT NO. 15629

IN THE UNINCORPORATED TERRITORY OF ORANGE COUNTY, STATE OF CALIFORNIA




DOUGLAS BENDER AND ASSOCIATES DOUGLAS W. BENDER R.C.E. 28946

SEE SHEET 3 FOR BASIS OF BEARINGS, DATUM STATEMENT, MONUMENT NOTES, EASEMENT NOTES AND BOUNDARY AND SHEET INDEX MAP.

LINE	BEARING	DISTANCE
L2	N52°57'47"E	15.71' RAD
L4	N48°28'12"W	50.40'
L5	N82°04'04"E	2.47'

CURVE	DELTA	RADIUS	LENGTH
C11	14°28'38"	65.00'	16.39'

SCALE: 1" = 40'

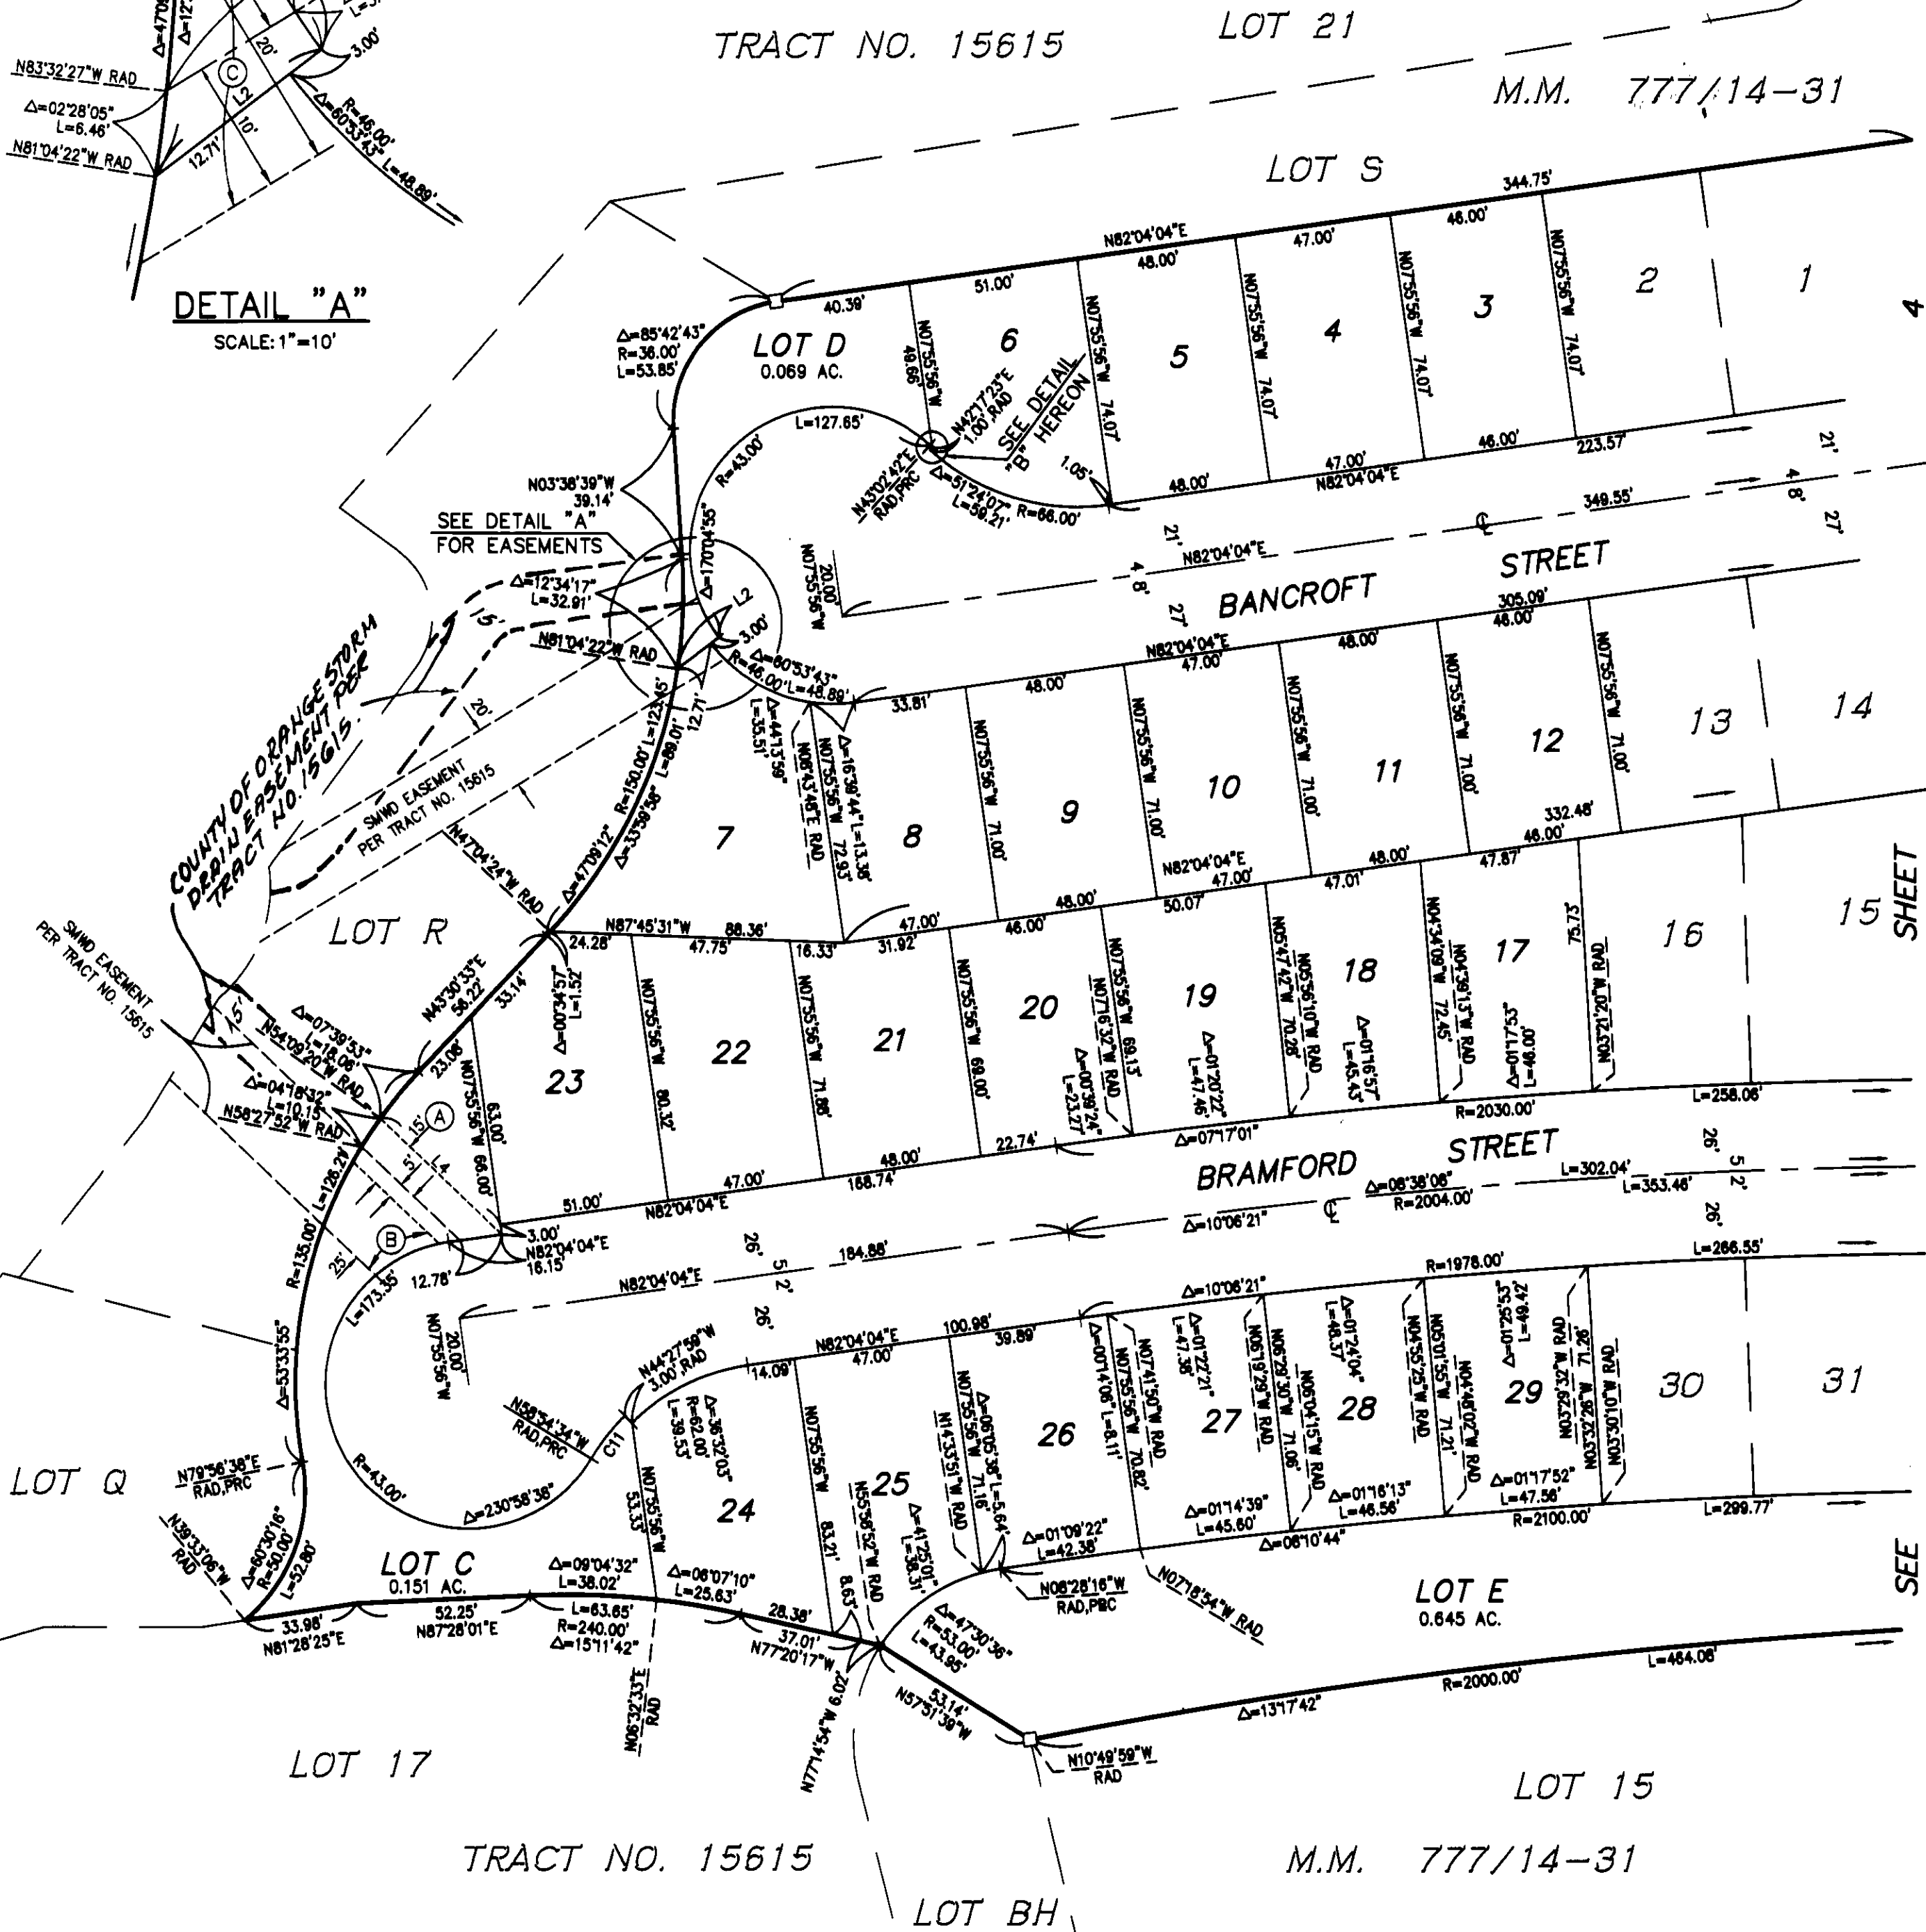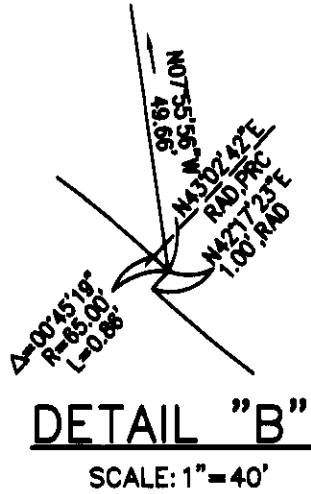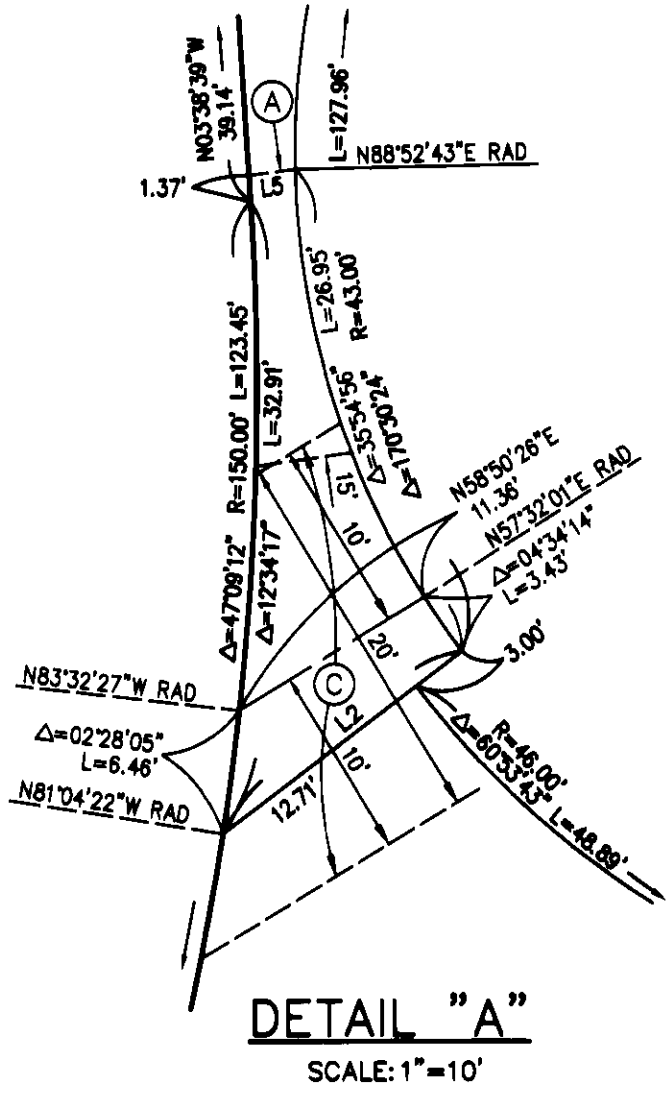

EASEMENT NOTES:

- (A) INDICATES AN EASEMENT FOR STORM DRAIN PURPOSES DEDICATED TO THE COUNTY OF ORANGE.
- (B) INDICATES AN EASEMENT FOR SEWER AND WATER PURPOSES DEDICATED TO THE SANTA MARGARITA WATER DISTRICT.
- (C) INDICATES AN EASEMENT FOR SEWER PURPOSES DEDICATED TO THE SANTA MARGARITA WATER DISTRICT.