

DUPLICATE

897

28

SHEET 1 OF 6 SHEETS

TRACT NO. 15793

ACCEPTED AND FILED AT THE REQUEST OF

FIRST AMERICAN TITLE INSURANCE CO.

ALL OF VESTING TENTATIVE TRACT NO. 15793

IN THE UNINCORPORATED TERRITORY OF ORANGE COUNTY, CALIFORNIA
BEING A SUBDIVISION OF A PORTION OF PARCEL 1 OF LOT LINE ADJUSTMENT NO. LL 96-026
AS SHOWN ON EXHIBIT "B" ATTACHED TO THAT CERTAIN DOCUMENT RECORDED NOVEMBER 21,
1996 AS INSTRUMENT NO. 19960587414 OF OFFICIAL RECORDS, RECORDS OF ORANGE COUNTY,
CALIFORNIA.

DATE DECEMBER 24, 2008
TIME 2:56 PM FEE \$ 22.00
INSTRUMENT NO. 2008000589633
BOOK 897 PAGE 28-33 M

DATE OF SURVEY:
JANUARY 1999 &
MARCH 2002

JULY 2008

JAMES F. GILLEN, L.S. 5557

HUITT-ZOLIARS

3 NUMBERED LOTS AND 4 LETTERED LOTS

57.908 ACRES

TOM DALY
COUNTY CLERK-RECORDER
BY [Signature]
DEPUTY

OWNERSHIP CERTIFICATE:

WE, THE UNDERSIGNED, BEING ALL PARTIES HAVING ANY RECORD TITLE INTEREST IN THE LAND COVERED BY THIS MAP, DO HEREBY CONSENT TO THE PREPARATION AND RECORDATION OF SAID MAP, AS SHOWN WITHIN THE DISTINCTIVE BORDER LINE.

WE ALSO HEREBY DEDICATE TO THE COUNTY OF ORANGE:

(1) THE EASEMENTS FOR PUBLIC PEDESTRIAN PURPOSES AS SHOWN ON SAID MAP.

SURVEYOR'S STATEMENT:

THIS MAP WAS PREPARED BY ME OR UNDER MY DIRECTION AND IS BASED UPON A FIELD SURVEY IN CONFORMANCE WITH THE REQUIREMENTS OF THE SUBDIVISION MAP ACT AND LOCAL ORDINANCES AT THE REQUEST OF RANCHO MISSION VIEJO, LLC ON MARCH 2002. I HEREBY STATE THAT ALL MONUMENTS ARE OF THE CHARACTER AND OCCUPY THE POSITIONS INDICATED, OR THAT THEY WILL BE SET IN SUCH POSITIONS, AND THAT SAID MONUMENTS ARE SUFFICIENT TO ENABLE THE SURVEY TO BE RETRACED. I HEREBY STATE THAT THIS FINAL MAP SUBSTANTIALLY CONFORMS TO THE CONDITIONALLY APPROVED TENTATIVE MAP.



JAMES F. GILLEN
L.S. 5557
EXPIRATION DATE: 9/30/09

DMB LADERA, LLC, A DELAWARE LIMITED LIABILITY COMPANY.

BY: RANCHO MISSION VIEJO, LLC, A DELAWARE LIMITED LIABILITY COMPANY,
ITS AUTHORIZED AGENT AND MANAGER.

BY: [Signature]
PRINT NAME: PAUL JOHNSON
PRINT TITLE: SR. V.P. COMMUNITY DEVELOPMENT


BY: [Signature]
PRINT NAME: Gregory S. Edwards
PRINT TITLE: SR. V.P. VICE CFO

COUNTY SURVEYOR'S STATEMENT:

I HEREBY STATE THAT I HAVE EXAMINED THIS MAP AND HAVE FOUND IT TO BE SUBSTANTIALLY IN CONFORMANCE WITH THE TENTATIVE MAP AS FILED WITH, AMENDED AND APPROVED BY THE ORANGE COUNTY SUBDIVISION COMMITTEE; THAT ALL PROVISIONS OF THE SUBDIVISION MAP ACT AND COUNTY SUBDIVISION REGULATIONS HAVE BEEN COMPLIED WITH AND I AM SATISFIED SAID MAP IS TECHNICALLY CORRECT.

DATED THIS 3RD DAY OF DECEMBER, 2008.

BY: [Signature], DEPUTY
RAYMOND L. MATHE, COUNTY SURVEYOR
LS 6185 EXPIRATION DATE: 3/31/10

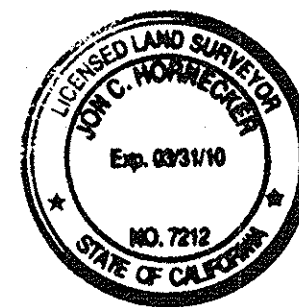

NOTARY ACKNOWLEDGMENT

STATE OF CALIFORNIA)
COUNTY OF ORANGE)


ON September 30, 2008 BEFORE ME, JOAN LEE DYER NOTARY PUBLIC,
PERSONALLY APPEARED PAUL JOHNSON and GREGORY S. EDWARDS, WHO PROVED TO ME ON THE BASIS OF SATISFACTORY EVIDENCE TO BE THE PERSON(S) WHOSE NAME(S) IS/ARE SUBSCRIBED TO THE WITHIN INSTRUMENT AND ACKNOWLEDGED TO ME THAT HE/SHE/they EXECUTED THE SAME IN his/her/their AUTHORIZED CAPACITY(IES), AND THAT BY his/her/their SIGNATURE(S) ON THE INSTRUMENT THE PERSON(S), OR THE ENTITY UPON BEHALF OF WHICH THE PERSON(S) ACTED, EXECUTED THE INSTRUMENT.

I CERTIFY UNDER PENALTY OF PERJURY UNDER THE LAWS OF THE STATE OF CALIFORNIA THAT THE FOREGOING PARAGRAPH IS TRUE AND CORRECT.

WITNESS MY HAND:
[Signature]
NOTARY PUBLIC IN AND FOR SAID STATE

MY COMMISSION EXPIRES 11-08-08
COMMISSION NO. 1525392

MY PRINCIPAL PLACE OF BUSINESS
IS IN Orange COUNTY

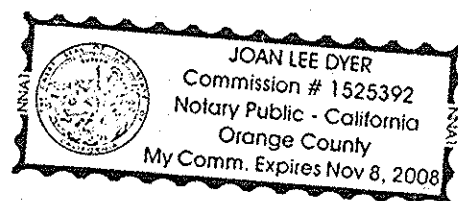

COUNTY TREASURER-TAX COLLECTOR'S CERTIFICATE:

STATE OF CALIFORNIA)
COUNTY OF ORANGE)

I HEREBY CERTIFY THAT ACCORDING TO THE RECORDS OF MY OFFICE THERE ARE NO LIENS AGAINST THE LAND COVERED BY THIS MAP OR ANY PART THEREOF FOR UNPAID STATE, COUNTY, MUNICIPAL OR LOCAL TAXES OR SPECIAL ASSESSMENTS COLLECTED AS TAXES. ~~EXCEPT TAXES OR SPECIAL ASSESSMENTS COLLECTED AS TAXES NOT YET PAYABLE~~
~~AND DO HEREBY CERTIFY TO THE RECORDER OF ORANGE COUNTY THAT THE PROVISIONS OF THE SUBDIVISION MAP ACT HAVE BEEN COMPLIED WITH REGARDING DEPOSITS TO SECURE PAYMENT OF TAXES OR SPECIAL ASSESSMENTS COLLECTED AS TAXES ON THE LAND COVERED BY THIS MAP.~~

DATED THIS 22nd DAY OF December, 2008.

CHRISS W. STREET
COUNTY TREASURER-TAX COLLECTOR
BY: [Signature], DEPUTY TREASURER-TAX COLLECTOR

CLERK OF THE BOARD OF SUPERVISORS' CERTIFICATE:

STATE OF CALIFORNIA)
COUNTY OF ORANGE)

I HEREBY CERTIFY THAT THIS MAP WAS PRESENTED FOR APPROVAL TO THE BOARD OF THE SUPERVISORS OF ORANGE COUNTY AT A REGULAR MEETING THEREOF HELD ON THE 16th DAY OF DECEMBER, 2008, AND THAT THEREUPON SAID BOARD DID, BY AN ORDER DULY PASSED AND ENTERED, APPROVE SAID MAP.

AND DID ALSO ACCEPT ON BEHALF OF THE COUNTY OF ORANGE:

(1) THE EASEMENTS FOR PUBLIC PEDESTRIAN PURPOSES AS DEDICATED.

AND DID ALSO APPROVE SUBJECT MAP PURSUANT TO THE PROVISIONS OF SECTION 66436(a) (3) (A) OF THE SUBDIVISION MAP ACT.

DATED THIS 16th DAY OF DECEMBER, 2008.

[Signature]
DARLENE J. BLOOM
CLERK OF THE BOARD OF SUPERVISORS



HIGH FIRE HAZARD AREA NOTE:

THE LOTS SHOWN ON THIS MAP ARE IN A HIGH FIRE HAZARD AREA DUE TO WILD LAND EXPOSURE.

NOTE:

SEE SHEET 2 FOR SIGNATURE OMISSIONS.

DUPLICATE

SHEET 2 OF 6 SHEETS

TRACT NO. 15793

ALL OF VESTING TENTATIVE
TRACT NO. 15793

IN THE UNINCORPORATED TERRITORY OF ORANGE COUNTY, CALIFORNIA

DATE OF SURVEY:
JANUARY 1999 &
MARCH 2002

JULY 2008

JAMES F. GILLEN, L.S. 5557

HUITT-ZOLIARS

3 NUMBERED LOTS AND 4 LETTERED LOTS

57.908 ACRES

SIGNATURE OMISSIONS:

IN ACCORDANCE WITH THE PROVISIONS OF SECTION 66436(a) (3) OF THE SUBDIVISION MAP ACT, THE FOLLOWING SIGNATURES HAVE BEEN OMITTED:

1. SFPP, L.P., HOLDER OF AN EASEMENT FOR PUBLIC UTILITIES AND INCIDENTAL PURPOSES RECORDED DECEMBER 6, 1999 AS INSTRUMENT NO. 19990831017 AS AMENDED BY A DOCUMENT RECORDED NOVEMBER 5, 2001 AS INSTRUMENT NO. 20010787529, BOTH OF OFFICIAL RECORDS.
2. SAN DIEGO GAS AND ELECTRIC COMPANY, HOLDER OF AN EASEMENT FOR UNDERGROUND FACILITIES, APPURTENANCES, AND INCIDENTAL PURPOSES RECORDED FEBRUARY 27, 2004 AS INSTRUMENT NO. 2004000153368 OF OFFICIAL RECORDS.
3. LADERA LAND CONSERVANCY, HOLDER OF AN EASEMENT FOR OPEN SPACE CONSERVATION PURPOSES PER DOCUMENT RECORDED JUNE 29, 2007 AS INSTRUMENT NO. 2007000412598 OF OFFICIAL RECORDS.
4. LADERA DEVELOPMENT COMPANY, LLC, OWNER OF OIL RIGHTS, MINERAL RIGHTS, NATURAL GAS RIGHTS, AND OTHER HYDROCARBONS, TOGETHER WITH WATER RIGHTS PER THE DEED RECORDED DECEMBER 10, 1996 AS INSTRUMENT NO. 19960624029 OF OFFICIAL RECORDS.

PROPOSED EASEMENT NOTES:

THE PROPOSED EASEMENTS DEPICTED ON THIS MAP AND IDENTIFIED BELOW BY LETTER DESIGNATION ARE INTENDED TO DEFINE EASEMENT LOCATION ONLY. SUBSEQUENT SEPERATE DOCUMENTS WILL BE RECORDED IN THE ORANGE COUNTY RECORDERS OFFICE WHICH WILL GRANT THE EASEMENTS IDENTIFIED, INCLUDING ACCESS EASEMENTS, AND ESTABLISH EASEMENT TERMS AND CONDITIONS.

- (A) INDICATES PROPOSED EASEMENT AREA TO BE GRANTED BY SEPARATE DOCUMENT.
- (B) INDICATES PROPOSED EASEMENT AREA TO BE GRANTED BY SEPARATE DOCUMENT.
- (C) INDICATES PROPOSED EASEMENT AREA TO BE GRANTED BY SEPARATE DOCUMENT.
- (D) INDICATES PROPOSED EASEMENT AREA TO BE GRANTED BY SEPARATE DOCUMENT.
- (E) INDICATES PROPOSED EASEMENT AREA TO BE GRANTED BY SEPARATE DOCUMENT.
- (F) INDICATES PROPOSED EASEMENT AREA TO BE GRANTED BY SEPARATE DOCUMENT.
- (G) INDICATES PROPOSED EASEMENT AREA TO BE GRANTED BY SEPARATE DOCUMENT.
- (H) INDICATES PROPOSED EASEMENT AREA TO BE GRANTED BY SEPARATE DOCUMENT.
- (I) INDICATES PROPOSED EASEMENT AREA TO BE GRANTED BY SEPARATE DOCUMENT.
- (J) INDICATES PROPOSED EASEMENT AREA TO BE GRANTED BY SEPARATE DOCUMENT.
- (K) INDICATES PROPOSED EASEMENT AREA TO BE GRANTED BY SEPARATE DOCUMENT.
- (L) INDICATES PROPOSED EASEMENT AREA TO BE GRANTED BY SEPARATE DOCUMENT.

EASEMENT NOTES:

- (M) INDICATES EASEMENT TO SFPP, L.P. FOR PUBLIC UTILITIES AND INCIDENTAL PURPOSES PER INSTRUMENT NO. 19990831017 AND AS AMENDED PER INSTRUMENT NO. 20010787529, BOTH OF OFFICIAL RECORDS.
- (N) INDICATES EASEMENT TO SAN DIEGO GAS AND ELECTRIC COMPANY FOR UNDERGROUND FACILITIES, APPURTENANCES, AND INCIDENTAL PURPOSES PER INSTRUMENT NO. 2004000153368 OF OFFICIAL RECORDS.
- (O) INDICATES LADERA LAND CONSERVANCY, HOLDER OF AN EASEMENT FOR OPEN SPACE CONSERVATION PURPOSES PER DOCUMENT RECORDED JUNE 29, 2007 AS INSTRUMENT NO. 2007000412598 OF OFFICIAL RECORDS.
- (P) INDICATES PUBLIC PEDESTRIAN EASEMENTS AS DEDICATED TO THE COUNTY OF ORANGE HEREON.

BASIS OF BEARINGS:

THE BEARINGS SHOWN HEREON, ARE BASED ON THE BEARING BETWEEN OCS HORIZONTAL CONTROL STATION GPS NO. 1417 AND STATION GPS NO. 1448, BEING N10°48'13"E PER RECORDS ON FILE IN THE OFFICE OF THE ORANGE COUNTY SURVEYOR.

DATUM STATEMENT:

COORDINATES SHOWN ARE BASED ON THE CALIFORNIA COORDINATE SYSTEM, (CCS83) ZONE VI, 1983 NAD, (1991.35 EPOCH OCS GPS ADJUSTMENT.)

ALL DISTANCES SHOWN ARE GROUND, UNLESS OTHERWISE NOTED. TO OBTAIN A GRID DISTANCE, MULTIPLY THE GROUND DISTANCE BY 0.999948295.

MONUMENT NOTES:

- INDICATES FD. 2" I.P. WITH TAG "LS 5557" PER R.S. 97-1086, R.S.B. 167/26-28, UNLESS OTHERWISE NOTED.
- INDICATES LOCATION OF 2" I.P. TAGGED "P.L.S. 5557" OR SPIKE & WASHER STAMPED "P.L.S. 5557" OR LEAD, TACK & TAG "P.L.S. 5557" TO BE SET WITHIN 90 DAYS AFTER ACCEPTANCE OF IMPROVEMENTS.
- (A) FD. 2 1/2" IRON PIPE W/2" OCS BRASS CAP STAMPED "GPS 1448 9-95" PER RECORDS ON FILE IN THE ORANGE COUNTY SURVEYORS OFFICE.
- (B) FD. 2 1/2" IRON PIPE W/2" OCS BRASS CAP STAMPED "GPS 1417 9-95" PER RECORDS ON FILE IN THE ORANGE COUNTY SURVEYORS OFFICE.

SHEET 3 OF 6 SHEETS

TRACT NO. 15793

IN THE UNINCORPORATED TERRITORY OF ORANGE COUNTY, CALIFORNIA

ALL OF VESTING TENTATIVE
TRACT NO. 15793

DATE OF SURVEY:
JANUARY 1999 &
MARCH 2002

JULY 2008

JAMES F. GILLEN, L.S. 5557

HUITT-ZOLLARS

3 NUMBERED LOTS AND 4 LETTERED LOTS


57.908 ACRES

CURVE DATA

- ① $\Delta=8^{\circ}37'55''$ $R=190.00'$ $L=28.62'$
- ② $\Delta=22^{\circ}21'57''$ $R=210.00'$ $L=81.98'$
- ③ $\Delta=63^{\circ}48'06''$ $R=47.50'$ $L=52.89'$
- ④ $\Delta=75^{\circ}57'17''$ $R=62.50'$ $L=82.85'$
- ⑤ $\Delta=75^{\circ}57'17''$ $R=45.00'$ $L=59.65'$
- ⑥ $\Delta=53^{\circ}04'10''$ $R=65.00'$ $L=60.21'$
- ⑦ $\Delta=67^{\circ}06'53''$ $R=25.00'$ $L=29.28'$
- ⑧ $\Delta=74^{\circ}50'35''$ $R=90.00'$ $L=117.56'$
- ⑨ $\Delta=74^{\circ}50'35''$ $R=110.00'$ $L=143.69'$
- ⑩ $\Delta=58^{\circ}56'04''$ $R=187.00'$ $L=192.35'$
- ⑪ $\Delta=03^{\circ}06'51''$ $R=651.00'$ $L=35.38'$
- ⑫ $\Delta=11^{\circ}00'40''$ $R=353.00'$ $L=67.84'$
- ⑬ $\Delta=12^{\circ}14'52''$ $R=363.00'$ $L=77.60'$
- ⑭ $\Delta=16^{\circ}17'58''$ $R=310.00'$ $L=88.19'$
- ⑮ $\Delta=16^{\circ}17'58''$ $R=290.00'$ $L=82.50'$
- ⑯ $\Delta=31^{\circ}55'58''$ $R=40.00'$ $L=22.29'$
- ⑰ $\Delta=3^{\circ}47'32''$ $R=1019.50'$ $L=67.48'$
- ⑱ $\Delta=5^{\circ}14'29''$ $R=210.00'$ $L=19.21'$
- ⑲ $\Delta=43^{\circ}49'24''$ $R=90.00'$ $L=68.84'$
- ⑳ $\Delta=30^{\circ}37'46''$ $R=50.00'$ $L=26.73'$

COURSE DATA

- 1 N 61°41'02" W 18.62'
- 2 N 61°41'02" W 61.67'
- 3 N 66°08'21" W 80.69'
- 4 N 48°56'53" W 56.80'
- 5 N 38°06'32" W 61.21'
- 6 N 52°42'22" W 64.46'
- 7 N 37°17'38" E 30.00'
- 8 N 84°09'51" E 51.00'
- 9 N 24°33'04" E 50.00'
- 10 N 52°42'22" W 4.15'
- 11 N 44°04'27" W 42.27'
- 12 N 44°33'49" W 3.59'
- 13 N 52°42'22" W 50.00'
- 14 N 07°41'46" E 52.11'
- 15 N 82°18'14" W 36.48'
- 16 N 82°18'14" W 14.09'
- 17 N 23°23'00" W 52.00'
- 18 N 11°33'21" E 73.48'
- 19 N 50°01'24" E 41.40'
- 20 N 66°10'08" W 23.15'
- 21 N 24°35'12" E 10.54'
- 22 N 47°02'57" W 5.00' RAD.
- 23 N 62°34'20" E 70.74'
- 24 N 75°50'07" W 26.42'
- 25 N 31°53'00" W 165.78'
- 26 N 83°20'56" W 18.14'
- 27 N 42°04'57" E 113.60'
- 28 N 58°03'37" W 116.33' RAD.

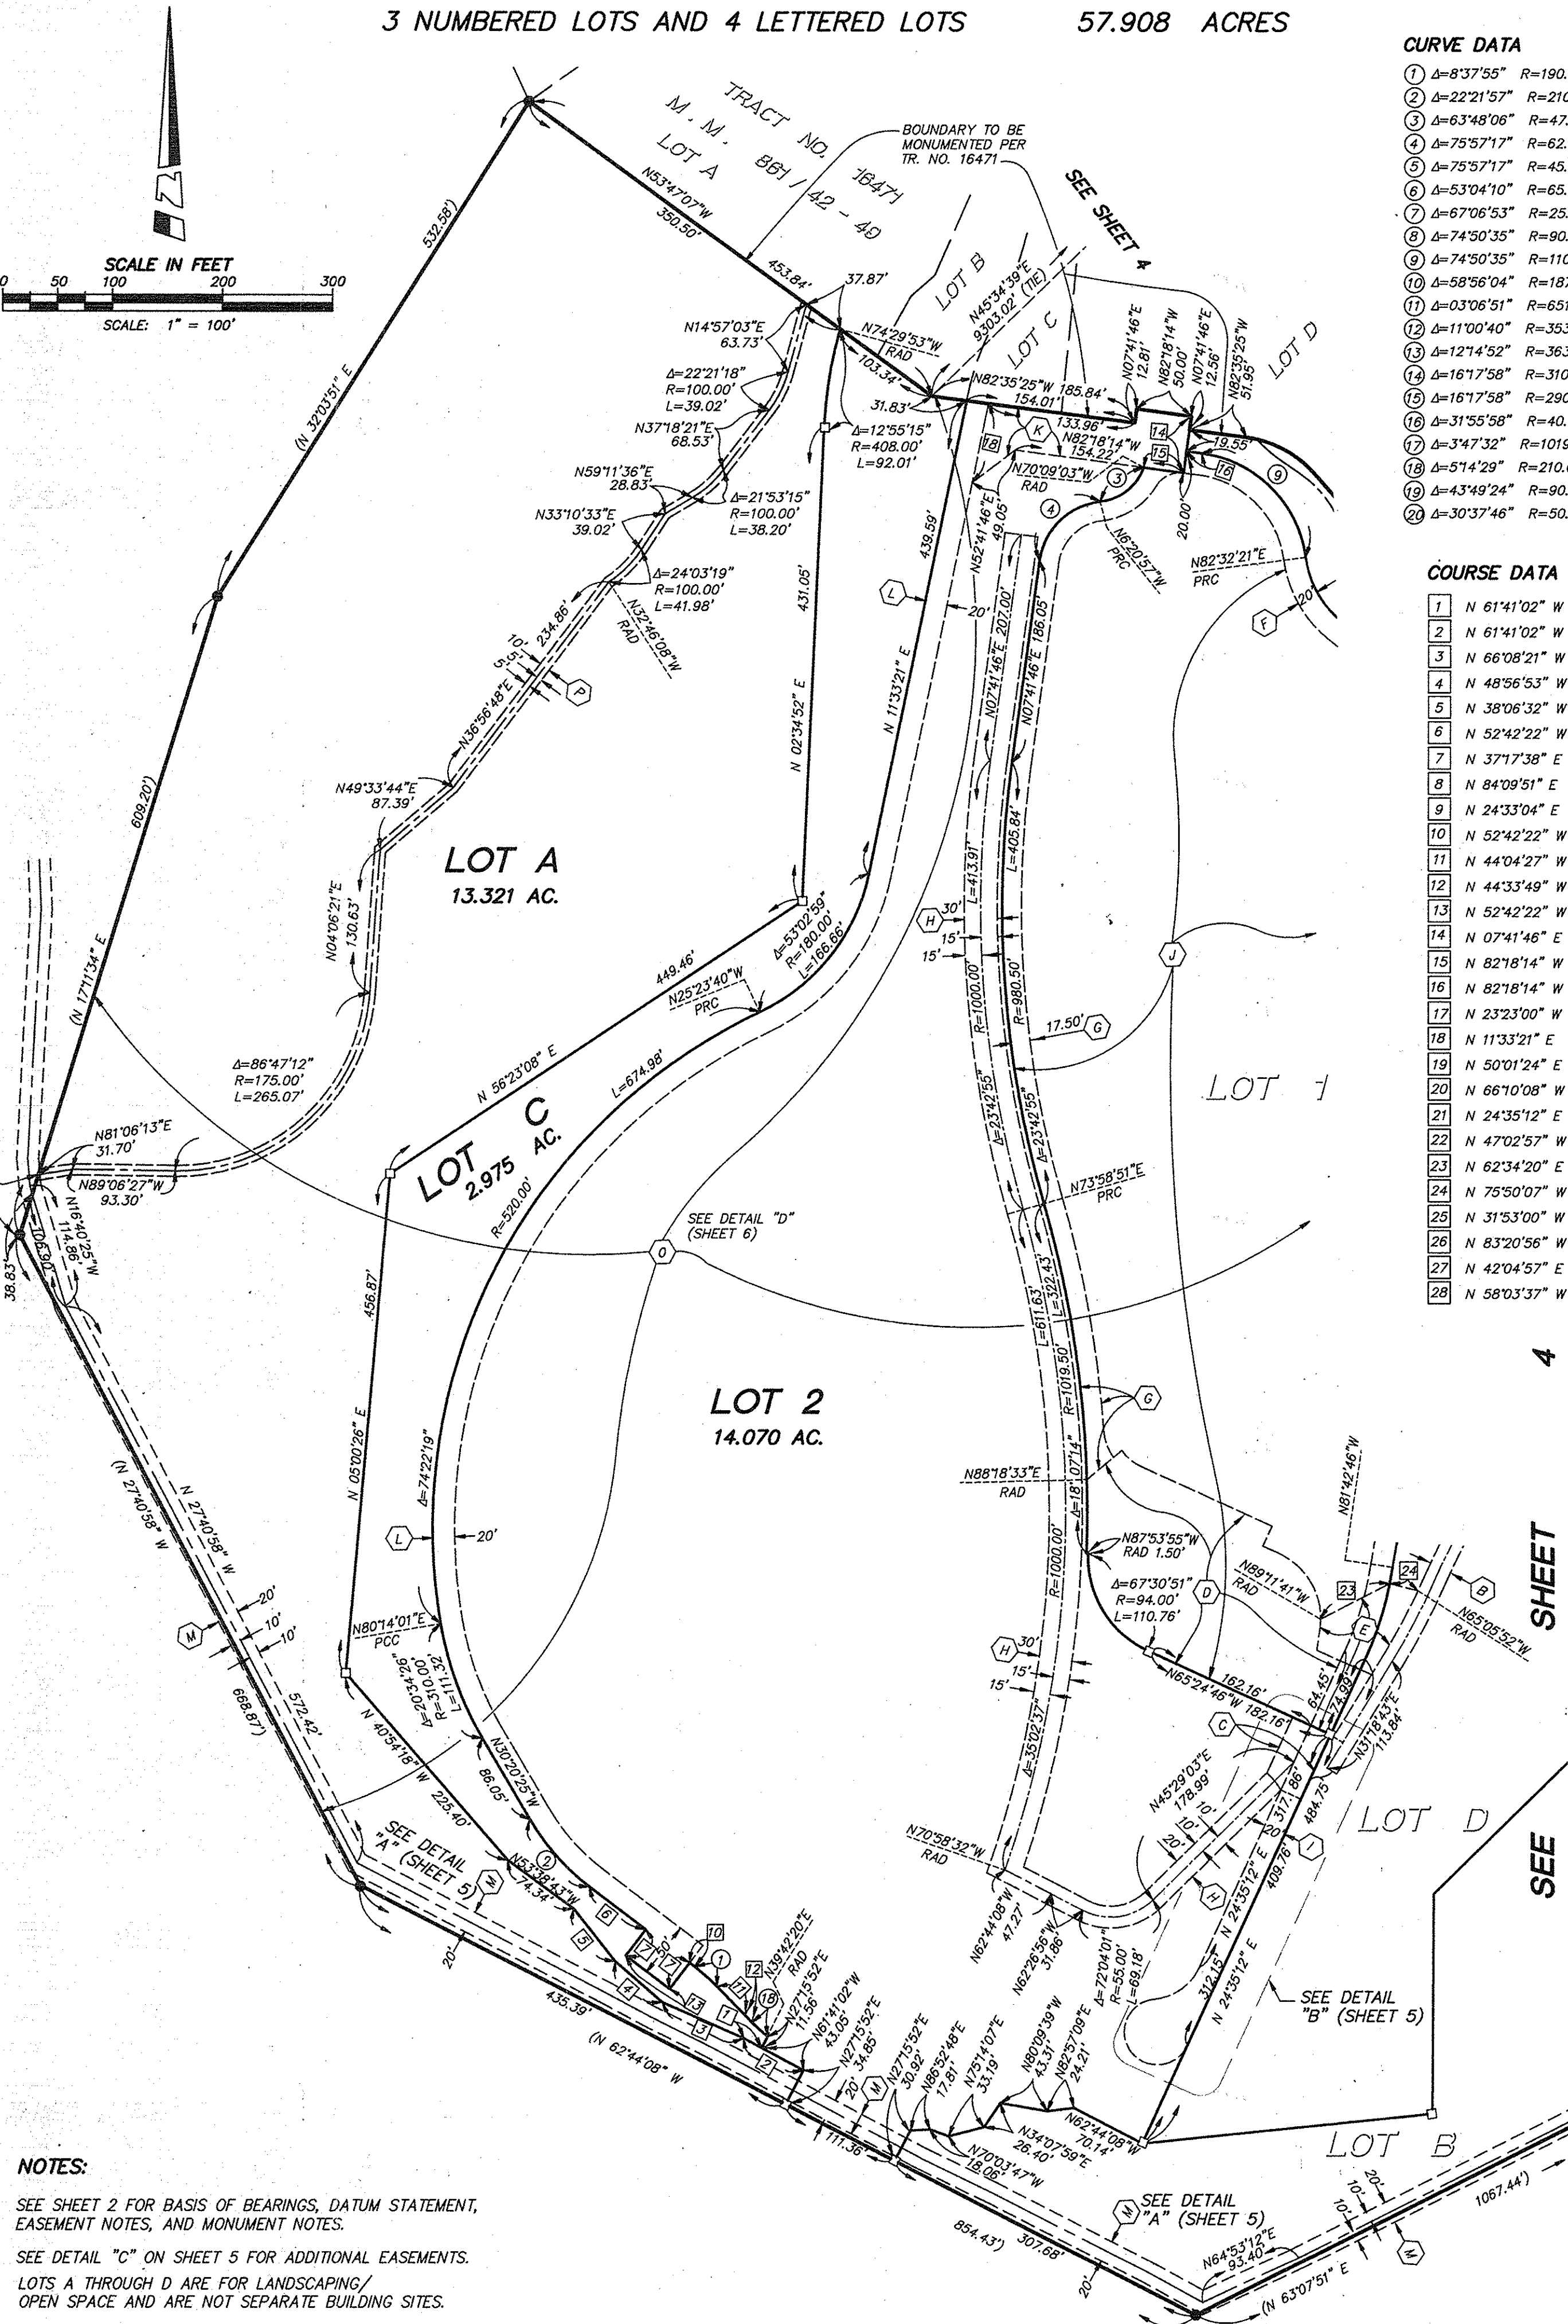

NOTES:

SEE SHEET 2 FOR BASIS OF BEARINGS, DATUM STATEMENT, EASEMENT NOTES, AND MONUMENT NOTES.

SEE DETAIL "C" ON SHEET 5 FOR ADDITIONAL EASEMENTS.

LOTS A THROUGH D ARE FOR LANDSCAPING/ OPEN SPACE AND ARE NOT SEPARATE BUILDING SITES.

() INDICATES MEASURED AND RECORD DATA PER LOT LINE ADJUSTMENT NO. LL 96-026 RECORDED AS INSTRUMENT NO. 19960587414, O.R.

SHEET 4 OF 6 SHEETS

TRACT NO. 15793

ALL OF VESTING TENTATIVE
TRACT NO. 15793

IN THE UNINCORPORATED TERRITORY OF ORANGE COUNTY, CALIFORNIA

DATE OF SURVEY:
JANUARY 1999 &
MARCH 2002


JULY 2008

JAMES F. GILLEN, L.S. 5557

HUITT-ZOLLARS

3 NUMBERED LOTS AND 4 LETTERED LOTS

57.908 ACRES

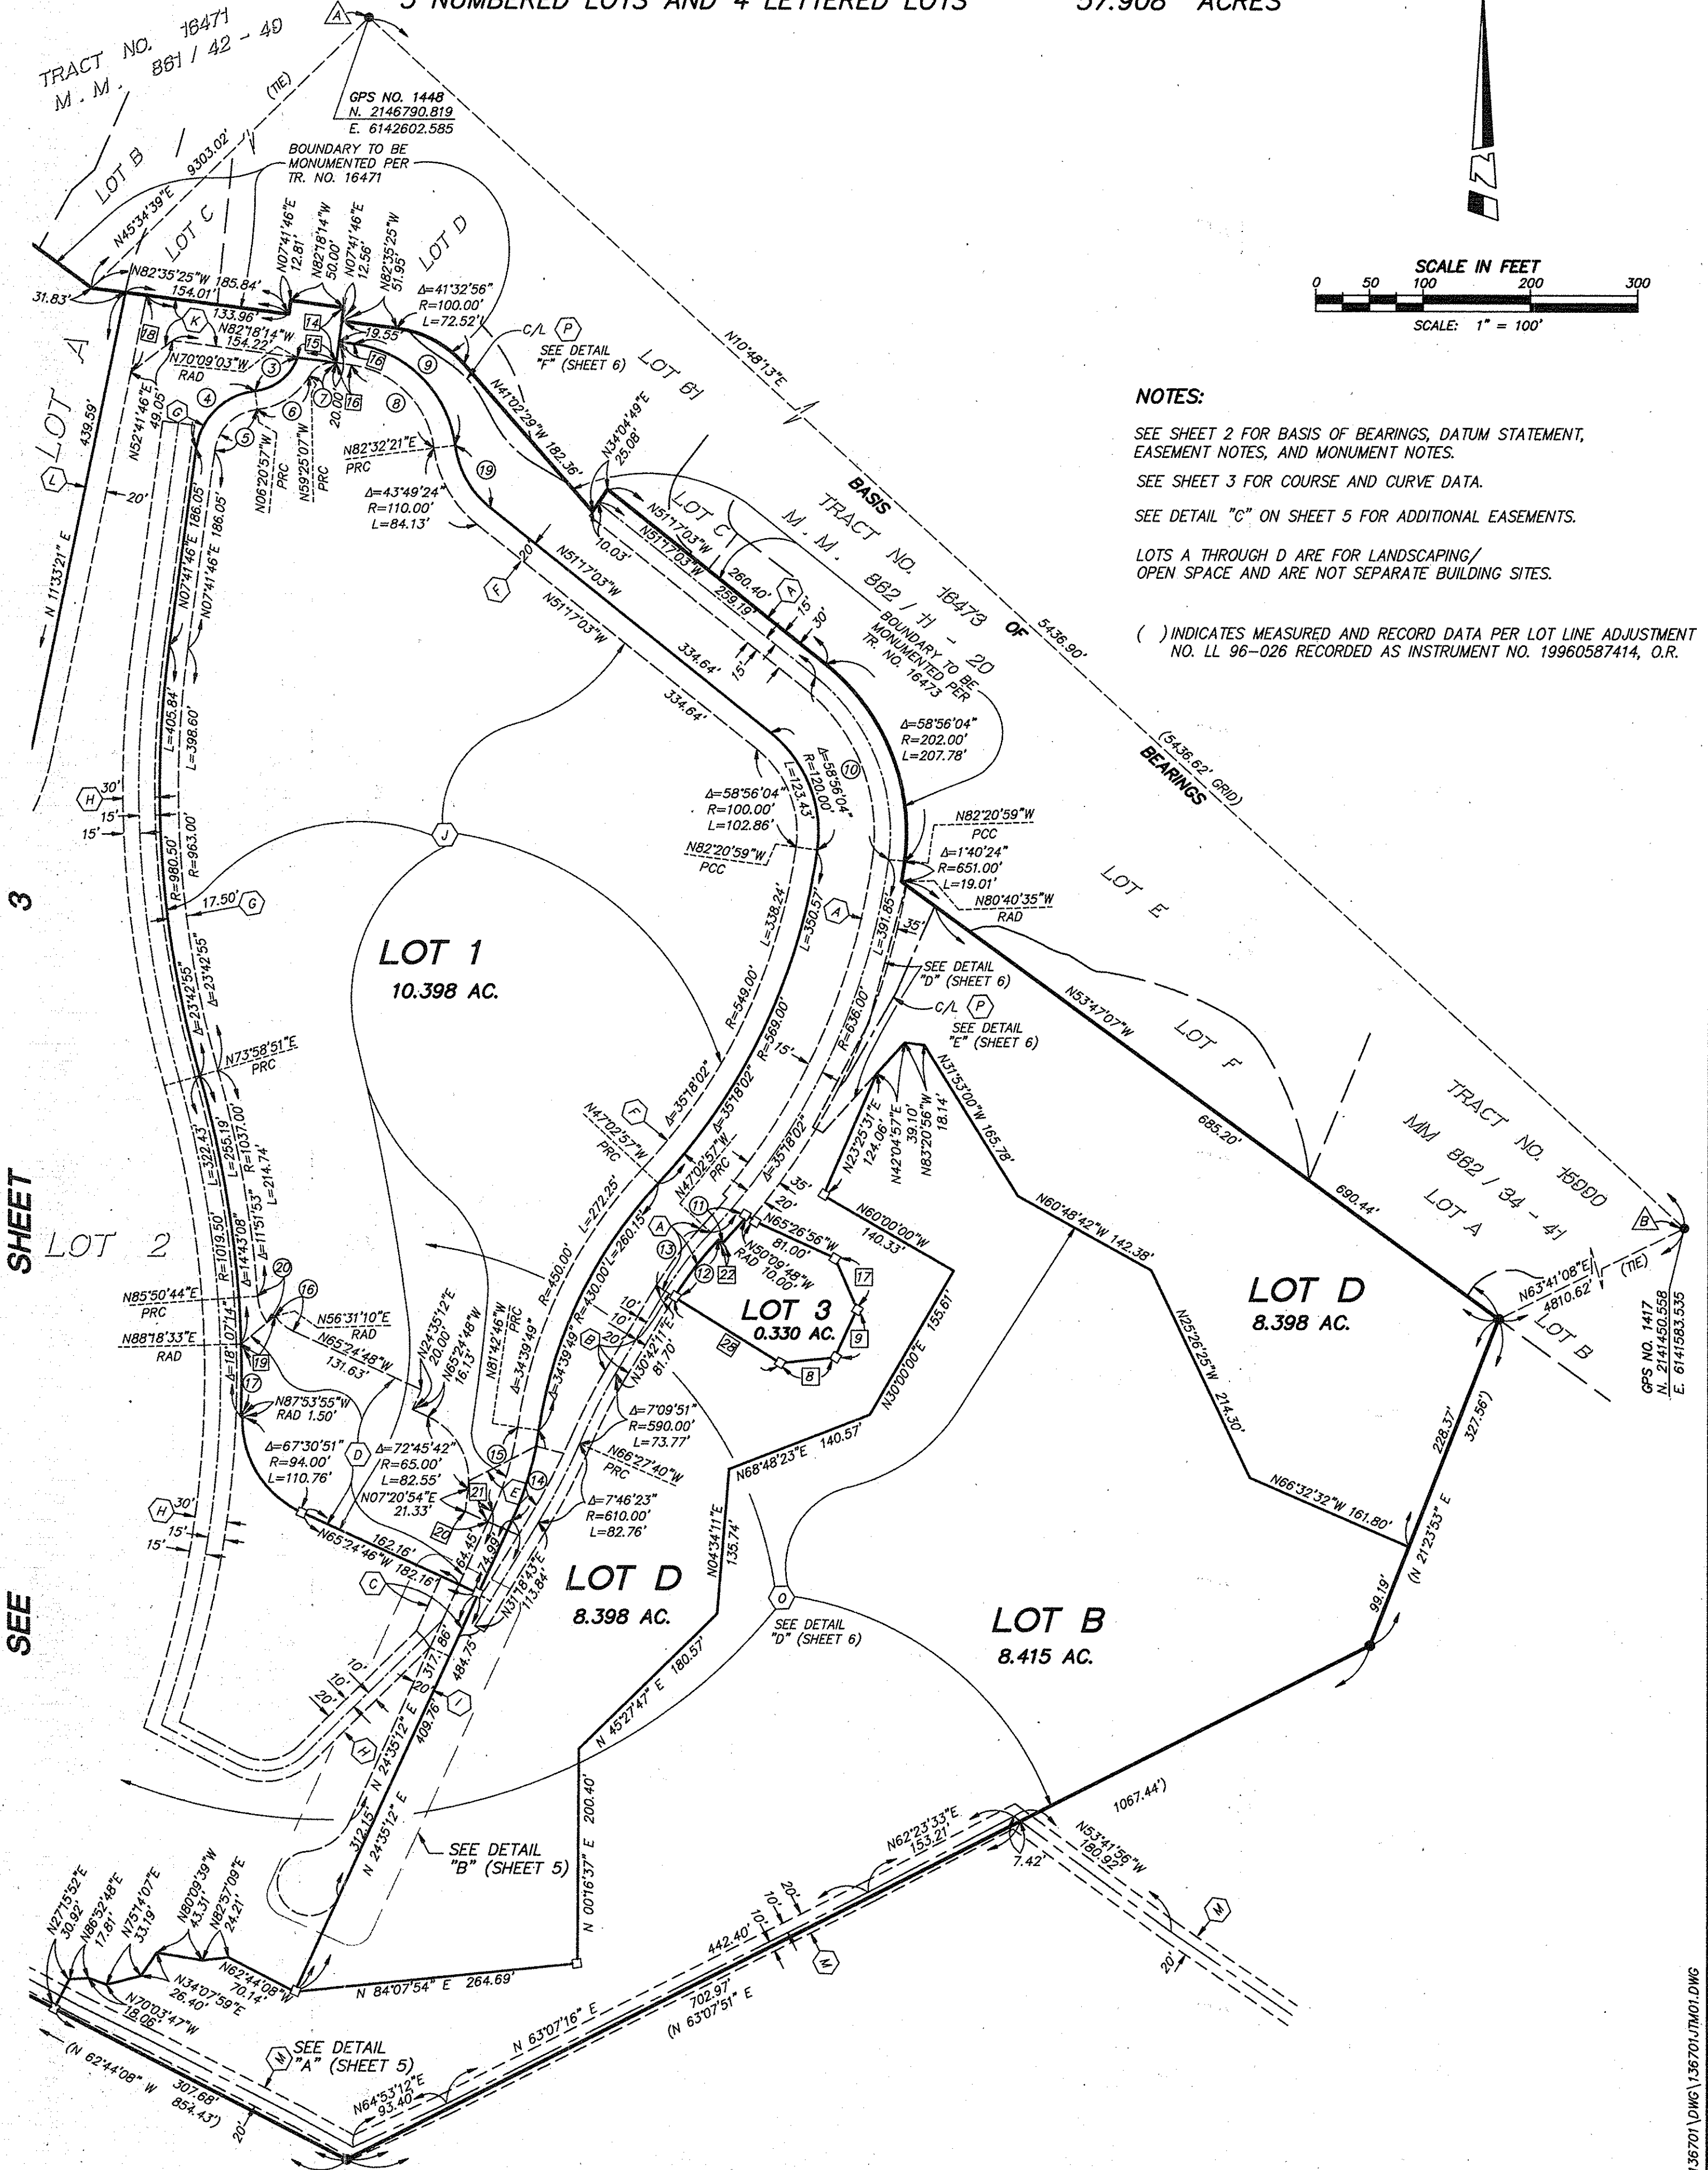

NOTES:

SEE SHEET 2 FOR BASIS OF BEARINGS, DATUM STATEMENT, EASEMENT NOTES, AND MONUMENT NOTES.

SEE SHEET 3 FOR COURSE AND CURVE DATA.

SEE DETAIL "C" ON SHEET 5 FOR ADDITIONAL EASEMENTS.

LOTS A THROUGH D ARE FOR LANDSCAPING/ OPEN SPACE AND ARE NOT SEPARATE BUILDING SITES.

() INDICATES MEASURED AND RECORD DATA PER LOT LINE ADJUSTMENT NO. LL 96-026 RECORDED AS INSTRUMENT NO. 19960587414, O.R.

SEE SHEET 3

SEE SHEET 3

SHEET 5 OF 6 SHEETS

TRACT NO. 15793

IN THE UNINCORPORATED TERRITORY OF ORANGE COUNTY, CALIFORNIA

ALL OF VESTING TENTATIVE
TRACT NO. 15793

JULY 2008


JAMES F. GILLEN, L.S. 5557

DATE OF SURVEY:
JANUARY 1999 &
MARCH 2002

HUITT-ZOLIARS

3 NUMBERED LOTS AND 4 LETTERED LOTS

57.908 ACRES

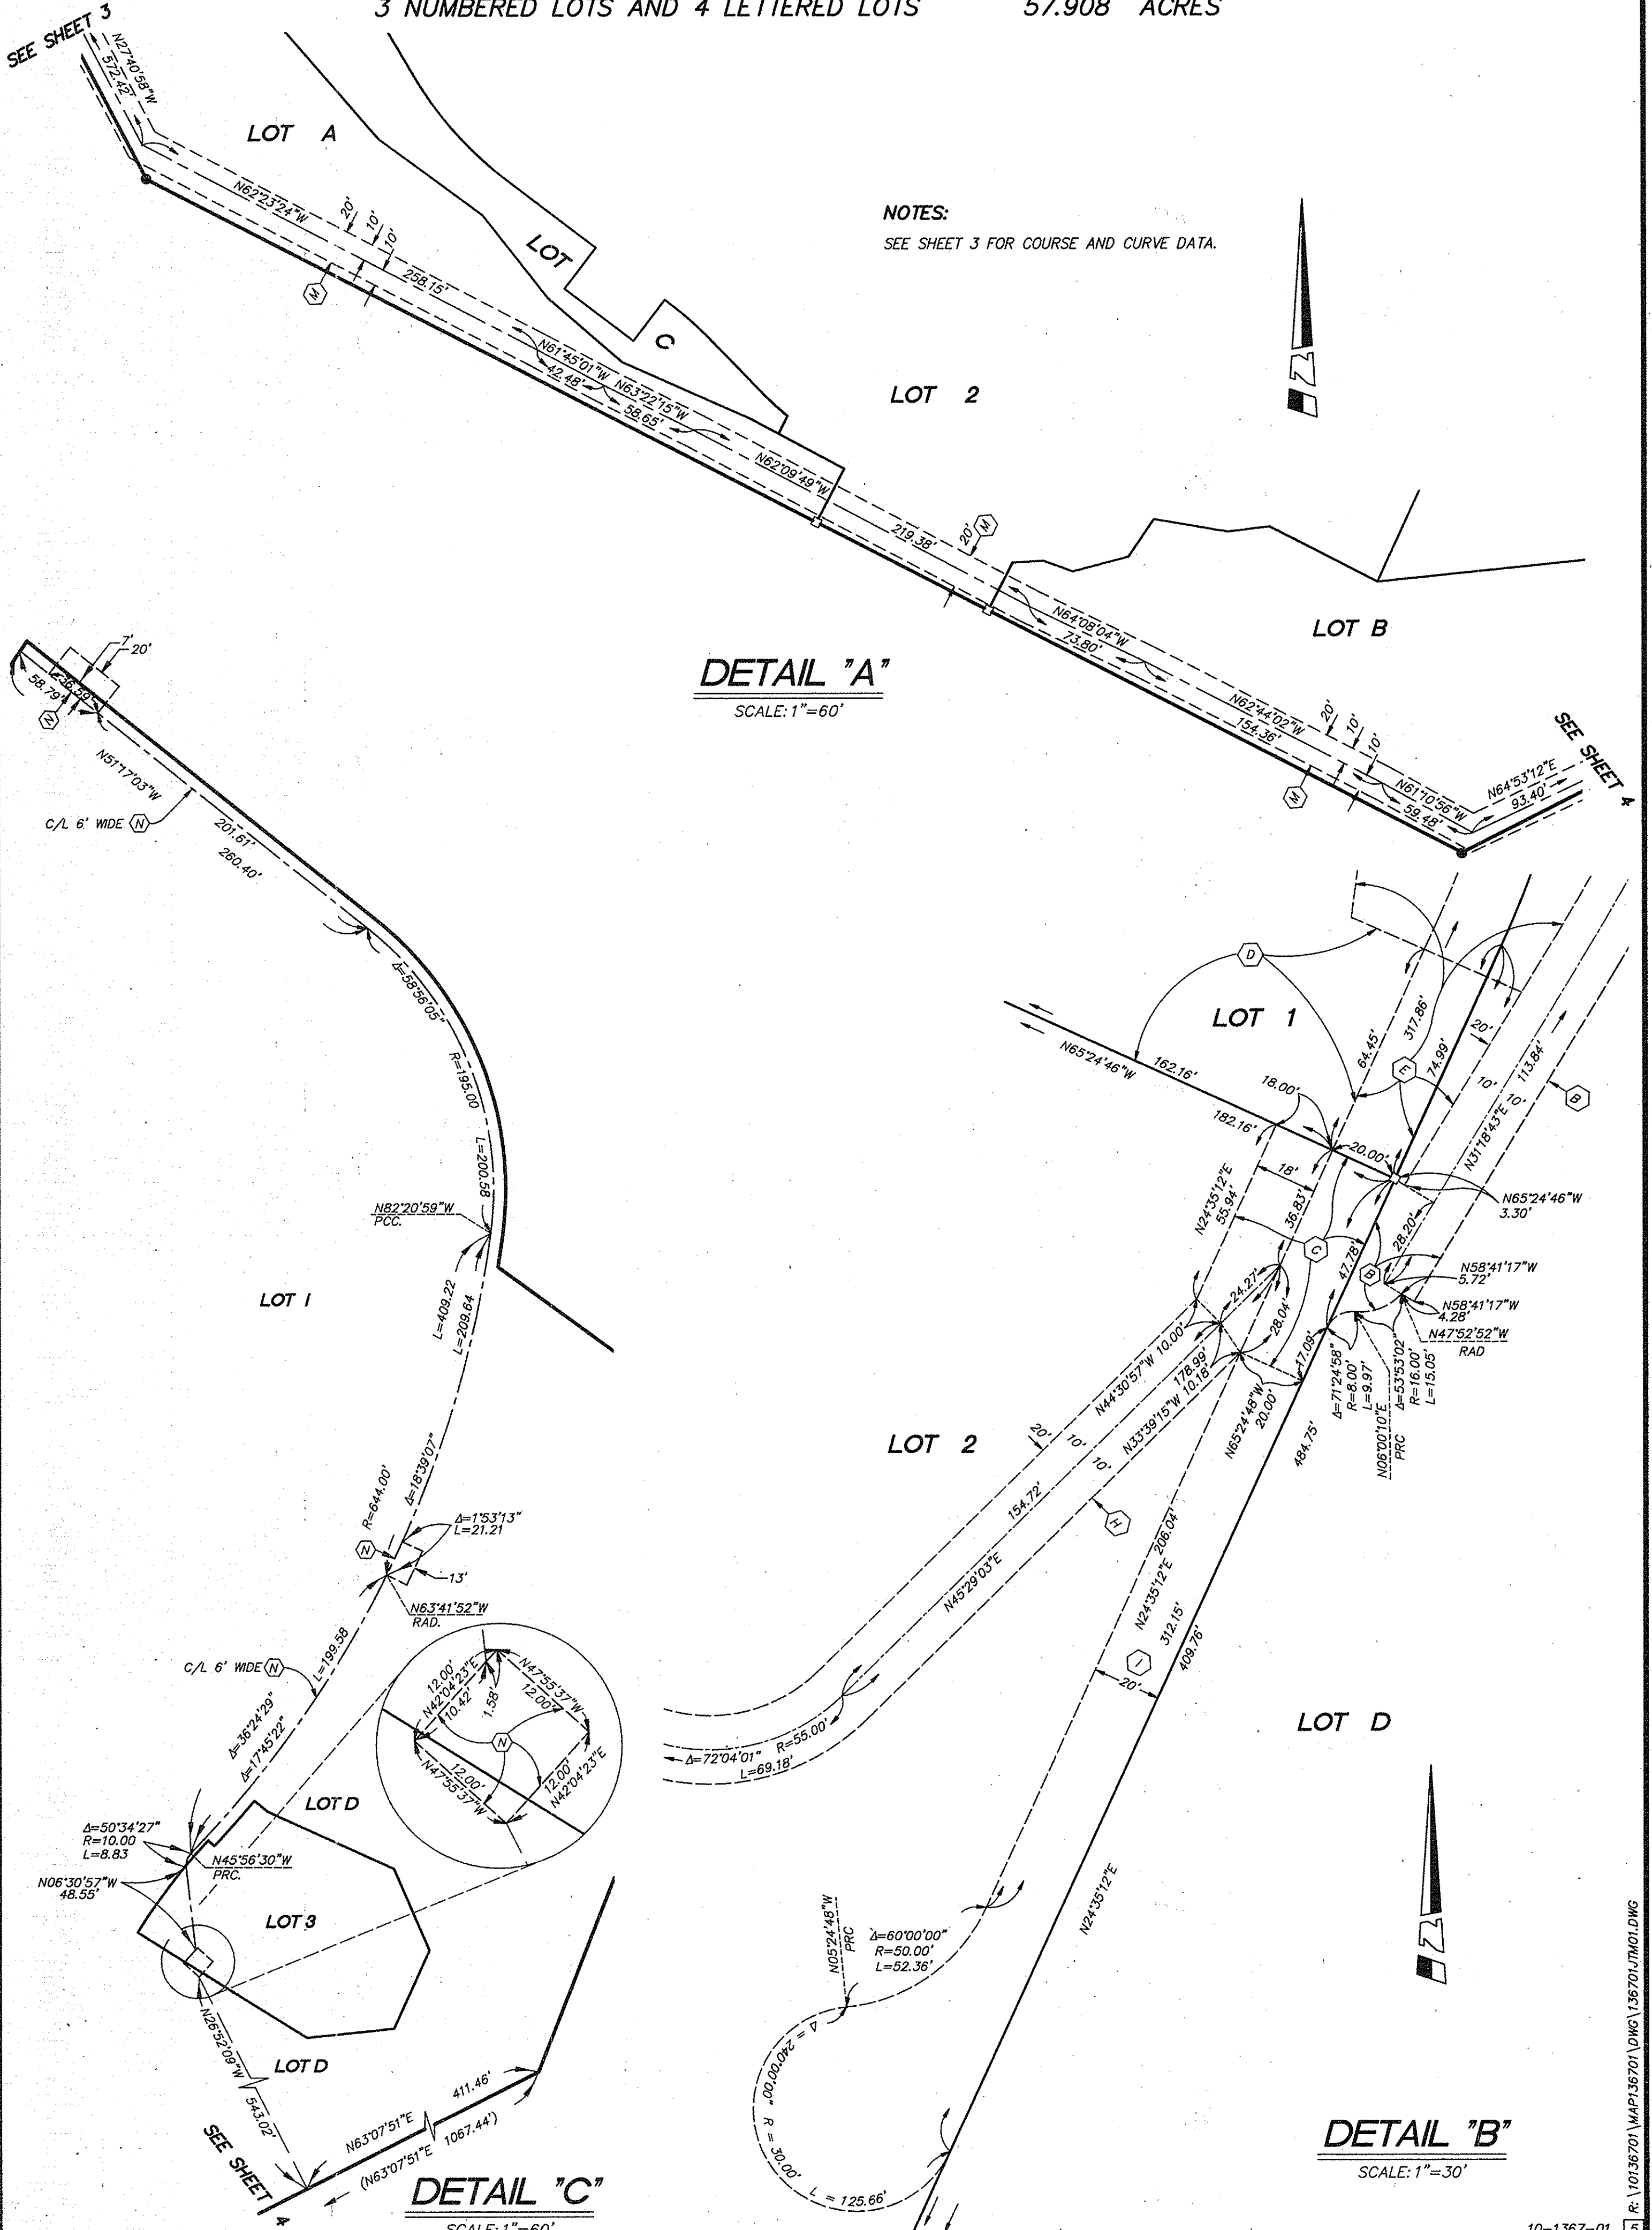

SHEET 6 OF 6 SHEETS

TRACT NO. 15793

ALL OF VESTING TENTATIVE
TRACT NO. 15793

IN THE UNINCORPORATED TERRITORY OF ORANGE COUNTY, CALIFORNIA

DATE OF SURVEY:
JANUARY 1999 &
MARCH 2002

JULY 2008

JAMES F. GILLEN, L.S. 5557

HUITT-ZOLIARS

3 NUMBERED LOTS AND 4 LETTERED LOTS

57.908 ACRES

