

ALL OF TENTATIVE TRACT NO. 15885
6.601 ACRES
NUMBERED LOTS: 7
LETTERED LOTS: 9
DATE OF SURVEY : FEBRUARY, 2000
BLOCK: 5157
MODULE: 06, 16 & 17

TRACT NO. 15885

IN THE UNINCORPORATED TERRITORY OF THE COUNTY OF ORANGE,
STATE OF CALIFORNIA

BEING A SUBDIVISION OF LOT 11 OF TRACT NO. 15884, AS SHOWN ON MAP FILED IN BOOK 794,
PAGES 33 TO 44 INCLUSIVE OF MISCELLANEOUS MAPS, RECORDS OF ORANGE COUNTY, CALIFORNIA.

MDS CONSULTING

FEBRUARY, 2000

GARY W. DOKICH, L.S. 4693

SHEET 1 OF 4 SHEETS

ACCEPTED AND FILED AT THE
REQUEST OF

FIRST AMERICAN TITLE Co.

DATE July 27, 2000

TIME 12:01pm FEE \$ 13.00

INSTRUMENT # 20000393851

BOOK 804 PAGE 30-33

GARY L. GRANVILLE
COUNTY CLERK - RECORDER

BY Mattie [Signature]
DEPUTY

OWNERSHIP CERTIFICATE

WE, THE UNDERSIGNED, BEING ALL PARTIES HAVING ANY RECORD TITLE INTEREST IN THE LAND COVERED BY THIS MAP, DO HEREBY CONSENT TO THE PREPARATION AND RECORDATION OF SAID MAP, AS SHOWN WITHIN THE DISTINCTIVE BORDERLINE. WE HEREBY DEDICATE TO THE PUBLIC FOR STREET PURPOSES: MAIN STREET.

WE ALSO HEREBY DEDICATE TO THE COUNTY OF ORANGE:

1. THE EASEMENTS FOR EMERGENCY AND PUBLIC SERVICE VEHICULAR INGRESS AND EGRESS AS SHOWN ON SAID MAP.

WE ALSO HEREBY RELEASE AND RELINQUISH TO THE COUNTY OF ORANGE:

1. ALL VEHICULAR ACCESS RIGHTS TO MAIN STREET EXCEPT AT STREET INTERSECTIONS.

WE ALSO HEREBY DEDICATE TO THE SANTA MARGARITA WATER DISTRICT THE EASEMENTS FOR SEWER AND WATER PURPOSES AS SHOWN ON SAID MAP, WHICH EASEMENTS SHALL BE SUBJECT TO THE SAME TERMS AND CONDITIONS AS ARE SHOWN IN THAT CERTAIN EASEMENT RECORDED OCTOBER 6, 1980 IN BOOK 13776, PAGE 341 OF OFFICIAL RECORDS, COUNTY OF ORANGE.

CENTEX HOMES, A NEVADA GENERAL PARTNERSHIP, OWNER

BY: CENTEX REAL ESTATE CORPORATION, A NEVADA CORPORATION, ITS MANAGING GENERAL PARTNER.

BY: [Signature]
PRINT NAME: ROLAND F. OSGOOD
PRINT TITLE: DIVISION PRESIDENT

DMB LADERA, LLC, A DELAWARE LIMITED LIABILITY COMPANY, BENEFICIARY UNDER DEED OF TRUST RECORDED FEBRUARY 3, 2000 AS INSTRUMENT NO. 20000060913 OF OFFICIAL RECORDS.


BY: RANCHO MISSION VIEJO, LLC, A DELAWARE LIABILITY COMPANY, ITS AUTHORIZED AGENT AND MANAGER

BY: [Signature]
PRINT NAME: Stephen C. Schenck
PRINT TITLE: Exec Vice President

SURVEYOR'S STATEMENT

I HEREBY STATE THAT THIS MAP CONSISTING OF 4 SHEETS, CORRECTLY REPRESENTS A TRUE AND COMPLETE SURVEY AS SHOWN MADE IN FEBRUARY, 2000; WAS MADE BY ME OR UNDER MY DIRECTION; THAT THE MONUMENTS ARE OF THE CHARACTER AND OCCUPY (OR WILL OCCUPY) THE POSITIONS INDICATED BY SAID MAP; AND THAT SAID MONUMENTS ARE (OR WILL BE) SUFFICIENT TO ENABLE THE SURVEY TO BE RETRACED.

GARY W. DOKICH
LICENSED LAND SURVEYOR NO. 4693
MY LICENSE EXPIRES: 9/30/03

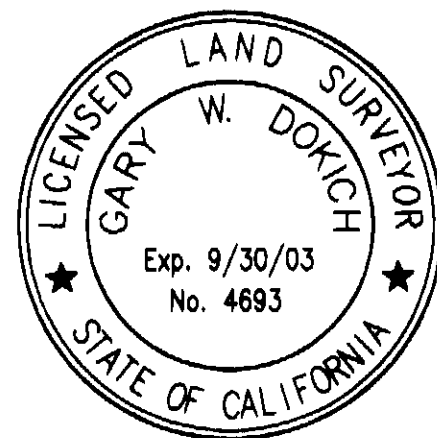


COUNTY SURVEYOR'S STATEMENT

I HEREBY STATE THAT I HAVE EXAMINED THIS MAP AND HAVE FOUND IT TO BE SUBSTANTIALLY IN CONFORMANCE WITH THE TENTATIVE MAP AS FILED WITH, AMENDED AND APPROVED BY THE ORANGE COUNTY SUBDIVISION COMMITTEE; THAT ALL PROVISIONS OF THE SUBDIVISION MAP ACT AND COUNTY SUBDIVISION REGULATIONS HAVE BEEN COMPLIED WITH AND I AM SATISFIED SAID MAP IS TECHNICALLY CORRECT.

DATED THIS 27th DAY OF July, 2000.

[Signature]
JOHN CANAS, COUNTY SURVEYOR
Robert Jelinek, Deputy County Surveyor

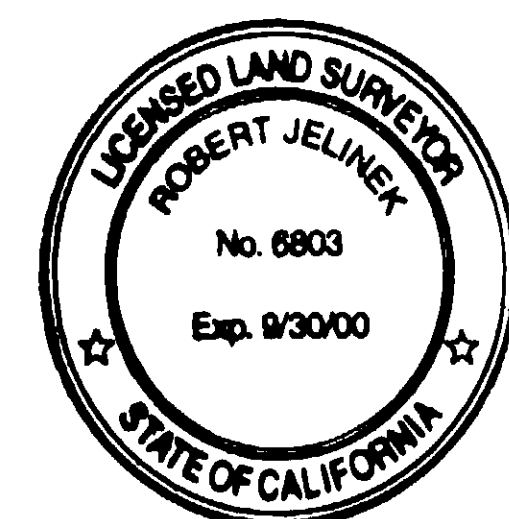

CLERK OF THE BOARD OF SUPERVISORS' CERTIFICATE

STATE OF CALIFORNIA)
COUNTY OF ORANGE) SS

I HEREBY CERTIFY THAT THIS MAP WAS PRESENTED FOR APPROVAL TO THE BOARD OF SUPERVISORS OF ORANGE COUNTY AT A REGULAR MEETING THEREOF HELD ON THE 20th DAY OF July, 2000, AND THAT THEREUPON SAID BOARD DID, BY AN ORDER DULY PASSED AND ENTERED, APPROVE SAID MAP AND DID ACCEPT ON BEHALF OF THE PUBLIC, SUBJECT TO IMPROVEMENTS; THE DEDICATION FOR STREET PURPOSES OF: MAIN STREET.

AND DID ALSO ACCEPT ON BEHALF OF THE COUNTY OF ORANGE:

1. THE EASEMENTS FOR EMERGENCY AND PUBLIC SERVICE VEHICULAR INGRESS AND EGRESS AS DEDICATED.
2. THE VEHICULAR ACCESS RIGHTS TO MAIN STREET AS RELEASED AND RELINQUISHED.

DATED THIS 20th DAY OF July, 2000.

[Signature]
DARLENE J. BLOOM
CLERK OF THE BOARD OF SUPERVISORS



NOTARY ACKNOWLEDGMENTS

STATE OF CALIFORNIA)
COUNTY OF ORANGE) SS

ON THIS 19th DAY OF JUNE, 2000, BEFORE ME, SUZETTE M. MORLEY, A NOTARY PUBLIC IN AND FOR SAID STATE, PERSONALLY APPEARED ROLAND F. OSGOOD, PERSONALLY KNOWN TO ME (OR PROVED TO ME ON THE BASIS OF SATISFACTORY EVIDENCE) TO BE THE PERSON(S) WHOSE NAME(S) IS/ARE SUBSCRIBED TO THE WITHIN INSTRUMENT AND ACKNOWLEDGED TO ME THAT HE/SHE/they EXECUTED THE SAME IN HIS/HER/their AUTHORIZED CAPACITY(IES), AND THAT BY HIS/HER/their SIGNATURE(S) ON THE INSTRUMENT THE PERSON(S), OR THE ENTITY UPON BEHALF OF WHICH THE PERSON(S) ACTED, EXECUTED THE INSTRUMENT.

WITNESS MY HAND:

[Signature]
NOTARY PUBLIC IN AND FOR SAID STATE

MY PRINCIPAL PLACE OF BUSINESS IS
IN ORANGE COUNTY

SUZETTE M. MORLEY
PRINT NAME

MY COMMISSION EXPIRES 12-9-03

STATE OF California)
COUNTY OF Orange) SS

ON THIS 8th DAY OF June, 2000, BEFORE ME, Tina T. Baker, A NOTARY PUBLIC IN AND FOR SAID STATE, PERSONALLY APPEARED Stephen C. Schenck, PERSONALLY KNOWN TO ME (OR PROVED TO ME ON THE BASIS OF SATISFACTORY EVIDENCE) TO BE THE PERSON(S) WHOSE NAME(S) IS/ARE SUBSCRIBED TO THE WITHIN INSTRUMENT AND ACKNOWLEDGED TO ME THAT HE/SHE/they EXECUTED THE SAME IN HIS/HER/their AUTHORIZED CAPACITY(IES), AND THAT BY HIS/HER/their SIGNATURE(S) ON THE INSTRUMENT THE PERSON(S), OR THE ENTITY UPON BEHALF OF WHICH THE PERSON(S) ACTED, EXECUTED THE INSTRUMENT.

WITNESS MY HAND:

[Signature]
NOTARY PUBLIC IN AND FOR SAID STATE

MY PRINCIPAL PLACE OF BUSINESS IS
IN Orange COUNTY

Tina T. Baker
PRINT NAME

MY COMMISSION EXPIRES 8-29-00

SIGNATURE OMISSIONS:

PURSUANT TO SECTION 66436 (a)(3) OF THE SUBDIVISION MAP ACT, THE FOLLOWING SIGNATURES HAVE BEEN OMITTED:

1. LADERA DEVELOPMENT COMPANY, L.L.C., HOLDER OF OIL, GAS, MINERAL AND WATER RIGHTS AS RESERVED IN DEED RECORDED DECEMBER 10, 1996 AS INSTRUMENT NO. 19960624029 OF OFFICIAL RECORDS.

2. DMB LADERA, LLC HOLDER OF EASEMENTS FOR CONSTRUCTION FACILITIES, TELECOMMUNICATIONS FACILITIES AND PUBLIC UTILITIES, ETC. AS RESERVED IN DEED RECORDED FEBRUARY 3, 2000 AS INSTRUMENT NO. 20000060911 OF OFFICIAL RECORDS. CANNOT BE LOCATED FROM THE RECORD.

CERTIFICATE OF ACCEPTANCE

THE UNDERSIGNED, BEING THE DULY APPOINTED AGENT OF THE SANTA MARGARITA WATER DISTRICT, A PUBLIC PUBLIC CORPORATION OF ORANGE COUNTY, CALIFORNIA, PURSUANT TO ITS RESOLUTION NO. 88-10-2, DOES HEREBY ACCEPT ON BEHALF OF SAID DISTRICT THE EASEMENTS FOR SEWER AND WATER PURPOSES, AS DEDICATED AND AS SHOWN ON THIS TRACT MAP, BY AND BETWEEN THE SANTA MARGARITA WATER DISTRICT AND CENTEX HOMES, AND DOES HEREBY CERTIFY THAT THE GRANTEE CONSENTS TO THE RECORDATION OF SAID TRACT.

[Signature]
DANIEL R. FERONS, CHIEF ENGINEER
SANTA MARGARITA WATER DISTRICT.

SANTA MARGARITA WATER DISTRICT NOTARY ACKNOWLEDGMENT

STATE OF CALIFORNIA)
COUNTY OF ORANGE) SS

ON THIS 14th DAY OF JUNE, 2000, BEFORE ME, ANDREA M. EVANS, A NOTARY PUBLIC IN AND FOR SAID STATE, PERSONALLY APPEARED DANIEL R. FERONS PERSONALLY KNOWN TO ME (OR PROVED TO ME ON THE BASIS OF SATISFACTORY EVIDENCE) TO BE THE PERSON WHOSE NAME IS SUBSCRIBED TO THE WITHIN INSTRUMENT AND ACKNOWLEDGED TO ME THAT HE EXECUTED THE SAME IN HIS AUTHORIZED CAPACITY, AND THAT BY HIS SIGNATURE ON THE INSTRUMENT THE PERSON, OR THE ENTITY UPON BEHALF OF WHICH THE PERSON ACTED, EXECUTED THE INSTRUMENT.

WITNESS MY HAND:

[Signature]
NOTARY PUBLIC IN AND FOR SAID STATE

MY PRINCIPAL PLACE OF BUSINESS IS
IN ORANGE COUNTY

ANDREA M. EVANS
PRINT NAME

MY COMMISSION EXPIRES 04-08-00

COUNTY TREASURER-TAX COLLECTOR'S CERTIFICATE

STATE OF CALIFORNIA)
COUNTY OF ORANGE) SS

I HEREBY CERTIFY THAT ACCORDING TO THE RECORDS OF MY OFFICE THERE ARE NO LIENS AGAINST THE LAND COVERED BY THIS MAP OR ANY PART THEREOF FOR UNPAID STATE, COUNTY, MUNICIPAL OR LOCAL TAXES OR SPECIAL ASSESSMENTS COLLECTED AS TAXES, EXCEPT TAXES OR SPECIAL ASSESSMENTS COLLECTED AS TAXES NOT YET PAYABLE.

AND DO ALSO CERTIFY TO THE RECORDER OF ORANGE COUNTY THAT THE PROVISIONS OF THE SUBDIVISION MAP ACT HAVE BEEN COMPLIED WITH REGARDING DEPOSITS TO SECURE THE PAYMENT OF TAXES OR SPECIAL ASSESSMENTS COLLECTED AS TAXES ON THE LAND COVERED BY THIS MAP.

DATED THIS 16 DAY OF JUNE, 2000.

JOHN M.W. MOORLACH
COUNTY TREASURER - TAX COLLECTOR

BY: [Signature]
DEPUTY TREASURER - TAX COLLECTOR

ALL OF TENTATIVE TRACT NO. 15885
6.601 ACRES
NUMBERED LOTS: 7
LETTERED LOTS: 9
DATE OF SURVEY : FEBRUARY, 2000

TRACT NO. 15885

IN THE UNINCORPORATED TERRITORY OF THE COUNTY OF ORANGE,
STATE OF CALIFORNIA

MDS CONSULTING

FEBRUARY, 2000

GARY W. DOKICH, L.S. 4693

BASIS OF BEARINGS:

THE BEARINGS SHOWN HEREON ARE BASED ON THE BEARING BETWEEN OCS HORIZONTAL CONTROL STATION GPS NO. 1417 AND STATION GPS NO. 1424, BEING N 1°36'34" E PER RECORDS ON FILE IN THE OFFICE OF THE ORANGE COUNTY SURVEYOR.

DATUM STATEMENT:

COORDINATES SHOWN ARE BASED ON THE CALIFORNIA COORDINATE SYSTEM, (CCS83) ZONE VI, 1983 NAD, (1991.35 EPOCH OCS GPS ADJUSTMENT).

ALL DISTANCES SHOWN ARE GROUND, UNLESS OTHERWISE NOTED. TO OBTAIN A GRID DISTANCE, MULTIPLY THE GROUND DISTANCE BY 0.999948295, AS SHOWN ON RECORD OF SURVEY 97-1086, R.S.B. 167/26-28.

MONUMENT NOTES:

- ALL MONUMENTS SHOWN AS SET WILL BE SET WITHIN 90 DAYS AFTER THE ACCEPTANCE OF IMPROVEMENTS, EXCEPT AS NOTED.
- TIES TO CENTERLINE MONUMENTS WILL BE MADE AND A COPY OF SAID TIES WILL BE FURNISHED TO THE COUNTY OF ORANGE. CENTERLINE TIES WILL BE SET FOR LOCATIONS INDICATED HEREON ONLY.
- A** INDICATES FOUND 2 1/2" IRON PIPE W/2" OCS BRASS CAP STAMPED "GPS 1424 9-95" PER RECORDS ON FILE IN THE ORANGE COUNTY SURVEYOR'S OFFICE.
N = 2,152,873.842, E = 6,141,904.527
- B** INDICATES FOUND 2 1/2" IRON PIPE W/2" OCS BRASS CAP STAMPED "GPS 1417 9-95" PER TRACT NO. 15884, M.M. 794/33-44, AND RECORDS ON FILE IN THE ORANGE COUNTY SURVEYOR'S OFFICE.
N = 2,141,450.558, E = 6,141,583.535

- INDICATES LOCATION OF 2" I.P. TAGGED "L.S. 5557" OR SPIKE AND WASHER STAMPED "L.S. 5557" OR LEAD, TACK AND TAG "L.S. 5557" TO BE SET PER TRACT NO. 15884, M.M. 794/33-44.
- INDICATES LOCATION OF 1" I.P. TAGGED "L.S. 5557" OR SPIKE AND WASHER STAMPED "L.S. 5557" OR LEAD, TACK AND TAG "L.S. 5557" TO BE SET PER TRACT NO. 15884, M.M. 794/33-44.
- INDICATES SET 2" IRON PIPE TAGGED "L.S. 4693".
- INDICATES SET SPIKE AND WASHER STAMPED "L.S. 4693" IN ASPHALT PAVING HAVING A THICKNESS OF 2" OR MORE, OR NAIL AND TAG "L.S. 4693" IN CONCRETE, OR A 2" IRON PIPE TAGGED "L.S. 4693".
- SET 1" IRON PIPE TAGGED "L.S. 4693" OR NAIL AND TAG "L.S. 4693" IN CONCRETE AT ALL LOT CORNERS, EXCEPT AS NOTED. (NO MONUMENTS WILL BE SET FOR ANGLE POINTS, CORNER CUTOFFS, B.C.'S, E.C.'S, P.R.C.'S OR P.C.C.'S THAT ABUT A STREET WHICH ARE NOT LOT CORNERS MARKING SIDELINES, UNLESS OTHERWISE NOTED.)
- SET 2" IRON PIPE TAGGED "L.S. 4693", OR SPIKE AND WASHER STAMPED "L.S. 4693" IN ASPHALT PAVING HAVING A THICKNESS OF 2" OR MORE, OR A NAIL AND TAG "L.S. 4693" IN CONCRETE AT ALL TRACT BOUNDARY CORNERS UNLESS OTHERWISE NOTED. (NO MONUMENTS WILL BE SET FOR ANGLE POINTS, B.C.'S OR E.C.'S THAT ABUT A STREET WHICH ARE NOT BOUNDARY CORNERS, UNLESS OTHERWISE NOTED.)


A GPS # 1424
N= 2152873.842
E= 6141904.527



SCALE 1" = 100'

SEE SHEET 4

SEE SHEET 3

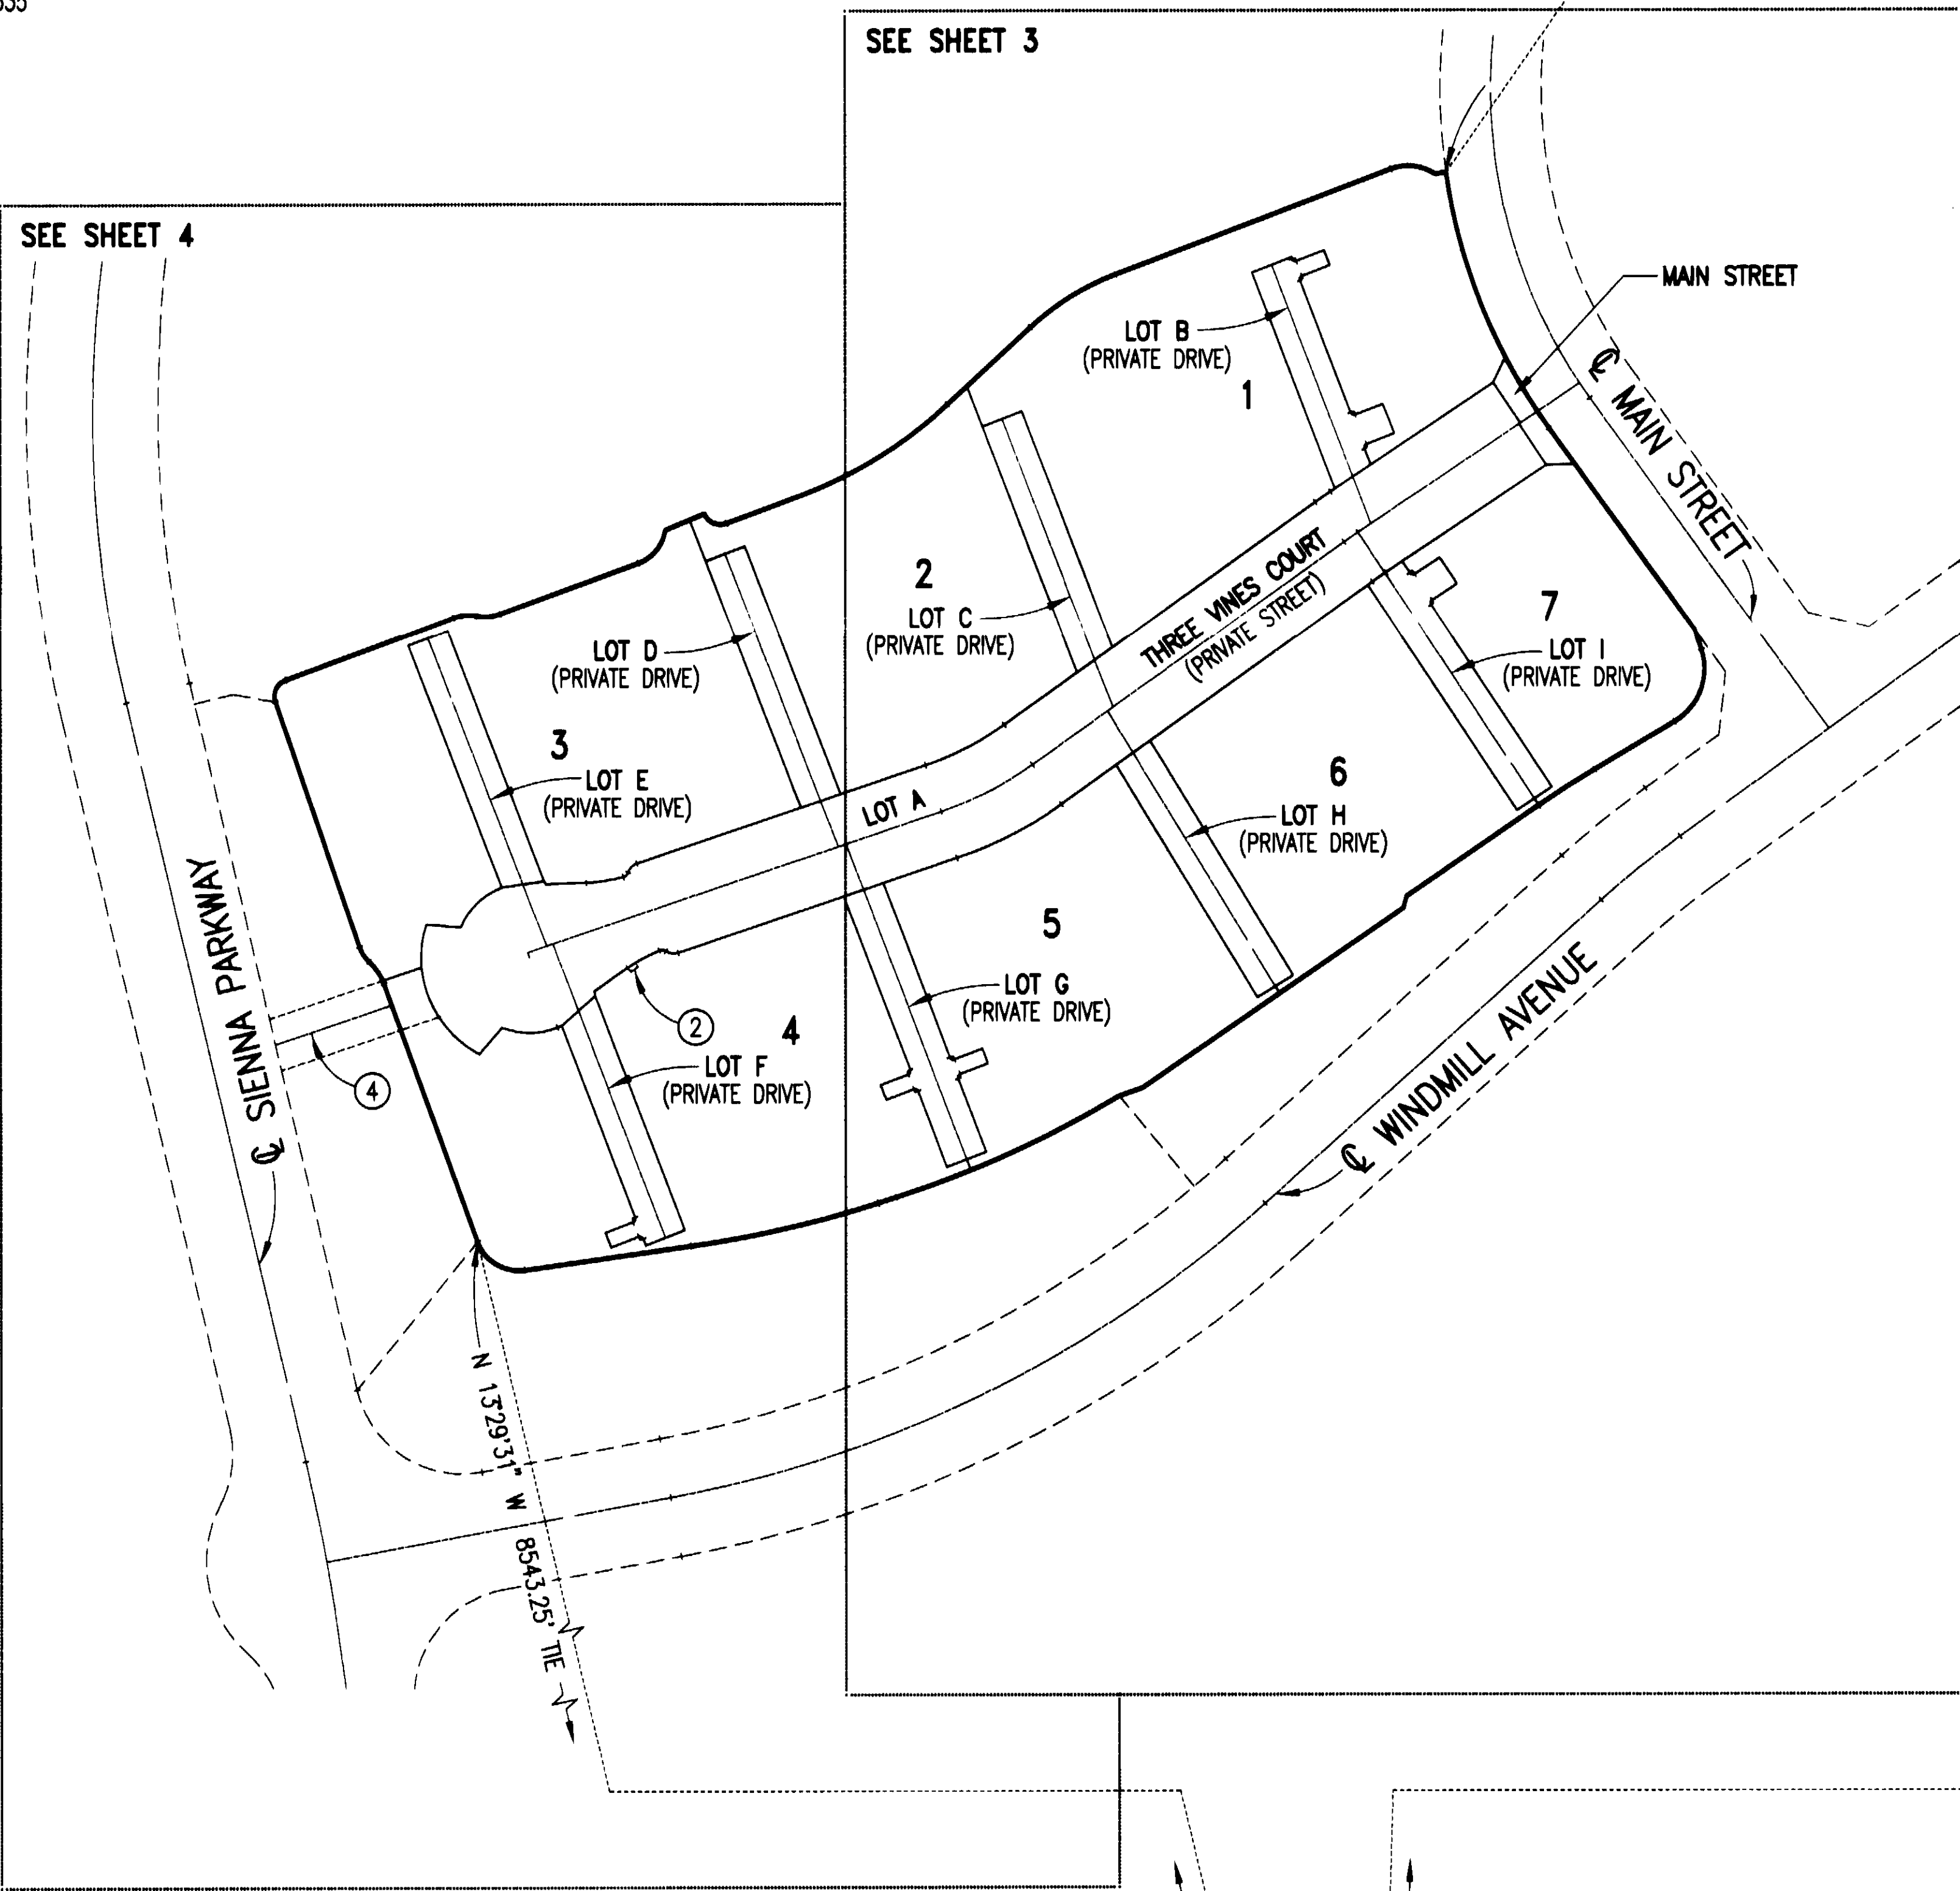

BASIS OF BEARINGS
N 1°36'34" E 11428.38' GROUND
11427.79' GRID

NOTES

- AUTOMATIC FIRE SPRINKLER NOTE:**
ALL STRUCTURES WITHIN THE BOUNDARIES OF THIS MAP SHALL BE PROTECTED BY AN AUTOMATIC FIRE SPRINKLER SYSTEM WHICH MEETS THE APPROVAL OF THE FIRE CHIEF.
- HIGH FIRE HAZARD AREA NOTE:**
THE LOTS SHOWN ON THIS MAP ARE IN A HIGH FIRE HAZARD AREA DUE TO WILDLAND EXPOSURE.
- SPECIAL FIRE PROTECTION NOTE:**
PROPERTY WITHIN THE BOUNDARIES OF THIS MAP IS IN A SPECIAL FIRE PROTECTION AREA. A TOTAL EXCLUSION HAS BEEN GRANTED FOR THIS TRACT.
- LOTS A, B, C, D, E, F, G, H AND I ARE NOT SEPARATE BUILDING SITES AND ARE TO BE DEDICATED TO THE HOMEOWNER'S ASSOCIATION FOR PRIVATE STREET / PRIVATE DRIVE PURPOSES.

EASEMENT NOTES:

- ① INDICATES AN EASEMENT DEDICATED TO THE COUNTY OF ORANGE HEREON FOR EMERGENCY AND PUBLIC SERVICE VEHICULAR INGRESS AND EGRESS PURPOSES.
- ② INDICATES AN EASEMENT DEDICATED TO THE SANTA MARGARITA WATER DISTRICT HEREON FOR SEWER AND WATER PURPOSES.
- ③ INDICATES AN EASEMENT FOR STORM DRAIN PURPOSES TO BE GRANTED TO THE HOMEOWNER'S ASSOCIATION.
- ④ INDICATES EASEMENT FOR SEWER, WATER AND ACCESS PURPOSES DEDICATED TO THE SANTA MARGARITA WATER DISTRICT PER TRACT NO. 15884, M.M. 794/33-44.
- ⑤ INDICATES AN EASEMENT RESERVED FOR PUBLIC UTILITY PURPOSES.

BOUNDARY CONTROL AND INDEX MAP

B GPS # 1417
N= 2141450.558
E= 6141583.535

ALL OF TENTATIVE TRACT NO. 15885
6.601 ACRES
NUMBERED LOTS: 7
LETTERED LOTS: 9
DATE OF SURVEY : FEBRUARY, 2000

TRACT NO. 15885

IN THE UNINCORPORATED TERRITORY OF THE COUNTY OF ORANGE,
STATE OF CALIFORNIA

MDS CONSULTING

FEBRUARY, 2000

GARY W. DOKICH, L.S. 4693

CURVE TABLE


NO	DELTA	RADIUS	ARC LGT	TAN
1	9°37'10"	655.00'	109.97'	55.11'
2	3°34'38"	613.00'	38.27'	19.14'
3	7°54'11"	35.00'	47.59'	28.29'
4	54°20'25"	28.00'	26.56'	14.37'
5	22°01'04"	150.00'	57.64'	29.18'
6	1°51'02"	272.00'	8.79'	4.39'
7	16°55'00"	228.00'	67.32'	33.91'
8	16°55'00"	172.00'	50.78'	25.58'
9	1°51'02"	328.00'	10.59'	5.30'
10	6°01'00"	550.00'	57.76'	28.90'
11	1°51'02"	300.00'	9.69'	4.84'
12	16°55'00"	200.00'	59.05'	29.74'
13	1°58'14"	300.00'	10.32'	5.16'
14	6°16'49"	329.00'	36.06'	18.05'
15	1°58'50"	329.00'	11.37'	5.69'
16	1°49'22"	272.00'	8.65'	4.33'
17	0°01'40"	272.00'	0.13'	0.07'
18	90°00'00"	2.00'	3.14'	2.00'

TRACT NO. 15884
M.M. 794/33-44

SEE SHEET 2

SCALE 1" = 40'

TRACT NO. 15884
M.M. 794/33-44

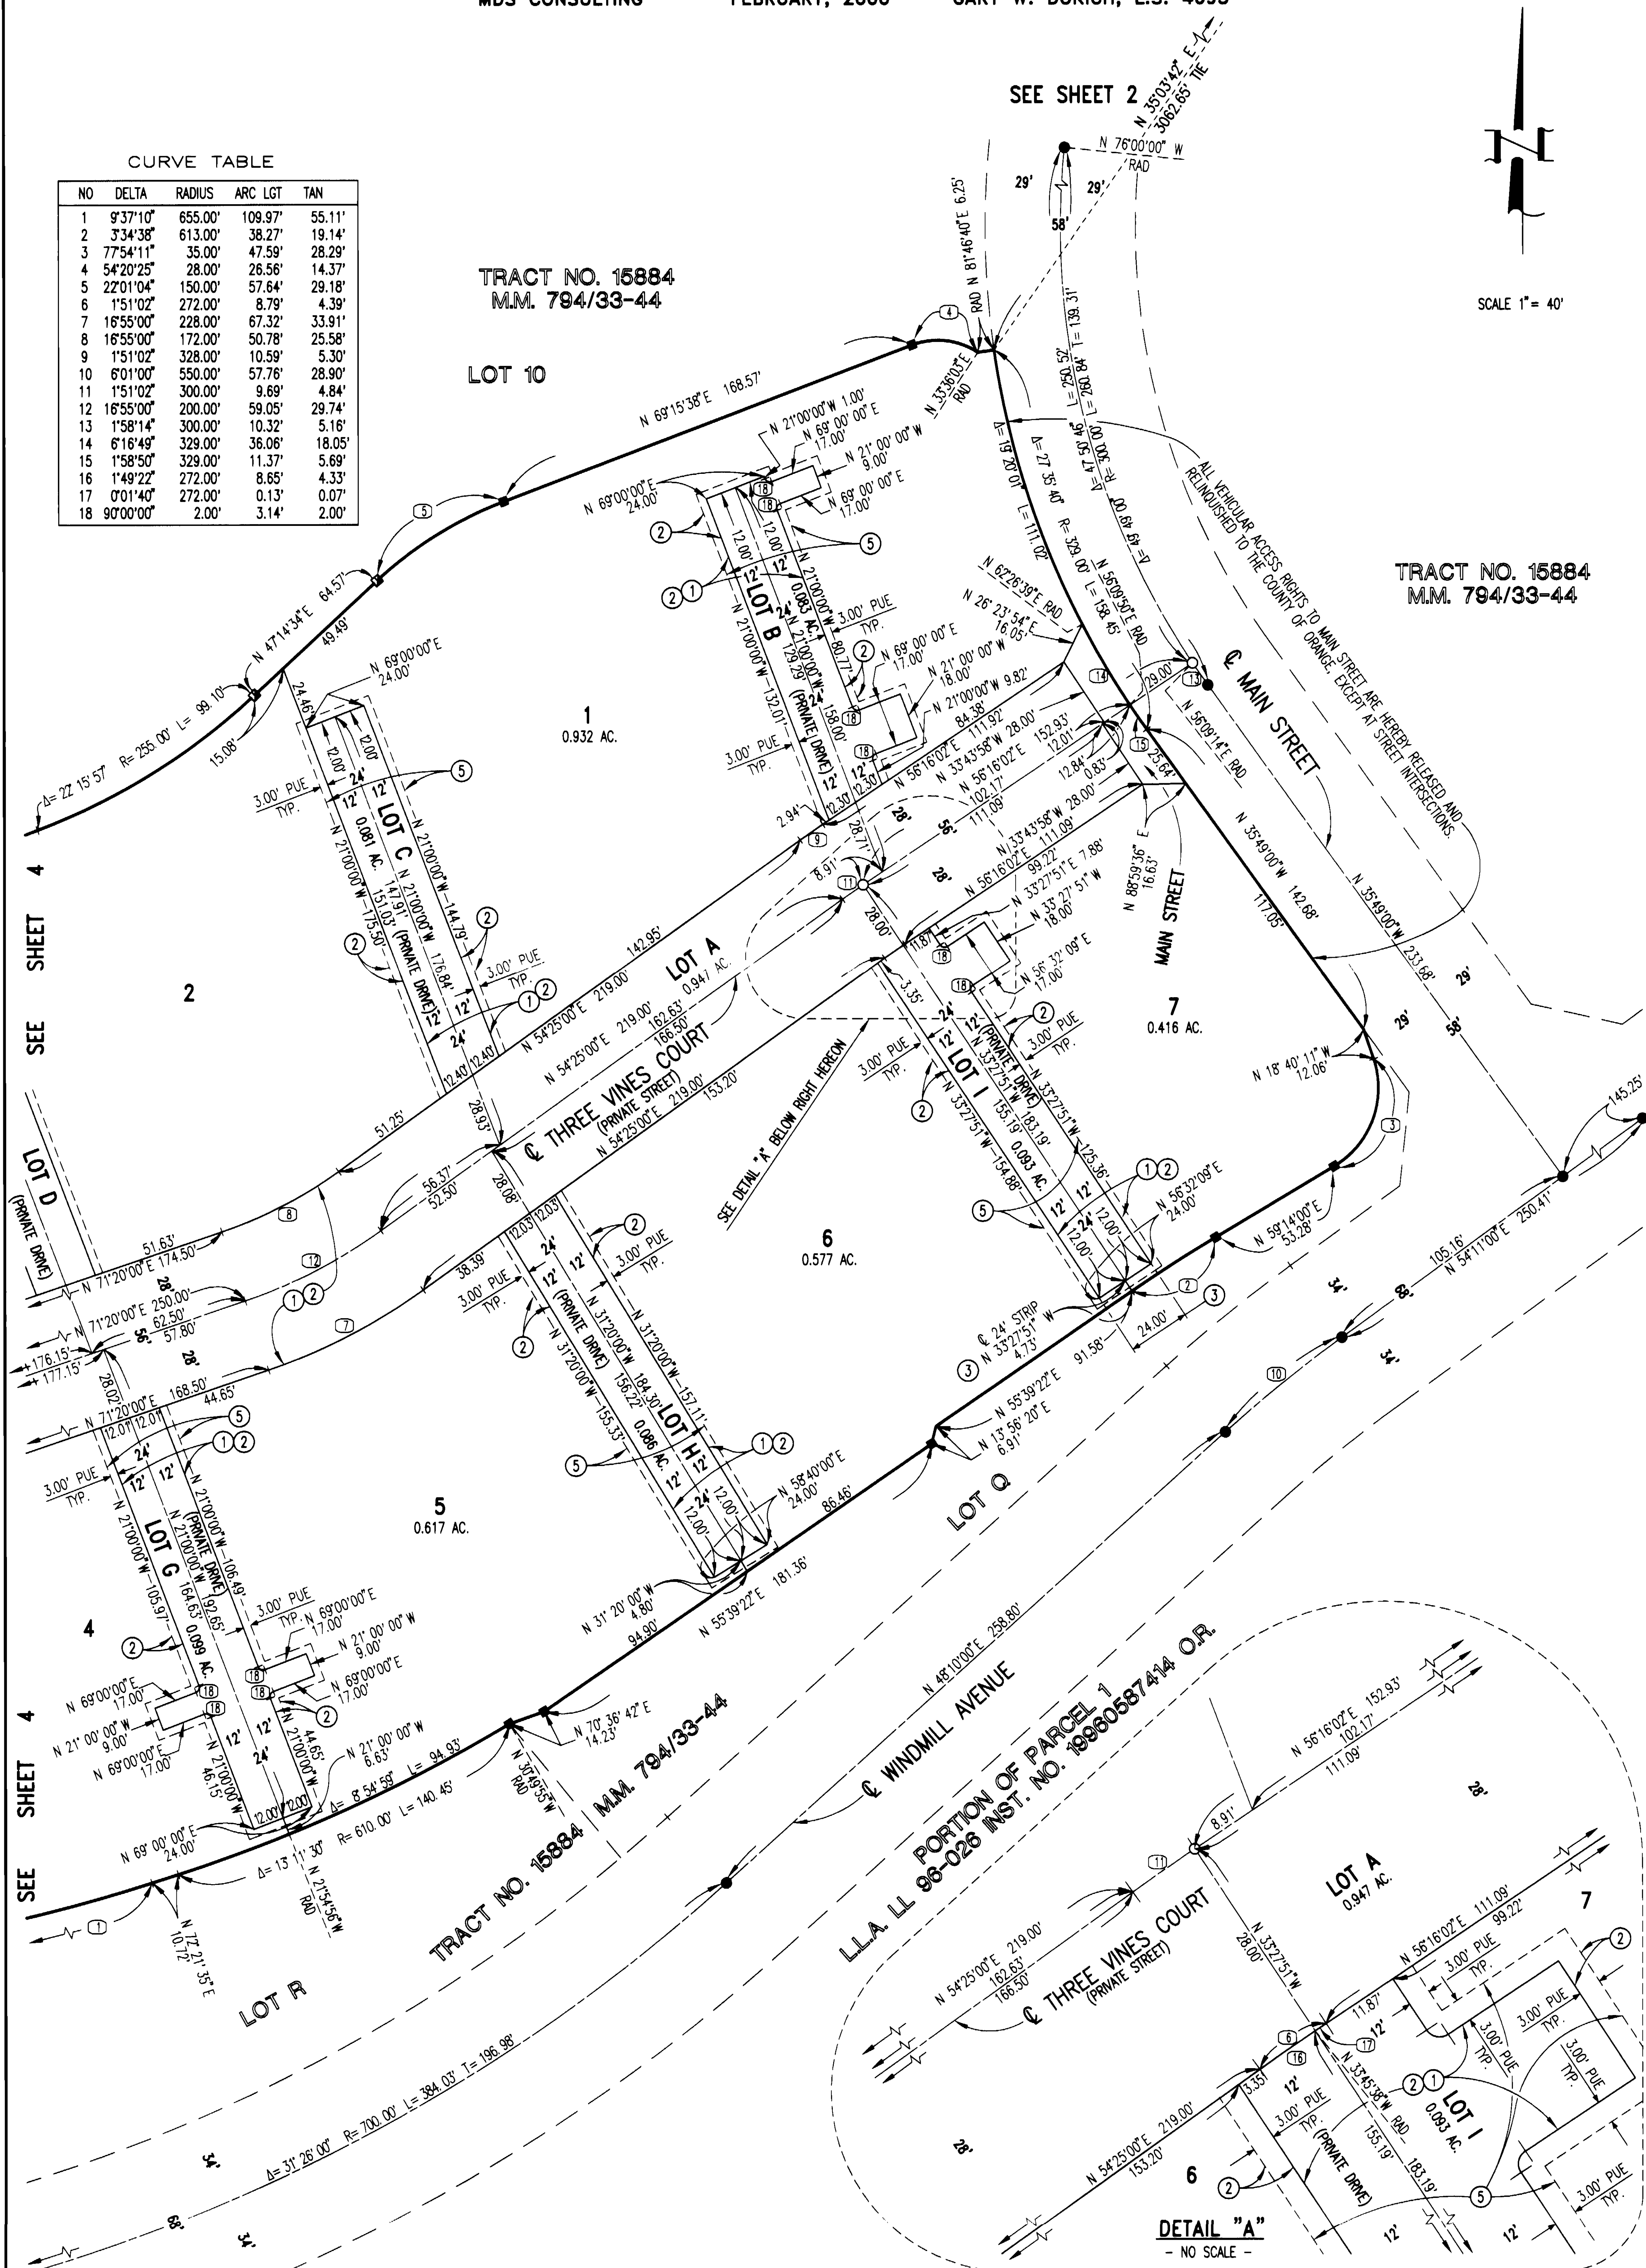

SEE SHEET 2 FOR BOUNDARY CONTROL MAP, INDEX MAP,
BASIS OF BEARINGS, DATUM STATEMENT, MONUMENT NOTES,
EASEMENT NOTES AND NOTES.

ALL OF TENTATIVE TRACT NO. 15885
6.601 ACRES
NUMBERED LOTS: 7
LETTERED LOTS: 9
DATE OF SURVEY : FEBRUARY, 2000

TRACT NO. 15885

IN THE UNINCORPORATED TERRITORY OF THE COUNTY OF ORANGE,
STATE OF CALIFORNIA

MDS CONSULTING

FEBRUARY, 2000

GARY W. DOKICH, L.S. 4693

SHEET 4 OF 4 SHEETS

CURVE TABLE

NO	DELTA	RADIUS	ARC LGT	TAN
1	28°43'21"	20.00'	10.03'	5.12'
2	27°39'06"	32.00'	15.44'	7.88'
3	78°03'33"	25.00'	34.06'	20.27'
4	22°01'04"	150.00'	57.64'	29.18'
5	87°50'38"	10.00'	15.33'	9.63'
6	61°12'42"	24.00'	25.64'	14.20'
7	30°58'03"	25.00'	13.51'	6.93'
8	31°10'46"	25.00'	13.60'	6.98'
9	88°34'35"	10.00'	15.46'	9.75'
10	16°55'00"	228.00'	67.32'	33.91'
11	53°17'13"	8.00'	7.44'	4.01'
12	56°49'39"	4.00'	3.97'	2.16'
13	12°32'57"	95.00'	20.81'	10.45'
14	16°14'37"	10.00'	2.84'	1.43'
15	12°58'44"	95.00'	21.52'	10.81'
16	11°08'50"	10.00'	1.95'	0.98'
17	44°30'46"	43.00'	33.41'	17.60'
18	80°22'50"	62.00'	86.98'	52.38'
19	43°16'45"	43.00'	32.48'	17.06'
20	16°55'00"	172.00'	50.78'	25.58'
21	2°54'00"	1150.00'	58.21'	29.11'
22	16°55'00"	200.00'	59.05'	29.74'
23	22°58'04"	62.00'	24.85'	12.60'
24	3°38'33"	32.00'	2.03'	1.02'
25	24°00'33"	32.00'	13.41'	6.80'
26	90°00'00"	2.00'	3.14'	2.00'
27	4°16'32"	610.00'	45.52'	22.77'

SCALE 1" = 40'




TRACT NO. 15884
M.M. 794/33-44

LOT 10

LOT 12

SEE SHEET 3

SEE SHEET 3

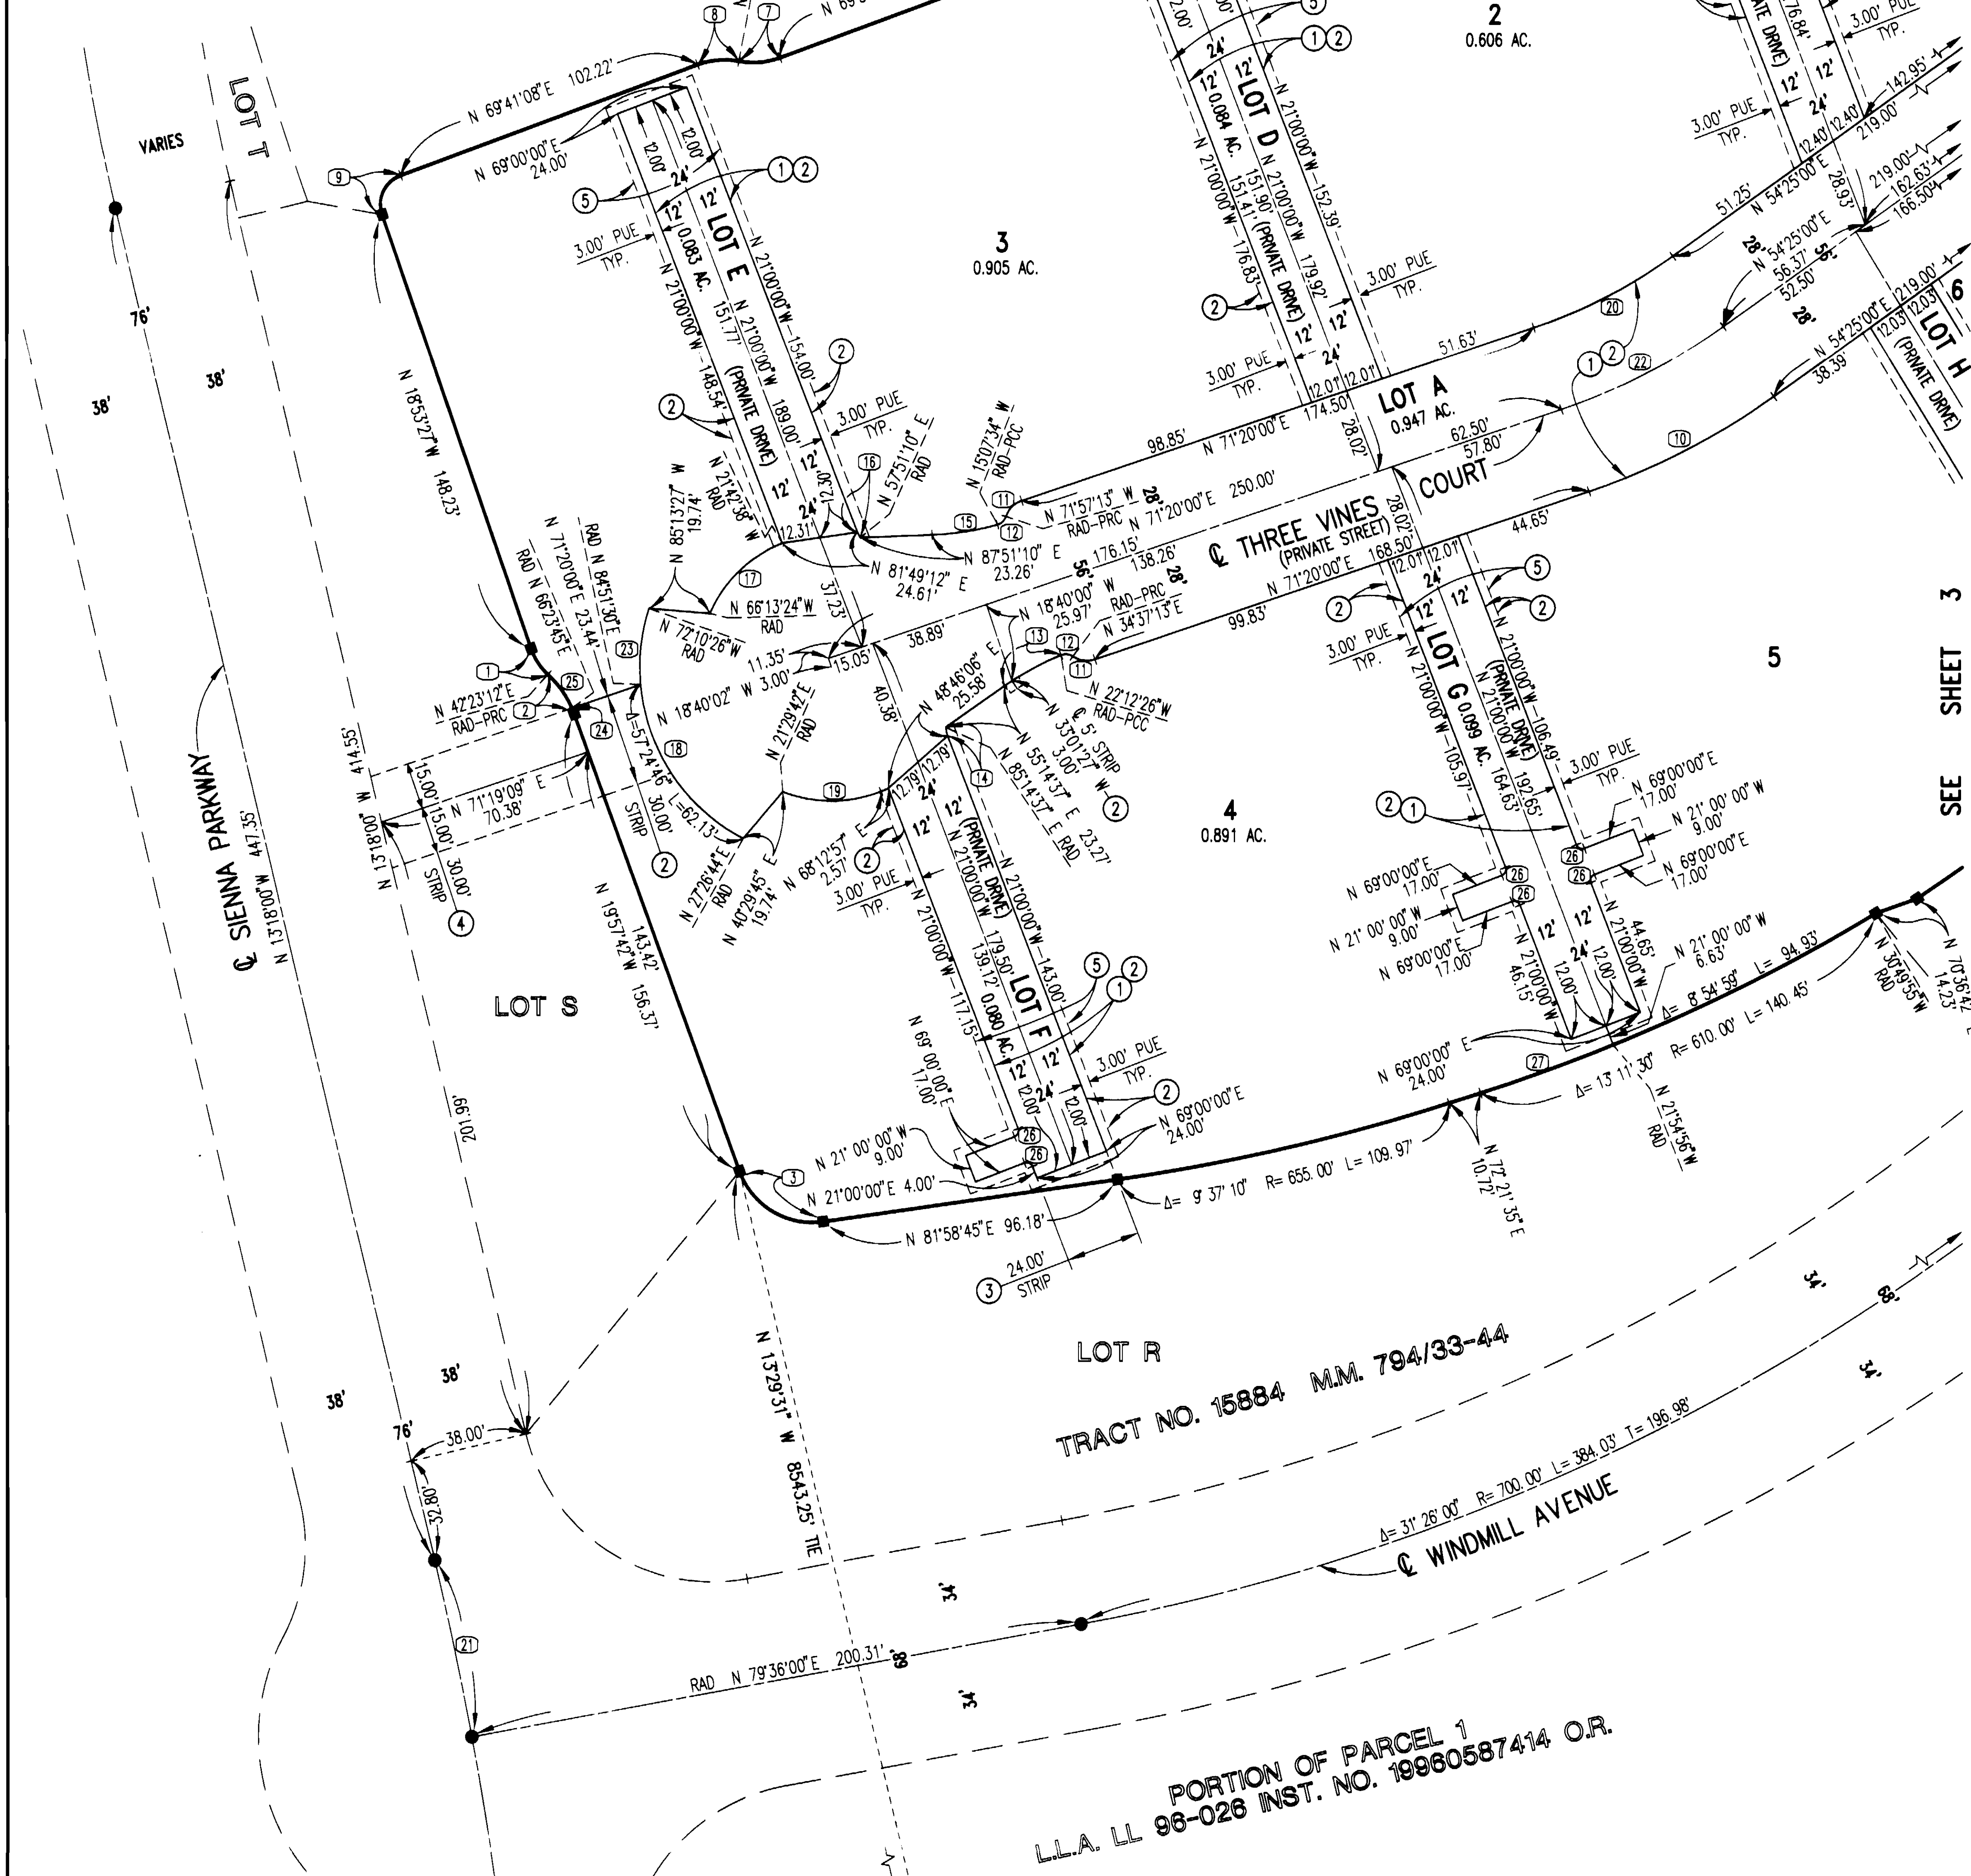

SEE SHEET 2 FOR BOUNDARY CONTROL MAP, INDEX MAP,
BASIS OF BEARINGS, DATUM STATEMENT, MONUMENT NOTES,
EASEMENT NOTES AND NOTES.

SEE SHEET 2