

SHEET 1 OF 4 SHEETS
61 NUMBERED LOTS AND LOTS
A THROUGH J, INCLUSIVE
6.186 ACRES
(ALL OF TENTATIVE
TRACT NO. 15886)

TRACT NO. 15886

IN THE UNINCORPORATED TERRITORY OF THE
COUNTY OF ORANGE, STATE OF CALIFORNIA

BEING A SUBDIVISION OF LOTS 7, N, O AND P OF TRACT NO. 15884, AS SHOWN ON A MAP FILED
IN BOOK 794, PAGES 33 THROUGH 44, INCLUSIVE, OF MISCELLANEOUS MAPS, IN THE OFFICE OF
THE COUNTY RECORDER OF SAID COUNTY OF ORANGE.

BLOCK: 5157
MODULE: 16 AND 17

HUNSAKER AND ASSOCIATES IRVINE, INC.
RORY S. WILLIAMS, L.S. 6654 DATE OF SURVEY: JANUARY, 2000

ACCEPTED AND FILED AT THE
REQUEST OF
LAWYERS TITLE COMPANY
DATE: OCTOBER 30, 2000
TIME: 9:02 A.M. FEE: \$13.00
INSTRUMENT NO. 20000583784
BOOK 807 PAGE 25-28 M/M
GARY L. GRANVILLE
COUNTY CLERK - RECORDER
BY [Signature] DEPUTY

OWNERSHIP STATEMENT:

WE, THE UNDERSIGNED, BEING ALL PARTIES HAVING ANY RECORD TITLE INTEREST IN THE LAND COVERED BY THIS MAP, DO HEREBY CONSENT TO THE PREPARATION AND RECORDATION OF SAID MAP, AS SHOWN WITHIN THE DISTINCTIVE BORDER LINE.

WE HEREBY DEDICATE TO THE COUNTY OF ORANGE:

AN EASEMENT FOR INGRESS AND EGRESS OF EMERGENCY AND PUBLIC SERVICE VEHICLES OVER LOTS G, H, I AND J.

WE RESERVE TO OURSELVES, OUR SUCCESSORS AND ASSIGNS THE PUBLIC UTILITY EASEMENTS SHOWN ON THIS MAP, FOR THE USE AND BENEFIT OF THE VARIOUS UTILITY COMPANIES AUTHORIZED TO PROVIDE SERVICE TO THE LOTS SHOWN HEREON.

WE ALSO DO HEREBY DECLARE THAT THE LAND COVERED BY THIS MAP IS LOCATED IN A HIGH FIRE HAZARD AREA DUE TO WILDLAND EXPOSURE BASED ON STATE GRA MAPS.

WE ALSO HEREBY DEDICATE TO THE SANTA MARGARITA WATER DISTRICT THE PIPELINE EASEMENTS FOR WATER, SEWER AND ACCESS PURPOSES, OVER ALL THE PRIVATE DRIVEWAYS AND PRIVATE STREETS TOGETHER WITH THE PIPELINE EASEMENT FOR WATER AND SEWER PURPOSES, ALL AS SHOWN ON THIS TRACT MAP, WHICH EASEMENTS SHALL BE SUBJECT TO THE SAME TERMS AND CONDITIONS AS SHOWN IN THAT CERTAIN EASEMENT, RECORDED OCTOBER 6, 1980, IN BOOK 13776, PAGE 341 OF OFFICIAL RECORDS OF ORANGE COUNTY, CALIFORNIA.

K. HOVNANIAN AT THE GABLES, LLC, A CALIFORNIA LIMITED LIABILITY COMPANY; OWNER.

BY: Nicholas Pappas BY: _____
NAME: NICHOLAS PAPPAS NAME: _____
TITLE: President TITLE: _____

DMB LADERA, LLC, A DELAWARE LIMITED LIABILITY COMPANY; BENEFICIARY UNDER DEED OF TRUST RECORDED AS INSTRUMENT NO. 20000080968 AND OPTIONEE PER DOCUMENT RECORDED AS INSTRUMENT NO. 20000080967 BOTH OF OFFICIAL RECORDS OF ORANGE COUNTY.

BY: RANCHO MISSION VIEJO, L.L.C., A DELAWARE LIMITED LIABILITY COMPANY, AS AGENT AND/OR MANAGER.

BY: Paul Johnson BY: _____
NAME: PAUL JOHNSON NAME: _____
TITLE: J.V. COMMUNITY DEVELOPMENT TITLE: _____

DMB CONSOLIDATED HOLDINGS, L.L.C., AN ARIZONA LIMITED LIABILITY COMPANY, BENEFICIARY UNDER DEEDS OF TRUST RECORDED AS INSTRUMENT NOS. 19960824030 AND 19990288616, BOTH OF OFFICIAL RECORDS OF ORANGE COUNTY.

BY: DMB ASSOCIATES, INC. AN ARIZONA CORPORATION, AS MANAGER.

BY: Terry D. Randall BY: _____
NAME: TERRY D. RANDALL NAME: _____
TITLE: VICE PRESIDENT TITLE: _____

NOTARY ACKNOWLEDGMENTS:

STATE OF CALIFORNIA }
COUNTY OF ORANGE } SS

ON Aug. 24, 2000 BEFORE ME, Karen R. Sauerwein, PERSONALLY
APPEARED Nicholas Pappas AND Terry D. Randall PERSONALLY
KNOWN TO ME (OR PROVED TO ME ON THE BASIS OF SATISFACTORY EVIDENCE) TO BE THE PERSON(S)
WHOSE NAME(S) IS/ARE SUBSCRIBED TO THE WITHIN INSTRUMENT AND ACKNOWLEDGED TO ME THAT
HE/SHE/THEY EXECUTED THE SAME IN HIS/HER/THEIR AUTHORIZED CAPACITY(IES), AND THAT BY
HIS/HER/THEIR SIGNATURE(S) ON THE INSTRUMENT THE PERSON(S), OR ENTITY UPON BEHALF OF
WHICH THE PERSON(S) ACTED, EXECUTED THE INSTRUMENT.

WITNESS MY HAND:

SIGNATURE Karen R. Sauerwein MY PRINCIPAL PLACE OF BUSINESS IS
NOTARY PUBLIC IN AND FOR SAID STATE IN Orange COUNTY.
Karen R. Sauerwein MY COMMISSION EXPIRES: 11/27/02
(NAME PRINTED)

STATE OF CALIFORNIA }
COUNTY OF ORANGE } SS

ON 8/31/00 BEFORE ME, JEANNINE CARTA-HANSON, PERSONALLY
APPEARED PAUL JOHNSON AND TERRY D. RANDALL PERSONALLY
KNOWN TO ME (OR PROVED TO ME ON THE BASIS OF SATISFACTORY EVIDENCE) TO BE THE PERSON(S)
WHOSE NAME(S) IS/ARE SUBSCRIBED TO THE WITHIN INSTRUMENT AND ACKNOWLEDGED TO ME THAT
HE/SHE/THEY EXECUTED THE SAME IN HIS/HER/THEIR AUTHORIZED CAPACITY(IES), AND THAT BY
HIS/HER/THEIR SIGNATURE(S) ON THE INSTRUMENT THE PERSON(S), OR ENTITY UPON BEHALF OF
WHICH THE PERSON(S) ACTED, EXECUTED THE INSTRUMENT.

WITNESS MY HAND:

SIGNATURE Jeannine Carta-Hanson MY PRINCIPAL PLACE OF BUSINESS IS
NOTARY PUBLIC IN AND FOR SAID STATE IN ORANGE COUNTY.
JEANNINE CARTA-HANSON MY COMMISSION EXPIRES: FEB. 25, 2003
(NAME PRINTED)

STATE OF CALIFORNIA }
COUNTY OF ORANGE } SS

ON _____ BEFORE ME, _____, PERSONALLY
APPEARED _____ AND _____ PERSONALLY
KNOWN TO ME (OR PROVED TO ME ON THE BASIS OF SATISFACTORY EVIDENCE) TO BE THE PERSON(S)
WHOSE NAME(S) IS/ARE SUBSCRIBED TO THE WITHIN INSTRUMENT AND ACKNOWLEDGED TO ME THAT
HE/SHE/THEY EXECUTED THE SAME IN HIS/HER/THEIR AUTHORIZED CAPACITY(IES), AND THAT BY
HIS/HER/THEIR SIGNATURE(S) ON THE INSTRUMENT THE PERSON(S), OR ENTITY UPON BEHALF OF
WHICH THE PERSON(S) ACTED, EXECUTED THE INSTRUMENT.

WITNESS MY HAND:

SIGNATURE _____ MY PRINCIPAL PLACE OF BUSINESS IS
NOTARY PUBLIC IN AND FOR SAID STATE IN _____ COUNTY.
(NAME PRINTED) MY COMMISSION EXPIRES: _____


NOTES:

THE PRIVATE STREETS CONSTRUCTED WITHIN THIS MAP SHALL BE OWNED, OPERATED AND MAINTAINED BY THE DEVELOPER, SUCCESSORS OR ASSIGNS. THE COUNTY OF ORANGE SHALL HAVE NO RESPONSIBILITY THEREFOR, UNLESS PURSUANT TO APPROPRIATE SECTIONS OF THE STREET AND HIGHWAYS CODE OF THE STATE OF CALIFORNIA, THE SAID PRIVATE STREETS HAVE BEEN ACCEPTED INTO THE COUNTY ROAD SYSTEM BY APPROPRIATE RESOLUTION OF THE ORANGE COUNTY BOARD OF SUPERVISORS.

SURVEYOR'S STATEMENT:

I HEREBY STATE THAT THIS MAP, CONSISTING OF 4 SHEETS, CORRECTLY REPRESENTS A TRUE AND COMPLETE SURVEY AS SHOWN MADE IN JANUARY, 2000; WAS MADE BY ME OR UNDER MY DIRECTION; THAT THE MONUMENTS ARE OF THE CHARACTER AND OCCUPY (OR WILL OCCUPY) THE POSITIONS INDICATED BY SAID MAP; AND THAT SAID MONUMENTS ARE (OR WILL BE) SUFFICIENT TO ENABLE THE SURVEY TO BE RETRACED.

Rory S. Williams
RORY S. WILLIAMS,
L.S. 6654
EXPIRATION DATE: 12/31/03

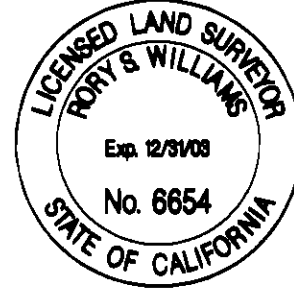


COUNTY SURVEYOR'S STATEMENT

I HEREBY STATE THAT I HAVE EXAMINED THIS MAP AND HAVE FOUND IT TO BE SUBSTANTIALLY IN CONFORMANCE WITH THE TENTATIVE MAP AS FILED WITH, AMENDED AND APPROVED BY THE ORANGE COUNTY SUBDIVISION COMMITTEE; THAT ALL PROVISIONS OF THE SUBDIVISION MAP ACT AND COUNTY SUBDIVISION REGULATIONS HAVE BEEN COMPLIED WITH AND I AM SATISFIED SAID MAP IS TECHNICALLY CORRECT.

DATED THIS 13th DAY OF October, 2000.

Robert J. Jelinek
JOHN CANAS, COUNTY SURVEYOR
Robert Jelinek, Deputy County Surveyor

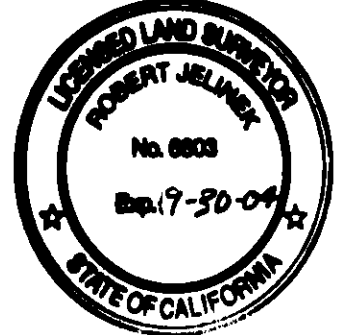

COUNTY TREASURER-TAX COLLECTOR'S CERTIFICATE:

STATE OF CALIFORNIA }
COUNTY OF ORANGE } SS

I HEREBY CERTIFY THAT ACCORDING TO THE RECORDS OF MY OFFICE THERE ARE NO LIENS AGAINST THE LAND COVERED BY THIS MAP OR ANY PART THEREOF FOR UNPAID STATE, COUNTY, MUNICIPAL OR LOCAL TAXES OR SPECIAL ASSESSMENTS COLLECTED AS TAXES, EXCEPT TAXES OR SPECIAL ASSESSMENTS COLLECTED AS TAXES NOT YET PAYABLE.

AND DO ALSO CERTIFY TO THE RECORDER OF ORANGE COUNTY THAT THE PROVISIONS OF THE SUBDIVISION MAP ACT HAVE BEEN COMPLIED WITH REGARDING DEPOSITS TO SECURE THE PAYMENT OF TAXES OR SPECIAL ASSESSMENTS COLLECTED AS TAXES ON THE LAND COVERED BY THIS MAP.

DATED THIS 19th DAY OF September, 2000.

JOHN M.W. MOORLACH BY: John M.W. Moorlach
COUNTY TREASURER-TAX COLLECTOR DEPUTY TREASURER-TAX COLLECTOR

CLERK OF THE BOARD OF SUPERVISOR'S CERTIFICATE:

STATE OF CALIFORNIA }
COUNTY OF ORANGE } SS

I HEREBY CERTIFY THAT THIS MAP WAS PRESENTED FOR APPROVAL TO THE BOARD OF SUPERVISOR'S OF THE COUNTY OF ORANGE AT REGULAR MEETING THEREOF HELD ON THE 24th DAY OF OCTOBER, 2000. AND THAT THEREUPON SAID BOARD DID, BY AN ORDER DULY PASSED AND ENTERED, APPROVE SAID MAP.


AND DID ACCEPT ON BEHALF OF THE COUNTY OF ORANGE:

THE EASEMENT FOR INGRESS AND EGRESS OF EMERGENCY AND PUBLIC SERVICE VEHICLES OVER LOTS G, H, I AND J.

AND DID ALSO APPROVE SAID MAP PURSUANT TO THE PROVISIONS OF SECTION 66436 (e)(3)(A) OF THE SUBDIVISION MAP ACT.

DATED THIS 24th DAY OF OCTOBER, 2000.

Darlene J. Bloom
CLERK OF THE BOARD OF SUPERVISORS
DARLENE J. BLOOM

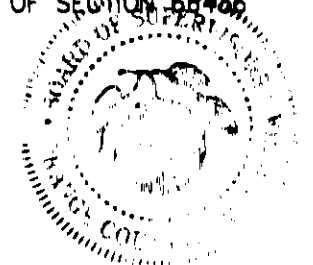

CERTIFICATE OF ACCEPTANCE - SANTA MARGARITA WATER DISTRICT

THE UNDERSIGNED, BEING THE DULY APPOINTED AGENT OF THE SANTA MARGARITA WATER DISTRICT, A PUBLIC CORPORATION IN ORANGE COUNTY, CALIFORNIA, PURSUANT TO ITS RESOLUTION NO. 88-10-2, DOES HEREBY ACCEPT ON BEHALF OF SAID DISTRICT, THE PIPELINE EASEMENTS FOR WATER, SEWER AND ACCESS PURPOSES AS DEDICATED AND SHOWN ON THIS TRACT MAP, BY AND BETWEEN THE SANTA MARGARITA WATER DISTRICT AND K. HOVNANIAN AT THE GABLES, L.L.C., A CALIFORNIA LIMITED LIABILITY COMPANY, AND DOES

HEREBY CERTIFY THAT THE GRANTEE CONSENTS TO THE RECORDATION OF SAID TRACT MAP.

Daniel R. Ferons
DANIEL R. FERONS, CHIEF ENGINEER
SANTA MARGARITA WATER DISTRICT

NOTARY ACKNOWLEDGMENT - SANTA MARGARITA WATER DISTRICT

STATE OF CALIFORNIA }
COUNTY OF ORANGE } SS

ON 9/11/00 BEFORE ME, ANDREA M. EVANS, PERSONALLY
APPEARED DANIEL R. FERONS, PERSONALLY
KNOWN TO ME (OR PROVED TO ME ON THE BASIS OF SATISFACTORY EVIDENCE) TO BE THE PERSON
WHOSE NAME IS SUBSCRIBED TO THE WITHIN INSTRUMENT AND ACKNOWLEDGED TO ME THAT
HE EXECUTED THE SAME IN HIS AUTHORIZED CAPACITY, AND THAT BY
HIS SIGNATURE ON THE INSTRUMENT THE PERSON, OR ENTITY UPON BEHALF OF
WHICH THE PERSON ACTED, EXECUTED THE INSTRUMENT.

WITNESS MY HAND:

SIGNATURE Andrea M. Evans MY PRINCIPAL PLACE OF BUSINESS IS
NOTARY PUBLIC IN AND FOR SAID STATE IN ORANGE COUNTY.
ANDREA M. EVANS MY COMMISSION EXPIRES: 4/08/04
(NAME PRINTED)

SIGNATURE OMISSIONS:

PURSUANT TO THE PROVISIONS OF SECTION 66436 (d)(3)(C) OF THE SUBDIVISION MAP ACT THE FOLLOWING SIGNATURES HAVE BEEN OMITTED:

THE COUNTY OF ORANGE, HOLDER OF EASEMENTS AS DEDICATED ON TRACT NO. 15884
SANTA MARGARITA WATER DISTRICT, HOLDER OF EASEMENTS AS DEDICATED ON TRACT NO. 15884
DMB LADERA, LLC, HOLDER OF EASEMENTS RESERVED IN DOCUMENT RECORDED AS INSTRUMENT NO. 20000080966 AND NO. 20000526755 BOTH OF OFFICIAL RECORDS.

LADERA DEVELOPMENT COMPANY, LLC OWNER OF ALL OIL, OIL RIGHTS, MINERAL RIGHTS, NATURAL GAS RIGHTS, OTHER HYDROCARBONS AND WATER RIGHTS, AS RESERVED IN DEED RECORDED AS INSTRUMENT NO. 19960624029, O.R.

**SHEET 2 OF 4 SHEETS
SCALE 1" = 200'
61 NUMBERED LOTS AND LOTS
A THROUGH J INCLUSIVE
ACREAGE: 6.185 ACRES
(ALL OF TENTATIVE
TRACT No. 15886)**

TRACT NO. 15886

**IN THE UNINCORPORATED TERRITORY OF THE COUNTY OF ORANGE,
STATE OF CALIFORNIA**

HUNSAKER AND ASSOCIATES IRVINE, INC.
RORY S. WILLIAMS, L.S. 6654 DATE OF SURVEY: JANUARY, 2000

BOUNDARY AND INDEX MAP

BASIS OF BEARINGS:

THE BEARINGS SHOWN HEREON ARE BASED ON THE BEARING BETWEEN O.C.S. HORIZONTAL CONTROL STATION GPS NO. 1424 AND STATION GPS NO. 1417 BEING $N01^{\circ}36'34"E$ PER RECORDS ON FILE IN THE OFFICE OF THE ORANGE COUNTY SURVEYOR.

DATUM STATEMENT:

COORDINATES SHOWN ARE BASED ON THE CALIFORNIA
COORDINATE SYSTEM (CCS83), ZONE VI, 1983 NAD,
(1991.35 EPOCH OCS GPS ADJUSTMENT).

ALL DISTANCES SHOWN ARE GROUND UNLESS OTHERWISE NOTED. TO OBTAIN GRID DISTANCE MULTIPLY GROUND DISTANCE BY 0.99994800.

MONUMENT NOTES:

1" I.P. TAGGED L.S. 6654 OR LEAD, TACK & TAG L.S. 6654 OR NAIL & TAG L.S. 6654 OR 8" S&W STAMPED L.S. 6654 TO BE SET AT ALL LOT CORNERS WITHIN 90 DAYS AFTER ACCEPTANCE OF IMPROVEMENTS, UNLESS OTHERWISE NOTED.

LEAD, TACK & TAG L.S. 6654 OR 8" S&W STAMPED L.S. 6654 TO BE SET IN TOP OF CURB ON ALL SIDE LOT LINES PRODUCED OR CONTINUED, 0.50' FROM INTERSECTION WITH 22.00' WIDE PRIVATE DRIVE RIGHTS OF WAY, IN LIEU OF AT LOT CORNERS, WITHIN 90 DAYS AFTER ACCEPTANCE OF IMPROVEMENTS.

8" S&W STAMPED L.S. 6654 OR LEAD, TACK & TAG L.S. 6654 OR 1" I.P. TAGGED L.S. 6654 IN MEDIAN TO BE SET AT ALL STREET CENTERLINE POINTS OF CONTROL, WITHIN 90 DAYS AFTER ACCEPTANCE OF IMPROVEMENTS, UNLESS OTHERWISE NOTED.

NO MONUMENTS WILL BE SET AT PRIVATE STREET LETTERED LOT CORNERS EXCEPT WHERE SAID CORNERS ARE COMMON WITH NUMBERED LOT CORNERS OR TRACT BOUNDARY CORNERS. UNLESS OTHERWISE NOTED.

- INDICATES FOUND MONUMENT AS NOTED OR LOCATION OF MONUMENT TO BE SET AS NOTED.
- INDICATES NOTHING TO BE SET.

NOTES:


THE PROPERTY IS IN A SPECIAL FIRE PROTECTION AREA.
TOTAL EXCLUSION GRANTED FOR THIS TRACT.

LOTS 3-12, 15-17, 20-29, 33-38, 41-44 AND 48-60
EXCEED FIRE DEPARTMENT REQUIREMENTS AND SHALL BE
PROVIDED WITH AUTOMATIC FIRE SPRINKLERS.

(X) INDICATES THE SHEET NUMBER

MONUMENT NOTES (CONTINUED):

- [1] INDICATES FD. # 1 1/2" O.C.S. BRASS DISK IN WELL MONUMENT PER TRACT NO. 15613, M.M. 795 / i-16.
- [2] INDICATES LOCATION OF 1" IRON PIPE TAGGED "L.S. 5557" OR SPIKE & WASHER STAMPED "L.S. 5557" OR LEAD, TACK & TAG "L.S. 5557" TO BE SET WITHIN 90 DAYS AFTER ACCEPTANCE OF IMPROVEMENTS, PER TRACT NO. 15884, M.M. 794 / 33-44.
- [3] INDICATES LOCATION OF 1" IRON PIPE TAGGED "L.S. 5557" OR SPIKE & WASHER STAMPED "L.S. 5557" OR LEAD, TACK & TAG "L.S. 5557" TO BE SET WITHIN 90 DAYS AFTER ACCEPTANCE OF IMPROVEMENTS, PER TRACT NO. 15615, M.M. 777 / 14-31.
- [4] INDICATES LOCATION OF 1" IRON PIPE TAGGED "L.S. 5557" OR SPIKE & WASHER STAMPED "L.S. 5557" OR LEAD, TACK & TAG "L.S. 5557" TO BE SET IN THE CORRECT POSITION, WITHIN 90 DAYS AFTER ACCEPTANCE OF IMPROVEMENTS, PER TRACT NO. 15884, M.M. 794 / 33-44.
- [5] INDICATES SET 2" IRON PIPE TAGGED " L.S. 6654 PRIOR TO THE RECORDATION OF THIS MAP.

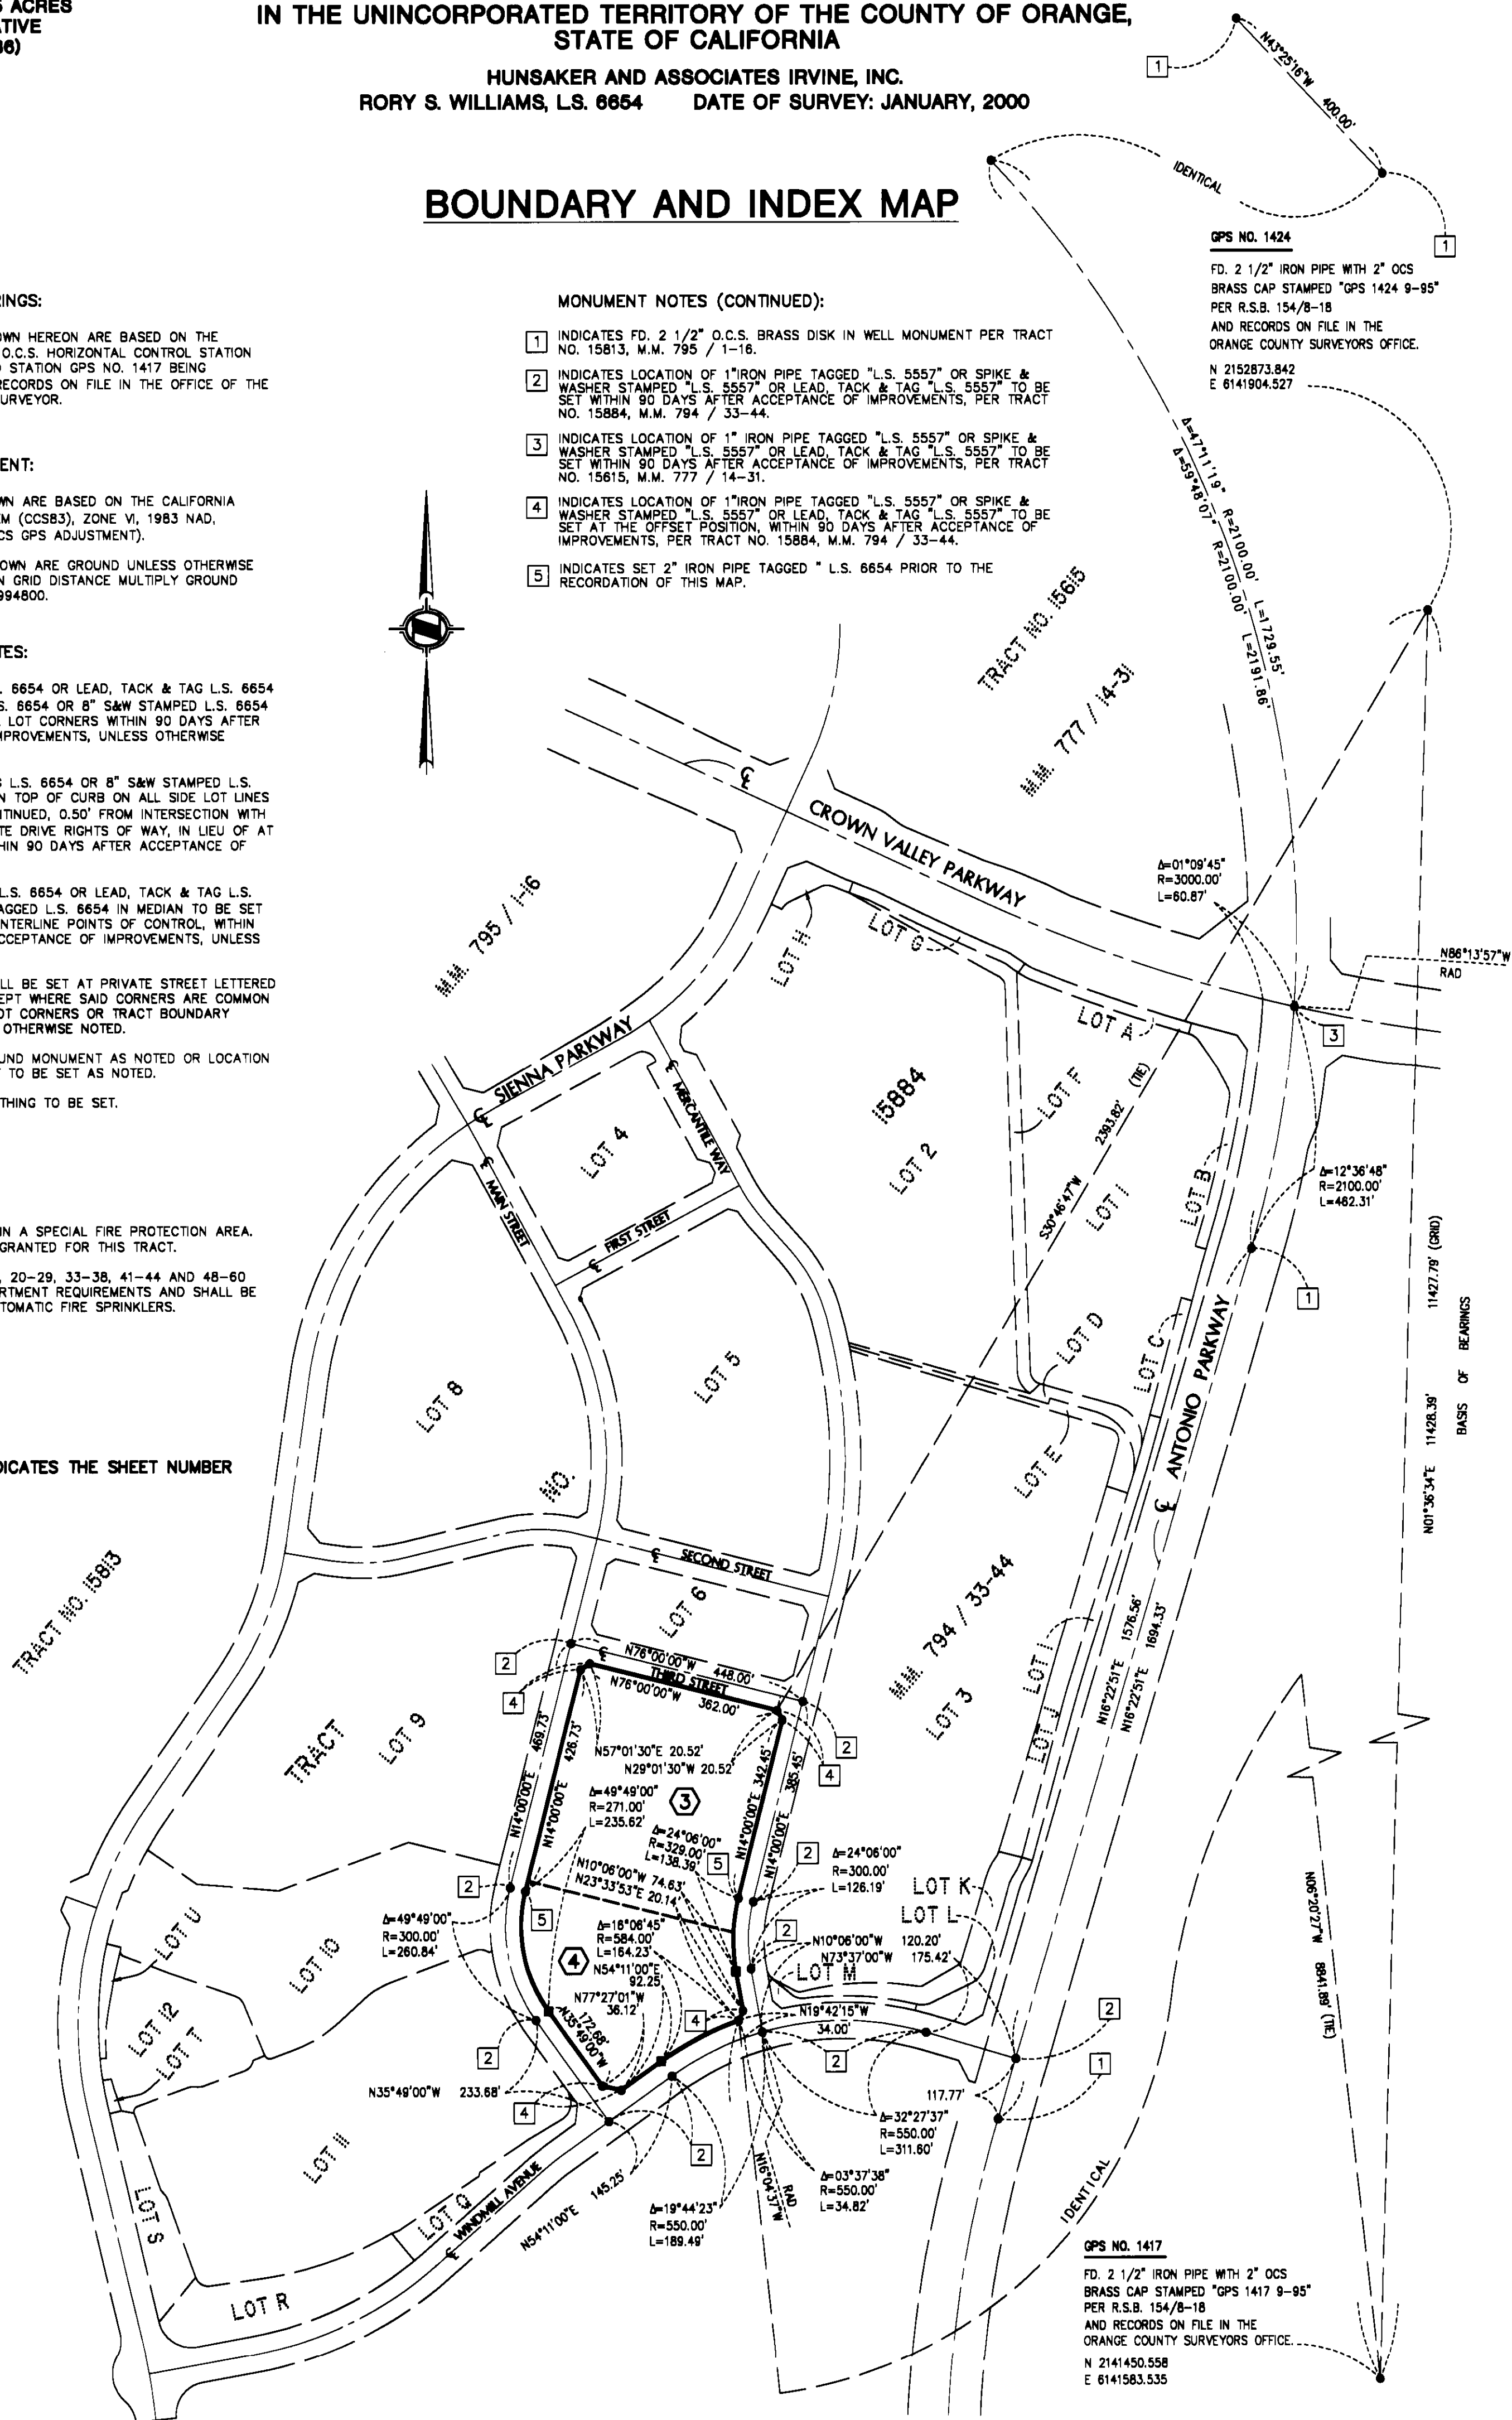

SHEET 3 OF 4 SHEETS
SCALE 1" = 30'
61 NUMBERED LOTS AND LOTS
A THROUGH J INCLUSIVE
ACREAGE: 6.186 ACRES
(ALL OF TENTATIVE
TRACT No. 15886)

TRACT NO. 15886

IN THE UNINCORPORATED TERRITORY OF THE COUNTY OF ORANGE,
STATE OF CALIFORNIA

HUNSAKER AND ASSOCIATES IRVINE, INC.
RORY S. WILLIAMS, L.S. 6654 DATE OF SURVEY: JANUARY, 2000

NOTES:

LOTS A THROUGH F, INCLUSIVE, ARE OPEN SPACE OR
LANDSCAPE LOTS RESERVED FOR FUTURE GRANT TO THE
HOMEOWNER'S ASSOCIATION BY SEPARATE INSTRUMENT
AND ARE NOT SEPARATE BUILDING SITES.



LOTS G THROUGH I, INCLUSIVE, ARE PRIVATE DRIVEWAYS.

LOT J IS A PRIVATE STREET.

EASEMENT NOTES:

- (A) INDICATES AN EASEMENT FOR WATER, SEWER AND ACCESS PURPOSES
DEDICATED TO SANTA MARGARITA WATER DISTRICT HEREON.
- (B) INDICATES A 2.00' WIDE EASEMENT FOR WATER LINE PURPOSES DEDICATED
HEREON TO SANTA MARGARITA WATER DISTRICT.
- (C) INDICATES AN EASEMENT FOR WATER AND ACCESS PURPOSES DEDICATED TO
SANTA MARGARITA WATER DISTRICT HEREON.
- (D) INDICATES AN EASEMENT FOR INGRESS AND EGRESS OF EMERGENCY AND
PUBLIC SERVICE VEHICLES DEDICATED HEREON TO THE COUNTY OF ORANGE.
- (H) INDICATES AN EASEMENT FOR PUBLIC UTILITY PURPOSES RESERVED HEREON
FOR FUTURE GRANT.

SEE SHEET 2 FOR BASIS OF BEARINGS,
DATUM STATEMENT, MONUMENT NOTES,
AND BOUNDARY AND INDEX MAP. SEE
SHEET 4 FOR DETAILS D AND E.

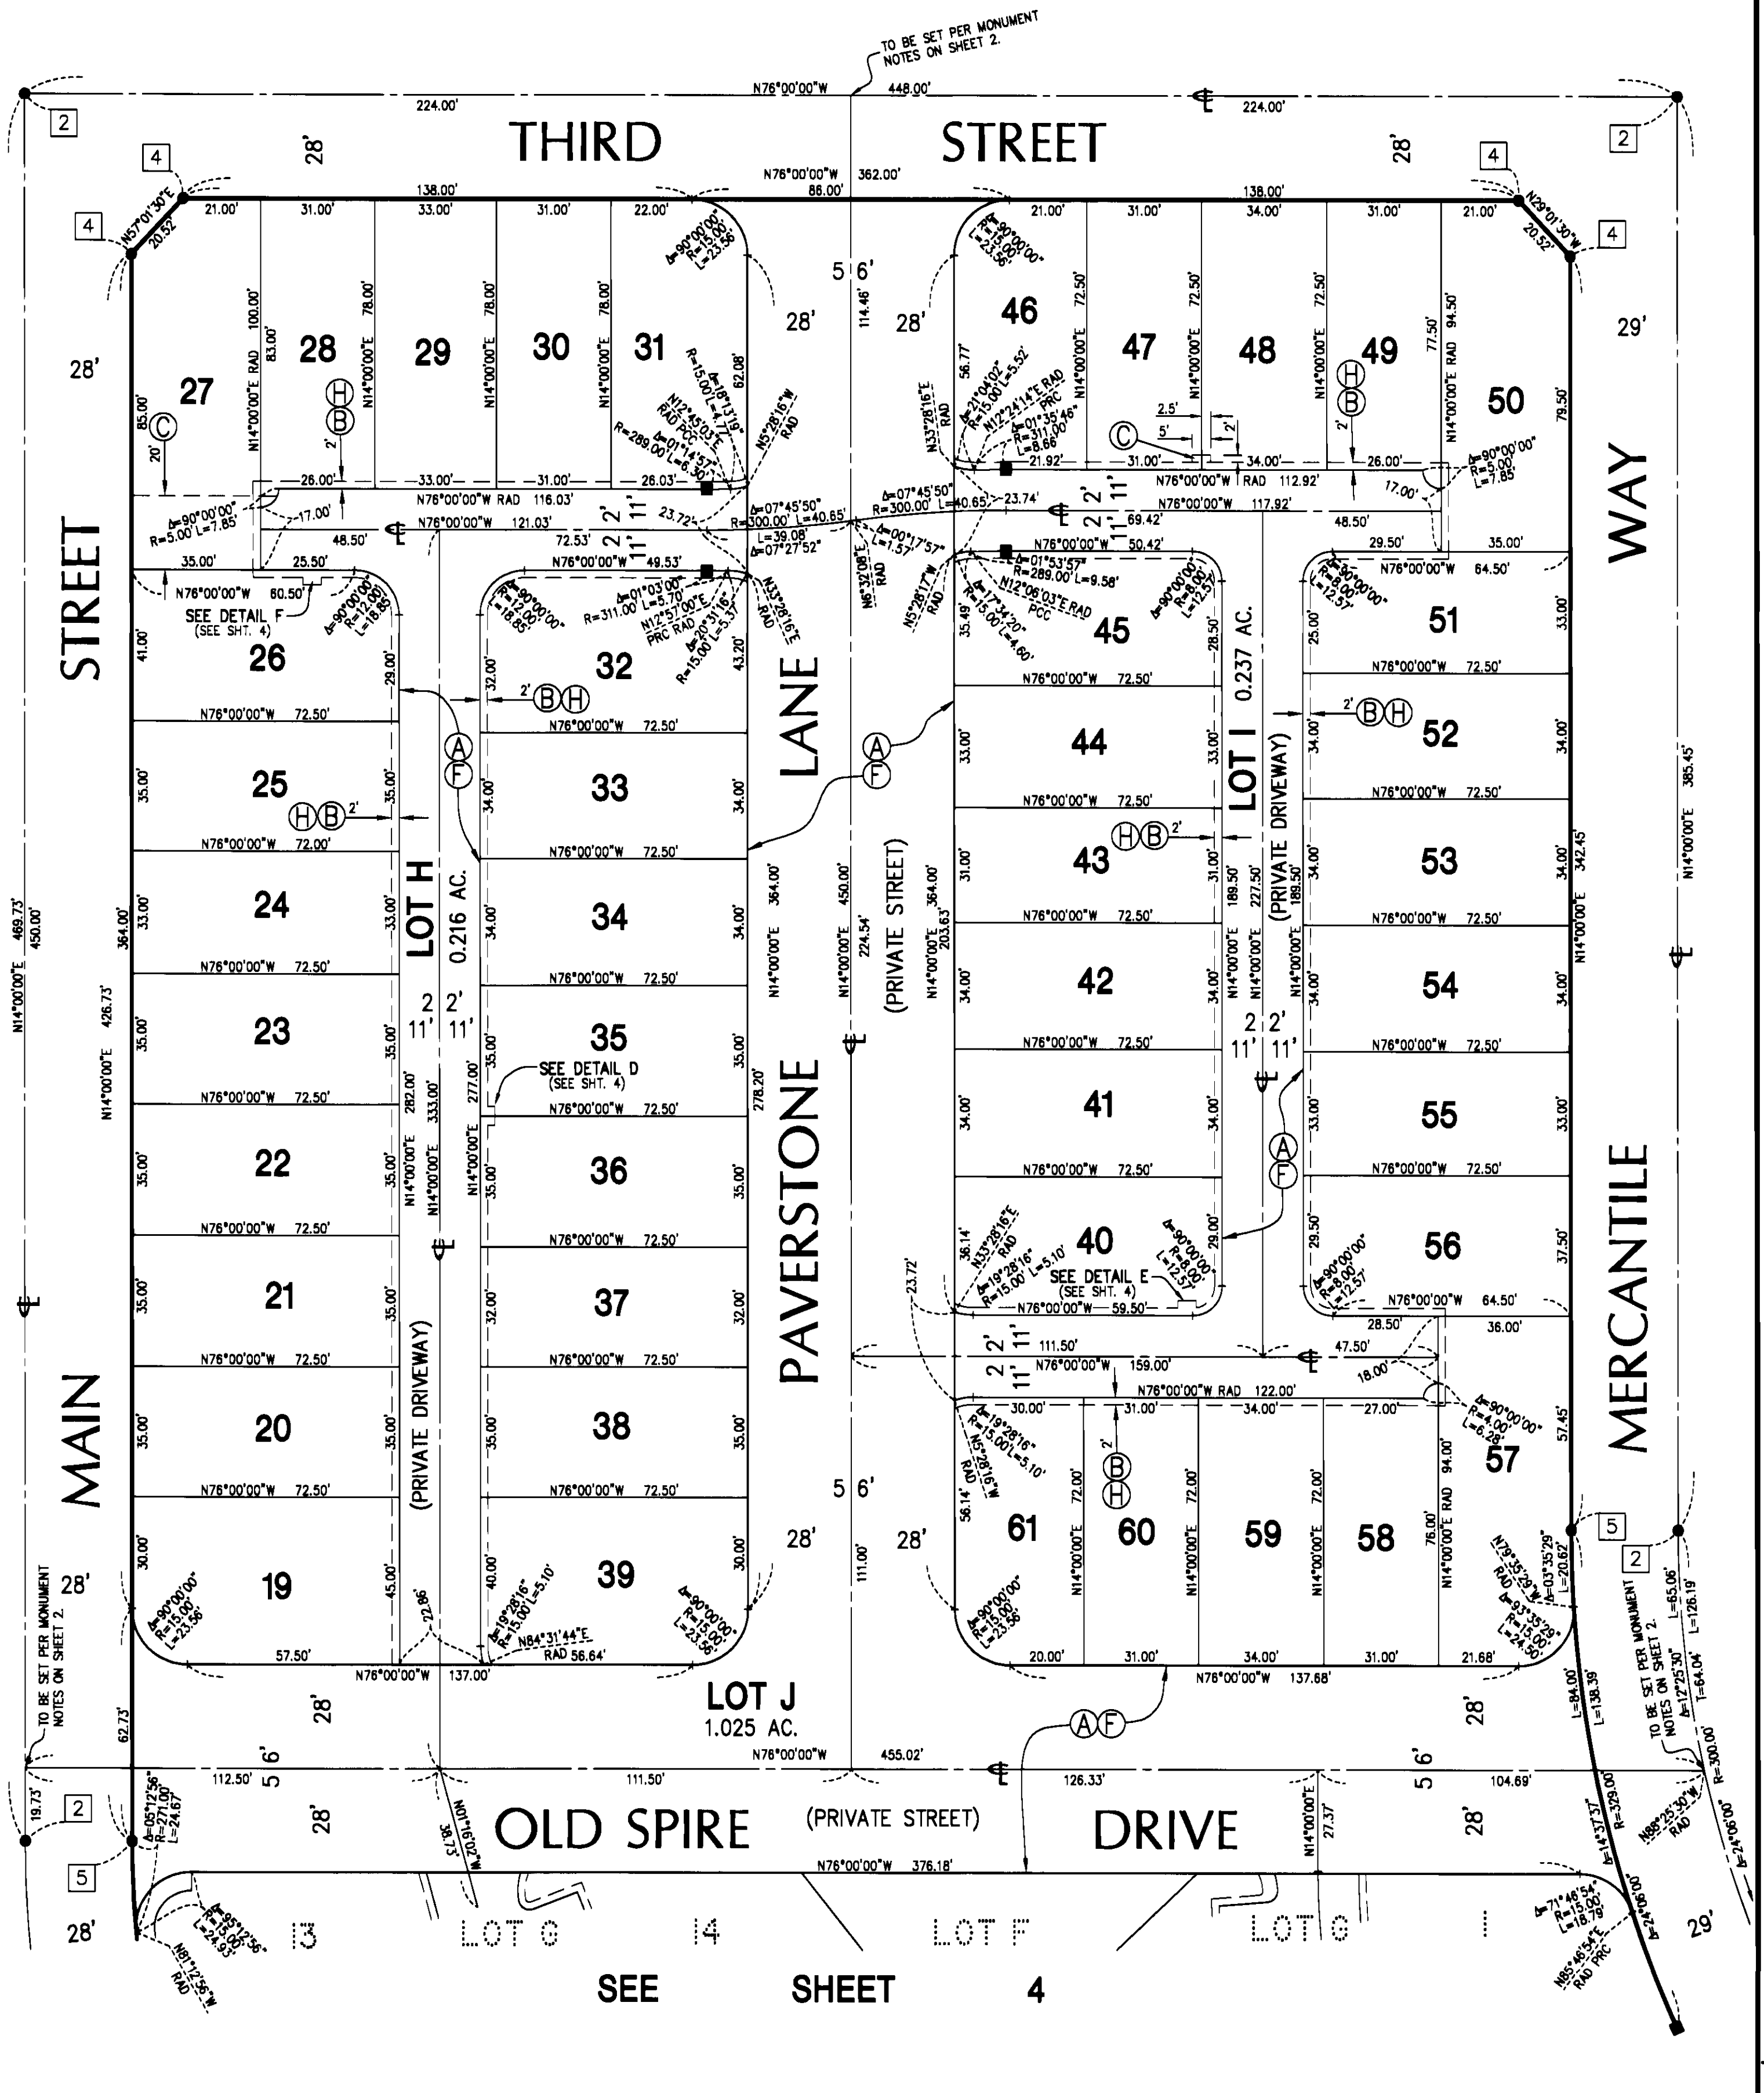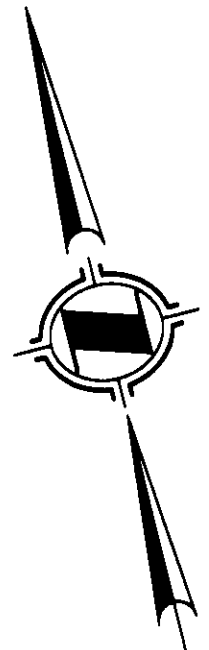

SHEET 4 OF 4 SHEETS
SCALE 1" = 30'
61 NUMBERED LOTS AND LOTS
A THROUGH J INCLUSIVE
ACREAGE: 6.185 ACRES
(ALL OF TENTATIVE
TRACT NO. 15886)

TRACT NO. 15886

IN THE UNINCORPORATED TERRITORY OF THE COUNTY OF ORANGE,
 STATE OF CALIFORNIA

HUNSAKER AND ASSOCIATES IRVINE, INC.
 RORY S. WILLIAMS, L.S. 6654 DATE OF SURVEY: JANUARY, 2000


NOTES:
 LOTS A THROUGH F, INCLUSIVE, ARE OPEN SPACE OR
 LANDSCAPE. LOTS RESERVED FOR FUTURE GRANT TO THE
 HOMEOWNER'S ASSOCIATION BY SEPARATE INSTRUMENT
 AND ARE NOT SEPARATE BUILDING SITES.

LOTS G THROUGH I, INCLUSIVE, ARE PRIVATE DRIVEWAYS.

LOT J IS A PRIVATE STREET.

EASEMENT NOTES:

- Ⓐ INDICATES AN EASEMENT FOR WATER, SEWER AND ACCESS PURPOSES DEDICATED TO SANTA MARGARITA WATER DISTRICT HEREON.
- Ⓑ INDICATES A 2.00' WIDE EASEMENT FOR WATER LINE PURPOSES DEDICATED HEREON TO SANTA MARGARITA WATER DISTRICT.
- Ⓒ INDICATES AN EASEMENT FOR WATER AND ACCESS PURPOSES DEDICATED TO SANTA MARGARITA WATER DISTRICT HEREON.
- Ⓓ INDICATES AN EASEMENT FOR SEWER AND ACCESS PURPOSES DEDICATED TO SANTA MARGARITA WATER DISTRICT HEREON.
- Ⓔ INDICATES AN EASEMENT FOR STORM DRAIN PURPOSES RESERVED HEREON FOR FUTURE GRANT.
- Ⓕ INDICATES AN EASEMENT FOR INGRESS AND EGRESS OF EMERGENCY AND PUBLIC SERVICE VEHICLES DEDICATED HEREON TO THE COUNTY OF ORANGE.
- Ⓖ INDICATES AN EASEMENT FOR SIDEWALK DEDICATED TO THE COUNTY OF ORANGE PER TRACT NO. 15884, 794/33-44 O.R.
- Ⓗ INDICATES AN EASEMENT FOR PUBLIC UTILITY PURPOSES RESERVED HEREON FOR FUTURE GRANT.
- Ⓢ INDICATES AN EASEMENT FOR SIDEWALK PURPOSES RESERVED HEREON FOR FUTURE GRANT.

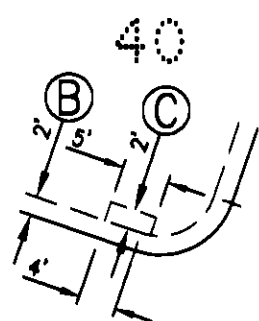


DETAIL E
 SCALE: 1"=20'

EASEMENT DETAIL
 SCALE: 1"=30'

SEE SHEET 2 FOR BASIS OF BEARINGS,
 DATUM STATEMENT, MONUMENT NOTES,
 AND BOUNDARY AND INDEX MAP.

DETAIL F
 SCALE: 1"=20'

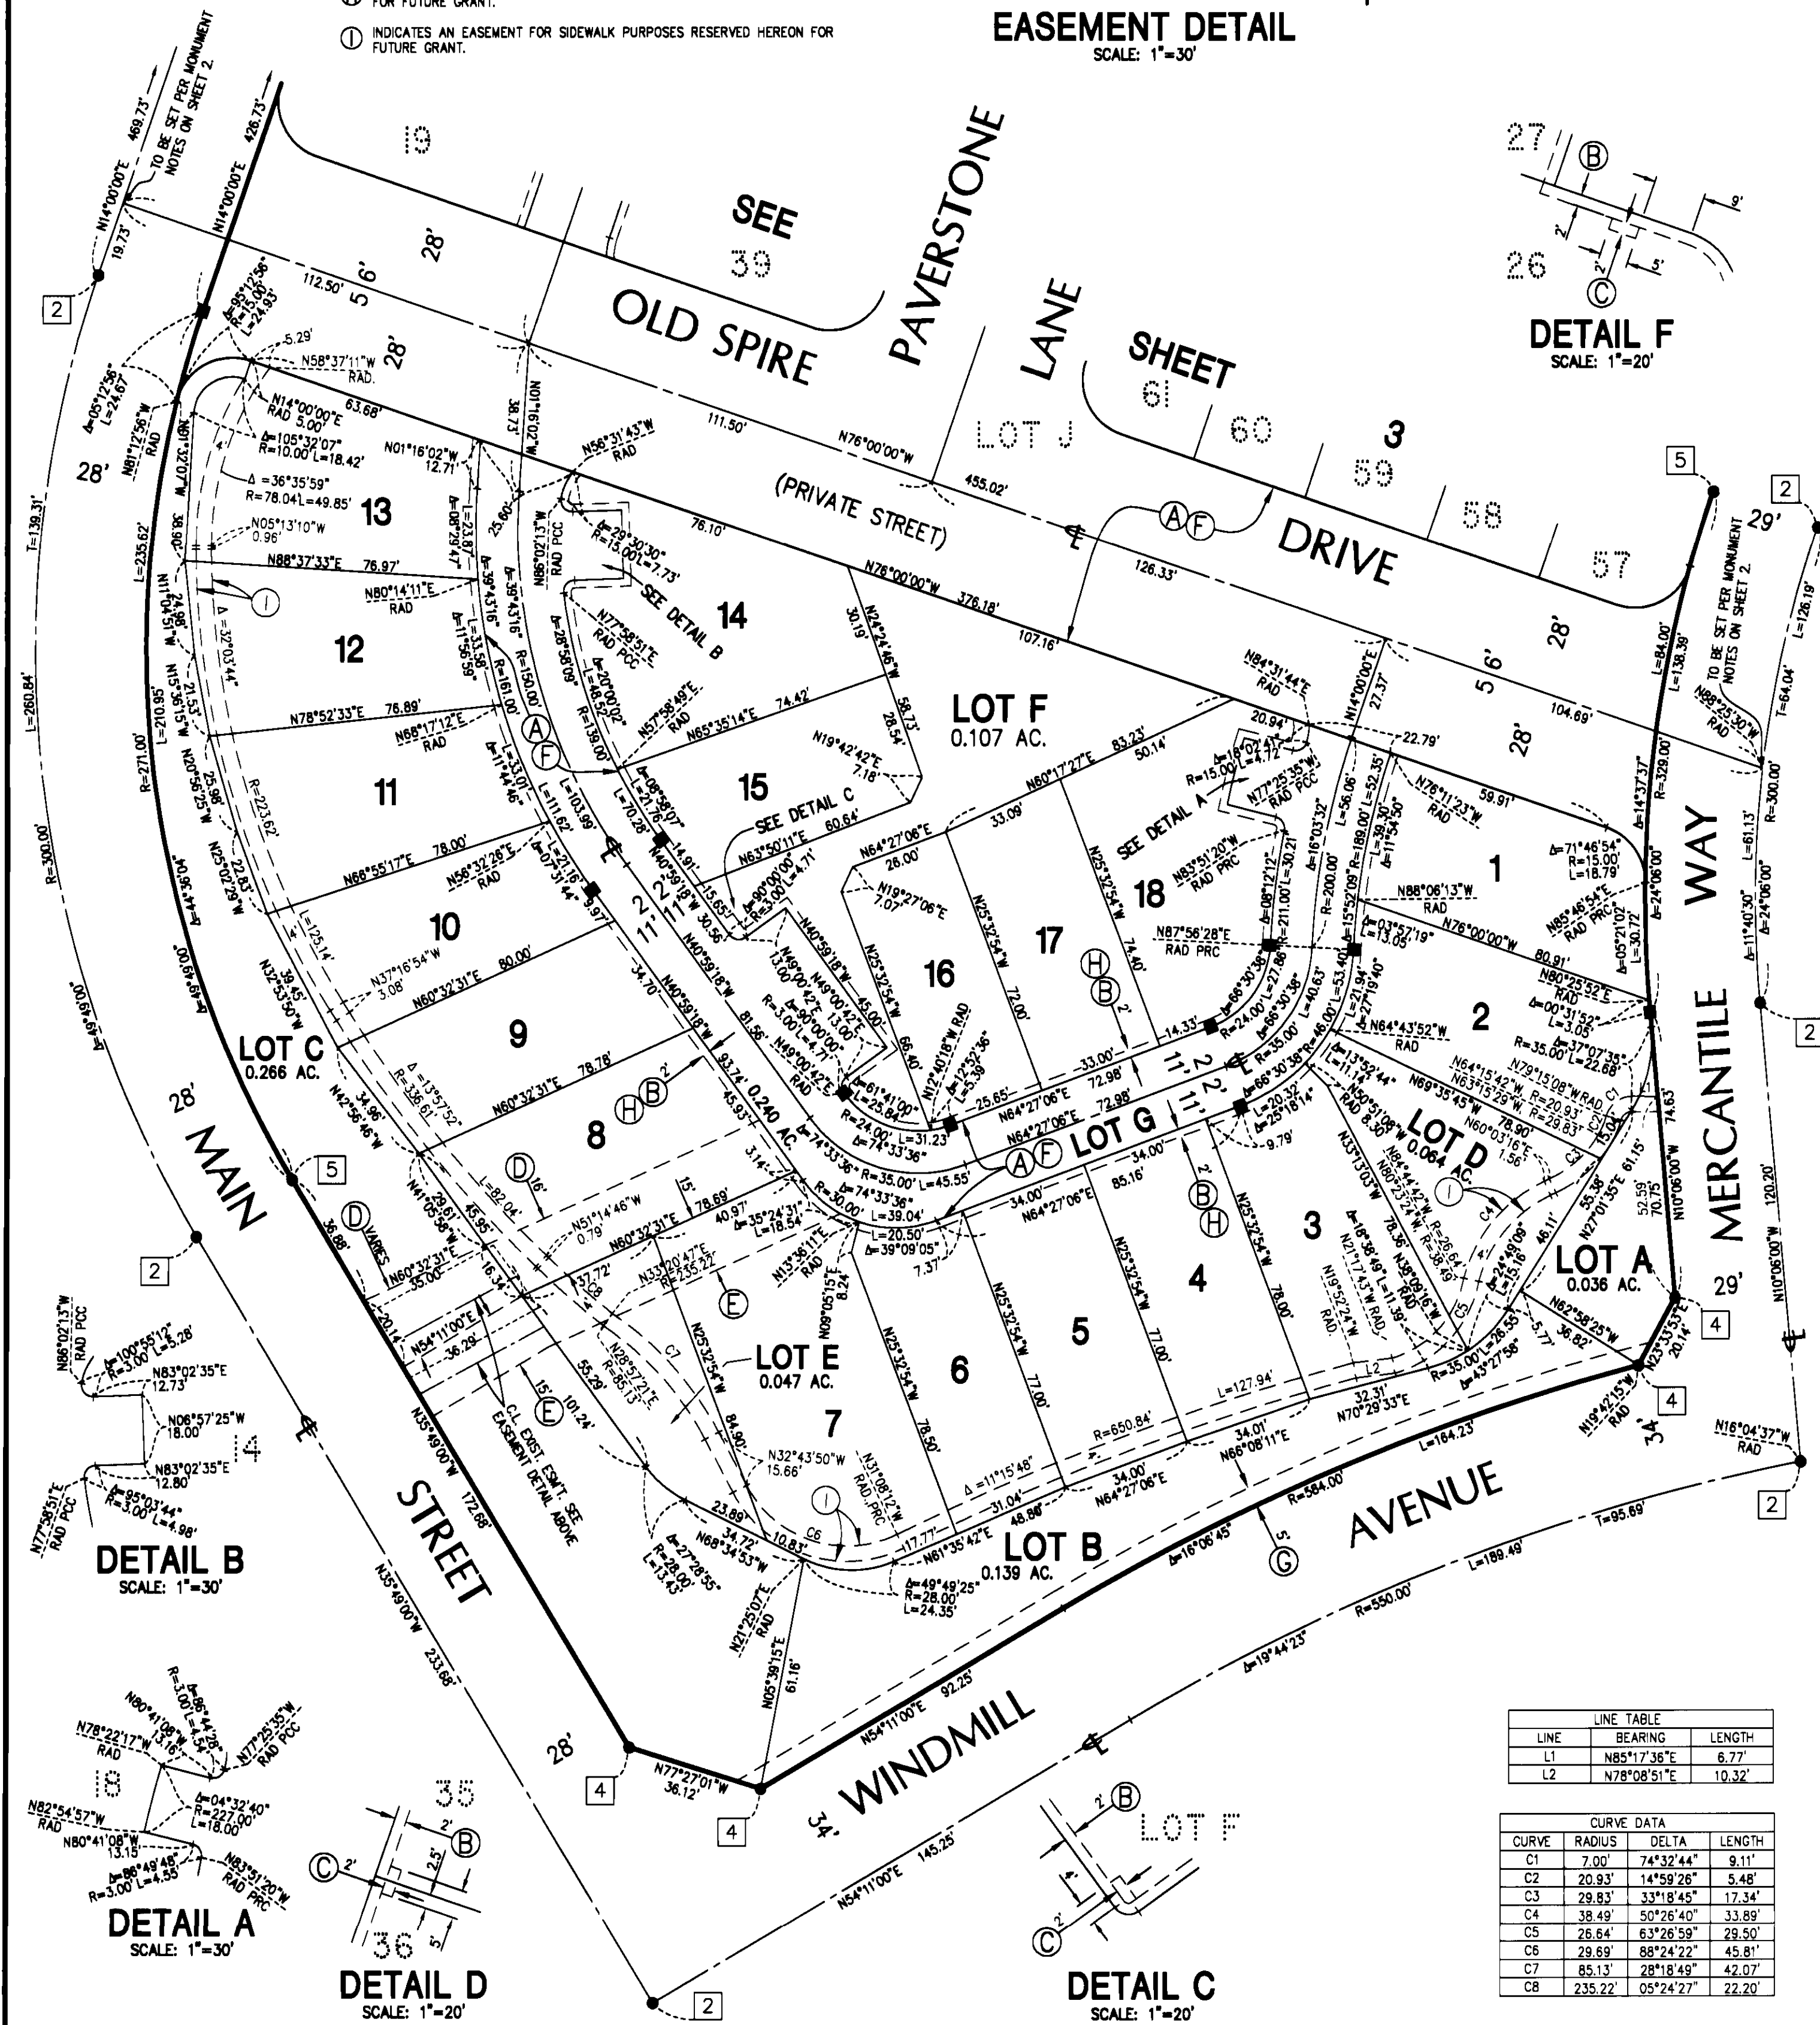

LINE TABLE		
LINE	BEARING	LENGTH
L1	N85°17'36"E	6.77'
L2	N78°08'51"E	10.32'

CURVE DATA			
CURVE	RADIUS	DELTA	LENGTH
C1	7.00'	74°32'44"	9.11'
C2	20.93'	14°59'28"	5.48'
C3	29.83'	33°18'45"	17.34'
C4	38.49'	50°26'40"	33.89'
C5	26.64'	63°26'59"	29.50'
C6	29.69'	88°24'22"	45.81'
C7	85.13'	28°18'49"	42.07'
C8	235.22'	05°24'27"	22.20'