

SHEET 1 OF 4 SHEETS
12 NUMBERED LOTS AND LOTS
A THROUGH O, INCLUSIVE
6.030 ACRES
(ALL OF TENTATIVE
TRACT NO. 15887)

TRACT NO. 15887

IN THE UNINCORPORATED TERRITORY OF THE
COUNTY OF ORANGE, STATE OF CALIFORNIA

BEING A SUBDIVISION OF LOT 8 OF TRACT NO. 15884, AS SHOWN ON A MAP FILED IN BOOK
794, PAGES 33 THROUGH 44, INCLUSIVE, OF MISCELLANEOUS MAPS, IN THE OFFICE OF THE
COUNTY RECORDER OF SAID COUNTY.

BLOCK: 5157
MODULE: 03, 04, 05

HUNSAKER AND ASSOCIATES IRVINE, INC.
RORY S. WILLIAMS L.S. 6654 DATE OF SURVEY: JANUARY, 2000

ACCEPTED AND FILED AT THE
REQUEST OF

FIRST AMERICAN TITLE Co.

DATE: Jan. 2, 2000

TIME: 2:41pm FEE: \$ 13.00

INSTRUMENT NO. 20000291358

BOOK 802 PAGE 25-28

GARY L. GRANVILLE
COUNTY CLERK - RECORDER

BY Deputy DEPUTY

OWNERSHIP CERTIFICATE:

WE, THE UNDERSIGNED, BEING ALL PARTIES HAVING ANY RECORD TITLE INTEREST IN THE LAND COVERED BY THIS MAP, DO HEREBY CONSENT TO THE PREPARATION AND RECORDATION OF SAID MAP, AS SHOWN WITHIN THE DISTINCTIVE BORDER LINE.

WE HEREBY DEDICATE TO THE COUNTY OF ORANGE:

AN EASEMENT FOR INGRESS AND EGRESS OF EMERGENCY AND PUBLIC SERVICE VEHICLES OVER LOTS B THROUGH N, INCLUSIVE.

WE ALSO HEREBY DEDICATE TO THE PUBLIC FOR STREET PURPOSES: MAIN STREET.

WE RESERVE TO OURSELVES, OUR SUCCESSORS AND ASSIGNS THE PUBLIC UTILITY EASEMENTS SHOWN ON THIS MAP, FOR THE USE AND BENEFIT OF THE VARIOUS UTILITY COMPANIES AUTHORIZED TO PROVIDE SERVICE TO THE LOTS SHOWN HEREON.

WE ALSO DO HEREBY DECLARE THAT THE LAND COVERED BY THIS MAP IS LOCATED IN A HIGH FIRE HAZARD AREA DUE TO WILDLAND EXPOSURE. THIS DECLARATION SHALL RUN WITH THE LAND UNTIL A DETERMINATION IS MADE BY THE FIRE AGENCY THAT THE PROPERTY IS NO LONGER LOCATED IN A HIGH FIRE HAZARD AREA.

WE ALSO HEREBY DEDICATE TO THE SANTA MARGARITA WATER DISTRICT THE PIPELINE EASEMENTS FOR WATER, SEWER AND ACCESS PURPOSES, ALL AS SHOWN ON THIS TRACT MAP, WHICH EASEMENTS SHALL BE SUBJECT TO THE SAME TERMS AND CONDITIONS AS SHOWN IN THAT CERTAIN EASEMENT RECORDED OCTOBER 6, 1980, IN BOOK 13776, PAGE 341 OF OFFICIAL RECORDS OF ORANGE COUNTY, CALIFORNIA.

GREYSTONE HOMES, INC., A DELAWARE CORPORATION, OWNER.

BY: A. Reynoso
NAME: Anta Reynoso
TITLE: Asst. Secretary

DMB LADERA, L.L.C., A DELAWARE LIMITED LIABILITY COMPANY, BENEFICIARY UNDER DEEDS OF TRUST RECORDED AS INSTRUMENT NO. 2000088094 OF OFFICIAL RECORDS.

BY: RANCHO MISSION VEJO, L.L.C. A DELAWARE LIMITED LIABILITY COMPANY,
AS AGENT AND/OR MANAGER.

BY: Paul Johnson
NAME: PAUL JOHNSON
TITLE: V.P. - COMMUNITY DEVELOPMENT

NOTARY ACKNOWLEDGMENTS:

STATE OF CALIFORNIA } SS
COUNTY OF ORANGE

ON 4/13/00, BEFORE ME, KELI ABURTON, Notary, PERSONALLY
APPEARED ANTA REYNOSO AND PAUL JOHNSON PERSONALLY
KNOWN TO ME (OR PROVED TO ME ON THE BASIS OF SATISFACTORY EVIDENCE) TO BE THE PERSON(S)
WHOSE NAME(S) IS/ARE SUBSCRIBED TO THE WITHIN INSTRUMENT AND ACKNOWLEDGED TO ME THAT
HE/SHE/they EXECUTED THE SAME IN HIS/HER/their AUTHORIZED CAPACITY(IES), AND THAT BY
HIS/HER/their SIGNATURE(S) ON THE INSTRUMENT THE PERSON(S), OR ENTITY UPON BEHALF OF
WHICH THE PERSON(S) ACTED, EXECUTED THE INSTRUMENT.

WITNESS MY HAND:

SIGNATURE Keli Aburton
NOTARY PUBLIC IN AND FOR SAID STATE
KELI ABURTON
(NAME PRINTED)

MY PRINCIPAL PLACE OF BUSINESS IS
IN ORANGE COUNTY.
MY COMMISSION EXPIRES: 2/1/03

STATE OF CALIFORNIA } SS
COUNTY OF ORANGE

ON 4/13/00, BEFORE ME, Jeannine CARTA-HANSON, PERSONALLY
APPEARED PAUL JOHNSON AND ANTA REYNOSO PERSONALLY
KNOWN TO ME (OR PROVED TO ME ON THE BASIS OF SATISFACTORY EVIDENCE) TO BE THE PERSON(S)
WHOSE NAME(S) IS/ARE SUBSCRIBED TO THE WITHIN INSTRUMENT AND ACKNOWLEDGED TO ME THAT
HE/SHE/they EXECUTED THE SAME IN HIS/HER/their AUTHORIZED CAPACITY(IES), AND THAT BY
HIS/HER/their SIGNATURE(S) ON THE INSTRUMENT THE PERSON(S), OR ENTITY UPON BEHALF OF
WHICH THE PERSON(S) ACTED, EXECUTED THE INSTRUMENT.

WITNESS MY HAND:

SIGNATURE Jeannine Carta-Hanson
NOTARY PUBLIC IN AND FOR SAID STATE
JEANNINE CARTA-HANSON
(NAME PRINTED)

MY PRINCIPAL PLACE OF BUSINESS IS
IN ORANGE COUNTY.
MY COMMISSION EXPIRES: 2/29/03

STATE OF CALIFORNIA } SS
COUNTY OF ORANGE

ON 4/12/00, BEFORE ME, CINDY R. LANE, Notary Public, PERSONALLY
APPEARED DANIEL R. FERONS, PERSONALLY
KNOWN TO ME (OR PROVED TO ME ON THE BASIS OF SATISFACTORY EVIDENCE) TO BE THE PERSON
WHOSE NAME IS SUBSCRIBED TO THE WITHIN INSTRUMENT AND ACKNOWLEDGED TO ME THAT
HE EXECUTED THE SAME IN HIS AUTHORIZED CAPACITY, AND THAT BY
HIS SIGNATURE ON THE INSTRUMENT THE PERSON, OR ENTITY UPON BEHALF OF
WHICH THE PERSON ACTED, EXECUTED THE INSTRUMENT.

WITNESS MY HAND:


SIGNATURE Cindy R. Lane
NOTARY PUBLIC IN AND FOR SAID STATE
CINDY R. LANE
(NAME PRINTED)

MY PRINCIPAL PLACE OF BUSINESS IS
IN ORANGE COUNTY.
MY COMMISSION EXPIRES: 2-20-2001

SURVEYOR'S STATEMENT:

I HEREBY STATE THAT THIS MAP, CONSISTING OF 4 SHEETS, CORRECTLY REPRESENTS A TRUE AND COMPLETE SURVEY AS SHOWN MADE IN JANUARY, 2000; WAS MADE BY ME OR UNDER MY DIRECTION; THAT THE MONUMENTS ARE OF THE CHARACTER AND OCCUPY (OR WILL OCCUPY) THE POSITIONS INDICATED BY SAID MAP; AND THAT SAID MONUMENTS ARE (OR WILL BE) SUFFICIENT TO ENABLE THE SURVEY TO BE RETRACED.

Rory S. Williams
RORY S. WILLIAMS,
L.S. 6654
LICENSE EXPIRES: DECEMBER 31, 2005

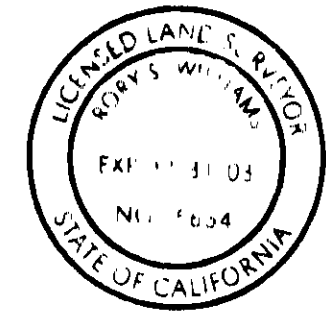

COUNTY SURVEYOR'S STATEMENT

I HEREBY STATE THAT I HAVE EXAMINED THIS MAP AND HAVE FOUND IT TO BE SUBSTANTIALLY IN CONFORMANCE WITH THE TENTATIVE MAP AS FILED WITH, AMENDED AND APPROVED BY THE ORANGE COUNTY SUBDIVISION COMMITTEE; THAT ALL PROVISIONS OF THE SUBDIVISION MAP ACT AND COUNTY SUBDIVISION REGULATIONS HAVE BEEN COMPLIED WITH AND I AM SATISFIED SAID MAP IS TECHNICALLY CORRECT.

DATED THIS 12th DAY OF May, 2000.

Robert Jelinek
JOHN CANAS, COUNTY SURVEYOR
ROBERT JELINEK, DEPUTY COUNTY SURVEYOR



COUNTY TREASURER-TAX COLLECTOR'S CERTIFICATE:

STATE OF CALIFORNIA } SS
COUNTY OF ORANGE

I HEREBY CERTIFY THAT ACCORDING TO THE RECORDS OF MY OFFICE THERE ARE NO LIENS AGAINST THE LAND COVERED BY THIS MAP OR ANY PART THEREOF FOR UNPAID STATE, COUNTY, MUNICIPAL OR LOCAL TAXES OR SPECIAL ASSESSMENTS COLLECTED AS TAXES, EXCEPT TAXES OR SPECIAL ASSESSMENTS COLLECTED AS TAXES NOT YET PAYABLE.

AND DO ALSO CERTIFY TO THE RECORDER OF ORANGE COUNTY THAT THE PROVISIONS OF THE SUBDIVISION MAP ACT HAVE BEEN COMPLIED WITH REGARDING DEPOSITS TO SECURE THE PAYMENT OF TAXES OR SPECIAL ASSESSMENTS COLLECTED AS TAXES ON THE LAND COVERED BY THIS MAP.

DATED THIS 4th DAY OF May, 2000.

John M.W. Moorlach
JOHN M.W. MOORLACH
COUNTY TREASURER-TAX COLLECTOR

BY: Deputy
DEPUTY TREASURER-TAX COLLECTOR

CLERK OF THE BOARD OF SUPERVISORS CERTIFICATE:

STATE OF CALIFORNIA } SS
COUNTY OF ORANGE

I HEREBY CERTIFY THAT THIS MAP WAS PRESENTED FOR APPROVAL TO THE BOARD OF SUPERVISORS OF THE COUNTY OF ORANGE AT REGULAR MEETING THEREOF HELD ON THE 23rd DAY OF May, 2000, AND THAT THEREUPON SAID BOARD DID, BY AN ORDER DULY PASSED AND ENTERED, APPROVED SAID MAP.

AND DID ACCEPT ON BEHALF OF THE COUNTY OF ORANGE:

THE EASEMENT FOR INGRESS AND EGRESS OF EMERGENCY AND PUBLIC SERVICE VEHICLES OVER LOTS B THROUGH N, INCLUSIVE.

AND DID ACCEPT ON BEHALF OF THE PUBLIC: MAIN STREET.

AND DID ALSO APPROVE SAID MAP PURSUANT TO THE PROVISIONS OF SECTION 66436 (a)(3)(A) OF THE SUBDIVISION MAP ACT.

DATED THIS 23rd DAY OF May, 2000.

Darlene J. Bloom
CLERK OF THE BOARD OF SUPERVISORS
DARLENE J. BLOOM



CERTIFICATE OF ACCEPTANCE - SANTA MARGARITA WATER DISTRICT

THE UNDERSIGNED, BEING THE DULY APPOINTED AGENT OF THE SANTA MARGARITA WATER DISTRICT, A PUBLIC CORPORATION IN ORANGE COUNTY, CALIFORNIA, PURSUANT TO ITS RESOLUTION NO. 88-10-2, DOES HEREBY ACCEPT ON BEHALF OF SAID DISTRICT, THE PIPELINE EASEMENTS FOR WATER, SEWER AND ACCESS PURPOSES AS DEDICATED AND SHOWN ON THIS TRACT MAP, BY AND BETWEEN THE SANTA MARGARITA WATER DISTRICT AND GREYSTONE HOMES, INC., A DELAWARE CORPORATION, AND DOES HEREBY CERTIFY THAT THE GRANTEE CONSENTS TO THE RECORDATION OF SAID TRACT MAP.

Daniel R. Ferons
DANIEL R. FERONS, CHIEF ENGINEER
SANTA MARGARITA WATER DISTRICT

NOTES:

THE PRIVATE STREETS CONSTRUCTED WITHIN THIS MAP SHALL BE OWNED, OPERATED AND MAINTAINED BY THE DEVELOPER, ITS SUCCESSORS OR ASSIGNS. THE COUNTY OF ORANGE SHALL HAVE NO RESPONSIBILITY THEREFOR, UNLESS PURSUANT TO APPROPRIATE SECTIONS OF THE STREET AND HIGHWAYS CODE OF THE STATE OF CALIFORNIA, THE SAID PRIVATE STREETS HAVE BEEN ACCEPTED INTO THE COUNTY ROAD SYSTEM BY APPROPRIATE RESOLUTION OF THE ORANGE COUNTY BOARD OF SUPERVISORS.

BUILDING PERMIT ISSUANCE SHALL BE PHASED IN ACCORDANCE WITH THE FOOTHILL CIRCULATION PHASING PLAN (FCPP) DEVELOPMENT PHASING PLAN, AND SHALL ALSO BE SUBJECT TO ANY OTHER BOARD OF SUPERVISORS APPROVED GROWTH MANAGEMENT PHASING PLAN PERTAINING TO THE TIMELY PROVISIONS OF PUBLIC SERVICES AND FACILITIES.

SIGNATURE OMISSIONS:

PURSUANT TO THE PROVISIONS OF SECTION 66436 (a)(3)(A)(C) OF THE SUBDIVISION MAP ACT THE FOLLOWING SIGNATURES HAVE BEEN OMITTED:

DMB LADERA LLC, HOLDER OF EASEMENTS RECORDED AS INSTRUMENT NO. 2000088092

LADERA DEVELOPMENT COMPANY, L.L.C. HOLDER OF OIL, GAS AND MINERAL RIGHTS; WATER AND WATER RIGHTS, RECORDED AS INSTRUMENT NO. 19960624029, O.R.

THE COUNTY OF ORANGE, HOLDER OF EASEMENT FOR SIDEWALK PURPOSES AS SHOWN AND DEDICATED ON THE MAP OF SAID TRACT NO. 15884.

SHEET 2 OF 4 SHEETS
SCALE 1" = 200'
12 NUMBERED LOTS AND LOTS
A THROUGH Q, INCLUSIVE
ACREAGE: 6.030 ACRES
(ALL OF TENTATIVE
TRACT No. 15887)

TRACT NO. 15887

IN THE UNINCORPORATED TERRITORY OF THE COUNTY OF ORANGE,
 STATE OF CALIFORNIA

HUNSAKER AND ASSOCIATES IRVINE, INC.
 RORY S. WILLIAMS, L.S. 6654

DATE OF SURVEY: JANUARY, 2000

BOUNDARY AND INDEX MAP

BASIS OF BEARINGS:

THE BEARINGS SHOWN HEREON ARE BASED ON THE BEARING BETWEEN O.C.S. HORIZONTAL CONTROL STATION GPS NO. 1424 AND STATION GPS NO. 1417 BEING N01°36'34"E PER RECORDS ON FILE IN THE OFFICE OF THE ORANGE COUNTY SURVEYOR.

DATUM STATEMENT:

COORDINATES SHOWN ARE BASED ON THE CALIFORNIA COORDINATE SYSTEM (CCS83), ZONE VI, 1983 NAD, (1991.35 EPOCH OCS GPS ADJUSTMENT).

ALL DISTANCES SHOWN ARE GROUND, UNLESS OTHERWISE NOTED. TO OBTAIN GRID DISTANCE MULTIPLY GROUND DISTANCE BY 0.99994800

MONUMENT NOTES:

1" I.P. TAGGED L.S. 6654 OR LEAD, TACK & TAG L.S. 6654 OR NAIL & TAG L.S. 6654 OR 8" S&W STAMPED L.S. 6654 TO BE SET AT ALL NUMBERED LOT CORNERS EXCEPT LOT CORNERS THAT ARE COMMON WITH PRIVATE OR PUBLIC STREET RIGHT OF WAY, WITHIN 90 DAYS AFTER ACCEPTANCE OF IMPROVEMENTS, UNLESS OTHERWISE NOTED.

■ INDICATES LEAD, TACK & TAG L.S. 6654 TO BE SET IN TOP OF CURB OR SIDEWALK ON ALL SIDE LOT LINES PRODUCED OR CONTINUED, 0.50' FROM INTERSECTION WITH PRIVATE OR PUBLIC STREET RIGHTS OF WAY, WITHIN 90 DAYS AFTER ACCEPTANCE OF IMPROVEMENTS, UNLESS OTHERWISE NOTED.

8" S&W STAMPED L.S. 6654 OR LEAD, TACK & TAG L.S. 6654 OR 1" I.P. TAGGED L.S. 6654 IN MEDIAN TO BE SET AT ALL STREET CENTERLINE POINTS OF CONTROL, WITHIN 90 DAYS AFTER ACCEPTANCE OF IMPROVEMENTS, UNLESS OTHERWISE NOTED.

NO MONUMENTS WILL BE SET AT PRIVATE STREET LETTERED LOT CORNERS, UNLESS OTHERWISE NOTED.

● INDICATES FOUND MONUMENT AS NOTED OR LOCATION OF MONUMENT TO BE SET AS NOTED.

NOTES:

LOT A AND O ARE OPEN SPACE OR LANDSCAPE LOTS, RESERVED FOR FUTURE GRANT TO THE HOMEOWNER'S ASSOCIATION BY SEPARATE INSTRUMENT AND ARE NOT A SEPARATE BUILDING SITE.

LOTS B THROUGH N, INCLUSIVE, ARE PRIVATE STREETS.

THE PROPERTY IS IN A SPECIAL FIRE PROTECTION AREA AND MUST MEET ALL REQUIREMENTS FOR DEVELOPMENT WITHIN THE AREA OR FILE FOR AN EXCLUSION WITH THE FIRE CHIEF.

ALL STRUCTURES SHALL BE PROTECTED WITH AUTOMATIC FIRE SPRINKLERS.

MONUMENT NOTES (CONTINUED):

1 INDICATES FD. 2 1/2" O.C.S. BRASS DISK IN WELL MONUMENT PER TRACT NO. 15813, M.M. 795 / 1-18.

2 INDICATES LOCATION OF 1" IRON PIPE TAGGED "L.S. 5557" OR SPIKE & WASHER STAMPED "L.S. 5557" OR LEAD, TACK & TAG "L.S. 5557" TO BE SET WITHIN 90 DAYS AFTER ACCEPTANCE OF IMPROVEMENTS, PER TRACT NO. 15884, M.M. 794 / 33-44.

3 INDICATES LOCATION OF 1" IRON PIPE TAGGED "L.S. 5557" OR SPIKE & WASHER STAMPED "L.S. 5557" OR LEAD, TACK & TAG "L.S. 5557" TO BE SET WITHIN 90 DAYS AFTER ACCEPTANCE OF IMPROVEMENTS, PER TRACT NO. 15815, M.M. 777 / 14-31.

4 INDICATES LOCATION OF 1" IRON PIPE TAGGED "L.S. 5557" OR SPIKE & WASHER STAMPED "L.S. 5557" OR LEAD, TACK & TAG "L.S. 5557" TO BE SET, AT THE OFFSET POSITION AND AS SHOWN, HEREON, IN DETAILS H, I AND J, WITHIN 90 DAYS AFTER ACCEPTANCE OF IMPROVEMENTS PER TRACT NO. 15884, M.M. 794 / 33-44.

EASEMENT NOTES:


(A) INDICATES AN EASEMENT FOR WATER, SEWER, AND ACCESS PURPOSES DEDICATED TO SANTA MARGARITA WATER DISTRICT HEREON.

(B) INDICATES AN EASEMENT FOR PUBLIC UTILITY PURPOSES RESERVED HEREON FOR FUTURE GRANT.

(C) INDICATES AN EASEMENT FOR INGRESS AND EGRESS OF EMERGENCY AND PUBLIC SERVICE VEHICLES DEDICATED HEREON TO THE COUNTY OF ORANGE.

(D) INDICATES AN EASEMENT FOR SIDEWALKS DEDICATED TO THE COUNTY OF ORANGE PER TRACT NO. 15884, M.M. 794 / 33-44.

○ INDICATES SHEET NUMBER

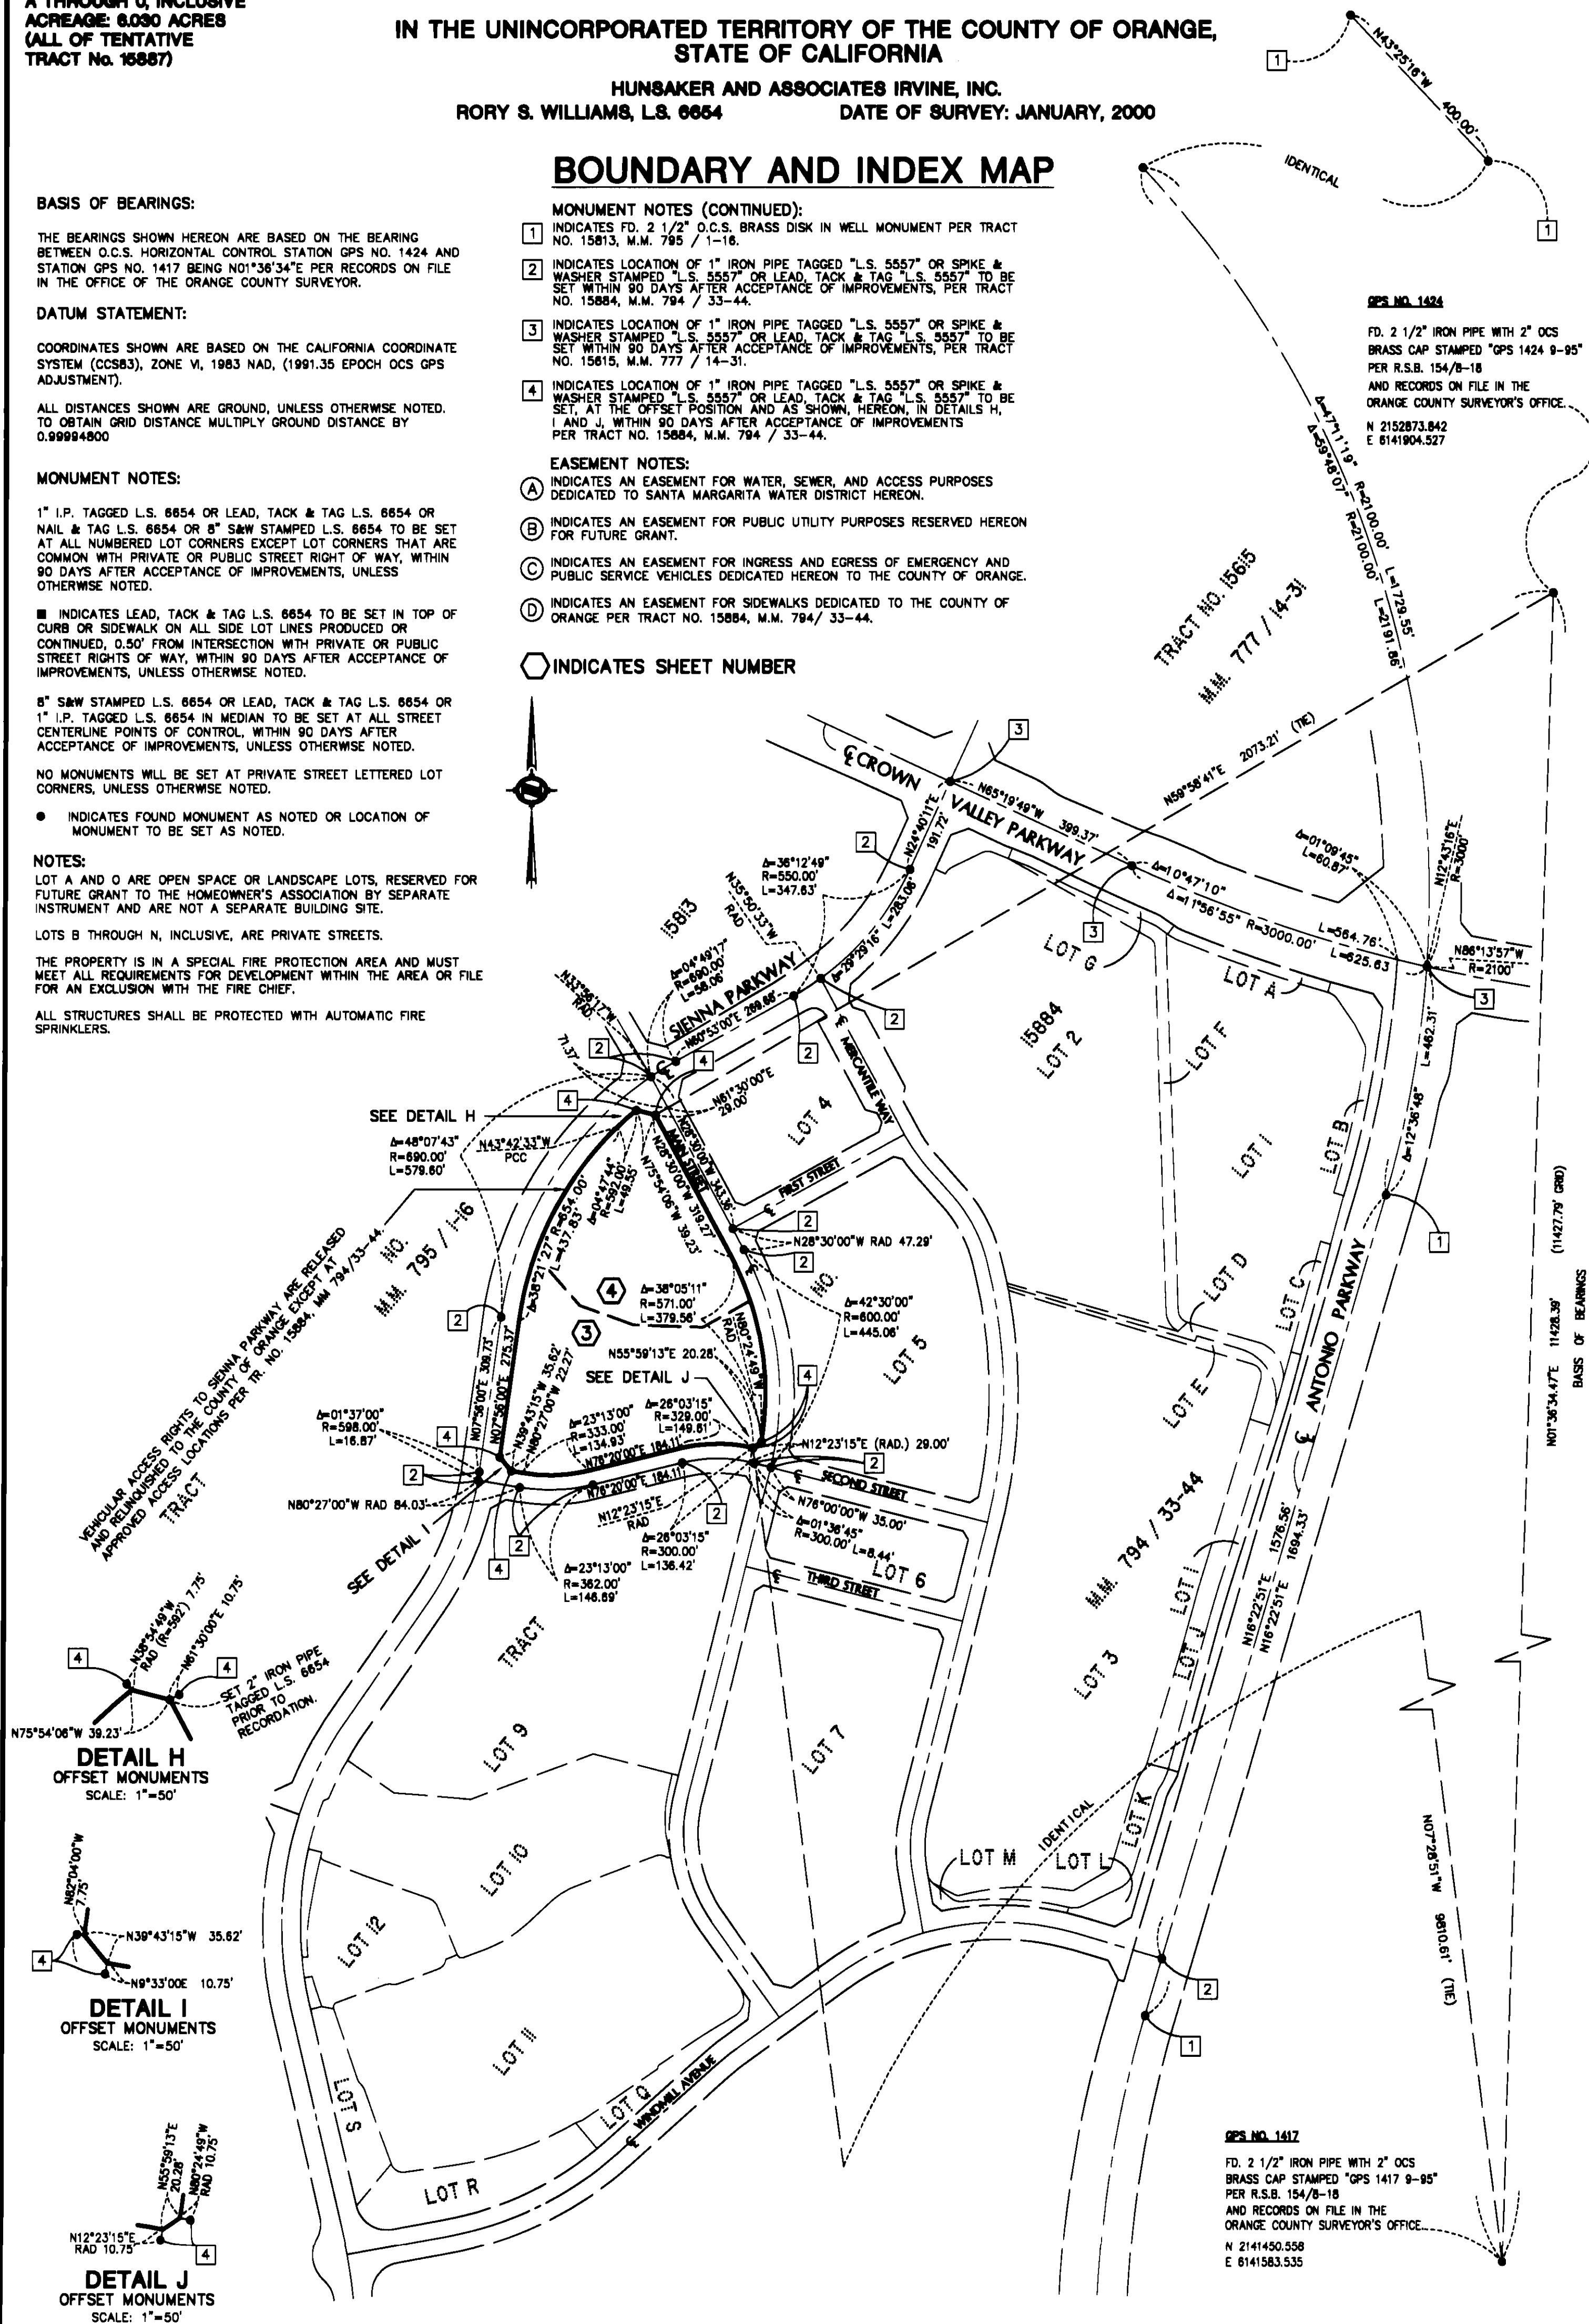


SHEET 3 OF 4 SHEETS
SCALE: 1" = 30'
12 NUMBERED LOTS AND LOTS
A THROUGH O, INCLUSIVE
ACREAGE: 60.90 ACRES
(ALL OF TENTATIVE
TRACT NO. 15887)

SEE SHEET 2 FOR BASIS OF BEARINGS, DATUM
STATEMENT, MONUMENT NOTES, BOUNDARY AND
SHEET INDEX MAP, EASEMENT NOTES
AND NOTES.


CURVE	DELTA	RADIUS	LENGTH	TANGENT
C1	90°00'00"	2.00'	3.14'	2.00'
C2	92°11'56"	3.00'	4.83'	3.12'
C3	86°12'18"	10.00'	15.05'	9.36'
C4	43°31'52"	10.00'	7.60'	3.89'
C5	61°10'35"	10.00'	10.68'	5.81'
C6	98°36'51"	3.00'	3.18'	3.51'
C7	86°23'25"	3.00'	4.52'	2.82'
C8	90°27'45"	5.00'	7.85'	5.04'
C9	109°22'49"	2.00'	3.82'	2.82'
C10	87°23'58"	10.00'	15.25'	9.56'
C11	87°23'58"	22.50'	34.32'	21.50'
C12	162°45'28"	5.88'	15.84'	36.77'
C13	67°15'21"	15.00'	17.61'	9.86'
C14	14°08'53"	150.00'	37.04'	18.61'
C15	93°56'20"	2.00'	3.28'	2.14'
C16	15°00'24"	150.00'	39.29'	19.76'

LINE	BEARING	LENGTH
L1	N78°56'37"E	14.00'
L2	N13°03'23"W	4.36'
L3	N13°03'23"W	1.00'
L4	N13°29'14"W	13.07'
L5	N13°29'14"W	12.91'
L6	N06°08'32"W	25.33'
L9	N06°21'20"E	18.79'
L10	N10°51'28"W	1.99'

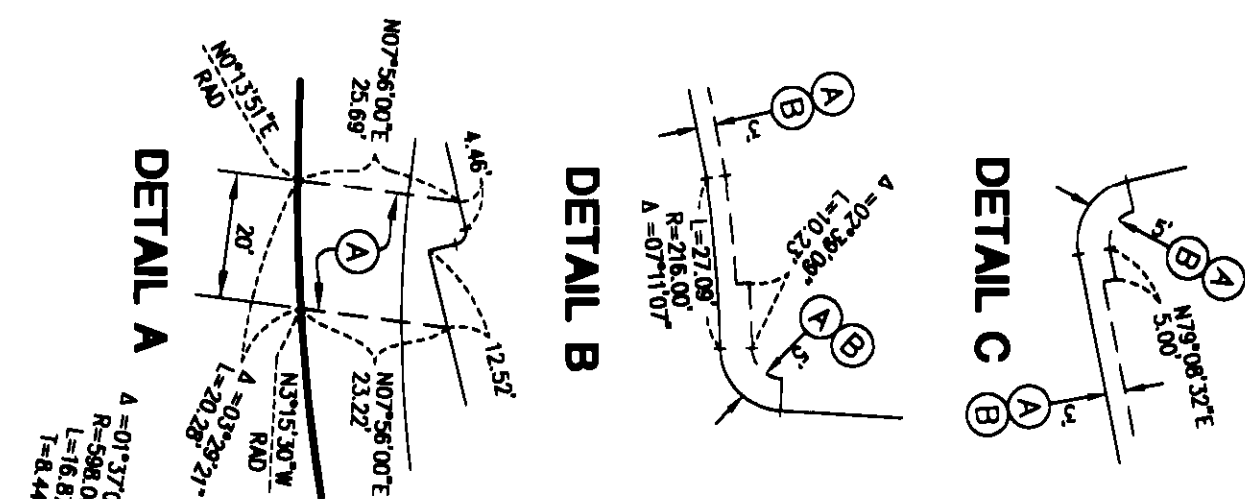

SEE SHEET

TRACT No. 15887
IN THE UNINCORPORATED TERRITORY OF THE
COUNTY OF ORANGE, STATE OF CALIFORNIA
HUNSAKER AND ASSOCIATES IRVINE, INC.
RORY S. WILLIAMS, L.S. 6654 DATE OF SURVEY: JANUARY, 2000

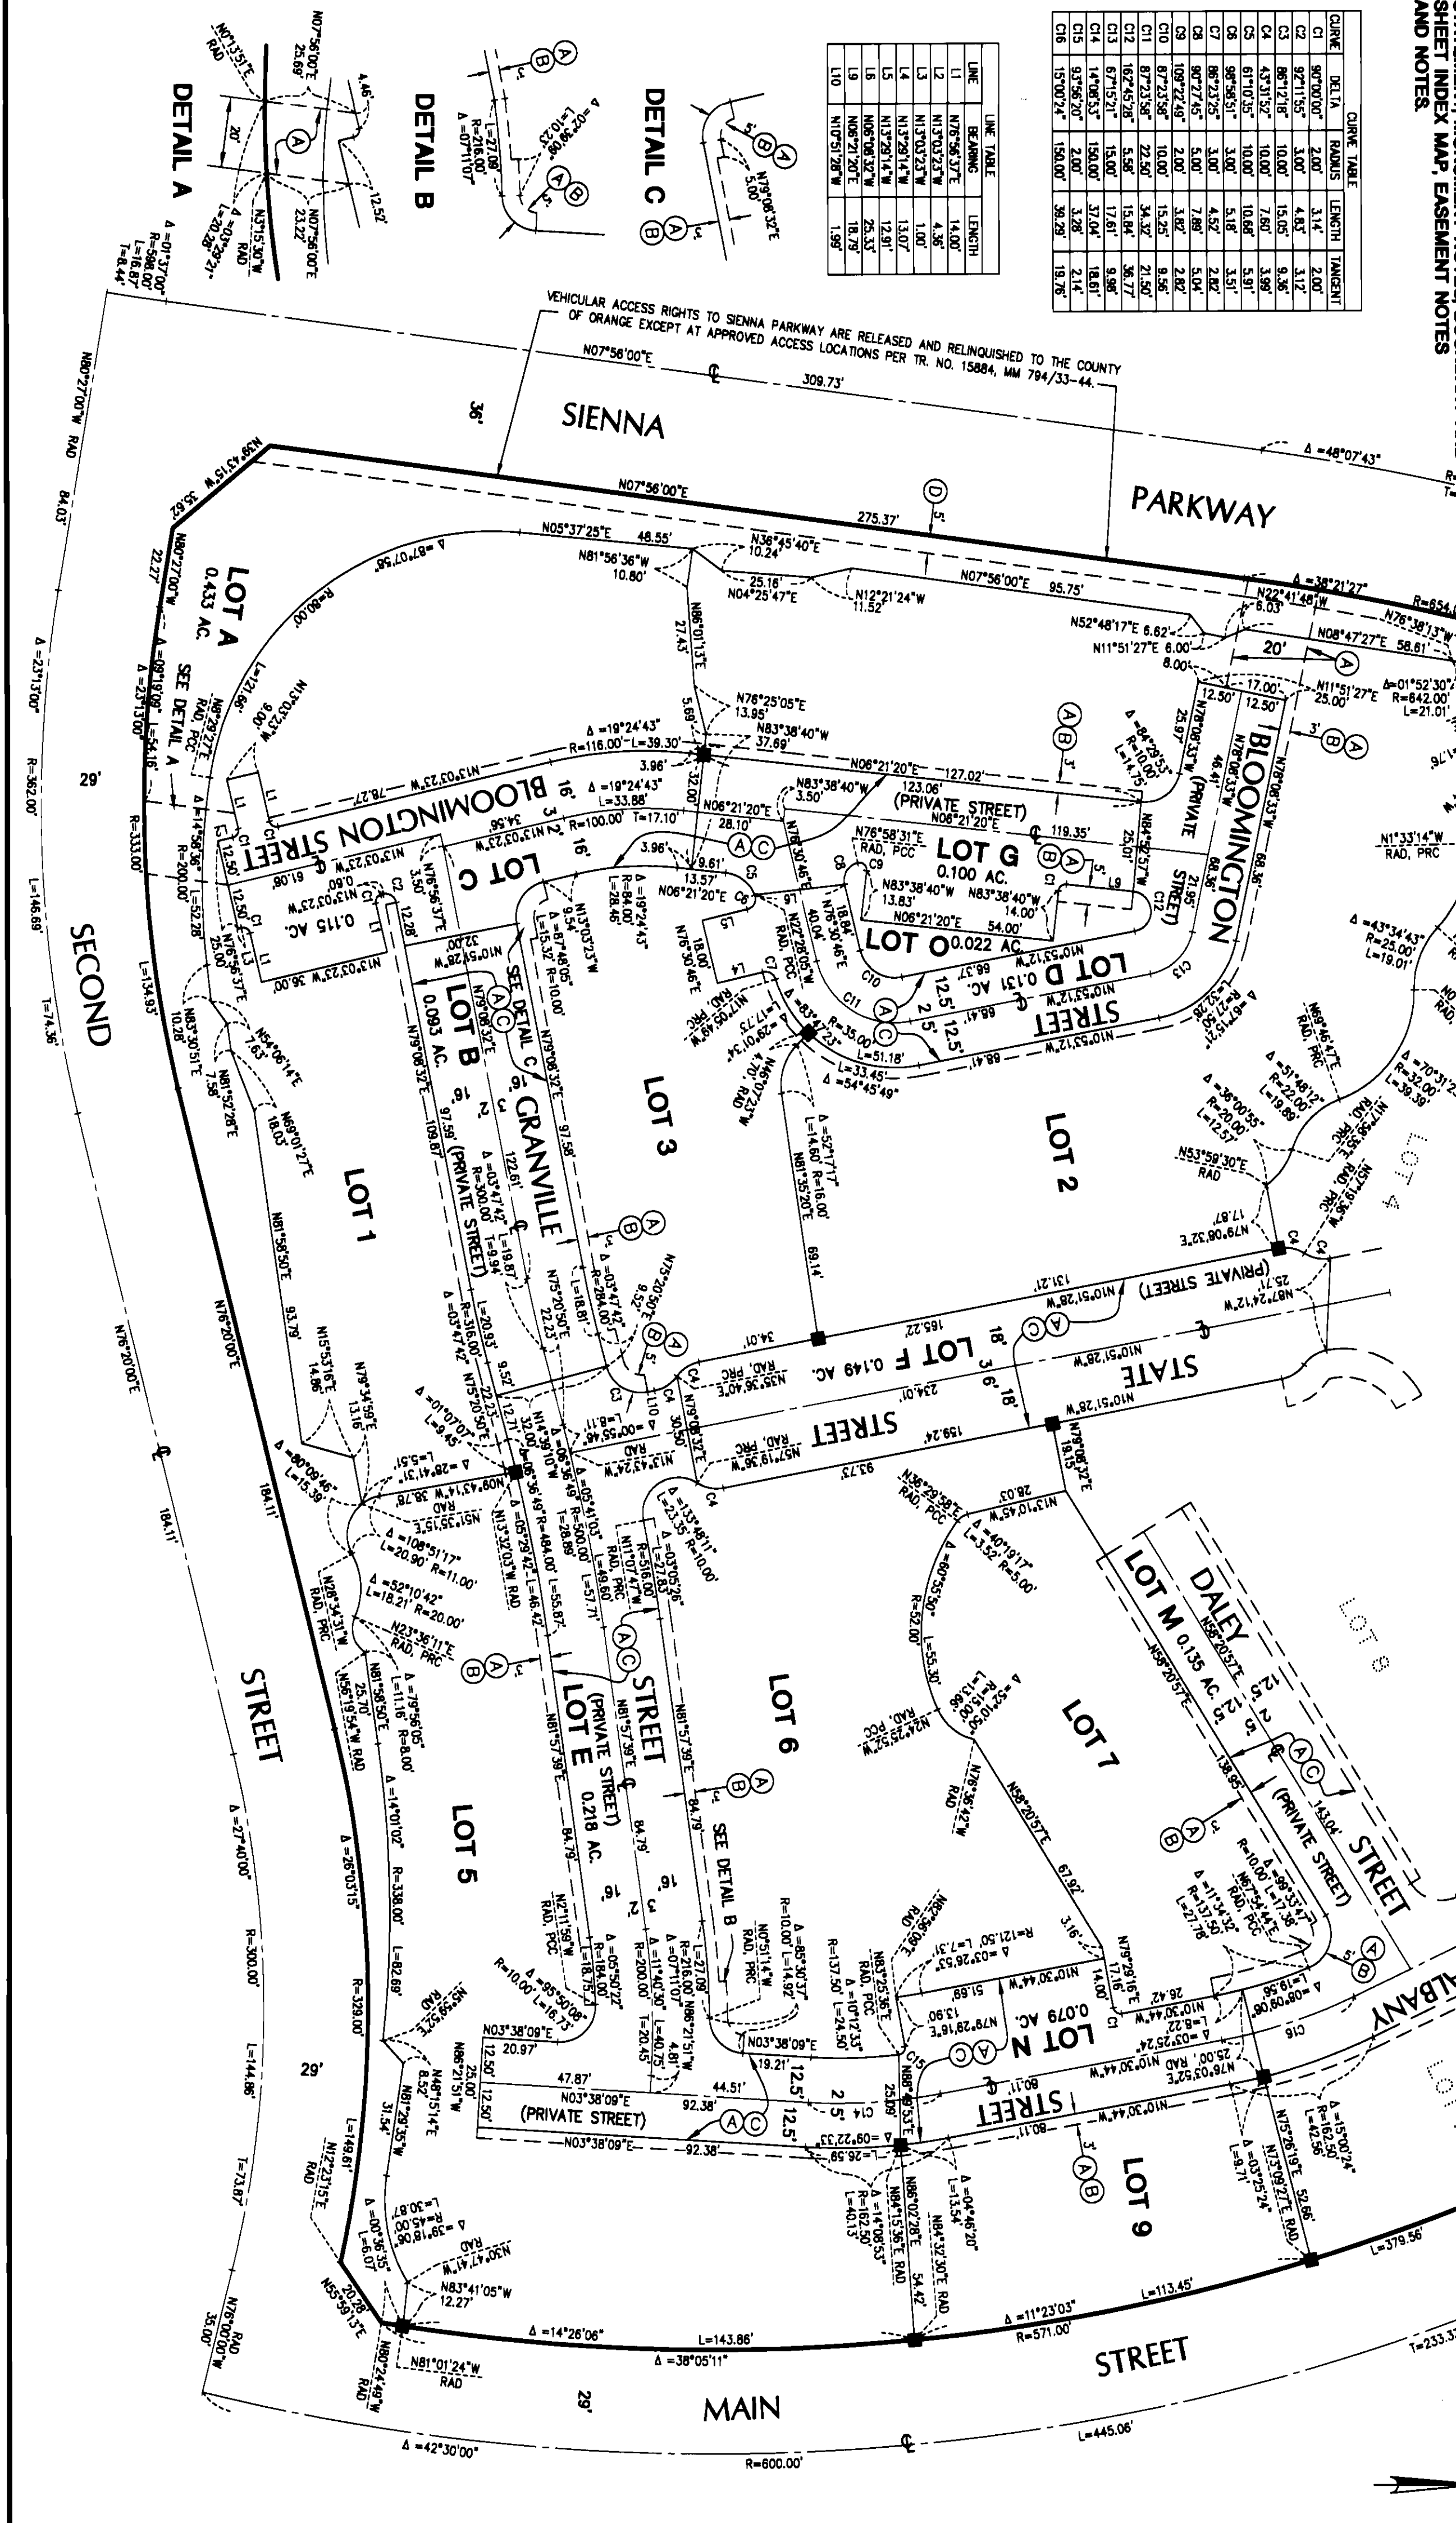

SHEET 4 OF 4 SHEETS
SCALE: 1" = 30'
12 NUMBERED LOTS AND LOTS
A THROUGH O, INCLUSIVE
ACREAGE: 6.030 ACRES
(ALL OF TENTATIVE
TRACT No. 15887)

TRACT No. 15887


IN THE UNINCORPORATED TERRITORY OF THE
COUNTY OF ORANGE, STATE OF CALIFORNIA.
HUNSAKER AND ASSOCIATES IRVINE, INC.
RORY S. WILLIAMS, L.S. 6654 DATE OF SURVEY: JANUARY, 2000

SEE SHEET 2 FOR BASIS OF BEARINGS, DATUM
STATEMENT, MONUMENT NOTES, BOUNDARY AND
SHEET INDEX MAP, EASEMENT NOTES AND NOTES.



CURVE TABLE				
CURVE	DELTA	RADIUS	LENGTH	TANGENT
C1	90°00'00"	2.00'	3.14'	2.00'
C4	43°31'52"	10.00'	7.80'	3.99'
C16	15°00'24"	150.00'	39.29'	19.76'
C17	32°13'51"	15.00'	8.44'	4.33'
C18	43°30'19"	10.00'	7.59'	3.89'
C19	43°42'24"	10.00'	7.83'	4.01'
C20	43°33'28"	10.00'	7.80'	4.00'
C21	43°21'05"	10.00'	7.57'	3.97'
C22	43°32'43"	10.00'	7.80'	3.99'
C23	43°11'18"	10.00'	7.54'	3.96'
C24	10°08'49"	150.00'	26.48'	13.27'
C25	30°52'45"	10.00'	5.39'	2.76'
C28	85°33'37"	10.00'	11.44'	8.44'
C27	81°25'31"	35.00'	49.74'	30.12'
C28	66°21'54"	35.00'	41.76'	23.77'
C29	13°03'37"	35.00'	7.98'	4.01'
C30	36°41'01"	40.00'	25.61'	13.26'
C31	109°50'15"	3.00'	5.75'	4.27'
C32	66°10'14"	10.00'	11.55'	6.52'
C33	02°19'18"	500.00'	20.26'	10.13'
C34	13°36'04"	100.00'	23.74'	11.93'
C35	90°00'00"	3.00'	4.71'	3.00'

LINE TABLE		
LINE	BEARING	LENGTH
L7	N23°55'02"W	12.92'
L8	N36°06'52"E	30.41'

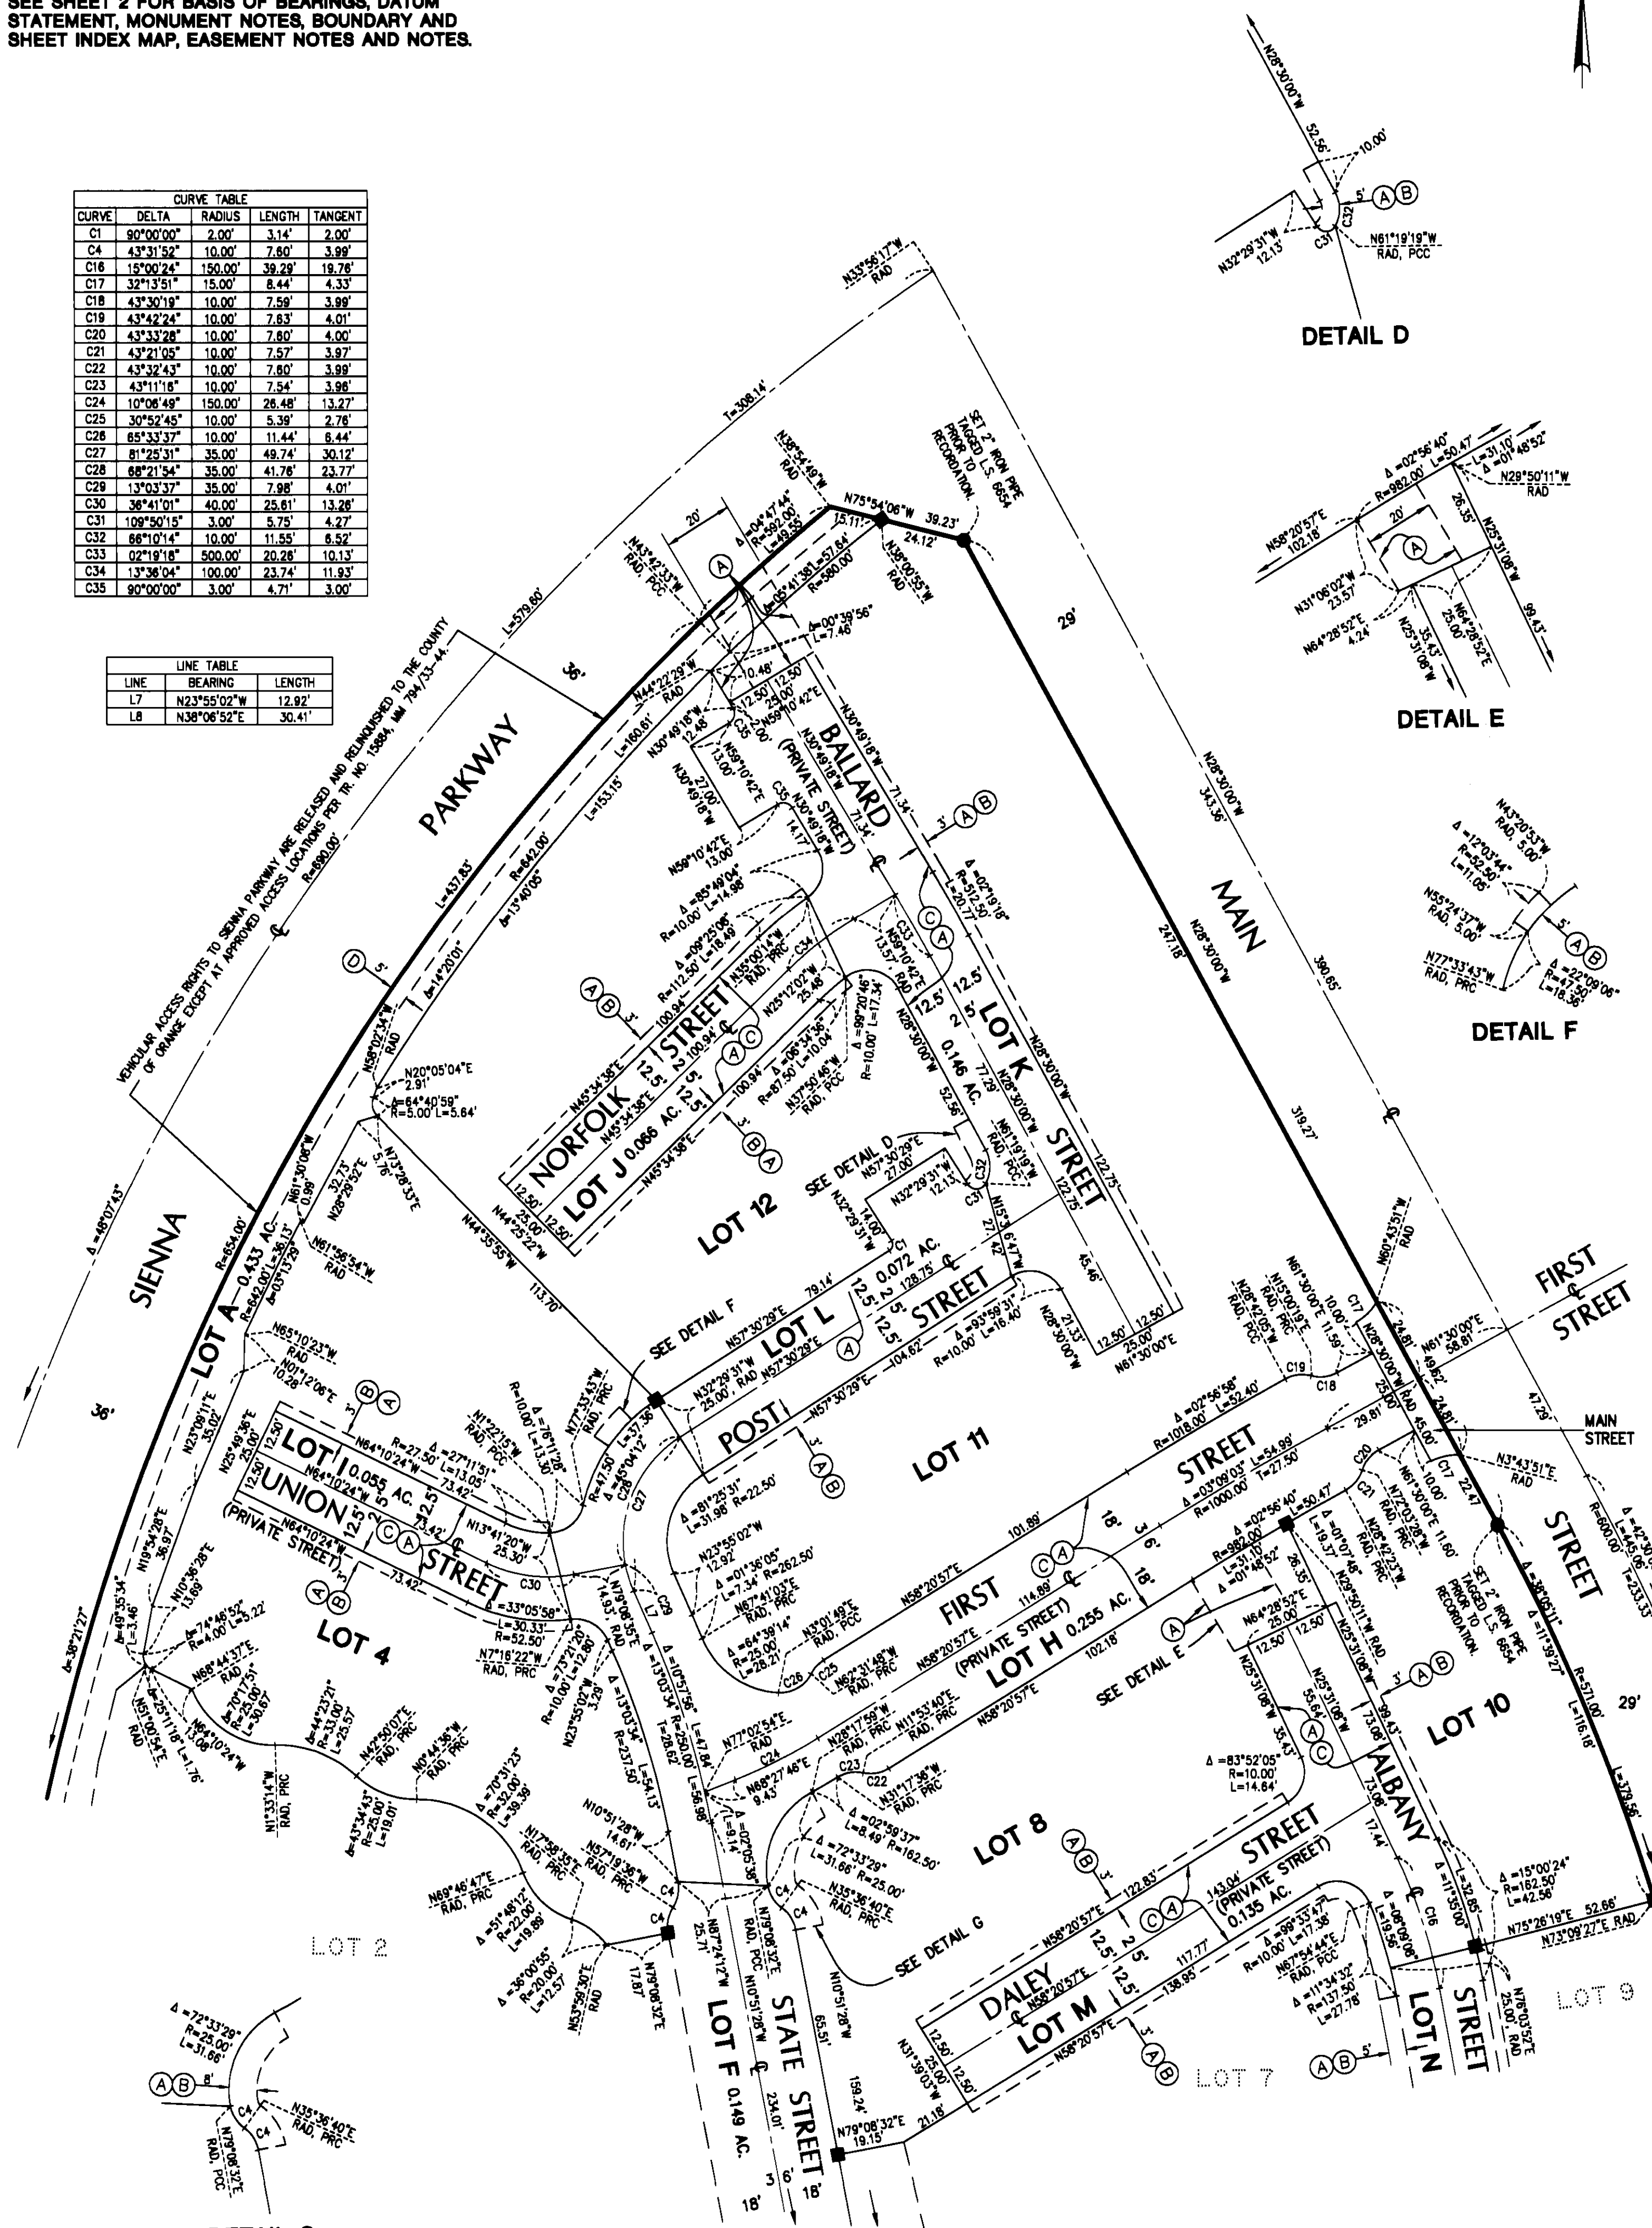

DETAIL G

SEE

SHEET

3

872
28