

SHEET 1 OF 4 SHEETS
60 NUMBERED LOTS AND LOTS
A THROUGH E, INCLUSIVE
5.221 ACRES
(ALL OF TENTATIVE
TRACT NO. 15888)

TRACT NO. 15888

IN THE UNINCORPORATED TERRITORY OF THE
COUNTY OF ORANGE, STATE OF CALIFORNIA

BEING A SUBDIVISION OF LOT 6 OF TRACT NO. 15884, AS SHOWN ON A MAP FILED IN FILED IN
BOOK 794, PAGES 33 THROUGH 44, INCLUSIVE, OF MISCELLANEOUS MAPS, IN THE OFFICE OF
THE COUNTY RECORDER OF SAID COUNTY OF ORANGE

BLOCK: 5157
MODULE: 27

HUNSAKER AND ASSOCIATES IRVINE, INC.
TOM R. McGANNON, R.C.E. 23956 DATE OF SURVEY: JANUARY, 2000

ACCEPTED AND FILED AT THE
REQUEST OF

LAWYERS TULE CO.
DATE: JUN. 2, 2000
TIME: 1:40pm FEE: \$13.00
INSTRUMENT NO. 20000290999
BOOK 802 PAGE 14-17

GARY L. GRANVILLE
COUNTY CLERK - RECORDER
BY John R. Hall DEPUTY

OWNERSHIP CERTIFICATE:

WE, THE UNDERSIGNED, BEING ALL PARTIES HAVING ANY RECORD TITLE INTEREST IN THE LAND COVERED BY THIS MAP, DO HEREBY CONSENT TO THE PREPARATION AND RECORDATION OF SAID MAP, AS SHOWN WITHIN THE DISTINCTIVE BORDER LINE.

WE HEREBY DEDICATE TO THE COUNTY OF ORANGE:

AN EASEMENT FOR INGRESS AND EGRESS OF EMERGENCY AND PUBLIC SERVICE VEHICLES OVER LOTS B, C, D AND E.

WE RESERVE TO OURSELVES, OUR SUCCESSORS AND ASSIGNS THE PUBLIC UTILITY EASEMENTS SHOWN ON THIS MAP, FOR THE USE AND BENEFIT OF THE VARIOUS UTILITY COMPANIES AUTHORIZED TO PROVIDE SERVICE TO THE LOTS SHOWN HEREON.

WE ALSO DO HEREBY DECLARE THAT THE LAND COVERED BY THIS MAP IS LOCATED IN A HIGH FIRE HAZARD AREA DUE TO WILDLAND EXPOSURE. THIS DECLARATION SHALL RUN WITH THE LAND UNTIL A DETERMINATION IS MADE BY THE FIRE AGENCY THAT THE PROPERTY IS NO LONGER LOCATED IN A HIGH FIRE HAZARD AREA.

WE ALSO HEREBY DEDICATE TO THE SANTA MARGARITA WATER DISTRICT THE PIPELINE EASEMENTS FOR ACCESS, WATER AND SEWER PURPOSES, OVER ALL THE PRIVATE DRIVES AND STREETS TOGETHER WITH THE PIPELINE EASEMENT FOR WATER, AND ACCESS PURPOSES, ALL AS SHOWN ON THIS TRACT MAP, WHICH EASEMENTS SHALL BE SUBJECT TO THE SAME TERMS AND CONDITIONS AS SHOWN IN THAT CERTAIN EASEMENT, RECORDED OCTOBER 6, 1980, IN BOOK 13776, PAGE 341 OF OFFICIAL RECORDS OF ORANGE COUNTY, CALIFORNIA.

K. HOVNIANIAN AT THE GABLES, LLC, A CALIFORNIA LIMITED LIABILITY COMPANY; OWNER.

BY: Nicholas Pappas
NAME: NICHOLAS PAPPAS
TITLE: PRESIDENT

DMB LADERA, L.L.C., A DELAWARE LIMITED LIABILITY COMPANY, BENEFICIARY UNDER DEED OF TRUST RECORDED AS INSTRUMENT NO. 20000080968, OF OFFICIAL RECORDS AND OPTIONEE PER DOCUMENT RECORDED AS INSTRUMENT NO. 20000080967 OF OFFICIAL RECORDS.

BY: RANCHO MISSION VIEJO, L.L.C., A DELAWARE LIMITED LIABILITY COMPANY, AS AGENT AND/OR MANAGER.

BY: Paul Johnson
NAME: PAUL JOHNSON
TITLE: V.P.

NOTARY ACKNOWLEDGMENTS:

STATE OF CALIFORNIA } SS
COUNTY OF ORANGE }

ON Apr. 19, 2000 BEFORE ME, Karen R. Sauerwein, PERSONALLY APPEARED Nicholas Pappas AND Paul Johnson, PERSONALLY KNOWN TO ME (OR PROVED TO ME ON THE BASIS OF SATISFACTORY EVIDENCE) TO BE THE PERSON(S) WHOSE NAME(S) IS/ARE SUBSCRIBED TO THE WITHIN INSTRUMENT AND ACKNOWLEDGED TO ME THAT HE/SHE/THEY EXECUTED THE SAME IN HIS/HER/THEIR AUTHORIZED CAPACITY(IES), AND THAT BY HIS/HER/THEIR SIGNATURE(S) ON THE INSTRUMENT THE PERSON(S), OR ENTITY UPON BEHALF OF WHICH THE PERSON(S) ACTED, EXECUTED THE INSTRUMENT.

WITNESS MY HAND:

SIGNATURE: Karen R. Sauerwein
NOTARY PUBLIC IN AND FOR SAID STATE
Karen R. Sauerwein
(NAME PRINTED)

MY PRINCIPAL PLACE OF BUSINESS IS
IN Orange COUNTY.
MY COMMISSION EXPIRES: Nov. 27, 2002

STATE OF CALIFORNIA } SS
COUNTY OF ORANGE }

ON 4-27-00 BEFORE ME, JEANNINE CARTA-HANSON, PERSONALLY APPEARED PAUL JOHNSON AND Paul Johnson, PERSONALLY KNOWN TO ME (OR PROVED TO ME ON THE BASIS OF SATISFACTORY EVIDENCE) TO BE THE PERSON(S) WHOSE NAME(S) IS/ARE SUBSCRIBED TO THE WITHIN INSTRUMENT AND ACKNOWLEDGED TO ME THAT HE/SHE/THEY EXECUTED THE SAME IN HIS/HER/THEIR AUTHORIZED CAPACITY(IES), AND THAT BY HIS/HER/THEIR SIGNATURE(S) ON THE INSTRUMENT THE PERSON(S), OR ENTITY UPON BEHALF OF WHICH THE PERSON(S) ACTED, EXECUTED THE INSTRUMENT.

WITNESS MY HAND:

SIGNATURE: Jeannine Carta-Hanson
NOTARY PUBLIC IN AND FOR SAID STATE
JEANNINE CARTA-HANSON
(NAME PRINTED)

MY PRINCIPAL PLACE OF BUSINESS IS
IN ORANGE COUNTY.
MY COMMISSION EXPIRES: Feb. 25, 2003

STATE OF CALIFORNIA } SS
COUNTY OF ORANGE }

ON 5-2-00 BEFORE ME, Cindy R. Lane, Notary Public, PERSONALLY APPEARED DANIEL R. FERONS, PERSONALLY KNOWN TO ME (OR PROVED TO ME ON THE BASIS OF SATISFACTORY EVIDENCE) TO BE THE PERSON WHOSE NAME IS SUBSCRIBED TO THE WITHIN INSTRUMENT AND ACKNOWLEDGED TO ME THAT HE EXECUTED THE SAME IN HIS AUTHORIZED CAPACITY, AND THAT BY HIS SIGNATURE ON THE INSTRUMENT THE PERSON, OR ENTITY UPON BEHALF OF WHICH THE PERSON ACTED, EXECUTED THE INSTRUMENT.

WITNESS MY HAND:

SIGNATURE: Cindy R. Lane
NOTARY PUBLIC IN AND FOR SAID STATE
CINDY R. LANE
(NAME PRINTED)

MY PRINCIPAL PLACE OF BUSINESS IS
IN ORANGE COUNTY.
MY COMMISSION EXPIRES: FEB. 20, 2001

ENGINEER'S STATEMENT:

I HEREBY STATE THAT THIS MAP, CONSISTING OF 4 SHEETS, CORRECTLY REPRESENTS TRUE AND COMPLETE SURVEY AS SHOWN MADE IN JANUARY, 2000; WAS MADE BY ME OR UNDER MY DIRECTION; THAT THE MONUMENTS ARE OF THE CHARACTER AND OCCUPY (OR WILL OCCUPY) THE POSITIONS INDICATED BY SAID MAP; AND THAT SAID MONUMENTS ARE (OR WILL BE) SUFFICIENT TO ENABLE THE SURVEY TO BE RETRACED.

Tom R. McGannon
TOM R. McGANNON,
R.C.E. NO. 23956
EXPIRATION DATE: 12/31/01




COUNTY SURVEYOR'S STATEMENT

I HEREBY STATE THAT I HAVE EXAMINED THIS MAP AND HAVE FOUND IT TO BE SUBSTANTIALLY IN CONFORMANCE WITH THE TENTATIVE MAP AS FILED WITH, AMENDED AND APPROVED BY THE ORANGE COUNTY SUBDIVISION COMMITTEE; THAT ALL PROVISIONS OF THE SUBDIVISION MAP ACT AND COUNTY SUBDIVISION REGULATIONS HAVE BEEN COMPLIED WITH AND I AM SATISFIED SAID MAP IS TECHNICALLY CORRECT.

DATED THIS 12th DAY OF May, 2000.

Robert Jelinek
JOHN CANAS, COUNTY SURVEYOR
ROBERT JELINEK, DEPUTY COUNTY SURVEYOR

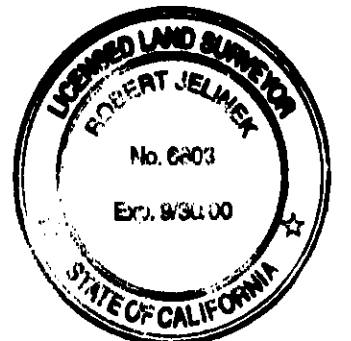

COUNTY TREASURER-TAX COLLECTOR'S CERTIFICATE:

STATE OF CALIFORNIA } SS
COUNTY OF ORANGE }

I HEREBY CERTIFY THAT ACCORDING TO THE RECORDS OF MY OFFICE THERE ARE NO LIENS AGAINST THE LAND COVERED BY THIS MAP OR ANY PART THEREOF FOR UNPAID STATE, COUNTY, MUNICIPAL OR LOCAL TAXES OR SPECIAL ASSESSMENTS COLLECTED AS TAXES, EXCEPT TAXES OR SPECIAL ASSESSMENTS COLLECTED AS TAXES NOT YET PAYABLE.

AND DO ALSO CERTIFY TO THE RECORDER OF ORANGE COUNTY THAT THE PROVISIONS OF THE SUBDIVISION MAP ACT HAVE BEEN COMPLIED WITH REGARDING DEPOSITS TO SECURE THE PAYMENT OF TAXES OR SPECIAL ASSESSMENTS COLLECTED AS TAXES ON THE LAND COVERED BY THIS MAP.

DATED THIS 5th DAY OF May, 2000.

John M.W. Moorlach
COUNTY TREASURER-TAX COLLECTOR

BY: John M.W. Moorlach
DEPUTY TREASURER-TAX COLLECTOR

CLERK OF THE BOARD OF SUPERVISORS' CERTIFICATE:

STATE OF CALIFORNIA } SS
COUNTY OF ORANGE }

I HEREBY CERTIFY THAT THIS MAP WAS PRESENTED FOR APPROVAL TO THE BOARD OF SUPERVISORS OF THE COUNTY OF ORANGE AT REGULAR MEETING THEREOF HELD ON THE 23rd DAY OF May, 2000. AND THAT THEREUPON SAID BOARD DID, BY AN ORDER DULY PASSED AND ENTERED, APPROVED SAID MAP.

AND DID ACCEPT ON BEHALF OF THE COUNTY OF ORANGE:

THE EASEMENT FOR INGRESS AND EGRESS OF EMERGENCY AND PUBLIC SERVICE VEHICLES OVER LOTS B, C, D AND E.

DATED THIS 23rd DAY OF May, 2000.

Darlene J. Bloom
CLERK OF THE BOARD OF SUPERVISORS
DARLENE J. BLOOM



CERTIFICATE OF ACCEPTANCE - SANTA MARGARITA WATER DISTRICT

THE UNDERSIGNED, BEING THE DULY APPOINTED AGENT OF THE SANTA MARGARITA WATER DISTRICT, A PUBLIC CORPORATION IN ORANGE COUNTY, CALIFORNIA, PURSUANT TO ITS RESOLUTION NO. 88-10-2, DOES HEREBY ACCEPT ON BEHALF OF SAID DISTRICT, THE PIPELINE EASEMENTS FOR WATER, SEWER AND ACCESS PURPOSES AS DEDICATED AND SHOWN ON THIS TRACT MAP, BY AND BETWEEN THE SANTA MARGARITA WATER DISTRICT AND K. HOVNIANIAN AT THE GABLES, LLC, A CALIFORNIA LIMITED LIABILITY COMPANY, AND DOES HEREBY CERTIFY THAT THE GRANTEE CONSENTS TO THE RECORDATION OF SAID TRACT MAP.

Daniel R. Ferons
DANIEL R. FERONS, CHIEF ENGINEER
SANTA MARGARITA WATER DISTRICT

NOTES:

THE PRIVATE STREETS CONSTRUCTED WITHIN THIS MAP SHALL BE OWNED, OPERATED AND MAINTAINED BY THE DEVELOPER, SUCCESSORS OR ASSIGNS. THE COUNTY OF ORANGE SHALL HAVE NO RESPONSIBILITY THEREFOR, UNLESS PURSUANT TO APPROPRIATE SECTIONS OF THE STREET AND HIGHWAYS CODE OF THE STATE OF CALIFORNIA, THE SAID PRIVATE STREETS HAVE BEEN ACCEPTED INTO THE COUNTY ROAD SYSTEM BY APPROPRIATE RESOLUTION OF THE ORANGE COUNTY BOARD OF SUPERVISORS.

BUILDING PERMIT ISSUANCE SHALL BE PHASED IN ACCORDANCE WITH THE FOOTHILL CIRCULATION PHASING PLAN (FCPP) DEVELOPMENT PHASING PLAN, AND SHALL ALSO BE SUBJECT TO ANY OTHER BOARD OF SUPERVISORS APPROVED GROWTH MANAGEMENT PHASING PLAN PERTAINING TO THE TIMELY PROVISIONS OF PUBLIC SERVICES AND FACILITIES.

SIGNATURE OMISSIONS:

PURSUANT TO THE PROVISIONS OF SECTION 86436 (a)(3)(C) OF THE SUBDIVISION MAP ACT THE FOLLOWING SIGNATURE HAS BEEN OMITTED:

DMB LADERA, LLC, HOLDER OF EASEMENTS RESERVED IN DOCUMENT RECORDED AS INSTRUMENT NO. 20000080966 OF OFFICIAL RECORDS.

LADERA DEVELOPMENT COMPANY, LLC OWNER OF ALL OIL, OIL RIGHTS, MINERALS, MINERAL RIGHTS, NATURAL GAS RIGHTS, OTHER HYDROCARBONS AND WATER RIGHTS, AS RESERVED IN DEED RECORDED AS INSTRUMENT NO. 19960624029, O.R.

802
14

SHEET 2 OF 4 SHEETS
SCALE 1" = 200'
59 NUMBERED LOTS AND LOTS
A THROUGH E, INCLUSIVE
ACREAGE: 5.221 ACRES
(ALL OF TENTATIVE
TRACT No. 15888)

TRACT No. 15888

IN UNINCORPORATED TERRITORY OF THE COUNTY OF ORANGE,
STATE OF CALIFORNIA

HUNSAKER AND ASSOCIATES IRVINE, INC.
TOM R. MCGANNON, R.C.E. 23956
DATE OF SURVEY: JANUARY, 2000

INDEX AND BOUNDARY MAP

BASIS OF BEARINGS:

THE BEARINGS SHOWN HEREON ARE BASED ON THE BEARING BETWEEN O.C.S. HORIZONTAL CONTROL STATION GPS NO. 1424 AND STATION GPS NO. 1417 BEING N01°36'34"E PER RECORDS ON FILE IN THE OFFICE OF THE ORANGE COUNTY SURVEYOR.

DATUM STATEMENT:

COORDINATES SHOWN ARE BASED ON THE CALIFORNIA COORDINATE SYSTEM (CCS83), ZONE VI, 1983 NAD, (1991.35 EPOCH OCS GPS ADJUSTMENT).

ALL DISTANCES SHOWN ARE GROUND UNLESS OTHERWISE NOTED. TO OBTAIN GRID DISTANCE MULTIPLY GROUND DISTANCE BY 0.99994800.

MONUMENT NOTES:

1" I.P. TAGGED R.C.E. 23956 OR LEAD, TACK & TAG R.C.E. 23956 OR NAIL & TAG R.C.E. 23956 OR 8" S&W STAMPED R.C.E. 23956 TO BE SET AT ALL LOT CORNERS EXCEPT LOT CORNERS THAT ARE THE INTERSECTION OF SIDE LOT LINES WITH STREET RIGHT OF WAY, WITHIN 90 DAYS AFTER ACCEPTANCE OF IMPROVEMENTS, UNLESS OTHERWISE NOTED.

LEAD, TACK & TAG R.C.E. 23956 OR 8" S&W STAMPED R.C.E. 23956 TO BE SET IN TOP OF CURB ON ALL SIDE LOT LINES PRODUCED OR CONTINUED, 0.50' FROM INTERSECTION WITH 22.00' WIDE PRIVATE DRIVE RIGHTS OF WAY, WITHIN 90 DAYS AFTER ACCEPTANCE OF IMPROVEMENTS.

8" S&W STAMPED R.C.E. 23956 OR LEAD, TACK & TAG R.C.E. 23956 OR 1" I.P. TAGGED R.C.E. 23956 IN MEDIAN TO BE SET AT ALL STREET CENTERLINE POINTS OF CONTROL, WITHIN 90 DAYS AFTER ACCEPTANCE OF IMPROVEMENTS, UNLESS OTHERWISE NOTED.

NO MONUMENTS WILL BE SET AT PRIVATE STREET LETTERED LOT CORNERS, EXCEPT WHERE SAID CORNERS ARE COMMON WITH NUMBERED LOT CORNERS OR TRACT BOUNDARY CORNERS, UNLESS OTHERWISE NOTED.

● INDICATES FOUND MONUMENT AS NOTED OR LOCATION OF MONUMENT TO BE SET AS NOTED.

■ INDICATES NOTHING TO BE SET.

NOTES:

THE PROPERTY IS IN A SPECIAL FIRE PROTECTION AREA, A TOTAL EXCLUSION HAS BEEN GRANTED FOR THIS TRACT.

ALL STRUCTURES EXCEEDING FIRE DEPARTMENT ACCESS REQUIREMENTS SHALL BE PROTECTED WITH AUTOMATIC FIRE SPRINKLERS.

MONUMENT NOTES (CONTINUED):


- 1 INDICATES FD. 2 1/2" O.C.S. BRASS DISK IN WELL MONUMENT PER TRACT NO. 15813, M.M. 795 / 1-16.
- 2 INDICATES LOCATION OF 1" IRON PIPE TAGGED "L.S. 5557" OR SPIKE & WASHER STAMPED "L.S. 5557" OR LEAD, TACK & TAG "L.S. 5557" TO BE SET WITHIN 90 DAYS AFTER ACCEPTANCE OF IMPROVEMENTS, PER TRACT NO. 15884, M.M. 794 / 33-44.
- 3 INDICATES LOCATION OF 1" IRON PIPE TAGGED "L.S. 5557" OR SPIKE & WASHER STAMPED "L.S. 5557" OR LEAD, TACK & TAG "L.S. 5557" TO BE SET WITHIN 90 DAYS AFTER ACCEPTANCE OF IMPROVEMENTS, PER TRACT NO. 15815, M.M. 777 / 14-31.
- 4 INDICATES SET 2" IRON PIPE TAGGED " R.C.E. 23956 PRIOR TO THE RECORDATION OF THIS MAP.

GPS NO. 1424

FD. 2 1/2" IRON PIPE WITH 2" OCS BRASS CAP STAMPED "GPS 1424 9-95" PER R.S.B. 154/8-18 AND RECORDS ON FILE IN THE ORANGE COUNTY SURVEYORS OFFICE.
N 2152873.842
E 6141904.527

GPS NO. 1417

FD. 2 1/2" IRON PIPE WITH 2" OCS BRASS CAP STAMPED "GPS 1417 9-95" PER R.S.B. 154/8-18 AND RECORDS ON FILE IN THE ORANGE COUNTY SURVEYORS OFFICE.
N 2141450.558
E 6141583.535


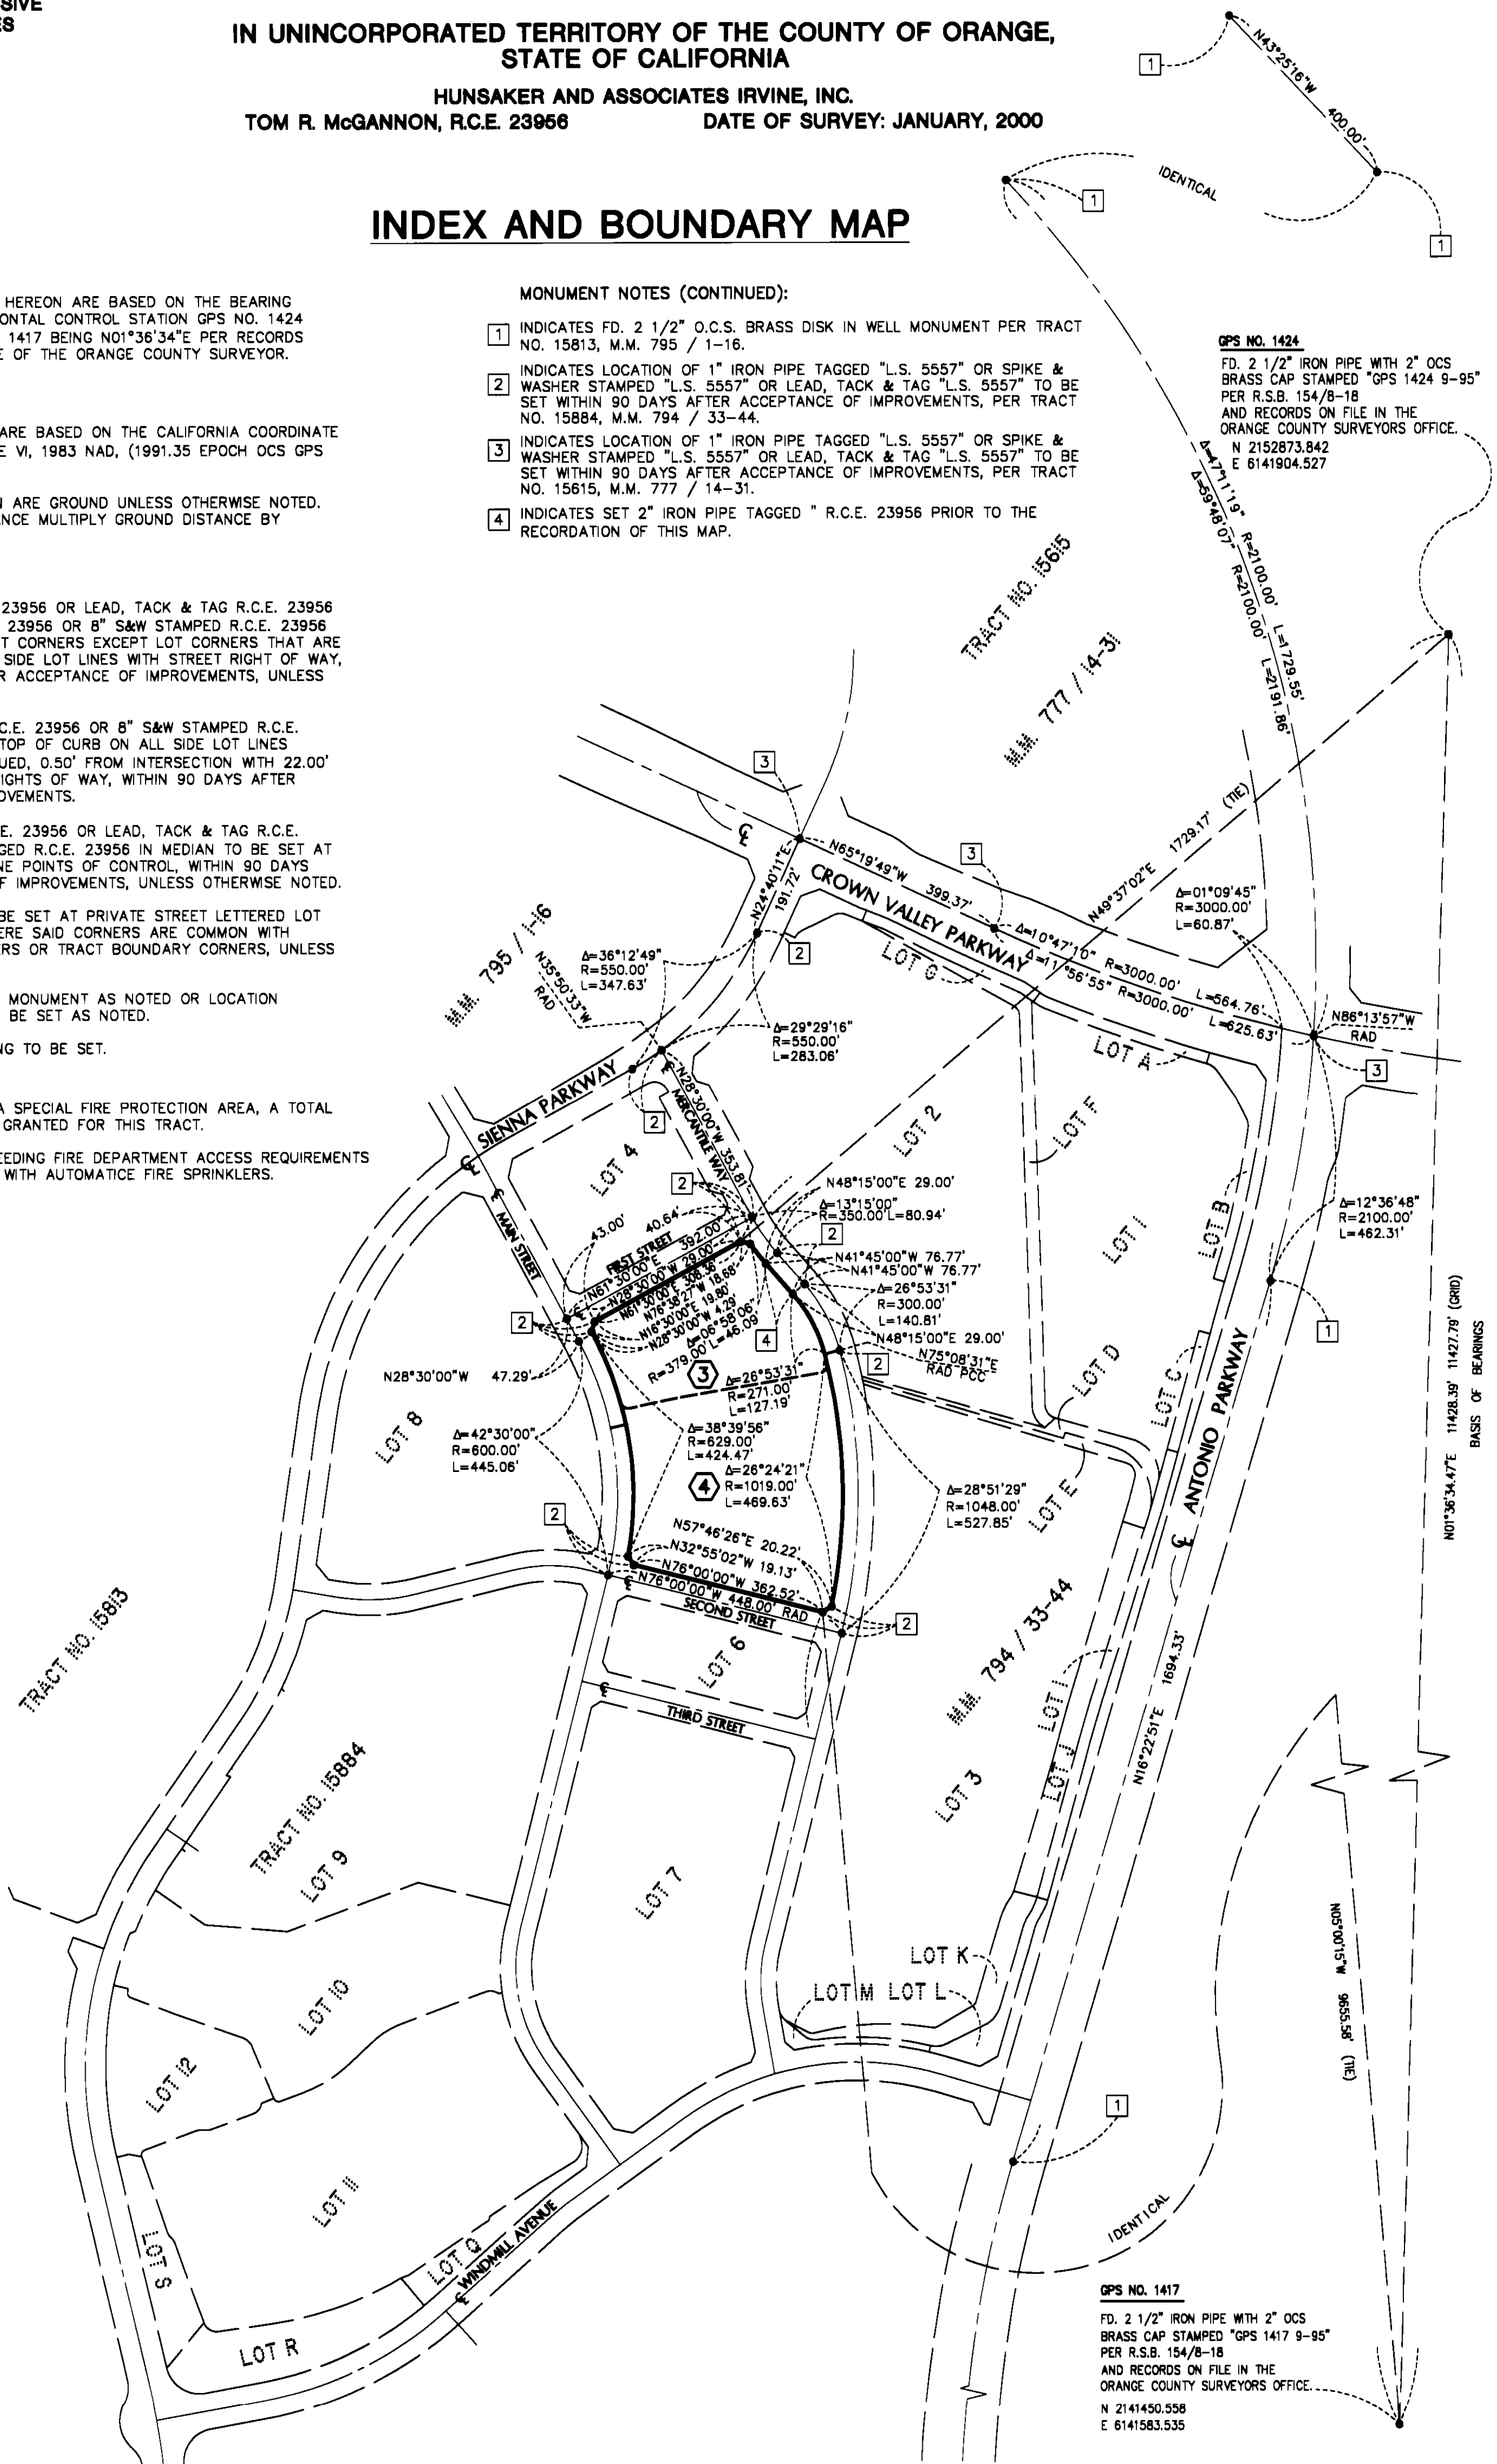


SHEET 3 OF 4 SHEETS
SCALE 1" = 30'
59 NUMBERED LOTS AND LOTS
A THROUGH E INCLUSIVE
ACREAGE: 5.221 ACRES
(ALL OF TENTATIVE
TRACT No. 15888)


TRACT No. 15888

IN THE UNINCORPORATED TERRITORY OF THE COUNTY OF ORANGE,
STATE OF CALIFORNIA


HUNSAKER AND ASSOCIATES IRVINE, INC.
TOM R. MCGANNON, R.C.E. 23966 DATE OF SURVEY: JANUARY, 2000

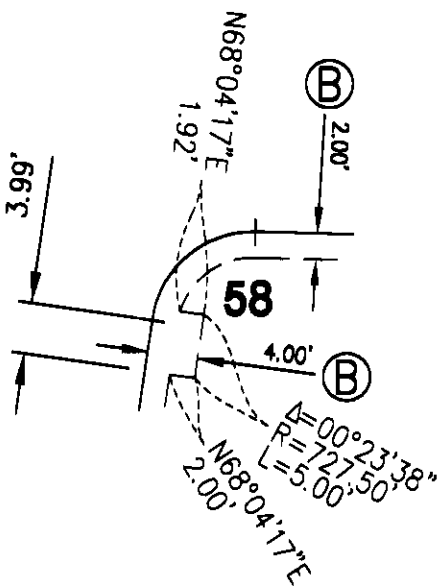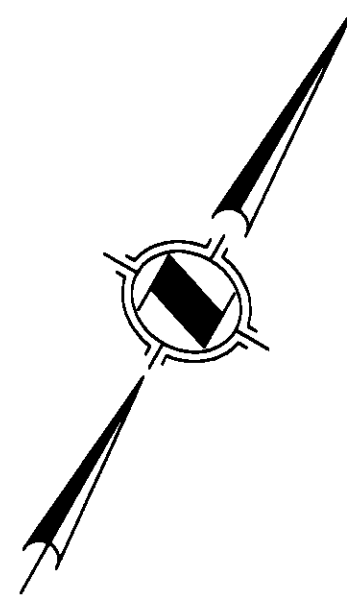

DETAIL A
NO SCALE

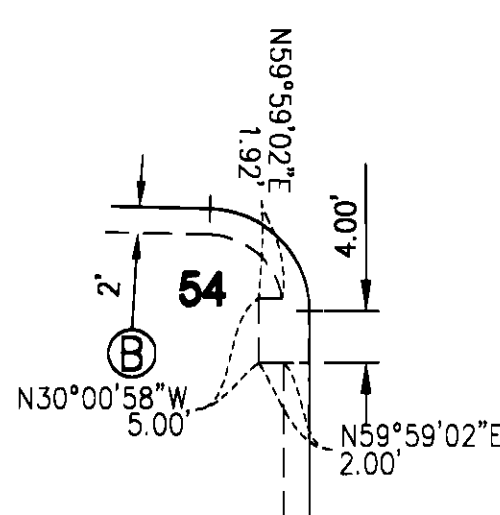

DETAIL B
NO SCALE

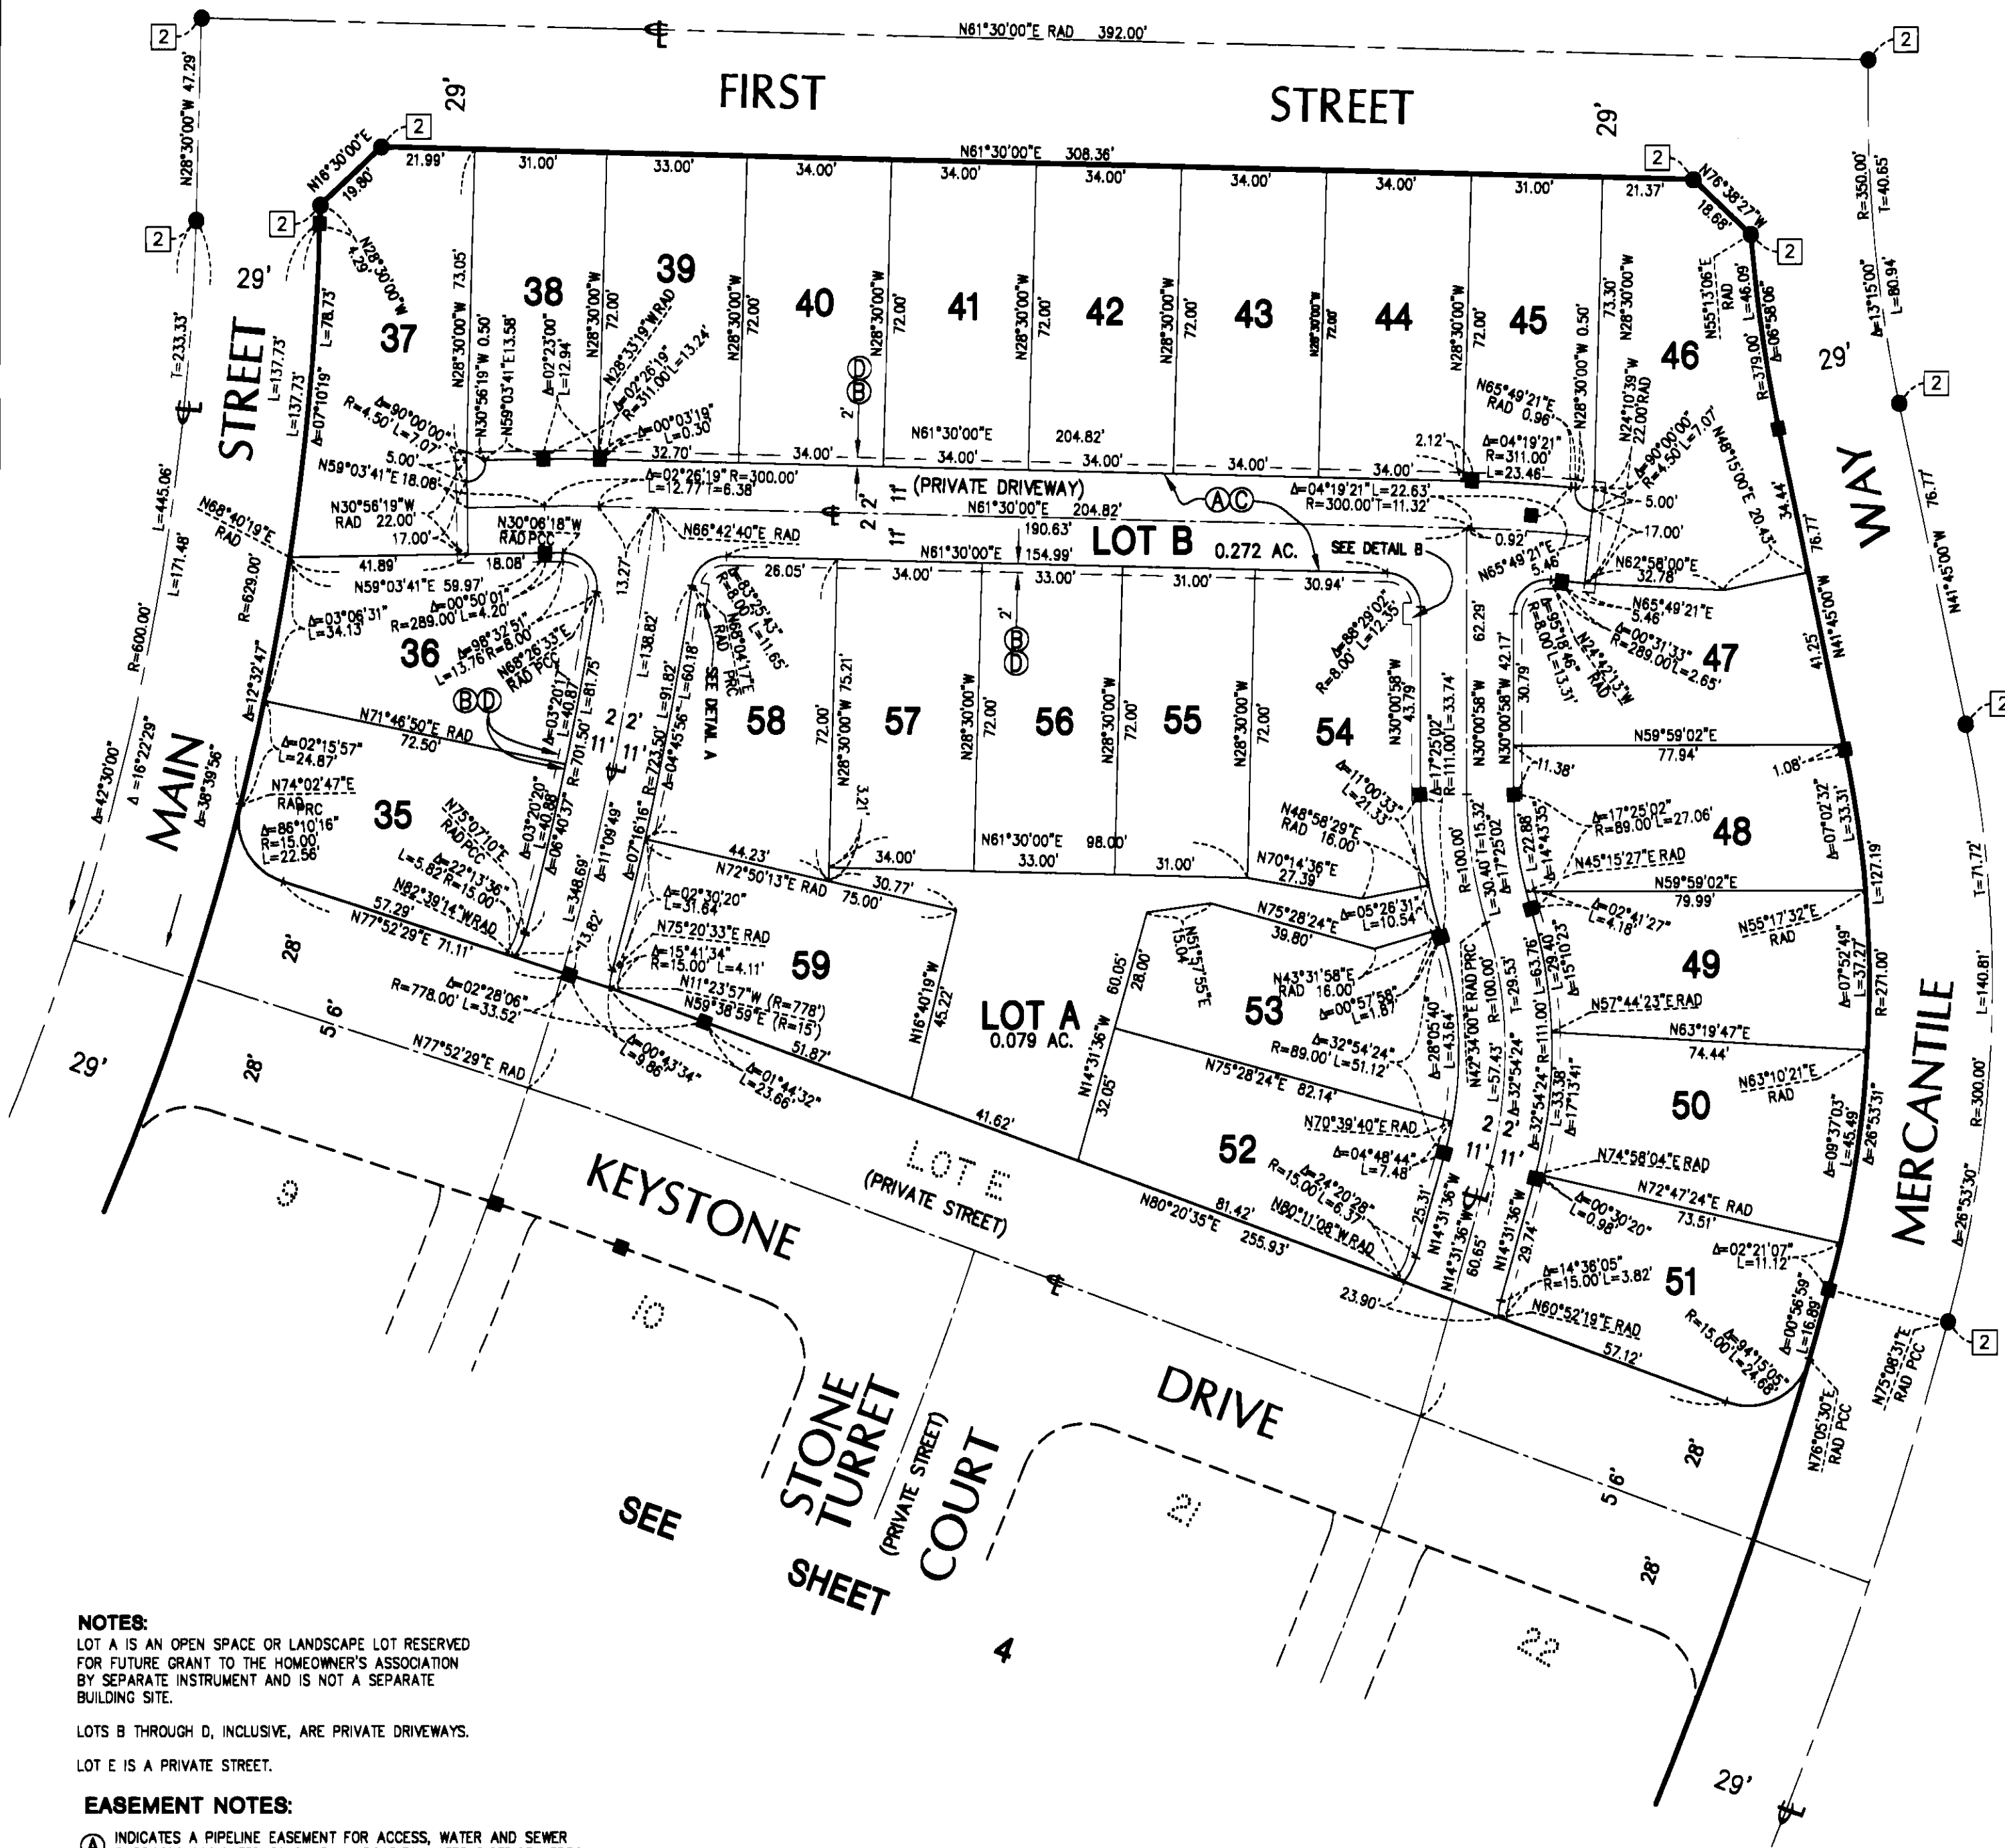

NOTES:
LOT A IS AN OPEN SPACE OR LANDSCAPE LOT RESERVED
FOR FUTURE GRANT TO THE HOMEOWNER'S ASSOCIATION
BY SEPARATE INSTRUMENT AND IS NOT A SEPARATE
BUILDING SITE.

LOTS B THROUGH D, INCLUSIVE, ARE PRIVATE DRIVEWAYS.
LOT E IS A PRIVATE STREET.

EASEMENT NOTES:

- (A) INDICATES A PIPELINE EASEMENT FOR ACCESS, WATER AND SEWER
PURPOSES DEDICATED TO SANTA MARGARITA WATER DISTRICT HEREON.
- (B) INDICATES A PIPELINE EASEMENT FOR WATER LINE AND ACCESS
PURPOSES DEDICATED HEREON TO SANTA MARGARITA WATER DISTRICT.
- (C) INDICATES AN EASEMENT FOR INGRESS AND EGRESS OF EMERGENCY
AND PUBLIC SERVICE VEHICLES DEDICATED HEREON TO SAID COUNTY
OF ORANGE.
- (D) INDICATES AN EASEMENT FOR PUBLIC UTILITY PURPOSES RESERVED
HEREON FOR FUTURE GRANT.

SEE SHEET 2 FOR BASIS OF BEARINGS, DATUM
STATEMENT, MONUMENT NOTES, AND INDEX AND
BOUNDARY MAP.



SHEET 4 OF 4 SHEETS
SCALE 1" = 30'
59 NUMBERED LOTS AND LOTS
A THROUGH E INCLUSIVE
ACREAGE: 6.221 ACRES
(ALL OF TENTATIVE
TRACT No. 15888)

TRACT No. 15888

IN THE UNINCORPORATED TERRITORY OF THE COUNTY OF ORANGE,
STATE OF CALIFORNIA

HUNSAKER AND ASSOCIATES IRVINE, INC.
TOM R. McGANNON, R.C.E. 23956

DATE OF SURVEY: JANUARY, 2000

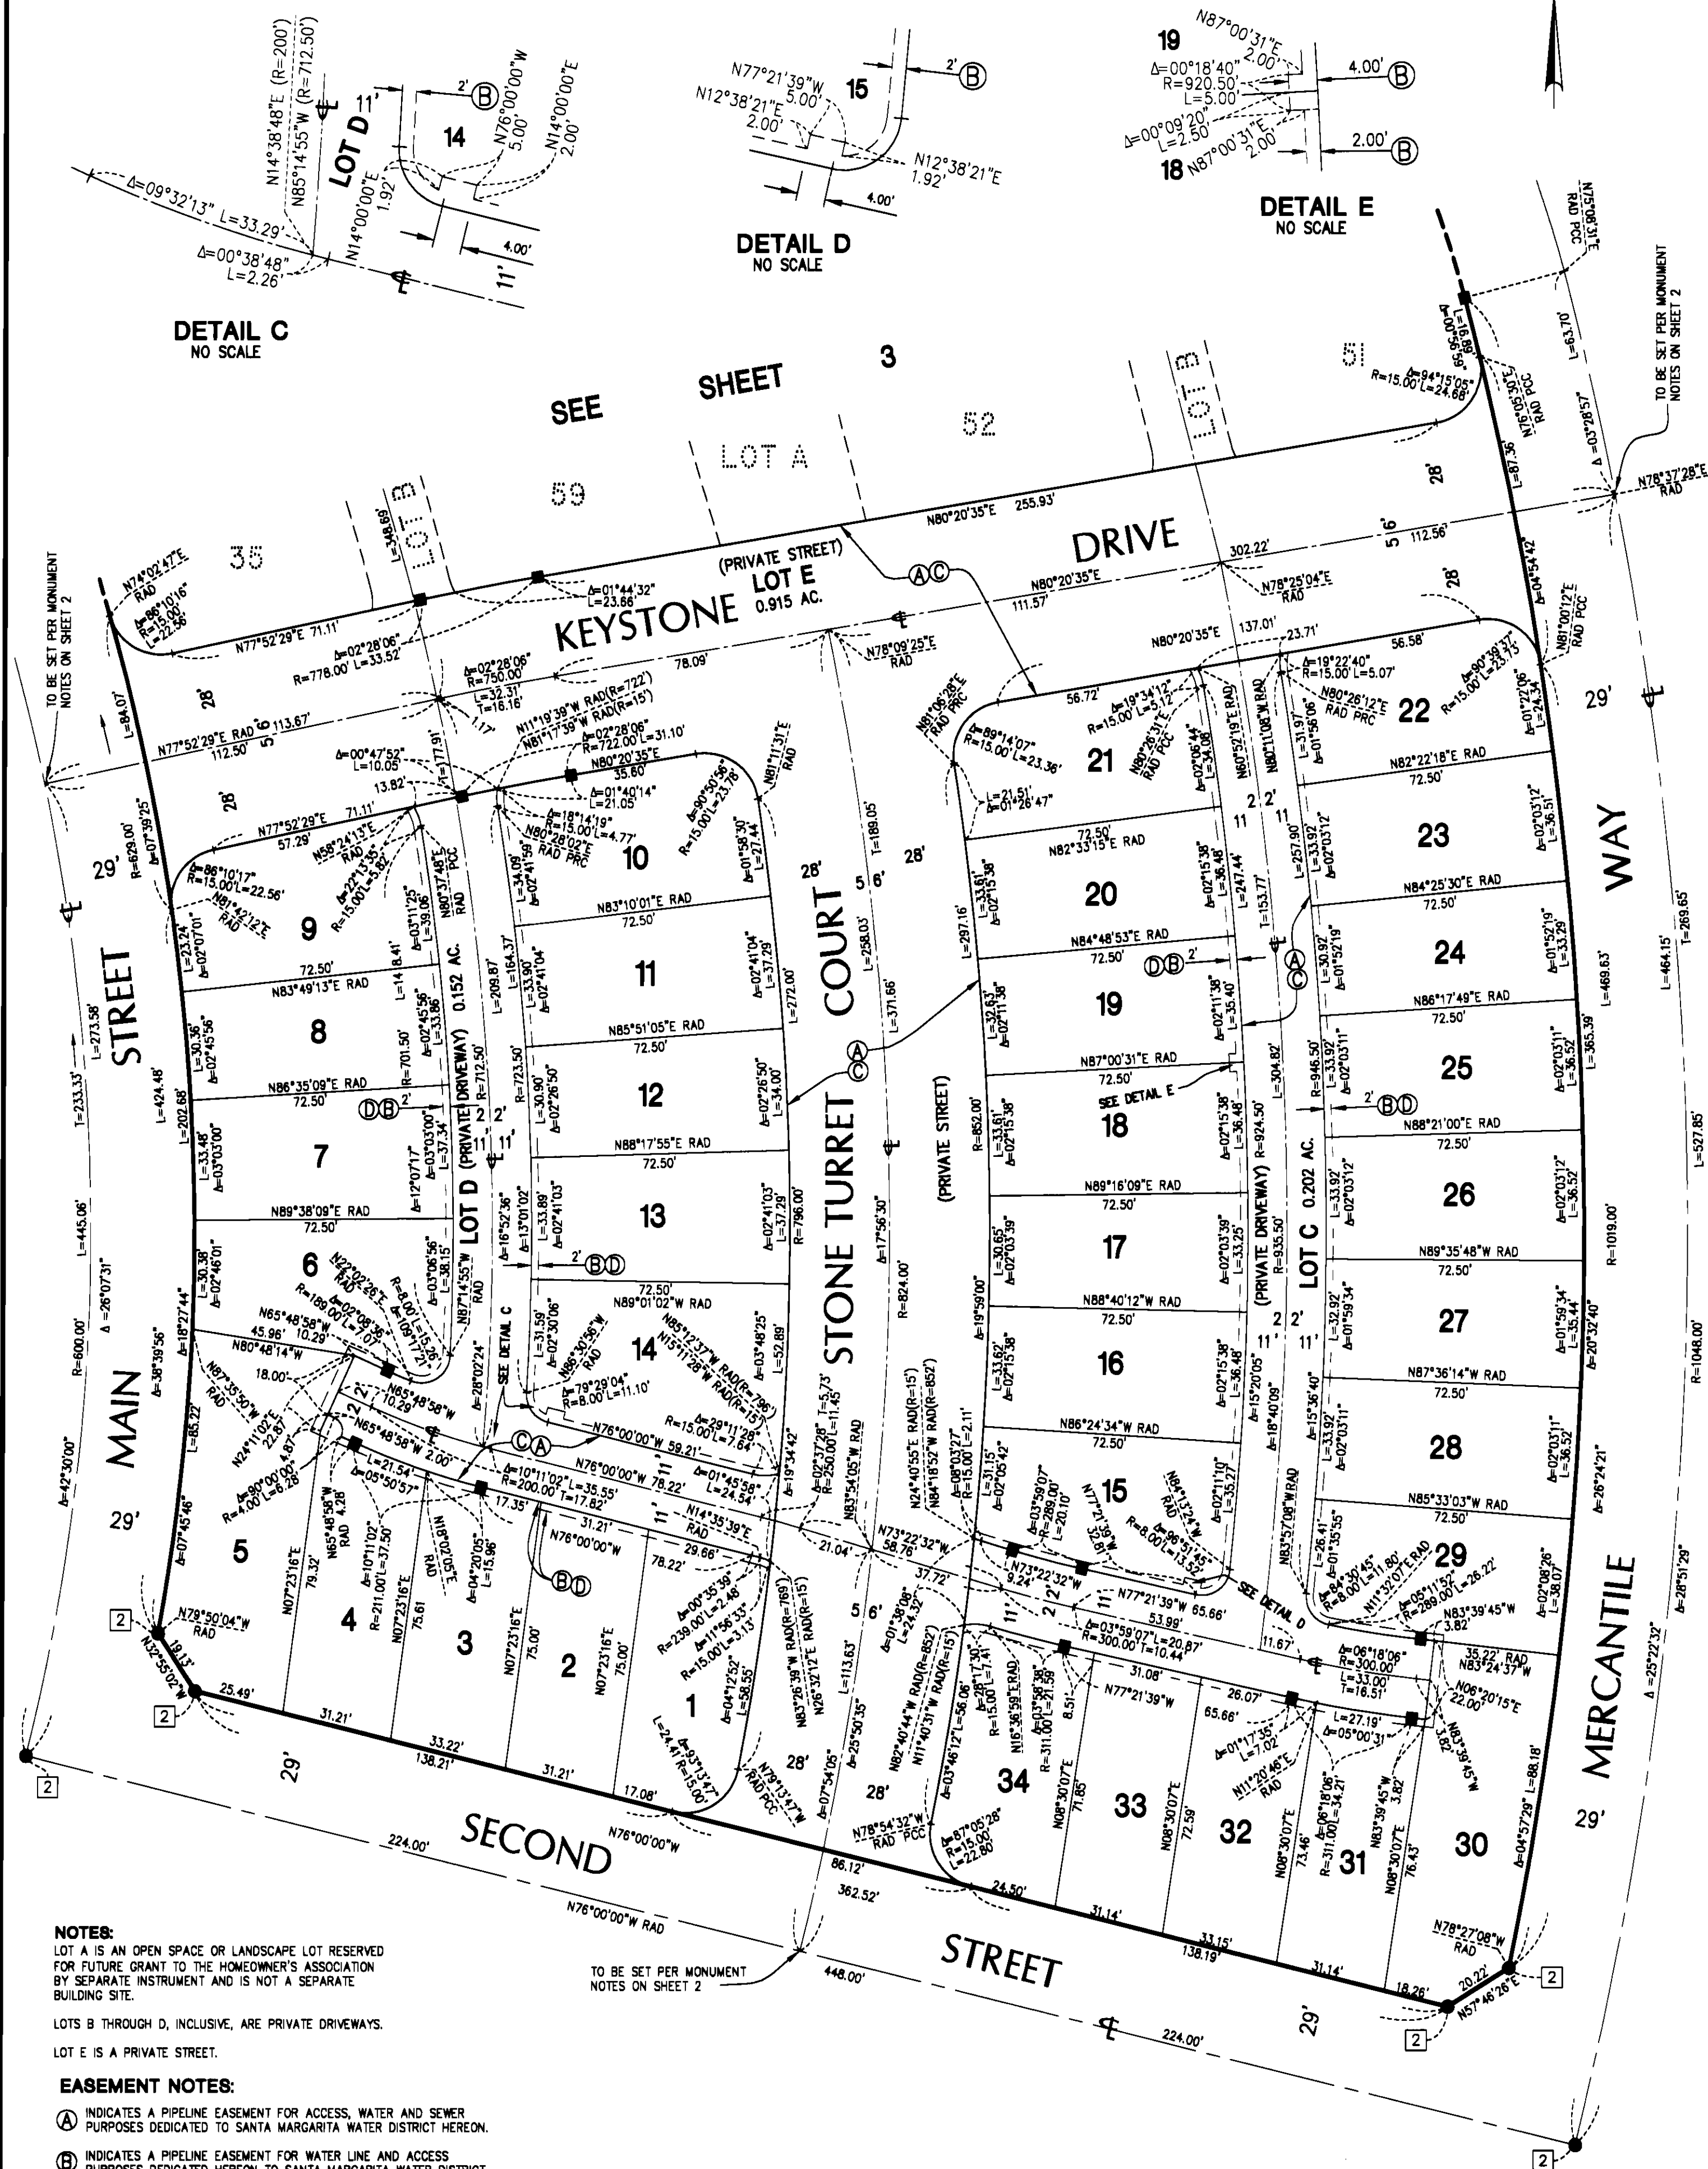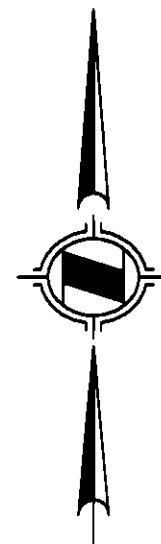

NOTES:

LOT A IS AN OPEN SPACE OR LANDSCAPE LOT RESERVED FOR FUTURE GRANT TO THE HOMEOWNER'S ASSOCIATION BY SEPARATE INSTRUMENT AND IS NOT A SEPARATE BUILDING SITE.

LOTS B THROUGH D, INCLUSIVE, ARE PRIVATE DRIVEWAYS.

LOT E IS A PRIVATE STREET.

EASEMENT NOTES:

(A) INDICATES A PIPELINE EASEMENT FOR ACCESS, WATER AND SEWER PURPOSES DEDICATED TO SANTA MARGARITA WATER DISTRICT HEREON.

(B) INDICATES A PIPELINE EASEMENT FOR WATER LINE AND ACCESS PURPOSES DEDICATED HEREON TO SANTA MARGARITA WATER DISTRICT.

(C) INDICATES AN EASEMENT FOR INGRESS AND EGRESS OF EMERGENCY AND PUBLIC SERVICE VEHICLES DEDICATED HEREON TO SAID COUNTY OF ORANGE.

(D) INDICATES AN EASEMENT FOR PUBLIC UTILITY PURPOSES RESERVED HEREON FOR FUTURE GRANT.

SEE SHEET 2 FOR BASIS OF BEARINGS, DATUM STATEMENT, MONUMENT NOTES, AND INDEX AND BOUNDARY MAP.