

SHEET 1 OF 3 SHEETS

3.172 ACRES GROSS
(BEING FINAL UNIT OF
TENTATIVE TRACT NO. 15901)
LOTS: 22 NUMBERED

BLOCK MODULE
5157 15

TRACT NO. 15901

IN THE UNINCORPORATED TERRITORY OF THE COUNTY OF ORANGE, STATE OF CALIFORNIA

BEING A SUBDIVISION OF LOT 2 OF TRACT NO. 15813 AS SHOWN ON THE MAP FILED IN
BOOK 795, PAGES 1 THROUGH 16 OF MISCELLANEOUS MAPS, IN THE OFFICE OF THE
COUNTY RECORDER OF SAID ORANGE COUNTY.

JAMES R. CRAWFORD L.S. 4965



DATE OF SURVEY: JANUARY, 2000

ACCEPTED AND FILED AT THE
REQUEST OF
FIRST AMERICAN TITLE INSURANCE COMPANY
DATE JULY 6, 2000
TIME 10:08 A.M. FEE \$ 11.⁰⁰
INSTRUMENT # 20000352377
BOOK 803 PAGE 48-50 MM
GARY L. GRANVILLE
CLERK-RECORDER
BY DEPUTY

OWNERSHIP CERTIFICATE:

WE THE UNDERSIGNED, BEING ALL PARTIES HAVING ANY RECORD TITLE INTEREST IN THE LAND COVERED BY
THIS MAP, DO HEREBY CONSENT TO THE PREPARATION AND RECORDATION OF SAID MAP AS SHOWN WITHIN
THE DISTINCTIVE BORDER LINE. WE ALSO HEREBY DEDICATE TO THE PUBLIC FOR STREET PURPOSES:
RESTON WAY.

RESTON ASSOCIATES, L.L.C., A DELAWARE LIMITED LIABILITY COMPANY

BY: PH INSTITUTIONAL VENTURES, A CALIFORNIA CORPORATION,
ITS MANAGING MEMBER

PRINT NAME: THOMAS J. MITCHELL
PRINT TITLE: SENIOR VICE PRESIDENT

PRINT NAME: MICHAEL D. GRUBBS
PRINT TITLE: VICE PRESIDENT

DMB LADERA, LLC, A DELAWARE LIMITED LIABILITY COMPANY, BENEFICIARY UNDER A DEED OF
TRUST RECORDED FEBRUARY 23, 2000 AS INSTRUMENT NO. 20000095518 OF OFFICIAL RECORDS.

BY: RANCHO MISSION VIEJO, L.L.C., A DELAWARE LIMITED LIABILITY COMPANY
AS AGENT OR MANAGER

PRINT NAME: PAUL JOHNSON
PRINT TITLE: V.P.

NOTARY ACKNOWLEDGEMENT FOR RESTON ASSOCIATES, LLC:

STATE OF California }
COUNTY OF Orange } SS

ON April 25, 2000, BEFORE ME, SUSAN E. MENARD, A NOTARY PUBLIC IN AND FOR SAID
STATE PERSONALLY APPEARED Thomas J. Mitchell AND Michael D. Grubbs PERSONALLY KNOWN TO ME
(OR PROVED TO ME ON THE BASIS OF OF SATISFACTORY EVIDENCE) TO BE THE PERSONS WHOSE NAMES ARE
SUBSCRIBED TO THE WITHIN INSTRUMENT AND ACKNOWLEDGED TO ME THAT THEY EXECUTED THE SAME IN
THEIR AUTHORIZED CAPACITIES AND THAT BY THEIR SIGNATURES ON THE INSTRUMENT THE PERSONS, OR THE
ENTITY UPON BEHALF OF WHICH THE PERSONS ACTED EXECUTED THE INSTRUMENT.

WITNESS MY HAND:

NOTARY PUBLIC IN AND FOR SAID STATE
SUSAN E. MENARD
(NAME PRINTED)

MY PRINCIPAL PLACE OF BUSINESS IS IN ORANGE
Sept. 5, 2003
MY COMMISSION EXPIRES:

NOTARY ACKNOWLEDGEMENT FOR DMB LADERA, LLC:

STATE OF California }
COUNTY OF Orange } SS

ON April 25, 2000, BEFORE ME, Lupe Martinez, A NOTARY PUBLIC IN AND FOR
SAID STATE PERSONALLY APPEARED Paul Johnson PERSONALLY KNOWN TO ME
(OR PROVED TO ME ON THE BASIS OF OF SATISFACTORY EVIDENCE) TO BE THE PERSON WHOSE NAME IS
SUBSCRIBED TO THE WITHIN INSTRUMENT AND ACKNOWLEDGED TO ME THAT HE EXECUTED THE SAME IN
HIS AUTHORIZED CAPACITY AND THAT BY HIS SIGNATURE ON THE INSTRUMENT THE PERSON, OR THE
ENTITY UPON BEHALF OF WHICH THE PERSON ACTED EXECUTED THE INSTRUMENT.

WITNESS MY HAND:


NOTARY PUBLIC IN AND FOR SAID STATE
Lupe Martinez
(NAME PRINTED)

MY PRINCIPAL PLACE OF BUSINESS IS
IN Tustin, CA
MY COMMISSION EXPIRES: 8-13-2002

SURVEYOR'S STATEMENT:

I HEREBY STATE THAT THIS MAP CONSISTING OF THREE (3) SHEETS CORRECTLY REPRESENTS THE TRUE AND
COMPLETE SURVEY AS SHOWN MADE IN JANUARY, 2000; WAS MADE BY ME OR UNDER MY DIRECTION; THAT
THE MONUMENTS ARE OF THE CHARACTER AND OCCUPY OR WILL OCCUPY THE POSITIONS INDICATED BY SAID
MAP; AND THAT SAID MONUMENTS ARE OR WILL BE SUFFICIENT TO ENABLE THE SURVEY TO BE RETRACED.

JAMES R. CRAWFORD, L.S. 4965
MY LICENSE EXPIRES: DECEMBER 31, 2001

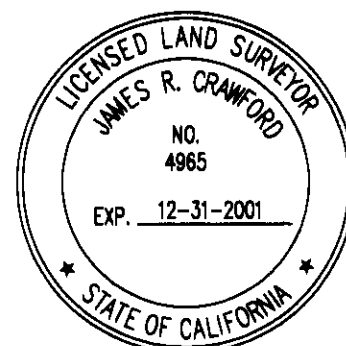

COUNTY SURVEYOR'S STATEMENT:

I HEREBY STATE THAT I HAVE EXAMINED THIS MAP AND FOUND IT TO BE SUBSTANTIALLY IN CONFORMANCE
WITH THE TENTATIVE MAP, IF REQUIRED, AS FILED WITH, AMENDED AND APPROVED BY THE ORANGE COUNTY
SUBDIVISION COMMITTEE; THAT ALL THE PROVISIONS OF THE SUBDIVISION MAP ACT AND COUNTY SUBDIVISION
REGULATIONS HAVE BEEN COMPLIED WITH, AND I AM SATISFIED SAID MAP IS TECHNICALLY CORRECT.

DATED THIS 15TH DAY OF JUNE, 2000.

JOHN CANAS, COUNTY SURVEYOR



CLERK OF THE BOARD OF SUPERVISORS' CERTIFICATE:

STATE OF CALIFORNIA }
COUNTY OF ORANGE } SS

I HEREBY CERTIFY THAT THIS MAP WAS PRESENTED FOR APPROVAL TO THE BOARD OF SUPERVISORS OF ORANGE
COUNTY AT A REGULAR MEETING THEREOF HELD ON THE 27 DAY OF June, 2000, AND
THAT THEREUPON SAID BOARD DID, BY AN ORDER DULY PASSED AND ENTERED, APPROVE SAID MAP AND DID
ACCEPT ON BEHALF OF THE PUBLIC, SUBJECT TO IMPROVEMENTS; THE DEDICATION FOR STREET PURPOSES OF:
RESTON WAY.

AND DID ALSO APPROVE SUBJECT MAP PURSUANT TO THE PROVISIONS OF SECTION 66436(a)(3) OF THE
SUBDIVISION MAP ACT.

DATED THIS 27 DAY OF June, 2000.

DARLENE J. BLOOM
CLERK OF THE BOARD OF SUPERVISORS



COUNTY TREASURER-TAX COLLECTOR'S CERTIFICATE:

STATE OF CALIFORNIA }
COUNTY OF ORANGE } SS

I HEREBY CERTIFY THAT ACCORDING TO THE RECORDS OF MY OFFICE THERE ARE NO LIENS AGAINST THE LAND
COVERED BY THIS MAP OR ANY PART THEREOF FOR UNPAID STATE, COUNTY, MUNICIPAL OR LOCAL TAXES OR
SPECIAL ASSESSMENTS COLLECTED AS TAXES, EXCEPT TAXES OR SPECIAL ASSESSMENTS COLLECTED AS
TAXES NOT YET PAYABLE.

I ALSO CERTIFY TO THE RECORDER OF ORANGE COUNTY THAT THE PROVISIONS OF THE SUBDIVISION MAP ACT
HAVE BEEN COMPLIED WITH REGARDING DEPOSITS TO SECURE THE PAYMENT OF TAXES OR SPECIAL ASSESSMENTS
COLLECTED AS TAXES ON THE LAND COVERED BY THIS MAP.

DATED THIS 31ST DAY OF May, 2000.

JOHN M. W. MOORLACH
COUNTY TREASURER-TAX COLLECTOR

BY
DEPUTY TREASURER-TAX COLLECTOR

3.172 ACRES GROSS
(BEING FINAL UNIT OF
TENTATIVE TRACT NO. 15901)
LOTS: 22 NUMBERED

TRACT NO. 15901

IN THE UNINCORPORATED TERRITORY OF THE COUNTY OF ORANGE, STATE OF CALIFORNIA

JAMES R. CRAWFORD L.S. 4965



DATE OF SURVEY: JANUARY, 2000

SIGNATURE OMISSION NOTE:

PURSUANT TO THE PROVISIONS OF SECTION 66436(a)(3)(C) OF THE SUBDIVISION MAP ACT THE FOLLOWING SIGNATURES HAVE BEEN OMITTED:

1. LADERA DEVELOPMENT COMPANY, L.L.C., HOLDER OF OIL, GAS AND MINERAL RIGHTS RECORDED AS INSTRUMENT NO. 19960624029 OF OFFICIAL RECORDS.
2. DMB LADERA, LLC, HOLDER OF EASEMENTS FOR CONSTRUCTION FACILITIES, TELECOMMUNICATIONS, PUBLIC UTILITIES, SURFACE RUNOFF AND ACCESS PURPOSES RECORDED AS INSTRUMENT NO. 20000095516 OF OFFICIAL RECORDS. (SAID EASEMENTS ARE BLANKET IN NATURE.)

GPS POINT LOCATIONS:

GPS # 1417 FOUND 2 1/2" IRON PIPE WITH 2" DIAMETER O.C.S. BRASS
N2141450.558 CAP STAMPED "GPS 1417 9-95" PER TRACT NO. 15615, M.M. 777/14-31
E6141583.535 AND RECORDS ON FILE IN THE OFFICE OF THE ORANGE COUNTY SURVEYOR.

GPS # 1424 FOUND 2 1/2" IRON PIPE WITH 2" DIAMETER O.C.S. BRASS
N2152873.842 CAP STAMPED "GPS 1424 9-95" PER RECORDS ON FILE IN THE OFFICE
E6141904.527 OF THE ORANGE COUNTY SURVEYOR.

DATUM STATEMENT:

COORDINATES SHOWN ARE BASED UPON THE CALIFORNIA COORDINATE SYSTEM (CCS83), ZONE VI 1983 NAD (1991.35 EPOCH O.C.S. GPS ADJUSTMENT). ALL DISTANCES SHOWN ARE GROUND UNLESS OTHERWISE NOTED. TO OBTAIN GRID DISTANCE, MULTIPLY THE GROUND DISTANCE BY 0.99993389.

BASIS OF BEARINGS NOTE:

THE BEARINGS SHOWN HEREON ARE BASED ON THE BEARING BETWEEN O.C.S. HORIZONTAL CONTROL STATION GPS NO. 1417 AND STATION GPS NO. 1424 BEING NORTH 01°36'34" EAST PER RECORDS ON FILE IN THE OFFICE OF THE ORANGE COUNTY SURVEYOR.

NOTES:

1. ALL DETACHED, SINGLE-FAMILY STRUCTURES EXCEEDING 5500 SQUARE FEET, AND THOSE SINGLE-FAMILY STRUCTURES ON ~~LOTS 9-12 AND 18-21~~ SHALL BE PROTECTED BY AN AUTOMATIC SPRINKLER SYSTEM.
2. THIS PROPERTY IS WITHIN A "SPECIAL FIRE PROTECTION AREA" AND MUST MEET ALL REQUIREMENTS FOR DEVELOPMENT WITHIN THE AREA OR FILE FOR AN EXCLUSION WITH THE FIRE CHIEF. THE APPLICANT HAS APPLIED FOR AND RECEIVED A "TOTAL EXCLUSION" FROM THIS ORANGE COUNTY "SPECIAL FIRE PROTECTION AREA" AND NO LOTS OR BUILDINGS ARE SUBJECT TO THE CONSTRUCTION FEATURES OF ORANGE COUNTY ORDINANCE 3960. THE EXCLUSION HAS BEEN GRANTED BASED ON THE FINDINGS FOUND IN A LETTER DATED FEBRUARY 9, 2000 SIGNED BY LAURA BLAUL OF THE ORANGE COUNTY FIRE AUTHORITY AND THE APPLICANT WILL KEEP A COPY OF SAID LETTER AVAILABLE IN THEIR RECORDS.
3. THIS PROPERTY IS IN A "HIGH FIRE HAZARD AREA" DUE TO WILDLAND EXPOSURE BASED ON STATE SRA MAPS.

MONUMENT NOTES

1. ALL MONUMENTS SHOWN SET WILL BE SET WITHIN 90 DAYS AFTER THE ACCEPTANCE OF IMPROVEMENTS, EXCEPT AS NOTED.
2. SET SPIKE W/ BRASS WASHER STAMPED "L.S. 4965" IN ASPHALT PAVEMENT HAVING A THICKNESS OF 2" OR MORE OR A LEAD, TACK AND TAG "L.S. 4965" IN CONCRETE, AT ALL CENTERLINE POINTS OF CONTROL, UNLESS OTHERWISE NOTED.
3. TIES TO CENTERLINE MONUMENTS WILL BE MADE AND A COPY OF SAID TIES WILL BE FURNISHED TO THE ORANGE COUNTY SURVEYOR'S OFFICE.
4. SET 1" IRON PIPE TAGGED "L.S. 4965" AT ALL LOT CORNERS EXCEPT LOT CORNERS THAT ABUT A STREET WHICH WILL BE MARKED ON A 8.75' OFFSET OUTSIDE THE TRUE LOT CORNER IN CONCRETE BY A LEAD, TACK AND TAG "L.S. 4965" ON SIDELINES PRODUCED, EXCEPT AS NOTED. (NO MONUMENTS WILL BE SET FOR ANGLE POINTS, CORNER CUTOFFS, B.C.'S, E.C.'S, P.C.C.'S OR P.R.C.'S THAT ABUT A STREET WHICH ARE NOT LOT CORNER MARKING SIDELINES, UNLESS OTHERWISE NOTED).
5. SET 2" IRON PIPE TAGGED "L.S. 4965" OR LEAD, TACK AND TAG "L.S. 4965" IN CONCRETE OR A SPIKE W/ BRASS WASHER STAMPED "L.S. 4965" IN ASPHALT PAVEMENT HAVING A THICKNESS OF 2" OR MORE AT ALL TRACT BOUNDARY CORNERS. (NO MONUMENTS WILL BE SET FOR ANGLE POINTS, CORNER CUTOFFS, B.C.'S, E.C.'S P.C.C.'S OR P.R.C.'S THAT ABUT A STREET WHICH ARE NOT BOUNDARY CORNERS MARKING SIDELINES, UNLESS OTHERWISE NOTED.)
6. ■ INDICATES SET MONUMENTS AS NOTED.

1

 SET LEAD, TACK AND TAG "L.S. 4965" IN CONCRETE ON OFFSET AS SHOWN OUTSIDE TRUE LOT CORNER ON SIDELINE PRODUCED.

2

 SET 2" IRON PIPE TAGGED "L.S.4965" PRIOR TO RECORDATION.
7. ● DENOTES FOUND OR TO BE SET MONUMENTS AS NOTED AND REFERENCED BELOW:

3

 INDICATES 2" IRON PIPE TAGGED "L.S. 5557" OR SPIKE AND WASHER STAMPED "L.S. 5557" OR LEAD, TACK AND TAG "L.S. 5557" TO BE SET PER TRACT NO. 15813, M.M. 795/1-16.

4


 INDICATES 1" IRON PIPE TAGGED "L.S. 5557" OR SPIKE AND WASHER STAMPED "L.S. 5557" OR LEAD, TACK AND TAG "L.S. 5557" TO BE SET PER TRACT NO. 15813, M.M. 795/1-16.

5

 INDICATES 1" IRON PIPE TAGGED "L.S. 5557" OR SPIKE AND WASHER STAMPED "L.S. 5557" OR LEAD, TACK AND TAG "L.S. 5557" TO BE SET PER TRACT NO. 15884, M.M. 794/33-44.

6

 INDICATES SPIKE AND WASHER STAMPED "L.S. 4965" IN ASPHALT OR LEAD, TACK AND TAG "L.S. 4965" IN CONCRETE TO BE SET PER TRACT NO. 15902, M.M. ~~803/28-30~~.
8. ▲ INDICATES FOUND ORANGE COUNTY SURVEYOR'S G.P.S. MONUMENT AS NOTED.

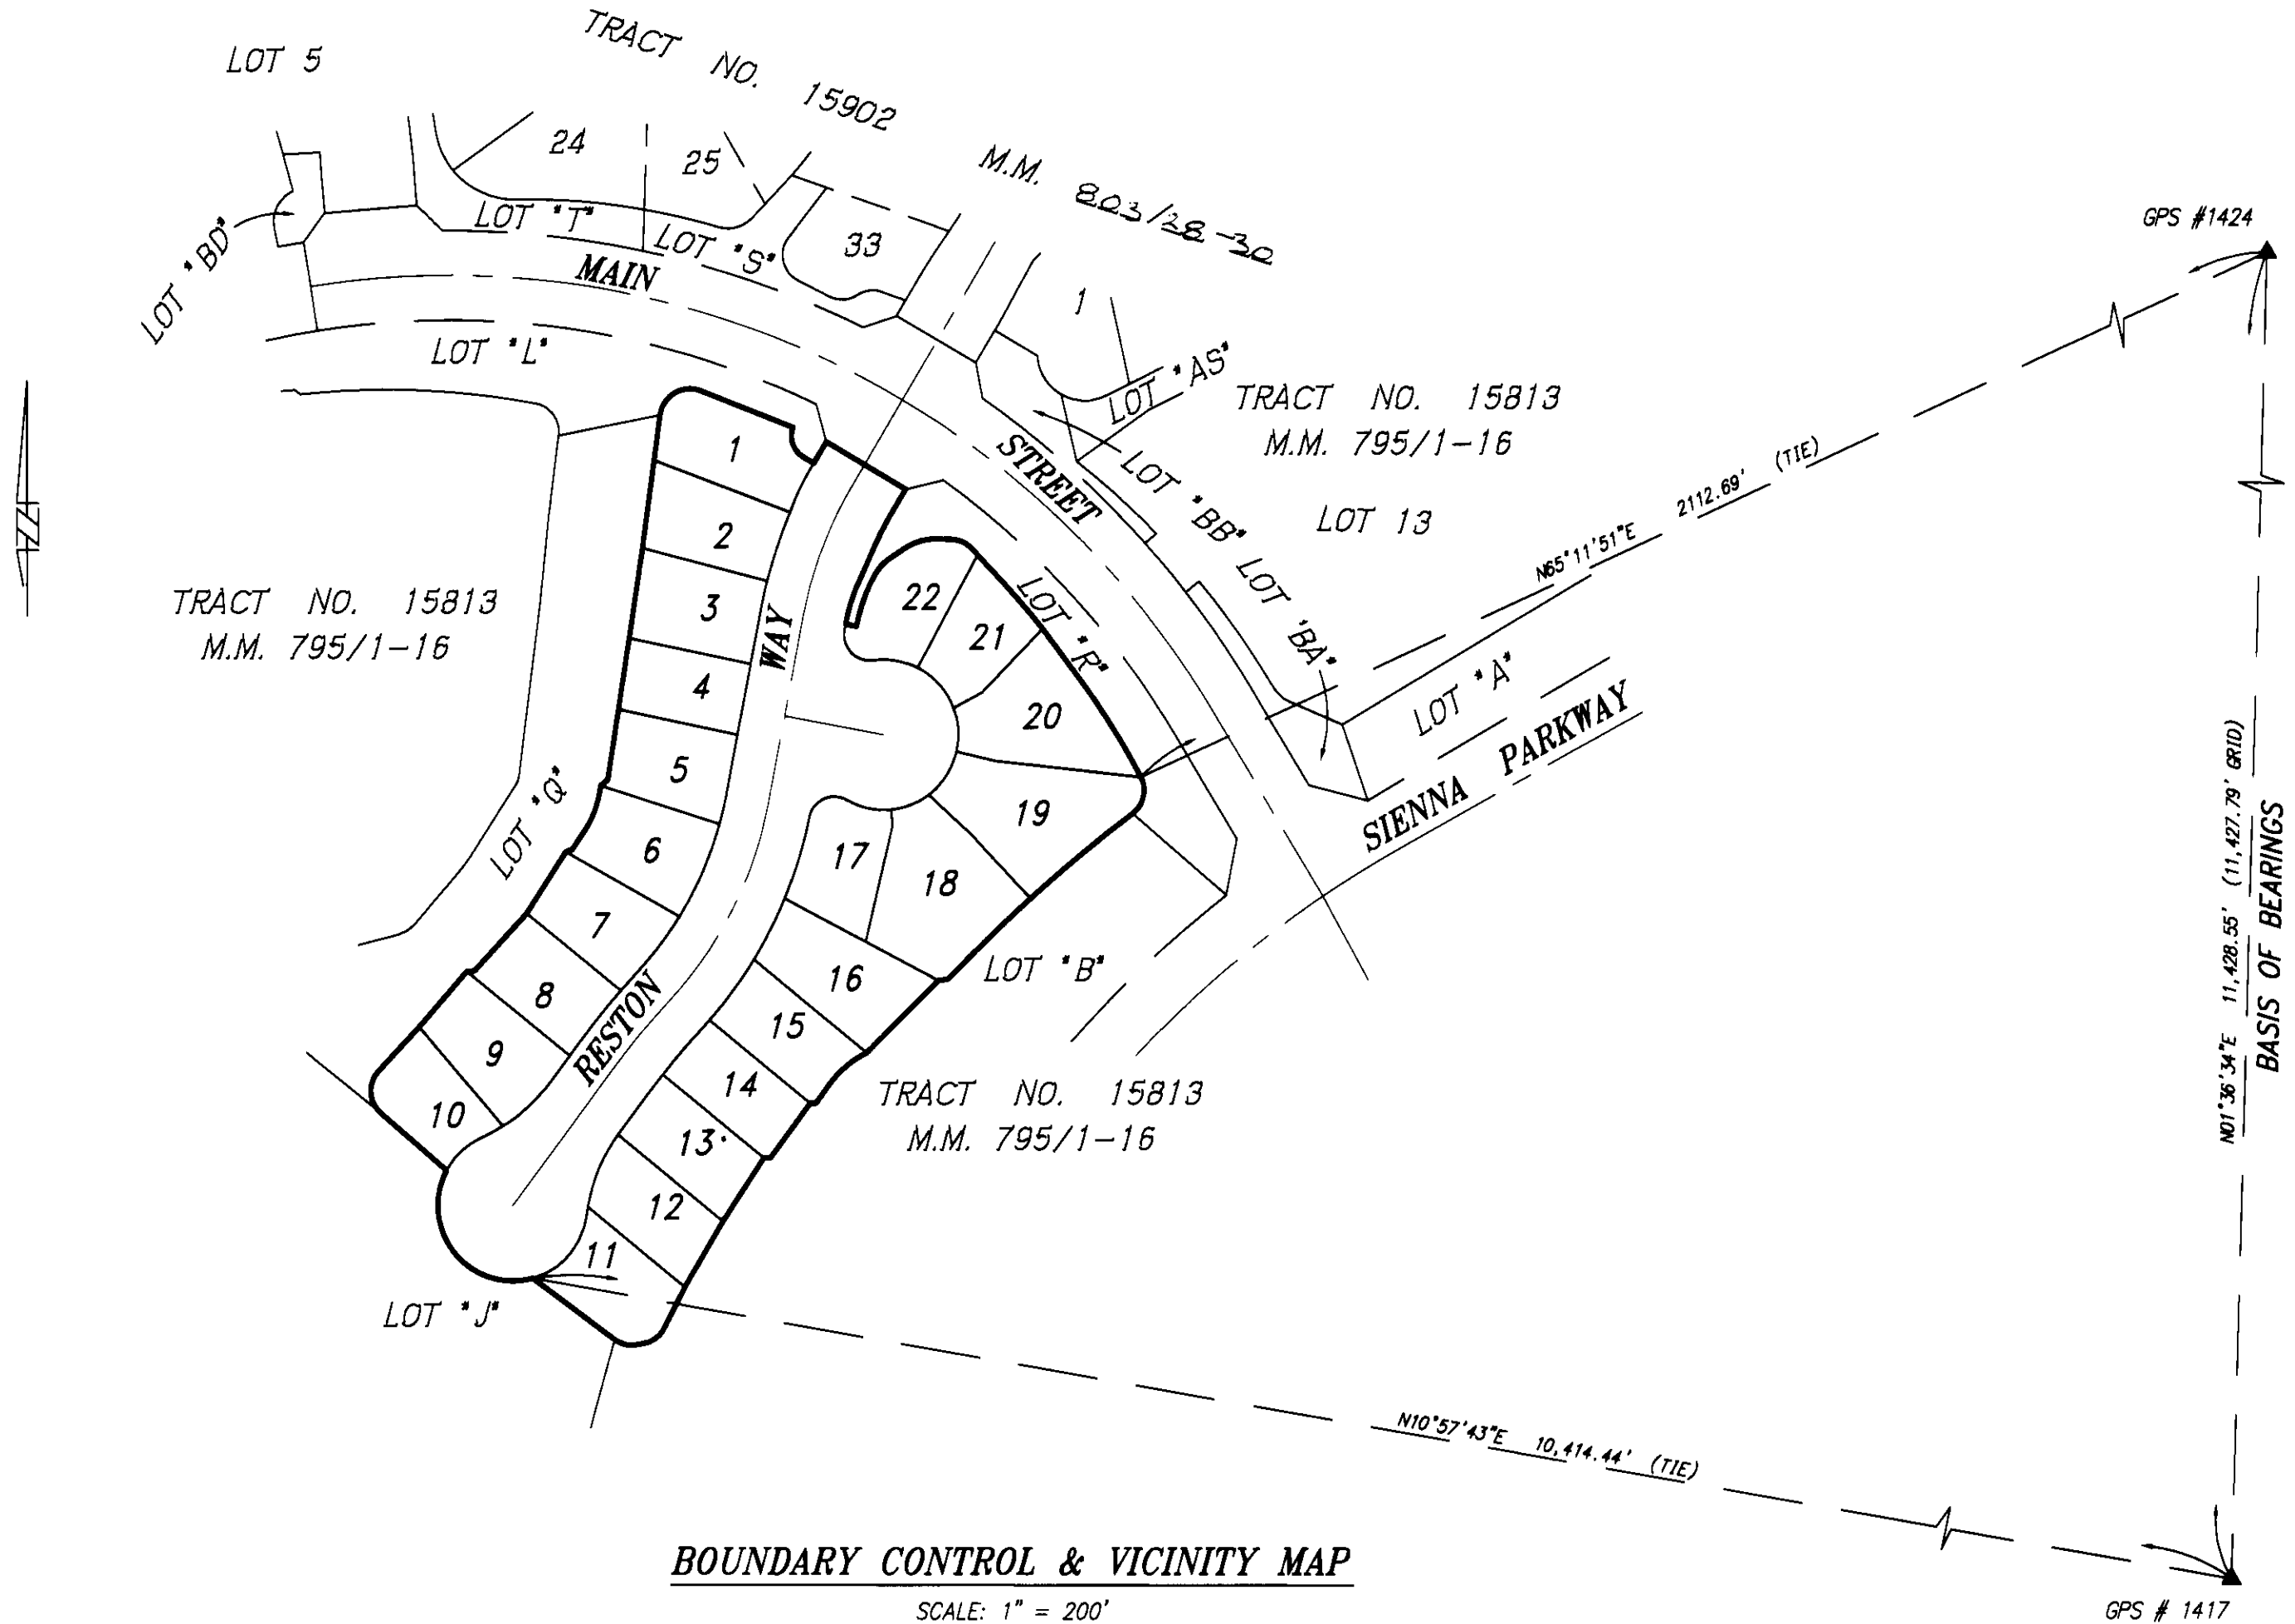

SHEET 3 OF 3 SHEETS
AREA: 3.172 ACRES GROSS
(BEING FINAL UNIT OF
TENTATIVE TRACT NO. 15901)
NUMBERED LOTS: 22

TRACT NO. 15901


IN THE UNINCORPORATED TERRITORY OF THE
COUNTY OF ORANGE, STATE OF CALIFORNIA

SCALE: 1" = 40'

JAMES R. CRAWFORD, L.S. 4965



DATE OF SURVEY: JANUARY, 2000

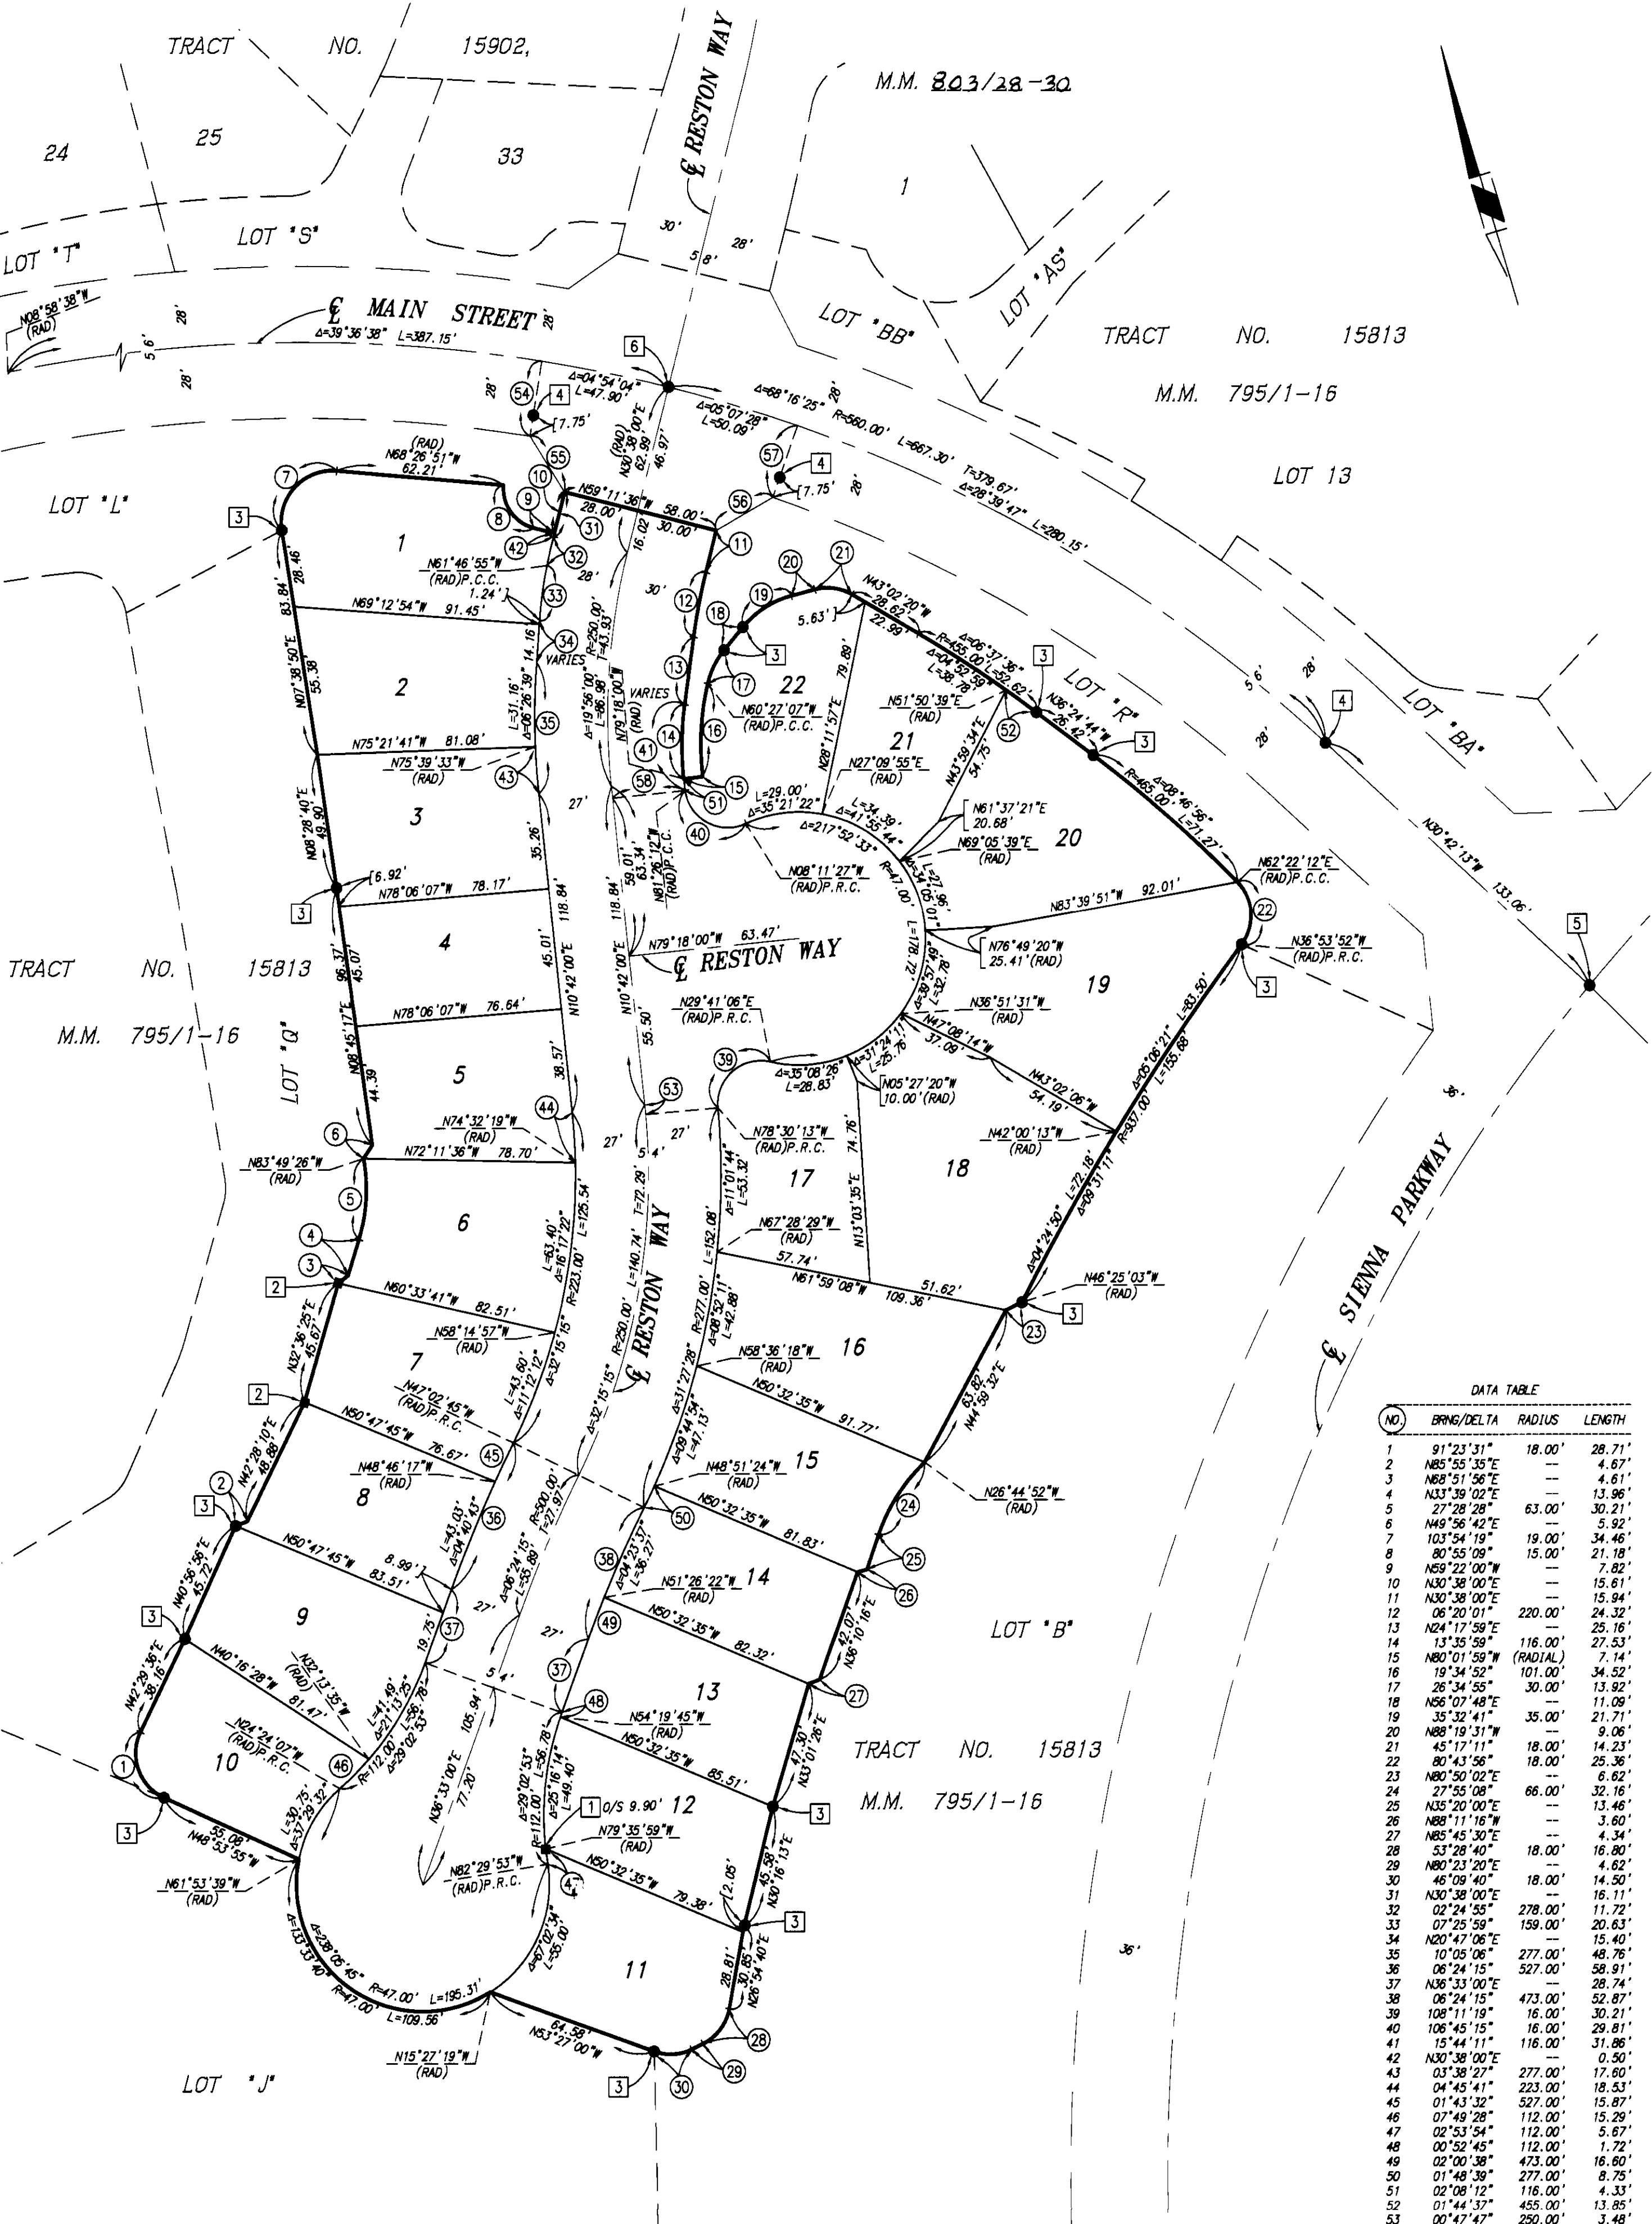

DATA TABLE			
NO.	Bearing/Delta	RADIUS	LENGTH
1	91°23'31"	18.00'	28.71'
2	N85°55'35"E	---	4.67'
3	N88°51'56"E	---	4.61'
4	N33°39'02"E	---	13.96'
5	27°28'28"	63.00'	30.21'
6	N49°56'42"E	---	5.92'
7	103°54'19"	19.00'	34.46'
8	80°55'09"	15.00'	21.18'
9	N59°22'00"W	---	7.82'
10	N30°38'00"E	---	15.61'
11	N30°38'00"E	---	15.94'
12	06°20'01"	220.00'	24.32'
13	N24°17'59"E	---	25.16'
14	13°35'59"	116.00'	27.53'
15	N80°01'59"W	(RADIAL)	7.14'
16	19°34'52"	101.00'	34.52'
17	26°34'55"	30.00'	13.92'
18	N56°07'48"E	---	11.09'
19	35°32'41"	35.00'	21.71'
20	N88°19'31"W	---	9.06'
21	45°17'11"	18.00'	14.23'
22	80°43'56"	18.00'	25.36'
23	N80°50'02"E	---	6.62'
24	27°55'08"	66.00'	32.16'
25	N35°20'00"E	---	13.46'
26	N88°11'16"W	---	3.60'
27	N85°45'30"E	---	4.34'
28	53°28'40"	18.00'	16.80'
29	N80°23'20"E	---	4.62'
30	46°09'40"	18.00'	14.50'
31	N30°38'00"E	---	16.11'
32	02°24'55"	278.00'	11.72'
33	07°25'59"	159.00'	20.63'
34	N20°47'06"E	---	15.40'
35	10°05'06"	277.00'	48.76'
36	06°24'15"	527.00'	58.91'
37	N36°33'00"E	---	28.74'
38	06°24'15"	473.00'	52.87'
39	108°11'19"	16.00'	30.21'
40	106°45'15"	16.00'	29.81'
41	15°44'11"	116.00'	31.86'
42	N30°38'00"E	---	0.50'
43	03°38'27"	277.00'	17.60'
44	04°45'41"	223.00'	18.53'
45	01°43'32"	527.00'	15.87'
46	07°49'28"	112.00'	15.29'
47	02°53'54"	112.00'	5.67'
48	00°52'45"	112.00'	1.72'
49	02°00'38"	473.00'	16.60'
50	01°48'39"	277.00'	8.75'
51	02°08'12"	116.00'	4.33'
52	01°44'37"	455.00'	13.85'
53	00°47'47"	250.00'	3.48'
54	N25°43'56"E	(RADIAL)	28.00'
55	N15°13'26"W	---	24.32'
56	N76°36'31"E	---	24.36'
57	N35°45'28"E	(RADIAL)	28.00'
58	N79°18'00"W	---	27.08'

SEE SHEET 2 FOR BASIS OF BEARINGS, GPS POINT LOCATIONS, DATUM STATEMENT,
BOUNDARY CONTROL AND INDEX MAP, MONUMENT NOTES, EASEMENT NOTES AND OTHER NOTES.