

SHEET 1 OF 6 SHEETS
6.264 ACRES
36 LOTS AND LOTS
"A", "B", "C" AND "D"
(ALL OF VESTING TENTATIVE
TRACT NO. 15903)
BLOCK 5157 MODULE 76

TRACT NO. 15903

IN THE UNINCORPORATED TERRITORY OF THE
COUNTY OF ORANGE, STATE OF CALIFORNIA

BEING A SUBDIVISION OF LOT 5 OF TRACT NO. 15813, PER MAP FILED
IN BOOK 795, PAGES 1 THROUGH 16, INCLUSIVE, OF MISCELLANEOUS
MAPS, RECORDS OF ORANGE COUNTY.

WAGNER HALLADAY, INC.

ROBERT N. MIM MACK L.S. 5314 DATE OF SURVEY: NOVEMBER, 1999

ACCEPTED AND FILED AT THE
REQUEST OF

FIRST AMERICAN TITLE Co.

DATE Jan. 16, 2000

TIME 10:27am FEE \$ 17.00

INSTRUMENT # 20000318110

BOOK 803 PAGE 22-27

GARY L. GRANVILLE
COUNTY CLERK-RECORDER

BY Matthew Kelly
DEPUTY

OWNERSHIP CERTIFICATE

WE, THE UNDERSIGNED, BEING ALL PARTIES HAVING ANY RECORD TITLE INTEREST IN THE LAND COVERED BY THIS MAP, DO HEREBY CONSENT TO THE PREPARATION AND RECORDATION OF SAID MAP, AS SHOWN WITHIN THE DISTINCTIVE BORDER LINE. WE HEREBY DEDICATE TO THE PUBLIC FOR STREET PURPOSES: COTTAGE HILL ROAD AND CHIMNEY LANE.

WE ALSO HEREBY DEDICATE TO THE COUNTY OF ORANGE:

(1) THE EASEMENT FOR STORM DRAIN PURPOSES AS SHOWN ON THIS MAP.

~~(2) THE EASEMENT FOR FIRE DEPARTMENT ACCESS PURPOSES AS SHOWN ON THIS MAP.~~

WE ALSO HEREBY DEDICATE TO THE SANTA MARGARITA WATER DISTRICT THE EASEMENTS FOR SEWER AND WATER PURPOSES AS SHOWN ON THIS MAP, WHICH EASEMENTS SHALL BE SUBJECT TO THE SAME TERMS AND CONDITIONS AS ARE SHOWN IN THAT CERTAIN EASEMENT RECORDED OCTOBER 6, 1980, IN BOOK 13776, PAGE 341, OF OFFICIAL RECORDS OF ORANGE COUNTY. THE SANTA MARGARITA WATER DISTRICT SHALL RESTORE OTHER IMPROVEMENTS OR FACILITIES LOCATED WITHIN THE EASEMENT, IF IT HAS CONSENTED TO THE LOCATION OF SUCH IMPROVEMENTS OR FACILITIES TO THE EXTENT THAT THE EXERCISE OF ITS RIGHTS IN CONNECTION WITH THE EASEMENT IMPACTS OTHER IMPROVEMENTS OR FACILITIES LOCATED WITHIN THE EASEMENT, HOWEVER, IN NO EVENT SHALL SANTA MARGARITA WATER DISTRICT BE RESPONSIBLE FOR THE COST OF RELOCATING ITS FACILITIES IN THE EVENT OF CONFLICTS WITH SUCH OTHER IMPROVEMENTS OR FACILITIES.

WL HOMES LLC, A DELAWARE LIMITED LIABILITY COMPANY
DBA JOHN LAING HOMES

BY: L. J. Edgcomb
L. J. Edgcomb DIVISION PRES.
PRINT NAME PRINT TITLE

BY: Tim McSunas
TIM MCSUNAS DIRECTOR
PRINT NAME PRINT TITLE

RESIDENTIAL FUNDING CORPORATION, A DELAWARE CORPORATION, AS BENEFICIARY UNDER DEED OF TRUST RECORDED February 14, 2000, AS INSTRUMENT NO. 200000079644, OFFICIAL RECORDS OF ORANGE COUNTY.

BY: Michael F. Ripling
MICHAEL F. RIPLING DIRECTOR
PRINT NAME PRINT TITLE

DMB LADERA, L.L.C., A DELAWARE LIMITED LIABILITY COMPANY, BENEFICIARY UNDER A DEED OF TRUST RECORDED January 28, 2000, AS INSTRUMENT NO. 200000051683 OF OFFICIAL RECORDS OF ORANGE COUNTY.

BY: RANCHO MISSION VIEJO, L.L.C., A DELAWARE LIMITED LIABILITY COMPANY,
AS AGENT AND OR MANAGER

BY: Paul Johnson
PAUL JOHNSON VICE-PRESIDENT
PRINT NAME PRINT TITLE

NOTARY ACKNOWLEDGMENT

STATE OF CALIFORNIA) SS
COUNTY OF ORANGE)

ON THIS 8th DAY OF MARCH, 2000, BEFORE ME FEDDY M. BLOCK
NOTARY Public, PERSONALLY APPEARED L. J. Edgcomb AND
TIM MCSUNAS PERSONALLY KNOWN TO ME OR PROVED TO ME ON THE BASIS
OF SATISFACTORY EVIDENCE TO BE THE PERSONS WHOSE NAMES ARE SUBSCRIBED TO THE WITHIN INSTRUMENT
AND ACKNOWLEDGED TO ME THAT THEY EXECUTED THE SAME IN THEIR AUTHORIZED CAPACITIES, AND THAT BY
THEIR SIGNATURES ON THE INSTRUMENT THE PERSONS, OR THE ENTITY UPON BEHALF OF WHICH THE PERSONS
ACTED, EXECUTED THE INSTRUMENT.

WITNESS MY HAND:

MY PRINCIPAL PLACE OF BUSINESS IS IN
ORANGE COUNTY.

MY COMMISSION EXPIRES: 2/10/2004

Feddy M. Block
NOTARY PUBLIC IN AND FOR SAID STATE
FEDDY M. BLOCK
(PRINT NAME)

SURVEYOR'S STATEMENT

I HEREBY STATE THAT THIS MAP CONSISTING OF 6 SHEETS, CORRECTLY REPRESENTS A TRUE AND COMPLETE SURVEY AS SHOWN MADE IN NOVEMBER, 1999; WAS MADE BY ME OR UNDER MY DIRECTION; THAT THE MONUMENTS ARE OF THE CHARACTER AND OCCUPY (OR WILL OCCUPY) THE POSITIONS INDICATED BY SAID MAP; AND THAT SAID MONUMENTS ARE (OR WILL BE) SUFFICIENT TO ENABLE THE SURVEY TO BE RETRACED.




Robert N. Mim Mack
ROBERT N. MIM MACK L.S. 5314
MY LICENSE EXPIRES: 12/31/03

COUNTY SURVEYOR'S STATEMENT

I HEREBY STATE THAT I HAVE EXAMINED THIS MAP AND HAVE FOUND IT TO BE SUBSTANTIALLY IN CONFORMANCE WITH THE TENTATIVE MAP AS FILED WITH, AMENDED AND APPROVED BY THE ORANGE COUNTY SUBDIVISION COMMITTEE; THAT ALL THE PROVISIONS OF THE SUBDIVISION MAP ACT AND COUNTY SUBDIVISION REGULATIONS HAVE BEEN COMPLIED WITH AND I AM SATISFIED THAT SAID MAP IS TECHNICALLY CORRECT.

DATED THIS 26th DAY OF May, 2000.

Robert Jelinek
JOHN CANAS, COUNTY SURVEYOR
Robert Jelinek, Deputy County Surveyor

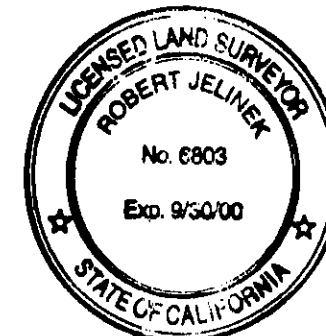

COUNTY TREASURER-TAX COLLECTOR'S CERTIFICATE

STATE OF CALIFORNIA) SS
COUNTY OF ORANGE)

I HEREBY CERTIFY THAT ACCORDING TO THE RECORDS OF MY OFFICE THERE ARE NO LIENS AGAINST THE LAND COVERED BY THIS MAP OR ANY PART THEREOF FOR UNPAID STATE, COUNTY, MUNICIPAL OR LOCAL TAXES OR SPECIAL ASSESSMENTS COLLECTED AS TAXES, EXCEPT TAXES OR SPECIAL ASSESSMENTS COLLECTED AS TAXES NOT YET PAYABLE.

AND DO ALSO HEREBY CERTIFY TO THE RECORDER OF ORANGE COUNTY THAT THE PROVISIONS OF THE SUBDIVISION MAP ACT HAVE BEEN COMPLIED WITH REGARDING DEPOSITS TO SECURE THE PAYMENT OF TAXES OR SPECIAL ASSESSMENTS COLLECTED AS TAXES ON THE LAND COVERED BY THIS MAP.

DATED THIS 9th DAY OF May, 2000.

JOHN M. W. MOORLACH
COUNTY TREASURER-TAX COLLECTOR

BY: Mia Jorgensen
DEPUTY TREASURER-TAX COLLECTOR

CLERK OF THE BOARD OF SUPERVISORS' CERTIFICATE

STATE OF CALIFORNIA) SS
COUNTY OF ORANGE)

I HEREBY CERTIFY THAT THIS MAP WAS PRESENTED FOR APPROVAL TO THE BOARD OF SUPERVISORS OF ORANGE COUNTY AT A REGULAR MEETING THEREOF HELD ON THE 13th DAY OF June, 2000, AND THAT THEREUPON SAID BOARD DID, BY AN ORDER DULY PASSED AND ENTERED, APPROVE SAID MAP, AND DID ACCEPT ON BEHALF OF THE PUBLIC, SUBJECT TO IMPROVEMENTS: THE DEDICATION FOR STREET PURPOSES OF: COTTAGE HILL ROAD AND CHIMNEY LANE.

AND DID ALSO ACCEPT ON BEHALF OF THE COUNTY OF ORANGE:

(1) THE EASEMENT FOR STORM DRAIN PURPOSES AS DEDICATED HEREON.

~~(2) THE EASEMENT FOR FIRE DEPARTMENT ACCESS PURPOSES AS DEDICATED HEREON.~~

AND DID ALSO APPROVE SUBJECT MAP PURSUANT TO THE PROVISIONS OF SECTION 66436 (a)(3)(A) OF THE SUBDIVISION MAP ACT.

DATED THIS 13th DAY OF June, 2000.

Darlene J. Bloom
DARLENE J. BLOOM
CLERK OF THE BOARD OF SUPERVISORS
OF ORANGE COUNTY, CALIFORNIA



SEE SHEET 2 FOR ADDITIONAL NOTARY ACKNOWLEDGMENTS, SIGNATURE OMISSIONS, ADDITIONAL DECLARATIONS AND SANTA MARGARITA WATER DISTRICT ACCEPTANCE CERTIFICATE AND NOTARY ACKNOWLEDGMENT.

SHEET 2 OF 6 SHEETS
6.264 ACRES
36 LOTS AND LOTS
"A", "B", "C" AND "D"
(ALL OF VESTING TENTATIVE
TRACT NO. 15903)

TRACT NO. 15903

IN THE UNINCORPORATED TERRITORY OF THE
COUNTY OF ORANGE, STATE OF CALIFORNIA

WAGNER HALLADAY, INC.

ROBERT N. MIM MACK L.S. 5314 DATE OF SURVEY: NOVEMBER, 1999

SIGNATURE OMISSIONS

PURSUANT TO SECTION 66436 (a)(3) OF THE SUBDIVISION MAP ACT, THE SIGNATURES OF THE FOLLOWING HAVE BEEN OMITTED:

1. LADERA DEVELOPMENT COMPANY, L.L.C., HOLDER OF OIL, GAS AND MINERAL RIGHTS PER DOCUMENT RECORDED AS INSTRUMENT NO. 19960624029 OF OFFICIAL RECORDS.
2. DMB LADERA, L.L.C., HOLDER OF EASEMENTS PER DOCUMENT RECORDED AS INSTRUMENT NO. 20000051621 OF OFFICIAL RECORDS.

FIRE HAZARD NOTIFICATION NOTE

THIS PROJECT IS LOCATED IN STATE RESPONSIBILITY AREA BASED ON MAPPING BY THE STATE OF CALIFORNIA, HOWEVER THIS PROJECT DOES NOT HAVE ANY EXPOSURE TO WILD LAND AREAS BASED UPON OC FIRE AUTHORITY LETTER DATED FEBRUARY 9, 2000 PER ORDINANCE 3959-3960 OF THE COUNTY OF ORANGE.

FIRE PROTECTION AREA NOTE

A TOTAL EXCLUSION FROM THE SPECIAL FIRE PROTECTION AREA HAS BEEN GRANTED BY THE OC FIRE AUTHORITY PER LETTER DATED FEBRUARY 9, 2000 FROM THE OC FIRE AUTHORITY AND THEREFORE, THIS PROJECT IS NO LONGER IN A SPECIAL FIRE PROTECTION AREA PER ORDINANCE 3959-3960 OF THE COUNTY OF ORANGE.

NOTE

PROPERTY MAY BE SUBJECT TO IMPACTS FROM THE PROPOSED FOOTHILL/EASTERN TRANSPORTATION CORRIDORS.

FOOTHILL CIRCULATION PHASING PLAN NOTE

BUILDING PERMIT ISSUANCE SHALL BE PHASED IN ACCORDANCE WITH THE FOOTHILL CIRCULATION PHASING PLAN (FCPP) DEVELOPMENT PHASING PLAN, AND SHALL ALSO BE SUBJECT TO ANY OTHER BOARD OF SUPERVISORS APPROVED GROWTH MANAGEMENT PHASING PLAN PERTAINING TO THE TIMELY PROVISION OF PUBLIC SERVICES AND FACILITIES.

EASEMENT NOTES

- Ⓐ INDICATES EASEMENT FOR STORM DRAIN PURPOSES DEDICATED TO THE COUNTY OF ORANGE.
Ⓑ INDICATES EASEMENT FOR SEWER AND WATER PURPOSES DEDICATED TO THE SANTA MARGARITA WATER DISTRICT.
Ⓒ INDICATES EASEMENT TO BE RESERVED FOR DRAINAGE PURPOSES.

AUTOMATIC FIRE SPRINKLER NOTE

ALL SINGLE-FAMILY STRUCTURES EXCEEDING 5,500 SQUARE FEET AND ALL STRUCTURES EXCEEDING FIRE DEPARTMENT ACCESS REQUIREMENTS SHALL BE PROTECTED BY AN AUTOMATIC FIRE SPRINKLER SYSTEM.

SANTA MARGARITA WATER DISTRICT CERTIFICATE OF ACCEPTANCE

THE UNDERSIGNED, BEING THE DULY APPOINTED AGENT OF THE SANTA MARGARITA WATER DISTRICT, A PUBLIC CORPORATION IN ORANGE COUNTY, CALIFORNIA, PURSUANT TO ITS RESOLUTION NO. 88-10-2, DOES HEREBY ACCEPT ON BEHALF OF SAID DISTRICT, THE EASEMENTS FOR WATER AND SEWER PURPOSES, AS DEDICATED AND AS SHOWN ON THIS TRACT MAP, AND DOES HEREBY ACCEPT ON BEHALF OF SAID DISTRICT ALL WATER AND WATER RIGHTS, AS DEDICATED ON THIS TRACT MAP, BY AND BETWEEN THE SANTA MARGARITA WATER DISTRICT AND WL HOMES, LLC, AND DOES HEREBY CERTIFY THAT THE GRANTEE CONSENTS TO THE RECORDATION OF SAID TRACT.

BY Daniel R. Ferons
DANIEL R. FERONS - CHIEF ENGINEER
SANTA MARGARITA WATER DISTRICT

NOTARY ACKNOWLEDGMENT

SANTA MARGARITA WATER DISTRICT

STATE OF CALIFORNIA)
COUNTY OF ORANGE) SS

ON THIS 3rd DAY OF May, 2000, BEFORE ME ANDREA M. EVANS
NOTARY PUBLIC, PERSONALLY APPEARED DANIEL R. FERONS, PERSONALLY KNOWN TO ME OR PROVED TO ME ON THE BASIS OF SATISFACTORY EVIDENCE TO BE THE PERSON WHOSE NAME IS SUBSCRIBED TO THE WITHIN INSTRUMENT AND ACKNOWLEDGED TO ME THAT HE EXECUTED THE SAME IN HIS AUTHORIZED CAPACITY, AND THAT BY HIS SIGNATURE ON THE INSTRUMENT THE PERSON, OR THE ENTITY UPON BEHALF OF WHICH THE PERSON ACTED, EXECUTED THE INSTRUMENT.

WITNESS MY HAND:

Andrea M. Evans
NOTARY PUBLIC IN AND FOR SAID STATE
ANDREA M. EVANS
(PRINT NAME)

MY PRINCIPAL PLACE OF BUSINESS IS IN
ORANGE COUNTY

MY COMMISSION EXPIRES: 4-8-2004

NOTARY ACKNOWLEDGMENT

STATE OF CALIFORNIA)
COUNTY OF Los Angeles) SS

ON THIS 15 DAY OF March, 2000, BEFORE ME Sonia C. Garcia
NOTARY PUBLIC, PERSONALLY APPEARED Michael F. Ripling AND
OF SATISFACTORY EVIDENCE TO BE THE PERSONS WHOSE NAMES ARE SUBSCRIBED TO THE WITHIN INSTRUMENT AND ACKNOWLEDGED TO ME THAT THEY EXECUTED THE SAME IN THEIR AUTHORIZED CAPACITIES, AND THAT BY THEIR SIGNATURES ON THE INSTRUMENT THE PERSONS, OR THE ENTITY UPON BEHALF OF WHICH THE PERSONS ACTED, EXECUTED THE INSTRUMENT.

WITNESS MY HAND:

MY PRINCIPAL PLACE OF BUSINESS IS IN
Los Angeles COUNTY.

MY COMMISSION EXPIRES: May 9, 2003

Sonia C. Garcia
NOTARY PUBLIC IN AND FOR SAID STATE
SONIA E. GARCIA
(PRINT NAME)

NOTARY ACKNOWLEDGMENT

STATE OF CALIFORNIA)
COUNTY OF ORANGE) SS

ON THIS 19th DAY OF April, 2000, BEFORE ME Tina T. Baker
Notary Public, PERSONALLY APPEARED Paul Johnson AND
PERSONALLY KNOWN TO ME OR PROVED TO ME ON THE BASIS
OF SATISFACTORY EVIDENCE TO BE THE PERSONS WHOSE NAMES ARE SUBSCRIBED TO THE WITHIN INSTRUMENT AND ACKNOWLEDGED TO ME THAT THEY EXECUTED THE SAME IN THEIR AUTHORIZED CAPACITIES, AND THAT BY THEIR SIGNATURES ON THE INSTRUMENT THE PERSONS, OR THE ENTITY UPON BEHALF OF WHICH THE PERSONS ACTED, EXECUTED THE INSTRUMENT.

WITNESS MY HAND:

MY PRINCIPAL PLACE OF BUSINESS IS IN
Orange COUNTY.

MY COMMISSION EXPIRES: 8/29/2000

Tina T. Baker
NOTARY PUBLIC IN AND FOR SAID STATE
Tina T. Baker
(PRINT NAME)

SHEET 3 OF 6 SHEETS
6.264 ACRES
SCALE: 1" = 60'

36 LOTS AND LOTS
"A", "B", "C" AND "D"

(ALL OF VESTING TENTATIVE
TRACT NO. 15903)

TRACT NO. 15903

IN THE UNINCORPORATED TERRITORY OF THE
COUNTY OF ORANGE, STATE OF CALIFORNIA

WAGNER HALLADAY, INC.

ROBERT N. MIM MACK L.S. 5314 DATE OF SURVEY: NOVEMBER, 1999

BOUNDARY CONTROL & SHEET INDEX MAP

LETTERED LOTS "A", "B", "C" AND
"D" ARE FOR LANDSCAPING AND
OPEN SPACE PURPOSES AND ARE
NOT SEPARATE BUILDING SITES

BASIS OF BEARINGS

THE BEARINGS SHOWN HEREON ARE BASED ON THE BEARING
BETWEEN OCS HORIZONTAL CONTROL STATION GPS NO. 1417 AND
STATION GPS NO. 1431, BEING N04°51'18"W PER RECORDS ON FILE
IN THE OFFICE OF THE ORANGE COUNTY SURVEYOR.


DATUM STATEMENT

COORDINATES SHOWN ON THIS MAP ARE BASED ON THE
CALIFORNIA COORDINATE SYSTEM (CCS83), ZONE VI,
1983 NAD, (1991.35 EPOCH OCS ADJUSTMENT).

ALL DISTANCES SHOWN HEREON ARE GROUND, UNLESS
OTHERWISE NOTED. TO OBTAIN GRID DISTANCE, MULTIPLY
THE GROUND DISTANCE BY THE COMBINATION FACTOR OF
0.99994092.

MONUMENT NOTES:

- INDICATES LOCATION OF 2" IRON PIPE TAGGED "L.S. 5557" OR SPIKE & WASHER STAMPED "L.S. 5557" OR LEAD, TACK & TAG "L.S. 5557" TO BE SET PER TRACT NO. 15813, M.M. 795/01-16, UNLESS OTHERWISE NOTED.
- INDICATES LOCATION OF 2" IRON PIPE TAGGED L.S. 5314 SET PRIOR TO RECORDATION.
- INDICATES OCS HORIZONTAL CONTROL POINT.
- 2" IRON PIPE TAGGED L.S. 5314 OR SPIKE AND WASHER STAMPED L.S. 5314 IN ASPHALT OR LEAD AND TAG L.S. 5314 IN CONCRETE TO BE SET AT ALL TRACT CORNERS WITHIN 90 DAYS AFTER ACCEPTANCE OF IMPROVEMENTS.
- 1" IRON PIPE TAGGED L.S. 5314 OR SPIKE AND WASHER STAMPED L.S. 5314 IN ASPHALT OR LEAD AND TAG L.S. 5314 IN CONCRETE TO BE SET AT ALL REAR LOT CORNERS WITHIN 90 DAYS AFTER ACCEPTANCE OF IMPROVEMENTS. LEAD AND TAG L.S. 5314 TO BE SET IN THE CONCRETE WALK ON A PROJECTION OF THE SIDE LOT LINE AT 0.50' OFFSET, UNLESS OTHERWISE NOTED, FOR FRONT LOT CORNERS WITHIN 90 DAYS AFTER ACCEPTANCE OF IMPROVEMENTS.
- 1" IRON PIPE TAGGED L.S. 5314 OR SPIKE AND WASHER STAMPED L.S. 5314 IN ASPHALT OR LEAD AND TAG L.S. 5314 IN CONCRETE TO BE SET AT ALL CENTERLINE INTERSECTIONS, B.C.'S, E.C.'S AND ALL OTHER CENTERLINE POINTS OF CONTROL WITHIN 90 DAYS AFTER ACCEPTANCE OF IMPROVEMENTS.

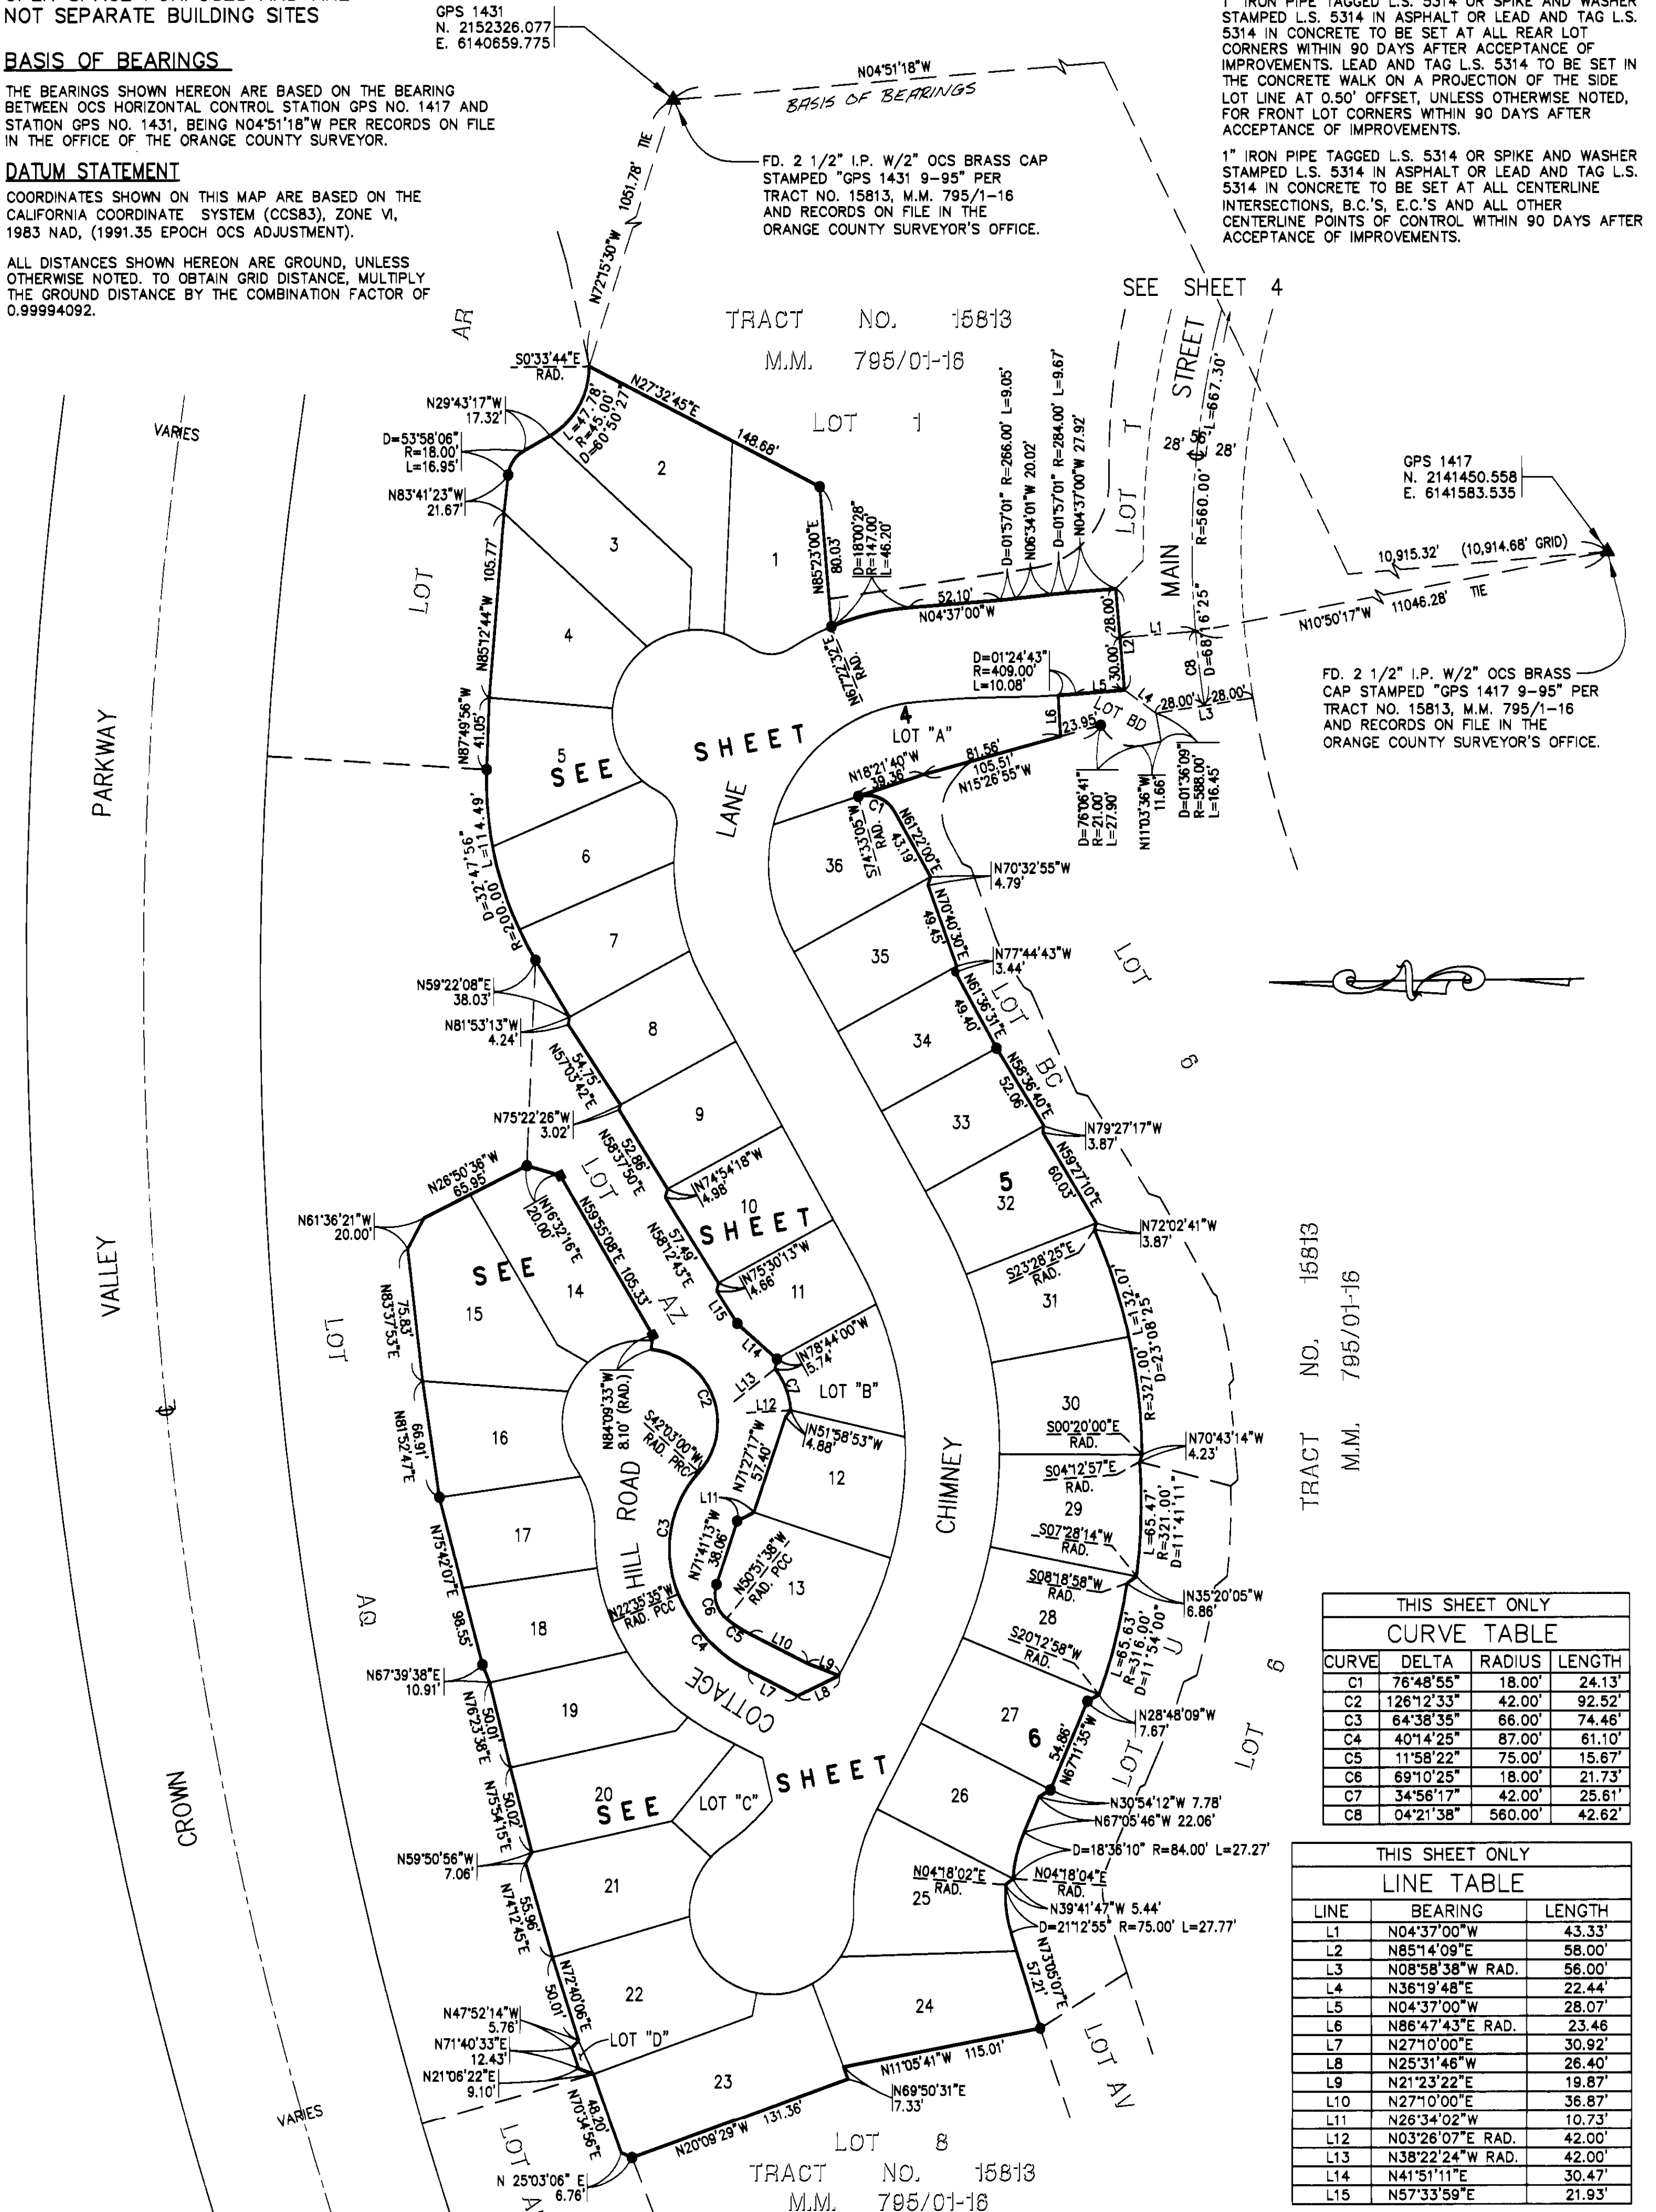

THIS SHEET ONLY			
CURVE TABLE			
CURVE	DELTA	RADIUS	LENGTH
C1	76°48'55"	18.00'	24.13'
C2	126°12'33"	42.00'	92.52'
C3	64°38'35"	66.00'	74.46'
C4	40°14'25"	87.00'	61.10'
C5	11°58'22"	75.00'	15.67'
C6	69°10'25"	18.00'	21.73'
C7	34°56'17"	42.00'	25.61'
C8	04°21'38"	560.00'	42.62'

THIS SHEET ONLY		
LINE TABLE		
LINE	BEARING	LENGTH
L1	N04°37'00"W	43.33'
L2	N85°14'09"E	58.00'
L3	N08°58'38"W RAD.	56.00'
L4	N36°19'48"E	22.44'
L5	N04°37'00"W	28.07'
L6	N86°47'43"E RAD.	23.46'
L7	N27°10'00"E	30.92'
L8	N25°31'46"W	26.40'
L9	N21°23'22"E	19.87'
L10	N27°10'00"E	36.87'
L11	N26°34'02"W	10.73'
L12	N03°26'07"E RAD.	42.00'
L13	N38°22'24"W RAD.	42.00'
L14	N41°51'11"E	30.47'
L15	N57°33'59"E	21.93'

SHEET 4 OF 6 SHEETS
6.264 ACRES
SCALE: 1" = 30'

36 LOTS AND LOTS
"A", "B", "C" AND "D"
(ALL OF VESTING TENTATIVE
TRACT NO. 15903)

TRACT NO. 15903


IN THE UNINCORPORATED TERRITORY OF THE
COUNTY OF ORANGE, STATE OF CALIFORNIA

WAGNER HALLADAY, INC.

ROBERT N. MIM MACK L.S. 5314 DATE OF SURVEY: NOVEMBER, 1999

NOTES:

SEE SHEET 2 FOR EASEMENT NOTES.
SEE SHEET 3 FOR BASIS OF BEARINGS, MONUMENT NOTES, BOUNDARY
CONTROL, AND INDEX MAP.
LETTERED LOTS "A", "B", "C" AND "D" ARE FOR LANDSCAPING AND OPEN
SPACE PURPOSES AND ARE NOT SEPARATE BUILDING SITES.

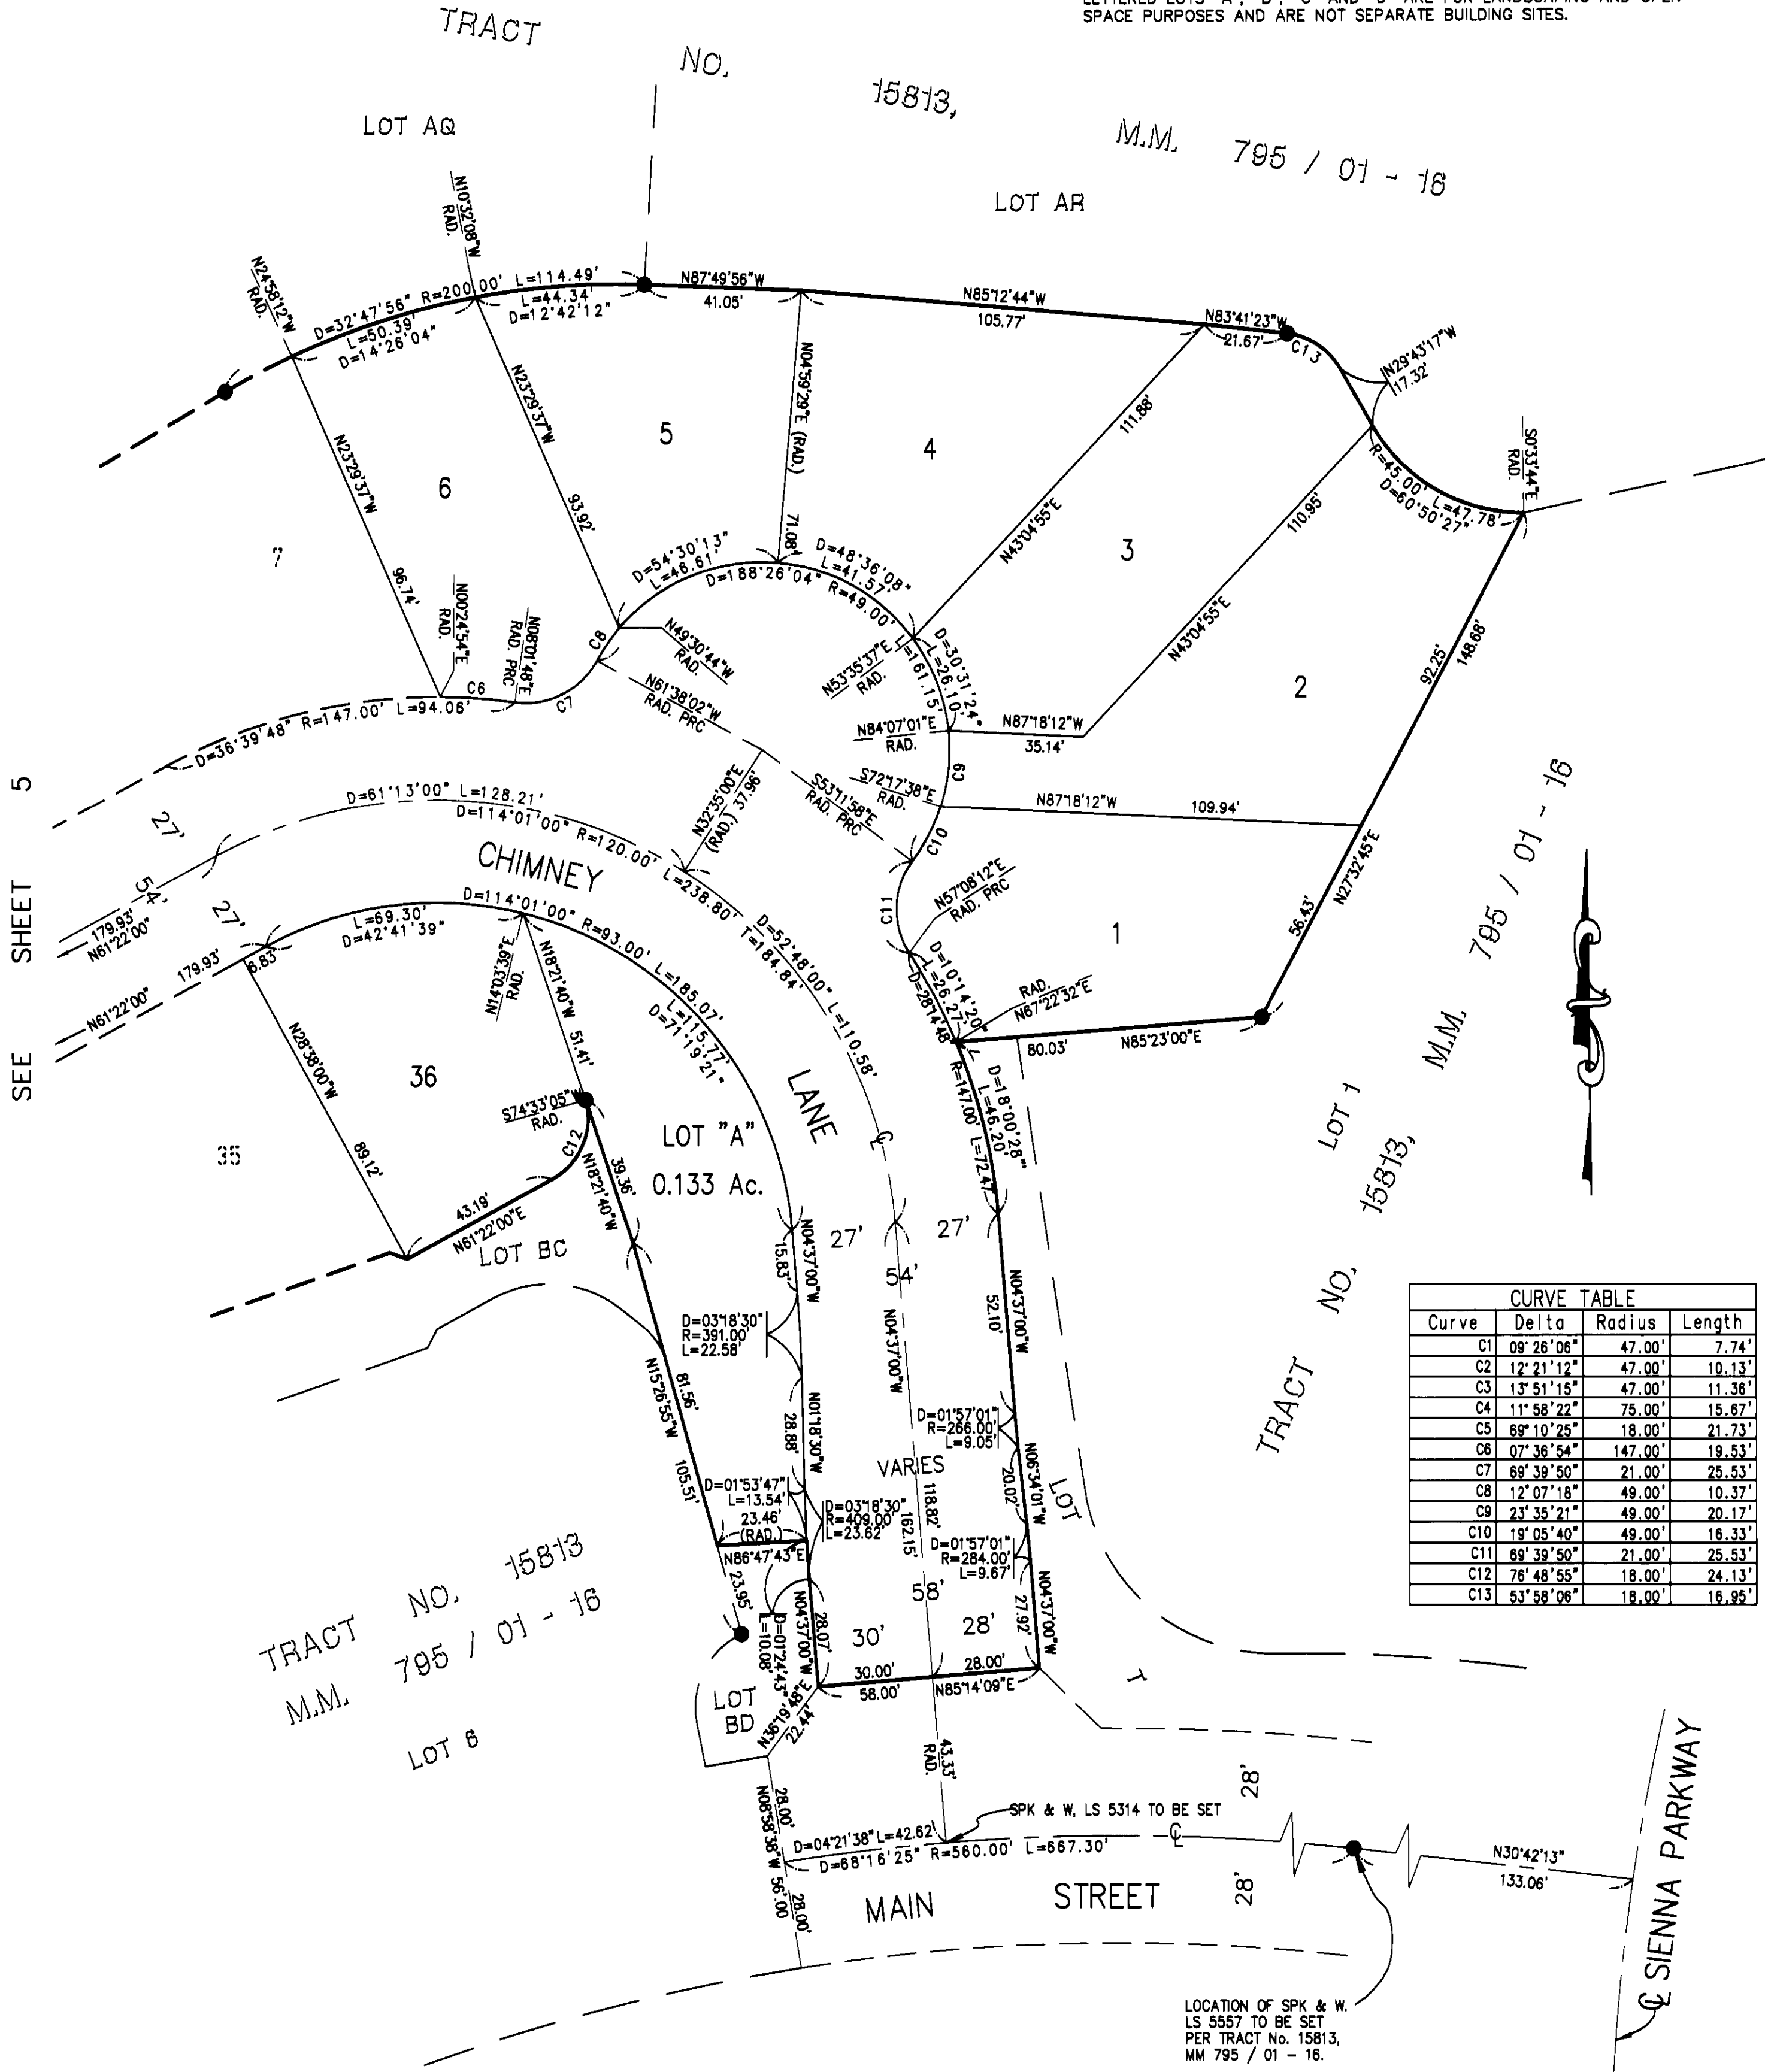

SHEET 5 OF 6 SHEETS
6.264 ACRES
SCALE: 1" = 30'
36 LOTS AND LOTS
"A", "B", "C" AND "D"
(ALL OF VESTING TENTATIVE
TRACT NO. 15903)


TRACT NO. 15903

IN THE UNINCORPORATED TERRITORY OF THE
COUNTY OF ORANGE, STATE OF CALIFORNIA

WAGNER HALLADAY, INC.
ROBERT N. MIM MACK L.S. 5314 DATE OF SURVEY: NOVEMBER, 1999

NOTES:

SEE SHEET 2 FOR EASEMENT NOTES.
SEE SHEET 3 FOR BASIS OF BEARINGS, MONUMENT NOTES, BOUNDARY
CONTROL, AND INDEX MAP.
LETTERED LOTS "A", "B", "C" AND "D" ARE FOR LANDSCAPING AND OPEN
SPACE PURPOSES AND ARE NOT SEPARATE BUILDING SITES.

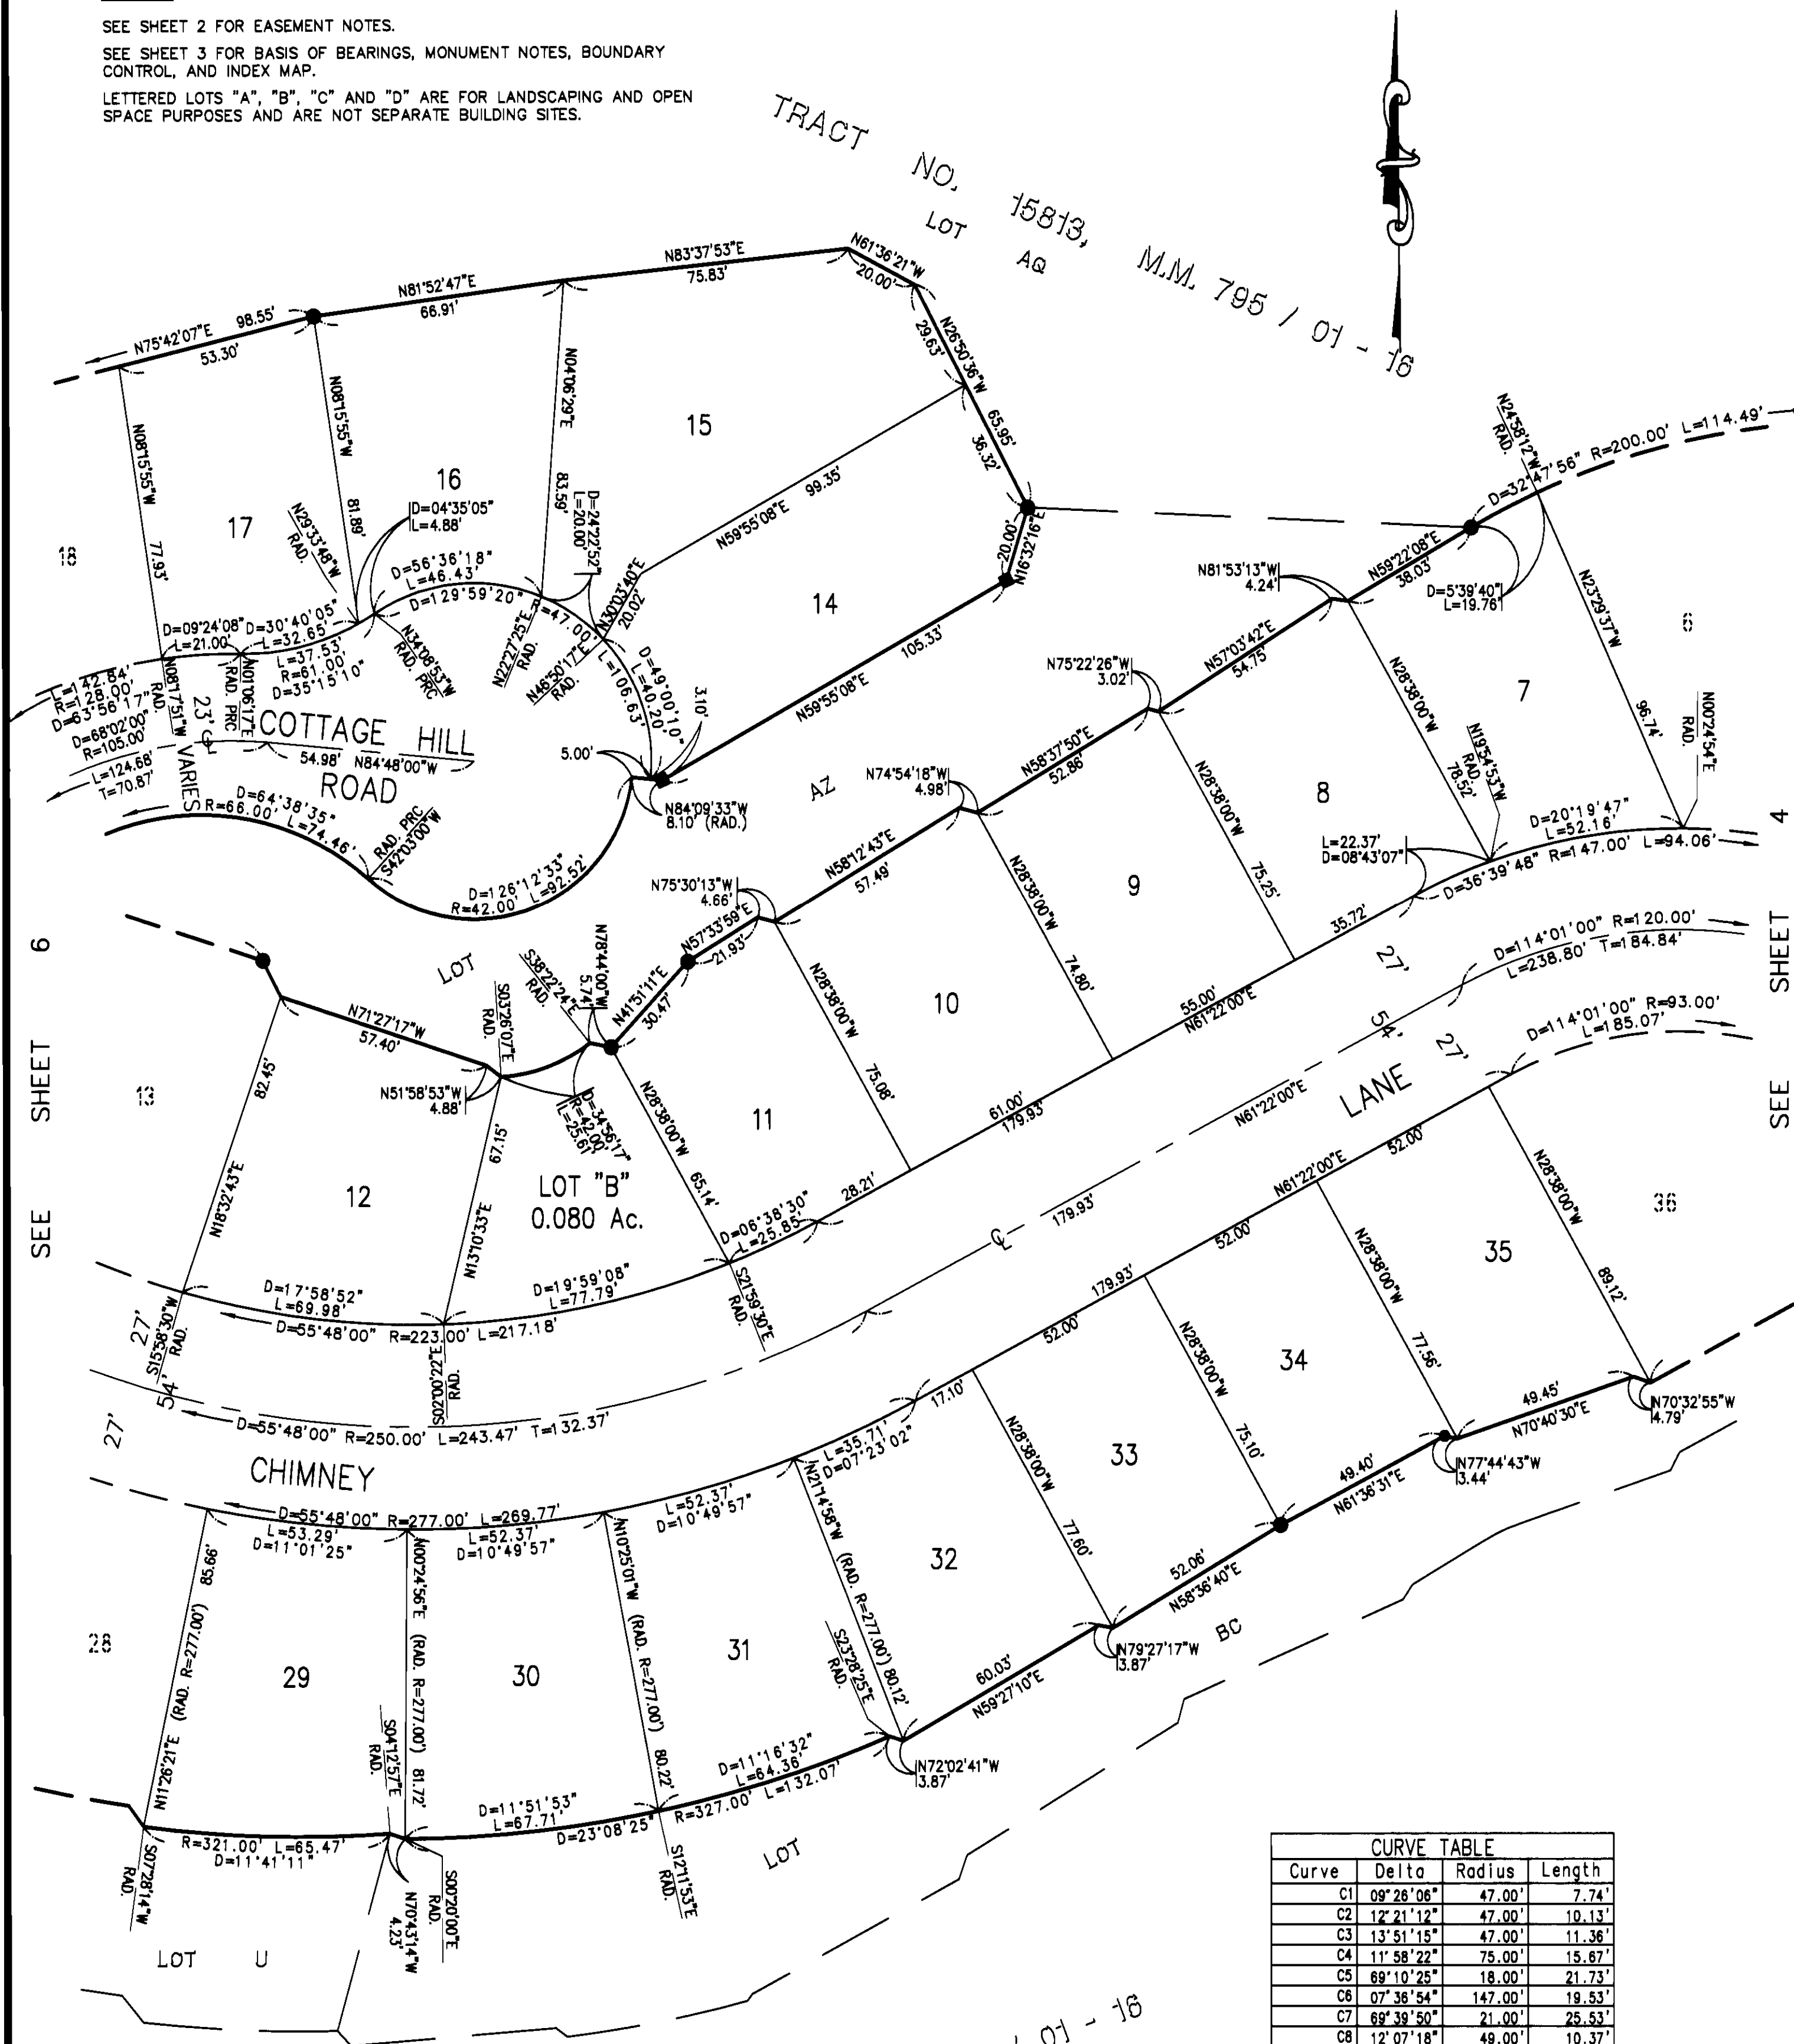

CURVE TABLE			
Curve	Delta	Radius	Length
C1	09° 26' 06"	47.00'	7.74'
C2	12° 21' 12"	47.00'	10.13'
C3	13° 51' 15"	47.00'	11.36'
C4	11° 58' 22"	75.00'	15.67'
C5	69° 10' 25"	18.00'	21.73'
C6	07° 36' 54"	147.00'	19.53'
C7	69° 39' 50"	21.00'	25.53'
C8	12° 07' 18"	49.00'	10.37'
C9	23° 35' 21"	49.00'	20.17'
C10	19° 05' 40"	49.00'	16.33'
C11	69° 39' 50"	21.00'	25.53'
C12	76° 48' 55"	18.00'	24.13'
C13	53° 58' 08"	18.00'	16.95'

TRACT NO. 15813, LOT 8 M.M. 795 / 01 - 16

SHEET 6 OF 6 SHEETS
6.264 ACRES
SCALE: 1" = 30'

TRACT NO. 15903

IN THE UNINCORPORATED TERRITORY OF THE
COUNTY OF ORANGE, STATE OF CALIFORNIA

36 LOTS AND LOTS "A", "B", "C" AND "D"

(ALL OF VESTING TENTATIVE
TRACT NO. 15903)

WAGNER HALLADAY, INC.

ROBERT N. MIM MACK L.S. 5314 DATE OF SURVEY: NOVEMBER, 1999

