

SHEET 1 OF 3 SHEETS

(ALL OF VESTING TENTATIVE
TRACT NO. 15905)TOTAL ACRES: 11.337 AC.
NUMBERED LOTS: 43
LETTERED LOTS: 4
DATE OF SURVEY: NOVEMBER 1997.

TRACT NO. 15905

IN THE UNINCORPORATED TERRITORY OF ORANGE COUNTY, STATE OF CALIFORNIA

BEING LOT 7 OF TRACT NO. 15813 IN THE UNINCORPORATED TERRITORY OF THE
COUNTY OF ORANGE, STATE OF CALIFORNIA, AS SHOWN ON A MAP FILED IN BOOK
795, PAGES 1 THROUGH 16, OF MISCELLANEOUS MAPS, RECORDS IN THE OFFICE
OF THE COUNTY RECORDER OF ORANGE COUNTY, CALIFORNIA.BLOCK: MODULE:
5157 04,05,14 & 15.

DOUGLAS BENDER AND ASSOCIATES DOUGLAS W. BENDER R.C.E. 28946

SEPTEMBER, 1999

ACCEPTED AND FILED AT THE
REQUEST OF

FIRST AMERICAN TITLE INSURANCE COMPANY

DATE AUGUST 16, 2000TIME 10:51 A.M. FEE \$ 11.00INSTRUMENT # 20000427611BOOK 805 PAGE 6-8 M/MGARY L. GRANVILLE
COUNTY CLERK-RECORDERBY [Signature]
DEPUTY

OWNERSHIP CERTIFICATE:

WE, THE UNDERSIGNED, BEING ALL PARTIES HAVING ANY RECORD TITLE
INTEREST IN THE LAND COVERED BY THIS MAP, DO HEREBY CONSENT TO
THE PREPARATION AND RECORDATION OF SAID MAP, AS SHOWN WITHIN
THE DISTINCTIVE BORDER LINE.WE ALSO HEREBY DEDICATE TO THE PUBLIC FOR STREET PURPOSES
WELDON HEIGHTS, NEWKIRK ROAD, SAYBROOKE LANE, WICKFORD LANE
AND BENNINGTON PATH.

WE ALSO HEREBY DEDICATE TO THE COUNTY OF ORANGE:

1. AN EASEMENT FOR SIDEWALK PURPOSES AS SHOWN ON SAID MAP.

ENGINEER'S STATEMENT:

I HEREBY STATE THAT THIS MAP CONSISTING OF 3 SHEETS, CORRECTLY REPRESENTS
A TRUE AND COMPLETE SURVEY AS SHOWN MADE IN NOVEMBER, 1997; WAS MADE BY
ME OR UNDER MY DIRECTION; THAT THE MONUMENTS ARE OF CHARACTER AND
OCCUPY (OR WILL OCCUPY) THE POSITIONS INDICATED BY SAID MAP; AND THAT
SAID MONUMENTS ARE (OR WILL BE) SUFFICIENT TO ENABLE THE SURVEY
TO BE RETRACED.DOUGLAS W. BENDER, R.C.E. 28946
MY REGISTRATION EXPIRES MARCH 31, 2003.

COUNTY SURVEYOR'S STATEMENT:

I HEREBY STATE THAT I HAVE EXAMINED THIS MAP AND HAVE FOUND IT TO BE
SUBSTANTIALLY IN CONFORMANCE WITH THE TENTATIVE MAP AS FILED WITH, AMENDED
AND APPROVED BY THE ORANGE COUNTY SUBDIVISION COMMITTEE; THAT ALL
PROVISIONS OF THE SUBDIVISION MAP ACT AND COUNTY SUBDIVISION REGULATIONS
HAVE BEEN COMPLIED WITH AND I AM SATISFIED SAID MAP IS TECHNICALLY CORRECT.DATED THIS 28 DAY OF July, 2000.Michael K. Sullivan
JOHN CANAS, COUNTY SURVEYORBY: MICHAEL K. SULLIVAN, DEPUTY
L.S. 6254 EXPIRES 6-30-02WARMINGTON LDR ASSOCIATES II, L.P.,
A CALIFORNIA LIMITED PARTNERSHIP, OWNER.Brian L. Sinderhoff
BRIAN L. SINDERHOFF
PRESIDENT, SOUTHERN CALIFORNIA DIVISIONRobert G. McClaire
ROBERT G. MCCLAIRE
VICE PRESIDENT, PROJECT DEVELOPMENTDMB LADERA, L.L.C., A DELAWARE LIMITED LIABILITY COMPANY, BENEFICIARY
UNDER A DEED OF TRUST RECORDED AS INST. NO. 20000110532, O.R.
BY: RANCHO MISSION VIEJO, LLC, A DELAWARE LIMITED LIABILITY COMPANY,
AS MANAGERPaul Johnson
PAUL JOHNSON
V.P. - COMMUNITY DEVELOPMENTCOMERICA BANK-CALIFORNIA, A CALIFORNIA BANKING CORPORATION
BENEFICIARY UNDER A DEED RECORDED AS INST. NO. 20000110533, O.R.Jeffrey M. Bloom
JEFFREY M. BLOOM
VICE PRESIDENTDon Bruner
DON BRUNER
VICE PRESIDENTFIRST
Senior

WARMINGTON LDR ASSOCIATES II

STATE OF CALIFORNIA)
) SS
COUNTY OF ORANGE)ON THIS June 5, 2000, BEFORE ME, Betty Jo Poston,
A NOTARY PUBLIC IN AND FOR SAID STATE, PERSONALLY APPEARED
BRIAN L. SINDERHOFF AND ROBERT G. MCCLAIREPERSONALLY KNOWN TO ME (OR PROVED TO ME ON THE BASIS OF SATISFACTORY EVIDENCE)
TO BE THE PERSON (S) WHOSE NAME (S) IS/ARE SUBSCRIBED TO THE WITHIN INSTRUMENT
AND ACKNOWLEDGED TO ME THAT HE/SHE/THEY EXECUTED THE SAME IN HIS/HER/THEIR
AUTHORIZED CAPACITY (IES), AND THAT BY HIS/HER/THEIR SIGNATURE (S) ON THE
INSTRUMENT THE PERSON (S), OR THE ENTITY UPON BEHALF OF WHICH THE PERSON (S)
ACTED, EXECUTED THE INSTRUMENT.

WITNESS MY HAND:

SIGNATURE Betty Jo Poston
NOTARY PUBLIC IN AND FOR SAID STATEMY PRINCIPAL PLACE OF BUSINESS IS
IN Orange COUNTY.Betty Jo Poston
(NAME PRINTED)MY COMMISSION EXPIRES 3/17/2001

DMB LADERA, L.L.C.

STATE OF CALIFORNIA)
) SS
COUNTY OF ORANGE)ON THIS June 23, 2000, BEFORE ME, Linda K. Ledger,
A NOTARY PUBLIC IN AND FOR SAID STATE, PERSONALLY APPEARED
Paul JohnsonPERSONALLY KNOWN TO ME (OR PROVED TO ME ON THE BASIS OF SATISFACTORY EVIDENCE)
TO BE THE PERSON (S) WHOSE NAME (S) IS/ARE SUBSCRIBED TO THE WITHIN INSTRUMENT
AND ACKNOWLEDGED TO ME THAT HE/SHE/THEY EXECUTED THE SAME IN HIS/HER/THEIR
AUTHORIZED CAPACITY (IES), AND THAT BY HIS/HER/THEIR SIGNATURE (S) ON THE
INSTRUMENT THE PERSON (S), OR THE ENTITY UPON BEHALF OF WHICH THE PERSON (S)
ACTED, EXECUTED THE INSTRUMENT.

WITNESS MY HAND:

SIGNATURE Linda K. Ledger
NOTARY PUBLIC IN AND FOR SAID STATEMY PRINCIPAL PLACE OF BUSINESS IS
IN ORANGE COUNTY.LINDA K. LEDGER
(NAME PRINTED)MY COMMISSION EXPIRES 3/9/2003

COMERICA BANK-CALIFORNIA

STATE OF CALIFORNIA)
) SS
COUNTY OF ORANGE)ON THIS June 8, 2000, BEFORE ME, Lisa M. Larson,
A NOTARY PUBLIC IN AND FOR SAID STATE, PERSONALLY APPEARED
PAUL HAYASHI AND DON BRUNER and Jeffrey M. BloomPERSONALLY KNOWN TO ME (OR PROVED TO ME ON THE BASIS OF SATISFACTORY EVIDENCE)
TO BE THE PERSON (S) WHOSE NAME (S) IS/ARE SUBSCRIBED TO THE WITHIN INSTRUMENT
AND ACKNOWLEDGED TO ME THAT HE/SHE/THEY EXECUTED THE SAME IN HIS/HER/THEIR
AUTHORIZED CAPACITY (IES), AND THAT BY HIS/HER/THEIR SIGNATURE (S) ON THE
INSTRUMENT THE PERSON (S), OR THE ENTITY UPON BEHALF OF WHICH THE PERSON (S)
ACTED, EXECUTED THE INSTRUMENT.

WITNESS MY HAND:

SIGNATURE Lisa M. Larson
NOTARY PUBLIC IN AND FOR SAID STATEMY PRINCIPAL PLACE OF BUSINESS IS
IN Orange COUNTY.Lisa M. Larson
(NAME PRINTED)MY COMMISSION EXPIRES Aug 4, 2001

CLERK OF THE BOARD OF SUPERVISOR'S CERTIFICATE:

STATE OF CALIFORNIA)
) SS
COUNTY OF ORANGE)I HEREBY CERTIFY THAT THIS MAP WAS PRESENTED FOR APPROVAL TO THE BOARD OF
SUPERVISORS OF ORANGE COUNTY AT A REGULAR MEETING THEREOF HELD ON THE 6th
DAY OF August, 2000, AND THAT THEREUPON SAID BOARD DID, BY AN ORDER
DULY PASSED AND ENTERED, APPROVE SAID MAP AND DID ACCEPT ON BEHALF OF THE
PUBLIC, SUBJECT TO IMPROVEMENTS, THE DEDICATION FOR STREET PURPOSES:
WELDON HEIGHTS, NEWKIRK ROAD, SAYBROOKE LANE, WICKFORD LANE AND BENNINGTON
PATH.

WE ALSO ACCEPT ON BEHALF OF COUNTY OF ORANGE:

1. AN EASEMENT FOR SIDEWALK PURPOSES AS SHOWN ON SAID MAP.

AND DID ALSO APPROVE SUBJECT MAP PURSUANT TO THE PROVISIONS OF CALIFORNIA
66438(a)(3)(A) OF THE SUBDIVISION MAP ACT.DATED THIS 6th DAY OF August, 2000.Darlene J. Bloom
DARLENE J. BLOOM
CLERK OF THE BOARD OF SUPERVISORS

COUNTY TREASURER-TAX COLLECTOR'S CERTIFICATE:

STATE OF CALIFORNIA)
) SS
COUNTY OF ORANGE)I HEREBY CERTIFY THAT ACCORDING TO THE RECORDS OF MY OFFICE THERE ARE NO
LIENS AGAINST THE LAND COVERED BY THIS MAP OR ANY PART THEREOF FOR UNPAID
STATE, COUNTY, MUNICIPAL OR LOCAL TAXES OR SPECIAL ASSESSMENTS COLLECTED
AS TAXES, EXCEPT TAXES OR SPECIAL ASSESSMENTS COLLECTED AS TAXES NOT YET
PAYABLE.AND DO ALSO CERTIFY TO THE RECORDER OF ORANGE COUNTY THAT THE PROVISIONS OF
THE SUBDIVISION MAP ACT HAVE BEEN COMPLIED WITH REGARDING DEPOSITS TO
SECURE THE PAYMENT OF TAXES OR SPECIAL ASSESSMENTS COLLECTED AS TAXES ON
THE LAND COVERED BY THIS MAP.DATED THIS 27th DAY OF June, 2000.JOHN M.W. MOORLACH
COUNTY TREASURER-TAX COLLECTORBY: [Signature]
DEPUTY TREASURER-TAX COLLECTOR

AUTOMATIC FIRE SPRINKLER NOTE:

ALL COMMERCIAL STRUCTURES OVER 6,000 SQUARE FEET; ALL MULTIFAMILY RESIDENTIAL
STRUCTURES; ALL DETACHED, SINGLE-FAMILY STRUCTURES EXCEEDING 5,500 SQUARE FEET,
AND ALL STRUCTURES EXCEEDING FIRE AUTHORITY ACCESS REQUIREMENTS SHALL BE
PROTECTED BY AN AUTOMATIC SPRINKLER SYSTEM, IN A MANNER MEETING THE APPROVAL
OF THE FIRE CHIEF.

SPECIAL FIRE PROTECTION NOTE:

THIS PROPERTY IS EXCLUDED FROM A SPECIAL FIRE PROTECTION AREA, BUT SHALL MEET
ROOFING AND STREET WIDTH REQUIREMENTS OF A SPECIAL FIRE PROTECTION AREA.

HIGH FIRE HAZARD AREA NOTE:

PROPERTY IS IN A HIGH/VERY HIGH FIRE HAZARD AREA DUE TO WILDLAND EXPOSURE BASED
ON STATE SRA MAPS.

NOTES:

PROPERTY MAY BE SUBJECT TO IMPACTS FROM THE FOOTHILL/EASTERN
TRANSPORTATION CORRIDOR.

SIGNATURE OMISSION:

PURSUANT TO SECTION 66438 (a) (3) OF THE SUBDIVISION MAP ACT, THE FOLLOWING
SIGNATURES HAVE BEEN OMITTED:1. LADERA DEVELOPMENT COMPANY, L.L.C., HOLDER OF OIL, GAS AND MINERAL RIGHTS
RECORDED DECEMBER 10, 1996 AS INSTRUMENT NO. 19960624029 OF OFFICIAL RECORDS.

SHEET 2 OF 3 SHEETS
(ALL OF VESTING TENTATIVE
TRACT NO. 15905)
TOTAL ACRES: 11.337 AC.
NUMBERED LOTS: 43
LETTERED LOTS: 4
DATE OF SURVEY: NOVEMBER, 1997.

TRACT NO. 15813
M. M. 795 / 1-16.


TRACT NO. 15905

IN THE UNINCORPORATED TERRITORY OF ORANGE COUNTY, STATE OF CALIFORNIA
DOUGLAS BENDER AND ASSOCIATES DOUGLAS W. BENDER R.C.E. 28946
SEPTEMBER, 1999.


BASIS OF BEARINGS:

THE BEARINGS SHOWN HEREON ARE BASED ON THE SOUTHWESTERLY LINE OF LOT 7 SHOWN AS N 37°19'18" W ON THE MAP OF TRACT NO. 15813, FILED IN BOOK 795, PAGES 1 THROUGH 16, INCLUSIVE, OF MISCELLANEOUS MAPS, RECORDS OF ORANGE COUNTY, CALIFORNIA.

ALL LETTERED LOTS ARE NOT SEPARATE BUILDING SITES.
LOTS A THROUGH D ARE FOR LANDSCAPE PURPOSES.

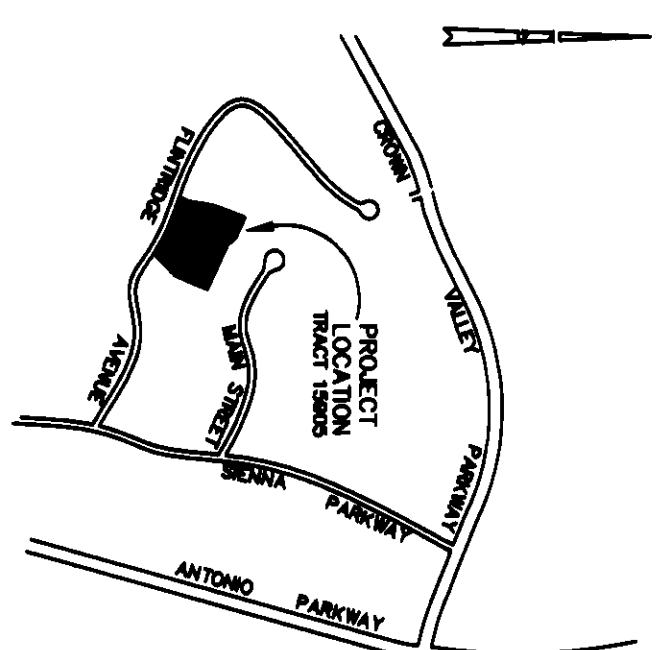

VICINITY MAP
NOT TO SCALE

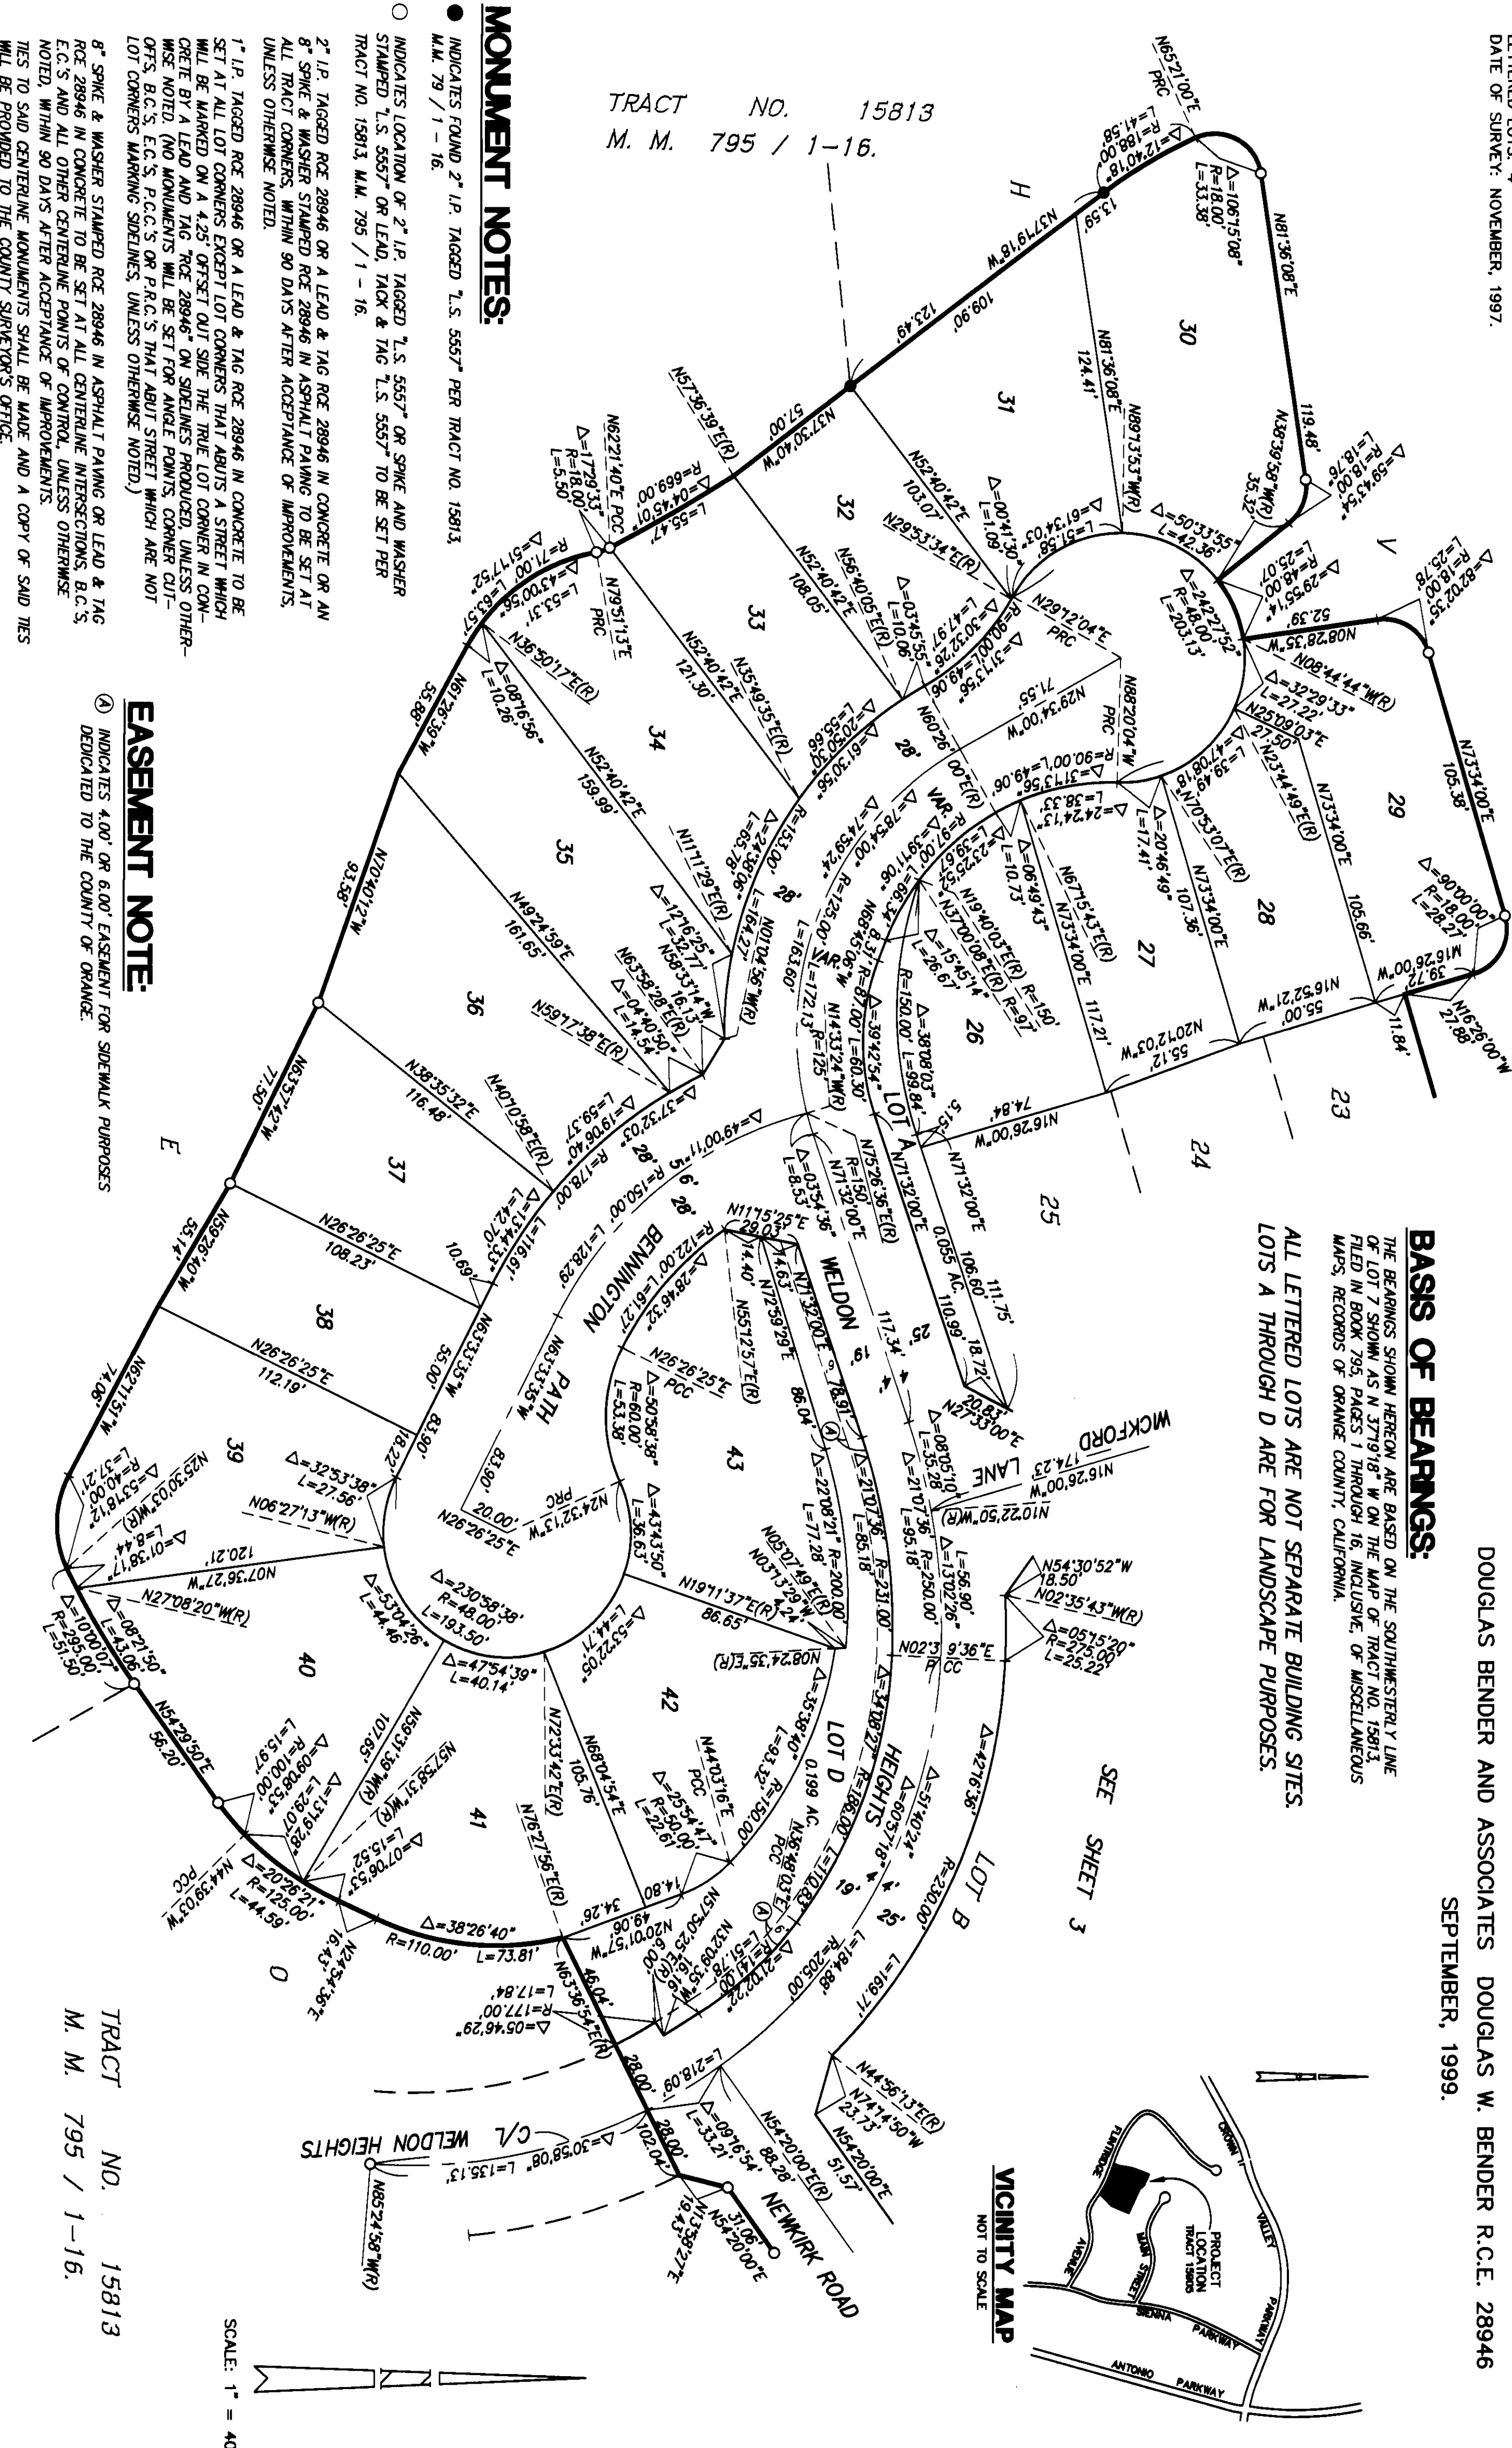

MONUMENT NOTES:

- INDICATES FOUND 2" I.P. TAGGED T.S. 5557" PER TRACT NO. 15813, M.M. 79 / 1 - 16.
- INDICATES LOCATION OF 2" I.P. TAGGED T.S. 5557" OR SPIKE AND WASHER STAMPED T.S. 5557" OR LEAD, TACK & TAG T.S. 5557" TO BE SET PER TRACT NO. 15813, M.M. 795 / 1 - 16.
- 2" I.P. TAGGED RCE 28946 OR A LEAD & TAG RCE 28946 IN CONCRETE OR AN 8" SPIKE & WASHER STAMPED RCE 28946 IN ASPHALT PAVING TO BE SET AT ALL TRACT CORNERS, WITHIN 90 DAYS AFTER ACCEPTANCE OF IMPROVEMENTS, UNLESS OTHERWISE NOTED.
- 1" I.P. TAGGED RCE 28946 OR A LEAD & TAG RCE 28946 IN CONCRETE TO BE SET AT ALL LOT CORNERS EXCEPT LOT CORNERS THAT ABUT A STREET WHICH WILL BE MARKED ON A 4.25' OFFSET OUTSIDE THE TRUE LOT CORNER IN CONCRETE BY A LEAD AND TAG RCE 28946 ON SIDELINES PRODUCED, UNLESS OTHERWISE NOTED. (NO MONUMENTS WILL BE SET FOR ANGLE POINTS, CORNER CUT-OFFS, B.C.'S, E.C.'S, P.C.'S OR P.R.C.'S THAT ABUT STREET WHICH ARE NOT LOT CORNERS MARKING SIDELINES, UNLESS OTHERWISE NOTED.)
- 8" SPIKE & WASHER STAMPED RCE 28946 IN ASPHALT PAVING OR LEAD & TAG RCE 28946 IN CONCRETE TO BE SET AT ALL CENTERLINE INTERSECTIONS, B.C.'S, E.C.'S AND ALL OTHER CENTERLINE POINTS OF CONTROL, UNLESS OTHERWISE NOTED, WITHIN 90 DAYS AFTER ACCEPTANCE OF IMPROVEMENTS.
- ALL TIES TO SAID CENTERLINE MONUMENTS SHALL BE MADE AND A COPY OF SAID TIES WILL BE PROVIDED TO THE COUNTY SURVEYOR'S OFFICE.

EASEMENT NOTE:

- ④ INDICATES 4.00' OR 6.00' EASEMENT FOR SIDEWALK PURPOSES DEDICATED TO THE COUNTY OF ORANGE.


SHEET 3 OF 3 SHEETS
(ALL OF VESTING TENTATIVE)
TRACT NO. 15905
TOTAL ACRES: 11.337 AC.
NUMBERED LOTS: 43
LETTERED LOTS: 4
DATE OF SURVEY: NOVEMBER, 1997.

TRACT NO. 15813
M. M. 795 / 1-16.

TRACT NO. 15905

IN THE UNINCORPORATED TERRITORY OF ORANGE COUNTY, STATE OF CALIFORNIA
DOUGLAS BENDER AND ASSOCIATES DOUGLAS W. BENDER R.C.E. 28946
SEPTEMBER, 1999.

TRACT NO. 15813
M. M. 795 / 1-16.

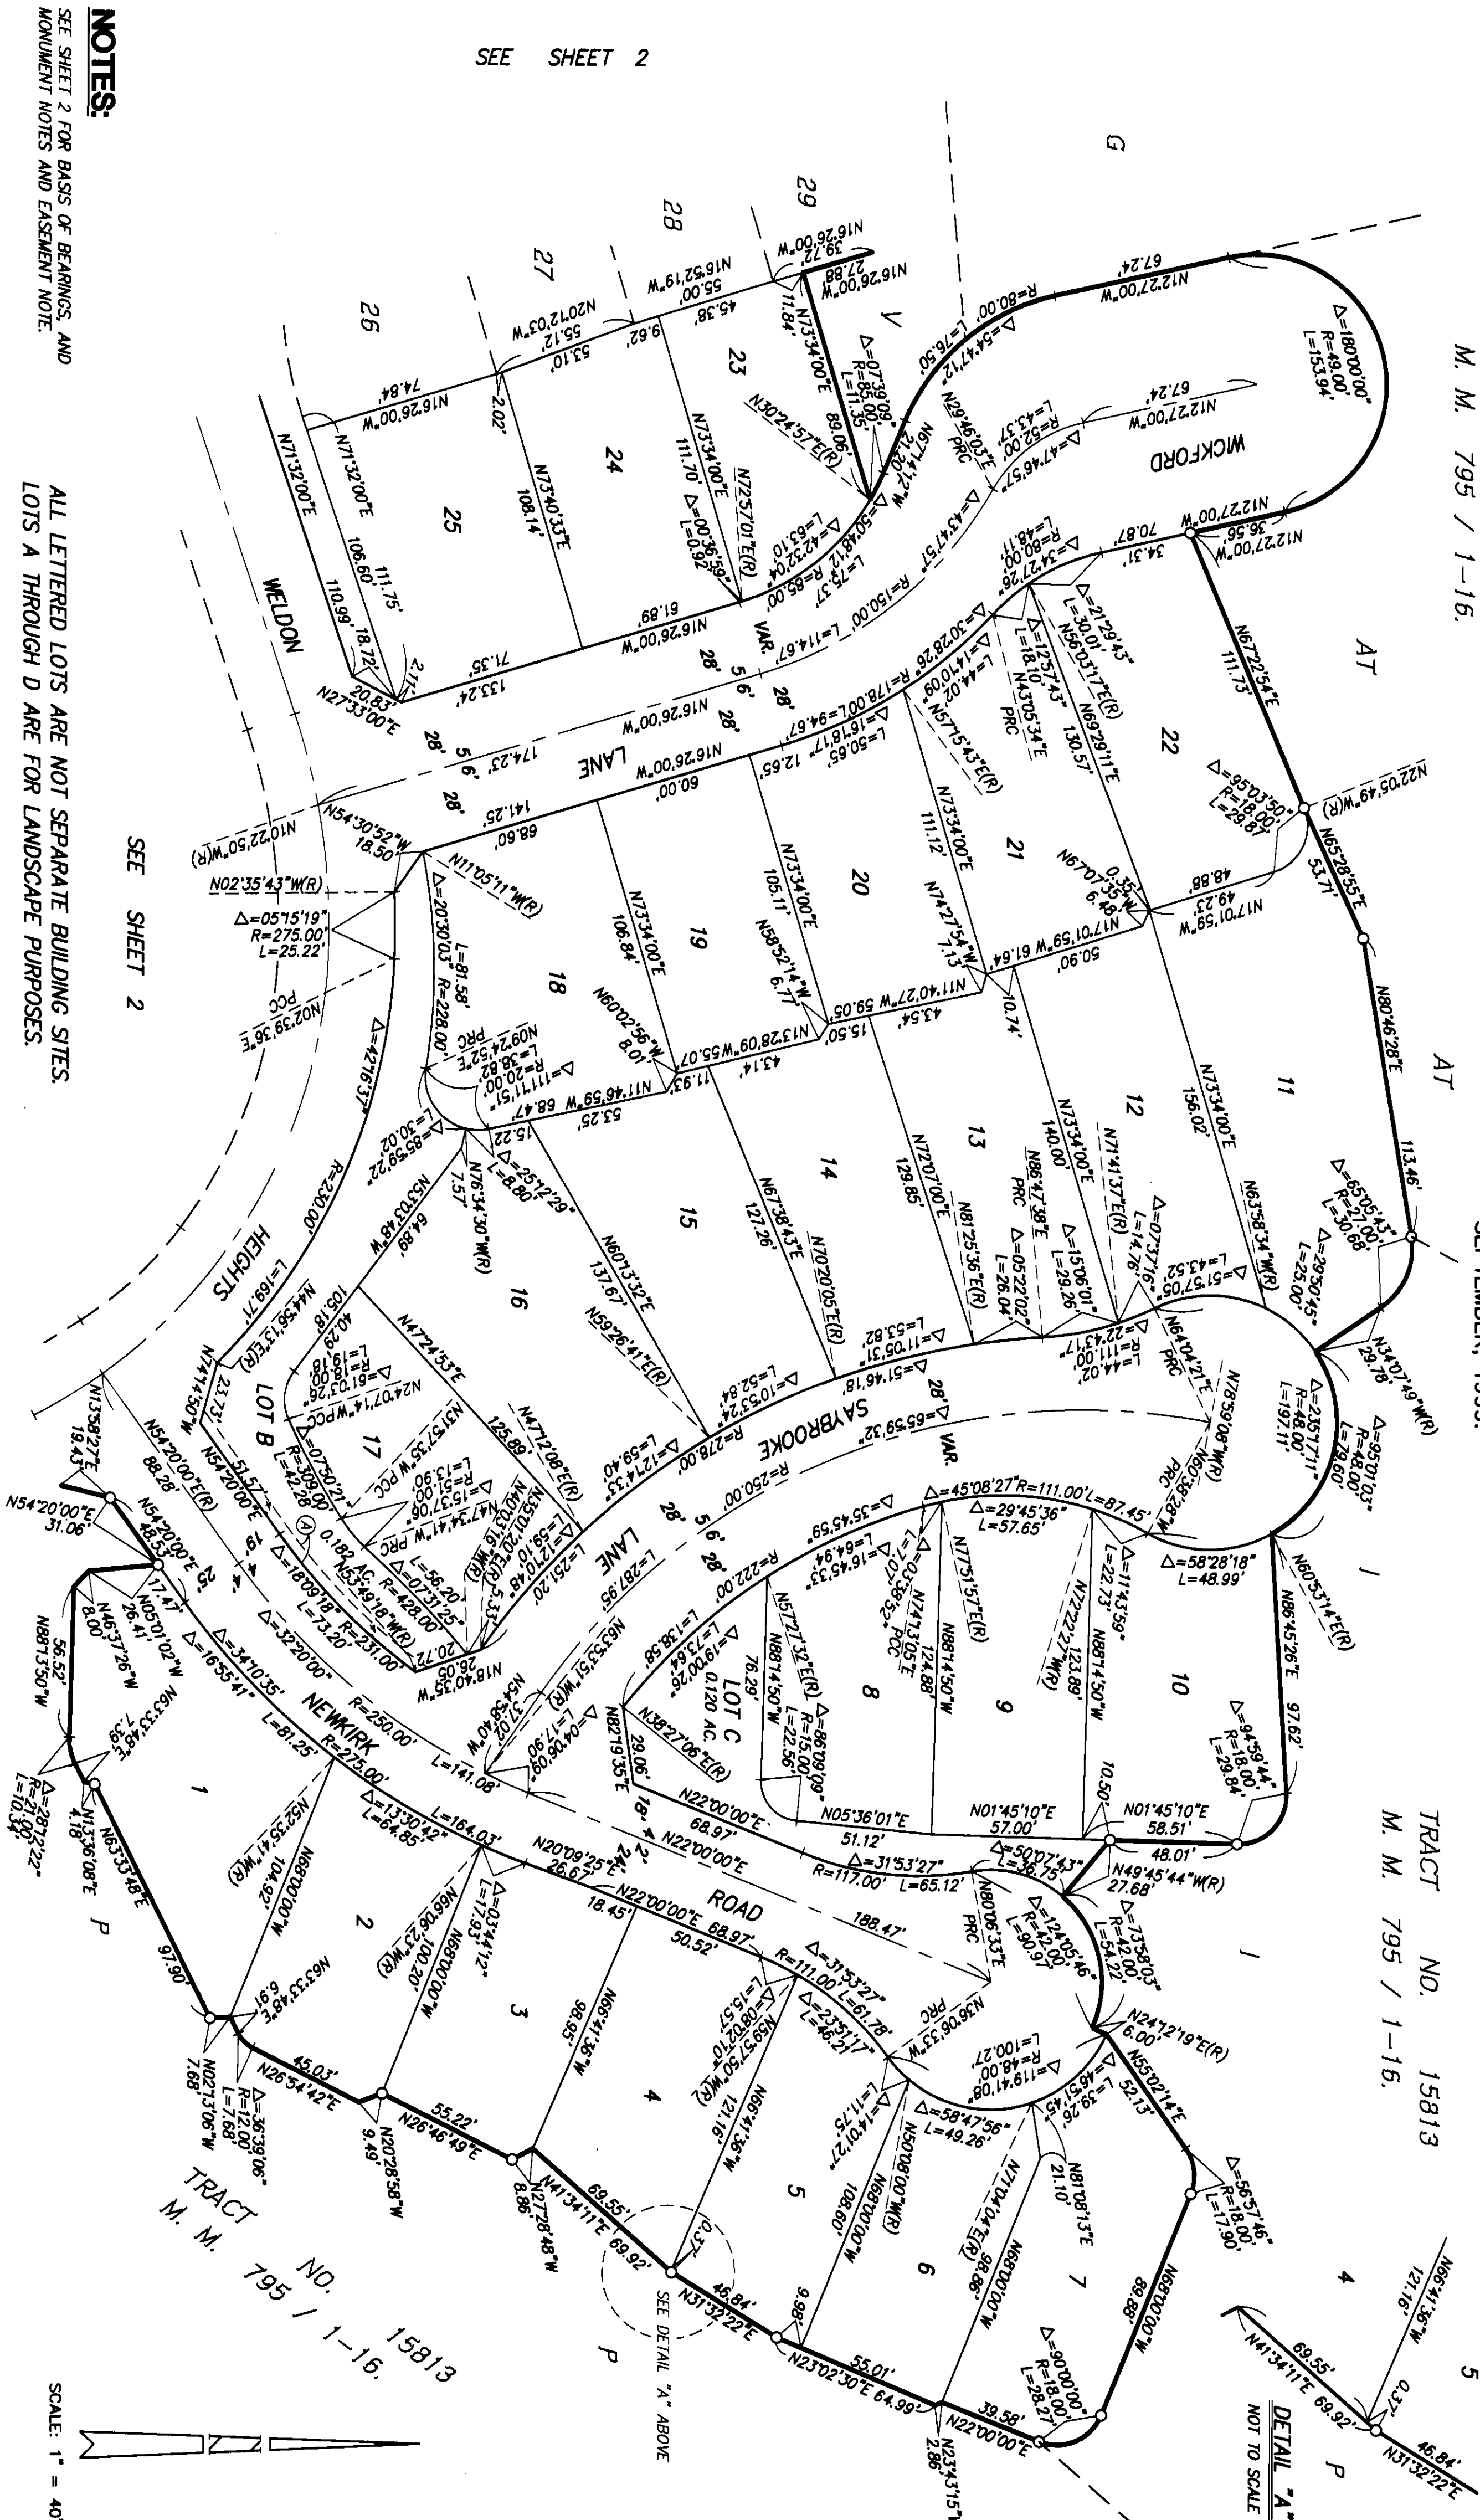

NOTES:

SEE SHEET 2 FOR BASIS OF BEARINGS, AND
MONUMENT NOTES AND EASEMENT NOTE.

ALL LETTERED LOTS ARE NOT SEPARATE BUILDING SITES.
LOTS A THROUGH D ARE FOR LANDSCAPE PURPOSES.

SEE SHEET 2

SEE SHEET 2

SCALE: 1" = 40'