

SHEET 1 OF 6 SHEETS
9.542 ACRES
56 LOTS AND LOTS "A"
"B", "C", AND "D"
(ALL OF VESTING TENTATIVE
TRACT NO. 15906)

BLOCK 5157 MODULE 6

TRACT NO. 15906

IN THE UNINCORPORATED TERRITORY OF THE
COUNTY OF ORANGE, STATE OF CALIFORNIA

BEING A SUBDIVISION OF LOT 3 OF TRACT NO. 15813, AS FILED IN
BOOK 795, PAGES 1 THROUGH 16, INCLUSIVE, OF MISCELLANEOUS
MAPS, RECORDS OF ORANGE COUNTY.

WAGNER HALLADAY, INC.

ROBERT N. MIM MACK L.S. 5314 DATE OF SURVEY: NOVEMBER, 1999

ACCEPTED AND FILED AT THE
REQUEST OF

FIRST AMERICAN TITLE CO.

DATE Jun. 16, 2000

TIME 10:20 am FEE \$ 17.00

INSTRUMENT # 20000318073

BOOK 803 PAGE 16-21

GARY L. GRANVILLE
COUNTY CLERK-RECORDER

BY Robert N. Mim Mack
DEPUTY

OWNERSHIP CERTIFICATE

WE, THE UNDERSIGNED, BEING ALL PARTIES HAVING ANY RECORD TITLE INTEREST IN THE LAND COVERED BY THIS MAP, DO HEREBY CONSENT TO THE PREPARATION AND RECORDATION OF SAID MAP, AS SHOWN WITHIN THE DISTINCTIVE BORDER LINE. WE HEREBY DEDICATE TO THE PUBLIC FOR STREET PURPOSES: HEARTHSIDE ROAD, BRYNWOOD LANE, FRANKLIN WAY AND NEWBURY WAY.

WE ALSO HEREBY DEDICATE TO THE COUNTY OF ORANGE:
THE EASEMENT FOR STORM DRAIN PURPOSES AS SHOWN ON THIS MAP.

WE ALSO HEREBY DEDICATE TO THE SANTA MARGARITA WATER DISTRICT THE EASEMENTS FOR SEWER AND WATER PURPOSES AS SHOWN ON THIS MAP, WHICH EASEMENTS SHALL BE SUBJECT TO THE SAME TERMS AND CONDITIONS AS ARE SHOWN IN THAT CERTAIN EASEMENT RECORDED OCTOBER 6, 1980, IN BOOK 13776, PAGE 341, OF OFFICIAL RECORDS OF ORANGE COUNTY. THE SANTA MARGARITA WATER DISTRICT SHALL RESTORE OTHER IMPROVEMENTS OR FACILITIES LOCATED WITHIN THE EASEMENT, IF IT HAS CONSENTED TO THE LOCATION OF SUCH IMPROVEMENTS OR FACILITIES TO THE EXTENT THAT THE EXERCISE OF ITS RIGHTS IN CONNECTION WITH THE EASEMENT IMPACTS OTHER IMPROVEMENTS OR FACILITIES LOCATED WITHIN THE EASEMENT, HOWEVER, IN NO EVENT SHALL SANTA MARGARITA WATER DISTRICT BE RESPONSIBLE FOR THE COST OF RELOCATING ITS FACILITIES IN THE EVENT OF CONFLICTS WITH SUCH OTHER IMPROVEMENTS OR FACILITIES.

WL HOMES LLC, A DELAWARE LIMITED LIABILITY COMPANY
DBA JOHN LAING HOMES

BY: L.J. Edgcomb
L.J. Edgcomb's Division Pres
PRINT NAME PRINT TITLE

BY: Tim McSunas
TIM MCSUNAS DIRECTOR
PRINT NAME PRINT TITLE

RESIDENTIAL FUNDING CORPORATION, A DELAWARE CORPORATION, AS BENEFICIARY UNDER DEED OF TRUST RECORDED FEBRUARY 14, 2000, AS INSTRUMENT NO. 20000079644, OFFICIAL RECORDS OF ORANGE COUNTY.

BY: Michael F. Ripling
MICHAEL F. RIPLING DIRECTOR
PRINT NAME PRINT TITLE

DMB LADERA, L.L.C., A DELAWARE LIMITED LIABILITY COMPANY, BENEFICIARY UNDER A DEED OF TRUST RECORDED JANUARY 28, 2000, AS INSTRUMENT NO. 20000051623 OF OFFICIAL RECORDS OF ORANGE COUNTY.

BY: RANCHO MISSION DIEJO, L.L.C., A-DELAWARE LIMITED LIABILITY COMPANY,
AS AGENT AND/OR MANAGER

BY: Paul Johnson
PAUL JOHNSON Vice President
PRINT NAME PRINT TITLE

NOTARY ACKNOWLEDGEMENT

STATE OF CALIFORNIA)
COUNTY OF ORANGE) SS

ON THIS 8th DAY OF MARCH, 2000, BEFORE ME PERRY M BLOCK
Notary Public, PERSONALLY APPEARED L.J. EDGCOMB AND
TIM MCSUNAS PERSONALLY KNOWN TO ME OR PROVED TO ME ON THE BASIS
OF SATISFACTORY EVIDENCE TO BE THE PERSONS WHOSE NAMES ARE SUBSCRIBED TO THE WITHIN INSTRUMENT
AND ACKNOWLEDGED TO ME THAT THEY EXECUTED THE SAME IN THEIR AUTHORIZED CAPACITIES, AND THAT BY
THEIR SIGNATURES ON THE INSTRUMENT THE PERSONS, OR THE ENTITY UPON BEHALF OF WHICH THE PERSONS
ACTED, EXECUTED THE INSTRUMENT.

WITNESS MY HAND:

MY PRINCIPAL PLACE OF BUSINESS IS IN
ORANGE COUNTY.

MY COMMISSION EXPIRES: 2/10/2004

Perry M Block
NOTARY PUBLIC IN AND FOR SAID STATE
PERRY M. BLOCK
(PRINT NAME)

SURVEYOR'S STATEMENT

I HEREBY STATE THAT THIS MAP CONSISTING OF 6 SHEETS, CORRECTLY REPRESENTS A TRUE AND COMPLETE SURVEY AS SHOWN MADE IN NOVEMBER, 1999; WAS MADE BY ME OR UNDER MY DIRECTION; THAT THE MONUMENTS ARE OF THE CHARACTER AND OCCUPY (OR WILL OCCUPY) THE POSITIONS INDICATED BY SAID MAP; AND THAT SAID MONUMENTS ARE (OR WILL BE) SUFFICIENT TO ENABLE THE SURVEY TO BE RETRACED.




Robert N. Mim Mack
ROBERT N. MIM MACK L.S. 5314
MY LICENSE EXPIRES: 12/31/03

COUNTY SURVEYOR'S STATEMENT

I HEREBY STATE THAT I HAVE EXAMINED THIS MAP AND HAVE FOUND IT TO BE SUBSTANTIALLY IN CONFORMANCE WITH THE TENTATIVE MAP AS FILED WITH, AMENDED AND APPROVED BY THE ORANGE COUNTY SUBDIVISION COMMITTEE; THAT ALL THE PROVISIONS OF THE SUBDIVISION MAP ACT AND COUNTY SUBDIVISION REGULATIONS HAVE BEEN COMPLIED WITH AND I AM SATISFIED THAT SAID MAP IS TECHNICALLY CORRECT.

DATED THIS 26th DAY OF May, 2000.

Robert Jelinek
JOHN CANAS, COUNTY SURVEYOR
Robert Jelinek, Deputy County Surveyor

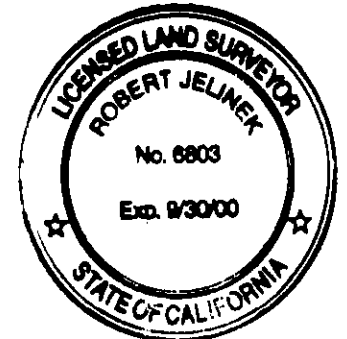

COUNTY TREASURER-TAX COLLECTOR'S CERTIFICATE

STATE OF CALIFORNIA)
COUNTY OF ORANGE) SS

I HEREBY CERTIFY THAT ACCORDING TO THE RECORDS OF MY OFFICE THERE ARE NO LIENS AGAINST THE LAND COVERED BY THIS MAP OR ANY PART THEREOF FOR UNPAID STATE, COUNTY, MUNICIPAL OR LOCAL TAXES OR SPECIAL ASSESSMENTS COLLECTED AS TAXES, EXCEPT TAXES OR SPECIAL ASSESSMENTS COLLECTED AS TAXES NOT YET PAYABLE.

AND DO ALSO HEREBY CERTIFY TO THE RECORDER OF ORANGE COUNTY THAT THE PROVISIONS OF THE SUBDIVISION MAP ACT HAVE BEEN COMPLIED WITH REGARDING DEPOSITS TO SECURE THE PAYMENT OF TAXES OR SPECIAL ASSESSMENTS COLLECTED AS TAXES ON THE LAND COVERED BY THIS MAP.

DATED THIS 9th DAY OF May, 2000.

JOHN M. W. MOORLACH
COUNTY TREASURER-TAX COLLECTOR

BY: John M. W. Moorlach
DEPUTY TREASURER-TAX COLLECTOR

CLERK OF THE BOARD OF SUPERVISORS' CERTIFICATE

STATE OF CALIFORNIA)
COUNTY OF ORANGE) SS

I HEREBY CERTIFY THAT THIS MAP WAS PRESENTED FOR APPROVAL TO THE BOARD OF SUPERVISORS OF ORANGE COUNTY AT A REGULAR MEETING THEREOF HELD ON THE 13th DAY OF June, 2000, AND THAT THEREUPON SAID BOARD DID, BY AN ORDER DULY PASSED AND ENTERED, APPROVE SAID MAP, AND DID ACCEPT ON BEHALF OF THE PUBLIC, SUBJECT TO IMPROVEMENTS; THE DEDICATION FOR STREET PURPOSES OF: HEARTHSIDE ROAD, BRYNWOOD LANE, FRANKLIN WAY AND NEWBURY WAY.


AND DID ALSO ACCEPT ON BEHALF OF THE COUNTY OF ORANGE:

THE EASEMENT FOR STORM DRAIN PURPOSES AS DEDICATED HEREON.

AND DID ALSO APPROVE SUBJECT MAP PURSUANT TO THE PROVISIONS OF SECTION 66436 (a)(3)(A) OF THE SUBDIVISION MAP ACT.

DATED THIS 13th DAY OF June, 2000.

Darlene J. Bloom
DARLENE J. BLOOM
CLERK OF THE BOARD OF SUPERVISORS
OF ORANGE COUNTY, CALIFORNIA

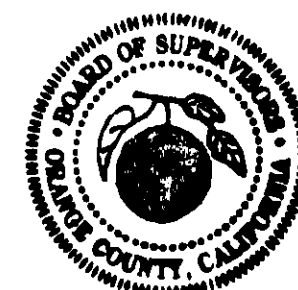

SEE SHEET 2 FOR ADDITIONAL NOTARY ACKNOWLEDGMENTS, SIGNATURE OMISSIONS, ADDITIONAL DECLARATIONS AND SANTA MARGARITA WATER DISTRICT ACCEPTANCE CERTIFICATE AND NOTARY ACKNOWLEDGMENT.

SHEET 2 OF 6 SHEETS
9.542 ACRES
56 LOTS AND LOTS "A",
"B", "C", AND "D"
(ALL OF VESTING TENTATIVE
TRACT NO. 15906)

TRACT NO. 15906

IN THE UNINCORPORATED TERRITORY OF THE
COUNTY OF ORANGE, STATE OF CALIFORNIA

WAGNER HALLADAY, INC.

ROBERT N. MIM MACK L.S. 5314 DATE OF SURVEY: NOVEMBER, 1999

SIGNATURE OMISSIONS

PURSUANT TO SECTION 66436 (a)(3) OF THE SUBDIVISION MAP ACT, THE SIGNATURES OF THE FOLLOWING HAVE BEEN OMITTED:

1. LADERA DEVELOPMENT COMPANY, L.L.C., HOLDER OF OIL, GAS AND MINERAL RIGHTS PER DOCUMENT RECORDED AS INSTRUMENT NO. 19960624029 OF OFFICIAL RECORDS.
2. **DMB LADERA**, L.L.C., HOLDER OF EASEMENTS PER DOCUMENT RECORDED AS INSTRUMENT NO. 20000136880 OF OFFICIAL RECORDS.

FIRE HAZARD NOTIFICATION NOTE

THIS PROJECT IS LOCATED IN STATE RESPONSIBILITY AREA BASED ON MAPPING BY THE STATE OF CALIFORNIA, HOWEVER THIS PROJECT DOES NOT HAVE ANY EXPOSURE TO WILD LAND AREAS BASED UPON OC FIRE AUTHORITY LETTER DATED FEBRUARY 9, 2000 PER ORDINANCE 3959-3960 OF THE COUNTY OF ORANGE.

FIRE PROTECTION AREA NOTE

A TOTAL EXCLUSION FROM THE SPECIAL FIRE PROTECTION AREA HAS BEEN GRANTED BY THE OC FIRE AUTHORITY PER LETTER DATED FEBRUARY 9, 2000 FROM THE OC FIRE AUTHORITY AND THEREFORE, THIS PROJECT IS NO LONGER IN A SPECIAL FIRE PROTECTION AREA PER ORDINANCE 3959-3960 OF THE COUNTY OF ORANGE.

NOTE

PROPERTY MAY BE SUBJECT TO IMPACTS FROM THE PROPOSED FOOTHILL/EASTERN TRANSPORTATION CORRIDORS.

FOOTHILL CIRCULATION PHASING PLAN NOTE

BUILDING PERMIT ISSUANCE SHALL BE PHASED IN ACCORDANCE WITH THE FOOTHILL CIRCULATION PHASING PLAN (FCPP) DEVELOPMENT PHASING PLAN, AND SHALL ALSO BE SUBJECT TO ANY OTHER BOARD OF SUPERVISORS APPROVED GROWTH MANAGEMENT PHASING PLAN PERTAINING TO THE TIMELY PROVISION OF PUBLIC SERVICES AND FACILITIES.

EASEMENT NOTES

- (A) INDICATES EASEMENT FOR STORM DRAIN PURPOSES DEDICATED TO THE COUNTY OF ORANGE.
(B) INDICATES EASEMENT FOR SEWER AND WATER PURPOSES DEDICATED TO THE SANTA MARGARITA WATER DISTRICT.

AUTOMATIC FIRE SPRINKLER NOTE

ALL SINGLE-FAMILY STRUCTURES EXCEEDING 5,500 SQUARE FEET AND ALL STRUCTURES EXCEEDING FIRE DEPARTMENT ACCESS REQUIREMENTS SHALL BE PROTECTED BY AN AUTOMATIC FIRE SPRINKLER SYSTEM.

SANTA MARGARITA WATER DISTRICT CERTIFICATE OF ACCEPTANCE

THE UNDERSIGNED, BEING THE DULY APPOINTED AGENT OF THE SANTA MARGARITA WATER DISTRICT, A PUBLIC CORPORATION IN ORANGE COUNTY, CALIFORNIA, PURSUANT TO ITS RESOLUTION NO. 88-10-2, DOES HEREBY ACCEPT ON BEHALF OF SAID DISTRICT, THE PIPELINE EASEMENTS FOR WATER AND SEWER PURPOSES, AS DEDICATED AND AS SHOWN ON THIS TRACT MAP, AND DOES HEREBY ACCEPT ON BEHALF OF SAID DISTRICT ALL WATER AND WATER RIGHTS, AS DEDICATED ON THIS TRACT MAP, BY AND BETWEEN THE SANTA MARGARITA WATER DISTRICT AND WL HOMES, LLC., AND DOES HEREBY CERTIFY THAT THE GRANTEE CONSENTS TO THE RECORDATION OF SAID TRACT.

BY *Daniel R. Ferons*
DANIEL R. FERONS - CHIEF ENGINEER
SANTA MARGARITA WATER DISTRICT

NOTARY ACKNOWLEDGEMENT

SANTA MARGARITA WATER DISTRICT

STATE OF CALIFORNIA) SS
COUNTY OF ORANGE

ON THIS 3rd DAY OF May, 2000, BEFORE ME ANDREA M. EVANS
Notary Public, PERSONALLY APPEARED DANIEL R. FERONS, PERSONALLY KNOWN TO ME OR PROVED TO ME ON THE BASIS OF SATISFACTORY EVIDENCE TO BE THE PERSON WHOSE NAME IS SUBSCRIBED TO THE WITHIN INSTRUMENT AND ACKNOWLEDGED TO ME THAT HE EXECUTED THE SAME IN HIS AUTHORIZED CAPACITY, AND THAT BY HIS SIGNATURE ON THE INSTRUMENT THE PERSON, OR THE ENTITY UPON BEHALF OF WHICH THE PERSON ACTED, EXECUTED THE INSTRUMENT.

WITNESS MY HAND:

Andrea M. Evans
NOTARY PUBLIC IN AND FOR SAID STATE
ANDREA M. EVANS
(PRINT NAME)

MY PRINCIPAL PLACE OF BUSINESS IS IN
ORANGE COUNTY

MY COMMISSION EXPIRES: 4-8-2004

NOTARY ACKNOWLEDGEMENT

STATE OF CALIFORNIA) SS
COUNTY OF ~~ORANGE~~ Los Angeles

ON THIS 15 DAY OF March, 2000, BEFORE ME Sonia C. Garcia
Notary Public, PERSONALLY APPEARED Michael F. Ripling AND
Sonia C. Garcia PERSONALLY KNOWN TO ME OR PROVED TO ME ON THE BASIS OF SATISFACTORY EVIDENCE TO BE THE PERSONS WHOSE NAMES ARE SUBSCRIBED TO THE WITHIN INSTRUMENT AND ACKNOWLEDGED TO ME THAT ~~SHE~~ THEY EXECUTED THE SAME IN ~~THEIR~~ THEIR AUTHORIZED CAPACITIES, AND THAT BY ~~THEIR~~ THEIR SIGNATURES ON THE INSTRUMENT THE PERSONS, OR THE ENTITY UPON BEHALF OF WHICH THE PERSONS ACTED, EXECUTED THE INSTRUMENT.

WITNESS MY HAND:

MY PRINCIPAL PLACE OF BUSINESS IS IN
Los Angeles COUNTY.

MY COMMISSION EXPIRES: May 9, 2003

Sonia C. Garcia
NOTARY PUBLIC IN AND FOR SAID STATE
SONIA E. GARCIA
(PRINT NAME)

NOTARY ACKNOWLEDGEMENT

STATE OF CALIFORNIA) SS
COUNTY OF ORANGE

ON THIS 19th DAY OF April, 2000, BEFORE ME Tina T. Baker
Notary Public, PERSONALLY APPEARED Paul Johnson AND
Tina T. Baker PERSONALLY KNOWN TO ME OR PROVED TO ME ON THE BASIS OF SATISFACTORY EVIDENCE TO BE THE PERSONS WHOSE NAMES ARE SUBSCRIBED TO THE WITHIN INSTRUMENT AND ACKNOWLEDGED TO ME THAT ~~THEY~~ THEY EXECUTED THE SAME IN ~~THEIR~~ THEIR AUTHORIZED CAPACITIES, AND THAT BY ~~THEIR~~ THEIR SIGNATURES ON THE INSTRUMENT THE PERSONS, OR THE ENTITY UPON BEHALF OF WHICH THE PERSONS ACTED, EXECUTED THE INSTRUMENT.

WITNESS MY HAND:

MY PRINCIPAL PLACE OF BUSINESS IS IN
Orange COUNTY.

MY COMMISSION EXPIRES: 8/29/2000

Tina T. Baker
NOTARY PUBLIC IN AND FOR SAID STATE
Tina T. Baker
(PRINT NAME)

SHEET 3 OF 6 SHEETS
9.542 ACRES
SCALE: 1" = 80'

56 LOTS AND LOTS "A",
"B", "C", AND "D"

(ALL OF VESTING TENTATIVE
TRACT NO. 15906)

TRACT NO. 15906

IN THE UNINCORPORATED TERRITORY OF THE
COUNTY OF ORANGE, STATE OF CALIFORNIA

WAGNER HALLADAY, INC.

ROBERT N. MIM MACK L.S. 5314 DATE OF SURVEY: NOVEMBER, 1999

BOUNDARY CONTROL & SHEET INDEX MAP

BASIS OF BEARINGS

THE BEARINGS SHOWN HEREON ARE BASED ON THE BEARING N69°49'00"W OF THE SOUTHERLY LINE OF FLINTRIDGE AVENUE AS SHOWN ON THE MAP OF TRACT NO. 15813, M.M. 795/01-16, RECORDS OF ORANGE COUNTY.


MONUMENT NOTES:

- INDICATES LOCATION OF 2" IRON PIPE TAGGED "L.S. 5557" OR SPIKE & WASHER STAMPED "L.S. 5557" OR LEAD, TACK & TAG "L.S. 5557" TO BE SET PER TRACT NO. 15813, M.M. 795/01-16, UNLESS OTHERWISE NOTED.
- INDICATES LOCATION OF 2" IRON PIPE TAGGED L.S. 5314 SET PRIOR TO RECORDATION.

2" IRON PIPE TAGGED L.S. 5314 OR SPIKE AND WASHER STAMPED L.S. 5314 IN ASPHALT OR LEAD AND TAG L.S. 5314 IN CONCRETE TO BE SET AT ALL TRACT CORNERS WITHIN 90 DAYS AFTER ACCEPTANCE OF IMPROVEMENTS.

1" IRON PIPE TAGGED L.S. 5314 OR SPIKE AND WASHER STAMPED L.S. 5314 IN ASPHALT OR LEAD AND TAG L.S. 5314 IN CONCRETE TO BE SET AT ALL REAR LOT CORNERS WITHIN 90 DAYS AFTER ACCEPTANCE OF IMPROVEMENTS. LEAD AND TAG L.S. 5314 TO BE SET IN CONCRETE WALK ON A PROJECTION OF THE SIDE LOT LINE AT 0.50' OFFSET, UNLESS OTHERWISE NOTED, FOR FRONT LOT CORNERS WITHIN 90 DAYS AFTER ACCEPTANCE OF IMPROVEMENTS.

1" IRON PIPE TAGGED L.S. 5314 OR SPIKE AND WASHER STAMPED L.S. 5314 IN ASPHALT OR LEAD AND TAG L.S. 5314 IN CONCRETE TO BE SET AT ALL CENTERLINE INTERSECTIONS, B.C.'S, E.C.'S AND ALL OTHER CENTERLINE POINTS OF CONTROL WITHIN 90 DAYS AFTER ACCEPTANCE OF IMPROVEMENTS.

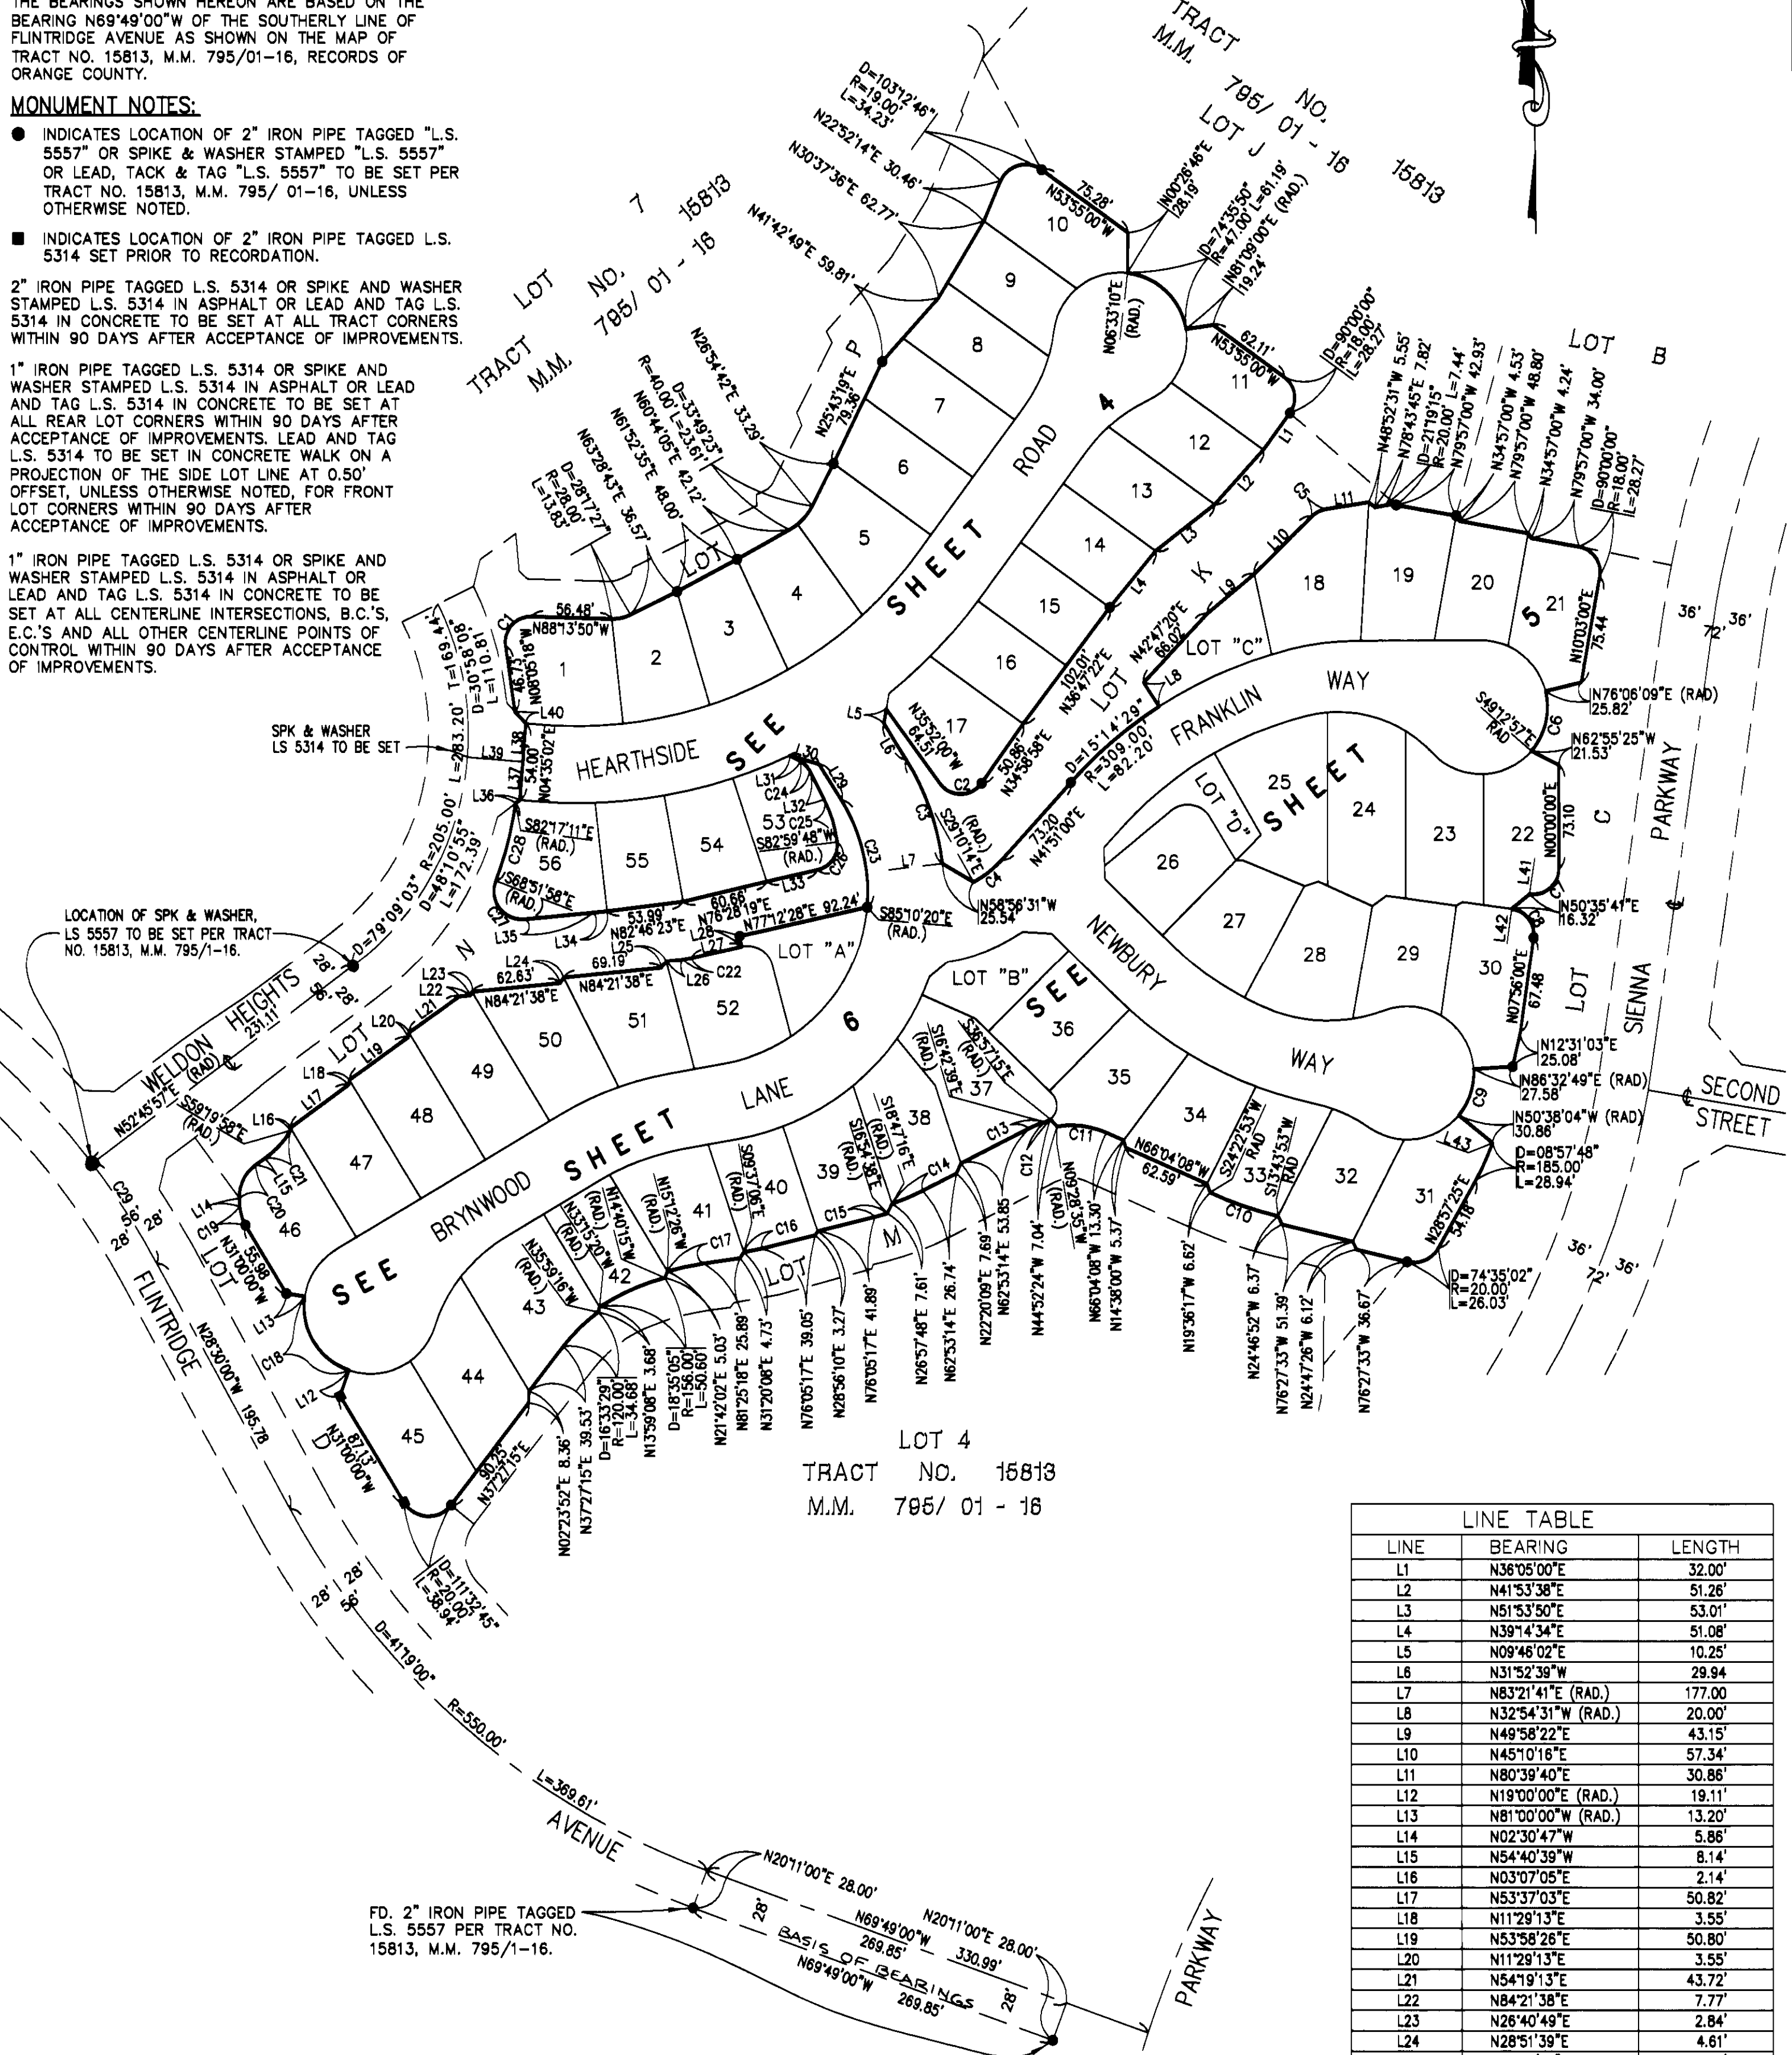

CURVE TABLE						
CURVE	DELTA	RADIUS	LENGTH	CURVE	DELTA	LENGTH
C1	99°51'28"	18.00'	31.37'	C16	04°17'37"	170.00'
C2	109°09'02"	18.00'	34.29'	C17	06°37'44"	226.00'
C3	25°14'20"	177.00'	77.97'	C18	80°00'00"	47.00'
C4	18°58'46"	76.00'	25.18'	C19	28°29'13"	28.00'
C5	35°29'24"	18.00'	11.15'	C20	57°11'26"	27.00'
C6	54°40'54"	47.00'	44.86'	C21	24°00'37"	64.00'
C7	97°56'00"	18.00'	30.77'	C22	07°09'10"	51.00'
C8	90°00'00"	18.00'	28.27'	C23	36°42'19"	123.00'
C9	42°49'07"	47.00'	35.12'	C24	34°49'46"	15.00'
C10	10°39'00"	273.00'	50.74'	C25	19°48'56"	91.00'
C11	33°24'27"	61.00'	35.57'	C26	84°12'40"	18.00'
C12	20°14'36"	12.00'	4.24'	C27	116°46'24"	20.00'
C13	10°24'07"	66.00'	11.98'	C28	13°25'13"	241.00'
C14	08°19'30"	163.00'	23.68'	C29	8°44'03"	550.00'
C15	02°59'55"	169.00'	8.84'			

LINE TABLE		
LINE	BEARING	LENGTH
L1	N36°05'00"E	32.00'
L2	N41°53'38"E	51.26'
L3	N51°53'50"E	53.01'
L4	N39°14'34"E	51.08'
L5	N09°46'02"E	10.25'
L6	N31°52'39"W	29.94'
L7	N83°21'41"E (RAD.)	177.00'
L8	N32°54'31"W (RAD.)	20.00'
L9	N49°58'22"E	43.15'
L10	N45°10'16"E	57.34'
L11	N80°39'40"E	30.86'
L12	N19°00'00"E (RAD.)	19.11'
L13	N81°00'00"W (RAD.)	13.20'
L14	N02°30'47"W	5.86'
L15	N54°40'39"W	8.14'
L16	N03°07'05"E	2.14'
L17	N53°37'03"E	50.82'
L18	N11°29'13"E	3.55'
L19	N53°58'26"E	50.80'
L20	N11°29'13"E	3.55'
L21	N54°19'13"E	43.72'
L22	N84°21'38"E	7.77'
L23	N26°40'49"E	2.84'
L24	N28°51'39"E	4.61'
L25	N34°56'17"E	6.06'
L26	N84°21'38"E	11.41'
L27	N77°12'28"E	36.54'
L28	N12°47'32"W	7.60'
L29	N31°52'39"W	29.94'
L30	N73°31'21"W	21.26'
L31	N61°38'54"W	8.50'
L32	N26°49'08"W	22.74'
L33	N77°12'28"W	36.57'
L34	N84°20'13"W	9.40'
L35	N84°21'38"E	48.67'
L36	N52°22'31"E	3.80'
L37	N04°35'02"E	27.00'
L38	N04°35'02"E	27.00'
L39	N85°24'58"W (RAD.)	39.24'
L40	N43°12'28"W	11.28'
L41	N07°56'00"W (RAD.)	18.00'
L42	N07°56'00"E (RAD.)	18.00'
L43	N70°00'23"E (RAD.)	185.00'

SHEET 4 OF 6 SHEETS
9.542 ACRES
SCALE: 1" = 40'
56 LOTS AND LOTS "A",
"B", "C", AND "D"

TRACT NO. 15906
IN THE UNINCORPORATED TERRITORY OF THE
COUNTY OF ORANGE, STATE OF CALIFORNIA

(ALL OF VESTING TENTATIVE
TRACT NO. 15906)


WAGNER HALLADAY, INC.
ROBERT N. MIM MACK L.S. 5314 DATE OF SURVEY: NOVEMBER, 1999

NOTES:

SEE SHEET 2 FOR EASEMENT NOTES.
SEE SHEET 3 FOR BASIS OF BEARINGS, MONUMENT NOTES, BOUNDARY
CONTROL, AND INDEX MAP.
LETTERED LOTS "A", "B", "C" AND "D" ARE FOR LANDSCAPING AND OPEN
SPACE PURPOSES AND ARE NOT SEPARATE BUILDING SITES.

LINE TABLE		
LINE	BEARING	LENGTH
L1	N43°12'28"W	11.28'
L2	N36°05'00"E	14.36'
L3	N36°05'00"E	12.00'
L4	N30°37'36"E	12.54'
L5	N09°46'02"E	11.01'
L6	N09°46'02"E	10.25'
L7	N86°53'00"E	18.60'
L8	N01°48'30"W	12.71'
L9	N01°48'30"W	9.38'
L10	N86°07'27"W	20.16'
L11	N50°27'05"E	16.41'
L12	N37°27'15"E	12.65'
L13	N37°27'15"E	26.88'
L14	N02°23'52"E	8.36'
L15	N37°27'15"E	11.18'
L16	N02°30'47"W	5.86'
L17	N54°40'39"E	8.14'
L18	N59°00'00"E	8.97'
L19	N84°21'38"E	11.41'
L20	N61°38'54"W	8.50'
L21	N26°49'08"W	22.74'
L22	N84°20'13"E	9.40'
L23	N52°22'31"E	3.80'
L24	S08°41'50"E RAD.	124.00'
L25	S35°09'42"E RAD.	124.00'
L26	N83°21'41"E RAD.	177.00'
L27	S25°10'03"E RAD.	352.00'
L28	S38°35'16"E RAD.	352.00'
L29	S79°32'48"E RAD.	150.00'

CURVE TABLE			
Curve	Delta	Radius	Length
C1	99°51'28"	18.00	31.37
C2	09°56'57"	40.00	6.95
C3	23°52'26"	40.00	16.67
C4	33°49'23"	40.00	23.61
C5	09°12'44"	112.00	18.01
C6	25°07'14"	47.00	20.61
C7	17°12'26"	112.00	33.64
C8	11°50'27"	112.00	23.14
C9	00°35'11"	352.00	3.60
C10	109°09'02"	18.00	34.29
C11	18°58'46"	76.00	25.18
C12	02°24'30"	309.00	12.99
C13	24°33'48"	47.00	20.15
C14	15°21'42"	91.00	24.40
C15	09°34'30"	91.00	15.21
C16	37°50'24"	18.00	11.89
C17	98°23'40"	18.00	30.91
C18	03°29'16"	223.00	13.58
C19	11°36'19"	112.00	22.69
C20	32°15'34"	47.00	26.46
C21	14°57'31"	112.00	29.24
C22	07°45'46"	112.00	15.17
C23	98°30'45"	12.00	20.63
C24	02°20'47"	277.00	11.35
C25	04°36'19"	177.00	14.23
C26	20°14'36"	12.00	4.24
C27	10°24'07"	66.00	11.98
C28	08°19'30"	163.00	23.68
C29	02°59'55"	169.00	8.84
C30	04°17'37"	170.00	12.74
C31	06°37'44"	226.00	26.15
C32	02°32'04"	173.00	7.65
C33	21°02'06"	112.00	41.12
C34	13°14'04"	112.00	25.87
C35	08°29'39"	112.00	16.60
C36	20°30'38"	112.00	40.09
C37	111°32'45"	20.00	38.94
C38	28°29'13"	28.00	13.92
C39	57°11'26"	27.00	26.95
C40	07°09'10"	51.00	6.37
C41	88°18'28"	18.00	27.74
C42	34°49'46"	15.00	9.12
C43	19°48'56"	91.00	31.47
C44	84°12'40"	18.00	26.46
C45	116°46'24"	20.00	40.76

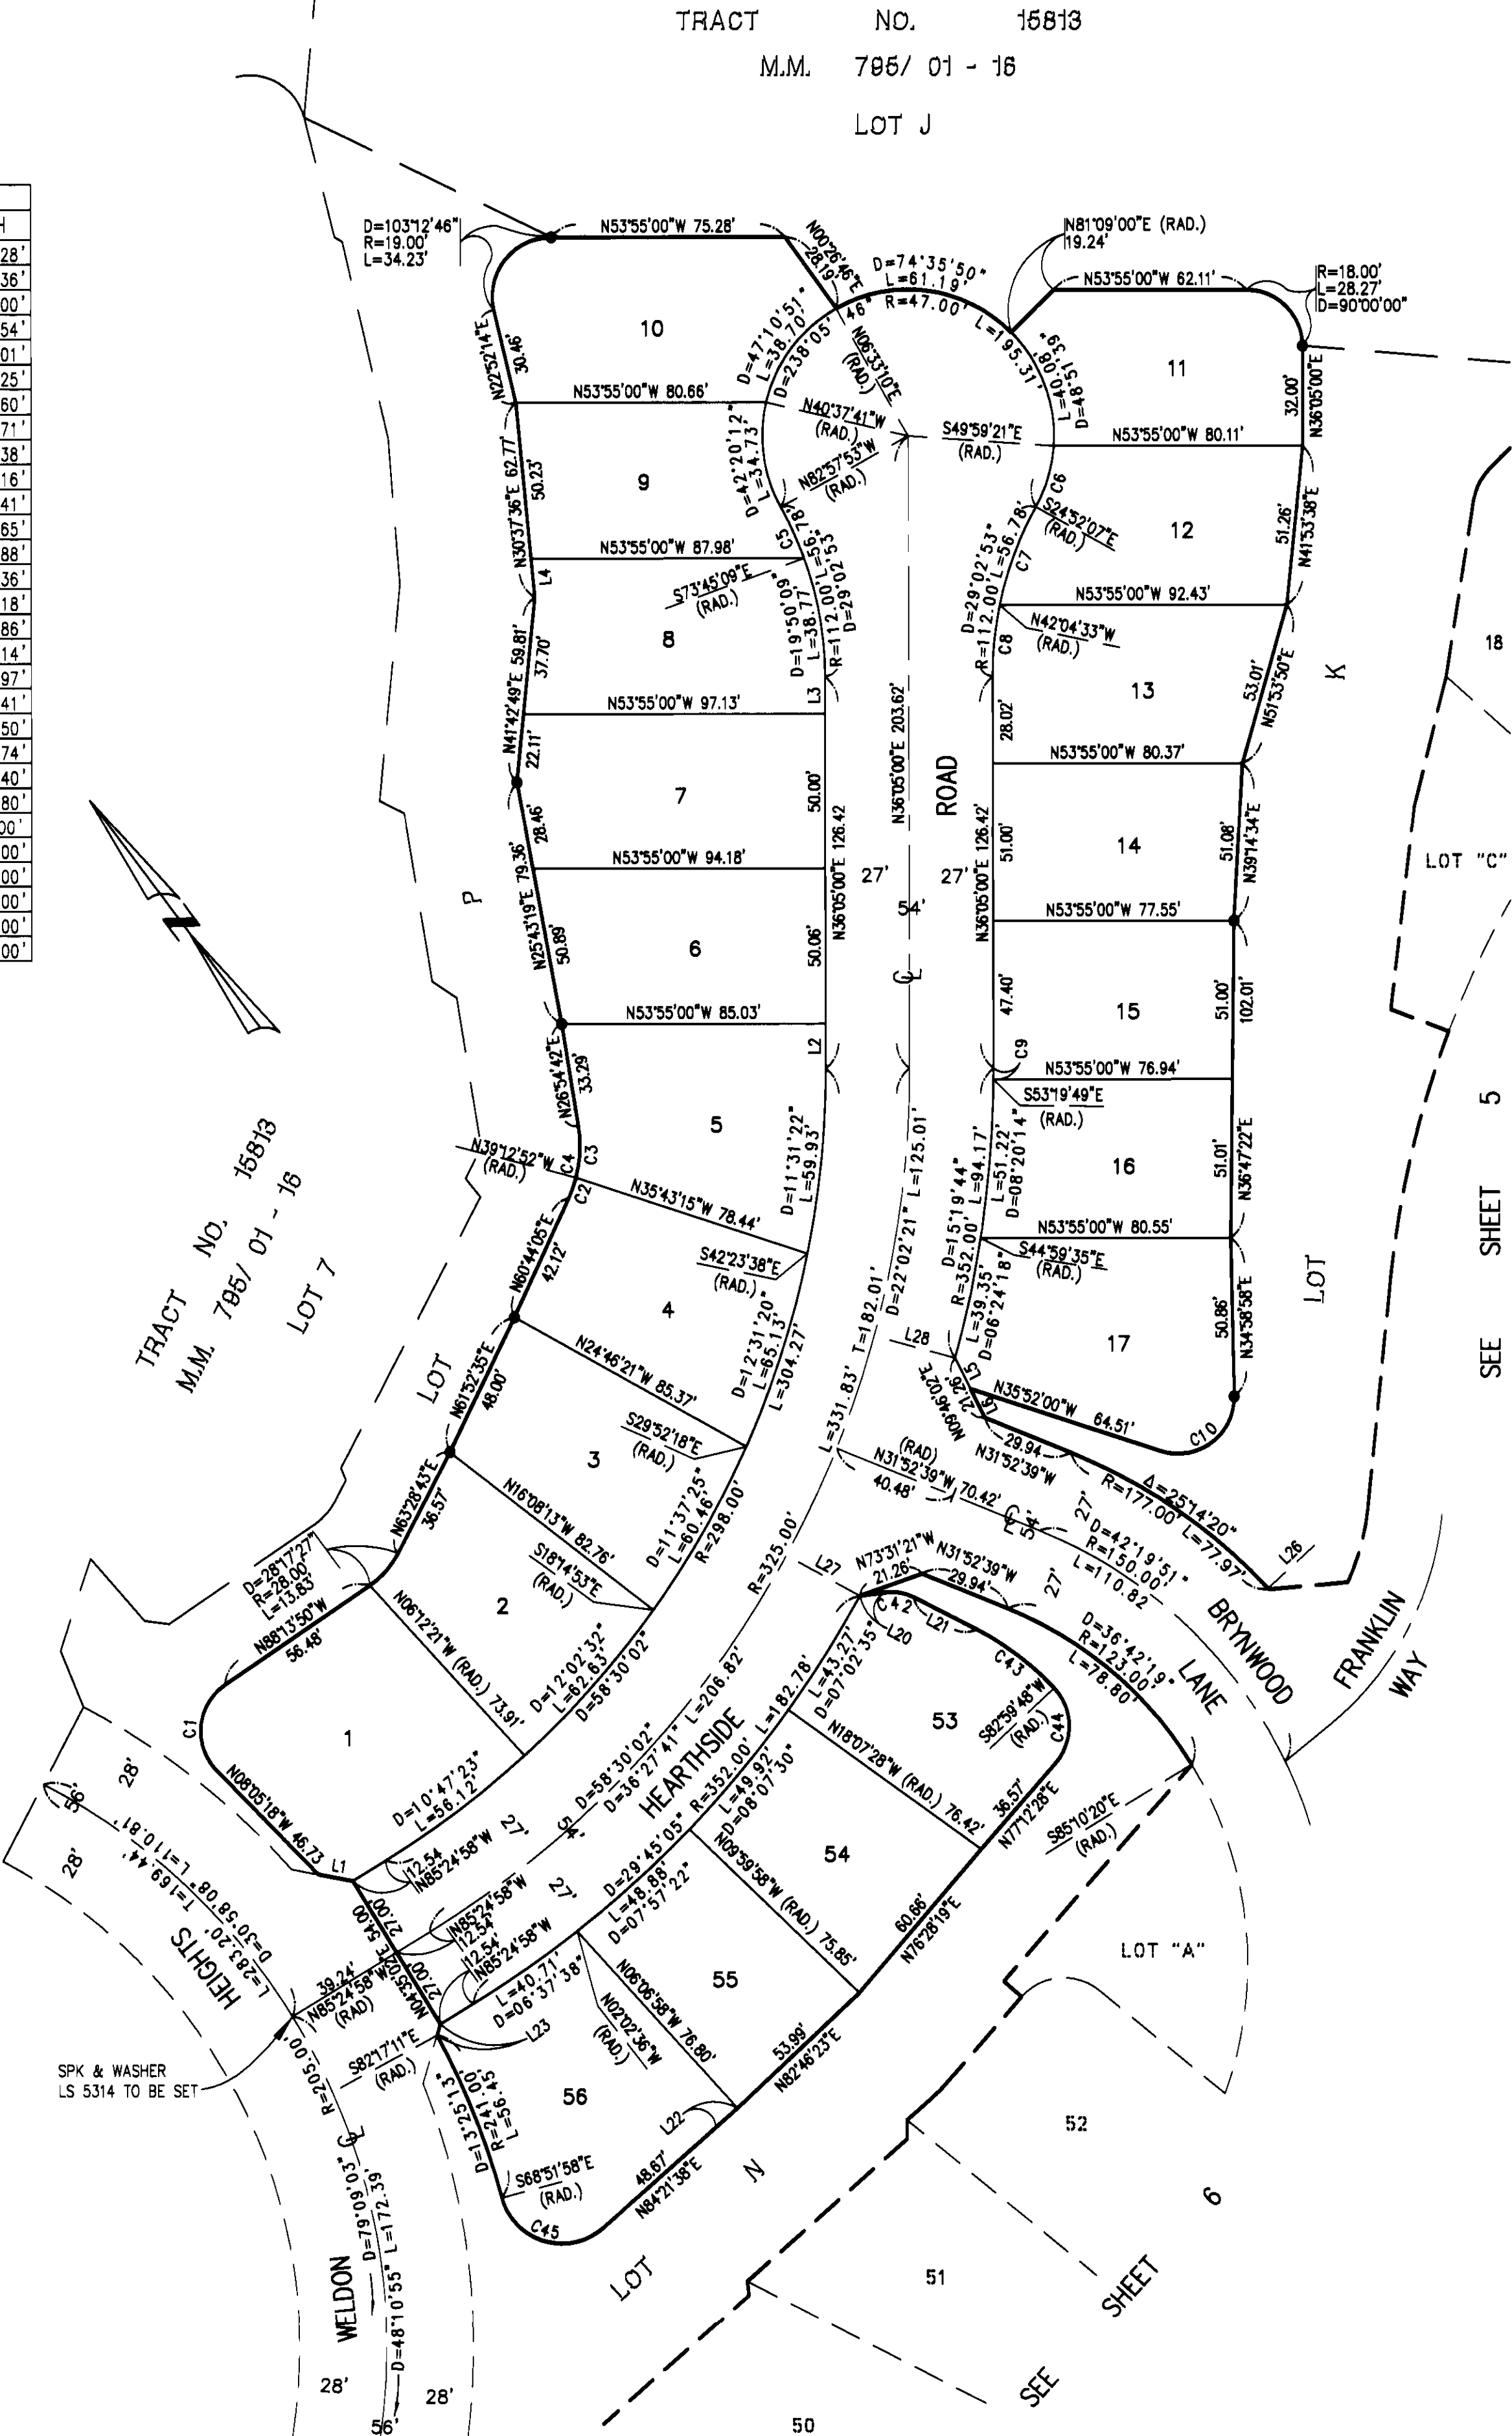

SHEET 5 OF 6 SHEETS
9.542 ACRES
SCALE: 1" = 40'
56 LOTS AND LOTS "A",
"B", "C", AND "D"
(ALL OF VESTING TENTATIVE
TRACT NO. 15906)

TRACT NO. 15906

IN THE UNINCORPORATED TERRITORY OF THE
COUNTY OF ORANGE, STATE OF CALIFORNIA

WAGNER HALLADAY, INC.

ROBERT N. MIM MACK L.S. 5314 DATE OF SURVEY: NOVEMBER, 1999

CURVE TABLE			
Curve	Delta	Radius	Length
C1	99°51'28"	18.00	31.37
C2	09°56'57"	40.00	6.95
C3	23°52'26"	40.00	16.67
C4	33°49'23"	40.00	23.61
C5	09°12'44"	112.00	18.01
C6	25°07'14"	47.00	20.61
C7	17°12'26"	112.00	33.64
C8	11°50'27"	112.00	23.14
C9	00°35'11"	352.00	3.60
C10	109°09'02"	18.00	34.29
C11	18°58'46"	76.00	25.18
C12	02°24'30"	309.00	12.99
C13	24°33'52"	47.00	20.15
C14	15°21'42"	91.00	24.40
C15	09°34'30"	91.00	15.21
C16	NOT USED		
C17	98°23'40"	18.00	30.91
C18	03°29'16"	223.00	13.58
C19	11°36'19"	112.00	22.69
C20	32°15'34"	47.00	26.46
C21	14°57'31"	112.00	29.24
C22	07°45'46"	112.00	15.17
C23	98°30'45"	12.00	20.63
C24	02°20'47"	277.00	11.35
C25	04°36'19"	177.00	14.23
C26	20°14'36"	12.00	4.24
C27	10°24'07"	66.00	11.98
C28	08°19'30"	163.00	23.68
C29	02°59'55"	169.00	8.84
C30	04°17'37"	170.00	12.74
C31	06°37'44"	226.00	26.15
C32	02°32'04"	173.00	7.65
C33	21°02'06"	112.00	41.12
C34	13°14'04"	112.00	25.87
C35	08°29'39"	112.00	16.60
C36	20°30'38"	112.00	40.09
C37	111°32'45"	20.00	38.94
C38	28°29'13"	28.00	13.92
C39	57°11'26"	27.00	26.95
C40	07°09'10"	51.00	6.37
C41	88°18'28"	18.00	27.74
C42	34°49'46"	15.00	9.12
C43	19°48'56"	91.00	31.47
C44	84°12'40"	18.00	26.46
C45	116°46'24"	20.00	40.76


LINE TABLE		
LINE	BEARING	LENGTH
L1	N43°12'28"W	11.28'
L2	N36°05'00"E	14.36'
L3	N36°05'00"E	12.00'
L4	N30°37'36"E	12.54'
L5	N09°46'02"E	11.01'
L6	N09°46'02"E	10.25'
L7	N88°53'00"E	18.60'
L8	N01°48'30"W	12.71'
L9	N01°48'30"W	9.38'
L10	N86°07'27"W	20.16'
L11	N50°27'05"E	16.41'
L12	N37°27'15"E	12.65'
L13	N37°27'15"E	26.88'
L14	N02°23'52"E	8.36'
L15	N37°27'15"E	11.18'
L16	N02°30'47"W	5.86'
L17	N54°40'39"E	8.14'
L18	N59°00'00"E	8.97'
L19	N84°21'38"E	11.41'
L20	N61°38'54"W	8.50'
L21	N26°49'08"W	22.74'
L22	N84°20'13"E	9.40'
L23	N52°22'31"E	3.80'
L24	S08°41'50"E RAD.	124.00'
L25	S35°09'42"E RAD.	124.00'
L26	N83°21'41"E RAD.	177.00'
L27	S25°10'03"E RAD.	352.00'
L28	S38°35'16"E RAD.	352.00'
L29	S79°32'48"E RAD.	150.00'

NOTES:

SEE SHEET 2 FOR EASEMENT NOTES.

SEE SHEET 3 FOR BASIS OF BEARINGS, MONUMENT NOTES, BOUNDARY CONTROL, AND INDEX MAP.

LETTERED LOTS "A", "B", "C" AND "D" ARE FOR LANDSCAPING AND OPEN SPACE PURPOSES AND ARE NOT SEPARATE BUILDING SITES.

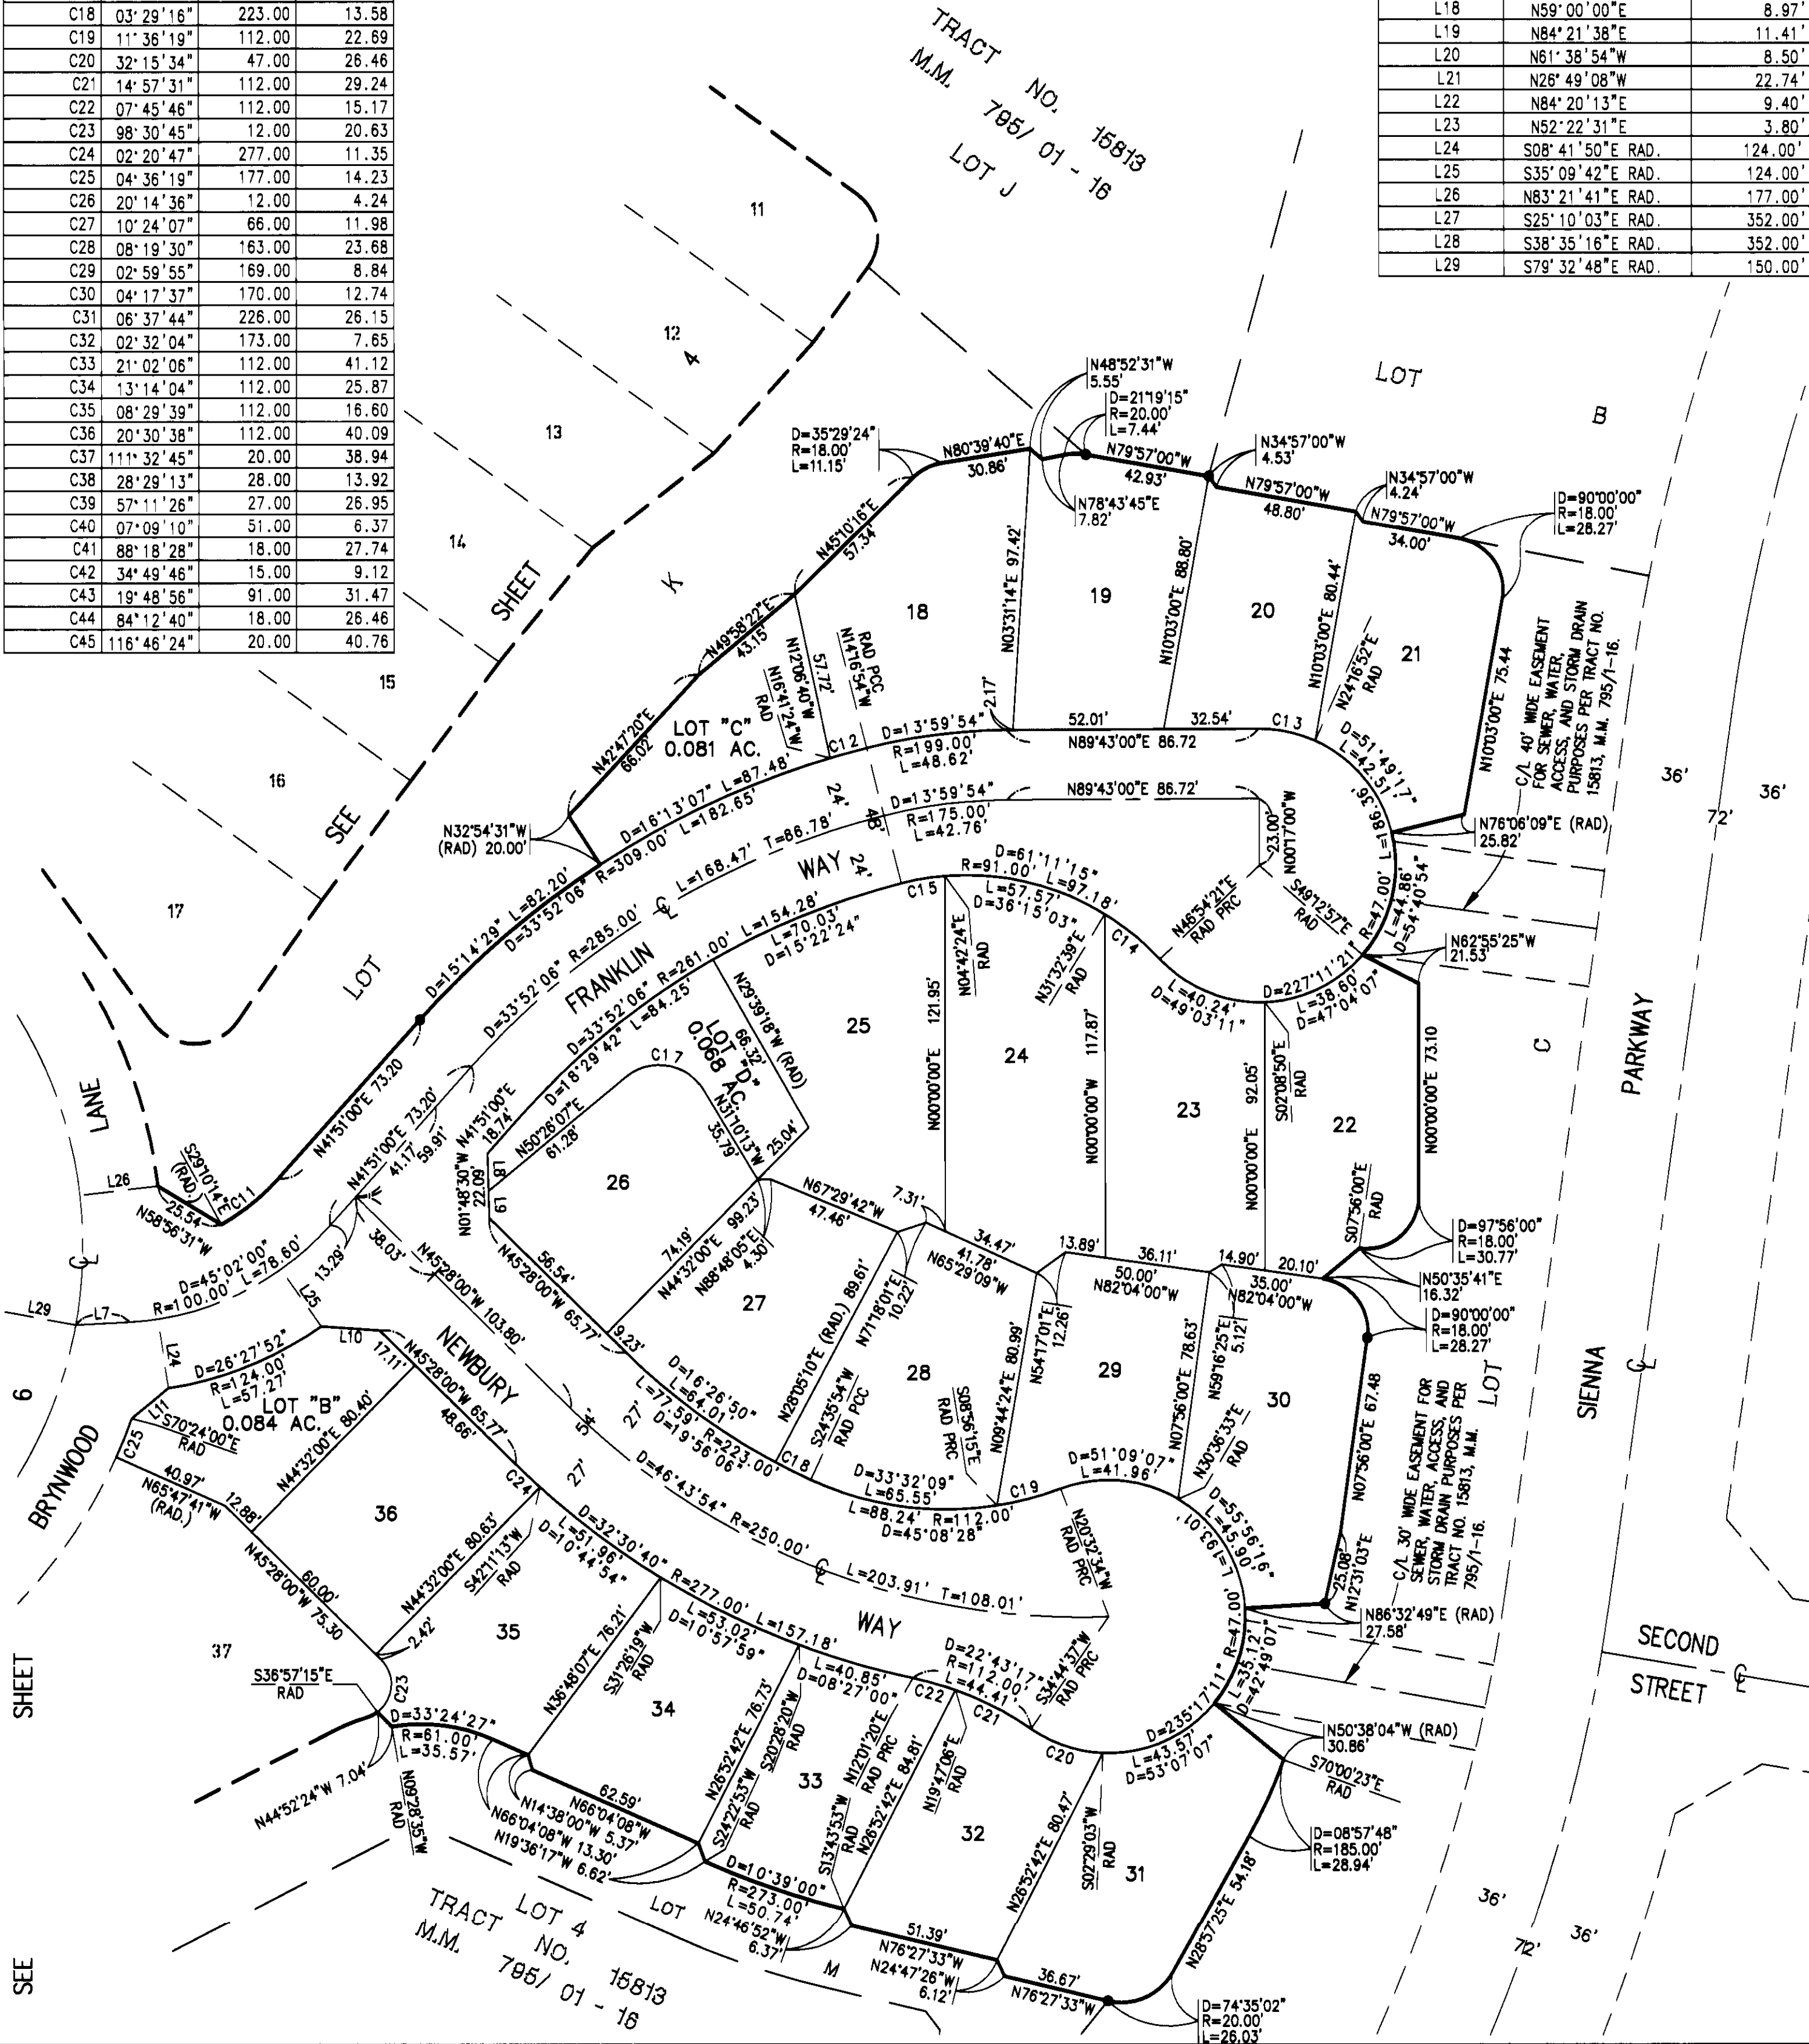

SHEET 6 OF 6 SHEETS
9.542 ACRES
SCALE: 1"=40'
56 LOTS AND LOTS "A",
"B", "C", AND "D"
(ALL OF VESTING TENTATIVE
TRACT NO. 15906)


TRACT NO. 15906
IN THE UNINCORPORATED TERRITORY OF THE
COUNTY OF ORANGE, STATE OF CALIFORNIA

WAGNER HALLADAY, INC.

ROBERT N. MIM MACK L.S. 5314 DATE OF SURVEY: NOVEMBER, 1999

SEE SHEET 4

NOTES:
SEE SHEET 2 FOR EASEMENT NOTES.
SEE SHEET 3 FOR BASIS OF BEARINGS, MONUMENT NOTES, BOUNDARY
CONTROL, AND INDEX MAP.
LETTERED LOTS "A", "B", "C" AND "D" ARE FOR LANDSCAPING AND OPEN
SPACE PURPOSES AND ARE NOT SEPARATE BUILDING SITES.

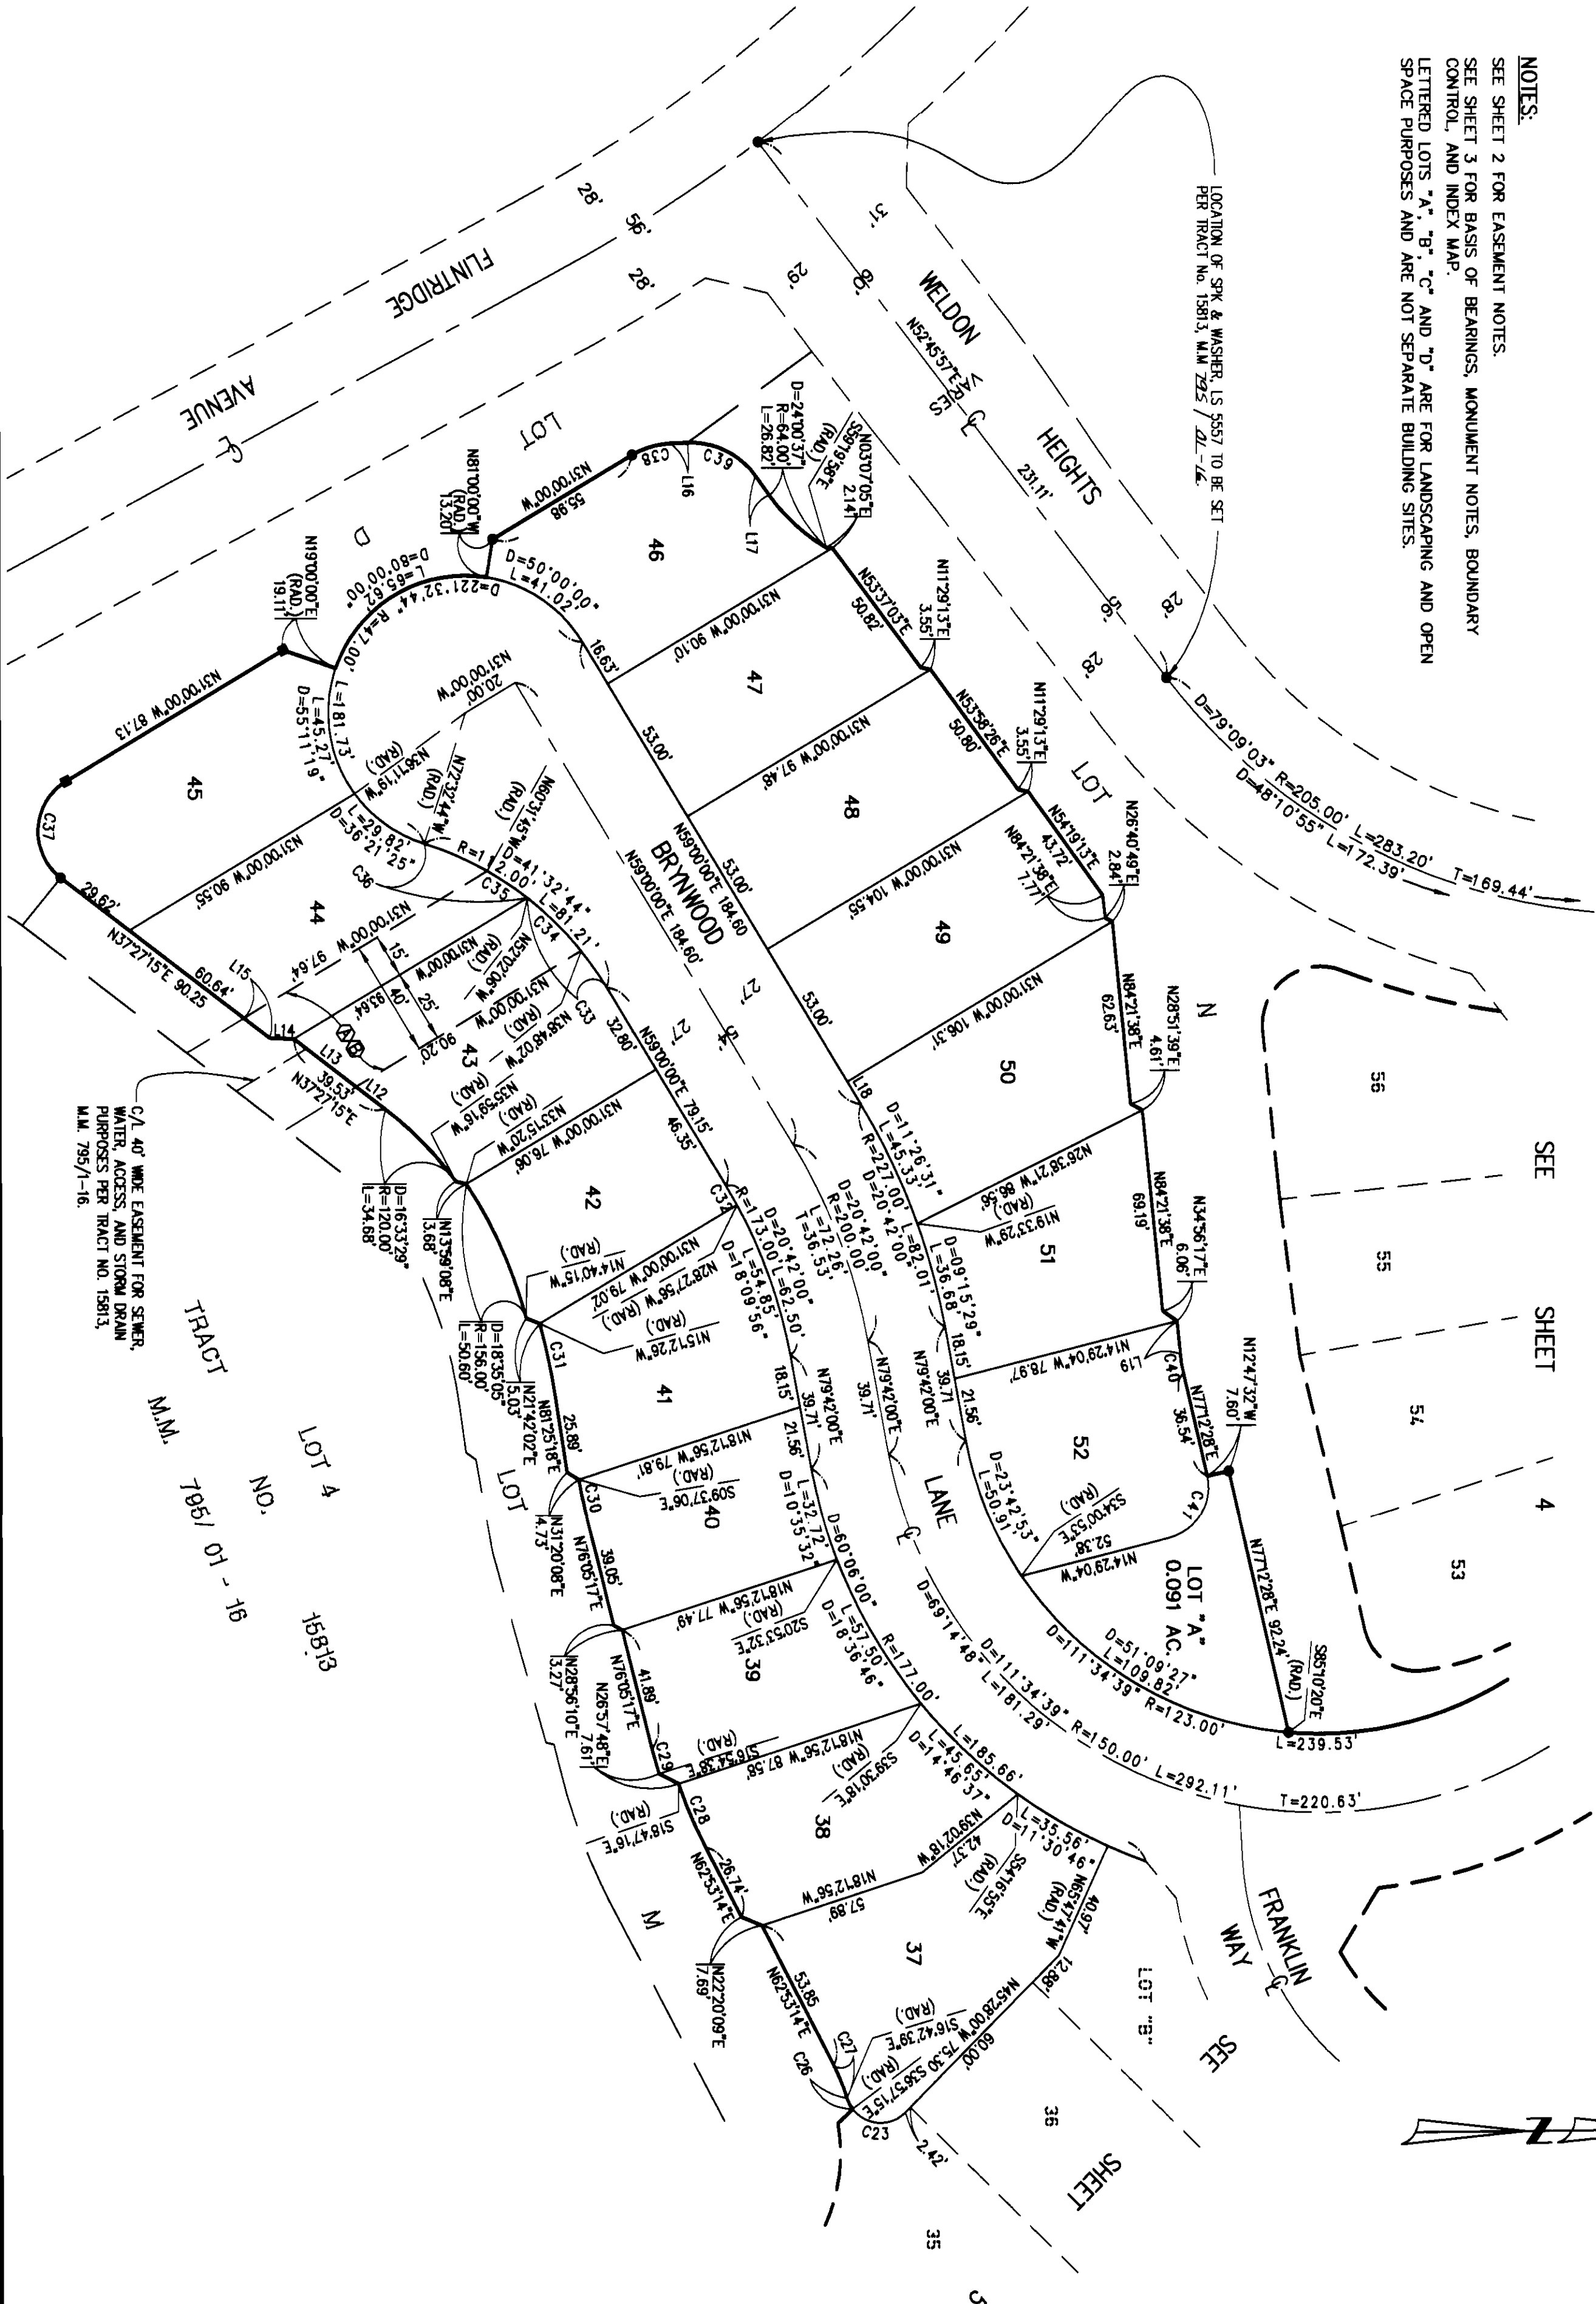

CURVE TABLE			
Curve	Delta	Radius	Length
C1	99°51'28"	18.00	31.37
C2	09°56'57"	40.00	6.95
C3	23°52'26"	40.00	16.67
C4	33°49'23"	40.00	23.61
C5	09°12'44"	112.00	18.01
C6	25°07'14"	47.00	20.61
C7	17°12'26"	112.00	33.64
C8	1°50'27"	112.00	23.14
C9	00°35'11"	352.00	3.60
C10	109°09'02"	18.00	34.29
C11	18°58'46"	76.00	25.18
C12	02°24'30"	309.00	12.99
C13	24°33'48"	47.00	20.15
C14	15°21'42"	91.00	24.40
C15	09°34'30"	91.00	15.21
C16	37°50'24"	18.00	11.89
C17	98°23'40"	18.00	30.91
C18	03°29'16"	223.00	13.58
C19	1°36'19"	112.00	22.69
C20	32°15'34"	47.00	26.46
C21	14°57'31"	112.00	29.24
C22	07°45'46"	112.00	15.17
C23	98°30'45"	12.00	20.63
C24	02°20'47"	277.00	11.35
C25	04°36'19"	177.00	14.23
C26	20°14'36"	12.00	4.24
C27	10°24'07"	66.00	11.96
C28	08°19'30"	163.00	23.68
C29	02°59'55"	169.00	8.84
C30	04°17'37"	170.00	12.74
C31	06°37'44"	226.00	26.15
C32	02°32'04"	173.00	7.65
C33	2°02'06"	112.00	41.12
C34	13°14'04"	112.00	25.87
C35	08°29'38"	112.00	16.60
C36	20°30'38"	112.00	40.09
C37	11°32'45"	20.00	38.94
C38	28°29'13"	28.00	13.92
C39	57°11'26"	27.00	26.95
C40	07°09'10"	51.00	6.37
C41	88°18'28"	18.00	27.74
C42	34°49'46"	15.00	9.12
C43	19°48'56"	91.00	31.47
C44	84°12'40"	18.00	26.46
C45	116°46'24"	20.00	40.76

LINE TABLE		
LINE	BEARING	LENGTH
L1	M43°12'28"W	11.28'
L2	M66°05'00"E	14.36'
L3	M36°05'00"E	12.00'
L4	M30°37'36"E	12.54'
L5	M09°46'02"E	11.01'
L6	M09°46'02"E	10.25'
L7	M86°53'00"E	18.60'
L8	N01°48'30"W	12.71'
L9	N01°48'30"W	9.38'
L10	M86°07'27"W	20.16'
L11	M50°27'05"E	16.41'
L12	M57°27'15"E	12.65'
L13	M37°27'15"E	26.88'
L14	N02°23'52"E	8.36'
L15	M37°27'15"E	11.18'
L16	N02°30'47"W	5.86'
L17	M54°40'39"E	8.14'
L18	M59°00'00"E	8.97'
L19	M84°21'38"E	11.41'
L20	M61°38'54"W	8.50'
L21	M26°49'08"W	22.74'
L22	M52°22'31"E	9.40'
L23	S08°41'50"E RAD.	124.00'
L24	S35°09'42"E RAD.	124.00'
L25	M83°21'41"E RAD.	177.00'
L26	S25°10'03"E RAD.	352.00'
L27	S38°35'16"E RAD.	352.00'
L28	S79°32'48"E RAD.	150.00'
L29		