

SHEET 1 OF 3 SHEETS

4.176 ACRES GROSS
(ALL OF VESTING TENTATIVE
TRACT NO. 15907)
LOTS: 28 NUMBERED
1 LETTERED LOT

BLOCK MODULE
5157 03-05

TRACT NO. 15907

IN THE UNINCORPORATED TERRITORY OF THE COUNTY OF ORANGE, STATE OF CALIFORNIA

BEING A SUBDIVISION OF LOT 4 OF TRACT NO. 15813 AS SHOWN ON THE MAP FILED IN
BOOK 795, PAGES 1 THROUGH 16 OF MISCELLANEOUS MAPS, IN THE OFFICE OF THE
COUNTY RECORDER OF SAID ORANGE COUNTY.

JAMES R. CRAWFORD L.S. 4965



DATE OF SURVEY: JANUARY, 2000

ACCEPTED AND FILED AT THE
REQUEST OF
FIRST AMERICAN TITLE INSURANCE COMPANY
DATE AUGUST 25, 2000
TIME 10:45 AM FEE \$11.00
INSTRUMENT # 20000444581
BOOK 805 PAGE 26-28 M/M
GARY L. GRANVILLE
COUNTY CLERK RECORDER
BY [Signature] DEPUTY

OWNERSHIP CERTIFICATE:

WE THE UNDERSIGNED, BEING ALL PARTIES HAVING ANY RECORD TITLE INTEREST IN THE LAND COVERED BY THIS MAP, DO HEREBY CONSENT TO THE PREPARATION AND RECORDATION OF SAID MAP AS SHOWN WITHIN THE DISTINCTIVE BORDER LINE. WE ALSO HEREBY DEDICATE TO THE PUBLIC FOR STREET PURPOSES: MINFORD CIRCLE AND PICKERING CIRCLE.

WE ALSO HEREBY DEDICATE TO THE COUNTY OF ORANGE THE EASEMENT FOR STORM DRAIN PURPOSES AS SHOWN HEREON.

WE ALSO HEREBY DEDICATE TO THE SANTA MARGARITA WATER DISTRICT THE EASEMENT FOR SEWER AND WATER LINE PURPOSES AS SHOWN HEREON WHICH EASEMENT SHALL BE SUBJECT TO THE SAME TERMS AND CONDITIONS AS ARE SHOWN IN THAT CERTAIN EASEMENT RECORDED OCTOBER 6, 1980, IN BOOK 13776, PAGE 341 OF OFFICIAL RECORDS OF THE COUNTY OF ORANGE. THE SANTA MARGARITA WATER DISTRICT SHALL RESTORE OTHER IMPROVEMENTS OR FACILITIES LOCATED WITHIN THE EASEMENT, IF IT HAS CONSENTED TO THE LOCATION OF SUCH IMPROVEMENTS OR FACILITIES TO THE EXTENT THAT THE EXERCISE OF ITS RIGHTS IN CONNECTION WITH THE EASEMENT IMPACTS OTHER IMPROVEMENTS OR FACILITIES LOCATED WITHIN THE EASEMENT, HOWEVER, IN NO EVENT SHALL SANTA MARGARITA WATER DISTRICT BE RESPONSIBLE FOR THE COST OF RELOCATING ITS FACILITIES IN THE EVENT OF CONFLICTS WITH SUCH OTHER IMPROVEMENTS OR FACILITIES.

RESTON ASSOCIATES, L.L.C., A DELAWARE LIMITED LIABILITY COMPANY

BY: PH INSTITUTIONAL VENTURES, A CALIFORNIA CORPORATION,
ITS MANAGING MEMBER

[Signature]
PRINT NAME: THOMAS J. MITCHELL
PRINT TITLE: SENIOR VICE PRESIDENT

[Signature]
PRINT NAME: BRIAN DOYLE
PRINT TITLE: ASSISTANT SECRETARY

DMB LADERA, LLC, A DELAWARE LIMITED LIABILITY COMPANY, BENEFICIARY UNDER A DEED OF TRUST RECORDED FEBRUARY 23, 2000 AS INSTRUMENT NO. 20000095518 OF OFFICIAL RECORDS.

BY: RANCHO MISSION VIEJO, L.L.C., A DELAWARE LIMITED LIABILITY COMPANY
AS AGENT OR MANAGER

[Signature]
PRINT NAME: PAUL JOHNSON
PRINT TITLE: VICE PRESIDENT OF COMMUNITY DEVELOPMENT

NOTARY ACKNOWLEDGEMENT FOR RESTON ASSOCIATES, LLC:

STATE OF CALIFORNIA }
COUNTY OF ORANGE } SS

ON JUNE 22, 2000, BEFORE ME, ROSE S. GONZALEZ A NOTARY PUBLIC IN AND FOR SAID STATE PERSONALLY APPEARED THOMAS J. MITCHELL AND BRIAN DOYLE PERSONALLY KNOWN TO ME (OR PROVED TO ME ON THE BASIS OF SATISFACTORY EVIDENCE) TO BE THE PERSONS WHOSE NAMES ARE SUBSCRIBED TO THE WITHIN INSTRUMENT AND ACKNOWLEDGED TO ME THAT THEY EXECUTED THE SAME IN THEIR AUTHORIZED CAPACITIES AND THAT BY THEIR SIGNATURES ON THE INSTRUMENT THE PERSONS, OR THE ENTITY UPON BEHALF OF WHICH THE PERSONS ACTED EXECUTED THE INSTRUMENT.

WITNESS MY HAND:

[Signature]
NOTARY PUBLIC IN AND FOR SAID STATE
ROSE S. GONZALEZ
(NAME PRINTED)

MY PRINCIPAL PLACE OF BUSINESS IS
IN ORANGE COUNTY
MY COMMISSION EXPIRES: MARCH 1, 2008

NOTARY ACKNOWLEDGEMENT FOR DMB LADERA, LLC:

STATE OF CALIFORNIA }
COUNTY OF ORANGE } SS

ON JULY 6, 2000, BEFORE ME, JEANNINE CARTA-HANSON A NOTARY PUBLIC IN AND FOR SAID STATE PERSONALLY APPEARED PAUL JOHNSON PERSONALLY KNOWN TO ME (OR PROVED TO ME ON THE BASIS OF SATISFACTORY EVIDENCE) TO BE THE PERSON WHOSE NAME IS SUBSCRIBED TO THE WITHIN INSTRUMENT AND ACKNOWLEDGED TO ME THAT HE EXECUTED THE SAME IN HIS AUTHORIZED CAPACITY AND THAT BY HIS SIGNATURE ON THE INSTRUMENT THE PERSON, OR THE ENTITY UPON BEHALF OF WHICH THE PERSON ACTED EXECUTED THE INSTRUMENT.

WITNESS MY HAND:

[Signature]
NOTARY PUBLIC IN AND FOR SAID STATE
JEANNINE CARTA-HANSON
(NAME PRINTED)

MY PRINCIPAL PLACE OF BUSINESS IS
IN ORANGE COUNTY
MY COMMISSION EXPIRES: FEB 25, 2003

SURVEYOR'S STATEMENT:

I HEREBY STATE THAT THIS MAP CONSISTING OF THREE (3) SHEETS CORRECTLY REPRESENTS THE TRUE AND COMPLETE SURVEY AS SHOWN MADE IN JANUARY, 2000; WAS MADE BY ME OR UNDER MY DIRECTION; THAT THE MONUMENTS ARE OF THE CHARACTER AND OCCUPY OR WILL OCCUPY THE POSITIONS INDICATED BY SAID MAP; AND THAT SAID MONUMENTS ARE OR WILL BE SUFFICIENT TO ENABLE THE SURVEY TO BE RETRACED.

[Signature]
JAMES R. CRAWFORD, L.S. 4965
MY LICENSE EXPIRES: DECEMBER 31, 2001




COUNTY SURVEYOR'S STATEMENT:

I HEREBY STATE THAT I HAVE EXAMINED THIS MAP AND HAVE FOUND IT TO BE SUBSTANTIALLY IN CONFORMANCE WITH THE TENTATIVE MAP AS FILED WITH, AMENDED AND APPROVED BY THE ORANGE COUNTY SUBDIVISION COMMITTEE; THAT ALL PROVISIONS OF THE SUBDIVISION MAP ACT AND COUNTY SUBDIVISION REGULATIONS HAVE BEEN COMPLIED WITH AND I AM SATISFIED SAID MAP IS TECHNICALLY CORRECT.

DATED THIS 5TH DAY OF AUGUST, 2000.

[Signature]
JOHN CANAS, COUNTY SURVEYOR

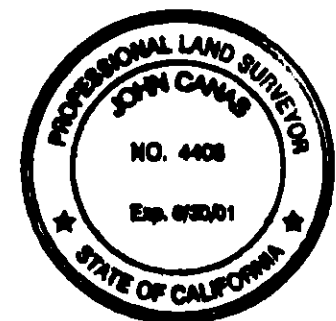

CLERK OF THE BOARD OF SUPERVISORS' CERTIFICATE:

STATE OF CALIFORNIA }
COUNTY OF ORANGE } SS

I HEREBY CERTIFY THAT THIS MAP WAS PRESENTED FOR APPROVAL TO THE BOARD OF SUPERVISORS OF ORANGE COUNTY AT A REGULAR MEETING THEREOF HELD ON THE 22ND DAY OF AUGUST, 2000, AND THAT THEREUPON SAID BOARD DID, BY AN ORDER DULY PASSED AND ENTERED, APPROVE SAID MAP AND DID ACCEPT ON BEHALF OF THE PUBLIC, SUBJECT TO IMPROVEMENTS; THE DEDICATION FOR STREET PURPOSES OF: MINFORD CIRCLE AND PICKERING CIRCLE.

AND DID ALSO ACCEPT ON BEHALF OF THE COUNTY OF ORANGE:
THE EASEMENT FOR STORM DRAIN PURPOSES AS DEDICATED, SUBJECT TO IMPROVEMENTS.

AND DID ALSO APPROVE SUBJECT MAP PURSUANT TO THE PROVISIONS OF SECTION 66436(a)(3) OF THE SUBDIVISION MAP ACT.

DATED THIS 22ND DAY OF AUGUST, 2000.

[Signature]
DARLENE J. BLOOM
CLERK OF THE BOARD OF SUPERVISORS



COUNTY TREASURER-TAX COLLECTOR'S CERTIFICATE:

STATE OF CALIFORNIA }
COUNTY OF ORANGE } SS

I HEREBY CERTIFY THAT ACCORDING TO THE RECORDS OF MY OFFICE, THERE ARE NO LIENS AGAINST THE LAND COVERED BY THIS MAP OR ANY PART THEREOF FOR UNPAID STATE, COUNTY, MUNICIPAL OR LOCAL TAXES OR SPECIAL ASSESSMENTS COLLECTED AS TAXES, EXCEPT TAXES OR SPECIAL ASSESSMENTS COLLECTED AS TAXES NOT YET PAYABLE.

AND DO CERTIFY TO THE RECORDER OF ORANGE COUNTY THAT THE PROVISIONS OF THE SUBDIVISION MAP ACT HAVE BEEN COMPLIED WITH REGARDING DEPOSITS TO SECURE PAYMENT OF TAXES OR SPECIAL ASSESSMENTS COLLECTED AS TAXES ON THE LAND COVERED BY THIS MAP.

DATED THIS 17TH DAY OF JULY, 2000.

JOHN M. W. MOORLACH
COUNTY TREASURER-TAX COLLECTOR

BY [Signature]
DEPUTY TREASURER-TAX COLLECTOR

SEE SHEET 2 FOR SANTA MARGARITA WATER DISTRICT ACCEPTANCE CERTIFICATE,
NOTARY ACKNOWLEDGMENT AND SIGNATURE OMISSIONS.

4.176 ACRES GROSS
(ALL OF VESTING TENTATIVE
TRACT NO. 15907)
LOTS: 28 NUMBERED
1 LETTERED LOT

TRACT NO. 15907

IN THE UNINCORPORATED TERRITORY OF THE COUNTY OF ORANGE, STATE OF CALIFORNIA

JAMES R. CRAWFORD L.S. 4965



DATE OF SURVEY: JANUARY, 2000

CERTIFICATE OF ACCEPTANCE - SANTA MARGARITA WATER DISTRICT:

THE UNDERSIGNED, BEING THE DULY APPOINTED AGENT OF THE SANTA MARGARITA WATER DISTRICT, A PUBLIC CORPORATION IN ORANGE COUNTY, CALIFORNIA, PURSUANT TO ITS RESOLUTION NO. 88-10-2, DOES HEREBY ACCEPT ON BEHALF OF SAID DISTRICT THE EASEMENT FOR SEWER AND WATER LINE PURPOSES, AS DEDICATED AND SHOWN ON THIS TRACT MAP, BY AND BETWEEN THE SANTA MARGARITA WATER DISTRICT AND RESTON ASSOCIATES LLC, AND DOES HEREBY CERTIFY THAT THE GRANTEE CONSENTS TO THE RECORDATION OF SAID TRACT MAP.

Daniel R. Ferons

DANIEL R. FERONS, CHIEF ENGINEER
SANTA MARGARITA WATER DISTRICT

NOTARY ACKNOWLEDGMENT FOR SANTA MARGARITA WATER DISTRICT:

STATE OF CALIFORNIA }
COUNTY OF ORANGE } SS

ON, JULY 12, 2000, BEFORE ME, ANDREA M. EVANS, A NOTARY PUBLIC IN AND FOR SAID STATE PERSONALLY APPEARED DANIEL R. FERONS, PERSONALLY KNOWN TO ME (OR PROVED TO ME ON THE BASIS OF SATISFACTORY EVIDENCE) TO BE THE PERSON WHOSE NAME IS SUBSCRIBED TO THE WITHIN INSTRUMENT AND ACKNOWLEDGED TO ME THAT HE EXECUTED THE SAME IN HIS AUTHORIZED CAPACITY AND THAT BY HIS SIGNATURE ON THE INSTRUMENT THE PERSON, OR THE ENTITY UPON BEHALF OF WHICH THE PERSON ACTED, EXECUTED THE INSTRUMENT.

WITNESS MY HAND:

Andrea M. Evans
NOTARY PUBLIC IN AND FOR SAID STATE

ANDREA M. EVANS
(NAME PRINTED)

MY PRINCIPAL PLACE OF BUSINESS IS
IN ORANGE COUNTY

MY COMMISSION EXPIRES: 04-08-04

SIGNATURE OMISSION NOTES:

PURSUANT TO THE PROVISIONS OF SECTION 66436(a)(3)(C) OF THE SUBDIVISION MAP ACT THE FOLLOWING SIGNATURES HAVE BEEN OMITTED:

- LADERA DEVELOPMENT COMPANY, L.L.C., HOLDER OF OIL, GAS AND MINERAL RIGHTS RECORDED AS INSTRUMENT NO. 19960624029 OF OFFICIAL RECORDS.
- DMB LADERA, L.L.C., HOLDER OF EASEMENTS RECORDED AS INSTRUMENT NO. 20000095516 OF OFFICIAL RECORDS.

NOTES:

- ALL DETACHED, SINGLE-FAMILY STRUCTURES EXCEEDING 5500 SQUARE FEET, AND ALL STRUCTURES EXCEEDING FIRE AUTHORITY ACCESS REQUIREMENTS SHALL BE PROTECTED BY AN AUTOMATIC FIRE SPRINKLER SYSTEM.
- THIS PROPERTY IS WITHIN A "SPECIAL FIRE PROTECTION AREA" AND MUST MEET ALL REQUIREMENTS FOR DEVELOPMENT WITHIN THE AREA OR FILE FOR AN EXCLUSION WITH THE FIRE CHIEF. THE APPLICANT HAS APPLIED FOR AND RECEIVED A "TOTAL EXCLUSION" FROM THIS ORANGE COUNTY "SPECIAL FIRE PROTECTION AREA" AND NO LOTS OR BUILDINGS ARE SUBJECT TO THE CONSTRUCTION FEATURES OF ORANGE COUNTY ORDINANCE 3960. THE EXCLUSION HAS BEEN GRANTED BASED ON THE FINDINGS FOUND IN A LETTER DATED FEBRUARY 9, 2000 SIGNED BY LAURA BLAUL OF THE ORANGE COUNTY FIRE AUTHORITY AND THE APPLICANT WILL KEEP A COPY OF SAID LETTER AVAILABLE IN THEIR RECORDS.
- THIS PROPERTY IS IN A "HIGH FIRE HAZARD AREA" DUE TO WILDLAND EXPOSURE.
- LOT "A" IS NOT A SEPARATE BUILDING SITE BUT IS PROPOSED TO BE GRANTED IN FEE TO THE HOMEOWNER'S ASSOCIATION FOR TRACT NO. 15907 FOR PRIVATE PARK AND LANDSCAPE MAINTENANCE PURPOSES.

GPS POINT LOCATIONS:

GPS # 1417 FOUND 2 1/2" IRON PIPE WITH 2" DIAMETER O.C.S. BRASS
N2141450.558 CAP STAMPED "GPS 1417 9-95" PER TRACT NO. 15615, M.M. 777/14-31
E6141583.535 AND RECORDS ON FILE IN THE OFFICE OF THE ORANGE COUNTY SURVEYOR.

GPS # 1424 FOUND 2 1/2" IRON PIPE WITH 2" DIAMETER O.C.S. BRASS
N2152873.842 CAP STAMPED "GPS 1424 9-95" PER RECORDS ON FILE IN THE OFFICE
E6141904.527 OF THE ORANGE COUNTY SURVEYOR.

DATUM STATEMENT:


COORDINATES SHOWN ARE BASED UPON THE CALIFORNIA COORDINATE SYSTEM (CCS83), ZONE VI 1983 NAD (1991.35 EPOCH O.C.S. GPS ADJUSTMENT). ALL DISTANCES SHOWN ARE GROUND UNLESS OTHERWISE NOTED. TO OBTAIN GRID DISTANCE, MULTIPLY THE GROUND DISTANCE BY 0.99993389.

BASIS OF BEARINGS NOTE:

THE BEARINGS SHOWN HEREON ARE BASED ON THE BEARING BETWEEN O.C.S. HORIZONTAL CONTROL STATION GPS NO. 1417 AND STATION GPS NO. 1424 BEING NORTH 01°36'34" EAST PER RECORDS ON FILE IN THE OFFICE OF THE ORANGE COUNTY SURVEYOR.

MONUMENT NOTES

- ALL MONUMENTS SHOWN SET WILL BE SET WITHIN 90 DAYS AFTER THE ACCEPTANCE OF IMPROVEMENTS, EXCEPT AS NOTED.
- SET SPIKE W/ BRASS WASHER STAMPED "L.S. 4965" IN ASPHALT PAVEMENT HAVING A THICKNESS OF 2" OR MORE OR A LEAD, TACK AND TAG "L.S. 4965" IN CONCRETE, AT ALL CENTERLINE POINTS OF CONTROL, UNLESS OTHERWISE NOTED.
- TIES TO CENTERLINE MONUMENTS WILL BE MADE AND A COPY OF SAID TIES WILL BE FURNISHED TO THE COUNTY SURVEYOR'S OFFICE.
- SET 1" IRON PIPE TAGGED "L.S. 4965" AT ALL LOT CORNERS EXCEPT LOT CORNERS THAT ABUT A STREET WHICH WILL BE MARKED ON A 8.75' OFFSET OUTSIDE THE TRUE LOT CORNER IN CONCRETE BY A LEAD, TACK AND TAG "L.S. 4965" ON SIDELINES PRODUCED, EXCEPT AS NOTED. (NO MONUMENTS WILL BE SET FOR ANGLE POINTS, CORNER CUTOFFS, B.C.'S, E.C.'S, P.C.C.'S OR P.R.C.'S THAT ABUT A STREET WHICH ARE NOT LOT CORNER MARKING SIDELINES, UNLESS OTHERWISE NOTED).
- SET 2" IRON PIPE TAGGED "L.S. 4965" OR LEAD, TACK AND TAG "L.S. 4965" IN CONCRETE OR A SPIKE W/ BRASS WASHER STAMPED "L.S. 4965" IN ASPHALT PAVEMENT HAVING A THICKNESS OF 2" OR MORE AT ALL TRACT BOUNDARY CORNERS. (NO MONUMENTS WILL BE SET FOR ANGLE POINTS, CORNER CUTOFFS, B.C.'S, E.C.'S P.C.C.'S OR P.R.C.'S THAT ABUT A STREET WHICH ARE NOT BOUNDARY CORNERS MARKING SIDELINES, UNLESS OTHERWISE NOTED.)
- INDICATES SET MONUMENTS AS NOTED.
- 1 SET LEAD, TACK AND TAG "L.S.4965" IN CONCRETE ON OFFSET AS SHOWN OUTSIDE TRUE LOT CORNER ON SIDELINE PRODUCED.
- 2 SET 2" IRON PIPE TAGGED "L.S.4965" PRIOR TO RECORDATION.
- DENOTES FOUND OR TO BE SET MONUMENTS AS NOTED AND REFERENCED BELOW:
 - 3 INDICATES 2" IRON PIPE TAGGED "L.S. 5557" OR SPIKE AND WASHER STAMPED "L.S. 5557" OR LEAD, TACK AND TAG "L.S. 5557" TO BE SET PER TRACT NO. 15813, M.M. 795/1-16.
 - 4 INDICATES 1" IRON PIPE TAGGED "L.S. 5557" OR SPIKE AND WASHER STAMPED "L.S. 5557" OR LEAD, TACK AND TAG "L.S. 5557" TO BE SET PER TRACT NO. 15813, M.M. 795/1-16.
 - 5 INDICATES 1" IRON PIPE TAGGED "L.S. 5557" OR SPIKE AND WASHER STAMPED "L.S. 5557" OR LEAD, TACK AND TAG "L.S. 5557" TO BE SET PER TRACT NO. 15884, M.M. 794 / 33-44.
- ▲ INDICATES FOUND ORANGE COUNTY SURVEYOR'S G.P.S. MONUMENT AS NOTED.

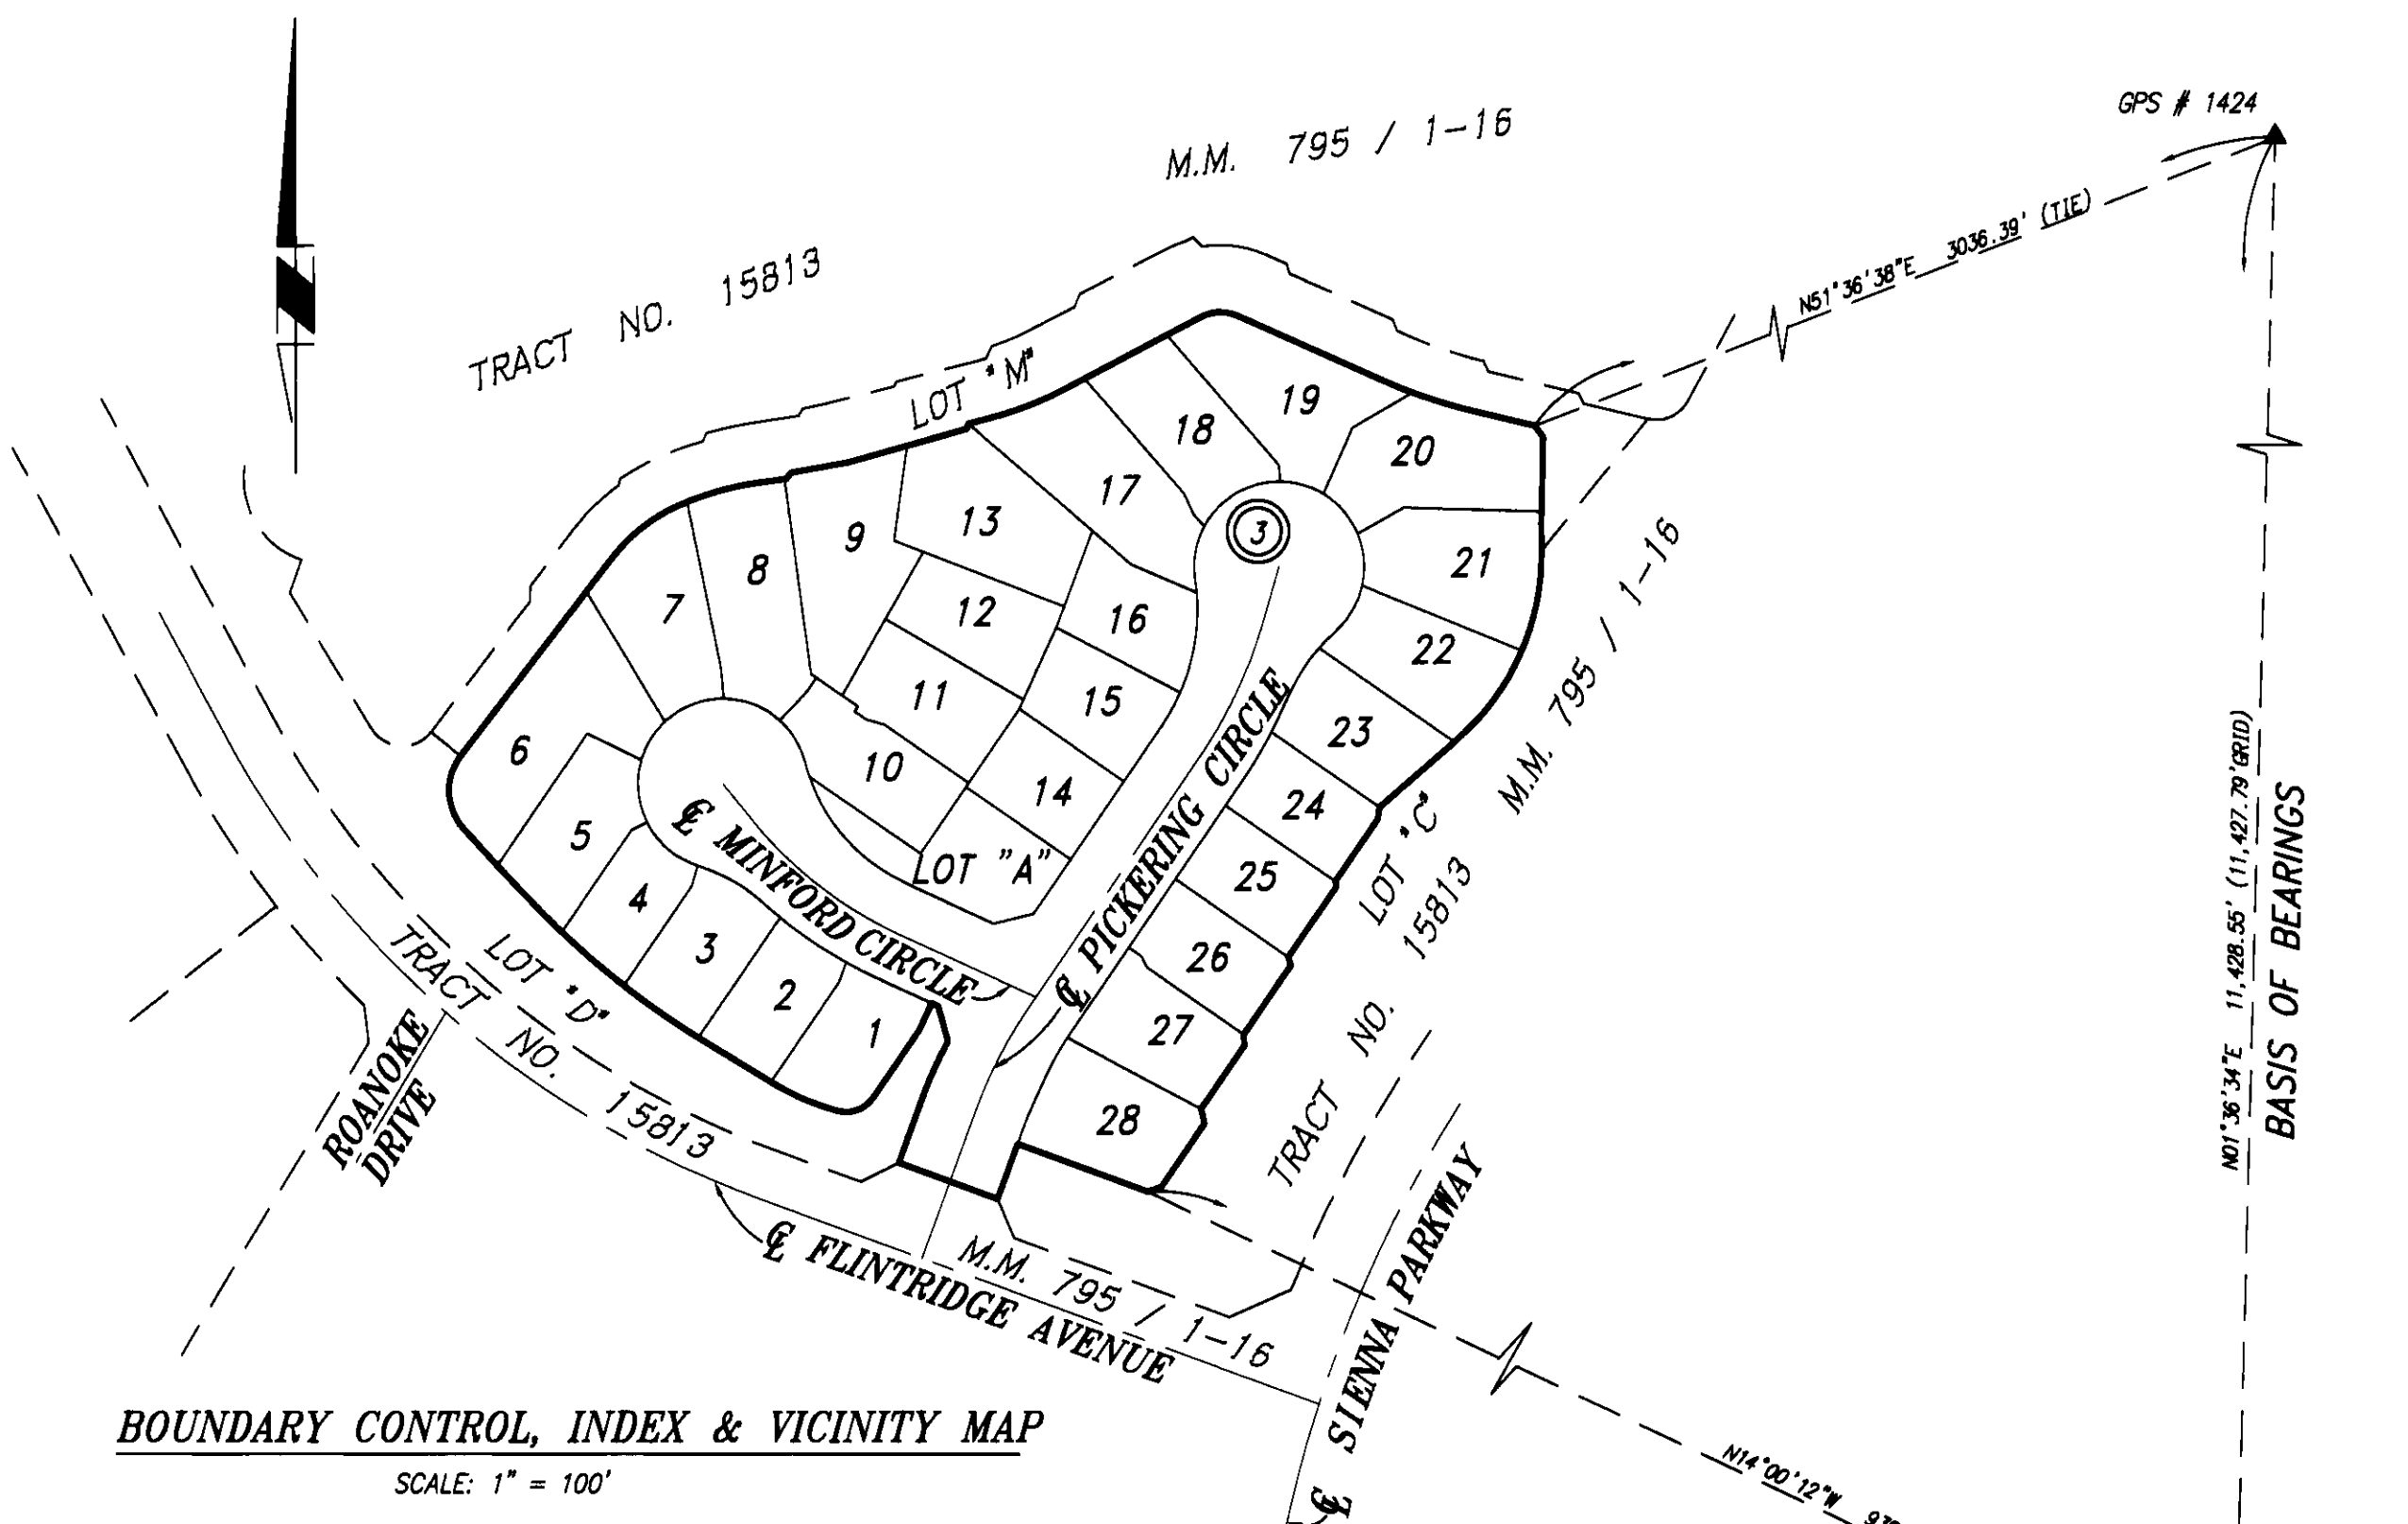

NOTE: (3) INDICATES SHEET NUMBER

SHEET 3 OF 3 SHEETS

AREA: 4.176 ACRES GROSS
(BEING ALL OF VESTING
TENTATIVE TRACT NO. 15907)
NUMBERED LOTS: 28
LETTERED LOTS: 1

SCALE: 1" = 40'

TRACT NO. 15907

IN THE UNINCORPORATED TERRITORY OF THE
COUNTY OF ORANGE, STATE OF CALIFORNIA


JAMES R. CRAWFORD, L.S. 4965



DATE OF SURVEY: JANUARY, 2000

NO.	BRNG/DELTA	RADIUS	LENGTH
1	N20°11'00"E	—	41.42'
2	09°32'42"	184.00'	30.65'
3	N15°36'43"W	—	20.28'
4	N65°23'00"W	—	3.84'
5	N24°37'00"E	—	16.25'
6	69°54'14"	18.00'	21.96'
7	16°34'47"	130.00'	37.62'
8	N82°13'01"E	—	15.32'
9	N37°13'01"E	—	4.24'
10	N13°24'17"E	—	2.93'
11	N76°05'17"E	—	9.96'
12	24°29'52"	100.00'	42.76'
13	04°43'03"	193.00'	15.89'
14	00°56'37"	223.00'	3.67'
15	23°55'28"	112.00'	46.77'
16	N23°53'00"E	—	1.80'
17	10°44'00"	277.00'	51.89'
18	09°45'29"	141.00'	24.01'
19	N24°51'31"E	—	18.46'
20	04°40'31"	166.00'	13.55'
21	07°30'51"	250.00'	32.79'
22	N23°53'00"E	—	1.80'
23	10°44'00"	250.00'	46.83'
24	08°09'28"	250.00'	35.59'
25	04°24'19"	247.00'	18.99'
26	02°42'54"	247.00'	11.70'
27	00°51'02"	475.00'	7.05'
28	02°28'06"	475.00'	20.46'
29	N16°28'11"E	—	11.93'
30	01°43'51"	170.00'	5.14'
31	N44°13'51"E	—	19.08'
32	04°46'20"	100.00'	8.33'
33	09°40'45"	112.00'	18.92'
34	03°41'11"	112.00'	7.21'
35	03°38'31"	290.00'	18.43'
36	N05°36'08"W	—	9.02'
37	N60°50'23"E	—	29.27'
38	07°05'23"	112.00'	13.86'
39	03°52'00"	277.00'	18.69'
40	00°11'01"	141.00'	0.45'
41	09°34'28"	141.00'	23.56'
42	21°19'34"	220.00'	81.89'
43	09°47'23"	250.00'	42.72'
44	N19°08'49"E	—	11.21'
45	N55°23'00"W	—	31.55'
46	N34°37'00"E	—	3.33'
47	N55°23'00"W	—	7.44'
48	N73°52'59"W	—	10.51'
49	N40°55'32"W	—	8.54'
50	N25°55'32"W	—	12.87'
51	N55°23'00"W	—	8.89'
52	N25°23'00"W	—	6.66'
53	238°04'03"	47.00'	195.29'
54	33°28'02"	47.00'	27.45'
55	41°39'22"	47.00'	34.17'


NO.	BRNG/DELTA	RADIUS	LENGTH
56	30°21'26"	47.00'	24.90'
57	42°49'23"	47.00'	35.13'
58	N64°12'21"W	—	33.15'
59	N45°33'01"W	—	29.45'
60	N44°26'59"E	—	24.00'
61	N34°37'00"E	—	39.12'
62	26°31'50"	—	6.95'
63	N08°05'10"E	15.00'	14.87'
64	N83°30'13"W	—	13.01'
65	N08°05'10"E	—	23.74'
66	N83°30'13"W	—	22.68'
67	N08°05'10"E	—	33.02'
68	25°50'57"	50.00'	22.56'
69	00°40'53"	50.00'	0.59'
70	N34°37'00"E	—	48.66'
71	09°36'51"	22.00'	3.69'
72	N34°37'00"E	—	8.41'

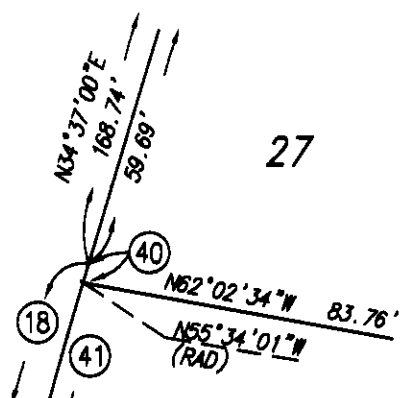

DETAIL "A"
NOT TO SCALE

DETAIL "B"
NOT TO SCALE

M.M. 795 / 1-16

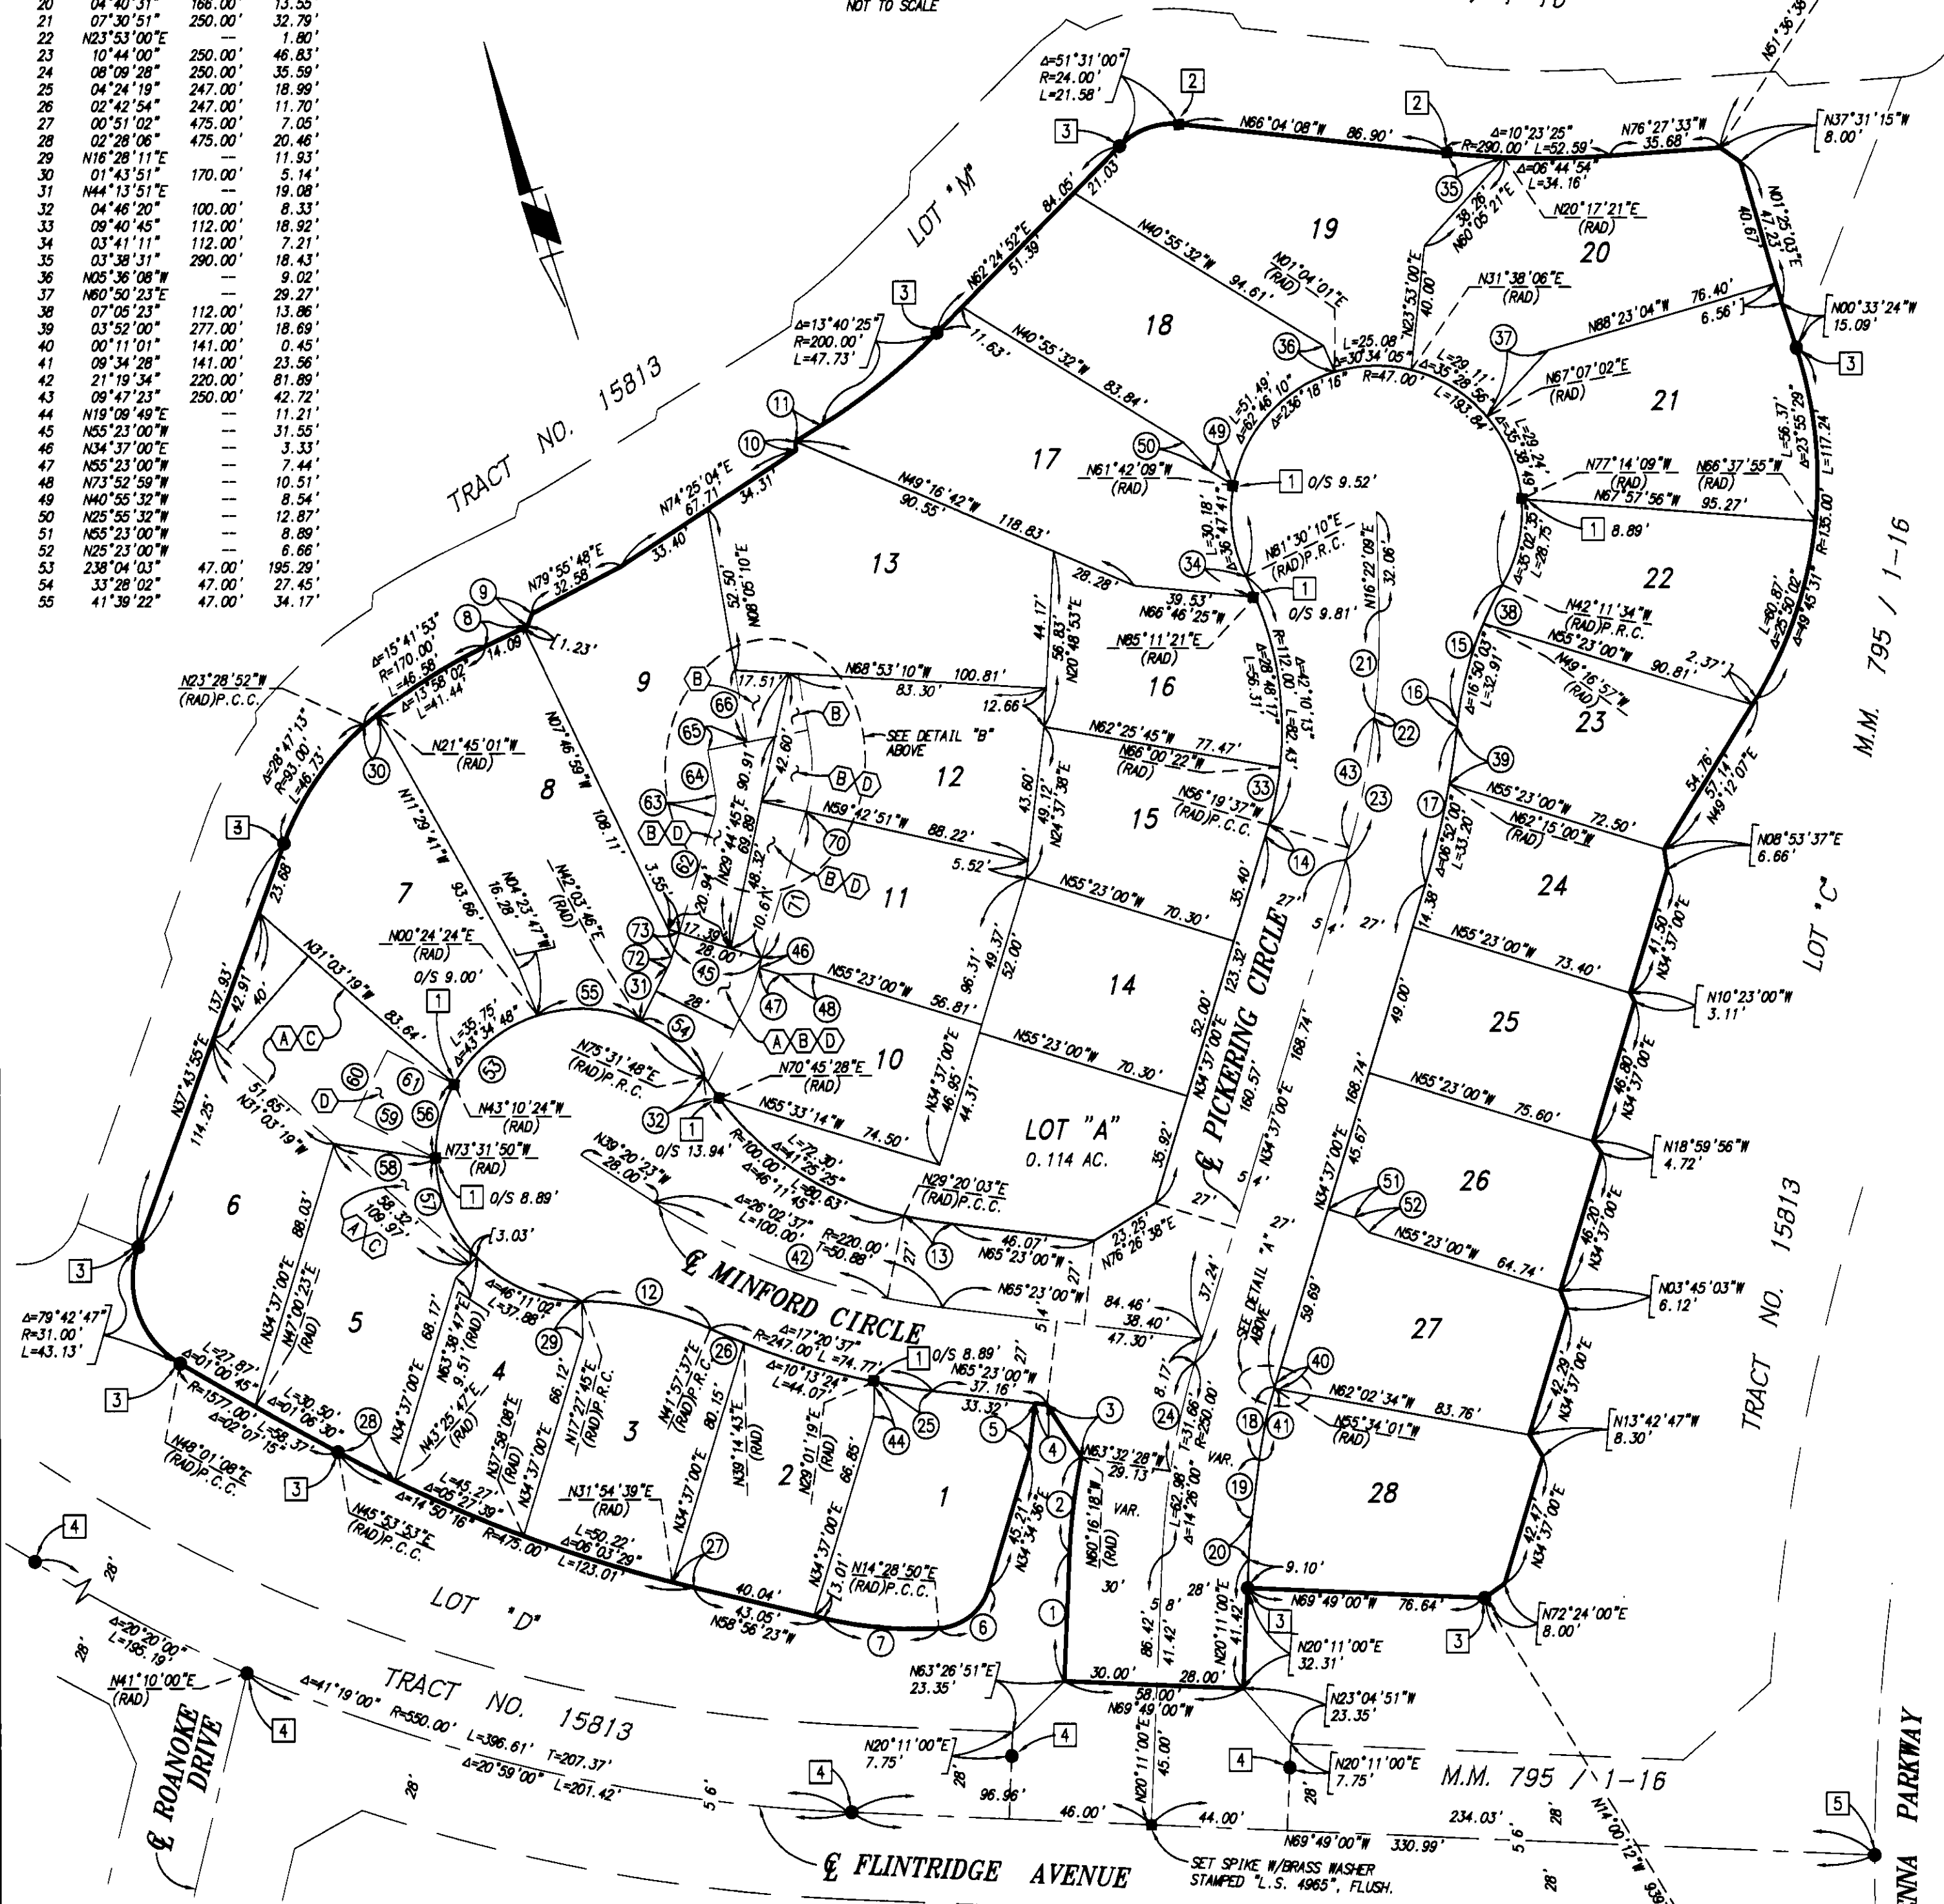

EASEMENT NOTES:

- (A) - DENOTES AN EASEMENT FOR SEWER AND WATER LINE PURPOSES IN FAVOR OF THE SANTA MARGARITA WATER DISTRICT BEING DEDICATED HEREON.
- (B) - DENOTES AN EASEMENT FOR INGRESS AND EGRESS PURPOSES TO BE GRANTED BY SEPARATE DOCUMENT.
- (C) - DENOTES AN EASEMENT FOR STORM DRAIN PURPOSES IN FAVOR OF THE COUNTY OF ORANGE BEING DEDICATED HEREON.
- (D) - DENOTES AN EASEMENT FOR FIRE PROTECTION ACCESS PURPOSES IN FAVOR OF THE COUNTY OF ORANGE BEING DEDICATED HEREON.

SEE SHEET 2 FOR BASIS OF BEARINGS, GPS POINT LOCATIONS, DATUM STATEMENT, BOUNDARY CONTROL AND VICINITY MAP, MONUMENT NOTES, AND OTHER NOTES.