

SHEET 1 OF 6 SHEETS
ALL OF TENTATIVE TRACT NO. 15908
TOTAL LOTS: 33 NUMBERED LOTS AND 3 LETTERED LOTS
TOTAL ACREAGE: 9.555 ACRES

BLOCK 5157
MODULE 14 & 15

TRACT NO. 15908

IN THE UNINCORPORATED TERRITORY OF THE COUNTY OF ORANGE,
STATE OF CALIFORNIA

BEING A SUBDIVISION OF LOT 9 OF TRACT NO. 15813, AS SHOWN ON A MAP FILED IN BOOK 795,
PAGES 1 TO 16 INCLUSIVE OF MISCELLANEOUS MAPS, RECORDS OF ORANGE COUNTY, CALIFORNIA.

TETRA TECH, INC. EUGENE A. SHAFFER, L.S. 4644
DATE OF SURVEY: APRIL, 2000

ACCEPTED AND FILED AT THE
REQUEST OF
FIRST AMERICAN TITLE INSURANCE CO.

DATE JUNE 29, 2001
TIME 3:06 P.M. FEE \$ 17.00
INSTRUMENT # 20010436852
BOOK 820 PAGE 10-15 M/M

GARY L. GRANVILLE
COUNTY CLERK RECORDER
BY [Signature]
DEPUTY

OWNER'S CERTIFICATE

WE THE UNDERSIGNED, BEING ALL PARTIES HAVING ANY RECORD TITLE INTEREST IN THE LAND COVERED BY THIS MAP, DO HEREBY CONSENT TO THE PREPARATION AND RECORDATION OF SAID MAP, AS SHOWN WITHIN THE DISTINCTIVE BORDER LINE. WE ALSO HEREBY DEDICATE TO THE PUBLIC FOR STREET PURPOSES: LEWISTON COURT, AND CRESTMONT COURT

WE ALSO GRANT BY DEDICATION TO THE SANTA MARGARITA WATER DISTRICT THE EASEMENTS FOR SEWER AND WATER AND ACCESS PURPOSES AS SHOWN ON SAID MAP, WHICH EASEMENTS SHALL BE SUBJECT TO THE SAME TERMS AND CONDITIONS AS ARE SHOWN IN THAT CERTAIN EASEMENT RECORDED OCTOBER 6, 1980 IN BOOK 13776, PAGE 341 OF OFFICIAL RECORDS, COUNTY OF ORANGE.

CENTEX HOMES. A NEVADA GENERAL PARTNERSHIP

BY: CENTEX REAL ESTATE CORPORATION
A NEVADA CORPORATION,
ITS MANAGING GENERAL PARTNER

BY: ROLAND F. OSGOOD
PRESIDENT, SOUTH COAST DIVISION

By: [Signature]
Martin Juliusen
Assistant Secretary

CERTIFICATE OF ACCEPTANCE

THE UNDERSIGNED, BEING THE DULY APPOINTED AGENT OF THE SANTA MARGARITA WATER DISTRICT, A PUBLIC CORPORATION OF ORANGE COUNTY, A CALIFORNIA, PURSUANT TO ITS RESOLUTION No. 88-10-2, DOES HEREBY ACCEPT ON BEHALF OF SAID DISTRICT THE EASEMENTS FOR SEWER AND WATER AND ACCESS PURPOSES, AS DEDICATED AND SHOWN ON THIS MAP, BY AND BETWEEN THE SANTA MARGARITA WATER DISTRICT AND DMB LADERA, L.L.C., AND DOES HEREBY CERTIFY THAT THE GRANTEE CONSENTS TO THE RECORDATION OF SAID TRACT.

[Signature]
DANIEL R. FERONS, CHIEF ENGINEER
SANTA MARGARITA WATER DISTRICT

NOTARY ACKNOWLEDGMENT

STATE OF CALIFORNIA)
COUNTY OF ORANGE) ss

ON THIS 30th DAY OF April, 2001, BEFORE ME, Rhonda Keiger Painter A NOTARY PUBLIC IN AND FOR SAID STATE, PERSONALLY APPEARED ROLAND F. OSGOOD, PERSONALLY KNOWN TO ME TO BE THE PERSON WHOSE NAME IS SUBSCRIBED TO THE WITHIN INSTRUMENT AND ACKNOWLEDGED TO ME THAT HE EXECUTED THE SAME IN HIS AUTHORIZED CAPACITY, AND THAT BY HIS SIGNATURE ON THE INSTRUMENT THE PERSON OR THE ENTITY UPON BEHALF OF WHICH THE PERSON ACTED, EXECUTED THE INSTRUMENT.

* and Martin Juliusen

WITNESS MY HAND:

[Signature]
Rhonda Keiger Painter
NOTARY PUBLIC IN AND FOR SAID STATE

PRINT NAME Rhonda Keiger Painter

MY PRINCIPAL PLACE OF BUSINESS IS IN Orange COUNTY.

MY COMMISSION EXPIRES: 12/9/03

DMB LADERA, L.L.C., A DELAWARE LIMITED LIABILITY COMPANY

BENEFICIARY UNDER A DEED OF TRUST RECORDED OCTOBER 3, 2000, AS INSTRUMENT NO. 20000525919 OF OFFICIAL RECORDS. BY: RANCHO MISSION VILLO, L.L.C., A DELAWARE LIMITED LIABILITY COMPANY AS AGENT OR MANAGER

PRINT NAME: Paul Johnson
PRINT TITLE: VP - Community Development

PRINT NAME: Richard Browning
PRINT TITLE: VP - Planning & Entitlement

SANTA MARGARITA WATER DISTRICT

STATE OF CALIFORNIA)
COUNTY OF ORANGE) ss

ON THIS 16th DAY OF MAY, 2001, BEFORE ME, Cindy R. Lane A NOTARY PUBLIC IN AND FOR SAID STATE, PERSONALLY APPEARED DANIEL R. FERONS PERSONALLY KNOWN TO ME (OR PROVED TO ME ON THE BASIS OF SATISFACTORY EVIDENCE) TO BE THE PERSON WHOSE NAME IS SUBSCRIBED TO THE WITHIN INSTRUMENT AND ACKNOWLEDGED TO ME THAT HE EXECUTED THE SAME IN HIS AUTHORIZED CAPACITY, AND THAT BY HIS SIGNATURE ON THE INSTRUMENT THE PERSON OR ENTITY UPON BEHALF OF WHICH THE PERSONS ACTED, EXECUTED THE INSTRUMENT.

WITNESS MY HAND:

[Signature]
Cindy R. Lane
NOTARY PUBLIC IN AND FOR SAID STATE

PRINT NAME CINDY R. LANE

MY PRINCIPAL PLACE OF BUSINESS IS IN ORANGE COUNTY.

MY COMMISSION EXPIRES: 2-20-2005

NOTARY ACKNOWLEDGEMENT FOR DMB LADERA, LLC:

STATE OF CALIFORNIA
COUNTY OF Orange) ss

ON JUNE 15, 2001, BEFORE ME, LINDA K. LEBBER A NOTARY, PUBLIC IN AND FOR SAID STATE PERSONALLY APPEARED Paul Johnson AND Richard Browning PERSONALLY KNOWN TO ME (OR PROVED TO ME ON THE BASIS OF SATISFACTORY EVIDENCE) TO BE THE PERSONS WHOSE NAMES ARE SUBSCRIBED TO THE WITHIN INSTRUMENT AND ACKNOWLEDGED TO ME THAT THEY EXECUTED THE SAME IN THEIR AUTHORIZED CAPACITIES AND THAT BY THEIR SIGNATURES ON THE INSTRUMENT THE PERSONS, OR THE ENTITY UPON BEHALF OF WHICH THE PERSONS ACTED EXECUTED THE INSTRUMENT.

WITNESS MY HAND:

[Signature]
Linda K. Lebbber
NOTARY PUBLIC IN AND FOR SAID STATE

PRINT NAME Linda K. Lebbber
(NAME PRINTED)

MY PRINCIPAL PLACE OF BUSINESS IS
IN ORANGE COUNTY, CA
MY COMMISSION EXPIRES: 2/2/03

SURVEYOR'S STATEMENT

I HEREBY STATE THAT THIS MAP, CONSISTING OF 6 SHEETS, CORRECTLY REPRESENTS TRUE AND COMPLETE SURVEY AS SHOWN MADE IN APRIL, 2000, WAS MADE BY ME OR UNDER MY DIRECTION: THAT THE MONUMENTS ARE OF THE CHARACTER AND OCCUPY (OR WILL OCCUPY) THE POSITIONS INDICATED BY SAID MAP; AND THAT SAID MONUMENTS ARE (OR WILL BE) SUFFICIENT TO ENABLE THE SURVEY TO BE RETRACED.


[Signature]
EUGENE A. SHAFFER, L.S. 4644
EXPIRES 9-30-2002

COUNTY SURVEYOR'S STATEMENT

I HEREBY STATE THAT I HAVE EXAMINED THIS MAP AND HAVE FOUND IT TO BE SUBSTANTIALLY IN CONFORMANCE WITH THE TENTATIVE MAP AS FILED WITH, AMENDED AND APPROVED BY THE ORANGE COUNTY SUBDIVISION COMMITTEE; THAT ALL PROVISIONS OF THE SUBDIVISION MAP ACT AND COUNTY SUBDIVISION REGULATIONS HAVE BEEN COMPLIED WITH AND I AM SATISFIED SAID MAP IS TECHNICALLY CORRECT.

DATED THIS 18th DAY OF JUNE, 2001.

[Signature]
JOHN CANAS, COUNTY SURVEYOR
LS 4608 EXPIRATION DATE: 9-30-01

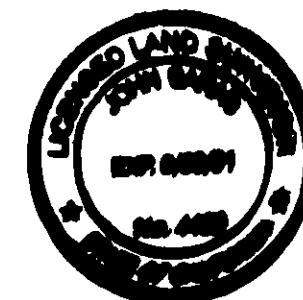

CLERK OF THE BOARD OF SUPERVISORS' CERTIFICATE

STATE OF CALIFORNIA)
COUNTY OF ORANGE) ss

I HEREBY CERTIFY THAT THIS MAP WAS PRESENTED FOR APPROVAL TO THE BOARD OF SUPERVISORS OF ORANGE COUNTY AT A REGULAR MEETING THEREOF HELD ON THE 26th DAY OF June, 2001, AND THAT THEREUPON SAID BOARD DID, BY AN ORDER DULY PASSED AND ENTERED, APPROVED SAID MAP AND DID ACCEPT ON BEHALF OF THE PUBLIC, SUBJECT TO IMPROVEMENTS: THE DEDICATION FOR STREET PURPOSES OF LEWISTON COURT, AND CRESTMONT COURT.

DATED THIS 26th DAY OF June, 2001.

[Signature]
DARLENE J. BLOOM
CLERK OF THE BOARD OF SUPERVISORS



COUNTY TREASURER-TAX COLLECTOR'S CERTIFICATE

STATE OF CALIFORNIA)
COUNTY OF ORANGE) ss

I HEREBY CERTIFY THAT ACCORDING TO THE RECORDS OF MY OFFICE THERE ARE NO LIENS AGAINST THE LAND COVERED BY THIS MAP OR ANY PART THEREOF FOR UNPAID STATE, COUNTY, MUNICIPAL OR LOCAL TAXES OR SPECIAL ASSESSMENTS COLLECTED AS TAXES, EXCEPT TAXES OR SPECIAL ASSESSMENTS COLLECTED AS TAXES NOT YET PAYABLE.

AND DO ALSO CERTIFY TO THE RECORDER OF ORANGE COUNTY THAT THE PROVISIONS OF THE SUBDIVISION MAP ACT HAVE BEEN COMPLIED WITH REGARDING DEPOSITS TO SECURE THE PAYMENT OF TAXES OR SPECIAL ASSESSMENTS COLLECTED AS TAXES ON THE LAND COVERED BY THIS MAP.

DATED THIS 24th DAY OF May, 2001.

JOHN M.W. MOORLACH BY: [Signature]
COUNTY TREASURER-TAX COLLECTOR DEPUTY TREASURER-TAX COLLECTOR

SIGNATURE OMISSIONS:

IN ACCORDANCE WITH THE PROVISIONS OF SECTION 66436(a) (3) OF THE SUBDIVISION MAP ACT, THE FOLLOWING SIGNATURES HAVE BEEN OMITTED:

1. LADERA DEVELOPMENT COMPANY, L.L.C., HOLDER OF OIL, GAS, MINERAL, AND WATER RIGHTS RECORDED DECEMBER 10, 1996 AS INSTRUMENT No. 19960624029 OF OFFICIAL RECORDS.

AUTOMATIC FIRE SPRINKLER NOTE

ALL COMMERCIAL STRUCTURES GREATER THAN 6000 SQUARE FEET; ALL MULTIFAMILY RESIDENCE STRUCTURES; ALL SINGLE-FAMILY STRUCTURES EXCEEDING 5500 SQUARE FEET, AND ALL STRUCTURES EXCEEDING FIRE DEPARTMENT ACCESS REQUIREMENTS SHALL BE PROTECTED BY AN AUTOMATIC FIRE SPRINKLER SYSTEM.

SPECIAL FIRE PROTECTION NOTE

PROPERTY IS IN A SPECIAL FIRE PROTECTION AREA AND MUST MEET ALL REQUIREMENTS FOR DEVELOPMENT WITHIN THE AREA.

HIGH FIRE HAZARD AREA NOTE



THE LOTS SHOWN ON THIS MAP ARE IN A HIGH FIRE HAZARD AREA DUE TO WILD LAND EXPOSURE

SHEET 2 OF 6 SHEETS
ALL OF TENTATIVE TRACT No. 15908
TOTAL LOTS: 33 NUMBERED LOTS AND 3 LETTERED LOTS
TOTAL ACREAGE: 9.555 ACRES

TRACT NO. 15908

IN THE UNINCORPORATED TERRITORY OF THE COUNTY OF ORANGE,
STATE OF CALIFORNIA

TETRA TECH, INC. EUGENE A. SHAFFER, L.S. 4644
DATE OF SURVEY: APRIL, 2000

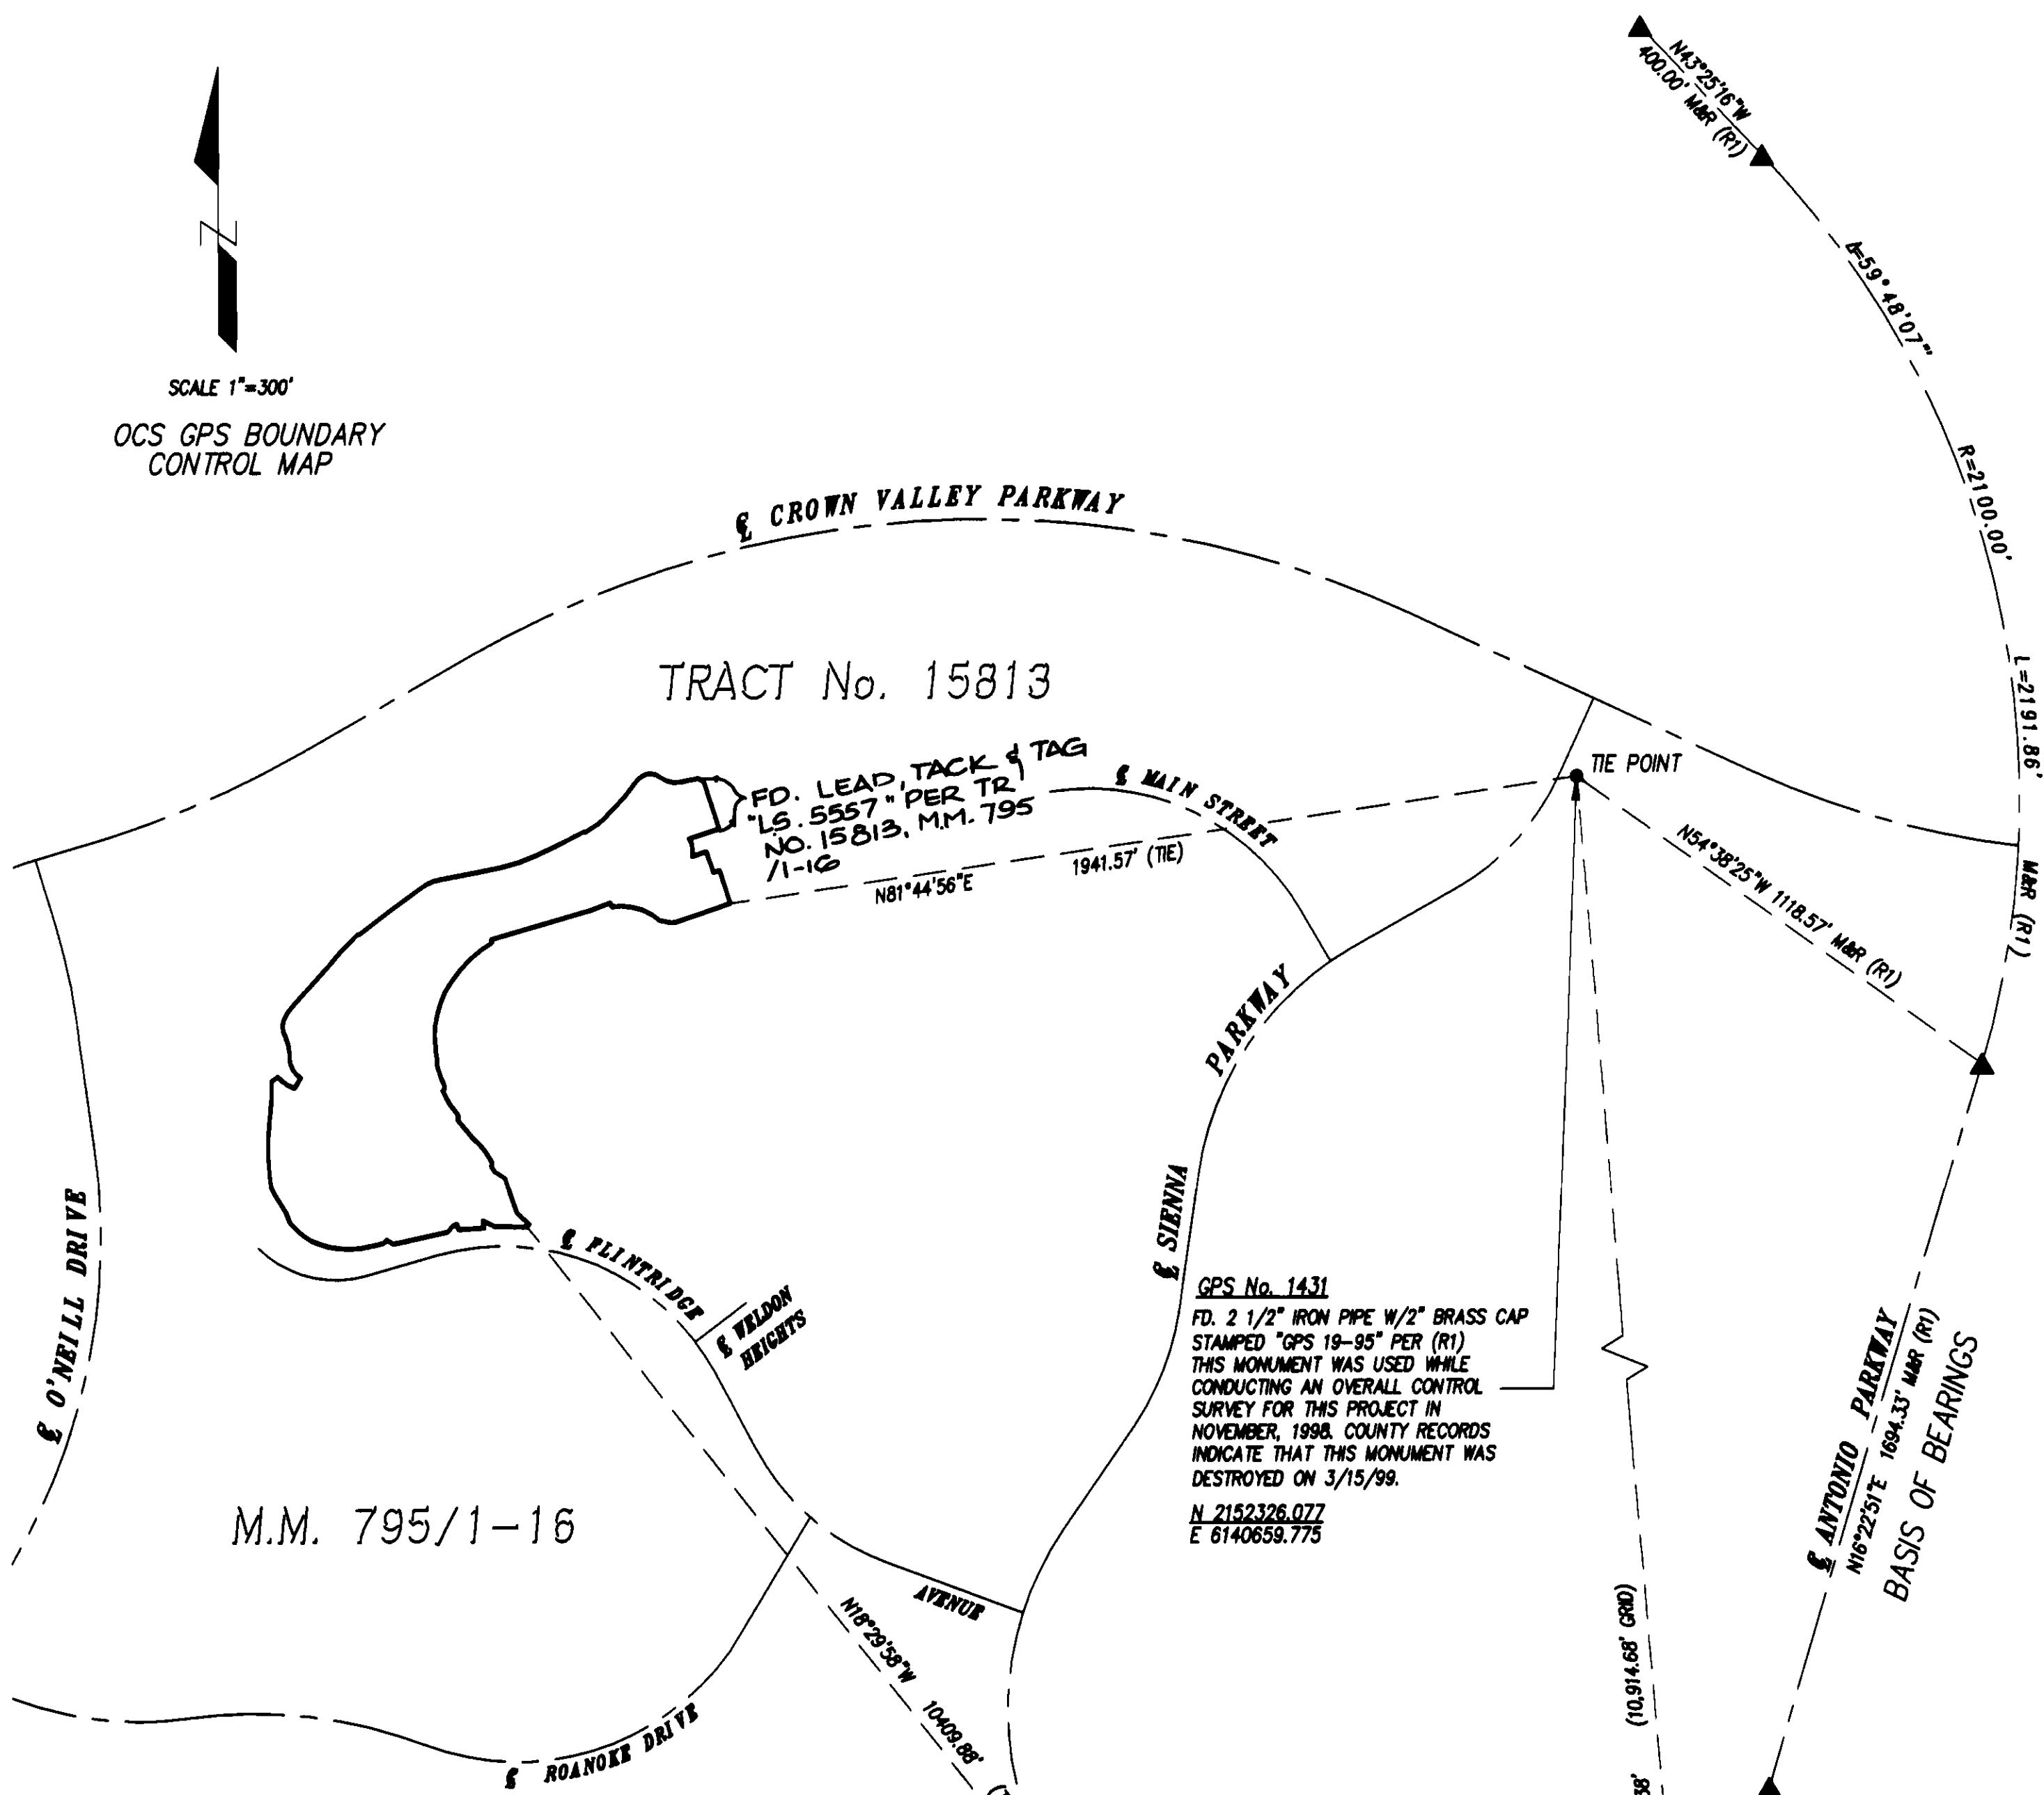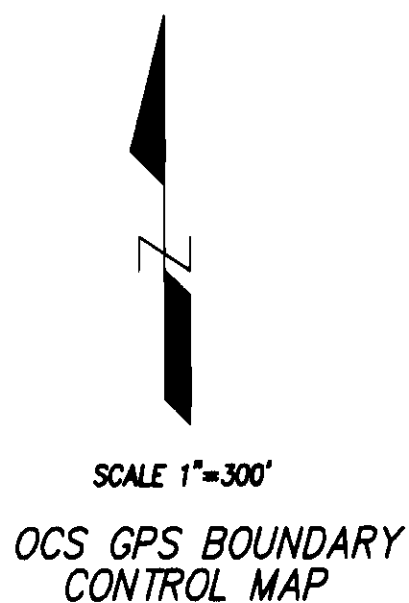

BASIS OF BEARINGS:
THE BEARING N16°22'51\"/>

DATUM STATEMENT:
COORDINATES SHOWN HEREON ARE BASED ON THE CALIFORNIA COORDINATE SYSTEM (CCS83), ZONE VI, 1983 NAD, (1991.35 EPOCH OCS GPS ADJUSTMENT)
ALL DISTANCES SHOWN ARE GROUND, UNLESS OTHERWISE NOTED. TO OBTAIN GRID DISTANCE MULTIPLY GROUND DISTANCE BY 0.99993576
GPS NO. 1431 WAS USED FOR THE INITIAL POINT FOR GRID TO GROUND CONVERSIONS.

- MONUMENT NOTES:**
- - INDICATES LOCATION OF 1\"/>
 - - INDICATES LOCATION OF 2\"/>
 - ▲ - INDICATES FD. OCS WELL MONUMENT WITH 2 1/2\"/>

2\"/>

1\"/>

8\" S&W STAMPED \"LS 4644\" OR LEAD, TACK & TAG \"LS 4644\" OR 1\" I.P. TAGGED \"LS 4644\" IN MEDIAN TO BE SET AT ALL STREET CENTERLINE POINTS OF CONTROL, WITHIN 90 DAYS AFTER ACCEPTANCE OF IMPROVEMENTS, UNLESS OTHERWISE NOTED.

REFERENCES:
R1 - TRACT No. 15813, M.M. 795/1-16

- EASEMENT NOTES:**
- Ⓐ - INDICATES SANTA MARGARITA WATER DISTRICT EASEMENT FOR SEWER AND WATER PURPOSES PER TRACT No. 15813, M.M. 795/1-16.
 - Ⓑ - INDICATES COUNTY OF ORANGE EASEMENT FOR STORM DRAIN PURPOSES PER TRACT 15813, M.M. 795/1-16.
 - Ⓒ - INDICATES FIRE DEPARTMENT ACCESS EASEMENT PER TRACT 15813, M.M. 795/1-16.
 - Ⓓ - INDICATES AN EASEMENT FOR SEWER, WATER AND ACCESS PURPOSES DEDICATED TO THE SANTA MARGARITA WATER DISTRICT HEREON.
 - Ⓔ - INDICATES A DRAINAGE EASEMENT TO THE HOMEOWNERS ASSOCIATION

NOTE:
SEE SHEET 3 FOR MAP SHEET INDEX

GPS No. 1417
FD. 2 1/2\"/>

SHEET 3 OF 6 SHEETS
ALL OF TENTATIVE TRACT No. 15908
TOTAL LOTS: 33 NUMBERED LOTS AND 3 LETTERED LOTS
TOTAL ACREAGE: 9.555 ACRES


TRACT NO. 15908

IN THE UNINCORPORATED TERRITORY OF THE COUNTY OF ORANGE,
STATE OF CALIFORNIA

TETRA TECH, INC. EUGENE A. SHAFFER, L.S. 4644
DATE OF SURVEY: APRIL, 2000




SCALE 1"=100'
SHEET INDEX MAP

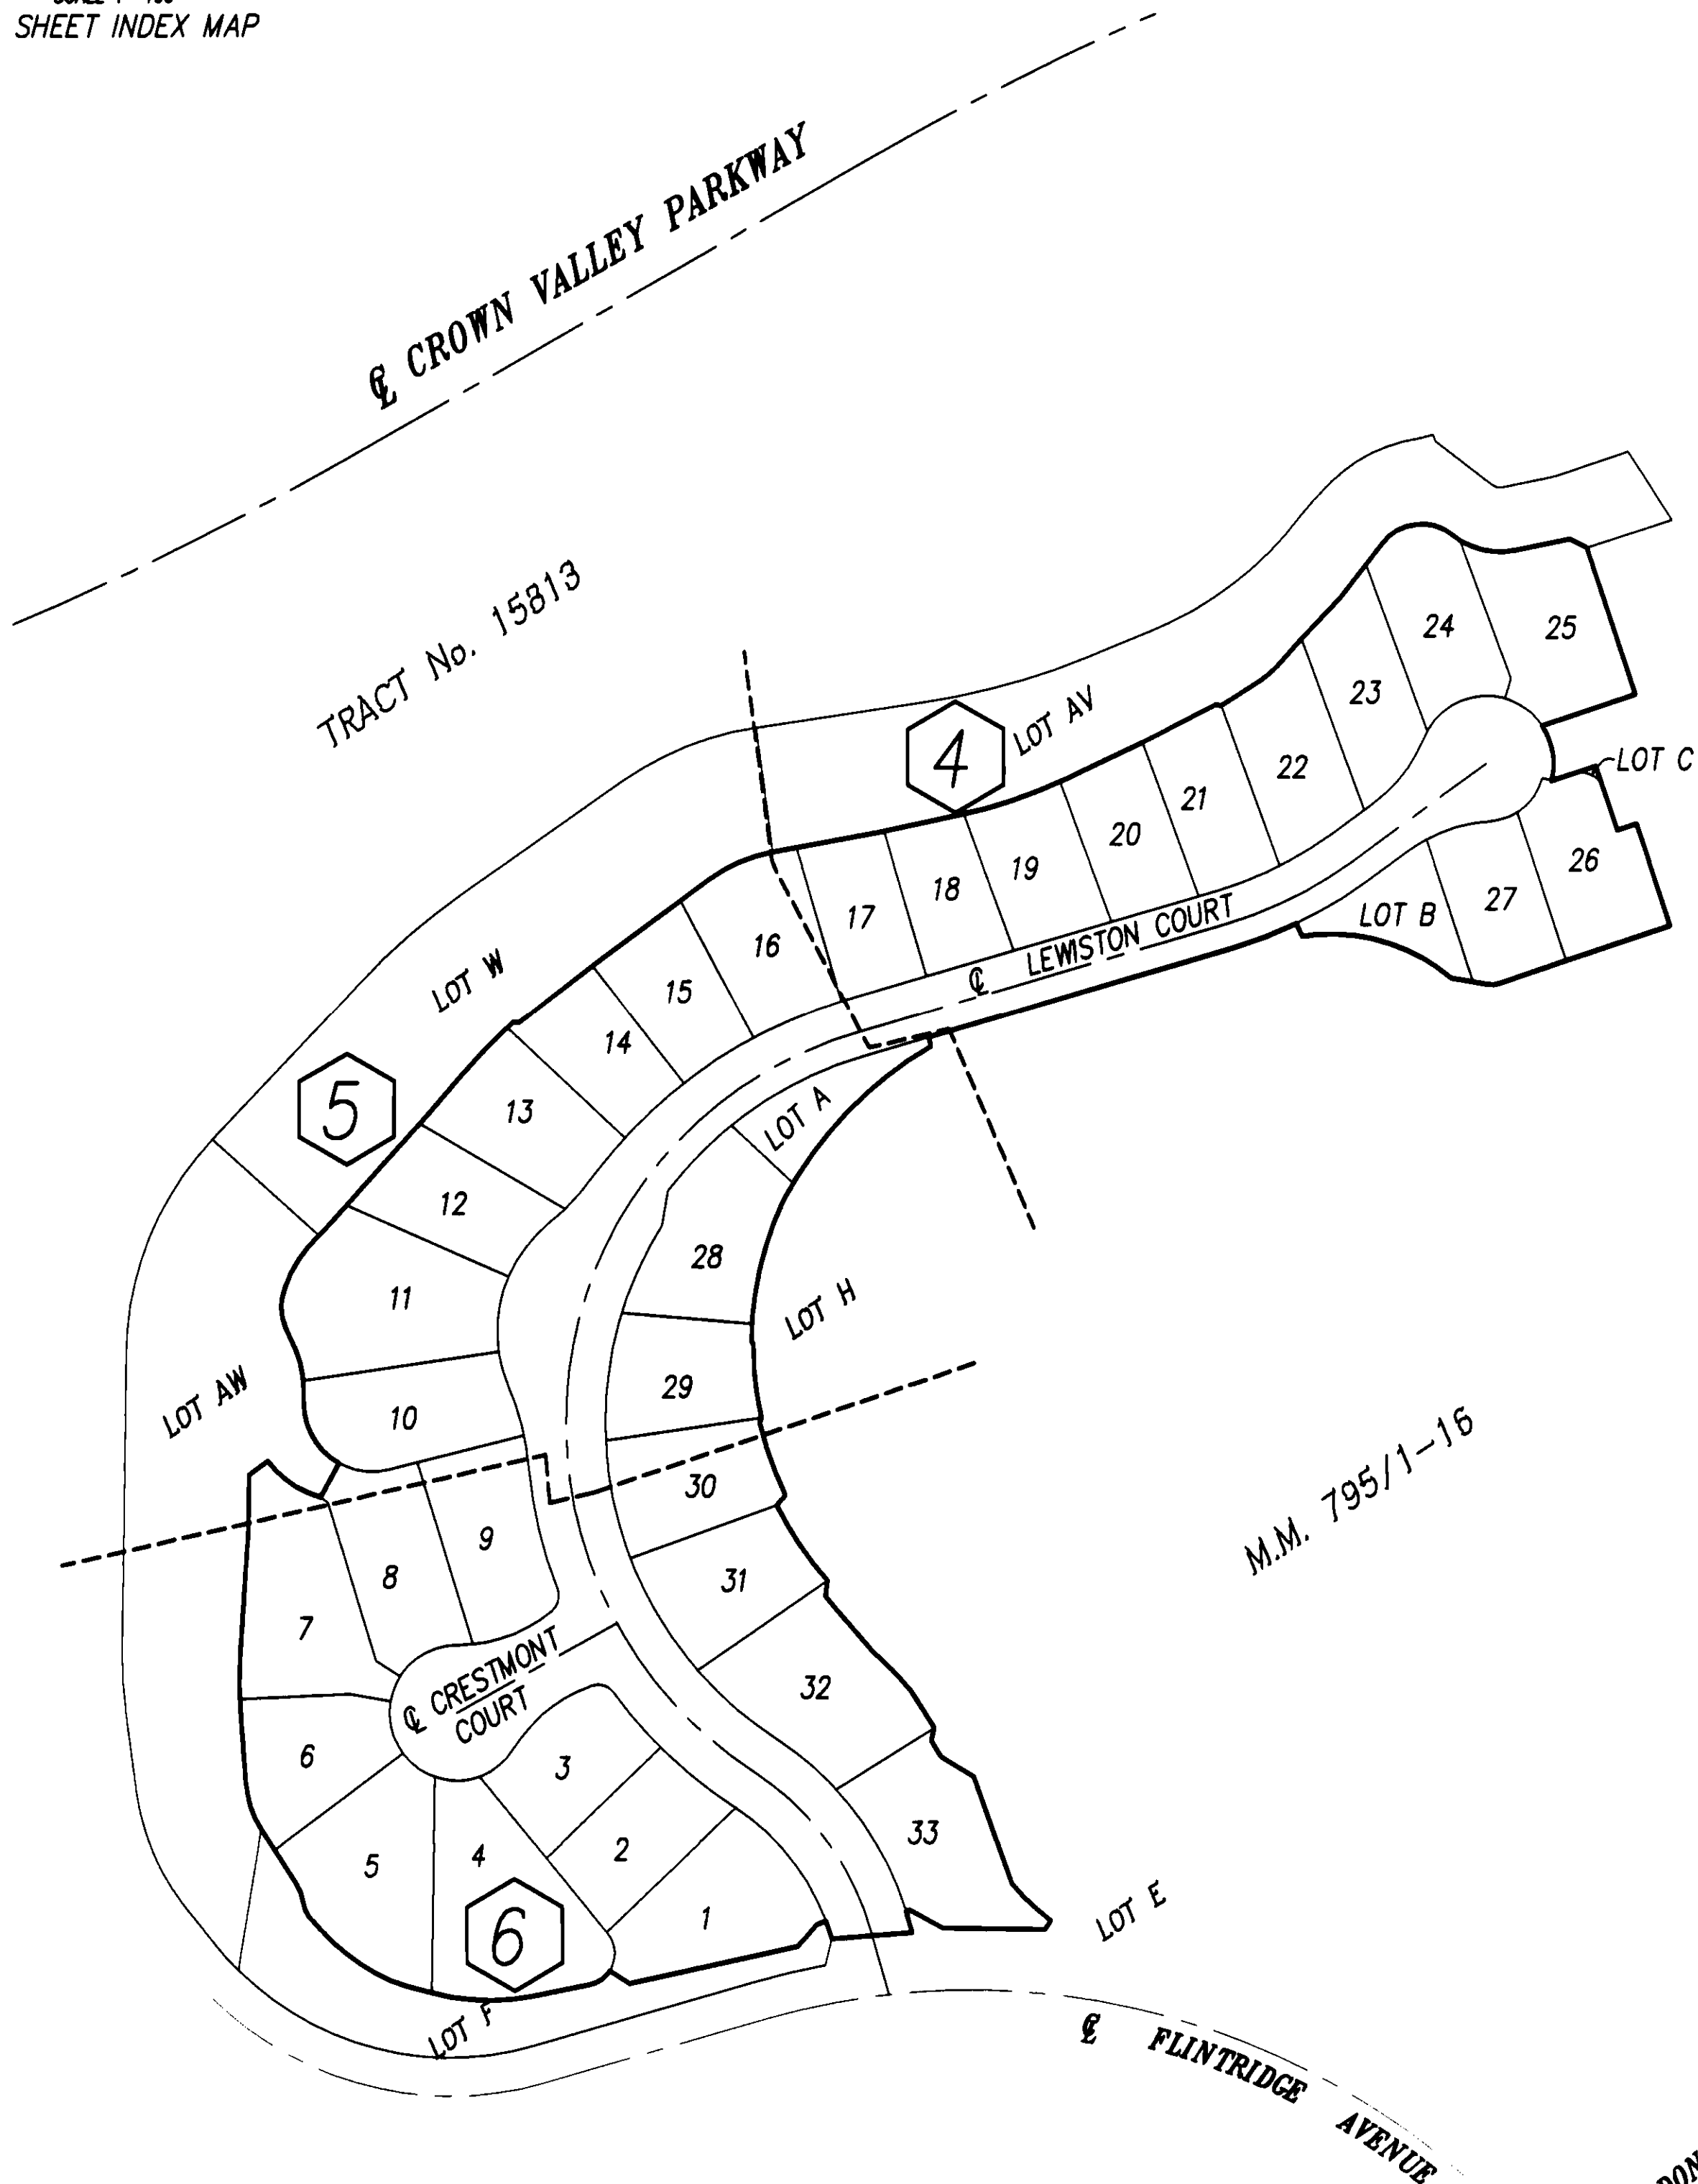

NOTES:

1. LETTERED LOTS A, B AND C CREATED BY THIS MAP ARE NOT BUILDING SITES.
2. ACREAGE AND INTENDED USE FOR LETTERED LOTS CREATED BY THIS MAP ARE AS FOLLOWS:
LOT A OPEN SPACE 0.135 AC.
LOT B OPEN SPACE 0.125 AC.
LOT C OPEN SPACE 0.001 AC.

SEE SHEET 2 FOR BASIS OF BEARING, DATUM STATEMENT,
MONUMENT NOTES, EASEMENT NOTES AND OCS GPS BOUNDARY
CONTROL MAP.

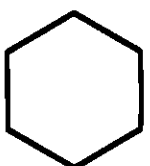

INDICATE SHEET NUMBER

TRACT NO. 15908


IN THE UNINCORPORATED TERRITORY OF THE COUNTY OF ORANGE,
STATE OF CALIFORNIA

TETRA TECH, INC. **EUGENE A. SHAFFER, L.S. 4644**
DATE OF SURVEY: APRIL 2000

CURVE TABLE							
CURVE	DELTA	RADIUS	LENGTH	CURVE	DELTA	RADIUS	LENGTH
C2	48°48'15"	137.00'	116.70'	C24	10°07'33"	275.00'	48.60'
C3	48°46'50"	49.00'	41.72'	C25	08°28'58"	275.00'	45.51'
C4	08°46'43"	318.00'	48.72'	C26	06°33'26"	49.00'	5.61'
C5	39°47'11"	49.00'	34.03'	C28	00°21'58"	350.00'	2.24'
C6	77°23'00"	49.00'	66.18'	C30	00°39'28"	352.00'	4.04'
C7	10°49'53"	318.00'	60.12'	C32	12°04'28"	352.00'	74.16'
C8	08°58'37"	117.00'	16.29'	C31	08°55'46"	49.00'	7.64'
C9	23°54'50"	117.00'	48.83'	C47	90°00'00"	18.00'	28.27'
C10	28°20'35"	42.00'	20.78'	C48	34°00'17"	42.00'	24.93'
C12	20°40'55"	352.00'	4.19'	C50	07°55'19"	137.00'	18.94'
C13	50°06'04"	55.00'	48.09'	C51	03°54'15"	318.00'	21.67'
C14	90°36'00"	36.00'	56.93'	C52	23°36'18"	49.00'	20.19'
C15	16°11'57"	55.00'	15.55'	C53	25°10'31"	49.00'	21.53'


C16	43°36'44"	55.00'	41.98'
C17	06°29'19"	55.00'	6.23'
C19	29°23'49"	18.00'	9.24'
C20	31°53'27"	110.00'	61.23'
C21	62°20'52"	42.00'	45.70'
C22	31°53'27"	117.00'	65.12'
C23	19°36'31"	300.00'	102.67'

LINE TABLE		
LINE		LENGTH
L1	N78°20'36"W	26.62'
L2	N74°28'53"W	3.69'
L3	N16°17'28"E	14.79'
L4	N77°44'00"E	15.00'
L5	N68°12'56"W	7.00'
L6	N24°57'50"W	10.29'
L7	N59°18'00"E	33.96'
L8	N42°06'03"E	27.27'
L9	N38°24'22"E	19.72'
L11	N63°16'00"W	14.14'
L12	N12°27'00"W	18.00'
L13	N77°44'00"E	16.08'
L14	N77°44'00"E	18.00'
L17	N77°44'00"E	34.08'
L18	N18°16'00"W	49.20'

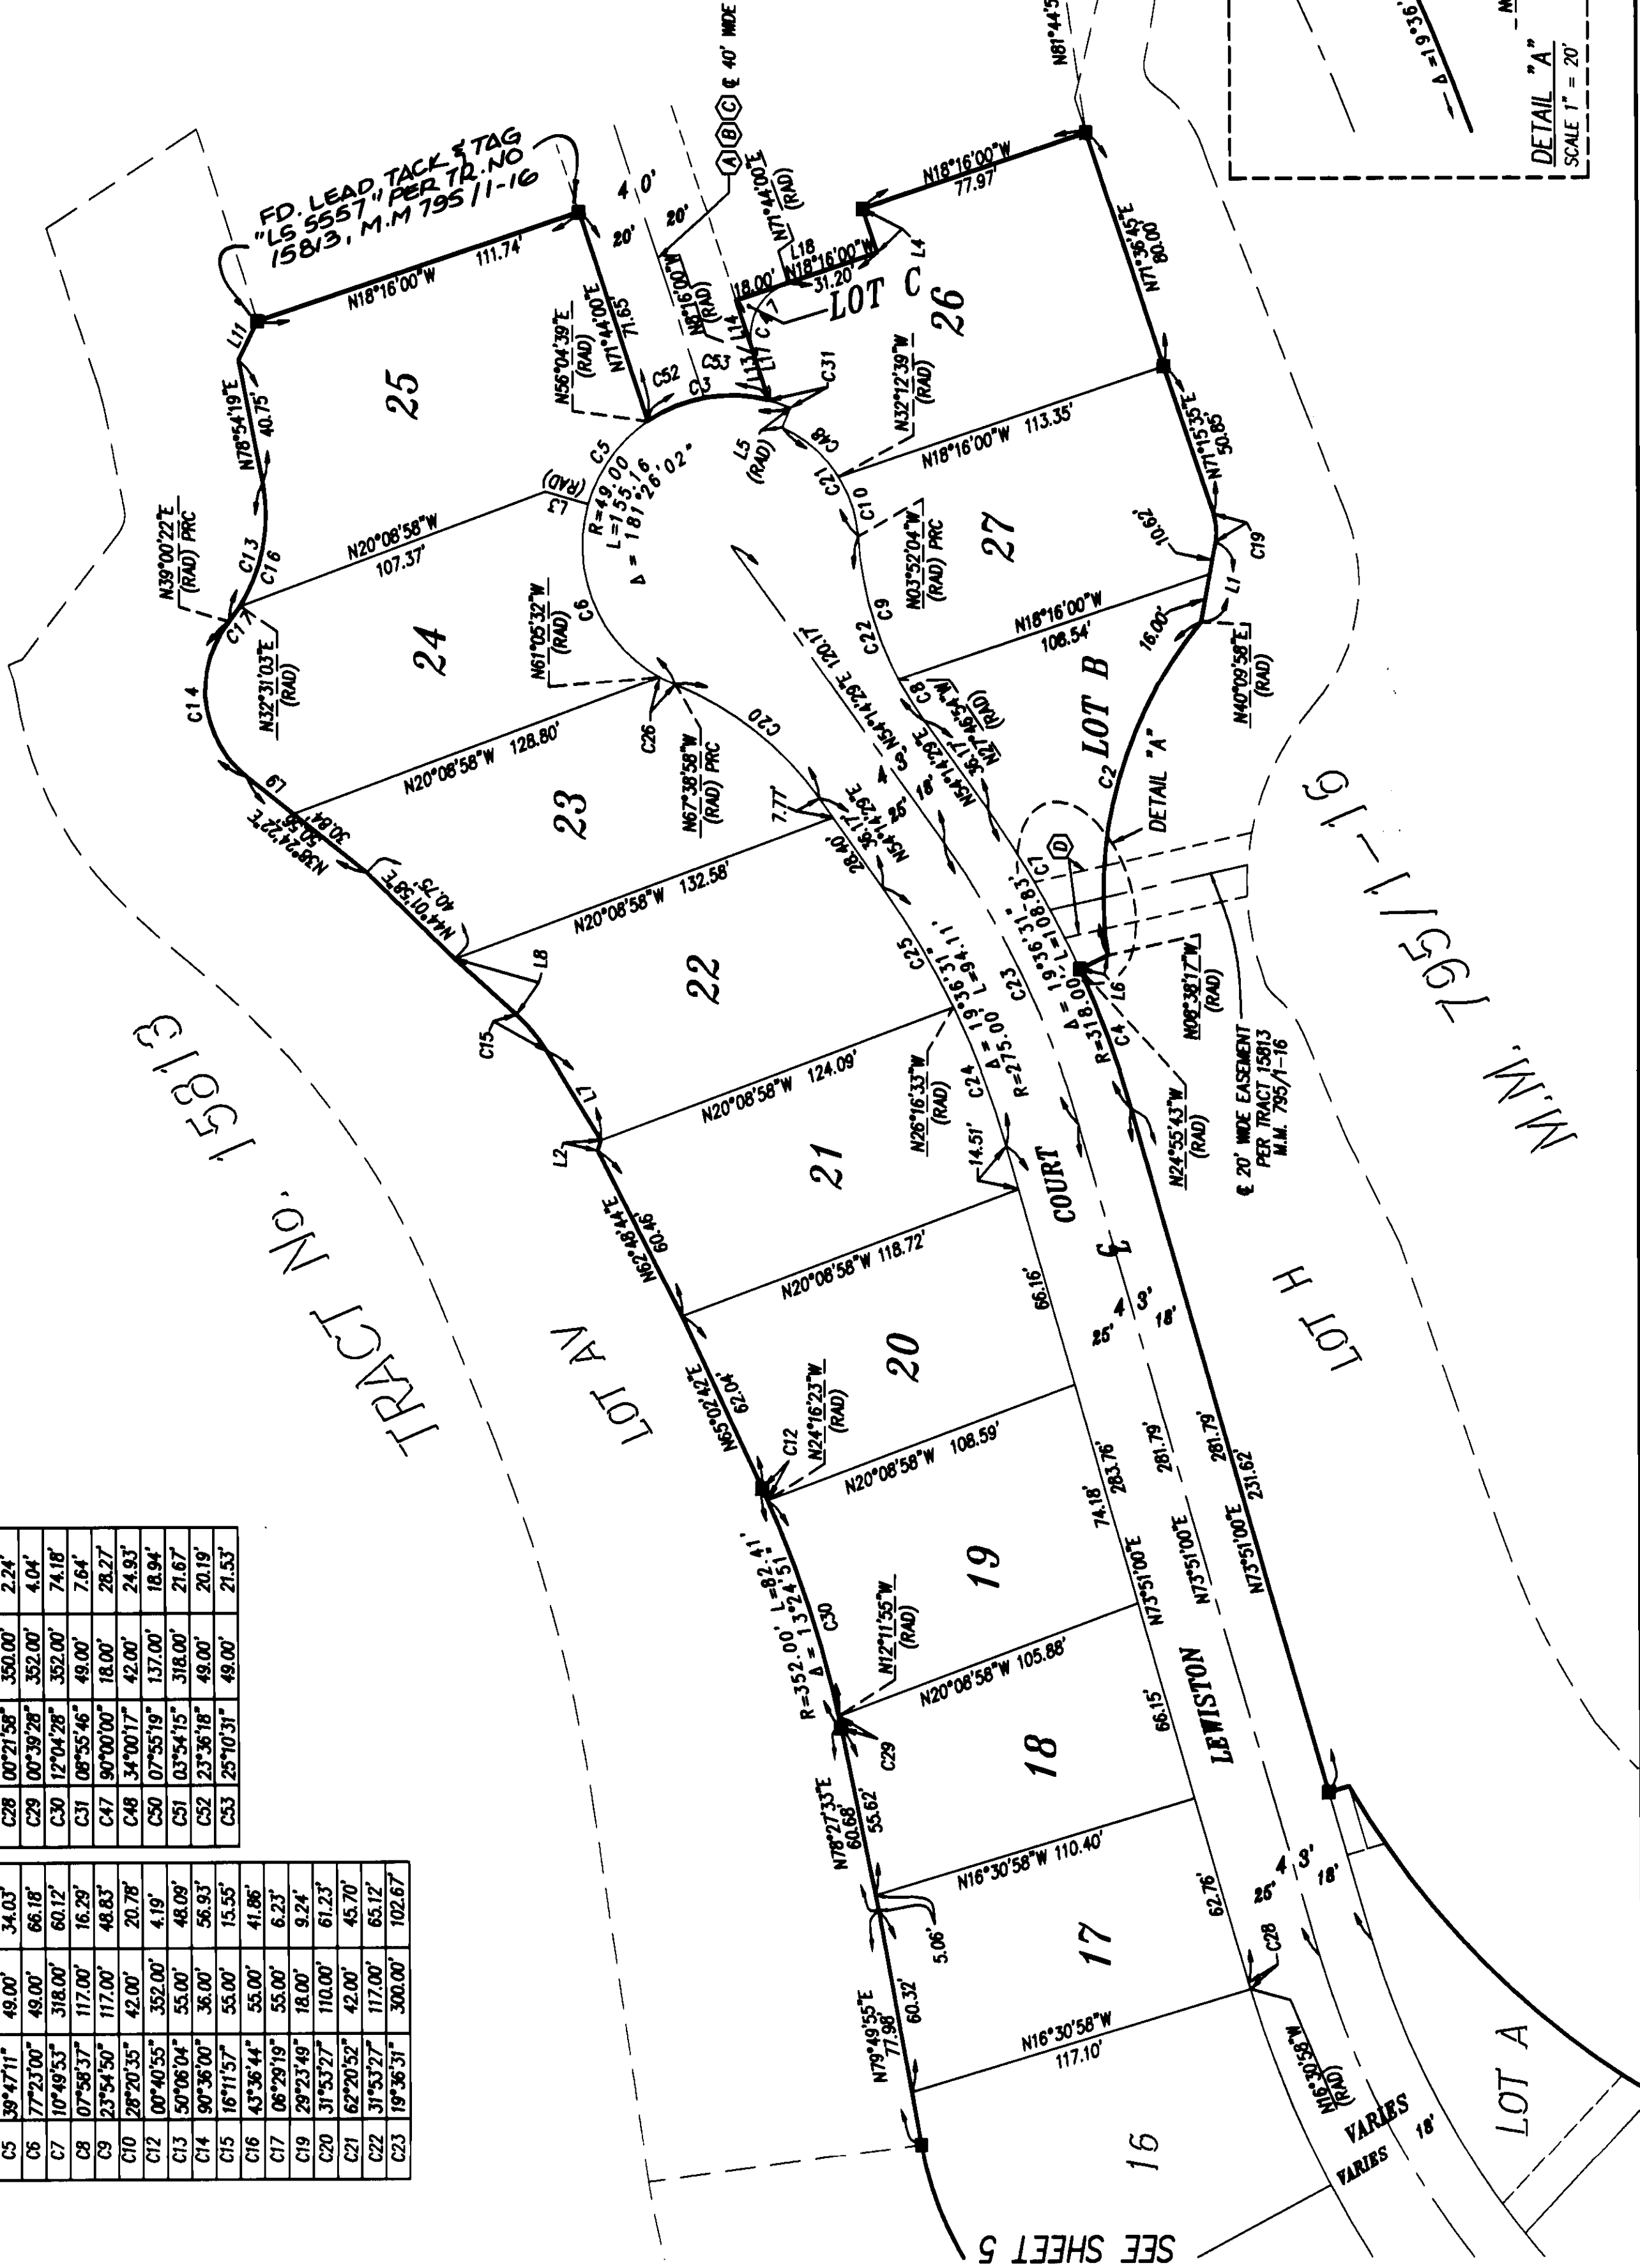

NOTES:
SEE SHEET 2 FOR BASIS OF BEARING, DATUM STATEMENT,
MONUMENT NOTES, EASEMENT NOTES AND OCS GPS BOUNDARY
CONTROL MAP.

SEE SHEET 3 FOR SHEET INDEX AND NOTES

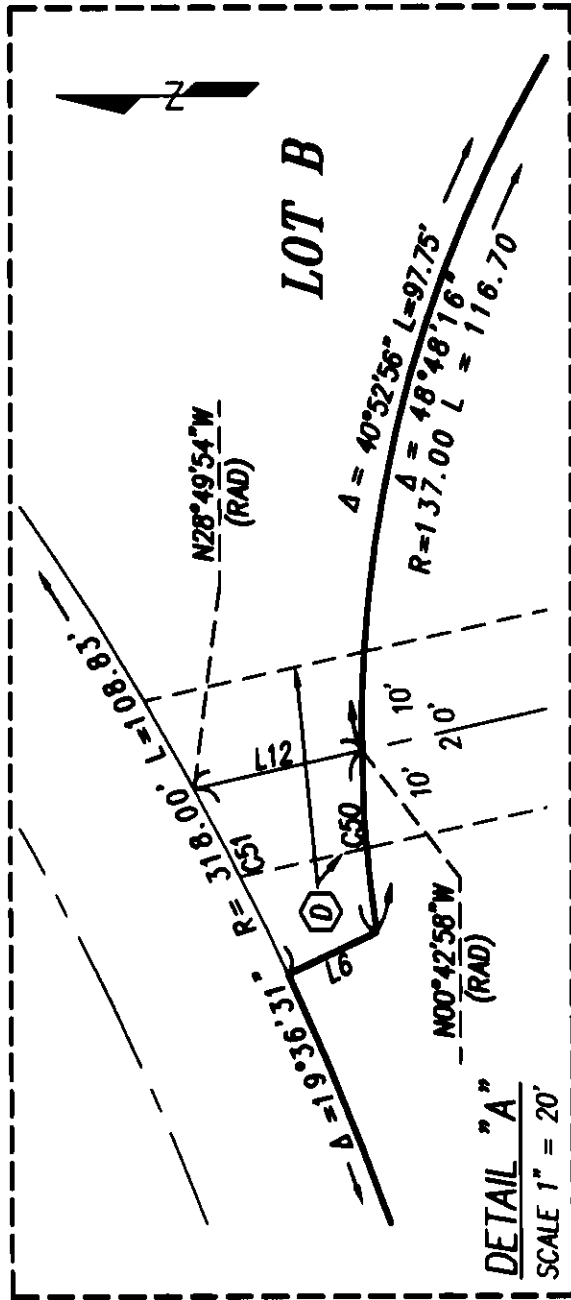


P:\LAND\PCA\TH\002\MP\TV\TR15908\KZ\TM920304.dwg 25 APR 2001

SHEET 5 OF 6 SHEETS
ALL OF TENTATIVE TRACT No. 15908
TOTAL LOTS: 33 NUMBERED LOTS AND 3 LETTERED LOTS
TOTAL ACRES: 9.555 ACRES

NOTES:
SEE SHEET 2 FOR BASIS OF BEARING, DATUM STATEMENT,
MONUMENT NOTES, EASEMENT NOTES AND OCS GPS BOUNDARY
CONTROL MAP.
SEE SHEET 3 FOR SHEET INDEX, AND NOTES

CURVE TABLE			
CURVE	DELTA	RADIUS	LENGTH
C1	07°10'35"	426.00'	53.36'
C2	50°08'32"	42.00'	36.77'
C4	29°04'00"	80.00'	40.58'
C5	10°07'42"	266.00'	41.02'
C6	09°51'38"	271.00'	46.64'
C7	14°07'43"	215.00'	53.02'
C8	13°39'54"	277.00'	66.08'
C9	12°34'44"	253.00'	55.54'
C10	60°22'40"	50.00'	52.69'
C11	25°55'02"	100.00'	45.23'
C12	26°01'45"	113.00'	51.34'
C13	15°54'22"	329.00'	91.34'
C14	17°29'53"	200.00'	61.08'
C15	14°11'45"	200.00'	49.55'
C16	14°40'27"	100.00'	25.61'
C17	10°54'40"	200.00'	38.09'
C18	103°27'14"	50.00'	90.28'
C19	31°49'43"	100.00'	55.55'
C20	27°14'17"	100.00'	47.54'
C21	04°58'00"	200.00'	17.34'
C22	09°13'45"	200.00'	32.22'
C23	05°47'13"	350.00'	35.35'
C24	09°34'15"	350.00'	58.46'
C25	09°56'47"	350.00'	60.76'
C26	11°24'29"	350.00'	69.69'
C27	00°21'50"	350.00'	2.24'
C28	00°46'04"	426.00'	5.71'
C29	24°33'44"	80.00'	34.30'
C30	04°30'16"	80.00'	6.29'
C31	02°52'00"	282.00'	14.11'
C32	03°01'41"	245.00'	12.95'
C34	06°24'31"	426.00'	47.85'

LINE TABLE		
LINE	BEARING	LENGTH
L1	N46°34'42"E	5.73'
L2	N29°11'28"E	28.02'
L3	N26°39'27"W	2.82'
L4	N17°01'16"E	3.95'
L5	N00°25'52"W	10.35'
L6	N89°28'12"W	4.45'
L7	N09°41'44"E	25.58'
L8	N16°09'00"W	6.87'
L9	N79°49'55"E	17.65'
L10	N52°45'41"E	6.55'
L11	N42°08'01"E	6.76'

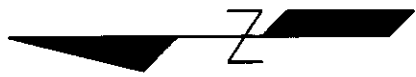


SCALE 1"=40'

TRACT NO. 15908

IN THE UNINCORPORATED TERRITORY OF THE COUNTY OF ORANGE,
STATE OF CALIFORNIA

TETRA TECH, INC. EUGENE A. SHAFFER, L.S. 4644
DATE OF SURVEY: APRIL, 2000

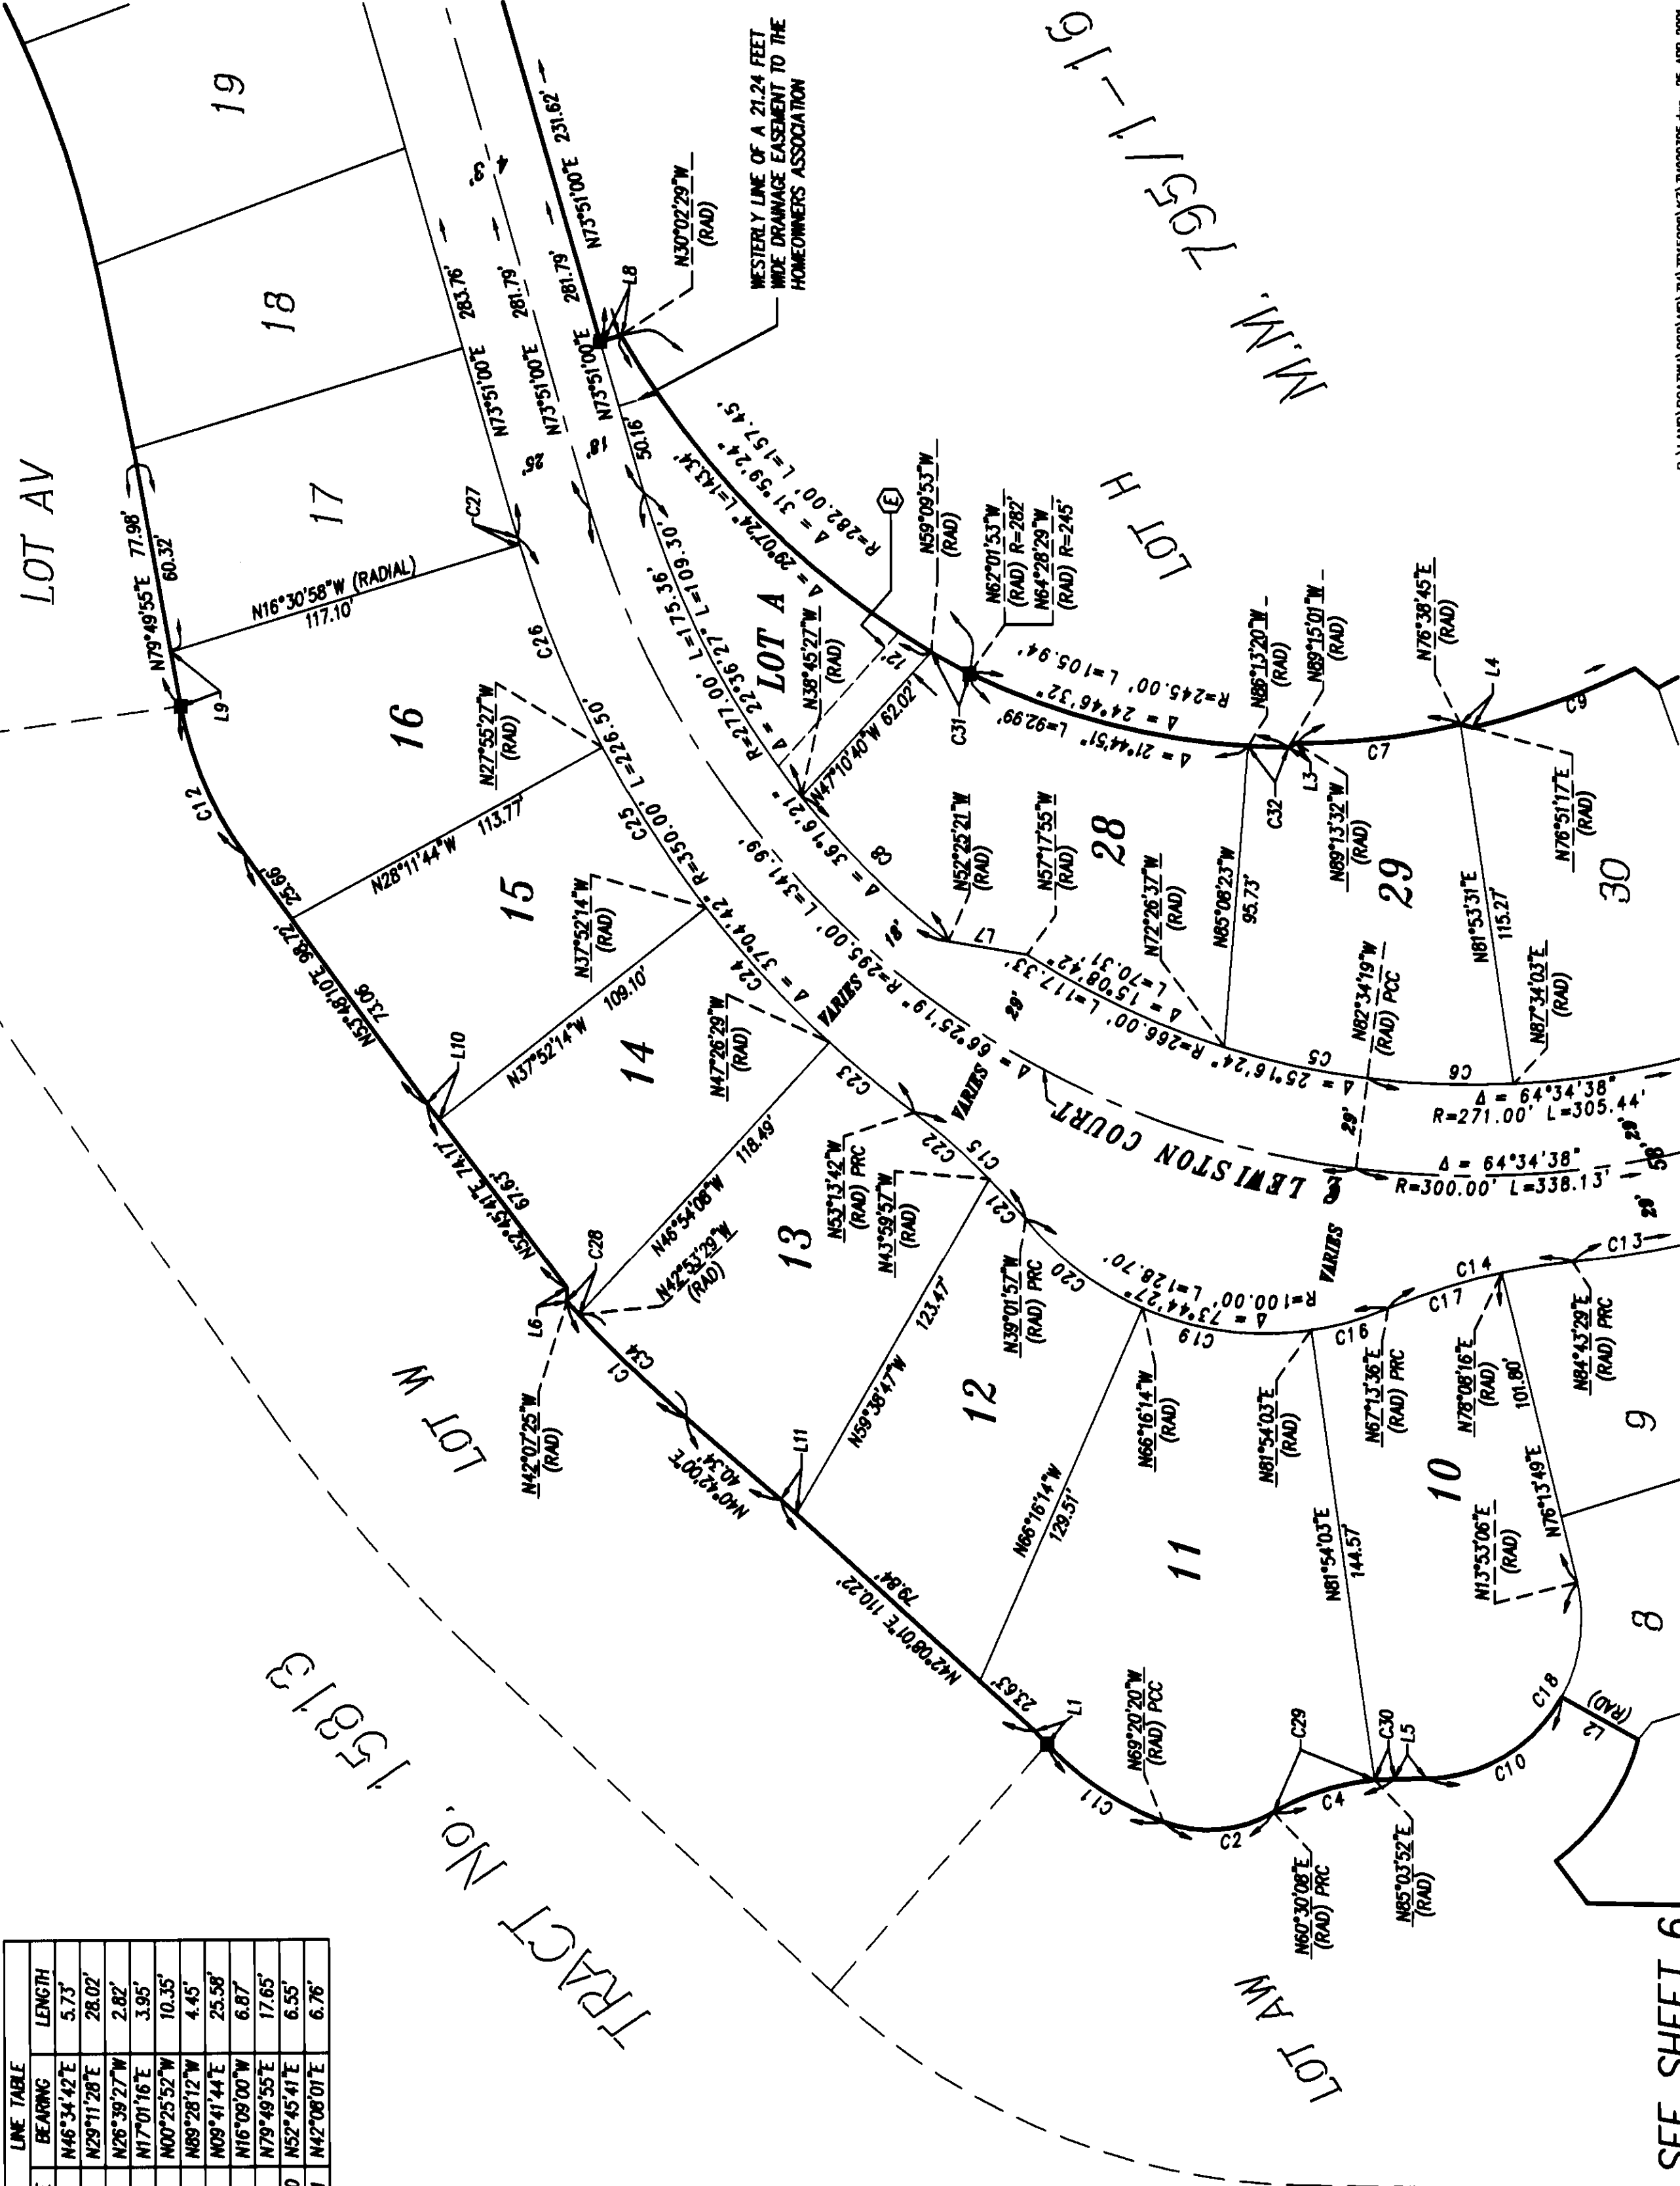

SEE SHEET 6

SEE SHEET 4

028

TRACT No. 15813

TETRA TECH, INC. EUGENE A. SHAFFER, L.S. 4644
DATE OF SURVEY: APRIL, 2000

LINE TABLE		
LINE	BEARING	LENGTH
L1	N29°11'20"E	20.02'
L2	N01°02'00"E	36.41'
L3	N85°46'07"E	58.20'
L4	N39°51'21"E	9.57'
L5	N07°46'33"E	11.25'
L7	N46°29'36"W	24.38'
L8	N41°21'27"W	16.37'
L9	N12°53'04"E	9.54'
L10	N31°36'37"E	13.73'
L11	N35°31'46"E	7.44'
L12	N72°32'12"E	2.70'
L14	N74°53'18"W	18.18'
L15	N32°10'46"W	32.53'
L16	N15°47'21"E	49.27'
L17	N59°07'00"W	21.52'
L18	N57°05'15"W	17.20'
L19	N41°02'20"E	21.03'
L20	N89°13'25"E	7.23'
L22	N53°43'06"E	16.83'
L24	N61°19'47"W	27.76'
L25	N39°20'53"W	0.63'
L27	N76°13'49"W	21.63'
L28	N17°01'16"E	3.95'
L29	N51°20'15"W	7.03'
L30	S15°47'21"E	10.76'
L32	S31°36'37"E	4.16'
L33	S31°36'37"E	9.57'
L34	S35°31'46"W	5.02'
L35	N61°19'47"W	35.60'
L36	N46°29'36"W	8.67'

LINE TABLE		
LINE	BEARING	LENGTH
L1	N29°11'20"E	20.02'
L2	N01°02'00"E	36.41'
L3	N85°46'07"E	58.20'
L4	N39°51'21"E	9.57'
L5	N07°46'33"E	11.25'
L7	N46°29'36"W	24.38'
L8	N41°21'27"W	16.37'
L9	N12°53'04"E	9.54'
L10	N31°36'37"E	13.73'
L11	N35°31'46"E	7.44'
L12	N72°32'12"E	2.70'
L14	N74°53'18"W	18.18'
L15	N32°10'46"W	32.53'
L16	N15°47'21"E	49.27'
L17	N59°07'00"W	21.52'
L18	N57°05'15"W	17.20'
L19	N41°02'20"E	21.03'
L20	N89°13'25"E	7.23'
L22	N53°43'06"E	16.83'
L24	N61°19'47"W	27.76'
L25	N39°20'53"W	0.63'
L27	N76°13'49"W	21.63'
L28	N17°01'16"E	3.95'
L29	N51°20'15"W	7.03'
L30	S15°47'21"E	10.76'
L32	S31°36'37"E	4.16'
L33	S31°36'37"E	9.57'
L34	S35°31'46"W	5.02'
L35	N61°19'47"W	35.60'
L36	N46°29'36"W	8.67'

SEE SHEET 3 FOR SHEET INDEX, AND NOTES

SEE SHEET 3 FOR SHEET INDEX, AND NOTES

