

SHEET 1 OF 6 SHEETS
ALL OF TENTATIVE TRACT No. 15909
TOTAL LOTS: 38 NUMBERED LOTS AND 5 LETTERED LOTS
TOTAL ACREAGE: 10.350 ACRES

BLOCK 5157 MODULE 4 AND 5

TRACT NO. 15909

IN THE UNINCORPORATED TERRITORY OF THE COUNTY OF ORANGE,
STATE OF CALIFORNIA

BEING A SUBDIVISION OF LOT 10 OF TRACT NO. 15813, AS SHOWN ON A MAP FILED IN BOOK 795,
PAGES 1 TO 16 INCLUSIVE OF MISCELLANEOUS MAPS, RECORDS OF ORANGE COUNTY, CALIFORNIA.

TETRA TECH, INC. EUGENE A. SHAFFER, L.S. 4644
DATE OF SURVEY: APRIL, 2000

ACCEPTED AND FILED AT THE
REQUEST OF
FIRST AMERICAN TITLE INSURANCE CO.

DATE JUNE 29, 2001
TIME 3:25 P.M. FEE \$ 17.00
INSTRUMENT # 20010437010
BOOK 820 PAGE 29-34 M/M

GARY L. GRANVILLE
COUNTY CLERK RECORDER
BY [Signature]
DEPUTY

OWNER'S CERTIFICATE

WE THE UNDERSIGNED, BEING ALL PARTIES HAVING ANY RECORD TITLE INTEREST IN THE LAND COVERED BY THIS MAP, DO HEREBY CONSENT TO THE PREPARATION AND RECORDATION OF SAID MAP, AS SHOWN WITHIN THE DISTINCTIVE BORDER LINE. WE ALSO HEREBY DEDICATE TO THE PUBLIC FOR STREET PURPOSES:
MERRILL HILL, STRATHMORE AND WESTFORD.

SURVEYOR'S STATEMENT

I HEREBY STATE THAT THIS MAP, CONSISTING OF 6 SHEETS, CORRECTLY REPRESENTS TRUE AND COMPLETE SURVEY AS SHOWN MADE IN APRIL, 2000, WAS MADE BY ME OR UNDER MY DIRECTION; THAT THE MONUMENTS ARE OF THE CHARACTER AND OCCUPY (OR WILL OCCUPY) THE POSITIONS INDICATED BY SAID MAP; AND THAT SAID MONUMENTS ARE (OR WILL BE) SUFFICIENT TO ENABLE THE SURVEY TO BE RETRACED.

EUGENE A. SHAFFER, L.S. 4644
EXPIRES 9-30-2002

COUNTY SURVEYOR'S STATEMENT

I HEREBY STATE THAT I HAVE EXAMINED THIS MAP AND HAVE FOUND IT TO BE SUBSTANTIALLY IN CONFORMANCE WITH THE TENTATIVE MAP AS FILED WITH, AMENDED AND APPROVED BY THE ORANGE COUNTY SUBDIVISION COMMITTEE; THAT ALL PROVISIONS OF THE SUBDIVISION MAP ACT AND COUNTY SUBDIVISION REGULATIONS HAVE BEEN COMPLIED WITH AND I AM SATISFIED SAID MAP IS TECHNICALLY CORRECT.

DATED THIS 18TH DAY OF JUNE, 2001.

[Signature]
JOHN CANAS, COUNTY SURVEYOR
L.S. 4408 EXPIRATION DATE: 9-30-01



CENTEX HOMES, A NEVADA GENERAL PARTNERSHIP

BY: CENTEX REAL ESTATE CORPORATION
A NEVADA CORPORATION,
ITS MANAGING GENERAL PARTNER

[Signature]
BY: ROLAND F. OSGOOD
PRESIDENT, SOUTH COAST DIVISION

[Signature]
By: Martin Juliossen
Assistant Secretary

DMB LADERA, L.L.C., A DELAWARE LIMITED LIABILITY COMPANY
BENEFICIARY UNDER A DEED OF TRUST RECORDED OCTOBER 3, 2000, AS INSTRUMENT NO. 20000525919
OF OFFICIAL RECORDS.

BY: RANCHO MISSION VIEJO, L.L.C., A DELAWARE LIMITED LIABILITY COMPANY
AS AGENT OR MANAGER

[Signature]
PRINT NAME: Paul Johnson
PRINT TITLE: VP - Community Development

[Signature]
PRINT NAME: Richard Broming
PRINT TITLE: VP - Planning & Entitlement


CLERK OF THE BOARD OF SUPERVISORS' CERTIFICATE

STATE OF CALIFORNIA }
COUNTY OF ORANGE } ss

I HEREBY CERTIFY THAT THIS MAP WAS PRESENTED FOR APPROVAL TO THE BOARD OF SUPERVISORS OF ORANGE COUNTY AT A REGULAR MEETING THEREOF HELD ON THE 26TH DAY OF JUNE, 2001, AND THAT THEREUPON SAID BOARD DID, BY AN ORDER DULY PASSED AND ENTERED, APPROVED SAID MAP AND DID ACCEPT ON BEHALF OF THE PUBLIC, SUBJECT TO IMPROVEMENTS: THE DEDICATION FOR STREET PURPOSES OF **MERRILL HILL, STRATHMORE, AND WESTFORD.**

DATED THIS 26TH DAY OF JUNE, 2001.

[Signature]
DARLENE J. BLOOM
CLERK OF THE BOARD OF SUPERVISORS

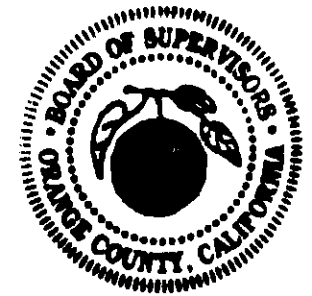

NOTARY ACKNOWLEDGMENT

STATE OF CALIFORNIA }
COUNTY OF ORANGE } ss

ON THIS 30TH DAY OF April, 2001, BEFORE ME, Rhonda Keiger Painter A NOTARY PUBLIC IN AND FOR SAID STATE, PERSONALLY APPEARED ROLAND F. OSGOOD PERSONALLY KNOWN TO ME TO BE THE PERSON WHOSE NAME IS SUBSCRIBED TO THE WITHIN INSTRUMENT AND ACKNOWLEDGED TO ME THAT HE EXECUTED THE SAME IN HIS AUTHORIZED CAPACITY, AND THAT BY HIS SIGNATURE ON THE INSTRUMENT THE PERSON OR THE ENTITY UPON BEHALF OF WHICH THE PERSON ACTED, EXECUTED THE INSTRUMENT.

* and Martin Juliossen

WITNESS MY HAND:

[Signature]
NOTARY PUBLIC IN AND FOR SAID STATE

Rhonda Keiger Painter
PRINT NAME

MY PRINCIPAL PLACE OF BUSINESS IS IN Orange COUNTY.

MY COMMISSION EXPIRES: 12/9/03

NOTARY ACKNOWLEDGEMENT FOR DMB LADERA, LLC:

STATE OF California }
COUNTY OF Orange } ss

ON JUNE 15, 2001, BEFORE ME, LINDA K. LEDGER A NOTARY PUBLIC IN AND FOR SAID STATE PERSONALLY APPEARED Paul Johnson AND Richard Broming PERSONALLY KNOWN TO ME TO BE THE PERSONS WHOSE NAMES ARE SUBSCRIBED TO THE WITHIN INSTRUMENT AND ACKNOWLEDGED TO ME THAT THEY EXECUTED THE SAME IN THEIR AUTHORIZED CAPACITIES AND THAT BY THEIR SIGNATURES ON THE INSTRUMENT THE PERSONS, OR THE ENTITY UPON BEHALF OF WHICH THE PERSONS ACTED EXECUTED THE INSTRUMENT.

WITNESS MY HAND:

[Signature]
NOTARY PUBLIC IN AND FOR SAID STATE

LINDA K. LEDGER
(NAME PRINTED)

MY PRINCIPAL PLACE OF BUSINESS IS
IN DAN JUAN CARABAY, ORANGE, CA
MY COMMISSION EXPIRES: 3/7/03

COUNTY TREASURER-TAX COLLECTOR'S CERTIFICATE

STATE OF CALIFORNIA }
COUNTY OF ORANGE } ss

I HEREBY CERTIFY THAT ACCORDING TO THE RECORDS OF MY OFFICE THERE ARE NO LIENS AGAINST THE LAND COVERED BY THIS MAP OR ANY PART THEREOF FOR UNPAID STATE, COUNTY, MUNICIPAL OR LOCAL TAXES OR SPECIAL ASSESSMENTS COLLECTED AS TAXES, EXCEPT TAXES OR SPECIAL ASSESSMENTS COLLECTED AS TAXES NOT YET PAYABLE.

AND DO ALSO CERTIFY TO THE RECORDER OF ORANGE COUNTY THAT THE PROVISIONS OF THE SUBDIVISION MAP ACT HAVE BEEN COMPLIED WITH REGARDING DEPOSITS TO SECURE THE PAYMENT OF TAXES OR SPECIAL ASSESSMENTS COLLECTED AS TAXES ON THE LAND COVERED BY THIS MAP.

DATED THIS 24TH DAY OF May, 2001.

JOHN M.W. MOORLACH
COUNTY TREASURER-TAX COLLECTOR

BY: [Signature]
DEPUTY TREASURER-TAX COLLECTOR

SIGNATURE OMISSIONS:

IN ACCORDANCE WITH THE PROVISIONS OF SECTION 66436(a) (3) OF THE SUBDIVISION MAP ACT, THE FOLLOWING SIGNATURES HAVE BEEN OMITTED:

1. LADERA DEVELOPMENT COMPANY, L.L.C., HOLDER OF OIL, GAS, MINERAL, AND WATER RIGHTS RECORDED DECEMBER 10, 1996 AS INSTRUMENT NO. 19960624029 OF OFFICIAL RECORDS.

AUTOMATIC FIRE SPRINKLER NOTE

ALL COMMERCIAL STRUCTURES GREATER THAN 6000 SQUARE FEET; ALL MULTIFAMILY RESIDENCE STRUCTURES; ALL SINGLE-FAMILY STRUCTURES EXCEEDING 5500 SQUARE FEET, AND ALL STRUCTURES EXCEEDING FIRE DEPARTMENT ACCESS REQUIREMENTS SHALL BE PROTECTED BY AN AUTOMATIC FIRE SPRINKLER SYSTEM.

SPECIAL FIRE PROTECTION NOTE

PROPERTY IS IN A SPECIAL FIRE PROTECTION AREA AND MUST MEET ALL REQUIREMENTS FOR DEVELOPMENT WITHIN THE AREA.

HIGH FIRE HAZARD AREA NOTE

THE LOTS SHOWN ON THIS MAP ARE IN A HIGH FIRE HAZARD AREA DUE TO WILD LAND EXPOSURE

SHEET 2 OF 6 SHEETS
ALL OF TENTATIVE TRACT No. 15909
TOTAL LOTS: 38 NUMBERED LOTS AND 5 LETTERED LOTS
TOTAL ACREAGE: 10.350 ACRES

TRACT NO. 15909


IN THE UNINCORPORATED TERRITORY OF THE COUNTY OF ORANGE,
STATE OF CALIFORNIA

TETRA TECH, INC. EUGENE A. SHAFFER, L.S. 4644
DATE OF SURVEY: APRIL, 2000



SCALE 1"=300'

BOUNDARY
CONTROL MAP

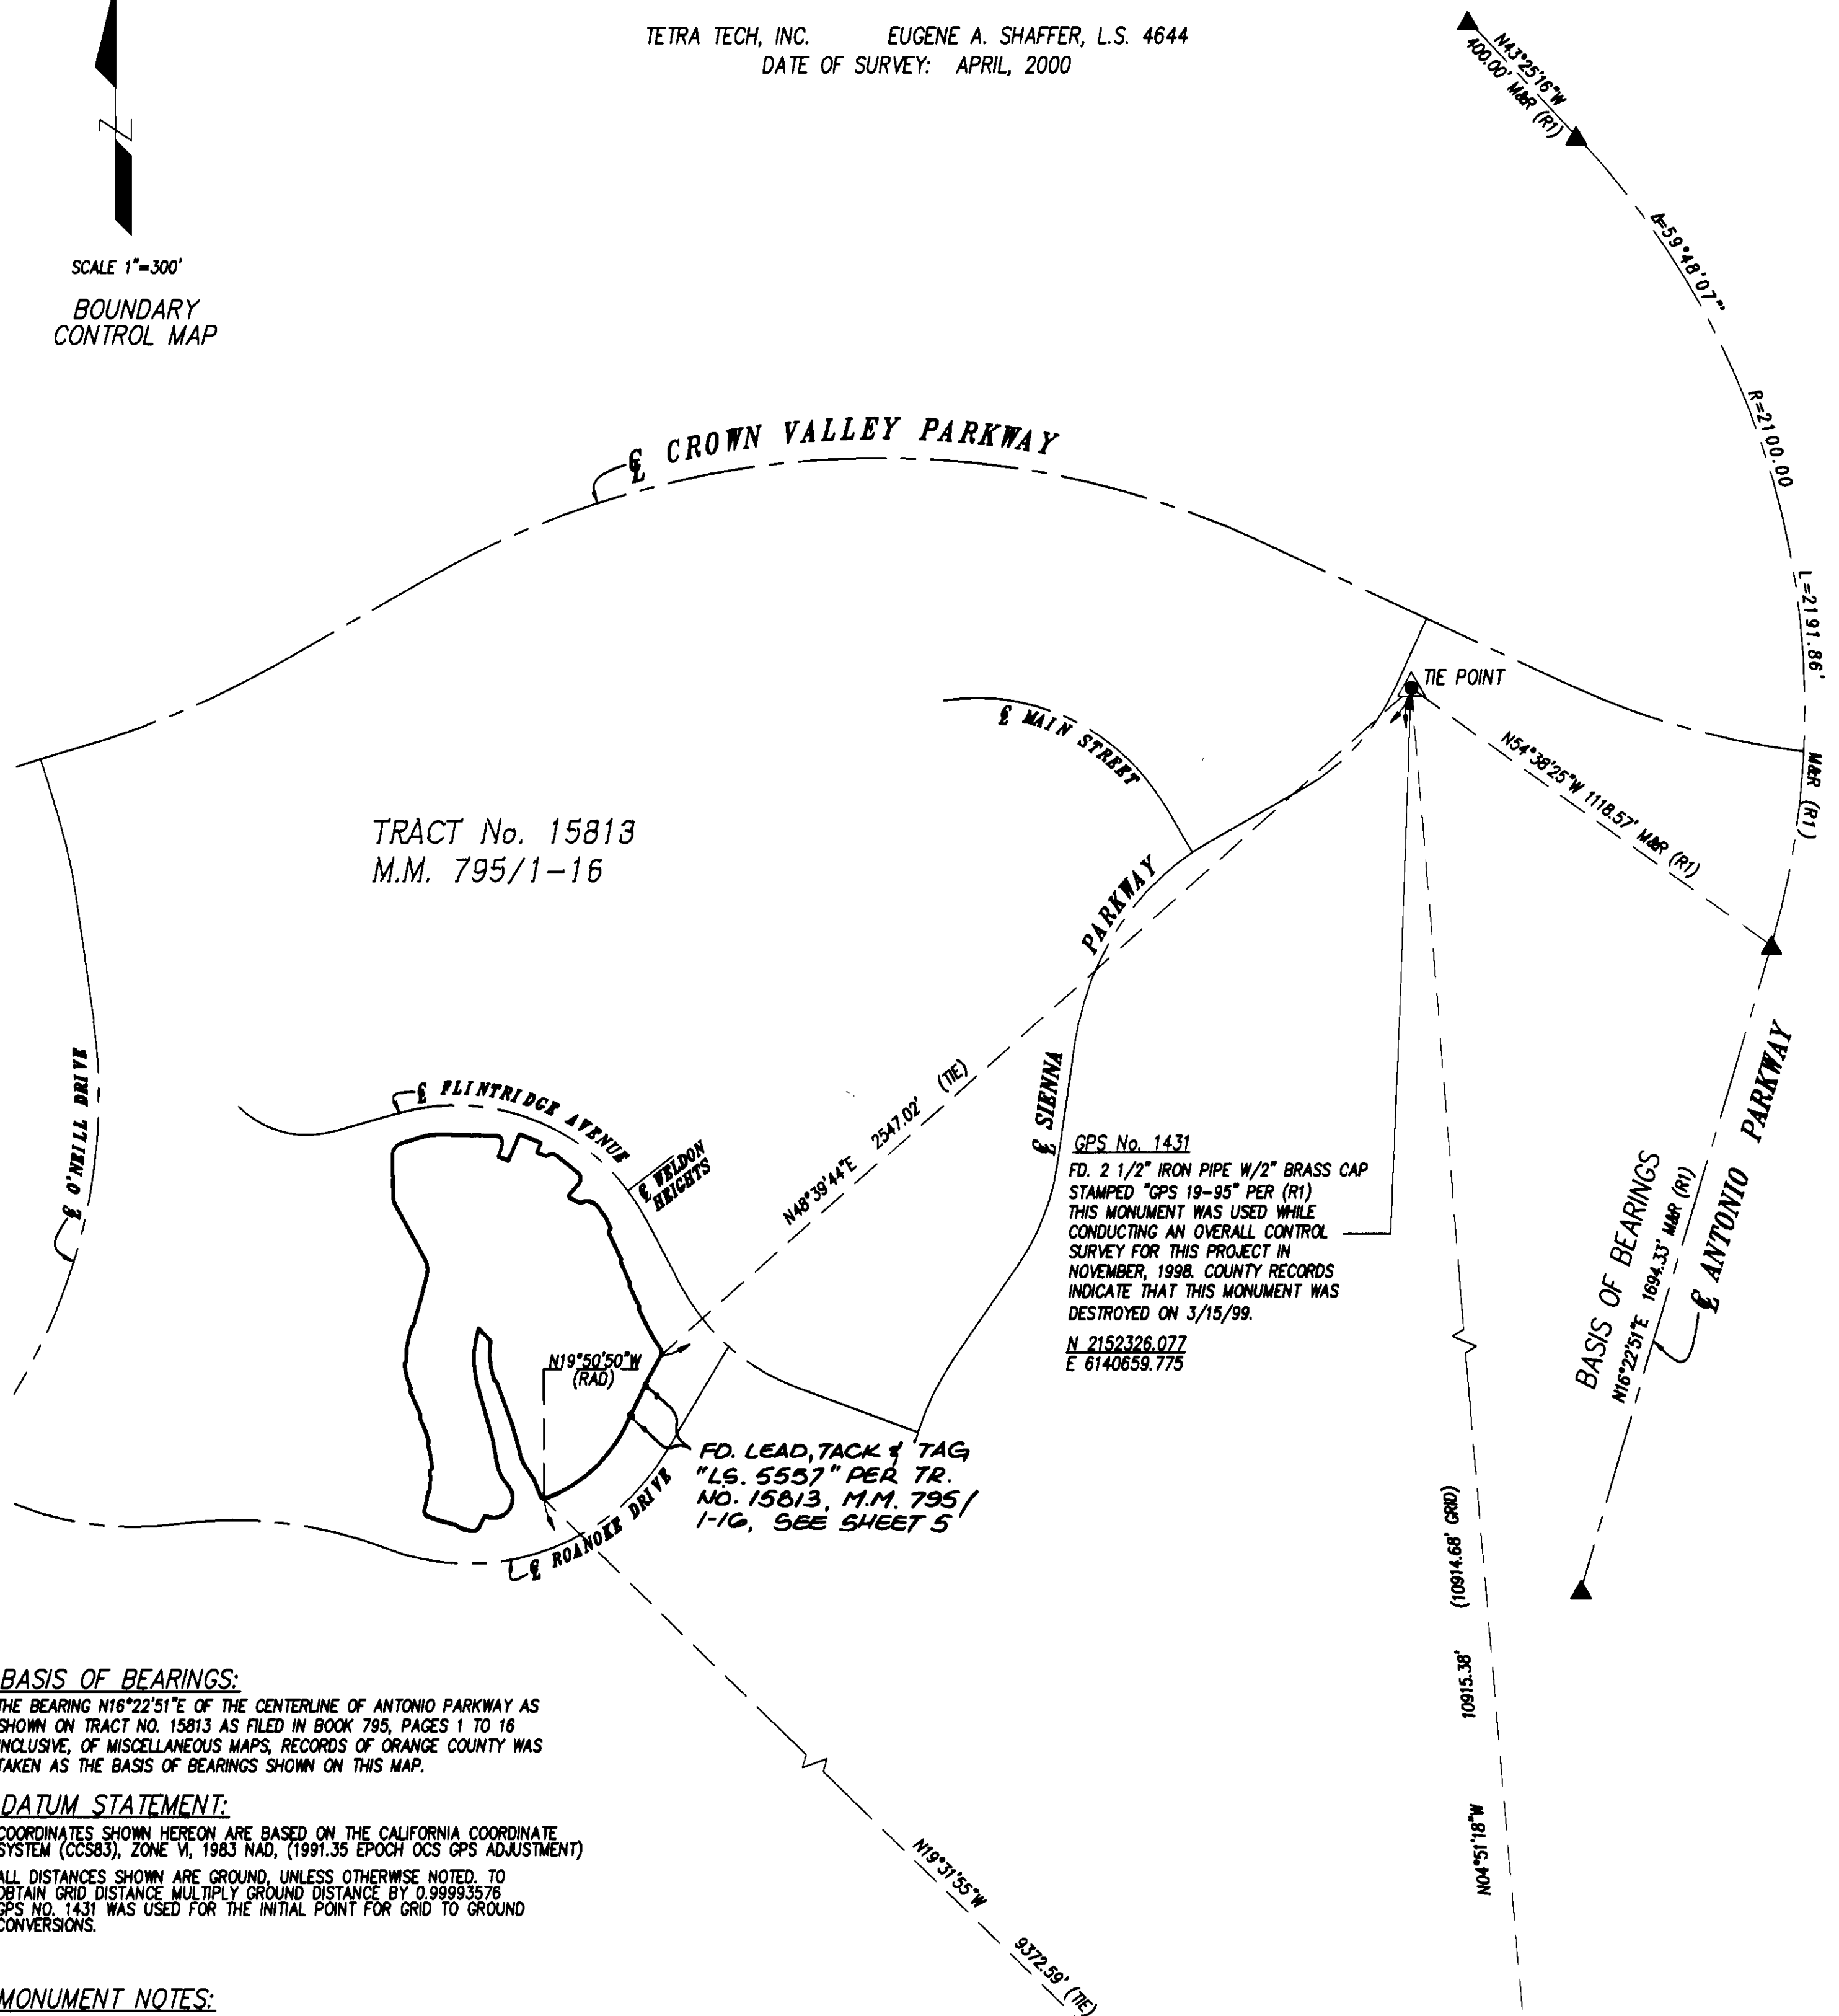

BASIS OF BEARINGS:

THE BEARING N16°22'51"E OF THE CENTERLINE OF ANTONIO PARKWAY AS SHOWN ON TRACT NO. 15813 AS FILED IN BOOK 795, PAGES 1 TO 16 INCLUSIVE, OF MISCELLANEOUS MAPS, RECORDS OF ORANGE COUNTY WAS TAKEN AS THE BASIS OF BEARINGS SHOWN ON THIS MAP.

DATUM STATEMENT:

COORDINATES SHOWN HEREON ARE BASED ON THE CALIFORNIA COORDINATE SYSTEM (CCS83), ZONE VI, 1983 NAD, (1991.35 EPOCH OCS GPS ADJUSTMENT)

ALL DISTANCES SHOWN ARE GROUND, UNLESS OTHERWISE NOTED. TO OBTAIN GRID DISTANCE MULTIPLY GROUND DISTANCE BY 0.99993576
GPS NO. 1431 WAS USED FOR THE INITIAL POINT FOR GRID TO GROUND CONVERSIONS.

MONUMENT NOTES:

- - INDICATES LOCATION OF 1" I.P. TAGGED "LS 5557" OR SPK. AND WASHER STAMPED "LS 5557" OR LEAD AND TACK TAG "LS 5557" TO BE SET PER TRACT 15813, M.M. 795/1-16 UNLESS OTHERWISE NOTED.
 - - INDICATES LOCATION OF 2" I.P. TAGGED "LS 5557" OR SPK. AND WASHER STAMPED "LS 5557" OR LEAD AND TACK TAG "LS 5557" TO BE SET PER TRACT 15813, M.M. 795/1-16
 - ▲ - INDICATES FD. OCS WELL MONUMENT WITH 2 1/2" BRASS CAP STAMPED "ORANGE COUNTY SURVEYOR" PER (R1)
- 2" I.P. TAGGED "LS 4666" OR LEAD, TACK & TAG "LS 4666" OR NAIL & TAG "LS 4666" OR 8" S&W STAMPED "LS 4666" TO BE SET AT ALL TRACT BOUNDARY CORNERS WITHIN 90 DAYS AFTER ACCEPTANCE OF IMPROVEMENTS, UNLESS OTHERWISE NOTED.
- 1" I.P. TAGGED "LS 4666" OR LEAD, TACK & TAG "LS 4666" OR NAIL & TAG "LS 4666" OR 8" S&W STAMPED "LS 4666" TO BE SET AT ALL LOT CORNERS THAT ARE THE INTERSECTION OF SIDE LOT LINES WITH STREET RIGHT-OF-WAY, WITHIN 90 DAYS AFTER ACCEPTANCE OF IMPROVEMENTS, UNLESS OTHERWISE NOTED.
- 8" S&W STAMPED "LS 4666" OR LEAD, TACK & TAG "LS 4666" OR 1" I.P. TAGGED "LS 4666" IN MEDIAN TO BE SET AT ALL STREET CENTERLINE POINTS OF CONTROL, WITHIN 90 DAYS AFTER ACCEPTANCE OF IMPROVEMENTS, UNLESS OTHERWISE NOTED.

REFERENCES:

REFERENCES:
R1 - TRACT 15813, M.M. 795/1-16

GPS No. 1417

FD. 2 1/2" IRON PIPE W/ 2" BRASS CAP
STAMPED "GPS 1417 9-95" PER (R1)


N 2141450.558
E 6141583.535

SHEET 3 OF 6 SHEETS
 ALL OF TENTATIVE TRACT No. 15909
 TOTAL LOTS: 38 NUMBERED LOTS AND 5 LETTERED LOTS
 TOTAL ACREAGE: 10.350 ACRES


TRACT NO. 15909

IN THE UNINCORPORATED TERRITORY OF THE COUNTY OF ORANGE,
 STATE OF CALIFORNIA

TETRA TECH, INC. EUGENE A. SHAFFER, L.S. 4644
 DATE OF SURVEY: APRIL, 2000

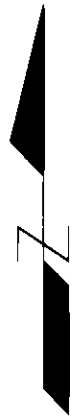


SCALE 1"=100'
 SHEET INDEX MAP

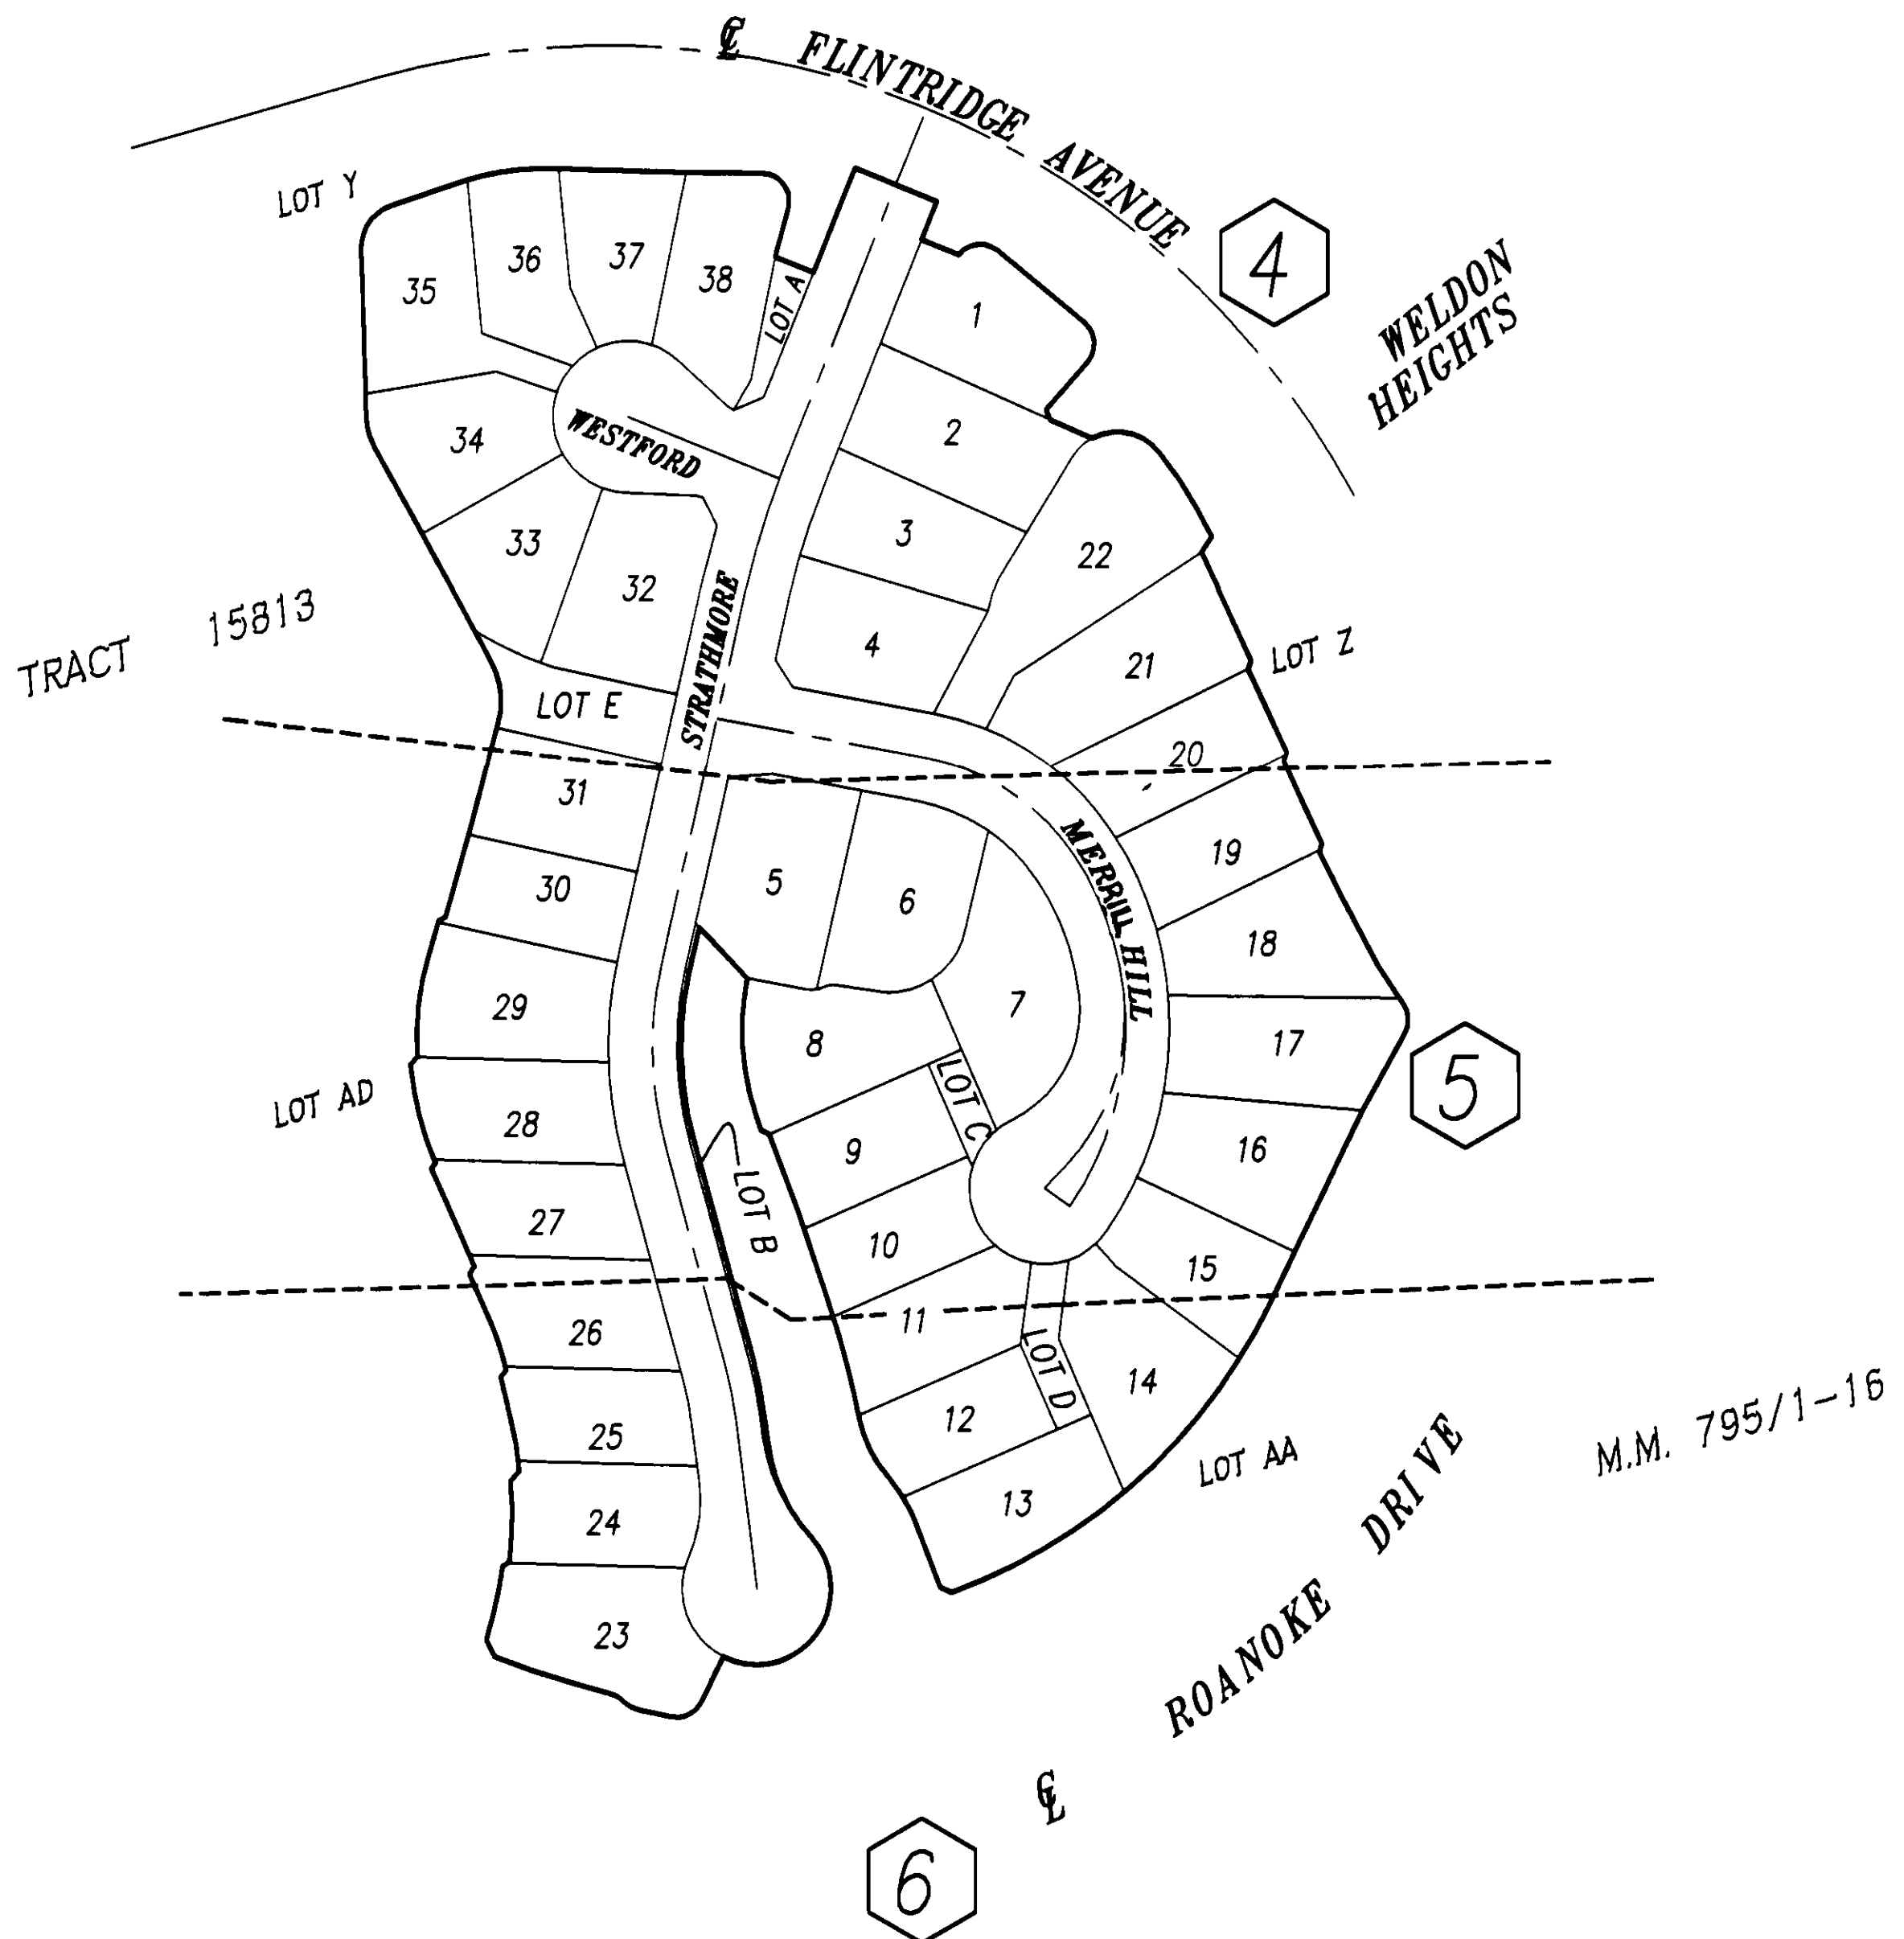

NOTES:

1. LETTERED LOTS A THROUGH E CREATED BY THIS MAP ARE NOT BUILDING SITES.
2. ACREAGE AND INTENDED USE FOR LETTERED LOTS CREATED BY THIS MAP ARE AS FOLLOWS:
 LOT A OPEN SPACE 0.040 AC.
 LOT B OPEN SPACE 0.026 AC.
 LOT C OPEN SPACE 0.035 AC.
 LOT D OPEN SPACE 0.059 AC.
 LOT E OPEN SPACE 0.127 AC.

SEE SHEET 2 FOR BASIS OF BEARING, DATUM STATEMENT,
 MONUMENT NOTES AND OCS GPS BOUNDARY CONTROL MAP.

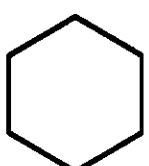

INDICATE SHEET NUMBER

TRACT NO. 15909
IN THE UNINCORPORATED TERRITORY OF THE COUNTY OF ORANGE,
STATE OF CALIFORNIA

TETRA TECH, INC. EUGENE A. SHAFFER, L.S. 4644
DATE OF SURVEY: APRIL, 2000


NOTES:
SEE SHEET 2 FOR BASIS OF BEARING, DATUM STATEMENT,
MONUMENT NOTES AND OCS GPS BOUNDARY CONTROL MAP.
SEE SHEET 3 FOR SHEET INDEX AND EASEMENT NOTES.

LINE TABLE		
LINE	BEARING	DISTANCE
L1	N89°20'15"W	2.55'
L2	N89°46'12"W	2.83'
L3	N01°48'13"W	16.48'
L4	N28°43'26"W	4.57'
L5	N28°43'26"W	22.20'
L28	N33°30'13"W	21.23'
L29	N12°28'52"E	39.13'
L36	N67°27'50"E	21.35'
L37	N67°55'03"W	27.13'
L38	N47°39'29"W	43.44'
L39	N87°12'58"W	46.93'
L40	N26°29'14"W	20.47'
L49	N67°55'03"W	26.10'
L50	N41°18'30"E	40.58'
L51	N21°58'19"W	7.15'
L53	N33°02'03"E	12.06'
L54	N19°29'10"E	5.70'
L82	N70°27'56"W	62.50'
L83	N71°09'16"W	41.76'
L84	N24°22'57"W	42.48'
L85	N15°04'52"E	32.46'
L86	N29°44'36"E	22.53'
L87	N79°16'00"W	15.18'
L95	N27°54'07"E	39.50'
L97	N14°15'28"E	11.30'
L99	N89°46'12"W	12.38'
L100	N14°24'03"E	3.59'
L106	N89°46'12"W	15.22'

SHEET 4 OF 6 SHEETS
ALL OF TENTATIVE TRACT No. 15909
TOTAL LOTS: 38 NUMBERED LOTS AND 5 LETTERED LOTS
TOTAL ACREAGE: 10.350 ACRES

CURVE TABLE		
CURVE	DELTA	LENGTH
C1	104°25'07"	18.00'
C2	17°50'21"	154.00'
C3	00°45'59"	154.00'
C4	73°25'41"	29.00'
C5	27°28'38"	37.00'
C6	43°07'29"	55.00'
C38	15°37'01"	179.00'
C39	11°16'10"	179.00'
C40	03°43'15"	471.00'
C41	05°52'50"	471.00'
C42	19°29'47"	15.00'
C43	23°34'11"	49.00'
C44	43°09'17"	49.00'
C45	23°23'10"	49.00'
C46	23°23'09"	49.00'
C47	48°13'29"	49.00'
C48	40°54'01"	49.00'
C49	16°56'12"	49.00'
C50	17°41'41"	15.00'
C51	04°03'57"	529.00'
C58	90°45'07"	18.00'
C59	91°51'29"	18.00'
C74	01°58'14"	235.29'
C75	11°59'21"	235.29'
C76	30°06'53"	35.00'
C77	12°56'22"	44.42'
C78	09°38'05"	471.00'
C84	13°37'35"	235.29'
C92	110°13'45"	35.00'

795/1-16
M.M.

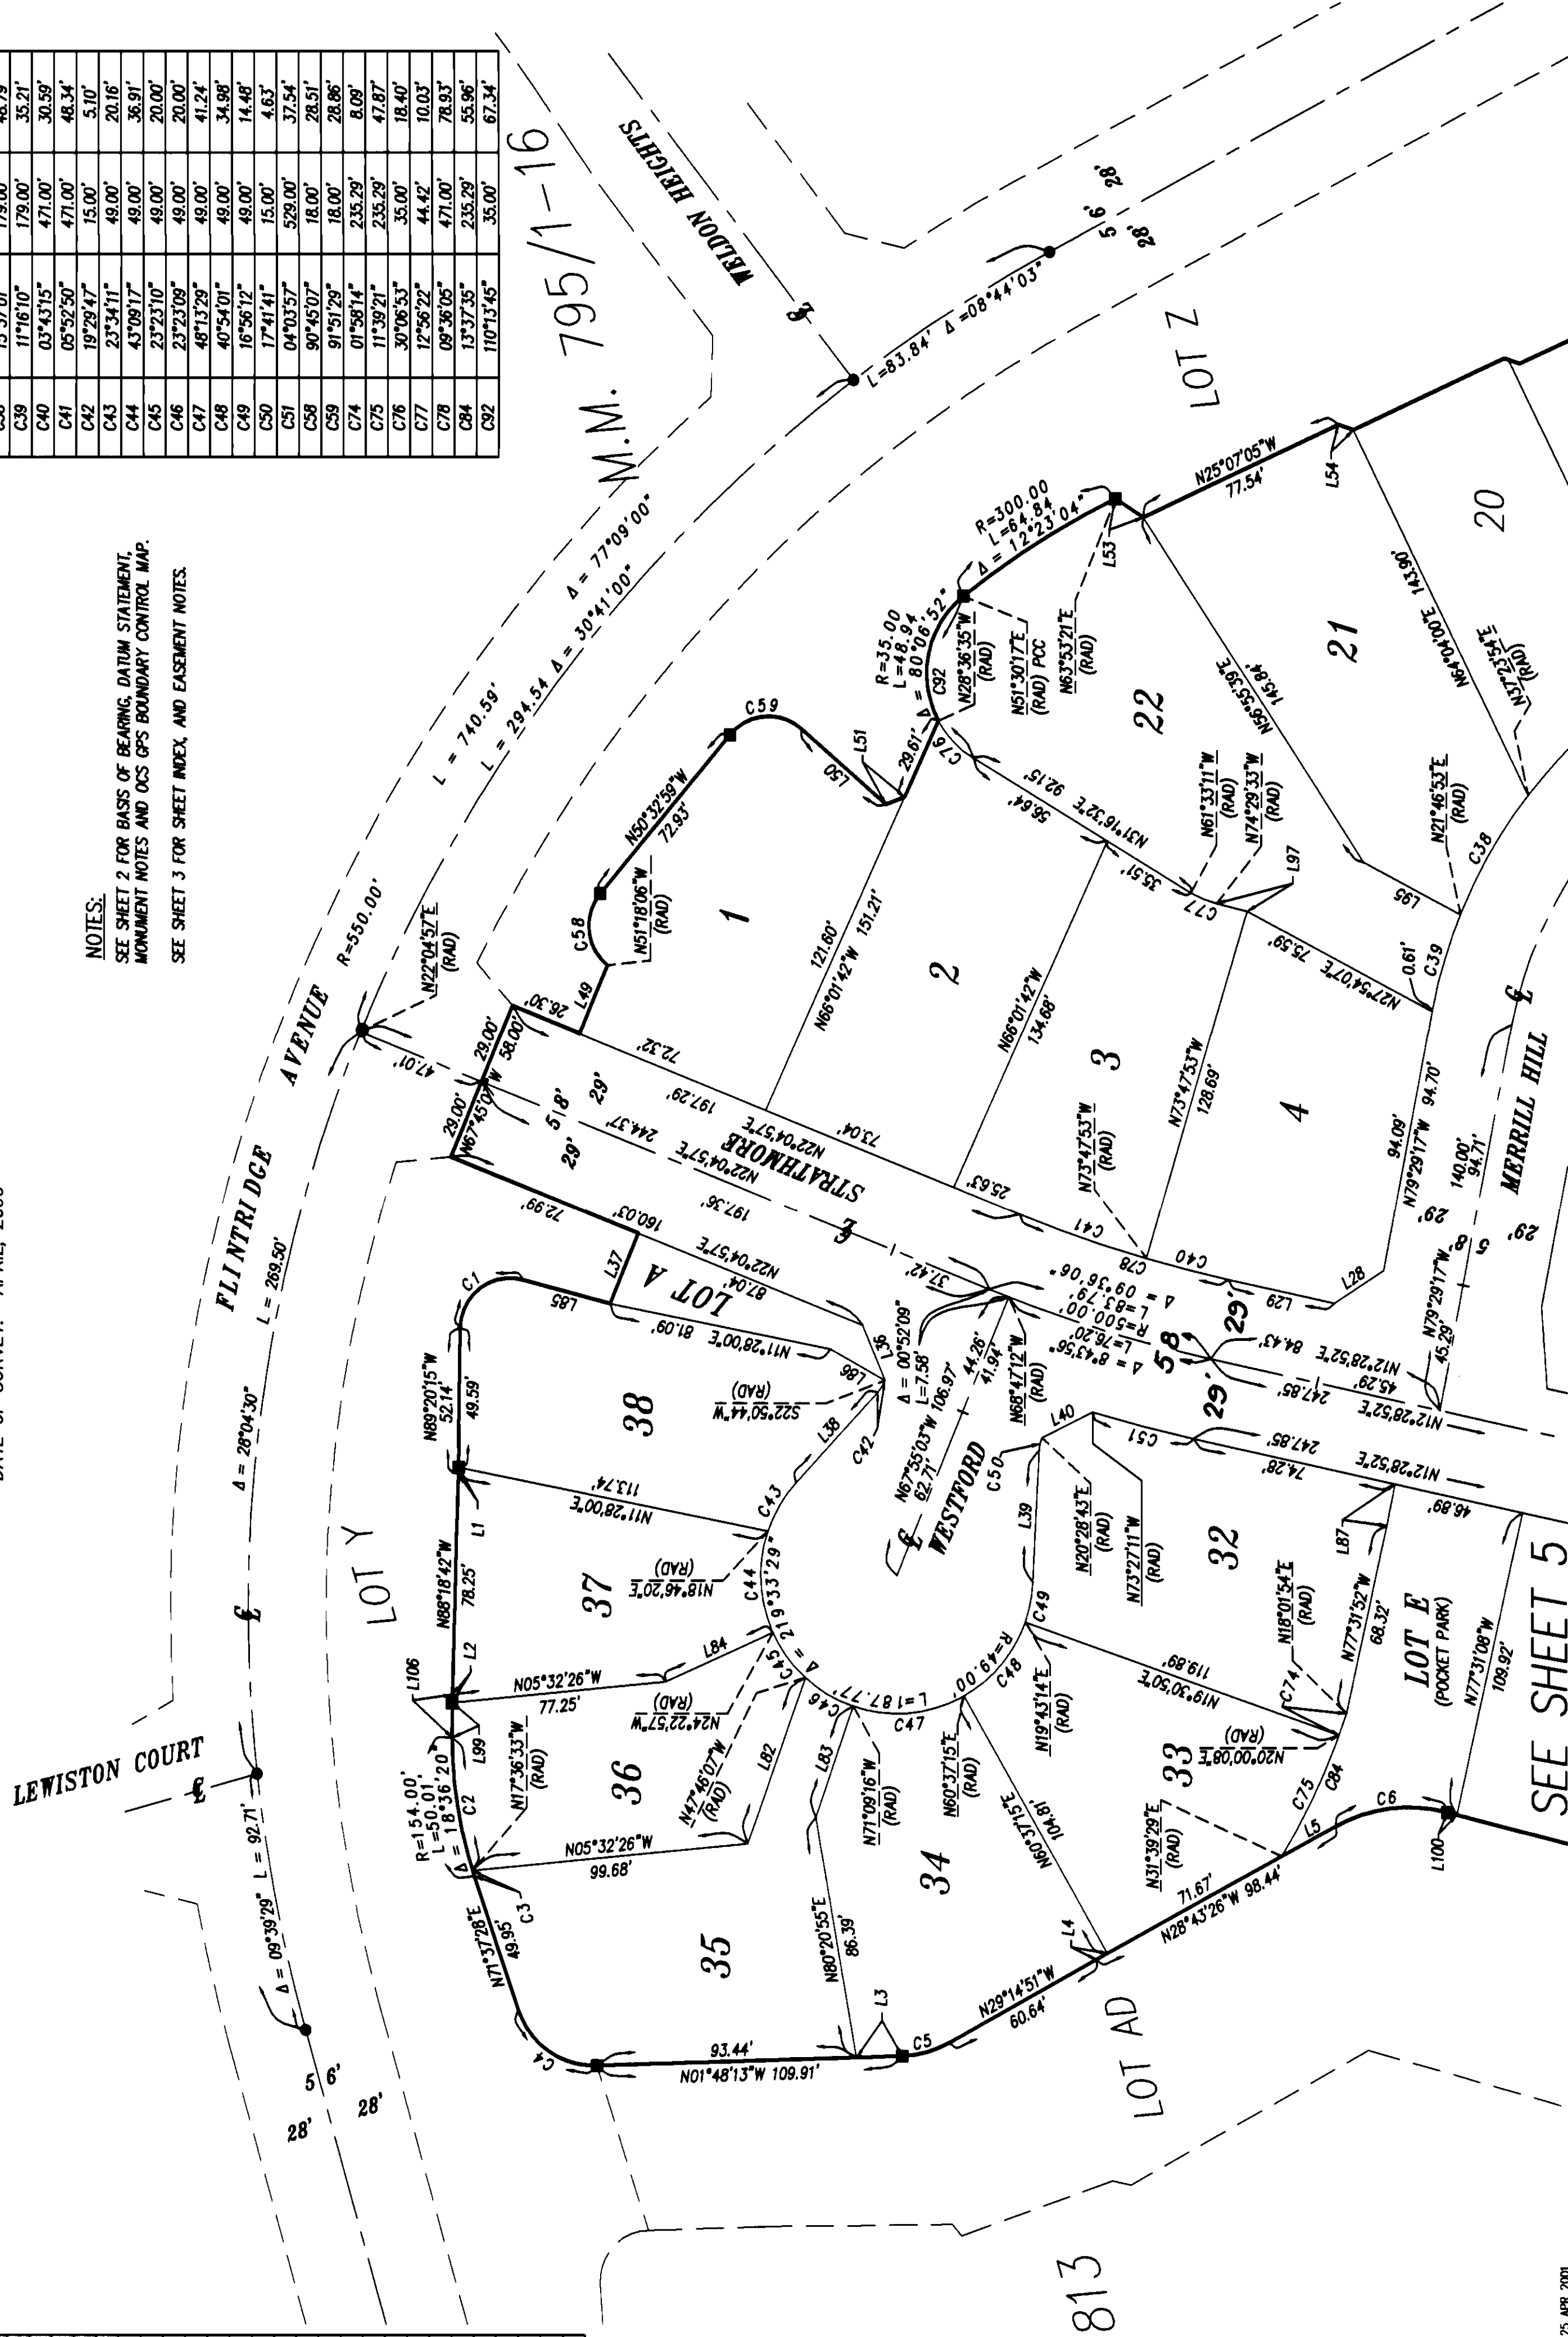

SEE SHEET 5

SHEET 5 OF 6 SHEETS
ALL OF TENTATIVE TRACT No. 15909
TOTAL LOTS: 38 NUMBERED LOTS AND 5 LETTERED LOTS
TOTAL ACREAGE: 10.350 ACRES

CURVE TABLE			
CURVE	DELTA	RADIUS	LENGTH
C6	43°07'29"	55.00'	41.40'
C7	19°24'46"	192.00'	65.05'
C8	18°16'48"	200.00'	63.81'
C9	00°35'12"	200.00'	2.05'
C22	23°54'15"	121.00'	50.48'
C23	21°40'08"	121.00'	45.76'
C24	13°54'32"	49.00'	11.90'
C25	34°04'10"	49.00'	29.14'
C26	65°21'42"	49.00'	55.90'
C27	30°44'04"	49.00'	26.28'
C28	28°59'56"	49.00'	24.80'
C29	23°56'02"	49.00'	20.47'
C30	11°56'51"	49.00'	10.22'
C31	10°14'07"	229.00'	40.91'
C32	14°24'21"	229.00'	57.58'
C33	15°53'29"	229.00'	63.51'
C34	10°43'36"	229.00'	42.87'
C35	16°34'41"	229.00'	66.26'
C36	01°23'29"	229.00'	5.56'
C37	18°41'12"	179.00'	58.38'
C38	15°37'01"	179.00'	48.79'

CURVE TABLE		
CURVE	DELTA	LENGTH
C39	11°16'10"	179.00'
C52	01°05'37"	279.00'
C53	13°22'46"	279.00'
C54	13°20'29"	279.00'
C60	62°55'25"	18.00'
C66	01°41'26"	1592.00'
C67	02°20'32"	1592.00'
C68	19°27'42"	21.70'
C70	16°04'08"	21.70'
C71	36°25'37"	12.92'
C72	35°15'15"	51.75'
C73	44°35'40"	51.75'
C79	79°50'55"	1592.00'
C83	00°01'09"	1592.00'
C85	18°52'00"	200.00'
C86	45°34'23"	121.00'
C93	35°31'51"	21.70'

TRACT NO. 15909


IN THE UNINCORPORATED TERRITORY OF THE COUNTY OF ORANGE,
STATE OF CALIFORNIA

TETRA TECH, INC. EUGENE A. SHAFFER, L.S. 4644
DATE OF SURVEY: APRIL, 2000

NOTES:
SEE SHEET 2 FOR BASIS OF BEARING, DATUM STATEMENT,
MONUMENT NOTES AND OCS GPS BOUNDARY CONTROL MAP.
SEE SHEET 3 FOR SHEET INDEX, AND EASEMENT NOTES

SEE SHEET 4

SEE SHEET 6

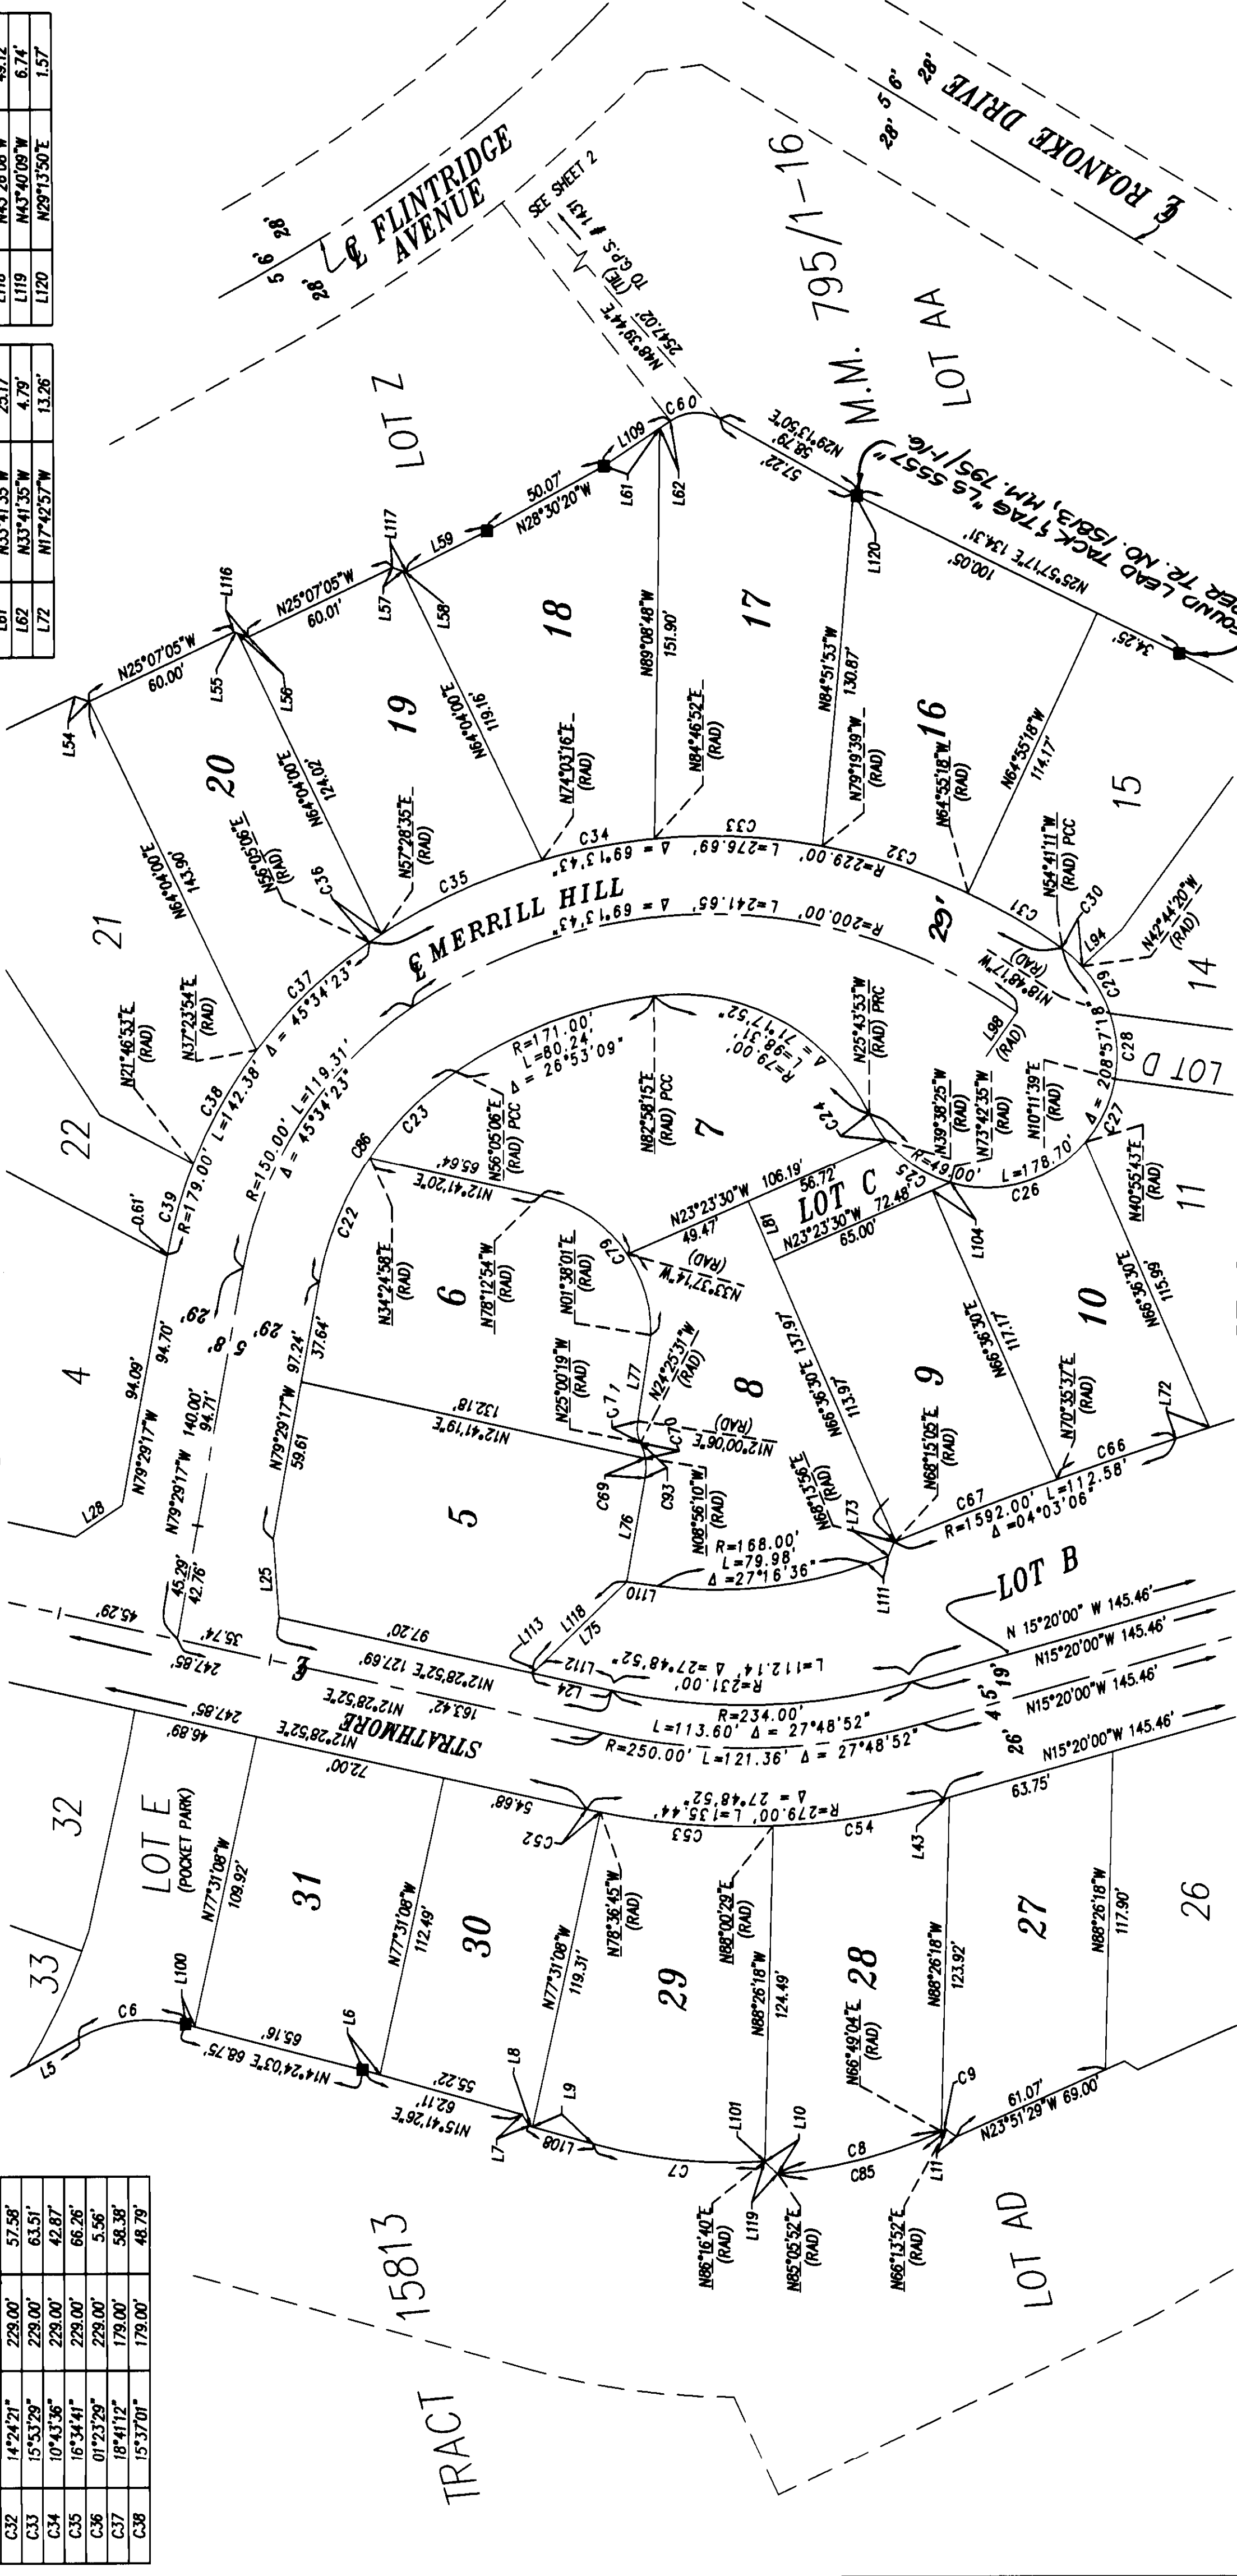

LINE TABLE		
LINE	BEARING	DISTANCE
L5	N28°43'26"W	98.44'
L6	N15°41'26"E	6.89'
L7	N59°05'41"E	4.95'
L8	N15°41'26"E	1.47'
L9	N15°41'26"E	23.47'
L10	N43°40'09"E	6.47'
L11	N34°00'14"E	4.72'
L24	N12°28'52"E	30.49'
L25	N85°57'57"E	28.92'
L28	N33°30'13"W	21.23'
L43	N15°20'00"W	2.31'
L54	N19°29'10"E	5.70'
L55	N19°28'27"E	1.43'
L56	N19°28'27"E	4.27'
L57	N18°19'04"E	4.19'
L58	N18°19'04"E	1.39'
L59	N26°40'21"W	33.78'
L61	N33°41'35"W	25.17'
L62	N33°41'35"W	4.79'
L72	N17°42'57"W	13.26'

LINE TABLE		
LINE	BEARING	DISTANCE
L73	N67°45'42"W	5.60'
L75	N43°26'08"W	45.50'
L76	N79°28'28"W	38.97'
L77	N81°16'50"W	32.35'
L81	N68°36'30"E	24.00'
L94	N42°44'20"W	20.30'
L98	N54°41'11"W	20.00'
L101	N43°40'09"E	0.26'
L104	N23°23'30"W	7.48'
L108	N15°41'26"E	24.94'
L109	N33°41'35"W	28.96'
L110	N07°50'47"E	11.71'
L111	N19°25'49"W	8.48'
L112	N17°28'52"E	28.46'
L113	N43°26'25"W	3.62'
L116	N19°28'27"W	5.70'
L117	N18°19'04"W	5.58'
L118	N43°26'08"W	49.12'
L119	N43°40'09"W	6.74'
L120	N29°13'50"E	1.57'

SCALE 1"=40'

