

SHEET 1 OF 3 SHEETS

1.280 ACRES
18 NUMBERED LOTS AND
LETTERED LOTS "A" THROUGH "C"
DATE OF SURVEY: FEBRUARY 2000
(FINAL UNIT OF VESTING
TENTATIVE TRACT No. 15914)

BLOCK MODULE
5157 19, 09, 18, 08

TRACT NO. 15914

IN THE UNINCORPORATED TERRITORY OF THE COUNTY OF ORANGE, STATE OF CALIFORNIA.

BEING A SUBDIVISION OF LOT 12 OF TRACT No. 15827 AS SHOWN ON
THE MAP THEREOF FILED IN BOOK 797 AT PAGES 32 THROUGH 39, INCLUSIVE, OF
MISCELLANEOUS MAPS, RECORDS OF ORANGE COUNTY, CALIFORNIA.

THOMAS EARL PROPST, P.L.S. 6098
FUSCOE ENGINEERING

FEBRUARY 2000

ACCEPTED AND FILED AT THE REQUEST OF

FIRST AMERICAN TITLE INSURANCE CO.

DATE MAY 30, 2001
TIME 10:14 A.M. FEE \$ 11.00
INSTRUMENT # 20010347975
BOOK 817 PAGE 45-47 M/M

GARY L. GRANVILLE
COUNTY CLERK-RECORDER
BY: [Signature]
DEPUTY

OWNERSHIP CERTIFICATE:

WE THE UNDERSIGNED, BEING ALL PARTIES HAVING ANY RECORD TITLE INTEREST IN THE LAND COVERED BY THIS MAP, DO HEREBY CONSENT TO THE PREPARATION AND RECORDATION OF SAID MAP, AS SHOWN WITHIN THE DISTINCTIVE BORDER LINE.

WE ALSO HEREBY DEDICATE TO THE COUNTY OF ORANGE THE EASEMENTS FOR STORM DRAIN PURPOSES OVER LOT "B" IN ITS ENTIRETY AND AS ADDITIONALLY DELINEATED ON SAID MAP.

WE ALSO HEREBY DEDICATE TO THE COUNTY OF ORANGE AN EASEMENT FOR EMERGENCY VEHICULAR ACCESS OVER LOTS "A" AND "B" IN THEIR ENTIRETY AS SHOWN ON SAID MAP.

WE ALSO HEREBY DEDICATE TO THE SANTA MARGARITA WATER DISTRICT PIPELINE EASEMENTS FOR SEWER AND WATER PURPOSES AS SHOWN ON THIS MAP, WHICH EASEMENTS SHALL BE SUBJECT TO THE SAME TERMS AND CONDITIONS AS ARE SHOWN IN THAT CERTAIN EASEMENT RECORDED OCTOBER 6, 1980 IN BOOK 13776, PAGE 341 OF OFFICIAL RECORDS, COUNTY OF ORANGE. THE SANTA MARGARITA WATER DISTRICT SHALL RESTORE OTHER IMPROVEMENTS OR FACILITIES LOCATED WITHIN THE EASEMENT, IF IT HAS CONSENTED TO THE LOCATION OF SUCH IMPROVEMENTS OR FACILITIES TO THE EXTENT THAT THE EXERCISE OF ITS RIGHTS IN CONNECTION WITH THE EASEMENT IMPACTS OTHER IMPROVEMENTS OR FACILITIES LOCATED WITHIN THE EASEMENT, HOWEVER, IN NO EVENT SHALL SANTA MARGARITA WATER DISTRICT BE RESPONSIBLE FOR THE COST OF RELOCATING ITS FACILITIES IN THE EVENT CONFLICTS WITH SUCH OTHER IMPROVEMENTS OR FACILITIES.

RICHMOND AMERICAN HOMES OF CALIFORNIA, INC., A COLORADO CORPORATION

BY: [Signature] BY: [Signature]
PRINT NAME Robert T. Shiota PRINT NAME Jon H. Sasaki
PRINT TITLE President PRINT TITLE asst. sec.

DMB LADERA, LLC, A DELAWARE LIMITED LIABILITY COMPANY, BENEFICIARY UNDER
A DEED OF TRUST RECORDED AS INSTRUMENT NO. 20000224838
BY RANCHO MISSION MEJO, LLC, A DELAWARE LIMITED LIABILITY COMPANY AS AGENT AND MANAGER

BY: [Signature]
PRINT NAME PAUL JOHNSON
PRINT TITLE V.P. - COMM. DEVEL.

STATE OF CALIFORNIA }
COUNTY OF ORANGE } SS

ON THIS 14 DAY OF June 2000, BEFORE ME, Monica Sierra
PERSONALLY APPEARED Robert T. Shiota, Jon H. Sasaki PERSONALLY KNOWN
TO ME (OR PROVED TO ME ON THE BASIS OF SATISFACTORY EVIDENCE) TO BE THE PERSON(S) WHOSE NAME(S)
IS/ARE SUBSCRIBED TO THE WITHIN INSTRUMENT AND ACKNOWLEDGED TO ME THAT HE/SHE/ THEY EXECUTED
THE SAME IN HIS/HER/ THEIR AUTHORIZED CAPACITY(IES), AND THAT BY HIS/HER/ THEIR SIGNATURE(S) ON THE
INSTRUMENT THE PERSON(S), OR THE ENTITY UPON BEHALF OF WHICH THE PERSON(S) ACTED, EXECUTED THE
INSTRUMENT

MY PRINCIPAL PLACE OF BUSINESS
IS IN Orange COUNTY

MY COMMISSION EXPIRES: 4-11-02

WITNESS MY HAND
Monica Sierra
(SIGNATURE)
NOTARY PUBLIC IN AND FOR SAID STATE
Monica Sierra
(PRINT NAME)

STATE OF CALIFORNIA }
COUNTY OF ORANGE } SS

ON THIS 15 DAY OF June 2000, BEFORE ME, JEANNINE CARTA-HANSON
PERSONALLY APPEARED PAUL JOHNSON PERSONALLY KNOWN
TO ME (OR PROVED TO ME ON THE BASIS OF SATISFACTORY EVIDENCE) TO BE THE PERSON(S) WHOSE NAME(S)
IS/ARE SUBSCRIBED TO THE WITHIN INSTRUMENT AND ACKNOWLEDGED TO ME THAT HE/SHE/ THEY EXECUTED
THE SAME IN HIS/HER/ THEIR AUTHORIZED CAPACITY(IES), AND THAT BY HIS/HER/ THEIR SIGNATURE(S) ON THE
INSTRUMENT THE PERSON(S), OR THE ENTITY UPON BEHALF OF WHICH THE PERSON(S) ACTED, EXECUTED THE
INSTRUMENT

MY PRINCIPAL PLACE OF BUSINESS
IS IN ORANGE COUNTY

MY COMMISSION EXPIRES 2-25-03

WITNESS MY HAND
Jeannine Carta-Hanson
(SIGNATURE)
NOTARY PUBLIC IN AND FOR SAID STATE
JEANNINE CARTA-HANSON
(PRINT NAME)

SANTA MARGARITA WATER DISTRICT
CERTIFICATE OF ACCEPTANCE:

THE UNDERSIGNED BEING THE DULY APPOINTED AGENT OF THE SANTA MARGARITA WATER DISTRICT, A PUBLIC CORPORATION IN ORANGE COUNTY, CALIFORNIA, PURSUANT TO ITS RESOLUTION NO. 88-10-2, DOES HEREBY ACCEPT ON BEHALF OF SAID DISTRICT THE PIPELINE EASEMENTS FOR SEWER AND WATER PURPOSES, AS DEDICATED AND AS SHOWN ON THIS TRACT MAP, BY AND BETWEEN THE SANTA MARGARITA WATER DISTRICT AND RICHMOND AMERICAN HOMES OF CALIFORNIA, INC., AND DOES HEREBY CERTIFY THAT THE GRANTEE CONSENTS TO THE RECORDATION OF SAID TRACT MAP.

[Signature]
DANIEL R. FERONS, CHIEF ENGINEER
SANTA MARGARITA WATER DISTRICT

STATE OF CALIFORNIA }
COUNTY OF ORANGE } SS

ON THIS 6 DAY OF DECEMBER 2000, BEFORE ME, ANDREA M. EVANS
PERSONALLY APPEARED DANIEL R. FERONS, PERSONALLY KNOWN TO ME (OR PROVED TO ME ON THE BASIS OF
SATISFACTORY EVIDENCE) TO BE THE PERSON WHOSE NAME IS SUBSCRIBED TO THE WITHIN INSTRUMENT AND
ACKNOWLEDGED TO ME THAT HE EXECUTED THE SAME IN HIS AUTHORIZED CAPACITY, AND THAT BY HIS SIGNATURE
ON THE INSTRUMENT THE PERSON, OR THE ENTITY UPON BEHALF OF WHICH THE PERSON ACTED, EXECUTED THE
INSTRUMENT

MY PRINCIPAL PLACE OF BUSINESS
IS IN ORANGE COUNTY

MY COMMISSION EXPIRES 4-8-04

WITNESS MY HAND:
Andrea M. Evans
(SIGNATURE)
NOTARY PUBLIC IN AND FOR SAID STATE
ANDREA M. EVANS
(PRINT NAME)

SURVEYOR'S STATEMENT:

I HEREBY STATE THAT THIS MAP CONSISTING OF 3 SHEETS, CORRECTLY REPRESENTS A TRUE AND COMPLETE SURVEY AS SHOWN MADE IN FEBRUARY 2000; WAS MADE BY ME OR UNDER MY DIRECTION; THAT THE MONUMENTS ARE OF THE CHARACTER AND OCCUPY (OR WILL OCCUPY) THE POSITIONS INDICATED BY SAID MAP; AND THAT SAID MONUMENTS ARE (OR WILL BE) SUFFICIENT TO ENABLE THE SURVEY TO BE RETRACED.

[Signature]
THOMAS EARL PROPST, P.L.S. 6098
LICENSE EXPIRES 12-31-01



COUNTY SURVEYOR'S STATEMENT:

I HEREBY STATE THAT I HAVE EXAMINED THIS MAP AND FOUND IT TO BE SUBSTANTIALLY IN CONFORMANCE WITH THE TENTATIVE MAP, AS FILED WITH, AMENDED AND APPROVED BY THE ORANGE COUNTY SUBDIVISION COMMITTEE, THAT ALL PROVISIONS OF THE SUBDIVISION MAP ACT AND COUNTY SUBDIVISION REGULATIONS HAVE BEEN COMPLIED WITH AND I AM SATISFIED SAID MAP IS TECHNICALLY CORRECT

DATED THIS 14th DAY OF May 2001

[Signature]
JOHN CANAS, COUNTY SURVEYOR
L.S. 4408 LICENSE EXPIRATION DATE: 9-30-01
L.S. 6803, Exp. 9-30-04
Robert Jelinek, Deputy County Surveyor



COUNTY TREASURER-TAX COLLECTOR'S CERTIFICATE:

STATE OF CALIFORNIA }
COUNTY OF ORANGE } SS

I HEREBY CERTIFY THAT ACCORDING TO THE RECORDS OF MY OFFICE THERE ARE NO LIENS AGAINST THE LAND COVERED BY THIS MAP OR ANY PART THEREOF FOR UNPAID STATE, COUNTY, MUNICIPAL OR LOCAL TAXES OR SPECIAL ASSESSMENTS COLLECTED AS TAXES, EXCEPT TAXES OR SPECIAL ASSESSMENTS COLLECTED AS TAXES NOT YET PAYABLE. AND DO ALSO CERTIFY TO THE RECORDER OF ORANGE COUNTY THAT THE PROVISIONS OF THE SUBDIVISION MAP ACT HAVE BEEN COMPLIED WITH REGARDING DEPOSITS TO SECURE THE PAYMENT OF TAXES OR SPECIAL ASSESSMENTS COLLECTED AS TAXES ON THE LAND COVERED BY THIS MAP.

DATED THIS 12th DAY OF March 2001

JOHN M. W. MOORLACH
COUNTY TREASURER-TAX COLLECTOR

BY: [Signature]
DEPUTY TREASURER-TAX COLLECTOR

CLERK OF THE BOARD OF SUPERVISOR'S CERTIFICATE:


STATE OF CALIFORNIA }
COUNTY OF ORANGE } SS

I HEREBY CERTIFY THAT THIS MAP WAS PRESENTED FOR APPROVAL TO THE BOARD OF SUPERVISORS OF ORANGE COUNTY AT A REGULAR MEETING THEREOF HELD ON THE 22nd DAY OF May 2001 AND THAT THEREUPON SAID BOARD DID, BY AN ORDER DULY PASSED AND ENTERED, APPROVE SAID MAP AND DID ACCEPT ON BEHALF OF THE COUNTY OF ORANGE:

1. THE EASEMENT FOR EMERGENCY VEHICULAR ACCESS AS DEDICATED
2. THE EASEMENT FOR STORM DRAIN PURPOSES AS DEDICATED

DATED THIS 22nd DAY OF May 2001

[Signature]
DARLENE J. BLOOM
CLERK OF THE BOARD OF SUPERVISORS
OF ORANGE COUNTY, CALIFORNIA

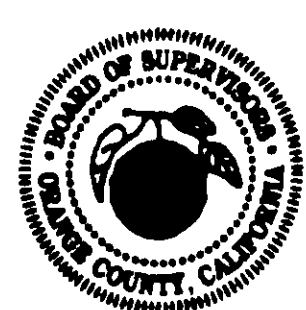

SIGNATURE OMISSION NOTES:

IN ACCORDANCE WITH THE PROVISIONS OF SECTION 66436(d)(3)(A) OF THE SUBDIVISION MAP ACT, THE FOLLOWING SIGNATURES HAVE BEEN OMITTED

- 1.) LADERA DEVELOPMENT COMPANY, L.L.C. HOLDER OF OIL, GAS, MINERAL, AND WATER RIGHTS RECORDED AS INSTRUMENT NO. 19960624029 OF OFFICIAL RECORDS.
- 2.) EASEMENTS, COVENANTS AND CONDITIONS CONTAINED IN THE DEED FROM DMB LADERA, LLC, A DELAWARE LIMITED LIABILITY COMPANY, AS GRANTOR, TO RICHMOND AMERICAN HOMES OF CALIFORNIA, INC., A COLORADO CORPORATION, AS GRANTEE, RECORDED MAY 1, 2001 AS INSTRUMENT NO. 20010272160 OF OFFICIAL RECORDS.

SHEET 2 OF 3 SHEETS
1.280 ACRES
18 NUMBERED LOTS AND
LETTERED LOTS "A" THROUGH "C"
DATE OF SURVEY: FEBRUARY 2000
(FINAL UNIT OF VESTING
TENTATIVE TRACT No. 15914)

TRACT NO. 15914

IN THE UNINCORPORATED TERRITORY OF THE COUNTY OF ORANGE, STATE OF CALIFORNIA.

THOMAS EARL PROPST, P.L.S. 6098

FEBRUARY 2000

FUSCOE ENGINEERING

MONUMENT NOTES:

■ DENOTES FOUND MONUMENT AS NOTED:

1 FOUND LEAD & TAG STAMPED "RCE 28946" IN CONCRETE PER TRACT 15827, M.M. 797/32-39.

2 FOUND 1" I.P. TAGGED "RCE 28946" PER TRACT 15827, M.M. 797/32-39.

3 2" I.P. TAGGED "RCE 28946" OR 1" I.P. TAGGED "RCE 28946" OR LEAD & TAG STAMPED "RCE 28946" IN CONCRETE TO BE SET AT ALL LOT CORNERS EXCEPT LOT CORNERS THAT ABUT A STREET WHICH WILL BE MARKED ON A 8.75' OFFSET OUTSIDE THE TRUE LOT CORNER IN CONCRETE BY A LEAD AND TAG "RCE 28946" ON SIDELINES PRODUCED, UNLESS OTHERWISE NOTED. (NO MONUMENTS WILL BE SET FOR ANGLE POINTS, CORNER CUTOFFS, B.C.'S, E.C.'S, P.C.C.'S OR P.R.C.'S THAT ABUT STREET WHICH ARE NOT LOT CORNERS MARKING SIDELINES, UNLESS OTHERWISE NOTED) PER TRACT 15827, M.M. 797/32-39.

4 8" SPIKE AND WASHER STAMPED "RCE 28946" IN ASPHALT PAVING OR LEAD AND TAG "RCE 28946" IN CONCRETE TO BE SET AT ALL CENTERLINE INTERSECTIONS, B.C.'S, E.C.'S AND ALL OTHER CENTERLINE POINTS OF CONTROL, UNLESS OTHERWISE NOTED, WITHIN 90 DAYS AFTER ACCEPTANCE OF IMPROVEMENTS PER TRACT 15827, M.M. 797/32-39.

5 1" I.P. TAGGED "L.S. 6098" OR SPIKE AND WASHER STAMPED "L.S. 6098" OR LEAD AND TAG "L.S. 6098" TO BE SET AT CENTERLINE POINTS OF CONTROL (UNLESS OTHERWISE NOTED) WITHIN 90 DAYS AFTER ACCEPTANCE OF IMPROVEMENTS PER TRACT No. 15915 M.M. 805/29-34

6 1" I.P. TAGGED "L.S. 6098" OR SPIKE AND WASHER STAMPED "L.S. 6098" OR LEAD AND TAG "L.S. 6098" TO BE SET AT LOT CORNERS EXCEPT LOT CORNERS THAT ABUT A STREET WHICH WILL BE MARKED ON A 8.75' OFFSET OUTSIDE THE TRUE LOT CORNER IN CONCRETE BY A LEAD AND TAG "L.S. 6098" ON SIDELINES PRODUCED, UNLESS OTHERWISE NOTED.

NO MONUMENTS WILL BE SET FOR ANGLE POINTS, CORNER CUTOFFS, B.C.'S, E.C.'S, P.C.C.'S OR P.R.C.'S THAT ABUT DEDICATED PUBLIC STREETS WHICH ARE NOT LOT CORNERS MARKING SIDELINES, UNLESS OTHERWISE NOTED.

SURVEYOR'S NOTES:

ALL LETTERED LOTS SHOWN HEREON ARE NOT SEPARATE BUILDING SITES. LOTS "A" AND "B" ARE FOR PRIVATE DRIVEWAYS, EMERGENCY VEHICULAR ACCESS, AND PIPELINE EASEMENTS FOR SEWER AND WATER PURPOSES AND ARE TO BE CONVEYED TO THE APPROPRIATE HOMEOWNERS ASSOCIATION. LOT "C" IS FOR LANDSCAPE PURPOSES AND IS TO BE CONVEYED TO THE APPROPRIATE HOMEOWNERS ASSOCIATION.

BASIS OF BEARINGS:

BEARINGS SHOWN HEREON ARE BASED ON THE LINE BETWEEN O.C.S. HORIZONTAL CONTROL STATION NO. 9009 AND STATION NO. 1426 BEARING NORTH 61°10'47" EAST PER RECORDS ON FILE IN THE OFFICE OF THE ORANGE COUNTY SURVEYOR.

DATUM STATEMENT:


BEARINGS SHOWN HEREON ARE BASED UPON THE CALIFORNIA COORDINATE SYSTEM (CCS83) ZONE VI 1983 NAD (1991.35 EPOCH O.C.S. GPS ADJUSTMENT). ALL DISTANCES SHOWN ARE GROUND DISTANCES UNLESS OTHERWISE NOTED. TO OBTAIN GRID DISTANCE MULTIPLY GROUND DISTANCE BY 0.99993923

NOTE:


THE PROPERTY IS "CONDITIONALLY EXCLUDED" FROM A "SPECIAL FIRE PROTECTION AREA". NO LOTS ARE SUBJECT TO CONSTRUCTION FEATURES OF THE ORANGE COUNTY ORDINANCE 3960 PER THE APPROVED FIRE MASTER PLAN FOR THIS TRACT.

HIGH/VERY HIGH FIRE HAZARD AREA NOTE:

THE LOTS SHOWN ON THIS MAP ARE IN A HIGH/VERY HIGH FIRE HAZARD AREA DUE TO WILDLAND EXPOSURE BASED ON SRA (STATE RESPONSIBILITY AREA) MAPS

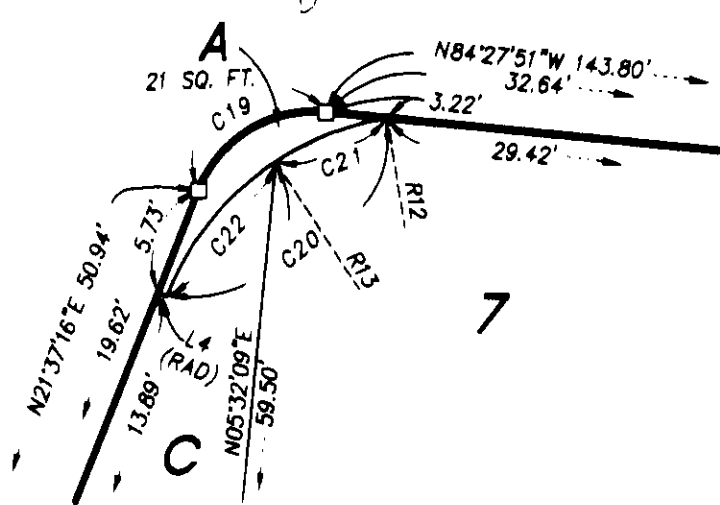

DETAIL 'A'
SCALE: 1"=10'

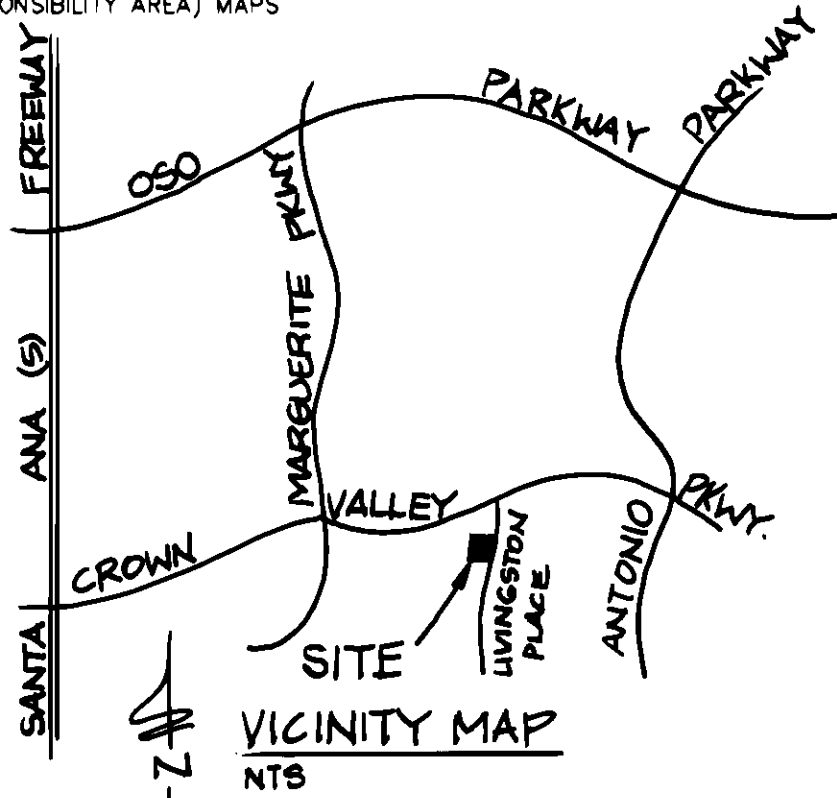


GPS NO. 1426
FD. 2 1/2" I.P. WITH 2" OCS BRASS CAP
STAMPED "GPS 1426 9-95"
PER R.S. 97-1086
R.S.B. 167/26-28.
E 81°40'77.3624"

GPS NO. 9009
STAMPED "LEMONHEAD OCS 9009"
PER R.S. 97-1086
R.S.B. 167/26-28.

N 215°259.152
E 61°33621.604


BASIS OF BEARINGS
N 61°10'47" E
(8163.14 GRID)

SAME POINT

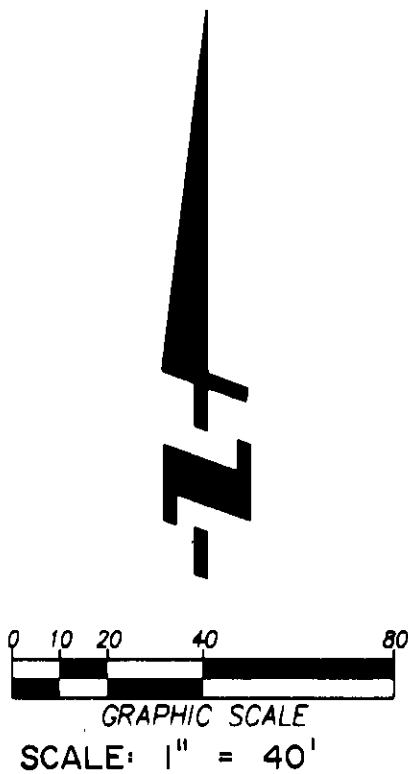

GRAPHIC SCALE
SCALE: 1" = 40'

RADIAL	BEARING
R1	N13°27'10"W
R2	N67°56'10"W
R3	N68°43'29"W
R4	N75°05'25"W
R5	N71°29'29"W
R6	N76°11'08"W
R7	N79°33'35"W
R8	N82°34'45"W
R9	N88°04'04"W
R10	N88°06'32"E
R11	N89°02'27"E
R12	N09°17'57"W
R13	N33°22'50"W
R14	N48°17'22"E

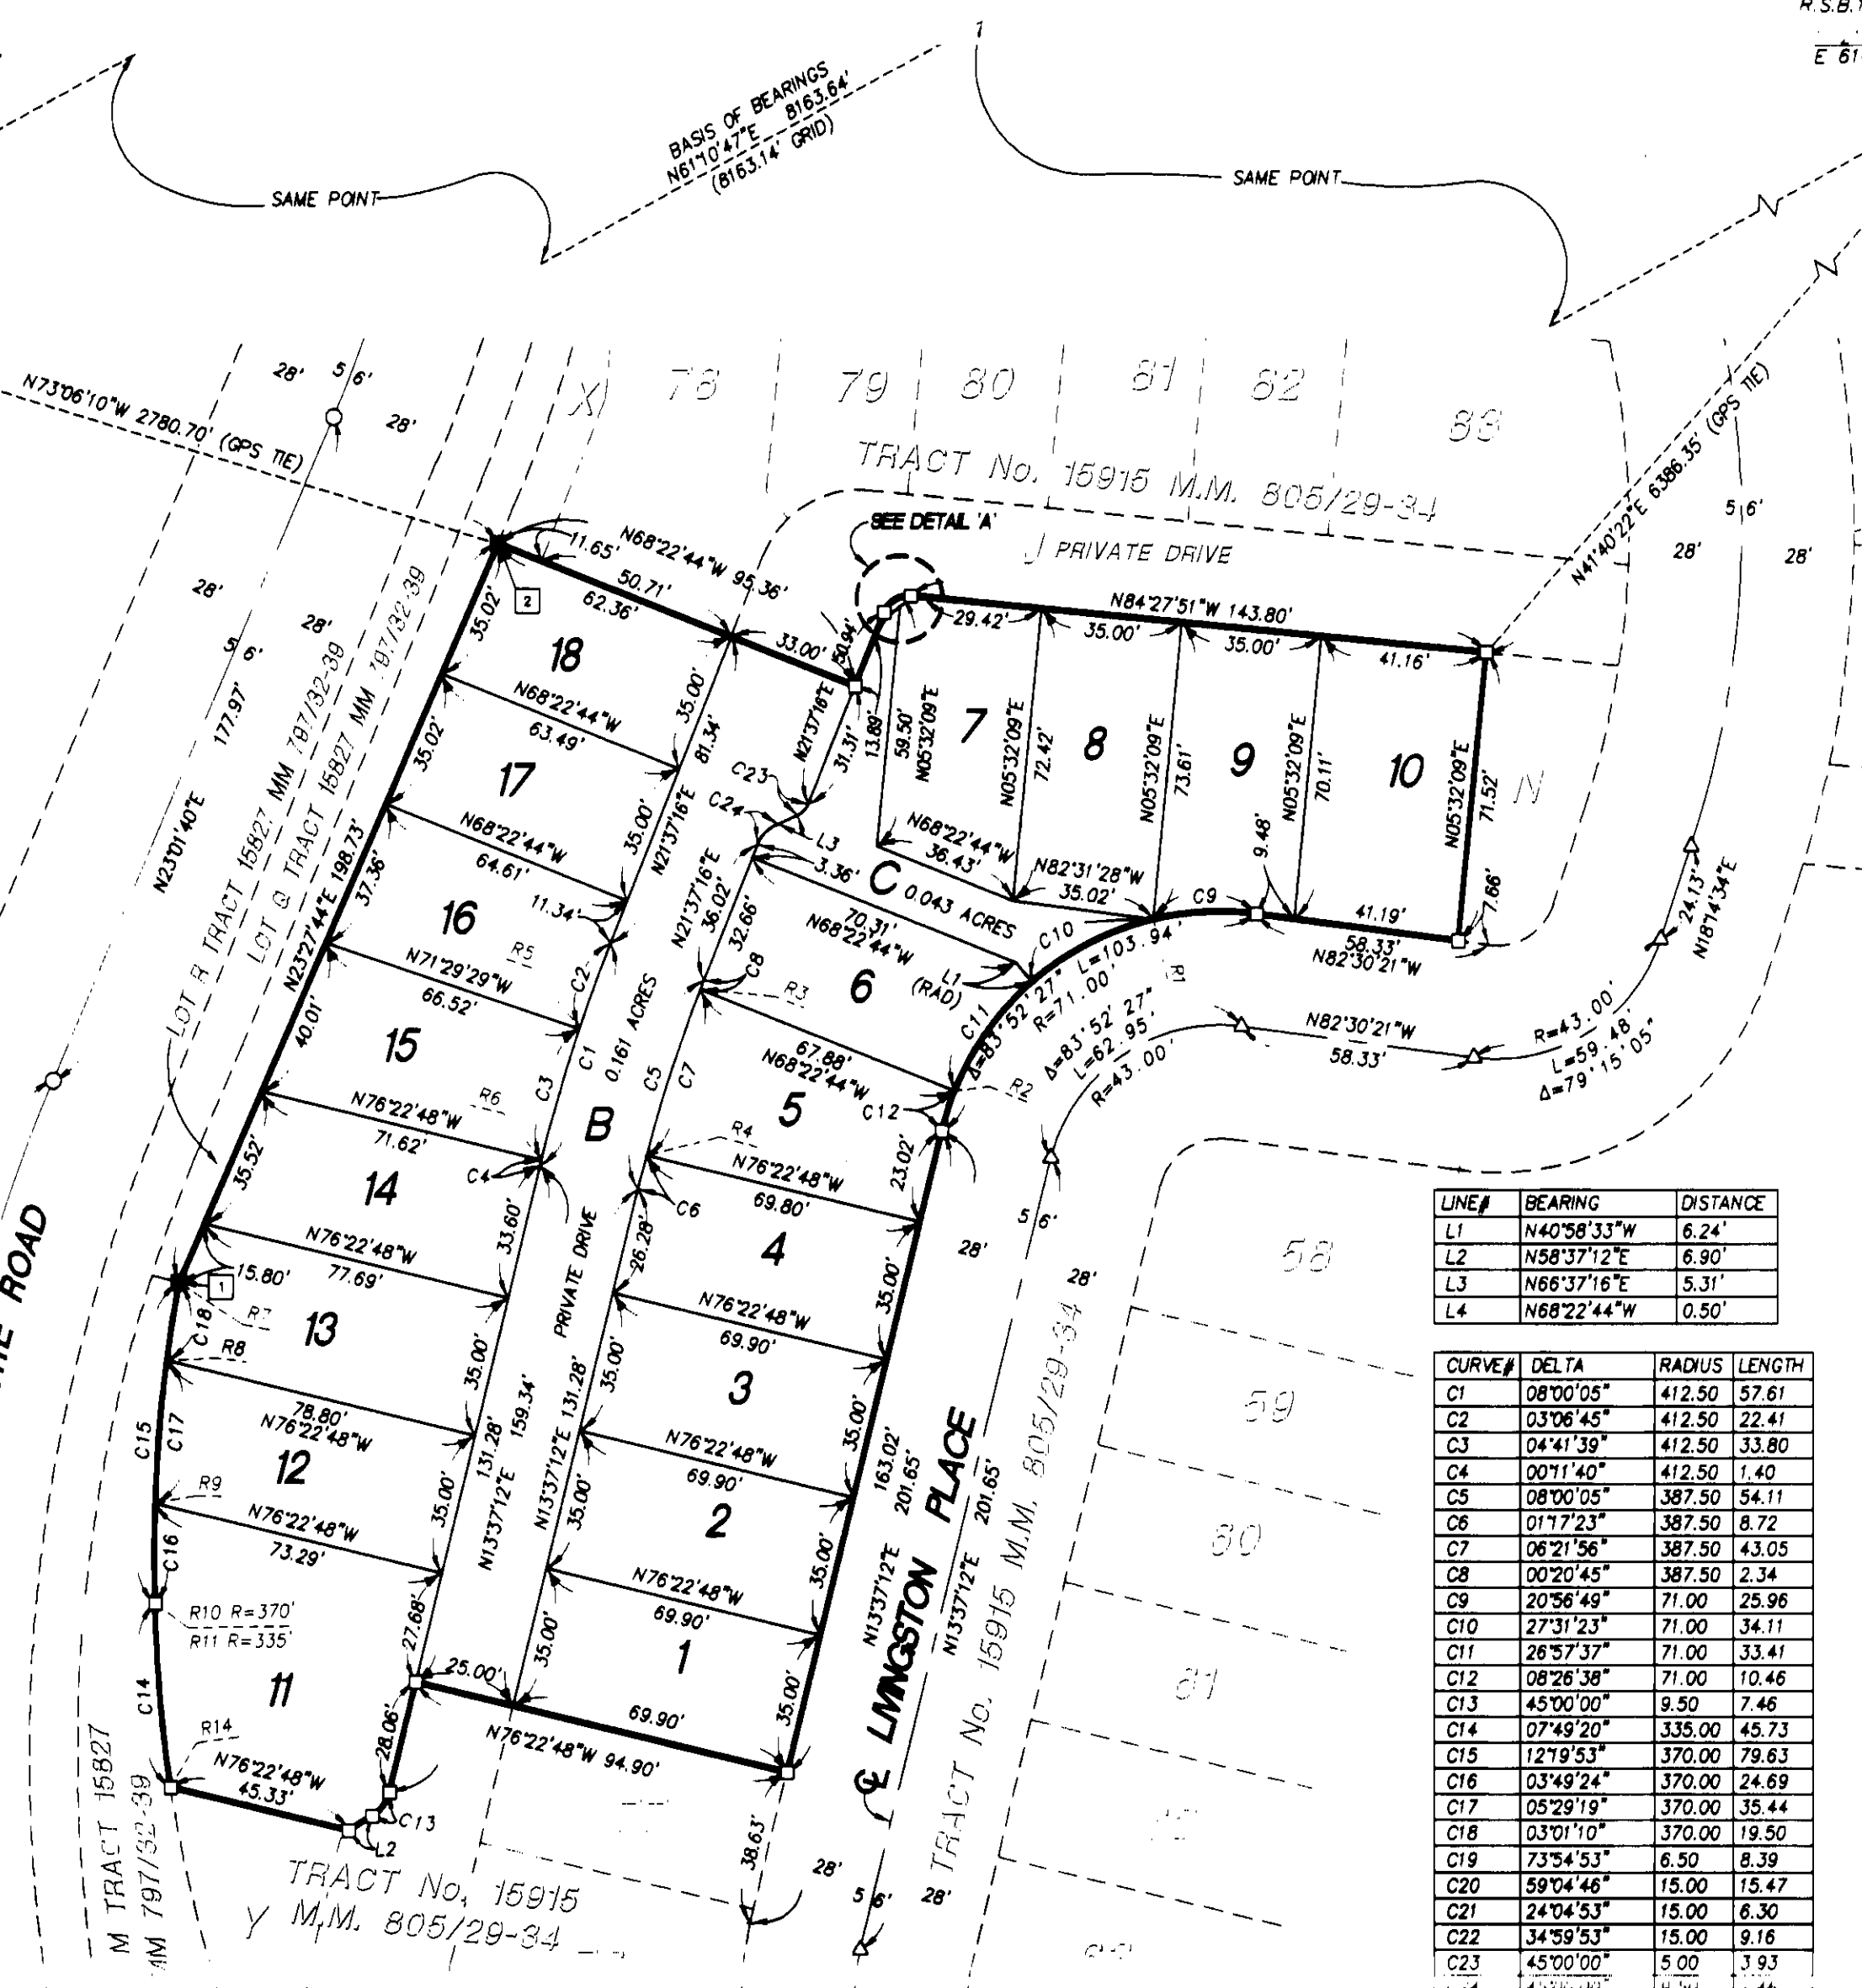

LINE#	BEARING	DISTANCE
L1	N40°58'33"W	6.24'
L2	N58°37'12"E	6.90'
L3	N66°37'16"E	5.31'
L4	N68°22'44"W	0.50'

CURVE#	DELTA	RADIUS	LENGTH
C1	08°00'05"	412.50	57.61
C2	03°06'45"	412.50	22.41
C3	04°41'39"	412.50	33.80
C4	00°11'40"	412.50	1.40
C5	08°00'05"	387.50	54.11
C6	01°17'23"	387.50	8.72
C7	06°21'56"	387.50	43.05
C8	00°20'45"	387.50	2.34
C9	20°56'49"	71.00	25.96
C10	27°31'23"	71.00	34.11
C11	26°57'37"	71.00	33.41
C12	08°26'38"	71.00	10.46
C13	45°00'00"	9.50	7.46
C14	07°49'20"	335.00	45.73
C15	12°19'53"	370.00	79.63
C16	03°49'24"	370.00	24.69
C17	05°29'19"	370.00	35.44
C18	03°01'10"	370.00	19.50
C19	73°54'53"	6.50	8.39
C20	59°04'46"	15.00	15.47
C21	24°04'53"	15.00	6.30
C22	34°59'53"	15.00	9.16
C23	45°00'00"	5.00	3.93
C24	45°00'00"	9.50	1.46

SEE SHEET 3 FOR EASEMENT NOTES AND LOCATIONS.


SHEET 3 OF 3 SHEETS
1.280 ACRES
18 NUMBERED LOTS AND
LETTERED LOTS "A" THROUGH "C"
DATE OF SURVEY: FEBRUARY 2000
(FINAL UNIT OF VESTING
TENTATIVE TRACT No. 15914)

TRACT NO. 15914

IN THE UNINCORPORATED TERRITORY OF THE COUNTY OF ORANGE, STATE OF CALIFORNIA.

THOMAS EARL PROPST, P.L.S. 6098
FUSCOE ENGINEERING

FEBRUARY 2000

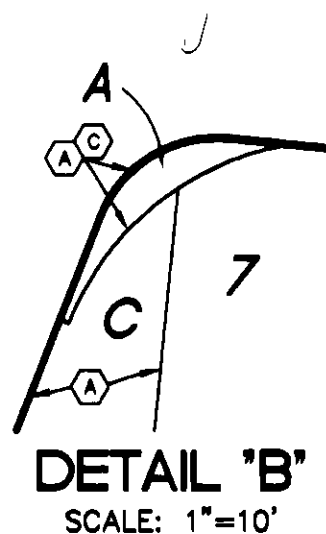

EASEMENT NOTES:

- (A) DENOTES AN EASEMENT TO THE SANTA MARGARITA WATER DISTRICT FOR SEWER AND WATER PURPOSES AS DEDICATED HEREON, OVER LOTS "A" THROUGH "C" IN THEIR ENTIRETY AND AS ADDITIONALLY DELINEATED HEREON.
- (B) DENOTES AN EASEMENT TO THE COUNTY OF ORANGE FOR STORM DRAIN PURPOSES AS DEDICATED HEREON, OVER LOT "B" IN ITS ENTIRETY, AND AS ADDITIONALLY DELINEATED HEREON.
- (C) DENOTES AN EASEMENT TO THE COUNTY OF ORANGE FOR EMERGENCY VEHICULAR ACCESS PURPOSES AS DEDICATED HEREON, OVER LOTS "A" AND "B" IN THEIR ENTIRETY.

EASEMENT LOCATIONS

