

SHEET 1 OF 6 SHEETS

9.937 ACRES
83 NUMBERED LOTS AND
LETTERED LOTS "A" THROUGH "Y"
DATE OF SURVEY: FEBRUARY 2000
(A PORTION OF VESTING
TENTATIVE TRACT No. 15914)

BLOCK MODULE
5157 19, 09, 18, 08

TRACT NO. 15915

IN THE UNINCORPORATED TERRITORY OF THE COUNTY OF ORANGE, STATE OF CALIFORNIA.

BEING A SUBDIVISION OF LOT 2 OF TRACT No. 15827 AS SHOWN ON
THE MAP THEREOF FILED IN BOOK 797 AT PAGES 32 THROUGH 39, INCLUSIVE, OF
MISCELLANEOUS MAPS, RECORDS OF ORANGE COUNTY, CALIFORNIA.

THOMAS EARL PROPST, P.L.S. 6098
FUSCOE ENGINEERING

FEBRUARY 2000

ACCEPTED AND FILED AT THE REQUEST OF

FIRSTAMERICAN TITLE INSURANCE CO.

DATE AUGUST 25, 2000
TIME 11:03 A.M. FEE \$ 17.00
INSTRUMENT # 20000444713
BOOK 805 PAGE 29-34 M/M

GARY L. GRANVILLE
COUNTY CLERK-RECORDER
BY: [Signature]
DEPUTY

OWNERSHIP CERTIFICATE:

WE THE UNDERSIGNED, BEING ALL PARTIES HAVING ANY RECORD TITLE INTEREST IN THE LAND COVERED BY THIS MAP, DO HEREBY CONSENT TO THE PREPARATION AND RECORDATION OF SAID MAP, AS SHOWN WITHIN THE DISTINCTIVE BORDER LINE.

WE HEREBY DEDICATE TO THE PUBLIC FOR STREET PURPOSES:
WESTCOTT LANE AND LIVINGSTON PLACE.

WE ALSO HEREBY DEDICATE TO THE COUNTY OF ORANGE AN EASEMENT FOR STORM DRAIN PURPOSES OVER LOTS "C" AND "J", IN THEIR ENTIRETY AND AS ADDITIONALLY DELINEATED ON SAID MAP.

WE ALSO HEREBY DEDICATE TO THE COUNTY OF ORANGE AN EASEMENT FOR EMERGENCY VEHICULAR ACCESS OVER LOTS "A" THROUGH "M", INCLUSIVE, IN THEIR ENTIRETY AS SHOWN ON SAID MAP.

WE ALSO HEREBY DEDICATE TO THE SANTA MARGARITA WATER DISTRICT PIPELINE EASEMENTS FOR SEWER AND WATER PURPOSES AS SHOWN ON THIS MAP, WHICH EASEMENTS SHALL BE SUBJECT TO THE SAME TERMS AND CONDITIONS AS ARE SHOWN IN THAT CERTAIN EASEMENT RECORDED OCTOBER 6, 1980 IN BOOK 13776, PAGE 341 OF OFFICIAL RECORDS, COUNTY OF ORANGE. THE SANTA MARGARITA WATER DISTRICT SHALL RESTORE OTHER IMPROVEMENTS OR FACILITIES LOCATED WITHIN THE EASEMENT, IF IT HAS CONSENTED TO THE LOCATION OF SUCH IMPROVEMENTS OR FACILITIES TO THE EXTENT THAT THE EXERCISE OF ITS RIGHTS IN CONNECTION WITH THE EASEMENT IMPACTS OTHER IMPROVEMENTS OR FACILITIES LOCATED WITHIN THE EASEMENT, HOWEVER, IN NO EVENT SHALL SANTA MARGARITA WATER DISTRICT BE RESPONSIBLE FOR THE COST OF RELOCATING ITS FACILITIES IN THE EVENT CONFLICTS WITH SUCH OTHER IMPROVEMENTS OR FACILITIES.

RICHMOND AMERICAN HOMES OF CALIFORNIA, INC., A COLORADO CORPORATION.

BY: [Signature]
PRINT NAME Robert T. Shiota
PRINT TITLE President

BY: [Signature]
PRINT NAME Jon H. Sasaki
PRINT TITLE asst. sec.

DMB LADERA, LLC, A DELAWARE LIMITED LIABILITY COMPANY, BENEFICIARY UNDER A DEED OF TRUST RECORDED AS INSTRUMENT NO. 20000224838 OF OFFICIAL RECORDS.
BY: RANCHO MISSION VENO, LLC, A DELAWARE LIMITED LIABILITY COMPANY, AS MANAGER

BY: [Signature]
PRINT NAME PAUL JOHNSON
PRINT TITLE V.P. - COMM. DEVEL

STATE OF CALIFORNIA }
COUNTY OF ORANGE } SS

ON THIS 14 DAY OF June, 2000, BEFORE ME, Monica Sierra
Robert T. Shiota and Jon H. Sasaki PERSONALLY KNOWN
TO ME (OR PROVED TO ME ON THE BASIS OF SATISFACTORY EVIDENCE) TO BE THE PERSON(S) WHOSE NAME(S)
IS/ARE SUBSCRIBED TO THE WITHIN INSTRUMENT AND ACKNOWLEDGED TO ME THAT HE/SHE/THEY EXECUTED
THE SAME IN HIS/HER/THEIR AUTHORIZED CAPACITY(IES), AND THAT BY HIS/HER/THEIR SIGNATURE(S) ON THE
INSTRUMENT THE PERSON(S), OR THE ENTITY UPON BEHALF OF WHICH THE PERSON(S) ACTED, EXECUTED THE
INSTRUMENT

MY PRINCIPAL PLACE OF BUSINESS
IS IN Orange COUNTY.

MY COMMISSION EXPIRES: 4-11-02

WITNESS MY HAND:
[Signature]
(SIGNATURE)
NOTARY PUBLIC IN AND FOR SAID STATE
Monica Sierra
(PRINT NAME)

STATE OF CALIFORNIA }
COUNTY OF ORANGE } SS

ON THIS 15 DAY OF June, 2000, BEFORE ME, JEANNINE CARTA-HANSON
PAUL JOHNSON PERSONALLY KNOWN
TO ME (OR PROVED TO ME ON THE BASIS OF SATISFACTORY EVIDENCE) TO BE THE PERSON(S) WHOSE NAME(S)
IS/ARE SUBSCRIBED TO THE WITHIN INSTRUMENT AND ACKNOWLEDGED TO ME THAT HE/SHE/THEY EXECUTED
THE SAME IN HIS/HER/THEIR AUTHORIZED CAPACITY(IES), AND THAT BY HIS/HER/THEIR SIGNATURE(S) ON THE
INSTRUMENT THE PERSON(S), OR THE ENTITY UPON BEHALF OF WHICH THE PERSON(S) ACTED, EXECUTED THE
INSTRUMENT

MY PRINCIPAL PLACE OF BUSINESS
IS IN ORANGE COUNTY.

MY COMMISSION EXPIRES: 2-25-03

WITNESS MY HAND:
[Signature]
(SIGNATURE)
NOTARY PUBLIC IN AND FOR SAID STATE

SANTA MARGARITA WATER DISTRICT CERTIFICATE OF ACCEPTANCE:

THE UNDERSIGNED BEING THE DULY APPOINTED AGENT OF THE SANTA MARGARITA WATER DISTRICT, A PUBLIC CORPORATION IN ORANGE COUNTY, CALIFORNIA, PURSUANT TO ITS RESOLUTION NO. 88-10-2, DOES HEREBY ACCEPT ON BEHALF OF SAID DISTRICT THE PIPELINE EASEMENTS FOR SEWER AND WATER PURPOSES, AS DEDICATED AND AS SHOWN ON THIS TRACT MAP, BY AND BETWEEN THE SANTA MARGARITA WATER DISTRICT AND RICHMOND AMERICAN HOMES OF CALIFORNIA, INC., AND DOES HEREBY CERTIFY THAT THE GRANTEE CONSENTS TO THE RECORDATION OF SAID TRACT MAP

[Signature]
DANIEL R. FERONS, CHIEF ENGINEER
SANTA MARGARITA WATER DISTRICT

STATE OF CALIFORNIA }
COUNTY OF ORANGE } SS

ON THIS 23rd DAY OF JUNE, 2000, BEFORE ME, ANDREA M. EVANS
PERSONALLY APPEARED DANIEL R. FERONS, PERSONALLY KNOWN TO ME (OR PROVED TO ME ON THE BASIS OF SATISFACTORY EVIDENCE) TO BE THE PERSON WHOSE NAME IS SUBSCRIBED TO THE WITHIN INSTRUMENT AND ACKNOWLEDGED TO ME THAT HE EXECUTED THE SAME IN HIS AUTHORIZED CAPACITY, AND THAT BY HIS SIGNATURE ON THE INSTRUMENT THE PERSON, OR THE ENTITY UPON BEHALF OF WHICH THE PERSON ACTED, EXECUTED THE INSTRUMENT

MY PRINCIPAL PLACE OF BUSINESS
IS IN ORANGE COUNTY

MY COMMISSION EXPIRES: 04/08/04

WITNESS MY HAND:
[Signature]
(SIGNATURE)
NOTARY PUBLIC IN AND FOR SAID STATE
ANDREA M. EVANS
(PRINT NAME)

SURVEYOR'S STATEMENT:

I HEREBY STATE THAT THIS MAP CONSISTING OF 6 SHEETS, CORRECTLY REPRESENTS A TRUE AND COMPLETE SURVEY AS SHOWN MADE IN FEBRUARY 2000; WAS MADE BY ME OR UNDER MY DIRECTION; THAT THE MONUMENTS ARE OF THE CHARACTER AND OCCUPY (OR WILL OCCUPY) THE POSITIONS INDICATED BY SAID MAP; AND THAT SAID MONUMENTS ARE (OR WILL BE) SUFFICIENT TO ENABLE THE SURVEY TO BE RETRACED.

[Signature]
THOMAS EARL PROPST, P.L.S. 6098
LICENSE EXPIRES 12-31-01



COUNTY SURVEYOR'S STATEMENT:

I HEREBY STATE THAT I HAVE EXAMINED THIS MAP AND FOUND IT TO BE SUBSTANTIALLY IN CONFORMANCE WITH THE TENTATIVE MAP, AS FILED WITH, AMENDED AND APPROVED BY THE ORANGE COUNTY SUBDIVISION COMMITTEE; THAT ALL PROVISIONS OF THE SUBDIVISION MAP ACT AND COUNTY SUBDIVISION REGULATIONS HAVE BEEN COMPLIED WITH AND I AM SATISFIED SAID MAP IS TECHNICALLY CORRECT.

DATED THIS 11th DAY OF August, 2000.

[Signature]
JOHN CANAS, COUNTY SURVEYOR



COUNTY TREASURER-TAX COLLECTOR'S CERTIFICATE:

STATE OF CALIFORNIA }
COUNTY OF ORANGE } SS

I HEREBY CERTIFY THAT ACCORDING TO THE RECORDS OF MY OFFICE THERE ARE NO LIENS AGAINST THE LAND COVERED BY THIS MAP OR ANY PART THEREOF FOR UNPAID STATE, COUNTY, MUNICIPAL OR LOCAL TAXES OR SPECIAL ASSESSMENTS COLLECTED AS TAXES, EXCEPT TAXES OR SPECIAL ASSESSMENTS COLLECTED AS TAXES NOT YET PAYABLE. AND DO ALSO CERTIFY TO THE RECORDER OF ORANGE COUNTY THAT THE PROVISIONS OF THE SUBDIVISION MAP ACT HAVE BEEN COMPLIED WITH REGARDING DEPOSITS TO SECURE THE PAYMENT OF TAXES OR SPECIAL ASSESSMENTS COLLECTED AS TAXES ON THE LAND COVERED BY THIS MAP.

DATED THIS 26th DAY OF July, 2000.

JOHN M. W. MOORLACH BY [Signature]
COUNTY TREASURER-TAX COLLECTOR DEPUTY TREASURER-TAX COLLECTOR

CLERK OF THE BOARD OF SUPERVISOR'S CERTIFICATE:

STATE OF CALIFORNIA }
COUNTY OF ORANGE } SS

I HEREBY CERTIFY THAT THIS MAP WAS PRESENTED FOR APPROVAL TO THE BOARD OF SUPERVISORS OF ORANGE COUNTY AT A REGULAR MEETING THEREOF HELD ON THE 22nd DAY OF August, 2000, AND THAT THEREUPON SAID BOARD DID, BY AN ORDER DULY PASSED AND ENTERED, APPROVE SAID MAP AND DID ACCEPT ON BEHALF OF THE PUBLIC, SUBJECT TO IMPROVEMENTS; THE DEDICATION FOR STREET PURPOSES OF: WESTCOTT LANE AND LIVINGSTON PLACE.

AND DID ALSO ACCEPT ON BEHALF OF THE COUNTY OF ORANGE;

1. THE EASMENT FOR EMERGENCY VEHICULAR ACCESS AS DEDICATED.
2. THE EASEMENT FOR STORM DRAIN PURPOSES AS DEDICATED.

AND DID ALSO APPROVE SAID MAP PURSUANT TO THE PROVISIONS OF SECTION 66436(a)(3)(A) OF THE SUBDIVISION MAP ACT.

DATED THIS 28th DAY OF August, 2000

[Signature]
DARLENE J. BLOOM
CLERK OF THE BOARD OF SUPERVISORS
OF ORANGE COUNTY, CALIFORNIA



SIGNATURE OMISSION NOTES:

IN ACCORDANCE WITH THE PROVISIONS OF SECTION 66436(a)(3)(A) OF THE SUBDIVISION MAP ACT, THE FOLLOWING SIGNATURES HAVE BEEN OMITTED:

- 1.) LADERA DEVELOPMENT COMPANY, L.L.C. HOLDER OF OIL, GAS, MINERAL, AND WATER RIGHTS RECORDED AS INSTRUMENT NO. 19960624029 OF OFFICIAL RECORDS.
- 2.) DMB LADERA, L.L.C., HOLDER OF EASEMENTS RECORDED AS INSTRUMENT NO. 20000224836 OF OFFICIAL RECORDS. (NOTE: SAID EASEMENTS ARE BLANKET IN NATURE AND ARE NOT PLOTTABLE)

SHEET 2 OF 6 SHEETS
9.937 ACRES
83 NUMBERED LOTS AND
LETTERED LOTS "A" THROUGH "Y"
DATE OF SURVEY: FEBRUARY 2000
(A PORTION OF VESTING
TENTATIVE TRACT NO. 15914)

TRACT NO. 15915

IN THE UNINCORPORATED TERRITORY OF THE COUNTY OF ORANGE, STATE OF CALIFORNIA.
THOMAS EARL PROPST, P.L.S. 6098
FUSCOE ENGINEERING
FEBRUARY 2000

MONUMENT NOTES:

▲ OCS GPS MONUMENT AS NOTED.

■ FOUND 1" I.P. TAGGED "RCE 28946" PER TRACT 15827, M.M. 797/32-39.

□ 1" I.P. TAGGED "RCE 28946" OR LEAD & TAG STAMPED "RCE 28946" IN CONCRETE TO BE SET AT ALL LOT CORNERS EXCEPT LOT CORNERS THAT ABUT A STREET WHICH WILL BE MARKED ON A 8.75' OFFSET OUTSIDE THE TRUE LOT CORNER IN CONCRETE BE A LEAD AND TAG "RCE 28946" ON SIDELINES PRODUCED, UNLESS OTHERWISE NOTED. (NO MONUMENTS WILL BE SET FOR ANGLE POINTS, CORNER CUTOFFS, B.C.'S, E.C.'S, P.C.C.'S OR P.R.C.'S THAT ABUT STREET WHICH ARE NOT LOT CORNERS MARKING SIDELINES, UNLESS OTHERWISE NOTED.) TO BE SET PER TRACT 15827, M.M. 797/32-39.

○ 8" SPIKE AND WASHER STAMPED "RCE 28946" IN ASPHALT PAVING OR LEAD AND TAG "RCE 28946" IN CONCRETE TO BE SET AT ALL CENTERLINE INTERSECTIONS, B.C.'S, E.C.'S AND ALL OTHER CENTERLINE POINTS OF CONTROL, UNLESS OTHERWISE NOTED, WITHIN 90 DAYS AFTER ACCEPTANCE OF IMPROVEMENTS. PER TRACT 15827, M.M. 797/32-39.

1" I.P. TAGGED "L.S. 6098" OR SPIKE AND WASHER STAMPED "L.S. 6098" OR LEAD AND TAG "L.S. 6098" TO BE SET AT LOT CORNERS (UNLESS OTHERWISE NOTED) WITHIN 90 DAYS AFTER ACCEPTANCE OF IMPROVEMENTS.

1" I.P. TAGGED "L.S. 6098" OR SPIKE AND WASHER STAMPED "L.S. 6098" OR LEAD AND TAG "L.S. 6098" TO BE SET AT ALL CENTERLINE POINTS OF CONTROL (UNLESS OTHERWISE NOTED) WITHIN 90 DAYS AFTER ACCEPTANCE OF IMPROVEMENTS.

NO MONUMENTATION WILL BE SET AT B.C.'S, E.C.'S, P.C.C.'S, OR P.R.C.'S OF DEDICATED PUBLIC STREET SIDE LINES WHICH ARE NOT LOT CORNERS MARKING LOT SIDELINES, UNLESS OTHERWISE NOTED.

SURVEYOR'S NOTES:

ALL LETTERED LOTS SHOWN HEREON ARE NOT SEPARATE BUILDING SITES.

LOTS "A" THROUGH "M", INCLUSIVE, ARE FOR PRIVATE DRIVEWAYS, EMERGENCY VEHICULAR ACCESS, AND PIPELINE EASEMENTS FOR SEWER AND WATER PURPOSES AND ARE TO BE CONVEYED TO THE APPROPRIATE HOMEOWNERS ASSOCIATION.

LOTS "N" THROUGH "Y", INCLUSIVE, ARE FOR LANDSCAPE PURPOSES AND ARE TO BE CONVEYED TO THE APPROPRIATE HOMEOWNERS ASSOCIATION.

BASIS OF BEARINGS:

BEARINGS SHOWN HEREON ARE BASED ON THE LINE BETWEEN O.C.S. HORIZONTAL CONTROL STATION NO. 9009 AND STATION NO. 1426 BEARING NORTH 61°10'47" EAST PER RECORDS ON FILE IN THE OFFICE OF THE ORANGE COUNTY SURVEYOR.

DATUM STATEMENT:


BEARINGS SHOWN HEREON ARE BASED UPON THE CALIFORNIA COORDINATE SYSTEM (CCS83) ZONE V 1983 NAD (1991.35 EPOCH O.C.S. GPS ADJUSTMENT). ALL DISTANCES SHOWN ARE GROUND DISTANCES UNLESS OTHERWISE NOTED. TO OBTAIN GRID DISTANCE MULTIPLY GROUND DISTANCE BY 0.99993923

NOTE:

THE PROPERTY IS "CONDITIONALLY EXCLUDED" FROM A "SPECIAL FIRE PROTECTION AREA". NO LOTS ARE SUBJECT TO CONSTRUCTION FEATURES OF THE ORANGE COUNTY ORDINANCE 3960 PER THE APPROVED FIRE MASTER PLAN FOR THIS TRACT.

HIGH/VERY HIGH FIRE HAZARD AREA NOTE:

THE LOTS SHOWN ON THIS MAP ARE IN A HIGH/VERY HIGH FIRE HAZARD AREA DUE TO WILDLAND EXPOSURE BASED ON SRA (STATE RESPONSIBILITY AREA) MAPS

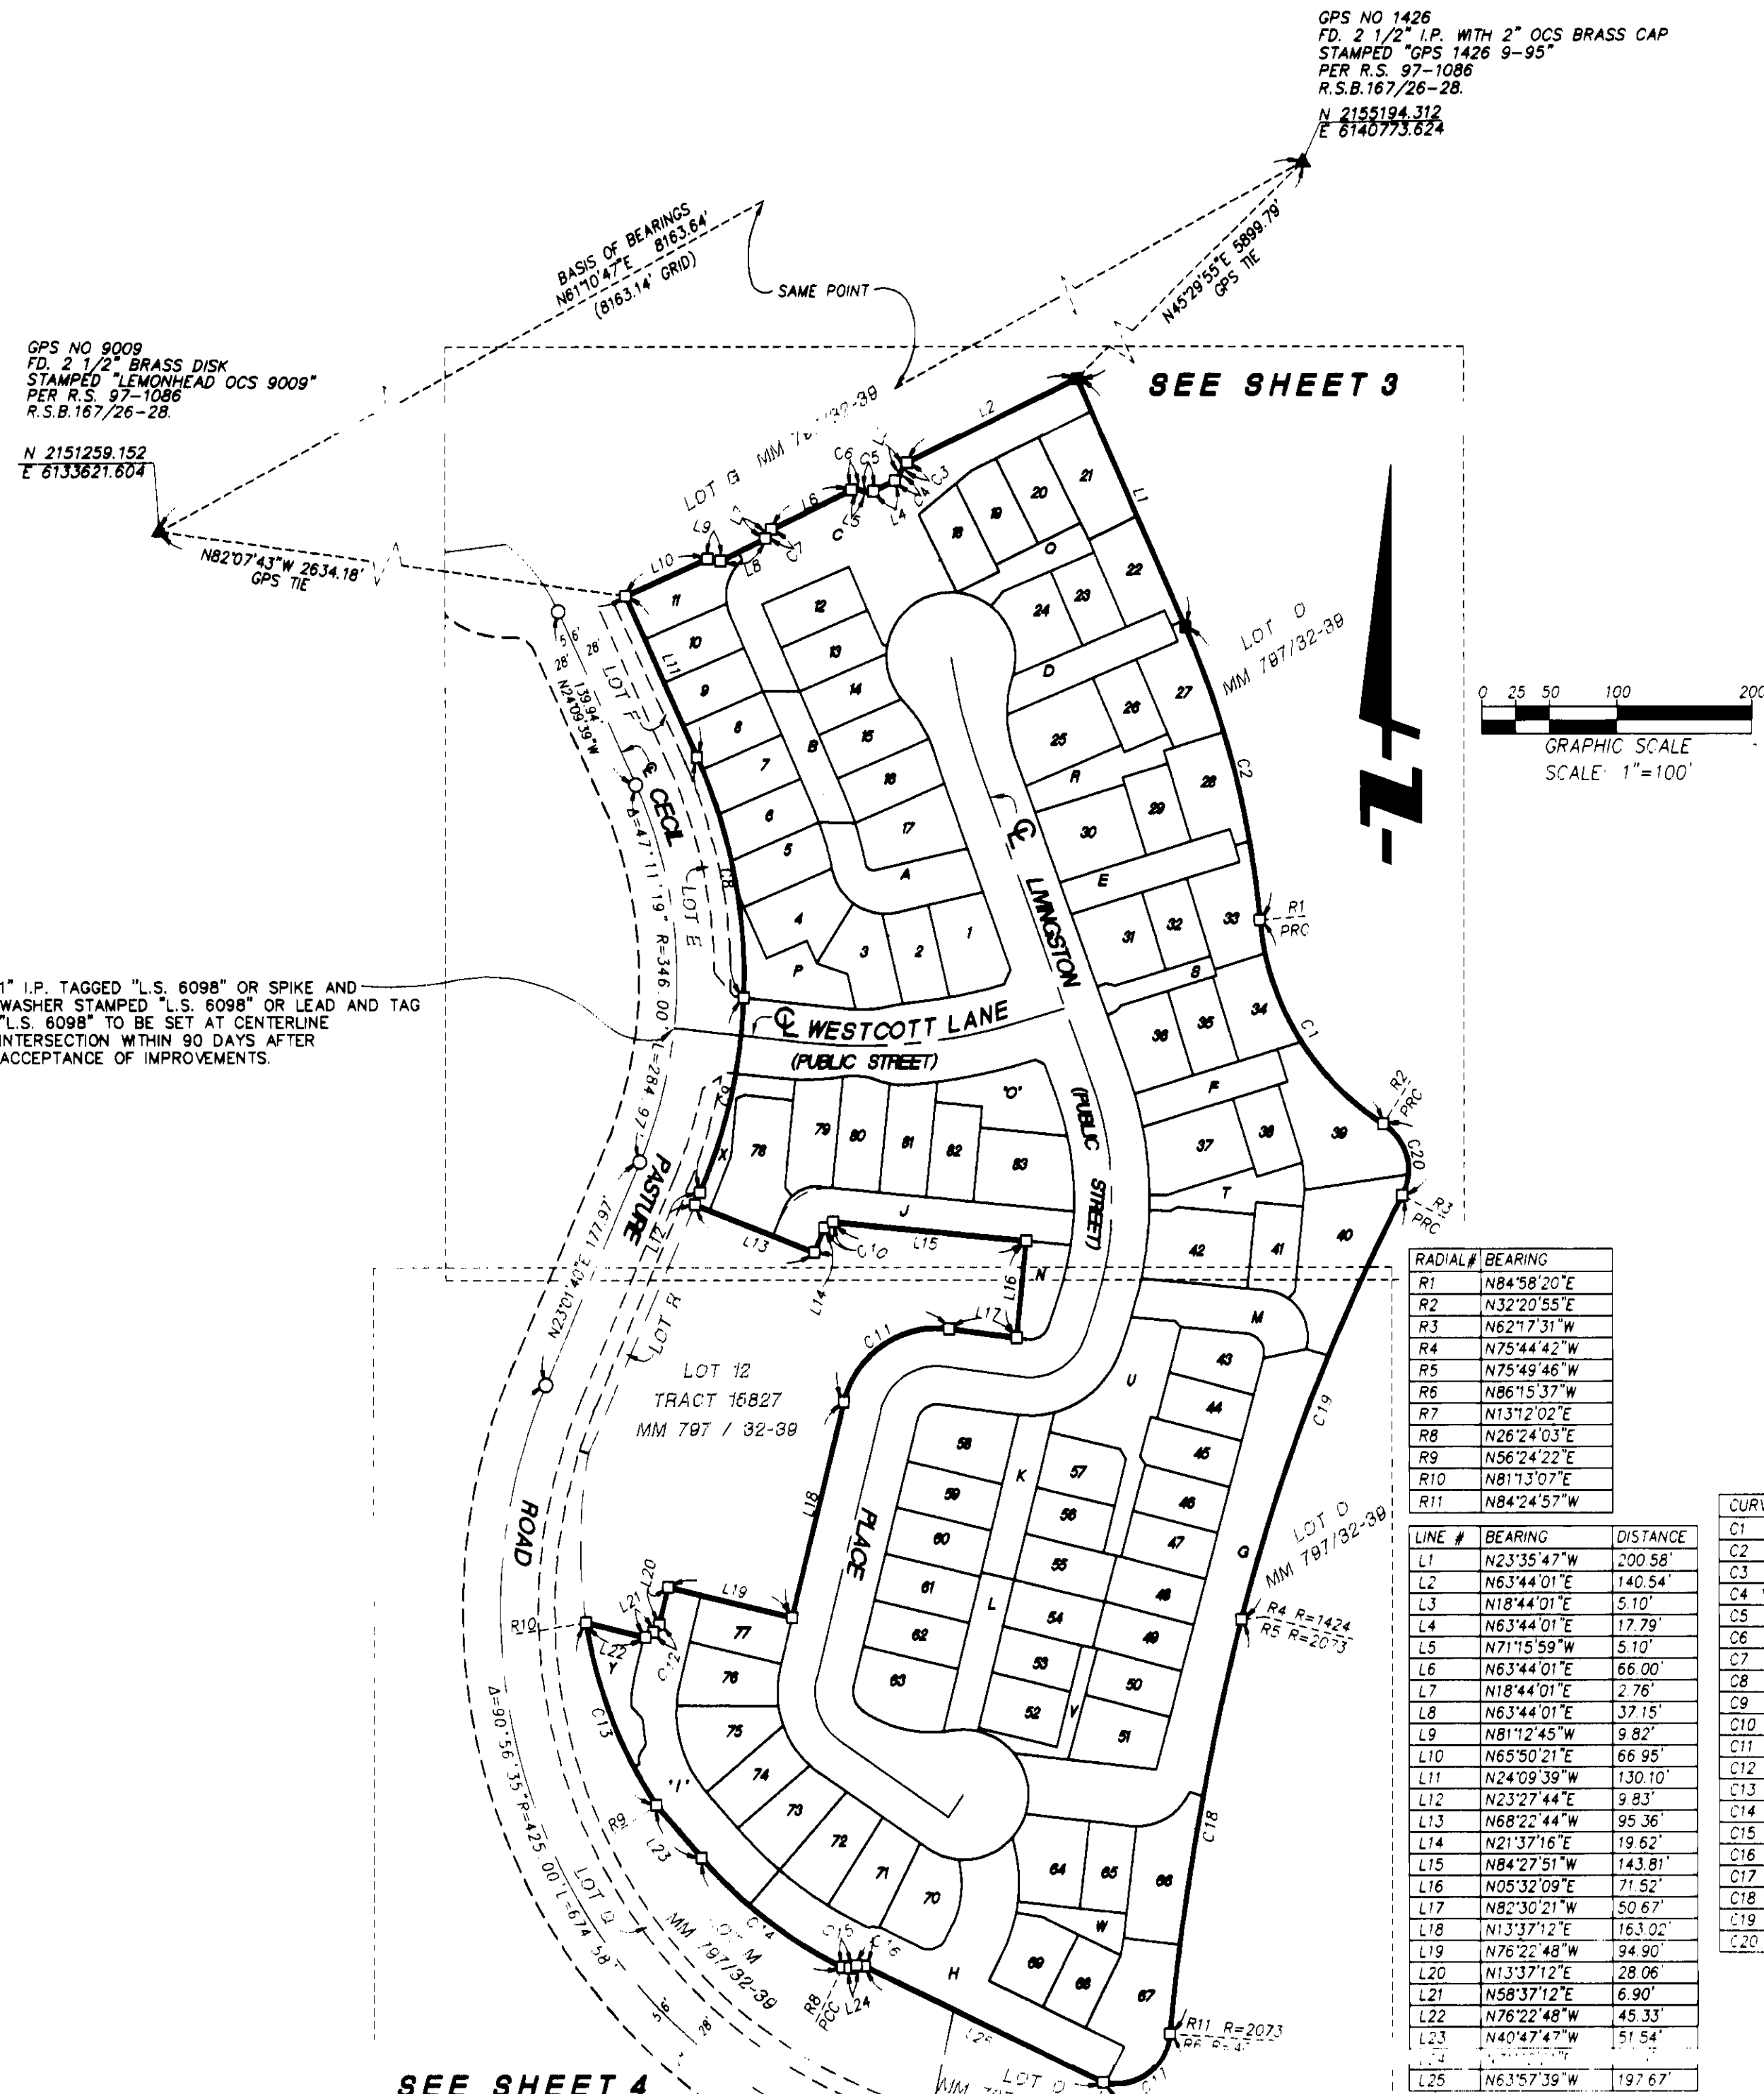

RADIAL#	BEARING
R1	N84°58'20"E
R2	N32°20'55"E
R3	N62°17'31"W
R4	N75°44'42"W
R5	N75°49'46"W
R6	N86°15'37"W
R7	N13°12'02"E
R8	N26°24'03"E
R9	N56°24'22"E
R10	N81°13'07"E
R11	N84°24'57"W

LINE #	BEARING	DISTANCE
L1	N23°35'47"W	200.58'
L2	N63°44'01"E	140.54'
L3	N18°44'01"E	5.10'
L4	N63°44'01"E	17.79'
L5	N71°15'59"W	5.10'
L6	N63°44'01"E	66.00'
L7	N18°44'01"E	2.76'
L8	N63°44'01"E	37.15'
L9	N81°12'45"W	9.82'
L10	N65°50'21"E	66.95'
L11	N24°09'39"W	130.10'
L12	N23°27'44"E	9.83'
L13	N68°22'44"W	95.36'
L14	N21°37'16"E	19.62'
L15	N84°27'51"W	143.81'
L16	N05°32'09"E	71.52'
L17	N82°30'21"W	50.67'
L18	N13°37'12"E	163.02'
L19	N76°22'48"W	94.90'
L20	N13°37'12"E	28.06'
L21	N58°37'12"E	6.90'
L22	N76°22'48"W	45.33'
L23	N40°47'47"W	51.54'
L24	N13°37'12"E	142.40'
L25	N63°57'39"W	197.67'

CURVE#	DELTA	RADIUS	LENGTH
C1	52°37'25"	198.00	181.85
C2	18°34'07"	690.00	223.62
C3	45°00'00"	7.00	5.50
C4	45°00'00"	8.00	6.28
C5	45°00'00"	8.00	6.28
C6	45°00'00"	7.00	5.50
C7	45°00'00"	7.00	5.50
C8	26°17'06"	396.00	181.67
C9	21°20'17"	396.00	147.48
C10	73°54'53"	6.50	8.39
C11	83°52'27"	71.00	103.94
C12	45°00'00"	9.50	7.46
C13	24°48'45"	335.00	145.08
C14	22°48'10"	334.00	132.93
C15	45°21'42"	7.00	5.54
C16	45°00'00"	8.00	6.28
C17	99°27'39"	40.00	69.44
C18	08°35'11"	2073.00	310.66
C19	13°27'11"	1424.00	334.35
C20	85°21'34"	40.00	59.59

SHEET 3 OF 6 SHEETS
9.937 ACRES
83 NUMBERED LOTS AND
LETTERED LOTS "A" THROUGH "Y"
DATE OF SURVEY: FEBRUARY 2000
(A PORTION OF VESTING
TENTATIVE TRACT NO. 15914)

TRACT NO. 15915


IN THE UNINCORPORATED TERRITORY OF THE COUNTY OF ORANGE, STATE OF CALIFORNIA.

THOMAS EARL PROPST, P.L.S. 6098

FUSCO ENGINEERING

FEBRUARY 2000

LINE #	BEARING	DISTANCE	CURVE #	DELTA	RADIUS	LENGTH
L1	N25°14'33"E	11.65'	C1	27°00'55"	90.00	42.43
L2	N70°14'33"E	28.00'	C2	37°07'02"	90.00	58.30
L3	N18°14'34"E	24.13'	C3	79°15'05"	15.00	20.75
L4	N18°14'34"E	24.13'	C4	25°38'20"	48.11	20.83
L5	N19°45'27"W	25.50'	C5	14°16'39"	209.92	52.31
L6	N64°45'27"W	7.85'	C6	06°32'55"	54.00	6.17
L7	N70°14'33"E	28.00'	C7	23°21'42"	40.00	16.31
L8	N23°22'40"W	54.62'	C8	19°38'31"	96.00	32.91
L9	N21°37'18"E	19.62'	C9	08°04'06"	104.00	14.65
L10	N81°12'45"W	9.82'	C10	73°54'53"	6.50	8.39
L11	N18°44'01"E	2.76'	C11	45°00'00"	7.00	5.50
L12	N71°15'59"W	5.10'	C12	45°00'00"	7.00	5.50
L13	N18°44'01"E	5.10'	C13	45°00'00"	8.00	6.28
L14	N88°31'20"W	26.67'	C14	20°27'01"	198.00	70.67
L15	N19°45'27"W	6.58'	C15	85°21'34"	40.00	59.59
L16	N23°22'40"W	11.40'	C16	59°18'58"	34.50	35.71
L17	N23°22'40"W	18.40'	C17	73°04'47"	34.50	44.00
L18	N70°40'22"W	24.08'	C18	13°45'49"	34.50	8.29
L19	N12°58'59"W	26.48'	C19	45°00'00"	8.00	6.28
L20	N50°28'43"E	50.82'	C20	45°00'00"	7.00	5.50
L21	N23°05'10"W	12.49'	C21	03°11'38"	396.00	22.07
L22	N21°30'28"W	9.80'	C22	05°07'08"	396.00	35.38
L23	N63°44'01"E	17.79'	C23	12°04'42"	262.50	55.34
L24	N38°37'18"W	8.43'	C24	06°58'10"	262.50	31.70
L25	N23°05'10"W	12.51'	C25	91°41'01"	5.00	8.00
L26	N66°24'13"E	9.14'	C26	02°25'56"	428.00	18.17
L27	N72°55'44"E	11.22'	C27	06°35'07"	90.00	10.34
L28	N23°27'44"E	9.83'	C28	05°09'32"	262.50	23.64
L29	N05°32'08"E	15.51'	C29	20°25'48"	90.00	32.09
L30	N05°32'08"E	15.12'	C30	42°56'31"	48.00	35.98
L31	N83°49'18"W	28.97'	C31	01°25'04"	396.00	9.80
L32	N68°32'54"E	6.49'	C32	05°04'24"	396.00	35.07
L33	N43°08'53"E	7.55'	C33	02°55'11"	104.00	5.30
L34	N89°29'33"W	27.34'	C34	04°37'30"	370.00	29.87
L35	N77°58'49"E	32.49'	C35	06°28'33"	370.00	41.82
L36	N44°39'47"W	6.24'	C36	91°31'21"	39.50	63.10
L37	N72°28'29"W	6.99'	C37	11°55'02"	237.50	49.40
L38	N79°35'30"W	3.70'	C38	15°59'29"	39.50	11.02
L39	N70°14'33"E	3.99'	C39	32°45'39"	39.50	22.59
L40	N70°14'33"E	3.99'	C40	42°46'13"	39.50	29.49
L41	N62°37'13"E	5.83'	C41	08°31'13"	237.50	35.32
L42			C42	03°01'29"	237.50	12.54
L43			C43	00°22'20"	237.50	1.20
L44			C44	13°15'18"	9.50	2.50
L45			C45	32°53'10"	48.00	27.55
L46			C46	18°08'30"	90.00	28.50
L47			C47	05°09'49"	278.00	25.05
L48			C48	01°11'58"	48.00	1.00
L49			C49	03°33'45"	278.00	17.29
L50			C50	02°17'44"	278.00	11.14
L51			C51	49°39'28"	25.50	22.10
L52			C52	24°15'25"	25.50	10.80
L53			C53	29°40'17"	34.50	17.87
L54			C54	04°03'17"	396.00	28.03
L55			C55	04°03'16"	396.00	28.02
L56			C56	07°12'39"	198.00	24.92
L57			C57	06°03'51"	278.00	28.42
L58			C58	18°58'32"	90.00	29.80
L59			C59	00°08'31"	278.00	0.69
L60			C60	06°27'20"	222.00	25.01
L61			C61	07°40'05"	222.00	29.71
L62			C62	22°05'43"	54.00	20.82
L63			C63	12°43'21"	430.00	95.48
L64			C64	99°17'36"	34.50	59.79
L65			C65	89°37'19"	34.50	41.92
L66			C66	81°59'52"	40.00	43.28
L67			C67	15°29'18"	96.00	25.95
L68			C68	05°08'55"	104.00	9.35
L69			C69	09°32'09"	222.00	36.95
L70			C70	14°20'27"	222.00	55.57
L71			C71	04°35'07"	48.00	3.84
L72			C72	73°54'53"	25.50	32.90
L73			C73	99°17'36"	14.50	25.13
L74			C74	04°09'13"	96.00	6.96
L75			C75	15°32'48"	54.00	14.65
L76			C76	07°13'18"	48.00	6.05
L77			C77	50°28'40"	11.00	9.88
L78			C78	42°28'06"	11.00	8.15
L79			C79	04°09'38"	209.92	15.24
L80			C80	09°40'04"	209.92	35.42
L81			C81	00°26'57"	209.92	1.65
L82			C82	09°56'51"	430.00	74.65
L83			C83	02°46'30"	430.00	20.83

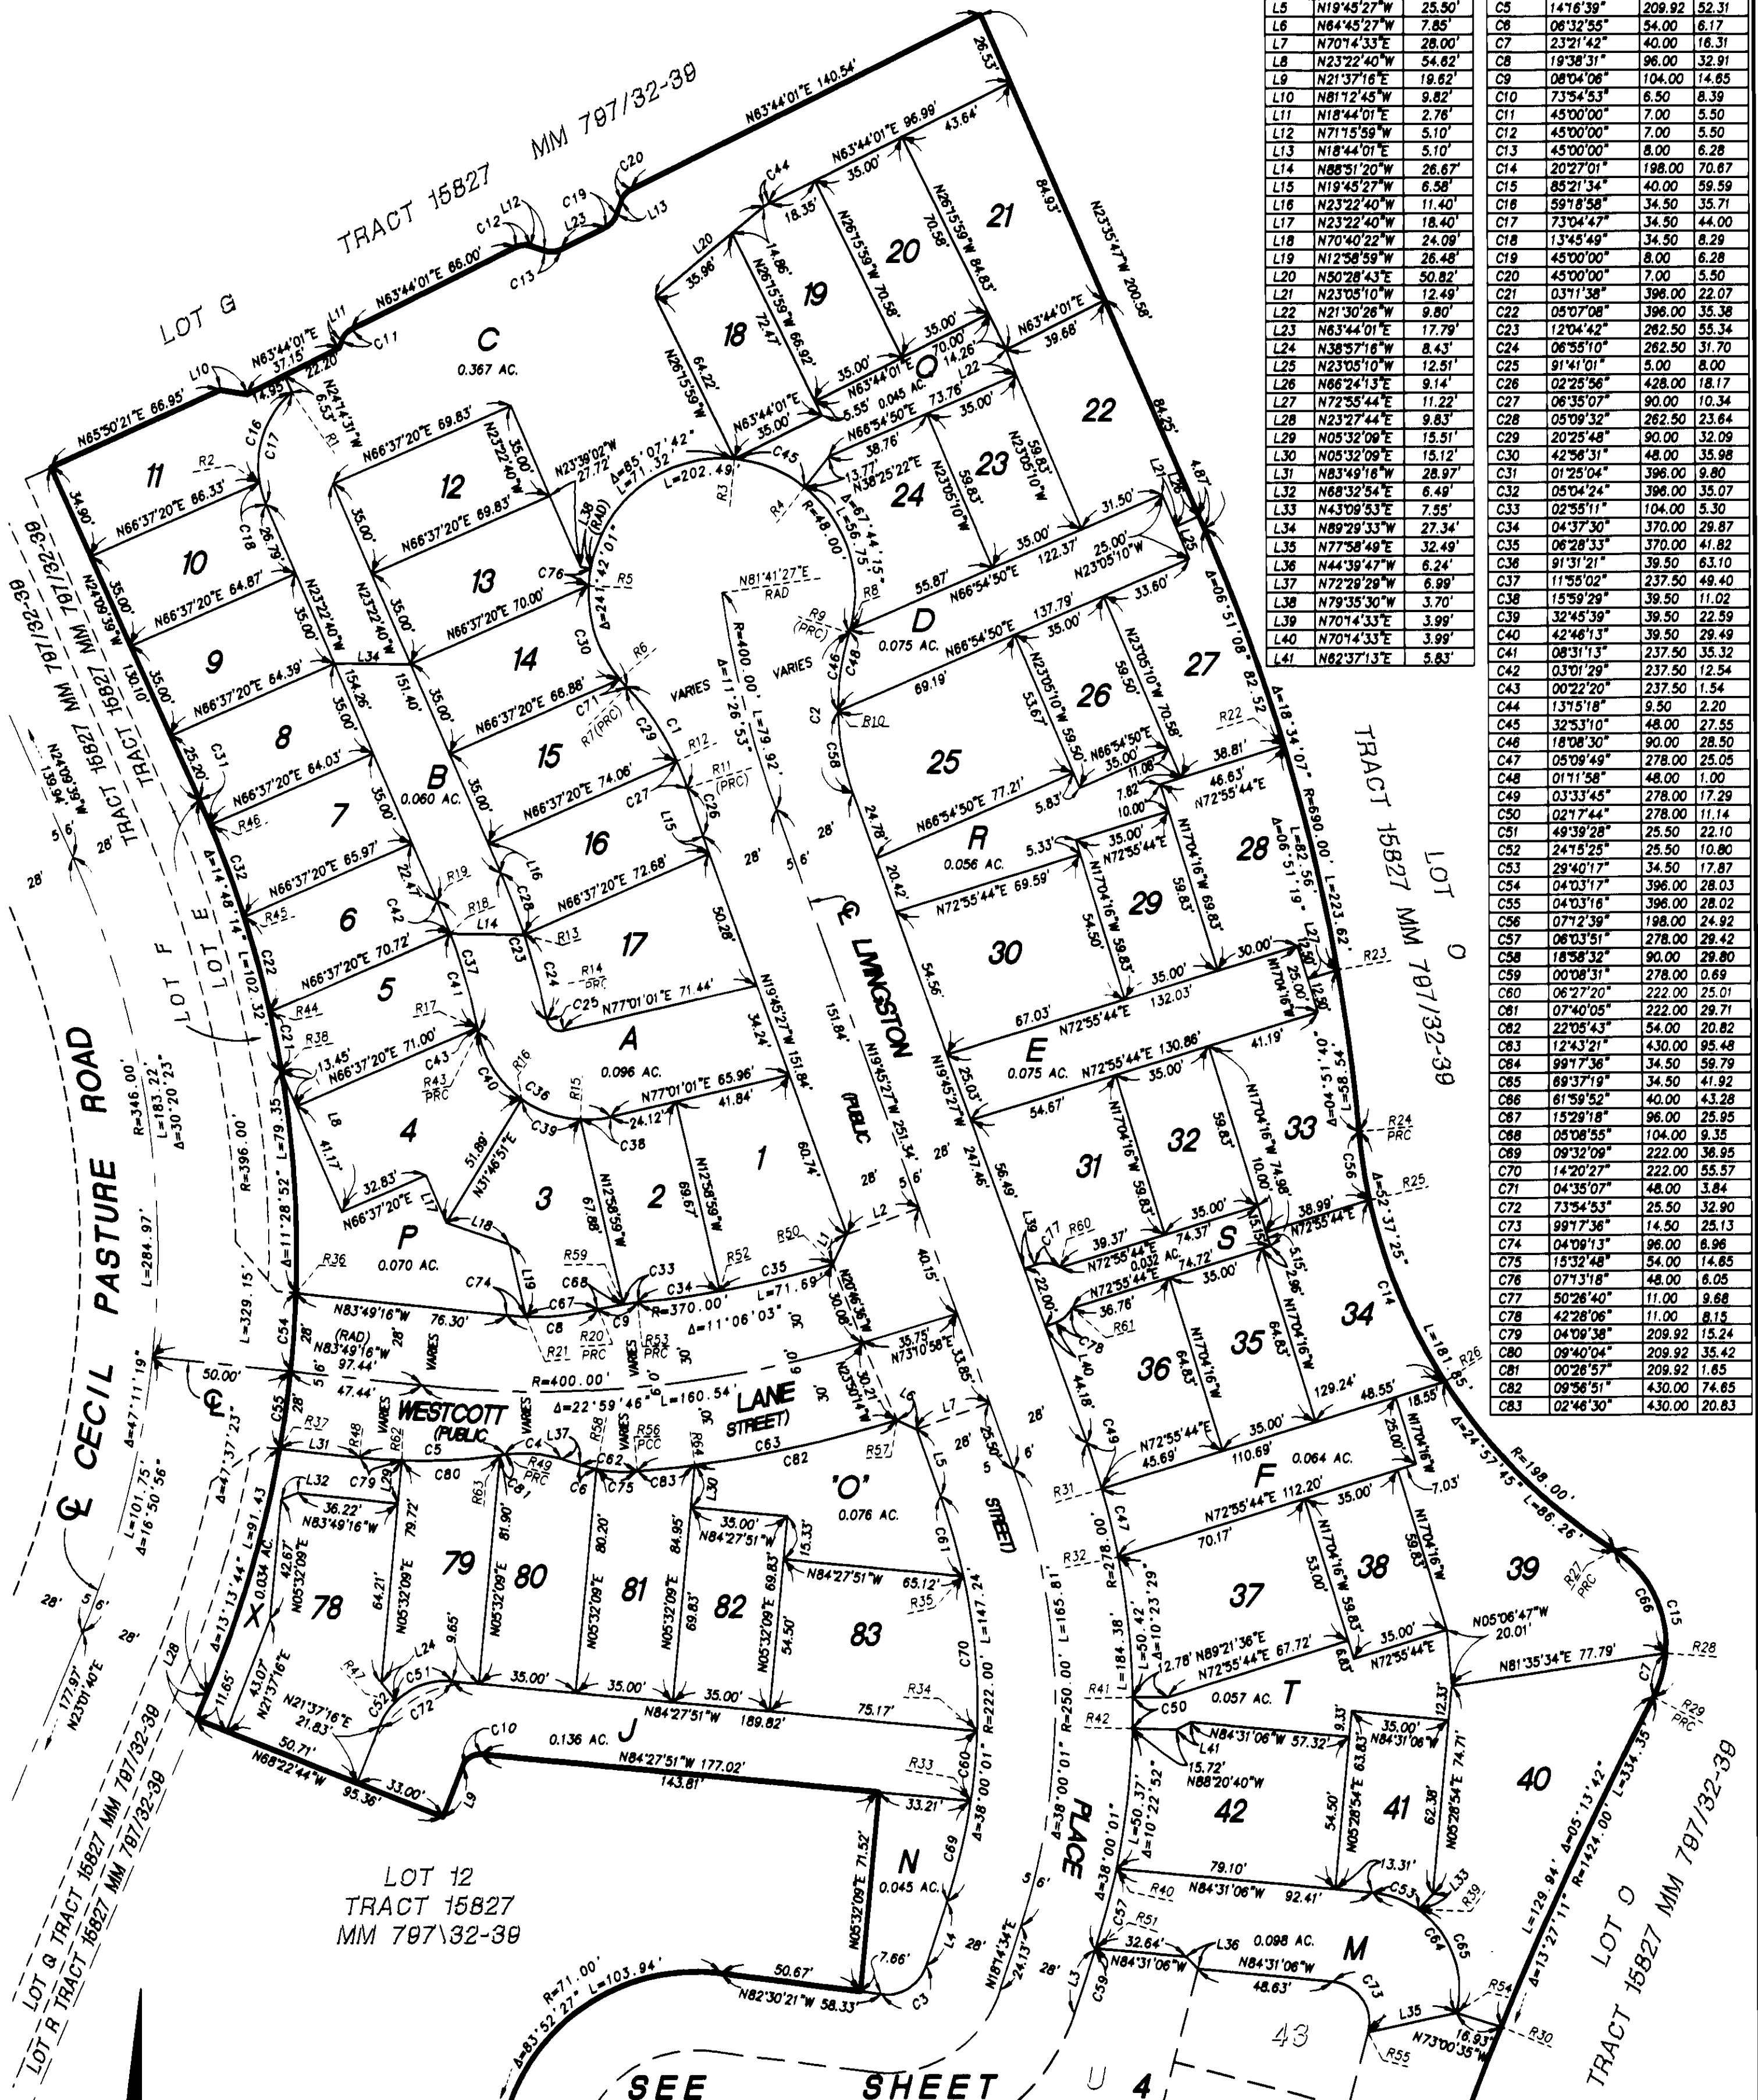

RADIAL #	BEARING	RADIAL #	BEARING	RADIAL #	BEARING	RADIAL #	BEARING	RADIAL #	BEARING
R1	N40°17'53"W	R16	N35°48'09"E	R31	N73°48'18"E	R46	N67°15'25"E	R61	N82°31'33"W
R2	N80°23'09"E	R17	N78°10'02"E	R32	N78°58'07"E	R47	N44°07'19"W	R62	N01°58'12"E
R3	N05°32'12"E	R18	N69°38'49"E	R33	N81°17'35"W	R48	N06°08'50"E	R63	N07°40'52"W
R4	N38°25'22"E	R19	N66°37'20"E	R34	N87°44'55"W	R49	N08°07'49"W	R64	N07°21'42"W
R5	N66°48'48"W	R20	N13°27'47"W	R35	N77°54'38"E	R50	N16°29'44"W		
R6	N50°14'41"E	R21	N02°01'31"E	R36	N87°52'33"W	R51	N71°53'57"W		
R7	N45°39'34"E	R22	N73°15'21"E	R37	N79°46'00"W	R52	N10°01'11"W		
R8	N73°50'23"W	R23	N80°06'40"E	R38	N80°38'35"E	R53	N05°23'41"W		
R9	N72°38'25"W	R24	N84°58'20"E	R39	N35°09'11"E	R54	N75°13'30"W		
R10	N89°13'05"E	R25	N77°45'41"E	R40	N77°37'48"W	R55	N75°13'30"W		
R11	N72°40'29"E	R26	N57°18'40"E	R41	N89°21'36"E	R56	N04°35'12"W		
R12	N66°05'22"E	R27	N32°20'55"E	R42	N88°20'40"W	R57	N17°78'33"W		
R13	N71°46'52"E	R28	N85°39'13"W	R43	N78°32'22"E	R58	N10°57'36"E		
R14	N78°42'02"E	R29	N82°17'31"W	R44	N77°28'57"E	R59	N08°18'52"W		
R15	N03°00'30"E	R30	N67°31'13"W	R45	N72°19'49"E	R60	N30°41'13"E		

SEE SHEET 2 FOR BASIS OF BEARINGS, DATUM STATEMENT, MONUMENT NOTES, NOTES, CONTROL SCHEME AND VICINITY AND INDEX MAP.
SEE SHEET 5 FOR EASEMENT NOTES AND EASEMENT LOCATIONS.

SHEET 4 OF 6 SHEETS
9.937 ACRES
83 NUMBERED LOTS AND
LETTERED LOTS "A" THROUGH "Y"
DATE OF SURVEY: FEBRUARY 2000
(A PORTION OF VESTING
TENTATIVE TRACT No. 15914)

TRACT NO. 15915


IN THE UNINCORPORATED TERRITORY OF THE COUNTY OF ORANGE, STATE OF CALIFORNIA.

THOMAS EARL PROPST, P.L.S. 6098

FUSCOE ENGINEERING

FEBRUARY 2000

SEE SHEET 3

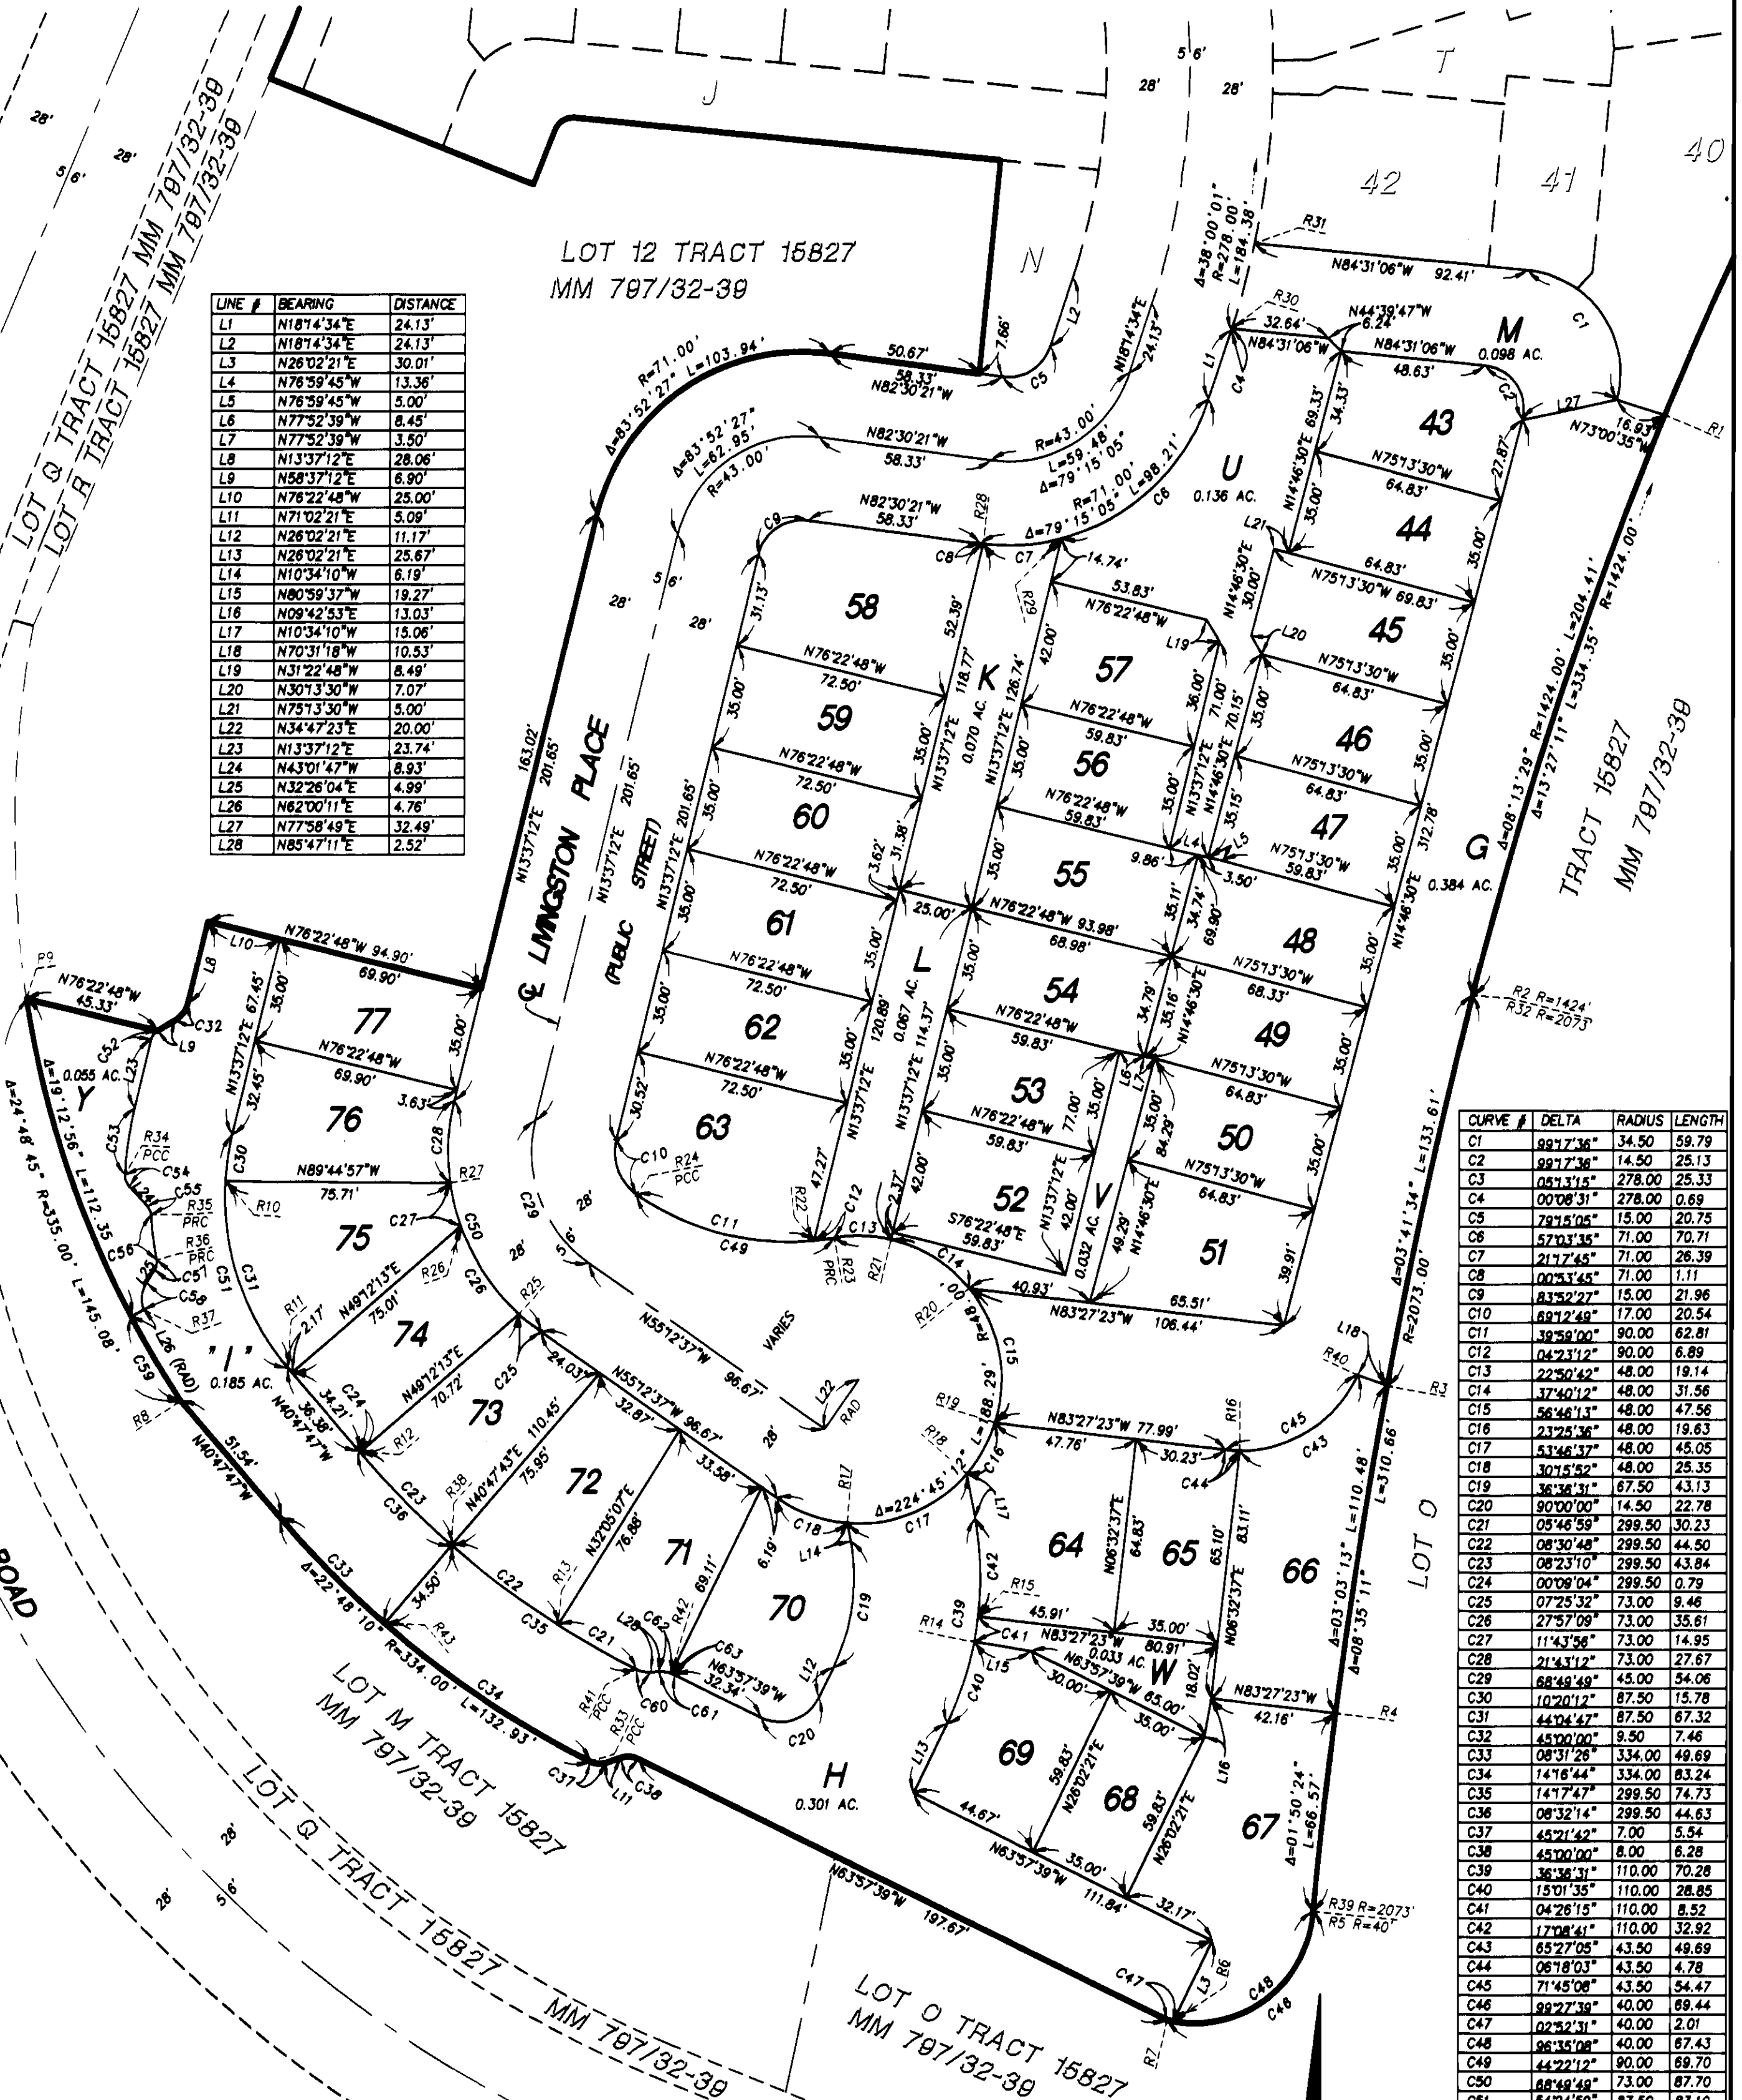


LINE #	BEARING	DISTANCE
L1	N187°43'34"E	24.13'
L2	N187°43'34"E	24.13'
L3	N26°02'21"E	30.01'
L4	N76°59'45"W	13.36'
L5	N76°59'45"W	5.00'
L6	N77°52'39"W	8.45'
L7	N77°52'39"W	3.50'
L8	N13°37'12"E	28.06'
L9	N58°37'12"E	6.90'
L10	N76°22'48"W	25.00'
L11	N71°02'21"E	5.09'
L12	N26°02'21"E	11.17'
L13	N26°02'21"E	25.67'
L14	N10°34'10"W	6.19'
L15	N80°59'37"W	19.27'
L16	N09°42'53"E	13.03'
L17	N10°34'10"W	15.06'
L18	N70°31'18"W	10.53'
L19	N31°22'48"W	8.49'
L20	N30°33'30"W	7.07'
L21	N75°13'30"W	5.00'
L22	N34°47'23"E	20.00'
L23	N13°37'12"E	23.74'
L24	N43°01'47"W	8.93'
L25	N32°26'04"E	4.99'
L26	N62°00'11"E	4.76'
L27	N77°58'49"E	32.49'
L28	N85°47'11"E	2.52'

CURVE #	DELTA	RADIUS	LENGTH
C1	99°17'36"	34.50	59.79
C2	99°17'36"	14.50	25.13
C3	05°13'15"	278.00	25.33
C4	00°08'31"	278.00	0.69
C5	79°15'05"	15.00	20.75
C6	57°03'35"	71.00	70.71
C7	21°17'45"	71.00	26.39
C8	00°53'45"	71.00	1.11
C9	83°52'27"	15.00	21.96
C10	89°12'49"	17.00	20.54
C11	39°58'00"	90.00	62.81
C12	04°23'12"	90.00	6.89
C13	22°50'42"	48.00	19.14
C14	37°40'12"	48.00	31.56
C15	56°46'13"	48.00	47.56
C16	23°25'36"	48.00	19.63
C17	53°46'37"	48.00	45.05
C18	30°15'52"	48.00	25.35
C19	36°36'31"	67.50	43.13
C20	90°00'00"	14.50	22.78
C21	05°46'59"	299.50	30.23
C22	08°30'48"	299.50	44.50
C23	08°23'10"	299.50	43.84
C24	00°09'04"	299.50	0.79
C25	07°25'32"	73.00	9.46
C26	27°57'09"	73.00	35.61
C27	11°43'56"	73.00	14.95
C28	21°43'12"	73.00	27.67
C29	88°49'49"	45.00	54.06
C30	10°20'12"	87.50	15.78
C31	44°04'47"	87.50	67.32
C32	45°00'00"	9.50	7.46
C33	08°31'28"	334.00	49.69
C34	14°16'44"	334.00	83.24
C35	14°17'47"	299.50	74.73
C36	08°32'14"	299.50	44.63
C37	45°21'42"	7.00	5.34
C38	45°00'00"	8.00	6.28
C39	36°36'31"	110.00	70.28
C40	15°01'35"	110.00	28.85
C41	04°26'15"	110.00	8.52
C42	17°08'41"	110.00	32.92
C43	65°27'05"	43.50	49.69
C44	08°18'03"	43.50	4.78
C45	71°45'08"	43.50	54.47
C46	99°27'39"	40.00	69.44
C47	02°32'31"	40.00	2.01
C48	96°35'08"	40.00	67.43
C49	44°22'12"	90.00	69.70
C50	68°49'49"	73.00	87.70
C51	54°24'59"	87.50	83.10
C52	45°00'00"	4.50	3.53
C53	10°39'37"	121.00	22.51
C54	45°59'22"	5.50	4.41
C55	39°52'41"	4.50	3.13
C56	07°46'47"	112.50	15.28
C57	43°21'57"	4.50	3.41
C58	51°37'28"	10.50	9.46
C59	05°35'49"	335.00	32.73
C60	30°35'01"	9.50	5.07
C61	30°15'10"	10.50	5.34
C62	23°45'05"	10.50	4.35
C63	08°30'05"	10.50	1.19

RADIAL #	BEARING	RADIAL #	BEARING	RADIAL #	BEARING
R1	N67°31'13"W	R18	N49°15'08"W	R35	N86°50'54"E
R2	N75°44'42"W	R19	N72°40'42"W	R36	N79°04'07"E
R3	N79°31'20"W	R20	N50°33'05"E	R37	N70°48'38"E
R4	N82°34'33"W	R21	N12°52'53"E	R38	N40°39'58"E
R5	N86°15'37"W	R22	N05°34'37"E	R39	N84°24'57"W
R6	N10°19'31"E	R23	N09°57'49"W	R40	N65°12'31"W
R7	N13°12'02"E	R24	N34°24'23"E	R41	N26°22'12"E
R8	N56°24'22"E	R25	N42°12'55"E	R42	N19°32'16"E
R9	N81°13'07"E	R26	N70°10'04"E	R43	N40°40'47"E
R10	N86°43'00"W	R27	N81°34'00"E		
R11	N49°12'13"E	R28	N08°35'54"E		
R12	N49°03'09"E	R29	N14°41'51"E		
R13	N32°09'11"E	R30	N71°53'57"W		
R14	N78°59'14"W	R31	N77°57'48"W		
R15	N83°25'29"E	R32	N75°49'48"W		
R16	N00°14'34"E	R33	N26°24'03"E		
R17	N04°31'31"E	R34	N87°02'25"W		

SEE SHEET 2 FOR BASIS OF BEARINGS, DATUM STATEMENT, MONUMENT NOTES, NOTES, CONTROL SCHEME AND VICINITY AND INDEX MAP.
SEE SHEET 6 FOR EASEMENT NOTES AND LOCATIONS

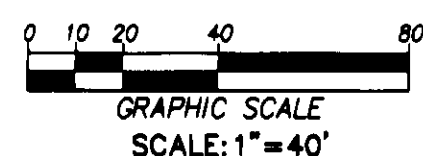

SHEET 5 OF 6 SHEETS
9.937 ACRES
83 NUMBERED LOTS AND
LETTERED LOTS "A" THROUGH "Y"
DATE OF SURVEY: FEBRUARY 2000
(A PORTION OF VESTING
TENTATIVE TRACT No. 15914)

TRACT NO. 15915

IN THE UNINCORPORATED TERRITORY OF THE COUNTY OF ORANGE, STATE OF CALIFORNIA.

THOMAS EARL PROPST, P.L.S. 6098

FUSCOE ENGINEERING



FEBRUARY 2000

EASEMENT LOCATIONS

EASEMENT NOTES:

- (A) DENOTES EASEMENTS TO THE SANTA MARGARITA WATER DISTRICT FOR SEWER AND WATER PURPOSES AS DEDICATED HEREON, OVER LOTS "A" THROUGH "M" IN THEIR ENTIRETY AND AS ADDITIONALLY DELINEATED HEREON.
- (B) DENOTES EASEMENTS TO THE COUNTY OF ORANGE FOR STORM DRAIN PURPOSES AS DEDICATED HEREON, OVER LOT "C" AND "J" IN THEIR ENTIRETY AND AS ADDITIONALLY DELINEATED HEREON.
- (C) DENOTES EASEMENTS TO THE COUNTY OF ORANGE FOR EMERGENCY VEHICULAR ACCESS AS DEDICATED HEREON, OVER LOTS "A" THROUGH "M" IN THEIR ENTIRETY AND AS ADDITIONALLY DELINEATED HEREON.
- (D) DENOTES THAT CERTAIN ACCESS EASEMENT FOR LOT 12 PER TRACT NO. 15827, M.B. 797/32-39.

CURVE#	DELTA	RADIUS	LENGTH
C1	73°54'53"	39.50	50.96
C2	17°39'02"	34.50	10.63

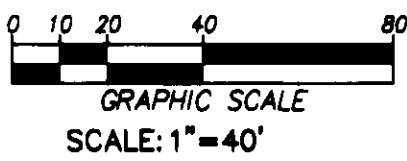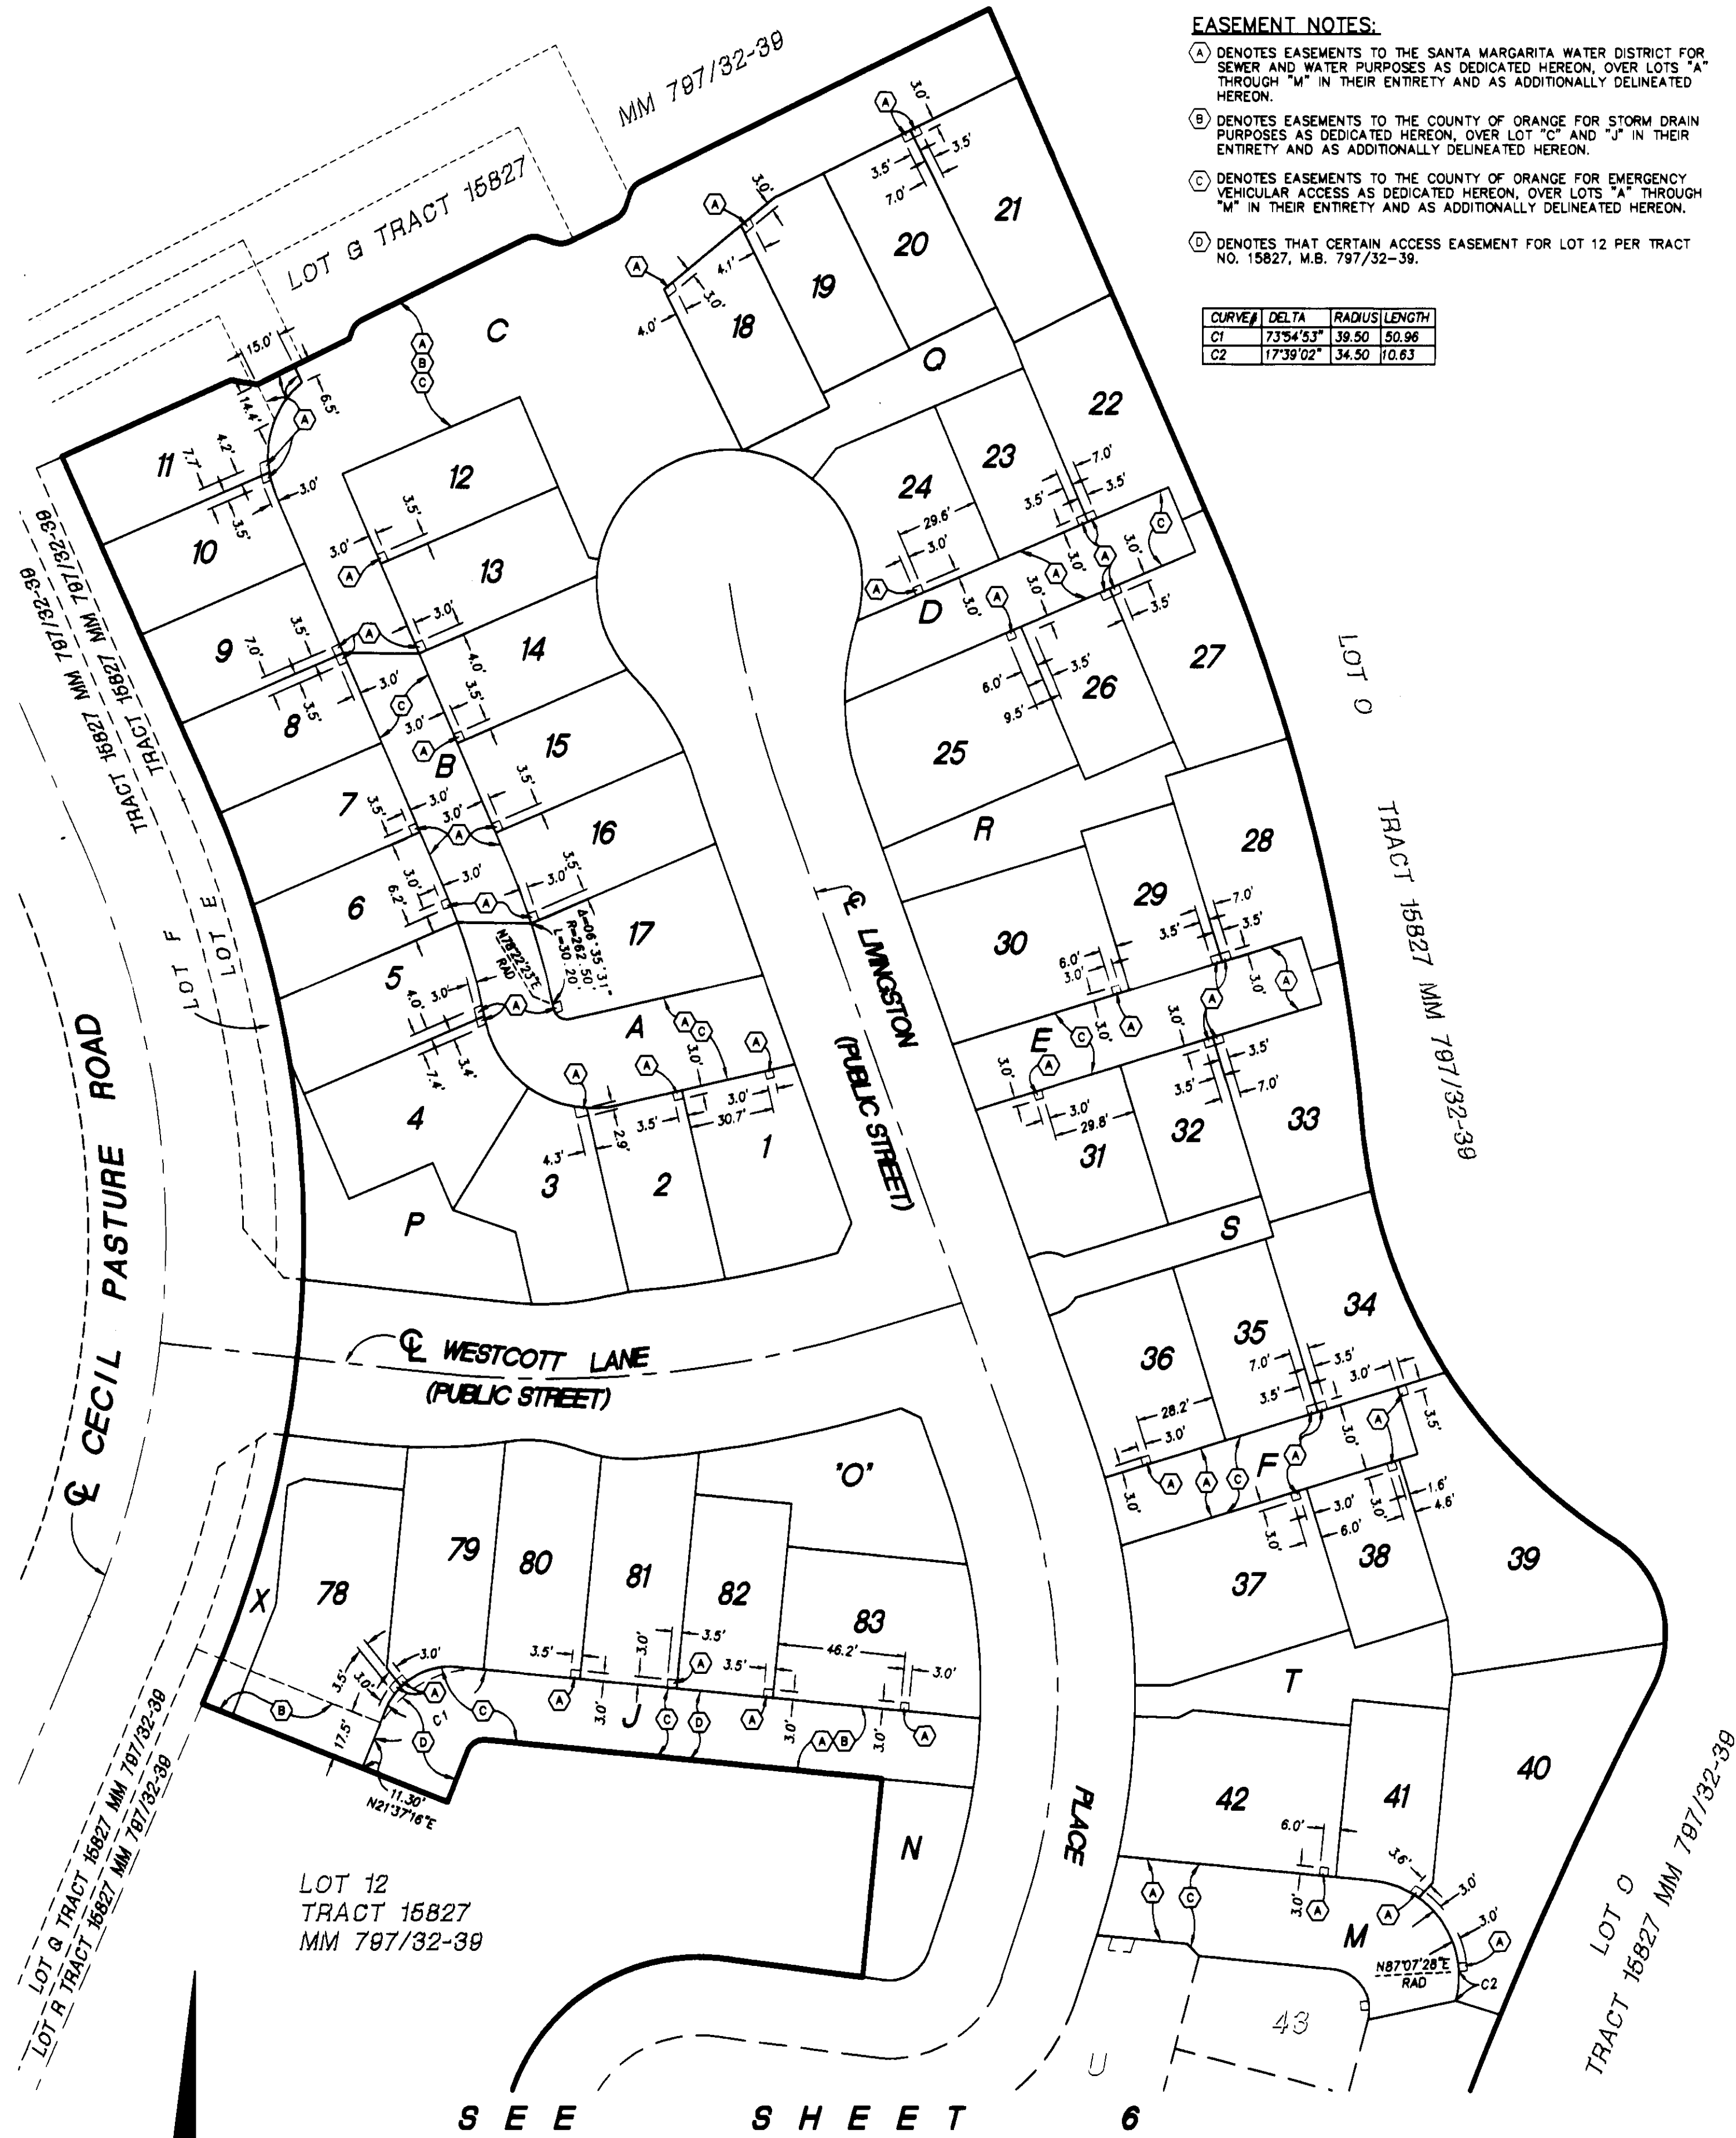

SEE SHEET 2 FOR BASIS OF BEARINGS, DATUM STATEMENT, MONUMENT NOTES, NOTES, CONTROL SCHEME AND VICINITY AND INDEX MAP.
SEE SHEET 3 FOR BOUNDARY DATA.

SHEET 6 OF 6 SHEETS
9.937 ACRES
83 NUMBERED LOTS AND
LETTERED LOTS "A" THROUGH "Y"
DATE OF SURVEY: FEBRUARY 2000
(A PORTION OF VESTING
TENTATIVE TRACT No. 15914)

TRACT NO. 15915

IN THE UNINCORPORATED TERRITORY OF THE COUNTY OF ORANGE, STATE OF CALIFORNIA.

THOMAS EARL PROPST, P.L.S. 6098




FUSCOE ENGINEERING

FEBRUARY 2000

EASEMENT NOTES:

- (A) DENOTES EASEMENTS TO THE SANTA MARGARITA WATER DISTRICT FOR SEWER AND WATER PURPOSES AS DEDICATED HEREON, OVER LOTS "A" THROUGH "M" IN THEIR ENTIRETY AND AS ADDITIONALLY DELINEATED HEREON.
- (C) DENOTES EASEMENTS TO THE COUNTY OF ORANGE FOR EMERGENCY VEHICULAR ACCESS AS DEDICATED HEREON, OVER LOTS "A" THROUGH "M" IN THEIR ENTIRETY AND AS ADDITIONALLY DELINEATED HEREON.

EASEMENT LOCATIONS

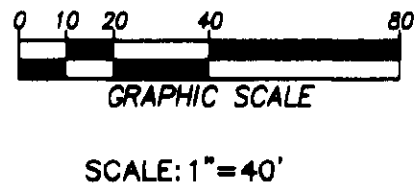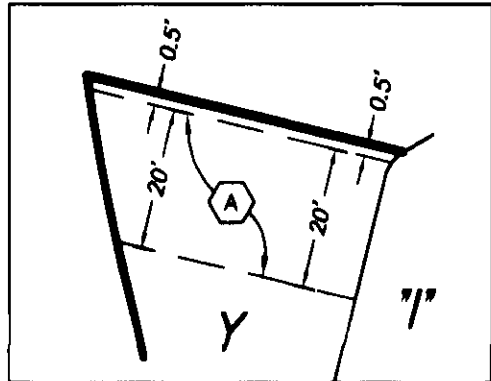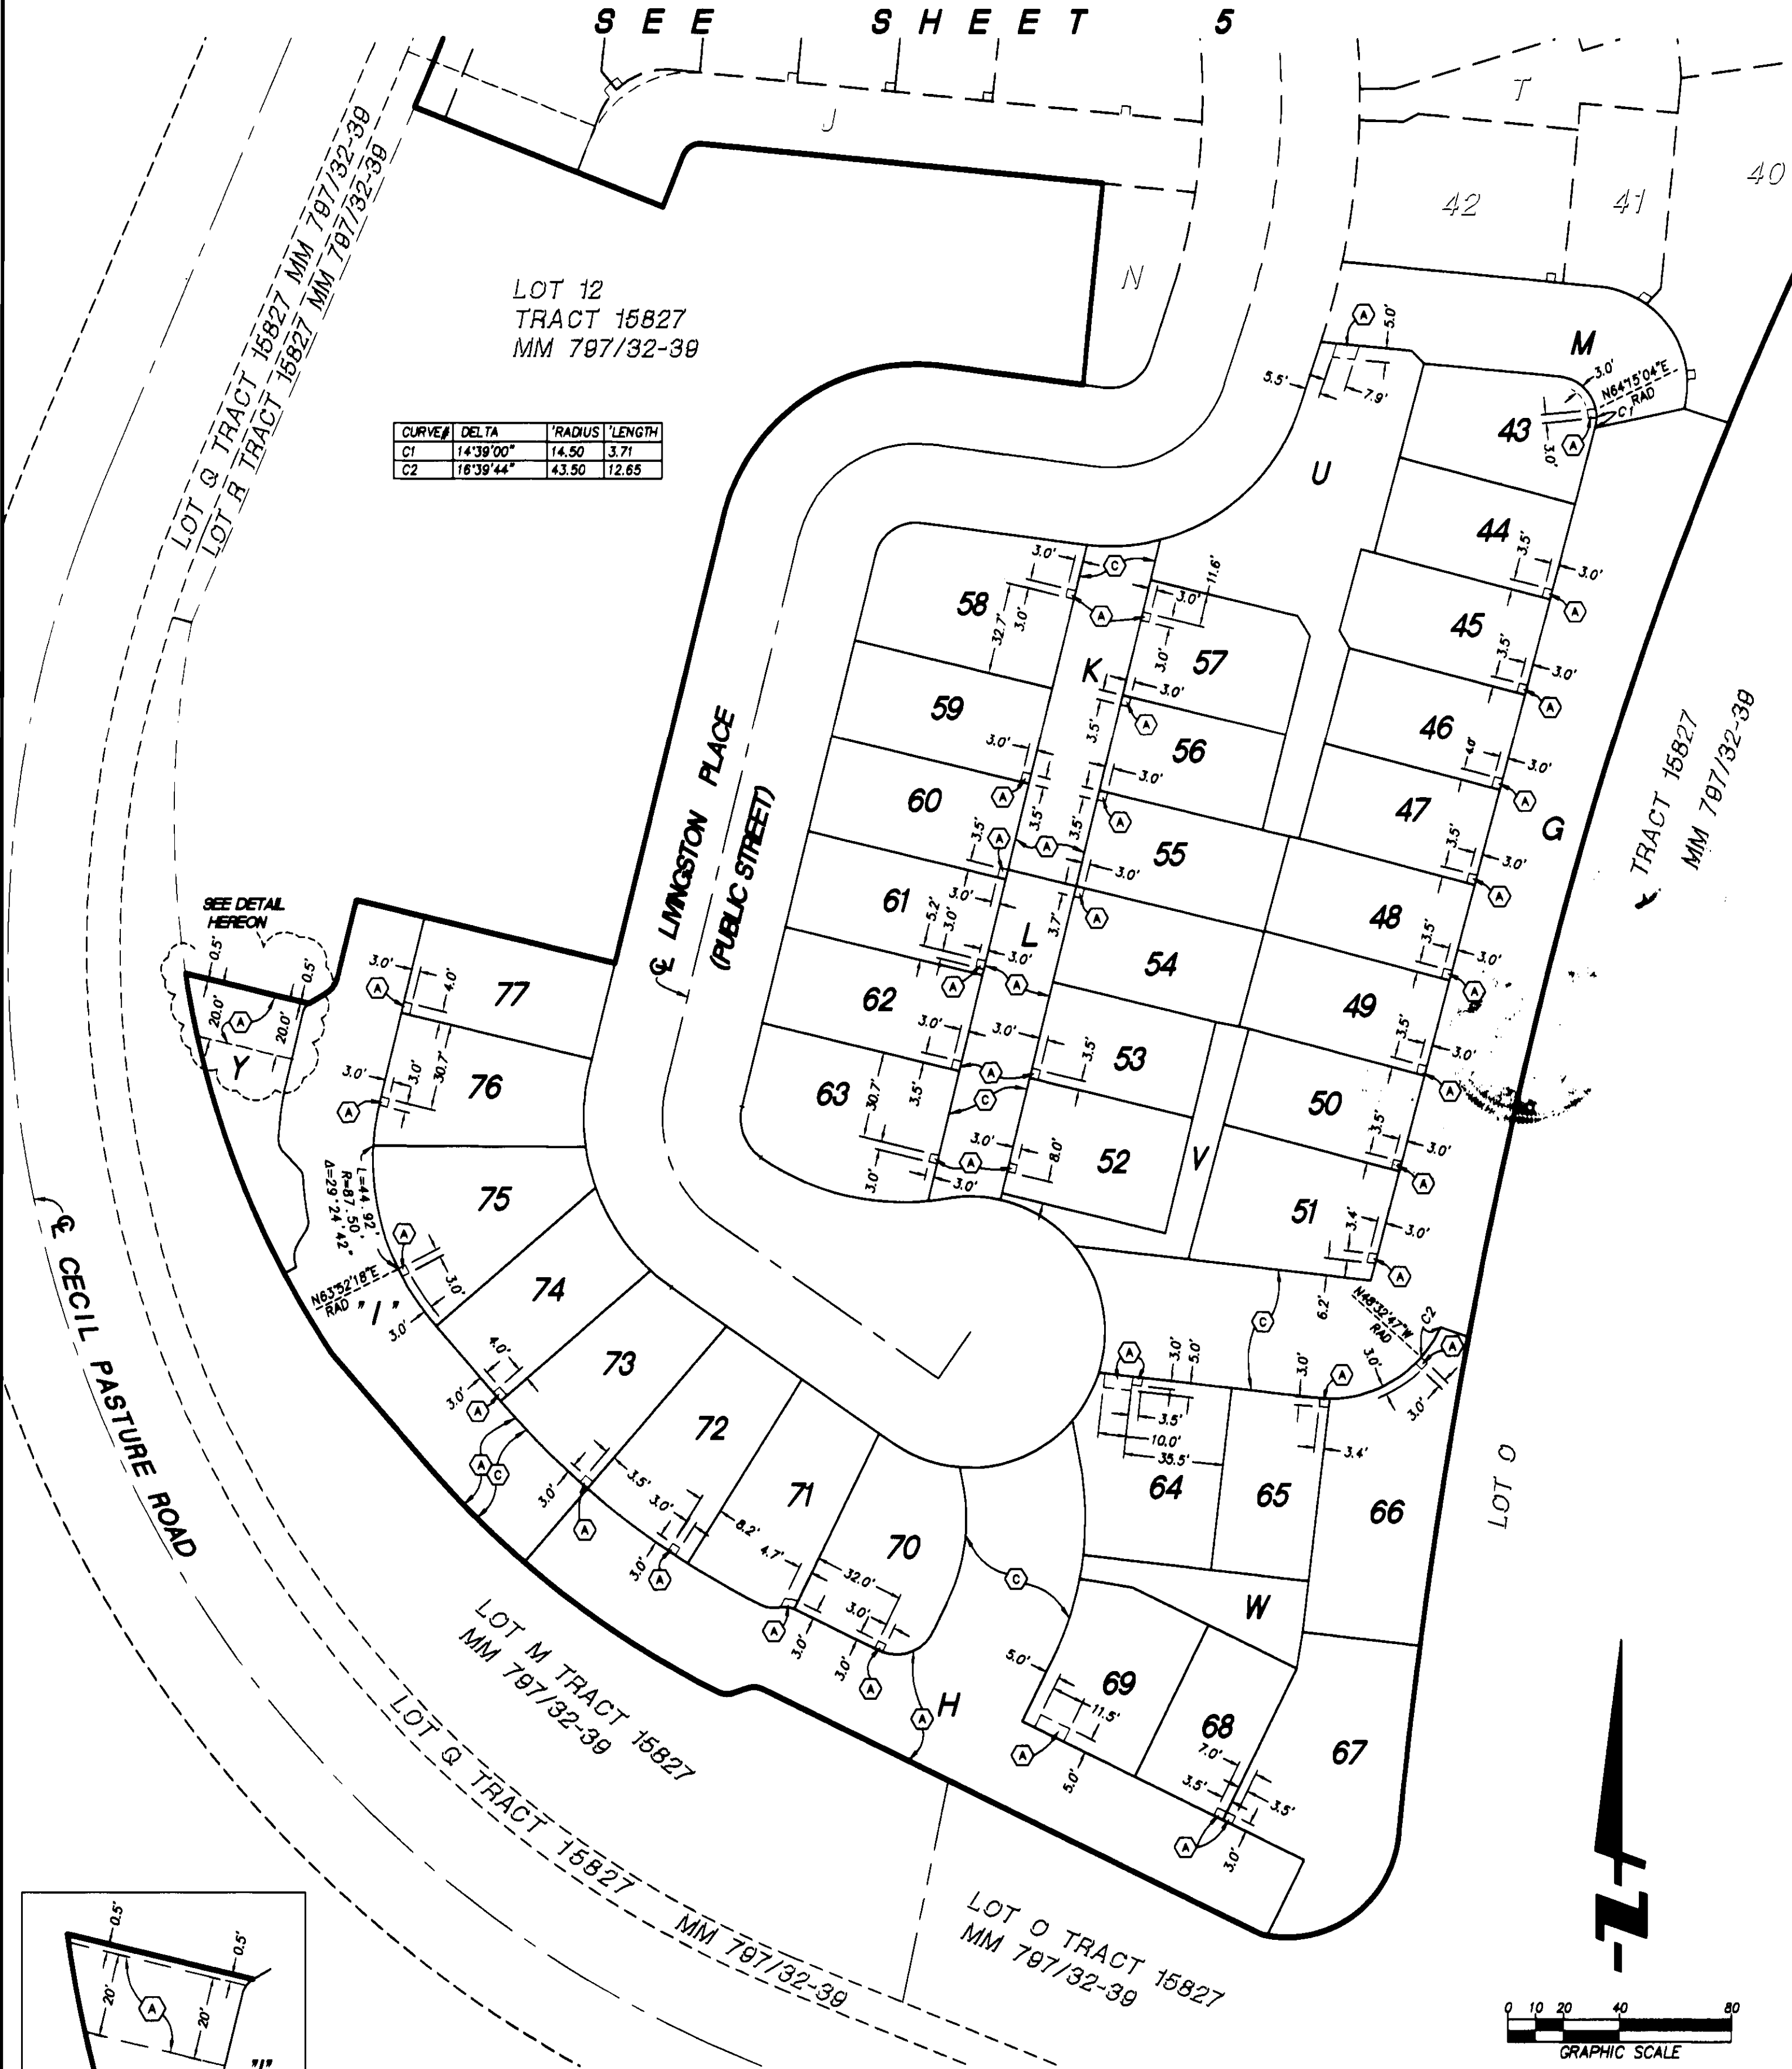

SEE SHEET 2 FOR BASIS OF BEARINGS, DATUM STATEMENT, MONUMENT NOTES, NOTES, CONTROL SCHEME AND VICINITY AND INDEX MAP.
SEE SHEET 4 FOR BOUNDARY DATA.