

842 8

SHEET 1 OF 13 SHEETS
87 NUMBERED LOTS
33 LETTERED LOTS
78.285 ACRES
ALL OF VESTING
T.T.M. 15985
DATE OF SURVEY:
JANUARY, 1999

TRACT MAP NO. 15985

IN THE UNINCORPORATED TERRITORY OF THE COUNTY OF ORANGE,
STATE OF CALIFORNIA

BEING A SUBDIVISION OF A PORTION OF PARCEL 1 OF LOT LINE ADJUSTMENT NO.
LL 96-026, IN THE UNINCORPORATED TERRITORY OF THE COUNTY OF ORANGE,
STATE OF CALIFORNIA, AS SHOWN ON EXHIBIT "B" ATTACHED TO THAT CERTAIN
DOCUMENT RECORDED NOVEMBER 21, 1996 AS INSTRUMENT NO. 19960587414 OF
OFFICIAL RECORDS, IN THE OFFICE OF THE COUNTY RECORDER OF SAID COUNTY.

HALL & FOREMAN, INC.

STEVEN C. SHAMBECK, P.L.S. 6217
MAY, 2002

ACCEPTED AND FILED AT THE
REQUEST OF

FIRST AMERICAN TITLE INSURANCE COMPANY

DATE APRIL 4, 2003

TIME 08:13 AM FEE \$ 81.00

INSTRUMENT # 2003000372580

BOOK 842 PAGE 8-20 m/m

TOM DALY
COUNTY CLERK-RECORDER

By Kame Spt
DEPUTY

OWNERSHIP STATEMENT

WE, THE UNDERSIGNED, BEING ALL PARTIES HAVING ANY RECORD TITLE INTEREST
IN THE LAND COVERED BY THIS MAP, DO HEREBY CONSENT TO THE PREPARATION
AND RECORDATION OF SAID MAP, AS SHOWN WITHIN THE DISTINCTIVE BORDER
LINE.

WE HEREBY DEDICATE TO THE PUBLIC FOR STREET PURPOSES: ANTONIO PARKWAY

WE ALSO HEREBY DEDICATE TO THE COUNTY OF ORANGE:

1. THE EASEMENT FOR SCENIC PRESERVATION PURPOSES AS SHOWN ON SAID MAP
FOR THE PURPOSES AND SUBJECT TO THE SAME CONDITIONS AND LIMITATIONS
AS SHOWN IN THAT CERTAIN EASEMENT RECORDED SEPTEMBER 19, 1991 AS INSTRUMENT
NO. 91-511820 OF OFFICIAL RECORDS.
2. THE EASEMENT FOR FIRE PROTECTION ACCESS PURPOSES AS SHOWN ON SAID MAP.
3. THE EASEMENT FOR EMERGENCY ACCESS PURPOSES OVER ALL OF LOTS BB, BC, BD, BE,
BF, BG, BH, BJ, BK, BL, BM, AND BN AS SHOWN ON SAID MAP.
4. THE EASEMENT FOR TRAFFIC SIGNAL MAINTENANCE
PURPOSES AS SHOWN ON SAID MAP.

WE ALSO HEREBY RELEASE AND RELINQUISH TO THE COUNTY OF ORANGE ALL VEHICULAR
ACCESS RIGHTS TO ANTONIO PARKWAY EXCEPT AT APPROVED ACCESS LOCATIONS.

WE ALSO HEREBY DEDICATE TO THE SANTA MARGARITA WATER DISTRICT THE EASEMENTS FOR
WATER, RECYCLED WATER, SEWER, DRAINAGE, AND ACCESS PURPOSES OVER THOSE EASEMENT
AREAS AS SHOWN ON SAID MAP WHICH EASEMENTS SHALL BE SUBJECT TO THE SAME
CONDITIONS AS ARE SHOWN IN THAT CERTAIN GRANT OF EASEMENT TO SANTA MARGARITA
WATER DISTRICT RECORDED SEPTEMBER 18, 2002 AS INSTRUMENT NO. 20020799401, OF
OFFICIAL RECORDS, COUNTY OF ORANGE.

DMB LADERA, L.L.C., A DELAWARE LIMITED LIABILITY COMPANY

BY: RANCHO MISSION VIEJO, L.L.C. A DELAWARE LIMITED LIABILITY COMPANY,
AS AGENT AND/OR MANAGER.

BY: [Signature]
PRINT NAME: DONALD T. STAHLIN
PRINT TITLE: DIRECTOR

BY: [Signature]
PRINT NAME: Stephen C. Schrank
PRINT TITLE: Exec VP-Development

NOTARY ACKNOWLEDGEMENT

STATE OF California
COUNTY OF Orange)SS

ON September 20, 2002 BEFORE ME, Tina Baker

Notary Public
PERSONALLY APPEARED Donald T. Stahlin and Stephen C. Schrank
PERSONALLY KNOWN TO ME (OR PROVED TO ME ON THE BASIS OF SATISFACTORY
EVIDENCE) TO BE THE PERSON(S) WHOSE NAME(S) IS/ARE SUBSCRIBED TO THE
WITHIN INSTRUMENT AND ACKNOWLEDGED TO ME THAT HE/SHE/THEY EXECUTED
THE SAME IN HIS/HER/THEIR AUTHORIZED CAPACITY(IES), AND THAT BY HIS/
HER/THEIR SIGNATURE(S) ON THE INSTRUMENT THE PERSON(S), OR THE ENTITY UPON
BEHALF OF WHICH THE PERSON(S) ACTED, EXECUTED THE INSTRUMENT.

WITNESS MY HAND:

[Signature]
NOTARY PUBLIC IN AND FOR SAID STATE

Tina T. Baker
PRINT NAME

MY PRINCIPAL PLACE OF BUSINESS IS IN Orange COUNTY
MY COMMISSION EXPIRES 8-29-04

CERTIFICATE OF ACCEPTANCE

THE UNDERSIGNED, BEING THE DULY APPOINTED AGENT OF THE SANTA MARGARITA
WATER DISTRICT, A PUBLIC CORPORATION OF ORANGE COUNTY, CALIFORNIA, PURSUANT
TO ITS RESOLUTION NO. 88-10-02, DOES HEREBY ACCEPT ON BEHALF OF SAID
DISTRICT THE EASEMENTS FOR, WATER, RECYCLED WATER, SEWER, DRAINAGE AND
ACCESS PURPOSES, AS DEDICATED AND AS SHOWN ON THIS TRACT MAP, BY AND
BETWEEN THE SANTA MARGARITA WATER DISTRICT AND DMB LADERA, L.L.C.,
AND DOES HEREBY CERTIFY THAT THE GRANTEE CONSENTS TO THE RECORDATION
OF SAID TRACT.

[Signature]
DANIEL R. FERONS, CHIEF ENGINEER
SANTA MARGARITA WATER DISTRICT


SEE SHEET 2 FOR ADDITIONAL NOTARY ACKNOWLEDGMENT AND SIGNATURE OMISSIONS

SURVEYOR'S STATEMENT

THIS MAP WAS PREPARED BY ME OR UNDER MY DIRECTION AND IS BASED UPON A
FIELD SURVEY IN CONFORMANCE WITH THE REQUIREMENTS OF THE SUBDIVISION MAP
ACT AND LOCAL ORDINANCE AT THE REQUEST OF DMB LADERA, LLC IN JANUARY,
1999. I HEREBY STATE THAT ALL MONUMENTS ARE OF THE CHARACTER AND
OCCUPY THE POSITIONS INDICATED, OR THAT THEY WILL BE SET IN SUCH
POSITIONS; AND THAT SAID MONUMENTS ARE SUFFICIENT TO ENABLE THE SURVEY
TO BE RETRACED. I HEREBY STATE THAT THIS FINAL MAP SUBSTANTIALLY
CONFORMS TO THE CONDITIONALLY APPROVED TENTATIVE MAP.

[Signature]
STEVEN C. SHAMBECK, P.L.S. 6217
LICENSE EXPIRES: 3/31/06

DATE 9/20/2002

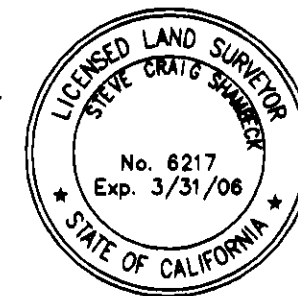

COUNTY SURVEYOR'S STATEMENT

I HEREBY STATE THAT I HAVE EXAMINED THIS MAP AND HAVE FOUND IT TO BE
SUBSTANTIALLY IN CONFORMANCE WITH THE TENTATIVE MAP AS FILED WITH,
AMENDED AND APPROVED BY THE ORANGE COUNTY SUBDIVISION COMMITTEE; THAT
ALL PROVISIONS OF THE SUBDIVISION MAP ACT AND COUNTY SUBDIVISION
REGULATIONS HAVE BEEN COMPLIED WITH AND I AM SATISFIED SAID MAP IS
TECHNICALLY CORRECT.

DATED THIS 7TH DAY OF MARCH, 2003.

[Signature]
JOHN CANAS, COUNTY SURVEYOR
L.S. 4408 EXPIRATION DATE: 9-30-05

BY: MICHAEL K. SULLIVAN, DEPUTY
L.S. 6254 EXPIRES 6/30/06



CLERK OF THE BOARD OF SUPERVISOR'S CERTIFICATE

STATE OF CALIFORNIA) SS
COUNTY OF ORANGE)

I HEREBY CERTIFY THAT THIS MAP WAS PRESENTED FOR APPROVAL TO THE
BOARD OF SUPERVISORS OF ORANGE COUNTY AT A REGULAR MEETING THEREOF
HELD ON THE 1st DAY OF April, 2003 AND THAT
THEREUPON SAID BOARD DID, BY AN ORDER DULY PASSED AND ENTERED,
APPROVE SAID MAP AND DID ACCEPT ON BEHALF OF THE PUBLIC, SUBJECT TO
IMPROVEMENTS; THE DEDICATION OF: ANTONIO PARKWAY

AND DID ALSO ACCEPT ON BEHALF OF THE COUNTY OF ORANGE:

1. THE EASEMENT FOR SCENIC PRESERVATION PURPOSES AS DEDICATED.
2. THE EASEMENT FOR FIRE PROTECTION ACCESS PURPOSES AS DEDICATED.
3. THE EASEMENT FOR EMERGENCY ACCESS PURPOSES OVER ALL OF LOTS BB,
BC, BD, BE, BF, BG, BH, BJ, BK, BL, BM, AND BN AS DEDICATED.
4. THE VEHICULAR ACCESS RIGHTS TO ANTONIO PARKWAY AS RELEASED AND
RELINQUISHED.
5. THE EASEMENT FOR TRAFFIC SIGNAL MAINTENANCE
PURPOSES AS DEDICATED.

AND DID ALSO APPROVE SUBJECT MAP PURSUANT TO THE PROVISIONS OF SECTION
66436(a)(3)(A) OF THE SUBDIVISION MAP ACT.

DATED THIS 1st DAY OF April, 2003

[Signature]
DARLENE J. BLOOM
CLERK OF THE BOARD OF SUPERVISORS



COUNTY TREASURER-TAX COLLECTOR'S CERTIFICATE

STATE OF CALIFORNIA) SS
COUNTY OF ORANGE)

I HEREBY CERTIFY THAT ACCORDING TO THE RECORDS OF MY
OFFICE THERE ARE NO LIENS AGAINST THE LAND COVERED BY THIS
MAP OR ANY PART THEREOF FOR UNPAID STATE, COUNTY, MUNICIPAL
OR LOCAL TAXES OR SPECIAL ASSESSMENTS COLLECTED AS TAXES,
EXCEPT TAXES OR SPECIAL ASSESSMENTS COLLECTED AS TAXES.

AND DO ALSO CERTIFY TO THE RECORDER OF THE COUNTY OF ORANGE
THAT THE PROVISIONS OF THE SUBDIVISION MAP ACT HAVE BEEN COMPLIED
WITH REGARDING DEPOSITS TO SECURE PAYMENT OF TAXES OR SPECIAL
ASSESSMENTS COLLECTED AS TAXES ON THE LAND COVERED BY THIS MAP.

DATED THIS 31 DAY OF January, 2003

JOHN M.W. MOORLACH
COUNTY TREASURER-TAX COLLECTOR

BY: [Signature]
DEPUTY TREASURER -
TAX COLLECTOR

842 8

SHEET 2 OF 13 SHEETS
87 NUMBERED LOTS
33 LETTERED LOTS
78.205 ACRES
ALL OF VESTING
T.T.M. 15985
DATE OF SURVEY:
JANUARY, 1999

TRACT MAP NO. 15985

IN THE UNINCORPORATED TERRITORY OF THE COUNTY OF ORANGE,
STATE OF CALIFORNIA

HALL & FOREMAN, INC.

STEVEN C. SHAMBECK, P.L.S. 6217
MAY, 2002

SANTA MARGARITA WATER DISTRICT

STATE OF CALIFORNIA)
COUNTY OF ORANGE)

ON THIS 20th DAY OF September 2002, BEFORE ME, Andrea M. Evans
A NOTARY PUBLIC IN AND FOR SAID STATE, PERSONALLY APPEARED DANIEL R.
FERONS PERSONALLY KNOWN TO ME OR PROVED TO ME ON THE BASIS OF SATISFACTORY
EVIDENCE TO BE THE PERSON WHOSE NAME IS SUBSCRIBED TO THE WITHIN INSTRUMENT
AND ACKNOWLEDGED TO ME THAT HE EXECUTED THE SAME IN HIS AUTHORIZED CAPACITY,
AND THAT BY HIS SIGNATURE ON THE INSTRUMENT THE PERSON OR THE ENTITY UPON
BEHALF OF WHICH THE PERSON ACTED, EXECUTED THE INSTRUMENT.

WITNESS MY HAND:

MY COMMISSION EXPIRES 4/8/04

Andrea M. Evans
NOTARY PUBLIC IN AND FOR SAID STATE

MY PRINCIPAL PLACE OF BUSINESS
IS IN Orange COUNTY

ANDREA M. EVANS
PRINT NAME

AUTOMATIC FIRE SPRINKLER NOTE:

ALL SINGLE FAMILY HOMES AND ALL MULTIFAMILY HOMES
SHALL BE PROTECTED WITH AUTOMATIC FIRE SPRINKLER
SYSTEMS.

SPECIAL FIRE PROTECTION NOTE:

PROPERTY IS IN A SPECIAL FIRE PROTECTION AREA AND
HAS RECIEVED A MODIFIED EXCLUSION FROM OCCA PER
EXCLUSION LETTER DATED AUGUST 24, 2001.

HIGH FIRE HAZARD AREA NOTE:

THE LOTS SHOWN ON THIS MAP ARE IN A HIGH FIRE HAZARD AREA DUE TO
WILD LAND EXPOSURE.

SIGNATURE OMISSIONS

PURSUANT TO THE PROVISIONS OF SECTION 66436 (a)(3)(A)(C) OF
THE SUBDIVISION MAP ACT, THE FOLLOWING SIGNATURES HAVE BEEN
OMITTED:

LADERA DEVELOPMENT COMPANY, L.L.C., HOLDER OF OIL, GAS, AND MINERAL
RIGHTS PER DEED RECORDED DECEMBER 10, 1996 AS INSTRUMENT NO.
19960624029 OF OFFICIAL RECORDS.

EASEMENT NOTES

- ☒ INDICATES STORM DRAIN EASEMENT RESERVED HEREON FOR THE
BENEFIT OF THE FUTURE HOMEOWNER'S ASSOCIATION.
- ☒ INDICATES WATER, RECYCLED WATER, SEWER AND ACCESS
EASEMENT DEDICATED TO SANTA MARGARITA WATER DISTRICT.
- ☒ INDICATES DRAINAGE EASEMENT DEDICATED TO SANTA MARGARITA
WATER DISTRICT.
- ☒ INDICATES SCENIC PRESERVATION EASEMENT AS DEDICATED TO THE
COUNTY OF ORANGE.
- ☒ INDICATES FIRE PROTECTION ACCESS EASEMENT AS DEDICATED TO
THE COUNTY OF ORANGE.
- ☒ INDICATES TRAFFIC SIGNAL MAINTENANCE EASEMENT
AS DEDICATED TO THE COUNTY OF ORANGE.

BASIS OF BEARINGS

THE BEARINGS SHOWN HEREON ARE BASED ON THE BEARING BETWEEN
O.C.S. HORIZONTAL CONTROL STATION GPS NO. 1417 AND STATION
GPS NO. 1448, BEING NORTH 10°48'13" EAST PER RECORDS ON FILE
IN THE OFFICE OF THE ORANGE COUNTY SURVEYOR.

DATUM STATEMENT

COORDINATES SHOWN ARE BASED ON THE CALIFORNIA COORDINATE
SYSTEM (CCS 83), ZONE VI, 1983 NAD (1991.35 EPOCH OCS GPS
ADJUSTMENT). ALL DISTANCES ARE GROUND DISTANCES UNLESS
OTHERWISE NOTED. TO OBTAIN GRID DISTANCE MULTIPLY GROUND
DISTANCE BY 0.999948295.

MONUMENT NOTES

- INDICATES FOUND MONUMENT AS NOTED.
- ☒ INDICATES FOUND 2 1/2" IRON PIPE W/2" OCS BRASS CAP STAMPED "GPS
1448 9-95" PER TRACT NO. 16203, M.M. 826/8-20 AND RECORD ON FILE
IN THE ORANGE COUNTY SURVEYORS OFFICE.
N2146790.819, E6142602.585
- ☒ INDICATES FOUND 2 1/2" IRON PIPE W/2" OCS BRASS CAP STAMPED "GPS
1417 9-95" PER TRACT NO. 16203, M.M. 826/8-20 AND RECORD ON FILE
IN THE ORANGE COUNTY SURVEYORS OFFICE.
N2141450.558, E6141583.535
- ☐ INDICATES 2" I.P. TAGGED L.S. 5557 OR SPIKE & WASHER STAMPED L.S.
5557 OR LEAD, TACK & TAG L.S. 5557 TO BE SET PER TRACT NO. 15987
M.M. 839/ 1-18, UNLESS OTHERWISE NOTED.
- ☒ INDICATES 1" I.P. TAGGED L.S. 5557 OR SPIKE & WASHER STAMPED L.S.
5557 OR LEAD, TACK & TAG L.S. 5557 TO BE SET PER TRACT NO. 15987
M.M. 839/ 1-18, UNLESS OTHERWISE NOTED.
- 2" I.P. TAGGED L.S. 6217 OR SPIKE & WASHER STAMPED L.S. 6217
OR LEAD, TACK & TAG L.S. 6217 TO BE SET AT ALL TRACT BOUNDARY
CORNERS WITHIN 90 DAYS AFTER ACCEPTANCE OF IMPROVEMENTS.
- 1" I.P. TAGGED L.S. 6217 OR SPIKE & WASHER STAMPED L.S. 6217 OR
LEAD, TACK & TAG L.S. 6217 TO BE SET AT LOT CORNERS WITHIN 90 DAYS
AFTER ACCEPTANCE OF IMPROVEMENTS.
- 1" I.P. TAGGED L.S. 6217 OR SPIKE & WASHER STAMPED L.S. 6217 OR
LEAD, TACK & TAG L.S. 6217 TO BE SET AT ALL CENTERLINE INTERSECTIONS,
E.C.'S AND B.C.'S WITHIN 90 DAYS AFTER ACCEPTANCE OF IMPROVEMENTS.

NOTES

LOTS BB, BC, BD, BE, BF, BG, BH, BJ, BK, BL, BM, AND BN ARE FOR PRIVATE
STREET PURPOSES AND ARE NOT SEPARATE BUILDING SITES.

LOTS A THROUGH T ARE FOR LANDSCAPE/OPEN SPACE PURPOSES AND
ARE NOT SEPARATE BUILDING SITES.

LOT BO IS FOR ANTONIO PARKWAY AS DEDICATED HEREON AND IS NOT A
SEPARATE BUILDING SITES.

() INDICATES MEASURED AND RECORD PER RECORD OF SURVEY 97-1086
R.S.B. 167/26-28.

[] INDICATES MEASURED AND RECORD PER TRACT NO. 15987 M.M. 839/ 1-18

LOT 87 IS FOR GUARD SHACK PURPOSES.

LOTS 81 THROUGH 86 ARE NOT RESIDENTIAL BUILDING SITES

SHEET 3 OF 13 SHEETS
87 NUMBERED LOTS
33 LETTERED LOTS
78.285 ACRES
ALL OF VESTING
T.T.M. 15985
DATE OF SURVEY:
JANUARY, 1999

TRACT MAP NO. 15985

IN THE UNINCORPORATED TERRITORY OF THE COUNTY OF ORANGE,
STATE OF CALIFORNIA

HALL & FOREMAN, INC.

STEVEN C. SHAMBECK, P.L.S. 6217

MAY, 2002

BOUNDARY AND INDEX SHEET


SEE SHEET 2 FOR BASIS OF
BEARINGS, DATUM STATEMENT,
MONUMENT NOTES, EASEMENT
NOTES AND NOTES

FD. OCS WELL MONUMENT WITH 2 1/2"
BRASS DISK STAMPED "ORANGE COUNTY
SURVEYOR" PER R.S. 95-1066, R.S.B.
154/8-18

TRACT NO. 15987
M.M. 839/1-18

LINE DATA		
LINE	BEARING	LENGTH
L1	N51°00'57"W	45.11
L2	N05°34'50"W	89.11
L3	N73°07'42"W	5.05
L4	N80°22'11"E	6.20
L5	N55°08'09"E	4.16
L6	N78°48'44"W	125.76
L7	N57°42'29"E	4.36
L8	N78°48'44"W	27.21
L9	N44°05'47"W	36.03
L10	N81°12'30"E	4.90
L11	N44°05'47"W	116.46
L12	N78°20'11"W	18.33
L13	N50°36'28"W	58.00 (RAD)
L14	N37°04'03"E	7.11
L15	N55°14'35"W	92.56
L16	N30°49'09"W	122.13
L17	N49°19'05"E	35.18
L18	N03°37'30"W	125.27
L19	N48°41'19"W	90.09
L20	N18°25'27"E	160.02
L21	N55°37'46"E	31.03
L22	N77°49'54"E	28.00 (RAD)
L23	N77°14'44"E	28.00 (RAD)
L24	N05°24'30"W	86.00 (RAD)
L25	N84°35'30"E	44.08
L26	N84°35'30"E	38.23
L27	N79°31'08"E	85.27
L28	N68°31'36"E	6.00 (RAD)
L29	N68°31'36"E	2.00 (RAD)

CURVE DATA				
CURVE	DELTA	RADIUS	LENGTH	TANGENT
C1	44°49'50"	58.00	45.36	23.92
C2	42°34'59"	145.00	107.77	56.51
C3	14°47'31"	250.00	64.54	32.45
C4	20°26'59"	150.00	53.54	27.06
C5	31°55'33"	145.00	80.80	41.48
C6	34°42'57"	91.00	55.14	28.44
C7	3°33'36"	604.00	37.53	18.77
C8	38°13'04"	80.00	40.02	20.79
C9	5°54'27"	640.00	65.99	33.02
C10	40°25'55"	185.00	130.55	68.13
C11	6°07'14"	200.00	21.36	10.69
C12	28°10'16"	60.00	27.41	13.95
C13	15°11'35"	260.00	68.94	34.68
C14	17°41'58"	220.00	67.96	34.25
C15	19°09'12"	578.00	193.22	97.52
C16	20°36'41"	500.00	179.87	90.92
C17	9°08'31"	659.00	105.15	52.69
C18	12°57'20"	492.00	111.25	55.86
C19	0°35'10"	550.00	5.63	2.81
C20	1°12'26"	504.00	10.62	5.31
C21	11°39'38"	248.00	50.47	25.32
C22	11°39'38"	285.00	58.00	29.10
C23	4°12'40"	749.00	55.05	27.54
C24	18°52'42"	230.00	75.78	38.24
C25	18°21'00"	285.00	91.28	46.03
C26	100°59'32"	75.00	132.20	90.97
C27	5°15'42"	2412.00	221.50	110.83
C28	7°27'07"	292.00	37.98	19.02
C29	99°14'48"	30.00	51.97	35.28
C30	98°08'20"	30.00	50.34	33.40

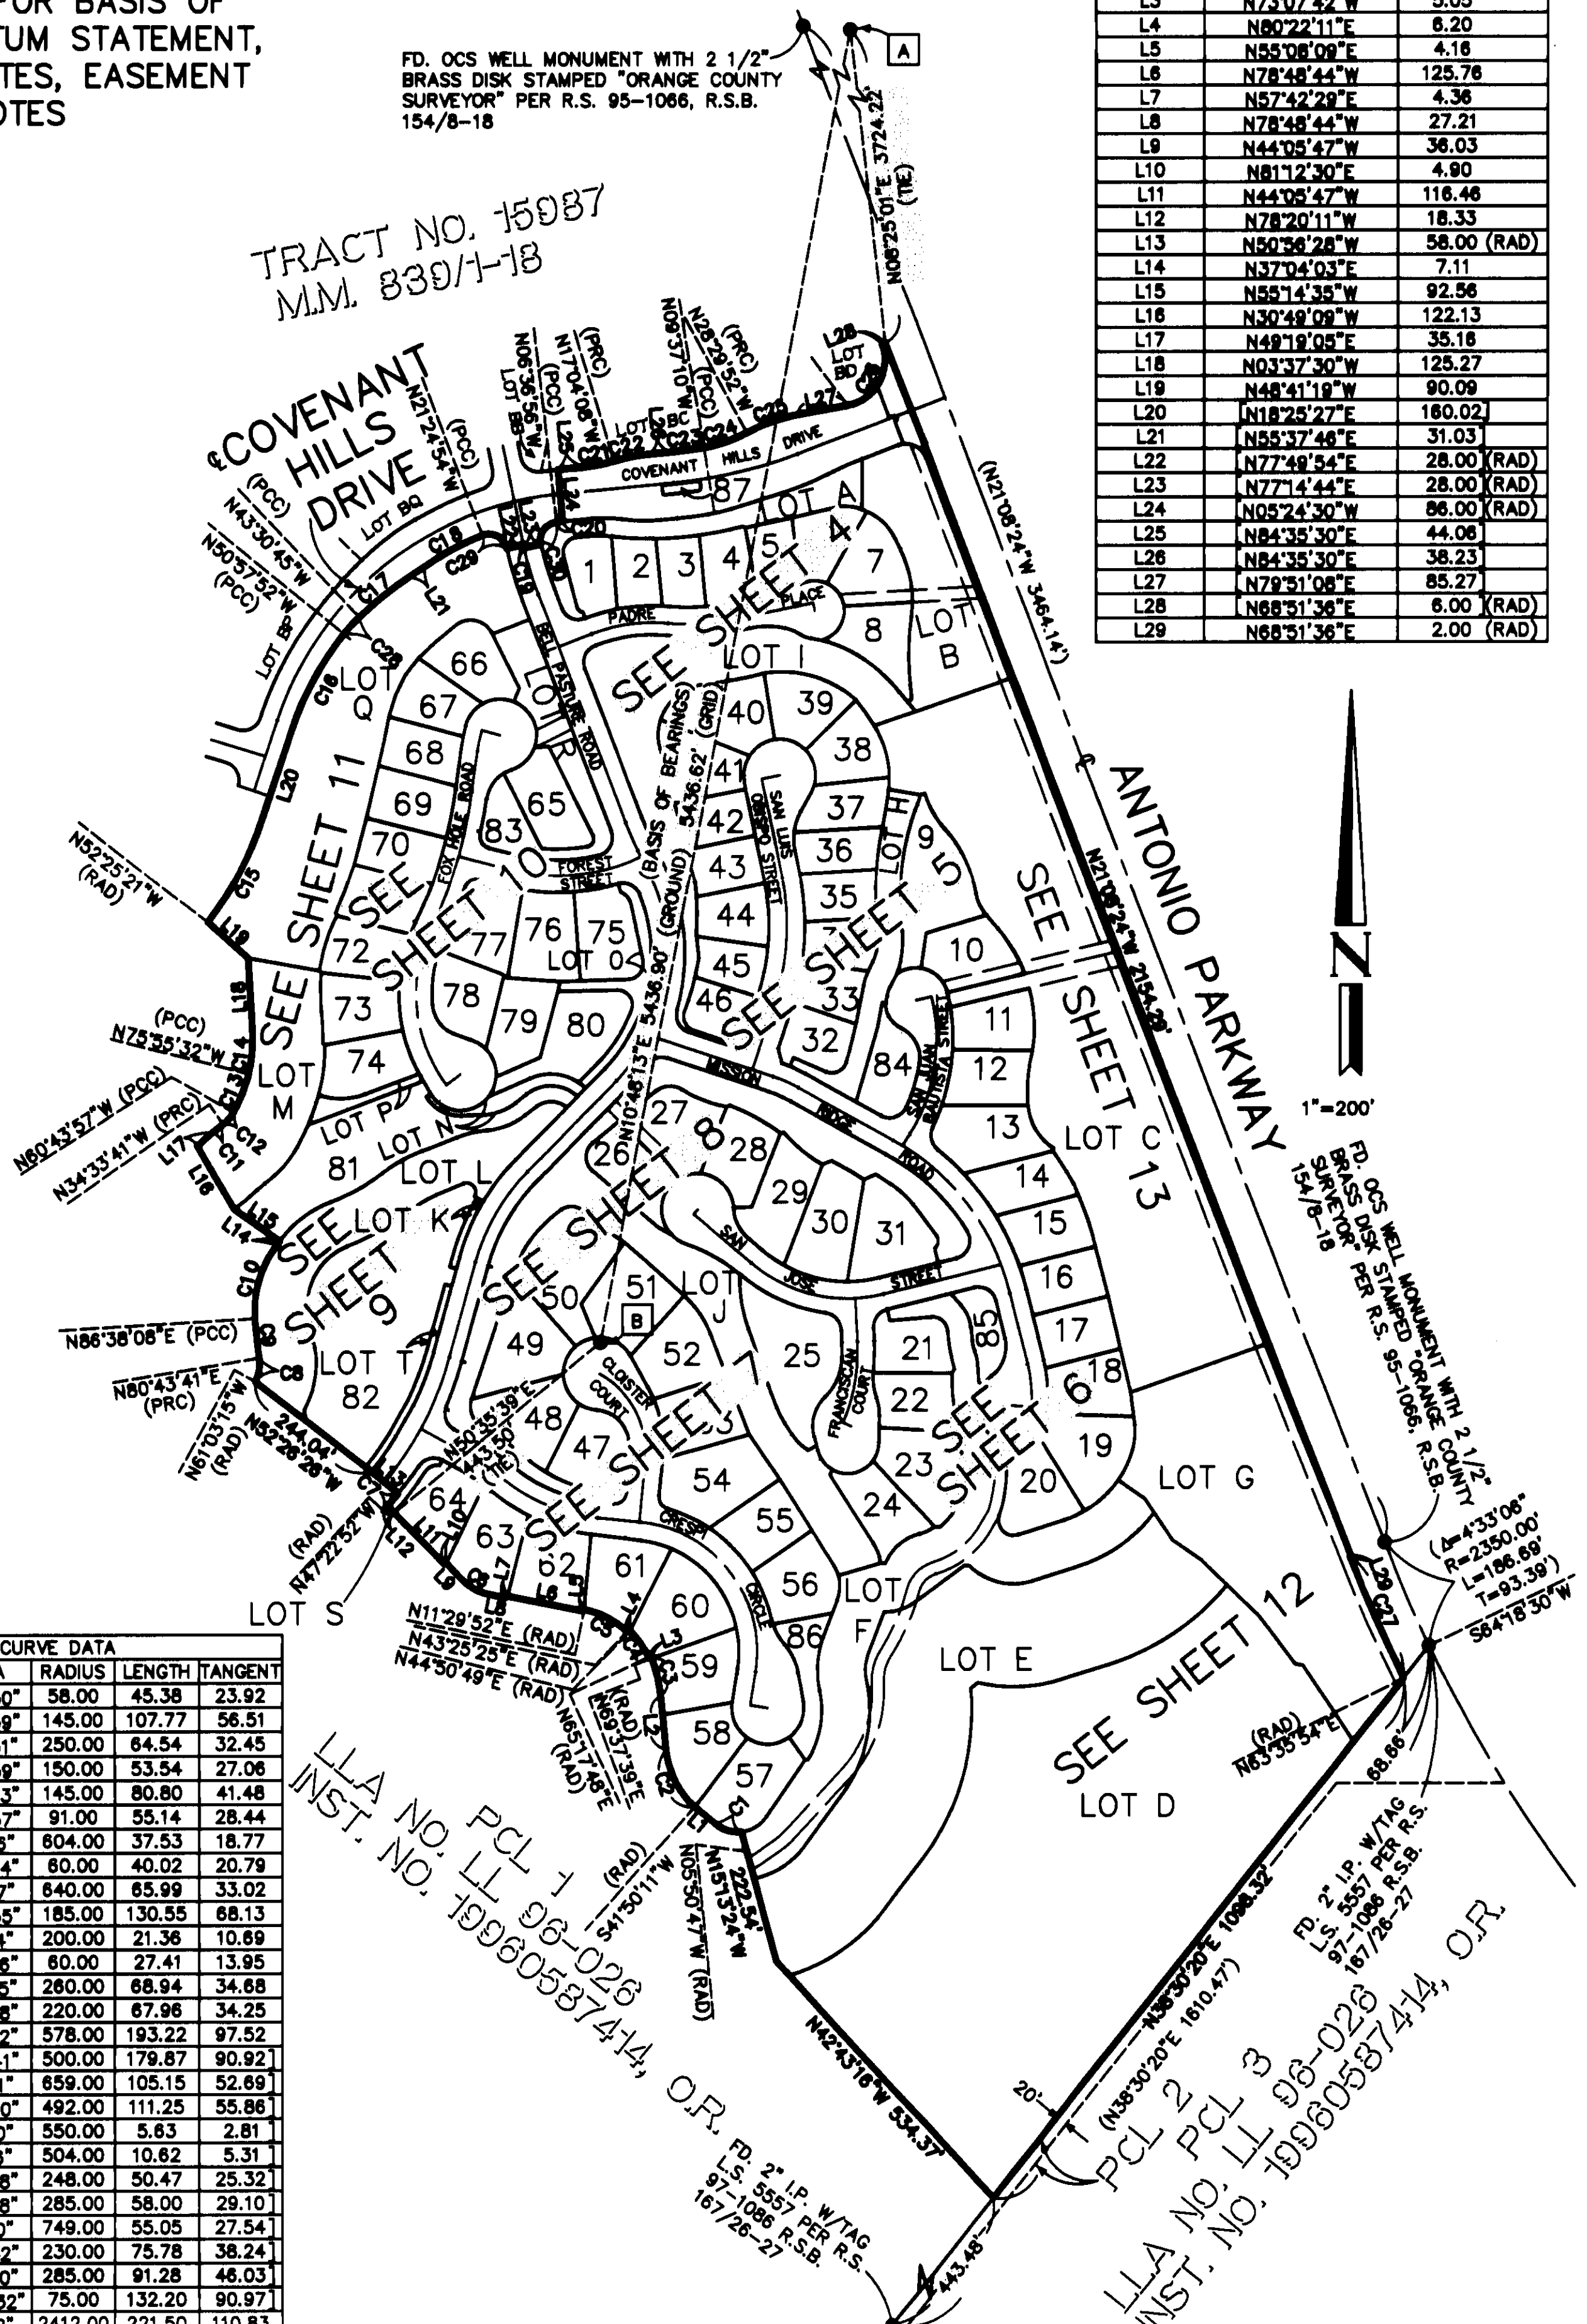

LLA NO. PCL 96-0263
INST. NO. 19960587414, O.R.

LLA NO. PCL 96-0263
INST. NO. 19960587414, O.R.

SHEET 4 OF 13 SHEETS
87 NUMBERED LOTS
33 LETTERED LOTS
78.285 ACRES
ALL OF VESTING
T.T.M. 15985
DATE OF SURVEY:
JANUARY, 1999

TRACT MAP NO. 15985

IN THE UNINCORPORATED TERRITORY OF THE COUNTY OF ORANGE,
STATE OF CALIFORNIA

HALL & FOREMAN, INC.


STEVEN C. SHAMBECK, P.L.S. 6217

MAY, 2002

CURVE DATA				
CURVE	DELTA	RADIUS	LENGTH	TANGENT
C1	100°59'32"	75.00	132.20	90.97
C2	54°59'15"	75.00	71.98	39.03
C3	46°00'17"	75.00	60.22	31.84
C4	1°50'14"	305.00	9.78	4.89
C5	168°35'47"	4.25	12.51	42.57
C6	89°27'43"	35.00	54.65	34.67
C7	74°47'56"	35.00	45.69	26.76
C8	14°39'47"	35.00	8.96	4.50
C9	89°38'42"	5.00	7.82	4.97
C10	2°44'53"	802.00	38.47	19.24
C11	90°00'00"	2.50	3.93	2.50
C12	2°45'02"	818.00	39.27	19.64
C13	90°21'09"	5.00	7.88	5.03
C14	9°22'32"	550.00	90.00	45.10
C15	8°18'47"	550.00	79.80	39.97
C16	0°35'10"	550.00	5.63	2.81

CURVE DATA				
CURVE	DELTA	RADIUS	LENGTH	TANGENT
C17	0°28'35"	550.00	4.57	2.29
C18	96°08'20"	30.00	50.34	33.40
C19	1°12'26"	504.00	10.62	5.31
C20	99°28'56"	25.00	43.39	29.50
C21	90°00'00"	30.00	47.12	30.00
C22	77°18'59"	10.00	13.49	8.00
C23	2°17'04"	308.00	12.28	6.14
C24	4°57'04"	205.00	17.71	8.86
C25	24°37'28"	48.00	19.77	10.04
C26	2°17'51"	72.00	26.78	13.54
C27	4°49'10"	600.00	50.47	25.25
C28	33°41'44"	4.25	2.50	1.29
C29	134°54'03"	4.25	10.01	10.24
C30	3°24'52"	859.00	51.19	25.60
C31	4°12'40"	800.00	58.80	29.41

LINE DATA		
LINE	BEARING	LENGTH
L1	N20°36'07"W	54.97
L2	N20°36'07"W	39.89
L3	N84°35'30"E	17.72
L4	N05°24'30"W	11.00
L5	N08°30'41"W	6.00
L6	N77°14'44"E	28.00 (RAD)
L7	N77°49'54"E	28.00 (RAD)
L8	N21°04'03"W	48.00
L9	N21°04'03"W	20.00
L10	N21°04'03"W	28.00
L11	N09°37'10"W	109.83
L12	N84°35'30"E	27.27

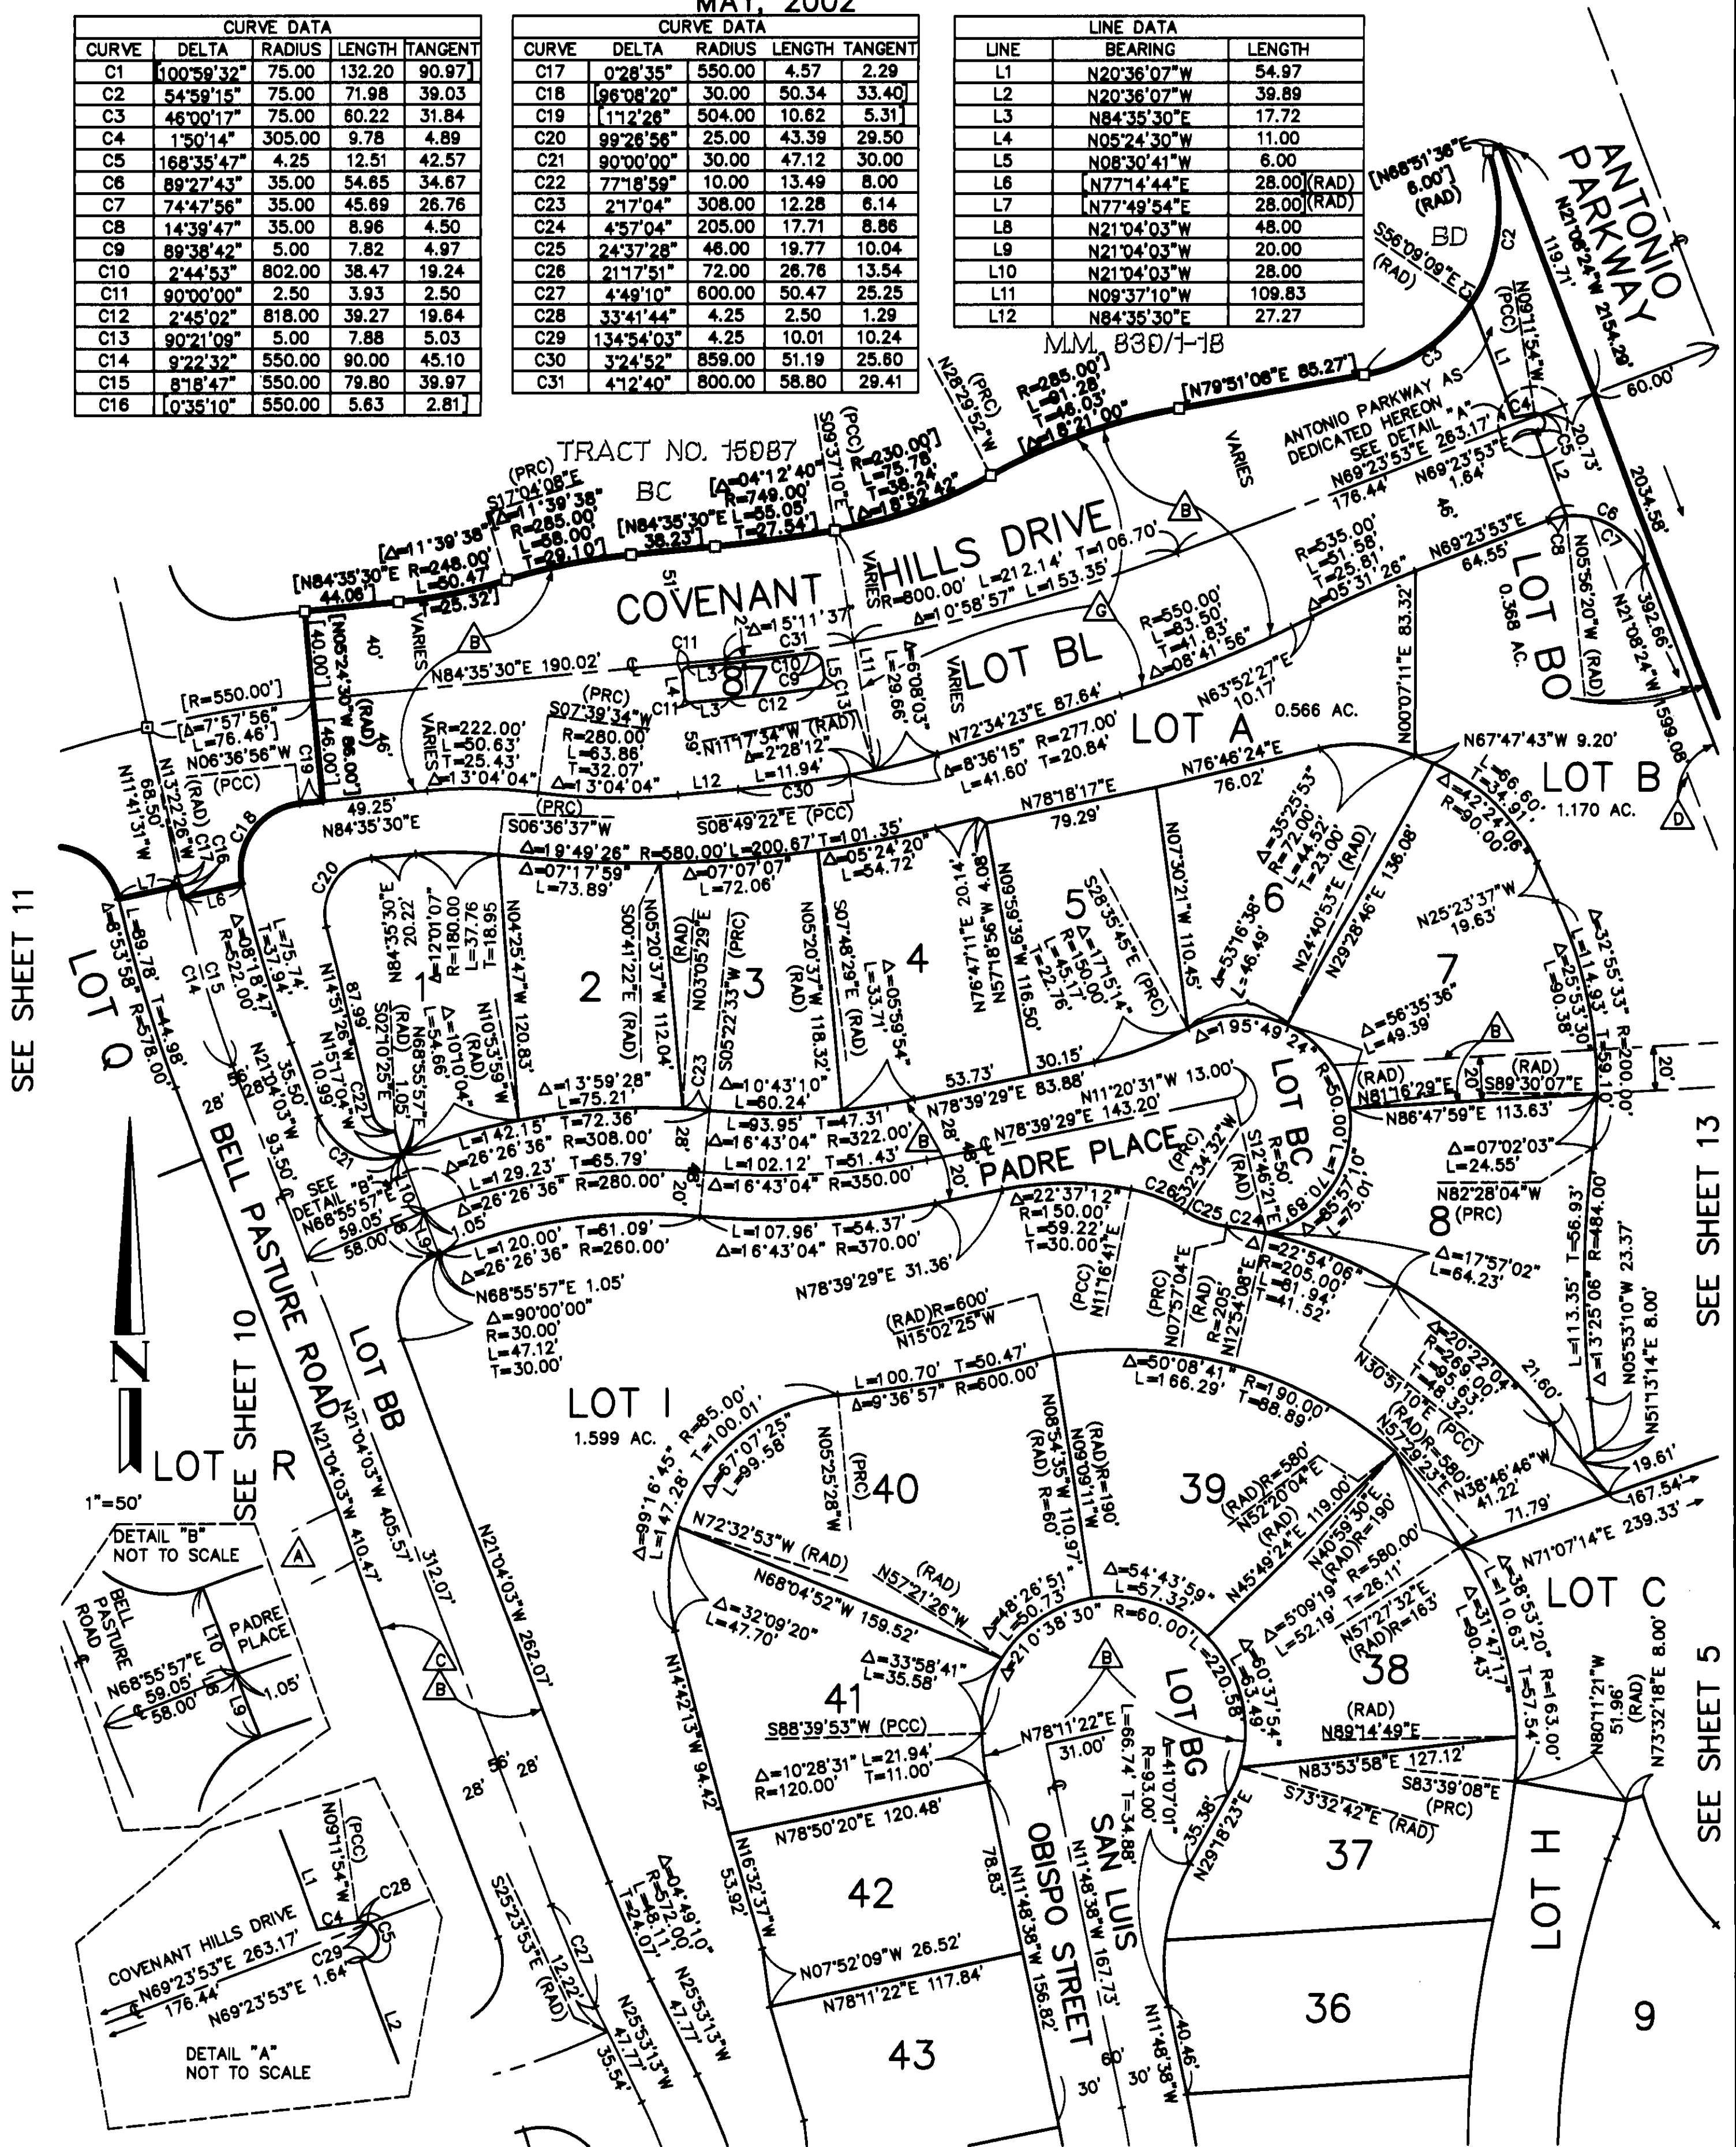

SEE SHEET 2 FOR BASIS OF BEARINGS,
DATUM STATEMENT, MONUMENT NOTES,
EASEMENT NOTES AND NOTES

SEE SHEET 5

SHEET 5 OF 13 SHEETS
87 NUMBERED LOTS
33 LETTERED LOTS
78.285 ACRES
ALL OF VESTING
T.T.M. 15985
DATE OF SURVEY:
JANUARY, 1999

TRACT MAP NO. 15985

IN THE UNINCORPORATED TERRITORY OF THE COUNTY OF ORANGE,
STATE OF CALIFORNIA

HALL & FOREMAN, INC.

STEVEN C. SHAMBECK, P.L.S. 6217


SEE SHEET 2 FOR BASIS OF BEARINGS,
DATUM STATEMENT, MONUMENT NOTES,
EASEMENT NOTES AND NOTES

MAY, 2002

SEE SHEET 4

LINE DATA		
LINE	BEARING	LENGTH
L1	N27°29'00"E	24.74
L2	N08°02'18"E	11.66
L3	N81°57'42"W	6.75 (RAD)
L4	N14°23'31"W	23.86
L5	N18°20'17"E	5.00
L6	N71°39'43"W	60.00
L7	N65°58'13"W	26.00 (RAD)
L8	N63°42'47"W	28.00 (RAD)
L9	N18°20'17"E	26.00

CURVE DATA				
CURVE	DELTA	RADIUS	LENGTH	TANGENT
C1	7°06'03"	163.00	20.20	10.11
C2	6°01'48"	600.00	63.15	31.60
C3	43°31'55"	54.00	41.03	21.56
C4	111°22'17"	54.00	104.97	79.12
C5	19°26'42"	48.00	16.29	8.22
C6	37°51'49"	33.00	21.81	11.32
C7	32°33'18"	52.00	29.55	15.18
C8	70°16'51"	56.00	68.69	39.42
C9	94°49'21"	30.00	49.65	32.64
C10	10°30'51"	250.00	45.88	23.00
C11	9°13'38"	276.00	44.45	22.27
C12	6°08'51"	276.00	29.61	14.82
C13	3°04'47"	276.00	14.84	7.42
C14	96°42'39"	25.00	42.20	28.11
C15	91°38'03"	25.00	39.97	25.71
C16	87°57'24"	30.00	46.05	28.95
C17	2°33'43"	400.00	17.89	8.94
C18	10°54'46"	250.00	47.62	23.88
C19	16°30'45"	60.00	17.29	8.71
C20	06°08'32"	100.00	10.72	5.37
C21	77°46'41"	30.00	40.72	24.20
C22	45°17'36"	300.00	237.16	125.16
C23	7°23'04"	300.00	38.66	19.36
C24	4°22'12"	328.00	25.02	12.51

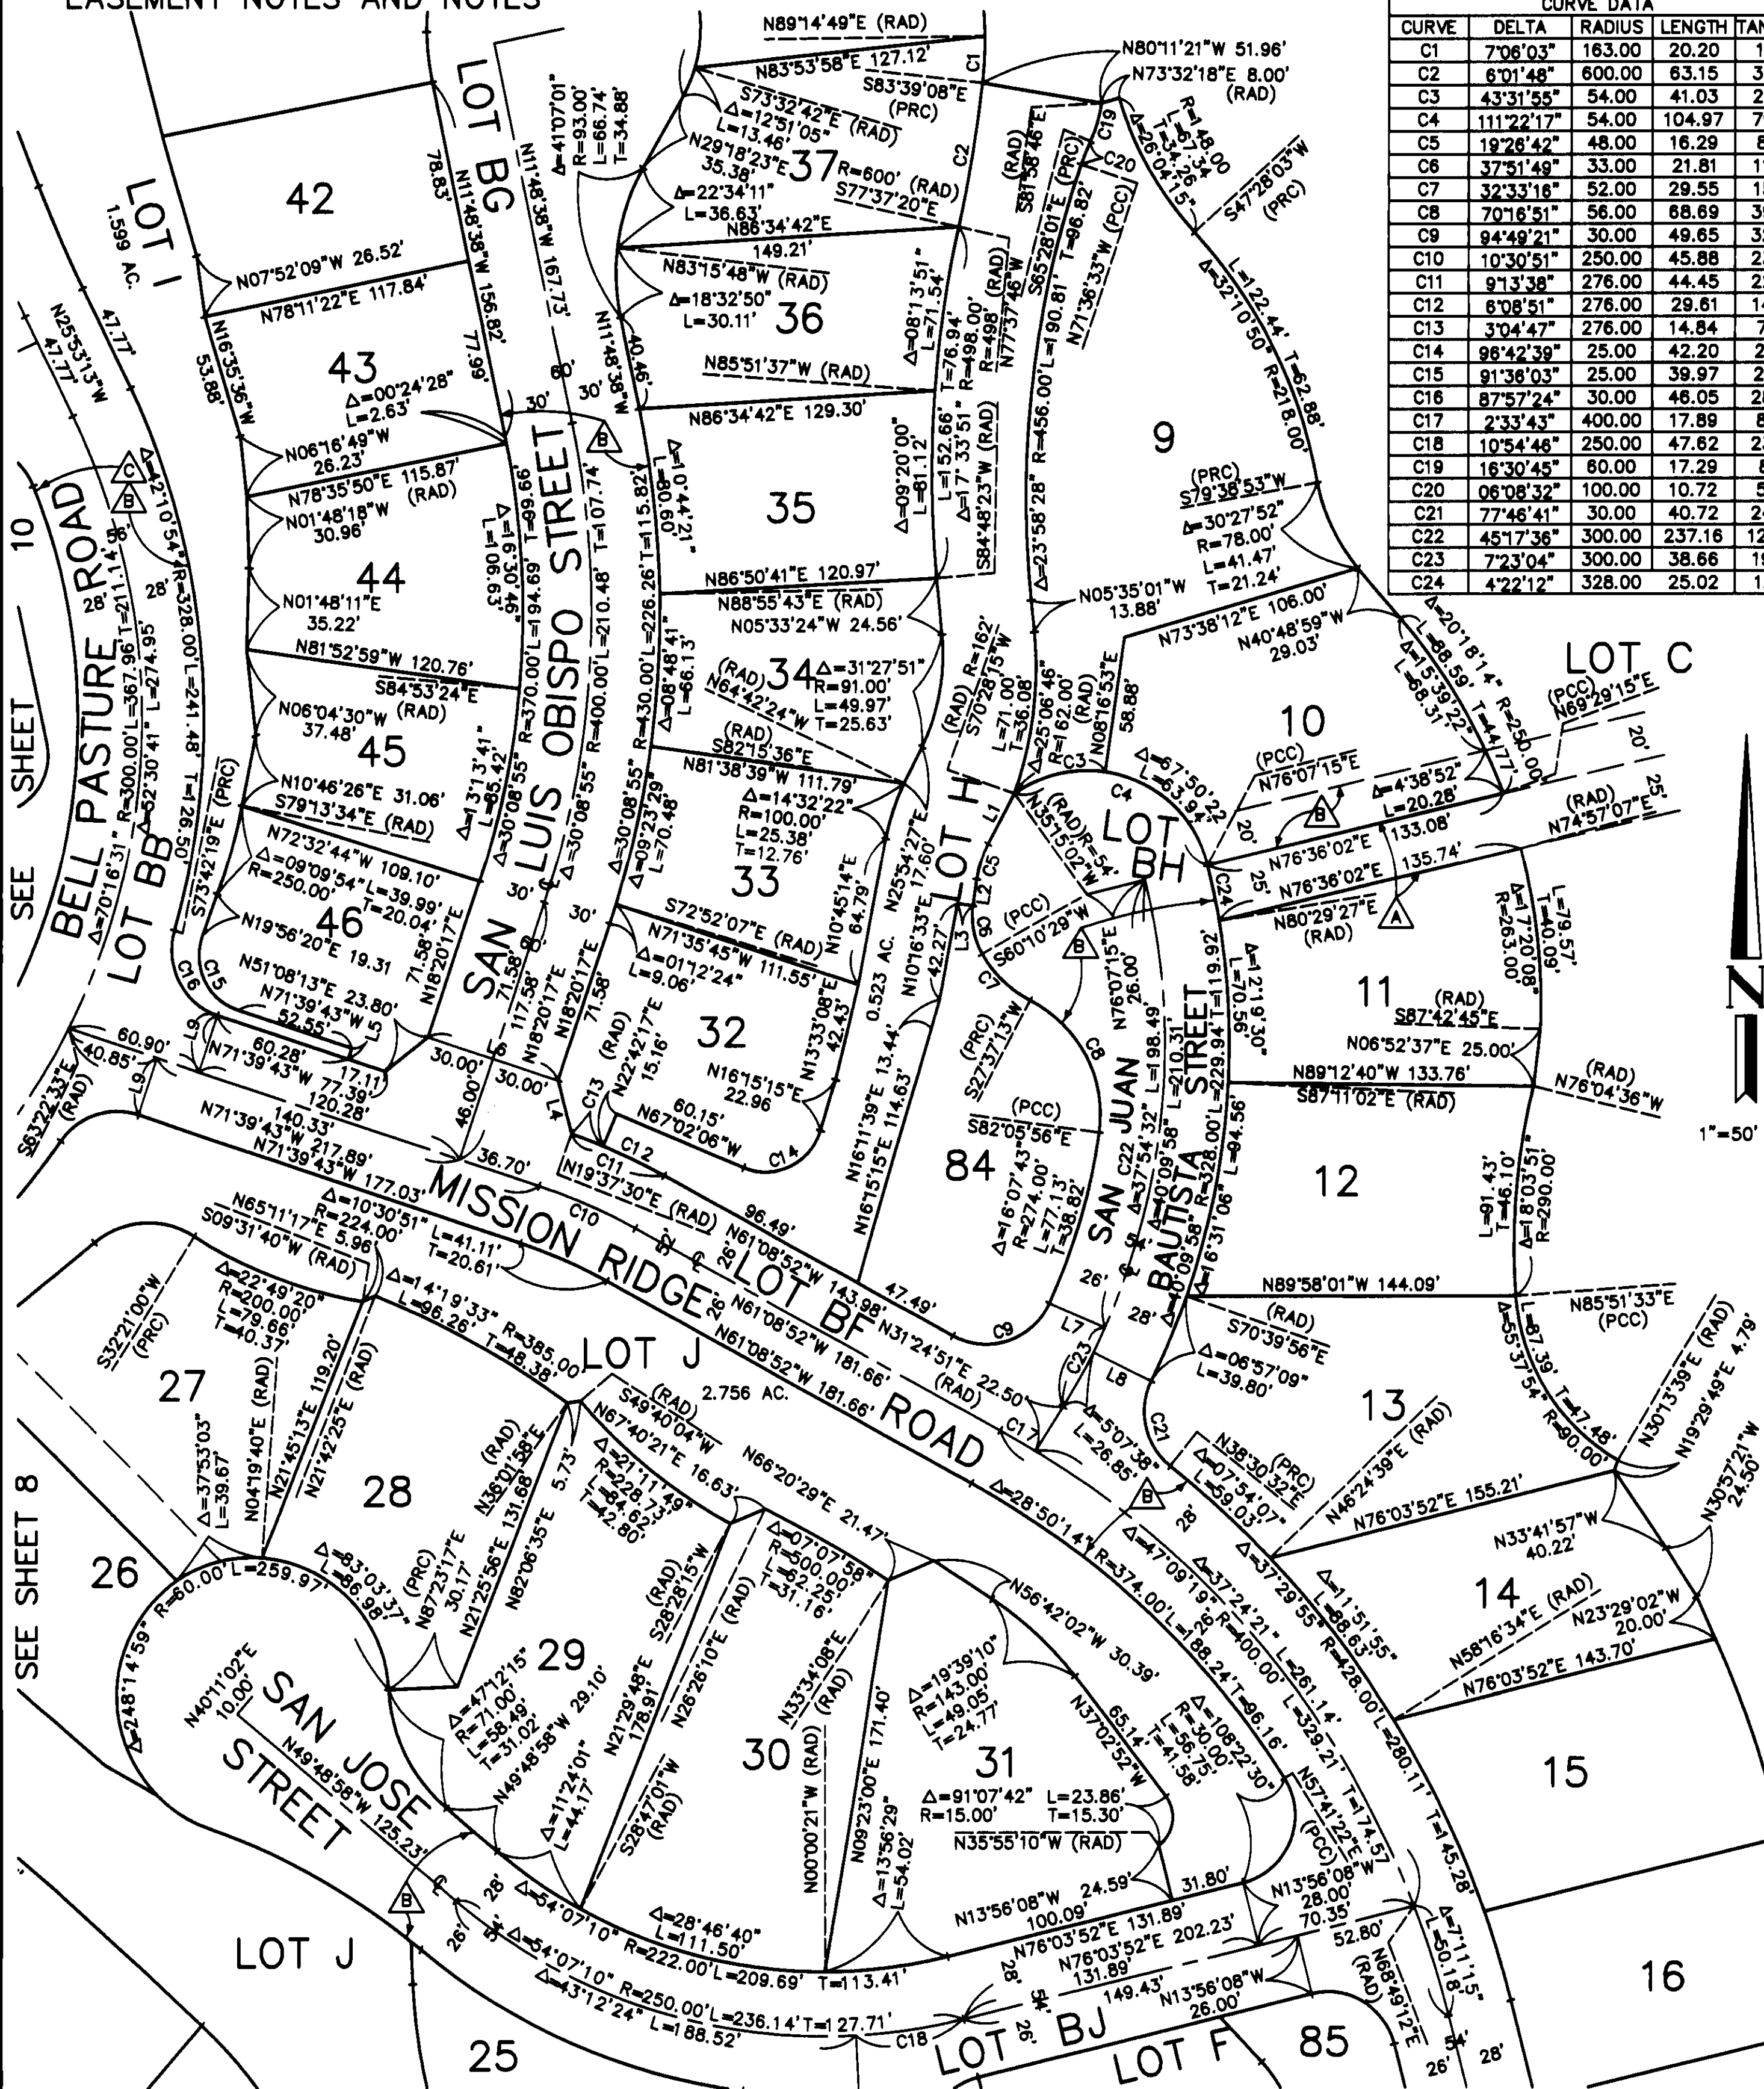

SEE SHEET 13

SEE SHEET 6

842 13

SHEET 6 OF 13 SHEETS
87 NUMBERED LOTS
33 LETTERED LOTS
78.285 ACRES
ALL OF VESTING
T.T.M. 15985
DATE OF SURVEY:
JANUARY, 1999

TRACT MAP NO. 15985

IN THE UNINCORPORATED TERRITORY OF THE COUNTY OF ORANGE,
STATE OF CALIFORNIA


HALL & FOREMAN, INC.

STEVEN C. SHAMBECK, P.L.S. 6217

MAY, 2002

SEE SHEET 2 FOR BASIS OF BEARINGS,
DATUM STATEMENT, MONUMENT NOTES,
EASEMENT NOTES AND NOTES

SEE SHEET 5

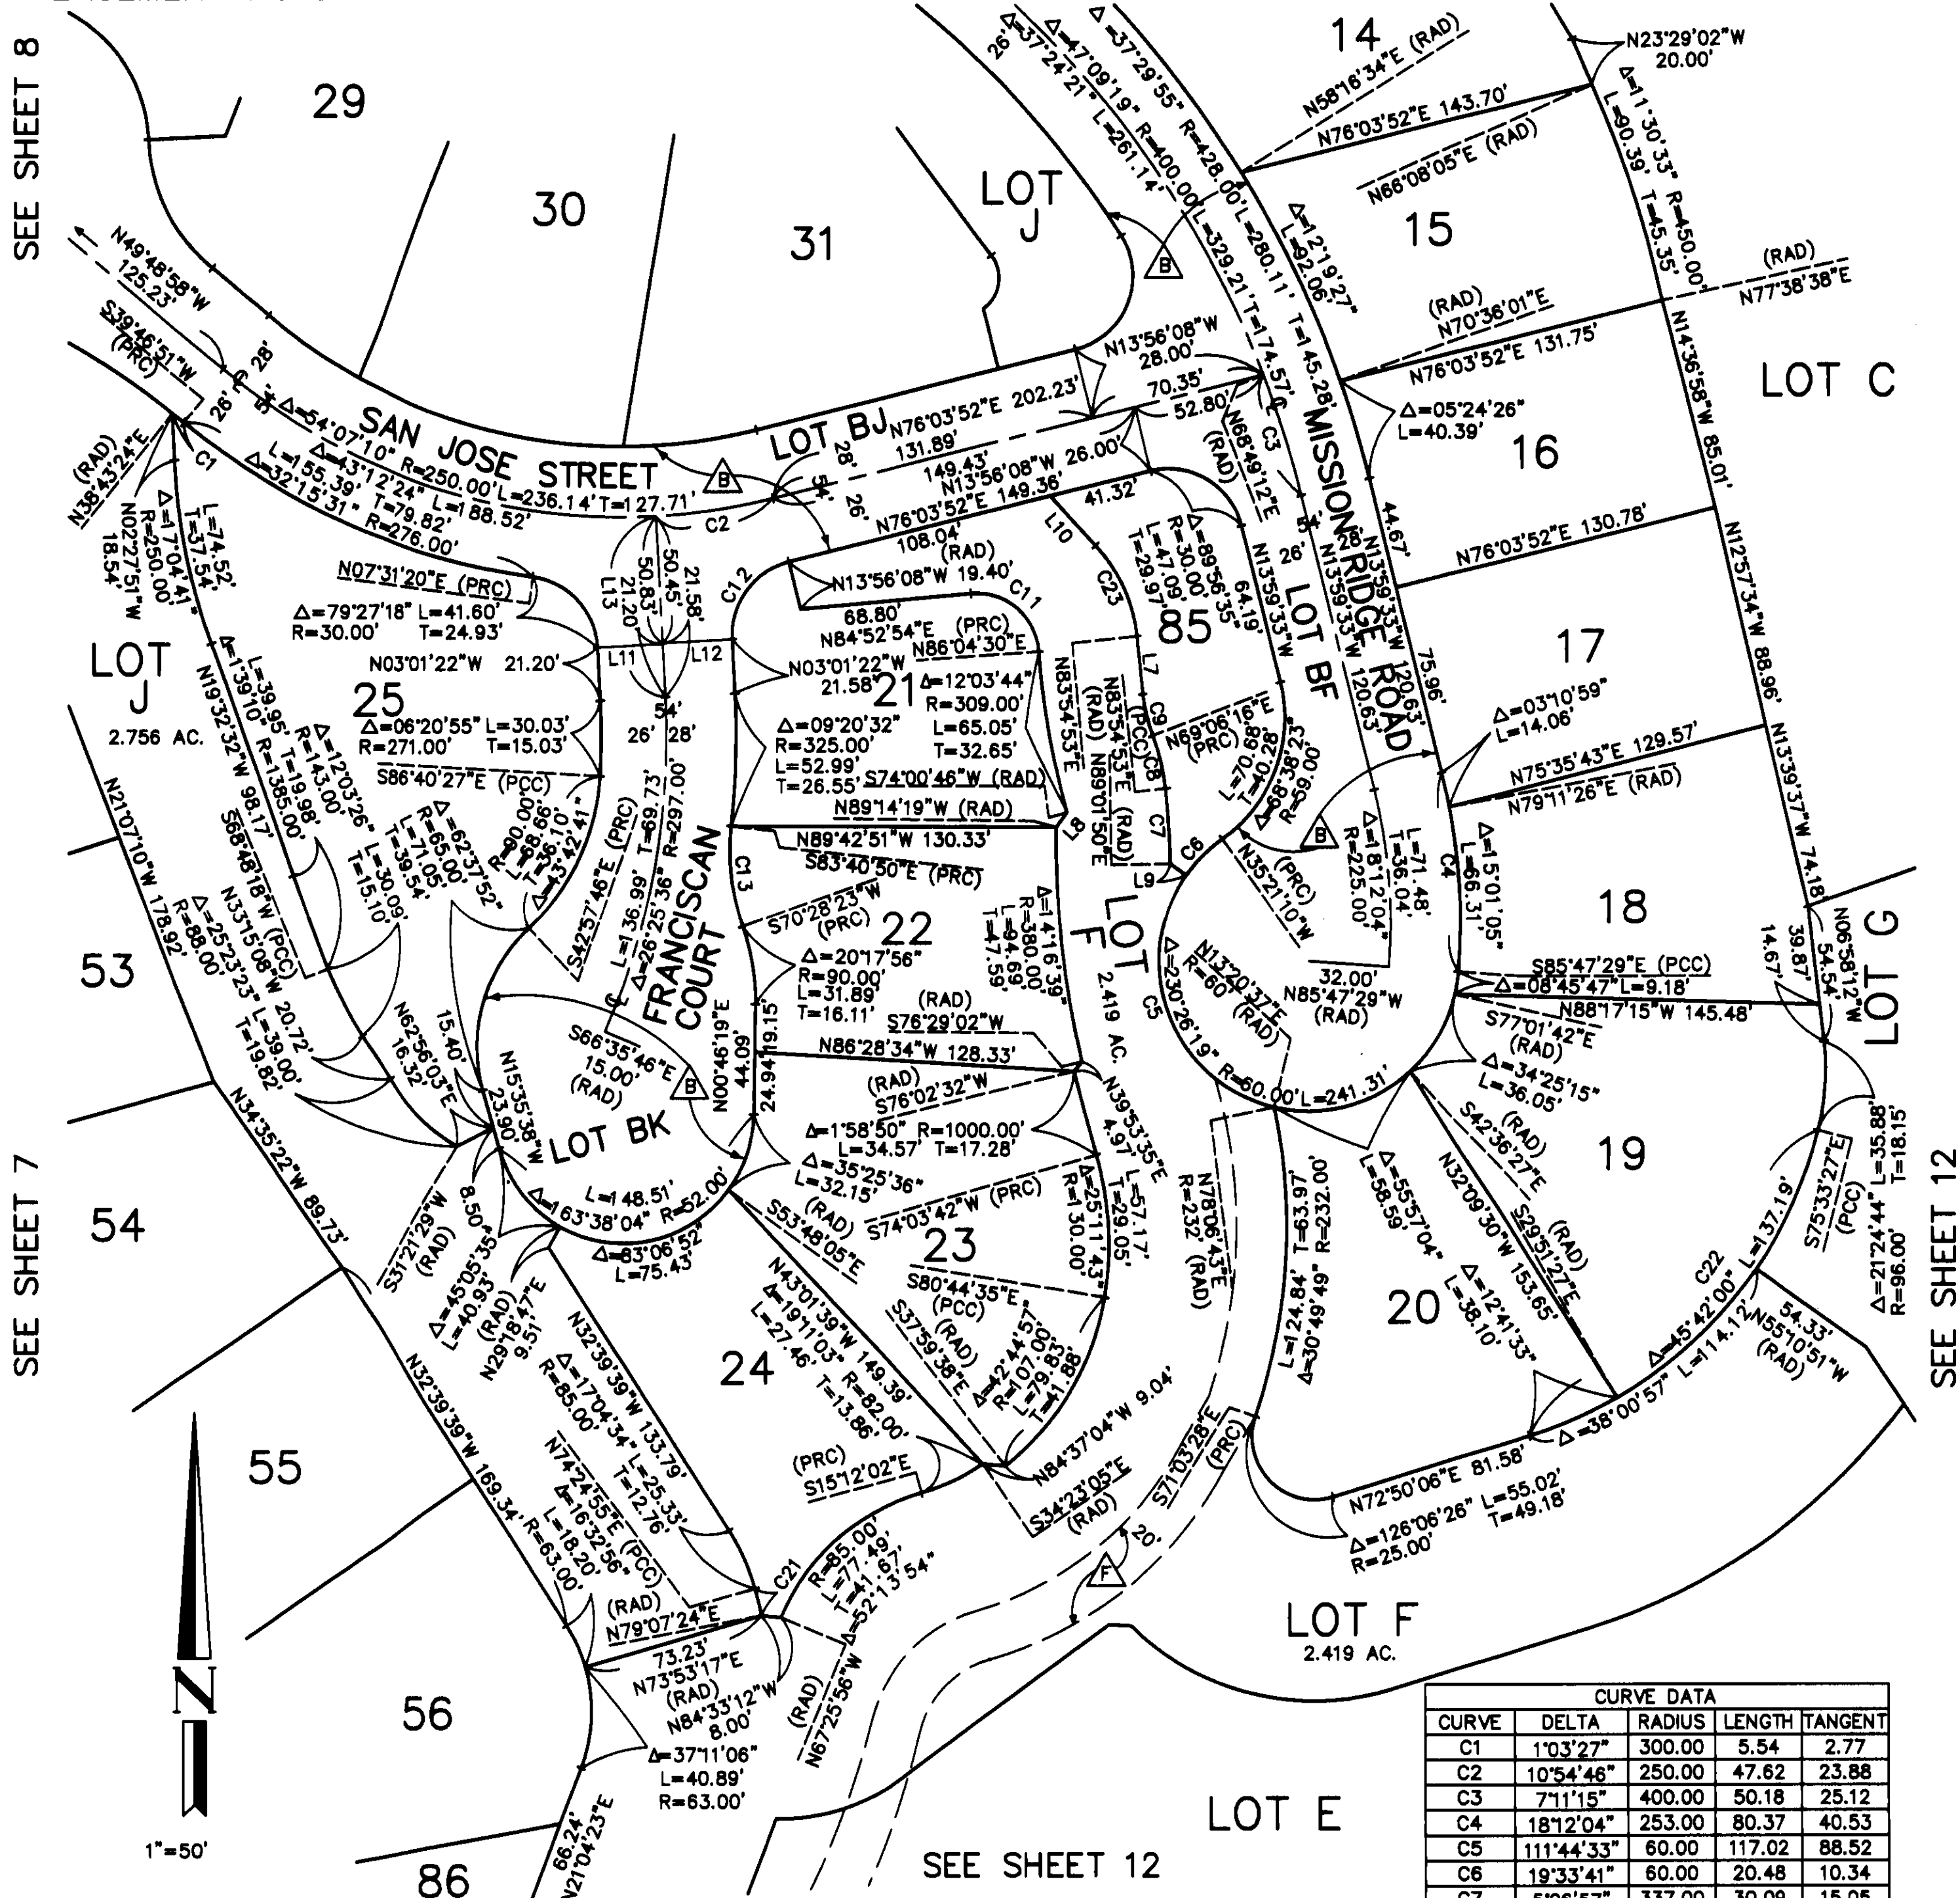

SEE SHEET 8

SEE SHEET 7

SEE SHEET 12

SEE SHEET 12

LINE DATA		
LINE	BEARING	LENGTH
L7	N06°07'34"W	23.21
L8	N36°16'32"E	7.42
L9	N54°54'51"W	8.06 (RAD)
L10	N42°42'42"W	26.79
L11	N86°58'38"W	26.00
L12	N86°58'38"W	28.00
L13	N03°01'22"W	72.03 (RAD)

CURVE DATA				
CURVE	DELTA	RADIUS	LENGTH	TANGENT
C1	1°03'27"	300.00	5.54	2.77
C2	10°54'48"	250.00	47.62	23.88
C3	7°11'15"	400.00	50.18	25.12
C4	18°12'04"	253.00	80.37	40.53
C5	11°44'33"	60.00	117.02	88.52
C6	19°33'41"	60.00	20.48	10.34
C7	5°06'57"	337.00	30.09	15.05
C8	14°48'37"	84.00	21.71	10.92
C9	14°46'10"	66.00	17.01	8.55
C11	91°11'36"	25.00	39.79	25.53
C12	79°05'14"	30.00	41.41	24.77
C13	25°50'47"	90.00	40.80	20.65
C21	4°42'29"	134.00	11.01	5.51
C22	58°23'34"	172.00	175.29	96.11
C23	36°37'35"	63.00	40.27	20.85

842 13

SHEET 7 OF 13 SHEETS
87 NUMBERED LOTS
33 LETTERED LOTS
78.285 ACRES
ALL OF VESTING
T.T.M. 15985
DATE OF SURVEY:
JANUARY, 1999

TRACT MAP NO. 15985


IN THE UNINCORPORATED TERRITORY OF THE COUNTY OF ORANGE,
STATE OF CALIFORNIA

HALL & FOREMAN, INC.

STEVEN C. SHAMBECK, P.L.S. 6217
MAY, 2002

SEE SHEET 2 FOR BASIS OF BEARINGS,
DATUM STATEMENT, MONUMENT NOTES,
EASEMENT NOTES AND NOTES

SEE SHEET 8

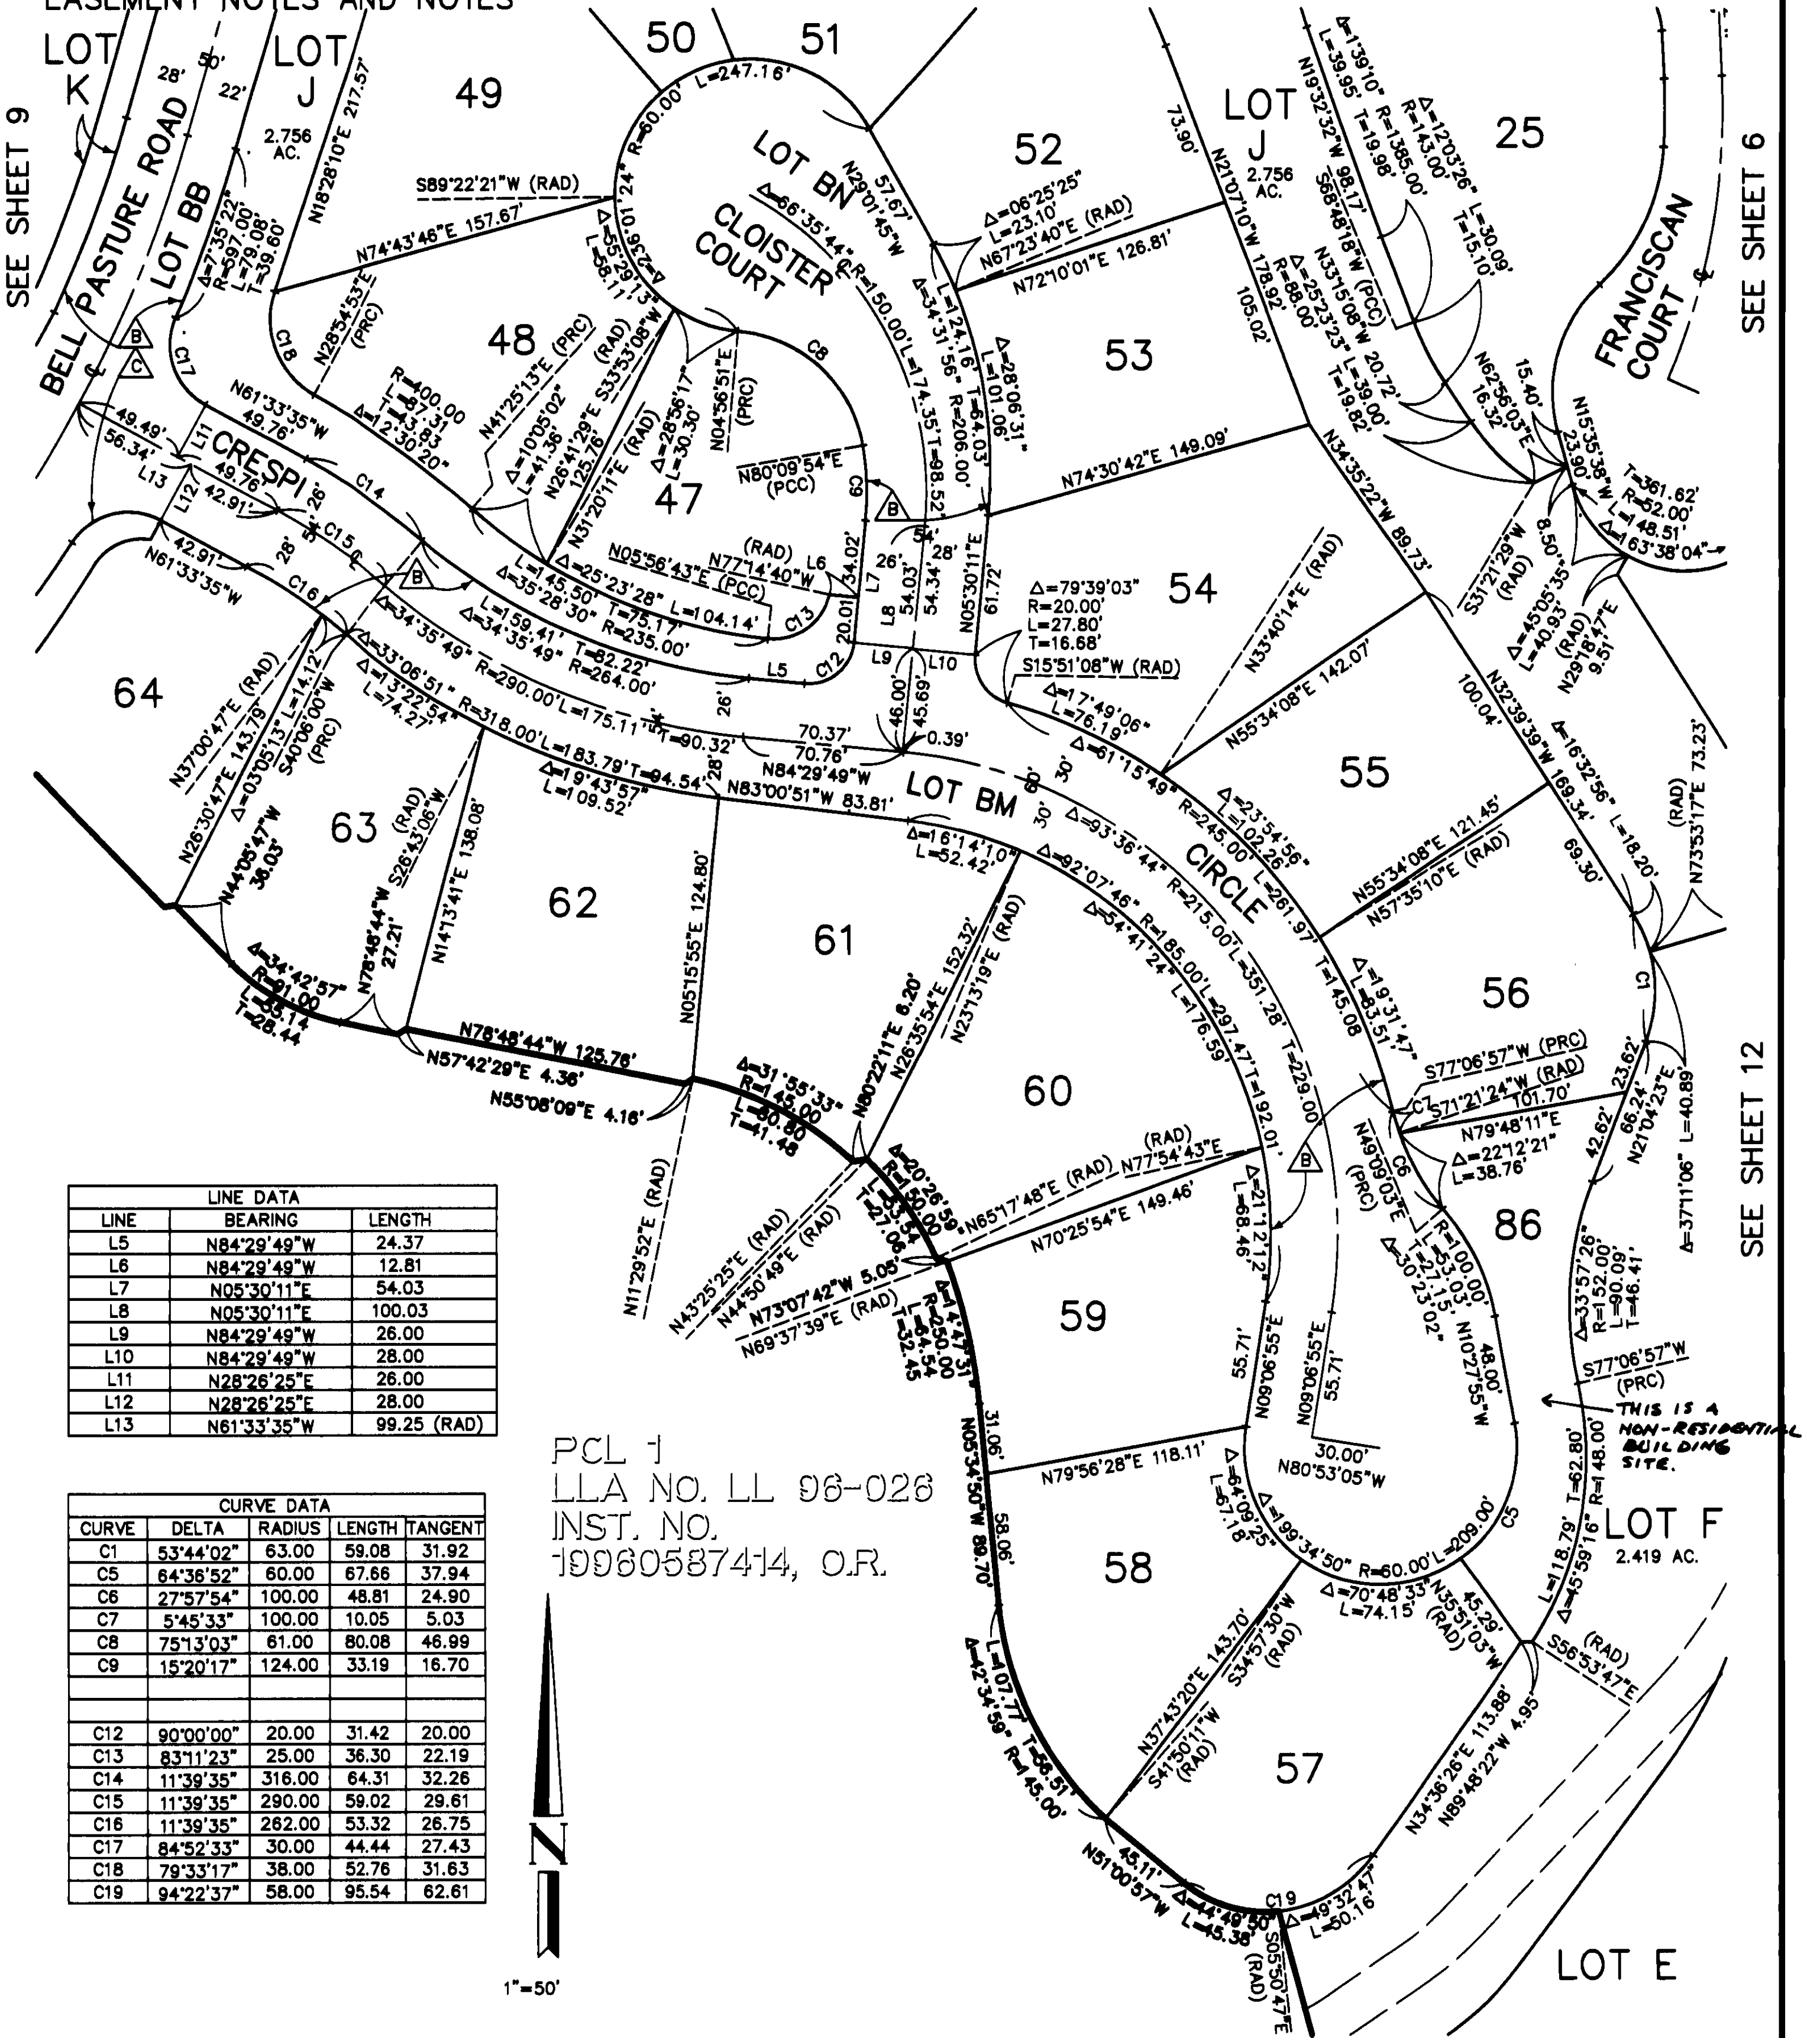

PCL 1
LLA NO. LL 96-026
INST. NO.
19960587414, O.R.

SEE SHEET 12

842 15

SHEET 8 OF 13 SHEETS
87 NUMBERED LOTS
33 LETTERED LOTS
78.285 ACRES
ALL OF VESTING
T.T.M. 15985
DATE OF SURVEY:
JANUARY, 1999

TRACT MAP NO. 15985

IN THE UNINCORPORATED TERRITORY OF THE COUNTY OF ORANGE,
STATE OF CALIFORNIA


HALL & FOREMAN, INC.

STEVEN C. SHAMBECK, P.L.S. 6217
MAY, 2002

SEE SHEET 2 FOR BASIS OF
BEARINGS, DATUM STATEMENT,
MONUMENT NOTES, EASEMENT
NOTES, AND NOTES

LINE DATA				
LINE	BEARING	LENGTH		
L1	N18°20'17"E	26.00		

CURVE DATA				
CURVE	DELTA	RADIUS	LENGTH	TANGENT
C1	10°30'51"	250.00	45.88	23.00
C2	20°38'34"	300.00	108.08	54.63
C3	9°40'32"	322.00	54.38	27.25
C4	73°37'31"	30.00	38.55	22.45

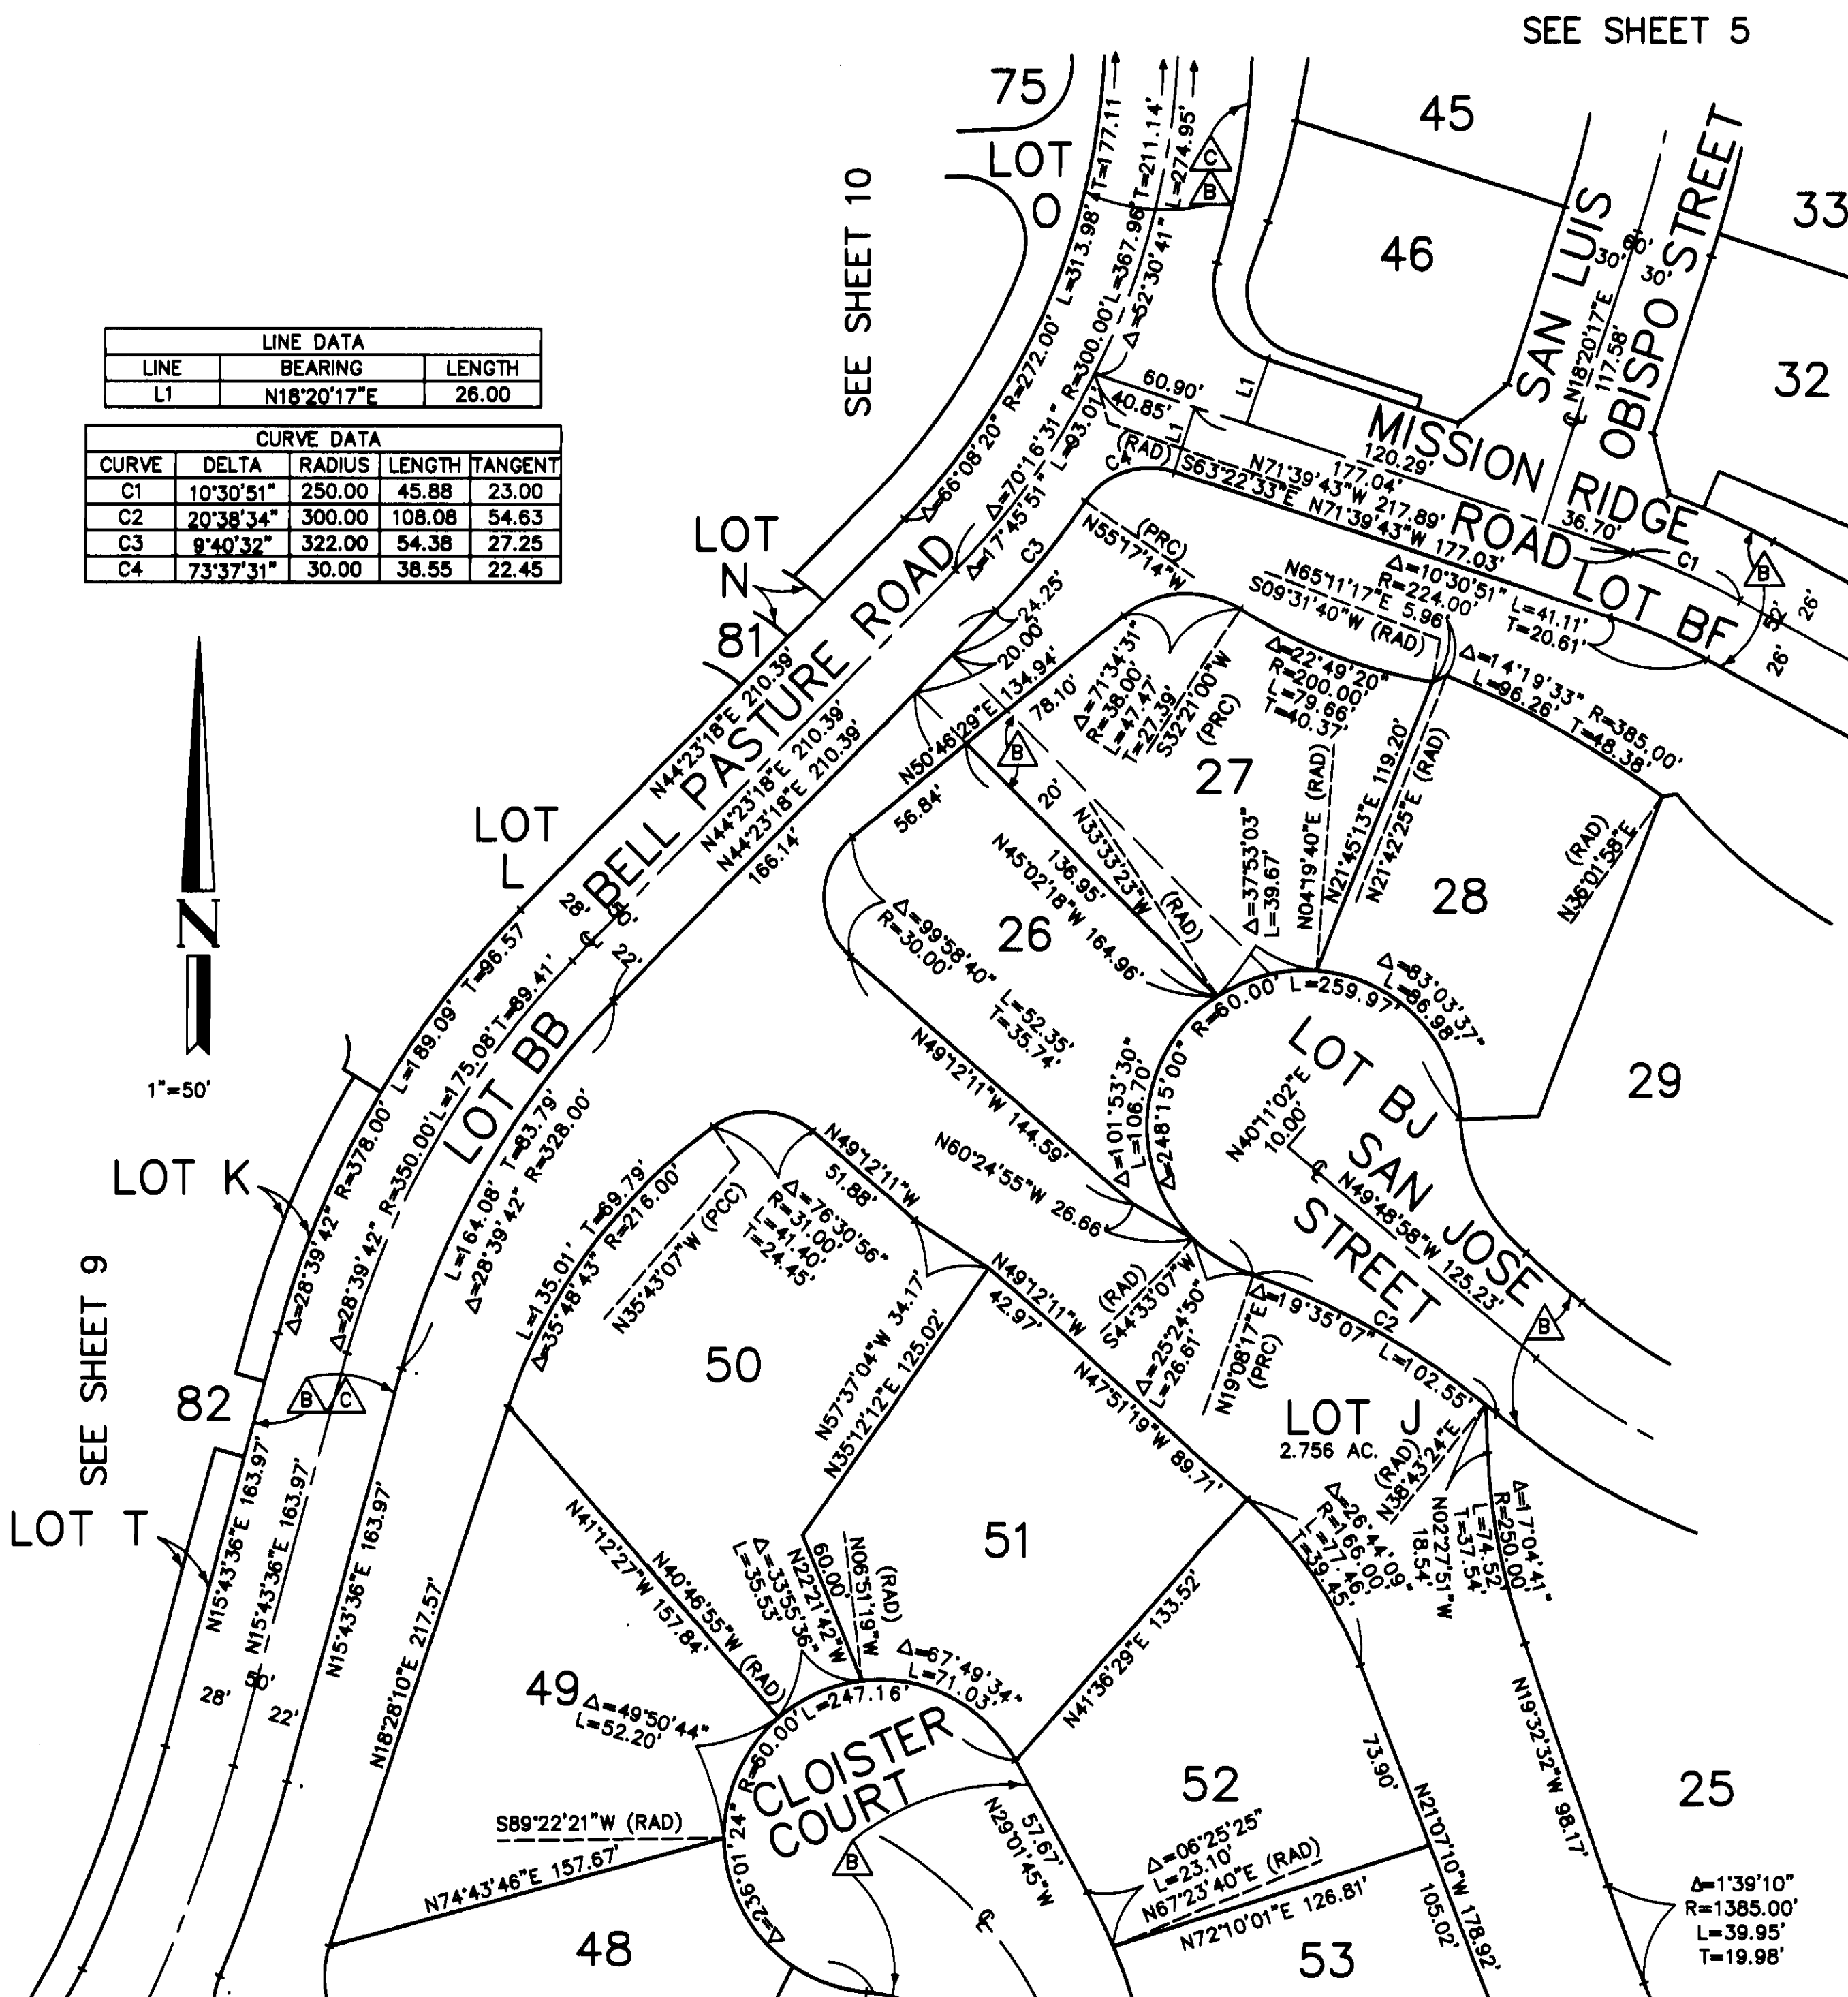

SEE SHEET 5

SEE SHEET 7

SEE SHEET 6

842 15

SHEET 10 OF 13 SHEETS
87 NUMBERED LOTS
33 LETTERED LOTS
78.285 ACRES
ALL OF VESTING
T.T.M. 15985
DATE OF SURVEY:
JANUARY, 1999

TRACT MAP NO. 15985

IN THE UNINCORPORATED TERRITORY OF THE COUNTY OF ORANGE,
STATE OF CALIFORNIA

HALL & FOREMAN, INC.

STEVEN C. SHAMBECK, P.L.S. 6217
MAY, 2002


SEE SHEET 2 FOR BASIS OF
BEARINGS, DATUM STATEMENT,
MONUMENT NOTES, EASEMENT
NOTES, AND NOTES

SEE SHEET 11

SEE SHEET 4

CURVE DATA				
CURVE	DELTA	RADIUS	LENGTH	TANGENT
C1	10°24'43"	83.00	15.08	7.56
C2	57°57'41"	83.00	83.98	45.87
C3	68°22'24"	83.00	99.05	56.38
C4	34°46'41"	60.00	36.42	18.79
C5	3°28'48"	60.00	3.64	1.82
C6	1°01'36"	278.00	4.98	2.49
C7	5°56'32"	300.00	31.11	15.57
C8	63°40'10"	56.00	62.23	34.77
C9	84°59'07"	20.00	29.67	18.32
C10	84°47'40"	30.00	44.40	27.39
C11	57°10'22"	30.00	29.84	16.35
C12	88°29'16"	20.00	30.89	19.48
C13	98°03'12"	30.00	51.34	34.54
C14	107°37'08"	13.00	24.42	17.77
C15	3°29'14"	300.00	18.26	9.13
C16	7°24'07"	300.00	38.76	19.41
C17	8°21'40"	294.00	42.90	21.49
C18	4°49'10"	600.00	50.47	25.25
C19	7°24'07"	272.00	35.14	17.59
C20	63°45'06"	60.00	66.76	37.31
C21	39°35'19"	320.00	221.11	115.17

LINE DATA		
LINE	BEARING	LENGTH
L1	N29°25'27"W	29.60
L2	N21°04'03"W	48.00
L3	N13°00'51"W	26.00 (PCC)
L4	N16°32'42"W	28.00 (RAD)
L5	N75°48'34"W	90.49
L6	N14°11'26"E	26.00
L7	N14°11'26"E	28.00

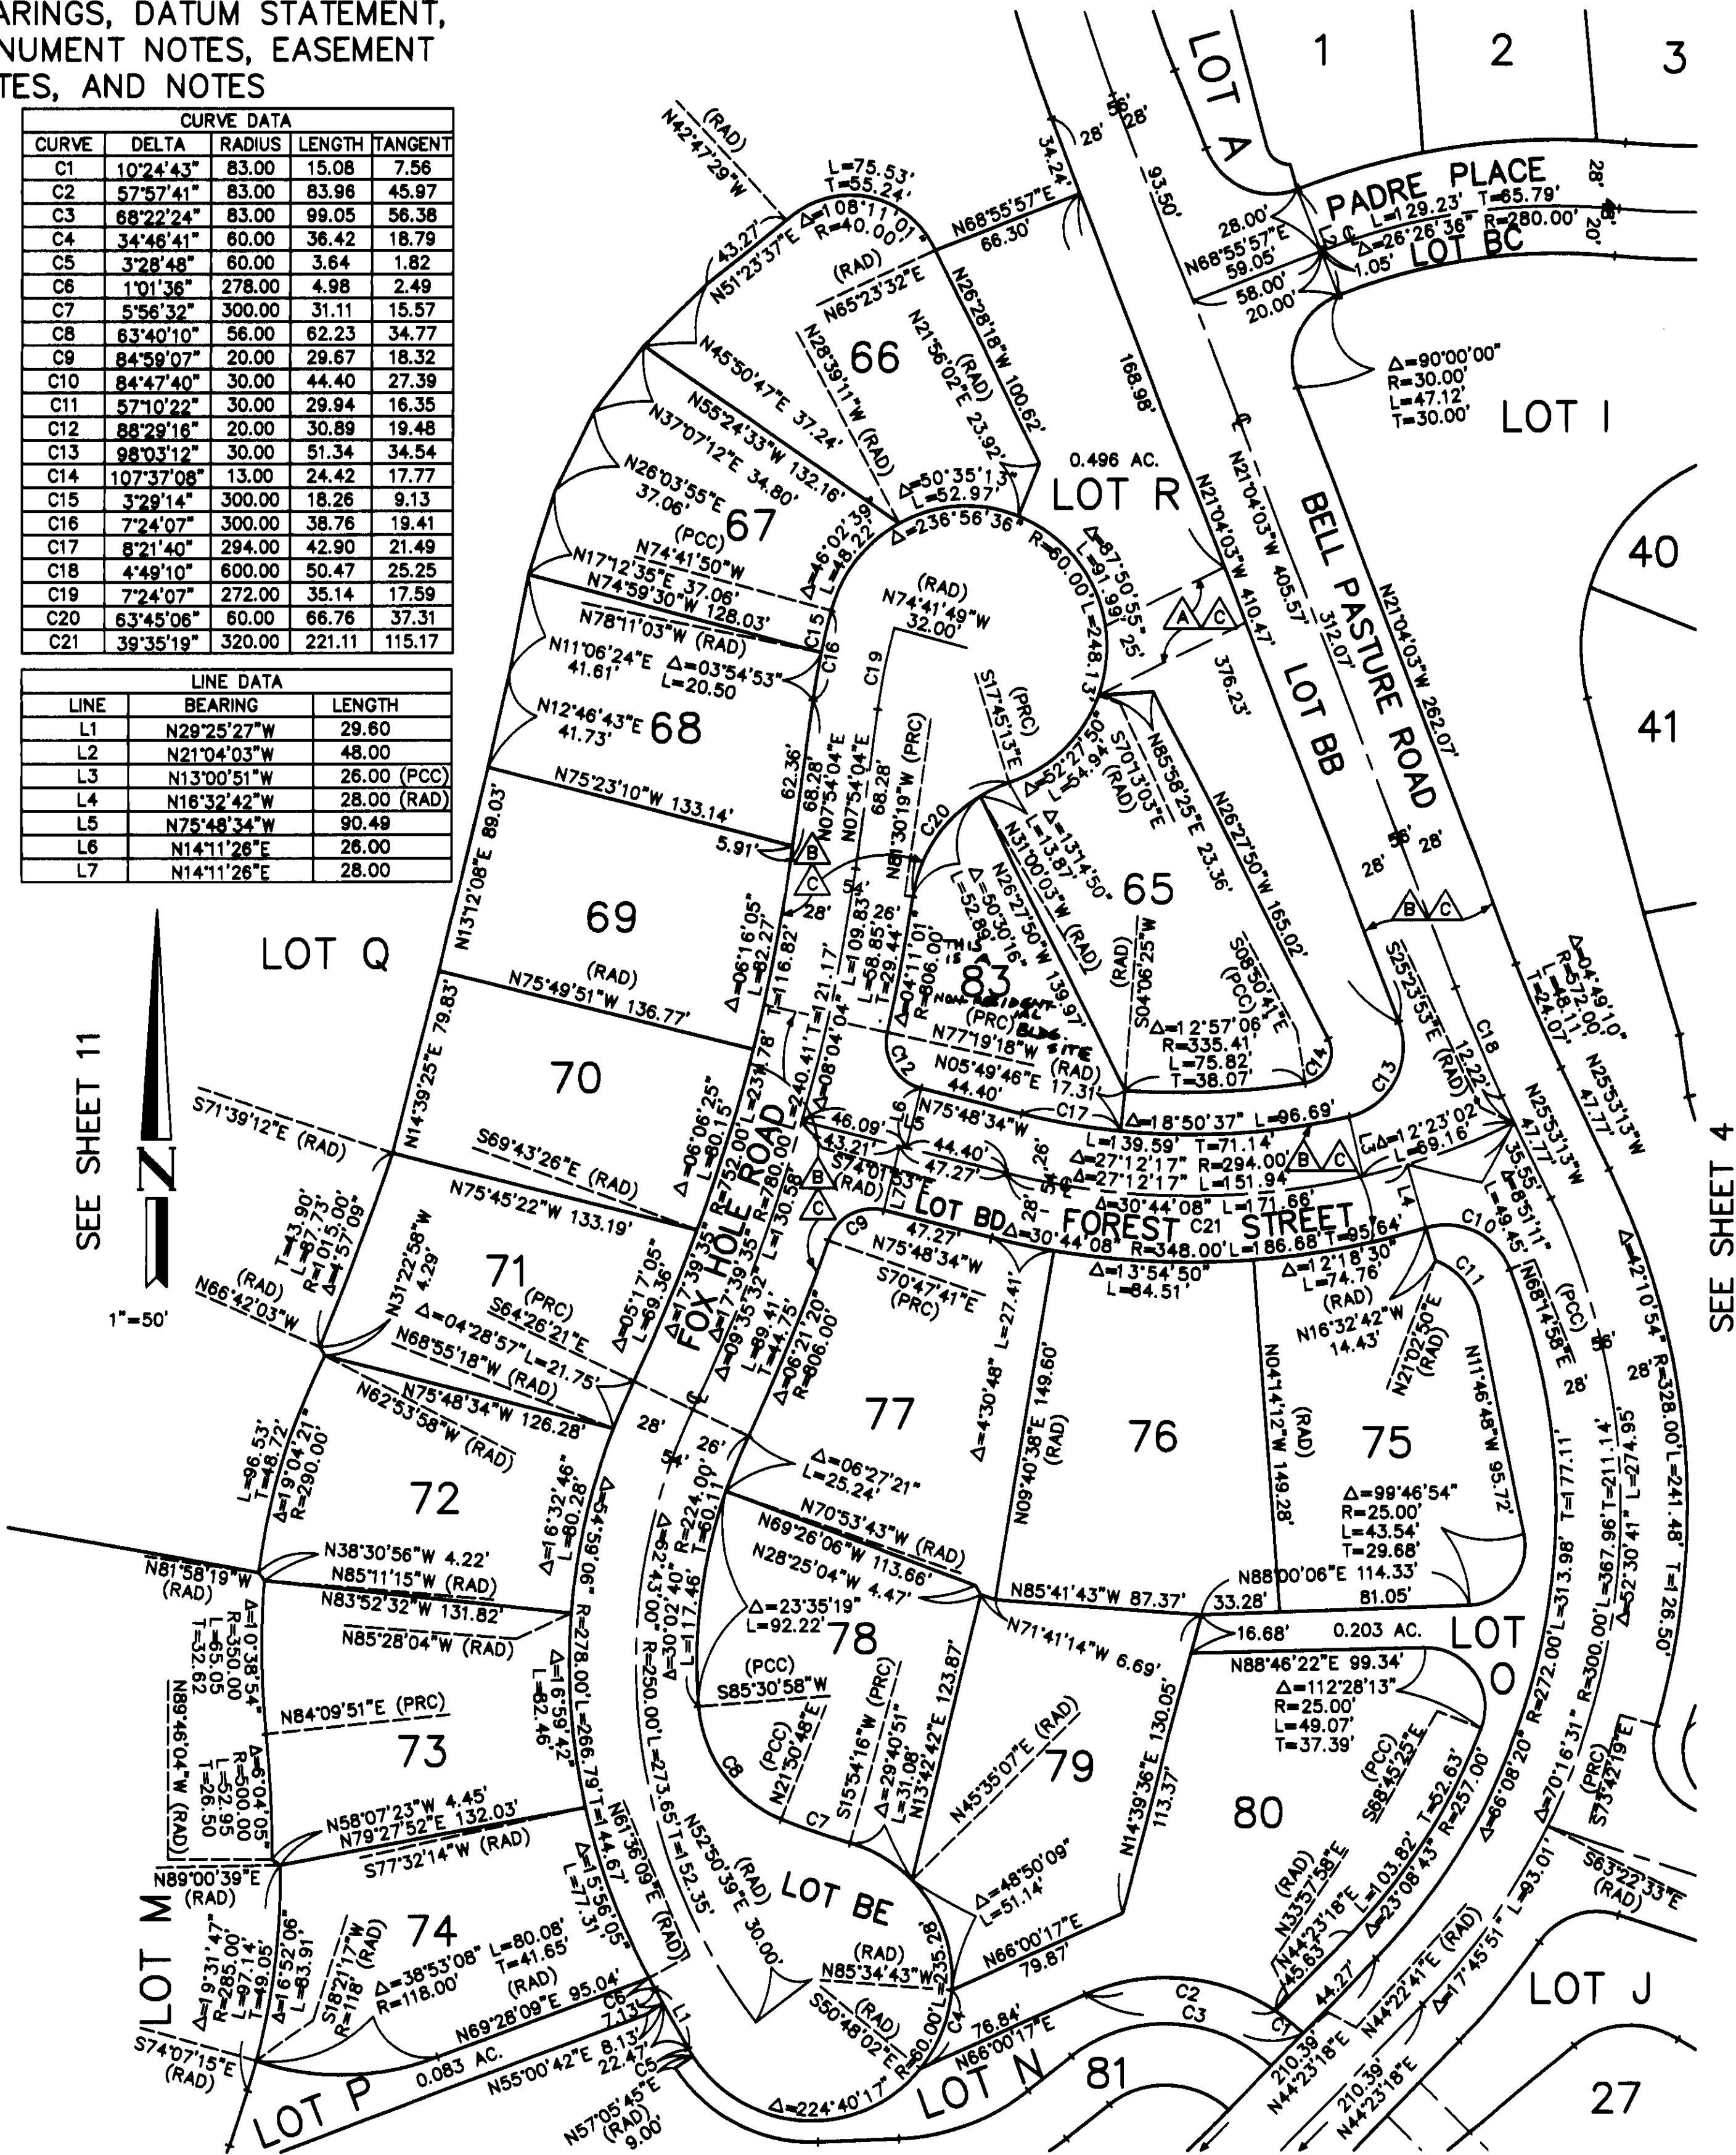

SEE SHEET 8

SHEET 11 OF 13 SHEETS
87 NUMBERED LOTS
33 LETTERED LOTS
78.285 ACRES
ALL OF VESTING
T.T.M. 15985
DATE OF SURVEY:
JANUARY, 1999


TRACT MAP NO. 15985

IN THE UNINCORPORATED TERRITORY OF THE COUNTY OF ORANGE,
STATE OF CALIFORNIA

HALL & FOREMAN, INC.

STEVEN C. SHAMBECK, P.L.S. 6217
MAY, 2002

SEE SHEET 2 FOR BASIS OF
BEARINGS, DATUM STATEMENT,
MONUMENT NOTES, EASEMENT
NOTES, AND NOTES

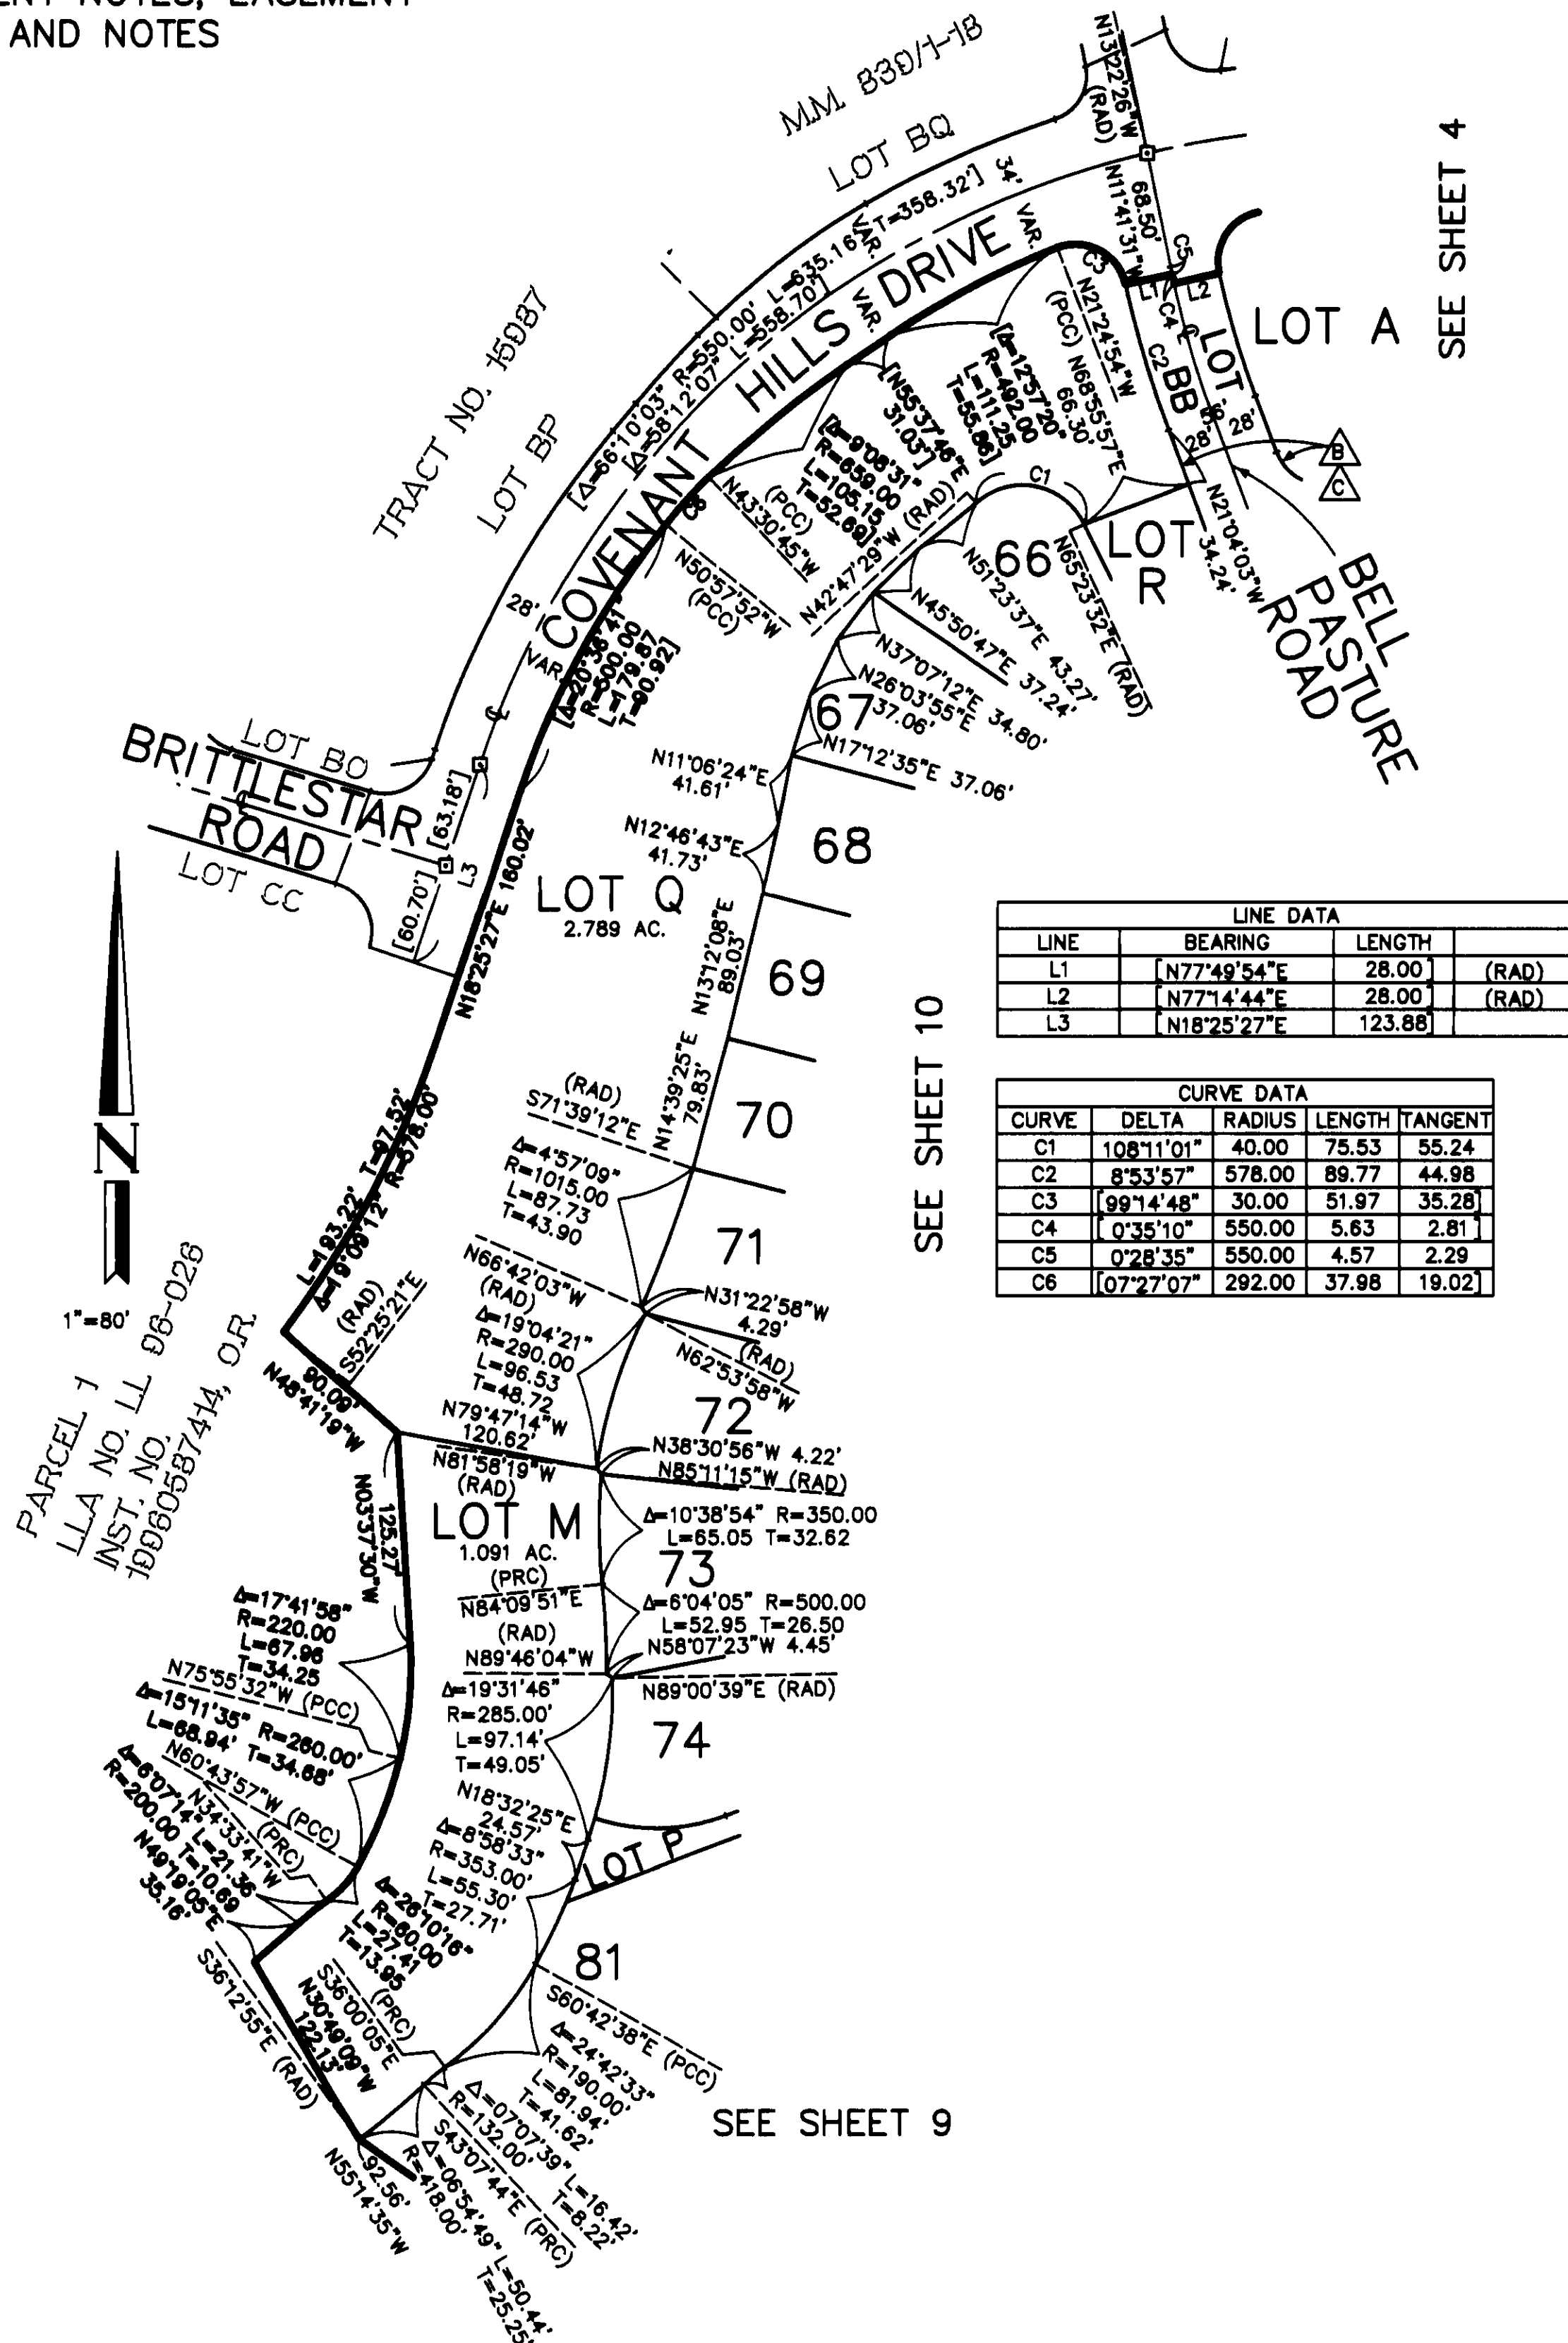

SHEET 12 OF 13 SHEETS
87 NUMBERED LOTS
33 LETTERED LOTS
78.285 ACRES
ALL OF VESTING
T.T.M. 15985
DATE OF SURVEY:
JANUARY, 1999

TRACT MAP NO. 15985

IN THE UNINCORPORATED TERRITORY OF THE COUNTY OF ORANGE,
STATE OF CALIFORNIA


HALL & FOREMAN, INC.

STEVEN C. SHAMBECK, P.L.S. 6217
MAY, 2002

SEE SHEET 2 FOR BASIS OF
BEARINGS, DATUM STATEMENT,
MONUMENT NOTES, EASEMENT
NOTES, AND NOTES

SEE SHEET 6

SEE SHEET 13

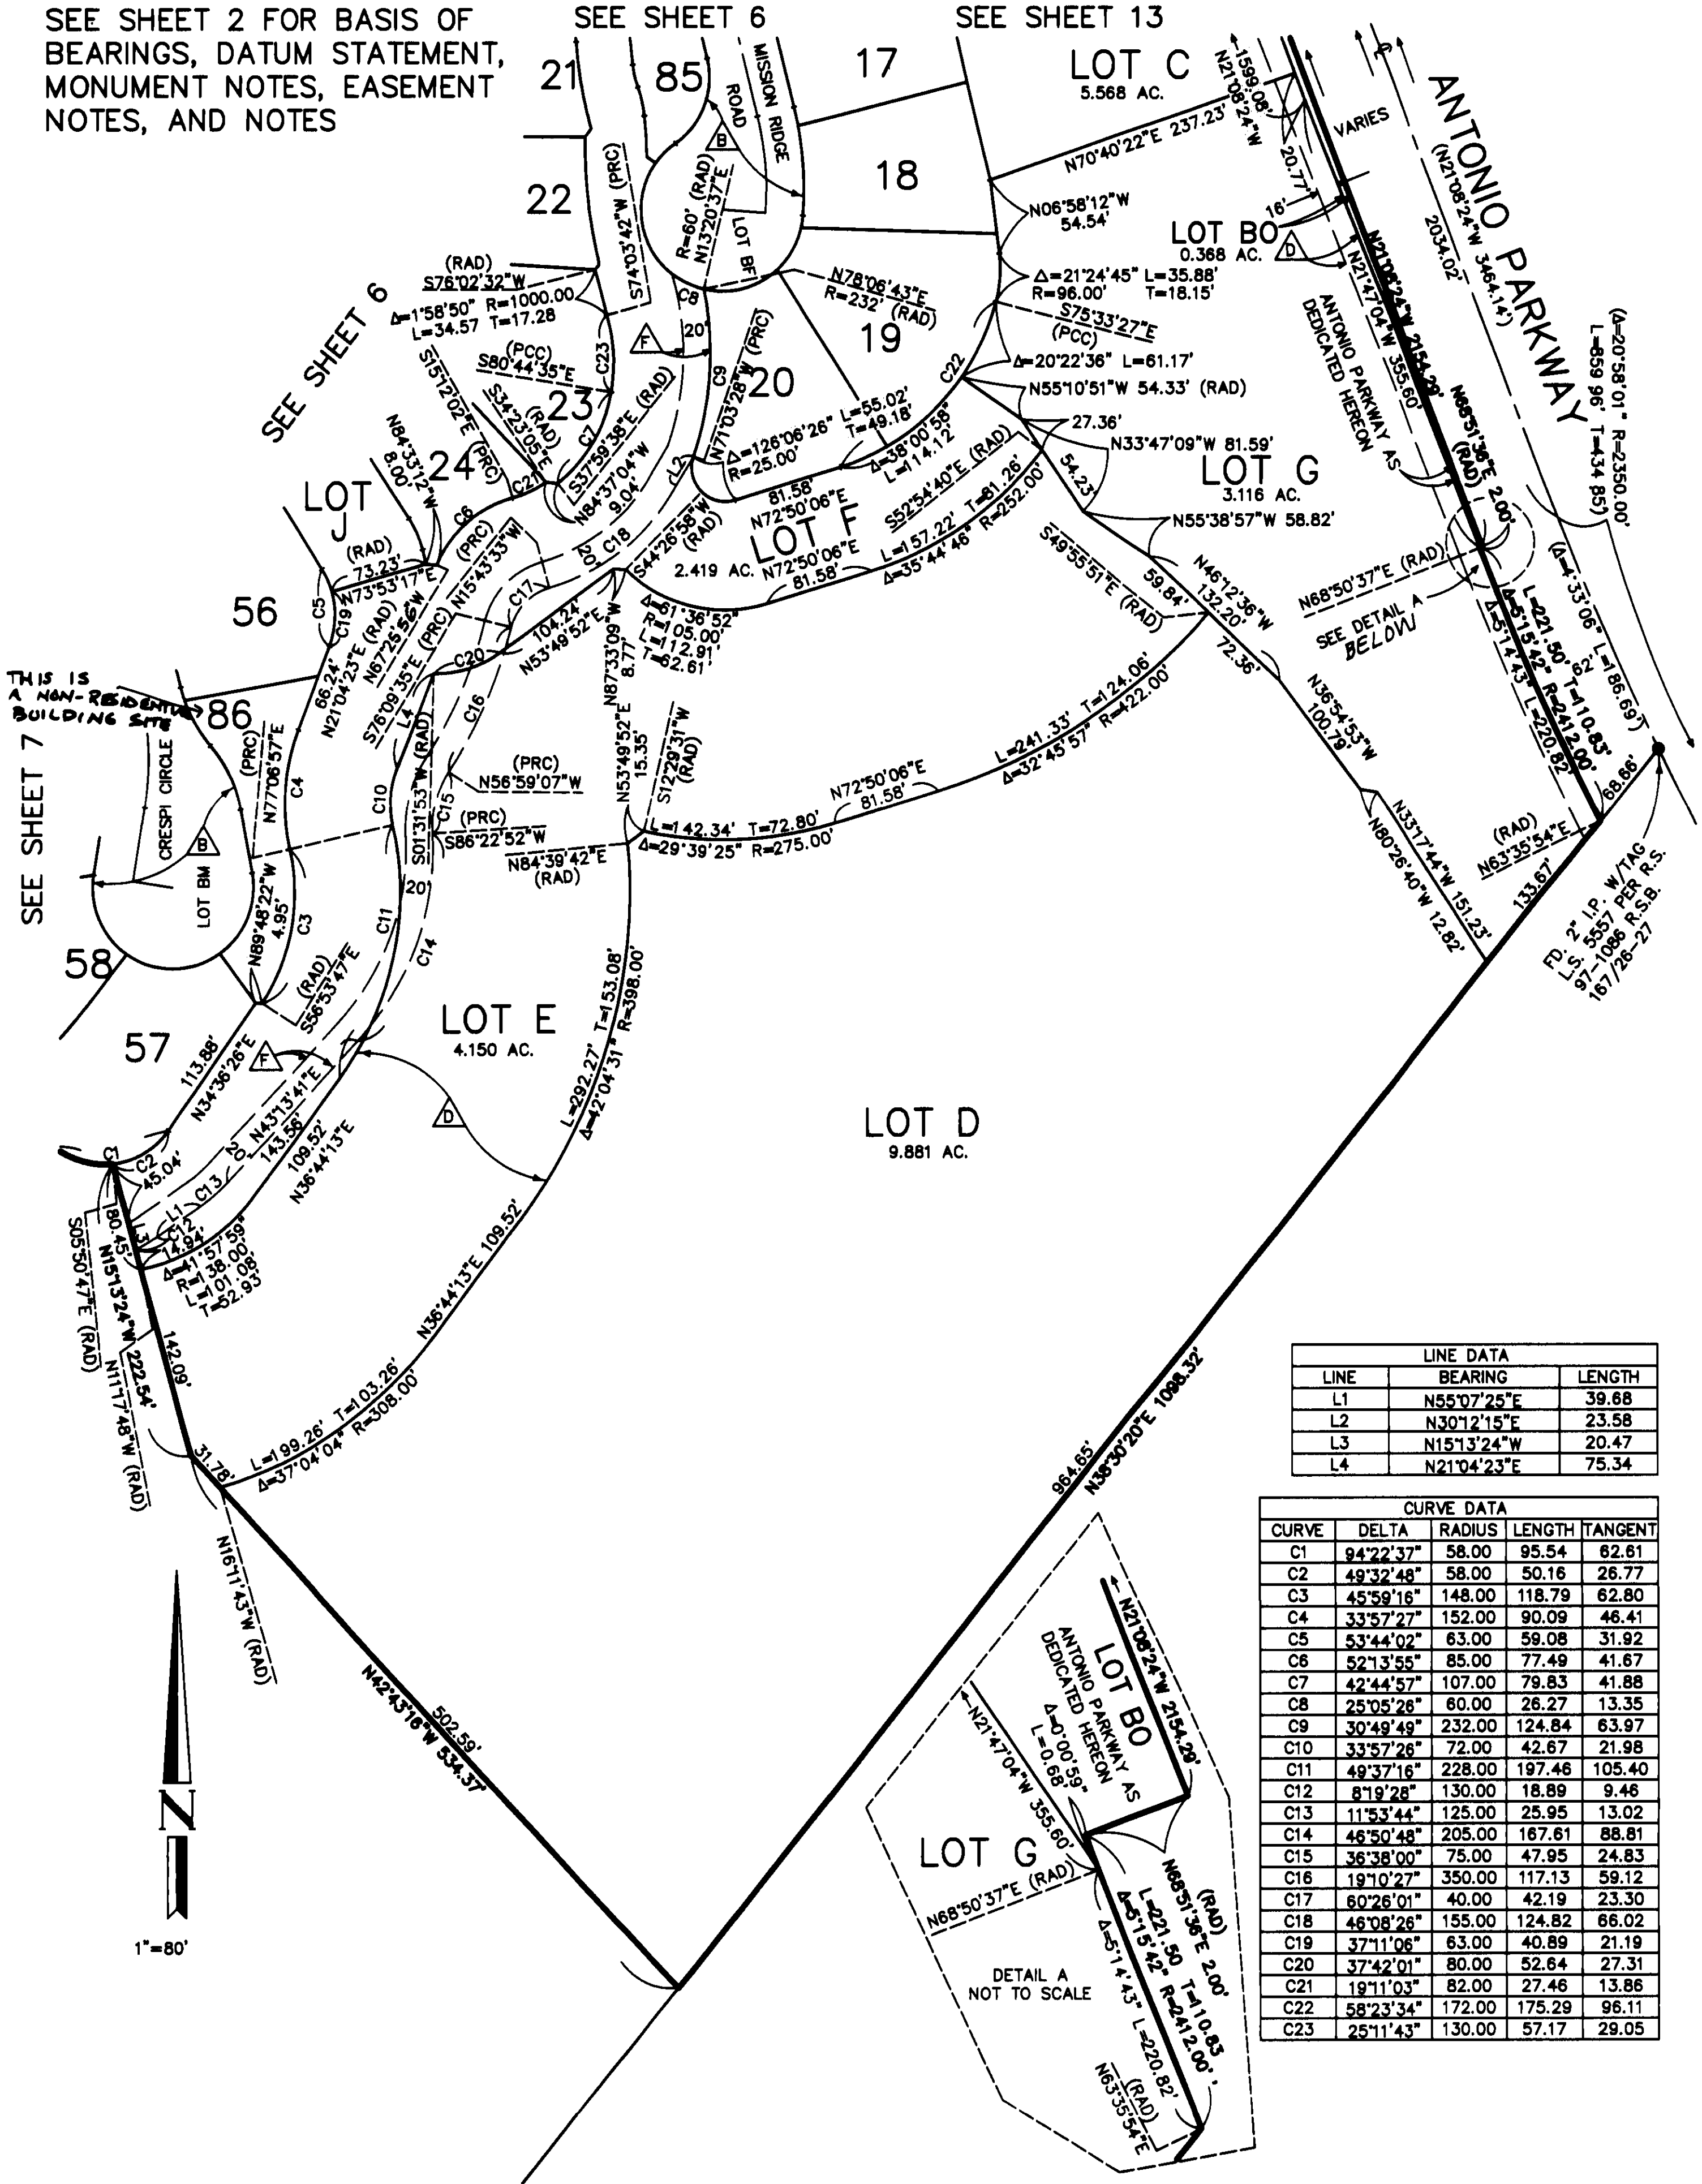

LINE DATA		
LINE	BEARING	LENGTH
L1	N55°07'25"E	39.68
L2	N30°12'15"E	23.58
L3	N15°13'24"W	20.47
L4	N21°04'23"E	75.34

CURVE DATA				
CURVE	DELTA	RADIUS	LENGTH	TANGENT
C1	94°22'37"	58.00	95.54	62.61
C2	49°32'48"	58.00	50.16	26.77
C3	45°59'16"	148.00	118.79	62.80
C4	33°57'27"	152.00	90.09	46.41
C5	53°44'02"	63.00	59.08	31.92
C6	52°13'55"	85.00	77.49	41.67
C7	42°44'57"	107.00	79.83	41.88
C8	25°05'28"	60.00	26.27	13.35
C9	30°49'49"	232.00	124.84	63.97
C10	33°57'26"	72.00	42.67	21.98
C11	49°37'16"	228.00	197.46	105.40
C12	8°19'28"	130.00	18.89	9.46
C13	11°53'44"	125.00	25.95	13.02
C14	46°50'48"	205.00	167.61	88.81
C15	36°38'00"	75.00	47.95	24.83
C16	19°10'27"	350.00	117.13	59.12
C17	60°26'01"	40.00	42.19	23.30
C18	46°08'26"	155.00	124.82	66.02
C19	37°11'06"	63.00	40.89	21.19
C20	37°42'01"	80.00	52.64	27.31
C21	19°11'03"	82.00	27.46	13.86
C22	58°23'34"	172.00	175.29	96.11
C23	25°11'43"	130.00	57.17	29.05

842 20

SHEET 13 OF 13 SHEETS
87 NUMBERED LOTS
33 LETTERED LOTS
78.285 ACRES
ALL OF VESTING
T.T.M. 15985
DATE OF SURVEY:
JANUARY, 1999

TRACT MAP NO. 15985

IN THE UNINCORPORATED TERRITORY OF THE COUNTY OF ORANGE,
STATE OF CALIFORNIA


HALL & FOREMAN, INC.

STEVEN C. SHAMBECK, P.L.S. 6217

MAY, 2002

SEE SHEET 2 FOR BASIS OF
BEARINGS, DATUM STATEMENT,
MONUMENT NOTES, EASEMENT
NOTES AND NOTES

SEE SHEET 4

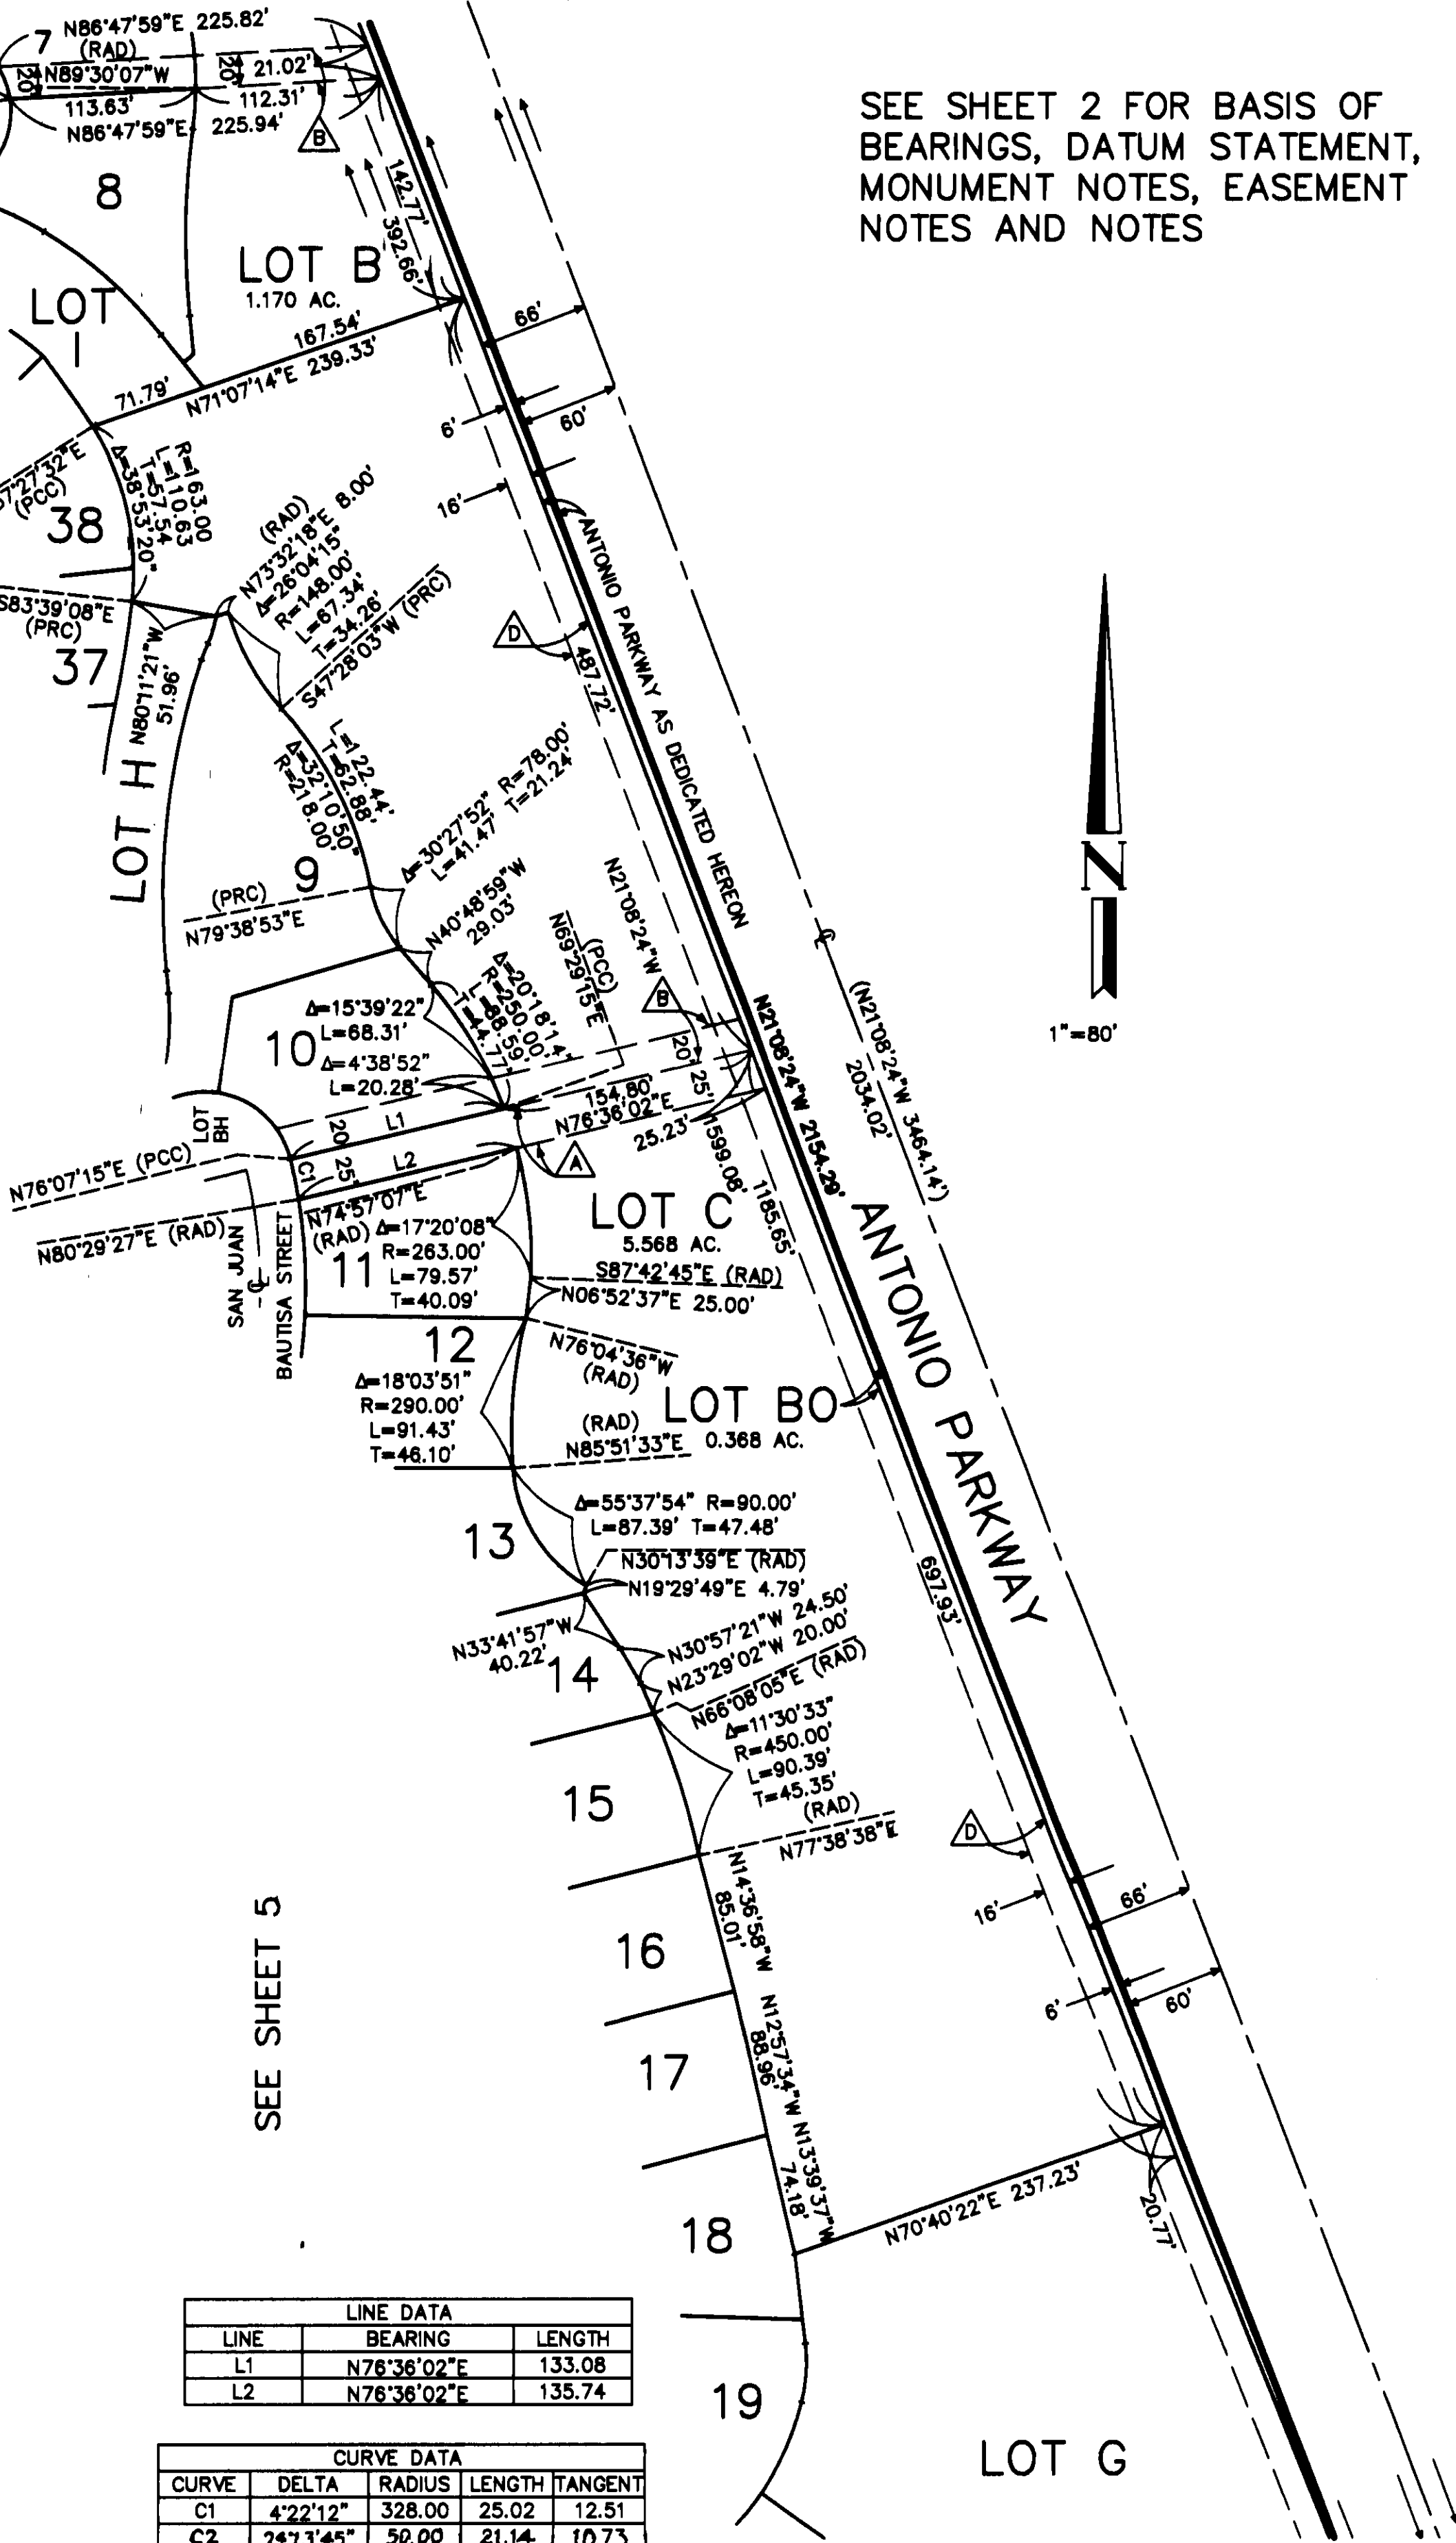

SEE SHEET 5

LINE DATA		
LINE	BEARING	LENGTH
L1	N76°36'02"E	133.08
L2	N76°36'02"E	135.74

CURVE DATA				
CURVE	DELTA	RADIUS	LENGTH	TANGENT
C1	4°22'12"	328.00	25.02	12.51
C2	24°3'45"	50.00	21.14	10.73

SEE SHEET 12

842 20