

ALL OF VESTING TENTATIVE
TRACT NO. 15986DATE OF SURVEY:
JANUARY 1999 &
MARCH 2002IN THE UNINCORPORATED TERRITORY OF ORANGE COUNTY, CALIFORNIA
BEING A SUBDIVISION OF A PORTION OF PARCEL 1 OF LOT LINE ADJUSTMENT NO. LL 96-026
AS SHOWN ON EXHIBIT "B" ATTACHED TO THAT CERTAIN DOCUMENT RECORDED NOVEMBER 21,
1996 AS INSTRUMENT NO. 19960587414 OF OFFICIAL RECORDS, RECORDS OF ORANGE COUNTY,
CALIFORNIA.

SEPTEMBER 2002

JAMES F. GILLEN, L.S. 5557

HUITT-ZOLLARS

13 NUMBERED LOTS AND 58 LETTERED LOTS

120.329 ACRES

ACCEPTED AND FILED AT THE
REQUEST OF

FIRST AMERICAN TITLE INSURANCE CO.

DATE AUGUST 28, 2003TIME 02:05 PM FEE \$ 35.00INSTRUMENT NO. 20030010458 39BOOK 849 PAGE 1-15 m/m

TOM DEWITT

COUNTY CLERK-RECORDER

BY [Signature]
DEPUTY

OWNERSHIP CERTIFICATE:

WE, THE UNDERSIGNED, BEING ALL PARTIES HAVING ANY RECORD TITLE INTEREST IN THE
LAND COVERED BY THIS MAP, DO HEREBY CONSENT TO THE PREPARATION AND RECORDATION
OF SAID MAP, AS SHOWN WITHIN THE DISTINCTIVE BORDER LINE.

WE ALSO HEREBY DEDICATE TO THE COUNTY OF ORANGE:

- (1) THE EASEMENTS FOR SIDEWALK PURPOSES AS SHOWN ON SAID MAP.
- (2) THE EASEMENT FOR PUBLIC PEDESTRIAN PURPOSES AS SHOWN ON SAID MAP.
- (3) THE EASEMENTS FOR EMERGENCY ACCESS PURPOSES OVER ALL OF LOTS AX, AY, AZ, BA, BB,
BC, BD, AND BE AS SHOWN ON SAID MAP.

- (4) THE EASEMENT FOR STORM DRAIN PURPOSES AS SHOWN ON SAID MAP.

WE ALSO HEREBY DEDICATE TO THE SANTA MARGARITA WATER DISTRICT THE EASEMENTS FOR WATER,
RECYCLED WATER, SEWER, DRAINAGE AND ACCESS PURPOSES OVER THOSE EASEMENT AREAS AS SHOWN
ON SAID MAP WHICH EASEMENTS SHALL BE SUBJECT TO THE SAME CONDITIONS AS ARE SHOWN IN
THAT CERTAIN GRANT OF EASEMENT TO SANTA MARGARITA WATER DISTRICT RECORDED SEPTEMBER 18,
2002 AS INSTRUMENT NO. 20020799401, OF OFFICIAL RECORDS, COUNTY OF ORANGE.

DMB LADERA, LLC, A DELAWARE LIMITED LIABILITY COMPANY.

BY: RANCHO MISSION VIEJO, LLC, A DELAWARE LIMITED LIABILITY COMPANY,
ITS AUTHORIZED AGENT AND MANAGER.BY: [Signature]
PRINT NAME: Donald T. Stahlman
PRINT TITLE: Director of Community DevelopmentBY: [Signature]
PRINT NAME: Stephen C. Scheant
PRINT TITLE: Exec. Vice President Development

CERTIFICATE OF ACCEPTANCE:

THE UNDERSIGNED, BEING THE DULY APPOINTED AGENT OF THE SANTA MARGARITA WATER
DISTRICT, A PUBLIC CORPORATION OF ORANGE COUNTY, CALIFORNIA, PURSUANT TO ITS
RESOLUTION NO. 88-10-2, DOES HEREBY ACCEPT ON BEHALF OF SAID DISTRICT THE EASEMENTS
FOR WATER, RECYCLED WATER, SEWER, DRAINAGE AND ACCESS PURPOSES, AS DEDICATED AND AS
SHOWN ON THIS TRACT MAP, BY AND BETWEEN THE SANTA MARGARITA WATER DISTRICT AND DMB
LADERA, L.L.C., AND DOES HEREBY CERTIFY THAT THE GRANTEE CONSENTS TO THE RECORDATION
OF SAID TRACT.[Signature]
DANIEL R. FERONS, CHIEF ENGINEER
SANTA MARGARITA WATER DISTRICT.

AUTOMATIC FIRE SPRINKLER NOTE:

ALL COMMERCIAL STRUCTURES GREATER THAN 6,000 SQUARE FEET; ALL MULTIFAMILY RESIDENTIAL
STRUCTURES; ALL SINGLE-FAMILY STRUCTURES EXCEEDING 5,500 SQUARE FEET, AND ALL STRUCTURES
EXCEEDING FIRE DEPARTMENT ACCESS REQUIREMENTS SHALL BE PROTECTED BY AN AUTOMATIC
SPRINKLER SYSTEM.

SPECIAL FIRE PROTECTION NOTE:

PROPERTY IS IN A SPECIAL FIRE PROTECTION AREA AND MUST MEET ALL REQUIREMENTS
FOR DEVELOPMENT WITHIN THE AREA.

HIGH FIRE HAZARD AREA NOTE:

THE LOTS SHOWN ON THIS MAP ARE IN A HIGH FIRE HAZARD AREA DUE TO
WILD LAND EXPOSURE.

NOTES:


"THE PRIVATE STREETS CONSTRUCTED WITHIN THIS MAP SHALL BE OWNED, OPERATED AND
MAINTAINED BY THE DEVELOPER, SUCCESSORS OR ASSIGNS. THE COUNTY OF ORANGE SHALL
HAVE NO RESPONSIBILITY THEREFORE UNLESS PURSUANT TO APPROPRIATE SECTIONS OF THE
STREETS AND HIGHWAYS CODE OF THE STATE OF CALIFORNIA. THE SAID PRIVATE STREETS
HAVE BEEN ACCEPTED INTO THE COUNTY ROAD SYSTEM BY APPROPRIATE RESOLUTION OF
THE ORANGE COUNTY BOARD OF SUPERVISORS."

SEE SHEET 2 FOR NOTARY ACKNOWLEDGMENTS AND SIGNATURE OMISSIONS.

SURVEYOR'S STATEMENT:

THIS MAP WAS PREPARED BY ME OR UNDER MY DIRECTION AND IS BASED UPON A FIELD
SURVEY IN CONFORMANCE WITH THE REQUIREMENTS OF THE SUBDIVISION MAP ACT AND
LOCAL ORDINANCES AT THE REQUEST OF RANCHO MISSION VIEJO, LLC ON MARCH 2002.
I HEREBY STATE THAT ALL MONUMENTS ARE OF THE CHARACTER AND OCCUPY THE
POSITIONS INDICATED, OR THAT THEY WILL BE SET IN SUCH POSITIONS; AND THAT SAID
MONUMENTS ARE SUFFICIENT TO ENABLE THE SURVEY TO BE RETRACED. I HEREBY STATE
THAT THIS FINAL MAP SUBSTANTIALLY CONFORMS TO THE CONDITIONALLY APPROVED TENTATIVE MAP.[Signature]
JAMES F. GILLEN
L.S. 5557
EXPIRATION DATE: 9/30/05

COUNTY SURVEYOR'S STATEMENT:

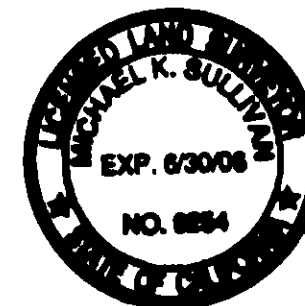I HEREBY STATE THAT I HAVE EXAMINED THIS MAP AND HAVE FOUND IT TO BE
SUBSTANTIALLY IN CONFORMANCE WITH THE TENTATIVE MAP AS FILED WITH, AMENDED AND
APPROVED BY THE ORANGE COUNTY SUBDIVISION COMMITTEE; THAT ALL PROVISIONS OF THE
SUBDIVISION MAP ACT AND COUNTY SUBDIVISION REGULATIONS HAVE BEEN COMPLIED WITH
AND I AM SATISFIED SAID MAP IS TECHNICALLY CORRECT.DATED THIS 11TH DAY OF AUGUST, 2003.[Signature]
JOHN CANAS, COUNTY SURVEYOR
LS 4408 EXPIRATION DATE: 09-30-05 BY: [Signature] MICHAEL K. SULLIVAN, DEPUTY
LS 6884 EXPIRES 8/30/08

COUNTY TREASURER-TAX COLLECTOR'S CERTIFICATE:

STATE OF CALIFORNIA)
COUNTY OF ORANGE)SSI HEREBY CERTIFY THAT ACCORDING TO THE RECORDS OF MY OFFICE THERE ARE NO LIENS
AGAINST THE LAND COVERED BY THIS MAP OR ANY PART THEREOF FOR UNPAID STATE,
COUNTY, MUNICIPAL OR LOCAL TAXES OR SPECIAL ASSESSMENTS COLLECTED AS TAXES,
EXCEPT TAXES OR SPECIAL ASSESSMENTS COLLECTED AS TAXES NOT YET PAYABLE.AND DO HEREBY CERTIFY TO THE RECORDER OF ORANGE COUNTY THAT THE PROVISIONS
OF THE SUBDIVISION MAP ACT HAVE BEEN COMPLIED WITH REGARDING DEPOSITS TO SECURE
PAYMENT OF TAXES OR SPECIAL ASSESSMENTS COLLECTED AS TAXES ON THE LAND
COVERED BY THIS MAP.DATED THIS 12TH DAY OF MARCH, 2003.JOHN M.W. MOORLACH
COUNTY TREASURER-TAX COLLECTOR BY: [Signature] DEPUTY TREASURER-TAX COLLECTOR

CLERK OF THE BOARD OF SUPERVISORS' CERTIFICATE:

STATE OF CALIFORNIA)
COUNTY OF ORANGE)SSI HEREBY CERTIFY THAT THIS MAP WAS PRESENTED FOR APPROVAL TO THE BOARD OF
SUPERVISORS OF ORANGE COUNTY AT A REGULAR MEETING THEREOF HELD ON THE 26TH DAY
OF August, 2003, AND THAT THEREUPON SAID BOARD DID, BY AN ORDER DULY PASSED
AND ENTERED, APPROVE SAID MAP.

AND DID ALSO ACCEPT ON BEHALF OF THE COUNTY OF ORANGE:

1. THE EASEMENTS FOR SIDEWALK PURPOSES AS DEDICATED.
2. THE EASEMENT FOR PUBLIC PEDESTRIAN PURPOSES AS DEDICATED.
3. THE EASEMENTS FOR EMERGENCY ACCESS PURPOSES OVER ALL OF LOTS AX, AY, AZ, BA, BB,
BC, BD, AND BE AS DEDICATED.
4. THE EASEMENT FOR STORM DRAIN PURPOSES AS DEDICATED.

AND DID ALSO APPROVE SUBJECT MAP PURSUANT TO THE PROVISIONS OF SECTION 66436(a) (3)
OF THE SUBDIVISION MAP ACT.DATED THIS 20TH DAY OF August, 2003.[Signature]
DARLENE J. BLOOM
CLERK OF THE BOARD OF SUPERVISORS

SHEET 2 OF 15 SHEETS

TRACT NO. 15986

ALL OF VESTING TENTATIVE
TRACT NO. 15986

IN THE UNINCORPORATED TERRITORY OF ORANGE COUNTY, CALIFORNIA

DATE OF SURVEY:
JANUARY 1999 &
MARCH 2002

SEPTEMBER 2002

JAMES F. GILLEN, L.S. 5557

HUITT-ZOLLARS

13 NUMBERED LOTS AND 58 LETTERED LOTS

120.329 ACRES

DMS LADERA, L.L.C.

STATE OF CALIFORNIA)
COUNTY OF ORANGE)SS

ON THIS 2nd DAY OF October, 2002, BEFORE ME,
Tina T. Baker, A NOTARY PUBLIC IN AND FOR SAID STATE,
PERSONALLY APPEARED Daniel T. Stealin AND
Stephen C. Schrank, PERSONALLY KNOWN TO ME OR PROVED TO ME
ON THE BASIS OF SATISFACTORY EVIDENCE TO BE THE PERSONS WHOSE NAMES
ARE SUBSCRIBED TO THE WITHIN INSTRUMENT AND ACKNOWLEDGED TO ME THAT
THEY EXECUTED THE SAME IN THEIR AUTHORIZED CAPACITIES, AND THAT BY THEIR
SIGNATURES ON THE INSTRUMENT THE PERSONS, OR THE ENTITY UPON BEHALF
OF WHICH THE PERSONS ACTED, EXECUTED THE INSTRUMENT.

WITNESS MY HAND:

MY COMMISSION EXPIRES 8-29-04Tina T. Baker
NOTARY PUBLIC IN AND FOR SAID STATEMY PRINCIPAL PLACE OF BUSINESS
IS IN Orange COUNTY.Tina T. Baker
PRINT NAME

SIGNATURE OMISSIONS:

IN ACCORDANCE WITH THE PROVISIONS OF SECTION 66436(a) (3) OF THE SUBDIVISION
MAP ACT, THE FOLLOWING SIGNATURES HAVE BEEN OMITTED:

1. SOUTHERN CALIFORNIA EDISON COMPANY, HOLDER OF AN EASEMENT FOR PUBLIC UTILITIES AND
INCIDENTAL PURPOSES RECORDED APRIL 16, 1965 IN BOOK 7485, PAGE 714 OF OFFICIAL RECORDS.
2. LADERA DEVELOPMENT COMPANY, L.L.C., HOLDER OF OIL, GAS, MINERAL, AND WATER RIGHTS
RECORDED DECEMBER 10, 1996 AS INSTRUMENT NO. 19960624029 OF OFFICIAL RECORDS.

SANTA MARGARITA WATER DISTRICT

STATE OF CALIFORNIA)
COUNTY OF ORANGE)SS

ON THIS 6th DAY OF February, 2003, BEFORE ME,
ANDREA M. EVANS, A NOTARY PUBLIC IN AND FOR SAID STATE,
PERSONALLY APPEARED DANIEL R. FERONS PERSONALLY KNOWN TO ME
OR PROVED TO ME ON THE BASIS OF SATISFACTORY EVIDENCE TO BE THE
PERSON WHOSE NAME IS SUBSCRIBED TO THE WITHIN INSTRUMENT AND ACKNOWLEDGED
TO ME THAT HE EXECUTED THE SAME IN HIS AUTHORIZED CAPACITY, AND THAT
BY HIS SIGNATURE ON THE INSTRUMENT THE PERSON, OR THE ENTITY UPON BEHALF
OF WHICH THE PERSON ACTED, EXECUTED THE INSTRUMENT.

WITNESS MY HAND:

MY COMMISSION EXPIRES 4-8-04Andrea M. Evans
NOTARY PUBLIC IN AND FOR SAID STATEMY PRINCIPAL PLACE OF BUSINESS
IS IN Orange COUNTY.ANDREA M. EVANS
PRINT NAME

EASEMENT NOTES:

- (A) INDICATES SIDEWALK EASEMENT DEDICATED TO THE COUNTY OF ORANGE.
- (B) INDICATES PUBLIC PEDESTRIAN EASEMENT DEDICATED TO THE COUNTY OF ORANGE.
- (C) INDICATES DRAINAGE EASEMENT DEDICATED TO THE SANTA MARGARITA WATER DISTRICT.
- (D) INDICATES SEWER, WATER, RECYCLED WATER AND ACCESS EASEMENT DEDICATED TO THE SANTA
MARGARITA WATER DISTRICT.
- (E) INDICATES STORM DRAIN EASEMENT DEDICATED TO THE COUNTY OF ORANGE.

NOTE:

"THE COUNTY OF ORANGE, ITS SUCCESSORS OR ASSIGNS, HEREBY RECOGNIZES SOUTHERN
CALIFORNIA EDISON COMPANY'S PRIOR EASEMENT RIGHTS IN AND TO THE ABOVE DESCRIBED
REAL PROPERTY AND AGREES NEVER TO ASSAIL OR RESIST SOUTHERN CALIFORNIA
EDISON'S INTEREST THEREIN. THE COUNTY OF ORANGE ALSO HEREBY AGREES THAT
PRIOR TO ANY CONSTRUCTION OF ITS STORM DRAIN FACILITY, THE COUNTY OF
ORANGE, ITS SUCCESSORS OR ASSIGNS, IS REQUIRED TO SECURE WRITTEN
APPROVAL FROM SOUTHERN CALIFORNIA EDISON COMPANY. CONTACT FOR SUCH
WRITTEN APPROVAL TO BE OBTAINED BY THE MANAGER OF TRANSMISSION. SAID
MANAGER CAN BE REACHED AT (714) 973-5409".

849 3

SHEET 3 OF 15 SHEETS

TRACT NO. 15986

IN THE UNINCORPORATED TERRITORY OF ORANGE COUNTY, CALIFORNIA

SEPTEMBER 2002

JAMES F. GILLEN, L.S. 5557

HUITT-ZOLIARS

13 NUMBERED LOTS AND 58 LETTERED LOTS

120.329 ACRES


ALL OF VESTING TENTATIVE
TRACT NO. 15986

DATE OF SURVEY:
JANUARY 1999 &
MARCH 2002

SCALE: 1"=600'

MONUMENT NOTES:

- INDICATES FOUND MONUMENT AS NOTED.
- INDICATES FOUND 2" I.P. TAGGED "P.L.S. 5557" PER TRACT NO. 15987, M.M. 839/1-18.
- △ INDICATES LOCATION OF 1" I.P. TAGGED "P.L.S. 5557" OR SPIKE & WASHER STAMPED "P.L.S. 5557" OR LEAD, TACK & TAG "P.L.S. 5557" TO BE SET PER TRACT NO. 15987, M.M. 839/1-18, UNLESS OTHERWISE NOTED.
- INDICATES LOCATION OF 2" I.P. TAGGED "P.L.S. 5557" OR SPIKE & WASHER STAMPED "P.L.S. 5557" OR LEAD, TACK & TAG "P.L.S. 5557" TO BE SET WITHIN 90 DAYS AFTER ACCEPTANCE OF IMPROVEMENTS.
- ⊙ INDICATES LOCATION OF OCS WELL MONUMENT WITH A 2" BRASS DISK STAMPED "PLS 5557" TO BE SET PER TRACT NO. 15987, M.M. 839/1-18.
- INDICATES LOCATION OF 1" I.P. TAGGED "P.L.S. 5557" OR SPIKE & WASHER STAMPED "P.L.S. 5557" OR LEAD, TACK & TAG "P.L.S. 5557" TO BE SET WITHIN 90 DAYS AFTER ACCEPTANCE OF IMPROVEMENTS.
- 2" I.P. TAGGED "P.L.S. 5557" OR SPIKE & WASHER STAMPED "P.L.S. 5557" OR LEAD, TACK & TAG "P.L.S. 5557" TO BE SET AT ALL TRACT BOUNDARY CORNERS WITHIN 90 DAYS AFTER ACCEPTANCE OF IMPROVEMENTS, UNLESS OTHERWISE NOTED. THE NORTHERLY TRACT BOUNDARY LINE CONTIGUOUS WITH TRACT NO. 15987 WILL BE MONUMENTED PER TRACT NO. 15987, M.M. 839/1-18.
- [A] FOUND 2 1/2" IRON PIPE W/2" OCS BRASS CAP STAMPED "GPS 1448 9-95" PER TRACT NO. 16203, M.M. 826/8-20 AND RECORDS ON FILE IN THE ORANGE COUNTY SURVEYORS OFFICE.
- [B] FOUND 2 1/2" IRON PIPE W/2" OCS BRASS CAP STAMPED "GPS 1417 9-95" PER TRACT NO. 16203, M.M. 826/8-20 AND RECORDS ON FILE IN THE ORANGE COUNTY SURVEYORS OFFICE.
- NO MONUMENTATION TO BE SET AT BC'S AND EC'S OF STREET RIGHT OF WAY LINES, UNLESS OTHERWISE SHOWN. NO ADDITIONAL MONUMENTS TO BE SET AT THE INTERIOR LOT CORNERS, OTHER THAN THOSE SHOWN.

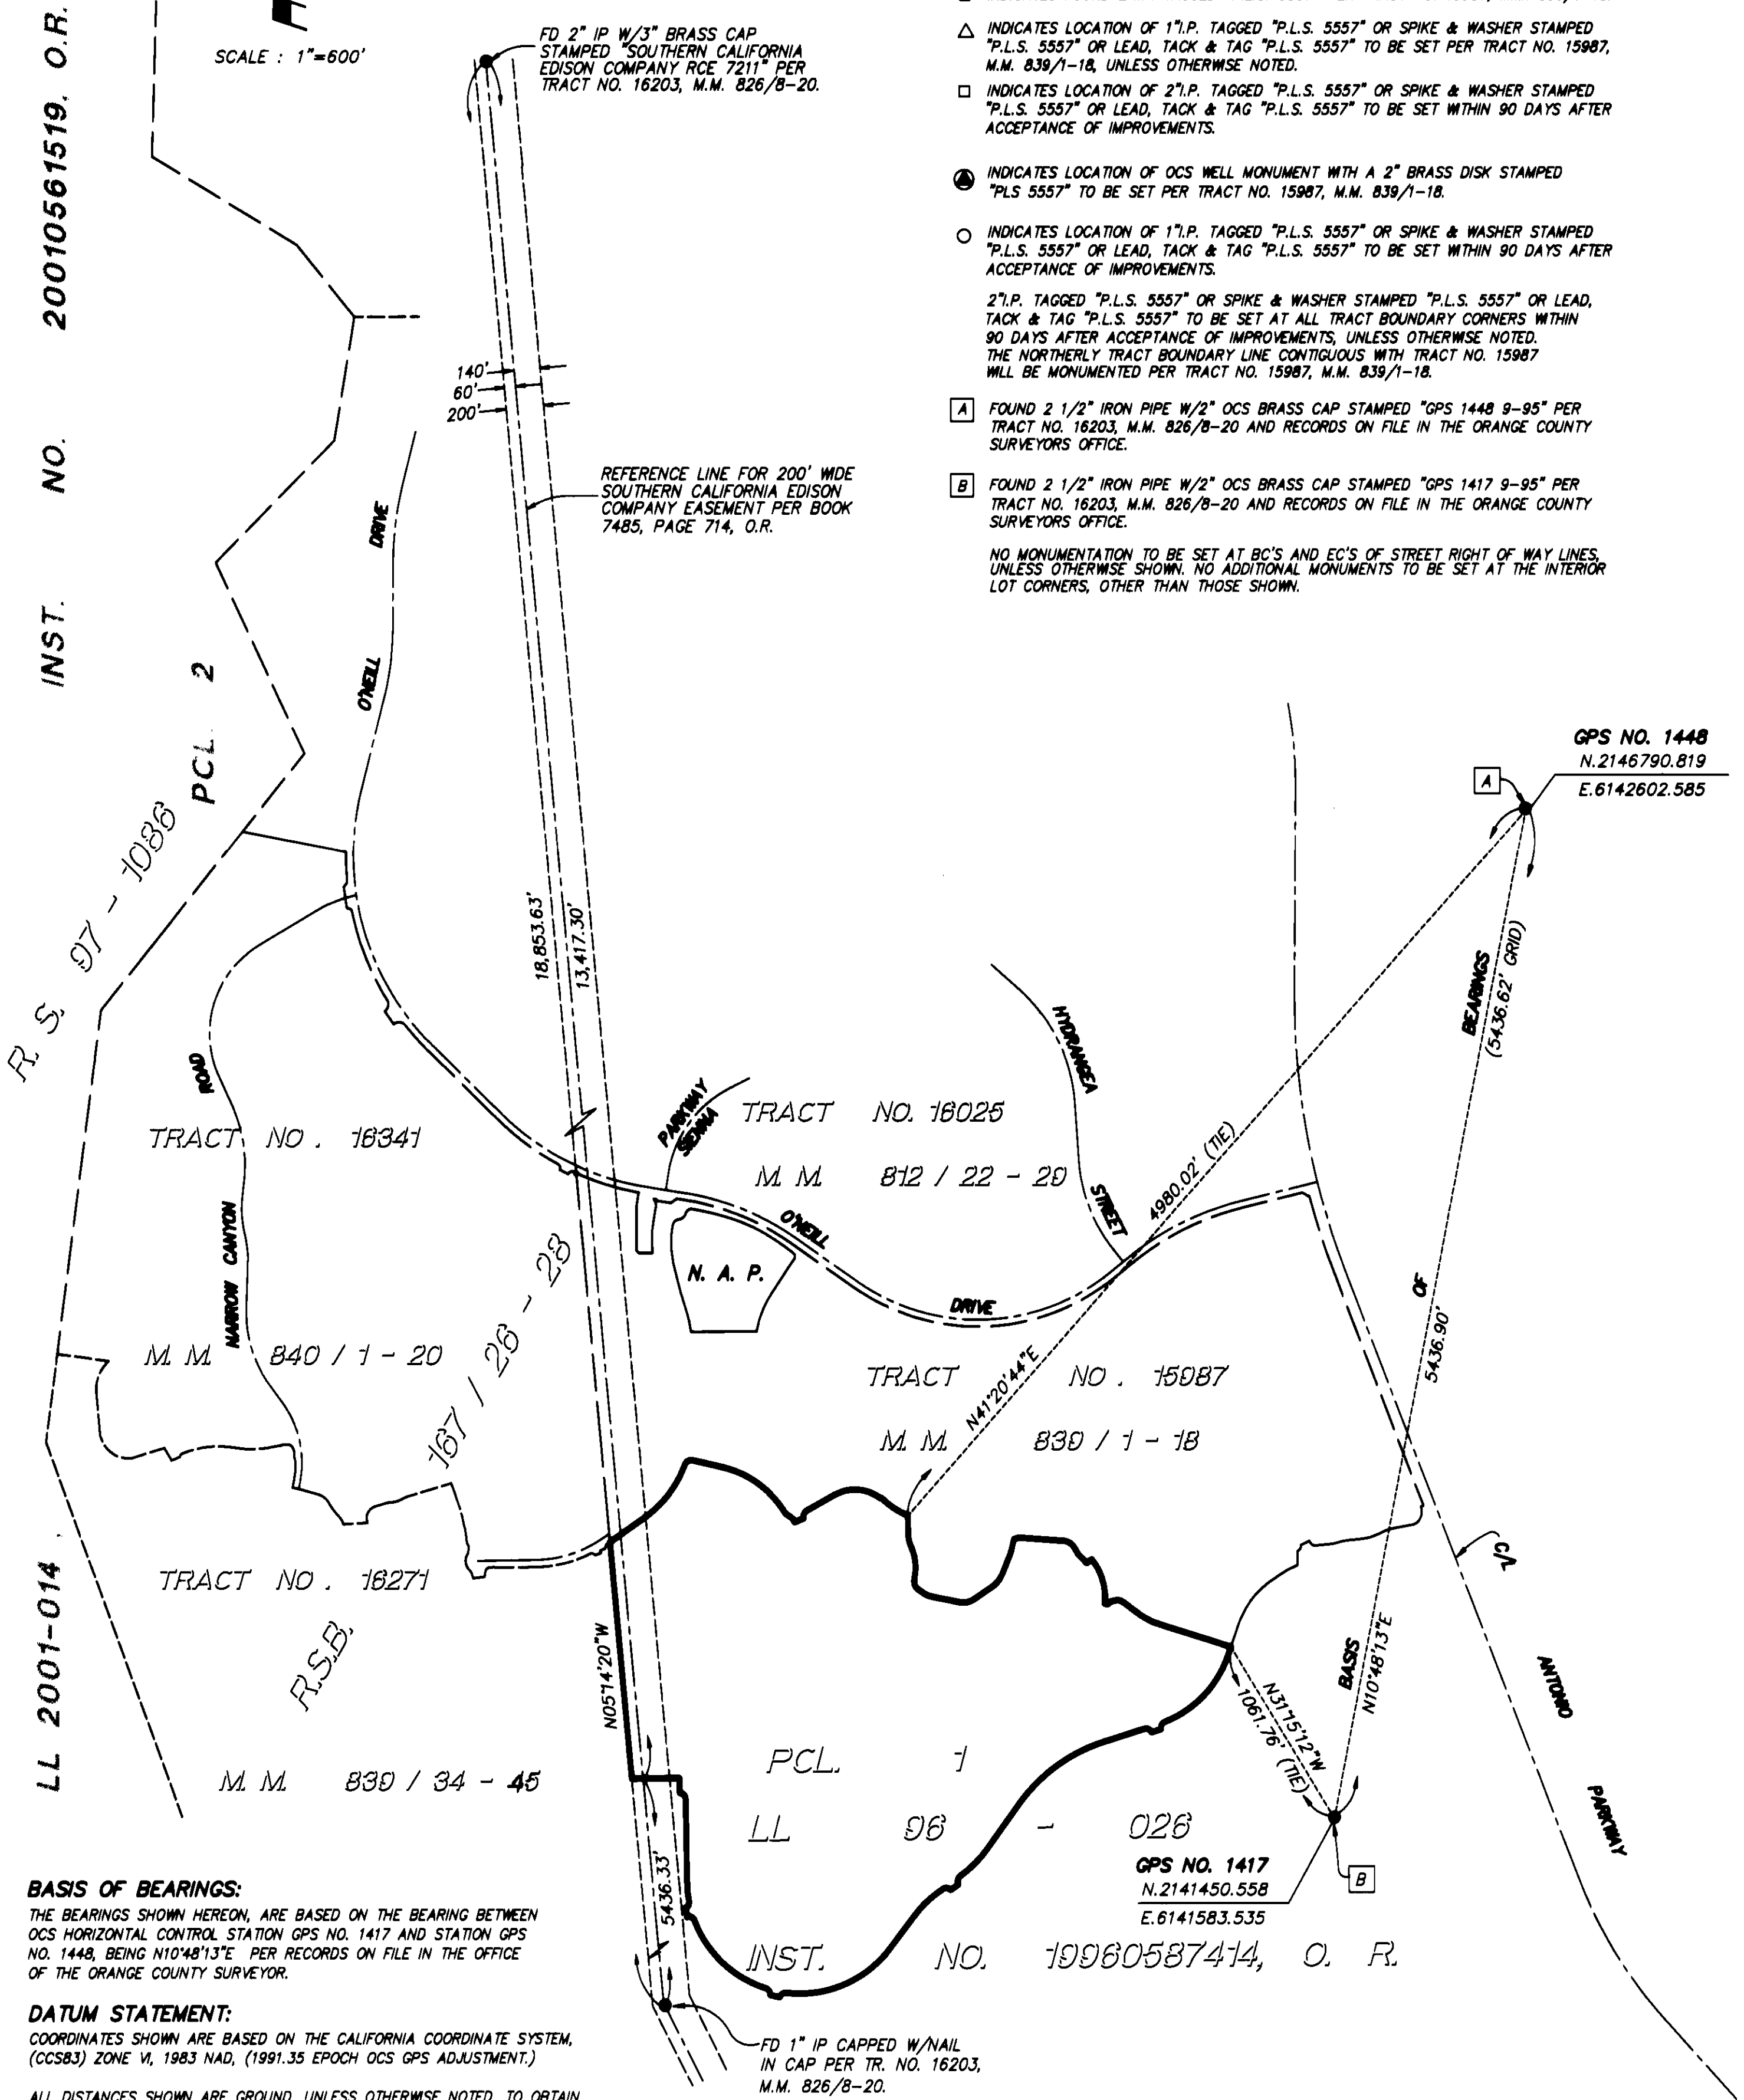

BASIS OF BEARINGS:

THE BEARINGS SHOWN HEREON, ARE BASED ON THE BEARING BETWEEN OCS HORIZONTAL CONTROL STATION GPS NO. 1417 AND STATION GPS NO. 1448, BEING N10°48'13"E PER RECORDS ON FILE IN THE OFFICE OF THE ORANGE COUNTY SURVEYOR.

DATUM STATEMENT:

COORDINATES SHOWN ARE BASED ON THE CALIFORNIA COORDINATE SYSTEM, (CCS83) ZONE VI, 1983 NAD, (1991.35 EPOCH OCS GPS ADJUSTMENT.)

ALL DISTANCES SHOWN ARE GROUND, UNLESS OTHERWISE NOTED. TO OBTAIN A GRID DISTANCE, MULTIPLY THE GROUND DISTANCE BY 0.999948295.

NOTE:

SEE SHEET 4 FOR SHEET INDEX MAP.

OCS GPS BOUNDARY CONTROL MAP

G:\10036755\TM\TR15986\TM15986.3.DWG

849 3

849 4

SHEET 4 OF 15 SHEETS

TRACT NO. 15986

ALL OF VESTING TENTATIVE
TRACT NO. 15986

IN THE UNINCORPORATED TERRITORY OF ORANGE COUNTY, CALIFORNIA

SEPTEMBER 2002



JAMES F. GILLEN, L.S. 5557

DATE OF SURVEY:
JANUARY 1999 &
MARCH 2002

HUITT-ZOLLARS

13 NUMBERED LOTS AND 58 LETTERED LOTS

120.329 ACRES

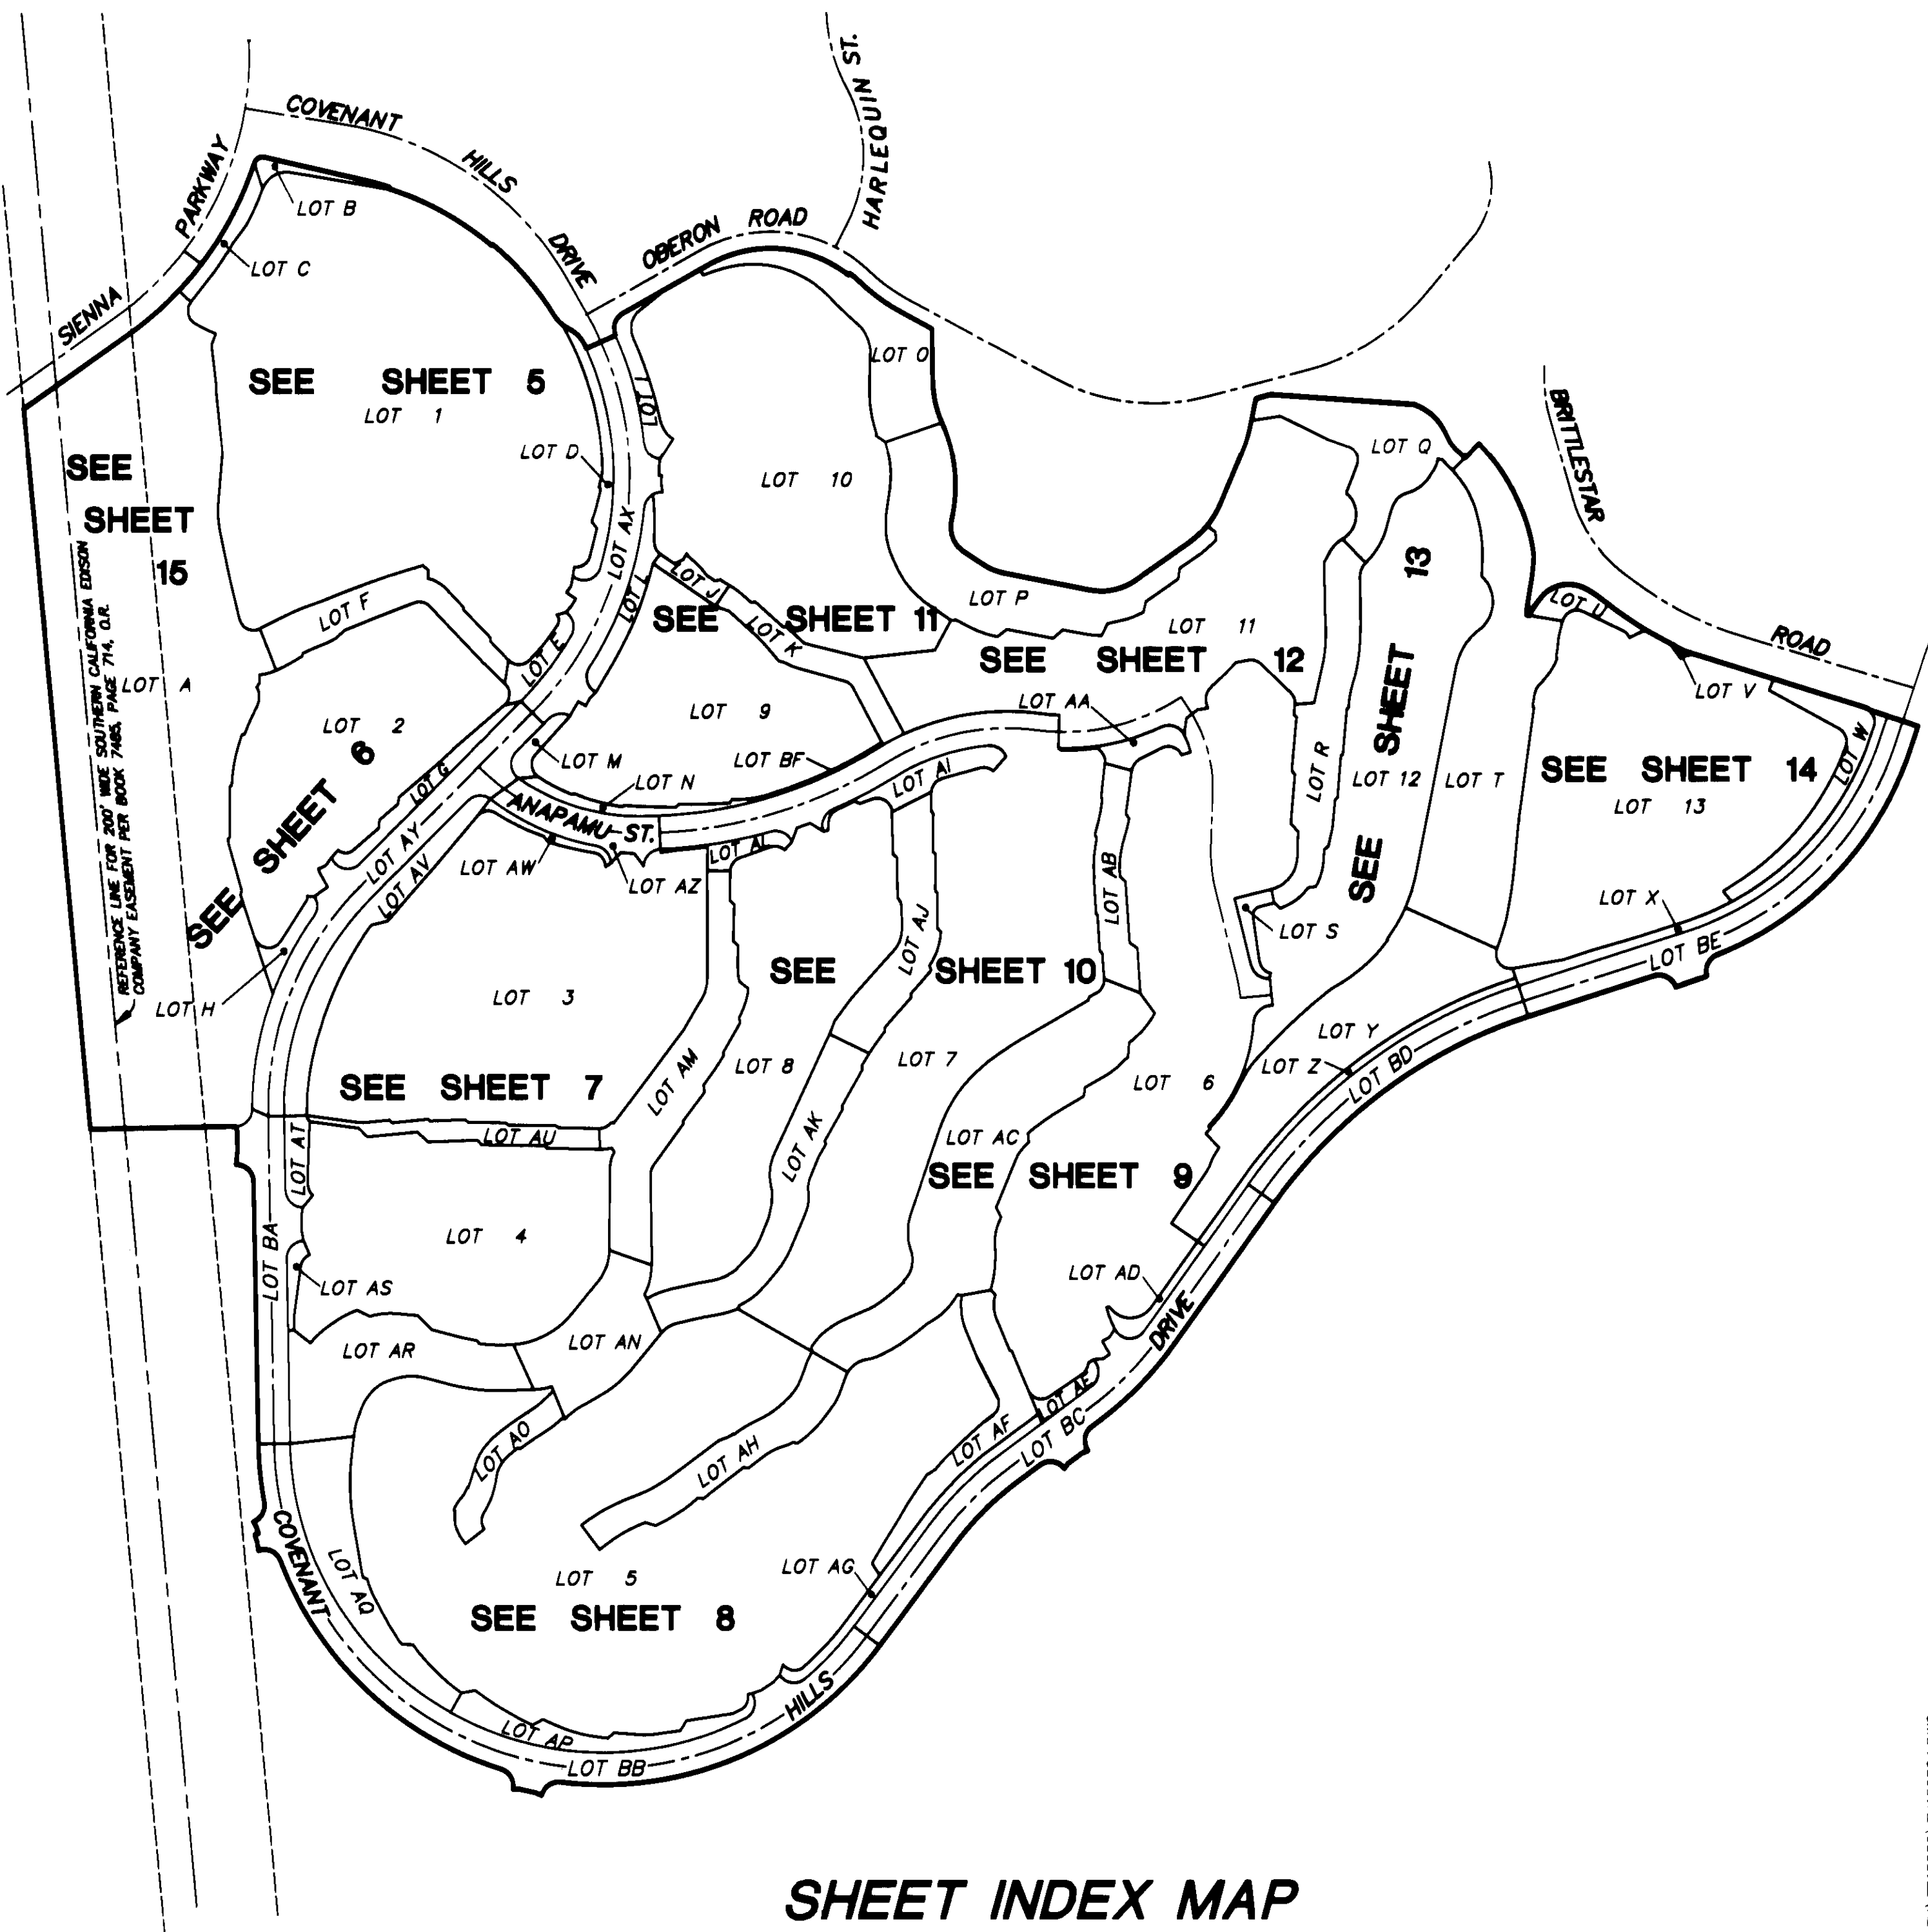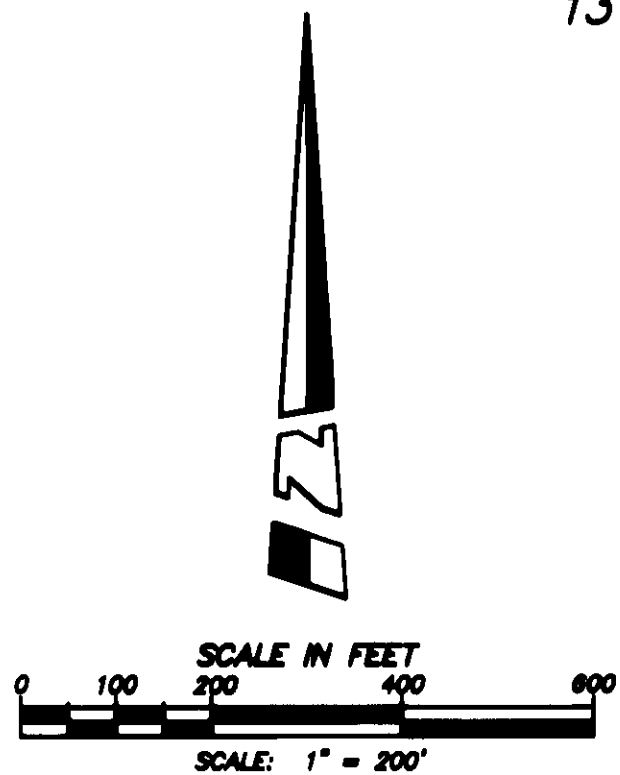

SHEET INDEX MAP

G:\10036762\TM\15986\159864.DWG

849 4

849 5

SHEET 5 OF 15 SHEETS

ALL OF VESTING TENTATIVE
TRACT NO. 15986

TRACT NO. 15986
IN THE UNINCORPORATED TERRITORY OF ORANGE COUNTY, CALIFORNIA
SEPTEMBER 2002



JAMES F. GILLEN, L.S. 5557

HUITT-ZOLLARS

13 NUMBERED LOTS AND 58 LETTERED LOTS

120.329 ACRES

DATE OF SURVEY:
JANUARY 1999 &
MARCH 2002

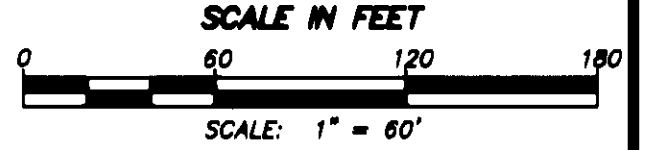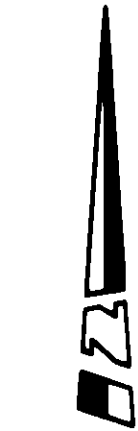


COURSE DATA
(THIS SHEET ONLY)

- 1 (N26°15'13"E PRC)
- 2 (N66°02'01"E RAD 56.00')
- 3 (N66°02'01"E RAD 28.00')
- 4 (N44°55'55"W RAD 56.00')
- 5 (N64°37'09"W PCC)
- 6 (N68°19'36"W PRC)
- 7 (N58°56'57"W PCC)
- 8 (N74°37'42"W RAD R=180.00'
N40°29'13"W RAD R=568.00')

CURVE DATA
(THIS SHEET ONLY)

- 1 (Δ = 31°43'48" R = 80.00' L = 33.23')
- 2 (Δ = 39°05'58" R = 80.00' L = 40.95')
- 3 (Δ = 00°40'49" R = 552.00' L = 6.55')
- 4 (Δ = 05°18'21" R = 580.00' L = 53.71')
- 5 (Δ = 84°41'39" R = 30.00' L = 44.35')
- 6 (Δ = 03°29'45" R = 425.00' L = 25.93')
- 7 (Δ = 83°33'08" R = 25.00' L = 36.80')
- 8 (Δ = 112°33'46" R = 30.00' L = 58.94')
- 9 (Δ = 04°33'23" R = 250.00' L = 19.88')
- 10 (Δ = 06°53'18" R = 30.00' L = 45.49')
- 11 (Δ = 74°36'25" R = 15.00' L = 19.62')
- 12 (Δ = 91°05'21" R = 25.00' L = 39.75')
- 13 (Δ = 05°29'15" R = 25.00' L = 2.39')
- 14 (Δ = 11°16'57" R = 588.00' L = 115.79')
- 15 (Δ = 20°36'38" R = 160.00' L = 57.56')

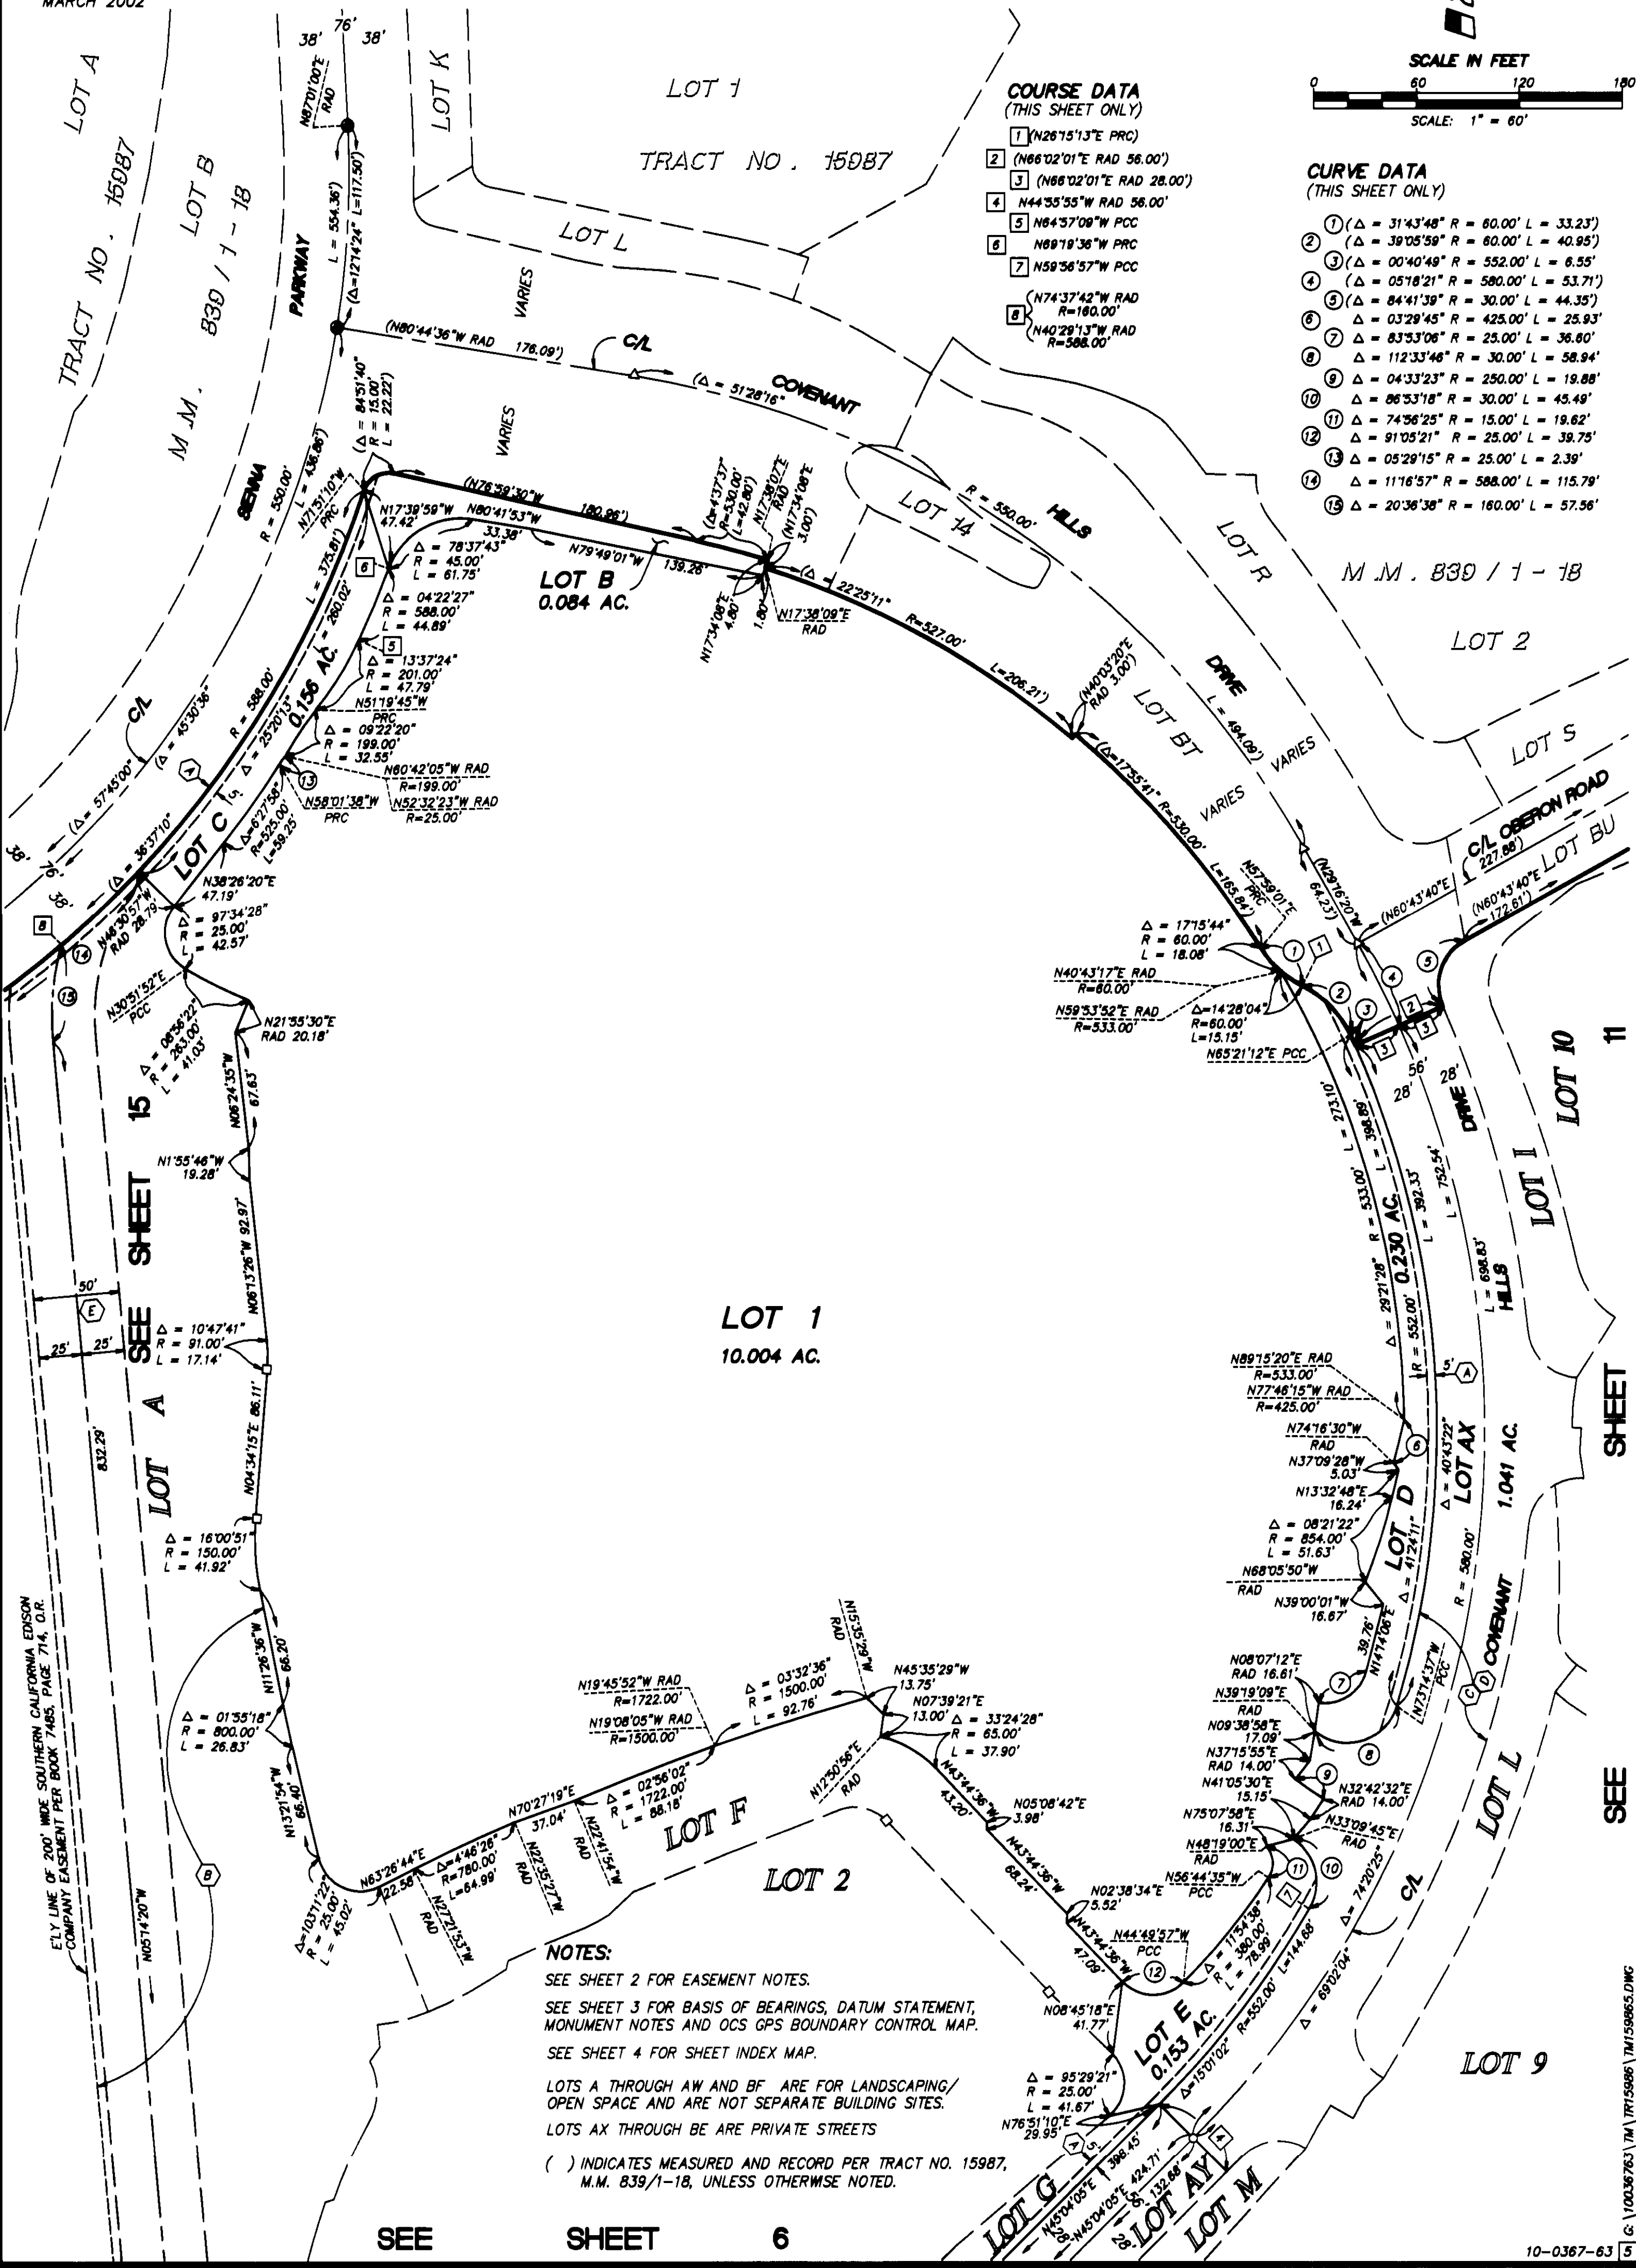

LOT 1
10.004 AC.

NOTES:
SEE SHEET 2 FOR EASEMENT NOTES.
SEE SHEET 3 FOR BASIS OF BEARINGS, DATUM STATEMENT, MONUMENT NOTES AND OCS GPS BOUNDARY CONTROL MAP.
SEE SHEET 4 FOR SHEET INDEX MAP.
LOTS A THROUGH AW AND BF ARE FOR LANDSCAPING/ OPEN SPACE AND ARE NOT SEPARATE BUILDING SITES.
LOTS AX THROUGH BE ARE PRIVATE STREETS
() INDICATES MEASURED AND RECORD PER TRACT NO. 15987, M.M. 839/1-18, UNLESS OTHERWISE NOTED.

SEE SHEET 6

SEE SHEET 11

SEE SHEET 15

849 5

849 6

SHEET 6 OF 15 SHEETS

ALL OF VESTING TENTATIVE
TRACT NO. 15986

TRACT NO. 15986

IN THE UNINCORPORATED TERRITORY OF ORANGE COUNTY, CALIFORNIA
SEPTEMBER 2002

JAMES F. GILLEN, L.S. 5557

HUITT-ZOLLARS

13 NUMBERED LOTS AND 58 LETTERED LOTS

120.329 ACRES

DATE OF SURVEY:
JANUARY 1999 &
MARCH 2002

SEE

SHEET



15

SEE

SHEET

5

SCALE IN FEET

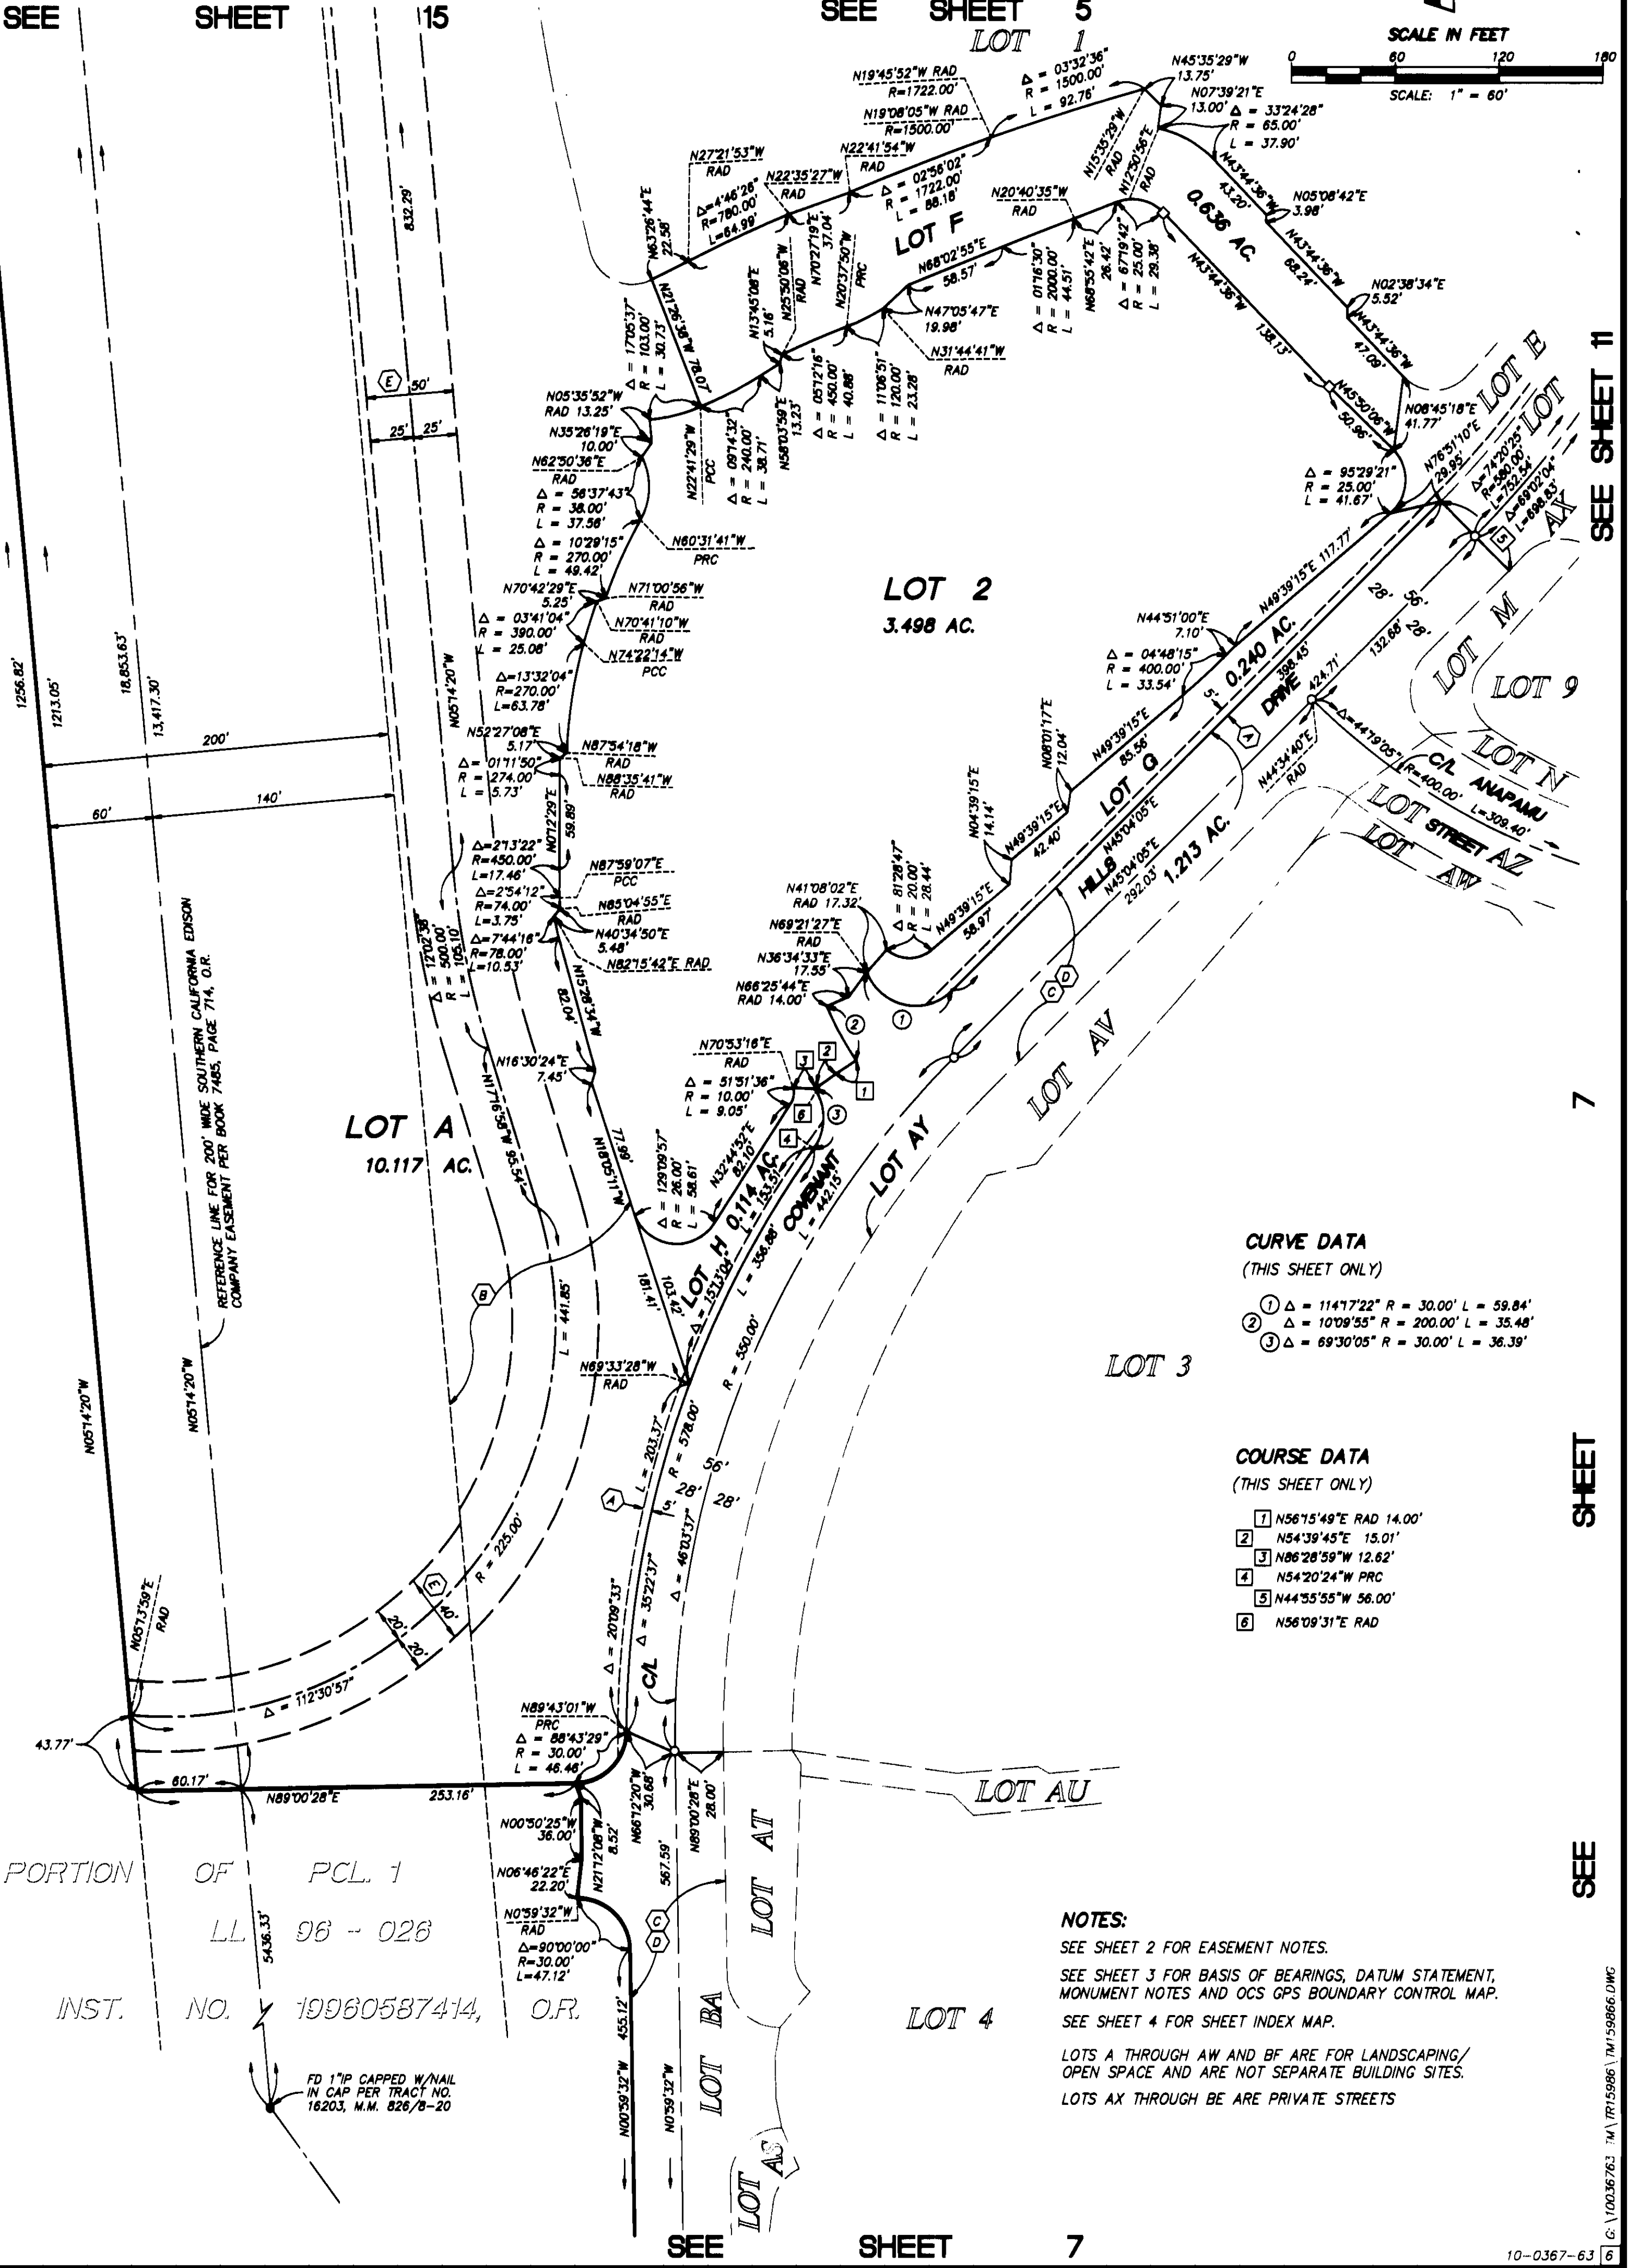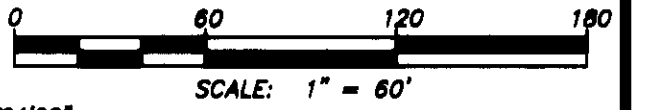

CURVE DATA

(THIS SHEET ONLY)

- ① $\Delta = 114^{\circ}17'22''$ R = 30.00' L = 59.84'
- ② $\Delta = 10^{\circ}09'55''$ R = 200.00' L = 35.48'
- ③ $\Delta = 89^{\circ}30'05''$ R = 30.00' L = 36.39'

COURSE DATA

(THIS SHEET ONLY)

- ① N56°15'49"E RAD 14.00'
- ② N54°39'45"E 15.01'
- ③ N86°28'59"W 12.62'
- ④ N54°20'24"W PRC
- ⑤ N44°55'55"W 56.00'
- ⑥ N56°09'31"E RAD

NOTES:

- SEE SHEET 2 FOR EASEMENT NOTES.
- SEE SHEET 3 FOR BASIS OF BEARINGS, DATUM STATEMENT, MONUMENT NOTES AND OCS GPS BOUNDARY CONTROL MAP.
- SEE SHEET 4 FOR SHEET INDEX MAP.
- LOTS A THROUGH AW AND BF ARE FOR LANDSCAPING/ OPEN SPACE AND ARE NOT SEPARATE BUILDING SITES.
- LOTS AX THROUGH BE ARE PRIVATE STREETS

SEE SHEET 11

7

SHEET

SEE

7

G:\10036763\TM\15986.DWG

849 7

SHEET 7 OF 15 SHEETS

ALL OF VESTING TENTATIVE
TRACT NO. 15986

TRACT NO. 15986
IN THE UNINCORPORATED TERRITORY OF ORANGE COUNTY, CALIFORNIA
SEPTEMBER 2002 JAMES F. GILLEN, L.S. 5557

DATE OF SURVEY:
JANUARY 1999 &
MARCH 2002

HUITT-ZOLLARS

13 NUMBERED LOTS AND 58 LETTERED LOTS

120.329 ACRES

SEE SHEET 6

CURVE DATA

(THIS SHEET ONLY)

- 1 $\Delta = 82^\circ 14' 06''$ R = 30.00' L = 43.06'
- 2 $\Delta = 82^\circ 10' 22''$ R = 25.00' L = 35.85'
- 3 $\Delta = 03^\circ 51' 15''$ R = 349.00' L = 23.48'
- 4 $\Delta = 82^\circ 51' 50''$ R = 25.00' L = 36.16'
- 5 $\Delta = 82^\circ 18' 35''$ R = 30.00' L = 43.10'
- 6 $\Delta = 90^\circ 00' 00''$ R = 30.00' L = 47.12'
- 7 $\Delta = 09^\circ 39' 22''$ R = 603.00' L = 101.62'
- 8 $\Delta = 13^\circ 17' 18''$ R = 849.00' L = 196.90'
- 9 $\Delta = 03^\circ 36' 44''$ R = 852.00' L = 53.71'
- 10 $\Delta = 85^\circ 20' 28''$ R = 30.00' L = 44.68'
- 11 $\Delta = 13^\circ 14' 44''$ R = 849.00' L = 196.27'
- 12 $\Delta = 00^\circ 02' 34''$ R = 849.00' L = 0.63'
- 13 $\Delta = 02^\circ 35' 55''$ R = 820.00' L = 37.19'

COURSE DATA

(THIS SHEET ONLY)

- 1 N10°07'40"E PRC
- 2 N37°22'40"E PRC
- 3 N89°00'28"E 56.00'
- 4 N89°00'28"E 11.00'
- 5 N51°55'56"W 35.37'
- 6 N0°22'13"W 5.05'
- 7 N02°17'48"W PRC
- 8 N10°57'14"W 5.85'
- 9 N02°20'20"W RAD 58.00'

NOTES:


SEE SHEET 2 FOR EASEMENT NOTES.

SEE SHEET 3 FOR BASIS OF BEARINGS, DATUM STATEMENT,
MONUMENT NOTES AND OCS GPS BOUNDARY CONTROL MAP.

SEE SHEET 4 FOR SHEET INDEX MAP.

LOTS A THROUGH AW AND BF ARE FOR LANDSCAPING/
OPEN SPACE AND ARE NOT SEPARATE BUILDING SITES.

LOTS AX THROUGH BE ARE PRIVATE STREETS.

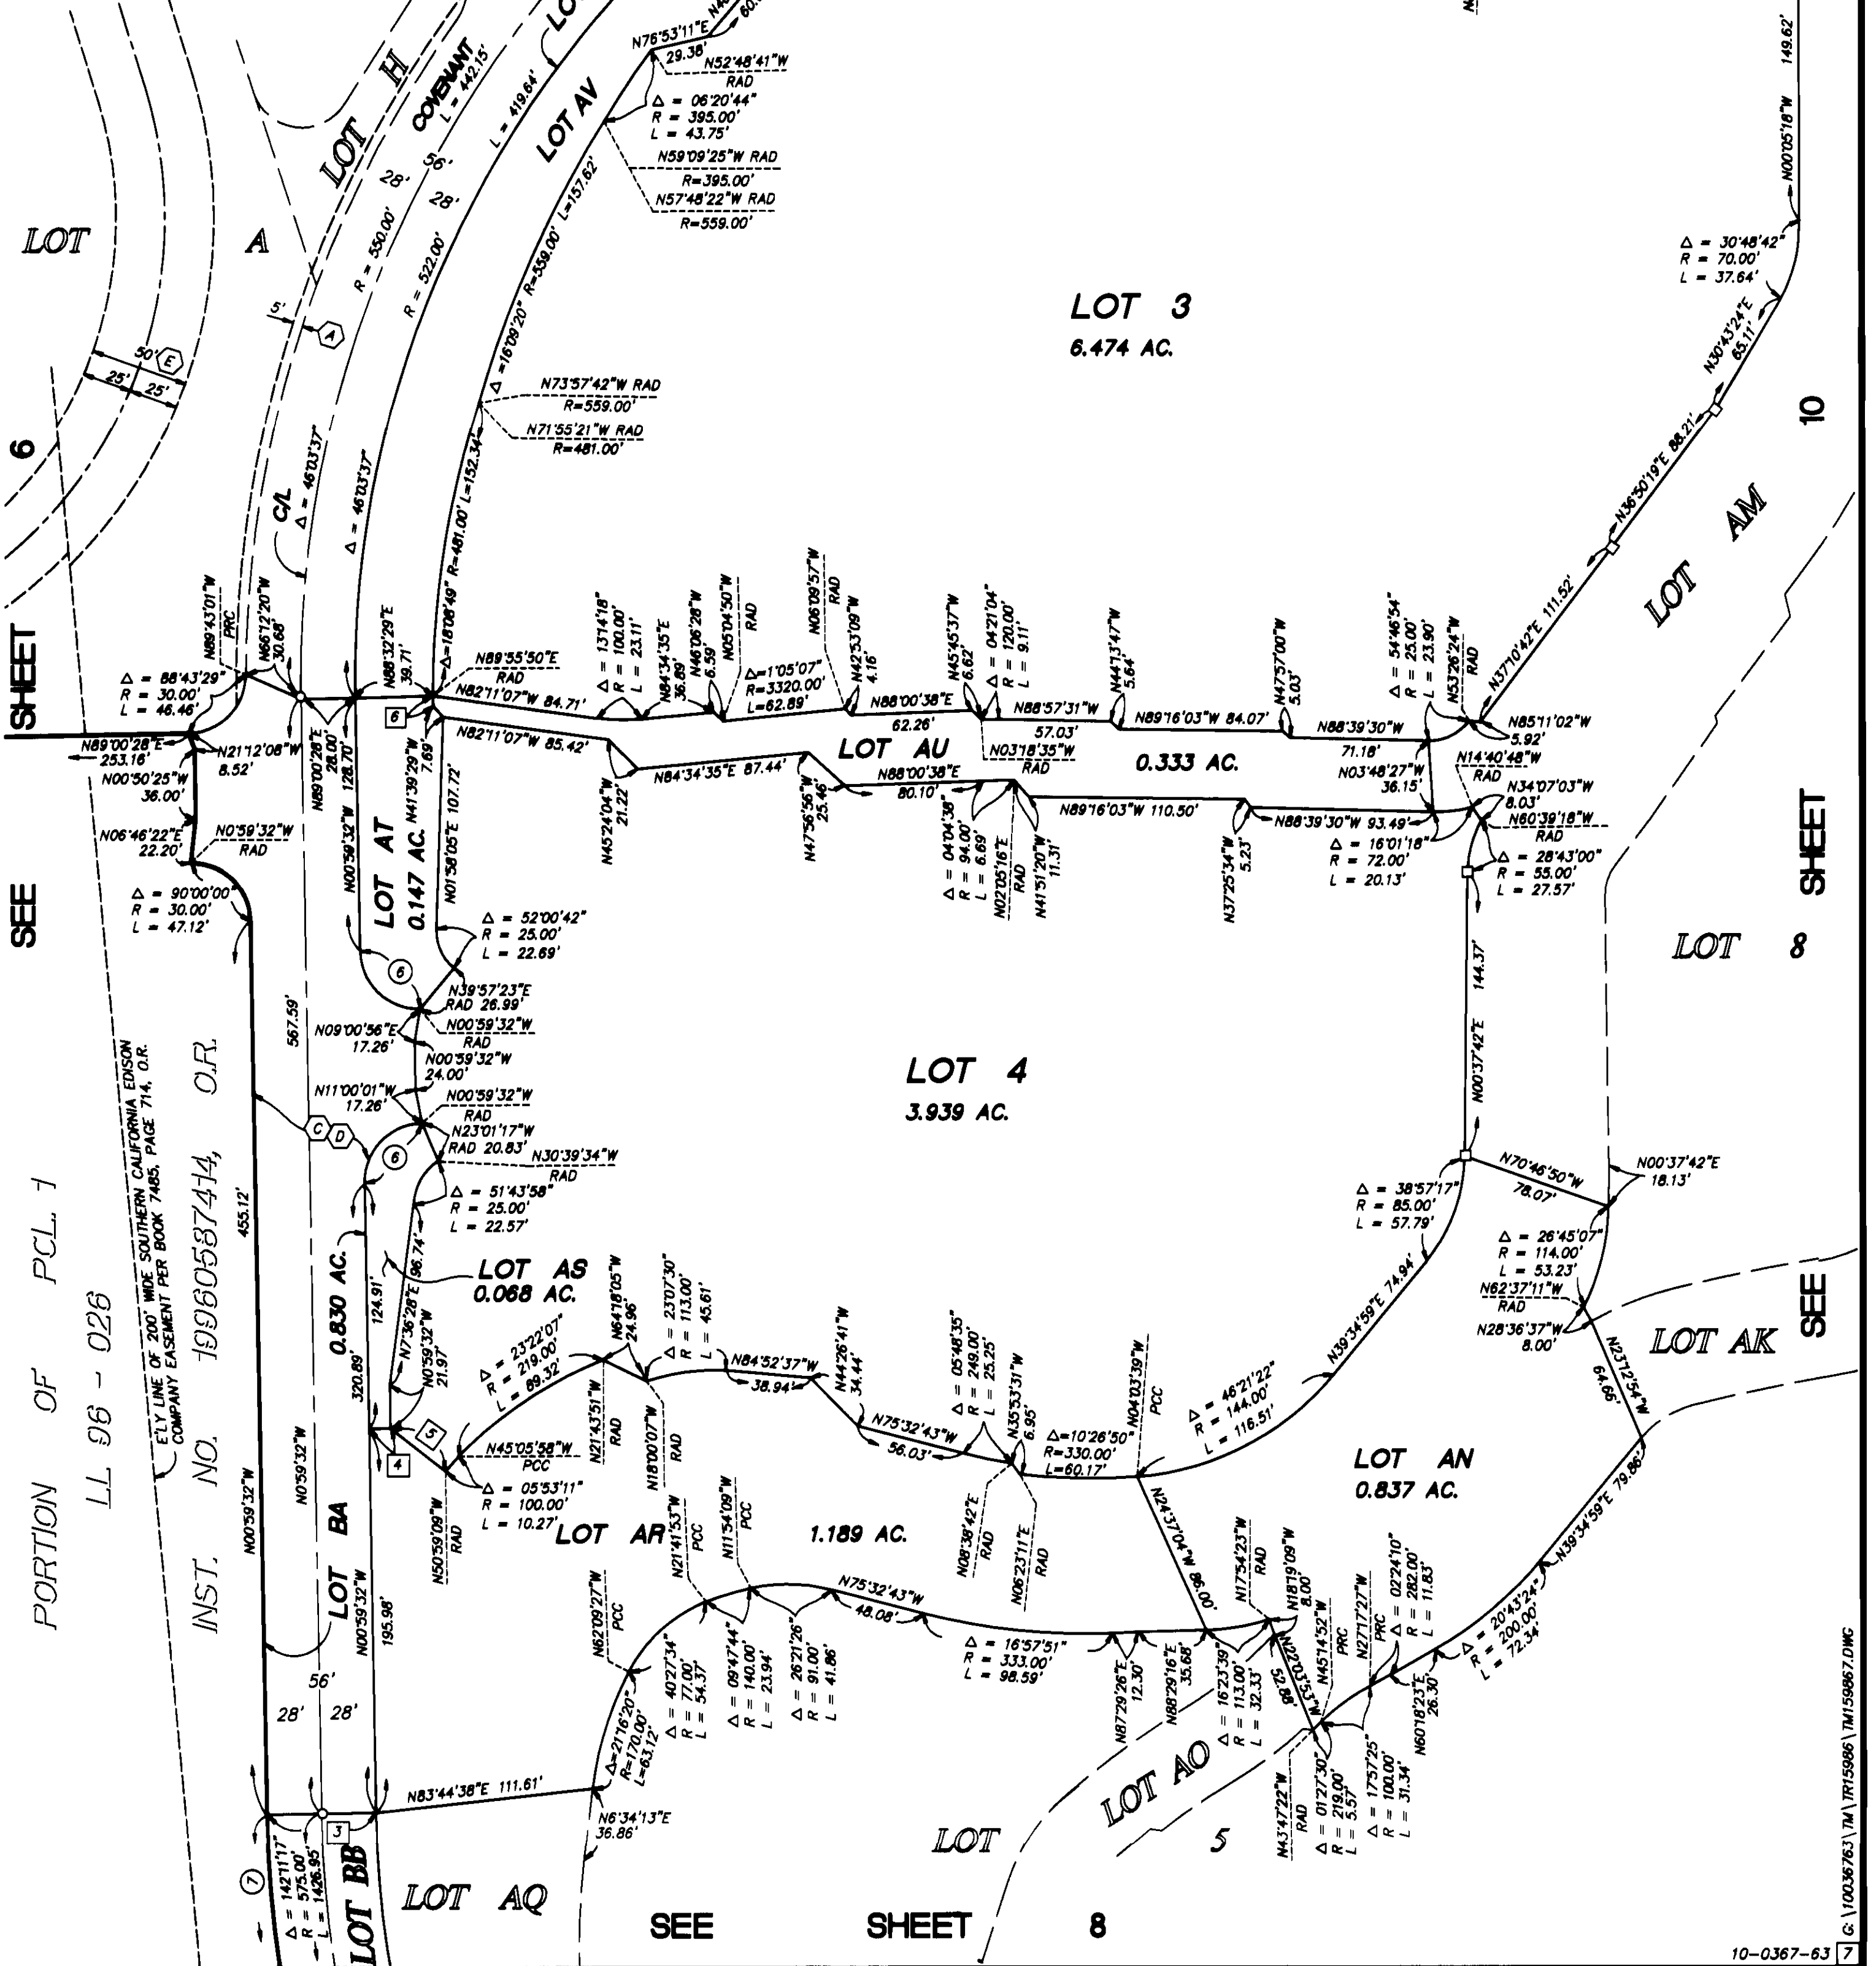

L bng

849 8

SHEET 8 OF 15 SHEETS

TRACT NO. 15986

IN THE UNINCORPORATED TERRITORY OF ORANGE COUNTY, CALIFORNIA

SEPTEMBER 2002

JAMES F. GILLEN, L.S. 5557


ALL OF VESTING TENTATIVE
TRACT NO. 15986

DATE OF SURVEY:
JANUARY 1999 &
MARCH 2002

HUITT-ZOLLARS

13 NUMBERED LOTS AND 58 LETTERED LOTS

120.329 ACRES

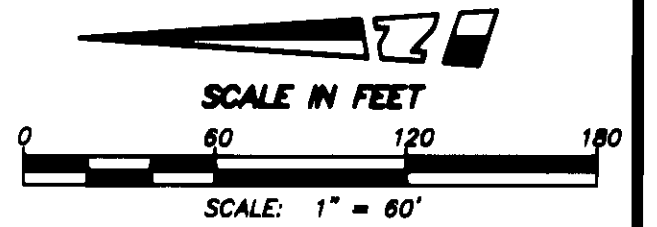


NOTES:

SEE SHEET 2 FOR EASEMENT NOTES.

SEE SHEET 3 FOR BASIS OF BEARINGS, DATUM STATEMENT,
MONUMENT NOTES AND OCS GPS BOUNDARY CONTROL MAP.

SEE SHEET 4 FOR SHEET INDEX MAP.

LOTS A THROUGH AW AND BF ARE FOR LANDSCAPING/
OPEN SPACE AND ARE NOT SEPARATE BUILDING SITES.
LOTS AX THROUGH BE ARE PRIVATE STREETS

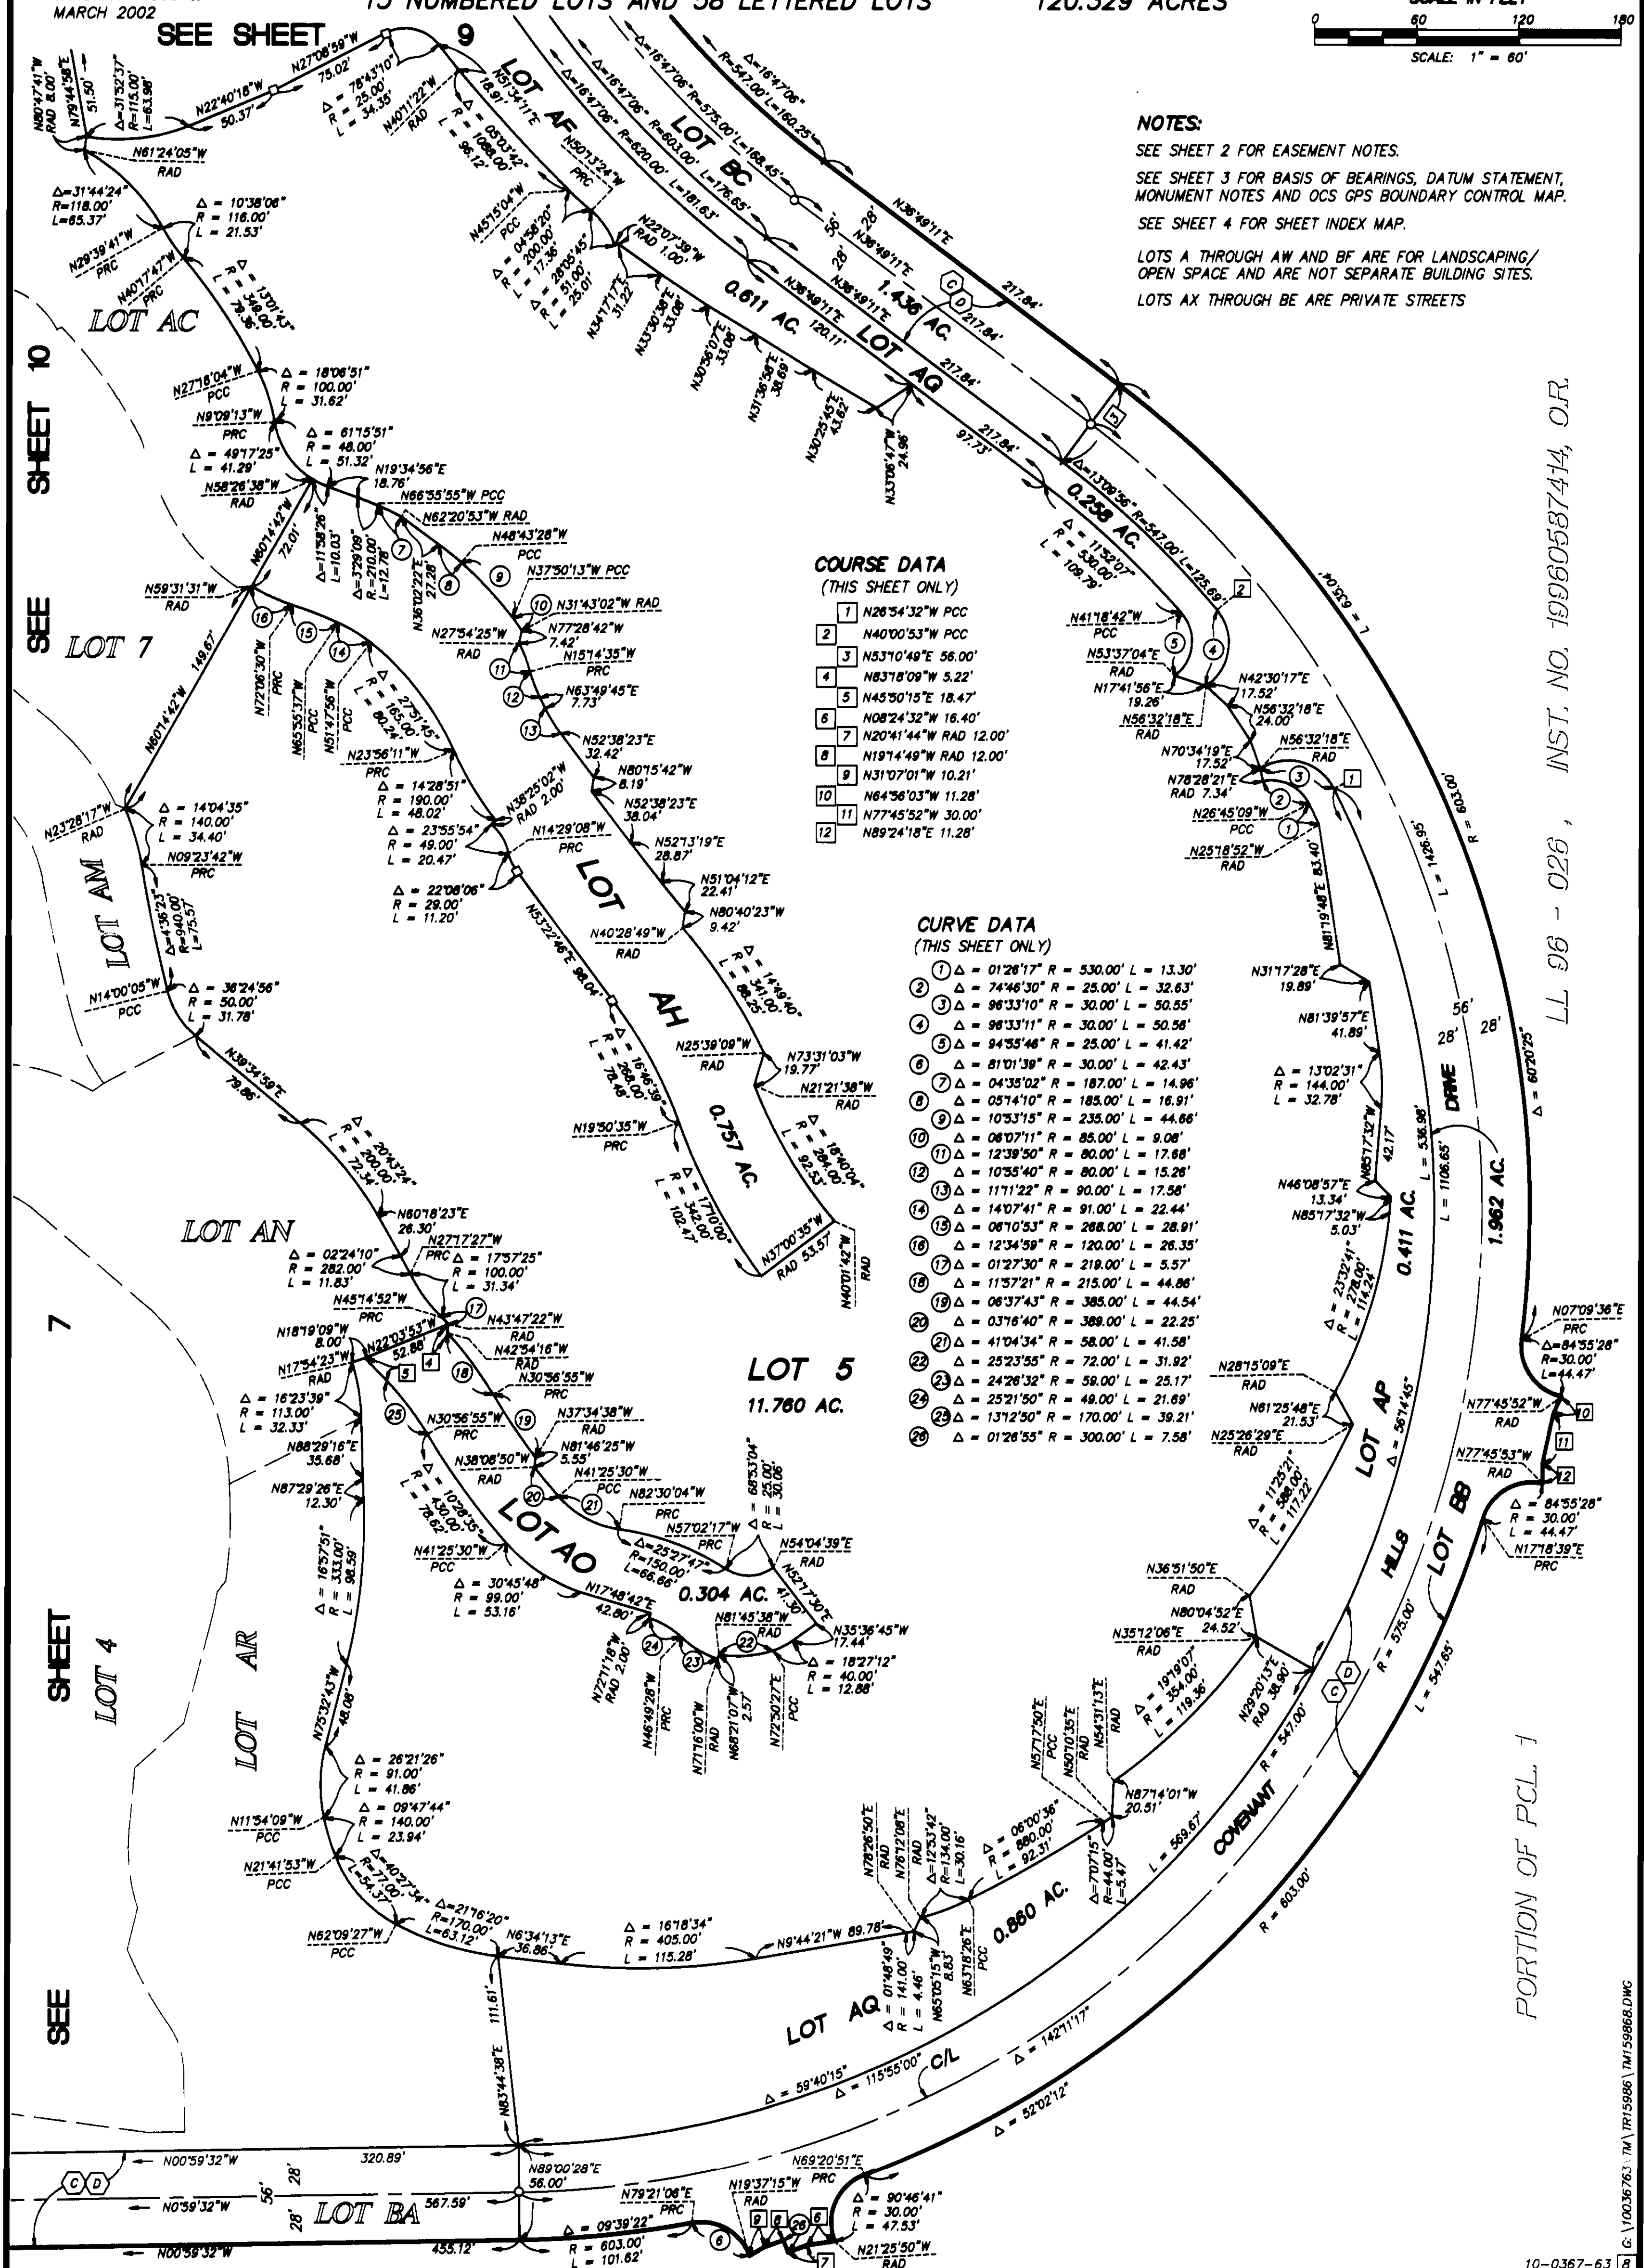

COURSE DATA (THIS SHEET ONLY)

- 1 N26°54'32"W PCC
- 2 N40°00'53"W PCC
- 3 N53°10'49"E 56.00'
- 4 N83°18'09"W 5.22'
- 5 N45°50'15"E 18.47'
- 6 N08°24'32"W 16.40'
- 7 N20°41'44"W RAD 12.00'
- 8 N19°14'49"W RAD 12.00'
- 9 N31°07'01"W 10.21'
- 10 N64°56'03"W 11.28'
- 11 N77°45'52"W 30.00'
- 12 N89°24'18"E 11.28'

CURVE DATA (THIS SHEET ONLY)

- 1 Δ = 01°28'17" R = 530.00' L = 13.30'
- 2 Δ = 74°46'30" R = 25.00' L = 32.63'
- 3 Δ = 96°33'10" R = 30.00' L = 50.55'
- 4 Δ = 96°33'11" R = 30.00' L = 50.58'
- 5 Δ = 94°55'48" R = 25.00' L = 41.42'
- 6 Δ = 81°01'39" R = 30.00' L = 42.43'
- 7 Δ = 04°35'02" R = 187.00' L = 14.96'
- 8 Δ = 05°14'10" R = 185.00' L = 16.91'
- 9 Δ = 10°53'15" R = 235.00' L = 44.66'
- 10 Δ = 08°07'11" R = 85.00' L = 9.08'
- 11 Δ = 12°39'50" R = 80.00' L = 17.68'
- 12 Δ = 10°55'40" R = 80.00' L = 15.28'
- 13 Δ = 11°11'22" R = 90.00' L = 17.58'
- 14 Δ = 14°07'41" R = 91.00' L = 22.44'
- 15 Δ = 06°10'53" R = 268.00' L = 28.91'
- 16 Δ = 12°34'58" R = 120.00' L = 26.35'
- 17 Δ = 01°27'30" R = 218.00' L = 5.57'
- 18 Δ = 11°57'21" R = 215.00' L = 44.86'
- 19 Δ = 06°37'43" R = 385.00' L = 44.54'
- 20 Δ = 03°16'40" R = 388.00' L = 22.25'
- 21 Δ = 41°04'34" R = 58.00' L = 41.58'
- 22 Δ = 25°23'55" R = 72.00' L = 31.92'
- 23 Δ = 24°26'32" R = 59.00' L = 25.17'
- 24 Δ = 25°21'50" R = 48.00' L = 21.69'
- 25 Δ = 13°12'50" R = 170.00' L = 39.21'
- 26 Δ = 01°26'55" R = 300.00' L = 7.58'

LL 96 - 026 , INST. NO. 19960587414, O.R.

PORTION OF PCL 1

G:\10036763.TM\15986.DWG

349 9

SHEET 9 OF 15 SHEETS

ALL OF VESTING TENTATIVE
TRACT NO. 15986



TRACT NO. 15986

IN THE UNINCORPORATED TERRITORY OF ORANGE COUNTY, CALIFORNIA
SEPTEMBER 2002 JAMES F. GILLEN, L.S. 5557

DATE OF SURVEY:
JANUARY 1999 &
MARCH 2002

HUITT-ZOLLARS
13 NUMBERED LOTS AND 58 LETTERED LOTS

120.329 ACRES

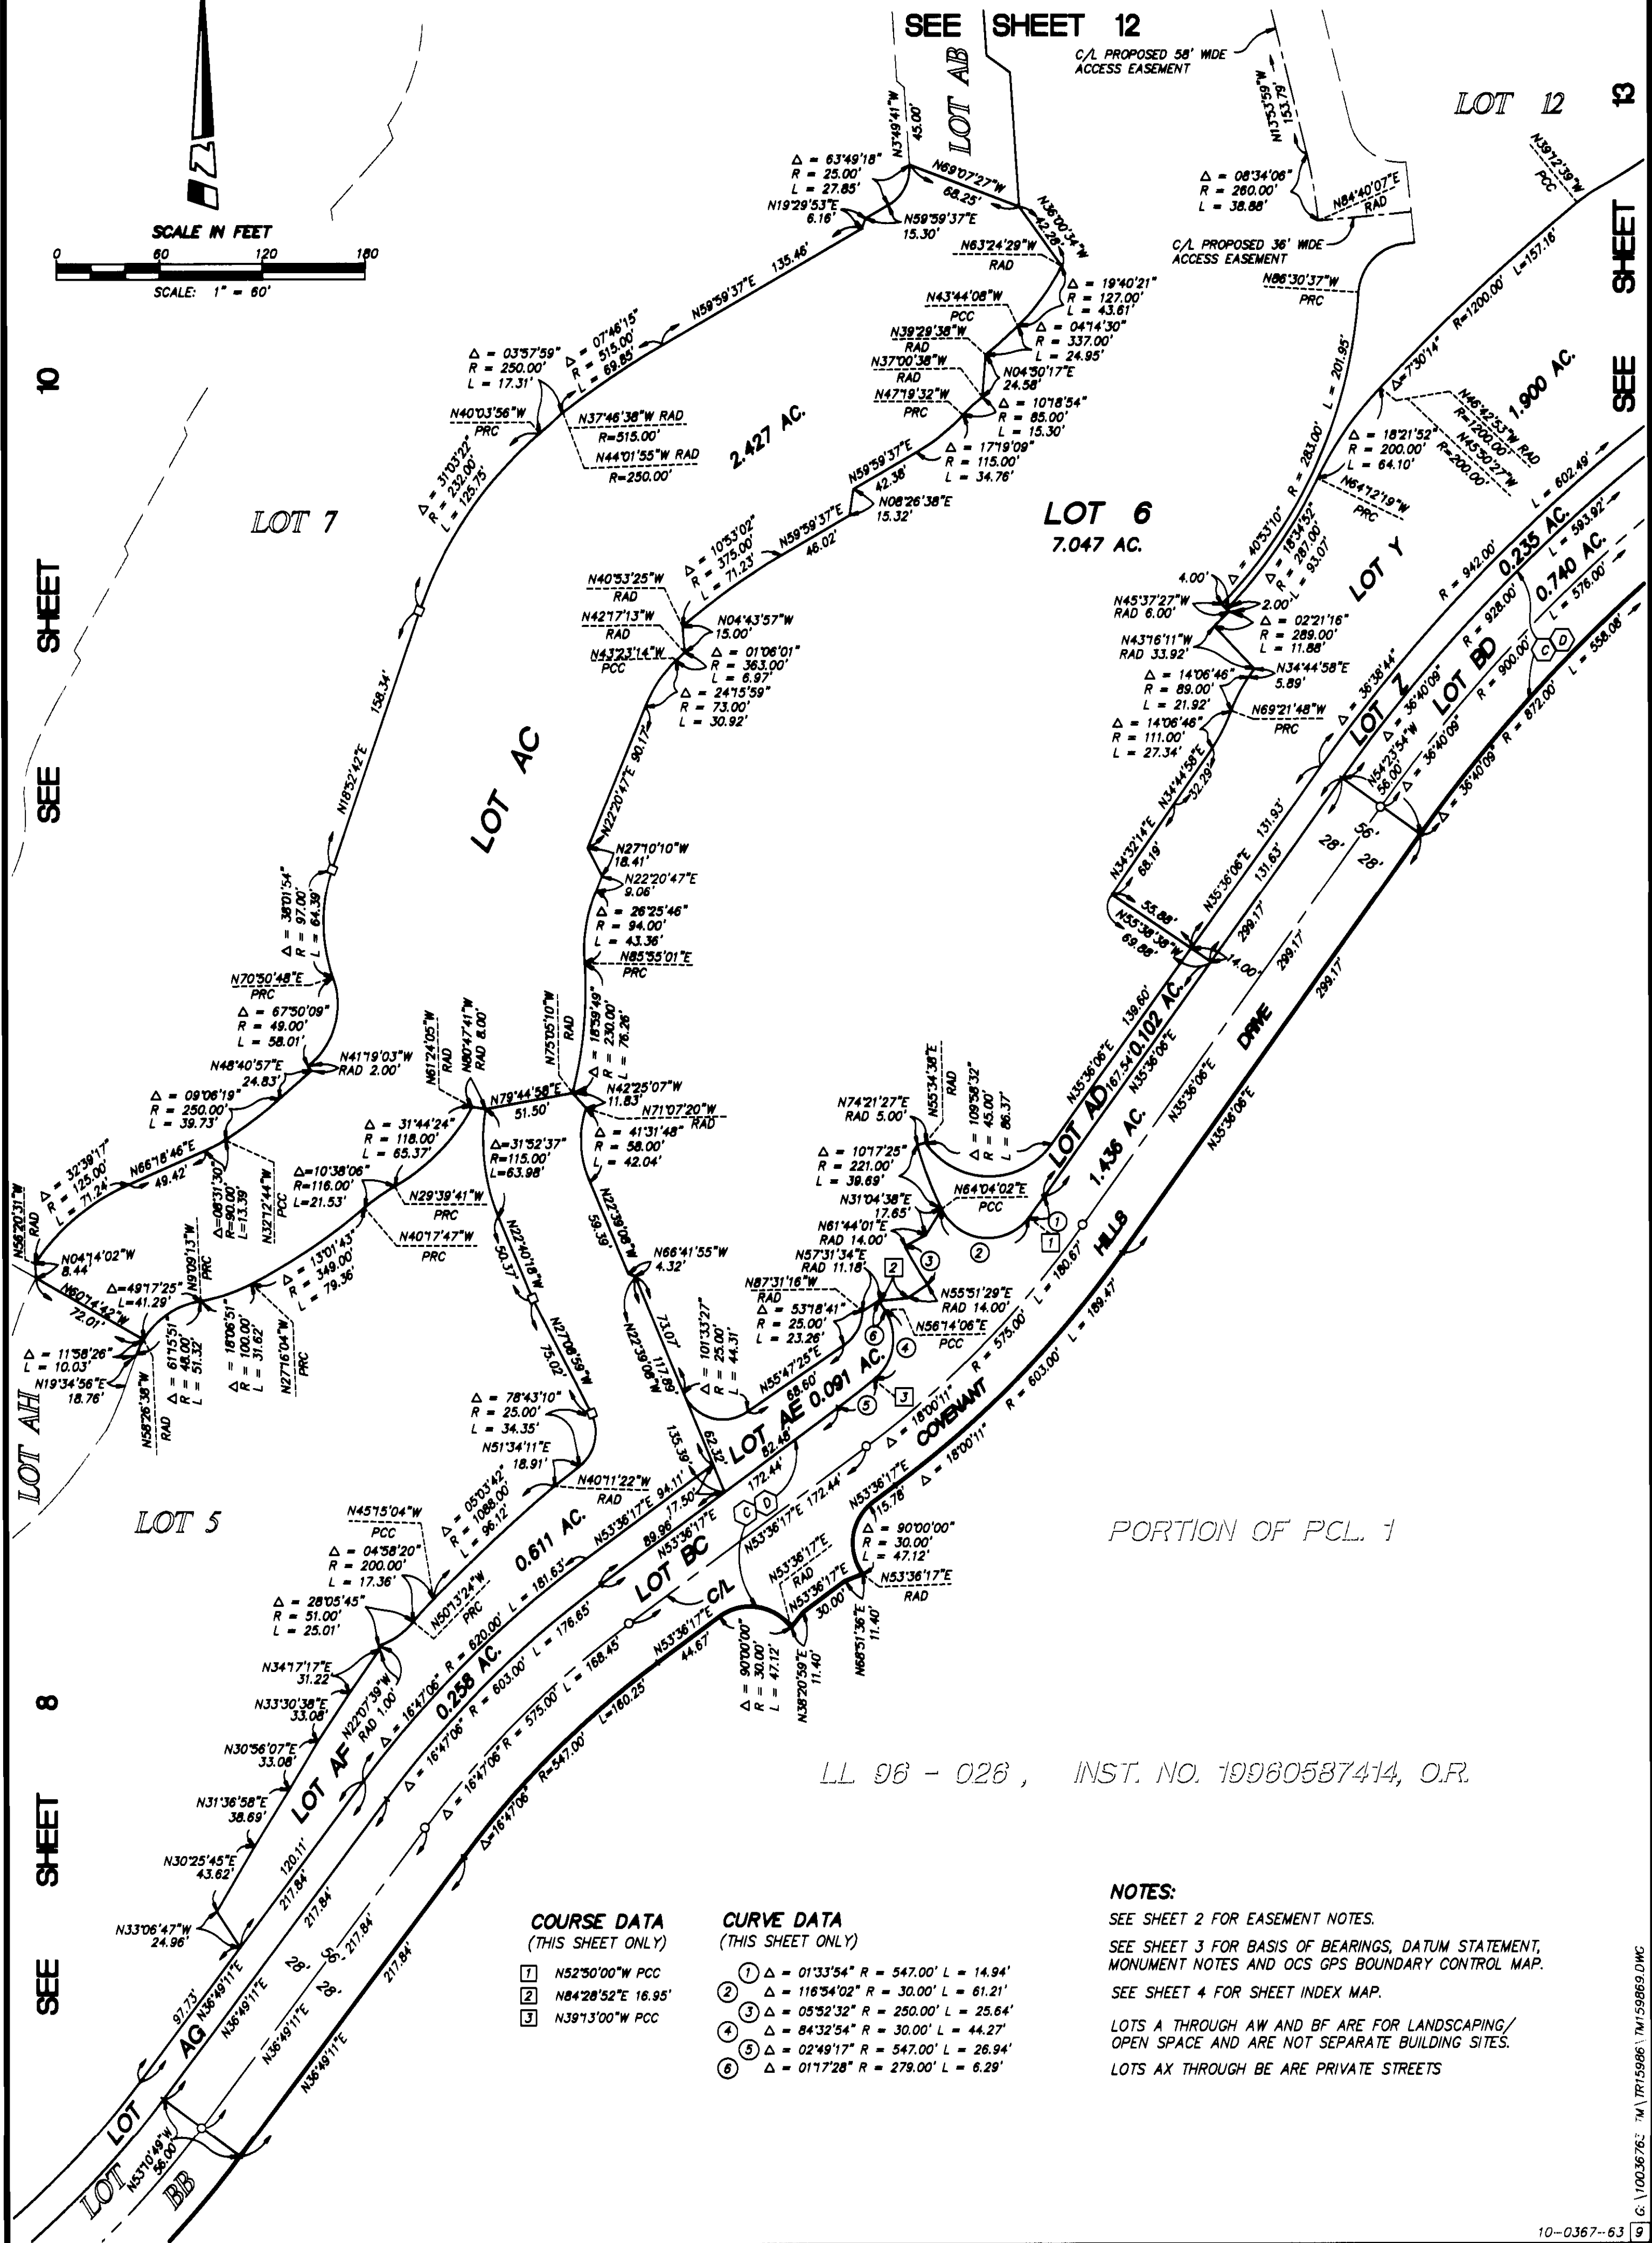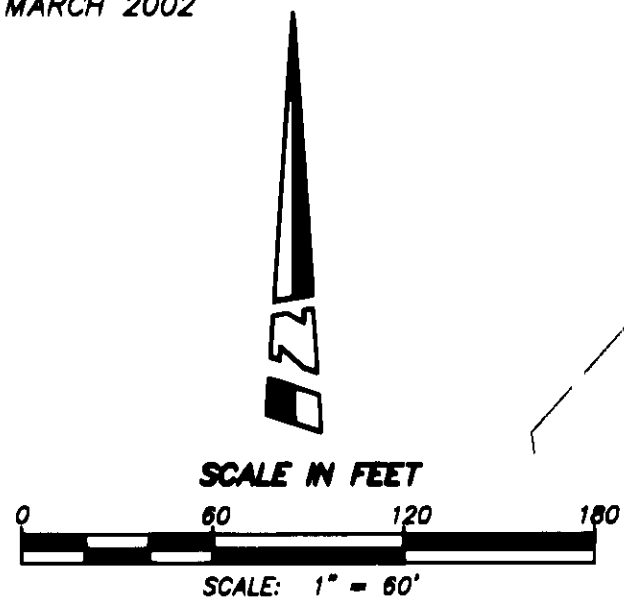

COURSE DATA (THIS SHEET ONLY)

- 1 N52°30'00"W PCC
- 2 N84°28'52"E 16.95'
- 3 N39°13'00"W PCC

CURVE DATA (THIS SHEET ONLY)

- 1 Δ = 01°33'54" R = 547.00' L = 14.94'
- 2 Δ = 116°54'02" R = 30.00' L = 61.21'
- 3 Δ = 05°52'32" R = 250.00' L = 25.64'
- 4 Δ = 84°32'54" R = 30.00' L = 44.27'
- 5 Δ = 02°49'17" R = 547.00' L = 26.94'
- 6 Δ = 01°17'28" R = 279.00' L = 6.29'

NOTES:

- SEE SHEET 2 FOR EASEMENT NOTES.
SEE SHEET 3 FOR BASIS OF BEARINGS, DATUM STATEMENT,
MONUMENT NOTES AND OCS GPS BOUNDARY CONTROL MAP.
SEE SHEET 4 FOR SHEET INDEX MAP.
LOTS A THROUGH AW AND BF ARE FOR LANDSCAPING/
OPEN SPACE AND ARE NOT SEPARATE BUILDING SITES.
LOTS AX THROUGH BE ARE PRIVATE STREETS

849 10

SHEET 10 OF 15 SHEETS

ALL OF VESTING TENTATIVE
TRACT NO. 15986

TRACT NO. 15986


IN THE UNINCORPORATED TERRITORY OF ORANGE COUNTY, CALIFORNIA
SEPTEMBER 2002 JAMES F. GILLEN, L.S. 5557

DATE OF SURVEY:
JANUARY 1999 &
MARCH 2002

HUITT-ZOLLARS
13 NUMBERED LOTS AND 58 LETTERED LOTS

120.329 ACRES

SEE SHEET 12

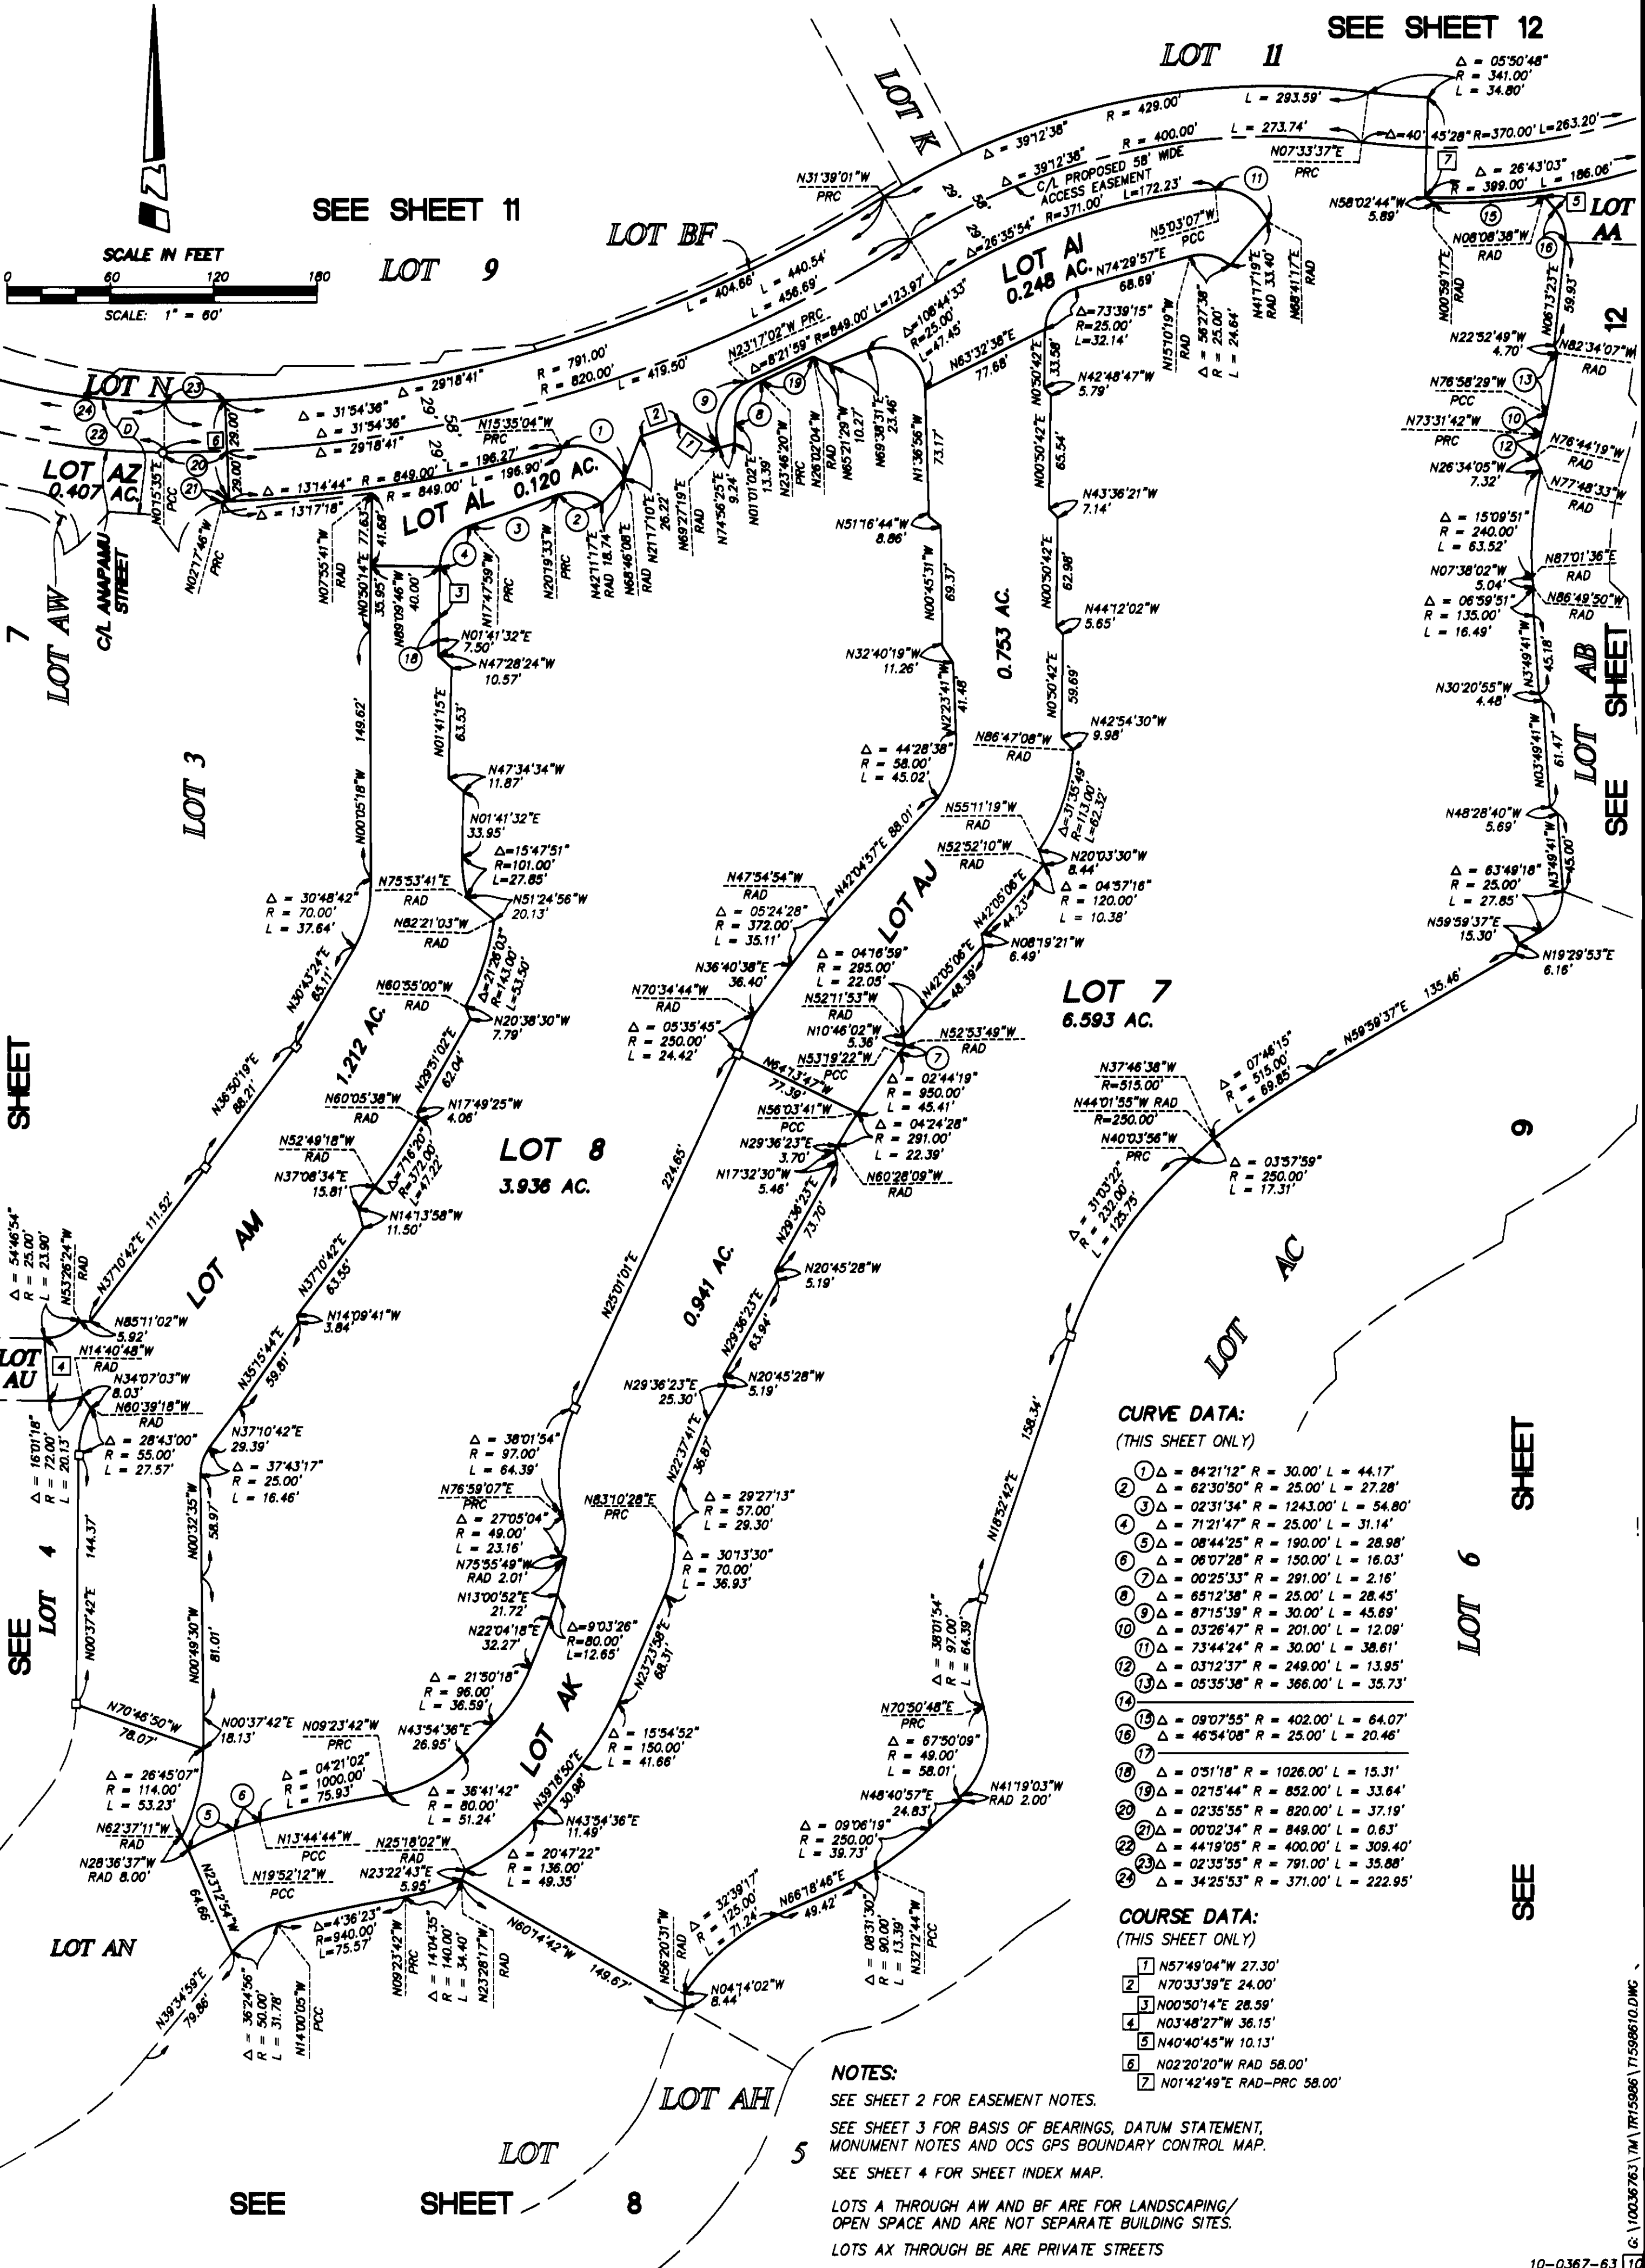

CURVE DATA: (THIS SHEET ONLY)

- 1 $\Delta = 84^{\circ}21'12''$ R = 30.00' L = 44.17'
- 2 $\Delta = 62^{\circ}30'50''$ R = 25.00' L = 27.28'
- 3 $\Delta = 02^{\circ}31'34''$ R = 1243.00' L = 54.80'
- 4 $\Delta = 71^{\circ}21'47''$ R = 25.00' L = 31.14'
- 5 $\Delta = 08^{\circ}44'25''$ R = 190.00' L = 28.98'
- 6 $\Delta = 06^{\circ}07'28''$ R = 150.00' L = 16.03'
- 7 $\Delta = 00^{\circ}25'33''$ R = 291.00' L = 2.16'
- 8 $\Delta = 65^{\circ}12'38''$ R = 25.00' L = 28.45'
- 9 $\Delta = 67^{\circ}15'39''$ R = 30.00' L = 45.69'
- 10 $\Delta = 03^{\circ}26'47''$ R = 201.00' L = 12.09'
- 11 $\Delta = 73^{\circ}44'24''$ R = 30.00' L = 38.61'
- 12 $\Delta = 03^{\circ}12'37''$ R = 249.00' L = 13.95'
- 13 $\Delta = 05^{\circ}35'38''$ R = 366.00' L = 35.73'
- 14 $\Delta = 09^{\circ}07'55''$ R = 402.00' L = 64.07'
- 15 $\Delta = 46^{\circ}54'08''$ R = 25.00' L = 20.46'
- 16 $\Delta = 03^{\circ}11'18''$ R = 1026.00' L = 15.31'
- 17 $\Delta = 02^{\circ}15'44''$ R = 852.00' L = 33.64'
- 18 $\Delta = 02^{\circ}35'55''$ R = 820.00' L = 37.19'
- 19 $\Delta = 00^{\circ}02'34''$ R = 849.00' L = 0.63'
- 20 $\Delta = 44^{\circ}19'05''$ R = 400.00' L = 309.40'
- 21 $\Delta = 02^{\circ}35'55''$ R = 791.00' L = 35.88'
- 22 $\Delta = 34^{\circ}25'53''$ R = 371.00' L = 222.95'

COURSE DATA: (THIS SHEET ONLY)

- 1 N57^{\circ}49'04''W 27.30'
- 2 N70^{\circ}33'39''E 24.00'
- 3 N00^{\circ}50'14''E 28.59'
- 4 N03^{\circ}48'27''W 36.15'
- 5 N40^{\circ}40'45''W 10.13'
- 6 N02^{\circ}20'20''W RAD 58.00'
- 7 N01^{\circ}42'49''E RAD-PRC 58.00'

NOTES:

SEE SHEET 2 FOR EASEMENT NOTES.

SEE SHEET 3 FOR BASIS OF BEARINGS, DATUM STATEMENT,
MONUMENT NOTES AND OCS GPS BOUNDARY CONTROL MAP.

SEE SHEET 4 FOR SHEET INDEX MAP.

LOTS A THROUGH AW AND BF ARE FOR LANDSCAPING/
OPEN SPACE AND ARE NOT SEPARATE BUILDING SITES.

LOTS AX THROUGH BE ARE PRIVATE STREETS

849 11

SHEET 11 OF 15 SHEETS

ALL OF VESTING TENTATIVE
TRACT NO. 15986

TRACT NO. 15986
IN THE UNINCORPORATED TERRITORY OF ORANGE COUNTY, CALIFORNIA
SEPTEMBER 2002


JAMES F. GILLEN, L.S. 5557

HUITT-ZOLLARS

13 NUMBERED LOTS AND 58 LETTERED LOTS

120.329 ACRES

DATE OF SURVEY:
JANUARY 1999 &
MARCH 2002

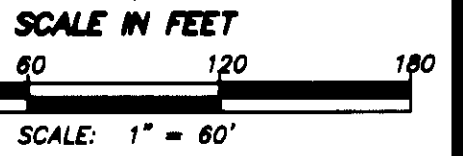


COURSE DATA
(THIS SHEET ONLY)

- 1 N51°33'20"E 4.22'
- 2 N22°36'18"E RAD
- 3 N34°41'28"E PCC
- 4 N44°55'55"W 58.00'
- 5 N44°55'55"W 28.00'
- 6 N46°07'22"W PRC
- 7 N56°52'33"W PRC
- 8 (Δ = 31°43'48"
R = 80.00'
L = 33.23')
- 9 N76°20'47"W RAD
R = 639.00'
- 10 N87°23'50"W PRC
- 11 N84°52'47"W PRC
- 12 N08°19'12"W 15.34'
- 13 N28°53'12"E 11.20'
- 14 N02°27'48"E RAD 14.00'
- 15 N55°47'41"W 16.73'
- 16 N34°12'19"E 43.73'
- 17 N84°29'14"E PRC
- 18 (N66°02'01"E RAD 56.00')
- 19 N66°02'01"E RAD 28.00'
- 20 N37°25'52"E RAD
- 21 N16°00'46"W RAD 3.00'

CURVE DATA
(THIS SHEET ONLY)

- 1 Δ = 98°42'05" R = 25.00' L = 43.07'
- 2 Δ = 100°22'37" R = 30.00' L = 52.56'
- 3 Δ = 01°11'27" R = 608.00' L = 12.64'
- 4 Δ = 77°21'22" R = 30.00' L = 40.50'
- 5 Δ = 03°30'37" R = 250.00' L = 15.32'
- 6 Δ = 96°25'57" R = 30.00' L = 50.49'
- 7 Δ = 13°19'36" R = 128.00' L = 29.77'
- 8 Δ = 05°36'10" R = 102.00' L = 10.57'
- 9 Δ = 58°23'51" R = 25.00' L = 25.48'
- 10 Δ = 56°08'10" R = 30.00' L = 29.38'
- 11 Δ = 89°03'09" R = 30.00' L = 46.63'
- 12 Δ = 01°02'40" R = 300.00' L = 5.47'
- 13 Δ = 81°45'07" R = 30.00' L = 42.81'
- 14 Δ = 14°08'35" R = 128.00' L = 31.63'
- 15 Δ = 00°49'59" R = 128.00' L = 1.86'
- 16 (Δ = 84°41'39" R = 30.00' L = 44.35')
- 17 (Δ = 05°18'21" R = 580.00' L = 53.71')
- 18 (Δ = 00°40'49" R = 552.00' L = 8.55')
- 19 Δ = 01°25'54" R = 428.00' L = 10.72'
- 20 Δ = 01°26'52" R = 432.00' L = 10.92'
- 21 Δ = 04°11'35" R = 789.00' L = 57.74'
- 22 Δ = 05°28'41" R = 429.00' L = 41.02'
- 23 Δ = 02°35'55" R = 791.00' L = 35.88'
- 24 Δ = 02°35'55" R = 820.00' L = 37.19'
- 25 Δ = 14°43'43" R = 160.00' L = 41.13'
- 26 Δ = 19°22'32" R = 35.00' L = 11.84'

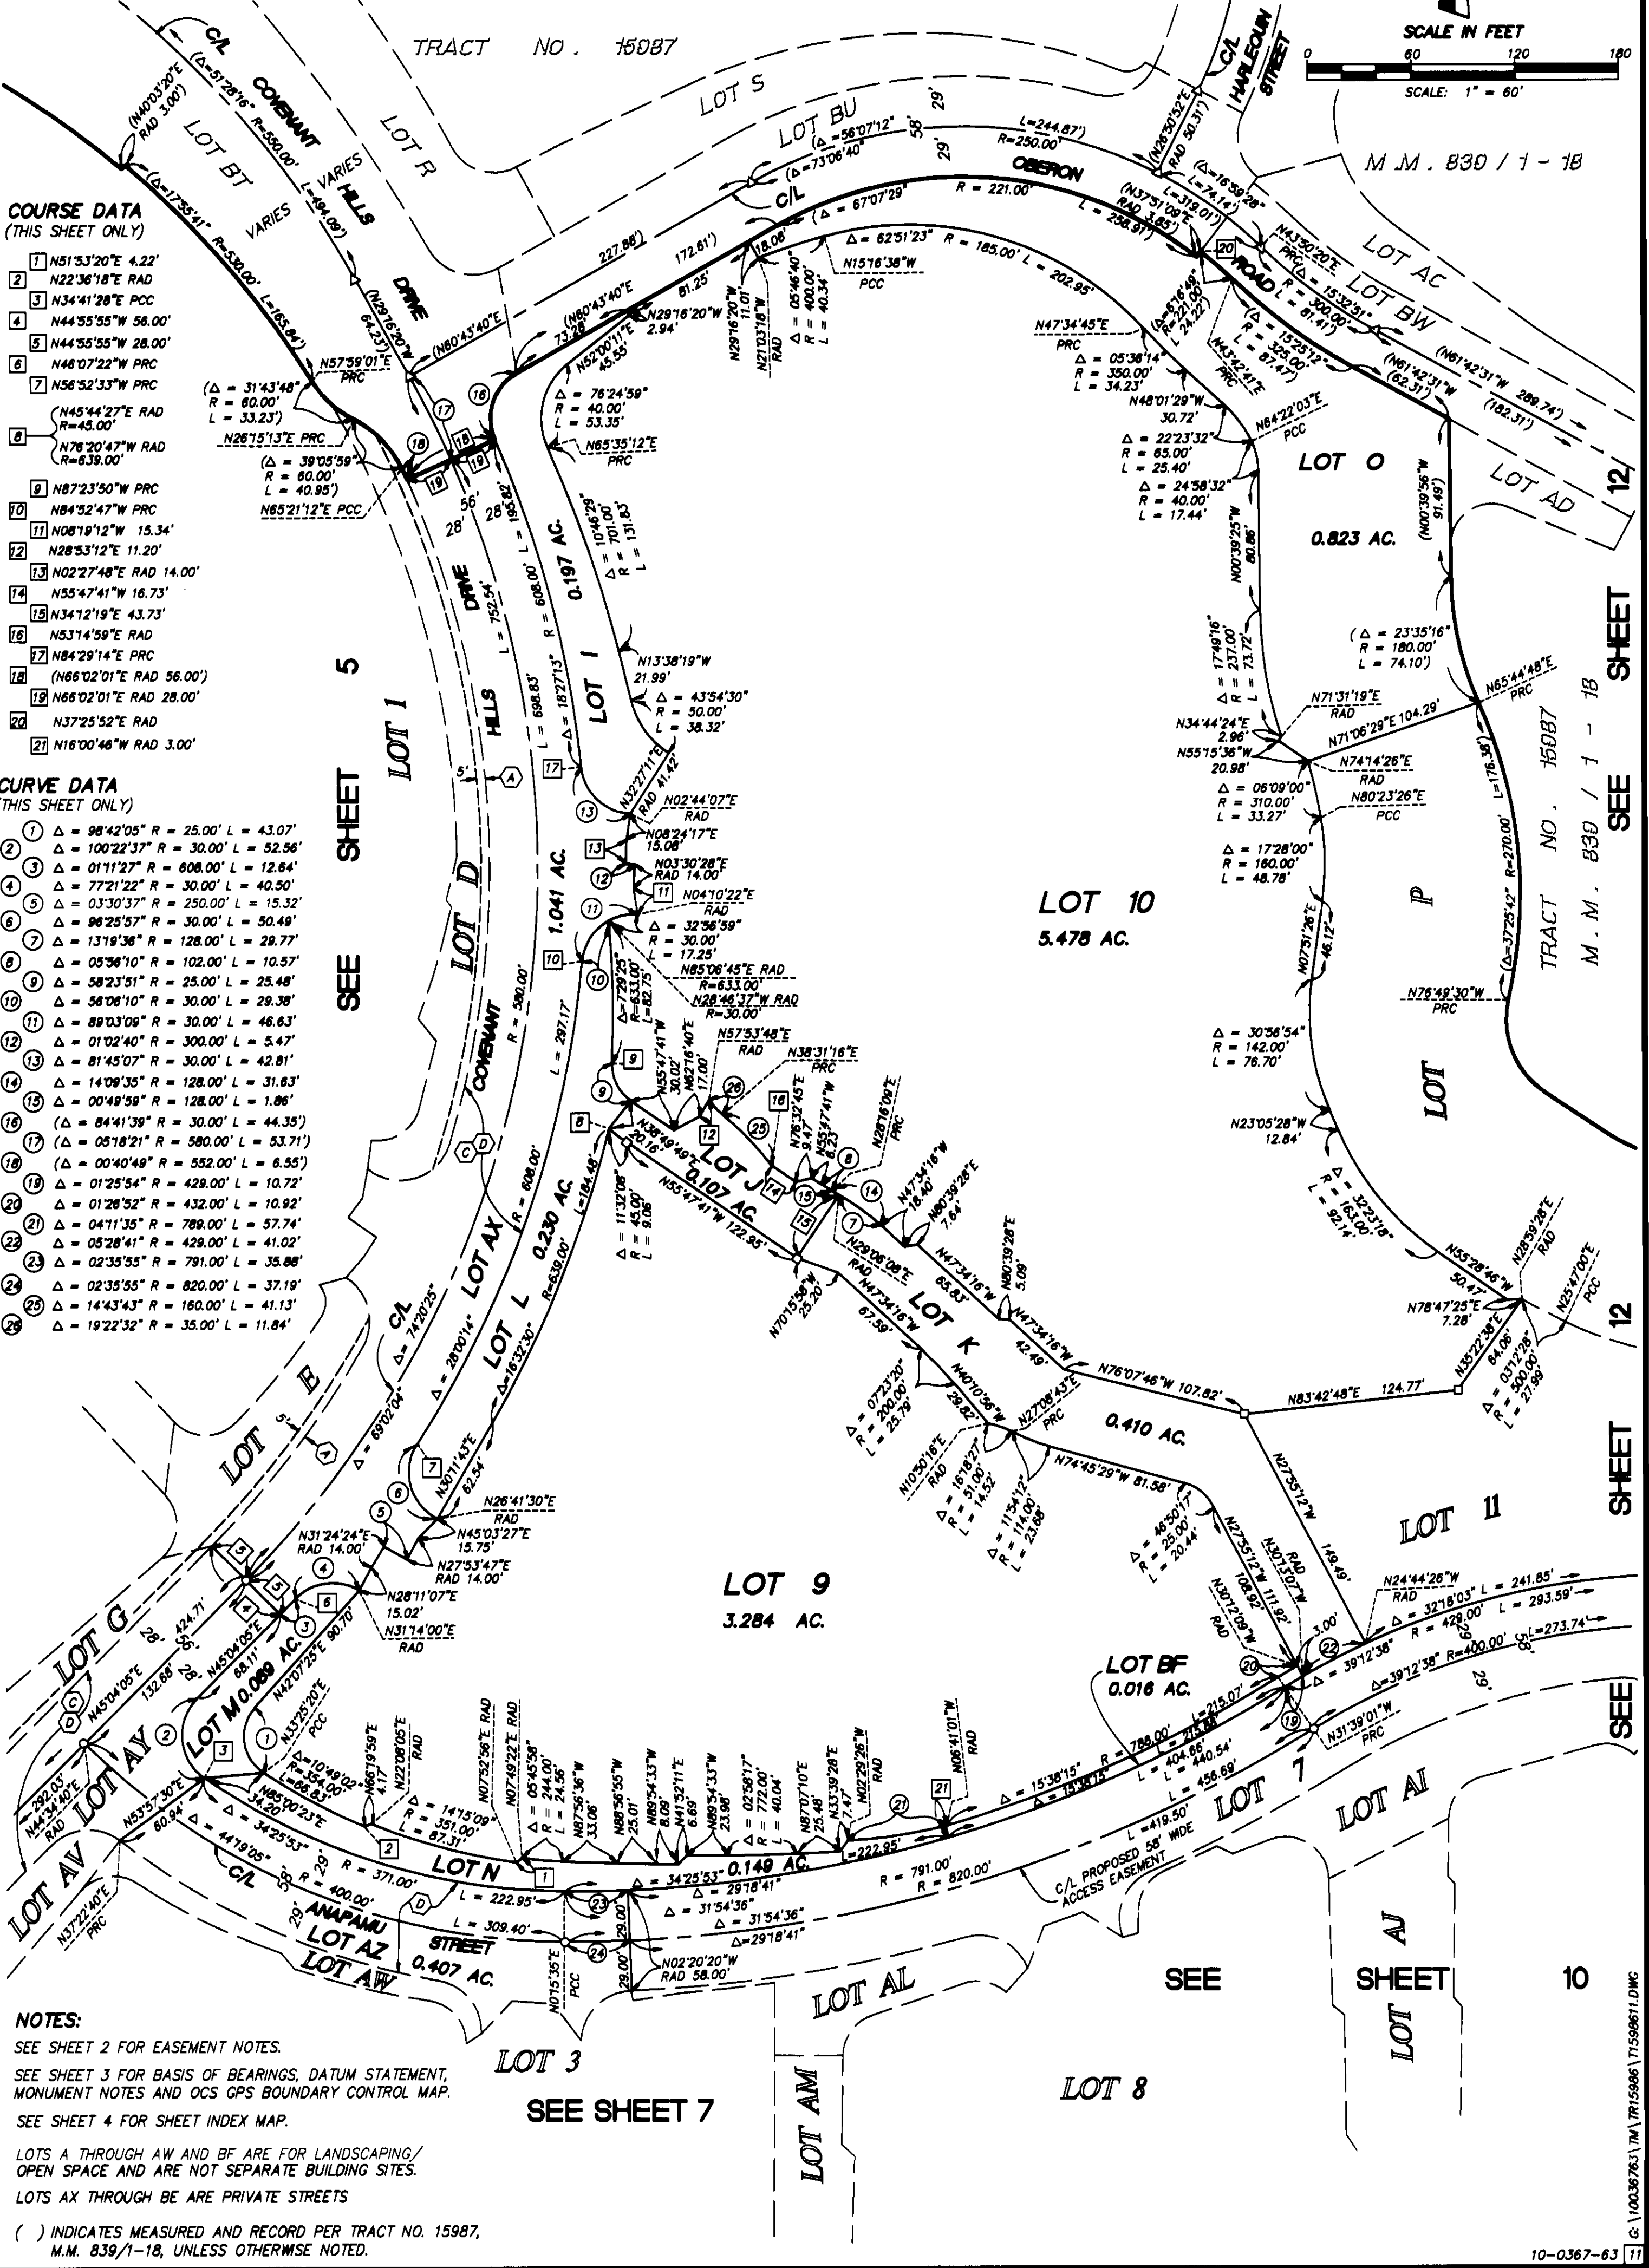

NOTES:

SEE SHEET 2 FOR EASEMENT NOTES.
SEE SHEET 3 FOR BASIS OF BEARINGS, DATUM STATEMENT,
MONUMENT NOTES AND OCS GPS BOUNDARY CONTROL MAP.
SEE SHEET 4 FOR SHEET INDEX MAP.

LOTS A THROUGH AW AND BF ARE FOR LANDSCAPING/
OPEN SPACE AND ARE NOT SEPARATE BUILDING SITES.
LOTS AX THROUGH BE ARE PRIVATE STREETS

() INDICATES MEASURED AND RECORD PER TRACT NO. 15987,
M.M. 839/1-18, UNLESS OTHERWISE NOTED.

849 12

SHEET 12 OF 15 SHEETS

ALL OF VESTING TENTATIVE
TRACT NO. 15986

TRACT NO. 15986
IN THE UNINCORPORATED TERRITORY OF ORANGE COUNTY, CALIFORNIA
SEPTEMBER 2002

JAMES F. GILLEN, L.S. 5557


HUITT-ZOLIARS

13 NUMBERED LOTS AND 58 LETTERED LOTS

120.329 ACRES

DATE OF SURVEY:
JANUARY 1999 &
MARCH 2002

TRACT NO. 15987

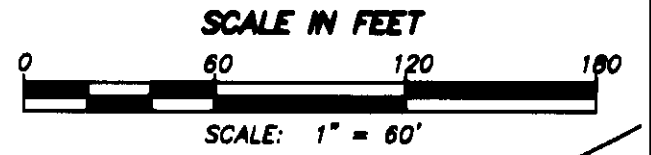

NOTES:

SEE SHEET 2 FOR EASEMENT NOTES.

SEE SHEET 3 FOR BASIS OF BEARINGS, DATUM STATEMENT,
MONUMENT NOTES AND OCS GPS BOUNDARY CONTROL MAP.


SEE SHEET 4 FOR SHEET INDEX MAP.

LOTS A THROUGH AW AND BF ARE FOR LANDSCAPING/
OPEN SPACE AND ARE NOT SEPARATE BUILDING SITES.

LOTS AX THROUGH BE ARE PRIVATE STREETS

() INDICATES MEASURED AND RECORD PER TRACT NO. 15987,
M.M. 839/1-18, UNLESS OTHERWISE NOTED.

M.M. 839 / 1 - 18

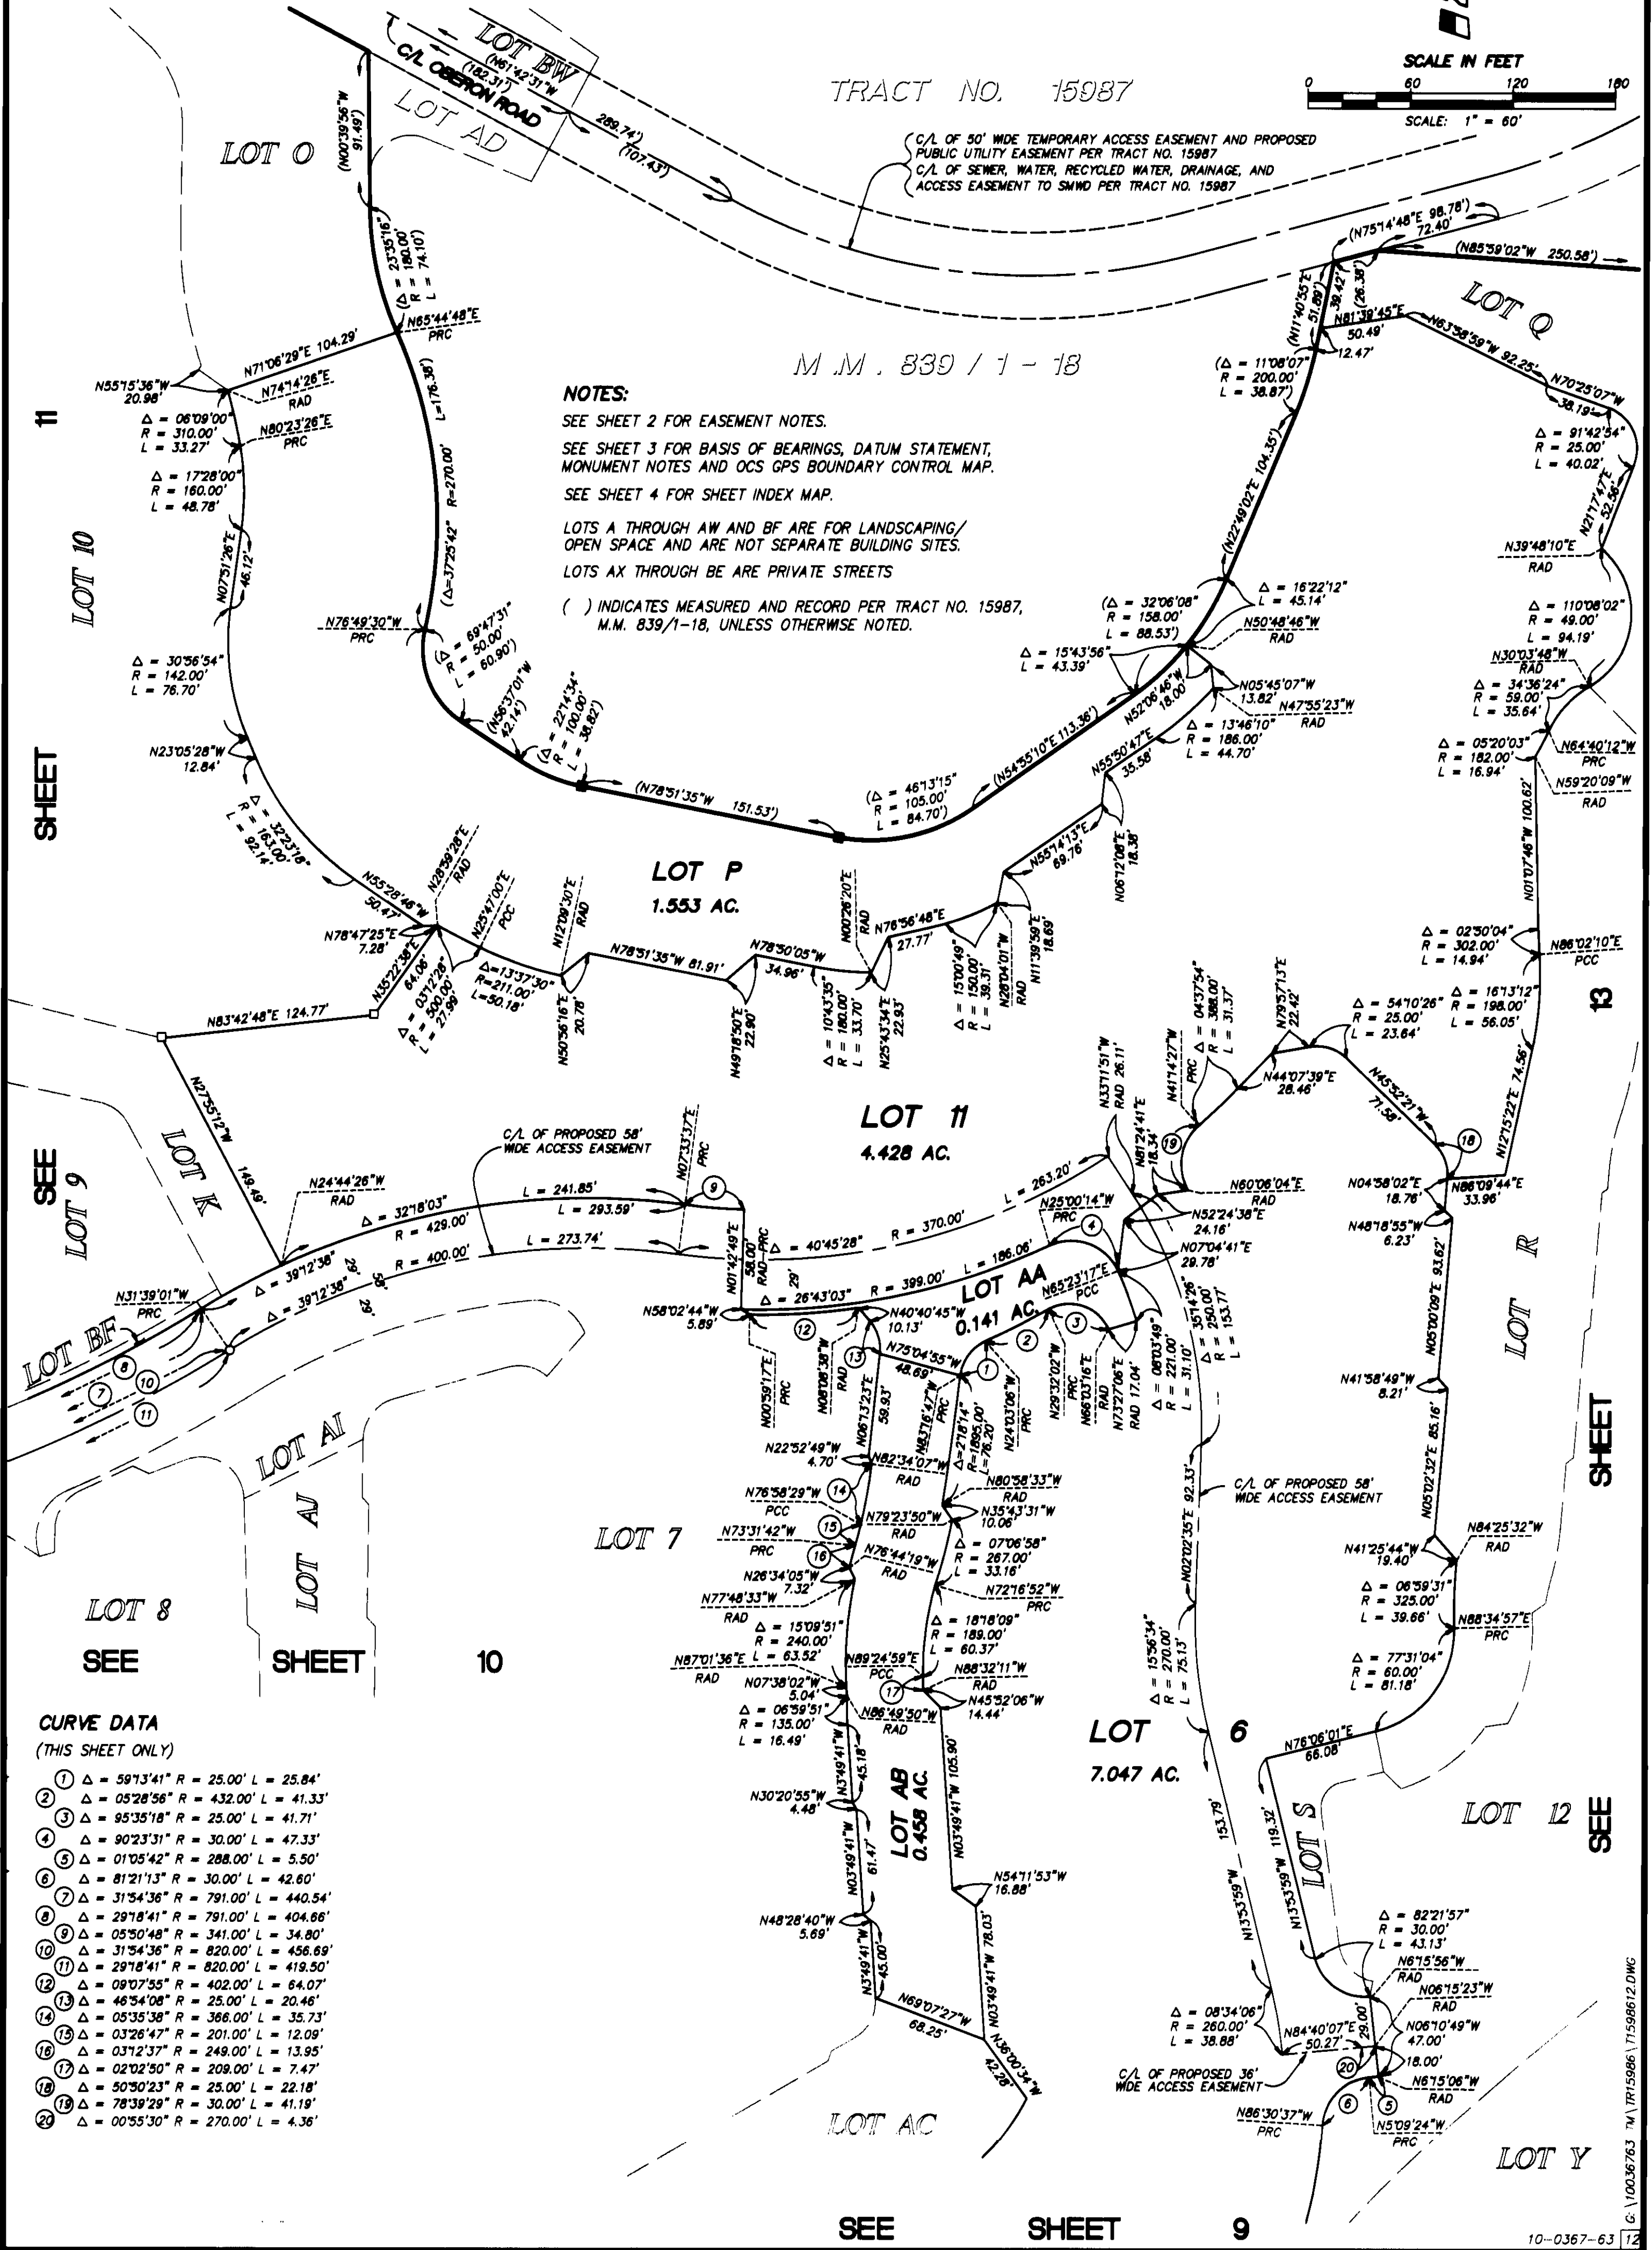

CURVE DATA
(THIS SHEET ONLY)

- ① $\Delta = 59^{\circ}13'41''$ R = 25.00' L = 25.84'
- ② $\Delta = 05^{\circ}28'56''$ R = 432.00' L = 41.33'
- ③ $\Delta = 95^{\circ}35'18''$ R = 25.00' L = 41.71'
- ④ $\Delta = 90^{\circ}23'31''$ R = 30.00' L = 47.33'
- ⑤ $\Delta = 01^{\circ}05'42''$ R = 288.00' L = 5.50'
- ⑥ $\Delta = 81^{\circ}21'13''$ R = 30.00' L = 42.80'
- ⑦ $\Delta = 31^{\circ}54'36''$ R = 791.00' L = 440.54'
- ⑧ $\Delta = 29^{\circ}18'41''$ R = 791.00' L = 404.66'
- ⑨ $\Delta = 05^{\circ}50'48''$ R = 341.00' L = 34.80'
- ⑩ $\Delta = 31^{\circ}54'36''$ R = 820.00' L = 456.69'
- ⑪ $\Delta = 29^{\circ}18'41''$ R = 820.00' L = 419.50'
- ⑫ $\Delta = 09^{\circ}07'55''$ R = 402.00' L = 64.07'
- ⑬ $\Delta = 46^{\circ}54'08''$ R = 25.00' L = 20.46'
- ⑭ $\Delta = 05^{\circ}35'38''$ R = 366.00' L = 35.73'
- ⑮ $\Delta = 03^{\circ}28'47''$ R = 201.00' L = 12.09'
- ⑯ $\Delta = 03^{\circ}12'37''$ R = 249.00' L = 13.95'
- ⑰ $\Delta = 02^{\circ}02'50''$ R = 209.00' L = 7.47'
- ⑱ $\Delta = 50^{\circ}50'23''$ R = 25.00' L = 22.18'
- ⑲ $\Delta = 78^{\circ}39'29''$ R = 30.00' L = 41.19'
- ⑳ $\Delta = 00^{\circ}55'30''$ R = 270.00' L = 4.36'

849 12

849 13

SHEET 13 OF 15 SHEETS

ALL OF VESTING TENTATIVE
TRACT NO. 15986

DATE OF SURVEY:
JANUARY 1999 &
MARCH 2002

TRACT NO. 15986


IN THE UNINCORPORATED TERRITORY OF ORANGE COUNTY, CALIFORNIA
SEPTEMBER 2002 JAMES F. GILLEN, L.S. 5557

HUITT-ZOLLARS

13 NUMBERED LOTS AND 58 LETTERED LOTS


120.329 ACRES

SCALE IN FEET

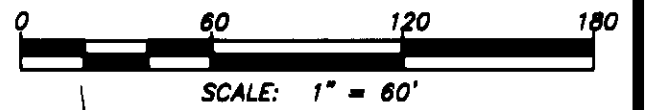

NO. 15987

M.M. 839 / 1-18

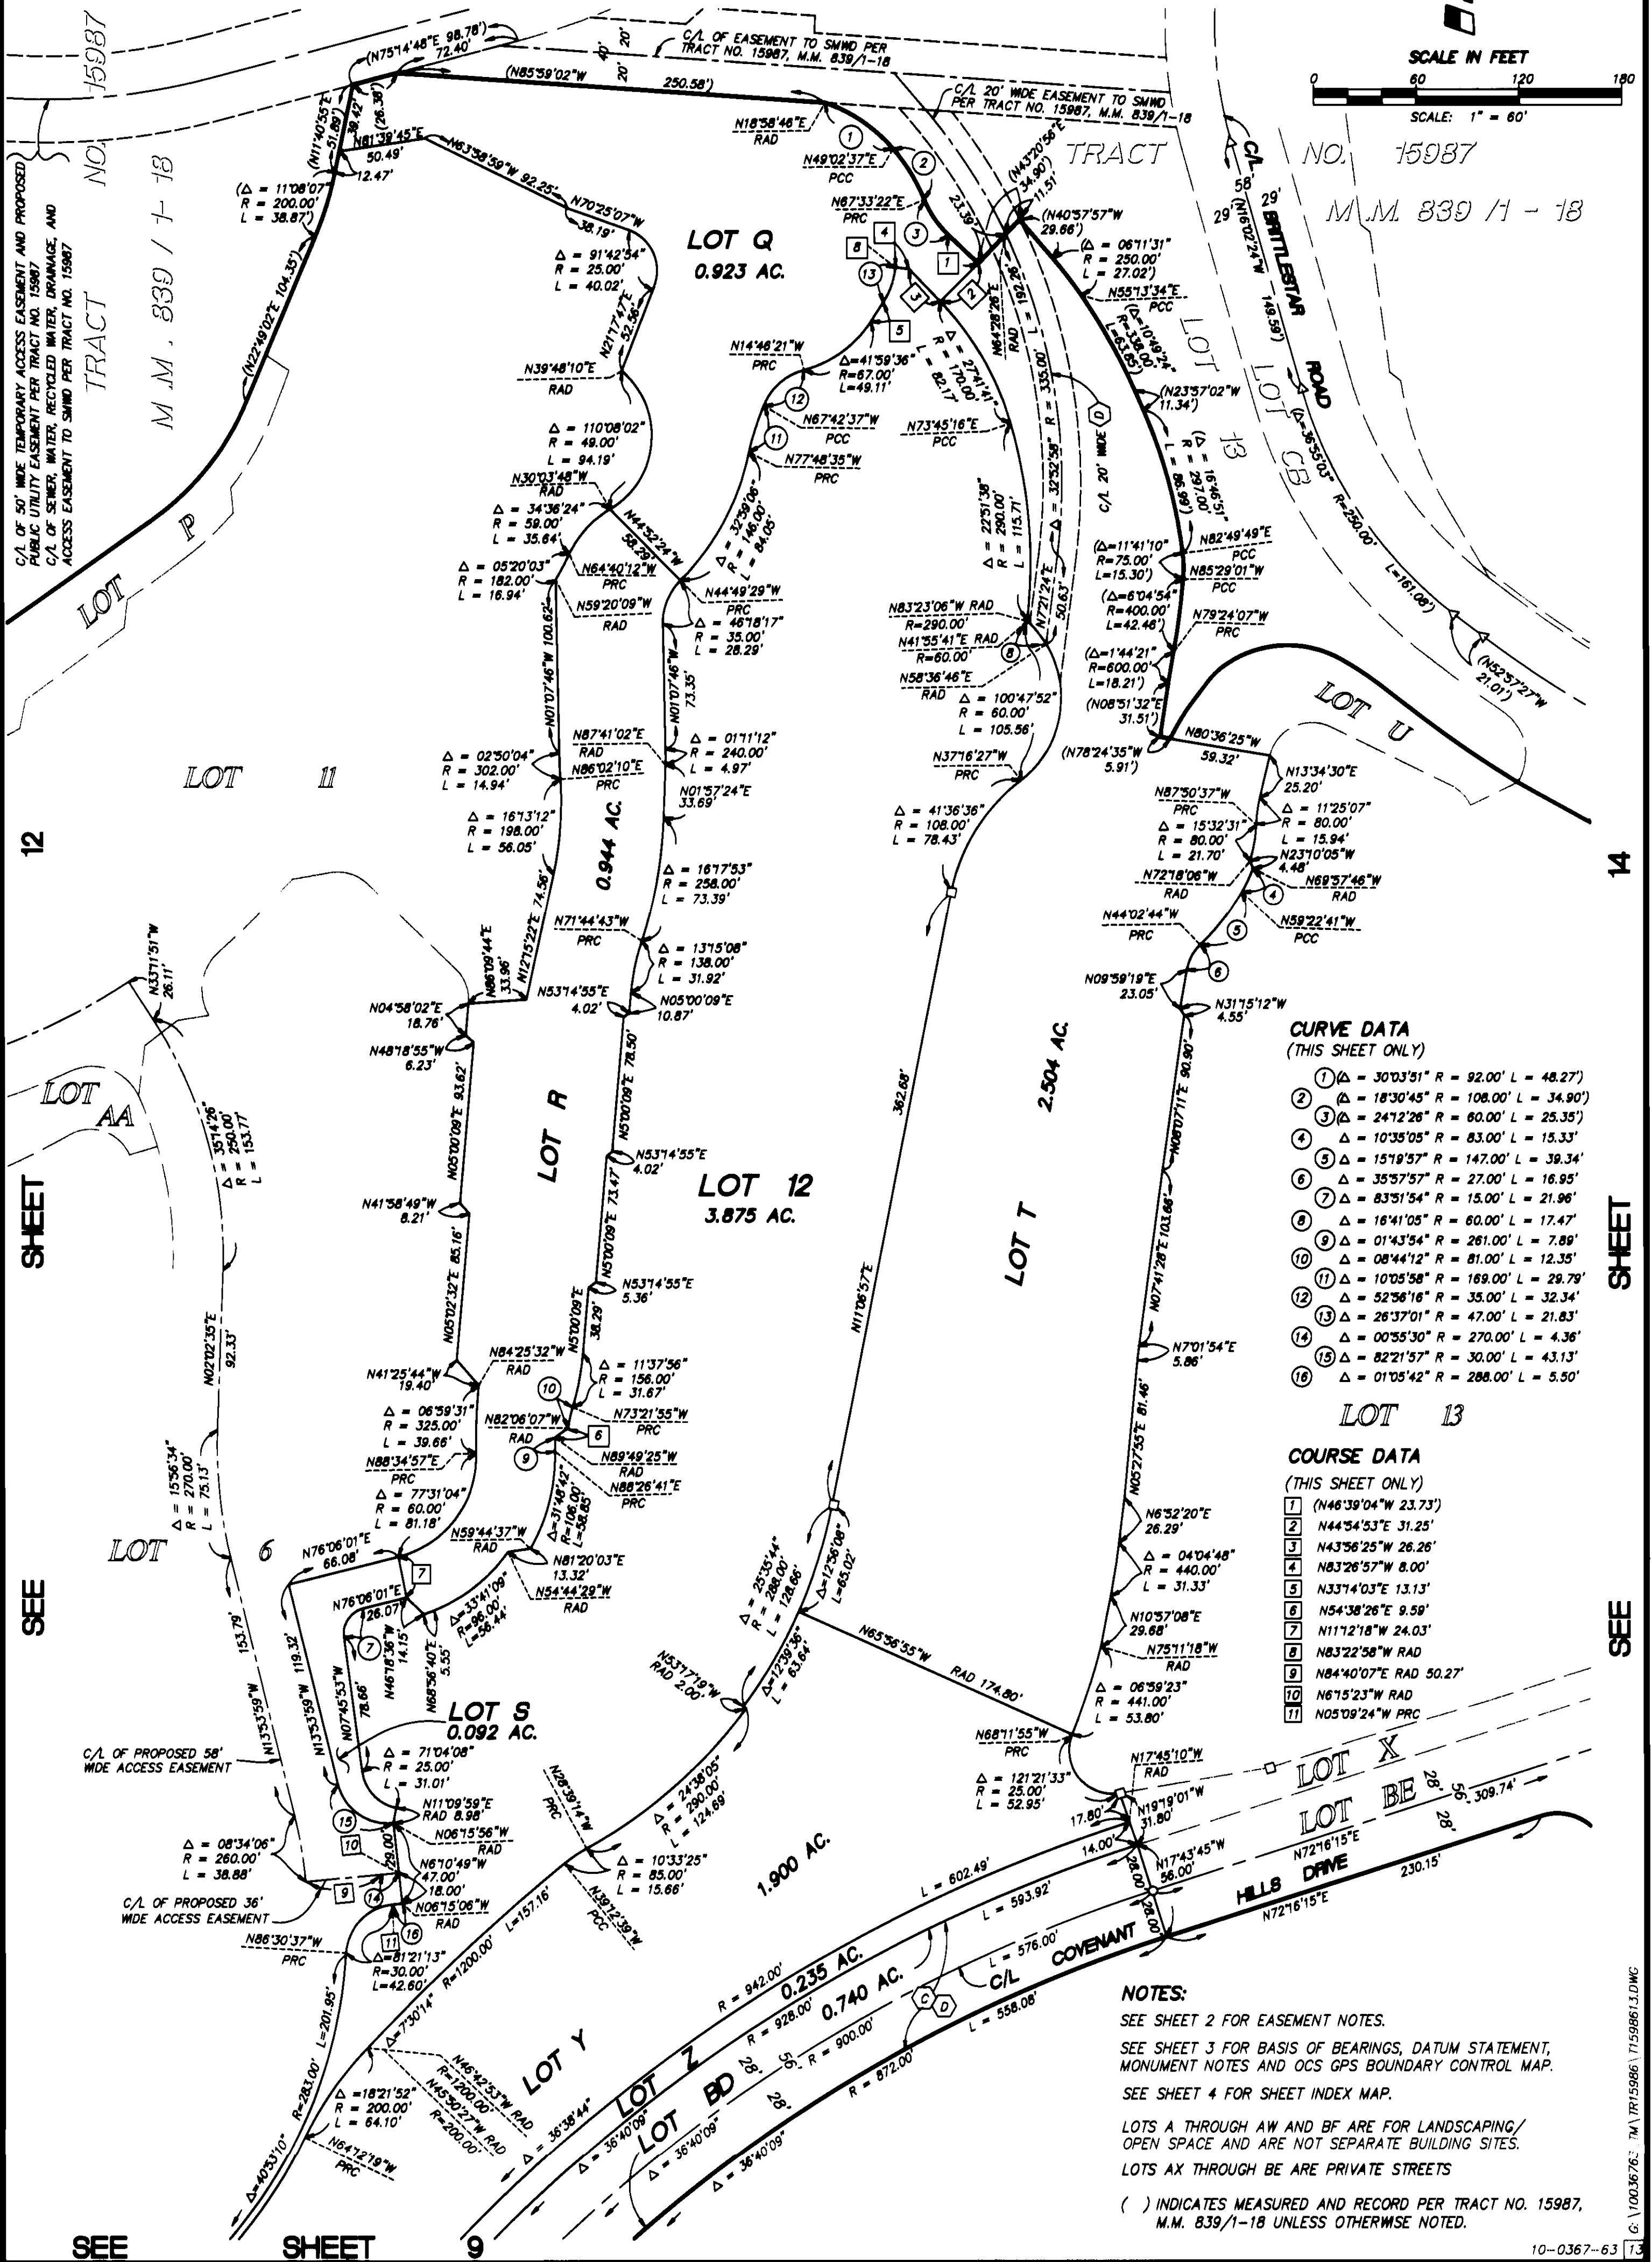

CURVE DATA (THIS SHEET ONLY)

- ① $\Delta = 30'03.51''$ R = 92.00' L = 48.27'
- ② $\Delta = 18'30.45''$ R = 108.00' L = 34.90'
- ③ $\Delta = 24'12.26''$ R = 60.00' L = 25.35'
- ④ $\Delta = 10'35.05''$ R = 83.00' L = 15.33'
- ⑤ $\Delta = 15'19.57''$ R = 147.00' L = 39.34'
- ⑥ $\Delta = 35'57.57''$ R = 27.00' L = 16.95'
- ⑦ $\Delta = 83'51.54''$ R = 15.00' L = 21.96'
- ⑧ $\Delta = 16'41.05''$ R = 60.00' L = 17.47'
- ⑨ $\Delta = 01'43.54''$ R = 261.00' L = 7.89'
- ⑩ $\Delta = 08'44.12''$ R = 81.00' L = 12.35'
- ⑪ $\Delta = 10'05.58''$ R = 169.00' L = 29.79'
- ⑫ $\Delta = 52'56.16''$ R = 35.00' L = 32.34'
- ⑬ $\Delta = 26'37.01''$ R = 47.00' L = 21.83'
- ⑭ $\Delta = 00'55.30''$ R = 270.00' L = 4.36'
- ⑮ $\Delta = 82'21.57''$ R = 30.00' L = 43.13'
- ⑯ $\Delta = 01'05.42''$ R = 288.00' L = 5.50'

COURSE DATA (THIS SHEET ONLY)

- ① (N46'39'04"W 23.73')
- ② (N44'54'53"E 31.25')
- ③ (N43'56'25"W 26.26')
- ④ (N83'26'57"W 8.00')
- ⑤ (N33'14'03"E 13.13')
- ⑥ (N54'38'26"E 9.59')
- ⑦ (N11'12'18"W 24.03')
- ⑧ (N83'22'58"W RAD 50.27')
- ⑨ (N84'40'07"E RAD 50.27')
- ⑩ (N67'52'33"W RAD 53.80')
- ⑪ (N05'09'24"W PRC)

NOTES:

- SEE SHEET 2 FOR EASEMENT NOTES.
- SEE SHEET 3 FOR BASIS OF BEARINGS, DATUM STATEMENT, MONUMENT NOTES AND OCS GPS BOUNDARY CONTROL MAP.
- SEE SHEET 4 FOR SHEET INDEX MAP.
- LOTS A THROUGH AW AND BF ARE FOR LANDSCAPING/ OPEN SPACE AND ARE NOT SEPARATE BUILDING SITES.
- LOTS AX THROUGH BE ARE PRIVATE STREETS
- () INDICATES MEASURED AND RECORD PER TRACT NO. 15987, M.M. 839 / 1-18 UNLESS OTHERWISE NOTED.

849 14

SHEET 14 OF 15 SHEETS

TRACT NO. 15986

IN THE UNINCORPORATED TERRITORY OF ORANGE COUNTY, CALIFORNIA

SEPTEMBER 2002

JAMES F. GILLEN, L.S. 5557

ALL OF VESTING TENTATIVE
TRACT NO. 15986

HUITT-ZOLLARS

13 NUMBERED LOTS AND 58 LETTERED LOTS

120.329 ACRES

DATE OF SURVEY:
JANUARY 1999 &
MARCH 2002

NOTES:

SEE SHEET 2 FOR EASEMENT NOTES.


SEE SHEET 3 FOR BASIS OF BEARINGS, DATUM STATEMENT,
MONUMENT NOTES AND OCS GPS BOUNDARY CONTROL MAP.

SEE SHEET 4 FOR SHEET INDEX MAP.

LOTS A THROUGH AW AND BF ARE FOR LANDSCAPING/
OPEN SPACE AND ARE NOT SEPARATE BUILDING SITES.


LOTS AX THROUGH BE ARE PRIVATE STREETS

() INDICATES MEASURED AND RECORD PER TRACT NO. 15987,
M.M. 839/1-18, UNLESS OTHERWISE NOTED.

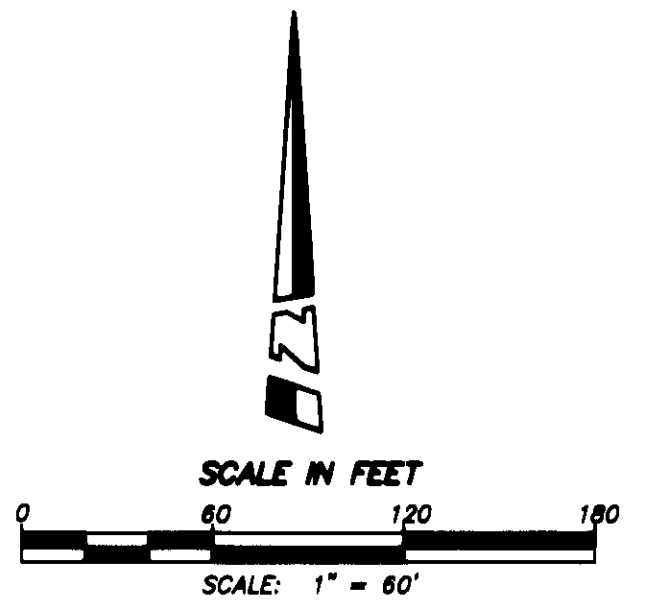

SEE SHEET 13

SEE SHEET 13

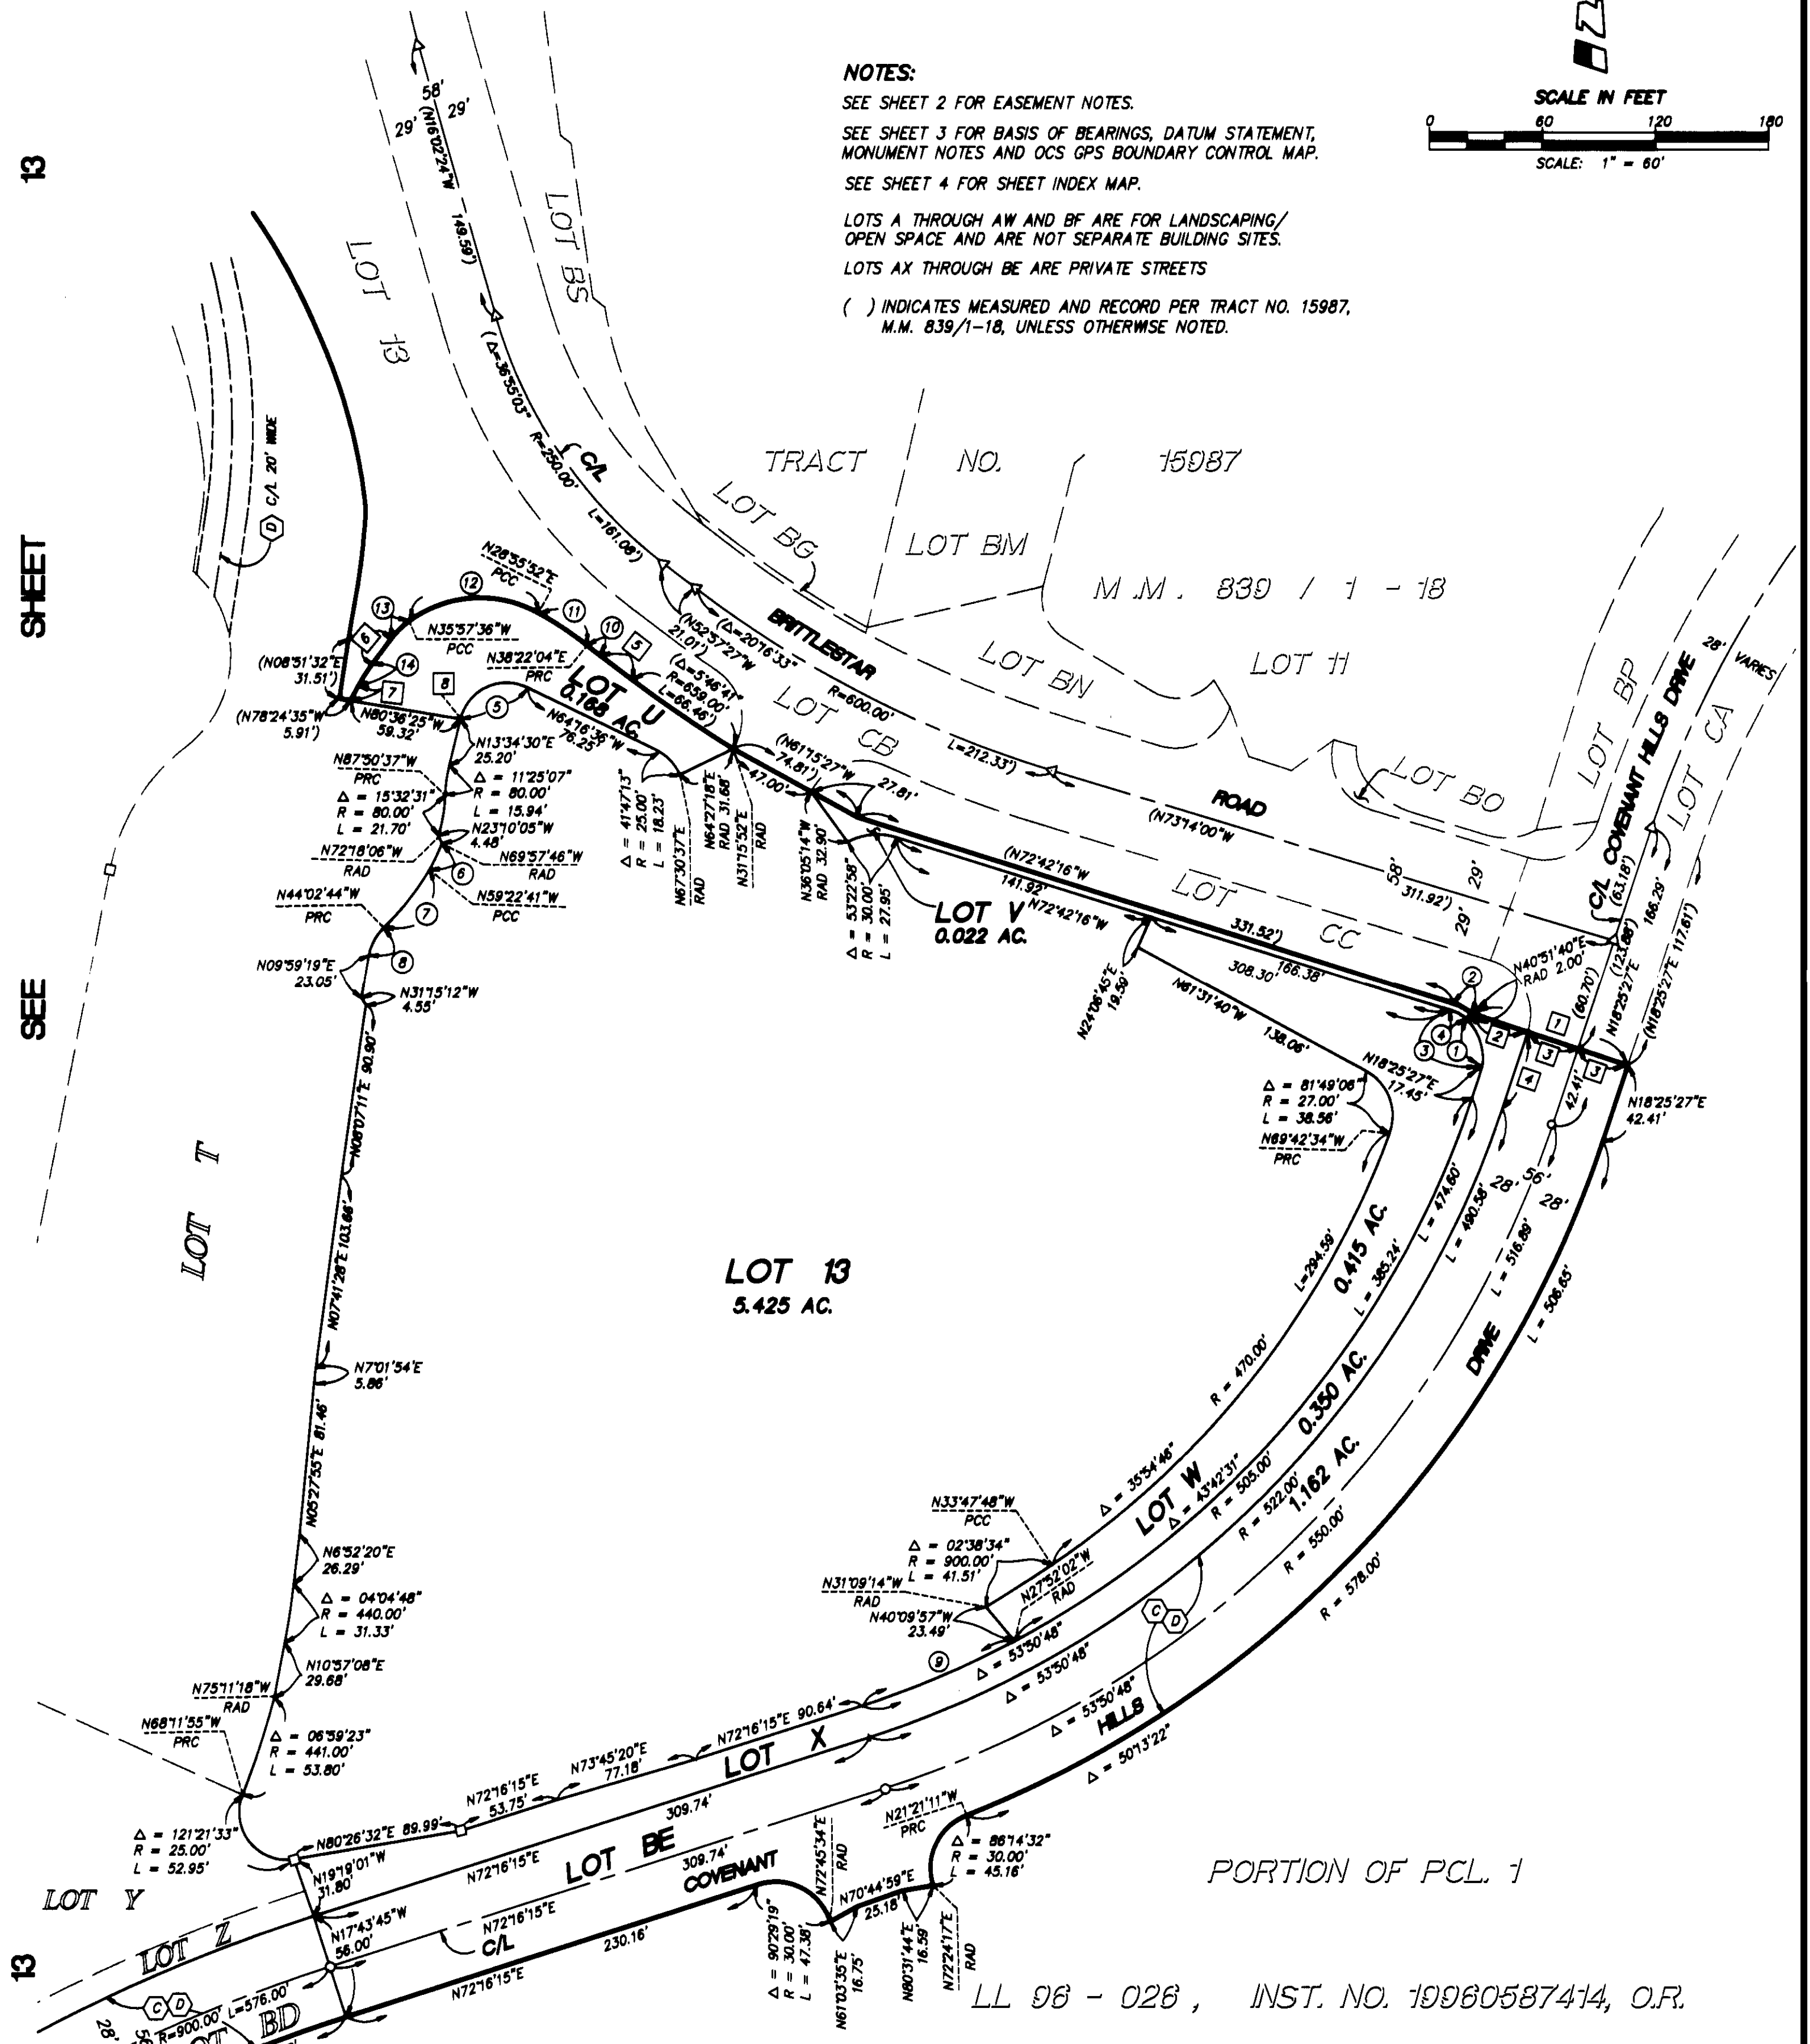

CURVE DATA (THIS SHEET ONLY)

- 1 $\Delta = 67^{\circ}33'47''$ $R = 25.00'$ $L = 29.48'$
- 2 $\Delta = 23^{\circ}33'56''$ $R = 27.00'$ $L = 11.11'$
- 3 $\Delta = 91^{\circ}07'43''$ $R = 25.00'$ $L = 39.76'$
- 4 $\Delta = 23^{\circ}33'56''$ $R = 25.00'$ $L = 10.28'$
- 5 $\Delta = 102^{\circ}08'54''$ $R = 25.00'$ $L = 44.57'$
- 6 $\Delta = 10^{\circ}35'05''$ $R = 83.00'$ $L = 15.33'$
- 7 $\Delta = 15^{\circ}19'57''$ $R = 147.00'$ $L = 39.34'$
- 8 $\Delta = 35^{\circ}57'57''$ $R = 27.00'$ $L = 16.95'$
- 9 $\Delta = 10^{\circ}08'17''$ $R = 505.00'$ $L = 89.36'$
- 10 $\Delta = 01^{\circ}19'31''$ $R = 308.00'$ $L = 7.15'$
- 11 $\Delta = 09^{\circ}26'12''$ $R = 190.00'$ $L = 31.29'$
- 12 $\Delta = 64^{\circ}53'28''$ $R = 64.00'$ $L = 72.48'$
- 13 $\Delta = 16^{\circ}51'28''$ $R = 45.00'$ $L = 13.24'$
- 14 $\Delta = 08^{\circ}33'21''$ $R = 100.00'$ $L = 14.93'$

COURSE DATA (THIS SHEET ONLY)

- 1 $(N71^{\circ}34'33''W \text{ RAD } 87.70')$
- 2 $(N71^{\circ}34'33''W \text{ RAD } 31.70')$
- 3 $(N71^{\circ}34'33''W \text{ RAD } 28.00')$
- 4 $(N18^{\circ}25'27''E \text{ RAD } 42.41')$
- 5 $(N52^{\circ}57'27''W \text{ RAD } 21.01')$
- 6 $(N37^{\circ}10'56''E \text{ RAD } 15.72')$
- 7 $(N28^{\circ}37'35''E \text{ RAD } 8.81')$
- 8 $(N76^{\circ}25'30''W \text{ RAD } 42.41')$

849 14

849 15

SHEET 15 OF 15 SHEETS

TRACT NO. 15986

IN THE UNINCORPORATED TERRITORY OF ORANGE COUNTY, CALIFORNIA

SEPTEMBER 2002

JAMES F. GILLEN, L.S. 5557



HUITT-ZOLLARS

13 NUMBERED LOTS AND 58 LETTERED LOTS

120.329 ACRES

ALL OF VESTING TENTATIVE
TRACT NO. 15986

DATE OF SURVEY:
JANUARY 1999 &
MARCH 2002

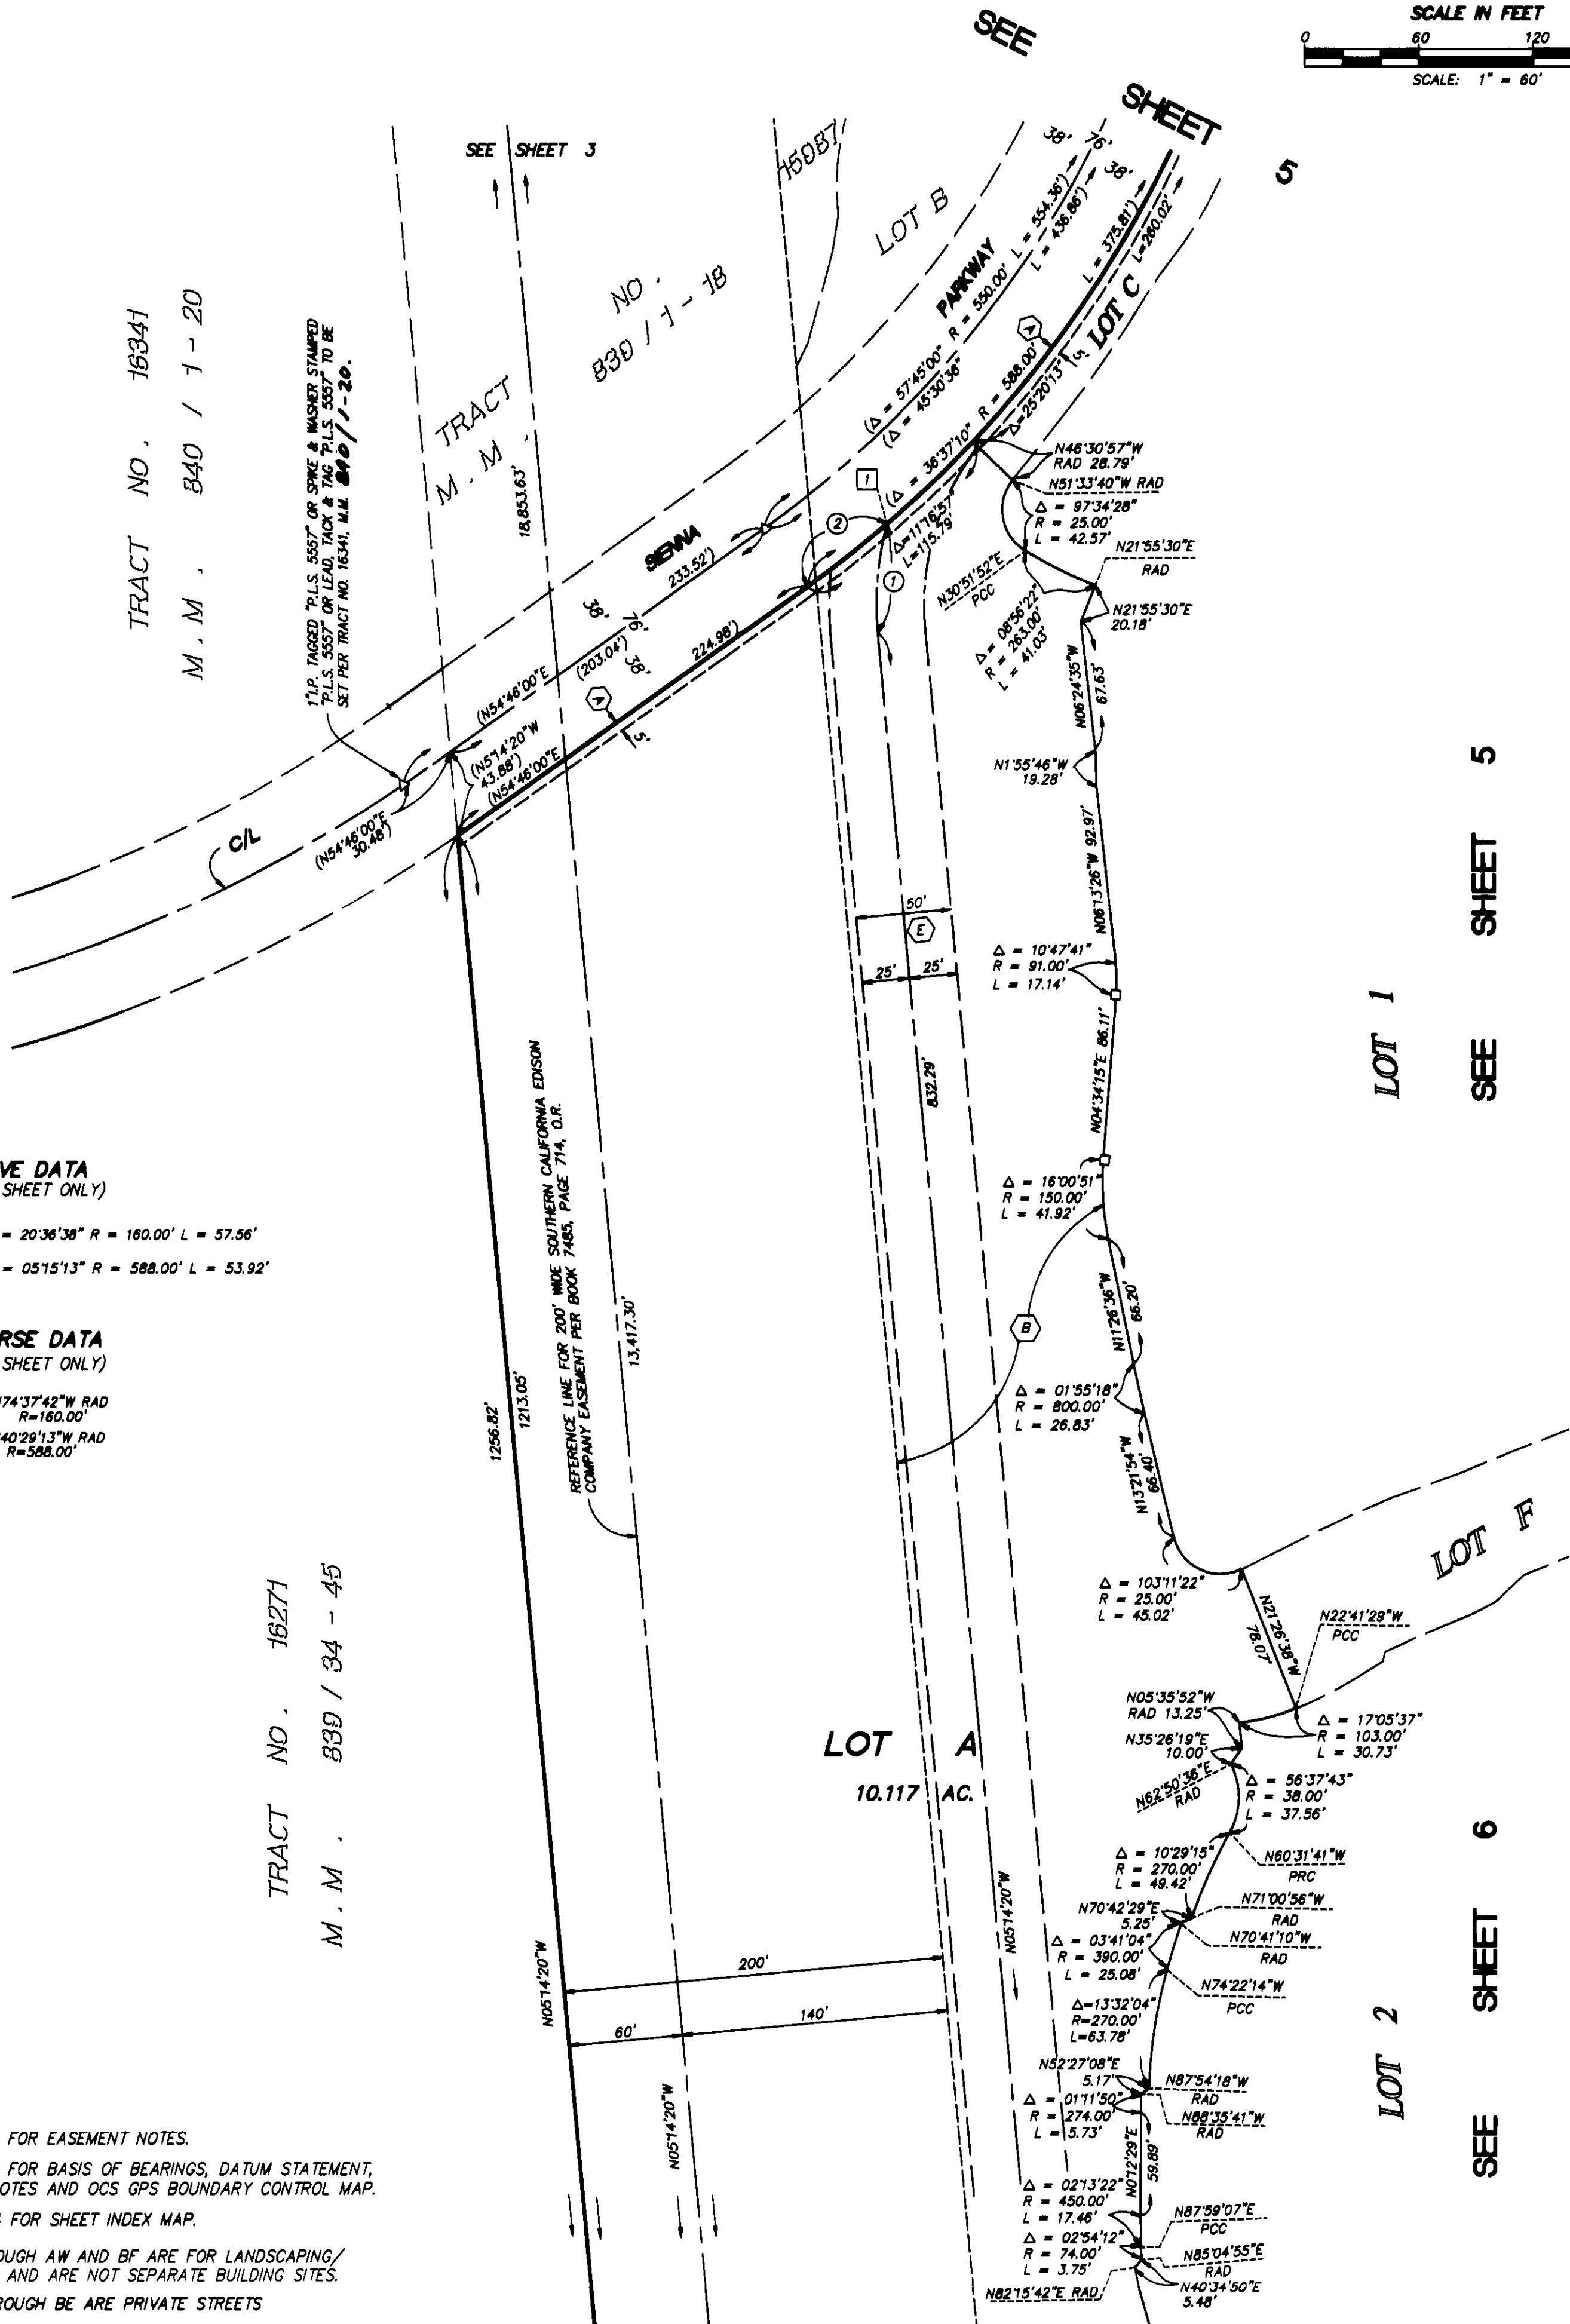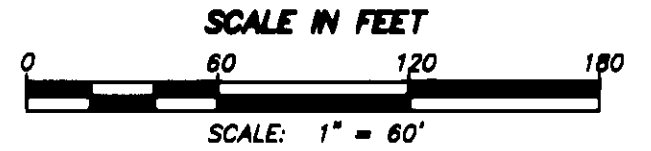

CURVE DATA (THIS SHEET ONLY)

- ① $\Delta = 20^\circ 36' 38''$ R = 160.00' L = 57.56'
- ② $\Delta = 05^\circ 15' 13''$ R = 588.00' L = 53.92'

COURSE DATA (THIS SHEET ONLY)

- ① (N74°37'42"W RAD R=160.00')
- ② (N40°28'13"W RAD R=588.00')

NOTES:

SEE SHEET 2 FOR EASEMENT NOTES.

SEE SHEET 3 FOR BASIS OF BEARINGS, DATUM STATEMENT, MONUMENT NOTES AND OCS GPS BOUNDARY CONTROL MAP.

SEE SHEET 4 FOR SHEET INDEX MAP.

LOTS A THROUGH AW AND BF ARE FOR LANDSCAPING/ OPEN SPACE AND ARE NOT SEPARATE BUILDING SITES.

LOTS AX THROUGH BE ARE PRIVATE STREETS

() INDICATES MEASURED AND RECORD PER TRACT NO. 15987, M.M. 839 / 1-18, UNLESS OTHERWISE NOTED.

10036763\7M\15986\1598615.DWG

849 15