

839

1

SHEET 1 OF 18 SHEETS

TRACT NO. 15987

ALL OF VESTING TENTATIVE
TRACT NO. 15987DATE OF SURVEY:
JANUARY 1999 &
APRIL 2002IN THE UNINCORPORATED TERRITORY OF ORANGE COUNTY, CALIFORNIA
BEING A SUBDIVISION OF A PORTION OF PARCEL 1 OF LOT LINE ADJUSTMENT NO. LL 96-026
AS SHOWN ON EXHIBIT "B" ATTACHED TO THAT CERTAIN DOCUMENT RECORDED NOVEMBER 21,
1996 AS INSTRUMENT NO. 19960587414 OF OFFICIAL RECORDS, RECORDS OF ORANGE COUNTY,
CALIFORNIA.

JULY 2002

JAMES F. GILLEN, L.S. 5557

HUITT-ZOLLARS

14 NUMBERED LOTS AND 82 LETTERED LOTS

142.174 ACRES

ACCEPTED AND FILED AT THE
REQUEST OF
FIRST AMERICAN TITLE INSURANCE CO.DATE DECEMBER 17, 2002
TIME 02:08 PM FEE \$ 41.00
INSTRUMENT NO. 2002001153/20
BOOK 839 PAGE 1-18 m/mDARLENE J. BLOOM
INTERIM COUNTY CLERK-RECORDERBY Rama Sign
DEPUTY

OWNERSHIP CERTIFICATE:

WE, THE UNDERSIGNED, BEING ALL PARTIES HAVING ANY RECORD TITLE INTEREST IN THE
LAND COVERED BY THIS MAP, DO HEREBY CONSENT TO THE PREPARATION AND RECORDATION
OF SAID MAP, AS SHOWN WITHIN THE DISTINCTIVE BORDER LINE. WE ALSO HEREBY DEDICATE
TO THE PUBLIC FOR STREET PURPOSES: SIENNA PARKWAY, AND
ANTONIO PARKWAY.

WE ALSO HEREBY DEDICATE TO THE COUNTY OF ORANGE:

(1) THE EASEMENTS FOR SIDEWALK PURPOSES AS SHOWN ON SAID MAP.

(2) THE EASEMENT FOR PUBLIC PEDESTRIAN PURPOSES AS SHOWN ON SAID MAP.

(3) THE EASEMENT FOR PUBLIC ACCESS PURPOSES AS SHOWN ON SAID MAP.

(4) THE EASEMENT FOR SCENIC PRESERVATION PURPOSES AS SHOWN ON SAID MAP FOR
THE PURPOSES AND SUBJECT TO THE SAME CONDITIONS AND LIMITATIONS AS SHOWN IN THAT
CERTAIN EASEMENT RECORDED SEPTEMBER 19, 1991 AS DOCUMENT 91-511820 OF OFFICIAL RECORDS.(5) THE EASEMENTS FOR EMERGENCY ACCESS PURPOSES OVER ALL OF LOTS BT, BU, BV, BW, BX, BY, BZ,
CA, AND CB AS SHOWN ON SAID MAP.WE ALSO HEREBY RELEASE AND RELINQUISH TO THE COUNTY OF ORANGE ALL VEHICULAR
ACCESS RIGHTS TO ANTONIO PARKWAY, EXCEPT AT APPROVED ACCESS LOCATIONS.PURSUANT TO SECTION 7050 OF THE GOVERNMENT CODE, WE HEREBY IRREVOCABLY
OFFER TO DEDICATE TO THE COUNTY OF ORANGE LOT 1 IN FEE SIMPLE FOR
PUBLIC LOCAL PARK PURPOSES, TOGETHER WITH THE RIGHT TO GRANT
EASEMENTS FOR PUBLIC UTILITIES OR OTHER ESSENTIAL PURPOSES.WE ALSO HEREBY DEDICATE TO THE COUNTY OF ORANGE AN EASEMENT OVER LOT 2 FOR
PRIVATE PARK PURPOSES, SUBJECT TO THE SAME TERMS AND CONDITIONS AS THAT
CERTAIN DOCUMENT RECORDED OCTOBER 7, 1987 AS INSTRUMENT NO. 87-563594, OF
OFFICIAL RECORDS, COUNTY OF ORANGE.WE ALSO HEREBY DEDICATE TO THE SANTA MARGARITA WATER DISTRICT THE EASEMENTS FOR WATER,
RECYCLED WATER, SEWER, DRAINAGE AND ACCESS PURPOSES OVER THOSE EASEMENT AREAS AS SHOWN
ON SAID MAP, WHICH EASEMENTS SHALL BE SUBJECT TO THE SAME CONDITIONS AS ARE SHOWN IN
THAT CERTAIN GRANT OF EASEMENT TO SANTA MARGARITA WATER DISTRICT RECORDED SEPTEMBER 12,
2002 AS INSTRUMENT NO. 20020799401, OF OFFICIAL RECORDS, COUNTY OF ORANGE.

DMB LADERA, L.L.C., A DELAWARE LIMITED LIABILITY COMPANY.

BY: RANCHO MISSION VIEJO, L.L.C., A DELAWARE LIMITED LIABILITY COMPANY,
AS AGENT AND/OR MANAGERBY: [Signature]
PRINT NAME: Donald T. Strallin
PRINT TITLE: DIRECTOR OF Community Dev.BY: [Signature]
PRINT NAME: Stephen C. Schrank
PRINT TITLE: Executive Vice President

CERTIFICATE OF ACCEPTANCE

THE UNDERSIGNED, BEING THE DULY APPOINTED AGENT OF THE SANTA MARGARITA WATER
DISTRICT, A PUBLIC CORPORATION OF ORANGE COUNTY, CALIFORNIA, PURSUANT TO ITS
RESOLUTION NO. 88-10-2, DOES HEREBY ACCEPT ON BEHALF OF SAID DISTRICT THE EASEMENTS
FOR WATER, RECYCLED WATER, SEWER, DRAINAGE AND ACCESS PURPOSES, AS DEDICATED AND AS
SHOWN ON THIS TRACT MAP, BY AND BETWEEN THE SANTA MARGARITA WATER DISTRICT AND
DMB LADERA, L.L.C., AND DOES HEREBY CERTIFY THAT THE GRANTEE CONSENTS TO THE RECORDATION
OF SAID TRACT.[Signature]
DANIEL R. FERONS, CHIEF ENGINEER
SANTA MARGARITA WATER DISTRICT.

AUTOMATIC FIRE SPRINKLER NOTE:

ALL COMMERCIAL STRUCTURES GREATER THAN 6,000 SQUARE FEET; ALL MULTIFAMILY RESIDENTIAL
STRUCTURES; ALL SINGLE-FAMILY STRUCTURES EXCEEDING 5,500 SQUARE FEET, AND ALL STRUCTURES
EXCEEDING FIRE DEPARTMENT ACCESS REQUIREMENTS SHALL BE PROTECTED BY AN AUTOMATIC
SPRINKLER SYSTEM.

SPECIAL FIRE PROTECTION NOTE:

PROPERTY IS IN A SPECIAL FIRE PROTECTION AREA AND MUST MEET ALL REQUIREMENTS
FOR DEVELOPMENT WITHIN THE AREA.

HIGH FIRE HAZARD AREA NOTE:


THE LOTS SHOWN ON THIS MAP ARE IN A HIGH FIRE HAZARD AREA DUE TO
WLD LAND EXPOSURE.

NOTES:

"THE PRIVATE STREETS CONSTRUCTED WITHIN THIS MAP SHALL BE OWNED, OPERATED AND
MAINTAINED BY THE DEVELOPER, SUCCESSORS OR ASSIGNS. THE COUNTY OF ORANGE SHALL
HAVE NO RESPONSIBILITY THEREFORE UNLESS PURSUANT TO APPROPRIATE SECTIONS OF THE
STREETS AND HIGHWAYS CODE OF THE STATE OF CALIFORNIA, THE SAID PRIVATE STREETS
HAVE BEEN ACCEPTED INTO THE COUNTY ROAD SYSTEM BY APPROPRIATE RESOLUTION OF
THE ORANGE COUNTY BOARD OF SUPERVISORS."

SEE SHEET 2 FOR NOTARY ACKNOWLEDGMENTS AND SIGNATURE OMISSIONS.

SURVEYOR'S STATEMENT:

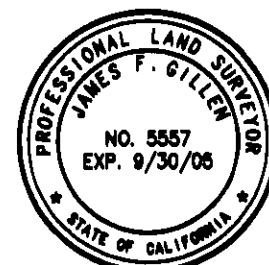THIS MAP WAS PREPARED BY ME OR UNDER MY DIRECTION AND IS BASED UPON A FIELD
SURVEY IN CONFORMANCE WITH THE REQUIREMENTS OF THE SUBDIVISION MAP ACT AND
LOCAL ORDINANCES AT THE REQUEST OF RANCHO MISSION VIEJO, LLC ON APRIL 2002.
I HEREBY STATE THAT ALL MONUMENTS ARE OF THE CHARACTER AND OCCUPY THE
POSITIONS INDICATED, OR THAT THEY WILL BE SET IN SUCH POSITIONS; AND THAT SAID
MONUMENTS ARE SUFFICIENT TO ENABLE THE SURVEY TO BE RETRACED. I HEREBY STATE
THAT THIS FINAL MAP SUBSTANTIALLY CONFORMS TO THE CONDITIONALLY APPROVED
TENTATIVE MAP.[Signature]
JAMES F. GILLEN
L.S. 5557
EXPIRATION DATE: 9/30/05

COUNTY SURVEYOR'S STATEMENT:

I HEREBY STATE THAT I HAVE EXAMINED THIS MAP AND HAVE FOUND IT TO BE
SUBSTANTIALLY IN CONFORMANCE WITH THE TENTATIVE MAP AS FILED WITH, AMENDED AND
APPROVED BY THE ORANGE COUNTY SUBDIVISION COMMITTEE; THAT ALL PROVISIONS OF THE
SUBDIVISION MAP ACT AND COUNTY SUBDIVISION REGULATIONS HAVE BEEN COMPLIED WITH
AND I AM SATISFIED SAID MAP IS TECHNICALLY CORRECT.DATED THIS 25TH DAY OF NOVEMBER, 2002.[Signature]
JOHN CANAS, COUNTY SURVEYOR
LS 4408 EXPIRATION DATE: 09-30-05 BY: Michael K. Sullivan, DEPUTY
LS 6254 EXPIRES 6/30/06

COUNTY TREASURER-TAX COLLECTOR'S CERTIFICATE:


STATE OF CALIFORNIA)
COUNTY OF ORANGE)I HEREBY CERTIFY THAT ACCORDING TO THE RECORDS OF MY OFFICE THERE ARE NO LIENS
AGAINST THE LAND COVERED BY THIS MAP OR ANY PART THEREOF FOR UNPAID STATE,
COUNTY, MUNICIPAL OR LOCAL TAXES OR SPECIAL ASSESSMENTS COLLECTED AS TAXES,
~~EXCEPT TAXES OR SPECIAL ASSESSMENTS COLLECTED AS TAXES NOT YET PAYABLE~~
~~AND DO ALSO HEREBY CERTIFY TO THE RECORDER OF ORANGE COUNTY THAT THE PAYMENTS~~
~~OF THE SUBDIVISION MAP ACT HAVE BEEN COMPLIED WITH REGARDING TAXES TO BE PAID~~
~~FOR PAYMENT OF TAXES OR SPECIAL ASSESSMENTS COLLECTED AS TAXES ON THE LAND~~
~~COVERED BY THIS MAP.~~DATED THIS 5th DAY OF November, 2002.JOHN M.W. MOORLACH
COUNTY TREASURER-TAX COLLECTOR BY: [Signature]
DEPUTY TREASURER-TAX COLLECTOR

CLERK OF THE BOARD OF SUPERVISORS' CERTIFICATE:

STATE OF CALIFORNIA)
COUNTY OF ORANGE)I HEREBY CERTIFY THAT THIS MAP WAS PRESENTED FOR APPROVAL TO THE BOARD OF
SUPERVISORS OF ORANGE COUNTY AT A REGULAR MEETING THEREOF HELD ON THE 16 DAY
OF December, 2002, AND THAT THEREUPON SAID BOARD DID, BY AN ORDER DULY PASSED
AND ENTERED, APPROVE SAID MAP AND DID ACCEPT ON BEHALF OF THE PUBLIC, SUBJECT TO
IMPROVEMENTS: THE DEDICATION FOR STREET PURPOSES OF : SIENNA PARKWAY,
AND ANTONIO PARKWAY.

AND DID ALSO ACCEPT ON BEHALF OF THE COUNTY OF ORANGE:

1. THE EASEMENTS FOR SIDEWALK PURPOSES AS DEDICATED.
2. THE EASEMENT FOR PUBLIC PEDESTRIAN PURPOSES AS DEDICATED.
3. THE EASEMENT FOR PUBLIC ACCESS PURPOSES AS DEDICATED.
4. THE EASEMENT FOR SCENIC PRESERVATION PURPOSES AS DEDICATED.
5. THE EASEMENTS FOR EMERGENCY ACCESS PURPOSES OVER ALL OF LOTS BT, BU, BV, BW, BX, BY, BZ, CA, AND CB AS DEDICATED.
6. THE VEHICULAR ACCESS RIGHTS TO ANTONIO PARKWAY AS RELEASED AND RELINQUISHED.

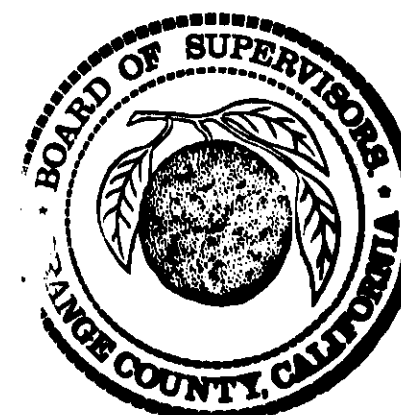AND DID NOT ACCEPT THE IRREVOCABLE OFFER OF: LOT 1 FOR PUBLIC LOCAL PARK
PURPOSES AS DEDICATED.AND DID ACCEPT THE EASEMENT OVER LOT 2 FOR PRIVATE PARK
PURPOSES AS DEDICATED.AND DID ALSO APPROVE SUBJECT MAP PURSUANT TO THE PROVISIONS OF SECTION 66436(a) (3)
OF THE SUBDIVISION MAP ACT.DATED THIS 16 DAY OF December, 2002.[Signature]
DARLENE J. BLOOM
CLERK OF THE BOARD OF SUPERVISORS

839

SHEET 2 OF 18 SHEETS

TRACT NO. 15987

ALL OF VESTING TENTATIVE
TRACT NO. 15987

IN THE UNINCORPORATED TERRITORY OF ORANGE COUNTY, CALIFORNIA

DATE OF SURVEY:
JANUARY 1999 &
APRIL 2002

JULY 2002

JAMES F. GILLEN, L.S. 5557

HUITT-ZOLIARS

14 NUMBERED LOTS AND 82 LETTERED LOTS

142.174 ACRES

DMB LADERA, L.L.C.

STATE OF CALIFORNIA)
COUNTY OF ORANGE)SS

ON THIS 11th DAY OF September, 2002, BEFORE ME,
Tina T. Baker, A NOTARY PUBLIC IN AND FOR SAID STATE,
PERSONALLY APPEARED Donna M. Evans AND
Stephen C. Schuch, PERSONALLY KNOWN TO ME OR PROVED TO ME
ON THE BASIS OF SATISFACTORY EVIDENCE TO BE THE PERSONS WHOSE NAMES
ARE SUBSCRIBED TO THE WITHIN INSTRUMENT AND ACKNOWLEDGED TO ME THAT
THEY EXECUTED THE SAME IN THEIR AUTHORIZED CAPACITIES, AND THAT BY THEIR
SIGNATURES ON THE INSTRUMENT THE PERSONS, OR THE ENTITY UPON BEHALF
OF WHICH THE PERSONS ACTED, EXECUTED THE INSTRUMENT.

WITNESS MY HAND:

MY COMMISSION EXPIRES

8-29-04

Tina T. Baker
NOTARY PUBLIC IN AND FOR SAID STATE IS IN Orange COUNTY.

Tina T. Baker

PRINT NAME

SANTA MARGARITA WATER DISTRICT

STATE OF CALIFORNIA)
COUNTY OF ORANGE)SS

ON THIS 29th DAY OF September, 2002, BEFORE ME,
Andrea M. Evans, A NOTARY PUBLIC IN AND FOR SAID STATE,
PERSONALLY APPEARED DANIEL R. FERONS PERSONALLY KNOWN TO ME
OR PROVED TO ME ON THE BASIS OF SATISFACTORY EVIDENCE TO BE THE
PERSON WHOSE NAME IS SUBSCRIBED TO THE WITHIN INSTRUMENT AND ACKNOWLEDGED
TO ME THAT HE EXECUTED THE SAME IN HIS AUTHORIZED CAPACITY, AND THAT
BY HIS SIGNATURE ON THE INSTRUMENT THE PERSON, OR THE ENTITY UPON BEHALF
OF WHICH THE PERSON ACTED, EXECUTED THE INSTRUMENT.

WITNESS MY HAND:

MY COMMISSION EXPIRES

4/8/04

Andrea M. Evans
NOTARY PUBLIC IN AND FOR SAID STATE IS IN Orange COUNTY.

ANDREA M. EVANS

PRINT NAME

SIGNATURE OMISSIONS:

IN ACCORDANCE WITH THE PROVISIONS OF SECTION 66436(a) (3) OF THE SUBDIVISION
MAP ACT, THE FOLLOWING SIGNATURES HAVE BEEN OMITTED:

1. SOUTHERN CALIFORNIA EDISON COMPANY, HOLDER OF AN EASEMENT FOR PUBLIC UTILITIES AND
INCIDENTAL PURPOSES RECORDED APRIL 16, 1965 IN BOOK 7485, PAGE 714 OF OFFICIAL RECORDS.
2. LADERA DEVELOPMENT COMPANY, L.L.C., HOLDER OF OIL, GAS, MINERAL, AND WATER RIGHTS
RECORDED DECEMBER 10, 1996 AS INSTRUMENT NO. 19960624029 OF OFFICIAL RECORDS.
3. SANTA MARGARITA WATER DISTRICT, HOLDER OF AN EASEMENT FOR SEWER, WATER,
RECYCLED WATER AND ACCESS PURPOSES RECORDED SEPTEMBER 18, 2002 AS
INST. NO. 20020799401, OF OFFICIAL RECORDS.

EASEMENT NOTES:

- (A) INDICATES EASEMENT FOR SCENIC PRESERVATION PURPOSES DEDICATED TO THE COUNTY OF ORANGE.
- (B) INDICATES SIDEWALK EASEMENT DEDICATED TO THE COUNTY OF ORANGE.
- (C) INDICATES PUBLIC PEDESTRIAN EASEMENT DEDICATED TO THE COUNTY OF ORANGE.
- (D) INDICATES SEWER, WATER, RECYCLED WATER AND ACCESS EASEMENT DEDICATED TO THE SANTA MARGARITA
WATER DISTRICT.
- (E) INDICATES PROPOSED ACCESS EASEMENT.
- (F) INDICATES DRAINAGE EASEMENT DEDICATED TO THE SANTA MARGARITA WATER DISTRICT.
- (G) INDICATES PUBLIC ACCESS EASEMENT DEDICATED TO THE COUNTY OF ORANGE.
- (H) INDICATES AN EASEMENT FOR PRIVATE PARK PURPOSES DEDICATED TO THE
COUNTY OF ORANGE.

TRACT NO. 15987

IN THE UNINCORPORATED TERRITORY OF ORANGE COUNTY, CALIFORNIA

JULY 2002

JAMES F. GILLEN, L.S. 5557

HUITT-ZOLLARS

14 NUMBERED LOTS AND 82 LETTERED LOTS


142.174 ACRES

ALL OF VESTING TENTATIVE
TRACT NO. 15987

DATE OF SURVEY:
JANUARY 1999 &
APRIL 2002

MONUMENT NOTES:

- INDICATES LOCATION OF 2" I.P. TAGGED "P.L.S. 5557" OR SPIKE & WASHER STAMPED "P.L.S. 5557" OR LEAD, TACK & TAG "P.L.S. 5557" TO BE SET PRIOR TO RECORDATION.
- ▲ FOUND OCS WELL MONUMENT WITH 2 1/2" BRASS DISK STAMPED "ORANGE COUNTY SURVEYOR" PER TRACT NO. 16156, M.M. 812/40-48.
- △ INDICATES LOCATION OF 1" I.P. TAGGED "P.L.S. 5557" OR SPIKE & WASHER STAMPED "P.L.S. 5557" OR LEAD, TACK & TAG "P.L.S. 5557" TO BE SET PER TRACT NO. 16025, M.M. 812/40-48, UNLESS OTHERWISE NOTED.
- INDICATES LOCATION OF 2" I.P. TAGGED "P.L.S. 5557" OR SPIKE & WASHER STAMPED "P.L.S. 5557" OR LEAD, TACK & TAG "P.L.S. 5557" TO BE SET WITHIN 90 DAYS AFTER ACCEPTANCE OF IMPROVEMENTS, UNLESS OTHERWISE NOTED.
- INDICATES LOCATION OF 1" I.P. TAGGED "P.L.S. 5557" OR SPIKE & WASHER STAMPED "P.L.S. 5557" OR LEAD, TACK & TAG "P.L.S. 5557" TO BE SET WITHIN 90 DAYS AFTER ACCEPTANCE OF IMPROVEMENTS.
- 2" I.P. TAGGED "P.L.S. 5557" OR SPIKE & WASHER STAMPED "P.L.S. 5557" OR LEAD, TACK & TAG "P.L.S. 5557" TO BE SET AT ALL TRACT BOUNDARY CORNERS WITHIN 90 DAYS AFTER ACCEPTANCE OF IMPROVEMENTS, UNLESS OTHERWISE NOTED.
- INDICATES LOCATION OF OCS WELL MONUMENT WITH A 2" BRASS DISK STAMPED "PLS 5557" TO BE SET WITHIN 90 DAYS AFTER ACCEPTANCE OF IMPROVEMENTS.
- A FD. 2 1/2" IRON PIPE W/2" OCS BRASS CAP STAMPED "GPS 1448 9-95" PER TRACT NO. 16203, M.M. 826/8-20 AND RECORDS ON FILE IN THE ORANGE COUNTY SURVEYORS OFFICE.
- B FD. 2 1/2" IRON PIPE W/2" OCS BRASS CAP STAMPED "GPS 1417 9-95" PER TRACT NO. 16203, M.M. 826/8-20 AND RECORDS ON FILE IN THE ORANGE COUNTY SURVEYORS OFFICE.
- NO MONUMENTATION TO BE SET AT BC'S AND EC'S OF STREET RIGHT OF WAY LINES, UNLESS OTHERWISE SHOWN. NO ADDITIONAL MONUMENTS TO BE SET AT THE INTERIOR LOT CORNERS, OTHER THAN THOSE SHOWN.
- () INDICATES MEASURED AND RECORD PER TRACT NO. 16156, M.M. 812/40-48.

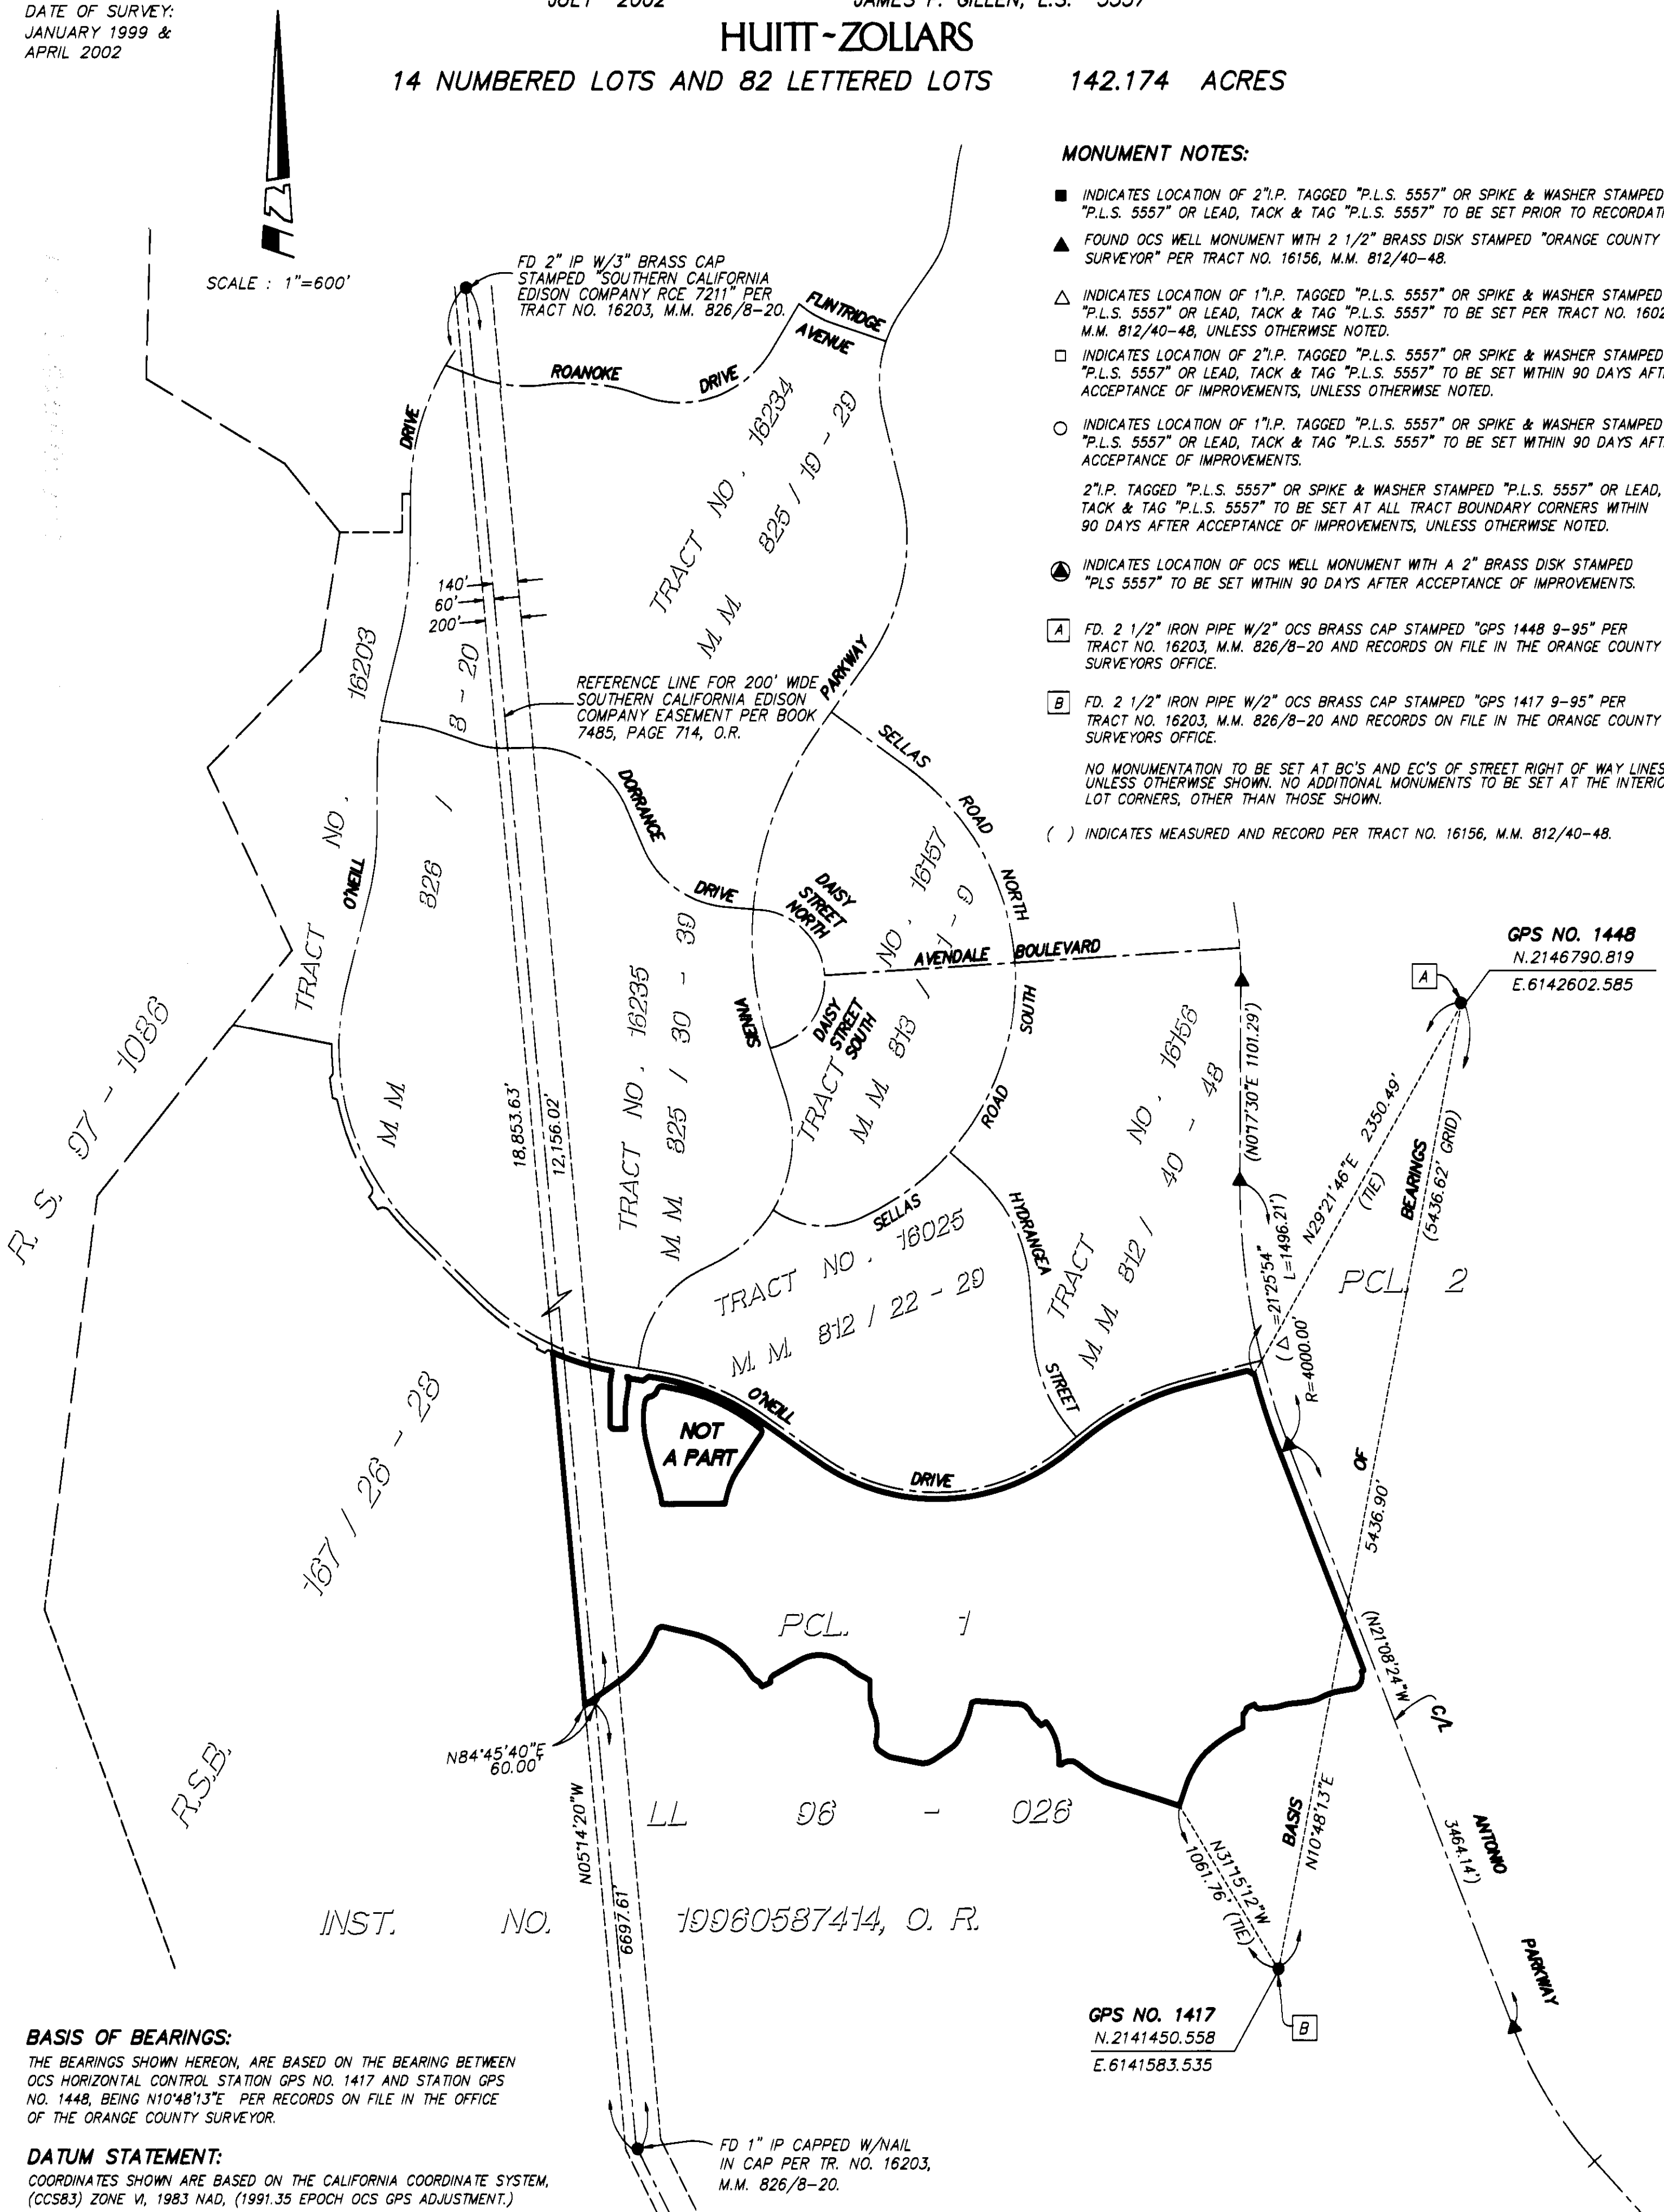

BASIS OF BEARINGS:

THE BEARINGS SHOWN HEREON, ARE BASED ON THE BEARING BETWEEN OCS HORIZONTAL CONTROL STATION GPS NO. 1417 AND STATION GPS NO. 1448, BEING N10°48'13"E PER RECORDS ON FILE IN THE OFFICE OF THE ORANGE COUNTY SURVEYOR.

DATUM STATEMENT:

COORDINATES SHOWN ARE BASED ON THE CALIFORNIA COORDINATE SYSTEM, (CCS83) ZONE VI, 1983 NAD, (1991.35 EPOCH OCS GPS ADJUSTMENT.)

ALL DISTANCES SHOWN ARE GROUND, UNLESS OTHERWISE NOTED. TO OBTAIN A GRID DISTANCE, MULTIPLY THE GROUND DISTANCE BY 0.999948295.

NOTE:

SEE SHEET 4 FOR SHEET INDEX MAP.

OCS GPS BOUNDARY CONTROL MAP

SHEET 4 OF 18 SHEETS

TRACT NO. 15987

ALL OF VESTING TENTATIVE
TRACT NO. 15987

IN THE UNINCORPORATED TERRITORY OF ORANGE COUNTY, CALIFORNIA

JULY 2002



JAMES F. GILLEN, L.S. 5557

DATE OF SURVEY:
JANUARY 1999 &
APRIL 2002

HUITT-ZOLLARS

14 NUMBERED LOTS AND 82 LETTERED LOTS

142.174 ACRES

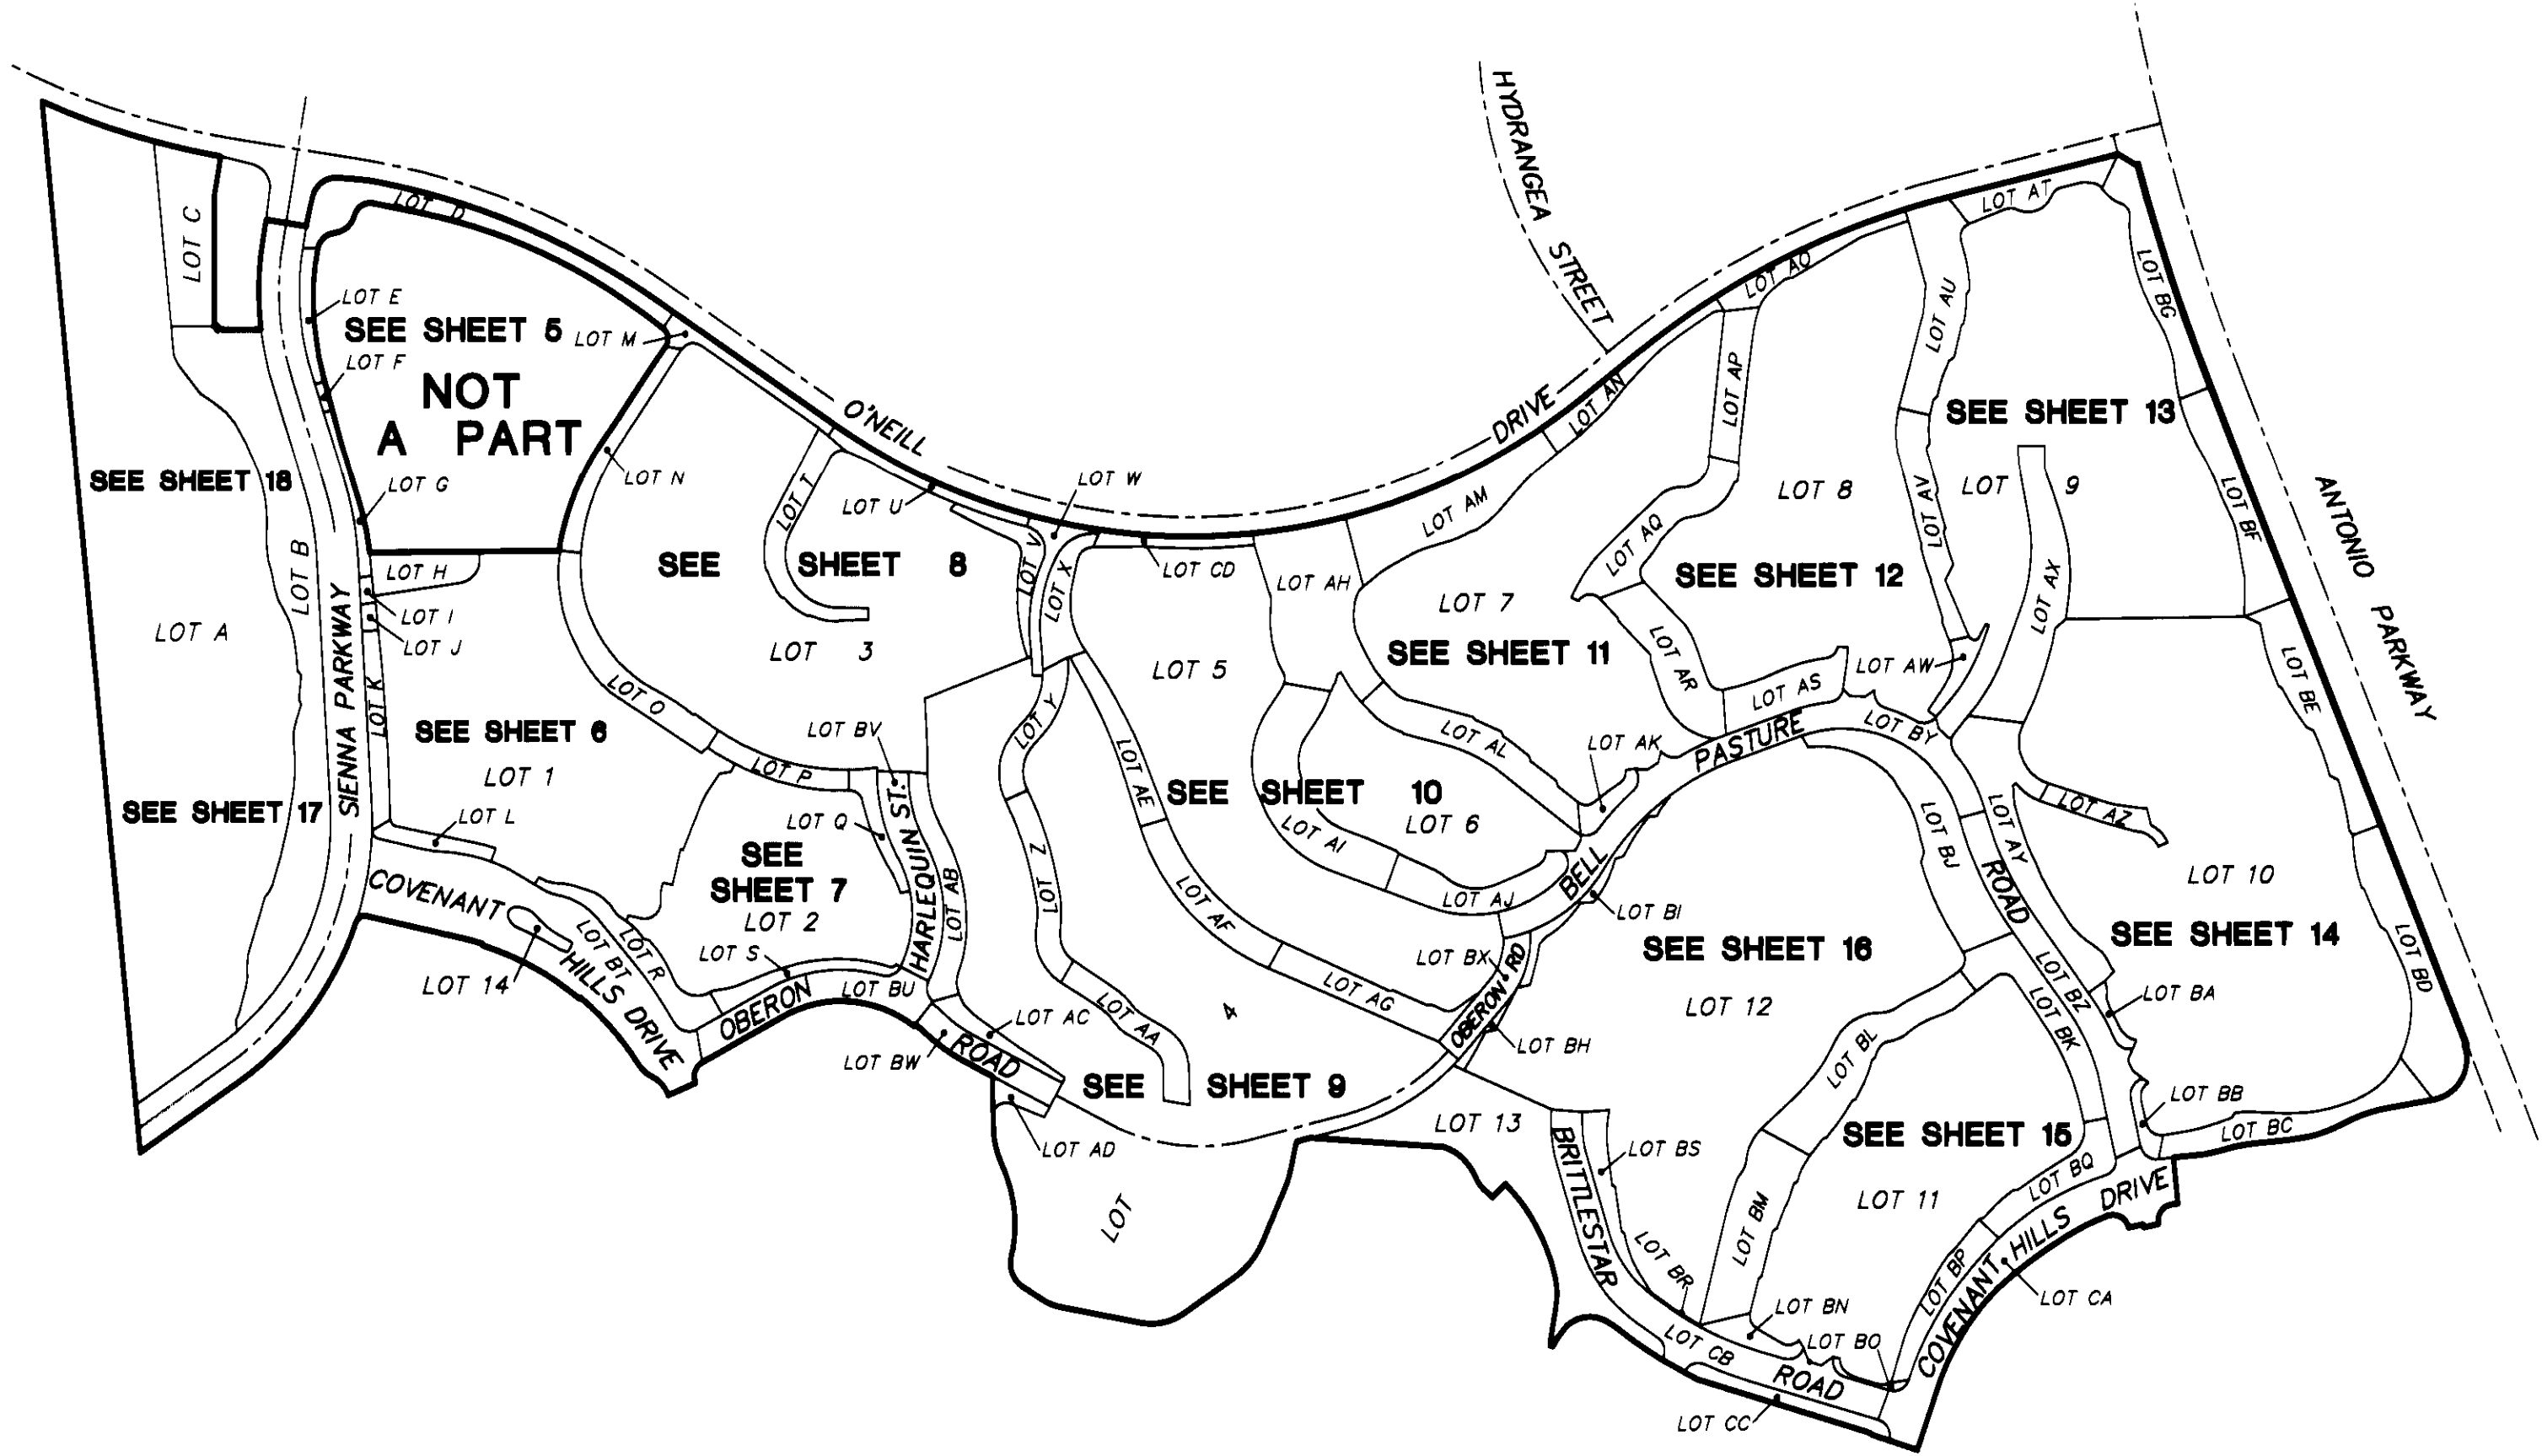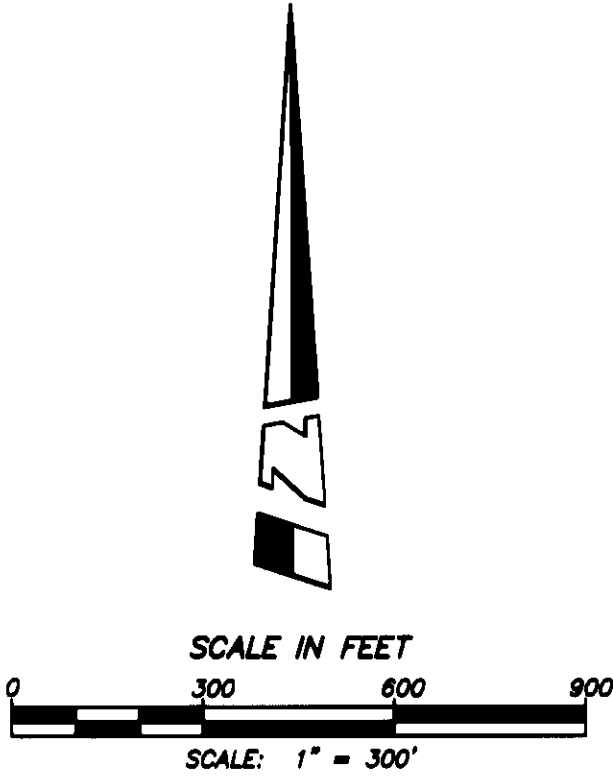

SHEET INDEX MAP

SHEET 5 OF 18 SHEETS
ALL OF VESTING TENTATIVE
TRACT NO. 15987

TRACT NO. 15987

IN THE UNINCORPORATED TERRITORY OF ORANGE COUNTY, CALIFORNIA

JULY 2002


JAMES F. GILLEN, L.S. 5557

HUITT-ZOLLARS

14 NUMBERED LOTS AND 82 LETTERED LOTS

142.174 ACRES

DATE OF SURVEY:
JANUARY 1999 &
APRIL 2002

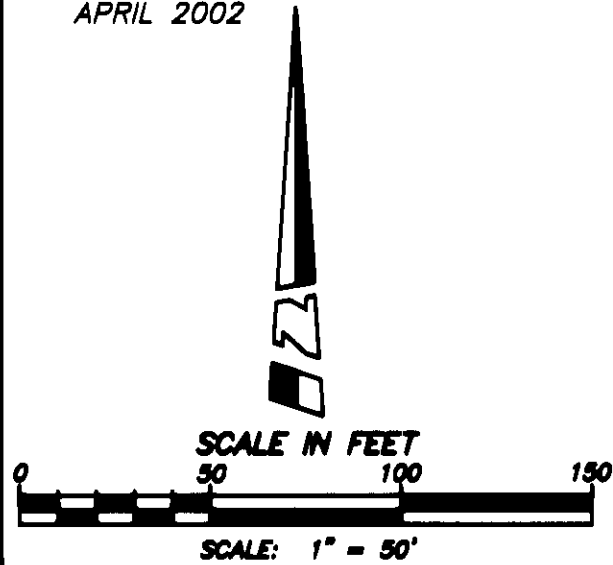

COURSE DATA: (THIS SHEET ONLY)

- | | |
|---|--------------------------|
| 1 | [N80°50'45"W RAD 76.00'] |
| 2 | [N80°50'45"W 38.00'] |
| 3 | [(N55°00'00"W 404.35')] |

NOTES:

SEE SHEET 2 FOR EASEMENT NOTES.

SEE SHEET 3 FOR BASIS OF BEARINGS, DATUM STATEMENT,
MONUMENT NOTES AND OCS GPS BOUNDARY CONTROL MAP.


SEE SHEET 4 FOR SHEET INDEX MAP.

LOTS A THROUGH BS AND LOTS CC AND CD ARE FOR LANDSCAPING/
OPEN SPACE AND ARE NOT SEPARATE BUILDING SITES.

LOTS BT THROUGH CB ARE PRIVATE STREETS.

(()) INDICATES MEASURED AND RECORD PER TRACT NO. 16025,
M.M. 812/22-29.

[] INDICATES MEASURED AND RECORD PER TRACT NO. 16235,
M.M. 825/30-39.

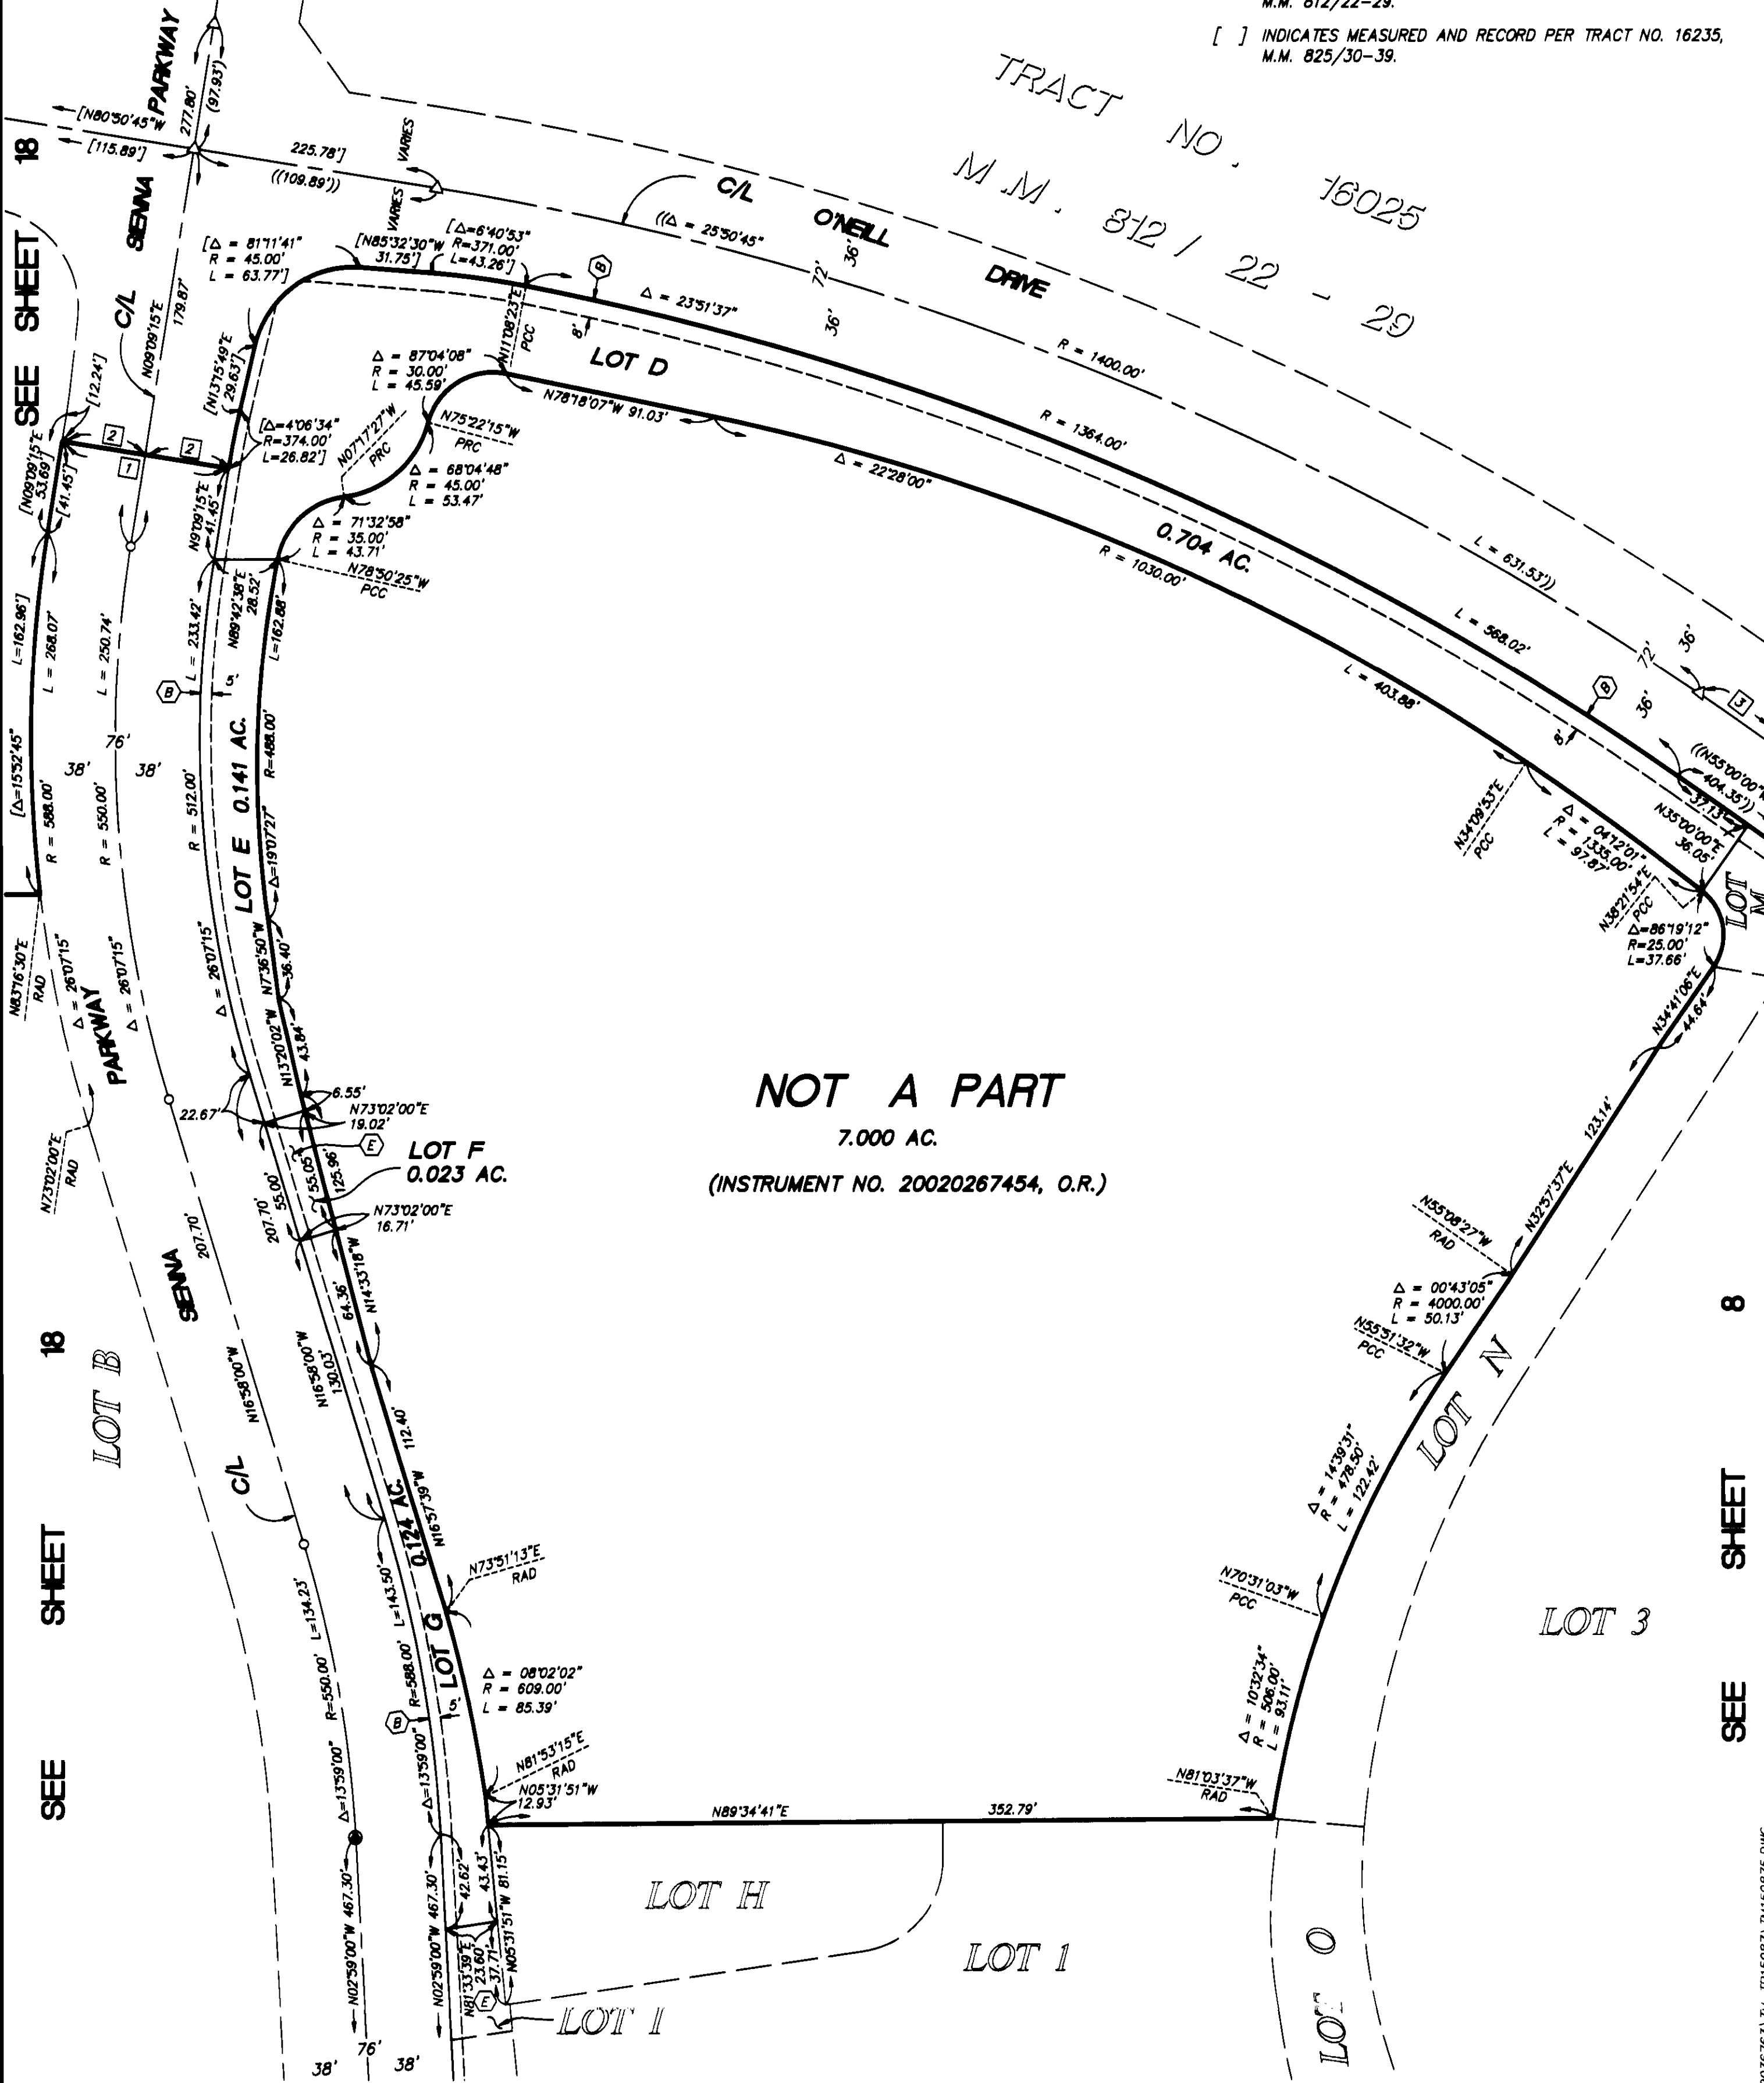

NOT A PART
7.000 AC.
(INSTRUMENT NO. 20020267454, O.R.)

TRACT NO. 16025
M.M. 812 / 22 - 29
O'NEILL DRIVE

SEE SHEET 8

LOT 3

SEE SHEET 6

SHEET 6 OF 18 SHEETS

TRACT NO. 15987

IN THE UNINCORPORATED TERRITORY OF ORANGE COUNTY, CALIFORNIA

JULY 2002

JAMES F. GILLEN, L.S. 5557


ALL OF VESTING TENTATIVE
TRACT NO. 15987

DATE OF SURVEY:
JANUARY 1999 &
APRIL 2002

HUITT-ZOLLARS

14 NUMBERED LOTS AND 82 LETTERED LOTS

142.174 ACRES

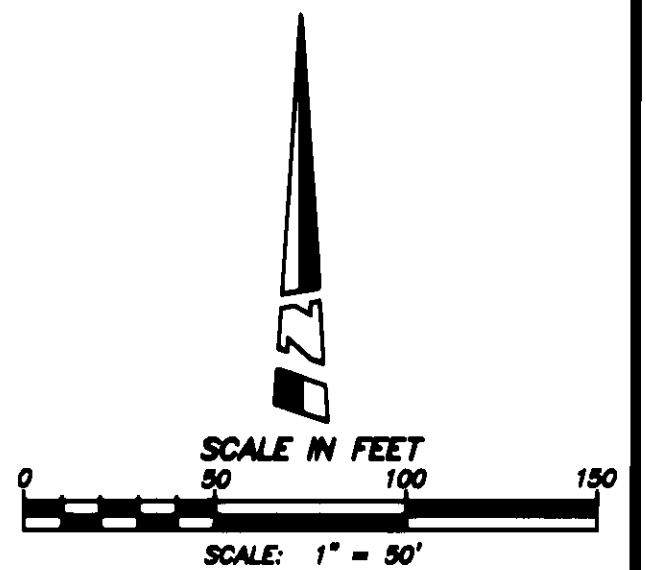

SEE SHEET 5

NOT A PART

8


SEE SHEET 8

COURSE DATA (THIS SHEET ONLY)

- | | |
|---|--------------------|
| 1 | N81°33'39"E 23.60' |
| 2 | N75°06'53"W 20.90' |
| 3 | N18°04'29"E 11.95' |
| 4 | N31°22'58"E 15.58' |

CURVE DATA (THIS SHEET ONLY)

- | | |
|----|--------------------------------------|
| 1 | Δ = 07°37'58" R = 294.00' L = 39.17' |
| 2 | Δ = 04°25'51" R = 588.00' L = 45.47' |
| 3 | Δ = 50°20'32" R = 50.00' L = 43.93' |
| 4 | Δ = 33°50'28" R = 50.00' L = 29.53' |
| 5 | Δ = 16°30'04" R = 50.00' L = 14.40' |
| 6 | Δ = 117°33'18" R = 15.00' L = 30.78' |
| 7 | Δ = 38°50'55" R = 40.00' L = 27.12' |
| 8 | Δ = 25°07'07" R = 40.00' L = 17.54' |
| 9 | Δ = 13°43'48" R = 40.00' L = 9.59' |
| 10 | Δ = 23°20'28" R = 109.00' L = 44.40' |
| 11 | Δ = 03°58'01" R = 109.00' L = 7.55' |
| 12 | Δ = 08°11'07" R = 125.00' L = 17.86' |
| 13 | Δ = 78°06'05" R = 15.00' L = 20.45' |

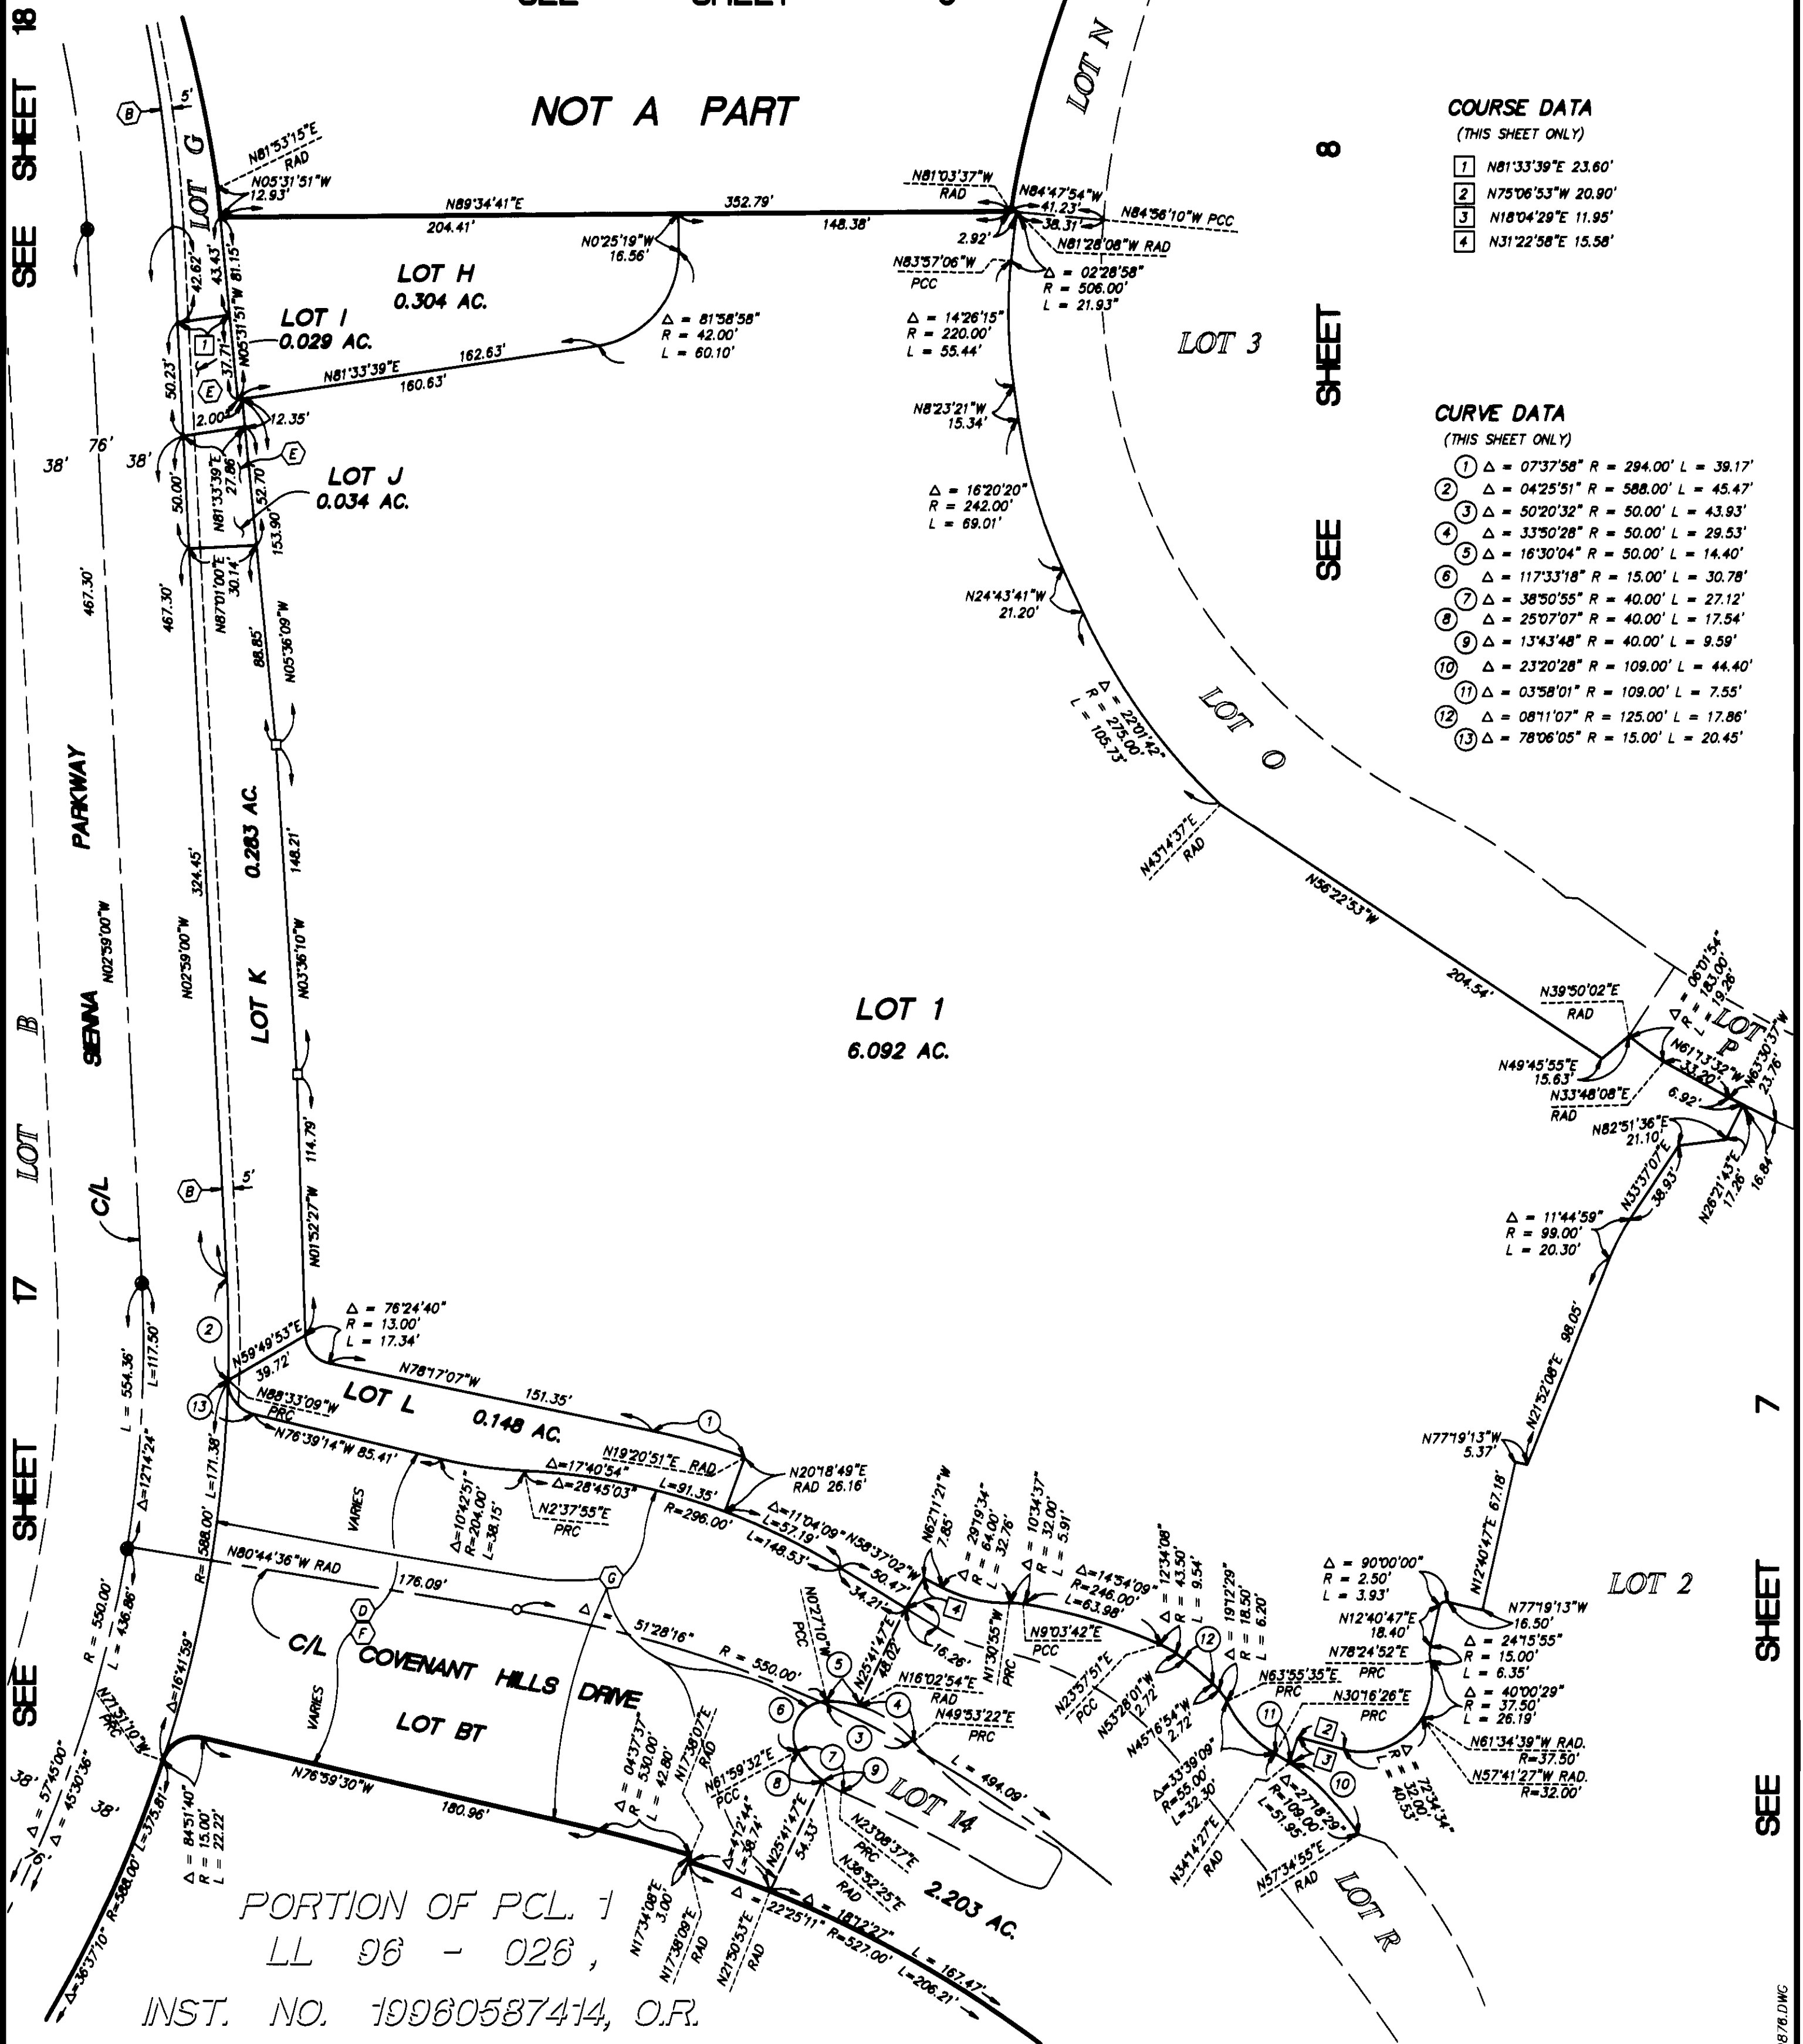

NOTES:

SEE SHEET 2 FOR EASEMENT NOTES.

SEE SHEET 3 FOR BASIS OF BEARINGS, DATUM STATEMENT,
MONUMENT NOTES AND OCS GPS BOUNDARY CONTROL MAP.

SEE SHEET 4 FOR SHEET INDEX MAP.

LOTS A THROUGH BS AND LOTS CC AND CD ARE FOR LANDSCAPING/
OPEN SPACE AND ARE NOT SEPARATE BUILDING SITES.

LOTS BT THROUGH CB ARE PRIVATE STREETS

7

SEE SHEET 7

SEE SHEET 8

SHEET 7 OF 18 SHEETS

ALL OF VESTING TENTATIVE
TRACT NO. 15987

TRACT NO. 15987

IN THE UNINCORPORATED TERRITORY OF ORANGE COUNTY, CALIFORNIA

JULY 2002


JAMES F. GILLEN, L.S. 5557

DATE OF SURVEY:
JANUARY 1999 &
APRIL 2002

HUITT-ZOLLARS

14 NUMBERED LOTS AND 82 LETTERED LOTS

142.174 ACRES

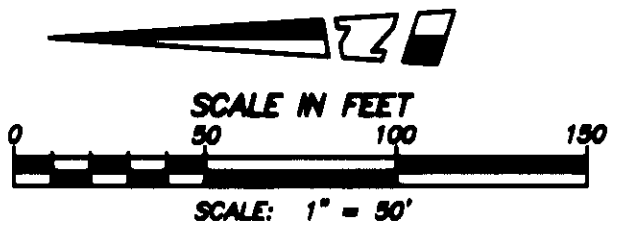

NOTES:

SEE SHEET 2 FOR EASEMENT NOTES.


SEE SHEET 3 FOR BASIS OF BEARINGS, DATUM STATEMENT,
MONUMENT NOTES AND OCS GPS BOUNDARY CONTROL MAP.

SEE SHEET 4 FOR SHEET INDEX MAP.

LOTS A THROUGH BS AND LOTS CC AND CD ARE FOR LANDSCAPING/
OPEN SPACE AND ARE NOT SEPARATE BUILDING SITES.

LOTS BT THROUGH CB ARE PRIVATE STREETS.

SEE SHEET 9

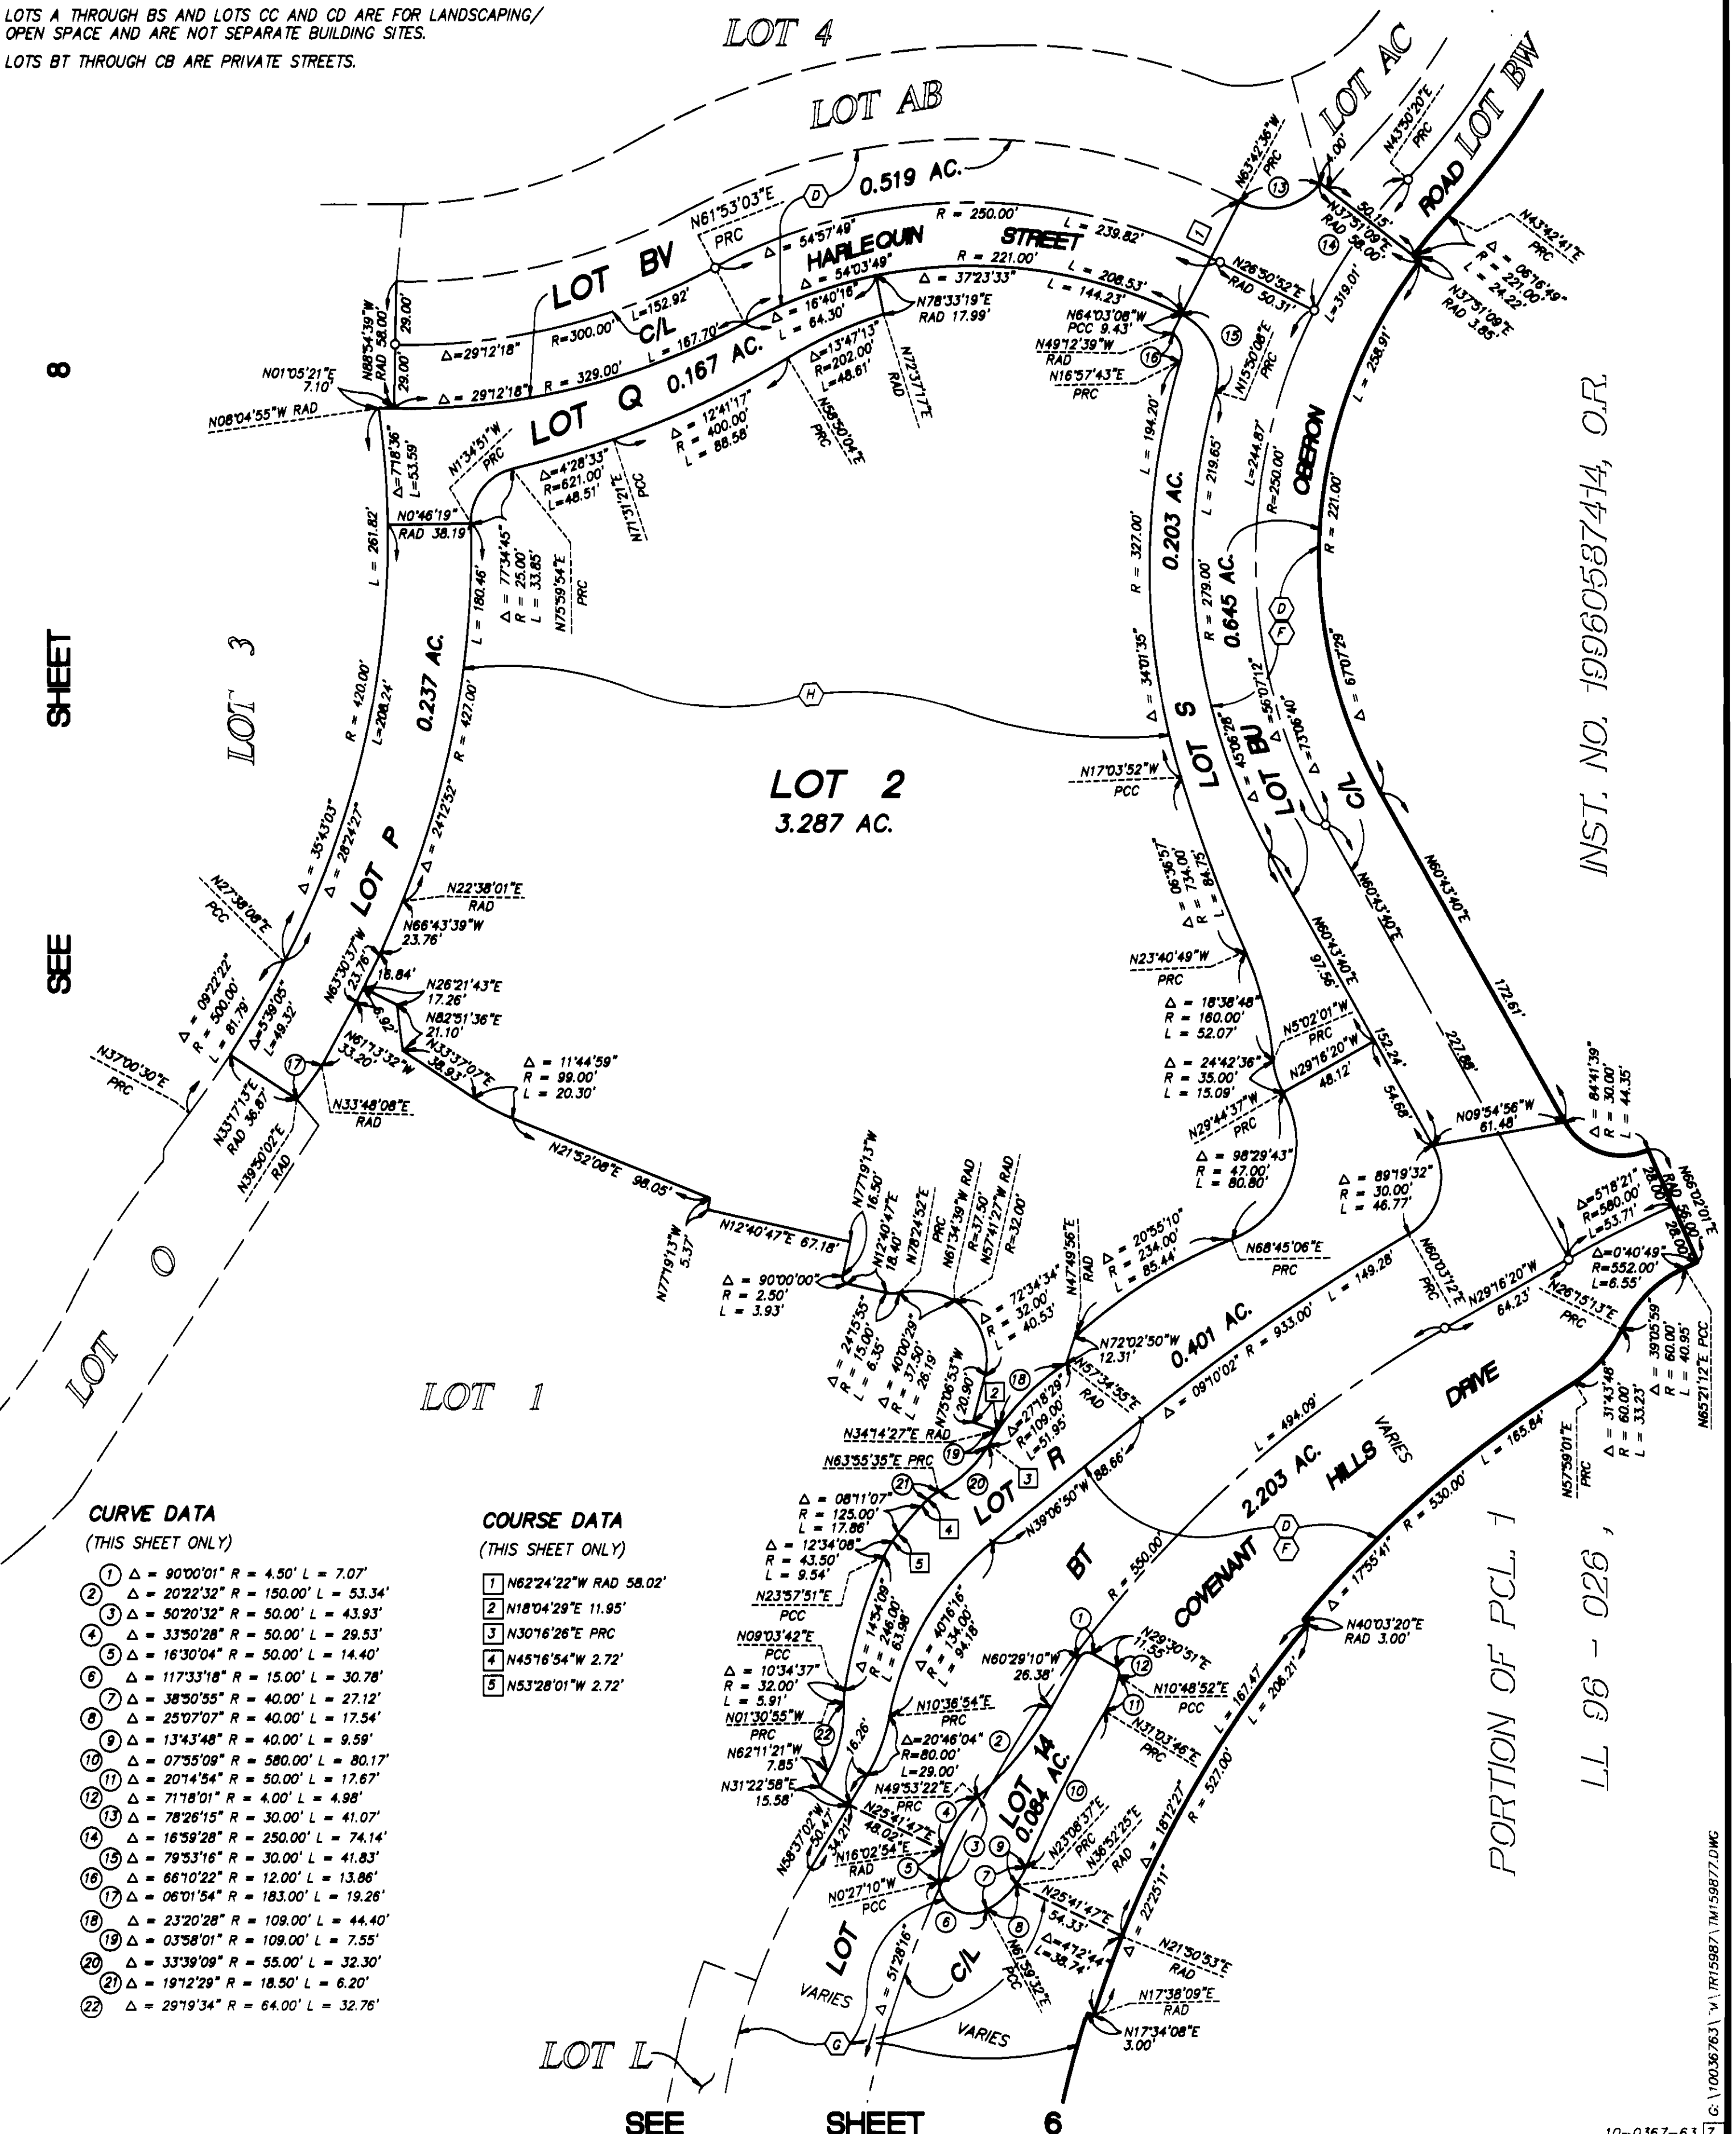

CURVE DATA
(THIS SHEET ONLY)

- 1 Δ = 90°00'01" R = 4.50' L = 7.07'
- 2 Δ = 20°22'32" R = 150.00' L = 53.34'
- 3 Δ = 50°20'32" R = 50.00' L = 43.93'
- 4 Δ = 33°50'28" R = 50.00' L = 29.53'
- 5 Δ = 16°30'04" R = 50.00' L = 14.40'
- 6 Δ = 117°33'18" R = 15.00' L = 30.78'
- 7 Δ = 38°50'55" R = 40.00' L = 27.12'
- 8 Δ = 25°07'07" R = 40.00' L = 17.54'
- 9 Δ = 13°43'48" R = 40.00' L = 9.59'
- 10 Δ = 07°55'09" R = 580.00' L = 80.17'
- 11 Δ = 20°14'54" R = 50.00' L = 17.67'
- 12 Δ = 71°78'01" R = 4.00' L = 4.98'
- 13 Δ = 78°26'15" R = 30.00' L = 41.07'
- 14 Δ = 16°59'28" R = 250.00' L = 74.14'
- 15 Δ = 79°53'16" R = 30.00' L = 41.83'
- 16 Δ = 66°10'22" R = 12.00' L = 13.86'
- 17 Δ = 06°01'54" R = 183.00' L = 19.26'
- 18 Δ = 23°20'28" R = 109.00' L = 44.40'
- 19 Δ = 03°58'01" R = 109.00' L = 7.55'
- 20 Δ = 33°39'09" R = 55.00' L = 32.30'
- 21 Δ = 19°12'29" R = 18.50' L = 6.20'
- 22 Δ = 29°19'34" R = 64.00' L = 32.76'

COURSE DATA
(THIS SHEET ONLY)

- 1 N62°24'22"W RAD 58.02'
- 2 N18°04'28"E 11.95'
- 3 N30°16'26"E PRC
- 4 N45°16'54"W 2.72'
- 5 N53°28'01"W 2.72'

INST. NO. 19960587414, O.R.

LL 96 - 026 ,

PORTION OF PCL 1

SHEET 8 OF 18 SHEETS

ALL OF VESTING TENTATIVE
TRACT NO. 15987

TRACT NO. 15987
IN THE UNINCORPORATED TERRITORY OF ORANGE COUNTY, CALIFORNIA

JULY 2002


JAMES F. GILLEN, L.S. 5557

HUITT-ZOLLARS

14 NUMBERED LOTS AND 82 LETTERED LOTS

142.174 ACRES

DATE OF SURVEY:
JANUARY 1999 &
APRIL 2002

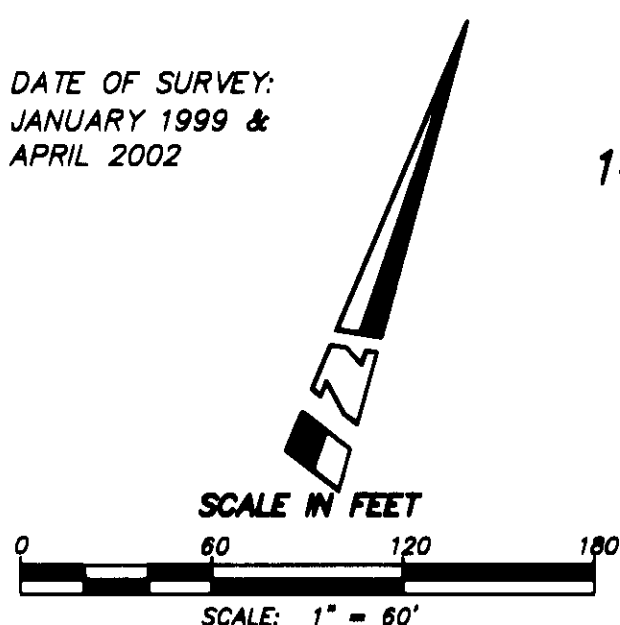

SEE SHEET 5
NOT A PART

COURSE DATA
(THIS SHEET ONLY)

- 1 N14°33'48"W 6.21'
 2 N51°00'32"W 6.60'
 3 N75°59'11"W 6.62'
 4 N79°49'01"E 6.65'
 5 N64°18'16"E 4.48'
 6 { N38°51'31"E RAD
 R=127.00'
 N38°50'46"E RAD
 R=140.00'

CURVE DATA
(THIS SHEET ONLY)

- ① $\Delta = 98^{\circ}8'04''$ $R = 45.00'$ $L = 77.21'$
- ② $\Delta = 13^{\circ}47'26''$ $R = 315.00'$ $L = 75.82'$
- ③ $\Delta = 06^{\circ}00'12''$ $R = 200.00'$ $L = 20.96'$
- ④ $\Delta = 03^{\circ}52'10''$ $R = 200.00'$ $L = 13.51'$
- ⑤ $\Delta = 02^{\circ}08'02''$ $R = 200.00'$ $L = 7.45'$
- ⑥ $\Delta = 78^{\circ}33'54''$ $R = 28.00'$ $L = 38.77'$
- ⑦ $\Delta = 02^{\circ}28'58''$ $R = 506.00'$ $L = 21.93'$
- ⑧ $\Delta = 14^{\circ}26'15''$ $R = 220.00'$ $L = 55.44'$
- ⑨ $\Delta = 16^{\circ}20'20''$ $R = 242.00'$ $L = 69.01'$
- ⑩ $\Delta = 22^{\circ}01'42''$ $R = 275.00'$ $L = 105.73'$
- ⑪ $\Delta = 03^{\circ}43'17''$ $R = 500.00'$ $L = 32.48'$
- ⑫ $\Delta = 02^{\circ}59'17''$ $R = 208.00'$ $L = 10.85'$
- ⑬ $\Delta = 15^{\circ}40'55''$ $R = 126.00'$ $L = 34.49'$
- ⑭ $\Delta = 14^{\circ}14'57''$ $R = 122.00'$ $L = 30.34'$
- ⑮ $\Delta = 08^{\circ}34'10''$ $R = 144.00'$ $L = 21.54'$
- ⑯ $\Delta = 11^{\circ}25'26''$ $R = 140.00'$ $L = 27.51'$
- ⑰ $\Delta = 10^{\circ}53'33''$ $R = 127.00'$ $L = 24.14'$

C/L 50' WIDE SANTA MARGARITA
WATER DISTRICT EASEMENT PER
INSTRUMENT NO. 20020799401, O.R.

LOT 1
0.213 AC.

LOT V
0.232 AC

LOT 3
9.293 AC.

NOTES:

SEE SHEET 2 FOR EASEMENT NOTES.

SEE SHEET 3 FOR BASIS OF BEARINGS, DATUM STATEMENT,
MONUMENT NOTES AND OCS GPS BOUNDARY CONTROL MAP.

SEE SHEET 4 FOR SHEET INDEX MAP.

LOTS A THROUGH BS AND LOTS CC AND CD ARE FOR LANDSCAPING/
OPEN SPACE AND ARE NOT SEPARATE BUILDING SITES.

LOTS BT THROUGH CB ARE PRIVATE STREETS.

(()) INDICATES MEASURED AND RECORD PER TRACT NO. 16025,
M.M. 812/22-29.

SEE

SHEET

9

C:\10036763 TM\TR15087\ TM150878 DMC

10-0367-63

8

TRACT NO. 15987

IN THE UNINCORPORATED TERRITORY OF ORANGE COUNTY, CALIFORNIA

JULY 2002

JAMES F. GILLEN, L.S. 5557

ALL OF VESTING TENTATIVE
TRACT NO. 15987

DATE OF SURVEY:
JANUARY 1999 &
APRIL 2002


HUITT-ZOLIARS

14 NUMBERED LOTS AND 82 LETTERED LOTS

142.174 ACRES

SEE SHEET 8

SEE SHEET 7

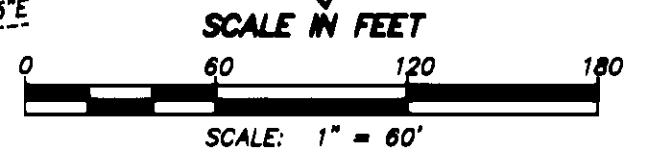

CURVE DATA (THIS SHEET ONLY)

- | | |
|----|--------------------------------------|
| 1 | Δ = 78°26'15" R = 30.00' L = 41.07' |
| 2 | Δ = 05°59'11" R = 275.00' L = 28.73' |
| 3 | Δ = 15°32'51" R = 275.00' L = 74.62' |
| 4 | Δ = 28°51'30" R = 78.00' L = 39.29' |
| 5 | Δ = 44°51'20" R = 78.00' L = 61.08' |
| 6 | Δ = 15°59'50" R = 78.00' L = 21.78' |
| 7 | Δ = 16°59'28" R = 250.00' L = 74.14' |
| 8 | Δ = 15°32'51" R = 300.00' L = 81.41' |
| 9 | Δ = 03°59'42" R = 110.00' L = 7.67' |
| 10 | Δ = 02°08'02" R = 200.00' L = 7.45' |
| 11 | Δ = 06°00'12" R = 200.00' L = 20.96' |
| 12 | Δ = 03°52'10" R = 200.00' L = 13.51' |
| 13 | Δ = 15°49'42" R = 100.00' L = 27.63' |
| 14 | Δ = 05°09'47" R = 440.00' L = 39.65' |
| 15 | Δ = 11°53'52" R = 24.00' L = 48.55' |
| 16 | Δ = 02°05'16" R = 400.00' L = 14.58' |

COURSE DATA (THIS SHEET ONLY)

- | | |
|---|------------------------|
| 1 | N37°51'09"E RAD 58.00' |
| 2 | N37°51'09"E RAD 50.15' |
| 3 | N01°37'09"W 19.30' |
| 4 | N37°25'52"E RAD |
| 5 | N62°24'22"W 58.02' |
| 6 | N40°09'28"E 129.04' |

NOTES:

- SEE SHEET 2 FOR EASEMENT NOTES.
- SEE SHEET 3 FOR BASIS OF BEARINGS, DATUM STATEMENT, MONUMENT NOTES AND OCS GPS BOUNDARY CONTROL MAP.
- SEE SHEET 4 FOR SHEET INDEX MAP.
- LOTS A THROUGH BS AND LOTS CC AND CD ARE FOR LANDSCAPING/ OPEN SPACE AND ARE NOT SEPARATE BUILDING SITES.
- LOTS BT THROUGH CB ARE PRIVATE STREETS

PORTION OF PCL. 1

INST. NO. 19960587414, O.R.

SHEET 10 OF 18 SHEETS

TRACT NO. 15987

IN THE UNINCORPORATED TERRITORY OF ORANGE COUNTY, CALIFORNIA

JULY 2002

JAMES F. GILLEN, L.S. 5557



ALL OF VESTING TENTATIVE
TRACT NO. 15987

DATE OF SURVEY:
JANUARY 1999 &
APRIL 2002

HUITT-ZOLLARS

14 NUMBERED LOTS AND 82 LETTERED LOTS

142.174 ACRES

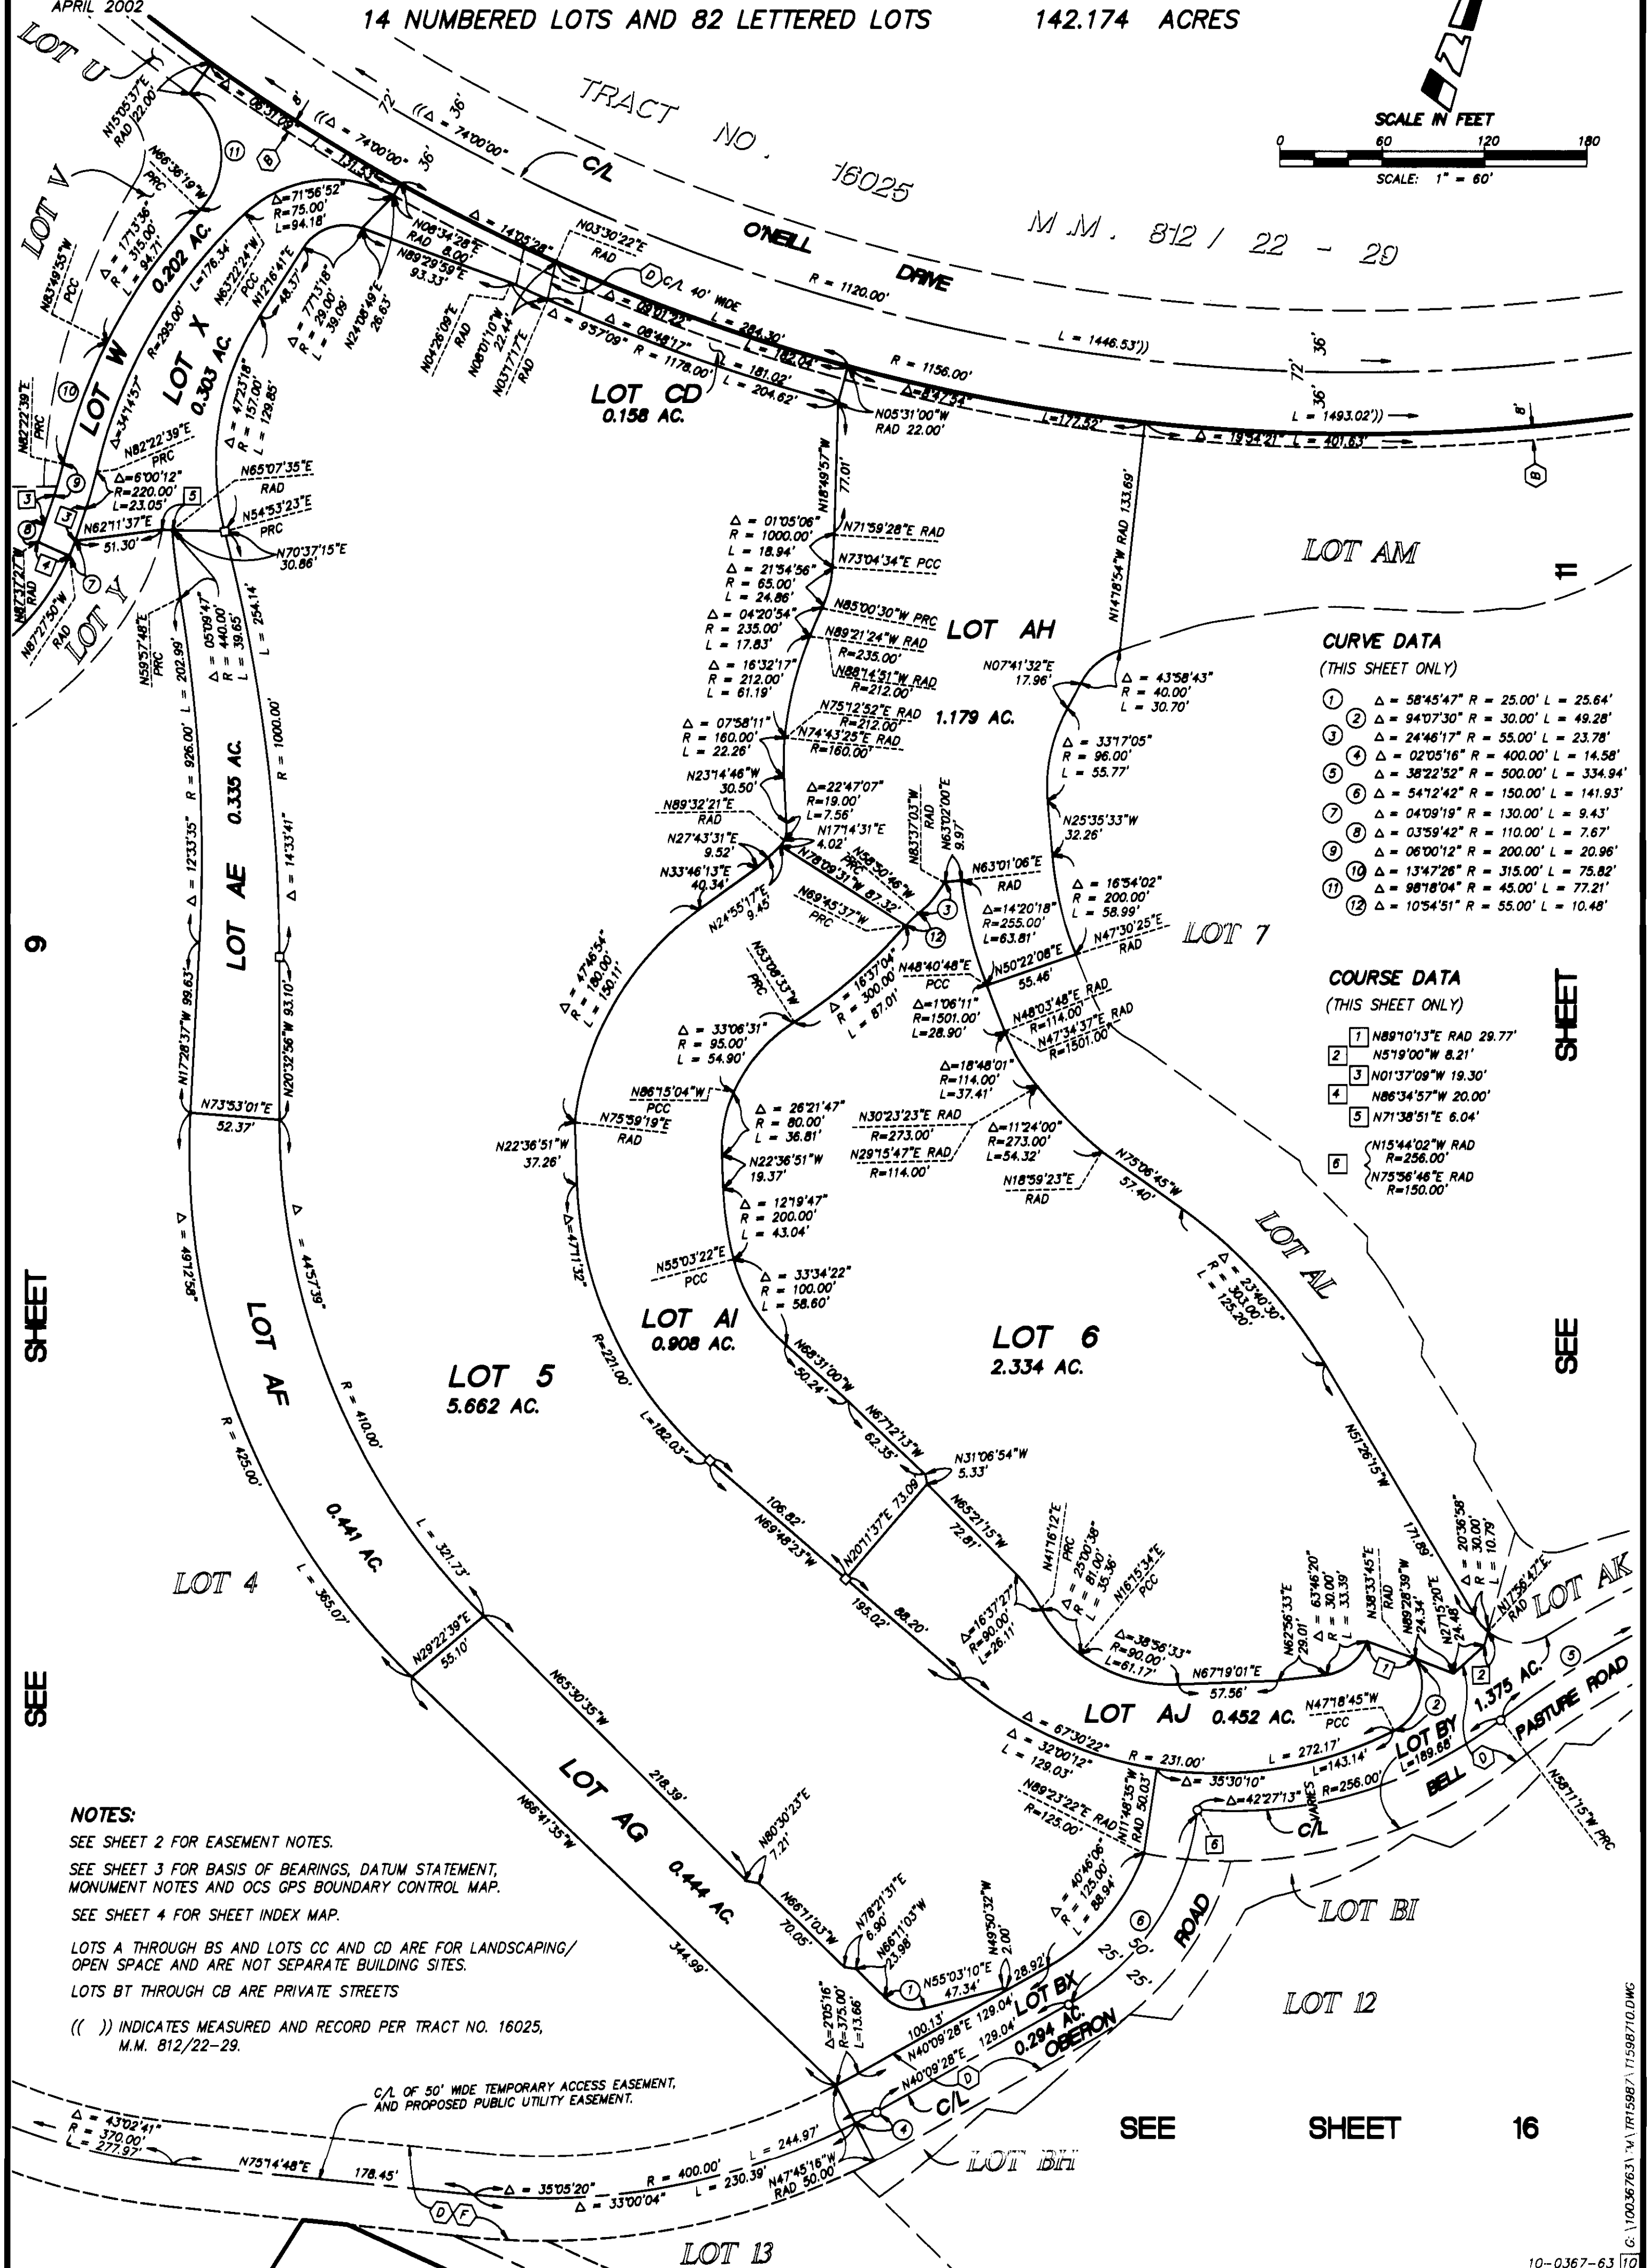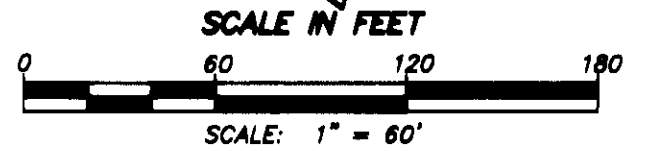

CURVE DATA (THIS SHEET ONLY)

- | | |
|----|--|
| 1 | $\Delta = 58^{\circ}45'47''$ R = 25.00' L = 25.64' |
| 2 | $\Delta = 94^{\circ}07'30''$ R = 30.00' L = 49.28' |
| 3 | $\Delta = 24^{\circ}46'17''$ R = 55.00' L = 23.78' |
| 4 | $\Delta = 02^{\circ}05'16''$ R = 400.00' L = 14.58' |
| 5 | $\Delta = 38^{\circ}22'52''$ R = 500.00' L = 334.94' |
| 6 | $\Delta = 54^{\circ}12'42''$ R = 150.00' L = 141.93' |
| 7 | $\Delta = 04^{\circ}09'19''$ R = 130.00' L = 9.43' |
| 8 | $\Delta = 03^{\circ}59'42''$ R = 110.00' L = 7.67' |
| 9 | $\Delta = 06^{\circ}00'12''$ R = 200.00' L = 20.96' |
| 10 | $\Delta = 13^{\circ}47'26''$ R = 315.00' L = 75.82' |
| 11 | $\Delta = 98^{\circ}18'04''$ R = 45.00' L = 77.21' |
| 12 | $\Delta = 10^{\circ}54'51''$ R = 55.00' L = 10.48' |

COURSE DATA (THIS SHEET ONLY)

- | | |
|---|--|
| 1 | N89^{\circ}10'13''E RAD 29.77' |
| 2 | N5^{\circ}19'00''W 8.21' |
| 3 | N01^{\circ}37'09''W 19.30' |
| 4 | N86^{\circ}34'57''W 20.00' |
| 5 | N71^{\circ}38'51''E 6.04' |
| 6 | { N15^{\circ}44'02''W RAD R=256.00'
N75^{\circ}56'46''E RAD R=150.00' |

SEE SHEET 16

NOTES:

- SEE SHEET 2 FOR EASEMENT NOTES.
- SEE SHEET 3 FOR BASIS OF BEARINGS, DATUM STATEMENT, MONUMENT NOTES AND OCS GPS BOUNDARY CONTROL MAP.
- SEE SHEET 4 FOR SHEET INDEX MAP.
- LOTS A THROUGH BS AND LOTS CC AND CD ARE FOR LANDSCAPING/ OPEN SPACE AND ARE NOT SEPARATE BUILDING SITES.
- LOTS BT THROUGH CB ARE PRIVATE STREETS
- (()) INDICATES MEASURED AND RECORD PER TRACT NO. 16025, M.M. 812/22-29.

C/L OF 50' WIDE TEMPORARY ACCESS EASEMENT,
AND PROPOSED PUBLIC UTILITY EASEMENT.

SHEET 11 OF 18 SHEETS

TRACT NO. 15987

ALL OF VESTING TENTATIVE
TRACT NO. 15987

IN THE UNINCORPORATED TERRITORY OF ORANGE COUNTY, CALIFORNIA

DATE OF SURVEY:
JANUARY 1999 &
APRIL 2002

JULY 2002

JAMES F. GILLEN, L.S. 5557

HUITT-ZOLLARS

14 NUMBERED LOTS AND 82 LETTERED LOTS

142.174 ACRES

CURVE DATA



(THIS SHEET ONLY)

- ① $\Delta = 38^{\circ}56'59''$ R = 25.00' L = 17.00'
- ② $\Delta = 70^{\circ}29'21''$ R = 30.00' L = 36.91'
- ③ $\Delta = 10^{\circ}32'00''$ R = 525.00' L = 96.52'
- ④ $\Delta = 86^{\circ}59'34''$ R = 30.00' L = 45.55'
- ⑤ $\Delta = 78^{\circ}38'17''$ R = 25.00' L = 34.31'
- ⑥ $\Delta = 02^{\circ}22'15''$ R = 525.00' L = 21.72'
- ⑦ $\Delta = 09^{\circ}59'02''$ R = 525.00' L = 91.48'
- ⑧ $\Delta = 07^{\circ}36'48''$ R = 525.00' L = 69.76'
- ⑨ $\Delta = 08^{\circ}14'37''$ R = 25.00' L = 3.60'

COURSE DATA

(THIS SHEET ONLY)

- 1 N42°00'34"W PRC
- 2 N52°32'34"W PRC
- 3 N05°39'29"E RAD R=115.00'
- 3 N22°10'38"W RAD R=525.00'

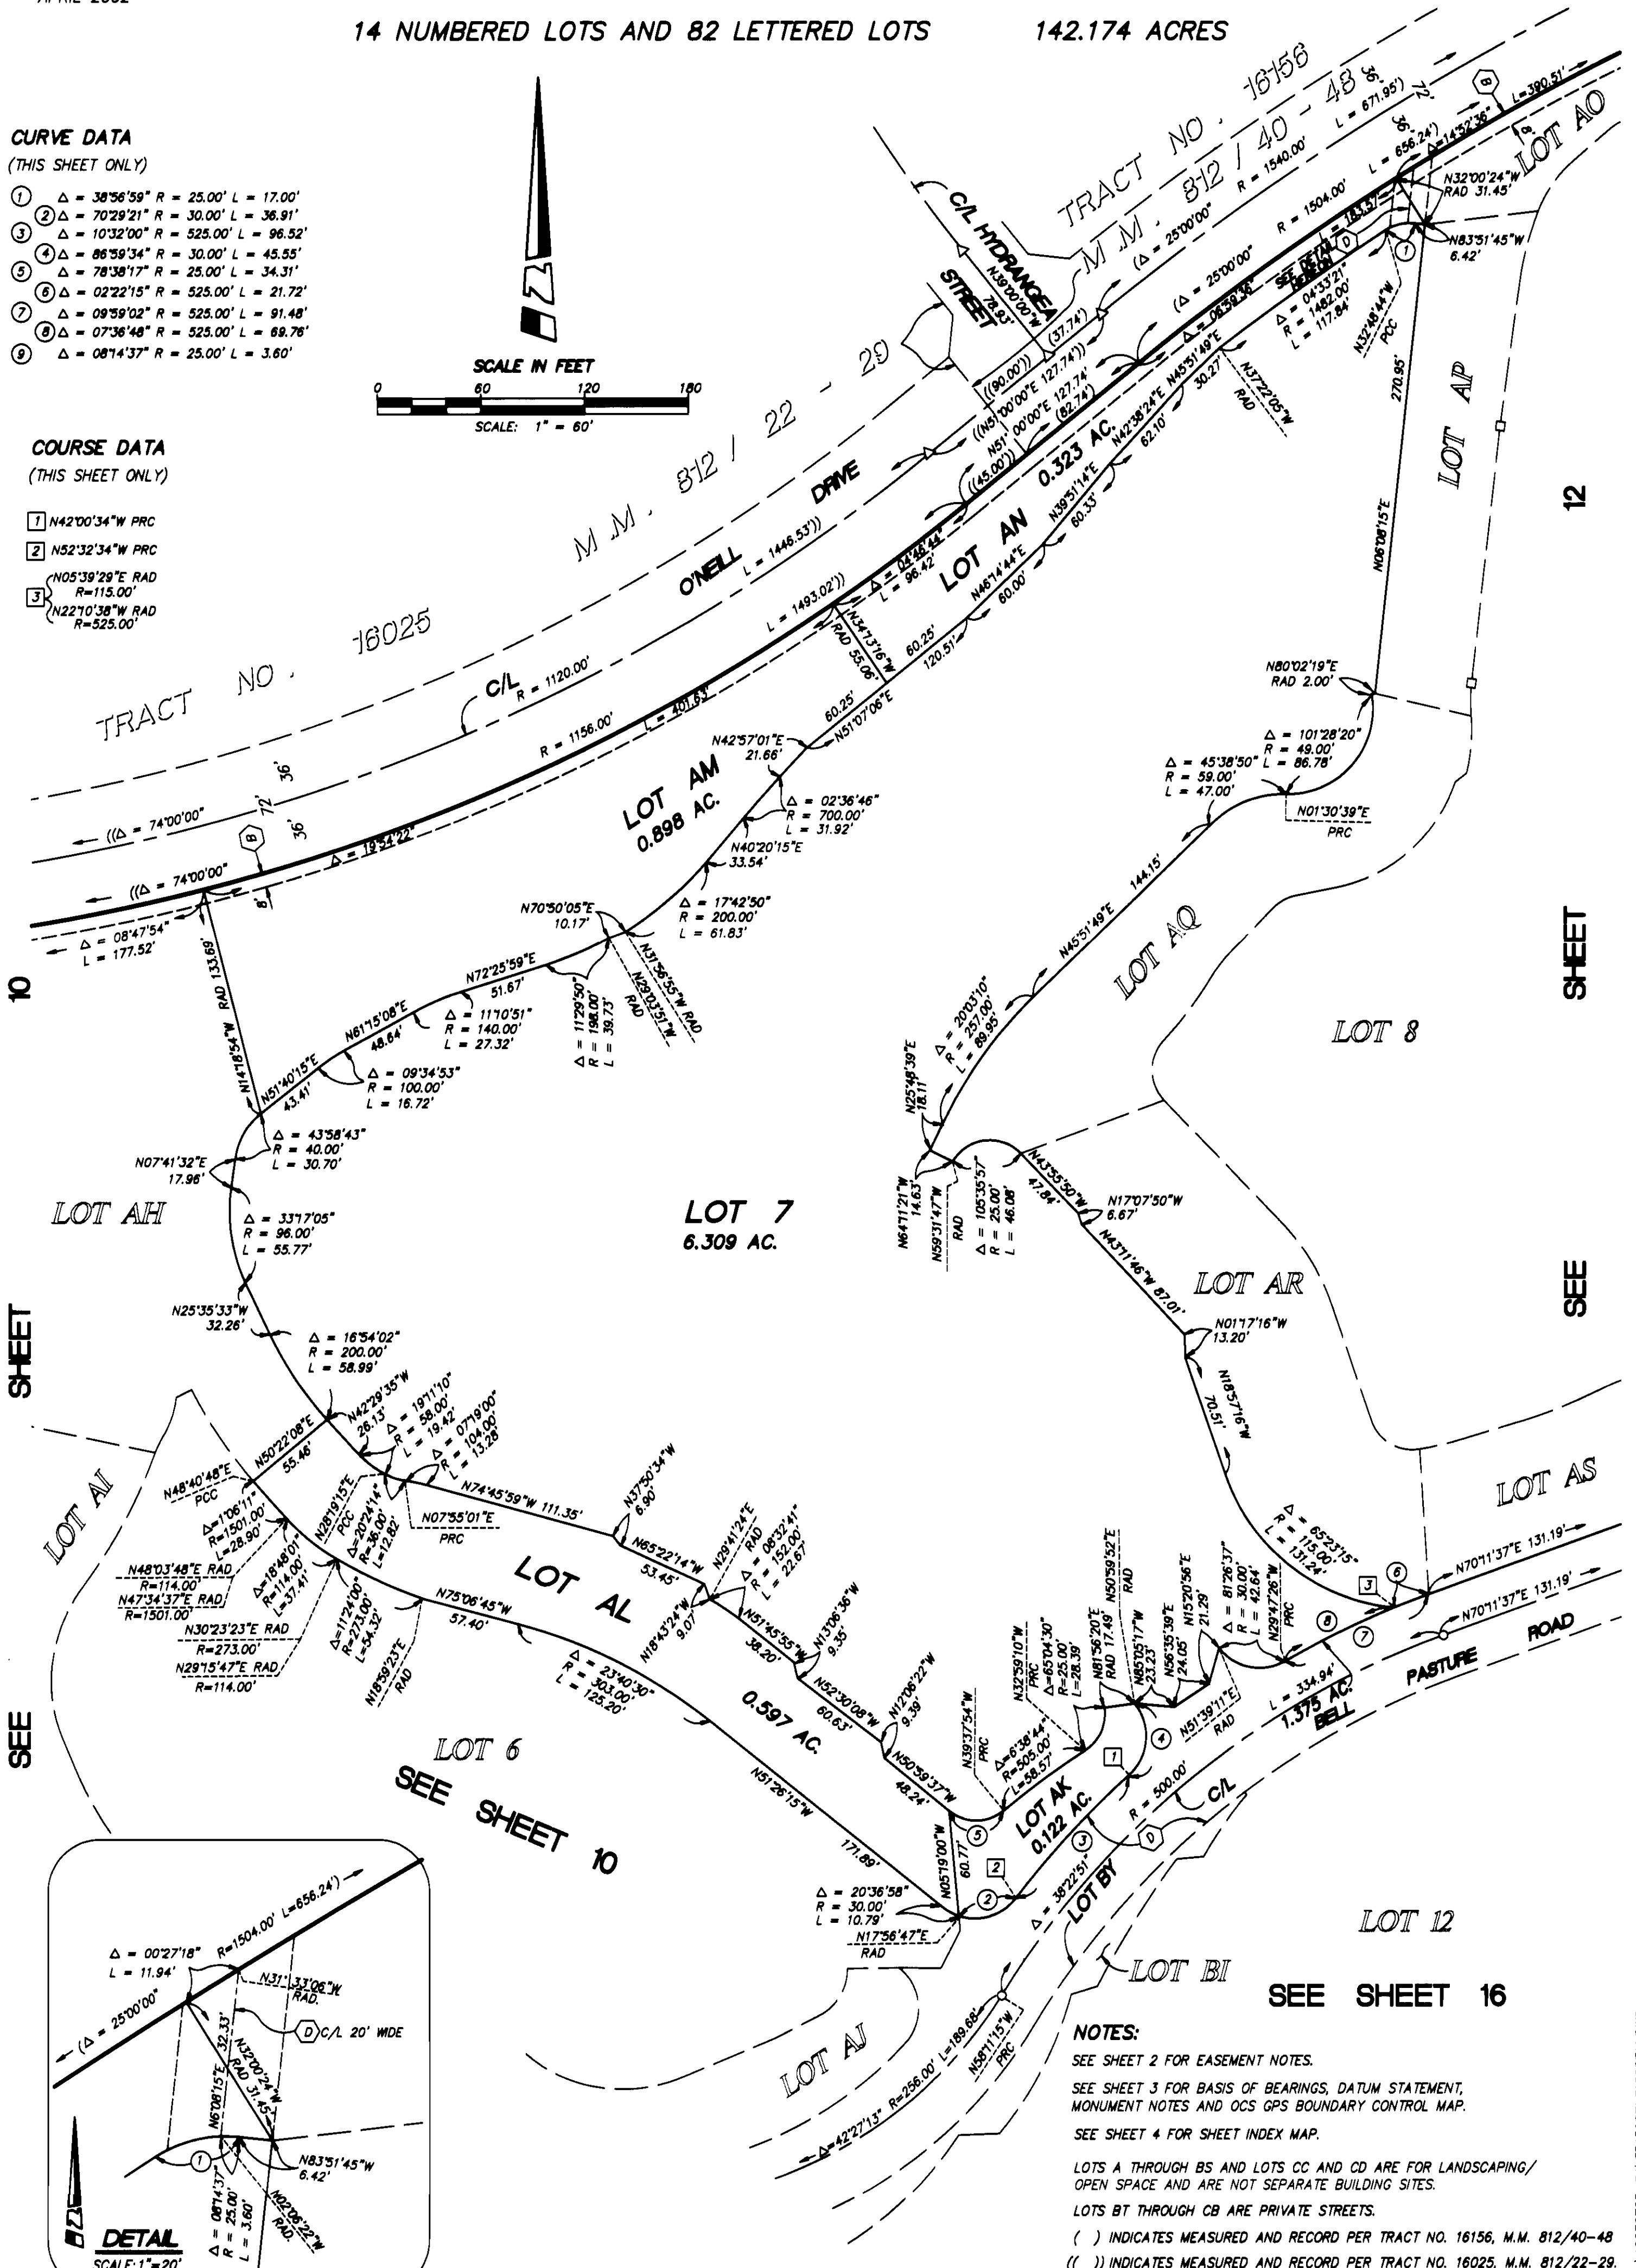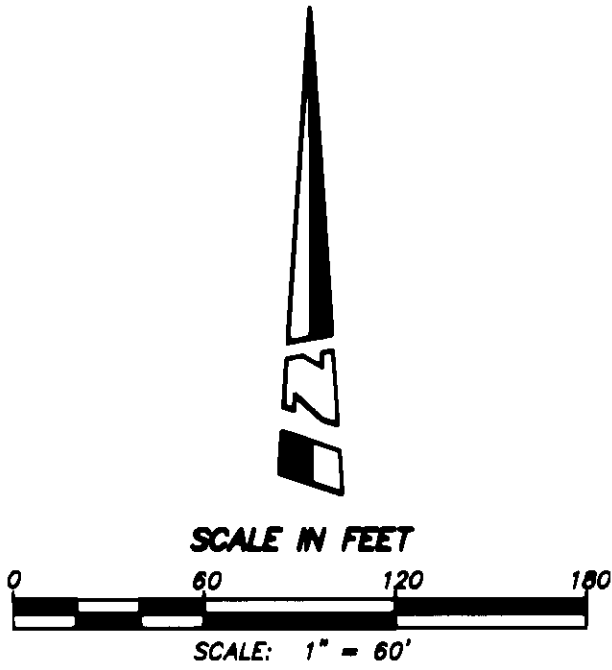

NOTES:

SEE SHEET 2 FOR EASEMENT NOTES.

SEE SHEET 3 FOR BASIS OF BEARINGS, DATUM STATEMENT, MONUMENT NOTES AND OCS GPS BOUNDARY CONTROL MAP.

SEE SHEET 4 FOR SHEET INDEX MAP.

LOTS A THROUGH BS AND LOTS CC AND CD ARE FOR LANDSCAPING/ OPEN SPACE AND ARE NOT SEPARATE BUILDING SITES.

LOTS BT THROUGH CB ARE PRIVATE STREETS.

() INDICATES MEASURED AND RECORD PER TRACT NO. 16156, M.M. 812/40-48

(()) INDICATES MEASURED AND RECORD PER TRACT NO. 16025, M.M. 812/22-29.

SHEET 12 OF 18 SHEETS

TRACT NO. 15987

IN THE UNINCORPORATED TERRITORY OF ORANGE COUNTY, CALIFORNIA

JULY 2002



JAMES F. GILLEN, L.S. 5557

DATE OF SURVEY:
JANUARY 1999 &
APRIL 2002

HUITT-ZOLLARS

14 NUMBERED LOTS AND 82 LETTERED LOTS

142.174 ACRES

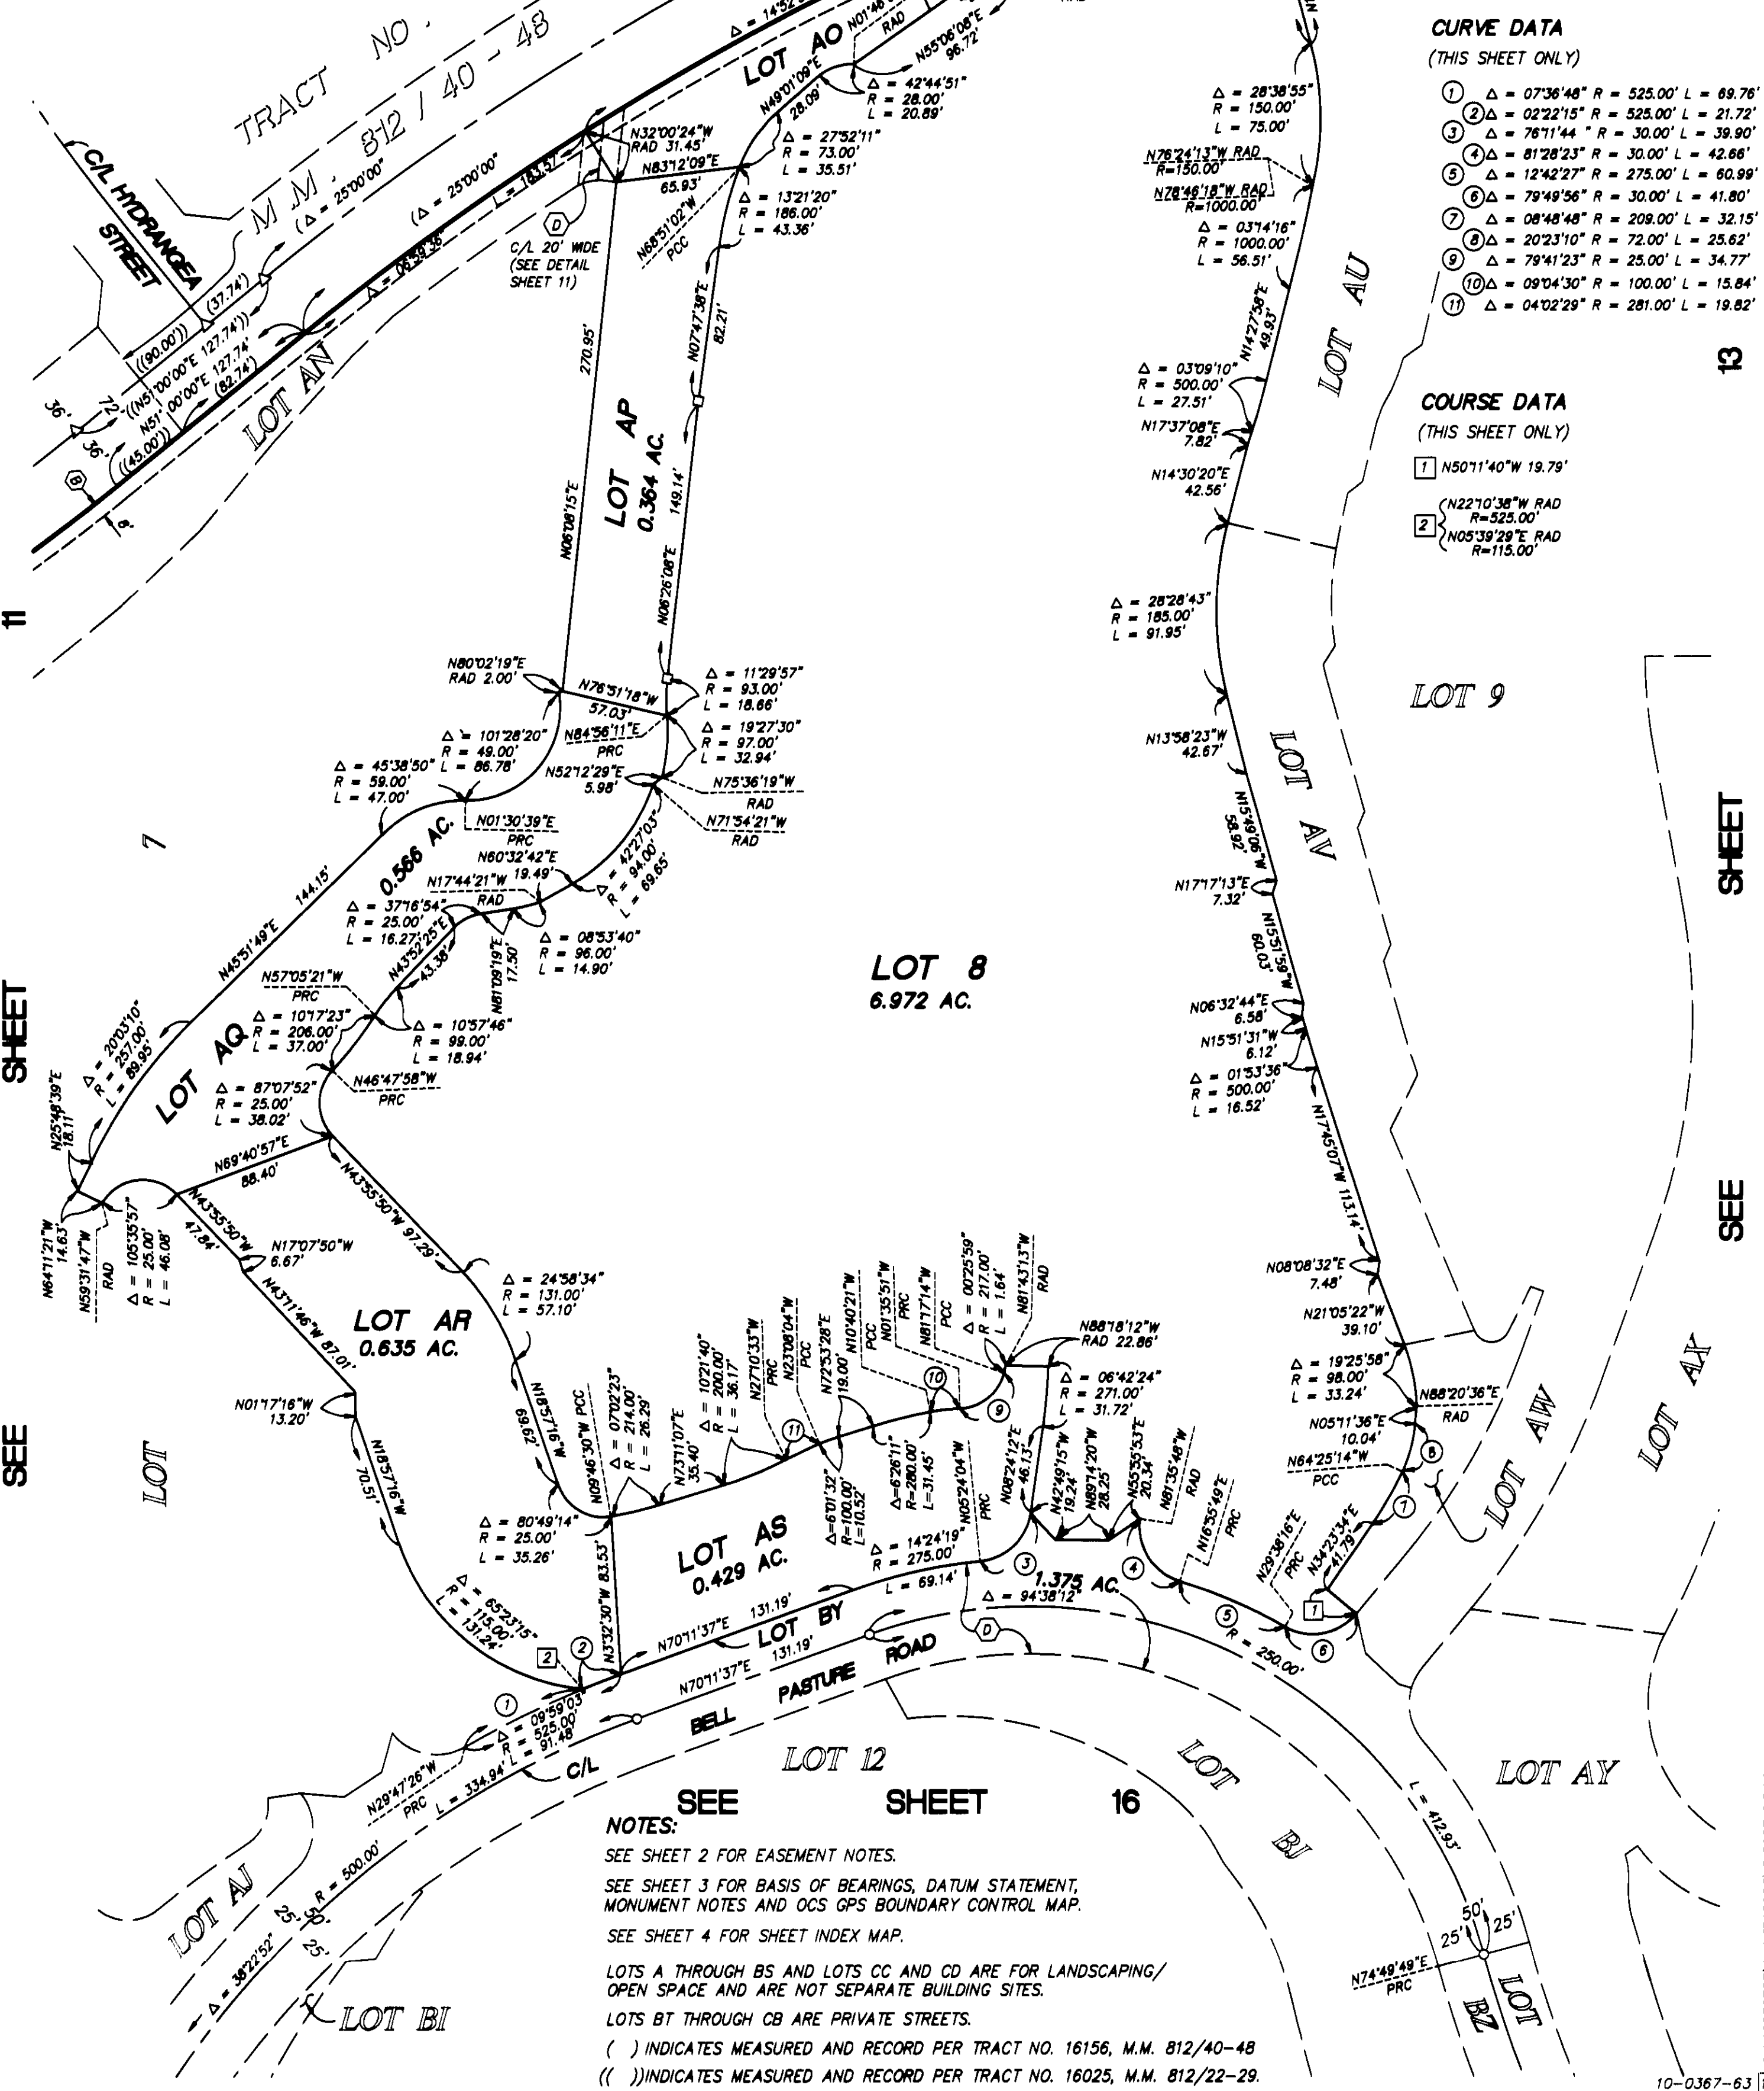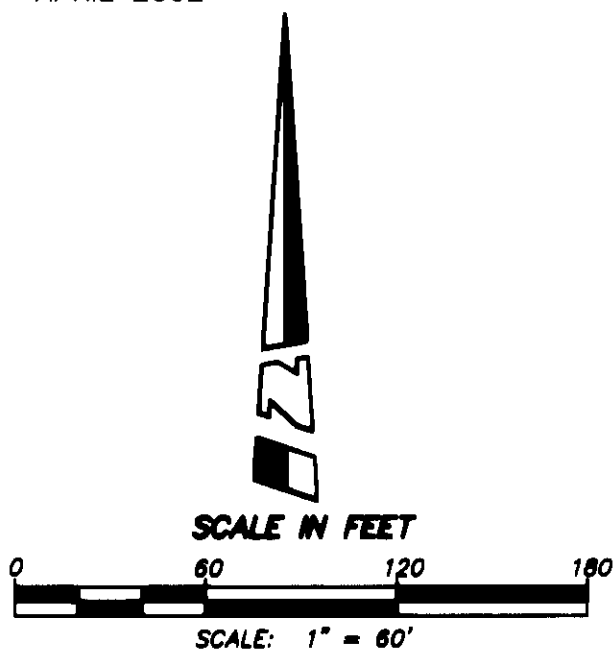

CURVE DATA (THIS SHEET ONLY)

- ① $\Delta = 07^{\circ}36'48''$ R = 525.00' L = 69.76'
- ② $\Delta = 02^{\circ}22'15''$ R = 525.00' L = 21.72'
- ③ $\Delta = 76^{\circ}11'44''$ R = 30.00' L = 39.90'
- ④ $\Delta = 81^{\circ}28'23''$ R = 30.00' L = 42.66'
- ⑤ $\Delta = 12^{\circ}42'27''$ R = 275.00' L = 60.99'
- ⑥ $\Delta = 79^{\circ}49'56''$ R = 30.00' L = 41.80'
- ⑦ $\Delta = 08^{\circ}48'48''$ R = 208.00' L = 32.15'
- ⑧ $\Delta = 20^{\circ}23'10''$ R = 72.00' L = 25.62'
- ⑨ $\Delta = 79^{\circ}41'23''$ R = 25.00' L = 34.77'
- ⑩ $\Delta = 09^{\circ}04'30''$ R = 100.00' L = 15.84'
- ⑪ $\Delta = 04^{\circ}02'29''$ R = 281.00' L = 19.82'

COURSE DATA (THIS SHEET ONLY)

- ① N50°11'40"W 19.79'
- ② { N22°10'38"W RAD R=525.00'
N05°39'29"E RAD R=115.00'

NOTES:

- SEE SHEET 2 FOR EASEMENT NOTES.
- SEE SHEET 3 FOR BASIS OF BEARINGS, DATUM STATEMENT, MONUMENT NOTES AND OCS GPS BOUNDARY CONTROL MAP.
- SEE SHEET 4 FOR SHEET INDEX MAP.
- LOTS A THROUGH BS AND LOTS CC AND CD ARE FOR LANDSCAPING/ OPEN SPACE AND ARE NOT SEPARATE BUILDING SITES.
- LOTS BT THROUGH CB ARE PRIVATE STREETS.
- () INDICATES MEASURED AND RECORD PER TRACT NO. 16156, M.M. 812/40-48
- (()) INDICATES MEASURED AND RECORD PER TRACT NO. 16025, M.M. 812/22-29.

SEE SHEET

SEE SHEET

SHEET 13 OF 18 SHEETS

TRACT NO. 15987

IN THE UNINCORPORATED TERRITORY OF ORANGE COUNTY, CALIFORNIA

JULY 2002

JAMES F. GILLEN, L.S. 5557

HUITT-ZOLLARS


14 NUMBERED LOTS AND 82 LETTERED LOTS

142.174 ACRES

ALL OF VESTING TENTATIVE
TRACT NO. 15987

DATE OF SURVEY:
JANUARY 1999 &
APRIL 2002

TRACT NO. 16156, M.M. 812/40 - 48

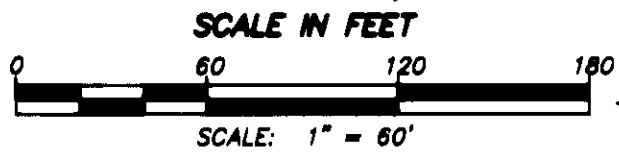

CURVE DATA (THIS SHEET ONLY)

- 1 $\Delta = 17'44.02''$ R = 40.00' L = 12.38'
- 2 $\Delta = 04'43.25''$ R = 151.00' L = 12.45'
- 3 $\Delta = 46'32.02''$ R = 25.00' L = 20.30'
- 4 $\Delta = 35'07.34''$ R = 74.00' L = 45.37'
- 5 $\Delta = 76'02.59''$ R = 25.00' L = 33.18'
- 6 $\Delta = 09'00.43''$ R = 100.00' L = 15.73'
- 7 $\Delta = 130'18.25''$ R = 10.00' L = 22.74'
- 8 $\Delta = 18'25.34''$ R = 25.00' L = 8.04'
- 9 $\Delta = 20'23.10''$ R = 72.00' L = 25.62'
- 10 $\Delta = 08'48.48''$ R = 209.00' L = 32.15'
- 11 $\Delta = 01'53.38''$ R = 500.00' L = 16.52'
- 12 $\Delta = 87'52.77''$ R = 374.00' L = 53.90'
- 13 $\Delta = 80'20.38''$ R = 30.00' L = 42.07'
- 14 $\Delta = 23'28.53''$ R = 30.00' L = 12.29'
- 15 $\Delta = 56'51.45''$ R = 30.00' L = 29.77'

COURSE DATA (THIS SHEET ONLY)

- 1 N50°11'40"W 19.79'
- 2 N78°40'22"E 37.91'
- 3 N47°01'04"W 24.04'
- 4 N88°20'36"E RAD
- 5 N73°40'33"W RAD 7.07'
- 6 N12°51'14"W 21.38'

LOT 9
7.696 AC.

ALL VEHICULAR ACCESS RIGHTS TO ANTONIO PARKWAY, EXCEPT AT APPROVED ACCESS LOCATIONS, ARE HEREBY RELEASED AND RELINQUISHED TO THE COUNTY OF ORANGE.

NOTES:

SEE SHEET 2 FOR EASEMENT NOTES.

SEE SHEET 3 FOR BASIS OF BEARINGS, DATUM STATEMENT, MONUMENT NOTES AND OCS GPS BOUNDARY CONTROL MAP.

SEE SHEET 4 FOR SHEET INDEX MAP.

LOTS A THROUGH BS AND LOTS CC AND CD ARE FOR LANDSCAPING/ OPEN SPACE AND ARE NOT SEPARATE BUILDING SITES.

LOTS BT THROUGH CB ARE PRIVATE STREETS.

() INDICATES MEASURED AND RECORD PER TRACT NO. 16156, M.M. 812/40-48

SEE SHEET 14

839 14

SHEET 14 OF 18 SHEETS

ALL OF VESTING TENTATIVE
TRACT NO. 15987

TRACT NO. 15987

IN THE UNINCORPORATED TERRITORY OF ORANGE COUNTY, CALIFORNIA

JULY 2002



JAMES F. GILLEN, L.S. 5557

HUITT-ZOLIARS

14 NUMBERED LOTS AND 82 LETTERED LOTS

142.174 ACRES

DATE OF SURVEY:
JANUARY 1999 &
APRIL 2002

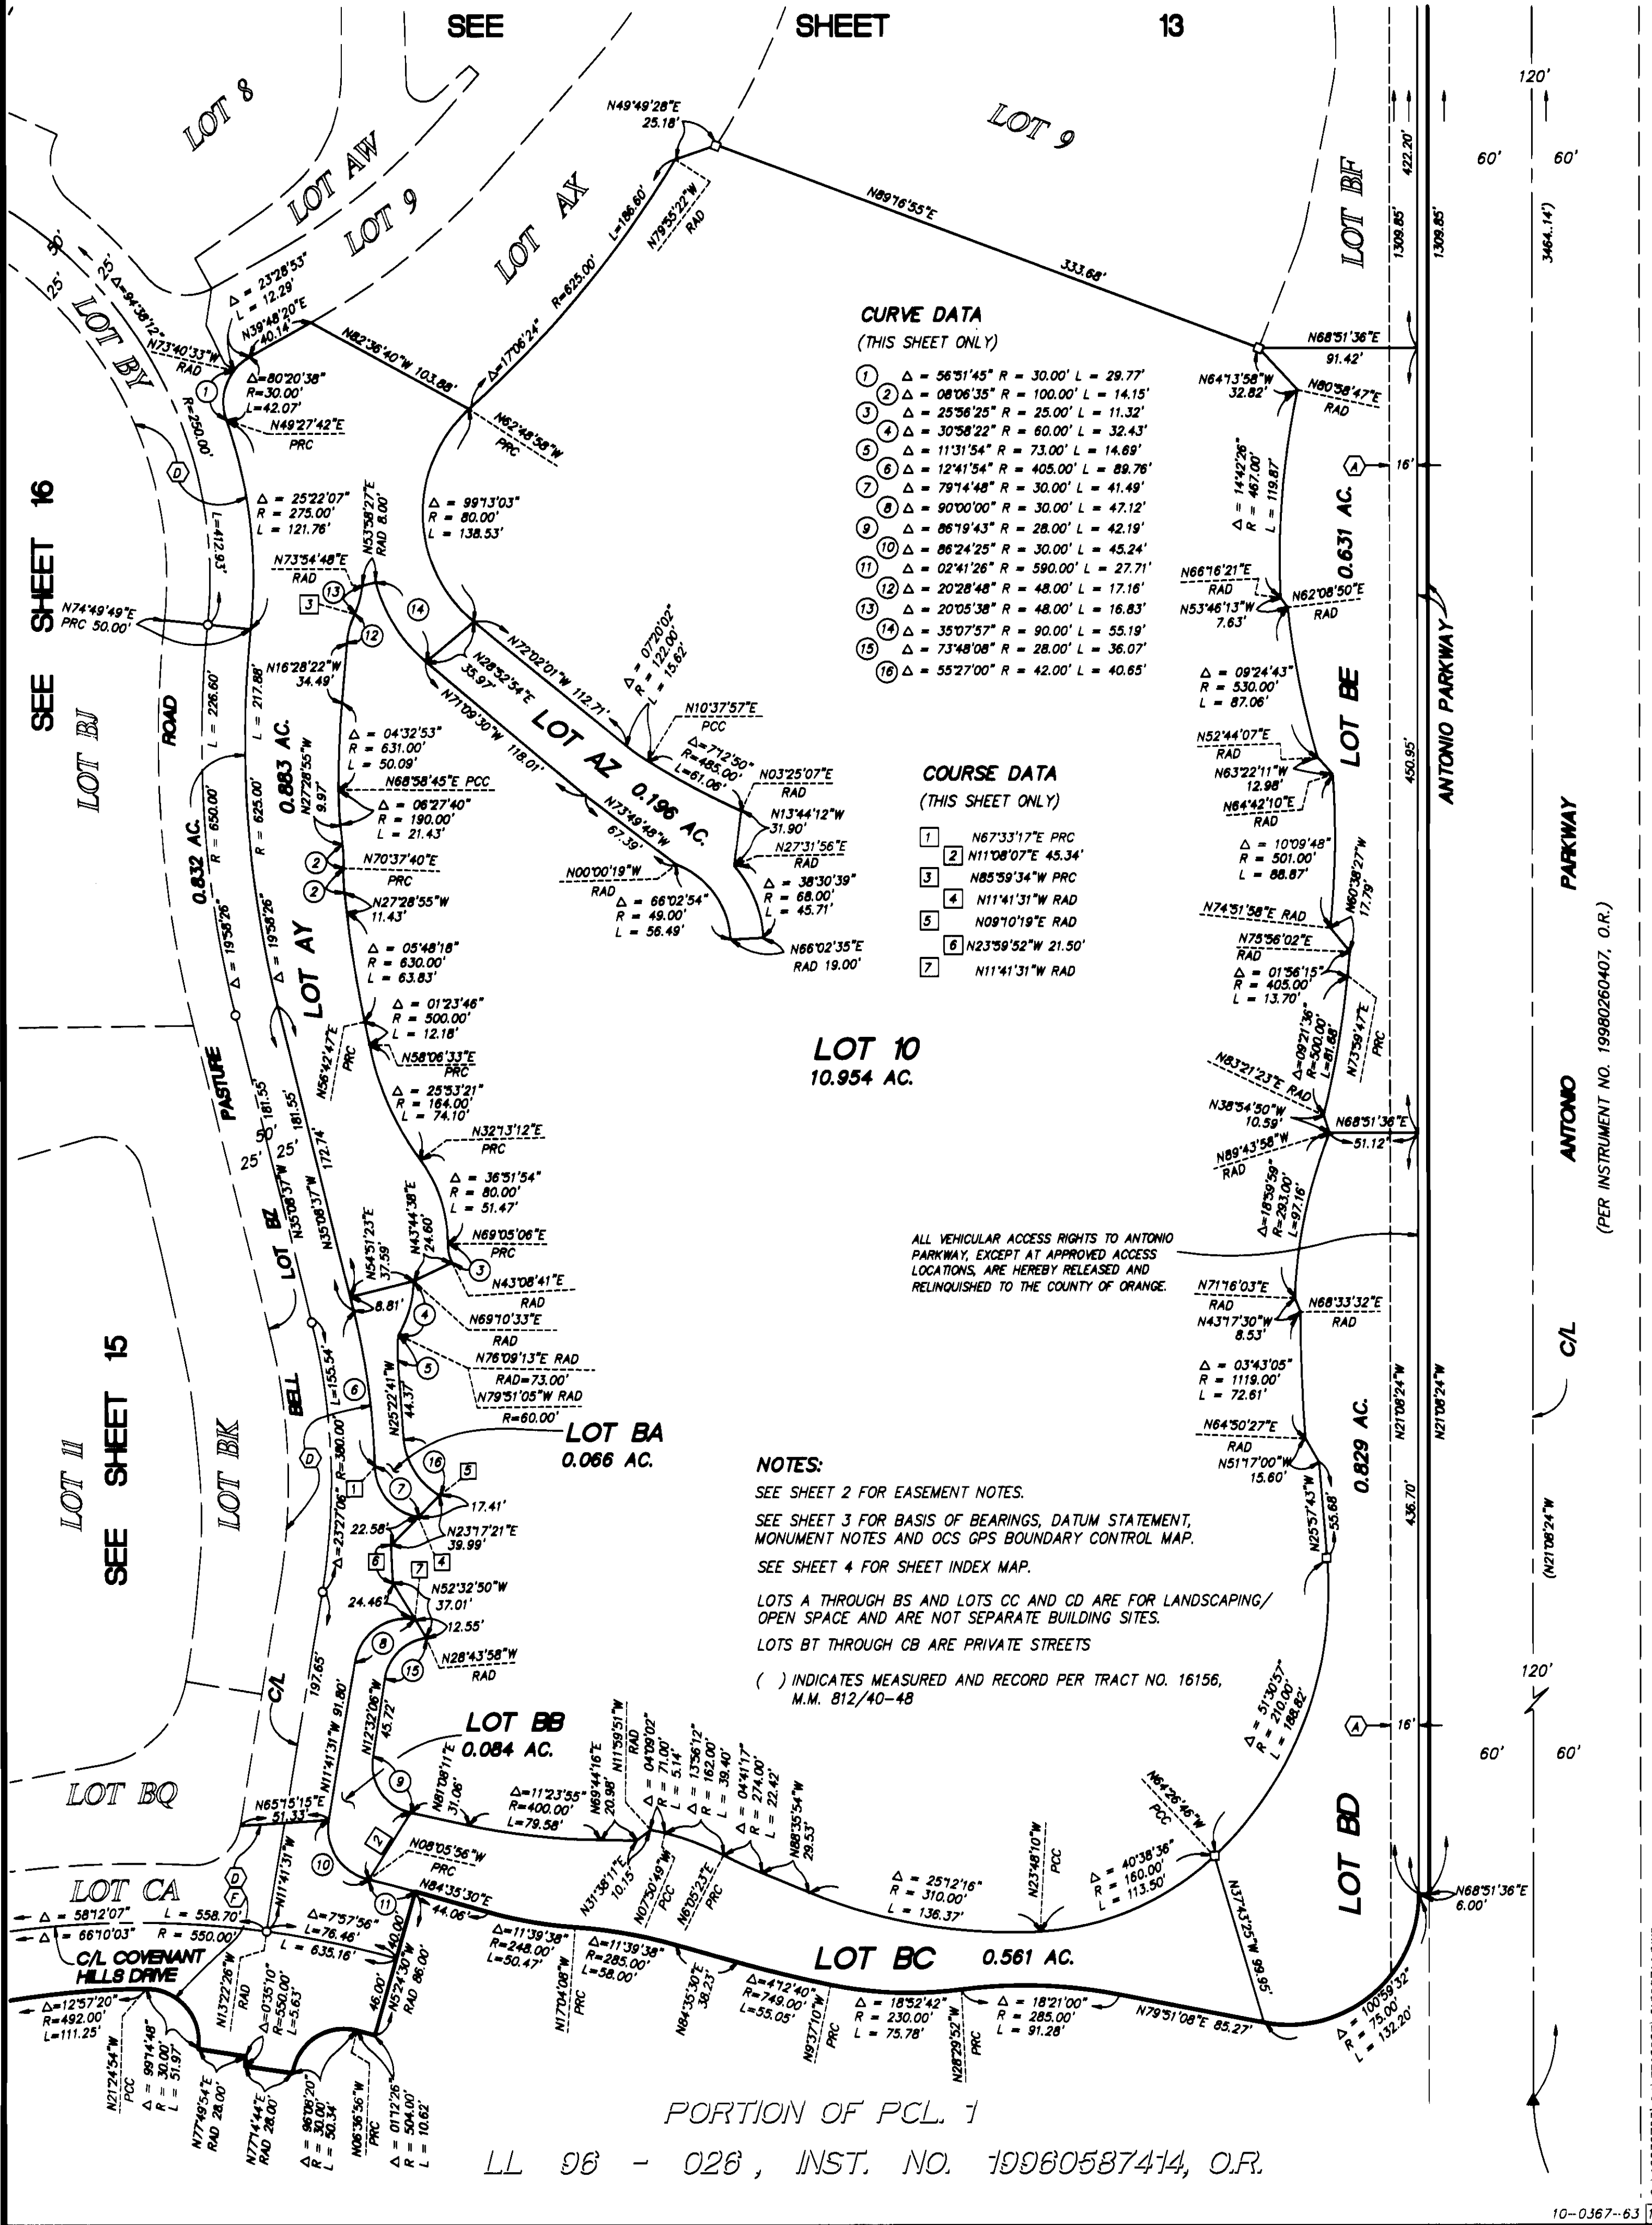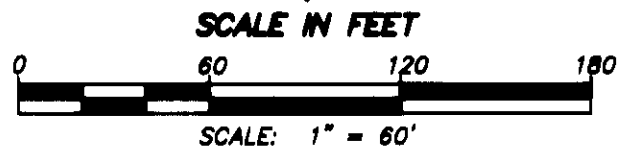

CURVE DATA (THIS SHEET ONLY)

1. $\Delta = 56^{\circ}51'45''$ R = 30.00' L = 29.77'
2. $\Delta = 08^{\circ}06'35''$ R = 100.00' L = 14.15'
3. $\Delta = 25^{\circ}58'25''$ R = 25.00' L = 11.32'
4. $\Delta = 30^{\circ}58'22''$ R = 60.00' L = 32.43'
5. $\Delta = 11^{\circ}31'54''$ R = 73.00' L = 14.89'
6. $\Delta = 12^{\circ}41'54''$ R = 405.00' L = 89.78'
7. $\Delta = 79^{\circ}14'48''$ R = 30.00' L = 41.49'
8. $\Delta = 90^{\circ}00'00''$ R = 30.00' L = 47.12'
9. $\Delta = 86^{\circ}19'43''$ R = 28.00' L = 42.19'
10. $\Delta = 86^{\circ}24'25''$ R = 30.00' L = 45.24'
11. $\Delta = 02^{\circ}41'26''$ R = 590.00' L = 27.71'
12. $\Delta = 20^{\circ}28'48''$ R = 48.00' L = 17.16'
13. $\Delta = 20^{\circ}05'38''$ R = 48.00' L = 16.83'
14. $\Delta = 35^{\circ}07'57''$ R = 90.00' L = 55.19'
15. $\Delta = 73^{\circ}48'08''$ R = 28.00' L = 36.07'
16. $\Delta = 55^{\circ}27'00''$ R = 42.00' L = 40.65'

COURSE DATA (THIS SHEET ONLY)

1. N67°33'17"E PRC
2. N11°08'07"E 45.34'
3. N85°59'34"W PRC
4. N11°41'31"W RAD
5. N09°10'19"E RAD
6. N23°59'52"W 21.50'
7. N11°41'31"W RAD

NOTES:

SEE SHEET 2 FOR EASEMENT NOTES.

SEE SHEET 3 FOR BASIS OF BEARINGS, DATUM STATEMENT,
MONUMENT NOTES AND OCS GPS BOUNDARY CONTROL MAP.

SEE SHEET 4 FOR SHEET INDEX MAP.

LOTS A THROUGH BS AND LOTS CC AND CD ARE FOR LANDSCAPING/
OPEN SPACE AND ARE NOT SEPARATE BUILDING SITES.

LOTS BT THROUGH CB ARE PRIVATE STREETS

() INDICATES MEASURED AND RECORD PER TRACT NO. 16156,
M.M. 812/40-48

(PER INSTRUMENT NO. 19980260407, O.R.)

PORTION OF PCL 1

LL 96 - 026, INST. NO. 19960587414, O.R.

839 14

SHEET 15 OF 18 SHEETS

TRACT NO. 15987

ALL OF VESTING TENTATIVE
TRACT NO. 15987

IN THE UNINCORPORATED TERRITORY OF ORANGE COUNTY, CALIFORNIA

JULY 2002



JAMES F. GILLEN, L.S. 5557

HUITT-ZOLIARS

14 NUMBERED LOTS AND 82 LETTERED LOTS

142.174 ACRES

DATE OF SURVEY:
JANUARY 1999 &
APRIL 2002

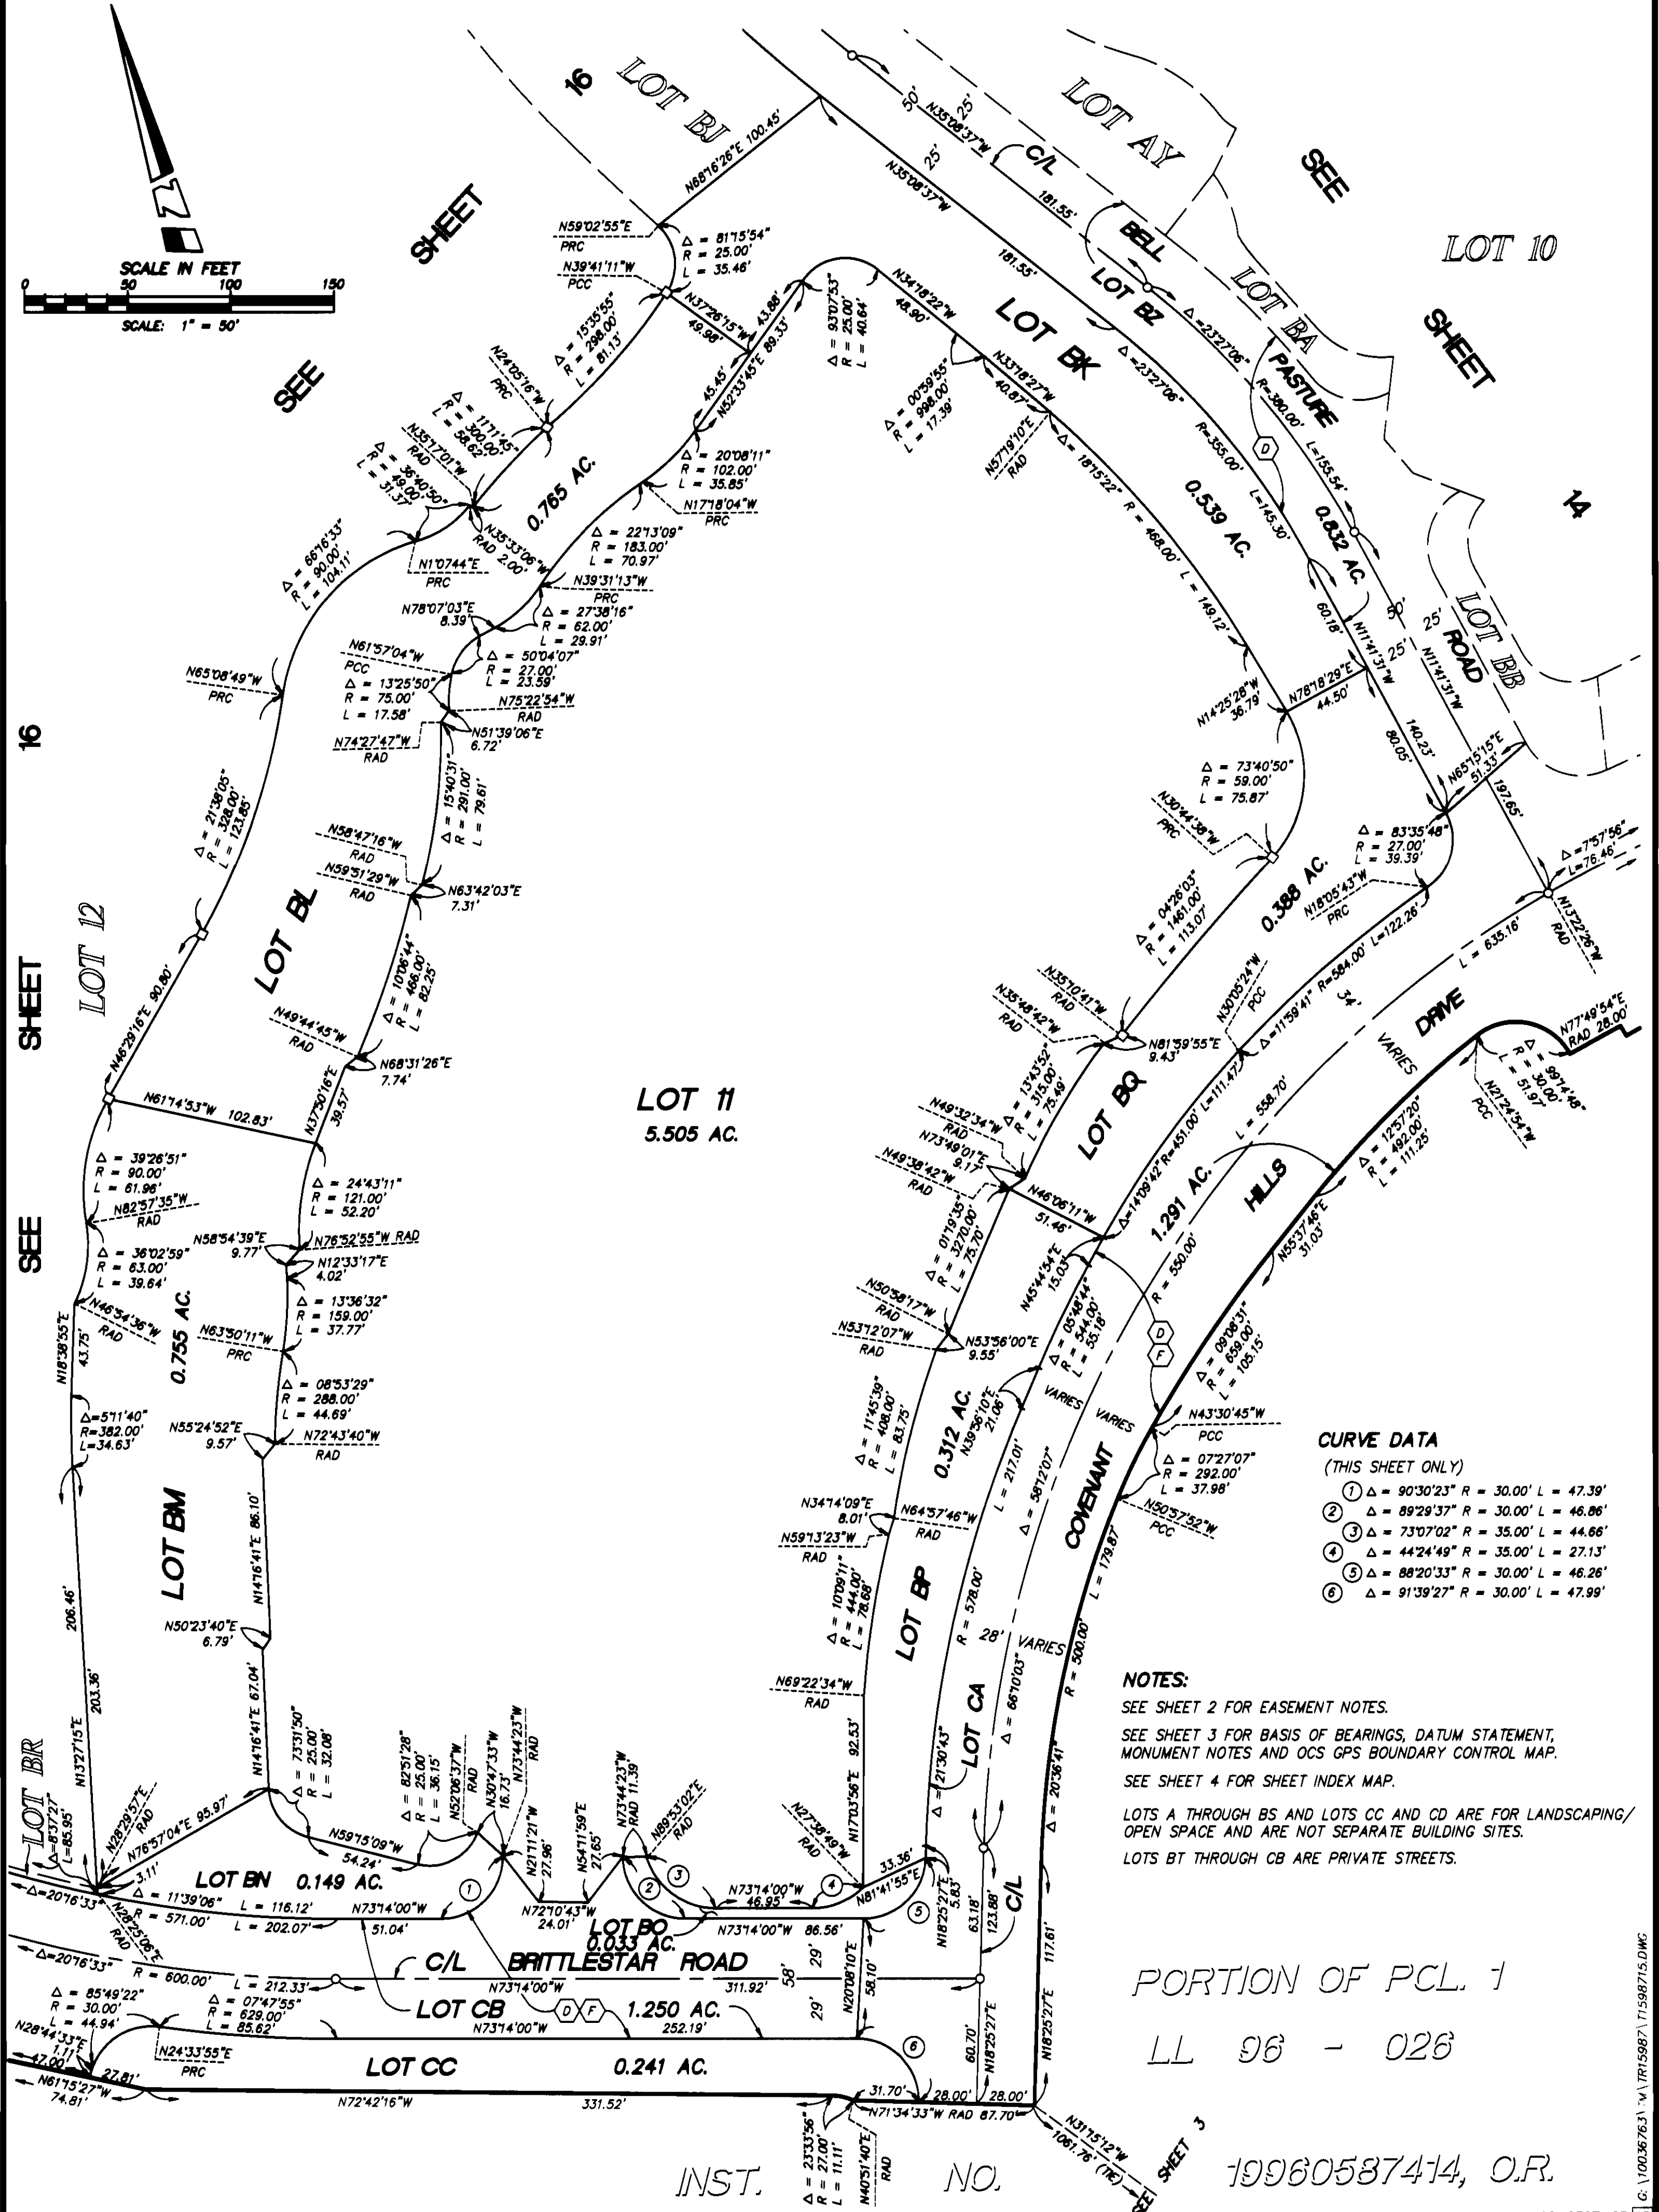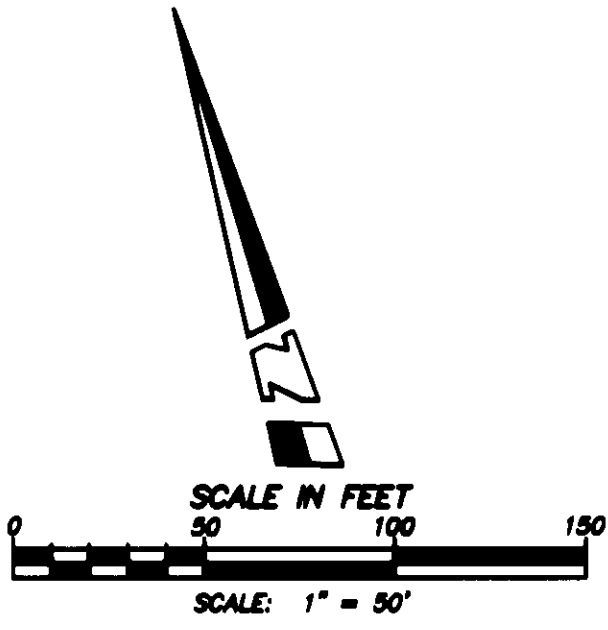

CURVE DATA
(THIS SHEET ONLY)

①	Δ = 90°30'23" R = 30.00' L = 47.39'
②	Δ = 89°29'37" R = 30.00' L = 46.86'
③	Δ = 73°07'02" R = 35.00' L = 44.66'
④	Δ = 44°24'49" R = 35.00' L = 27.13'
⑤	Δ = 88°20'33" R = 30.00' L = 46.26'
⑥	Δ = 91°39'27" R = 30.00' L = 47.99'

NOTES:
SEE SHEET 2 FOR EASEMENT NOTES.
SEE SHEET 3 FOR BASIS OF BEARINGS, DATUM STATEMENT, MONUMENT NOTES AND OCS GPS BOUNDARY CONTROL MAP.
SEE SHEET 4 FOR SHEET INDEX MAP.
LOTS A THROUGH BS AND LOTS CC AND CD ARE FOR LANDSCAPING/ OPEN SPACE AND ARE NOT SEPARATE BUILDING SITES.
LOTS BT THROUGH CB ARE PRIVATE STREETS.

PORTION OF PCL. 1

LL 96 - 026

19960587414, O.R.

INST.

NO.

SEE SHEET 3

SHEET 16 OF 18 SHEETS

TRACT NO. 15987

IN THE UNINCORPORATED TERRITORY OF ORANGE COUNTY, CALIFORNIA

JULY 2002

JAMES F. GILLEN, L.S. 5557

ALL OF VESTING TENTATIVE
TRACT NO. 15987

DATE OF SURVEY:
JANUARY 1999 &
APRIL 2002


14 NUMBERED LOTS AND 82 LETTERED LOTS

142.174 ACRES

SEE

SHEET

12

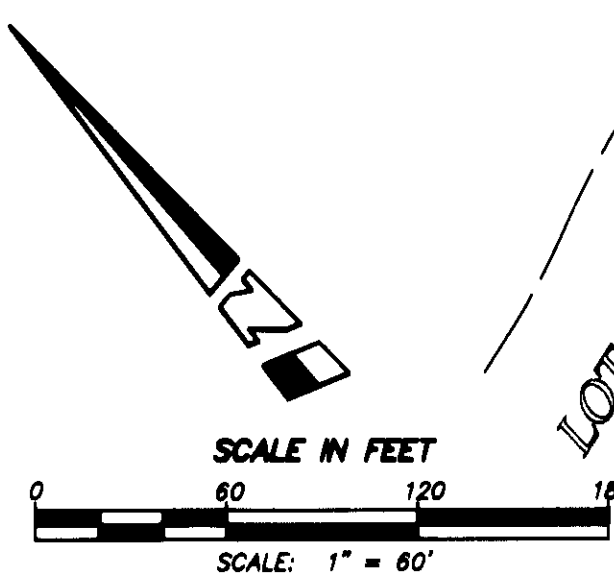

SEE SHEET 11

SEE SHEET 10

SEE SHEET 9

15

SHEET

SEE

CURVE DATA (THIS SHEET ONLY)

- 1 $\Delta = 84^{\circ}51'49''$ R = 30.00' L = 44.43'
- 2 $\Delta = 03^{\circ}09'49''$ R = 628.00' L = 34.73'
- 3 $\Delta = 01^{\circ}19'31''$ R = 309.00' L = 7.15'
- 4 $\Delta = 09^{\circ}26'12''$ R = 190.00' L = 31.29'
- 5 $\Delta = 16^{\circ}31'28''$ R = 45.00' L = 13.24'
- 6 $\Delta = 08^{\circ}33'21''$ R = 100.00' L = 14.93'
- 7 $\Delta = 01^{\circ}44'21''$ R = 600.00' L = 18.21'
- 8 $\Delta = 06^{\circ}04'54''$ R = 400.00' L = 42.46'
- 9 $\Delta = 03^{\circ}57'37''$ R = 425.00' L = 29.38'
- 10 $\Delta = 02^{\circ}05'16''$ R = 425.00' L = 15.49'
- 11 $\Delta = 06^{\circ}06'21''$ R = 256.00' L = 27.28'
- 12 $\Delta = 10^{\circ}41'17''$ R = 275.00' L = 51.30'
- 13 $\Delta = 54^{\circ}12'42''$ R = 150.00' L = 141.93'
- 14 $\Delta = 45^{\circ}04'53''$ R = 175.00' L = 137.69'
- 15 $\Delta = 35^{\circ}51'12''$ R = 175.00' L = 109.51'
- 16 $\Delta = 09^{\circ}13'41''$ R = 175.00' L = 28.19'
- 17 $\Delta = 20^{\circ}44'10''$ R = 279.00' L = 100.97'
- 18 $\Delta = 06^{\circ}04'00''$ R = 425.00' L = 45.00'
- 19 $\Delta = 04^{\circ}10'30''$ R = 279.00' L = 20.33'
- 20 $\Delta = 31^{\circ}02'37''$ R = 25.00' L = 13.55'

COURSE DATA (THIS SHEET ONLY)

- 1 N52°57'27"W 21.01'
- 2 N52°57'27"W 17.96'
- 3 N52°57'27"W 3.04'
- 4 N33°52'44"E PRC
- 5 N78°24'35"W 5.91'
- 6 N20°50'33"W RAD
R=275.00'
- 7 N85°04'35"E RAD
R=175.00'
- 8 N15°44'02"W RAD
R=256.00'
- 9 N75°56'46"E RAD
R=150.00'
- 10 N74°49'49"E PRC 50.00'
- 11 N85°59'02"W 56.08'
- 12 N48°48'19"E 14.09'

NOTES:

SEE SHEET 2 FOR EASEMENT NOTES.

SEE SHEET 3 FOR BASIS OF BEARINGS, DATUM STATEMENT,
MONUMENT NOTES AND OCS GPS BOUNDARY CONTROL MAP.

SEE SHEET 4 FOR SHEET INDEX MAP.

LOTS A THROUGH BS AND LOTS CC AND CD ARE FOR LANDSCAPING/
OPEN SPACE AND ARE NOT SEPARATE BUILDING SITES.

LOTS BT THROUGH CB ARE PRIVATE STREETS.

LOT 12
10.891 AC.

PORTION OF PCL. 1


LL 96 - 026, INST. NO.

19960587414, O.R.

ALL OF VESTING TENTATIVE
TRACT NO. 15987

DATE OF SURVEY:
JANUARY 1999 &
APRIL 2002

839 18

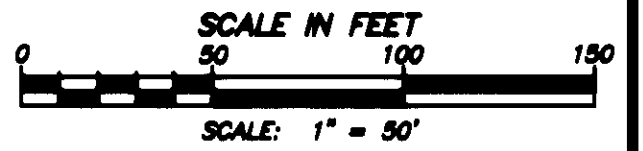


TRACT NO.
16025

M.M. 812 /
22 - 29

TRACT NO. 16235
M.M. 825 / 30-39

17.P. TAGGED "P.L.S. 5557" OR SPIKE & WASHER STAMPED
"P.L.S. 5557" OR LEAD, TACK & TAG "P.L.S. 5557" TO BE
SET PER TRACT NO. 16235, M.M. 825/30-39

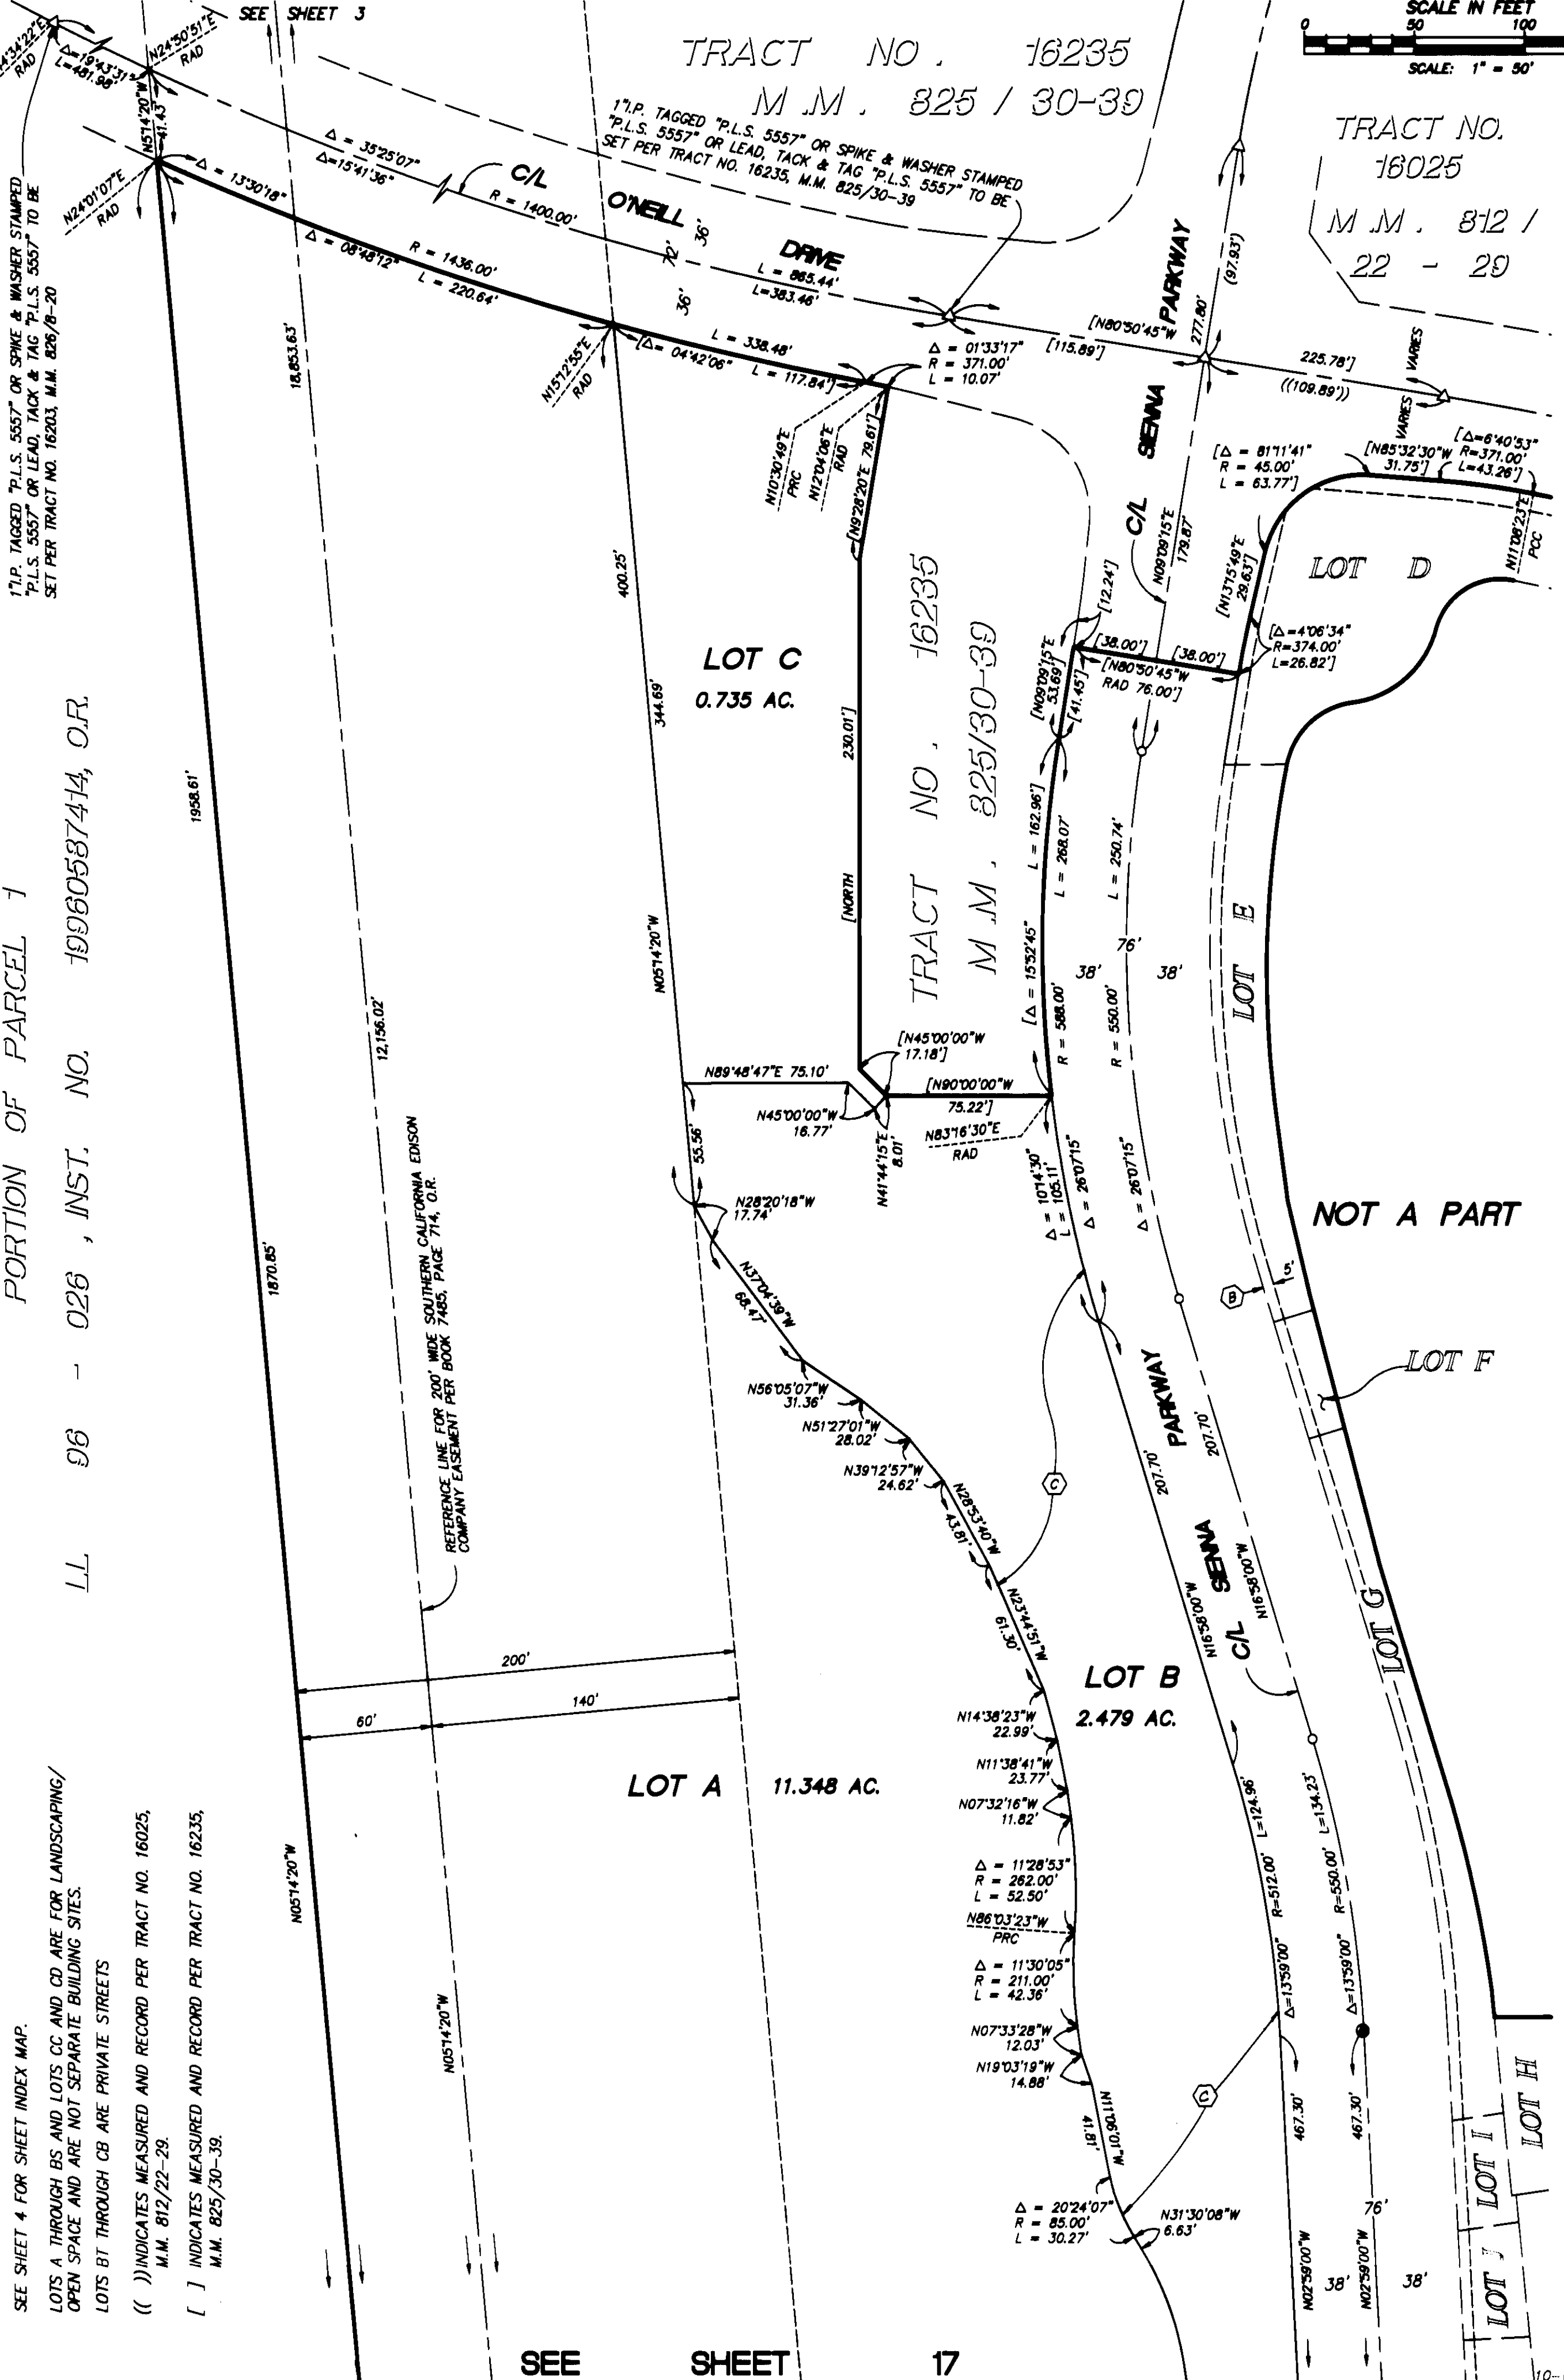

5

SHEET

SEE

NOTES:

- SEE SHEET 2 FOR EASEMENT NOTES.
- SEE SHEET 3 FOR BASIS OF BEARINGS, DATUM STATEMENT, MONUMENT NOTES AND OCS GPS BOUNDARY CONTROL MAP.
- SEE SHEET 4 FOR SHEET INDEX MAP.
- LOTS A THROUGH BS AND LOTS CC AND CD ARE FOR LANDSCAPING/ OPEN SPACE AND ARE NOT SEPARATE BUILDING SITES.
- LOTS BT THROUGH CB ARE PRIVATE STREETS
- (()) INDICATES MEASURED AND RECORD PER TRACT NO. 16025, M.M. 812/22-29.
- [] INDICATES MEASURED AND RECORD PER TRACT NO. 16235, M.M. 825/30-39.

SEE

SHEET

17

839 18