

SHEET 1 OF 11 SHEETS
60 NUMBERED LOTS
23 LETTERED LOTS
83.560 ACRES
ALL OF VESTING
T.T.M. 15988
DATE OF SURVEY:
JANUARY, 1999

TRACT MAP NO. 15988

IN THE UNINCORPORATED TERRITORY OF THE COUNTY OF ORANGE,
STATE OF CALIFORNIA

BEING A SUBDIVISION OF A PORTION OF PARCEL 1 OF LOT LINE ADJUSTMENT NO. LL 96-026, IN THE UNINCORPORATED TERRITORY OF THE COUNTY OF ORANGE, STATE OF CALIFORNIA, AS SHOWN ON EXHIBIT "B" ATTACHED TO THAT CERTAIN DOCUMENT RECORDED NOVEMBER 21, 1996 AS INSTRUMENT NO. 19960587414 OF OFFICIAL RECORDS, IN THE OFFICE OF THE COUNTY RECORDER OF SAID COUNTY.

HALL & FOREMAN, INC.

STEVEN C. SHAMBECK, P.L.S. 6217
FEBRUARY, 2003

ACCEPTED AND FILED AT THE
REQUEST OF

FIRST AMERICAN TITLE INSURANCE COMPANY

DATE January 30, 2004

TIME 3:13 PM FEES 3700

INSTRUMENT # 2004000739939m

BOOK 854 PAGE 6-16

TOM DALY
COUNTY CLERK-RECORDER

BY Julien Escamela
DEPUTY

OWNERSHIP CERTIFICATE

WE, THE UNDERSIGNED, BEING ALL PARTIES HAVING ANY RECORD TITLE INTEREST IN THE LAND COVERED BY THIS MAP, DO HEREBY CONSENT TO THE PREPARATION AND RECORDATION OF SAID MAP, AS SHOWN WITHIN THE DISTINCTIVE BORDER LINE.

WE HEREBY DEDICATE TO THE COUNTY OF ORANGE:

1. THE EASEMENT FOR SCENIC PRESERVATION PURPOSES AS SHOWN ON SAID MAP FOR THE PURPOSES AND SUBJECT TO THE SAME CONDITIONS AND LIMITATIONS AS SHOWN IN THAT CERTAIN EASEMENT RECORDED SEPTEMBER 12, 1991 AS INSTRUMENT NO. 91-511820 OF OFFICIAL RECORDS.
2. THE EASEMENT FOR FIRE PROTECTION ACCESS PURPOSES AS SHOWN ON SAID MAP.
3. THE EASEMENT FOR EMERGENCY ACCESS PURPOSES OVER ALL OF LOTS BA THROUGH BF AS SHOWN ON SAID MAP.

WE ALSO HEREBY DEDICATE TO THE SANTA MARGARITA WATER DISTRICT THE EASEMENTS FOR WATER, RECYCLED WATER, SEWER, DRAINAGE, AND ACCESS PURPOSES OVER THOSE EASEMENT AREAS AS SHOWN ON SAID MAP WHICH EASEMENTS SHALL BE SUBJECT TO THE SAME CONDITIONS AS ARE SHOWN IN THAT CERTAIN GRANT OF EASEMENT TO SANTA MARGARITA WATER DISTRICT RECORDED SEPTEMBER 18, 2002 AS INSTRUMENT NO. 20020799401, OF OFFICIAL RECORDS, COUNTY OF ORANGE.

DMB LADERA, L.L.C., A DELAWARE LIMITED LIABILITY COMPANY

BY: RANCHO MISSION VIEJO, L.L.C. A DELAWARE LIMITED LIABILITY COMPANY,
AS ITS AUTHORIZED AGENT AND MANAGER

BY: [Signature] BY: [Signature]
PRINT NAME: Donald T. Stahl PRINT NAME: Greg Edwards
PRINT TITLE: Vice President PRINT TITLE: CA

NOTARY ACKNOWLEDGEMENT

STATE OF California
COUNTY OF Orange)SS

ON Sept. 5, 2003 BEFORE ME, Diana L. Binks,
Notary Public

PERSONALLY APPEARED Donald T. Stahl and Greg Edwards
PERSONALLY KNOWN TO ME (OR PROVED TO ME ON THE BASIS OF SATISFACTORY EVIDENCE) TO BE THE PERSON(S) WHOSE NAME(S) IS/ARE SUBSCRIBED TO THE WITHIN INSTRUMENT AND ACKNOWLEDGED TO ME THAT HE/SHE/they EXECUTED THE SAME IN HIS/HER/their AUTHORIZED CAPACITY(IES), AND THAT BY HIS/HER/their SIGNATURE(S) ON THE INSTRUMENT THE PERSON(S) OR THE ENTITY UPON BEHALF OF WHICH THE PERSON(S) ACTED, EXECUTED THE INSTRUMENT.

WITNESS MY HAND:

Diana L. Binks
NOTARY PUBLIC IN AND FOR SAID STATE

Diana L. Binks
PRINT NAME

MY PRINCIPAL PLACE OF BUSINESS IS IN Orange COUNTY
MY COMMISSION EXPIRES Dec. 12, 2006

CERTIFICATE OF ACCEPTANCE

THE UNDERSIGNED, BEING THE DULY APPOINTED AGENT OF THE SANTA MARGARITA WATER DISTRICT, A PUBLIC CORPORATION OF ORANGE COUNTY, CALIFORNIA, PURSUANT TO ITS RESOLUTION NO. 88-10-02, DOES HEREBY ACCEPT ON BEHALF OF SAID DISTRICT THE EASEMENTS FOR, WATER, RECYCLED WATER, SEWER, DRAINAGE AND ACCESS PURPOSES, AS DEDICATED AND AS SHOWN ON THIS TRACT MAP, BY AND BETWEEN THE SANTA MARGARITA WATER DISTRICT AND DMB LADERA, L.L.C., AND DOES HEREBY CERTIFY THAT THE GRANTEE CONSENTS TO THE RECORDATION OF SAID TRACT.

[Signature]
DANIEL R. FERONS, CHIEF ENGINEER
SANTA MARGARITA WATER DISTRICT


SEE SHEET 2 FOR ADDITIONAL NOTARY ACKNOWLEDGMENT AND SIGNATURE OMISSIONS

SURVEYOR'S STATEMENT

THIS MAP WAS PREPARED BY ME OR UNDER MY DIRECTION AND IS BASED UPON A FIELD SURVEY IN CONFORMANCE WITH THE REQUIREMENTS OF THE SUBDIVISION MAP ACT AND LOCAL ORDINANCE AT THE REQUEST OF DMB LADERA, LLC IN JANUARY, 1999. I HEREBY STATE THAT ALL MONUMENTS ARE OF THE CHARACTER AND OCCUPY THE POSITIONS INDICATED, OR THAT THEY WILL BE SET IN SUCH POSITIONS; AND THAT SAID MONUMENTS ARE SUFFICIENT TO ENABLE THE SURVEY TO BE RETRACED. I HEREBY STATE THAT THIS FINAL MAP SUBSTANTIALLY CONFORMS TO THE CONDITIONALLY APPROVED TENTATIVE MAP.

[Signature]
STEVEN C. SHAMBECK, P.L.S. 6217
LICENSE EXPIRES: 3/31/06

8-31-03
DATE

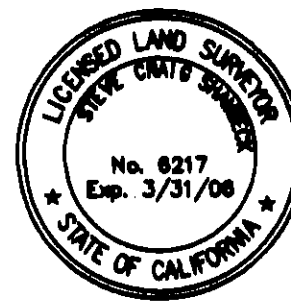


COUNTY SURVEYOR'S STATEMENT

I HEREBY STATE THAT I HAVE EXAMINED THIS MAP AND HAVE FOUND IT TO BE SUBSTANTIALLY IN CONFORMANCE WITH THE TENTATIVE MAP AS FILED WITH, AMENDED AND APPROVED BY THE ORANGE COUNTY SUBDIVISION COMMITTEE; THAT ALL PROVISIONS OF THE SUBDIVISION MAP ACT AND COUNTY SUBDIVISION REGULATIONS HAVE BEEN COMPLIED WITH AND I AM SATISFIED SAID MAP IS TECHNICALLY CORRECT.

DATED THIS 6th DAY OF JANUARY, 2004

[Signature]
JOHN CANAS, COUNTY SURVEYOR
L.S. 4408 EXPIRATION DATE: 9-30-05

BY: MICHAEL K. SULLIVAN, DEPUTY
L.S. 6884 EXPIRES 6/30/05

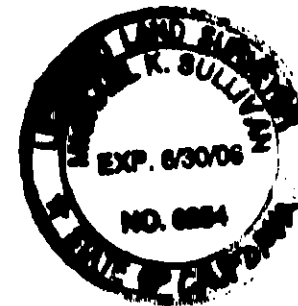

CLERK OF THE BOARD OF SUPERVISOR'S CERTIFICATE

STATE OF CALIFORNIA)
COUNTY OF ORANGE) SS

I HEREBY CERTIFY THAT THIS MAP WAS PRESENTED FOR APPROVAL TO THE BOARD OF SUPERVISORS OF ORANGE COUNTY AT A REGULAR MEETING THEREOF HELD ON THE 27th DAY OF JANUARY, 2004 AND THAT THEREUPON SAID BOARD DID, BY AN ORDER DULY PASSED AND ENTERED, APPROVE SAID MAP.

AND DID ACCEPT ON BEHALF OF THE COUNTY OF ORANGE:

1. THE EASEMENT FOR SCENIC PRESERVATION PURPOSES AS DEDICATED.
2. THE EASEMENT FOR FIRE PROTECTION ACCESS PURPOSES AS DEDICATED.
3. THE EASEMENT FOR EMERGENCY ACCESS PURPOSES OVER ALL OF LOTS BA THROUGH BF AS DEDICATED.

AND DID ALSO APPROVE SUBJECT MAP PURSUANT TO THE PROVISIONS OF SECTION 66436(a)(3)(A) OF THE SUBDIVISION MAP ACT.

DATED THIS 27th DAY OF JANUARY, 2004

[Signature]
DARLENE J. BLOOM
CLERK OF THE BOARD OF SUPERVISORS

COUNTY TREASURER-TAX COLLECTOR'S CERTIFICATE

STATE OF CALIFORNIA)
COUNTY OF ORANGE) SS

I HEREBY CERTIFY THAT ACCORDING TO THE RECORDS OF MY OFFICE THERE ARE NO LIENS AGAINST THE LAND COVERED BY THIS MAP OR ANY PART THEREOF FOR UNPAID STATE, COUNTY, MUNICIPAL OR LOCAL TAXES OR SPECIAL ASSESSMENTS COLLECTED AS TAXES, EXCEPT TAXES OR SPECIAL ASSESSMENTS COLLECTED AS TAXES NOT YET PAYABLE.

AND DO ALSO CERTIFY TO THE RECORDER OF THE COUNTY OF ORANGE THAT THE PROVISIONS OF THE SUBDIVISION MAP ACT HAVE BEEN COMPLIED WITH REGARDING DEPOSITS TO SECURE PAYMENT OF TAXES OR SPECIAL ASSESSMENTS COLLECTED AS TAXES ON THE LAND COVERED BY THIS MAP.

DATED THIS 5th DAY OF JANUARY, 2004

JOHN M.W. MOORLACH
COUNTY TREASURER-TAX COLLECTOR

BY: [Signature]
DEPUTY TREASURER -
TAX COLLECTOR

Board of Supervisor



Orange County, California

SHEET 2 OF 11 SHEETS
60 NUMBERED LOTS
23 LETTERED LOTS
83.560 ACRES
ALL OF VESTING
T.T.M. 15988
DATE OF SURVEY:
JANUARY, 1999

TRACT MAP NO. 15988

IN THE UNINCORPORATED TERRITORY OF THE COUNTY OF ORANGE,
STATE OF CALIFORNIA

HALL & FOREMAN, INC.

STEVEN C. SHAMBECK, P.L.S. 6217
FEBRUARY, 2003

SANTA MARGARITA WATER DISTRICT

STATE OF CALIFORNIA)
COUNTY OF ORANGE)

ON THIS 23rd DAY OF October 2003, BEFORE ME, Cindy R. Lane
A NOTARY PUBLIC IN AND FOR SAID STATE, PERSONALLY APPEARED DANIEL R. FERONS PERSONALLY KNOWN TO ME ~~OR PROVED TO ME ON THE BASIS OF SATISFACTORY EVIDENCE~~ TO BE THE PERSON WHOSE NAME IS SUBSCRIBED TO THE WITHIN INSTRUMENT AND ACKNOWLEDGED TO ME THAT HE EXECUTED THE SAME IN HIS AUTHORIZED CAPACITY, AND THAT BY HIS SIGNATURE ON THE INSTRUMENT THE PERSON OR THE ENTITY UPON BEHALF OF WHICH THE PERSON ACTED, EXECUTED THE INSTRUMENT.

WITNESS MY HAND:

MY COMMISSION EXPIRES 2-20-2005

Cindy R. Lane
NOTARY PUBLIC IN AND FOR SAID STATE

MY PRINCIPAL PLACE OF BUSINESS
IS IN ORANGE COUNTY

CINDY R. LANE
PRINT NAME

AUTOMATIC FIRE SPRINKLER NOTE:
ALL SINGLE FAMILY HOMES AND ALL MULTI FAMILY HOMES SHALL BE PROTECTED WITH AUTOMATIC SPRINKLER SYSTEMS.

SPECIAL FIRE PROTECTION NOTE:
PROPERTY IS IN FROM A SPECIAL FIRE PROTECTION AREA AND HAS RECIEVED A MODIFIED EXCLUSION FROM OCFA PER EXCLUSION LETTER DATED AUGUST 24, 2001

HIGH FIRE HAZARD AREA NOTE:
THE LOTS SHOWN ON THIS MAP ARE IN A HIGH FIRE HAZARD AREA DUE TO WILD LAND EXPOSURE.

SIGNATURE OMISSIONS

PURSUANT TO THE PROVISIONS OF SECTION 66436 (a)(3)(A)(C) OF THE SUBDIVISION MAP ACT, THE FOLLOWING SIGNATURES HAVE BEEN OMITTED:

LADERA DEVELOPMENT COMPANY, L.L.C., HOLDER OF OIL, GAS, AND MINERAL RIGHTS PER DEED RECORDED DECEMBER 10, 1996 AS INSTRUMENT NO. 19960624029 OF OFFICIAL RECORDS.

EASEMENT NOTES

- ☐ B INDICATES WATER, RECYCLED WATER, SEWER AND ACCESS EASEMENT DEDICATED TO SANTA MARGARITA WATER DISTRICT.
- ☐ C INDICATES DRAINAGE AND ACCESS EASEMENT DEDICATED TO SANTA MARGARITA WATER DISTRICT.
- ☐ D INDICATES SCENIC PRESERVATION EASEMENT AS DEDICATED TO THE COUNTY OF ORANGE.
- ☐ F INDICATES FIRE PROTECTION ACCESS EASEMENT AS DEDICATED TO THE COUNTY OF ORANGE.
- ☒ A INDICATS TRAIL FOR COMMUNITY PEDESTRIAN PURPOSES

BASIS OF BEARINGS

THE BEARINGS SHOWN HEREON ARE BASED ON THE BEARING BETWEEN O.C.S. HORIZONTAL CONTROL STATION GPS NO. 1417 AND STATION GPS NO. 1448, BEING NORTH 10°48'13" EAST PER RECORDS ON FILE IN THE OFFICE OF THE ORANGE COUNTY SURVEYOR.

DATUM STATEMENT

COORDINATES SHOWN ARE BASED ON THE CALIFORNIA COORDINATE SYSTEM (CCS 83), ZONE VI, 1983 NAD (1991.35 EPOCH OCS GPS ADJUSTMENT). ALL DISTANCES ARE GROUND DISTANCES UNLESS OTHERWISE NOTED. TO OBTAIN GRID DISTANCE MULTIPLY GROUND DISTANCE BY 0.999948295. THIS FACTOR IS PROJECT-SPECIFIC.

MONUMENT NOTES

- INDICATES FOUND MONUMENT AS NOTED.
- ☐ A INDICATES FOUND 2 1/2" IRON PIPE W/2" OCS BRASS CAP STAMPED "GPS 1448 9-95" PER TRACT NO. 16203, M.M. 826/8-20 AND RECORD ON FILE IN THE ORANGE COUNTY SURVEYORS OFFICE. N2146790.819, E6142602.585
- ☐ B INDICATES FOUND 2 1/2" IRON PIPE W/2" OCS BRASS CAP STAMPED "GPS 1417 9-95" PER TRACT NO. 16203, M.M. 826/8-20 AND RECORD ON FILE IN THE ORANGE COUNTY SURVEYORS OFFICE. N2141450.558, E6141583.535
- ☐ O INDICATES 2" I.P. TAGGED L.S. 6217 OR SPIKE & WASHER STAMPED L.S. 6217 OR LEAD, TACK & TAG L.S. 6217 TO BE SET PER TRACT NO. 15985 M.M. 842/8-20, UNLESS OTHERWISE NOTED.
- ☐ I INDICATES 1" I.P. TAGGED P.L.S. 5557 OR SPIKE & WASHER STAMPED P.L.S. 5557 OR LEAD, TACK & TAG P.L.S. 5557 TO BE SET PER TRACT NO. 15986 M.M. 849/1-15 UNLESS OTHERWISE NOTED.
- 2" I.P. TAGGED L.S. 6217 OR SPIKE & WASHER STAMPED L.S. 6217 OR LEAD, TACK & TAG L.S. 6217 TO BE SET AT ALL TRACT BOUNDARY CORNERS WITHIN 90 DAYS AFTER ACCEPTANCE OF IMPROVEMENTS.
- 1" I.P. TAGGED L.S. 6217 OR SPIKE & WASHER STAMPED L.S. 6217 OR LEAD, TACK & TAG L.S. 6217 TO BE SET AT LOT CORNERS WITHIN 90 DAYS AFTER ACCEPTANCE OF IMPROVEMENTS.
- 1" I.P. TAGGED L.S. 6217 OR SPIKE & WASHER STAMPED L.S. 6217 OR LEAD, TACK & TAG L.S. 6217 TO BE SET AT ALL CENTERLINE INTERSECTIONS, E.C.'S AND B.C.'S WITHIN 90 DAYS AFTER ACCEPTANCE OF IMPROVEMENTS.

NOTES

LOTS BA THROUGH BF ARE FOR PRIVATE STREET PURPOSES AND ARE NOT SEPARATE BUILDING SITES.

LOTS A THROUGH P AND R ARE FOR LANDSCAPE/OPEN SPACE PURPOSES AND ARE NOT SEPARATE RESIDENTIAL BUILDING SITES.

LOTS 55 THROUGH 60 ARE NOT RESIDENTIAL BUILDING SITES, **BUT ARE PRIVATE RECREATION SITES.**

- () INDICATES MEASURED AND RECORD PER RECORD OF SURVEY 97-1086 R.S.B. 167/26-28.
- [] INDICATES MEASURED AND RECORD PER TRACT NO. 15985 M.M. 842/8-20.
- { } INDICATES MEASURED AND RECORD PER TRACT NO. 15986 M.M. 849/1-15

SHEET 3 OF 11 SHEETS
60 NUMBERED LOTS
23 LETTERED LOTS
83.560 ACRES
ALL OF VESTING
T.T.M. 15988
DATE OF SURVEY:
JANUARY, 1999

TRACT MAP NO. 15988

IN THE UNINCORPORATED TERRITORY OF THE COUNTY OF ORANGE,
STATE OF CALIFORNIA

HALL & FOREMAN, INC.

STEVEN C. SHAMBECK, P.L.S. 6217
FEBRUARY, 2003


BOUNDARY AND INDEX SHEET

SEE SHEET 2 FOR BASIS OF
BEARINGS, DATUM STATEMENT,
MONUMENT NOTES, EASEMENT
NOTES AND NOTES

LINE	BEARING	LENGTH
L1	N53°36'17"E	15.78
L2	N68°51'36"E	11.40
L3	N53°36'17"E	30.00
L4	N38°20'59"E	11.40
L5	N38°23'43"W	10.60
L6	N57°39'06"W	28.00 (RAD)
L7	N58°11'58"W	22.00 (RAD)
L8	N67°30'17"W	36.10
L9	N77°42'51"E	0.29
L10	N54°40'40"E	2.15
L11	N51°00'57"W	45.11
L12	N73°07'42"W	5.05
L13	N80°22'11"E	6.20

LINE	BEARING	LENGTH
L14	N55°08'09"E	4.16
L15	N57°42'29"E	4.36
L16	N78°48'44"W	27.21
L17	N44°05'47"W	36.03
L18	N81°12'30"E	4.90
L19	N78°20'11"W	18.33
L20	N49°19'05"E	35.16
L21	N80°31'44"E	16.59
L22	N70°44'58"E	25.18
L23	N61°03'35"E	16.75

TRACT NO. 15988
M.M. 840/1-15

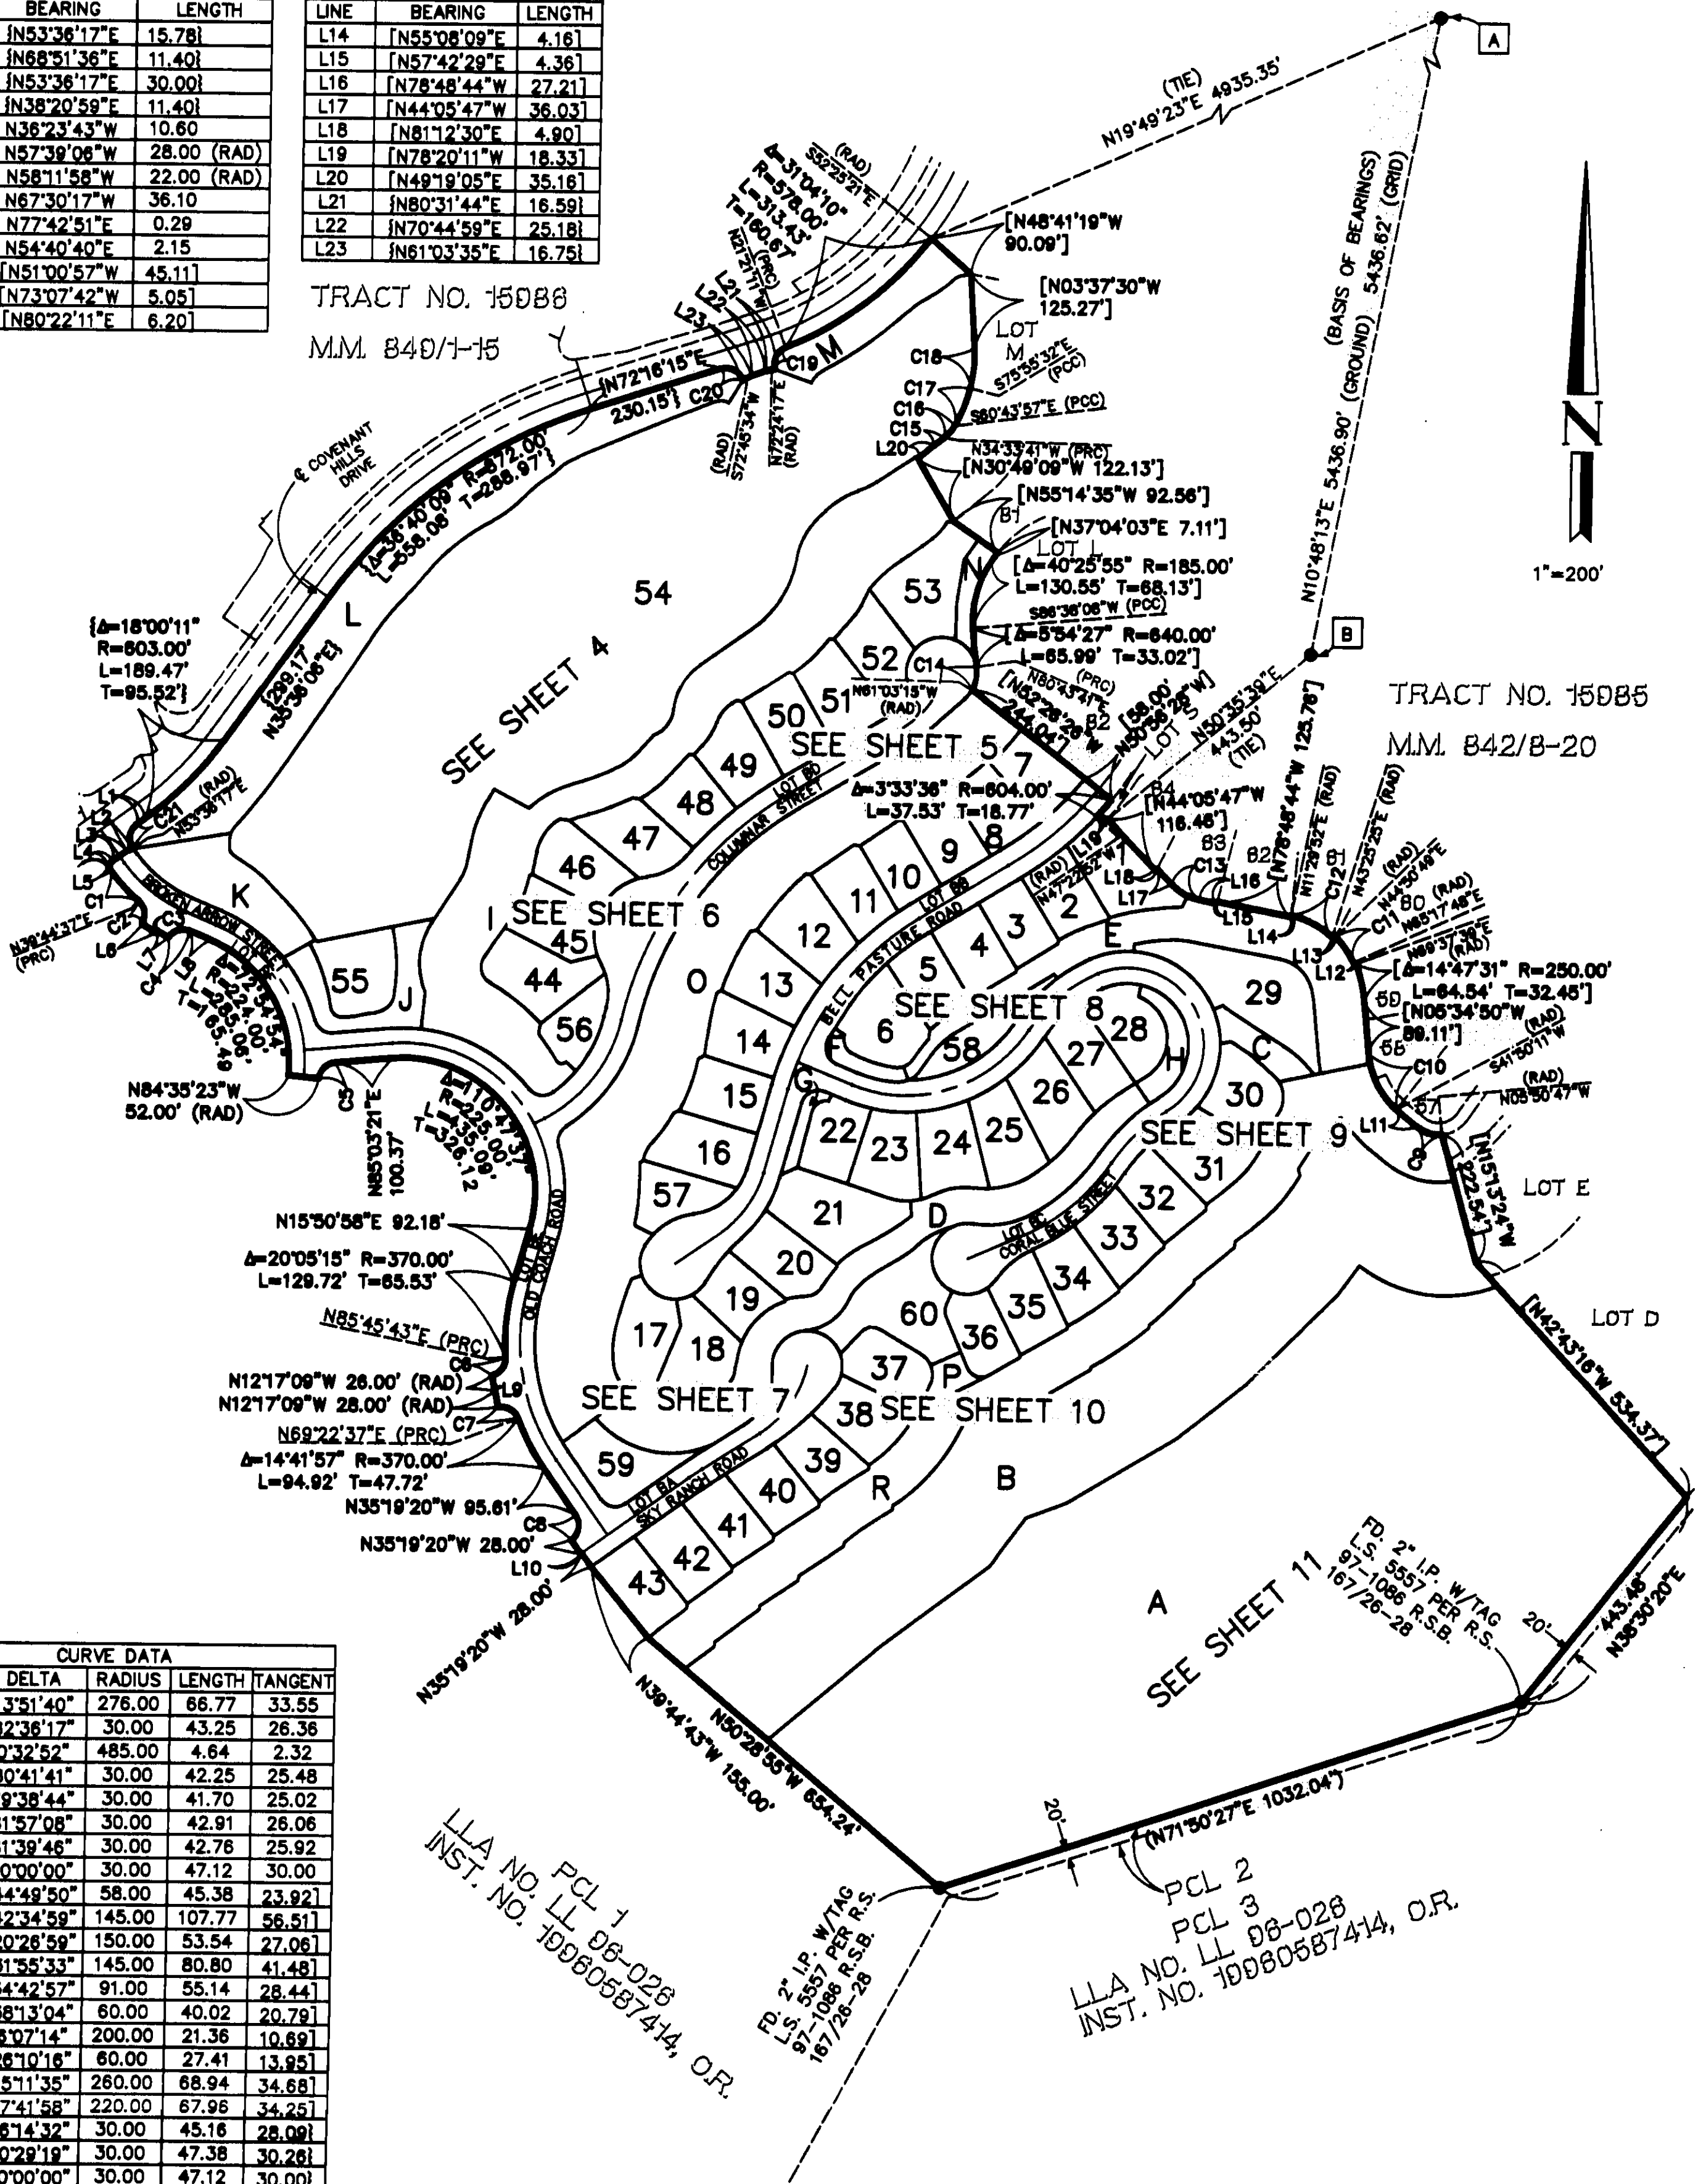

CURVE	DELTA	RADIUS	LENGTH	TANGENT
C1	13°51'40"	276.00	66.77	33.55
C2	82°36'17"	30.00	43.25	26.36
C3	0°32'52"	485.00	4.64	2.32
C4	80°41'41"	30.00	42.25	25.48
C5	79°38'44"	30.00	41.70	25.02
C6	81°57'08"	30.00	42.91	26.06
C7	81°39'46"	30.00	42.78	25.92
C8	90°00'00"	30.00	47.12	30.00
C9	44°49'50"	58.00	45.38	23.92
C10	42°34'59"	145.00	107.77	56.51
C11	20°28'59"	150.00	53.54	27.06
C12	31°55'33"	145.00	80.80	41.48
C13	34°42'57"	91.00	55.14	28.44
C14	38°13'04"	60.00	40.02	20.79
C15	6°07'14"	200.00	21.36	10.69
C16	28°10'16"	60.00	27.41	13.95
C17	15°11'35"	260.00	68.94	34.68
C18	17°41'58"	220.00	67.96	34.25
C19	18°14'32"	30.00	45.16	28.09
C20	19°29'19"	30.00	47.38	30.28
C21	19°00'00"	30.00	47.12	30.00

SHEET 4 OF 11 SHEETS
60 NUMBERED LOTS
23 LETTERED LOTS
83.560 ACRES
ALL OF VESTING
T.T.M. 15988
DATE OF SURVEY:
JANUARY, 1999

TRACT MAP NO. 15988

IN THE UNINCORPORATED TERRITORY OF THE COUNTY OF ORANGE,
STATE OF CALIFORNIA

HALL & FOREMAN, INC.

STEVEN C. SHAMBECK, P.L.S. 6217
FEBRUARY, 2003

SEE SHEET 2 FOR BASIS OF
BEARINGS, DATUM STATEMENT,
MONUMENT NOTES, EASEMENT
NOTES AND NOTES

TRACT NO. 15986
M.M. 849/1-15

LOT X


COVENANT
HILLS
DRIVE

M.M. 842/8-20

TRACT NO. 15985

SEE SHEET 5

SEE SHEET 6

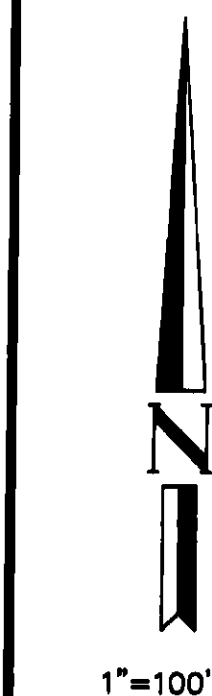

BROKEN
ARROW
STREET

OLD COACH
ROAD

PCL 1
LLA NO. LL 96-026
INST. NO. 19960587414, O.R.

CURVE DATA				
CURVE	DELTA	RADIUS	LENGTH	TANGENT
C1	6°07'14"	200.00	21.36	10.69
C2	26°10'16"	60.00	27.41	13.95
C3	17°41'58"	220.00	67.96	34.25
C4	22°04'32"	69.00	26.59	13.46
C5	17°23'01"	186.00	56.43	28.43
C6	14°15'45"	175.00	43.56	21.89
C7	42°48'32"	35.00	26.15	13.72
C8	88°14'32"	30.00	45.16	28.09
C9	90°29'19"	30.00	47.38	30.26
C10	52°49'38"	25.00	23.05	12.42
C11	5°47'59"	270.00	27.33	13.68
C12	18°06'57"	72.00	22.77	11.48
C13	15°42'28"	45.00	12.34	6.21
C14	13°34'04"	200.00	47.36	23.79
C16	26°14'45"	25.00	11.45	5.83
C17	20°35'36"	67.00	24.08	12.17
C18	52°23'35"	18.00	16.46	8.86
C19	12°40'12"	80.00	17.69	8.88
C20	90°00'00"	30.00	47.12	30.00
C21	31°06'34"	224.00	121.62	62.35
C22	13°09'53"	338.00	77.66	39.00
C23	70°29'45"	5.00	6.15	3.53
C24	27°39'27"	276.00	133.23	67.94
C25	20°57'46"	313.00	114.52	57.91
C26	22°16'42"	299.00	116.26	58.87
C27	24°32'54"	276.00	118.25	60.05
C28	79°38'43"	30.00	41.70	25.02
C29	86°10'39"	20.00	30.08	18.71
C30	11°49'25"	183.00	37.76	18.95
C31	76°34'14"	35.00	46.77	27.63
C32	10°37'03"	275.00	50.96	25.55
C33	13°51'40"	276.00	66.77	33.55
C34	82°36'17"	30.00	43.25	26.36
C35	80°41'41"	30.00	42.25	25.48
C36	31°06'34"	250.00	135.74	69.59
C37	72°54'54"	250.00	318.15	184.70
C38	110°47'37"	250.00	483.43	362.35
C39	55°38'00"	275.00	267.02	145.09
C40	10°21'16"	126.00	45.18	22.65
C41	55°49'02"	250.00	122.75	66.74
C42	52°12'22"	276.00	251.48	135.23

LINE DATA		
LINE	BEARING	LENGTH
L1	N80°31'44"E	16.59
L2	N70°44'59"E	25.18
L3	N61°03'35"E	16.75
L4	N31°32'48"E	44.51 (RAD)
L5	N53°36'17"E	15.78
L6	N68°51'36"E	11.40
L7	N53°36'17"E	30.00
L8	N38°20'59"E	11.40
L9	N36°23'43"W	10.60
L10	N36°23'43"W	10.60
L11	N36°23'43"W	13.60
L12	N60°17'24"E	61.84
L13	N60°17'24"E	50.36
L14	N60°17'24"E	11.28
L15	N85°03'21"E	18.41
L16	N85°03'21"E	100.37
L17	N67°30'17"W	54.60
L18	N85°03'21"E	151.39
L19	N04°56'39"W	50.00

SHEET 5 OF 11 SHEETS
 60 NUMBERED LOTS
 23 LETTERED LOTS
 83.560 ACRES
 ALL OF VESTING
 T.T.M. 15988
 DATE OF SURVEY:
 JANUARY, 1999

TRACT MAP NO. 15988

IN THE UNINCORPORATED TERRITORY OF THE COUNTY OF ORANGE,
 STATE OF CALIFORNIA


HALL & FOREMAN, INC.

STEVEN C. SHAMBECK, P.L.S. 6217
 FEBRUARY, 2003

SEE SHEET 2 FOR BASIS OF
 BEARINGS, DATUM STATEMENT,
 MONUMENT NOTES, EASEMENT
 NOTES AND NOTES

SEE SHEET 4

CURVE DATA				
CURVE	DELTA	RADIUS	LENGTH	TANGENT
C1	2°41'12"	220.00	10.32	5.16
C2	1°24'59"	59.00	1.46	0.73
C3	12°17'01"	250.00	53.60	26.90
C4	3°33'36"	604.00	37.53	18.77

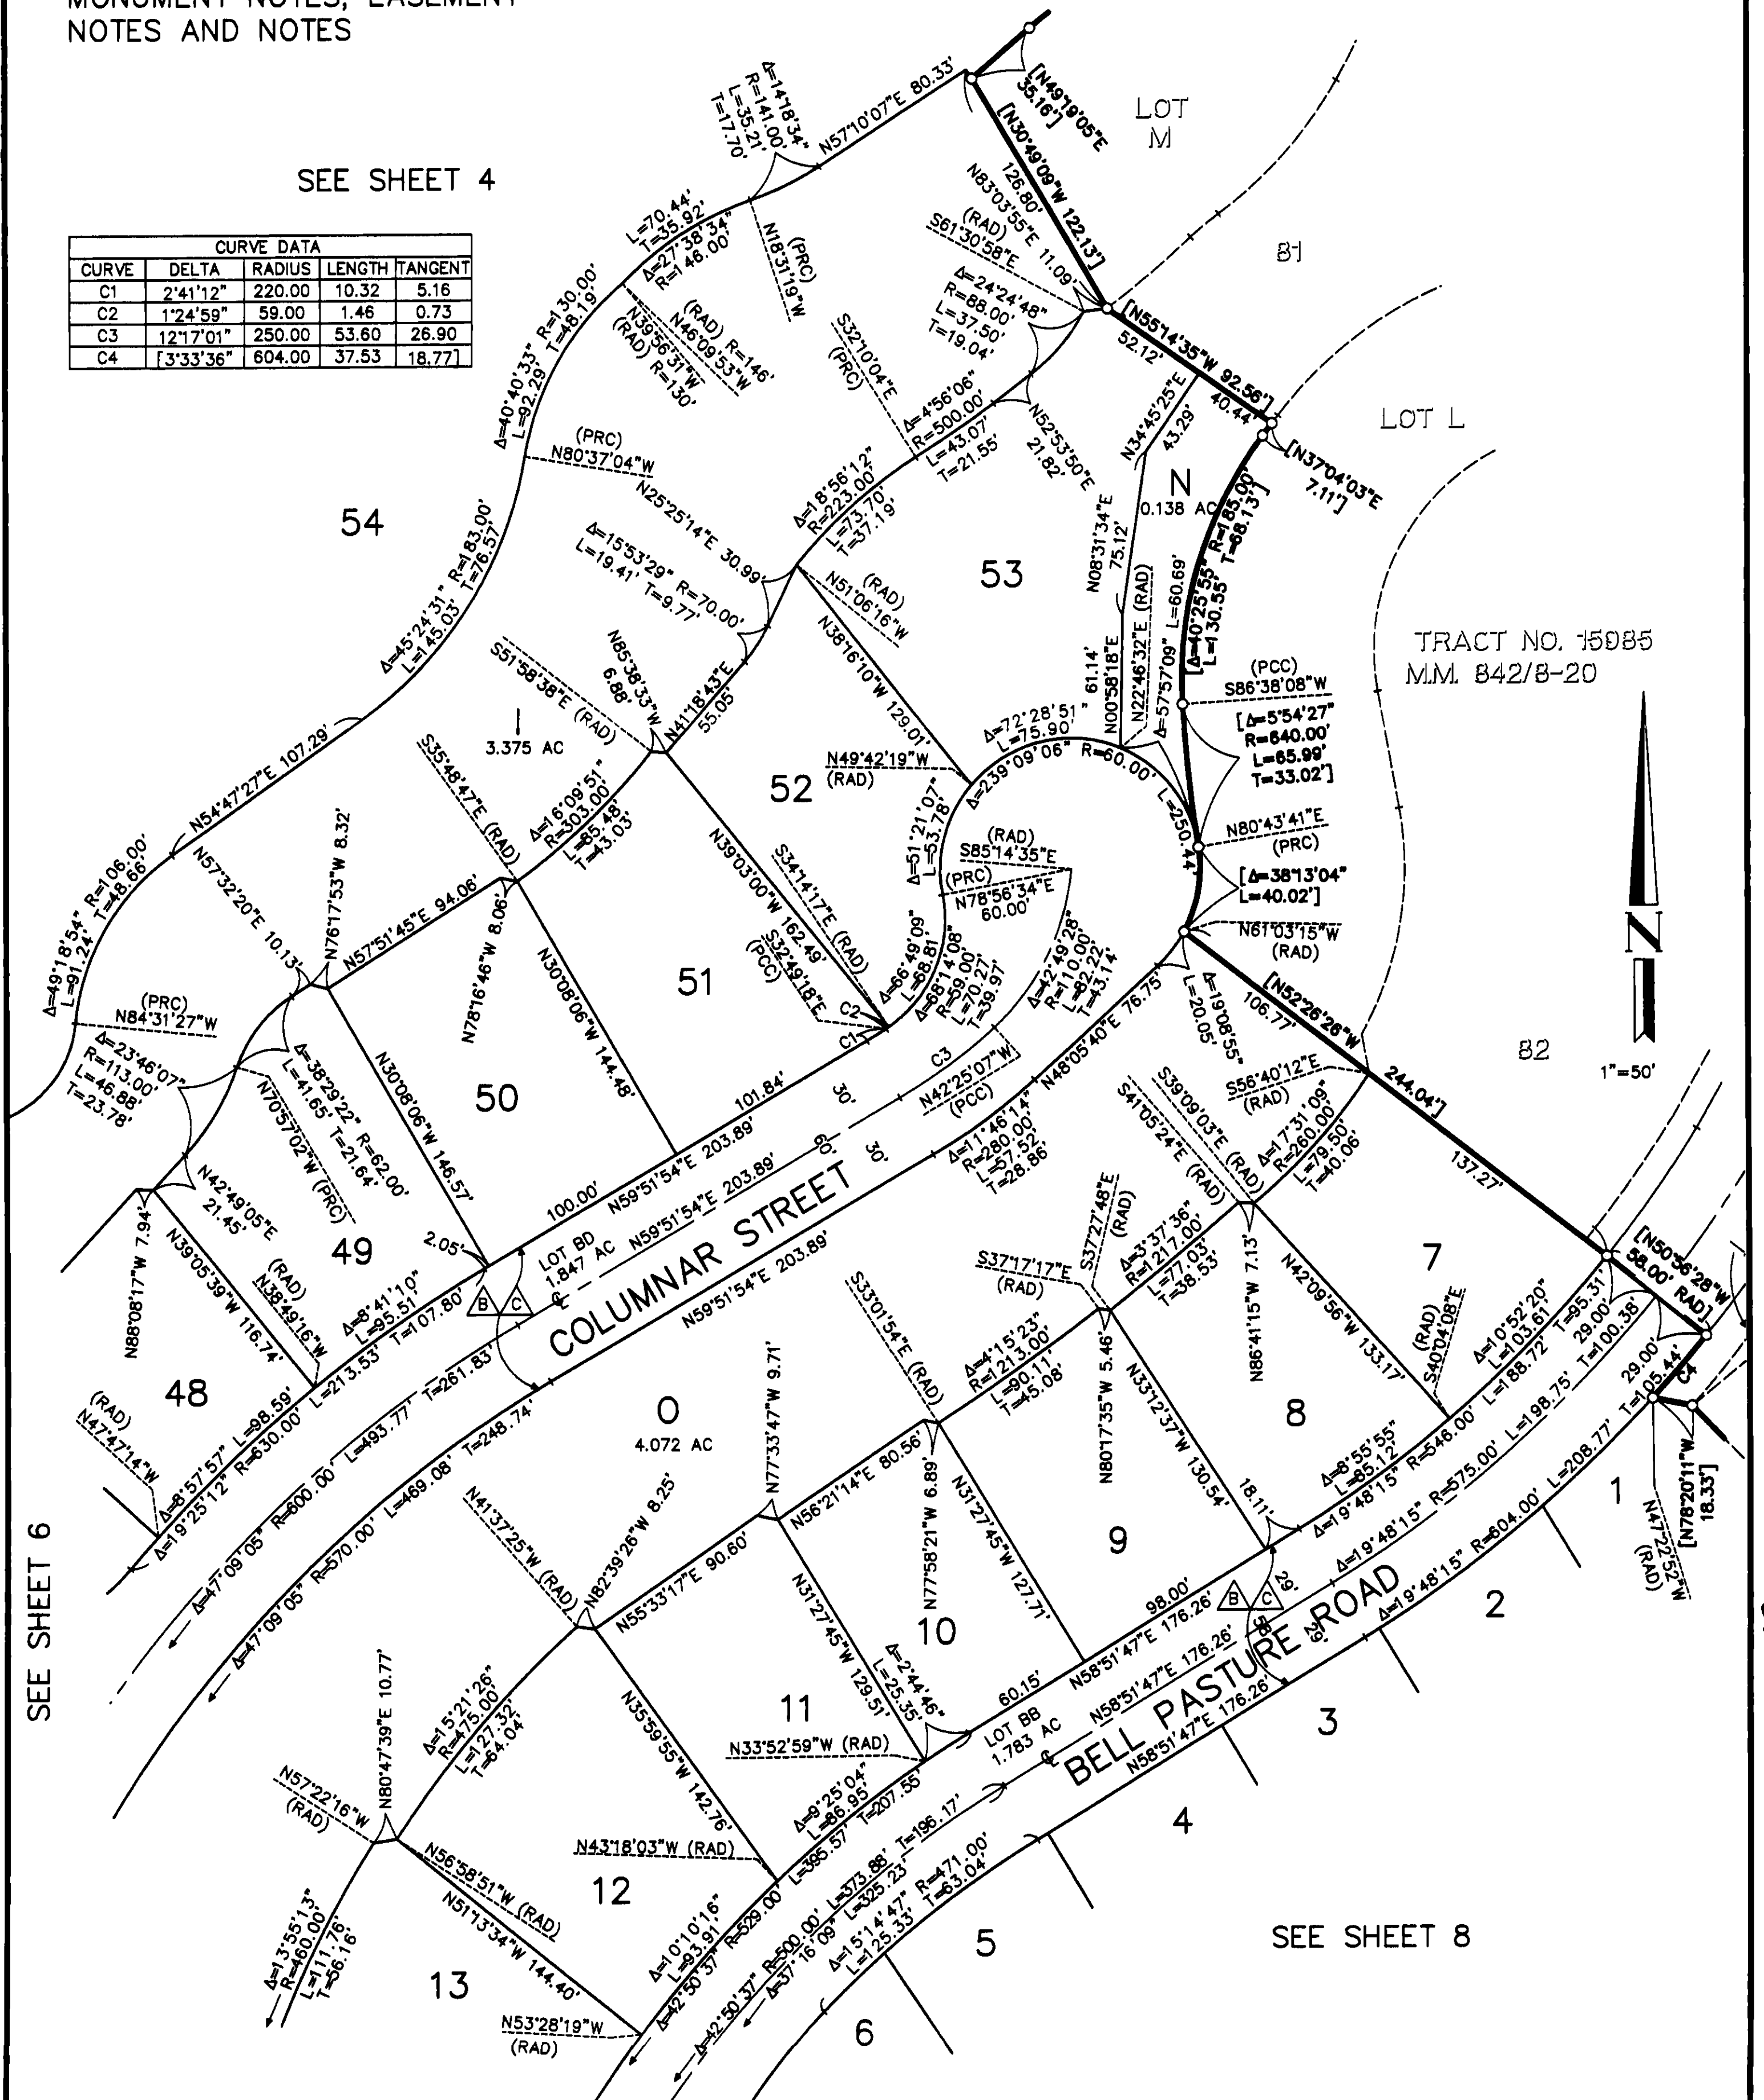

SHEET 6 OF 11 SHEETS
60 NUMBERED LOTS
23 LETTERED LOTS
83.560 ACRES
ALL OF VESTING
T.T.M. 15988
DATE OF SURVEY:
JANUARY, 1999

TRACT MAP NO. 15988

IN THE UNINCORPORATED TERRITORY OF THE COUNTY OF ORANGE,
STATE OF CALIFORNIA

HALL & FOREMAN, INC.


STEVEN C. SHAMBECK, P.L.S. 6217
FEBRUARY, 2003

SEE SHEET 2 FOR BASIS OF
BEARINGS, DATUM STATEMENT,
MONUMENT NOTES, EASEMENT
NOTES AND NOTES

SEE SHEET 4

CURVE DATA				
CURVE	DELTA	RADIUS	LENGTH	TANGENT
C1	1°21'25"	630.00	14.92	7.46
C2	9°54'14"	100.00	17.29	8.66
C3	8°59'49"	100.00	15.70	7.87
C4	13°35'09"	220.00	52.17	26.21
C5	86°53'47"	30.00	45.50	28.42
C6	8°39'25"	250.00	37.77	18.92
C7	5°25'35"	250.00	23.68	11.85

LINE DATA		
LINE	BEARING	LENGTH
L1	N36°12'26"W	30.00 (PCC)
L2	N32°58'36"W	30.00 (PCC)
L3	N62°26'59"E	20.00 (RAD)

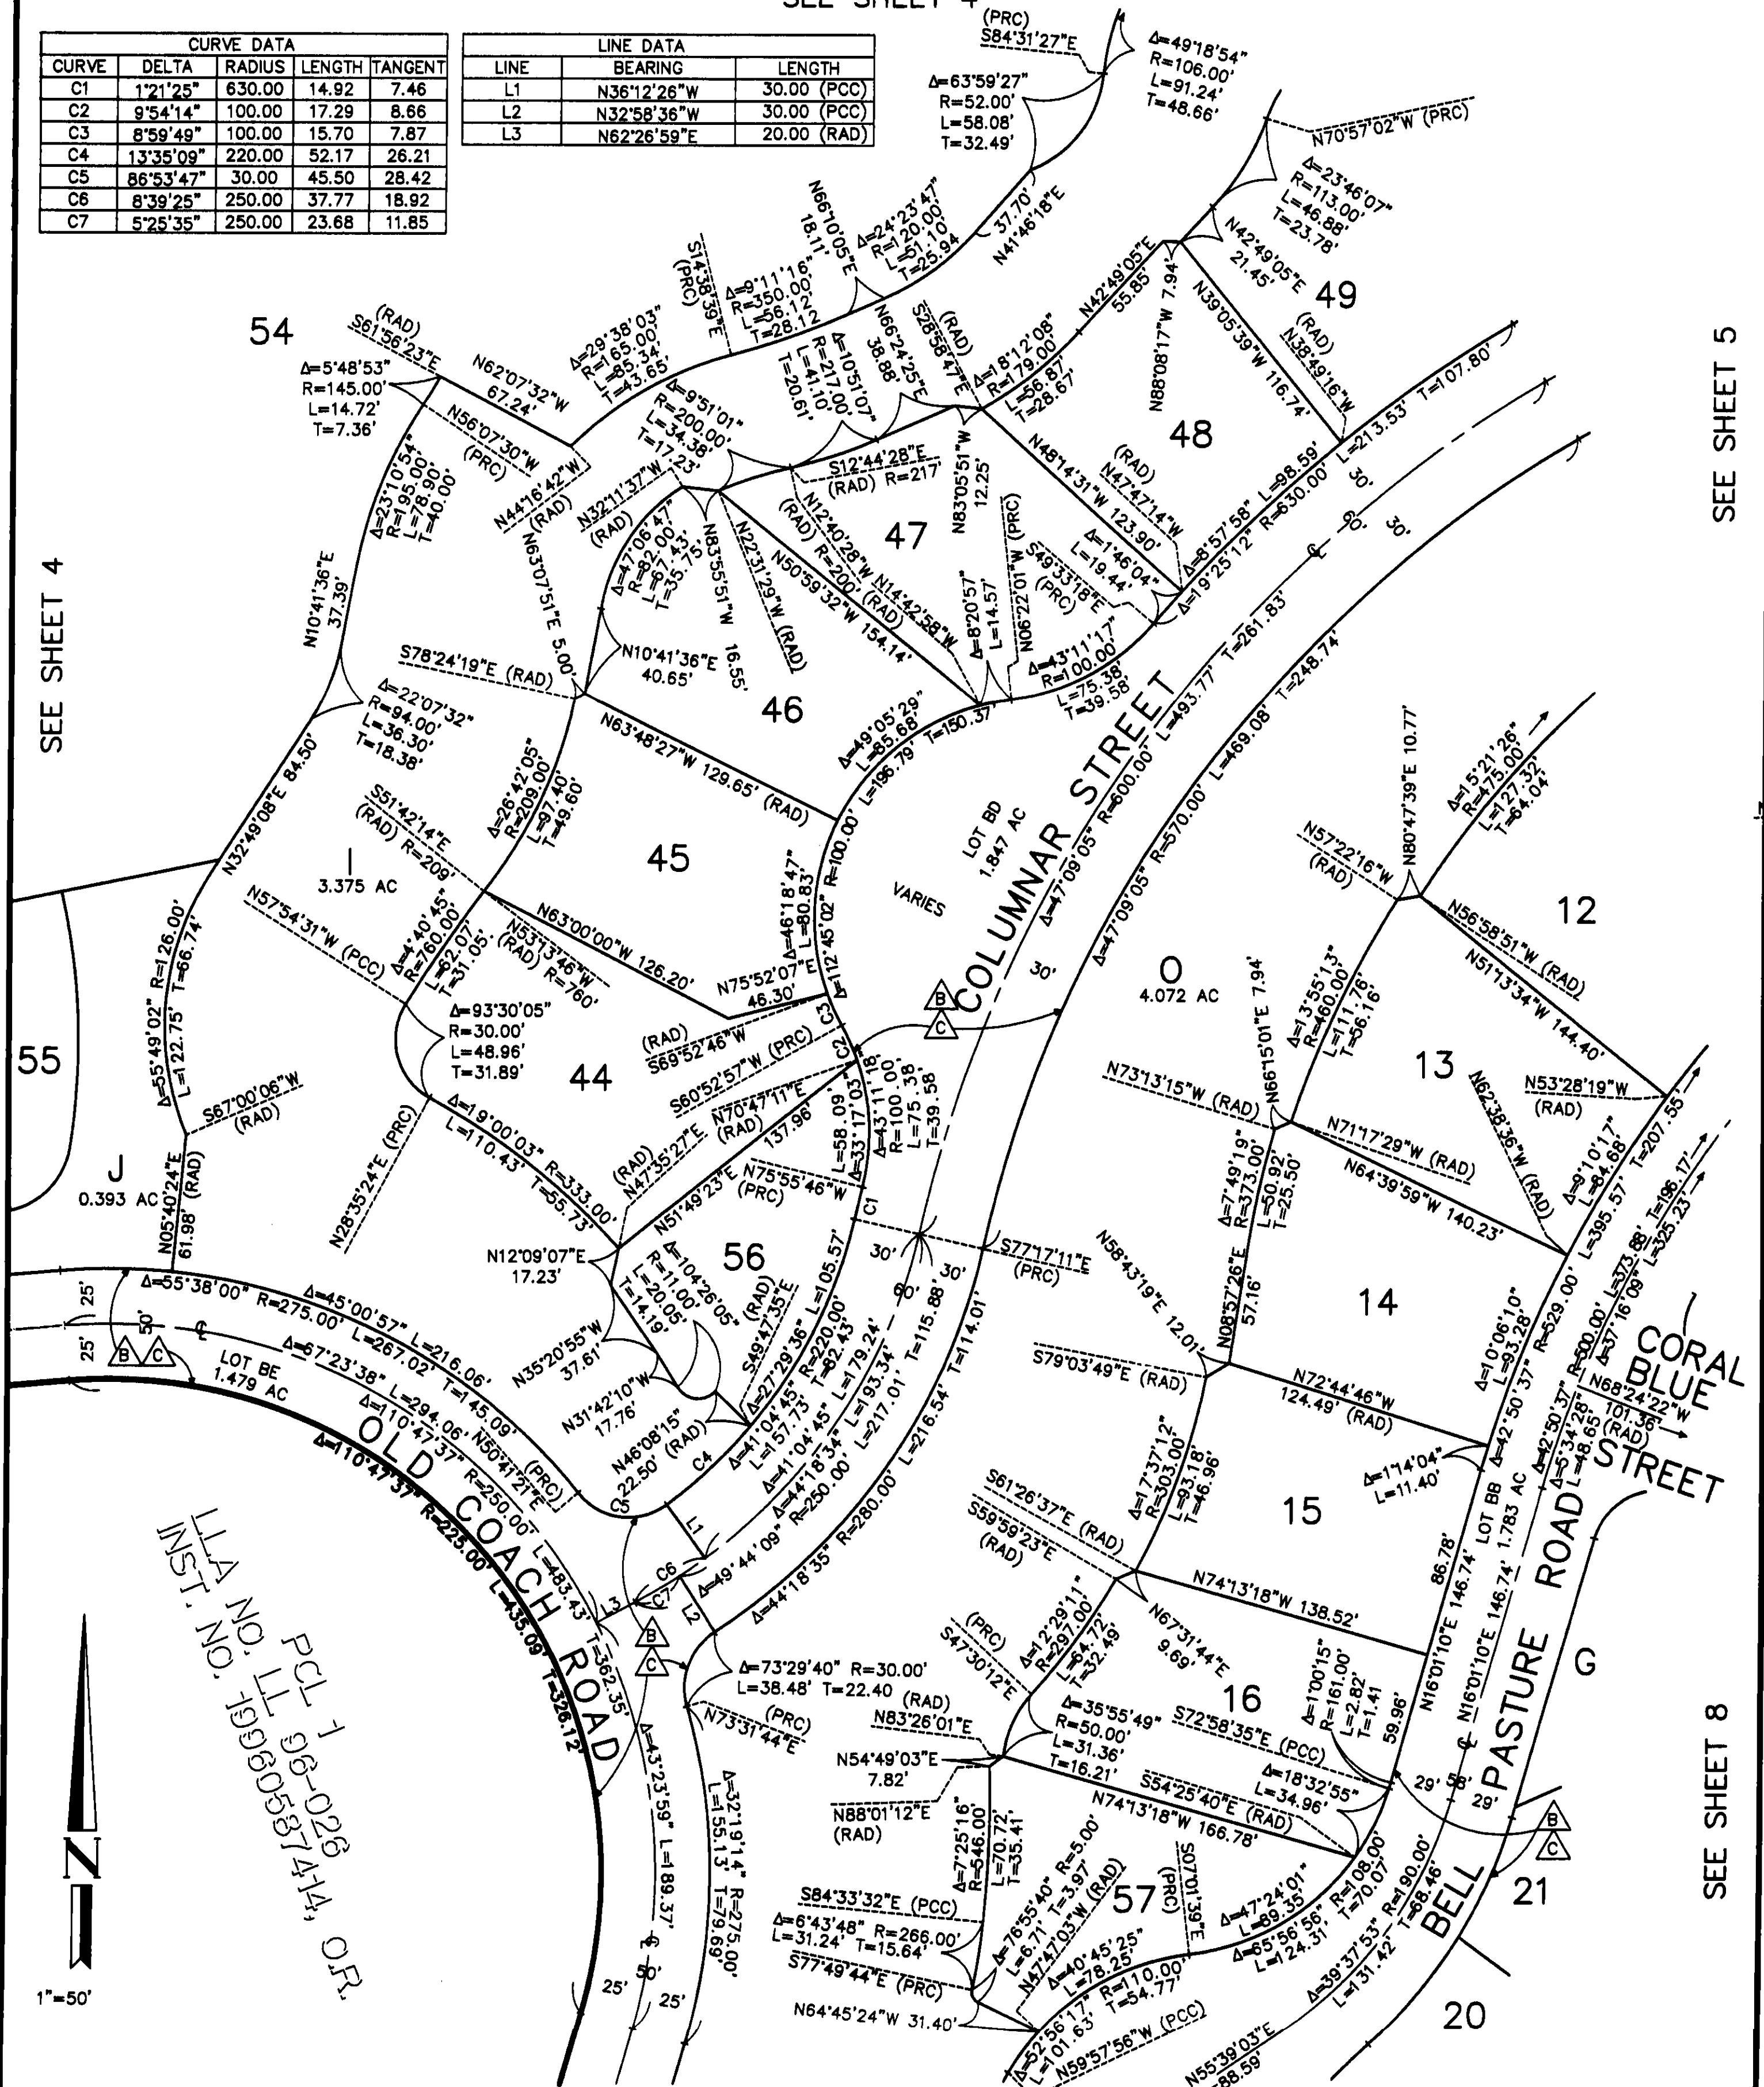

SEE SHEET 7

**SHEET 7 OF 11 SHEETS
60 NUMBERED LOTS
23 LETTERED LOTS
83.560 ACRES
ALL OF VESTING
T.T.M. 15988
DATE OF SURVEY:
JANUARY, 1999**

TRACT MAP NO. 15988

IN THE UNINCORPORATED TERRITORY OF THE COUNTY OF ORANGE,
STATE OF CALIFORNIA

HALL & FOREMAN, INC.

STEVEN C. SHAMBECK, P.L.S. 6217
FEBRUARY, 2003

SEE SHEET 2 FOR BASIS OF
BEARINGS, DATUM STATEMENT,
MONUMENT NOTES, EASEMENT
NOTES AND NOTES

SEE SHEET 6


CURVE DATA				
CURVE	DELTA	RADIUS	LENGTH	TANGENT
C1	14°51'09"	70.00	18.15	9.12
C2	21°05'06"	124.00	45.63	23.08
C3	11°30'26"	63.00	12.65	6.35
C4	9°51'53"	57.00	9.81	4.92
C5	8°40'51"	450.00	68.18	34.15

-BELL PASTURE ROAD

SEE SHEET 8

SEE SHEET 10

B/h 854 pg 12

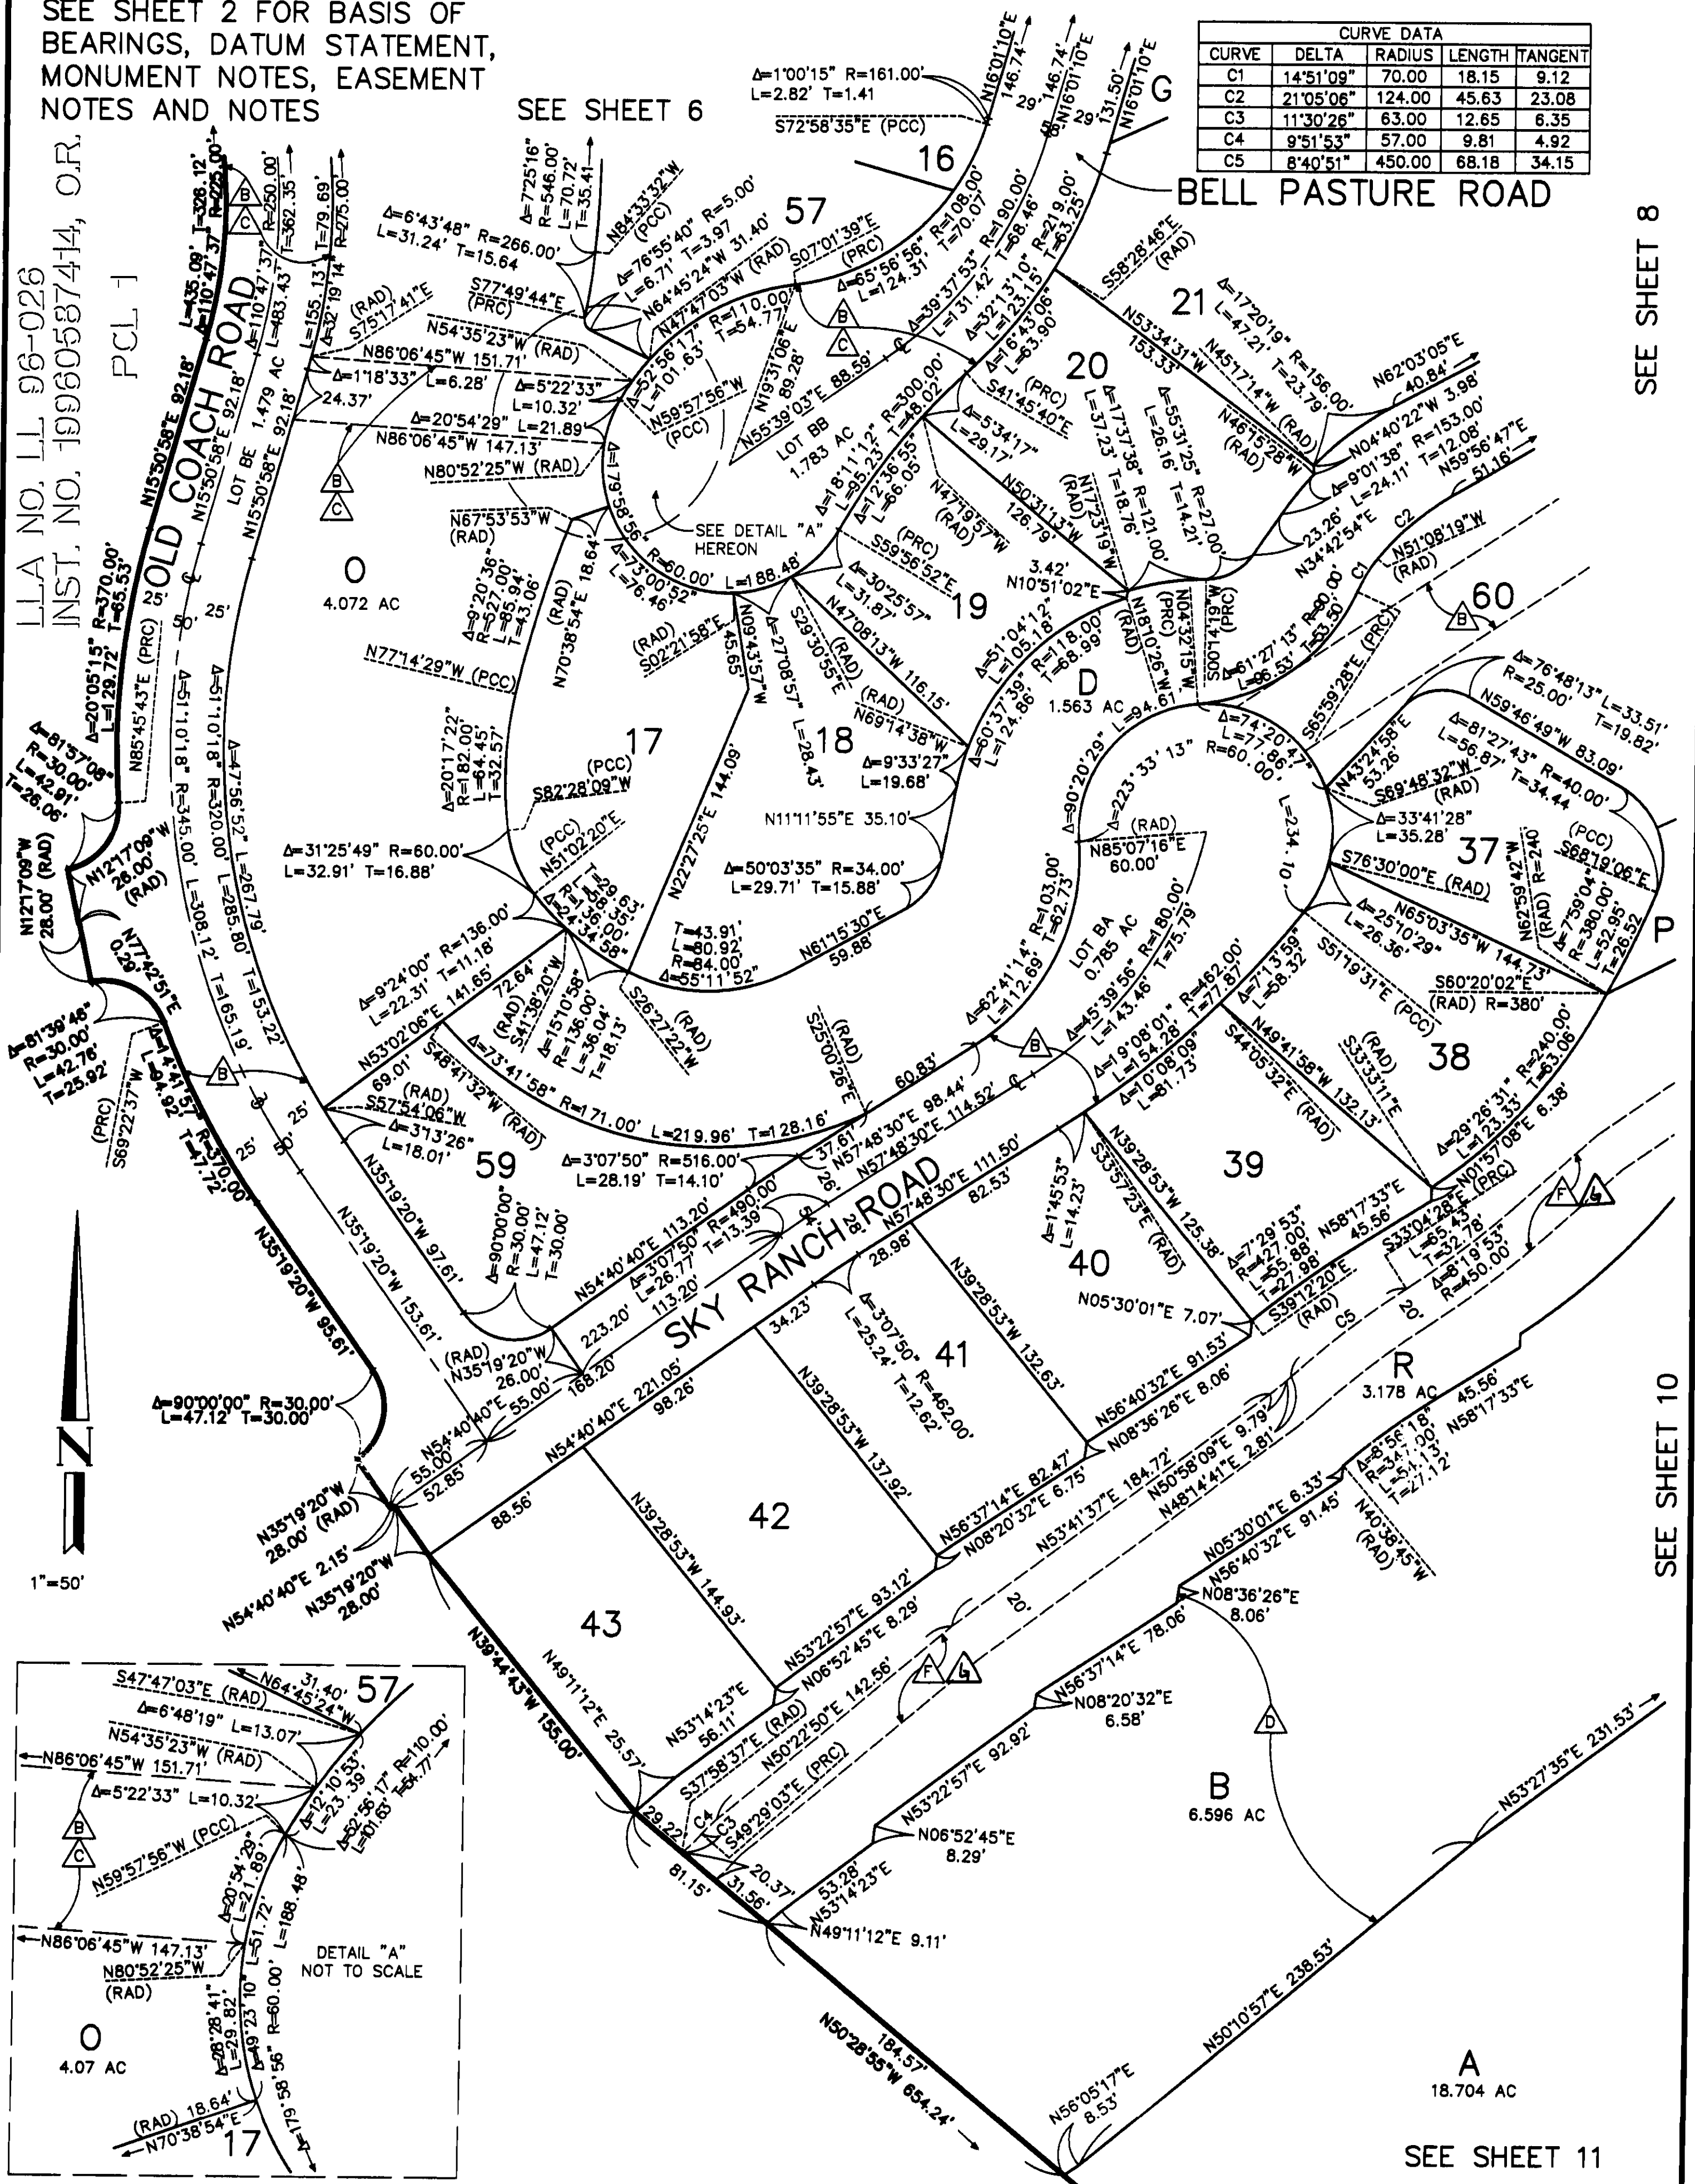

SEE SHEET 11

SHEET 8 OF 11 SHEETS
60 NUMBERED LOTS
23 LETTERED LOTS
83.560 ACRES
ALL OF VESTING
T.T.M. 15988
DATE OF SURVEY:
JANUARY, 1999

TRACT MAP NO. 15988

IN THE UNINCORPORATED TERRITORY OF THE COUNTY OF ORANGE,
STATE OF CALIFORNIA


HALL & FOREMAN, INC.

STEVEN C. SHAMBECK, P.L.S. 6217
FEBRUARY, 2003

SEE SHEET 2 FOR BASIS OF
BEARINGS, DATUM STATEMENT,
MONUMENT NOTES, EASEMENT
NOTES AND NOTES

SEE SHEET 5

TRACT NO. 15085
M.M. 842/B-20

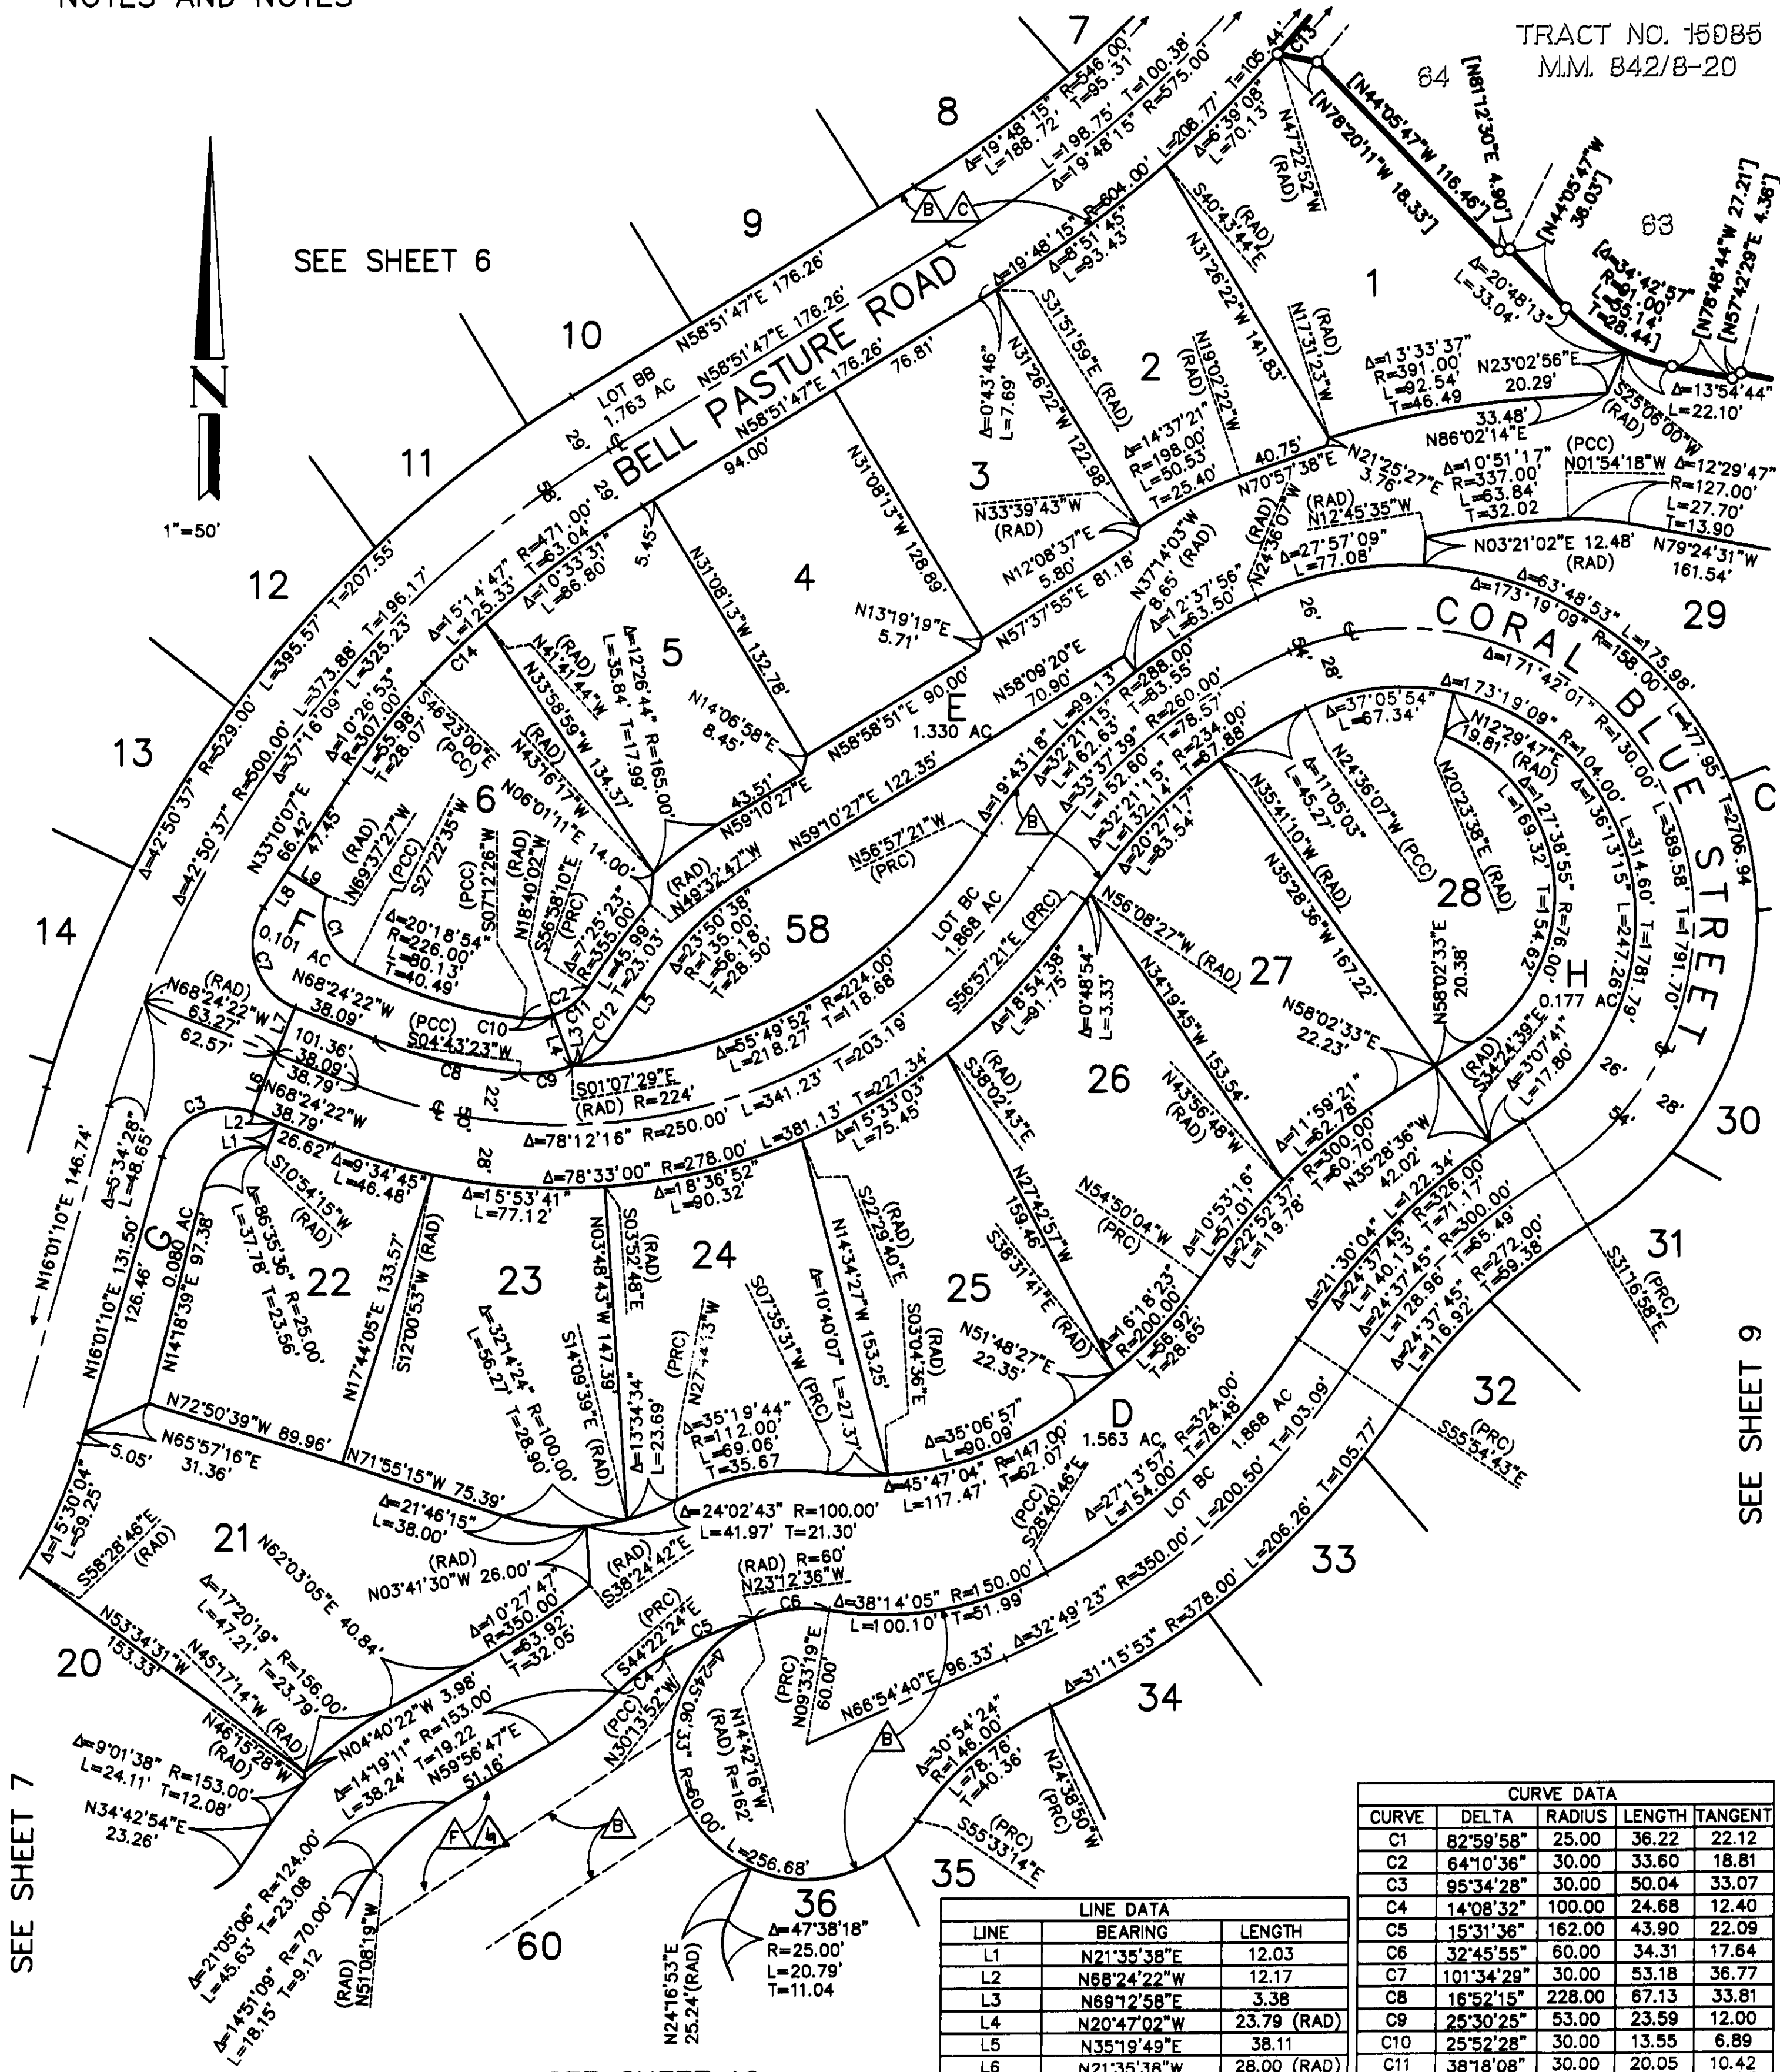

CURVE DATA				
CURVE	DELTA	RADIUS	LENGTH	TANGENT
C1	82°59'58"	25.00	36.22	22.12
C2	64°10'36"	30.00	33.60	18.81
C3	95°34'28"	30.00	50.04	33.07
C4	14°08'32"	100.00	24.68	12.40
C5	15°31'36"	162.00	43.90	22.09
C6	32°45'55"	60.00	34.31	17.64
C7	101°34'29"	30.00	53.18	36.77
C8	16°52'15"	228.00	67.13	33.81
C9	25°30'25"	53.00	23.59	12.00
C10	25°52'28"	30.00	13.55	6.89
C11	38°18'08"	30.00	20.05	10.42
C12	33°53'09"	30.00	17.74	9.14
C13	3°33'38"	604.00	37.53	18.77
C14	4°41'16"	471.00	38.54	19.28

LINE DATA		
LINE	BEARING	LENGTH
L1	N21°35'38"E	12.03
L2	N68°24'22"W	12.17
L3	N89°12'58"E	3.38
L4	N20°47'02"W	23.79 (RAD)
L5	N35°19'49"E	38.11
L6	N21°35'38"W	28.00 (RAD)
L7	N21°35'38"E	22.00 (RAD)
L8	N33°10'07"E	18.97
L9	N58°59'52"W	20.52

SEE SHEET 7

SEE SHEET 10

SEE SHEET 9

3h 854 pg 13


TRACT MAP NO. 15988

IN THE UNINCORPORATED TERRITORY OF THE COUNTY OF ORANGE,
STATE OF CALIFORNIA

HALL & FOREMAN, INC.

STEVEN C. SHAMBECK, P.L.S. 6217
FEBRUARY, 2003

SEE SHEET 2 FOR BASIS OF
BEARINGS, DATUM STATEMENT,
MONUMENT NOTES, EASEMENT
NOTES AND NOTES

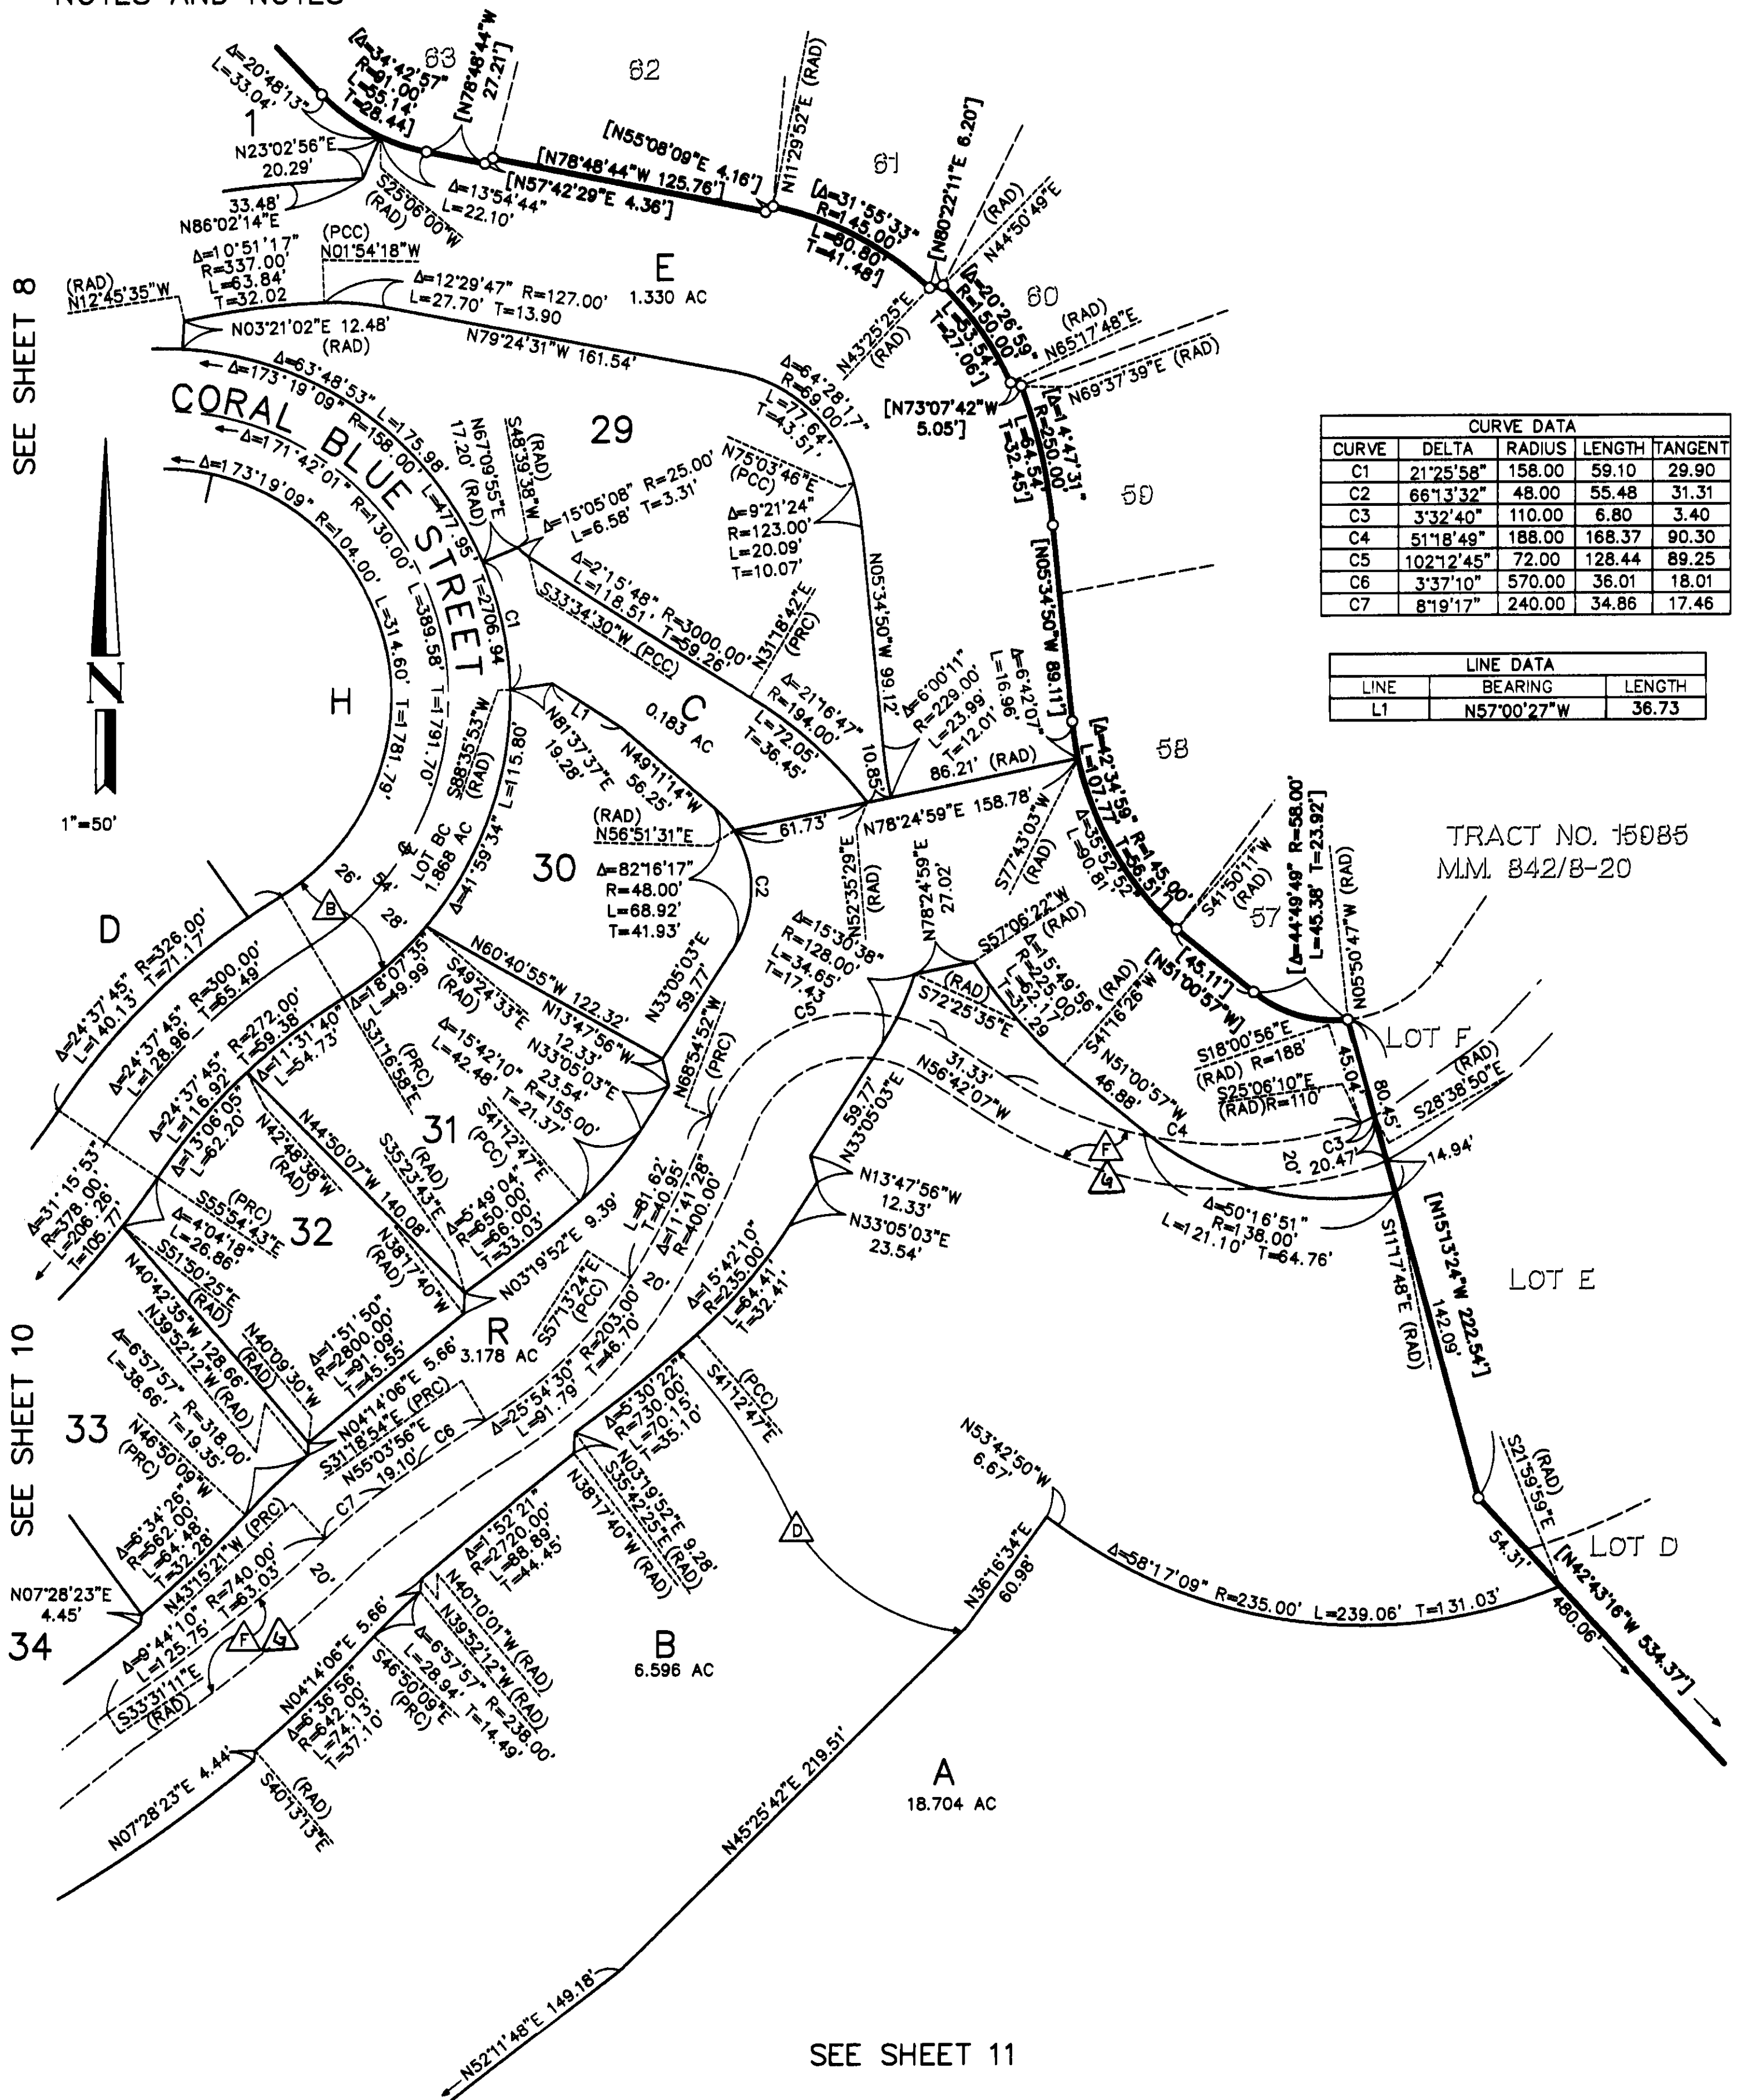

CURVE DATA				
CURVE	DELTA	RADIUS	LENGTH	TANGENT
C1	21°25'58"	158.00	59.10	29.90
C2	66°13'32"	48.00	55.48	31.31
C3	3°32'40"	110.00	6.80	3.40
C4	51°18'49"	188.00	168.37	90.30
C5	102°12'45"	72.00	128.44	89.25
C6	3°37'10"	570.00	36.01	18.01
C7	8°19'17"	240.00	34.86	17.46

LINE DATA		
LINE	BEARING	LENGTH
L1	N57°00'27"W	36.73

TRACT NO. 15085
MM. 842/8-20

BK 854 pg 14

TRACT MAP NO. 15988


IN THE UNINCORPORATED TERRITORY OF THE COUNTY OF ORANGE,
STATE OF CALIFORNIA

HALL & FOREMAN, INC.

STEVEN C. SHAMBECK, P.L.S. 6217
FEBRUARY, 2003

SEE SHEET 2 FOR BASIS OF
BEARINGS, DATUM STATEMENT,
MONUMENT NOTES, EASEMENT
NOTES AND NOTES

CURVE DATA				
CURVE	DELTA	RADIUS	LENGTH	TANGENT
C1	76°48'13"	25.00	33.51	19.82
C2	81°27'43"	40.00	56.87	34.44
C3	36°33'34"	40.00	25.52	13.21
C4	44°54'09"	40.00	31.35	16.53

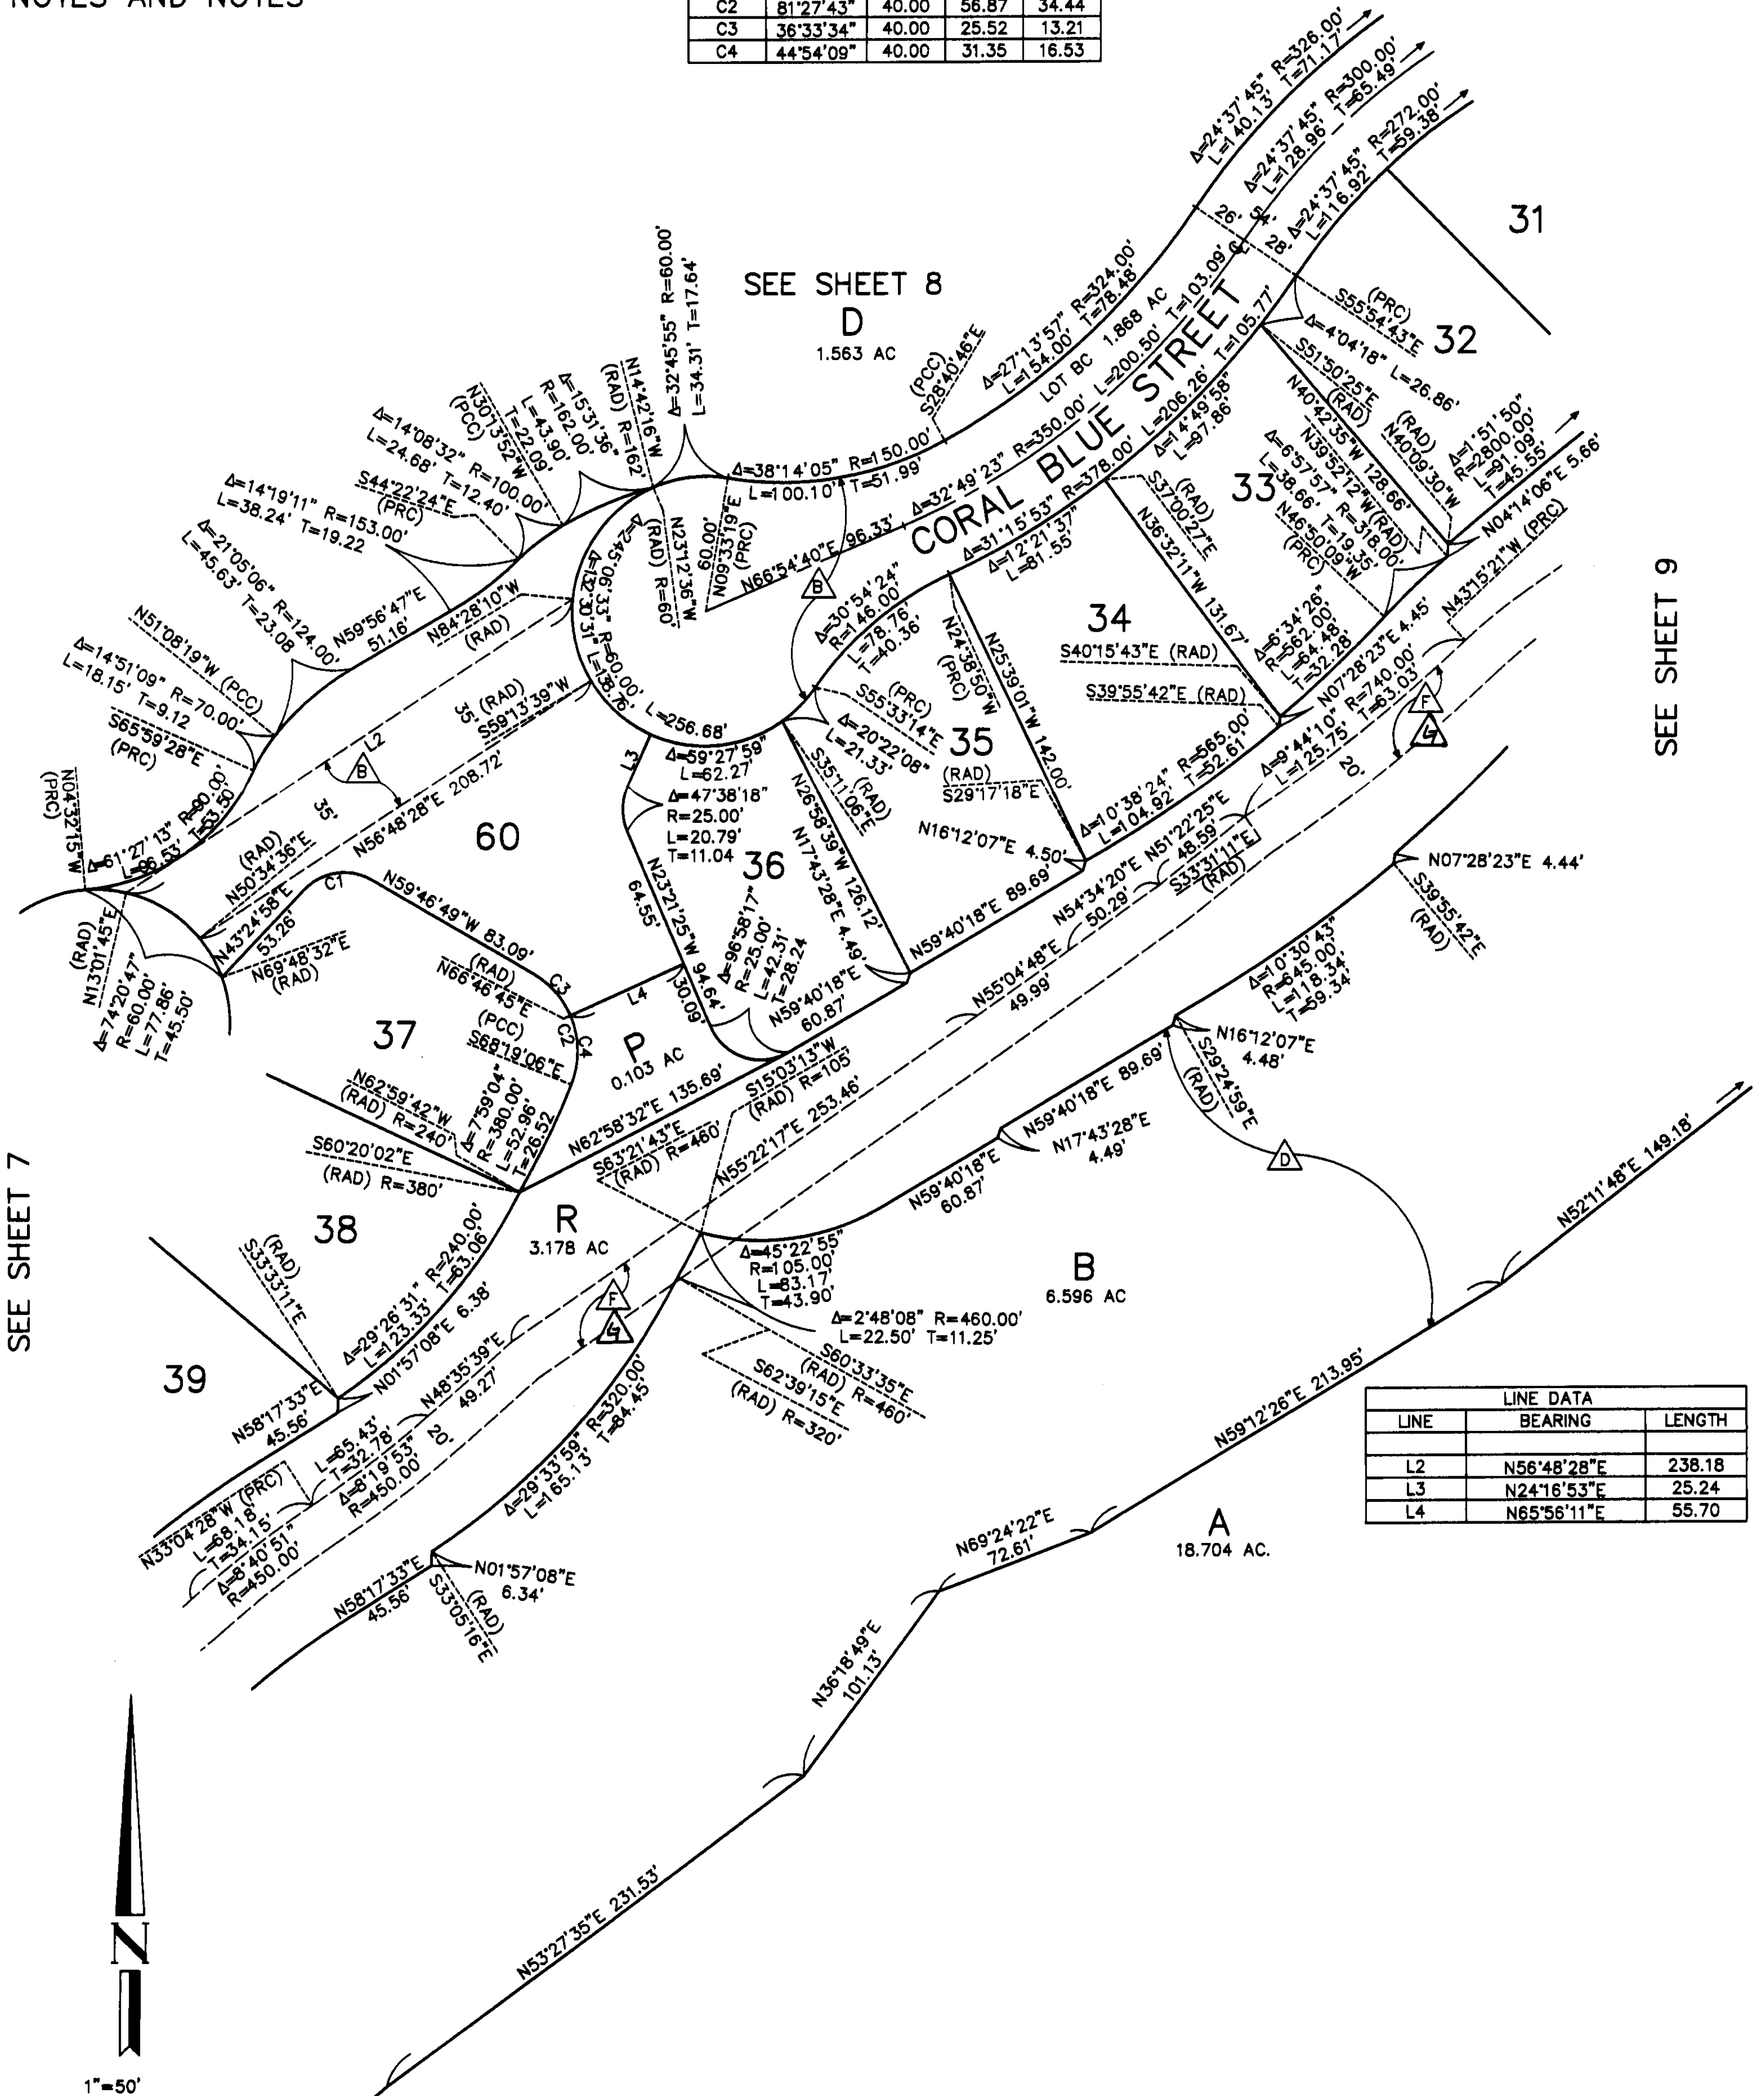

LINE DATA		
LINE	BEARING	LENGTH
L2	N56°48'28"E	238.18
L3	N24°16'53"E	25.24
L4	N65°56'11"E	55.70

SHEET 11 OF 11 SHEETS
60 NUMBERED LOTS
23 LETTERED LOTS
83,560 ACRES
ALL OF VESTING
T.T.M. 15988
DATE OF SURVEY:
JANUARY, 1999

TRACT MAP NO. 15988

IN THE UNINCORPORATED TERRITORY OF THE COUNTY OF ORANGE,
STATE OF CALIFORNIA


HALL & FOREMAN, INC.

STEVEN C. SHAMBECK, P.L.S. 6217

FEBRUARY, 2003

SEE SHEET 9

SEE SHEET 2 FOR BASIS OF BEARINGS, DATUM STATEMENT, MONUMENT NOTES, EASEMENT NOTES AND NOTES

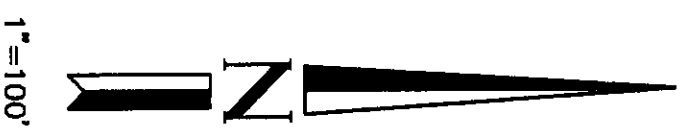

SEE SHEET 7

SEE SHEET 10

R
3.178 AC

B
6.596 AC.

N52°11'48"E
149.18'

48: _____