

SHEET 1 OF 7 SHEETS
37 NUMBERED LOTS
13 LETTERED LOTS
25.212 ACRES
FINAL UNIT OF VESTING
T.T.M. 15989
DATE OF SURVEY:
JANUARY, 1999

TRACT MAP NO. 15989

IN THE UNINCORPORATED TERRITORY OF THE COUNTY OF ORANGE,
STATE OF CALIFORNIA

BEING A SUBDIVISION OF A PORTION OF PARCEL 1 OF LOT LINE ADJUSTMENT NO.
LL 96-026, IN THE UNINCORPORATED TERRITORY OF THE COUNTY OF ORANGE,
STATE OF CALIFORNIA, AS SHOWN ON EXHIBIT "B" ATTACHED TO THAT CERTAIN
DOCUMENT RECORDED NOVEMBER 21, 1996 AS INSTRUMENT NO. 19960587414 OF
OFFICIAL RECORDS, IN THE OFFICE OF THE COUNTY RECORDER OF SAID COUNTY.

HALL & FOREMAN, INC.

STEVEN C. SHAMBECK, P.L.S. 6217
JUNE, 2004

ACCEPTED AND FILED AT THE
REQUEST OF

FIRST AMERICAN TITLE INSURANCE COMPANY
DATE November 15, 2004
TIME 2:50 PM FEES 25.00
INSTRUMENT # 2004001019766
BOOK 863 PAGE 8-14 MM

TOM DALY
COUNTY CLERK-RECORDER

DEPUTY

OWNERSHIP CERTIFICATE

WE, THE UNDERSIGNED, BEING ALL PARTIES HAVING ANY RECORD TITLE INTEREST
IN THE LAND COVERED BY THIS MAP, DO HEREBY CONSENT TO THE PREPARATION
AND RECORDATION OF SAID MAP, AS SHOWN WITHIN THE DISTINCTIVE BORDER
LINE.

WE ALSO HEREBY DEDICATE TO THE COUNTY OF ORANGE:

1. AN EASEMENT FOR EMERGENCY ACCESS PURPOSES OVER ALL OF LOTS BA
THROUGH BC
2. THE EASEMENT FOR PUBLIC PEDESTRIAN PURPOSES AS
DEDICATED.

WE ALSO HEREBY DEDICATE TO THE SANTA MARGARITA WATER DISTRICT THE EASEMENTS
FOR WATER, RECYCLED WATER, SEWER, AND ACCESS PURPOSES OVER THOSE EASEMENT
AREAS AS SHOWN ON SAID MAP WHICH EASEMENTS SHALL BE SUBJECT TO THE SAME
CONDITIONS AS ARE SHOWN IN THAT CERTAIN GRANT OF EASEMENT TO SANTA MARGARITA
WATER DISTRICT RECORDED SEPTEMBER 18, 2002 AS INSTRUMENT NO. 20020799401, OF
OFFICIAL RECORDS, COUNTY OF ORANGE.

DMB LADERA, L.L.C., A DELAWARE LIMITED LIABILITY COMPANY

BY: RANCHO MISSION VIEJO, L.L.C. A DELAWARE LIMITED LIABILITY COMPANY,
IT'S AUTHORIZED AGENT OR MANAGER.

BY: Paul Johnson BY: Gregory S. Edwards
PRINT NAME: PAUL JOHNSON PRINT NAME: GREGORY S. EDWARDS
PRINT TITLE: SVP - COMM. DEVELOP. PRINT TITLE: SVP - C.F.O.

NOTARY ACKNOWLEDGEMENT

STATE OF CALIFORNIA
COUNTY OF ORANGE)SS

ON August 2, 2004 BEFORE ME, LINDA K. LEDGER,
NOTARY PUBLIC
PERSONALLY APPEARED PAUL JOHNSON and GREGORY S. EDWARDS
PERSONALLY KNOWN TO ME (OR PROVED TO ME ON THE BASIS OF SATISFACTORY
EVIDENCE) TO BE THE PERSON(S) WHOSE NAME(S) IS/ARE SUBSCRIBED TO THE
WITHIN INSTRUMENT AND ACKNOWLEDGED TO ME THAT HE/SHE/HEY EXECUTED
THE SAME IN HIS/HER/THEIR AUTHORIZED CAPACITY(IES), AND THAT BY HIS/
HER/THEIR SIGNATURE(S) ON THE INSTRUMENT THE PERSON(S), OR THE ENTITY UPON
BEHALF OF WHICH THE PERSON(S) ACTED, EXECUTED THE INSTRUMENT.

WITNESS MY HAND:

Linda K. Ledger
NOTARY PUBLIC IN AND FOR SAID STATE

LINDA K. LEDGER
PRINT NAME

MY PRINCIPAL PLACE OF BUSINESS IS IN ORANGE COUNTY
MY COMMISSION EXPIRES 03/07/07

CERTIFICATE OF ACCEPTANCE

THE UNDERSIGNED, BEING THE DULY APPOINTED AGENT OF THE SANTA MARGARITA
WATER DISTRICT, A PUBLIC CORPORATION OF ORANGE COUNTY, CALIFORNIA, PURSUANT
TO ITS RESOLUTION NO. 88-10-02, DOES HEREBY ACCEPT ON BEHALF OF SAID
DISTRICT THE EASEMENTS FOR, WATER, RECYCLED WATER, SEWER, AND ACCESS
PURPOSES, AS DEDICATED AND AS SHOWN ON THIS TRACT MAP, BY AND BETWEEN
THE SANTA MARGARITA WATER DISTRICT AND DMB LADERA, L.L.C., AND DOES HEREBY
CERTIFY THAT THE GRANTEE CONSENTS TO THE RECORDATION OF SAID TRACT.

Daniel R. Perons
DANIEL R. PERONS, CHIEF ENGINEER
SANTA MARGARITA WATER DISTRICT


SEE SHEET 2 FOR ADDITIONAL NOTARY ACKNOWLEDGMENT AND SIGNATURE OMISSIONS

SURVEYOR'S STATEMENT

THIS MAP WAS PREPARED BY ME OR UNDER MY DIRECTION AND IS BASED UPON A
FIELD SURVEY IN CONFORMANCE WITH THE REQUIREMENTS OF THE SUBDIVISION MAP
ACT AND LOCAL ORDINANCE AT THE REQUEST OF DMB LADERA, LLC IN JANUARY,
1999. I HEREBY STATE THAT ALL MONUMENTS ARE OF THE CHARACTER AND
OCCUPY THE POSITIONS INDICATED, OR THAT THEY WILL BE SET IN SUCH
POSITIONS; AND THAT SAID MONUMENTS ARE SUFFICIENT TO ENABLE THE SURVEY
TO BE RETRACED. I HEREBY STATE THAT THIS FINAL MAP SUBSTANTIALLY
CONFORMS TO THE CONDITIONALLY APPROVED TENTATIVE MAP.

Steven C. Shambeck
STEVEN C. SHAMBECK, P.L.S. 6217
LICENSE EXPIRES: 3/31/06

7-30-2004
DATE

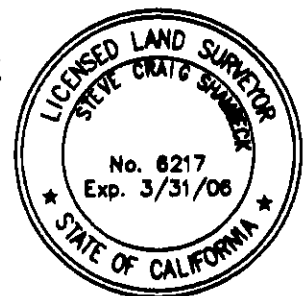

COUNTY SURVEYOR'S STATEMENT

I HEREBY STATE THAT I HAVE EXAMINED THIS MAP AND HAVE FOUND IT TO BE
SUBSTANTIALLY IN CONFORMANCE WITH THE TENTATIVE MAP AS FILED WITH,
AMENDED AND APPROVED BY THE ORANGE COUNTY SUBDIVISION COMMITTEE; THAT
ALL PROVISIONS OF THE SUBDIVISION MAP ACT AND COUNTY SUBDIVISION
REGULATIONS HAVE BEEN COMPLIED WITH AND I AM SATISFIED SAID MAP IS
TECHNICALLY CORRECT.

DATED THIS 12TH DAY OF OCTOBER, 2004.

Michael K. Sullivan
RAYMOND L. MATHE, COUNTY SURVEYOR
L.S. 6185 EXPIRATION DATE: 3-31-06

BY: MICHAEL K. SULLIVAN, DEPUTY
LS 6254 EXPIRES 03/31/06



CLERK OF THE BOARD OF SUPERVISOR'S CERTIFICATE

STATE OF CALIFORNIA)
COUNTY OF ORANGE) SS

I HEREBY CERTIFY THAT THIS MAP WAS PRESENTED FOR APPROVAL TO THE
BOARD OF SUPERVISORS OF ORANGE COUNTY AT A REGULAR MEETING THEREOF
HELD ON THE 9th DAY OF November, 2004 AND THAT
THEREUPON SAID BOARD DID, BY AN ORDER DULY PASSED AND ENTERED,
APPROVE SAID MAP.


AND DID ALSO ACCEPT ON BEHALF OF THE COUNTY OF ORANGE:

1. THE EASEMENT FOR EMERGENCY ACCESS PURPOSES OVER ALL OF
LOTS BA THROUGH BC AS DEDICATED.
2. THE EASEMENT FOR PUBLIC PEDESTRIAN PURPOSES
AS DEDICATED.

AND DID ALSO APPROVE SUBJECT MAP PURSUANT TO THE PROVISIONS OF
SECTION 66436(a)(3) OF THE SUBDIVISION MAP ACT.

DATED THIS 9th DAY OF November, 2004

Darlene J. Bloom
DARLENE J. BLOOM
CLERK OF THE BOARD OF SUPERVISORS

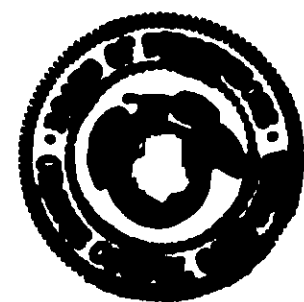

COUNTY TREASURER-TAX COLLECTOR'S CERTIFICATE

STATE OF CALIFORNIA)
COUNTY OF ORANGE) SS

I HEREBY CERTIFY THAT ACCORDING TO THE RECORDS OF MY OFFICE
THERE ARE NO LIENS AGAINST THE LAND COVERED BY THIS MAP OR
ANY PART THEREOF FOR UNPAID STATE, COUNTY, MUNICIPAL OR LOCAL
TAXES OR SPECIAL ASSESSMENTS COLLECTED AS TAXES, EXCEPT TAXES
OR SPECIAL ASSESSMENTS COLLECTED AS TAXES NOT YET PAYABLE.

AND DO CERTIFY TO THE RECORDER OF THE COUNTY OF ORANGE
THAT THE PROVISIONS OF THE SUBDIVISION MAP ACT HAVE BEEN COMPLIED
WITH REGARDING DEPOSITS TO SECURE PAYMENT OF TAXES OR SPECIAL
ASSESSMENTS COLLECTED AS TAXES ON THE LAND COVERED BY THIS MAP.

DATED THIS 27th DAY OF September, 2004.

John M.W. Moorlach
JOHN M.W. MOORLACH
COUNTY TREASURER-TAX COLLECTOR

BY: Mac Jorgensen
DEPUTY TREASURER -
TAX COLLECTOR

SHEET 2 OF 7 SHEETS
37 NUMBERED LOTS
13 LETTERED LOTS
25.212 ACRES
FINAL UNIT OF VESTING
T.T.M. 15989
DATE OF SURVEY:
JANUARY, 1999

TRACT MAP NO. 15989

IN THE UNINCORPORATED TERRITORY OF THE COUNTY OF ORANGE,
STATE OF CALIFORNIA

HALL & FOREMAN, INC.

STEVEN C. SHAMBECK, P.L.S. 6217
JUNE, 2004

SANTA MARGARITA WATER DISTRICT

STATE OF CALIFORNIA)
COUNTY OF ORANGE)

ON THIS 20th DAY OF August 2004, BEFORE ME, Kristen S. Collins
A NOTARY PUBLIC IN AND FOR SAID STATE, PERSONALLY APPEARED DANIEL R.
PERONS PERSONALLY KNOWN TO ME OR PROVED TO ME ON THE BASIS OF SATISFACTORY
EVIDENCE TO BE THE PERSON WHOSE NAME IS SUBSCRIBED TO THE WITHIN INSTRUMENT
AND ACKNOWLEDGED TO ME THAT HE EXECUTED THE SAME IN HIS AUTHORIZED CAPACITY,
AND THAT BY HIS SIGNATURE ON THE INSTRUMENT THE PERSON OR THE ENTITY UPON
BEHALF OF WHICH THE PERSON ACTED, EXECUTED THE INSTRUMENT.

WITNESS MY HAND:

MY COMMISSION EXPIRES January 20, 2008

Kristen S. Collins MY PRINCIPAL PLACE OF BUSINESS
NOTARY PUBLIC IN AND FOR SAID STATE IS IN Orange COUNTY

Kristen S. Collins
PRINT NAME

AUTOMATIC FIRE SPRINKLER NOTE:
ALL SINGLE FAMILY HOMES AND ALL MULTI FAMILY HOMES SHALL BE PROTECTED
WITH AUTOMATIC SPRINKLER SYSTEMS.

SPECIAL FIRE PROTECTION NOTE:
PROPERTY IS IN A SPECIAL FIRE PROTECTION AREA AND HAS RECIEVED A MODIFIED
EXCLUSION FROM OCFA PER EXCLUSION LETTER DATED AUGUST 24, 2001.

HIGH FIRE HAZARD AREA NOTE:
THE LOTS SHOWN ON THIS MAP ARE IN A HIGH FIRE HAZARD AREA DUE TO WILD
LAND EXPOSURE.

SIGNATURE OMISSIONS

PURSUANT TO THE PROVISIONS OF SECTION 66436 (a)(3)(A) AND (C) OF
THE SUBDIVISION MAP ACT, THE FOLLOWING SIGNATURES HAVE BEEN
OMITTED:

SOUTHERN CALIFORNIA EDISON COMPANY HOLDER OF AN EASEMENT FOR PUBLIC
UTILITIES AND INCIDENTAL PURPOSES PER DOCUMENT RECORDED APRIL 16, 1965
IN BOOK 7485 PAGE 714 OF OFFICIAL RECORDS.

LADERA DEVELOPMENT COMPANY, L.L.C., HOLDER OF OIL, GAS, AND MINERAL
RIGHTS PER DEED RECORDED DECEMBER 10, 1996 AS INSTRUMENT NO.
19960424029 OF OFFICIAL RECORDS.

BASIS OF BEARINGS

THE BEARINGS SHOWN HEREON ARE BASED ON THE BEARING BETWEEN
O.C.S. HORIZONTAL CONTROL STATION GPS NO. 1417 AND STATION
GPS NO. 1448, BEING NORTH 10°48'13" EAST PER RECORDS ON FILE
IN THE OFFICE OF THE ORANGE COUNTY SURVEYOR.

DATUM STATEMENT

COORDINATES SHOWN ARE BASED ON THE CALIFORNIA COORDINATE
SYSTEM (CCS 83), ZONE VI, 1983 NAD (1991.35 EPOCH OCS GPS
ADJUSTMENT). ALL DISTANCES ARE GROUND DISTANCES UNLESS
OTHERWISE NOTED. TO OBTAIN GRID DISTANCE MULTIPLY GROUND
DISTANCE BY 0.999948295. THIS FACTOR IS PROJECT-SPECIFIC.

NOTES:

"THE PRIVATE STREETS CONSTRUCTED WITHIN
THIS MAP SHALL BE OWNED, OPERATED AND MAINTAINED
BY THE DEVELOPER, SUCCESSORS OR ASSIGNS. THE
COUNTY OF ORANGE SHALL HAVE NO RESPONSIBILITY THEREFORE
UNLESS PURSUANT TO APPROPRIATE SECTIONS OF THE
STREETS AND HIGHWAYS CODE OF THE STATE OF CALIFORNIA.
THE SAID PRIVATE STREETS HAVE BEEN ACCEPTED INTO
THE COUNTY ROAD SYSTEM BY APPROPRIATE RESOLUTION OF
THE ORANGE COUNTY BOARD OF SUPERVISORS."

EASEMENT NOTES

- ☐ INDICATES SOUTHERN CALIFORNIA EDISON EASEMENT FOR PUBLIC
UTILITIES AND INCIDENTAL PURPOSES PER DOCUMENT RECORDED
APRIL 16, 1965 IN BOOK 7485 PAGE 714 OF OFFICIAL RECORDS
- ☐ INDICATES WATER, RECYCLED WATER, SEWER & ACCESS
EASEMENT DEDICATED TO SANTA MARGARITA WATER DISTRICT
- ☐ INDICATES PUBLIC PEDESTRIAN EASEMENT AS
DEDICATED TO THE COUNTY OF ORANGE.

MONUMENT NOTES

- INDICATES FOUND MONUMENT AS NOTED.
- ☐ INDICATES FOUND 2" IRON PIPE W/1-3/4" OCS BRASS CAP STAMPED "GPS
1448 9-95" PER TRACT NO. 16203, M.M. 826/8-20 AND RECORDS ON FILE
IN THE ORANGE COUNTY SURVEYORS OFFICE.
N2146790.819, E6142602.585
- ☐ INDICATES FOUND 2 1/2" IRON PIPE W/2" OCS BRASS CAP STAMPED "GPS
1417 9-95" PER TRACT NO. 16203, M.M. 826/8-20 AND RECORDS ON FILE
IN THE ORANGE COUNTY SURVEYORS OFFICE.
N2141450.558, E6141583.535
- INDICATES 2" I.P. TAGGED L.S. 6217 OR SPIKE & WASHER STAMPED L.S.
6217 OR LEAD, TACK & TAG L.S. 6217 TO BE SET PER TRACT NO. 15990
M.M. 862/ 34-41, UNLESS OTHERWISE NOTED.
- INDICATES 2" I.P. TAGGED L.S. 6217 OR SPIKE & WASHER STAMPED L.S.
6217 OR LEAD, TACK & TAG L.S. 6217 TO BE SET PER TRACT NO. 16586
M.M. 858/29-44, UNLESS OTHERWISE NOTED.
- △ 2" I.P. TAGGED P.L.S. 5557 OR SPIKE & WASHER STAMPED P.L.S. 5557
OR LEAD, TACK & TAG P.L.S. 5557 TO BE SET PER TRACT NO. 15986
M.M. 849/1-15, UNLESS OTHERWISE NOTED.
- 2" I.P. TAGGED L.S. 6217 OR SPIKE & WASHER STAMPED L.S. 6217
OR LEAD, TACK & TAG L.S. 6217 TO BE SET AT ALL TRACT BOUNDARY
CORNERS WITHIN 90 DAYS AFTER ACCEPTANCE OF IMPROVEMENTS.
- 1" I.P. TAGGED L.S. 6217 OR SPIKE & WASHER STAMPED L.S. 6217 OR
LEAD, TACK & TAG L.S. 6217 TO BE SET AT LOT CORNERS WITHIN 90 DAYS
AFTER ACCEPTANCE OF IMPROVEMENTS.
- 1" I.P. TAGGED L.S. 6217 OR SPIKE & WASHER STAMPED L.S. 6217 OR
LEAD, TACK & TAG L.S. 6217 TO BE SET AT ALL CENTERLINE INTERSECTIONS,
E.C.'S AND B.C.'S WITHIN 90 DAYS AFTER ACCEPTANCE OF IMPROVEMENTS.

NOTES

LOTS BA THROUGH BC ARE FOR PRIVATE STREET PURPOSES AND ARE NOT
SEPARATE BUILDING SITES.

LOT A IS NOT A SEPARATE BUILDING SITE.

LOTS B THROUGH J ARE FOR LANDSCAPE/OPEN SPACE PURPOSES AND
ARE NOT SEPARATE BUILDING SITES.

LOTS 36 THROUGH 37 ARE NOT RESIDENTIAL BUILDING SITES, BUT ARE
PRIVATE RECREATION SITES

{ } INDICATES MEASURED AND RECORD PER TRACT NO. 15990 M.M. 862/ 34-41

() INDICATES MEASURED AND RECORD PER TRACT NO. 16586 M.M. 858/29-44.

[] INDICATES MEASURED AND RECORD PER TRACT NO. 15986 M.M. 819/1-15.

863 10

SHEET 3 OF 7 SHEETS
37 NUMBERED LOTS
13 LETTERED LOTS
25.212 ACRES
FINAL PORTION OF
VESTING T.T.M. 15989
DATE OF SURVEY:
JANUARY, 1999

TRACT MAP NO. 15989

IN THE UNINCORPORATED TERRITORY OF THE COUNTY OF ORANGE,
STATE OF CALIFORNIA

HALL & FOREMAN, INC.


STEVEN C. SHAMBECK, P.L.S. 6217

JUNE, 2004

BOUNDARY AND INDEX SHEET

TRACT NO. 15986

M.M. 849/1-15

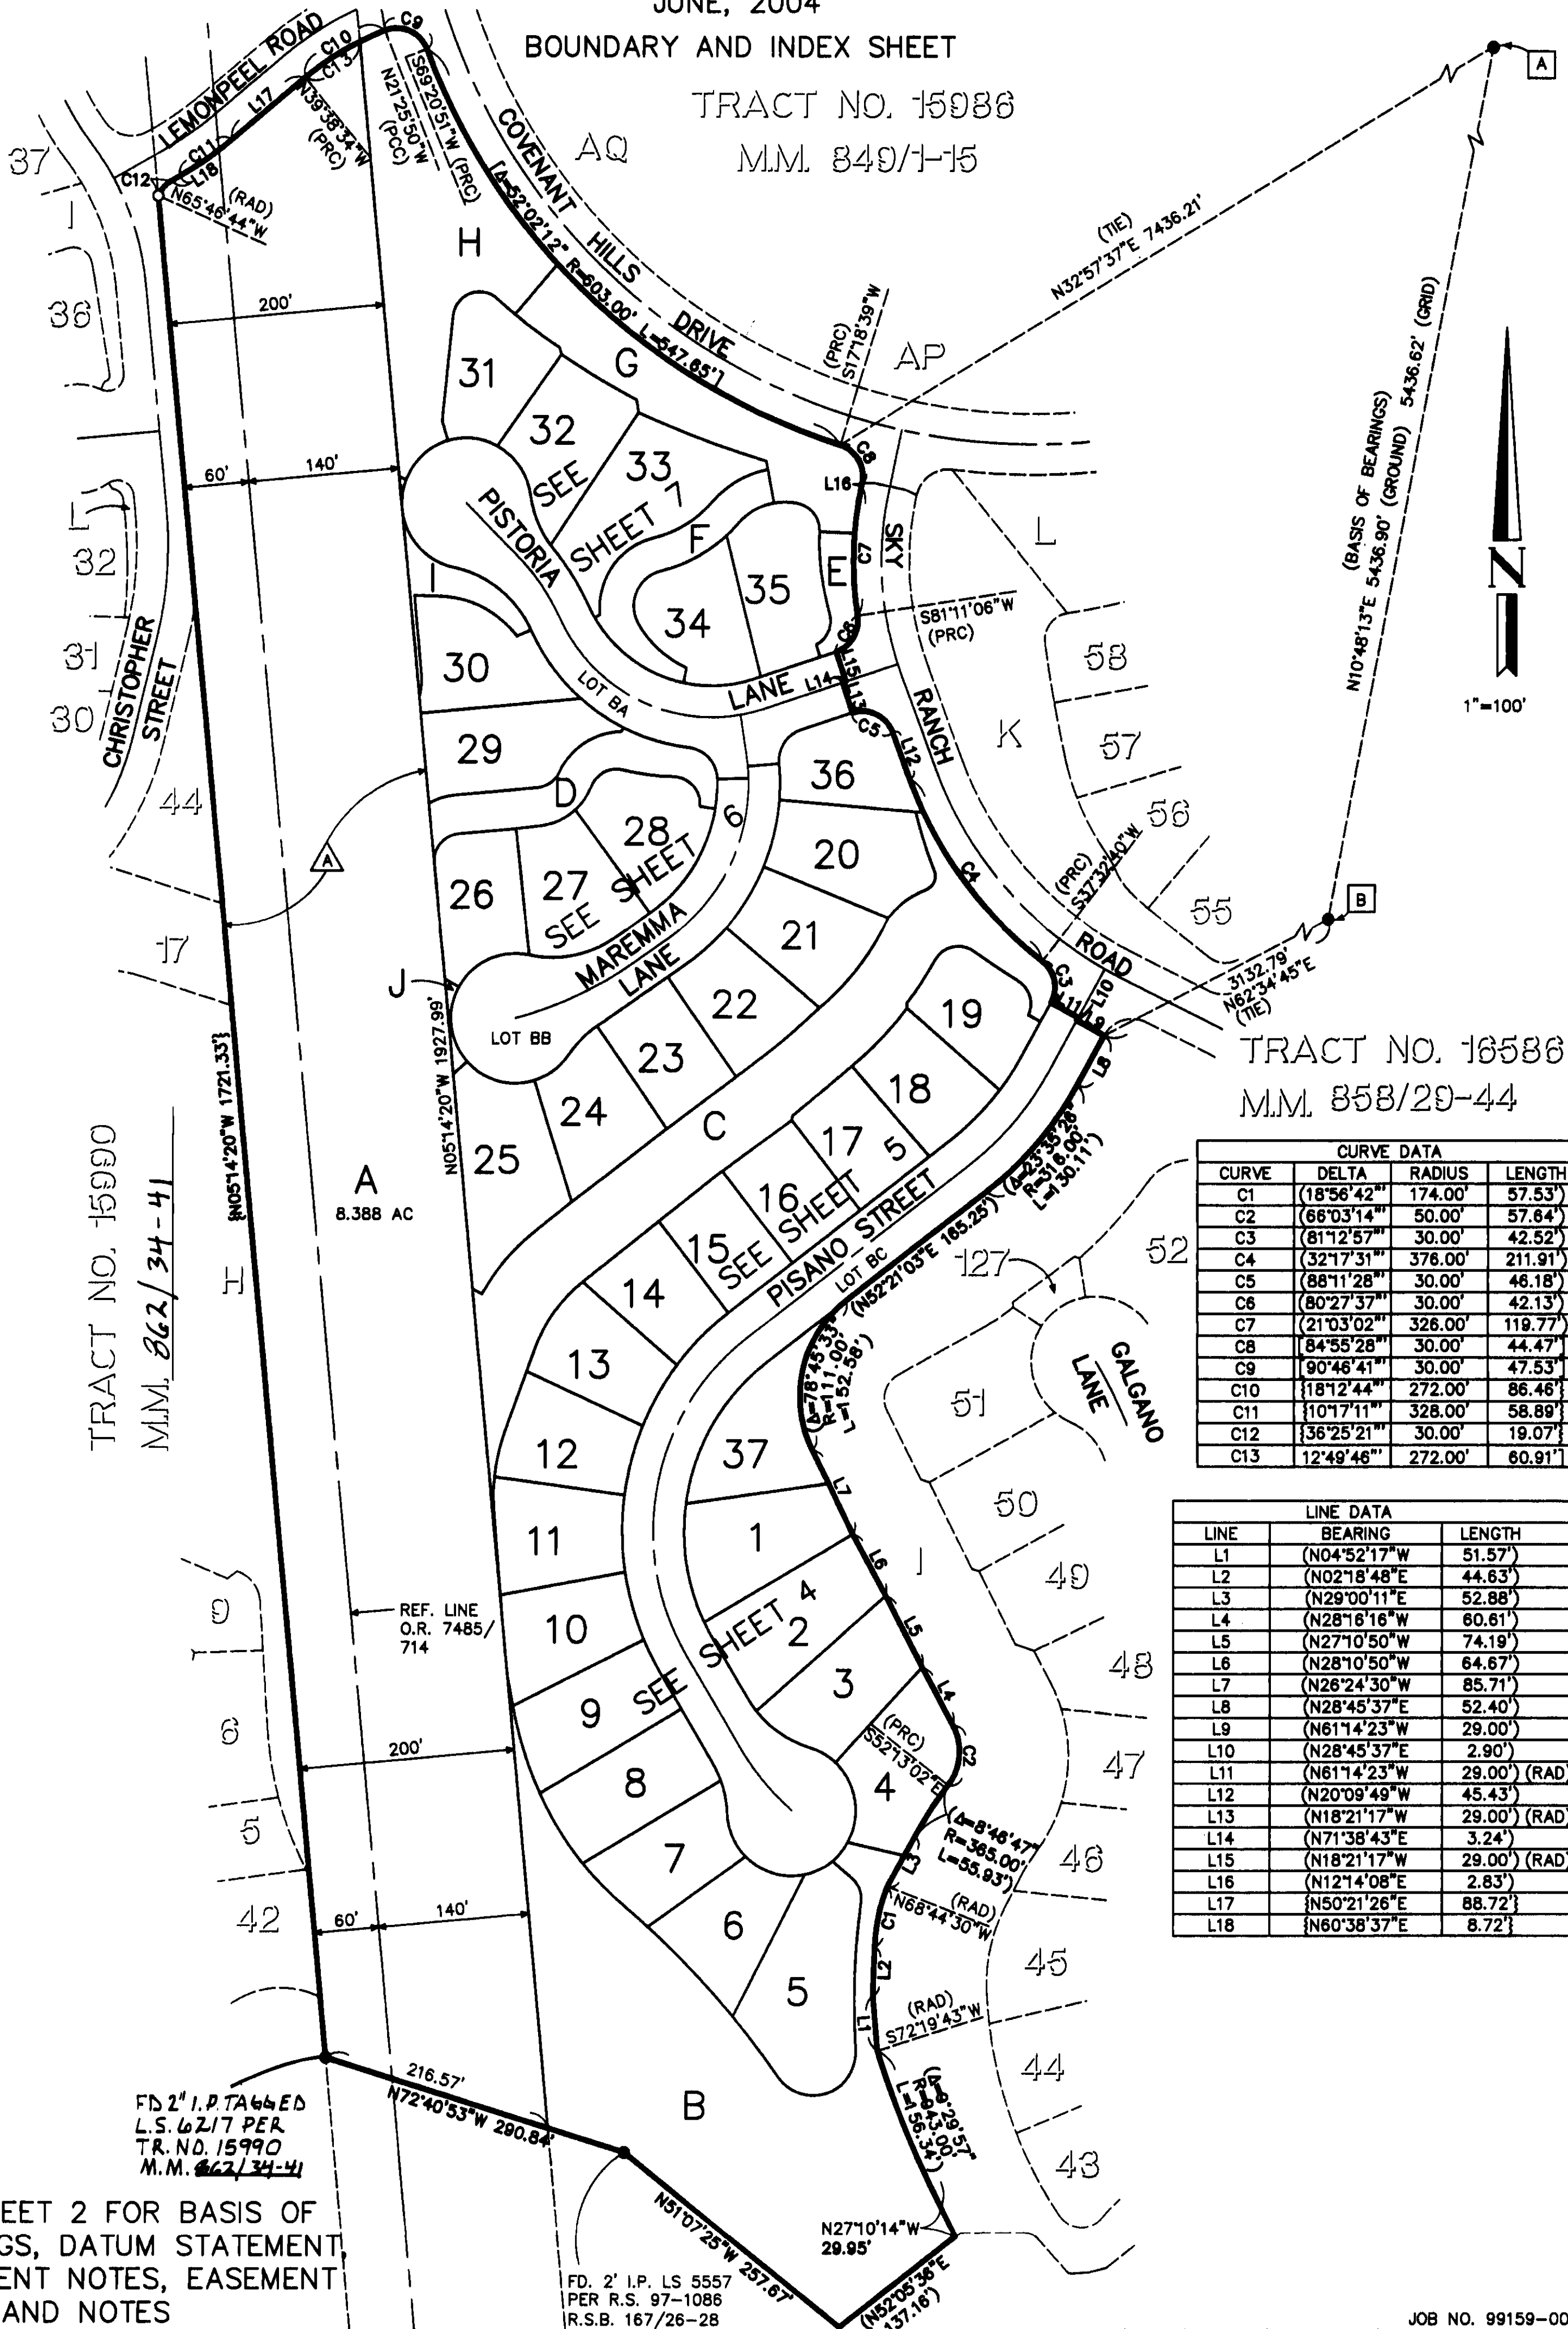

CURVE DATA			
CURVE	DELTA	RADIUS	LENGTH
C1	(18°56'42")	174.00'	57.53'
C2	(66°03'14")	50.00'	57.64'
C3	(81°12'57")	30.00'	42.52'
C4	(32°17'31")	376.00'	211.91'
C5	(88°11'28")	30.00'	48.18'
C6	(80°27'37")	30.00'	42.13'
C7	(21°03'02")	326.00'	119.77'
C8	(84°55'28")	30.00'	44.47'
C9	(90°46'41")	30.00'	47.53'
C10	(18°12'44")	272.00'	86.46'
C11	(10°17'11")	328.00'	58.89'
C12	(36°25'21")	30.00'	19.07'
C13	(12°49'46")	272.00'	60.91'

LINE DATA		
LINE	BEARING	LENGTH
L1	(N04°52'17"W	51.57'
L2	(N02°18'48"E	44.63'
L3	(N29°00'11"E	52.88'
L4	(N28°16'16"W	60.61'
L5	(N27°10'50"W	74.19'
L6	(N28°10'50"W	64.67'
L7	(N26°24'30"W	85.71'
L8	(N28°45'37"E	52.40'
L9	(N61°14'23"W	29.00'
L10	(N28°45'37"E	2.90'
L11	(N61°14'23"W	29.00' (RAD)
L12	(N20°09'49"W	45.43'
L13	(N18°21'17"W	29.00' (RAD)
L14	(N71°38'43"E	3.24'
L15	(N18°21'17"W	29.00' (RAD)
L16	(N12°14'08"E	2.83'
L17	(N50°21'26"E	88.72'
L18	(N60°38'37"E	8.72'

863 10

863 11

SHEET 4 OF 7 SHEETS
37 NUMBERED LOTS
13 LETTERED LOTS
25.212 ACRES
FINAL PORTION OF
VESTING T.T.M. 15989
DATE OF SURVEY:
JANUARY, 1999

TRACT MAP NO. 15989

IN THE UNINCORPORATED TERRITORY OF THE COUNTY OF ORANGE,
STATE OF CALIFORNIA


HALL & FOREMAN, INC.

STEVEN C. SHAMBECK, P.L.S. 6217
JUNE, 2004

SEE SHEET 2 FOR BASIS OF
BEARINGS, DATUM STATEMENT,
MONUMENT NOTES, EASEMENT
NOTES AND NOTES

SEE SHEET 5

TRACT NO.

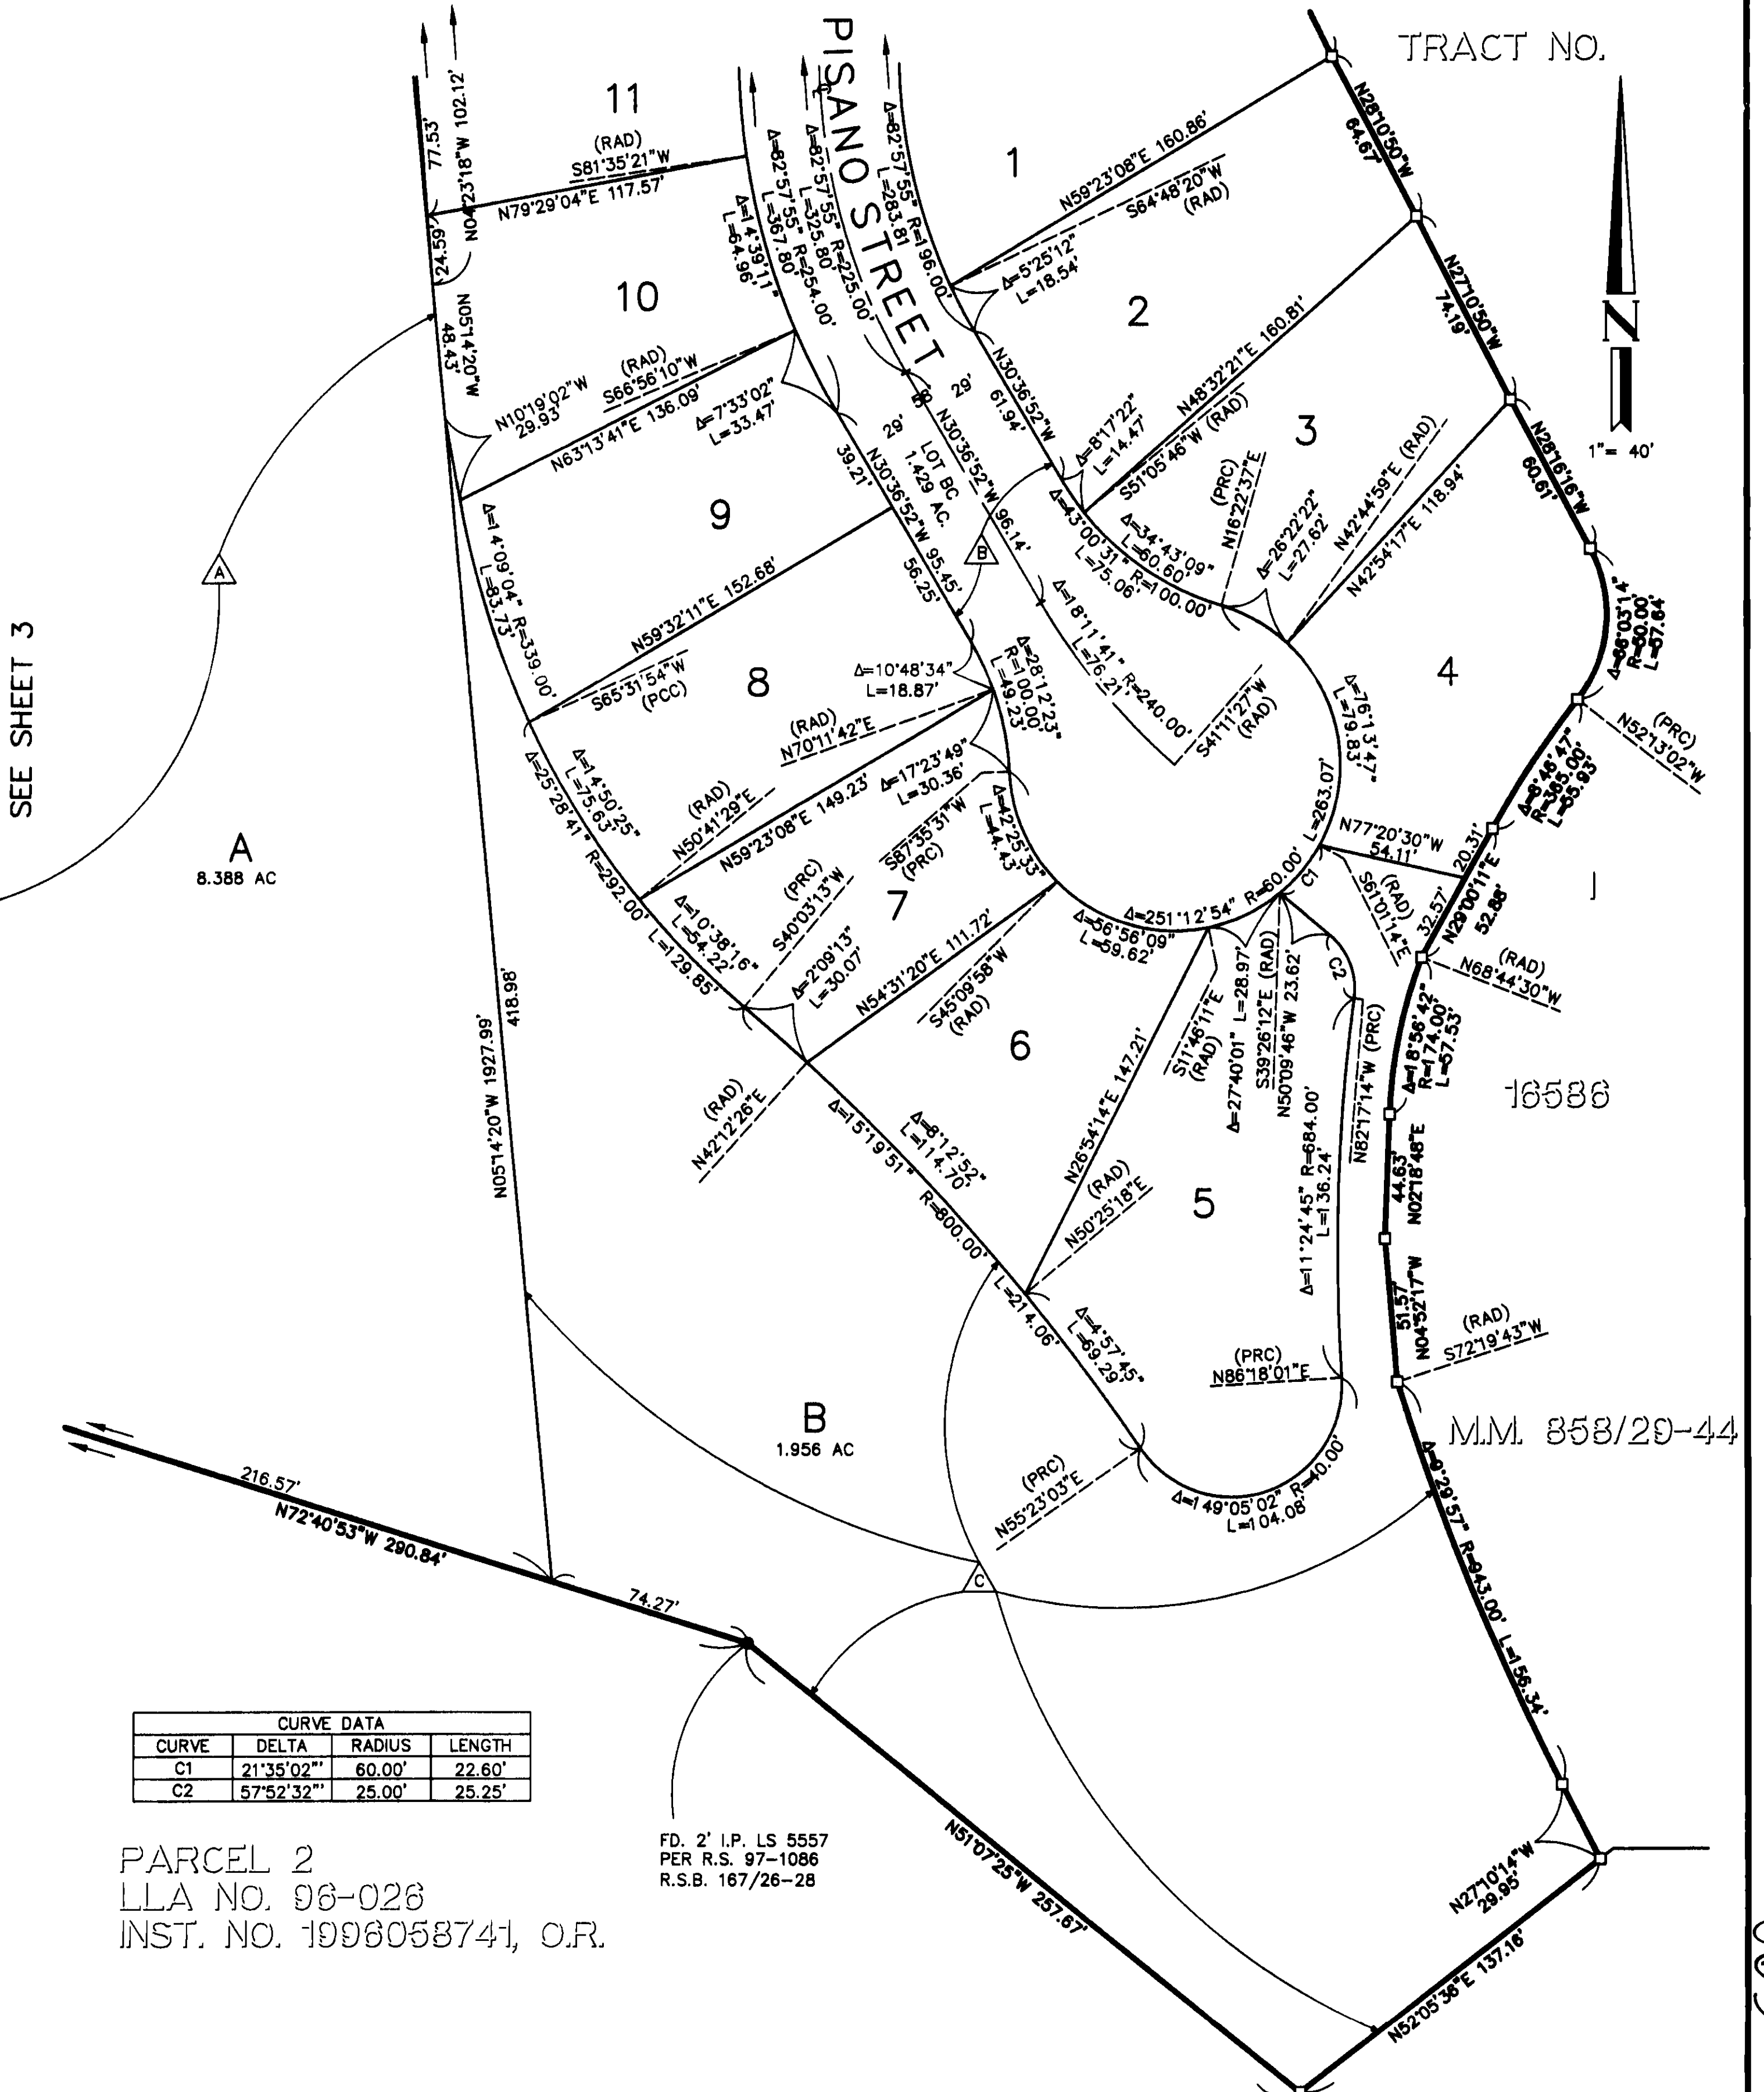

CURVE DATA			
CURVE	DELTA	RADIUS	LENGTH
C1	21°35'02"	60.00'	22.60'
C2	57°52'32"	25.00'	25.25'

PARCEL 2
LLA NO. 96-026
INST. NO. 1996058741, O.R.

FD. 2' I.P. LS 5557
PER R.S. 97-1086
R.S.B. 167/26-28

863 11

863 12

SHEET 5 OF 7 SHEETS
37 NUMBERED LOTS
13 LETTERED LOTS
25.212 ACRES
FINAL PORTION OF
VESTING T.T.M. 15989
DATE OF SURVEY:
JANUARY, 1999

TRACT MAP NO. 15989

IN THE UNINCORPORATED TERRITORY OF THE COUNTY OF ORANGE,
STATE OF CALIFORNIA

HALL & FOREMAN, INC.

STEVEN C. SHAMBECK, P.L.S. 6217
JUNE, 2004


SEE SHEET 2 FOR BASIS OF
BEARINGS, DATUM STATEMENT,
MONUMENT NOTES, EASEMENT
NOTES AND NOTES

SEE SHEET 6



LINE DATA		
LINE	BEARING	LENGTH
L1	N28°45'37"E	2.90'
L2	N61°14'23"W	29.00' (RAD)
L3	N61°14'23"W	29.00'

CURVE DATA			
CURVE	DELTA	RADIUS	LENGTH
C1	82°54'35"	25.00'	36.18'
C2	24°22'53"	173.00'	73.62'

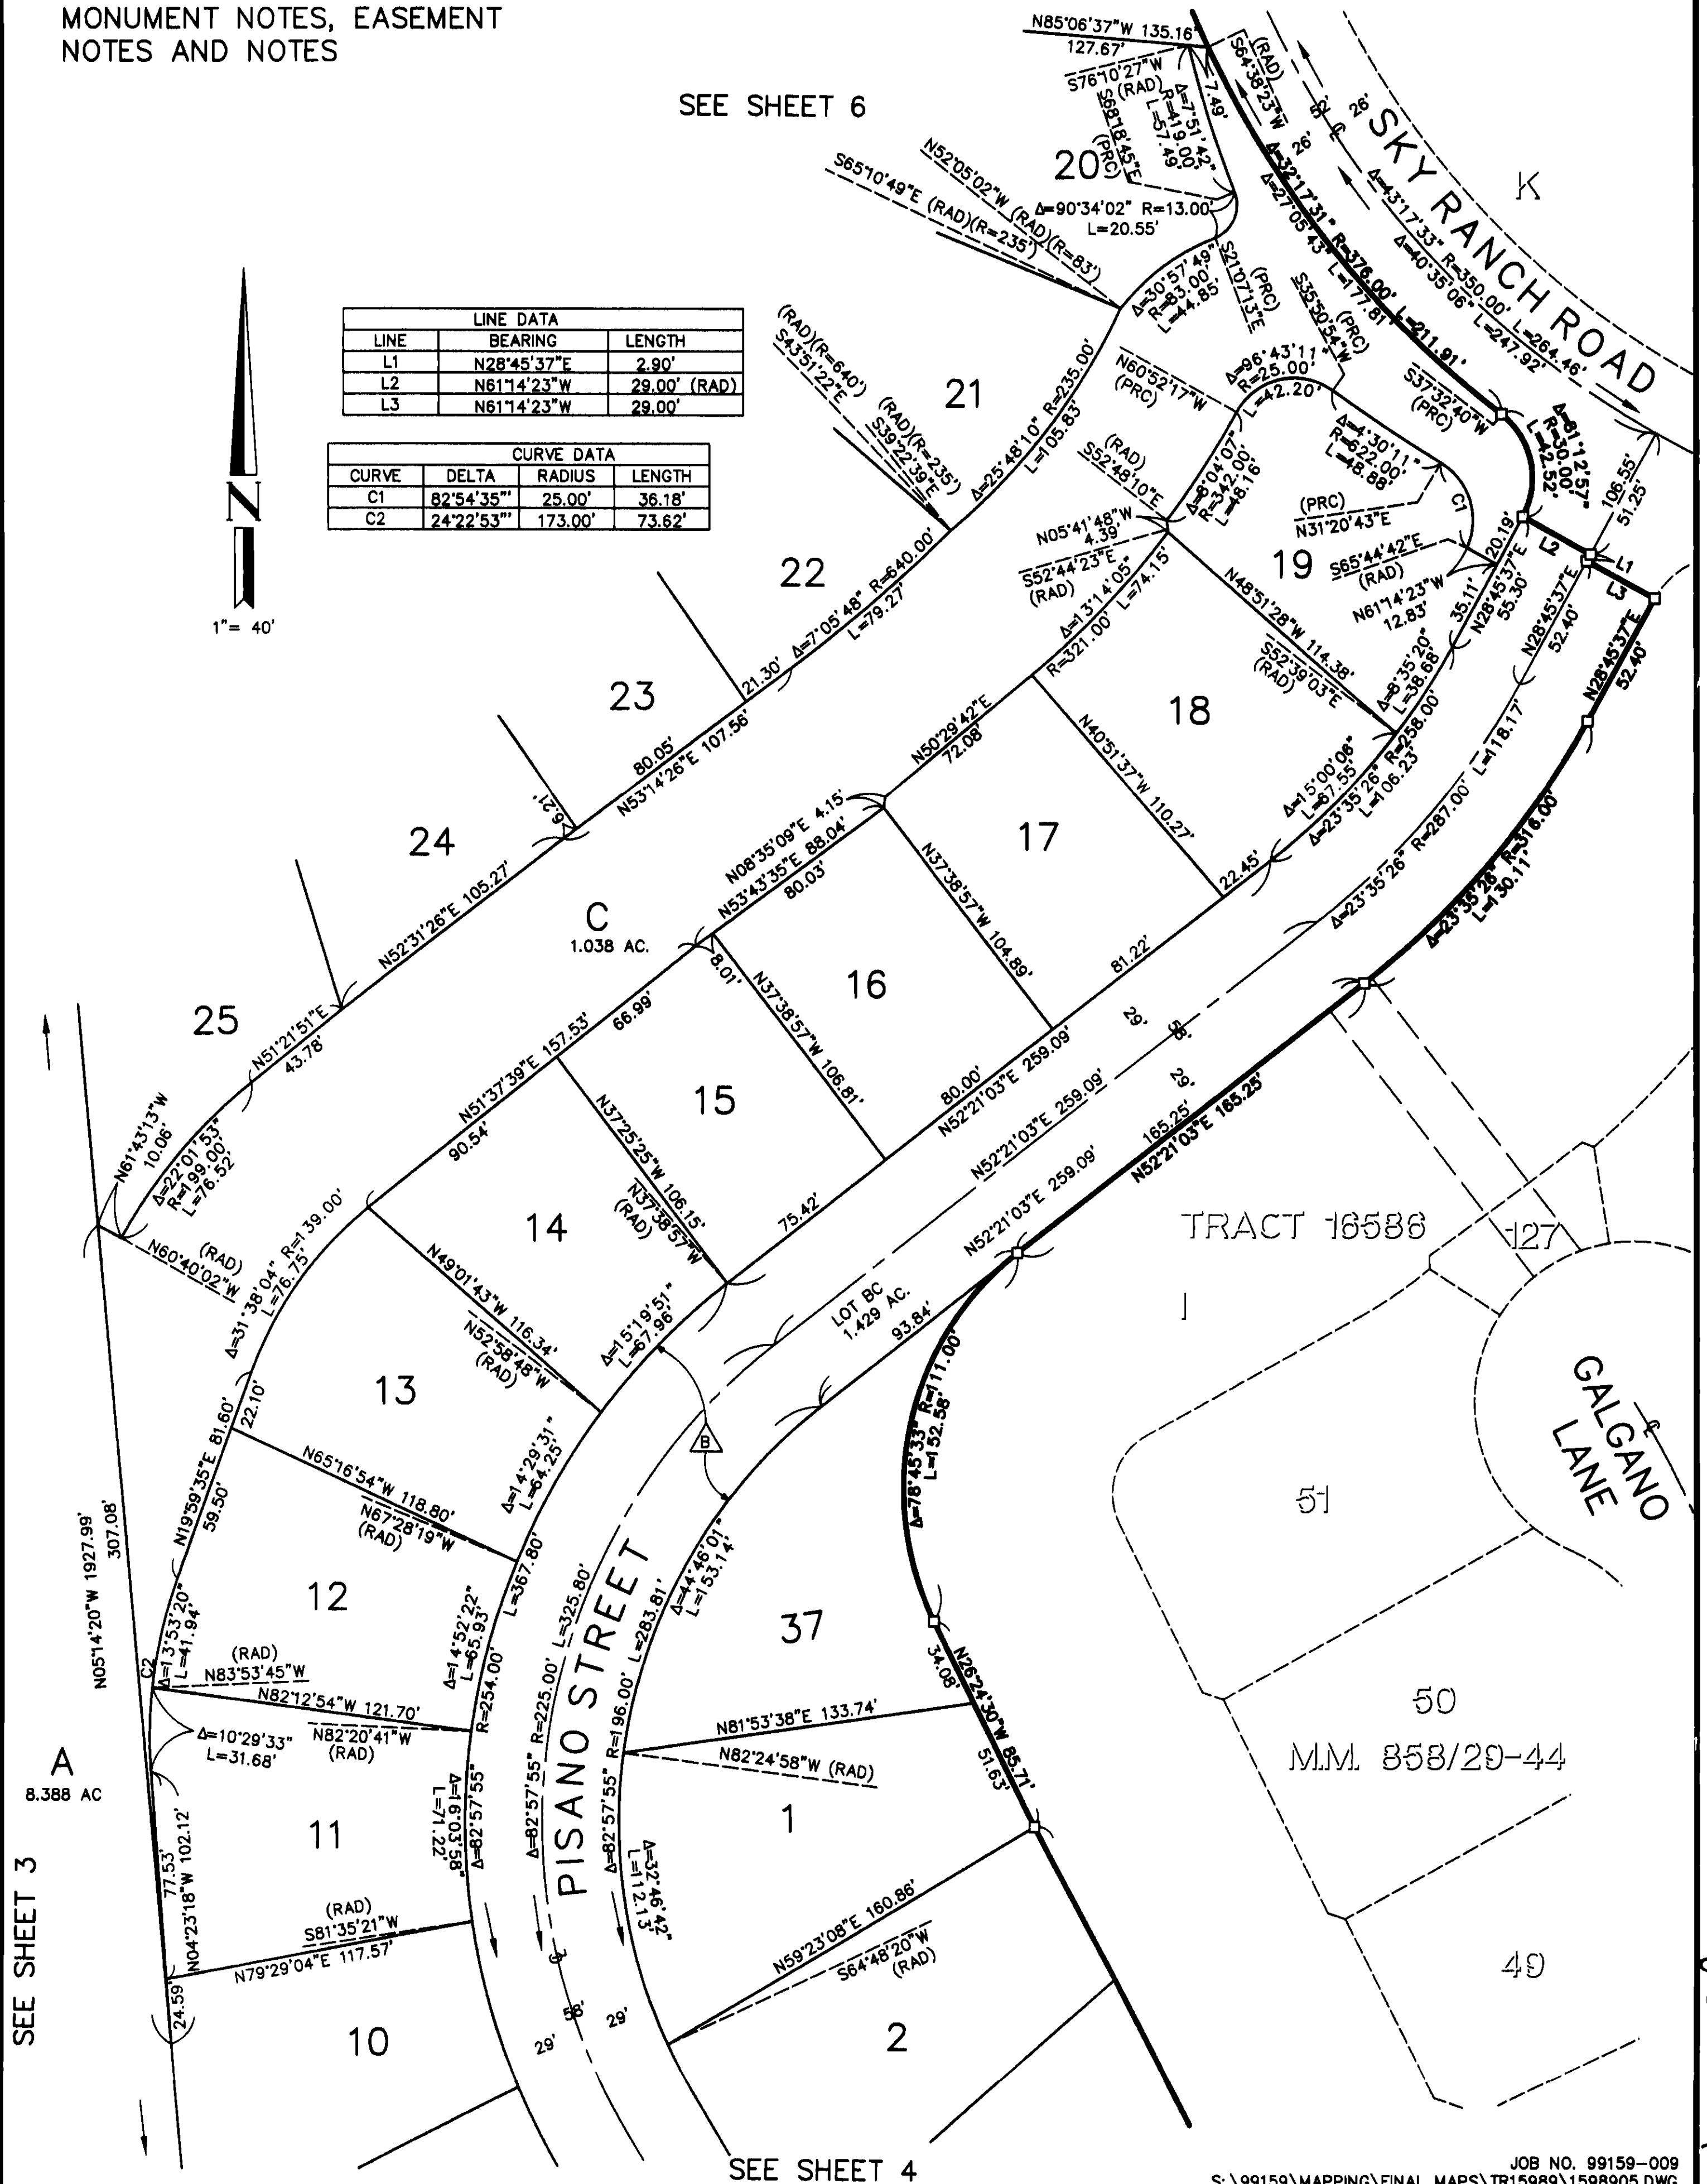

SEE SHEET 3

SEE SHEET 4

863 12

863 14

SHEET 7 OF 7 SHEETS
37 NUMBERED LOTS
13 LETTERED LOTS
25.212 ACRES
FINAL PORTION OF
VESTING T.T.M. 15989
DATE OF SURVEY:
JANUARY, 1999

TRACT MAP NO. 15989


IN THE UNINCORPORATED TERRITORY OF THE COUNTY OF ORANGE,
STATE OF CALIFORNIA

HALL & FOREMAN, INC.

STEVEN C. SHAMBECK, P.L.S. 6217

JULY, 2003

SEE SHEET 2 FOR BASIS OF
BEARINGS, DATUM STATEMENT,
MONUMENT NOTES, EASEMENT
NOTES AND NOTES

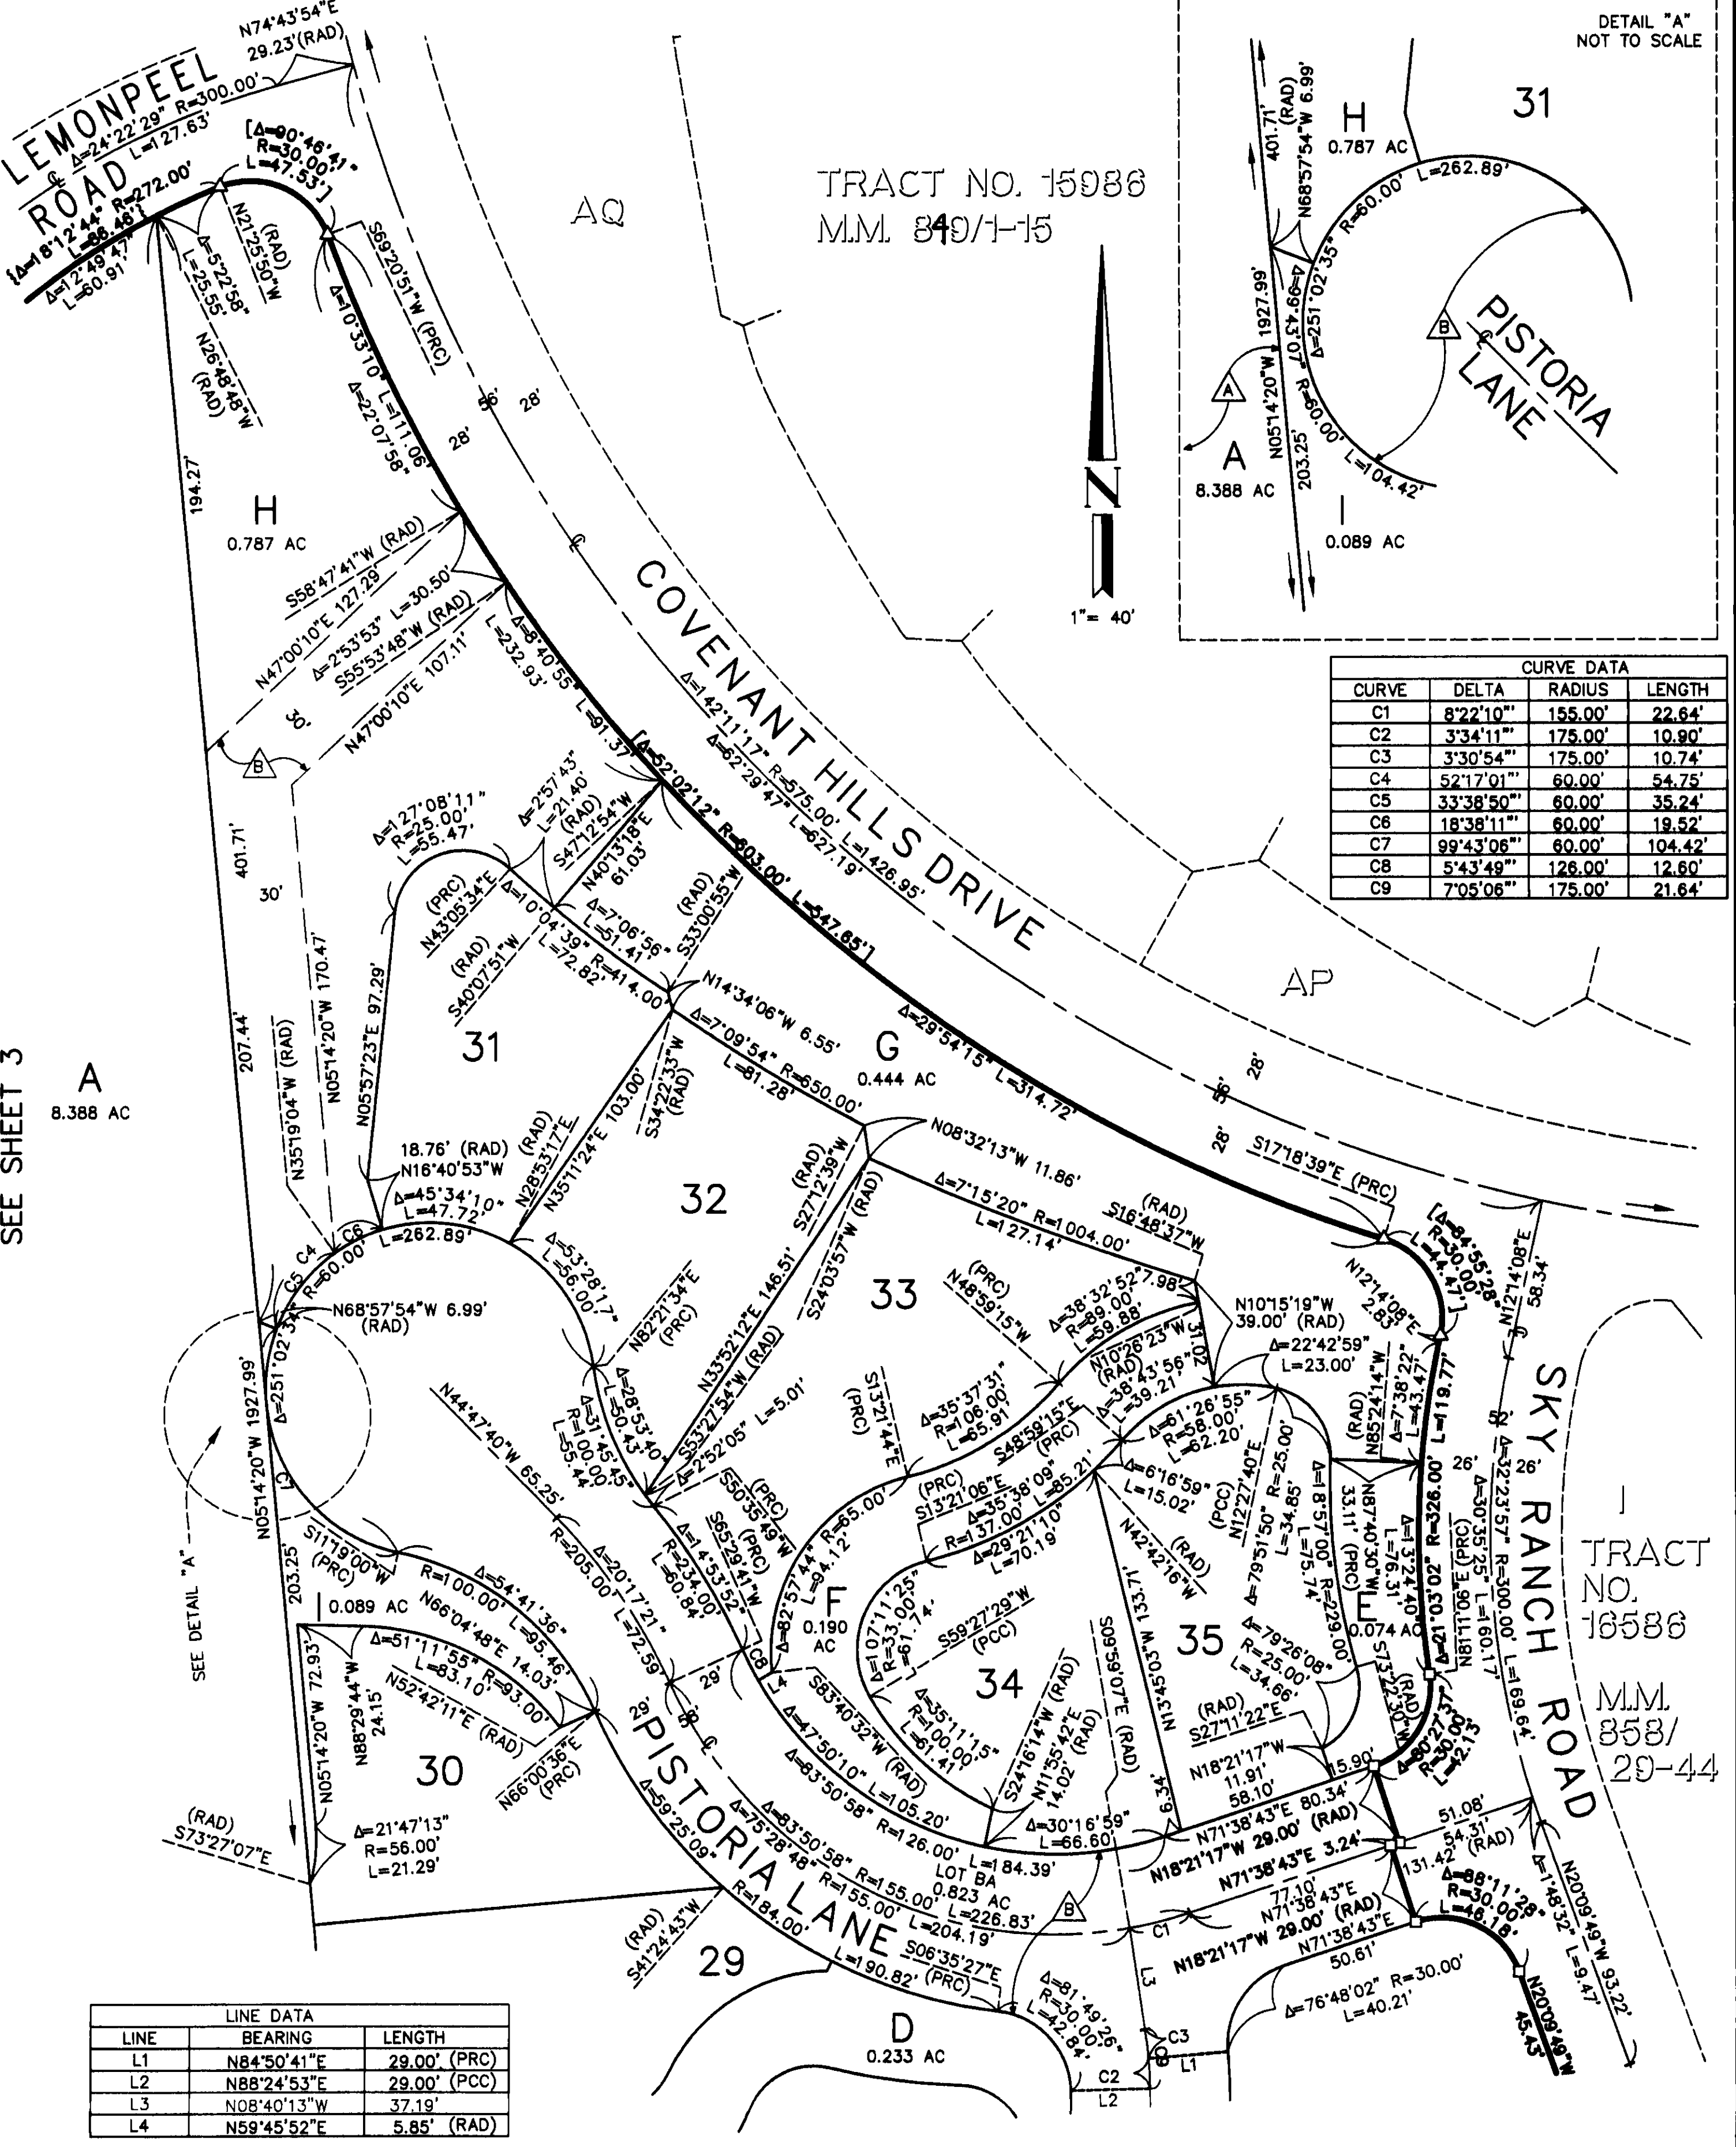

SEE SHEET 3

LINE DATA		
LINE	BEARING	LENGTH
L1	N84°50'41"E	29.00' (PRC)
L2	N88°24'53"E	29.00' (PCC)
L3	N08°40'13"W	37.19'
L4	N59°45'52"E	5.85' (RAD)

CURVE DATA			
CURVE	DELTA	RADIUS	LENGTH
C1	8°22'10"	155.00'	22.64'
C2	3°34'11"	175.00'	10.90'
C3	3°30'54"	175.00'	10.74'
C4	52°17'01"	60.00'	54.75'
C5	33°38'50"	60.00'	35.24'
C6	18°38'11"	60.00'	19.52'
C7	99°43'06"	60.00'	104.42'
C8	5°43'49"	128.00'	12.60'
C9	7°05'06"	175.00'	21.64'

TRACT
NO. 16586
M.M. 858/
20-44

SEE SHEET 6

863 14