

SHEET 1 OF 8 SHEETS
44 NUMBERED LOTS
16 LETTERED LOTS
21.336 ACRES
FINAL UNIT OF VESTING
T.T.M. 15990
DATE OF SURVEY:
JANUARY, 1999

TRACT MAP NO. 15990

IN THE UNINCORPORATED TERRITORY OF THE COUNTY OF ORANGE,
STATE OF CALIFORNIA

BEING A SUBDIVISION OF A PORTION OF PARCEL 1 OF LOT LINE ADJUSTMENT NO.
LL 96-026, IN THE UNINCORPORATED TERRITORY OF THE COUNTY OF ORANGE,
STATE OF CALIFORNIA, AS SHOWN ON EXHIBIT "B" ATTACHED TO THAT CERTAIN
DOCUMENT RECORDED NOVEMBER 21, 1996 AS INSTRUMENT NO. 19960587414 OF
OFFICIAL RECORDS, IN THE OFFICE OF THE COUNTY RECORDER OF SAID COUNTY.

HALL & FOREMAN, INC.

STEVEN C. SHAMBECK, P.L.S. 6217

MAY, 2004

ACCEPTED AND FILED AT THE
REQUEST OF

FIRST AMERICAN TITLE INSURANCE COMPANY

DATE October 28, 2004

TIME 3:18 PM FEE \$ 281.00

INSTRUMENT # 2004000974704

BOOK 862 PAGE 34-41 mm

TOM DALY
COUNTY CLERK-RECORDER

BY Sammy G. Demulder
DEPUTY

OWNERSHIP CERTIFICATE

WE, THE UNDERSIGNED, BEING ALL PARTIES HAVING ANY RECORD TITLE INTEREST
IN THE LAND COVERED BY THIS MAP, DO HEREBY CONSENT TO THE PREPARATION
AND RECORDATION OF SAID MAP, AS SHOWN WITHIN THE DISTINCTIVE BORDER
LINE.

WE ALSO HEREBY DEDICATE TO THE COUNTY OF ORANGE:

1. AN EASEMENT FOR EMERGENCY ACCESS PURPOSES OVER ALL OF LOTS BA THROUGH BD
2. THE EASEMENT FOR EMERGENCY ACCESS PURPOSES AS SHOWN ON SAID MAP
3. THE EASEMENT FOR PUBLIC PEDESTRIAN PURPOSES AS SHOWN ON SAID MAP.

WE ALSO HEREBY DEDICATE TO THE SANTA MARGARITA WATER DISTRICT THE EASEMENTS
FOR WATER, RECYCLED WATER, SEWER, DRAINAGE, AND ACCESS PURPOSES OVER THOSE
EASEMENT AREAS AS SHOWN ON SAID MAP WHICH EASEMENTS SHALL BE SUBJECT TO THE
SAME CONDITIONS AS ARE SHOWN IN THAT CERTAIN GRANT OF EASEMENT TO SANTA
MARGARITA WATER DISTRICT RECORDED SEPTEMBER 18, 2002 AS INSTRUMENT NO.
20020799401, OF OFFICIAL RECORDS, COUNTY OF ORANGE.

DMB LADERA, L.L.C., A DELAWARE LIMITED LIABILITY COMPANY

BY: RANCHO MISSION VIEJO, L.L.C. A DELAWARE LIMITED LIABILITY COMPANY,
IT'S AUTHORIZED AGENT OR MANAGER.

BY: Paul Johnson BY: Gregory S. Edwards
PRINT NAME: PAUL JOHNSON PRINT NAME: GREGORY S. EDWARDS
PRINT TITLE: SVP - COMM. MGMT. PRINT TITLE: SVP - CEO

NOTARY ACKNOWLEDGEMENT

STATE OF CALIFORNIA)
COUNTY OF ORANGE) SS

ON August 2, 2004 BEFORE ME, LINDA K. LEDGER
Notary Public
PERSONALLY APPEARED PAUL JOHNSON and GREGORY S. EDWARDS
PERSONALLY KNOWN TO ME (OR PROVED TO ME ON THE BASIS OF SATISFACTORY
EVIDENCE) TO BE THE PERSON(S) WHOSE NAME(S) IS/ARE SUBSCRIBED TO THE
WITHIN INSTRUMENT AND ACKNOWLEDGED TO ME THAT HE/SHE/THEY EXECUTED
THE SAME IN HIS/HER/THEIR AUTHORIZED CAPACITIES, AND THAT BY HIS/
HER/THEIR SIGNATURE(S) ON THE INSTRUMENT THE PERSON(S), OR THE ENTITY UPON
BEHALF OF WHICH THE PERSON(S) ACTED, EXECUTED THE INSTRUMENT.

WITNESS MY HAND:

Linda K. Ledger
NOTARY PUBLIC IN AND FOR SAID STATE

LINDA K. LEDGER
PRINT NAME

MY PRINCIPAL PLACE OF BUSINESS IS IN ORANGE COUNTY
MY COMMISSION EXPIRES 03/07/07

CERTIFICATE OF ACCEPTANCE

THE UNDERSIGNED, BEING THE DULY APPOINTED AGENT OF THE SANTA MARGARITA
WATER DISTRICT, A PUBLIC CORPORATION OF ORANGE COUNTY, CALIFORNIA, PURSUANT
TO ITS RESOLUTION NO. 88-10-02, DOES HEREBY ACCEPT ON BEHALF OF SAID
DISTRICT THE EASEMENTS FOR, WATER, RECYCLED WATER, SEWER, AND ACCESS
PURPOSES, AS DEDICATED AND AS SHOWN ON THIS TRACT MAP, BY AND BETWEEN
THE SANTA MARGARITA WATER DISTRICT AND DMB LADERA, L.L.C., AND DOES HEREBY
CERTIFY THAT THE GRANTEE CONSENTS TO THE RECORDATION OF SAID TRACT.

Daniel R. Feron
DANIEL R. FERONS, CHIEF ENGINEER
SANTA MARGARITA WATER DISTRICT

SURVEYOR'S STATEMENT

THIS MAP WAS PREPARED BY ME OR UNDER MY DIRECTION AND IS BASED UPON A
FIELD SURVEY IN CONFORMANCE WITH THE REQUIREMENTS OF THE SUBDIVISION MAP
ACT AND LOCAL ORDINANCE AT THE REQUEST OF DMB LADERA, LLC IN JANUARY,
1999. I HEREBY STATE THAT ALL MONUMENTS ARE OF THE CHARACTER AND
OCCUPY THE POSITIONS INDICATED, OR THAT THEY WILL BE SET IN SUCH
POSITIONS; AND THAT SAID MONUMENTS ARE SUFFICIENT TO ENABLE THE SURVEY
TO BE RETRACED. I HEREBY STATE THAT THIS FINAL MAP SUBSTANTIALLY
CONFORMS TO THE CONDITIONALLY APPROVED TENTATIVE MAP.

Steven C. Shambeck
STEVEN C. SHAMBECK, P.L.S. 6217
LICENSE EXPIRES: 3/31/06

7-28-2004
DATE




COUNTY SURVEYOR'S STATEMENT

I HEREBY STATE THAT I HAVE EXAMINED THIS MAP AND HAVE FOUND IT TO BE
SUBSTANTIALLY IN CONFORMANCE WITH THE TENTATIVE MAP AS FILED WITH,
AMENDED AND APPROVED BY THE ORANGE COUNTY SUBDIVISION COMMITTEE; THAT
ALL PROVISIONS OF THE SUBDIVISION MAP ACT AND COUNTY SUBDIVISION
REGULATIONS HAVE BEEN COMPLIED WITH AND I AM SATISFIED SAID MAP IS
TECHNICALLY CORRECT.

DATED THIS 1st DAY OF OCTOBER, 2004.

Michael K. Sullivan
RAYMOND L. MATHE, COUNTY SURVEYOR
L.S. 6185 EXPIRATION DATE: 3-31-06
BY: MICHAEL K. SULLIVAN, DEPUTY
LS 6254 EXPIRES 4/30/06

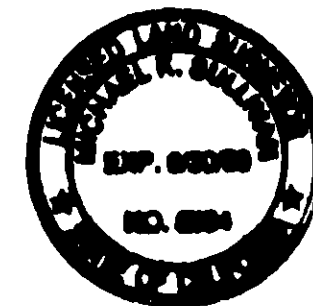

CLERK OF THE BOARD OF SUPERVISOR'S CERTIFICATE

STATE OF CALIFORNIA)
COUNTY OF ORANGE) SS

I HEREBY CERTIFY THAT THIS MAP WAS PRESENTED FOR APPROVAL TO THE
BOARD OF SUPERVISORS OF ORANGE COUNTY AT A REGULAR MEETING THEREOF
HELD ON THE 26th DAY OF October, 2004 AND THAT
THEREUPON SAID BOARD DID, BY AN ORDER DULY PASSED AND ENTERED,
APPROVE SAID MAP.

AND DID ALSO ACCEPT ON BEHALF OF THE COUNTY OF ORANGE:

1. THE EASEMENT FOR EMERGENCY ACCESS PURPOSES OVER ALL OF LOTS BA THROUGH BD AS DEDICATED.
2. THE EASEMENT FOR EMERGENCY ACCESS PURPOSES AS DEDICATED.
3. THE EASEMENT FOR PUBLIC PEDESTRIAN PURPOSES AS DEDICATED.

DATED THIS 26th DAY OF October, 2004

Darlene J. Bloom
DARLENE J. BLOOM
CLERK OF THE BOARD OF SUPERVISORS



COUNTY TREASURER-TAX COLLECTOR'S CERTIFICATE

STATE OF CALIFORNIA)
COUNTY OF ORANGE) SS

I HEREBY CERTIFY THAT ACCORDING TO THE RECORDS OF MY OFFICE
THERE ARE NO LIENS AGAINST THE LAND COVERED BY THIS MAP OR
ANY PART THEREOF FOR UNPAID STATE, COUNTY, MUNICIPAL OR LOCAL
TAXES OR SPECIAL ASSESSMENTS COLLECTED AS TAXES, EXCEPT TAXES
OR SPECIAL ASSESSMENTS COLLECTED AS TAXES NOT YET PAYABLE.

AND DO CERTIFY TO THE RECORDER OF THE COUNTY OF ORANGE
THAT THE PROVISIONS OF THE SUBDIVISION MAP ACT HAVE BEEN COMPLIED
WITH REGARDING DEPOSITS TO SECURE PAYMENT OF TAXES OR SPECIAL
ASSESSMENTS COLLECTED AS TAXES ON THE LAND COVERED BY THIS MAP.

DATED THIS 8th DAY OF September, 2004.

John M.W. Moorlach
JOHN M.W. MOORLACH
COUNTY TREASURER-TAX COLLECTOR

BY: John M.W. Moorlach
DEPUTY TREASURER -
TAX COLLECTOR

SEE SHEET 2 FOR ADDITIONAL NOTARY ACKNOWLEDGMENT AND SIGNATURE OMISSIONS

SHEET 2 OF 8 SHEETS
44 NUMBERED LOTS
16 LETTERED LOTS
21.336 ACRES
FINAL UNIT OF VESTING
T.T.M. 15990
DATE OF SURVEY:
JANUARY, 1999

TRACT MAP NO. 15990

IN THE UNINCORPORATED TERRITORY OF THE COUNTY OF ORANGE,
STATE OF CALIFORNIA

HALL & FOREMAN, INC.

STEVEN C. SHAMBECK, P.L.S. 6217
MAY, 2004

SANTA MARGARITA WATER DISTRICT

STATE OF CALIFORNIA)
COUNTY OF ORANGE)SS

ON THIS 23rd DAY OF SEPT 2004, BEFORE ME, CINDY R. LANE
A NOTARY PUBLIC IN AND FOR SAID STATE, PERSONALLY APPEARED DANIEL R.
FERONS PERSONALLY KNOWN TO ME OR ~~PROVED TO ME ON THE BASIS OF SATISFACTORY~~
~~EVIDENCE~~ TO BE THE PERSON WHOSE NAME IS SUBSCRIBED TO THE WITHIN INSTRUMENT
AND ACKNOWLEDGED TO ME THAT HE EXECUTED THE SAME IN HIS AUTHORIZED CAPACITY,
AND THAT BY HIS SIGNATURE ON THE INSTRUMENT THE PERSON OR THE ENTITY UPON
BEHALF OF WHICH THE PERSON ACTED, EXECUTED THE INSTRUMENT.

WITNESS MY HAND:

MY COMMISSION EXPIRES 2-20-2005

Cindy R. Lane
NOTARY PUBLIC IN AND FOR SAID STATE

MY PRINCIPAL PLACE OF BUSINESS
IS IN ORANGE COUNTY

CINDY R. LANE
PRINT NAME

AUTOMATIC FIRE SPRINKLER NOTE:
ALL MULTIFAMILY RESIDENTIAL STRUCTURES; ALL SINGLE FAMILY STRUCTURES EXCEEDING
5,500 SQUARE FEET; AND ALL STRUCTURES EXCEEDING FIRE DEPARTMENT ACCESS
REQUIREMENTS SHALL BE PROTECTED BY AN AUTOMATIC SPRINKLER SYSTEM, IN A
MANNER MEETING THE APPROVAL OF THE FIRE CHIEF.

SPECIAL FIRE PROTECTION NOTE:
PROPERTY IS IN A SPECIAL FIRE PROTECTION AREA.

HIGH FIRE HAZARD AREA NOTE:
THE LOTS SHOWN ON THIS MAP ARE IN A HIGH FIRE HAZARD AREA DUE TO
WILD LAND EXPOSURE.

SIGNATURE OMISSIONS

PURSUANT TO THE PROVISIONS OF SECTION 66436 (a)(3)(A)(C) OF
THE SUBDIVISION MAP ACT, THE FOLLOWING SIGNATURES HAVE BEEN
OMITTED:

SOUTHERN CALIFORNIA EDISON HOLDER OF AN EASEMENT FOR PUBLIC UTILITIES
AND PURPOSES INCIDENTAL PER DOCUMENT RECORDED APRIL 16, 1965 IN BOOK
7485 PAGE 714 OF OFFICIAL RECORDS

LADERA DEVELOPMENT COMPANY, L.L.C., HOLDER OF OIL, GAS, AND MINERAL
RIGHTS PER DEED RECORDED DECEMBER 10, 1996 AS INSTRUMENT NO.
19960624029 OF OFFICIAL RECORDS.

LADERA LAND CONSERVANCY, HOLDER OF AN EASEMENT FOR OPEN SPACES
CONSERVATION PURPOSES PER DOCUMENT RECORDED JANUARY 29, 2002 AS
INSTRUMENT NO. 20020074876 OF OFFICIAL RECORDS.

BASIS OF BEARINGS

THE BEARINGS SHOWN HEREON ARE BASED ON THE BEARING BETWEEN
O.C.S. HORIZONTAL CONTROL STATION GPS NO. 1417 AND STATION
GPS NO. 1448, BEING NORTH 10°48'13" EAST PER RECORDS ON FILE
IN THE OFFICE OF THE ORANGE COUNTY SURVEYOR.

DATUM STATEMENT

COORDINATES SHOWN ARE BASED ON THE CALIFORNIA COORDINATE
SYSTEM (CCS 83), ZONE VI, 1983 NAD (1991.35 EPOCH OCS GPS
ADJUSTMENT). ALL DISTANCES ARE GROUND DISTANCES UNLESS
OTHERWISE NOTED. TO OBTAIN GRID DISTANCE MULTIPLY GROUND
DISTANCE BY 0.999948295. THIS FACTOR IS PROJECT-SPECIFIC.

NOTES:

THE PRIVATE STREETS CONSTRUCTED WITHIN THIS MAP
SHALL BE OWNED, OPERATED AND MAINTAINED BY THE
DEVELOPER, SUCCESSORS OR ASSIGNS. THE COUNTY OF
ORANGE SHALL HAVE NO RESPONSIBILITY THEREFORE
UNLESS PURSUANT TO APPROPRIATE SECTIONS OF THE
STREETS AND HIGHWAYS CODE OF THE STATE OF CALIFORNIA,
THE SAID PRIVATE STREETS HAVE BEEN ACCEPTED INTO
THE COUNTY ROAD SYSTEM BY APPROPRIATE RESOLUTION
OF THE ORANGE COUNTY BOARD OF SUPERVISORS.

EASEMENT NOTES

- ☒ INDICATES SOUTHERN CALIFORNIA EDISON EASEMENT FOR PUBLIC
UTILITIES AND INCIDENTAL PURPOSES PER DOCUMENT RECORDED
APRIL 16, 1965 IN BOOK 7485 PAGE 714 OF OFFICIAL RECORDS
- ☒ INDICATES WATER, RECYCLED WATER, SEWER & ACCESS
EASEMENT DEDICATED TO SANTA MARGARITA WATER DISTRICT
- ☒ INDICATES DRAINAGE AND ACCESS EASEMENT DEDICATED TO
SANTA MARGARITA WATER DISTRICT
- ☒ INDICATES LADERA LAND CONSERVANCY, HOLDER OF AN EASEMENT
FOR OPEN SPACED CONSERVATION PURPOSES PER DOCUMENT
RECORDED JANUARY 29, 2002 AS INSTRUMENT NO. 20020074876
OF OFFICIAL RECORDS.
- ☒ INDICATES EMERGENCY ACCESS EASEMENT DEDICATED TO THE
COUNTY OF ORANGE
- ☒ INDICATES PUBLIC PEDESTRIAN EASEMENT AS
DEDICATED TO THE COUNTY OF ORANGE.

MONUMENT NOTES

- INDICATES FOUND MONUMENT AS NOTED.
- ☒ INDICATES FOUND 2 1/2" IRON PIPE W/2" OCS BRASS CAP STAMPED "GPS
1448 9-95" PER TRACT NO. 16203, M.M. 826/8-20 AND RECORDS ON FILE
IN THE ORANGE COUNTY SURVEYORS OFFICE.
N2146790.819, E6142602.585
- ☒ INDICATES FOUND 2 1/2" IRON PIPE W/2" OCS BRASS CAP STAMPED "GPS
1417 9-95" PER TRACT NO. 16203, M.M. 826/8-20 AND RECORDS ON FILE
IN THE ORANGE COUNTY SURVEYORS OFFICE.
N2141450.558, E6141583.535
- ☐ INDICATES 2" I.P. TAGGED L.S. 6217 OR SPIKE & WASHER STAMPED L.S.
6217 OR LEAD, TACK & TAG L.S. 6217 TO BE SET PER TRACT NO. 16471
M.M. _____, UNLESS OTHERWISE NOTED.
- ☐ INDICATES 2" I.P. TAGGED L.S. 6217 OR SPIKE & WASHER STAMPED L.S.
6217 OR LEAD, TACK & TAG L.S. 6217 TO BE SET PER TRACT NO. 16472
M.M. _____, UNLESS OTHERWISE NOTED.
- ☐ INDICATES 2" I.P. TAGGED L.S. 6217 OR SPIKE & WASHER STAMPED L.S.
6217 OR LEAD, TACK & TAG L.S. 6217 TO BE SET PER TRACT NO. 16473
M.M. _____, UNLESS OTHERWISE NOTED.
- ☐ 2" I.P. TAGGED P.L.S. 5557 OR SPIKE & WASHER STAMPED P.L.S. 5557
OR LEAD, TACK & TAG P.L.S. 5557 TO BE SET PER TRACT NO. 15986
M.M. 849/1-15, UNLESS OTHERWISE NOTED.
- 2" I.P. TAGGED L.S. 6217 OR SPIKE & WASHER STAMPED L.S. 6217
OR LEAD, TACK & TAG L.S. 6217 TO BE SET AT ALL TRACT BOUNDARY
CORNERS WITHIN 90 DAYS AFTER ACCEPTANCE OF IMPROVEMENTS.
- 1" I.P. TAGGED L.S. 6217 OR SPIKE & WASHER STAMPED L.S. 6217 OR
LEAD, TACK & TAG L.S. 6217 TO BE SET AT LOT CORNERS WITHIN 90 DAYS
AFTER ACCEPTANCE OF IMPROVEMENTS.
- 1" I.P. TAGGED L.S. 6217 OR SPIKE & WASHER STAMPED L.S. 6217 OR
LEAD, TACK & TAG L.S. 6217 TO BE SET AT ALL CENTERLINE INTERSECTIONS,
E.C.'S AND B.C.'S WITHIN 90 DAYS AFTER ACCEPTANCE OF IMPROVEMENTS.
- 2" I.P. TAGGED L.S. 6217 OR SPIKE & WASHER STAMPED
L.S. 6217 OR LEAD, TACK & TAG L.S. 6217 TO BE SET
PRIOR TO MAP RECORDATION.

NOTES

LOTS BA THROUGH BD ARE FOR PRIVATE STREET PURPOSES AND ARE NOT
SEPARATE BUILDING SITES.

LOTS A THROUGH K ARE FOR LANDSCAPE/OPEN SPACE PURPOSES AND
ARE NOT SEPARATE BUILDING SITES.

LOT 42 THROUGH 44 ARE NOT RESIDENTIAL BUILDING SITES, BUT ARE
PRIVATE RECREATION SITES

[] INDICATES MEASURED AND RECORD PER TRACT NO. 16471 M.M. _____/

() INDICATES MEASURED AND RECORD PER TRACT NO. 16472 M.M. _____/

{ } INDICATES MEASURED AND RECORD PER TRACT NO. 16473 M.M. _____/

[()] INDICATES MEASURED AND RECORD PER TRACT NO. 15986 M.M. 819/1-15.

862 36

SHEET 3 OF 8 SHEETS
44 NUMBERED LOTS
16 LETTERED LOTS
21.336 ACRES
FINAL UNIT OF VESTING
T.T.M. 15990
DATE OF SURVEY:
JANUARY, 1999

TRACT MAP NO. 15990

IN THE UNINCORPORATED TERRITORY OF THE COUNTY OF ORANGE,
STATE OF CALIFORNIA

HALL & FOREMAN, INC.

STEVEN C. SHAMBECK, P.L.S. 6217


MAY, 2004

SEE SHEET 2 FOR BASIS OF
BEARINGS, DATUM STATEMENT,
MONUMENT NOTES, EASEMENT
NOTES AND NOTES

BOUNDARY AND INDEX SHEET

CURVE DATA			
CURVE	DELTA	RADIUS	LENGTH
C1	98°07'01"	57.00'	97.61'
C2	23°41'21"	155.00'	64.09'
C3	9°56'58"	99.00'	17.19'
C4	13°27'38"	194.00'	45.58'
C5	25°35'31"	141.00'	62.98'
C6	25°59'49"	141.00'	63.98'
C7	6°52'50"	200.00'	24.02'
C8	5°48'17"	365.00'	36.98'
C9	1°55'23"	450.00'	15.10'
C10	15°40'27"	333.00'	91.10'
C11	2°43'15"	289.00'	13.72'
C12	4°11'25"	245.00'	17.92'
C13	9°55'28"	125.00'	21.65'
C14	25°11'20"	25.00'	10.99'
C15	11°00'25"	77.00'	14.79'
C16	9°40'10"	50.00'	8.44'
C17	20°36'32"	164.00'	58.99'
C18	11°37'21"	168.00'	34.08'
C19	1°25'28"	158.00'	3.93'
C20	13°32'32"	55.00'	13.00'
C21	58°08'28"	157.00'	159.32'
C22	13°32'32"	55.00'	13.00'
C23	15°50'59"	158.00'	43.71'
C24	1°20'26"	82.00'	1.92'
C25	38°41'54"	75.00'	50.66'
C26	12°28'51"	50.00'	10.89'
C27	9°51'25"	113.00'	19.44'
C28	18°31'49"	120.00'	38.81'
C29	22°57'37"	108.57'	58.03'
C30	17°29'12"	213.00'	65.01'
C31	6°14'03"	213.00'	23.18'
C32	13°57'13"	401.00'	97.66'
C33	1°09'15"	1000.00'	20.14'
C34	9°02'11"	143.00'	22.55'
C35	2°14'47"	315.00'	12.35'
C36	9°31'14"	28.00'	45.54'
C37	36°25'21"	30.00'	19.07'
C38	10°17'11"	328.00'	58.89'
C39	18°12'44"	272.00'	86.46'
C40	1°26'55"	300.00'	7.58'
C41	20°01'20"	322.00'	112.52'
C42	10°17'11"	278.00'	49.91'

LINE DATA		
LINE	BEARING	LENGTH
L1	N47°50'31"E	4.71
L2	N04°16'02"E	70.41
L3	N55°37'53"E	2.51
L4	N66°30'42"W	4.00
L5	N35°06'40"E	16.88
L6	N01°19'45"W	29.40
L7	N33°13'09"W	4.12
L8	N03°50'16"E	4.46
L9	N00°29'31"W	9.47
L10	N46°11'20"E	59.97
L11	N04°59'12"W	6.14
L12	N16°37'29"W	4.94
L13	N08°01'07"W	2.79
L14	N18°07'22"E	65.74
L15	N33°24'26"W	6.39
L16	N18°07'22"E	24.55
L17	N16°58'07"E	31.09
L18	N03°01'51"E	98.74
L19	N79°47'17"E	45.01
L20	N84°18'16"E	96.51
L21	N60°38'37"E	8.72
L22	N50°21'26"E	88.72
L23	N08°24'32"W	16.40
L24	N20°41'44"W	12.00 (RAD)
L25	N19°14'49"W	12.00
L26	N31°07'01"W	10.21 (RAD)
L27	N50°21'26"E	88.72
L28	N60°38'37"E	1.53

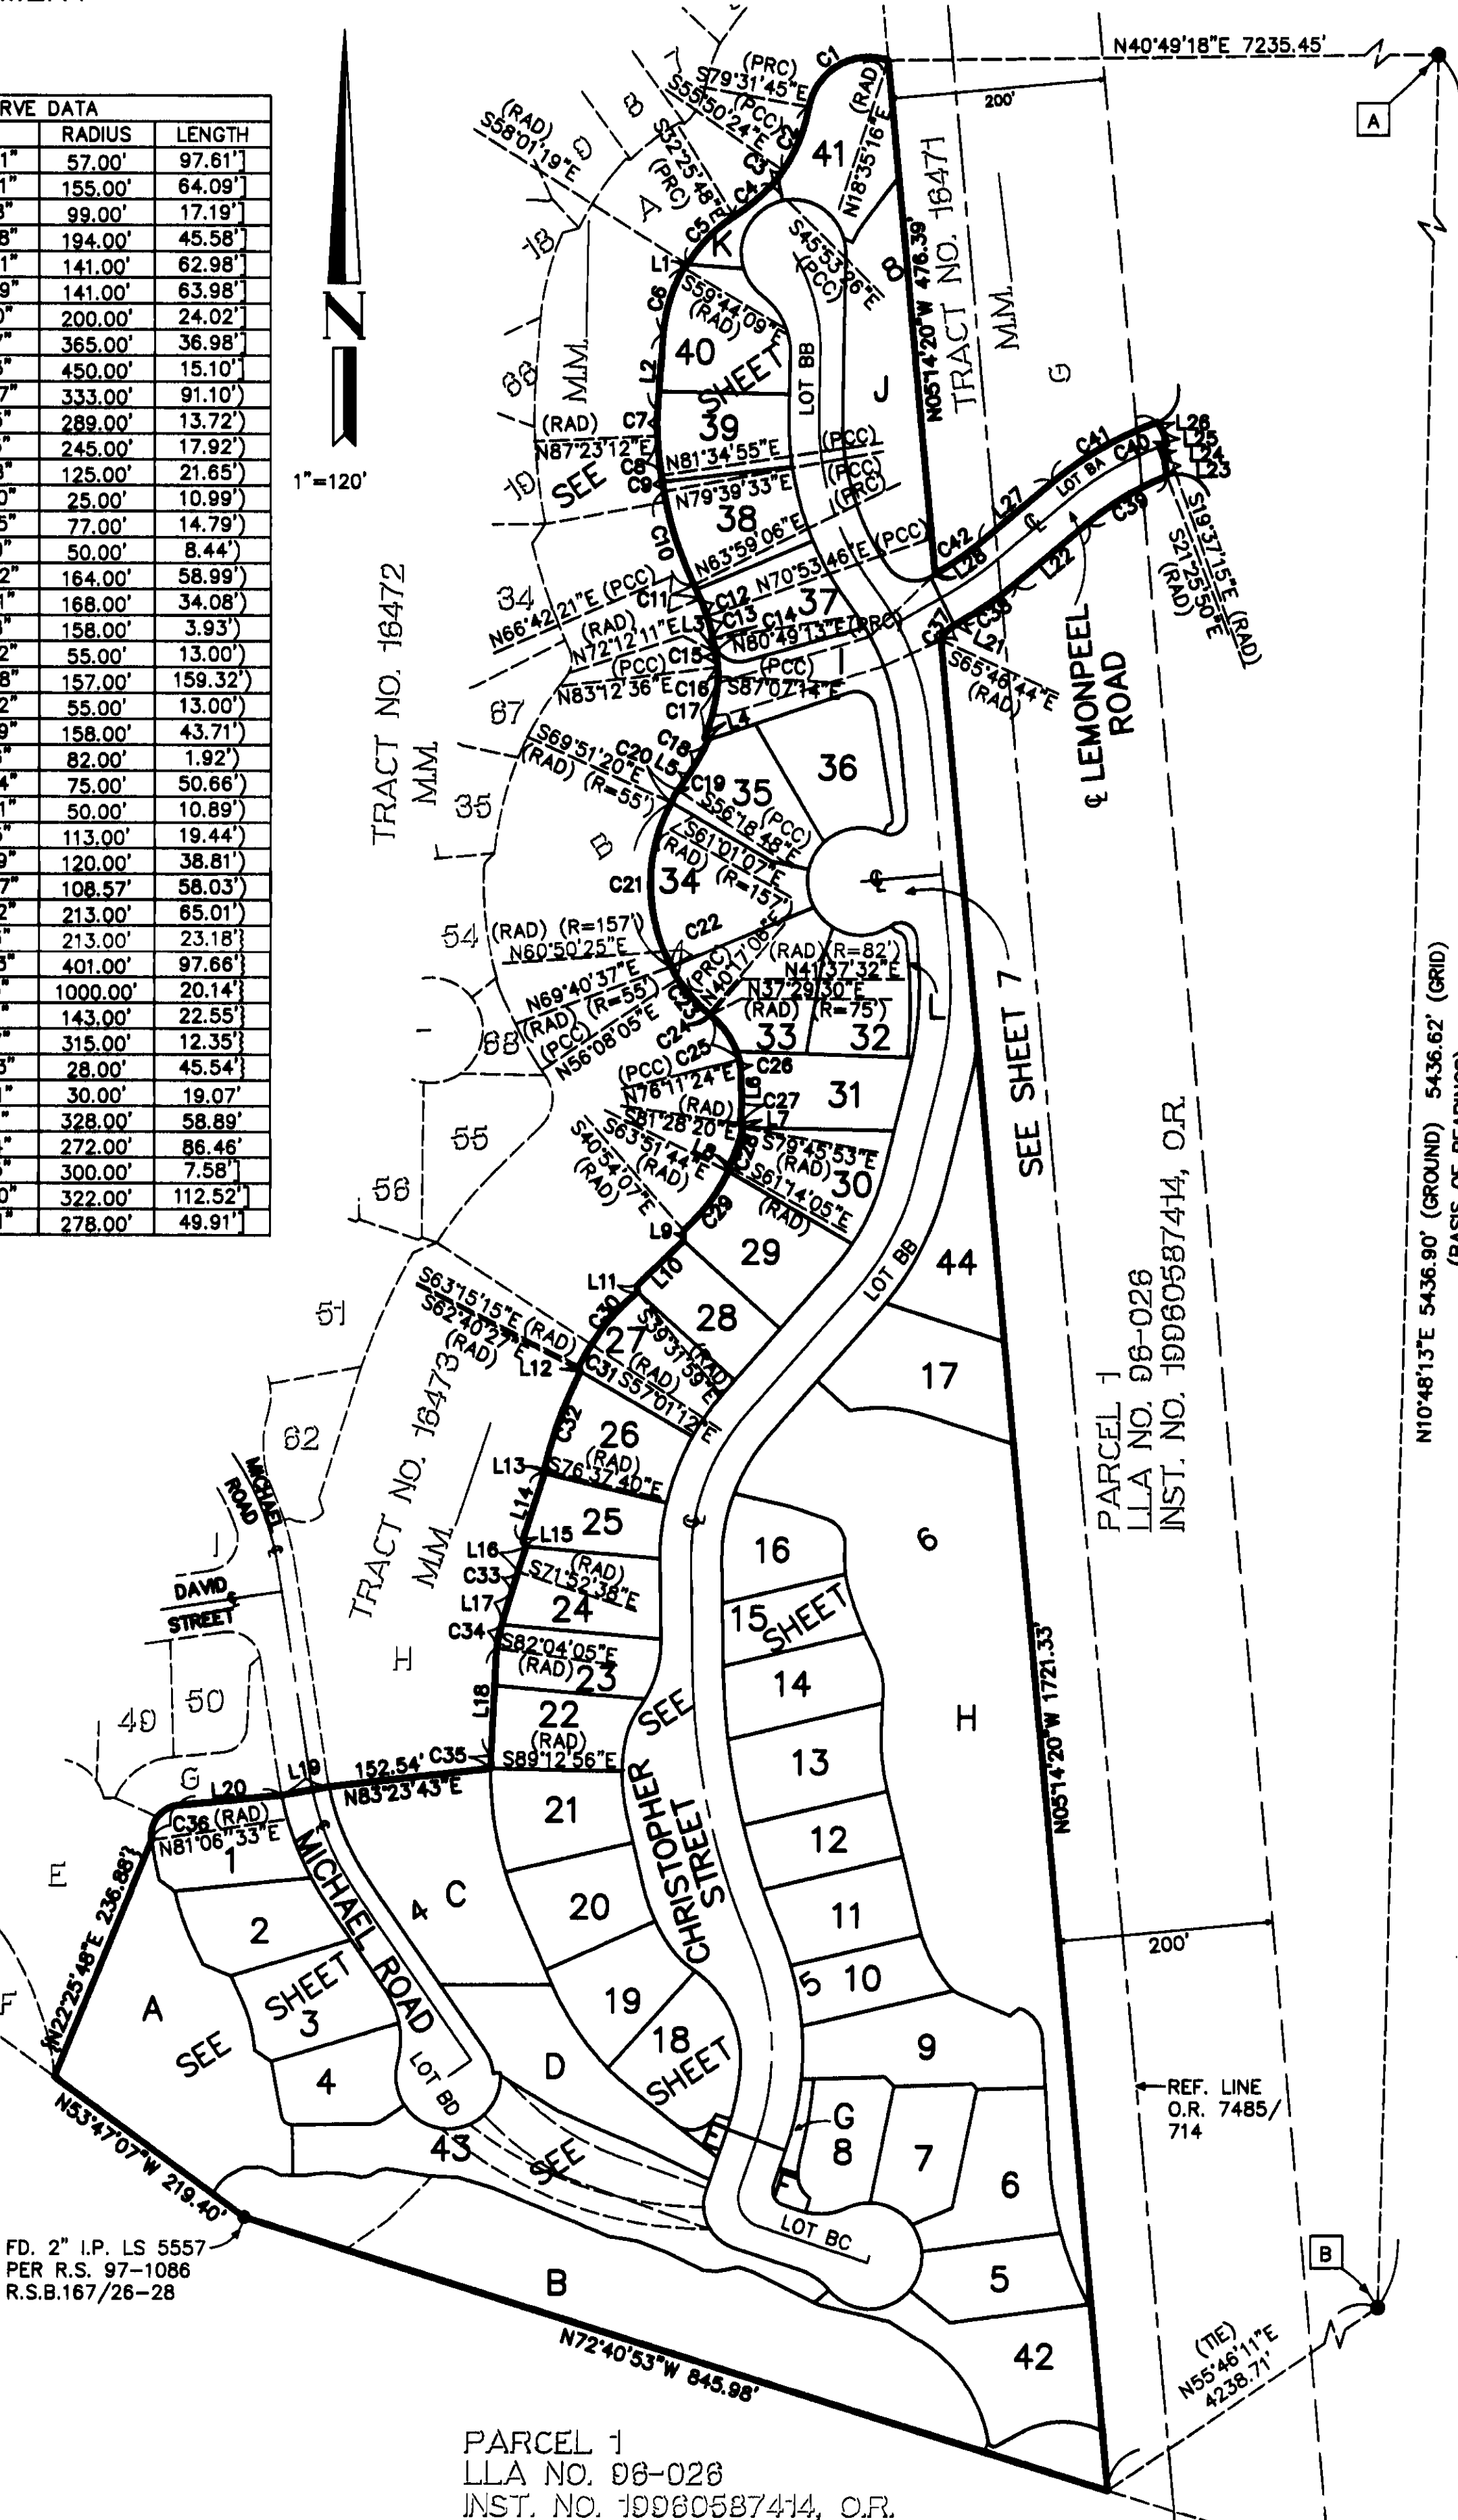

PARCEL 1
LLA NO. 96-026
INST. NO. 19960587414, O.R.

862 36

862 38

SHEET 5 OF 8 SHEETS
44 NUMBERED LOTS
16 LETTERED LOTS
21.336 ACRES
FINAL UNIT OF VESTING
T.T.M. 15990
DATE OF SURVEY:
JANUARY, 1999

TRACT MAP NO. 15990

IN THE UNINCORPORATED TERRITORY OF THE COUNTY OF ORANGE,
STATE OF CALIFORNIA


HALL & FOREMAN, INC.

STEVEN C. SHAMBECK, P.L.S. 6217

MAY, 2004

SEE SHEET 2 FOR BASIS OF
BEARINGS, DATUM STATEMENT,
MONUMENT NOTES, EASEMENT
NOTES AND NOTES


SEE SHEET 6

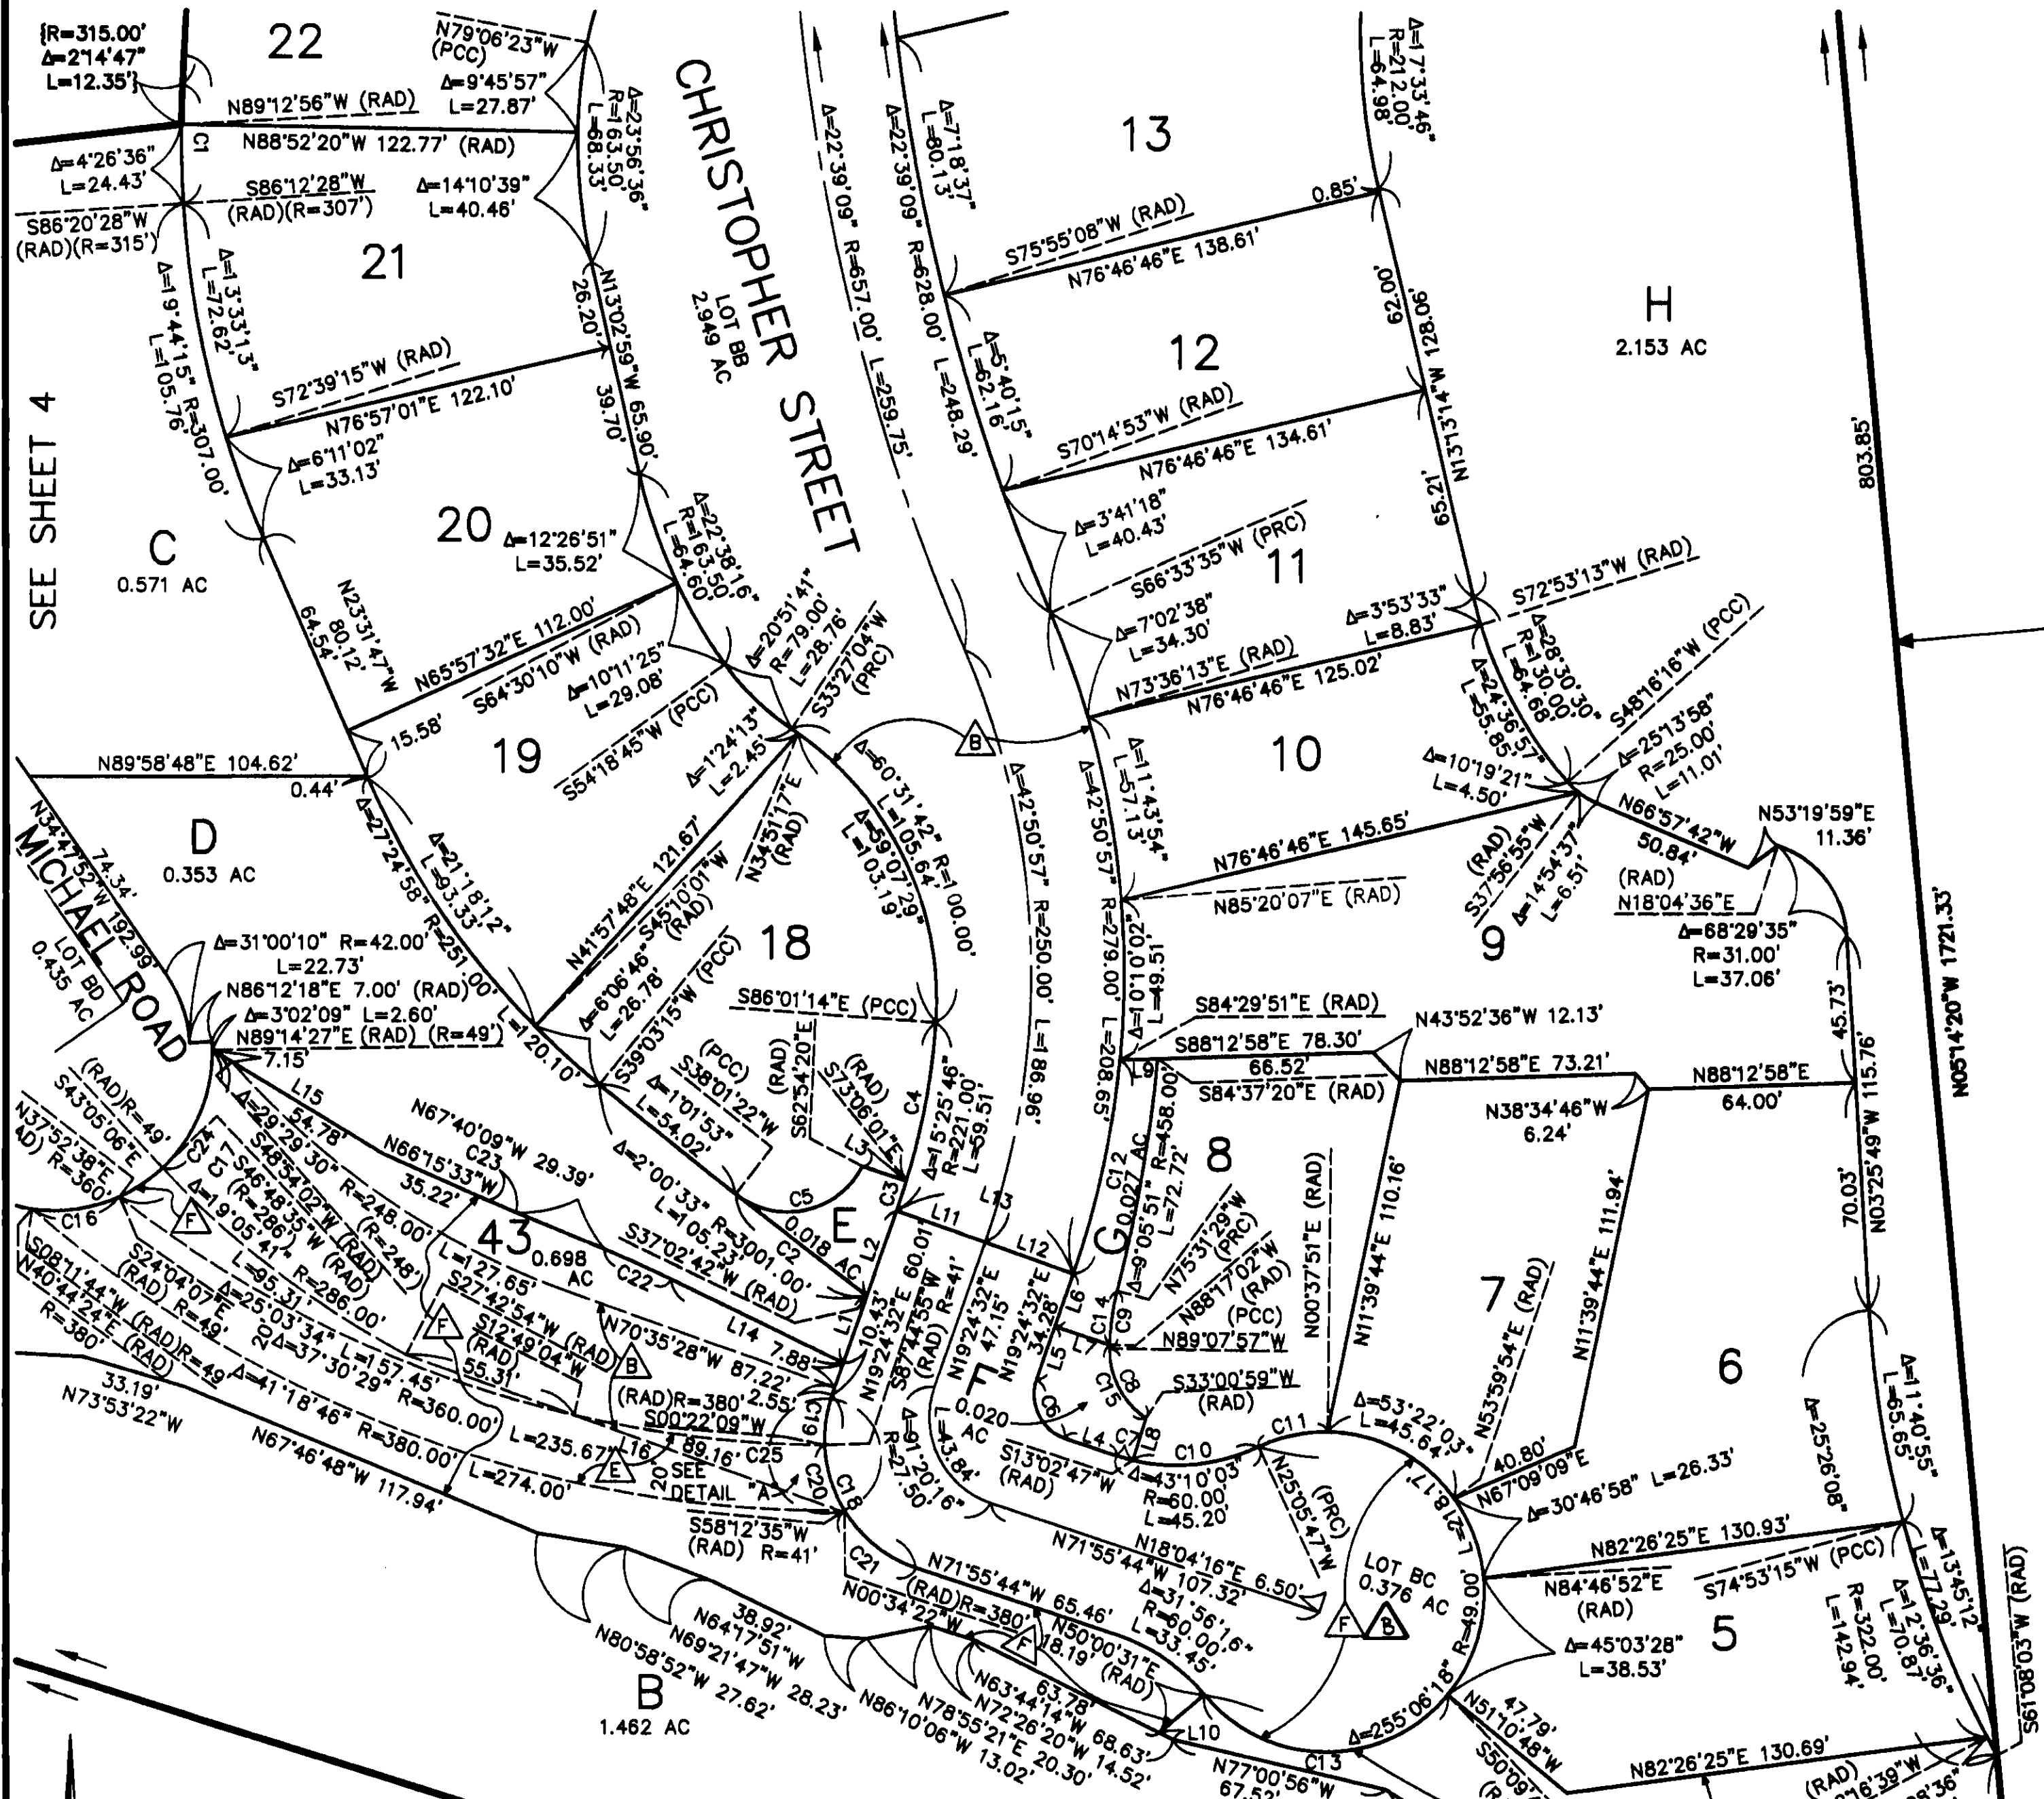

CURVE DATA			
CURVE	DELTA	RADIUS	LENGTH
C1	6°41'22"	315.00'	36.78'
C2	0°58'40"	3001.00'	51.21'
C3	2°30'33"	221.00'	9.68'
C4	12°55'13"	221.00'	49.84'
C5	100°55'42"	26.00'	45.80'
C6	91°20'17"	14.00'	22.32'
C7	5°01'29"	60.00'	5.26'
C8	57°51'03"	25.00'	25.24'
C9	13°36'29"	75.00'	17.81'
C10	38°08'34"	60.00'	39.94'
C11	25°43'38"	49.00'	22.00'
C12	13°54'23"	279.00'	67.72'
C13	100°10'11"	49.00'	85.67'
C14	12°45'34"	75.00'	16.70'
C15	60°15'43"	25.06'	26.36'
C16	32°15'51"	49.00'	27.59'
C17	66°41'26"	49.00'	57.03'
C18	91°20'17"	41.00'	65.36'
C19	21°39'38"	41.00'	15.50'
C20	29°32'19"	41.00'	21.14'
C21	40°08'20"	41.00'	28.72'
C22	31°14'48"	400.00'	22.67'
C23	1°24'36"	400.00'	9.84'
C24	47°40'27"	49.00'	40.77'
C25	12°26'54"	360.00'	78.22'
C26	52°19'07"	41.00'	37.44'

LINE DATA		
LINE	BEARING	LENGTH
L1	N19°24'32"E	21.82'
L2	N19°24'32"E	27.75'
L3	N71°55'44"W	14.40'
L4	N71°55'44"W	16.96'
L5	N19°24'32"E	17.18'
L6	N19°24'32"E	17.10'
L7	N71°55'44"W	18.05'
L8	N18°04'16"E	13.45'
L9	N88°12'58"E	11.79'
L10	N63°44'14"W	4.85'
L11	N70°35'28"W	29.00'
L12	N70°35'28"W	29.00'
L13	N70°35'28"W	58.00'
L14	N64°25'21"W	59.17'
L15	N58°40'08"W	61.93'
L16	N70°35'28"W	144.47'

DETAIL "A"
NOT TO SCALE

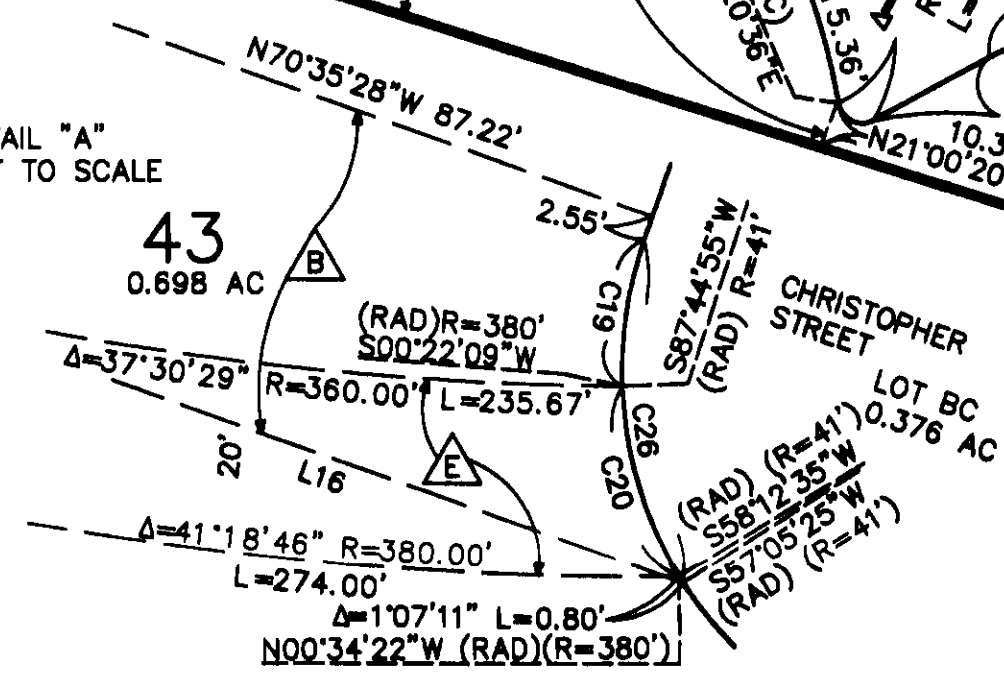

862 38

862 39

SHEET 6 OF 8 SHEETS
44 NUMBERED LOTS
16 LETTERED LOTS
21.336 ACRES
FINAL UNIT OF VESTING
T.T.M. 15990
DATE OF SURVEY:
JANUARY, 1999

TRACT MAP NO. 15990

IN THE UNINCORPORATED TERRITORY OF THE COUNTY OF ORANGE,
STATE OF CALIFORNIA


HALL & FOREMAN, INC.

STEVEN C. SHAMBECK, P.L.S. 6217

MAY, 2004

SEE SHEET 2 FOR BASIS OF
BEARINGS, DATUM STATEMENT,
MONUMENT NOTES, EASEMENT
NOTES AND NOTES

SEE SHEET 7

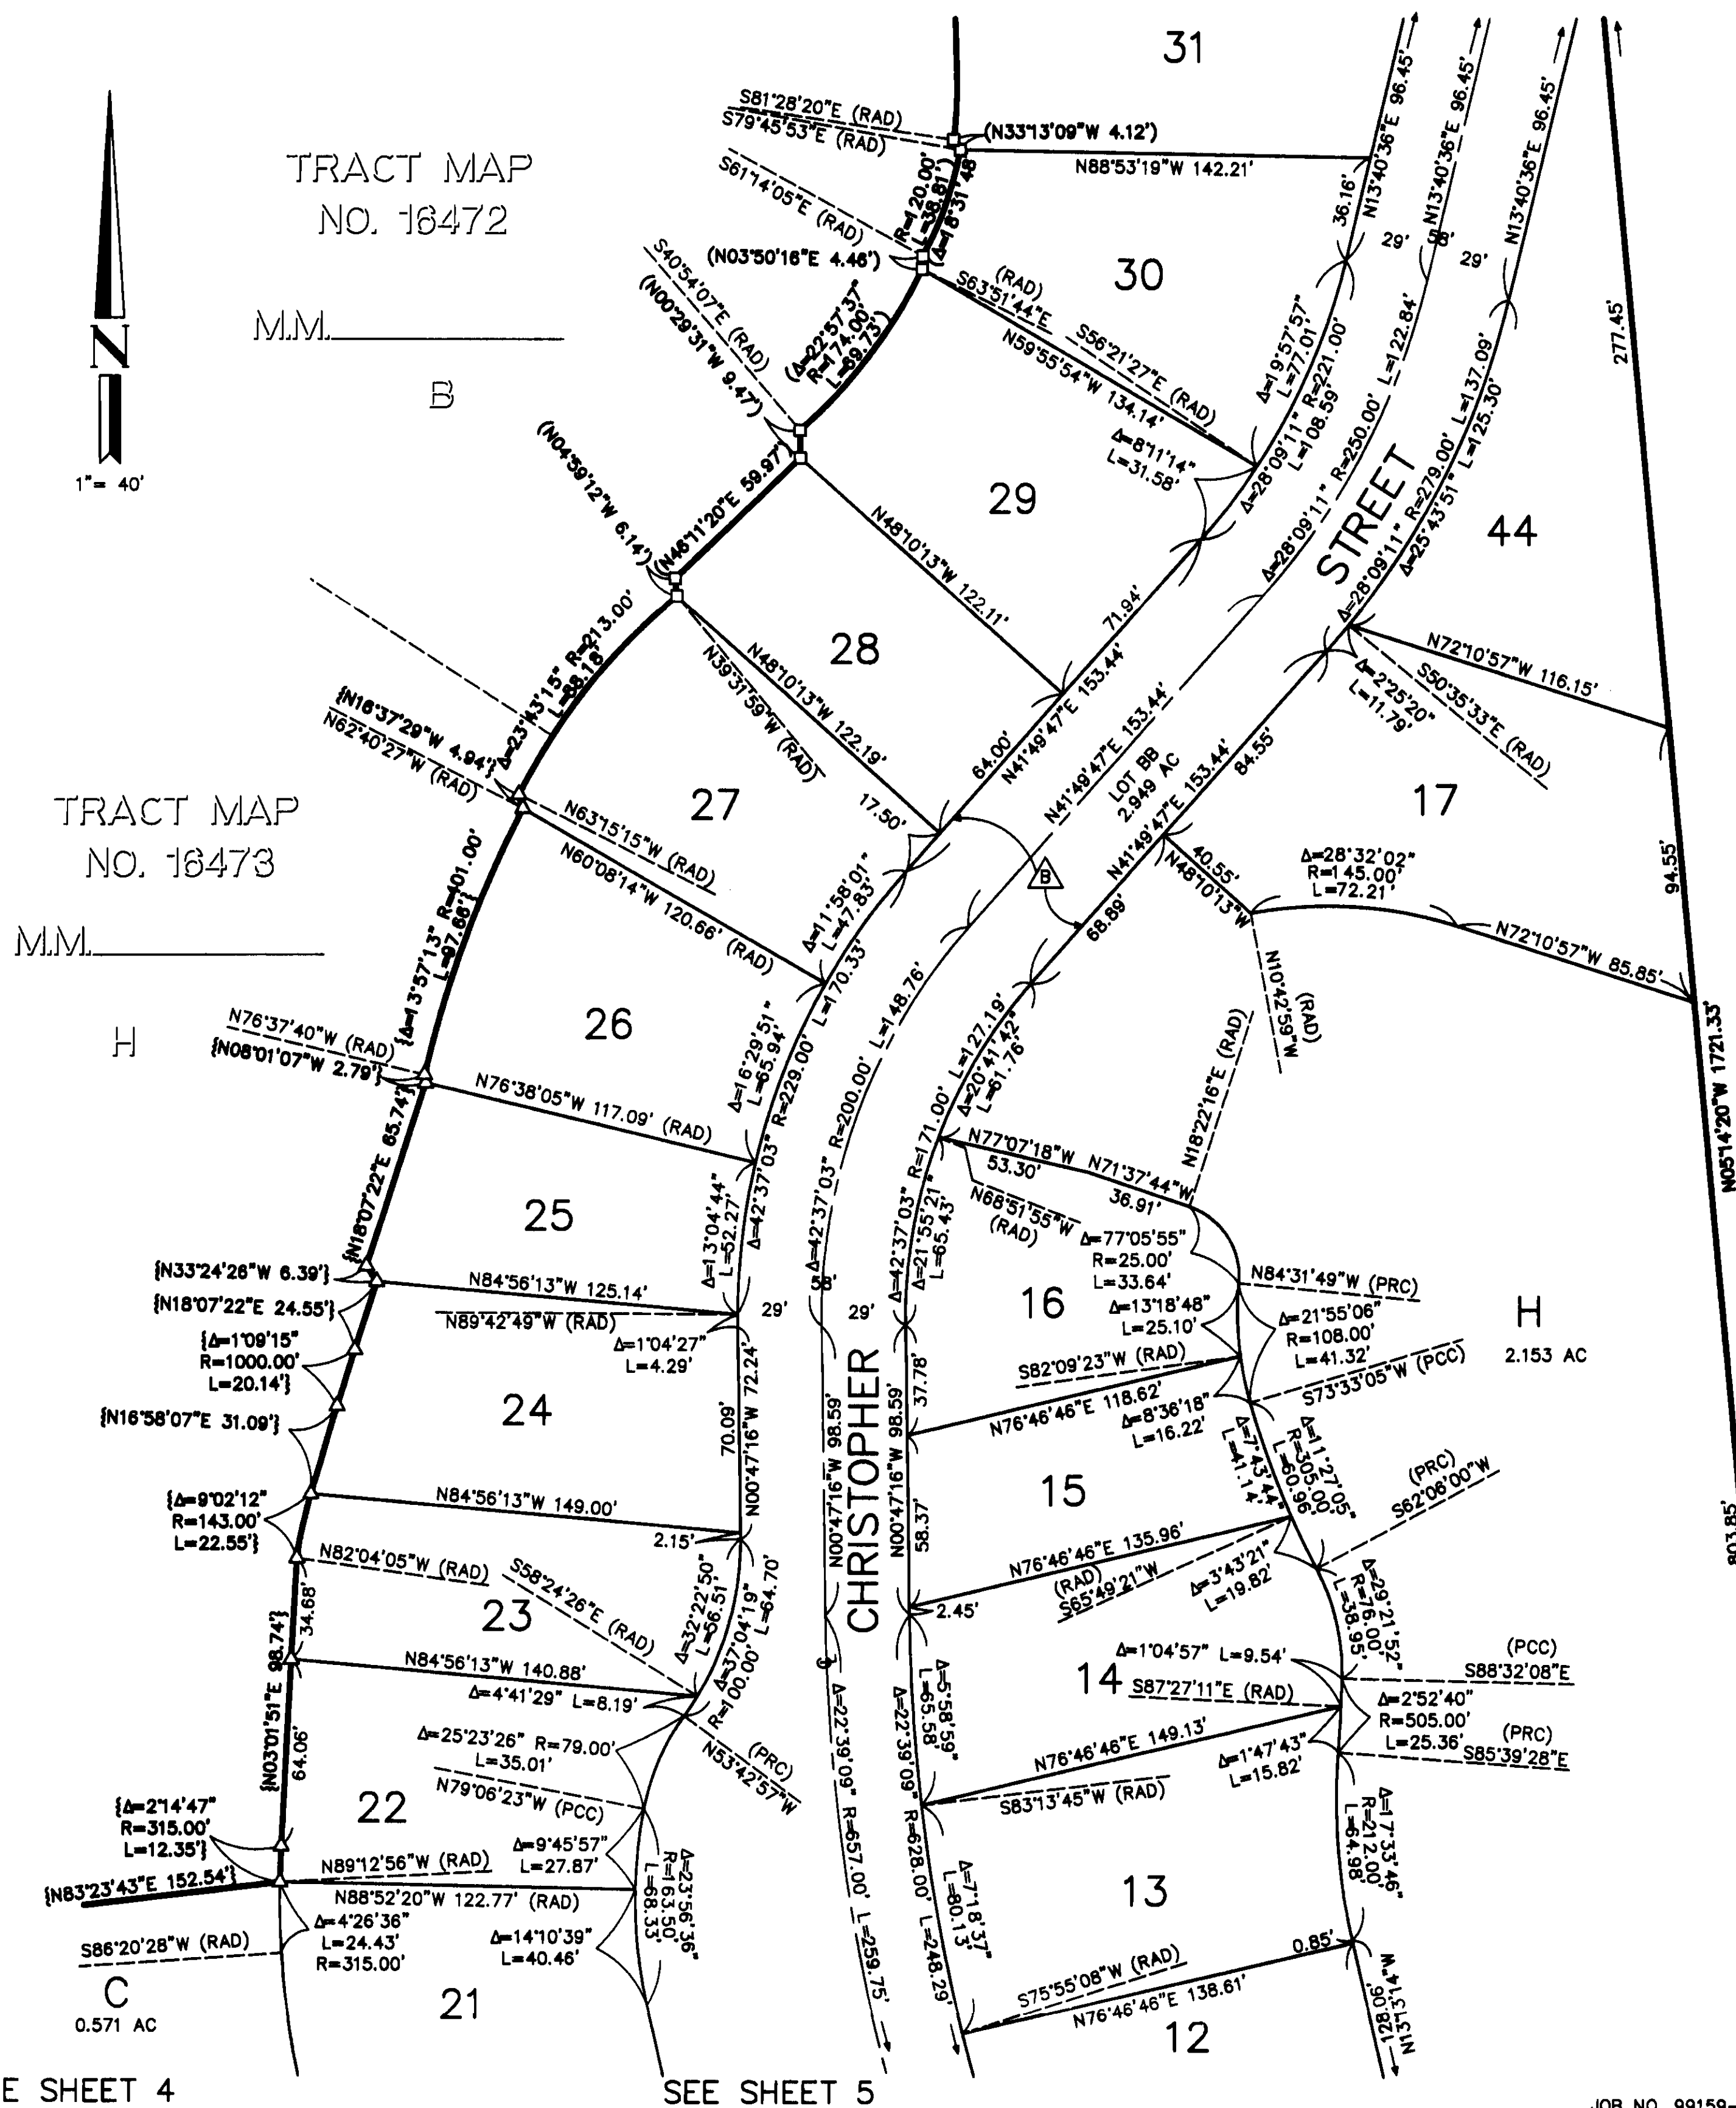

SEE SHEET 4

SEE SHEET 5

862 39

SHEET 7 OF 8 SHEETS
44 NUMBERED LOTS
16 LETTERED LOTS
21.334 ACRES
FINAL UNIT OF VESTING
T.T.M. 15990
DATE OF SURVEY:
JANUARY, 1999

TRACT MAP NO. 15990


IN THE UNINCORPORATED TERRITORY OF THE COUNTY OF ORANGE,
STATE OF CALIFORNIA

HALL & FOREMAN, INC.

STEVEN C. SHAMBECK, P.L.S. 6217
MAY, 2004

SEE SHEET 2 FOR BASIS OF
BEARINGS, DATUM STATEMENT,
MONUMENT NOTES, EASEMENT
NOTES AND NOTES

SEE SHEET 8

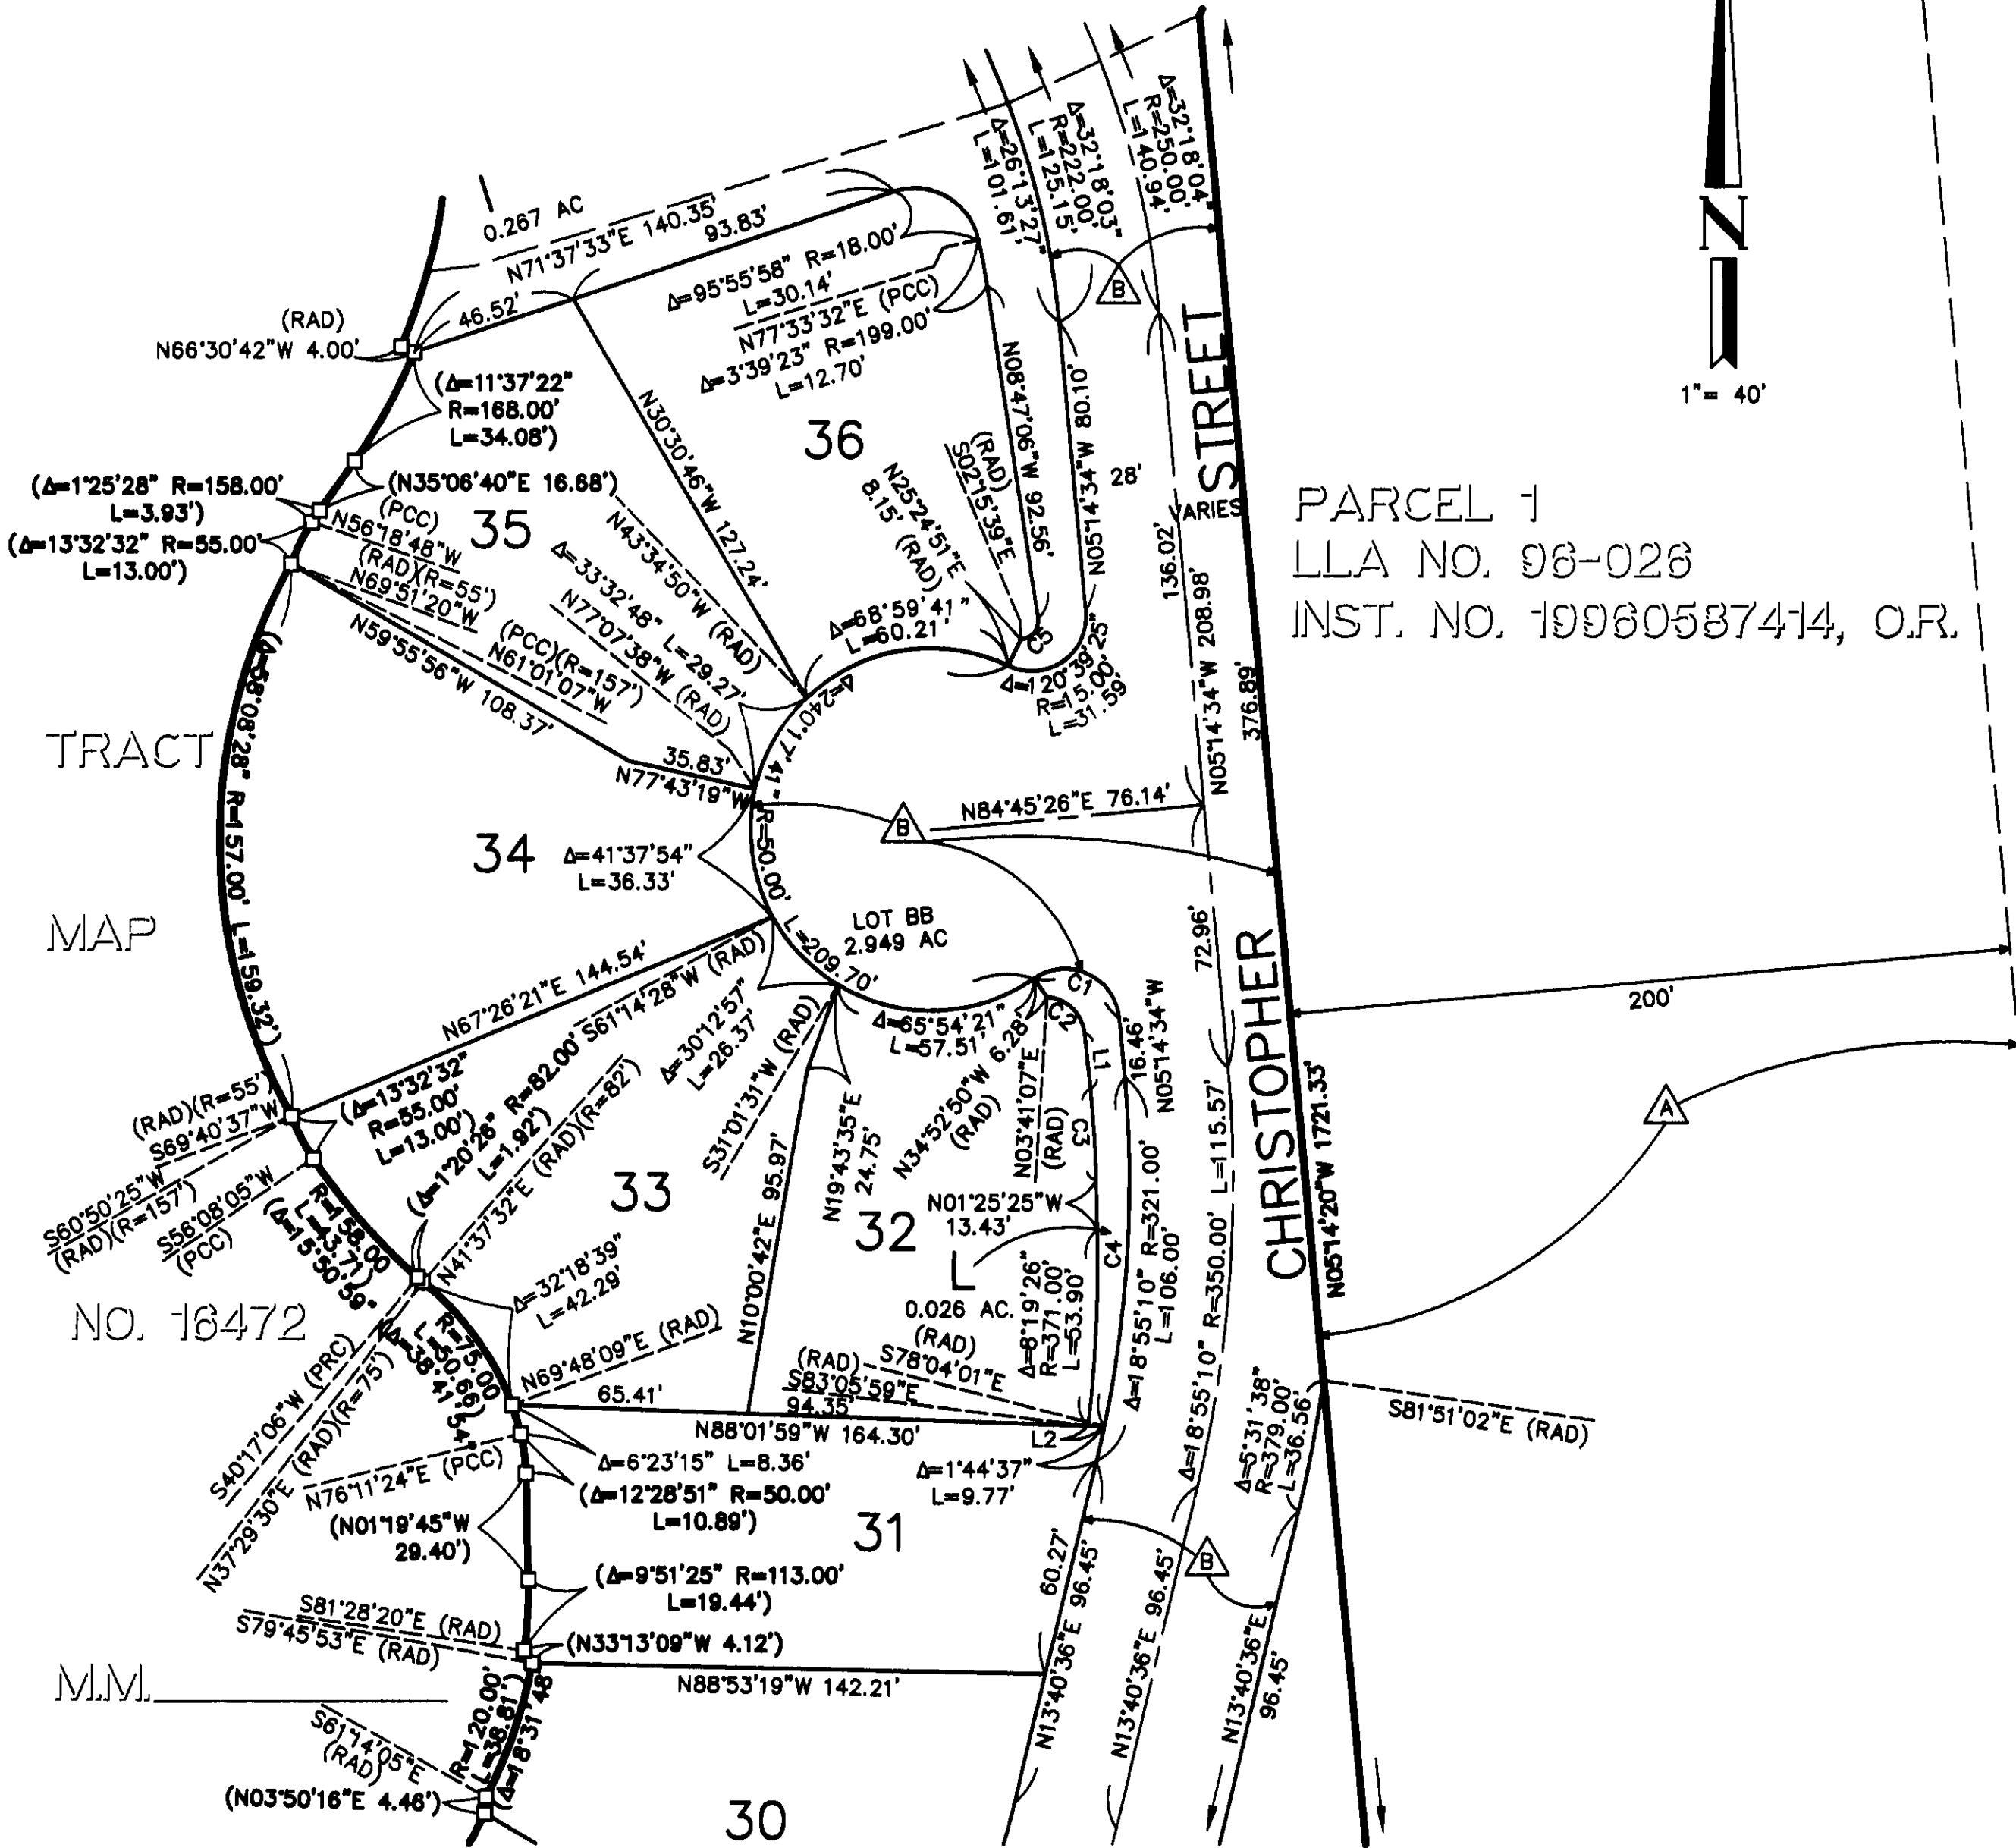

CURVE DATA			
CURVE	DELTA	RADIUS	LENGTH
C1	119°38'16"	15.00'	31.32'
C2	80°14'05"	11.00'	15.40'
C3	4°39'23"	310.00'	25.19'
C4	17°10'33"	321.00'	96.23'
C5	96°31'27"	5.00'	8.42'

LINE DATA		
LINE	BEARING	LENGTH
L1	N06°04'48"W	15.66'
L2	N88°01'59"W	4.54'

862 41

SHEET 8 OF 8 SHEETS
44 NUMBERED LOTS
16 LETTERED LOTS
21.336 ACRES
FINAL UNIT OF VESTING
T.T.M. 15990
DATE OF SURVEY:
JANUARY, 1999

TRACT MAP NO. 15990


IN THE UNINCORPORATED TERRITORY OF THE COUNTY OF ORANGE,
STATE OF CALIFORNIA

HALL & FOREMAN, INC.

STEVEN C. SHAMBECK, P.L.S. 6217


MAY, 2004

SEE SHEET 2 FOR BASIS OF
BEARINGS, DATUM STATEMENT,
MONUMENT NOTES, EASEMENT
NOTES AND NOTES

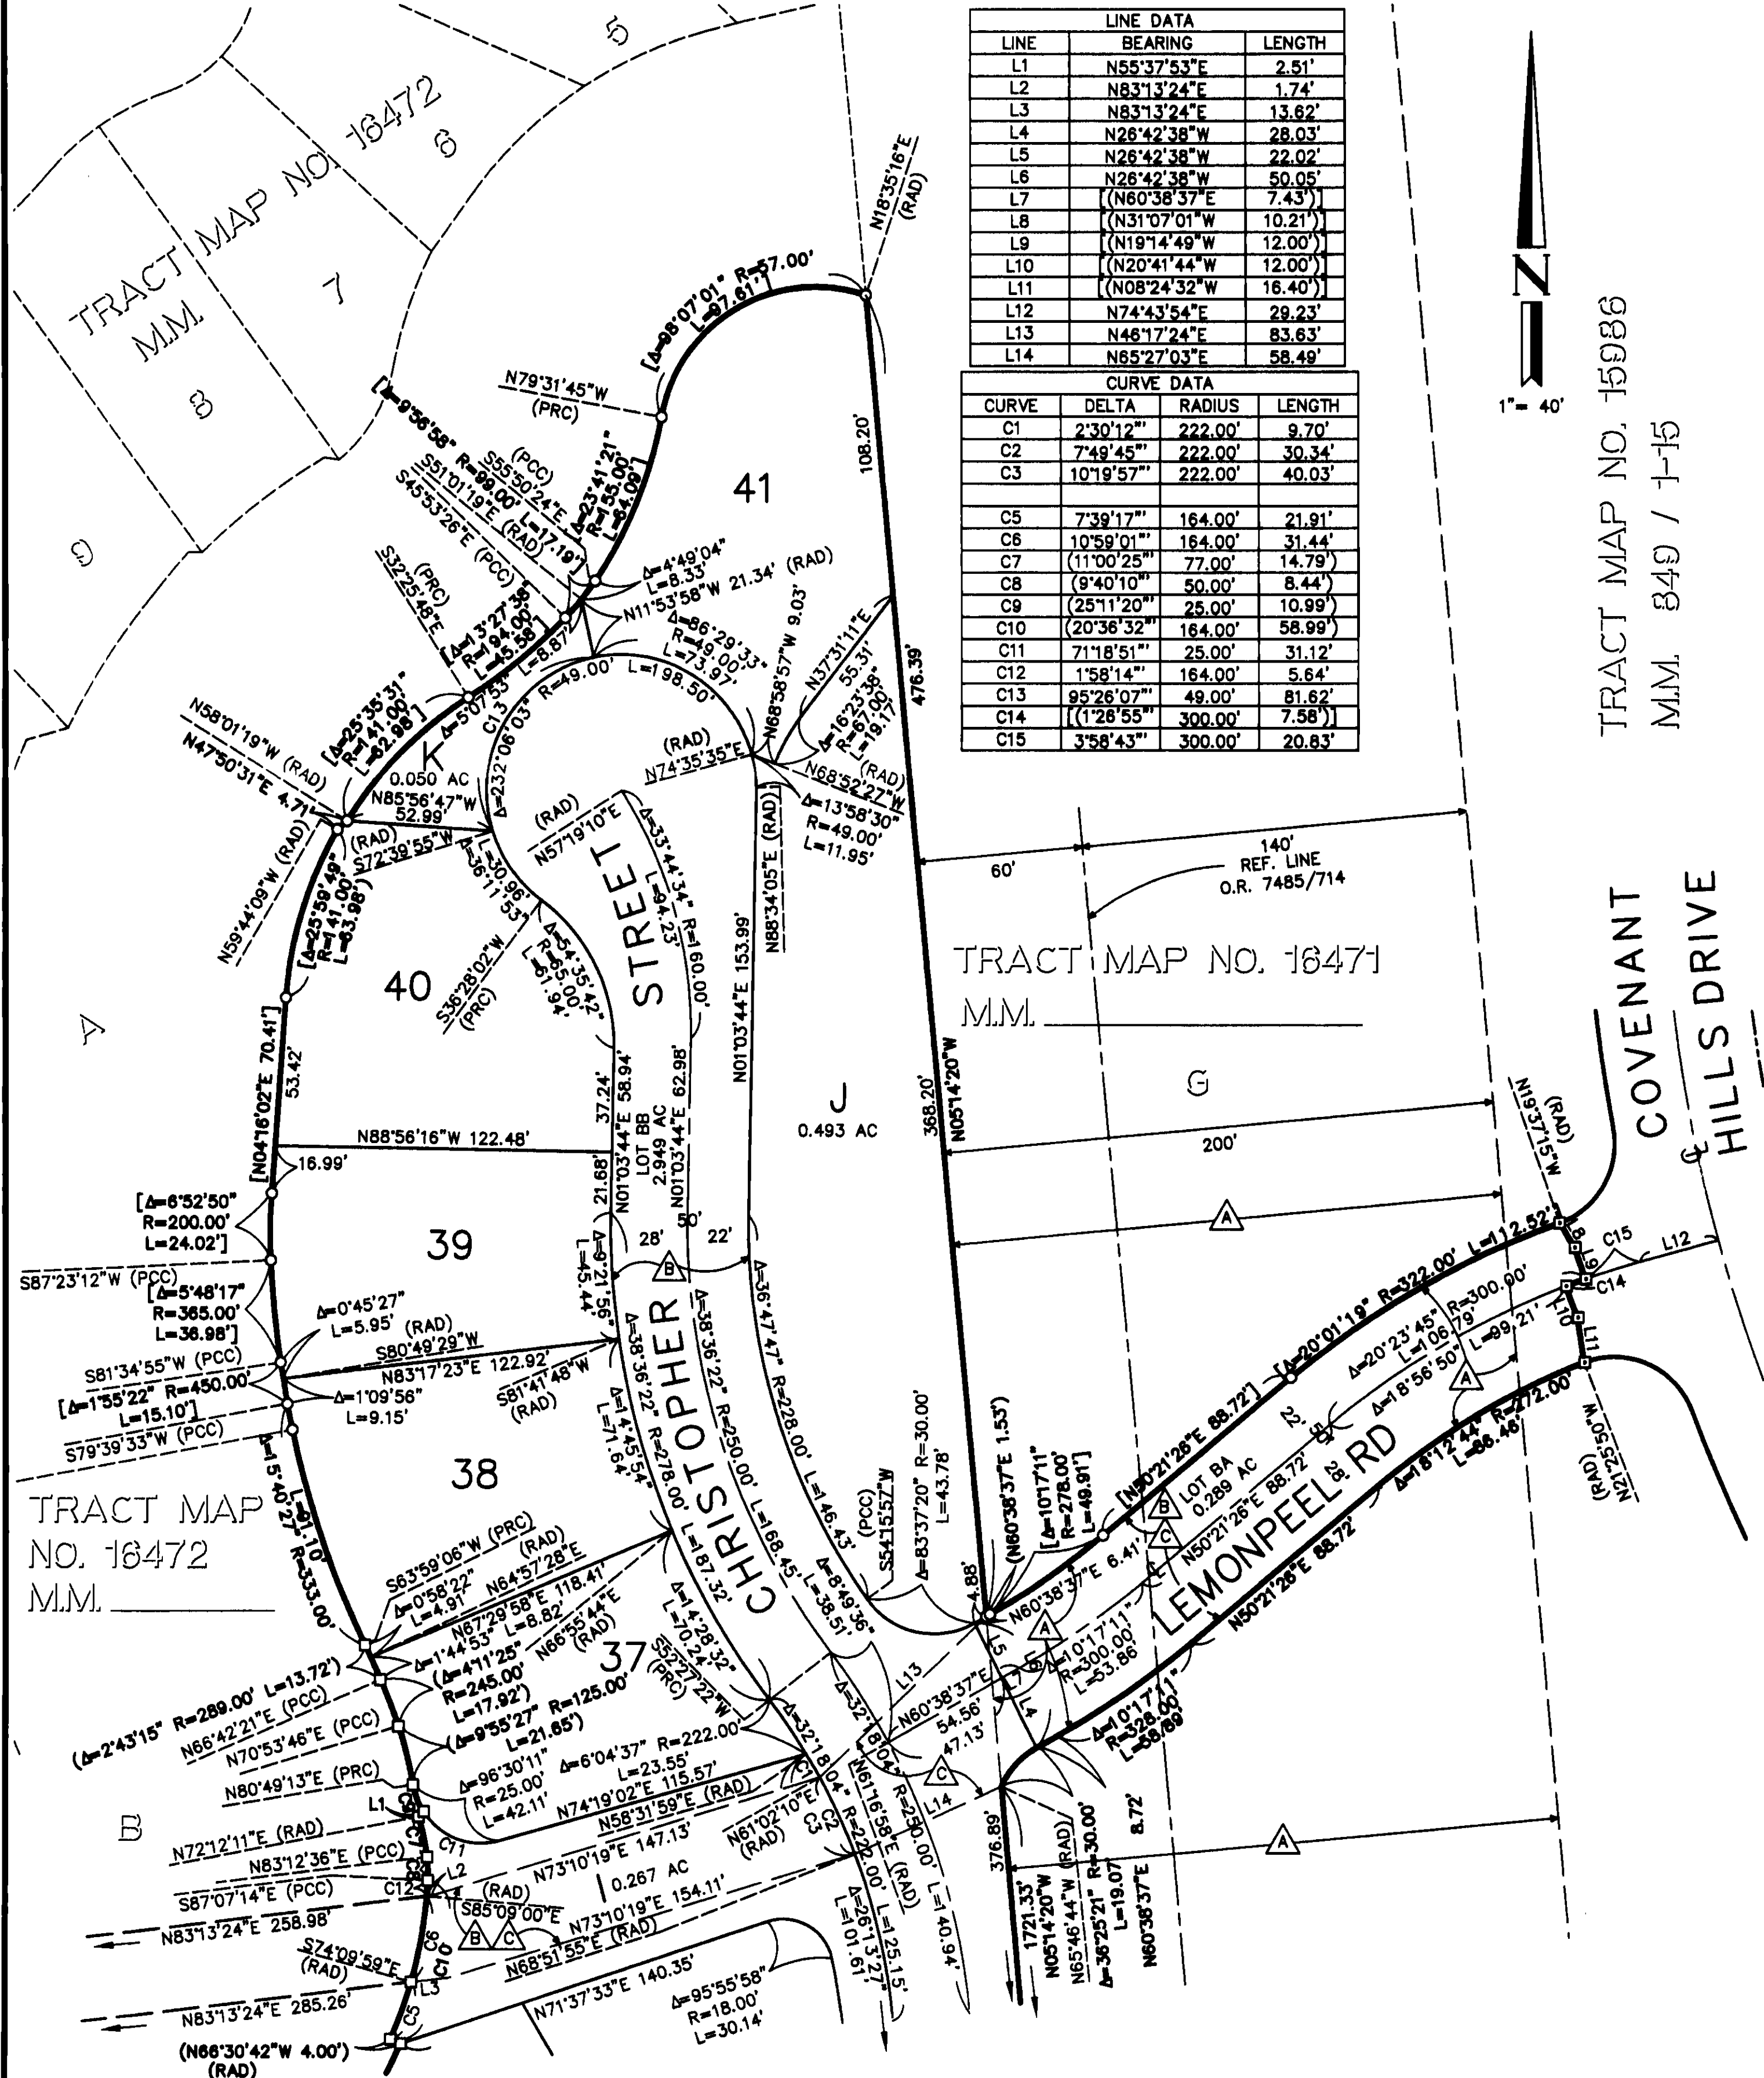

LINE DATA		
LINE	BEARING	LENGTH
L1	N55°37'53"E	2.51'
L2	N83°13'24"E	1.74'
L3	N83°13'24"E	13.62'
L4	N26°42'38"W	28.03'
L5	N26°42'38"W	22.02'
L6	N26°42'38"W	50.05'
L7	(N60°38'37"E	7.43')
L8	(N31°07'01"W	10.21')
L9	(N19°14'49"W	12.00')
L10	(N20°41'44"W	12.00')
L11	(N08°24'32"W	16.40')
L12	N74°43'54"E	29.23'
L13	N46°17'24"E	83.63'
L14	N65°27'03"E	58.49'

CURVE DATA			
CURVE	DELTA	RADIUS	LENGTH
C1	2°30'12"	222.00'	9.70'
C2	7°49'45"	222.00'	30.34'
C3	10°19'57"	222.00'	40.03'
C5	7°39'17"	164.00'	21.91'
C6	10°59'01"	164.00'	31.44'
C7	(11°00'25"	77.00'	14.79')
C8	(9°40'10"	50.00'	8.44')
C9	(25°11'20"	25.00'	10.99')
C10	(20°36'32"	164.00'	58.99')
C11	71°18'51"	25.00'	31.12'
C12	1°58'14"	164.00'	5.64'
C13	95°26'07"	49.00'	81.62'
C14	(1°28'55"	300.00'	7.58')
C15	3°58'43"	300.00'	20.83'

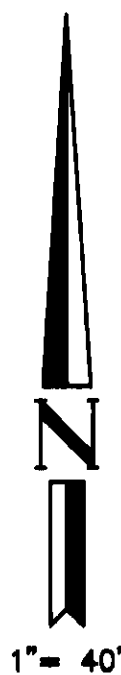

TRACT MAP NO. 15986
M.M. 849 / 1-15

COVENANT
HILLS DRIVE

SEE SHEET 7

862 41