

SHEET 1 OF 8 SHEETS

TRACT NO. 16025

FINAL UNIT OF VESTING
TENTATIVE TRACT NO. 16025BLOCK MODULE
5057 27, 28, 36, 37, 38
39, 47, 48DATE OF SURVEY:
JANUARY 1999

IN UNINCORPORATED TERRITORY OF ORANGE COUNTY, CALIFORNIA

BEING A SUBDIVISION OF A PORTION OF PARCEL 1 OF LOT LINE ADJUSTMENT NO. LL 96-026
AS SHOWN ON EXHIBIT "B" ATTACHED TO THAT CERTAIN DOCUMENT RECORDED NOVEMBER 21,
1996 AS INSTRUMENT NO. 19960587414 OF OFFICIAL RECORDS, RECORDS OF ORANGE COUNTY,
CALIFORNIA.

DECEMBER 2000

JAMES F. GILLEN, L.S. 5557

HUITT-ZOLIARS

8 NUMBERED LOTS AND 18 LETTERED LOTS

63.623 ACRES

ACCEPTED AND FILED AT THE
REQUEST OF

FIRST AMERICAN TITLE INSURANCE CO.

DATE JANUARY 26, 2001

TIME 3:55 PM. FEE \$21.00

INSTRUMENT NO. 20010047443

BOOK 812 PAGE 22-29 M/M

GARY L. GRANVILLE
COUNTY CLERK-RECORDERBY *[Signature]*
DEPUTY

OWNERSHIP CERTIFICATE:

WE, THE UNDERSIGNED, BEING ALL PARTIES HAVING ANY RECORD TITLE INTEREST IN THE
LAND COVERED BY THIS MAP, DO HEREBY CONSENT TO THE PREPARATION AND RECORDATION
OF SAID MAP, AS SHOWN WITHIN THE DISTINCTIVE BORDER LINE. WE ALSO HEREBY DEDICATE
TO THE PUBLIC FOR STREET PURPOSES: SIENNA PARKWAY, ~~SELAS ROAD SOUTH~~,
BARBERRY STREET, TUBEROSE STREET, AGAPANTHUS STREET, ~~AND~~ O'NEILL DRIVE, AND CLEOME
STREET.

WE ALSO HEREBY DEDICATE TO THE COUNTY OF ORANGE:

- (1) THE EASEMENTS FOR SIDEWALK PURPOSES AS SHOWN ON SAID MAP.
- (2) THE EASEMENTS FOR STORM DRAIN PURPOSES AS SHOWN ON SAID MAP.

WE ALSO HEREBY RELEASE AND RELINQUISH TO THE COUNTY OF ORANGE ALL VEHICULAR
ACCESS RIGHTS TO SIENNA PARKWAY, EXCEPT AT APPROVED ACCESS LOCATIONS.PURSUANT TO SECTION 7050 OF THE GOVERNMENT CODE, WE HEREBY IRREVOCABLY OFFER TO
DEDICATE TO THE COUNTY OF ORANGE LOT 4 IN FEE SIMPLE FOR LOCAL PARK PURPOSES,
TOGETHER WITH THE RIGHT TO GRANT EASEMENTS FOR PUBLIC UTILITIES OR OTHER ESSENTIAL
PURPOSES.WE ALSO HEREBY DEDICATE TO THE SANTA MARGARITA WATER DISTRICT THE EASEMENTS FOR
SEWER, WATER, AND ACCESS PURPOSES AS SHOWN ON SAID MAP, WHICH EASEMENTS SHALL BE
SUBJECT TO THE SAME TERMS AND CONDITIONS AS ARE SHOWN IN THAT CERTAIN EASEMENT
RECORDED OCTOBER 6, 1980 IN BOOK 13776, PAGE 341, OF OFFICIAL RECORDS, COUNTY OF ORANGE.
THE SANTA MARGARITA WATER DISTRICT SHALL RESTORE OTHER IMPROVEMENTS OR FACILITIES
LOCATED WITHIN THE EASEMENT, IF IT HAS CONSENTED TO THE LOCATION OF SUCH IMPROVEMENTS
OR FACILITIES TO THE EXTENT THAT THE EXERCISE OF ITS RIGHTS IN CONNECTION WITH THE EASEMENT
IMPACTS OTHER IMPROVEMENTS OR FACILITIES LOCATED WITHIN THE EASEMENT, HOWEVER, IN NO EVENT
SHALL SANTA MARGARITA WATER DISTRICT BE RESPONSIBLE FOR THE COST OF RELOCATING ITS FACILITIES
IN THE EVENT OF CONFLICTS WITH SUCH OTHER IMPROVEMENTS OR FACILITIES.

DMB LADERA, L.L.C., A DELAWARE LIMITED LIABILITY COMPANY.

BY: RANCHO MISSION VIEJO, L.L.C., A DELAWARE LIMITED LIABILITY COMPANY,
AS AGENT AND/OR MANAGER.BY: *[Signature]*
PRINT NAME: PAUL JOHNSON
PRINT TITLE: V.P.-COMMUNITY DEV.BY: *[Signature]*
PRINT NAME: STEPHEN C. SCHWAB
PRINT TITLE: Gen. Vice Pres.DMB CONSOLIDATED HOLDINGS, L.L.C., AN ARIZONA LIMITED LIABILITY COMPANY,
BENEFICIARY UNDER DEEDS OF TRUSTS RECORDED DECEMBER 10, 1996 AS INSTRUMENT
NO. 19960624030, AND RECORDED APRIL 20, 1999 AS INSTRUMENT NO. 19990288616,
BOTH OF OFFICIAL RECORDS.BY: DMB ASSOCIATES, INC., AN ARIZONA CORPORATION,
AS MANAGER.BY: *[Signature]*
PRINT NAME: TONY D. BARNETT
PRINT TITLE:BY: *[Signature]*
PRINT NAME: TERRY T. ALLEN
PRINT TITLE: President/CEO

CERTIFICATE OF ACCEPTANCE

THE UNDERSIGNED, BEING THE DULY APPOINTED AGENT OF THE SANTA MARGARITA WATER
DISTRICT, A PUBLIC CORPORATION OF ORANGE COUNTY, CALIFORNIA, PURSUANT TO ITS
RESOLUTION NO. 88-10-2, DOES HEREBY ACCEPT ON BEHALF OF SAID DISTRICT THE EASEMENTS
FOR SEWER, WATER, AND ACCESS PURPOSES, AS DEDICATED AND AS SHOWN ON THIS TRACT MAP,
BY AND BETWEEN THE SANTA MARGARITA WATER DISTRICT AND DMB LADERA, L.L.C., AND
DOES HEREBY CERTIFY THAT THE GRANTEE CONSENTS TO THE RECORDATION OF SAID TRACT.*[Signature]*
DANIEL R. FEROWS, CHIEF ENGINEER
SANTA MARGARITA WATER DISTRICT.

AUTOMATIC FIRE SPRINKLER NOTE:

ALL COMMERCIAL STRUCTURES GREATER THAN 6,000 SQUARE FEET; ALL MULTIFAMILY RESIDENTIAL
STRUCTURES; ALL SINGLE-FAMILY STRUCTURES EXCEEDING 5,500 SQUARE FEET; AND ALL STRUCTURES
EXCEEDING FIRE DEPARTMENT ACCESS REQUIREMENTS SHALL BE PROTECTED BY AN AUTOMATIC
SPRINKLER SYSTEM.

SPECIAL FIRE PROTECTION NOTE:

PROPERTY IS IN A SPECIAL FIRE PROTECTION AREA AND MUST MEET ALL REQUIREMENTS
FOR DEVELOPMENT WITHIN THE AREA.
PROPERTY IS TOTALLY EXCLUDED FROM A SPECIAL FIRE PROTECTION AREA.

HIGH FIRE HAZARD AREA NOTE:

THE LOTS SHOWN ON THIS MAP ARE IN A HIGH FIRE HAZARD AREA DUE TO
WLD LAND EXPOSURE.

NOTE:

SEE SHEET 2 FOR NOTARY ACKNOWLEDGMENTS AND SIGNATURE OMISSIONS.

SURVEYOR'S STATEMENT:

I HEREBY STATE THAT THIS MAP CONSISTING OF 8 SHEETS, CORRECTLY REPRESENTS A TRUE AND
COMPLETE SURVEY AS SHOWN MADE IN JANUARY, 1999; WAS MADE BY ME OR UNDER MY DIRECTION;
THAT THE MONUMENTS ARE OF THE CHARACTER AND OCCUPY OR WILL OCCUPY THE POSITIONS
INDICATED BY SAID MAP; AND THAT SAID MONUMENTS WILL BE SUFFICIENT TO ENABLE THE
SURVEY TO BE RETRACED.*[Signature]*
JAMES F. GILLEN
COUNTY CLERK-RECORDER
EXPIRATION DATE: 9/30/01

COUNTY SURVEYOR'S STATEMENT:

I HEREBY STATE THAT I HAVE EXAMINED THIS MAP AND HAVE FOUND IT TO BE
SUBSTANTIALLY IN CONFORMANCE WITH THE TENTATIVE MAP AS FILED WITH, AMENDED AND
APPROVED BY THE ORANGE COUNTY SUBDIVISION COMMITTEE; THAT ALL PROVISIONS OF THE
SUBDIVISION MAP ACT AND COUNTY SUBDIVISION REGULATIONS HAVE BEEN COMPLIED WITH
AND I AM SATISFIED SAID MAP IS TECHNICALLY CORRECT.DATED THIS 17TH DAY OF JANUARY, 2001.*[Signature]*
JOHN CANAS, COUNTY SURVEYOR
PLS 4408, EXPIRATION DATE: 9/30/01BY: MICHAEL K. SULLIVAN, DEPUTY
L.S. 6254 EXPIRES 6-30-02

COUNTY TREASURER-TAX COLLECTOR'S CERTIFICATE:

STATE OF CALIFORNIA)
COUNTY OF ORANGE)I HEREBY CERTIFY THAT ACCORDING TO THE RECORDS OF MY OFFICE THERE ARE NO LIENS
AGAINST THE LAND COVERED BY THIS MAP OR ANY PART THEREOF FOR UNPAID STATE,
COUNTY, MUNICIPAL OR LOCAL TAXES OR SPECIAL ASSESSMENTS COLLECTED AS TAXES,
EXCEPT TAXES OR SPECIAL ASSESSMENTS COLLECTED AS TAXES NOT YET PAYABLE.AND DO ALSO HEREBY CERTIFY TO THE RECORDER OF ORANGE COUNTY THAT THE PROVISIONS
OF THE SUBDIVISION MAP ACT HAVE BEEN COMPLIED WITH REGARDING DEPOSITS TO SECURE
THE PAYMENT OF TAXES OR SPECIAL ASSESSMENTS COLLECTED AS TAXES ON THE LAND
COVERED BY THIS MAP.

DATED THIS 12 DAY OF JANUARY, 2001.

JOHN M.W. MOORLACH
COUNTY TREASURER-TAX COLLECTORBY: *[Signature]*
DEPUTY TREASURER-TAX COLLECTOR

CLERK OF THE BOARD OF SUPERVISORS' CERTIFICATE:

STATE OF CALIFORNIA)
COUNTY OF ORANGE)I HEREBY CERTIFY THAT THIS MAP WAS PRESENTED FOR APPROVAL TO THE BOARD OF
SUPERVISORS OF ORANGE COUNTY AT A REGULAR MEETING THEREOF HELD ON THE 26TH DAY
OF JANUARY, 2001, AND THAT THEREUPON SAID BOARD DID, BY AN ORDER DULY PASSED
AND ENTERED, APPROVE SAID MAP AND DID ACCEPT ON BEHALF OF THE PUBLIC, SUBJECT TO
IMPROVEMENTS: THE DEDICATION FOR STREET PURPOSES OF: SIENNA PARKWAY, ~~SELAS ROAD SOUTH~~,
BARBERRY STREET, TUBEROSE STREET, AGAPANTHUS STREET, ~~AND~~ O'NEILL DRIVE, AND CLEOME STREET.

AND DID ALSO ACCEPT ON BEHALF OF THE COUNTY OF ORANGE:

1. THE EASEMENTS FOR SIDEWALK PURPOSES AS DEDICATED.
 2. THE EASEMENTS FOR STORM DRAIN PURPOSES AS DEDICATED.
 3. THE VEHICULAR ACCESS RIGHTS TO SIENNA PARKWAY AS RELEASED AND RELINQUISHED.
- AND DID NOT ACCEPT THE IRREVOCABLE OFFER OF: LOT 4 FOR LOCAL PARK PURPOSES AS DEDICATED.

DATED THIS 33RD DAY OF JANUARY, 2001.*[Signature]*
DARLENE J. BLOOM
CLERK OF THE BOARD OF SUPERVISORS

SHEET 2 OF 8 SHEETS

TRACT NO. 16025

FINAL UNIT OF VESTING
TENTATIVE TRACT NO. 16025

IN UNINCORPORATED TERRITORY OF ORANGE COUNTY, CALIFORNIA

DECEMBER 2000

JAMES F. GILLEN, L.S. 5557

DATE OF SURVEY:
JANUARY 1999

HUITT-ZOLIARS

8 NUMBERED LOTS AND 18 LETTERED LOTS

63.623 ACRES

DMB LADERA, L.L.C.

STATE OF CALIFORNIA)
COUNTY OF ORANGE)SS

ON THIS 21st DAY OF December, 2000, BEFORE ME,
JEANNINE CARTA HANSON, A NOTARY PUBLIC IN AND FOR SAID STATE,
PERSONALLY APPEARED Paul Johnson AND
Stephen C. Schrank, PERSONALLY KNOWN TO ME OR PROVED TO ME
ON THE BASIS OF SATISFACTORY EVIDENCE TO BE THE PERSONS WHOSE NAMES
ARE SUBSCRIBED TO THE WITHIN INSTRUMENT AND ACKNOWLEDGED TO ME THAT
THEY EXECUTED THE SAME IN THEIR AUTHORIZED CAPACITIES, AND THAT BY THEIR
SIGNATURES ON THE INSTRUMENT THE PERSONS, OR THE ENTITY UPON BEHALF
OF WHICH THE PERSONS ACTED, EXECUTED THE INSTRUMENT.

WITNESS MY HAND:

MY COMMISSION EXPIRES FEB. 25, 2003NOTARY PUBLIC IN AND FOR SAID STATE IS IN ORANGE COUNTY.

JEANNINE CARTA HANSON
PRINT NAME

SIGNATURE OMISSIONS:

IN ACCORDANCE WITH THE PROVISIONS OF SECTION 66436(a) (3) OF THE SUBDIVISION
MAP ACT, THE FOLLOWING SIGNATURE HAS BEEN OMITTED:

1. LADERA DEVELOPMENT COMPANY, L.L.C., HOLDER OF OIL, GAS, MINERAL, AND WATER RIGHTS
RECORDED DECEMBER 10, 1996 AS INSTRUMENT NO. 19960624029 OF OFFICIAL RECORDS.

EASEMENT NOTES:

- (A) INDICATES EASEMENT FOR STORM DRAIN PURPOSES DEDICATED TO THE COUNTY OF ORANGE.
(B) INDICATES SIDEWALK EASEMENT DEDICATED TO THE COUNTY OF ORANGE.
(C) INDICATES EASEMENT FOR SEWER, WATER, AND ACCESS PURPOSES DEDICATED TO THE SANTA MARGARITA
WATER DISTRICT.

DMB CONSOLIDATED HOLDINGS, L.L.C.

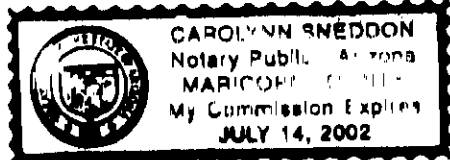
STATE OF Arizona)
COUNTY OF Maricopa)SS

ON THIS 26th DAY OF December, 2000, BEFORE ME,
Carolynn Sneddon, A NOTARY PUBLIC IN AND FOR SAID STATE,
PERSONALLY APPEARED Terry D. Randall PERSONALLY KNOWN TO ME
OR PROVED TO ME ON THE BASIS OF SATISFACTORY EVIDENCE TO BE THE
PERSON WHOSE NAME IS SUBSCRIBED TO THE WITHIN INSTRUMENT AND ACKNOWLEDGED
TO ME THAT HE EXECUTED THE SAME IN HIS AUTHORIZED CAPACITY, AND THAT
BY HIS SIGNATURE ON THE INSTRUMENT THE PERSON, OR THE ENTITY UPON BEHALF
OF WHICH THE PERSON ACTED, EXECUTED THE INSTRUMENT, AS BENEFICIARY.

WITNESS MY HAND:

MY COMMISSION EXPIRES 07-14-02NOTARY PUBLIC IN AND FOR SAID STATE IS IN Maricopa COUNTY.

Carolynn Sneddon
PRINT NAME



DMB CONSOLIDATED HOLDINGS, L.L.C.

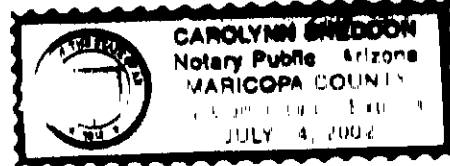
STATE OF Arizona)
COUNTY OF Maricopa)SS

ON THIS 26th DAY OF December, 2000, BEFORE ME,
Carolynn Sneddon, A NOTARY PUBLIC IN AND FOR SAID STATE,
PERSONALLY APPEARED Timothy A. Kachr PERSONALLY KNOWN TO ME
OR PROVED TO ME ON THE BASIS OF SATISFACTORY EVIDENCE TO BE THE
PERSON WHOSE NAME IS SUBSCRIBED TO THE WITHIN INSTRUMENT AND
ACKNOWLEDGED TO ME THAT HE EXECUTED THE SAME IN HIS AUTHORIZED
CAPACITY, AND THAT BY HIS SIGNATURE ON THE INSTRUMENT THE PERSON,
OR THE ENTITY UPON BEHALF OF WHICH THE PERSON ACTED, EXECUTED THE
INSTRUMENT, AS BENEFICIARY.

WITNESS MY HAND :

MY COMMISSION EXPIRES 07-14-02NOTARY PUBLIC IN AND FOR SAID STATE IS IN Maricopa COUNTY.

Carolynn Sneddon
PRINT NAME



SANTA MARGARITA WATER DISTRICT

STATE OF CALIFORNIA)
COUNTY OF ORANGE)SS

ON THIS 22nd DAY OF December, 2000, BEFORE ME,
Lupe Martinez, A NOTARY PUBLIC IN AND FOR SAID STATE,
PERSONALLY APPEARED DANIEL R. FERONS PERSONALLY KNOWN TO ME
OR PROVED TO ME ON THE BASIS OF SATISFACTORY EVIDENCE TO BE THE
PERSON WHOSE NAME IS SUBSCRIBED TO THE WITHIN INSTRUMENT AND ACKNOWLEDGED
TO ME THAT HE EXECUTED THE SAME IN HIS AUTHORIZED CAPACITY, AND THAT
BY HIS SIGNATURE ON THE INSTRUMENT THE PERSON, OR THE ENTITY UPON BEHALF
OF WHICH THE PERSON ACTED, EXECUTED THE INSTRUMENT.

WITNESS MY HAND:

MY COMMISSION EXPIRES 8-13-2002NOTARY PUBLIC IN AND FOR SAID STATE IS IN Orange COUNTY.

Lupe Martinez
PRINT NAME

SHEET 3 OF 8 SHEETS

TRACT NO. 16025

IN UNINCORPORATED TERRITORY OF ORANGE COUNTY, CALIFORNIA

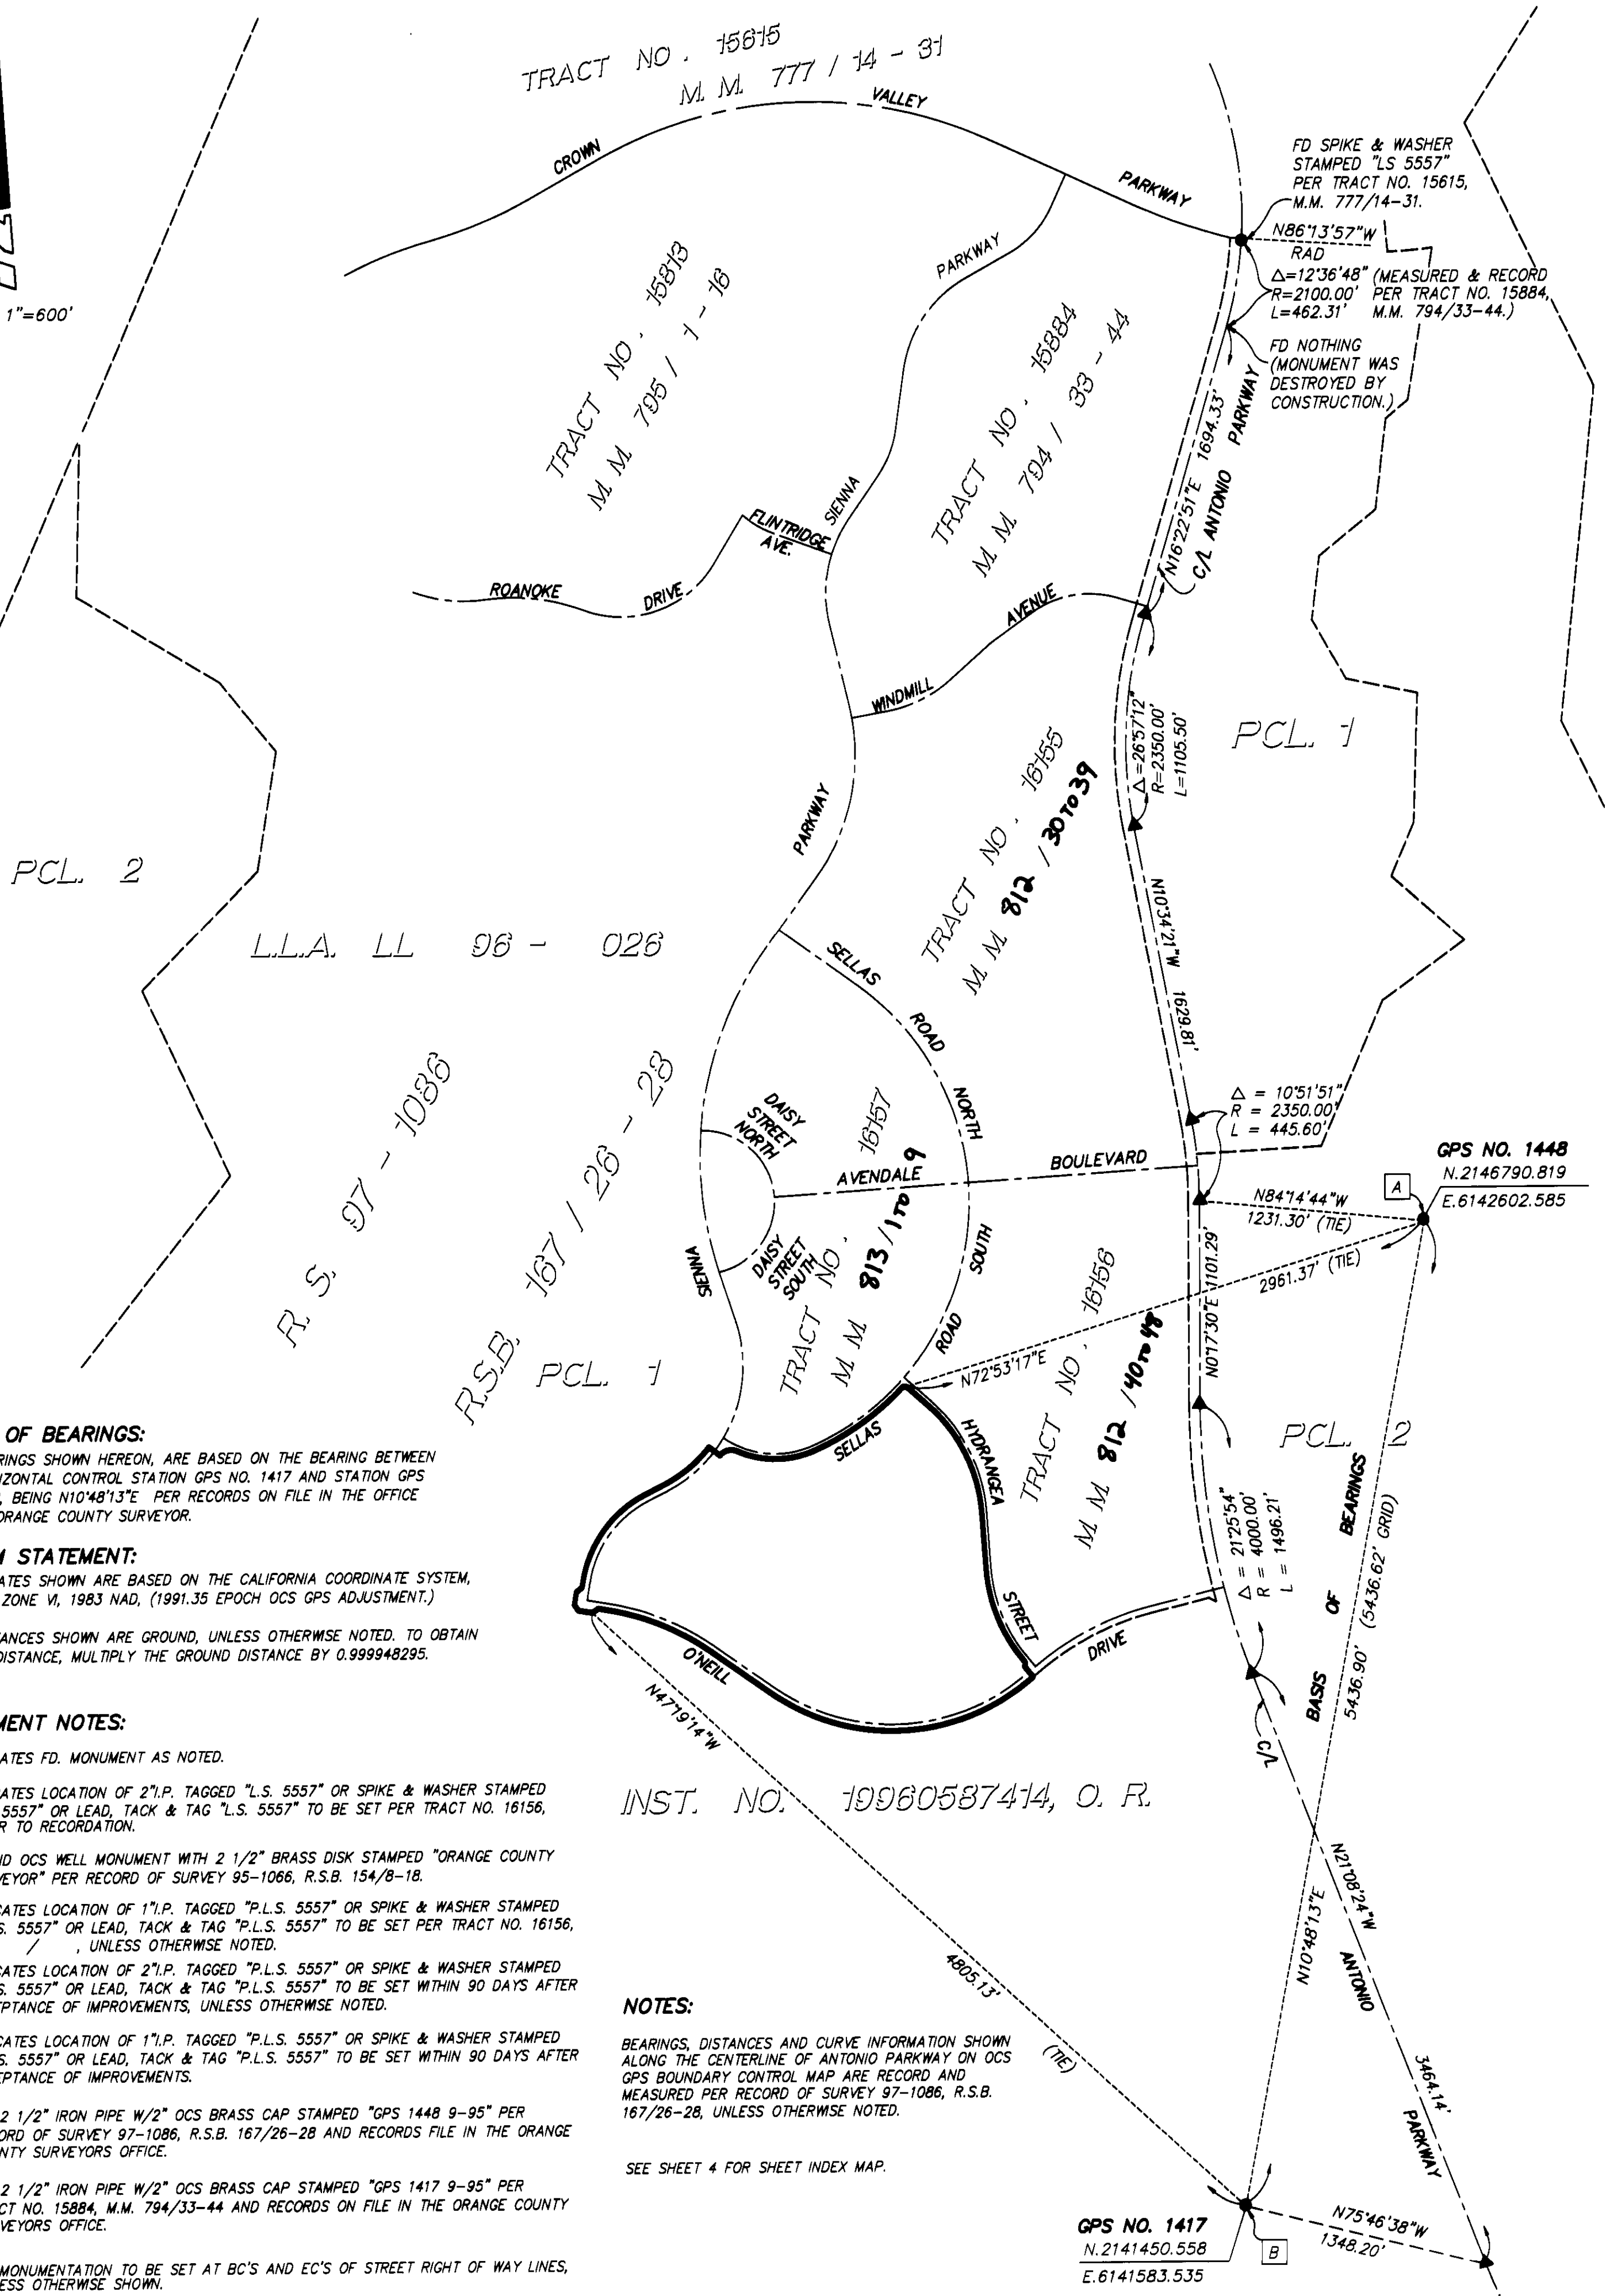
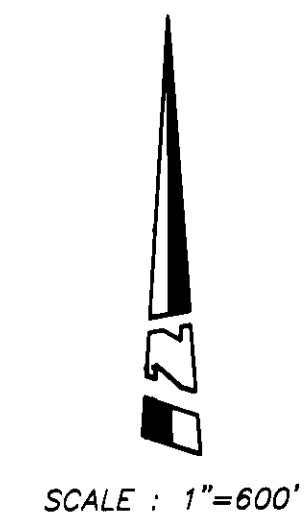
DECEMBER 2000

JAMES F. GILLEN, L.S. 5557

HUITT-ZOLLARS

8 NUMBERED LOTS AND 18 LETTERED LOTS

63.623 ACRES

FINAL UNIT OF VESTING
TENTATIVE TRACT NO. 16025DATE OF SURVEY:
JANUARY 1999

BASIS OF BEARINGS:

THE BEARINGS SHOWN HEREON, ARE BASED ON THE BEARING BETWEEN
OCS HORIZONTAL CONTROL STATION GPS NO. 1417 AND STATION GPS
NO. 1448, BEING N10°48'13"E PER RECORDS ON FILE IN THE OFFICE
OF THE ORANGE COUNTY SURVEYOR.

DATUM STATEMENT:

COORDINATES SHOWN ARE BASED ON THE CALIFORNIA COORDINATE SYSTEM,
(CCS83) ZONE VI, 1983 NAD, (1991.35 EPOCH OCS GPS ADJUSTMENT.)

ALL DISTANCES SHOWN ARE GROUND, UNLESS OTHERWISE NOTED. TO OBTAIN
A GRID DISTANCE, MULTIPLY THE GROUND DISTANCE BY 0.999948295.

MONUMENT NOTES:

- INDICATES FD. MONUMENT AS NOTED.
- INDICATES LOCATION OF 2" I.P. TAGGED "L.S. 5557" OR SPIKE & WASHER STAMPED "L.S. 5557" OR LEAD, TACK & TAG "L.S. 5557" TO BE SET PER TRACT NO. 16156, PRIOR TO RECORDATION.
- ▲ FOUND OCS WELL MONUMENT WITH 2 1/2" BRASS DISK STAMPED "ORANGE COUNTY SURVEYOR" PER RECORD OF SURVEY 95-1066, R.S.B. 154/8-18.
- △ INDICATES LOCATION OF 1" I.P. TAGGED "P.L.S. 5557" OR SPIKE & WASHER STAMPED "P.L.S. 5557" OR LEAD, TACK & TAG "P.L.S. 5557" TO BE SET PER TRACT NO. 16156, M.M. / , UNLESS OTHERWISE NOTED.
- INDICATES LOCATION OF 2" I.P. TAGGED "P.L.S. 5557" OR SPIKE & WASHER STAMPED "P.L.S. 5557" OR LEAD, TACK & TAG "P.L.S. 5557" TO BE SET WITHIN 90 DAYS AFTER ACCEPTANCE OF IMPROVEMENTS, UNLESS OTHERWISE NOTED.
- INDICATES LOCATION OF 1" I.P. TAGGED "P.L.S. 5557" OR SPIKE & WASHER STAMPED "P.L.S. 5557" OR LEAD, TACK & TAG "P.L.S. 5557" TO BE SET WITHIN 90 DAYS AFTER ACCEPTANCE OF IMPROVEMENTS.
- [A] FD. 2 1/2" IRON PIPE W/2" OCS BRASS CAP STAMPED "GPS 1448 9-95" PER RECORD OF SURVEY 97-1086, R.S.B. 167/26-28 AND RECORDS FILE IN THE ORANGE COUNTY SURVEYORS OFFICE.
- [B] FD. 2 1/2" IRON PIPE W/2" OCS BRASS CAP STAMPED "GPS 1417 9-95" PER TRACT NO. 15884, M.M. 794/33-44 AND RECORDS ON FILE IN THE ORANGE COUNTY SURVEYORS OFFICE.

NO MONUMENTATION TO BE SET AT BC'S AND EC'S OF STREET RIGHT OF WAY LINES,
UNLESS OTHERWISE SHOWN.

NOTES:

BEARINGS, DISTANCES AND CURVE INFORMATION SHOWN
ALONG THE CENTERLINE OF ANTONIO PARKWAY ON OCS
GPS BOUNDARY CONTROL MAP ARE RECORD AND
MEASURED PER RECORD OF SURVEY 97-1086, R.S.B.
167/26-28, UNLESS OTHERWISE NOTED.

SEE SHEET 4 FOR SHEET INDEX MAP.

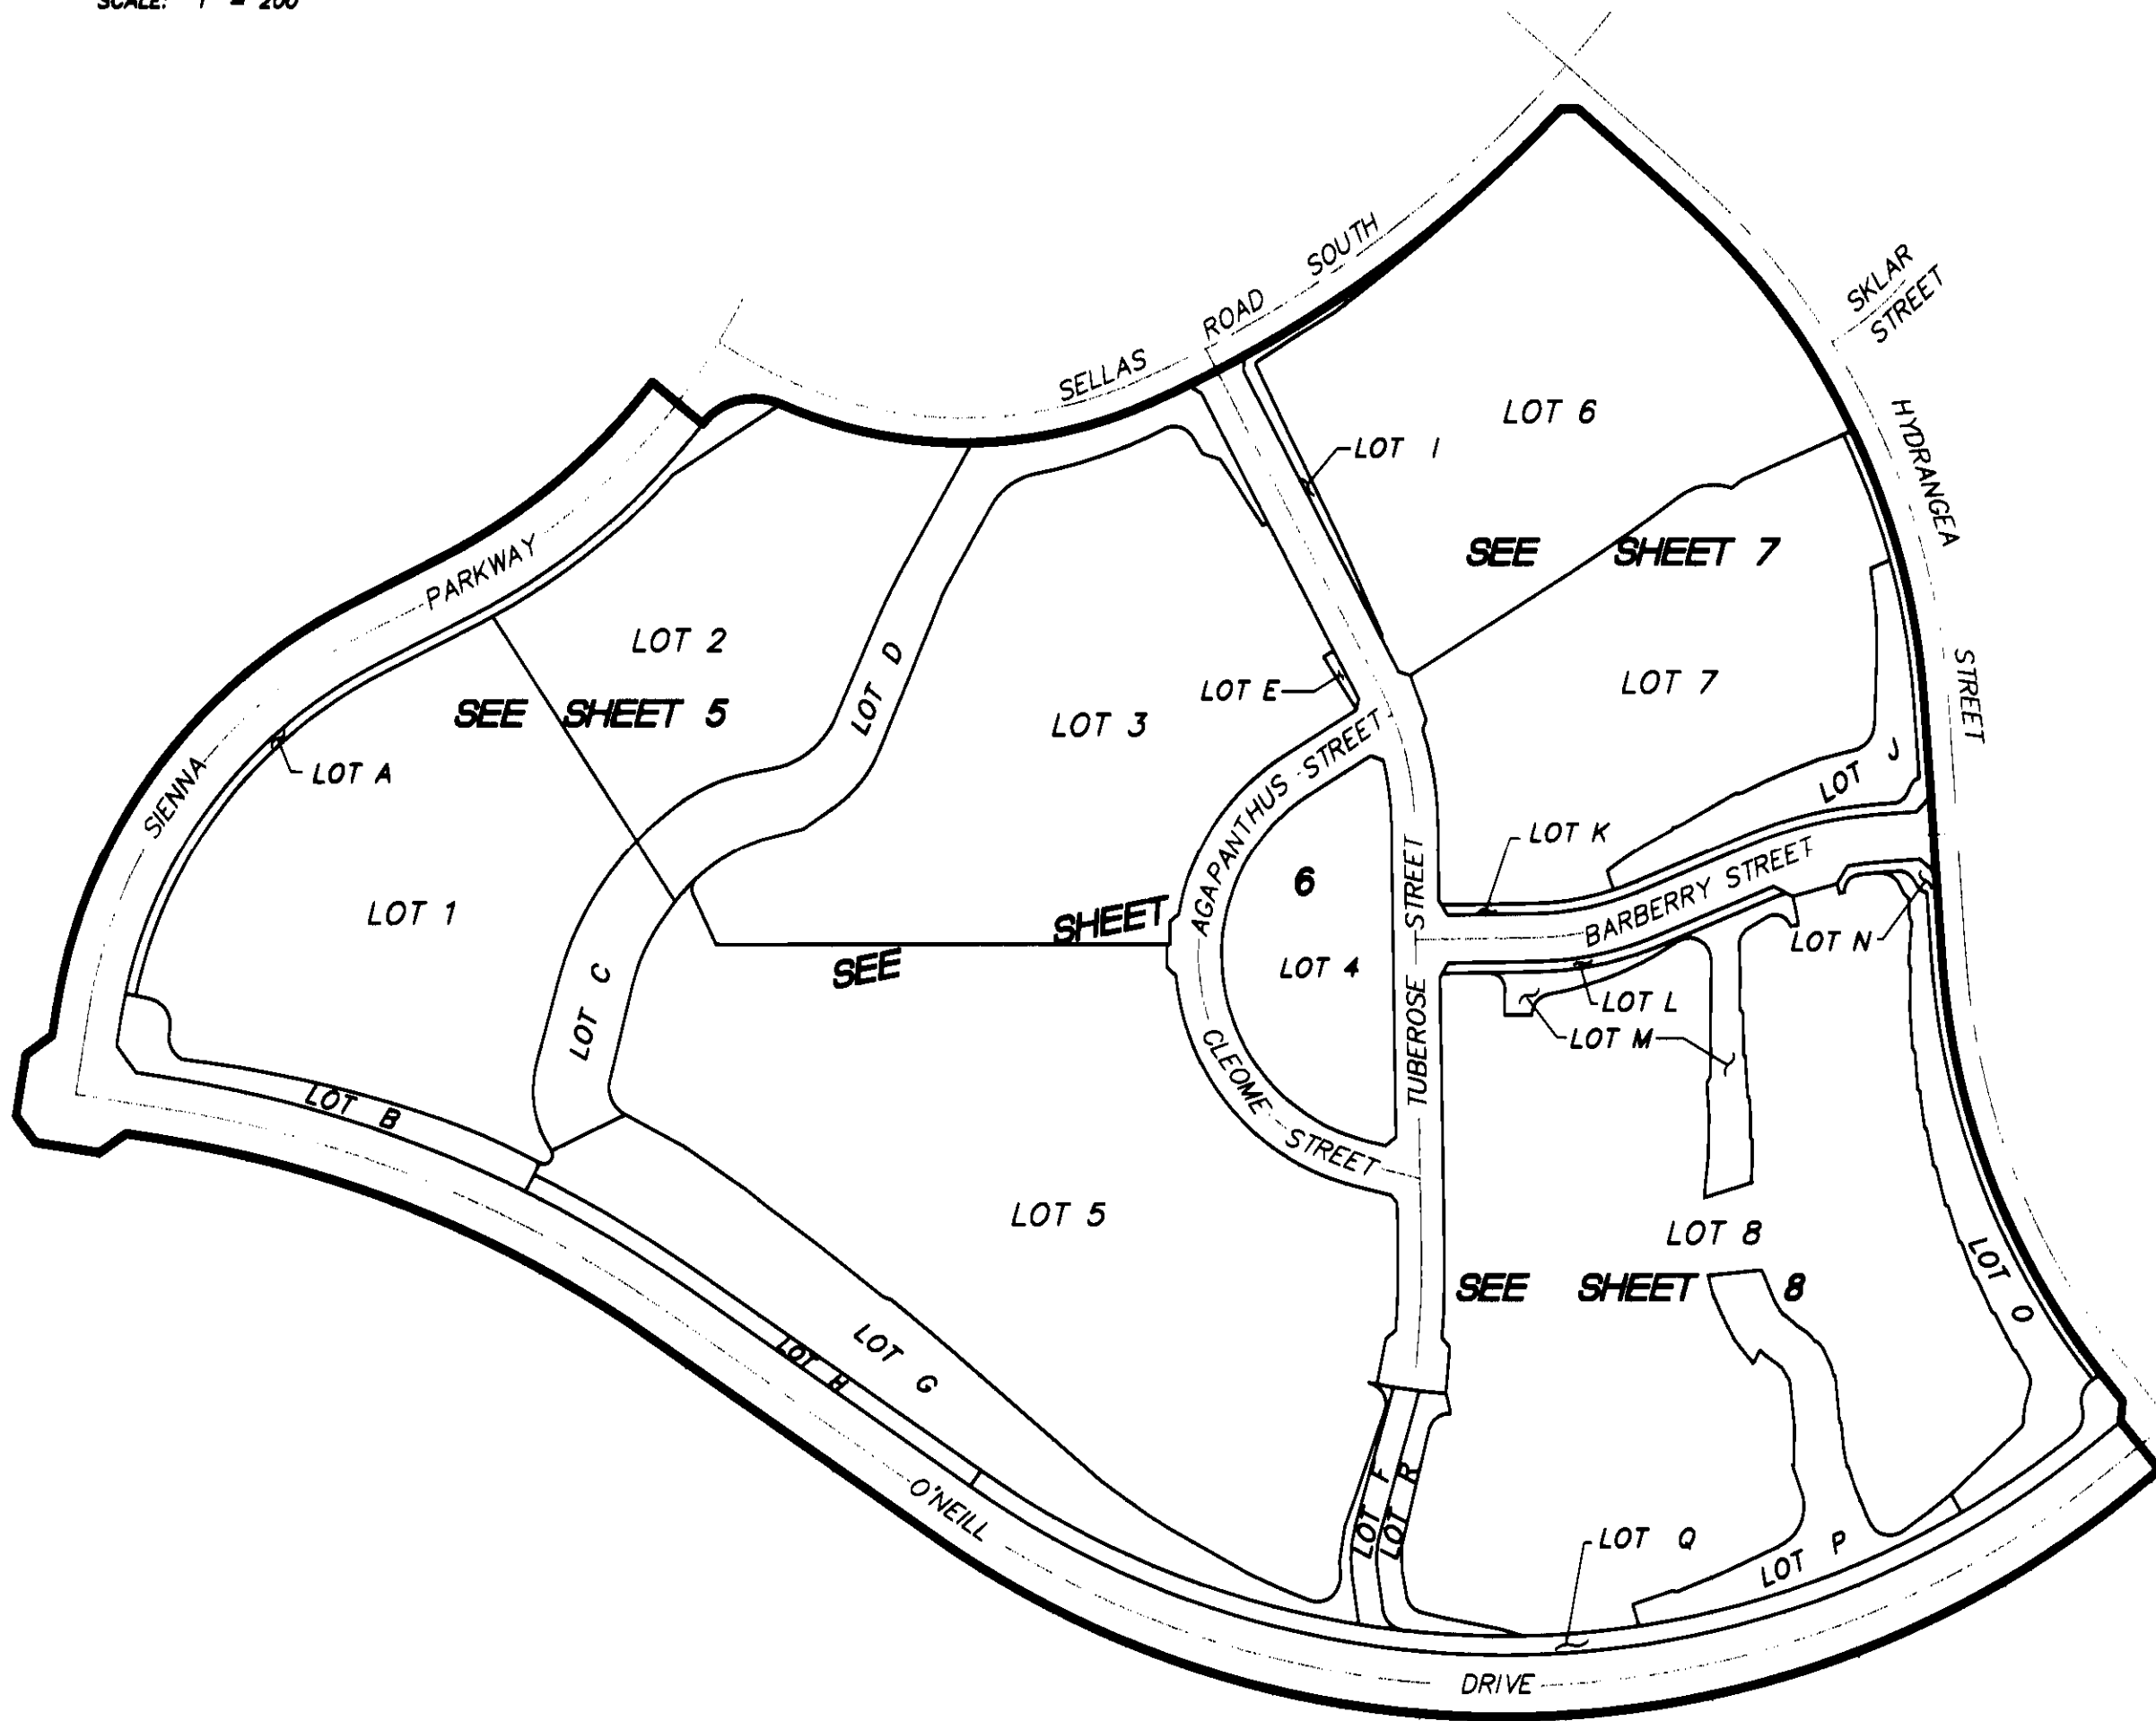
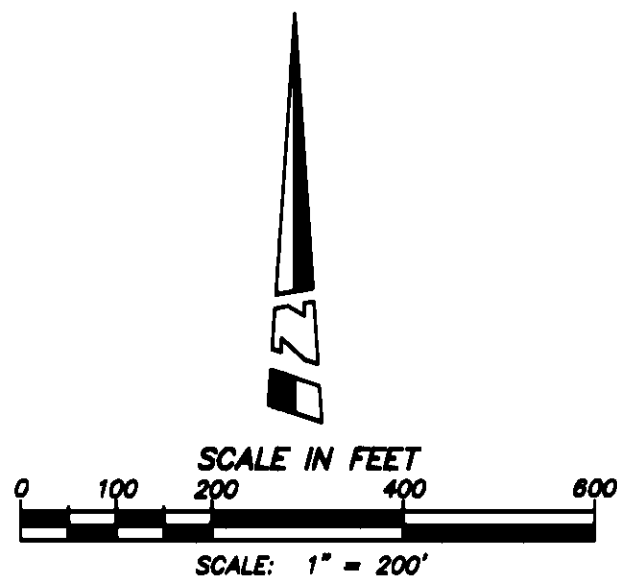
OCS GPS BOUNDARY CONTROL MAP

SHEET 4 OF 8 SHEETS

FINAL UNIT OF VESTING TENTATIVE
TRACT NO. 16025

DATE OF SURVEY:
JANUARY 1999

TRACT NO. 16025
IN UNINCORPORATED TERRITORY OF ORANGE COUNTY, CALIFORNIA
DECEMBER 2000 JAMES F. GILLEN, L.S. 5557
HUITT-ZOLLARS
8 NUMBERED LOTS AND 18 LETTERED LOTS 63.623 ACRES



SHEET INDEX MAP

SHEET 5 OF 8 SHEETS

FINAL UNIT OF VESTING
TENTATIVE TRACT NO. 16025DATE OF SURVEY:
JANUARY 1999**TRACT NO. 16025**

IN UNINCORPORATED TERRITORY OF ORANGE COUNTY, CALIFORNIA

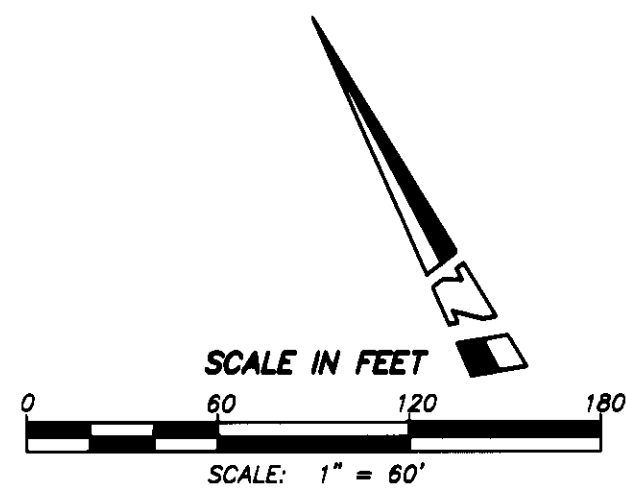
DECEMBER 2000

JAMES F. GILLEN, L.S. 5557

HUITT-ZOLLARS

8 NUMBERED LOTS AND 18 LETTERED LOTS

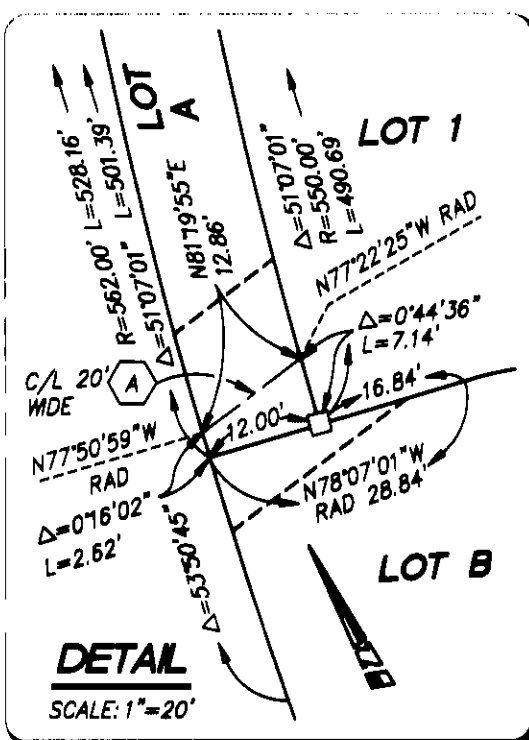
63.623 ACRES

TRACT NO. 16157
M. M. 813 / 1 to 9**NOTES:**

SEE SHEET 2 FOR EASEMENT NOTES.

SEE SHEET 3 FOR BASIS OF BEARINGS, DATUM STATEMENT,
MONUMENT NOTES AND OCS GPS BOUNDARY CONTROL MAP.

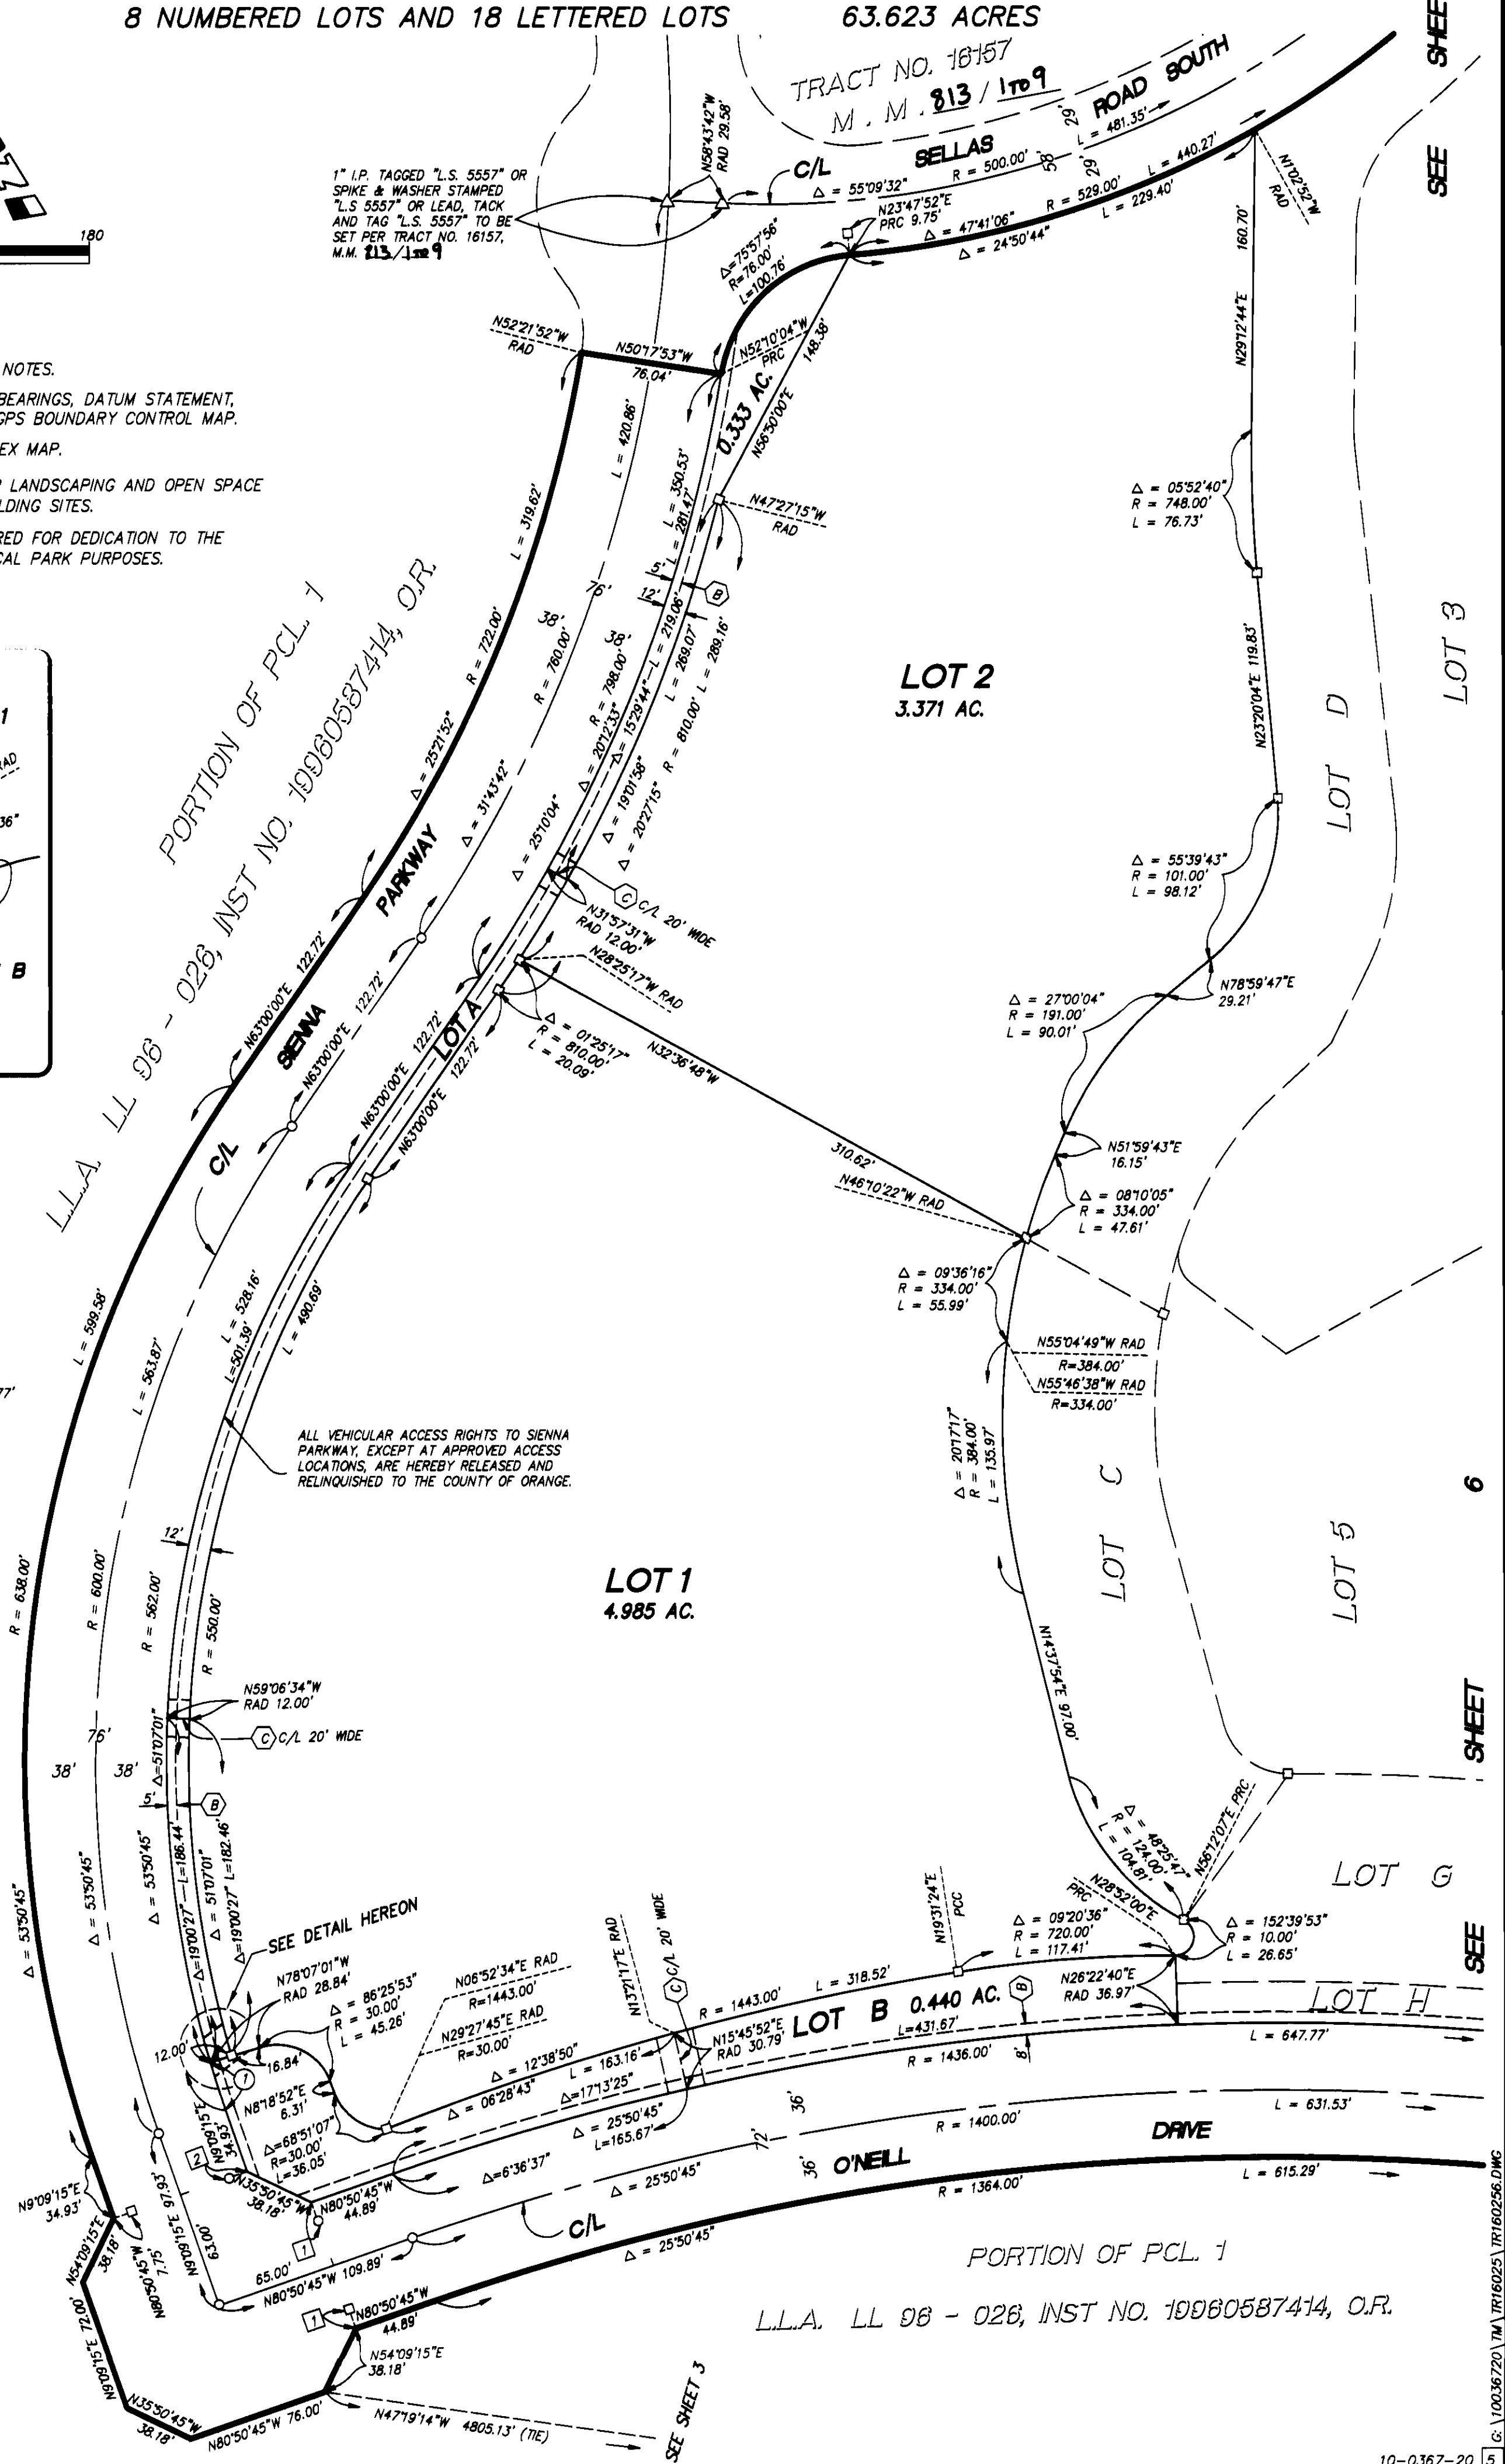
SEE SHEET 4 FOR SHEET INDEX MAP.

LOTS A THROUGH R ARE FOR LANDSCAPING AND OPEN SPACE
AND ARE NOT SEPARATE BUILDING SITES.LOT 4 IS IRREVOCABLY OFFERED FOR DEDICATION TO THE
COUNTY OF ORANGE FOR LOCAL PARK PURPOSES.**CURVE DATA:**
(THIS SHEET ONLY)① $\Delta = 02^{\circ}43'44''$ $R = 562.00'$ $L = 26.77'$ **COURSE DATA:**
(THIS SHEET ONLY)

- | | |
|---|-------------------|
| 1 | N09°09'15"E 7.75' |
| 2 | N80°50'45"W 7.75' |

ALL VEHICULAR ACCESS RIGHTS TO SIENNA
PARKWAY, EXCEPT AT APPROVED ACCESS
LOCATIONS, ARE HEREBY RELEASED AND
RELINQUISHED TO THE COUNTY OF ORANGE.

SEE DETAIL HEREON



SEE SHEET 6

LOT 3

6

SHEET

SEE

LOT 6

SEE SHEET 3

5

812

26

SHEET 6 OF 8 SHEETS

TRACT NO. 16025

IN UNINCORPORATED TERRITORY OF ORANGE COUNTY, CALIFORNIA

DECEMBER 2000

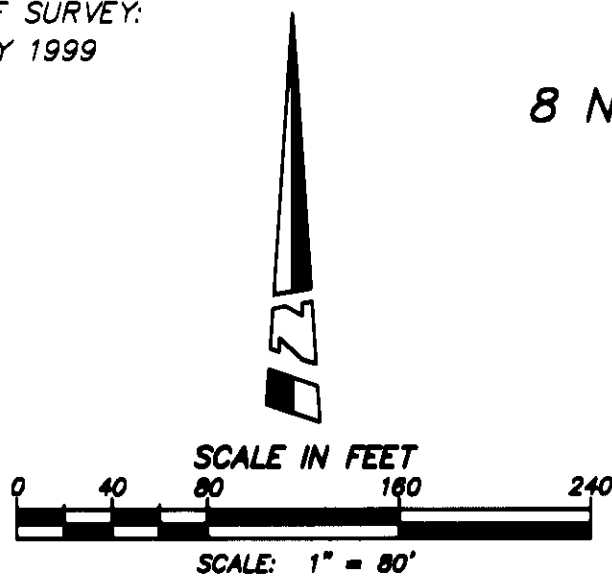
JAMES F. GILLEN, L.S. 5557

FINAL UNIT OF VESTING
TENTATIVE TRACT NO. 16025DATE OF SURVEY:
JANUARY 1999

HUITT-ZOLLARS

8 NUMBERED LOTS AND 18 LETTERED LOTS

63.623 ACRES

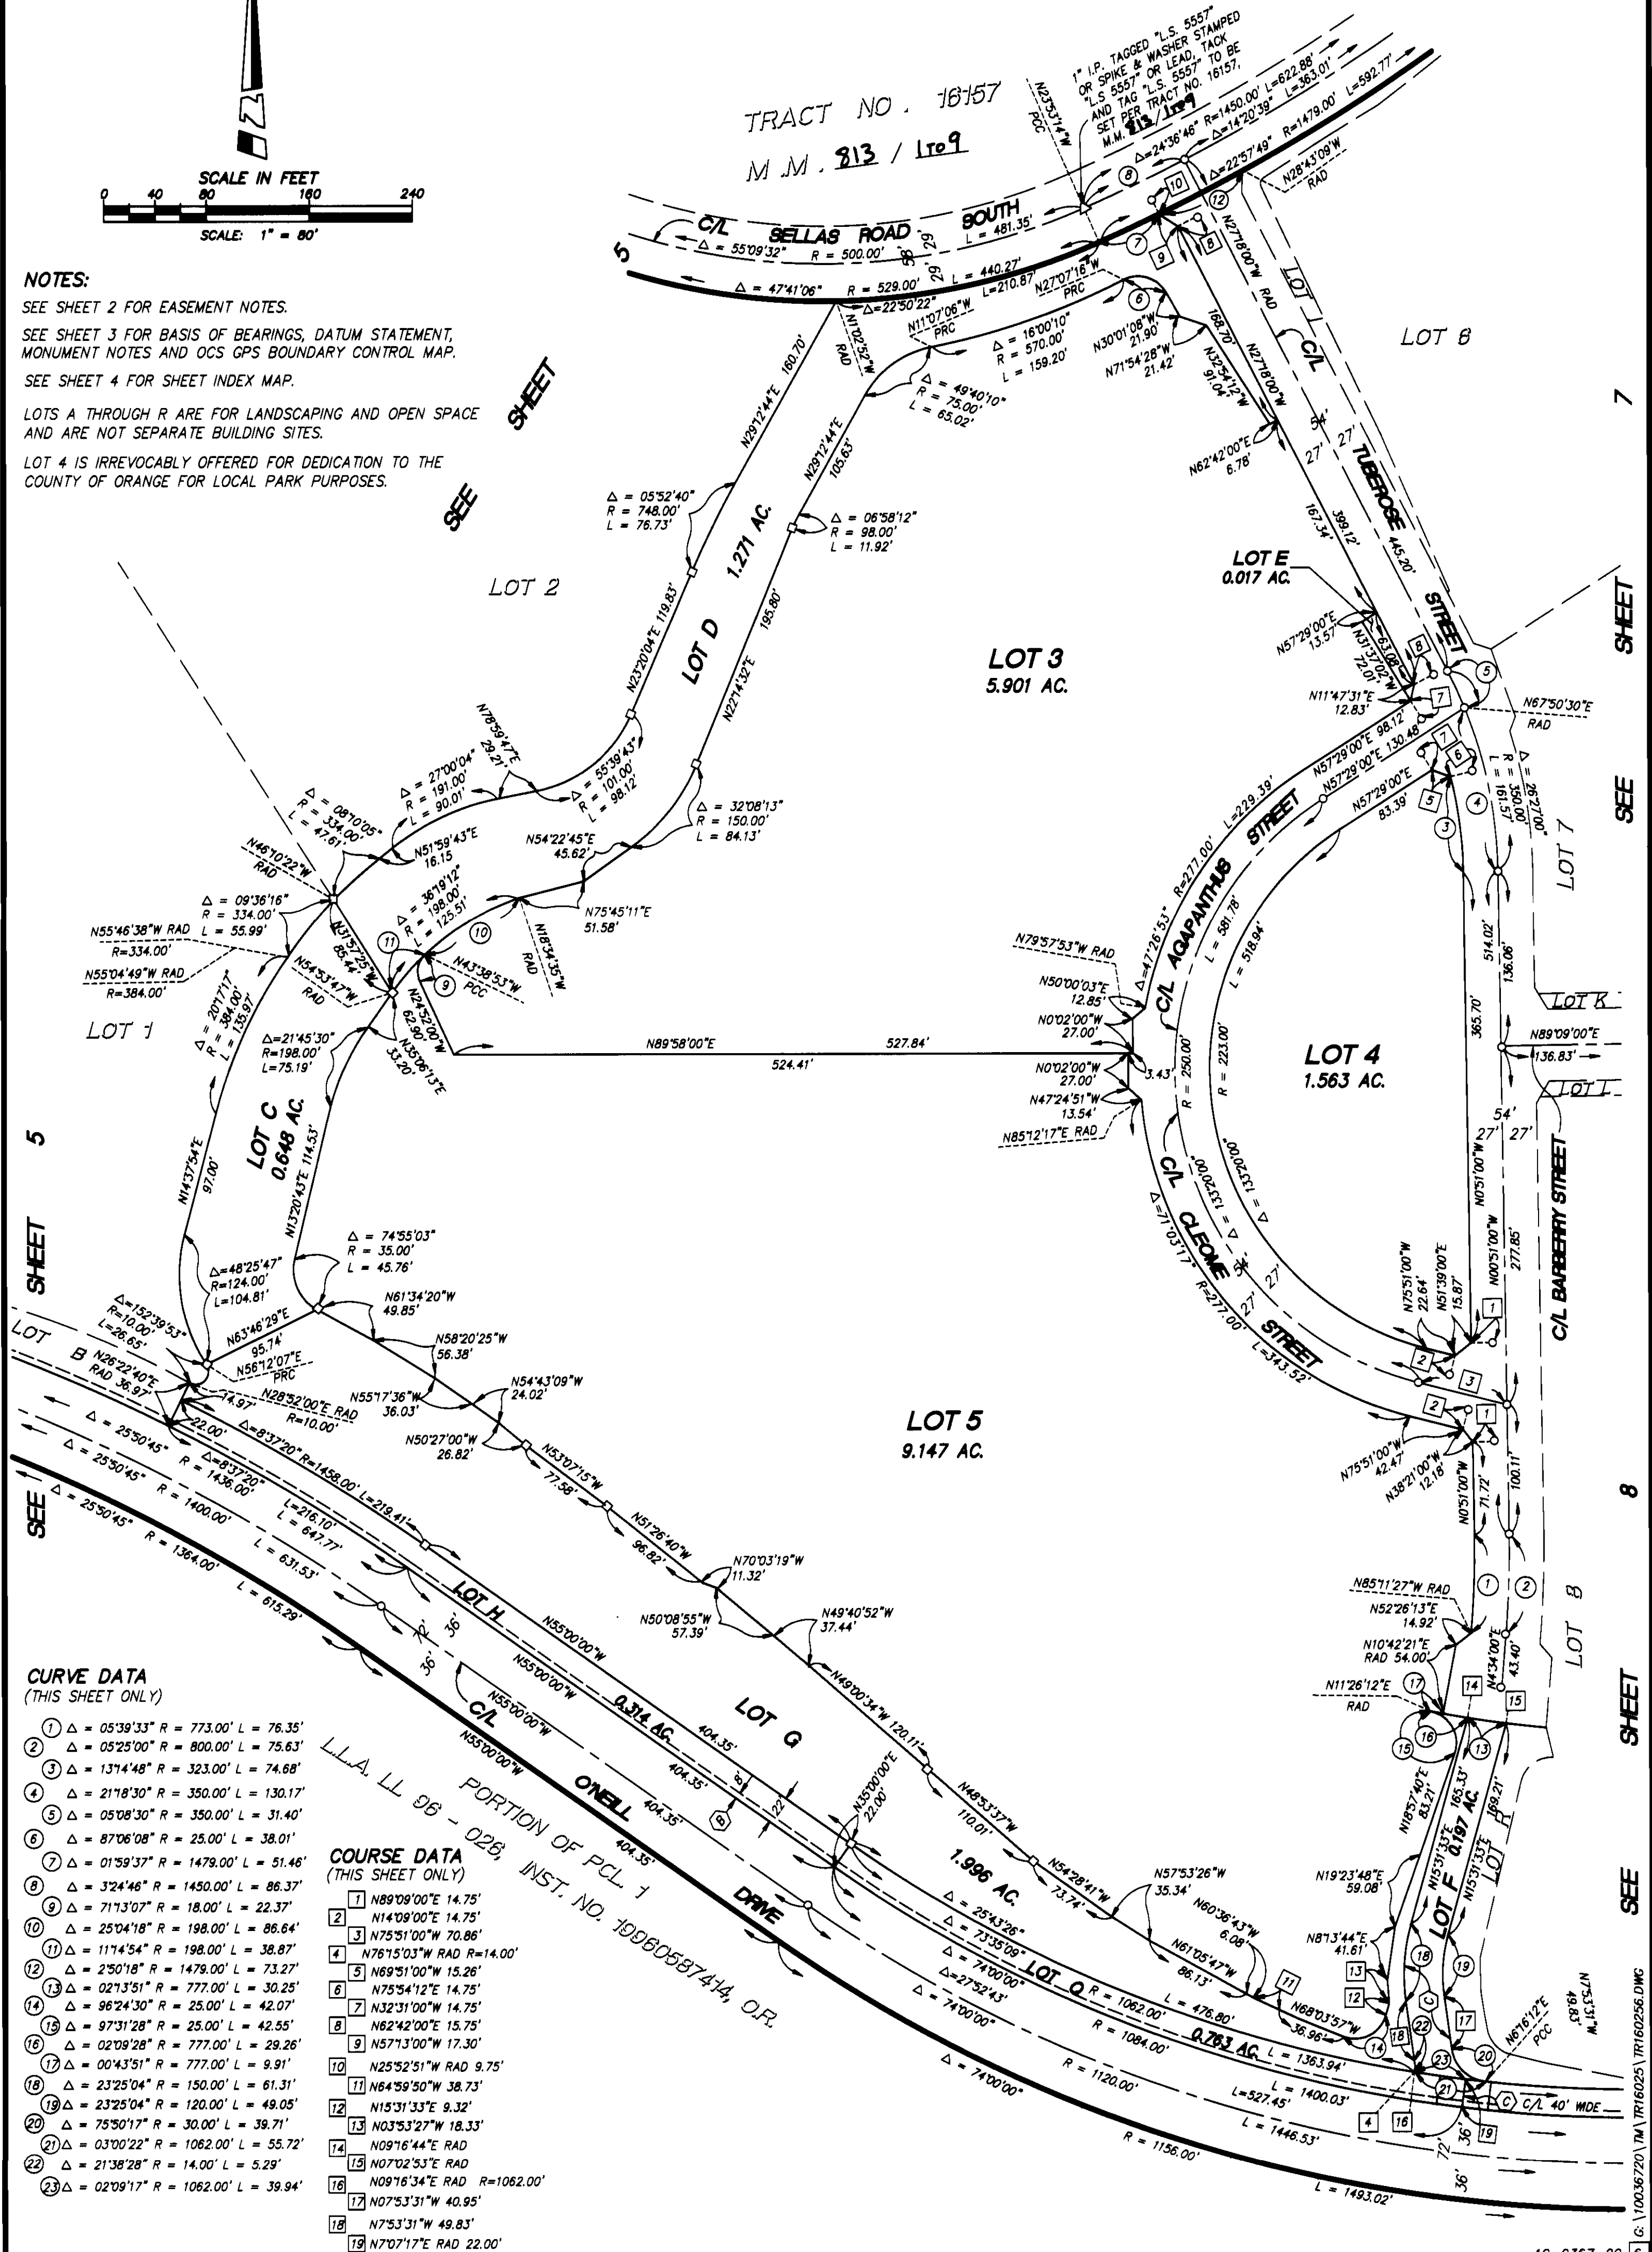


NOTES:

SEE SHEET 2 FOR EASEMENT NOTES.

SEE SHEET 3 FOR BASIS OF BEARINGS, DATUM STATEMENT,
MONUMENT NOTES AND OCS GPS BOUNDARY CONTROL MAP.

SEE SHEET 4 FOR SHEET INDEX MAP.

LOTS A THROUGH R ARE FOR LANDSCAPING AND OPEN SPACE
AND ARE NOT SEPARATE BUILDING SITES.LOT 4 IS IRREVOCABLY OFFERED FOR DEDICATION TO THE
COUNTY OF ORANGE FOR LOCAL PARK PURPOSES.CURVE DATA
(THIS SHEET ONLY)

- ① $\Delta = 05^{\circ}39'33''$ R = 773.00' L = 76.35'
- ② $\Delta = 05^{\circ}25'00''$ R = 800.00' L = 75.63'
- ③ $\Delta = 13^{\circ}14'48''$ R = 323.00' L = 74.68'
- ④ $\Delta = 21^{\circ}18'30''$ R = 350.00' L = 130.17'
- ⑤ $\Delta = 05^{\circ}08'30''$ R = 350.00' L = 31.40'
- ⑥ $\Delta = 87^{\circ}06'08''$ R = 25.00' L = 38.01'
- ⑦ $\Delta = 01^{\circ}59'37''$ R = 1479.00' L = 51.46'
- ⑧ $\Delta = 3^{\circ}24'46''$ R = 1450.00' L = 86.37'
- ⑨ $\Delta = 71^{\circ}37'07''$ R = 18.00' L = 22.37'
- ⑩ $\Delta = 25^{\circ}04'18''$ R = 198.00' L = 86.64'
- ⑪ $\Delta = 11^{\circ}14'54''$ R = 198.00' L = 38.87'
- ⑫ $\Delta = 2^{\circ}50'18''$ R = 1479.00' L = 73.27'
- ⑬ $\Delta = 02^{\circ}13'51''$ R = 777.00' L = 30.25'
- ⑭ $\Delta = 96^{\circ}24'30''$ R = 25.00' L = 42.07'
- ⑮ $\Delta = 97^{\circ}31'28''$ R = 25.00' L = 42.55'
- ⑯ $\Delta = 02^{\circ}09'28''$ R = 777.00' L = 29.26'
- ⑰ $\Delta = 00^{\circ}43'51''$ R = 777.00' L = 9.91'
- ⑱ $\Delta = 23^{\circ}25'04''$ R = 150.00' L = 61.31'
- ⑲ $\Delta = 23^{\circ}25'04''$ R = 120.00' L = 49.05'
- ⑳ $\Delta = 75^{\circ}50'17''$ R = 30.00' L = 39.71'
- ㉑ $\Delta = 03^{\circ}00'22''$ R = 1062.00' L = 55.72'
- ㉒ $\Delta = 21^{\circ}38'28''$ R = 14.00' L = 5.29'
- ㉓ $\Delta = 02^{\circ}09'17''$ R = 1062.00' L = 39.94'

COURSE DATA
(THIS SHEET ONLY)

- 1 N89°09'00"E 14.75'
- 2 N14°09'00"E 14.75'
- 3 N75°51'00"W 70.86'
- 4 N76°15'03"W RAD R=14.00'
- 5 N69°51'00"W 15.26'
- 6 N75°54'12"E 14.75'
- 7 N32°31'00"W 14.75'
- 8 N62°42'00"E 15.75'
- 9 N57°13'00"W 17.30'
- 10 N25°52'51"W RAD 9.75'
- 11 N64°59'50"W 38.73'
- 12 N15°31'33"E 9.32'
- 13 N03°53'27"W 18.33'
- 14 N09°16'44"E RAD
- 15 N07°02'53"E RAD
- 16 N09°16'34"E RAD R=1062.00'
- 17 N07°53'31"W 40.95'
- 18 N7°53'31"W 49.83'
- 19 N7°07'17"E RAD 22.00'

SHEET 7 OF 8 SHEETS

TRACT NO. 16025

IN UNINCORPORATED TERRITORY OF ORANGE COUNTY, CALIFORNIA

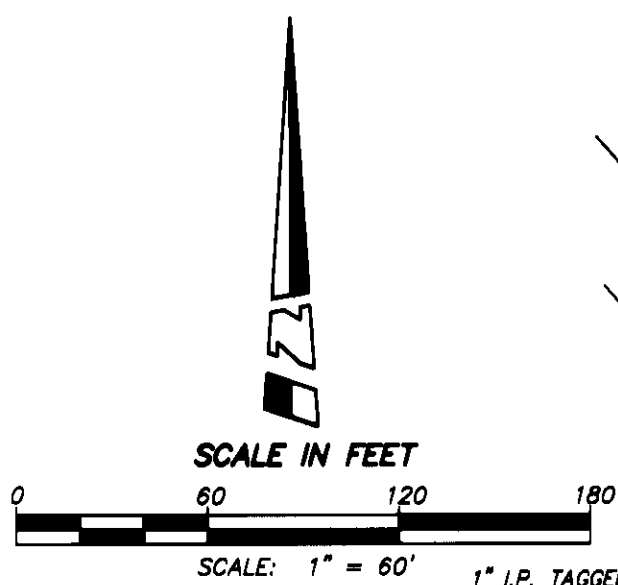
DECEMBER 2000

JAMES F. GILLEN, L.S. 5557

HUITT-ZOLLARS

8 NUMBERED LOTS AND 18 LETTERED LOTS

63.623 ACRES

FINAL UNIT OF VESTING
TENTATIVE TRACT NO. 16025DATE OF SURVEY:
JANUARY 1999

1" I.P. TAGGED "L.S. 5557" OR SPIKE & WASHER STAMPED "L.S. 5557" OR LEAD, TACK AND TAG "L.S. 5557" TO BE SET PER TRACT NO. 16157, M.M. 213/159

2" I.P. TAGGED "P.L.S. 5557" OR SPIKE & WASHER STAMPED "P.L.S. 5557" OR LEAD, TACK AND TAG "P.L.S. 5557" TO BE SET PER TRACT NO. 16156, M.M. 212/48 to 48

SEE SHEET 3

TRACT
M.M.TRACT
NO. 81216156
40 to 48LOT 6
5.446 AC.LOT 7
4.253 AC.CURVE DATA
(THIS SHEET ONLY)

- ① $\Delta = 44^\circ 18' 12''$ R = 18.00' L = 13.92'
- ② $\Delta = 62^\circ 05' 42''$ R = 18.00' L = 19.51'
- ③ $\Delta = 82^\circ 16' 13''$ R = 5.00' L = 7.18'
- ④ $\Delta = 73^\circ 55' 09''$ R = 32.00' L = 41.28'
- ⑤ $\Delta = 02^\circ 50' 18''$ R = 1479.00' L = 73.27'

COURSE DATA
(THIS SHEET ONLY)

- 1 N356°00'W 7.75'
- 2 N41°04'00'E 24.04'
- 3 N21°43'30"W RAD
- 4 N23°58'18"E 10.01'
- 5 N86°04'00"E 19.64'
- 6 N31°18'56"W 19.72'
- 7 N31°18'56"W 13.92'
- 8 N31°18'56"W 5.80'
- 9 N0°51'00"W 7.75'
- 10 N89°09'00"E 14.75'
- 11 N62°42'00"E 15.75'
- 12 N2°37'00"E 17.30'
- 13 N28°43'09"W RAD 9.75'
- 14 N46°51'03"W RAD 9.75'
- 15 N41°30'00"E 10.75'
- 16 N72°01'11"W RAD
- 17 N3°56'00"W 90.00'
- 18 N86°04'00"E 7.75'
- 19 N86°04'00"E 90.64'

NOTES:

SEE SHEET 2 FOR EASEMENT NOTES.

SEE SHEET 3 FOR BASIS OF BEARINGS, DATUM STATEMENT, MONUMENT NOTES AND OCS GPS BOUNDARY CONTROL MAP.

SEE SHEET 4 FOR SHEET INDEX MAP.

LOTS A THROUGH R ARE FOR LANDSCAPING AND OPEN SPACE AND ARE NOT SEPARATE BUILDING SITES.

LOT 4 IS IRREVOCABLY OFFERED FOR DEDICATION TO THE COUNTY OF ORANGE FOR LOCAL PARK PURPOSES.

SHEET 8 OF 8 SHEETS

TRACT NO. 16025

FINAL UNIT OF VESTING
TENTATIVE TRACT NO. 16025

IN UNINCORPORATED TERRITORY OF ORANGE COUNTY, CALIFORNIA

DECEMBER 2000

JAMES F. GILLEN, L.S. 5557

DATE OF SURVEY:
JANUARY 1999

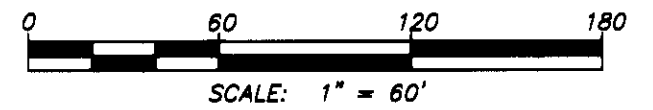
HUITT-ZOLLARS

8 NUMBERED LOTS AND 18 LETTERED LOTS

63.623 ACRES

SEE SHEET 7

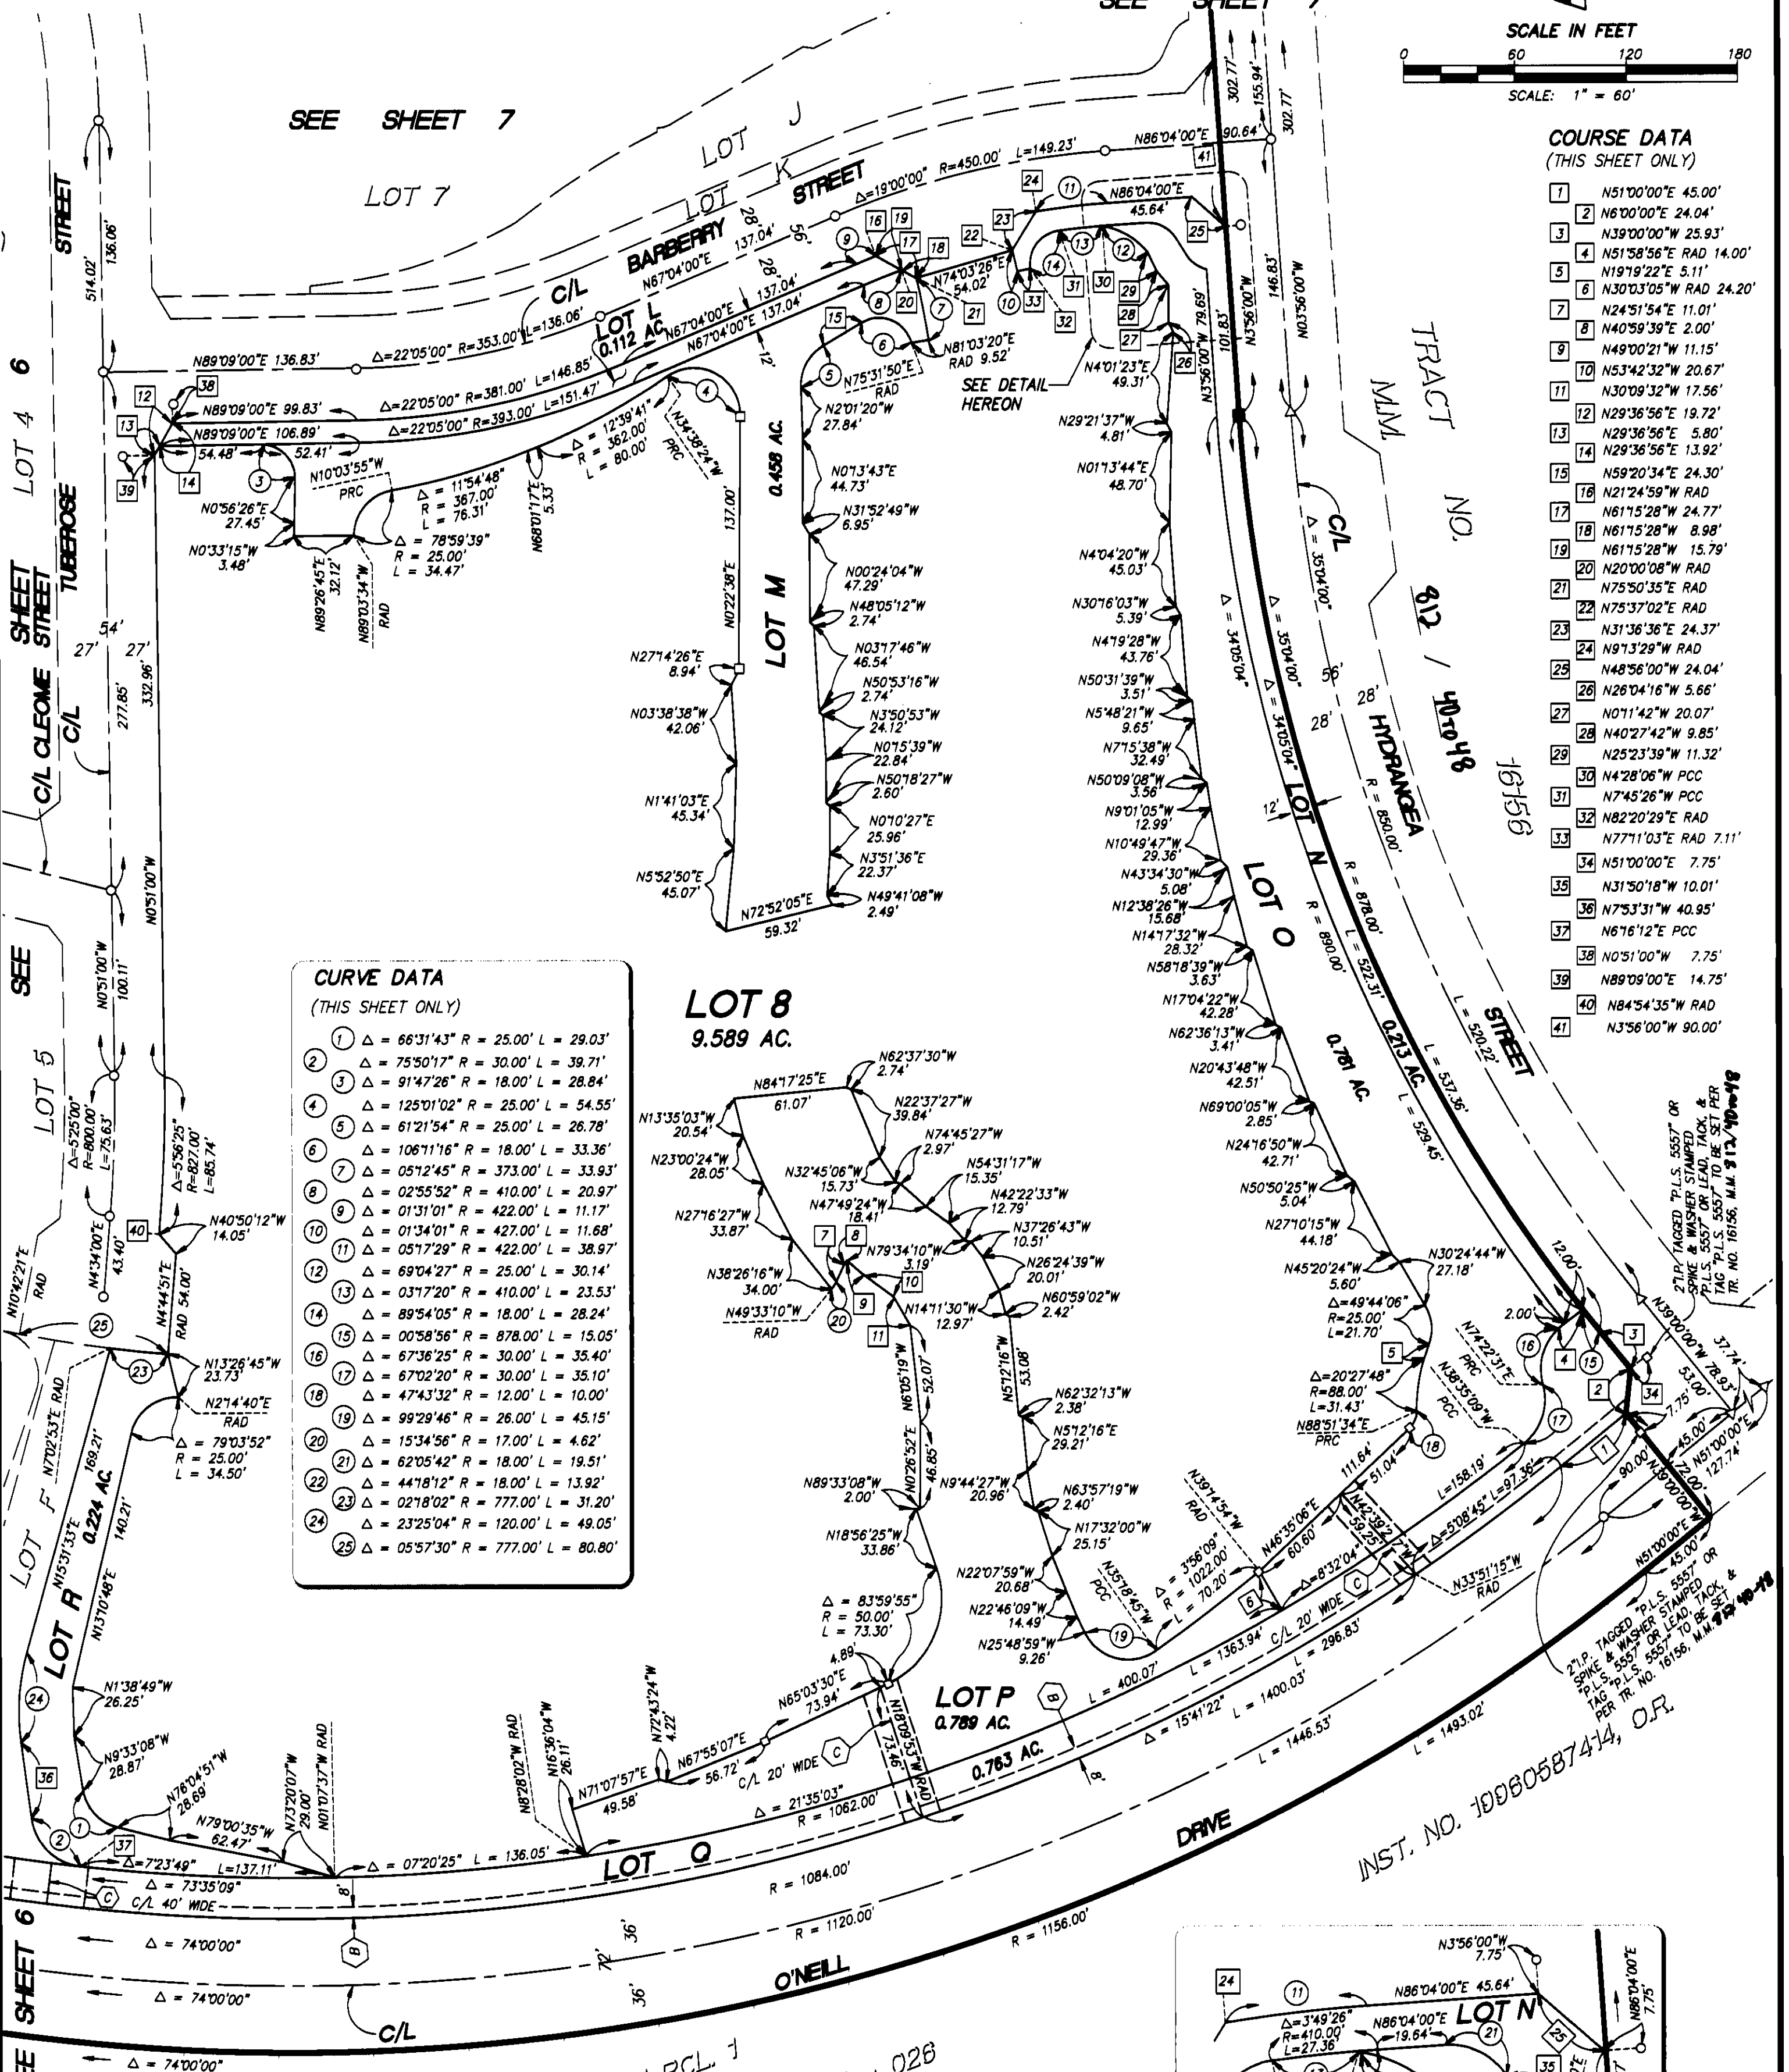
SCALE IN FEET

COURSE DATA
(THIS SHEET ONLY)

1	N51°00'00"E 45.00'
2	N6°00'00"E 24.04'
3	N39°00'00"W 25.93'
4	N51°58'56"E RAD 14.00'
5	N19°19'22"E 5.11'
6	N30°03'05"W RAD 24.20'
7	N24°51'54"E 11.01'
8	N40°59'39"E 2.00'
9	N49°00'21"W 11.15'
10	N53°42'32"W 20.67'
11	N30°09'32"W 17.56'
12	N29°36'56"E 19.72'
13	N29°36'56"E 5.80'
14	N29°36'56"E 13.92'
15	N59°20'34"E 24.30'
16	N21°24'59"W RAD
17	N61°15'28"W 24.77'
18	N61°15'28"W 8.98'
19	N61°15'28"W 15.79'
20	N20°00'08"W RAD
21	N75°50'35"E RAD
22	N75°37'02"E RAD
23	N31°36'36"E 24.37'
24	N9°13'29"W RAD
25	N48°56'00"W 24.04'
26	N26°04'16"W 5.66'
27	N01°14'22"W 20.07'
28	N40°27'42"W 9.85'
29	N25°23'39"W 11.32'
30	N4°28'06"W PCC
31	N7°45'26"W PCC
32	N82°20'29"E RAD
33	N77°11'03"E RAD 7.11'
34	N51°00'00"E 7.75'
35	N31°50'18"W 10.01'
36	N7°53'31"W 40.95'
37	N6°16'12"E PCC
38	N0°51'00"W 7.75'
39	N89°09'00"E 14.75'
40	N84°54'35"W RAD
41	N3°56'00"W 90.00'

CURVE DATA
(THIS SHEET ONLY)

1	Δ = 66°31'43" R = 25.00' L = 29.03'
2	Δ = 75°50'17" R = 30.00' L = 39.71'
3	Δ = 91°47'26" R = 18.00' L = 26.84'
4	Δ = 125°01'02" R = 25.00' L = 54.55'
5	Δ = 61°21'54" R = 25.00' L = 26.78'
6	Δ = 106°11'16" R = 18.00' L = 33.36'
7	Δ = 05°12'45" R = 373.00' L = 33.93'
8	Δ = 02°55'52" R = 410.00' L = 20.97'
9	Δ = 01°31'01" R = 422.00' L = 11.17'
10	Δ = 01°34'01" R = 427.00' L = 11.68'
11	Δ = 05°17'29" R = 422.00' L = 38.97'
12	Δ = 69°04'27" R = 25.00' L = 30.14'
13	Δ = 03°17'20" R = 410.00' L = 23.53'
14	Δ = 89°54'05" R = 18.00' L = 28.24'
15	Δ = 00°58'56" R = 878.00' L = 15.05'
16	Δ = 67°36'25" R = 30.00' L = 35.40'
17	Δ = 67°02'20" R = 30.00' L = 35.10'
18	Δ = 47°43'32" R = 12.00' L = 10.00'
19	Δ = 99°29'46" R = 26.00' L = 45.15'
20	Δ = 15°34'56" R = 17.00' L = 4.62'
21	Δ = 62°05'42" R = 18.00' L = 19.51'
22	Δ = 44°18'12" R = 18.00' L = 13.92'
23	Δ = 02°18'02" R = 777.00' L = 31.20'
24	Δ = 23°25'04" R = 120.00' L = 49.05'
25	Δ = 05°57'30" R = 777.00' L = 80.80'

LOT 8
9.589 AC.

INST. NO. 10980587414, O.R.

NOTES:

SEE SHEET 2 FOR EASEMENT NOTES.

SEE SHEET 3 FOR BASIS OF BEARINGS, DATUM STATEMENT,
MONUMENT NOTES AND OCS GPS BOUNDARY CONTROL MAP.

SEE SHEET 4 FOR SHEET INDEX MAP.

LOTS A THROUGH R ARE FOR LANDSCAPING AND OPEN SPACE
AND ARE NOT SEPARATE BUILDING SITES.LOT 4 IS IRREVOCABLY OFFERED FOR DEDICATION TO THE
COUNTY OF ORANGE FOR LOCAL PARK PURPOSES.