

SHEET 1 OF 5 SHEETS

AREA: 11.997 ACRES GROSS
(BEING ALL OF
TENTATIVE TRACT NO. 16101
NUMBERED LOTS: 54
LETTERED LOTS: 12

BLOCK 5057 MODULE 88, 89, 98, 99

TRACT NO. 16101

IN THE UNINCORPORATED TERRITORY OF THE
COUNTY OF ORANGE, STATE OF CALIFORNIA

BEING A SUBDIVISION OF LOT 1 OF TRACT NO. 16155 AS SHOWN ON A
MAP FILED IN BOOK 812, PAGES 30 THROUGH 39 OF MISCELLANEOUS
MAPS, IN THE OFFICE OF THE COUNTY RECORDER OF SAID COUNTY.

JAMES R. CRAWFORD, L.S. 4965



DATE OF SURVEY: OCTOBER, 2000

ACCEPTED AND FILED AT THE
REQUEST OF
FIRST AMERICAN TITLE INSURANCE CO.

DATE JUNE 29, 2001

TIME 3:47 P.M. FEE \$15.00

INSTRUMENT # 20010437396

BOOK 820 PAGE 21-25 MVM

GARY L. GRANVILLE
COUNTY CLERK-RECORDER

BY DEPUTY

OWNERSHIP CERTIFICATE:

WE THE UNDERSIGNED, BEING ALL PARTIES HAVING ANY RECORD TITLE INTEREST IN THE LAND COVERED BY THIS MAP, DO HEREBY CONSENT TO THE PREPARATION AND RECORDATION OF SAID MAP AS SHOWN WITHIN THE DISTINCTIVE BORDER LINE. WE ALSO HEREBY DEDICATE TO THE PUBLIC FOR STREET PURPOSES: STERLING GLEN, SHELTON COURT, LANESBORO ROAD AND SUTHERLAND DRIVE.

WE ALSO HEREBY DEDICATE TO THE SANTA MARGARITA WATER DISTRICT THE EASEMENT FOR SEWER, WATER AND ACCESS PURPOSES AS SHOWN HEREON WHICH EASEMENT SHALL BE SUBJECT TO THE SAME TERMS AND CONDITIONS AS ARE SHOWN IN THAT CERTAIN EASEMENT RECORDED OCTOBER 6, 1980, IN BOOK 13776, PAGE 341 OF OFFICIAL RECORDS OF THE COUNTY OF ORANGE.

WILLIAM LYON HOMES, INC., A CALIFORNIA CORPORATION,

PRINT NAME: THOMAS J. MITCHELL
PRINT TITLE: SENIOR VICE PRESIDENT

PRINT NAME: THOMAS G. GRABLE
PRINT TITLE: ASSISTANT SECRETARY

DMB LADERA, L.L.C., A DELAWARE LIMITED LIABILITY COMPANY
BENEFICIARY UNDER A DEED OF TRUST RECORDED FEBRUARY 28, 2001, AS INSTRUMENT NO. 20010110730 OF OFFICIAL RECORDS.

BY: RANCHO MISSION VIEJO, L.L.C., A DELAWARE LIMITED LIABILITY COMPANY
AS AGENT OR MANAGER

PRINT NAME: Paul Johnson
PRINT TITLE: VP Community Development

PRINT NAME: Stephen C. Schrank
PRINT TITLE: Executive VP Development

RESIDENTIAL FUNDING CORPORATION, A DELAWARE CORPORATION,
BENEFICIARY UNDER A DEED OF TRUST RECORDED FEBRUARY 28, 2001, AS INSTRUMENT NO. 20010110731 OF OFFICIAL RECORDS.

PRINT NAME: PETER FISCHEN
PRINT TITLE: DIRECTOR

PRINT NAME: MICHAEL F. RIPLEY
PRINT TITLE: DIRECTOR

NOTARY ACKNOWLEDGEMENT FOR WILLIAM LYON HOMES, INC.:

STATE OF CALIFORNIA }
COUNTY OF ORANGE } SS

ON April 12, 2001, BEFORE ME, SUSAN E. MENARD, A NOTARY PUBLIC IN AND FOR SAID STATE PERSONALLY APPEARED THOMAS J. MITCHELL AND THOMAS G. GRABLE PERSONALLY KNOWN TO ME (OR PROVED TO ME ON THE BASIS OF OF SATISFACTORY EVIDENCE) TO BE THE PERSONS WHOSE NAMES ARE SUBSCRIBED TO THE WITHIN INSTRUMENT AND ACKNOWLEDGED TO ME THAT THEY EXECUTED THE SAME IN THEIR AUTHORIZED CAPACITIES AND THAT BY THEIR SIGNATURES ON THE INSTRUMENT THE PERSONS, OR THE ENTITY UPON BEHALF OF WHICH THE PERSONS ACTED EXECUTED THE INSTRUMENT.

WITNESS MY HAND:

NOTARY PUBLIC IN AND FOR SAID STATE
SUSAN E. MENARD
(NAME PRINTED)

MY PRINCIPAL PLACE OF BUSINESS IS
IN NEWPORT BEACH
MY COMMISSION EXPIRES: SEPT. 5, 2003

NOTARY ACKNOWLEDGEMENT FOR DMB LADERA, LLC:

STATE OF California }
COUNTY OF Orange } SS

ON 5-2-01, 2001, BEFORE ME, Tina T. Baker, A NOTARY PUBLIC IN AND FOR SAID STATE PERSONALLY APPEARED Paul Johnson AND Stephen C. Schrank PERSONALLY KNOWN TO ME (OR PROVED TO ME ON THE BASIS OF OF SATISFACTORY EVIDENCE) TO BE THE PERSONS WHOSE NAMES ARE SUBSCRIBED TO THE WITHIN INSTRUMENT AND ACKNOWLEDGED TO ME THAT THEY EXECUTED THE SAME IN THEIR AUTHORIZED CAPACITIES AND THAT BY THEIR SIGNATURES ON THE INSTRUMENT THE PERSONS, OR THE ENTITY UPON BEHALF OF WHICH THE PERSONS ACTED EXECUTED THE INSTRUMENT.

WITNESS MY HAND:

NOTARY PUBLIC IN AND FOR SAID STATE
Tina T. Baker
(NAME PRINTED)


MY PRINCIPAL PLACE OF BUSINESS IS
IN Orange County
MY COMMISSION EXPIRES: 8-29-04

SEE SHEET 2 FOR SANTA MARGARITA WATER DISTRICT SIGNATURE AND ACKNOWLEDGMENT,
SIGNATURE OMISSIONS AND NOTES.

SURVEYOR'S STATEMENT:

I HEREBY STATE THAT THIS MAP CONSISTING OF FIVE (5) SHEETS CORRECTLY REPRESENTS THE TRUE AND COMPLETE SURVEY AS SHOWN MADE IN OCTOBER, 2000; WAS MADE BY ME OR UNDER MY DIRECTION; THAT THE MONUMENTS ARE OF THE CHARACTER AND OCCUPY OR WILL OCCUPY THE POSITIONS INDICATED BY SAID MAP; AND THAT SAID MONUMENTS ARE OR WILL BE SUFFICIENT TO ENABLE THE SURVEY TO BE RETRACED.

JAMES R. CRAWFORD, L.S. 4965
MY LICENSE EXPIRES: DECEMBER 31, 2001

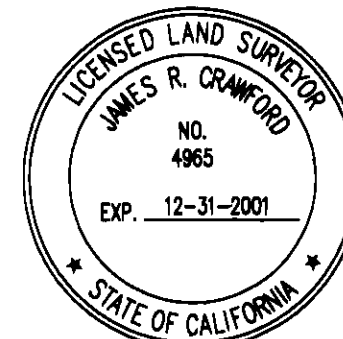


COUNTY SURVEYOR'S STATEMENT:

I HEREBY STATE THAT I HAVE EXAMINED THIS MAP AND FOUND IT TO BE SUBSTANTIALLY IN CONFORMANCE WITH THE TENTATIVE MAP AS FILED WITH, AMENDED AND APPROVED BY THE ORANGE COUNTY SUBDIVISION COMMITTEE; THAT ALL PROVISIONS OF THE SUBDIVISION MAP ACT AND COUNTY SUBDIVISION REGULATIONS HAVE BEEN COMPLIED WITH AND I AM SATISFIED SAID MAP IS TECHNICALLY CORRECT.

DATED THIS 15TH DAY OF JUNE, 2001.

JOHN CANAS, COUNTY SURVEYOR
L.S. 4408 EXPIRATION DATE: 09-30-01 BY: MICHAEL K. SULLIVAN, DEPUTY
L.S. 6254 EXPIRES 6-30-02

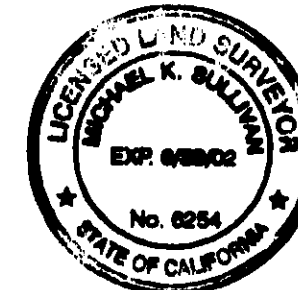

CLERK OF THE BOARD OF SUPERVISORS' CERTIFICATE:

STATE OF CALIFORNIA }
COUNTY OF ORANGE } SS

I HEREBY CERTIFY THAT THIS MAP WAS PRESENTED FOR APPROVAL TO THE BOARD OF SUPERVISORS OF ORANGE COUNTY AT A REGULAR MEETING THEREOF HELD ON THE 26th DAY OF June, 2001, AND THAT THEREUPON SAID BOARD DID, BY AN ORDER DULY PASSED AND ENTERED, APPROVE SAID MAP AND DID ACCEPT ON BEHALF OF THE PUBLIC, SUBJECT TO IMPROVEMENTS; THE DEDICATION FOR STREET PURPOSES OF: STERLING GLEN, SHELTON COURT, LANESBORO ROAD AND SUTHERLAND DRIVE.

AND DID ALSO APPROVE SUBJECT MAP PURSUANT TO THE PROVISIONS OF SECTION 66436(a)(3) OF THE SUBDIVISION MAP ACT.

DATED THIS 26th DAY OF June, 2001.

DARLENE J. BLOOM
CLERK OF THE BOARD OF SUPERVISORS



COUNTY TREASURER-TAX COLLECTOR'S CERTIFICATE:

STATE OF CALIFORNIA }
COUNTY OF ORANGE } SS

I HEREBY CERTIFY THAT ACCORDING TO THE RECORDS OF MY OFFICE, THERE ARE NO LIENS AGAINST THE LAND COVERED BY THIS MAP OR ANY PART THEREOF FOR UNPAID STATE, COUNTY, MUNICIPAL OR LOCAL TAXES OR SPECIAL ASSESSMENTS COLLECTED AS TAXES, EXCEPT TAXES OR SPECIAL ASSESSMENTS COLLECTED AS TAXES NOT YET PAYABLE.

AND DO CERTIFY TO THE RECORDER OF ORANGE COUNTY THAT THE PROVISIONS OF THE SUBDIVISION MAP ACT HAVE BEEN COMPLIED WITH REGARDING DEPOSITS TO SECURE THE PAYMENT OF TAXES OR SPECIAL ASSESSMENTS COLLECTED AS TAXES ON THE LAND COVERED BY THIS MAP.

DATED THIS 22nd DAY OF May, 2001.

JOHN M. W. MOORLACH
COUNTY TREASURER-TAX COLLECTOR

BY
DEPUTY TREASURER-TAX COLLECTOR

NOTARY ACKNOWLEDGEMENT FOR RESIDENTIAL FUNDING CORPORATION:

STATE OF California }
COUNTY OF Los Angeles } SS

ON April 16, 2001, BEFORE ME, Sonia B. Garcia, A NOTARY PUBLIC IN AND FOR SAID STATE PERSONALLY APPEARED Peter Fischen AND Michael F. Ripling PERSONALLY KNOWN TO ME (OR PROVED TO ME ON THE BASIS OF OF SATISFACTORY EVIDENCE) TO BE THE PERSONS WHOSE NAMES ARE SUBSCRIBED TO THE WITHIN INSTRUMENT AND ACKNOWLEDGED TO ME THAT THEY EXECUTED THE SAME IN THEIR AUTHORIZED CAPACITIES AND THAT BY THEIR SIGNATURES ON THE INSTRUMENT THE PERSONS, OR THE ENTITY UPON BEHALF OF WHICH THE PERSONS ACTED EXECUTED THE INSTRUMENT.

WITNESS MY HAND:

NOTARY PUBLIC IN AND FOR SAID STATE
SONIA B. GARCIA
(NAME PRINTED)

MY PRINCIPAL PLACE OF BUSINESS IS
IN Los Angeles County
MY COMMISSION EXPIRES: May 9, 2003

SHEET 2 OF 5 SHEETS

AREA: 11.997 ACRES GROSS
(BEING ALL OF
TENTATIVE TRACT NO. 16101)
NUMBERED LOTS: 54
LETTERED LOTS: 12

TRACT NO. 16101

IN THE UNINCORPORATED TERRITORY OF THE
COUNTY OF ORANGE, STATE OF CALIFORNIA

JAMES R. CRAWFORD, L.S. 4965



DATE OF SURVEY: JANUARY, 2000

MONUMENT NOTES:

- ALL MONUMENTS SHOWN SET WILL BE SET WITHIN 90 DAYS AFTER THE ACCEPTANCE OF IMPROVEMENTS, EXCEPT AS NOTED.
- SET SPIKE W/ BRASS WASHER STAMPED "L.S. 4965" IN ASPHALT PAVEMENT HAVING A THICKNESS OF 2" OR MORE OR A LEAD, TACK AND TAG "L.S. 4965" IN CONCRETE, AT ALL CENTERLINE POINTS OF CONTROL, UNLESS OTHERWISE NOTED.
- TIES TO CENTERLINE MONUMENTS WILL BE MADE AND A COPY OF SAID TIES WILL BE FURNISHED TO THE COUNTY SURVEYOR'S OFFICE.
- SET 1" IRON PIPE TAGGED "L.S. 4965" AT ALL LOT CORNERS EXCEPT LOT CORNERS THAT ABUT A STREET WHICH WILL BE MARKED ON A 9.75' OFFSET OUTSIDE THE TRUE LOT CORNER IN CONCRETE BY A LEAD, TACK AND TAG "L.S. 4965" ON SIDELINES PRODUCED, EXCEPT AS NOTED. (NO MONUMENTS WILL BE SET FOR ANGLE POINTS, CORNER CUTOFFS, B.C.'S, E.C.'S, P.C.C.'S OR P.R.C.'S THAT ABUT A STREET WHICH ARE NOT LOT CORNER MARKING SIDELINES, UNLESS OTHERWISE NOTED).
- SET 2" IRON PIPE TAGGED "L.S. 4965" OR LEAD, TACK AND TAG "L.S. 4965" IN CONCRETE OR A SPIKE W/ BRASS WASHER STAMPED "L.S. 4965" IN ASPHALT PAVEMENT HAVING A THICKNESS OF 2" OR MORE AT ALL TRACT BOUNDARY CORNERS EXCEPT BOUNDARY CORNERS THAT ABUT A STREET WHICH WILL BE MARKED ON A 10.75' OFFSET INSIDE STREET RIGHT-OF-WAY ON BOUNDARY LINES PRODUCED, EXCEPT AS NOTED. (NO MONUMENTS WILL BE SET FOR ANGLE POINTS, CORNER CUTOFFS, B.C.'S, E.C.'S, P.C.C.'S OR P.R.C.'S THAT ABUT A STREET WHICH ARE NOT BOUNDARY CORNERS MARKING SIDELINES, UNLESS OTHERWISE NOTED.)
- INDICATES SET MONUMENTS AS NOTED.
 - SET LEAD, TACK AND TAG "L.S. 4965" IN CONCRETE ON OFFSET AS SHOWN OUTSIDE TRUE LOT CORNER ON SIDELINE PRODUCED.
 - SET 2" IRON PIPE TAGGED "L.S. 4965" PRIOR TO RECORDATION.
- INDICATES SET MONUMENTS AS NOTED AND REFERENCED BELOW:
 - INDICATES 1" IRON PIPE TAGGED "L.S. 5557" OR SPIKE AND WASHER STAMPED "L.S. 5557" OR LEAD, TACK AND TAG "L.S. 5557" TO BE SET PER TRACT NO. 16155, M.M. 812/30-39.
 - INDICATES 1" IRON PIPE TAGGED "L.S. 5557" OR SPIKE AND WASHER STAMPED "L.S. 5557" OR LEAD, TACK AND TAG "L.S. 5557" TO BE SET PER TRACT NO. 15884, M.M. 794/33-44.
 - INDICATES 2" IRON PIPE TAGGED "L.S. 5557" OR LEAD, TACK AND TAG "L.S. 5557" TO BE SET PER TRACT NO. 16155, M.M. 812/30-39.
 - FOUND OCS WELL MONUMENT WITH 2 1/2" BRASS DISK STAMPED "ORANGE COUNTY SURVEYOR" PER RECORD OF SURVEY 95-1066, R.S.B. 154/8-18.
- INDICATES FOUND ORANGE COUNTY SURVEYOR'S G.P.S. MONUMENT AS NOTED.

NOTES:

- THIS PROPERTY IS WITHIN A "SPECIAL FIRE PROTECTION AREA" AND MUST MEET ALL REQUIREMENTS FOR DEVELOPMENT WITHIN THE AREA OR FILE FOR AN EXCLUSION WITH THE FIRE CHIEF. THE APPLICANT HAS APPLIED FOR AND RECEIVED A "TOTAL EXCLUSION" FROM THIS ORANGE COUNTY "SPECIAL FIRE PROTECTION AREA" AND NO LOTS OR BUILDINGS ARE SUBJECT TO THE CONSTRUCTION FEATURES OF ORANGE COUNTY ORDINANCE 3960. THE EXCLUSION HAS BEEN GRANTED BASED ON THE FINDINGS FOUND IN A LETTER DATED FEBRUARY 9, 2000 SIGNED BY LAURA BLAUL OF THE ORANGE COUNTY FIRE AUTHORITY AND THE APPLICANT WILL KEEP A COPY OF SAID LETTER AVAILABLE IN THEIR RECORDS.
- THIS PROPERTY IS IN A "VERY HIGH FIRE HAZARD AREA" DUE TO WILDLAND EXPOSURE BASED ON STATE RESPONSIBILITY AREA (SRA) MAPS.
- LOTS "F", "G" AND "K" ARE NOT SEPARATE BUILDING SITES AND ARE PROPOSED TO BE GRANTED IN FEE TO THE HOMEOWNER'S ASSOCIATION FOR TRACT NO. 16101 FOR PRIVATE PARK AND LANDSCAPE MAINTENANCE PURPOSES.
- LOTS "A" THROUGH "E", "H" THROUGH "J" AND "L" ARE NOT SEPARATE BUILDING SITES AND ARE PROPOSED TO BE GRANTED IN FEE TO THE HOMEOWNER'S ASSOCIATION FOR TRACT NO. 16101 FOR LANDSCAPE MAINTENANCE PURPOSES.

CERTIFICATE OF ACCEPTANCE - SANTA MARGARITA WATER DISTRICT:

THE UNDERSIGNED, BEING THE DULY APPOINTED AGENT OF THE SANTA MARGARITA WATER DISTRICT, A PUBLIC CORPORATION IN ORANGE COUNTY, CALIFORNIA, PURSUANT TO ITS RESOLUTION NO. 88-10-2, DOES HEREBY ACCEPT ON BEHALF OF SAID DISTRICT THE EASEMENT FOR SEWER, WATER AND ACCESS PURPOSES, AS DEDICATED AND SHOWN ON THIS TRACT MAP, BY AND BETWEEN THE SANTA MARGARITA WATER DISTRICT AND WILLIAM LYON HOMES, INC., AND DOES HEREBY CERTIFY THAT THE GRANTEE CONSENTS TO THE RECORDATION OF SAID TRACT MAP.

Daniel R. Ferons
DANIEL R. FERONS, CHIEF ENGINEER
SANTA MARGARITA WATER DISTRICT

NOTARY ACKNOWLEDGMENT FOR SANTA MARGARITA WATER DISTRICT:

STATE OF CALIFORNIA }
COUNTY OF ORANGE } SS

ON, MAY 16, 2001, BEFORE ME CINDY R. LANE A NOTARY PUBLIC IN AND FOR SAID STATE PERSONALLY APPEARED DANIEL R. FERONS, PERSONALLY KNOWN TO ME (OR PROVED TO ME ON THE BASIS OF SATISFACTORY EVIDENCE) TO BE THE PERSON WHOSE NAME IS SUBSCRIBED TO THE WITHIN INSTRUMENT AND ACKNOWLEDGED TO ME THAT HE EXECUTED THE SAME IN HIS AUTHORIZED CAPACITY AND THAT BY HIS SIGNATURE ON THE INSTRUMENT THE PERSON, OR THE ENTITY UPON BEHALF OF WHICH THE PERSON ACTED, EXECUTED THE INSTRUMENT.

WITNESS MY HAND:

Cindy R. Lane
NOTARY PUBLIC IN AND FOR SAID STATE
CINDY R. LANE
(NAME PRINTED)

MY PRINCIPAL PLACE OF BUSINESS IS
IN ORANGE COUNTY

MY COMMISSION EXPIRES: 2-20-2005

SIGNATURE OMISSION NOTES:

PURSUANT TO THE PROVISIONS OF SECTION 66436(a)(3)(C) OF THE SUBDIVISION MAP ACT THE FOLLOWING SIGNATURES HAVE BEEN OMITTED:

- LADERA DEVELOPMENT COMPANY, L.L.C., HOLDER OF OIL, GAS, WATER AND MINERAL RIGHTS RECORDED AS INSTRUMENT NO. 19960624029 OF OFFICIAL RECORDS.
- DMB LADERA, L.L.C., HOLDER OF EASEMENTS FOR CONSTRUCTION FACILITIES, TELECOMMUNICATION FACILITIES, PUBLIC UTILITIES, SURFACE RUNOFF, VEHICULAR AND PEDESTRIAN INGRESS AND EGRESS AND IRRIGATION FACILITIES RECORDED AS INSTRUMENT NO. 20010110728 OF OFFICIAL RECORDS.

GPS POINT LOCATIONS:


GPS # 1417 FOUND 2 1/2" IRON PIPE WITH 2" DIAMETER O.C.S. BRASS
N2141450.558 CAP STAMPED "GPS 1417 9-95" PER RECORDS ON FILE IN THE OFFICE
E6141583.535 OF THE ORANGE COUNTY SURVEYOR.

GPS # 1424 FOUND 2 1/2" IRON PIPE WITH 2" DIAMETER O.C.S. BRASS
N2152873.842 CAP STAMPED "GPS 1424 9-95" PER RECORDS ON FILE IN THE OFFICE
E6141904.527 OF THE ORANGE COUNTY SURVEYOR.

BOUNDARY CONTROL, INDEX & VICINITY MAP

SCALE: 1" = 200'

③ - INDICATES SHEET NUMBER

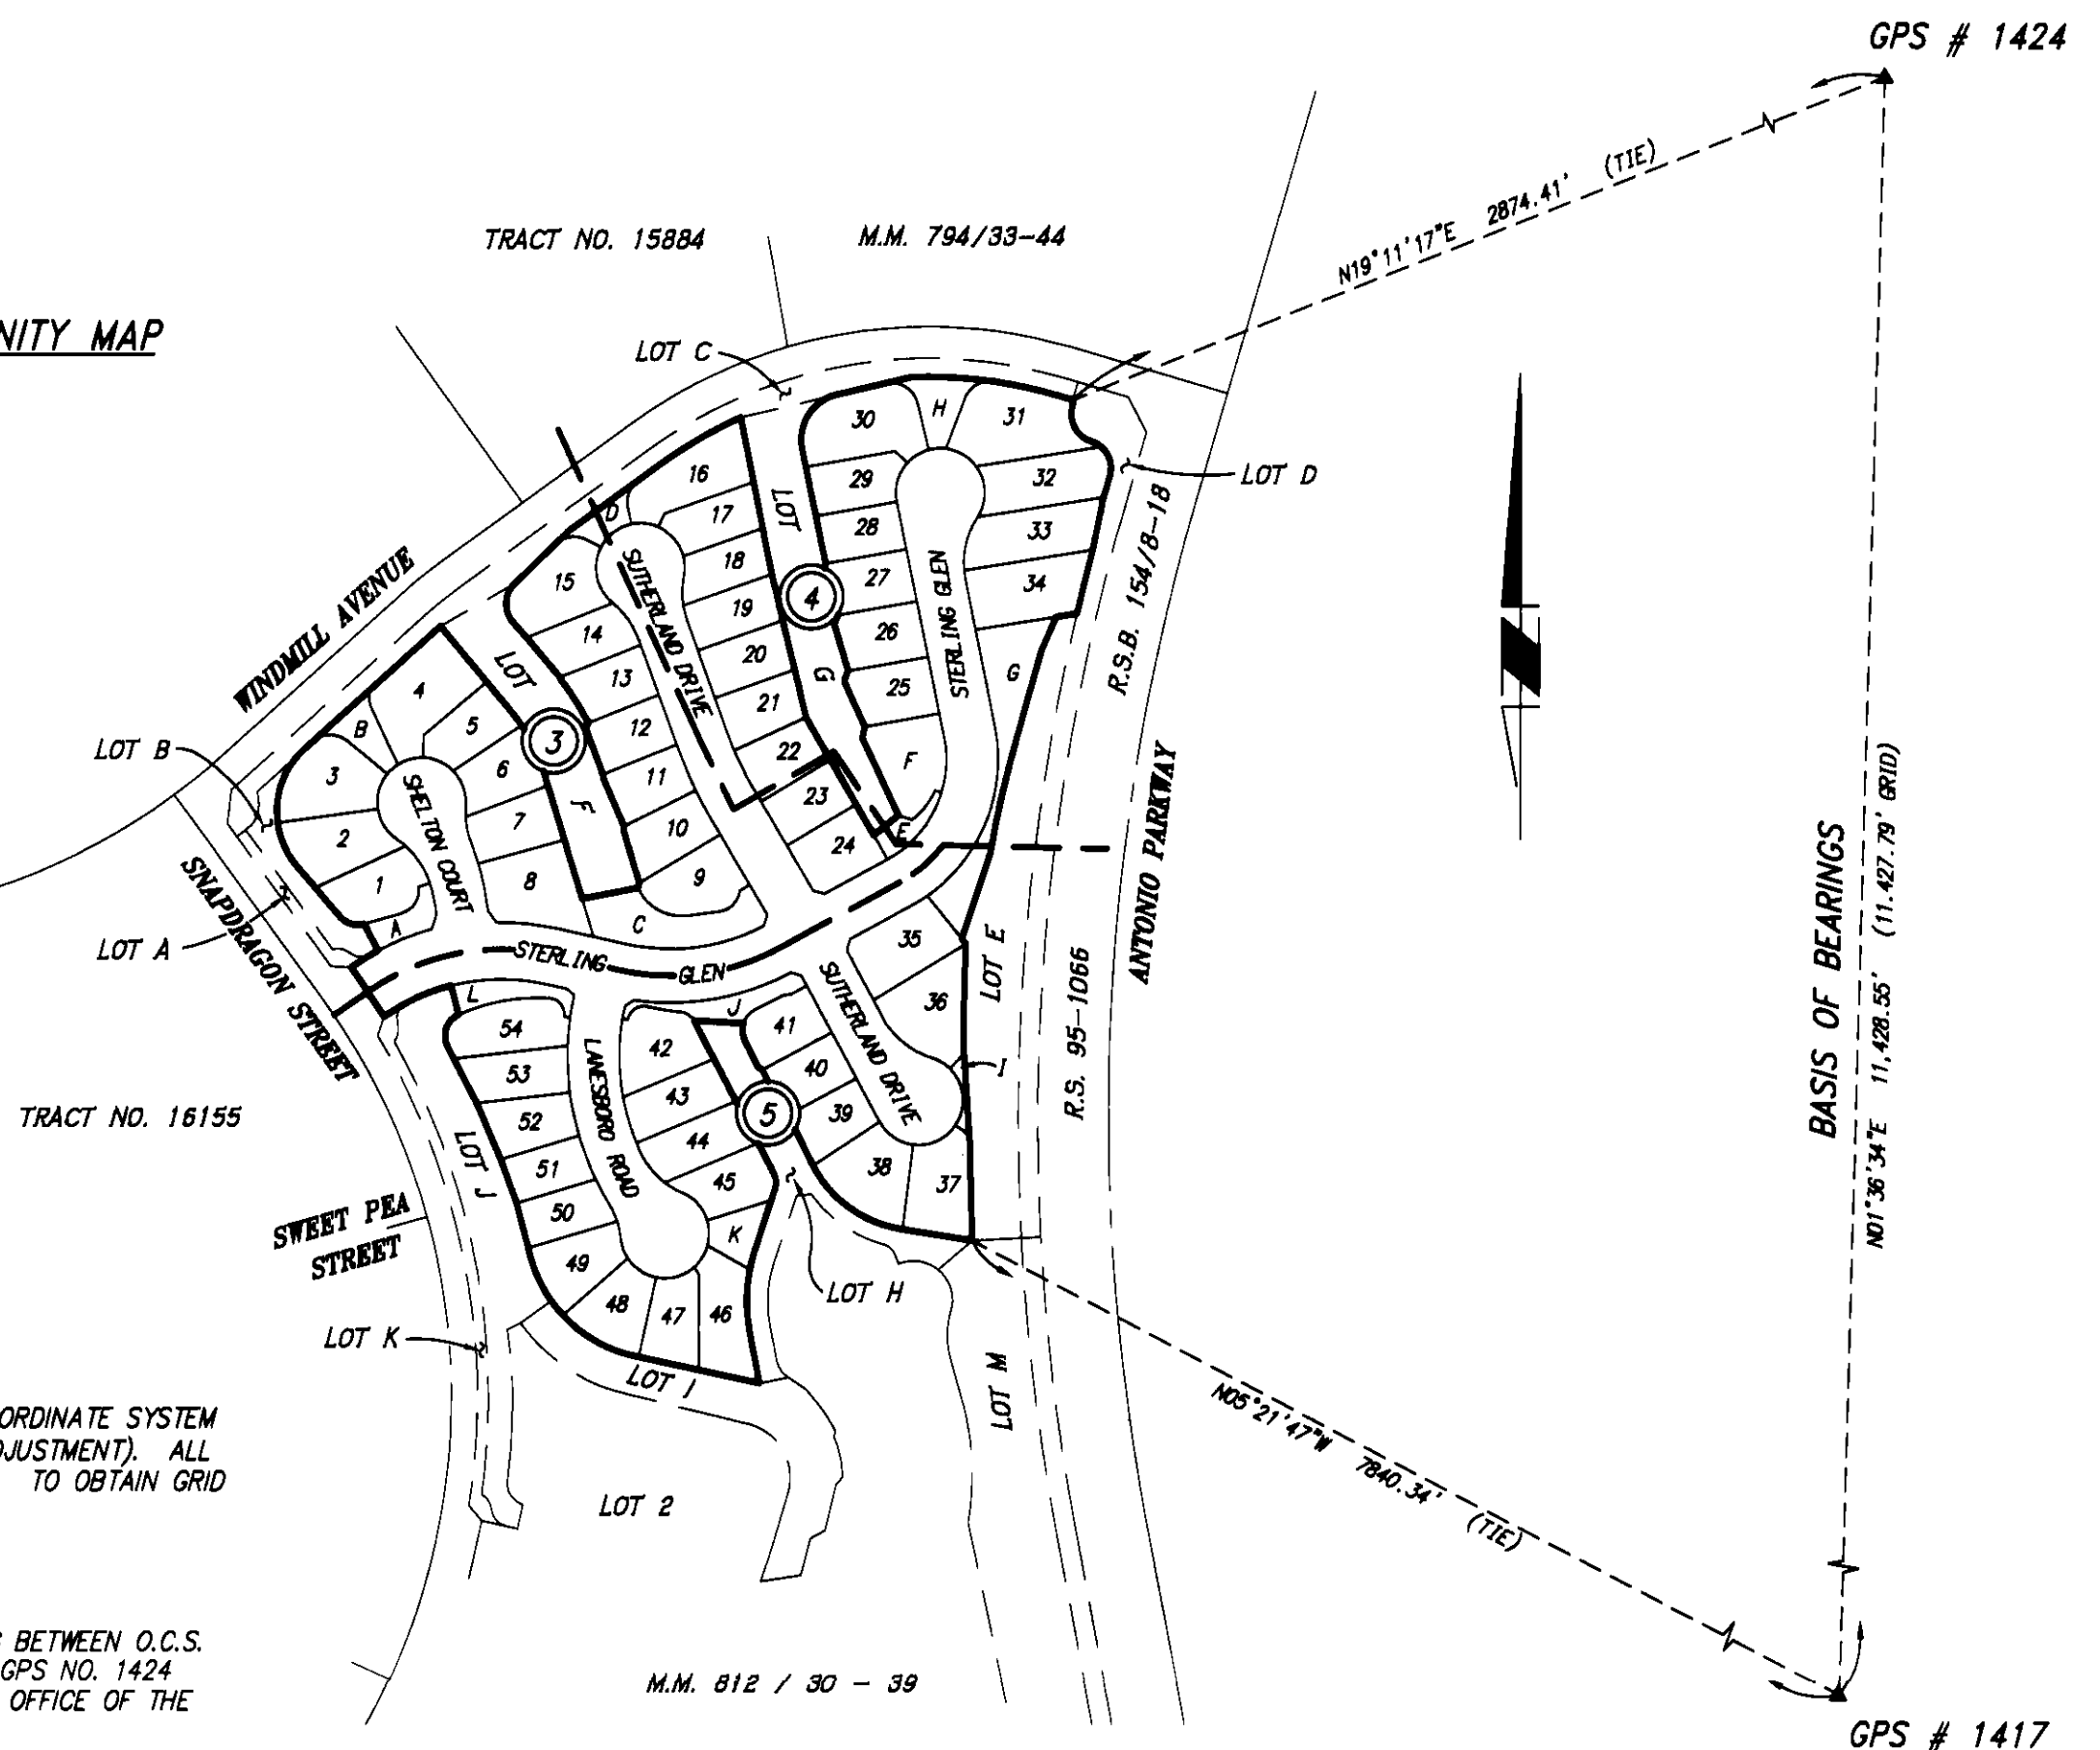

DATUM STATEMENT:

COORDINATES SHOWN ARE BASED UPON THE CALIFORNIA COORDINATE SYSTEM (CCS83), ZONE VI 1983 NAD (1991.35 EPOCH O.C.S. GPS ADJUSTMENT). ALL DISTANCES SHOWN ARE GROUND UNLESS OTHERWISE NOTED. TO OBTAIN GRID DISTANCE, MULTIPLY THE GROUND DISTANCE BY 0.99993389.

BASIS OF BEARINGS NOTE:

THE BEARINGS SHOWN HEREON ARE BASED ON THE BEARING BETWEEN O.C.S. HORIZONTAL CONTROL STATION GPS NO. 1417 AND STATION GPS NO. 1424 BEING NORTH 01°36'34" EAST PER RECORDS ON FILE IN THE OFFICE OF THE ORANGE COUNTY SURVEYOR.

SHEET 4 OF 5 SHEETS
AREA: 11.997 ACRES GROSS
(BEING ALL OF
TENTATIVE TRACT NO. 16101)
NUMBERED LOTS: 34
LETTERED LOTS: 12
SCALE: 1" = 40'

TRACT NO. 16101


IN THE UNINCORPORATED TERRITORY OF THE
COUNTY OF ORANGE, STATE OF CALIFORNIA

JAMES R. CRAWFORD, L.S. 4965



DATE OF SURVEY: OCTOBER, 2000

TRACT NO. 15884

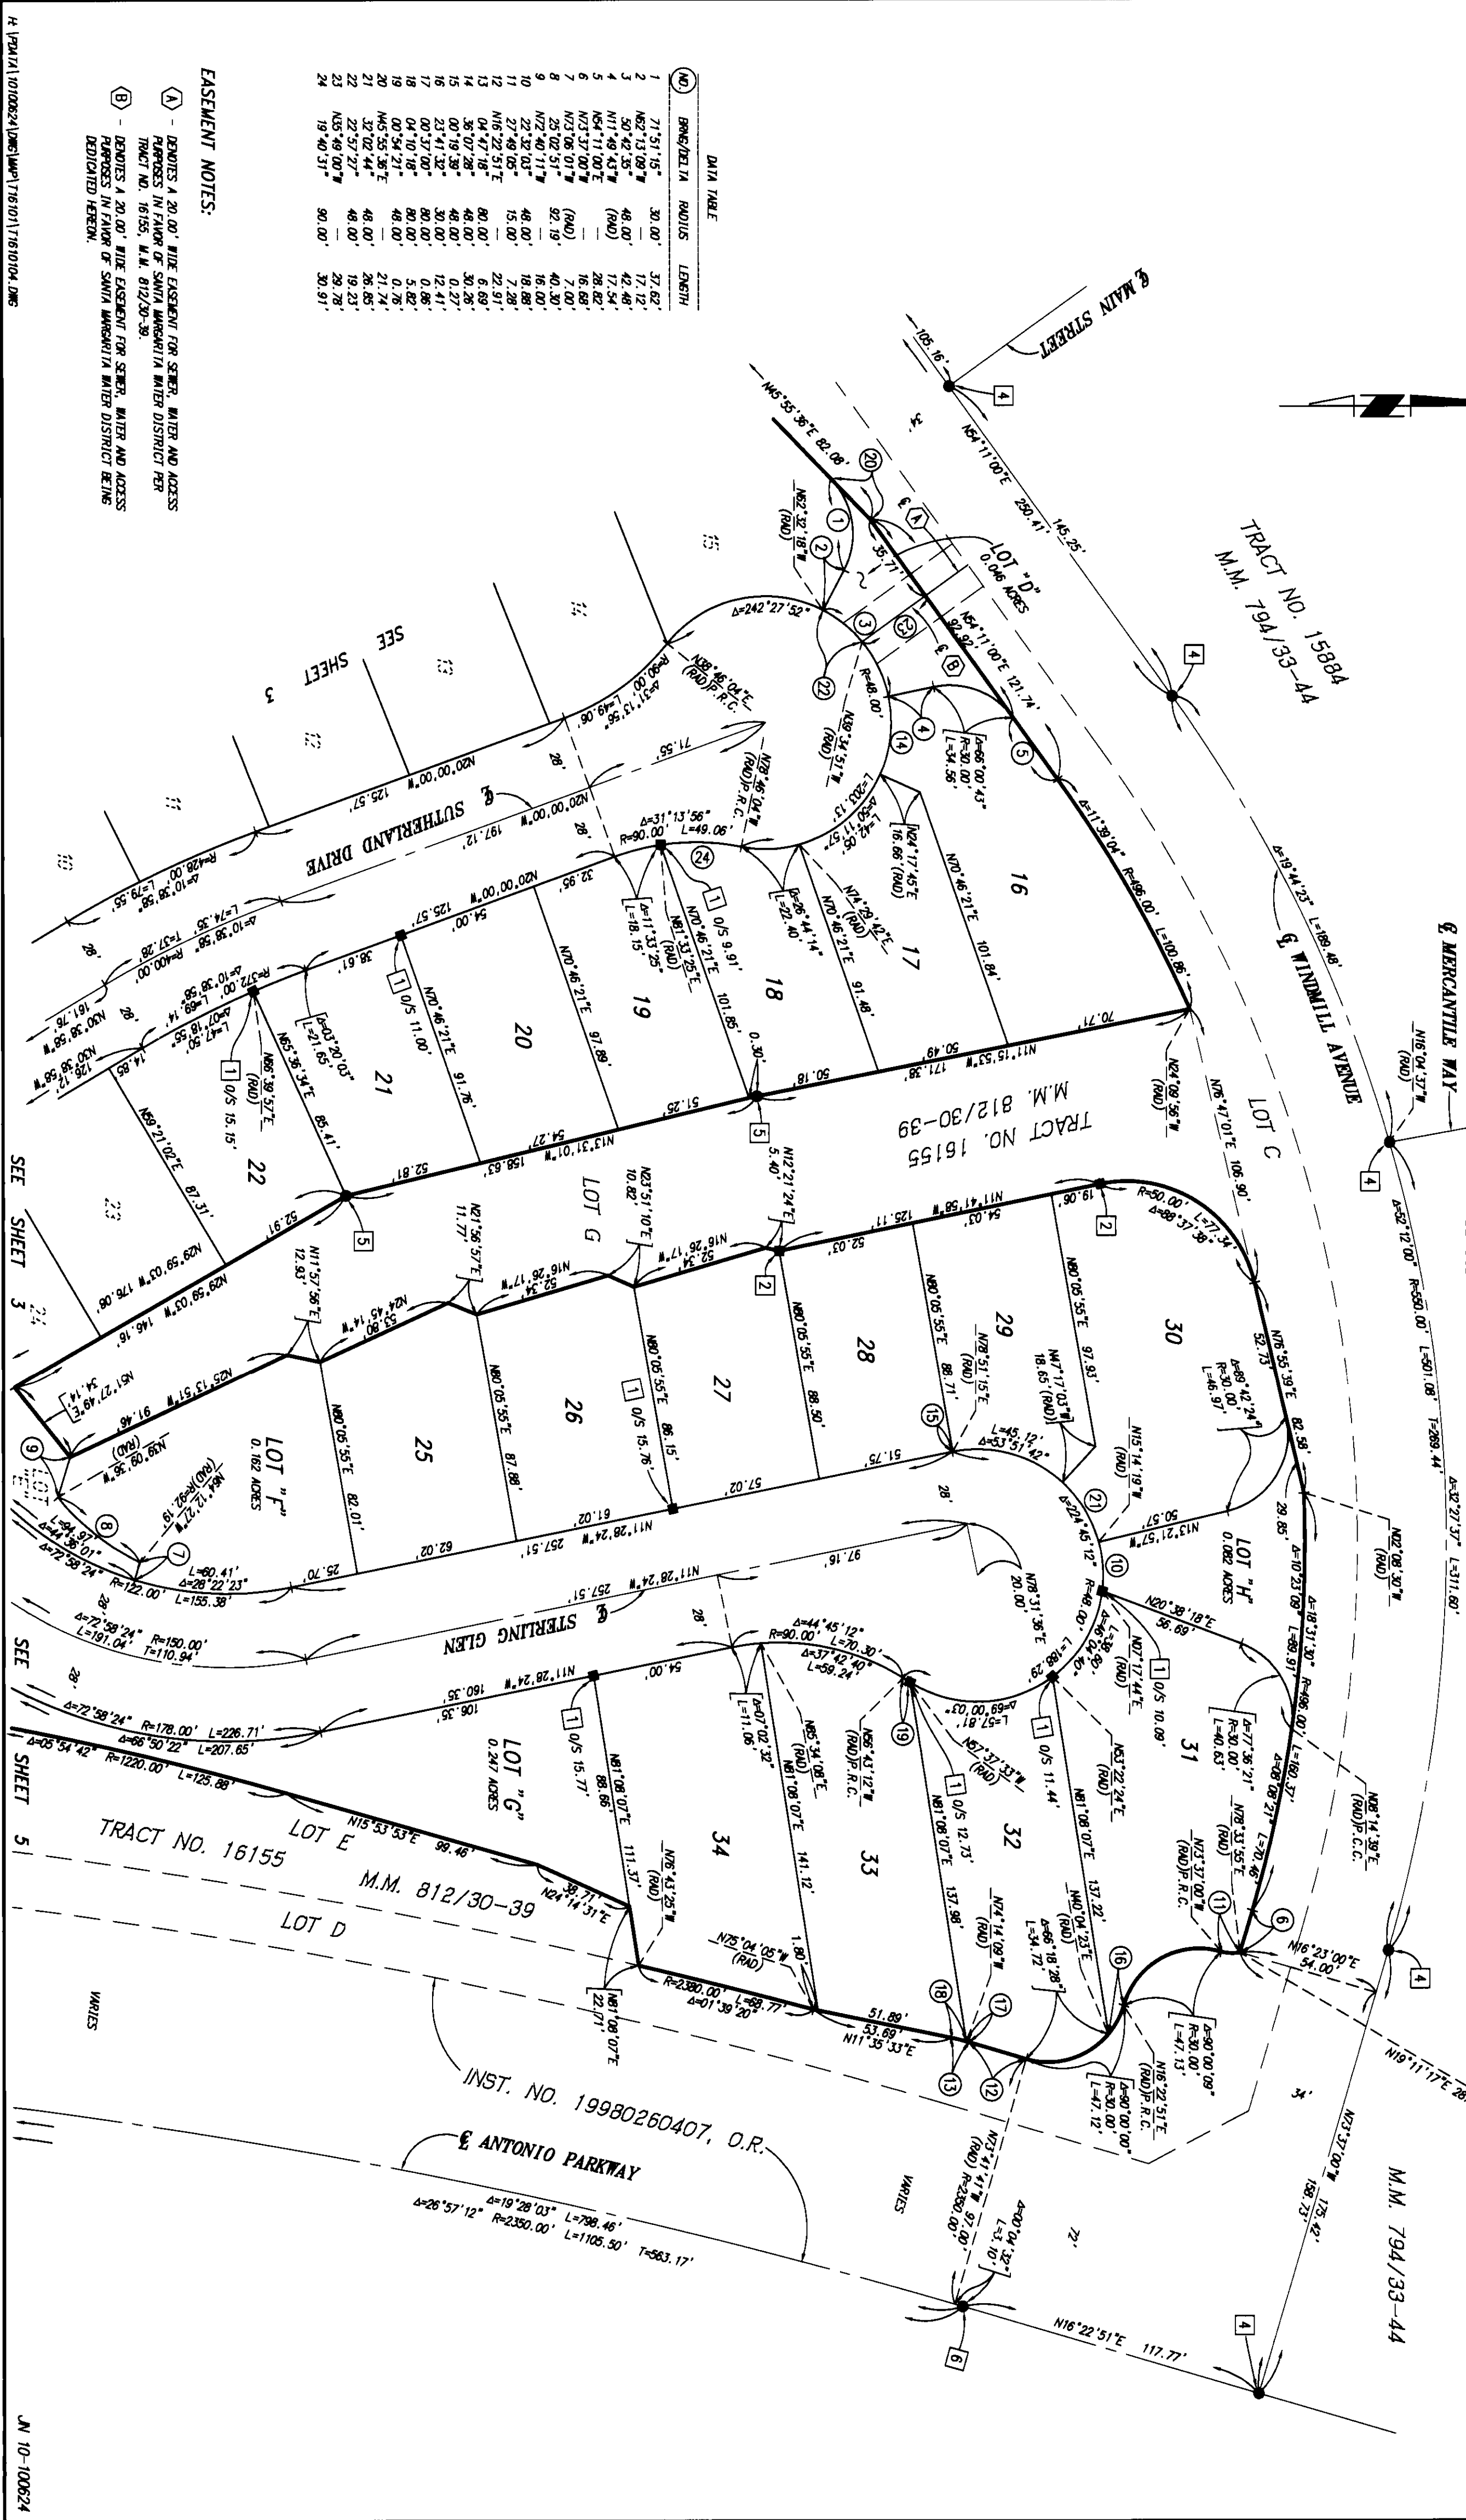

DATA TABLE

NO.	BREX/DELTA	RAJULUS	LENGTH
1	71.51.15"	30.00'	37.62'
2	N62°13.09'W	—	17.12'
3	S50°42.35'E	48.00'	42.48'
4	N11°49.43'W	(RAD)	17.54'
5	N54°11.00'E	—	28.82'
6	N73°37.00'W	(RAD)	16.68'
7	N73°06.01'W	92.19'	7.00'
8	N72°40.11'W	—	16.00'
9	N22°32.03'E	48.00'	18.88'
10	N16°22.51'E	15.00'	7.28'
11	N27°49.05'E	—	22.91'
12	N6°47.18'E	48.00'	6.89'
13	S6°07.28'E	48.00'	30.26'
14	S0°19.39'E	48.00'	12.41'
15	S23°41.32'E	30.00'	0.86'
16	S0°10.18'E	48.00'	5.82'
17	S0°34.21'E	48.00'	0.76'
18	N45°35.36'E	—	21.74'
19	S2°02.44'E	48.00'	26.85'
20	S22°57.27'E	48.00'	19.23'
21	N55°49.00'W	—	29.78'
22	—	90.00'	30.91'
23	—	—	—
24	—	—	—

EASEMENT NOTES:

- (A) - DENOTES A 20.00' WIDE EASEMENT FOR SEWER, WATER AND ACCESS PURPOSES IN FAVOR OF SANTA MARGARITA WATER DISTRICT PER TRACT NO. 16155, M.M. 812/30-39.
- (B) - DENOTES A 20.00' WIDE EASEMENT FOR SEWER, WATER AND ACCESS PURPOSES IN FAVOR OF SANTA MARGARITA WATER DISTRICT BEING DEDICATED HEREIN.

H:\PWA\10100624\DWG\MAP\16101\1610104.DWG

