

SHEET 1 OF 6 SHEETS
78 NUMBERED LOTS AND LOTS
A THROUGH F, INCLUSIVE
ACREAGE: 12.208 ACRES
(ALL OF TENTATIVE
TRACT NO. 16104)

TRACT NO. 16104

IN UNINCORPORATED TERRITORY OF THE COUNTY OF ORANGE,
STATE OF CALIFORNIA

BEING A SUBDIVISION OF LOT 5 OF TRACT NO. 16155, AS SHOWN ON A MAP
FILED IN BOOK 812, PAGES 30 THROUGH 39, INCLUSIVE, OF MISCELLANEOUS
MAPS, IN THE OFFICE OF THE COUNTY RECORDER OF SAID COUNTY.

BLOCK: 5157
MODULE: 16 AND 17

HUNSAKER AND ASSOCIATES IRVINE, INC.
RORY S. WILLIAMS, L.S. 6654 DATE OF SURVEY: DECEMBER, 2000

ACCEPTED AND FILED AT THE
REQUEST OF
BENEFIT LAND TITLE INSURANCE COMPANY

DATE: JULY 31, 2001
TIME: 1:48 PM. FEE: \$17.00
INSTRUMENT NO. 20010520749
BOOK 821 PAGE 35-40 M/M

GARY L. GRANVILLE
COUNTY CLERK - RECORDER
BY [Signature]
DEPUTY

OWNERSHIP CERTIFICATE:

WE, THE UNDERSIGNED, BEING ALL PARTIES HAVING ANY RECORD TITLE INTEREST IN THE LAND COVERED BY THIS MAP, DO HEREBY CONSENT TO THE PREPARATION AND RECORDATION OF SAID MAP, AS SHOWN WITHIN THE DISTINCTIVE BORDER LINE.

WE HEREBY DEDICATE TO THE PUBLIC FOR STREET PURPOSES:

CAPRICORN DRIVE, CASTOR COURT, COMET TRAIL, FLORA COURT, GOSSAMER PLACE, SOLSTICE DRIVE, TERRASTAR LANE AND TETHER MOON LANE.

WE ALSO DO HEREBY DECLARE THAT THE LAND COVERED BY THIS MAP IS LOCATED IN A VERY HIGH FIRE HAZARD AREA DUE TO WILDLAND EXPOSURE BASED ON STATE SRA MAPS.

WE ALSO HEREBY DEDICATE TO THE SANTA MARGARITA WATER DISTRICT THE PIPELINE EASEMENTS FOR WATER LINE, SANITARY SEWER AND ACCESS PURPOSES, AS SHOWN ON THIS TRACT MAP, WHICH EASEMENTS SHALL BE SUBJECT TO THE SAME TERMS AND CONDITIONS AS SHOWN IN THAT CERTAIN EASEMENT RECORDED OCTOBER 6, 1980, IN BOOK 13776, PAGE 341 OF OFFICIAL RECORDS OF ORANGE COUNTY, CALIFORNIA.

CENTEX HOMES, A NEVADA GENERAL PARTNERSHIP, OWNER.

BY: CENTEX REAL ESTATE CORPORATION, A NEVADA CORPORATION,
ITS MANAGING GENERAL PARTNER.

BY: [Signature]
NAME: ROLAND OSGOOD
TITLE: DIVISION PRESIDENT

BY: [Signature]
NAME: Martin Suliussen
TITLE: Controller/Assistant Secretary

DMB LADERA, LLC, A DELAWARE LIMITED LIABILITY COMPANY, BENEFICIARY UNDER DEED OF TRUST RECORDED FEBRUARY 3, 2000, AS INSTRUMENT NO. 20000060913 OF OFFICIAL RECORDS, AND UNDER DEED OF TRUST RECORDED APRIL 3, 2001, AS INSTRUMENT NO. 2001-0195570 OF OFFICIAL RECORDS.
BY: RANCHO MISSION VIEJO, L.L.C., A DELAWARE LIMITED LIABILITY COMPANY, ITS AUTHORIZED AGENT AND MANAGER.

BY: [Signature]
NAME: Stephen C. Schrank
TITLE: Executive VP of Development

BY: [Signature]
NAME: Paul Johnson
TITLE: VP of Community Development

NOTARY ACKNOWLEDGMENTS:

STATE OF CALIFORNIA }
COUNTY OF ORANGE } SS

ON April 2, 2001, BEFORE ME, Rhonda Keiger Painter, PERSONALLY APPEARED Roland F. Osgood AND Martin Suliussen PERSONALLY KNOWN TO ME (OR PROVED TO ME ON THE BASIS OF SATISFACTORY EVIDENCE) TO BE THE PERSON(S) WHOSE NAME(S) IS/ARE SUBSCRIBED TO THE WITHIN INSTRUMENT AND ACKNOWLEDGED TO ME THAT HE/SHE/IT/THEY EXECUTED THE SAME IN HIS/HER/ITS/THEIR AUTHORIZED CAPACITY(IES), AND THAT BY HIS/HER/ITS/THEIR SIGNATURE(S) ON THE INSTRUMENT THE PERSON(S), OR ENTITY UPON BEHALF OF WHICH THE PERSON(S) ACTED, EXECUTED THE INSTRUMENT.

WITNESS MY HAND:

SIGNATURE [Signature]
NOTARY PUBLIC IN AND FOR SAID STATE
Rhonda Keiger Painter
(NAME PRINTED)

MY PRINCIPAL PLACE OF BUSINESS IS
IN Orange COUNTY.
MY COMMISSION EXPIRES: 12/19/03

STATE OF CALIFORNIA }
COUNTY OF ORANGE } SS

ON April 9, 2001, BEFORE ME, Holly Broman, PERSONALLY APPEARED Stephen C. Schrank AND Paul Johnson PERSONALLY KNOWN TO ME (OR PROVED TO ME ON THE BASIS OF SATISFACTORY EVIDENCE) TO BE THE PERSON(S) WHOSE NAME(S) IS/ARE SUBSCRIBED TO THE WITHIN INSTRUMENT AND ACKNOWLEDGED TO ME THAT HE/SHE/IT/THEY EXECUTED THE SAME IN HIS/HER/ITS/THEIR AUTHORIZED CAPACITY(IES), AND THAT BY HIS/HER/ITS/THEIR SIGNATURE(S) ON THE INSTRUMENT THE PERSON(S), OR ENTITY UPON BEHALF OF WHICH THE PERSON(S) ACTED, EXECUTED THE INSTRUMENT.

WITNESS MY HAND:


SIGNATURE [Signature]
NOTARY PUBLIC IN AND FOR SAID STATE
Holly Broman
(NAME PRINTED)

MY PRINCIPAL PLACE OF BUSINESS IS
IN ORANGE COUNTY.
MY COMMISSION EXPIRES: 3/3/04

SURVEYOR'S STATEMENT:

I HEREBY STATE THAT THIS MAP, CONSISTING OF 6 SHEETS, CORRECTLY REPRESENTS A TRUE AND COMPLETE SURVEY AS SHOWN MADE IN DECEMBER, 2000; WAS MADE BY ME OR UNDER MY DIRECTION; THAT THE MONUMENTS ARE OF THE CHARACTER AND OCCUPY (OR WILL OCCUPY) THE POSITIONS INDICATED BY SAID MAP; AND THAT SAID MONUMENTS ARE (OR WILL BE) SUFFICIENT TO ENABLE THE SURVEY TO BE RETRACED.

Rory S. Williams 3/29/01
RORY S. WILLIAMS, L.S. 6654 DATE
EXPIRATION DATE: 12/31/03

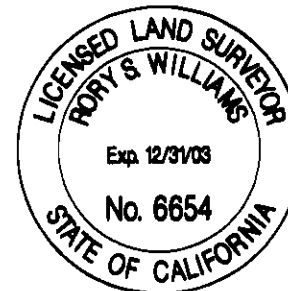

COUNTY SURVEYOR'S STATEMENT

I HEREBY STATE THAT I HAVE EXAMINED THIS MAP AND HAVE FOUND IT TO BE SUBSTANTIALLY IN CONFORMANCE WITH THE TENTATIVE MAP AS FILED WITH, AMENDED AND APPROVED BY THE ORANGE COUNTY SUBDIVISION COMMITTEE; THAT ALL PROVISIONS OF THE SUBDIVISION MAP ACT AND COUNTY SUBDIVISION REGULATIONS HAVE BEEN COMPLIED WITH AND I AM SATISFIED SAID MAP IS TECHNICALLY CORRECT.

DATED THIS 13TH DAY OF JULY, 2001.

Michael K. Sullivan
JOHN CANAS, COUNTY SURVEYOR
LS 4408, EXPIRATION DATE: 9-30-01 BY: MICHAEL K. SULLIVAN, DEPUTY
LS 6254 EXPIRES 6-30-02



COUNTY TREASURER-TAX COLLECTOR'S CERTIFICATE:

STATE OF CALIFORNIA }
COUNTY OF ORANGE } SS

I HEREBY CERTIFY THAT ACCORDING TO THE RECORDS OF MY OFFICE THERE ARE NO LIENS AGAINST THE LAND COVERED BY THIS MAP OR ANY PART THEREOF FOR UNPAID STATE, COUNTY, MUNICIPAL OR LOCAL TAXES OR SPECIAL ASSESSMENTS COLLECTED AS TAXES, EXCEPT TAXES OR SPECIAL ASSESSMENTS COLLECTED AS TAXES NOT YET PAYABLE.

AND DO CERTIFY TO THE RECORDER OF ORANGE COUNTY THAT THE PROVISIONS OF THE SUBDIVISION MAP ACT HAVE BEEN COMPLIED WITH REGARDING DEPOSITS TO SECURE PAYMENT OF TAXES OR SPECIAL ASSESSMENTS COLLECTED AS TAXES ON THE LAND COVERED BY THIS MAP.

DATED THIS 27th DAY OF June, 2001.

JOHN M.W. MOORLACH
COUNTY TREASURER-TAX COLLECTOR BY: Dixie Tennies
DEPUTY TREASURER-TAX COLLECTOR

CLERK OF THE BOARD OF SUPERVISORS' CERTIFICATE:

STATE OF CALIFORNIA }
COUNTY OF ORANGE } SS

I HEREBY CERTIFY THAT THIS MAP WAS PRESENTED FOR APPROVAL TO THE BOARD OF SUPERVISORS OF THE COUNTY OF ORANGE AT REGULAR MEETING THEREOF HELD ON THE 24th DAY OF July, 2001, AND THAT THEREUPON SAID BOARD DID, BY AN ORDER DULY PASSED AND ENTERED, APPROVE SAID MAP AND DID ACCEPT ON BEHALF OF THE PUBLIC, SUBJECT TO IMPROVEMENTS, THE DEDICATION FOR STREET PURPOSES OF CAPRICORN DRIVE, CASTOR COURT, COMET TRAIL, FLORA COURT, GOSSAMER PLACE, SOLSTICE DRIVE, TERRASTAR LANE AND TETHER MOON LANE.

DATED THIS 24th DAY OF July, 2001.

[Signature]
CLERK OF THE BOARD OF SUPERVISORS
DARLENE J. BLOOM



CERTIFICATE OF ACCEPTANCE - SANTA MARGARITA WATER DISTRICT

THE UNDERSIGNED, BEING THE DULY APPOINTED AGENT OF THE SANTA MARGARITA WATER DISTRICT, A PUBLIC CORPORATION IN ORANGE COUNTY, CALIFORNIA, PURSUANT TO ITS RESOLUTION NO. 88-10-2, DOES HEREBY ACCEPT ON BEHALF OF SAID DISTRICT, THE PIPELINE EASEMENTS FOR WATER LINE, SANITARY SEWER AND ACCESS PURPOSES AS DEDICATED AND SHOWN ON THIS TRACT MAP, BY AND BETWEEN THE SANTA MARGARITA WATER DISTRICT AND CENTEX HOMES, A NEVADA GENERAL PARTNERSHIP, AND DOES HEREBY CERTIFY THAT THE GRANTEE CONSENTS TO THE RECORDATION OF SAID TRACT MAP.

[Signature]
DANIEL R. FERONS, CHIEF ENGINEER
SANTA MARGARITA WATER DISTRICT

NOTARY ACKNOWLEDGMENT - SANTA MARGARITA WATER DISTRICT

STATE OF CALIFORNIA }
COUNTY OF ORANGE } SS

ON MAY 18, 2001, BEFORE ME, ANDREA M. EVANS, PERSONALLY APPEARED DANIEL R. FERONS, PERSONALLY KNOWN TO ME (OR PROVED TO ME ON THE BASIS OF SATISFACTORY EVIDENCE) TO BE THE PERSON WHOSE NAME IS SUBSCRIBED TO THE WITHIN INSTRUMENT AND ACKNOWLEDGED TO ME THAT HE EXECUTED THE SAME IN HIS AUTHORIZED CAPACITY, AND THAT BY HIS SIGNATURE ON THE INSTRUMENT THE PERSON, OR ENTITY UPON BEHALF OF WHICH THE PERSON ACTED, EXECUTED THE INSTRUMENT.

WITNESS MY HAND:

SIGNATURE [Signature]
NOTARY PUBLIC IN AND FOR SAID STATE
ANDREA M. EVANS
(NAME PRINTED)

MY PRINCIPAL PLACE OF BUSINESS IS
IN ORANGE COUNTY.
MY COMMISSION EXPIRES: 4/08/02

SIGNATURE OMISSIONS:

PURSUANT TO THE PROVISIONS OF SECTION 66436 (e)(3)(C) OF THE SUBDIVISION MAP ACT, THE FOLLOWING SIGNATURES HAVE BEEN OMITTED:

LADERA DEVELOPMENT COMPANY, L.L.C., HOLDER OF OIL, GAS AND MINERAL RIGHTS RECORDED AS INSTRUMENT NO. 19960624029 OF OFFICIAL RECORDS.

DMB LADERA, L.L.C., A DELAWARE LIMITED LIABILITY COMPANY, HOLDER OF AN EASEMENT RECORDED AS INSTRUMENT NO. 2001-195568 OF OFFICIAL RECORDS.

SHEET 2 OF 6 SHEETS
SCALE 1" = 80'
78 NUMBERED LOTS AND LOTS
A THROUGH F, INCLUSIVE
ACREAGE: 12.208 ACRES
(ALL OF TENTATIVE
TRACT NO. 16104)

TRACT NO. 16104

IN UNINCORPORATED TERRITORY OF THE COUNTY OF ORANGE,
STATE OF CALIFORNIA

HUNSAKER AND ASSOCIATES IRVINE, INC.
RORY S. WILLIAMS, L.S. 6654 DATE OF SURVEY: DECEMBER, 2000



SHEET INDEX AND GPS CONTROL MAP

3 INDICATES SHEET NUMBER

PORTION OF PCL. 1

LLA LL 96-026,

INST. NO. 19960587414, O.R.

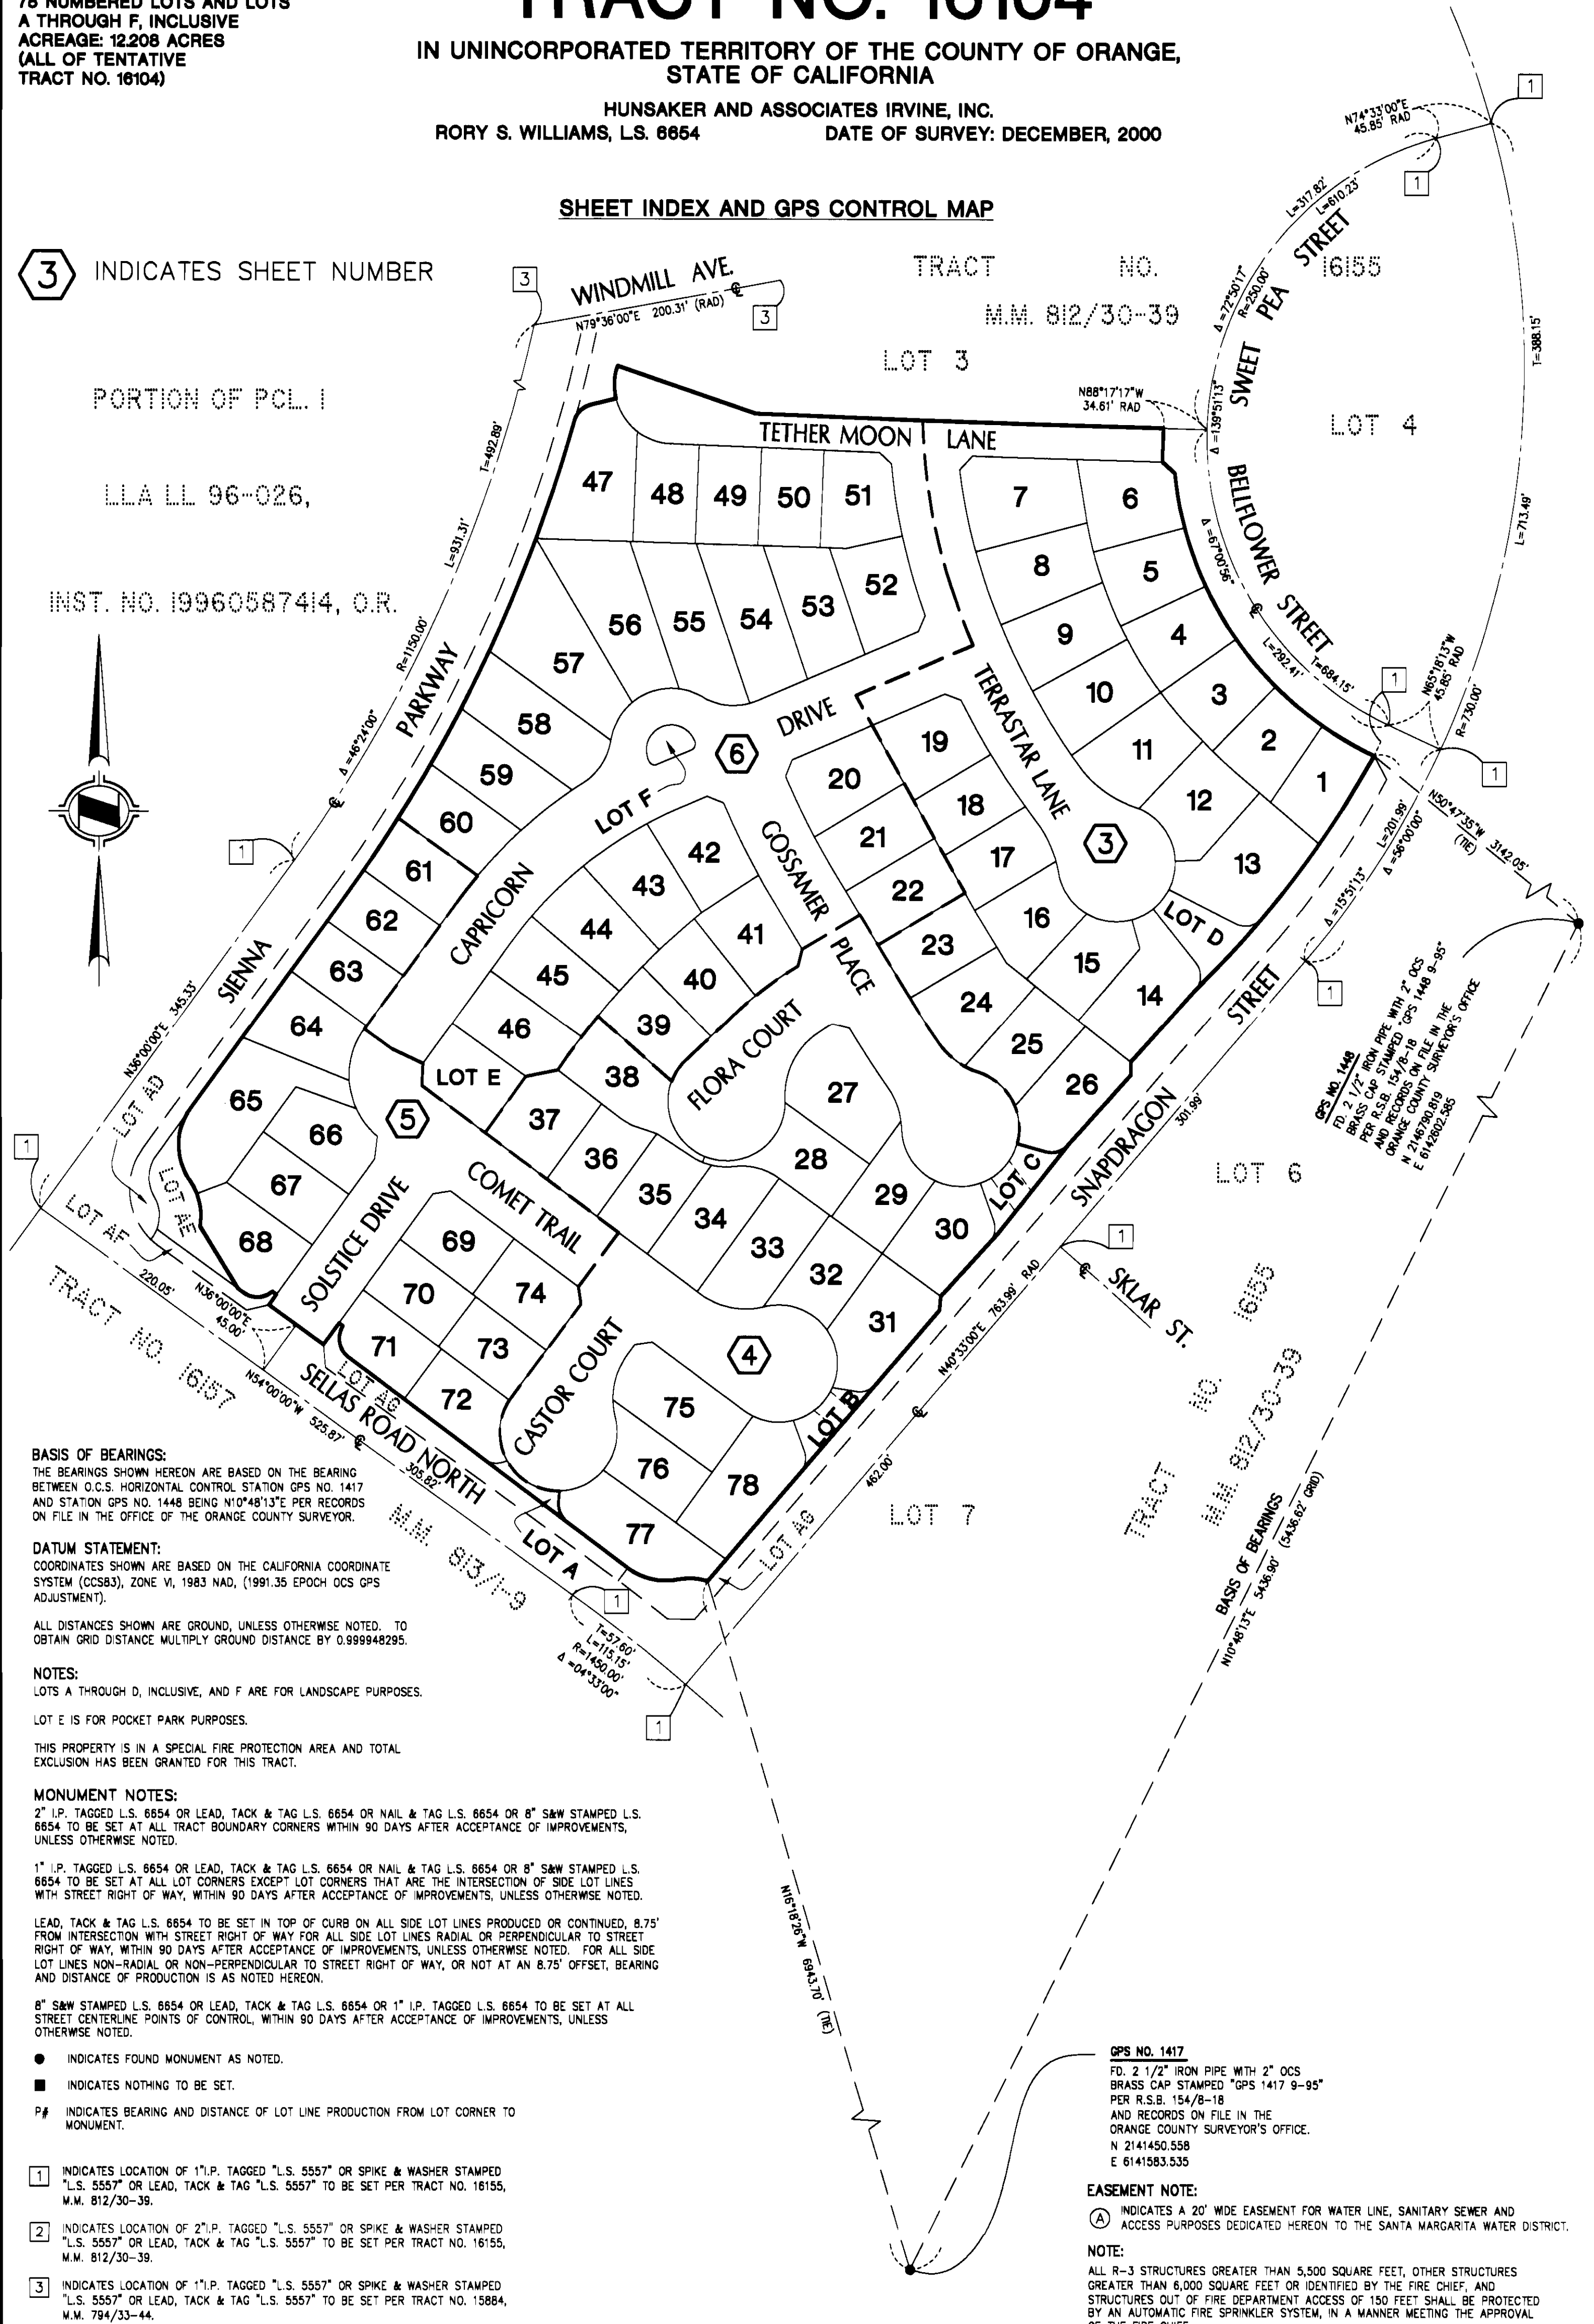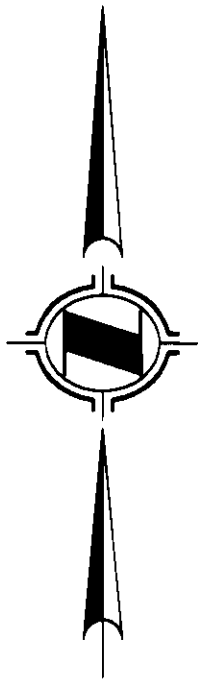

BASIS OF BEARINGS:
THE BEARINGS SHOWN HEREON ARE BASED ON THE BEARING BETWEEN O.C.S. HORIZONTAL CONTROL STATION GPS NO. 1417 AND STATION GPS NO. 1448 BEING N10°48'13"E PER RECORDS ON FILE IN THE OFFICE OF THE ORANGE COUNTY SURVEYOR.

DATUM STATEMENT:
COORDINATES SHOWN ARE BASED ON THE CALIFORNIA COORDINATE SYSTEM (CCS83), ZONE VI, 1983 NAD, (1991.35 EPOCH OCS GPS ADJUSTMENT).

ALL DISTANCES SHOWN ARE GROUND, UNLESS OTHERWISE NOTED. TO OBTAIN GRID DISTANCE MULTIPLY GROUND DISTANCE BY 0.999948295.

NOTES:
LOTS A THROUGH D, INCLUSIVE, AND F ARE FOR LANDSCAPE PURPOSES.
LOT E IS FOR POCKET PARK PURPOSES.

THIS PROPERTY IS IN A SPECIAL FIRE PROTECTION AREA AND TOTAL EXCLUSION HAS BEEN GRANTED FOR THIS TRACT.

MONUMENT NOTES:
2" I.P. TAGGED L.S. 6654 OR LEAD, TACK & TAG L.S. 6654 OR NAIL & TAG L.S. 6654 OR 8" S&W STAMPED L.S. 6654 TO BE SET AT ALL TRACT BOUNDARY CORNERS WITHIN 90 DAYS AFTER ACCEPTANCE OF IMPROVEMENTS, UNLESS OTHERWISE NOTED.

1" I.P. TAGGED L.S. 6654 OR LEAD, TACK & TAG L.S. 6654 OR NAIL & TAG L.S. 6654 OR 8" S&W STAMPED L.S. 6654 TO BE SET AT ALL LOT CORNERS EXCEPT LOT CORNERS THAT ARE THE INTERSECTION OF SIDE LOT LINES WITH STREET RIGHT OF WAY, WITHIN 90 DAYS AFTER ACCEPTANCE OF IMPROVEMENTS, UNLESS OTHERWISE NOTED.

LEAD, TACK & TAG L.S. 6654 TO BE SET IN TOP OF CURB ON ALL SIDE LOT LINES PRODUCED OR CONTINUED, 8.75' FROM INTERSECTION WITH STREET RIGHT OF WAY FOR ALL SIDE LOT LINES RADIAL OR PERPENDICULAR TO STREET RIGHT OF WAY, WITHIN 90 DAYS AFTER ACCEPTANCE OF IMPROVEMENTS, UNLESS OTHERWISE NOTED. FOR ALL SIDE LOT LINES NON-RADIAL OR NON-PERPENDICULAR TO STREET RIGHT OF WAY, OR NOT AT AN 8.75' OFFSET, BEARING AND DISTANCE OF PRODUCTION IS AS NOTED HEREON.

8" S&W STAMPED L.S. 6654 OR LEAD, TACK & TAG L.S. 6654 OR 1" I.P. TAGGED L.S. 6654 TO BE SET AT ALL STREET CENTERLINE POINTS OF CONTROL, WITHIN 90 DAYS AFTER ACCEPTANCE OF IMPROVEMENTS, UNLESS OTHERWISE NOTED.

● INDICATES FOUND MONUMENT AS NOTED.

■ INDICATES NOTHING TO BE SET.

P# INDICATES BEARING AND DISTANCE OF LOT LINE PRODUCTION FROM LOT CORNER TO MONUMENT.

1 INDICATES LOCATION OF 1" I.P. TAGGED "L.S. 5557" OR SPIKE & WASHER STAMPED "L.S. 5557" OR LEAD, TACK & TAG "L.S. 5557" TO BE SET PER TRACT NO. 16155, M.M. 812/30-39.

2 INDICATES LOCATION OF 2" I.P. TAGGED "L.S. 5557" OR SPIKE & WASHER STAMPED "L.S. 5557" OR LEAD, TACK & TAG "L.S. 5557" TO BE SET PER TRACT NO. 16155, M.M. 812/30-39.

3 INDICATES LOCATION OF 1" I.P. TAGGED "L.S. 5557" OR SPIKE & WASHER STAMPED "L.S. 5557" OR LEAD, TACK & TAG "L.S. 5557" TO BE SET PER TRACT NO. 15884, M.M. 794/33-44.

GPS NO. 1417
FD. 2 1/2" IRON PIPE WITH 2" OCS
BRASS CAP STAMPED "GPS 1417 9-95"
PER R.S.B. 154/B-18
AND RECORDS ON FILE IN THE
ORANGE COUNTY SURVEYOR'S OFFICE.
N 2141450.558
E 6141583.535

EASEMENT NOTE:

(A) INDICATES A 20' WIDE EASEMENT FOR WATER LINE, SANITARY SEWER AND ACCESS PURPOSES DEDICATED HEREON TO THE SANTA MARGARITA WATER DISTRICT.

NOTE:

ALL R-3 STRUCTURES GREATER THAN 5,500 SQUARE FEET, OTHER STRUCTURES GREATER THAN 6,000 SQUARE FEET OR IDENTIFIED BY THE FIRE CHIEF, AND STRUCTURES OUT OF FIRE DEPARTMENT ACCESS OF 150 FEET SHALL BE PROTECTED BY AN AUTOMATIC FIRE SPRINKLER SYSTEM, IN A MANNER MEETING THE APPROVAL OF THE FIRE CHIEF.


SHEET 3 OF 8 SHEETS
SCALE 1" = 30'
78 NUMBERED LOTS AND LOTS
A THROUGH F, INCLUSIVE
ACREAGE: 12.208 ACRES
(ALL OF TENTATIVE
TRACT NO. 16104)

TRACT NO. 16104

IN UNINCORPORATED TERRITORY OF THE COUNTY OF ORANGE,
STATE OF CALIFORNIA

HUNSAKER AND ASSOCIATES IRVINE, INC.
RORY S. WILLIAMS, L.S. 6654
DATE OF SURVEY: DECEMBER, 2000

SEE SHEET 2 FOR BASIS OF BEARINGS,
DATUM STATEMENT, NOTES, MONUMENT
NOTES, EASEMENT NOTES AND SHEET
INDEX AND GPS CONTROL MAP.

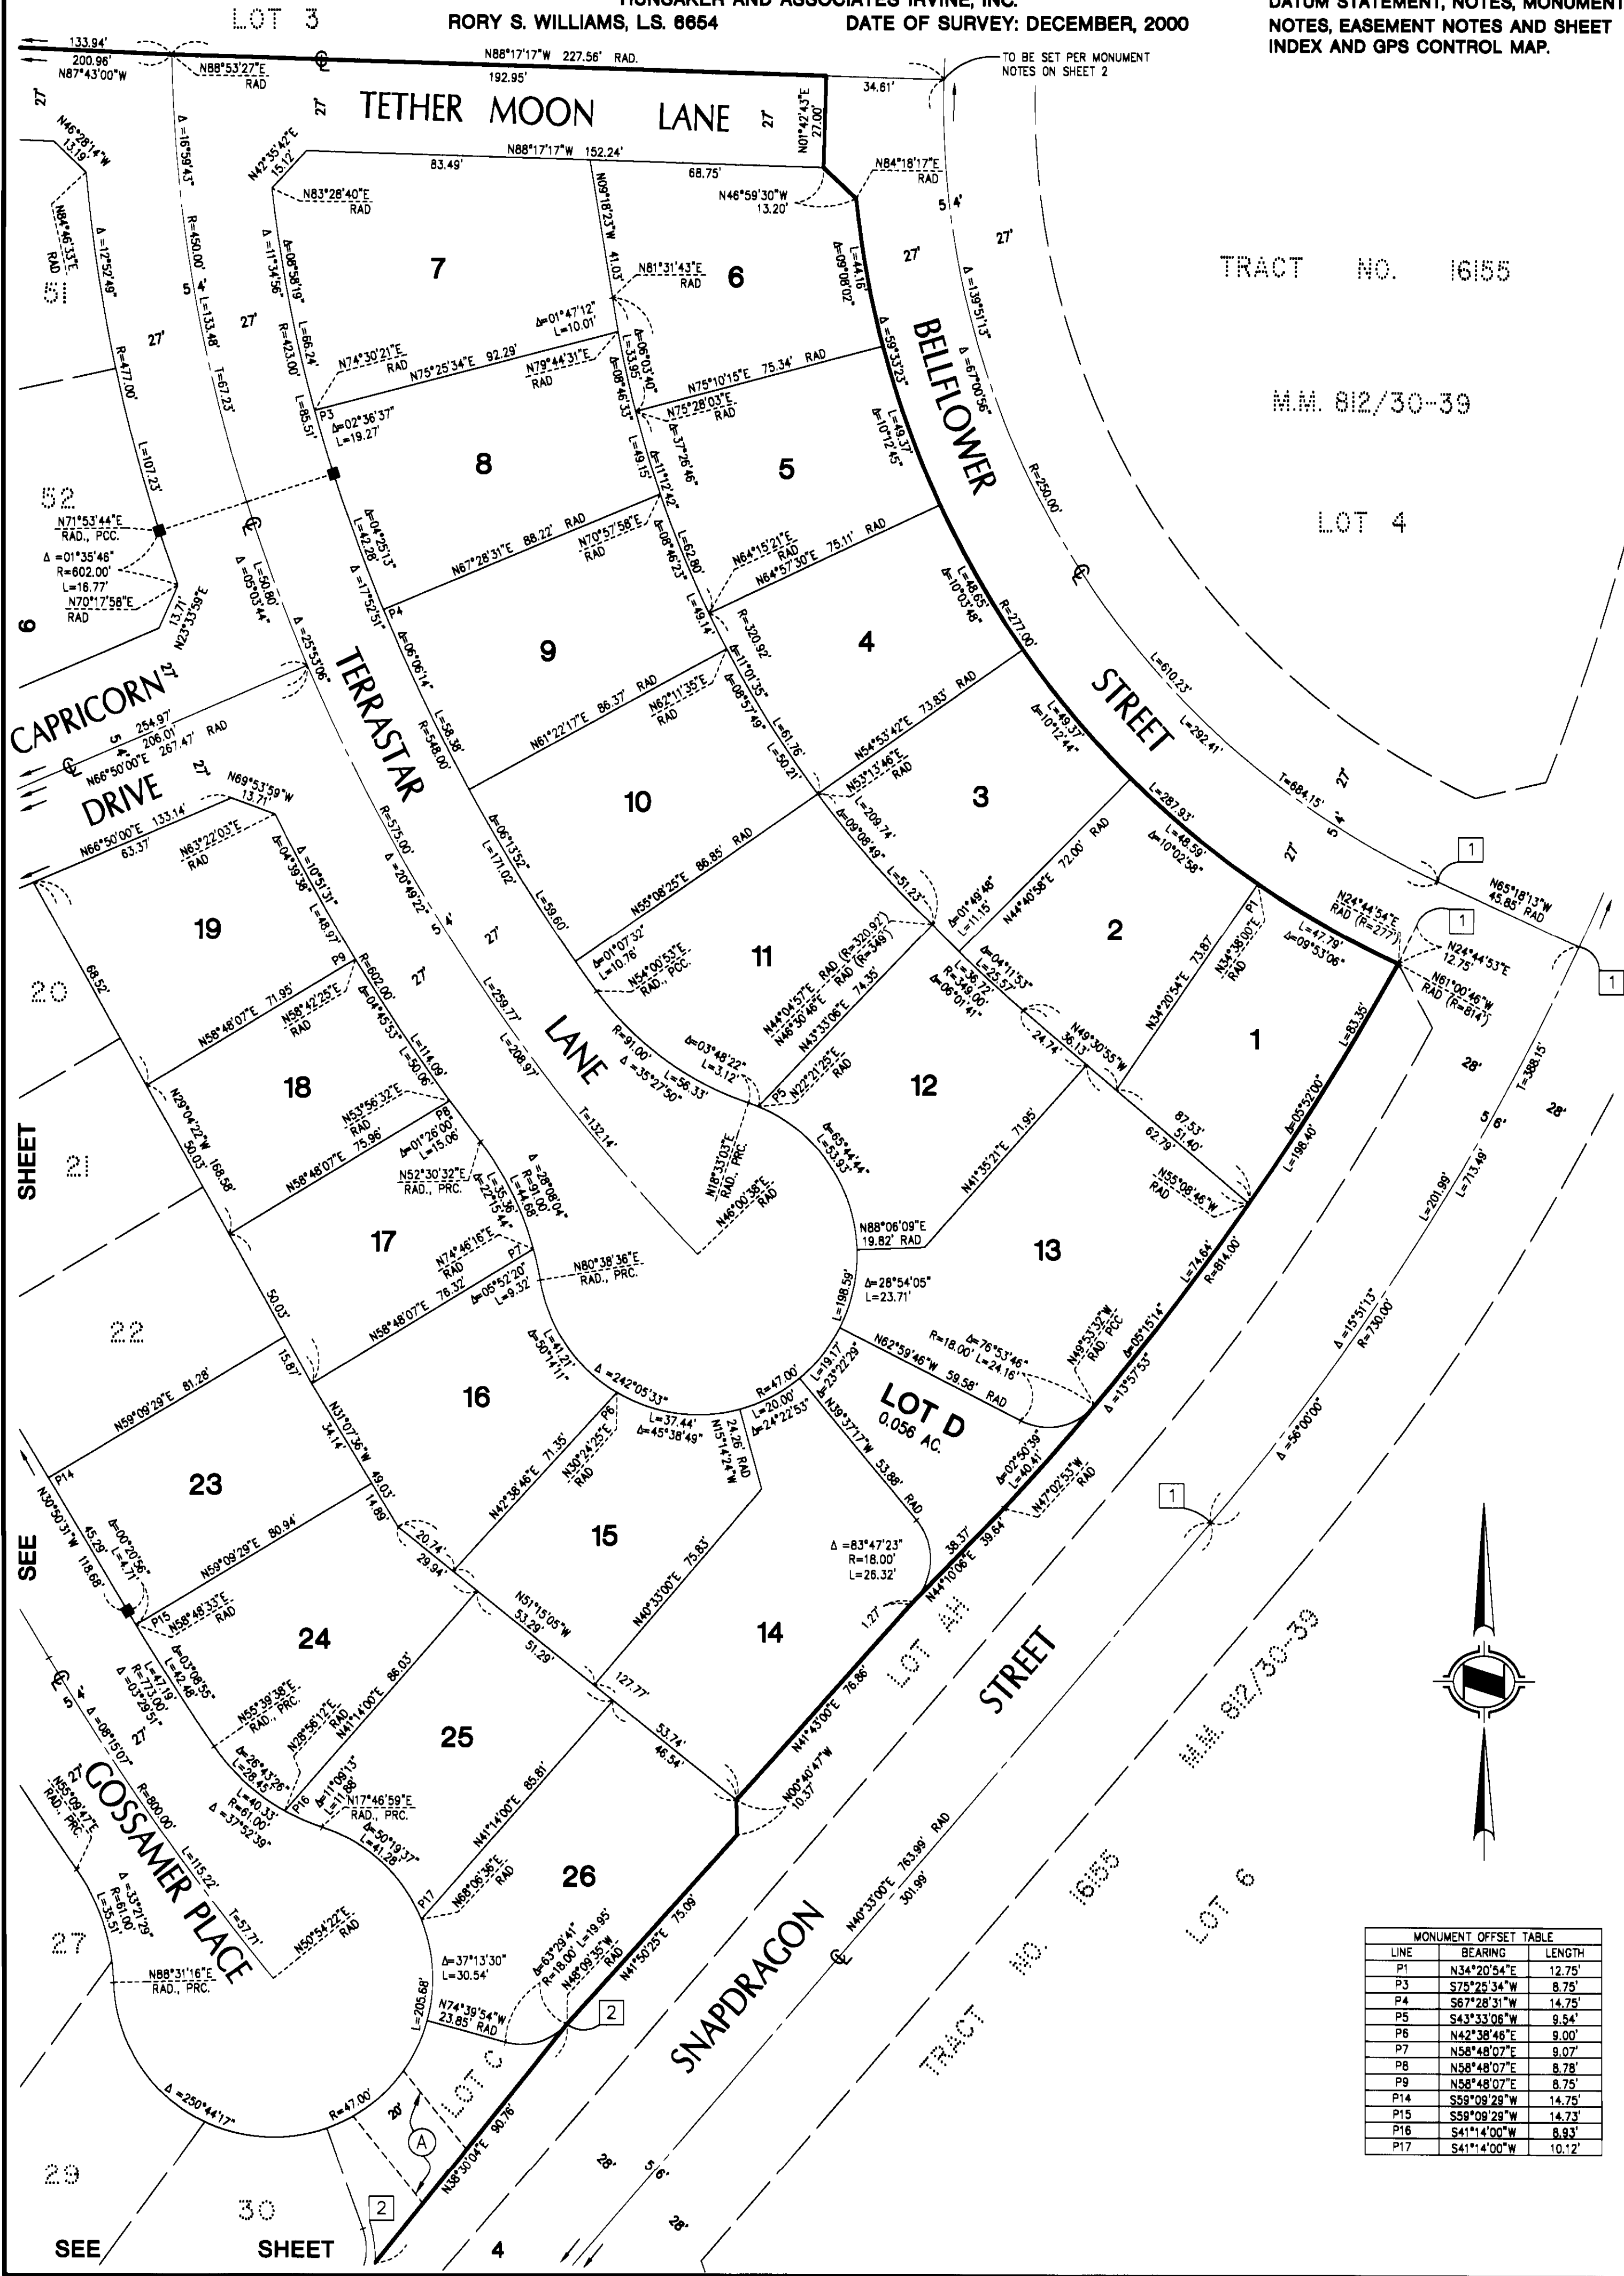


MONUMENT OFFSET TABLE		
LINE	BEARING	LENGTH
P1	N34°20'54"E	12.75'
P3	S75°25'34"W	8.75'
P4	S67°28'31"W	14.75'
P5	S43°33'06"W	9.54'
P6	N42°38'46"E	9.00'
P7	N58°48'07"E	9.07'
P8	N58°48'07"E	8.78'
P9	N58°48'07"E	8.75'
P14	S58°09'29"W	14.73'
P15	S58°09'29"W	14.73'
P16	S41°14'00"W	8.83'
P17	S41°14'00"W	10.12'

SHEET 4 OF 6 SHEETS
SCALE 1" = 30'
78 NUMBERED LOTS AND LOTS
A THROUGH F, INCLUSIVE
ACREAGE: 12.208 ACRES
(ALL OF TENTATIVE
TRACT NO. 16104)

TRACT NO. 16104

IN UNINCORPORATED TERRITORY OF THE COUNTY OF ORANGE,
STATE OF CALIFORNIA

HUNSAKER AND ASSOCIATES IRVINE, INC.
RORY S. WILLIAMS, L.S. 6654 DATE OF SURVEY: DECEMBER, 2000

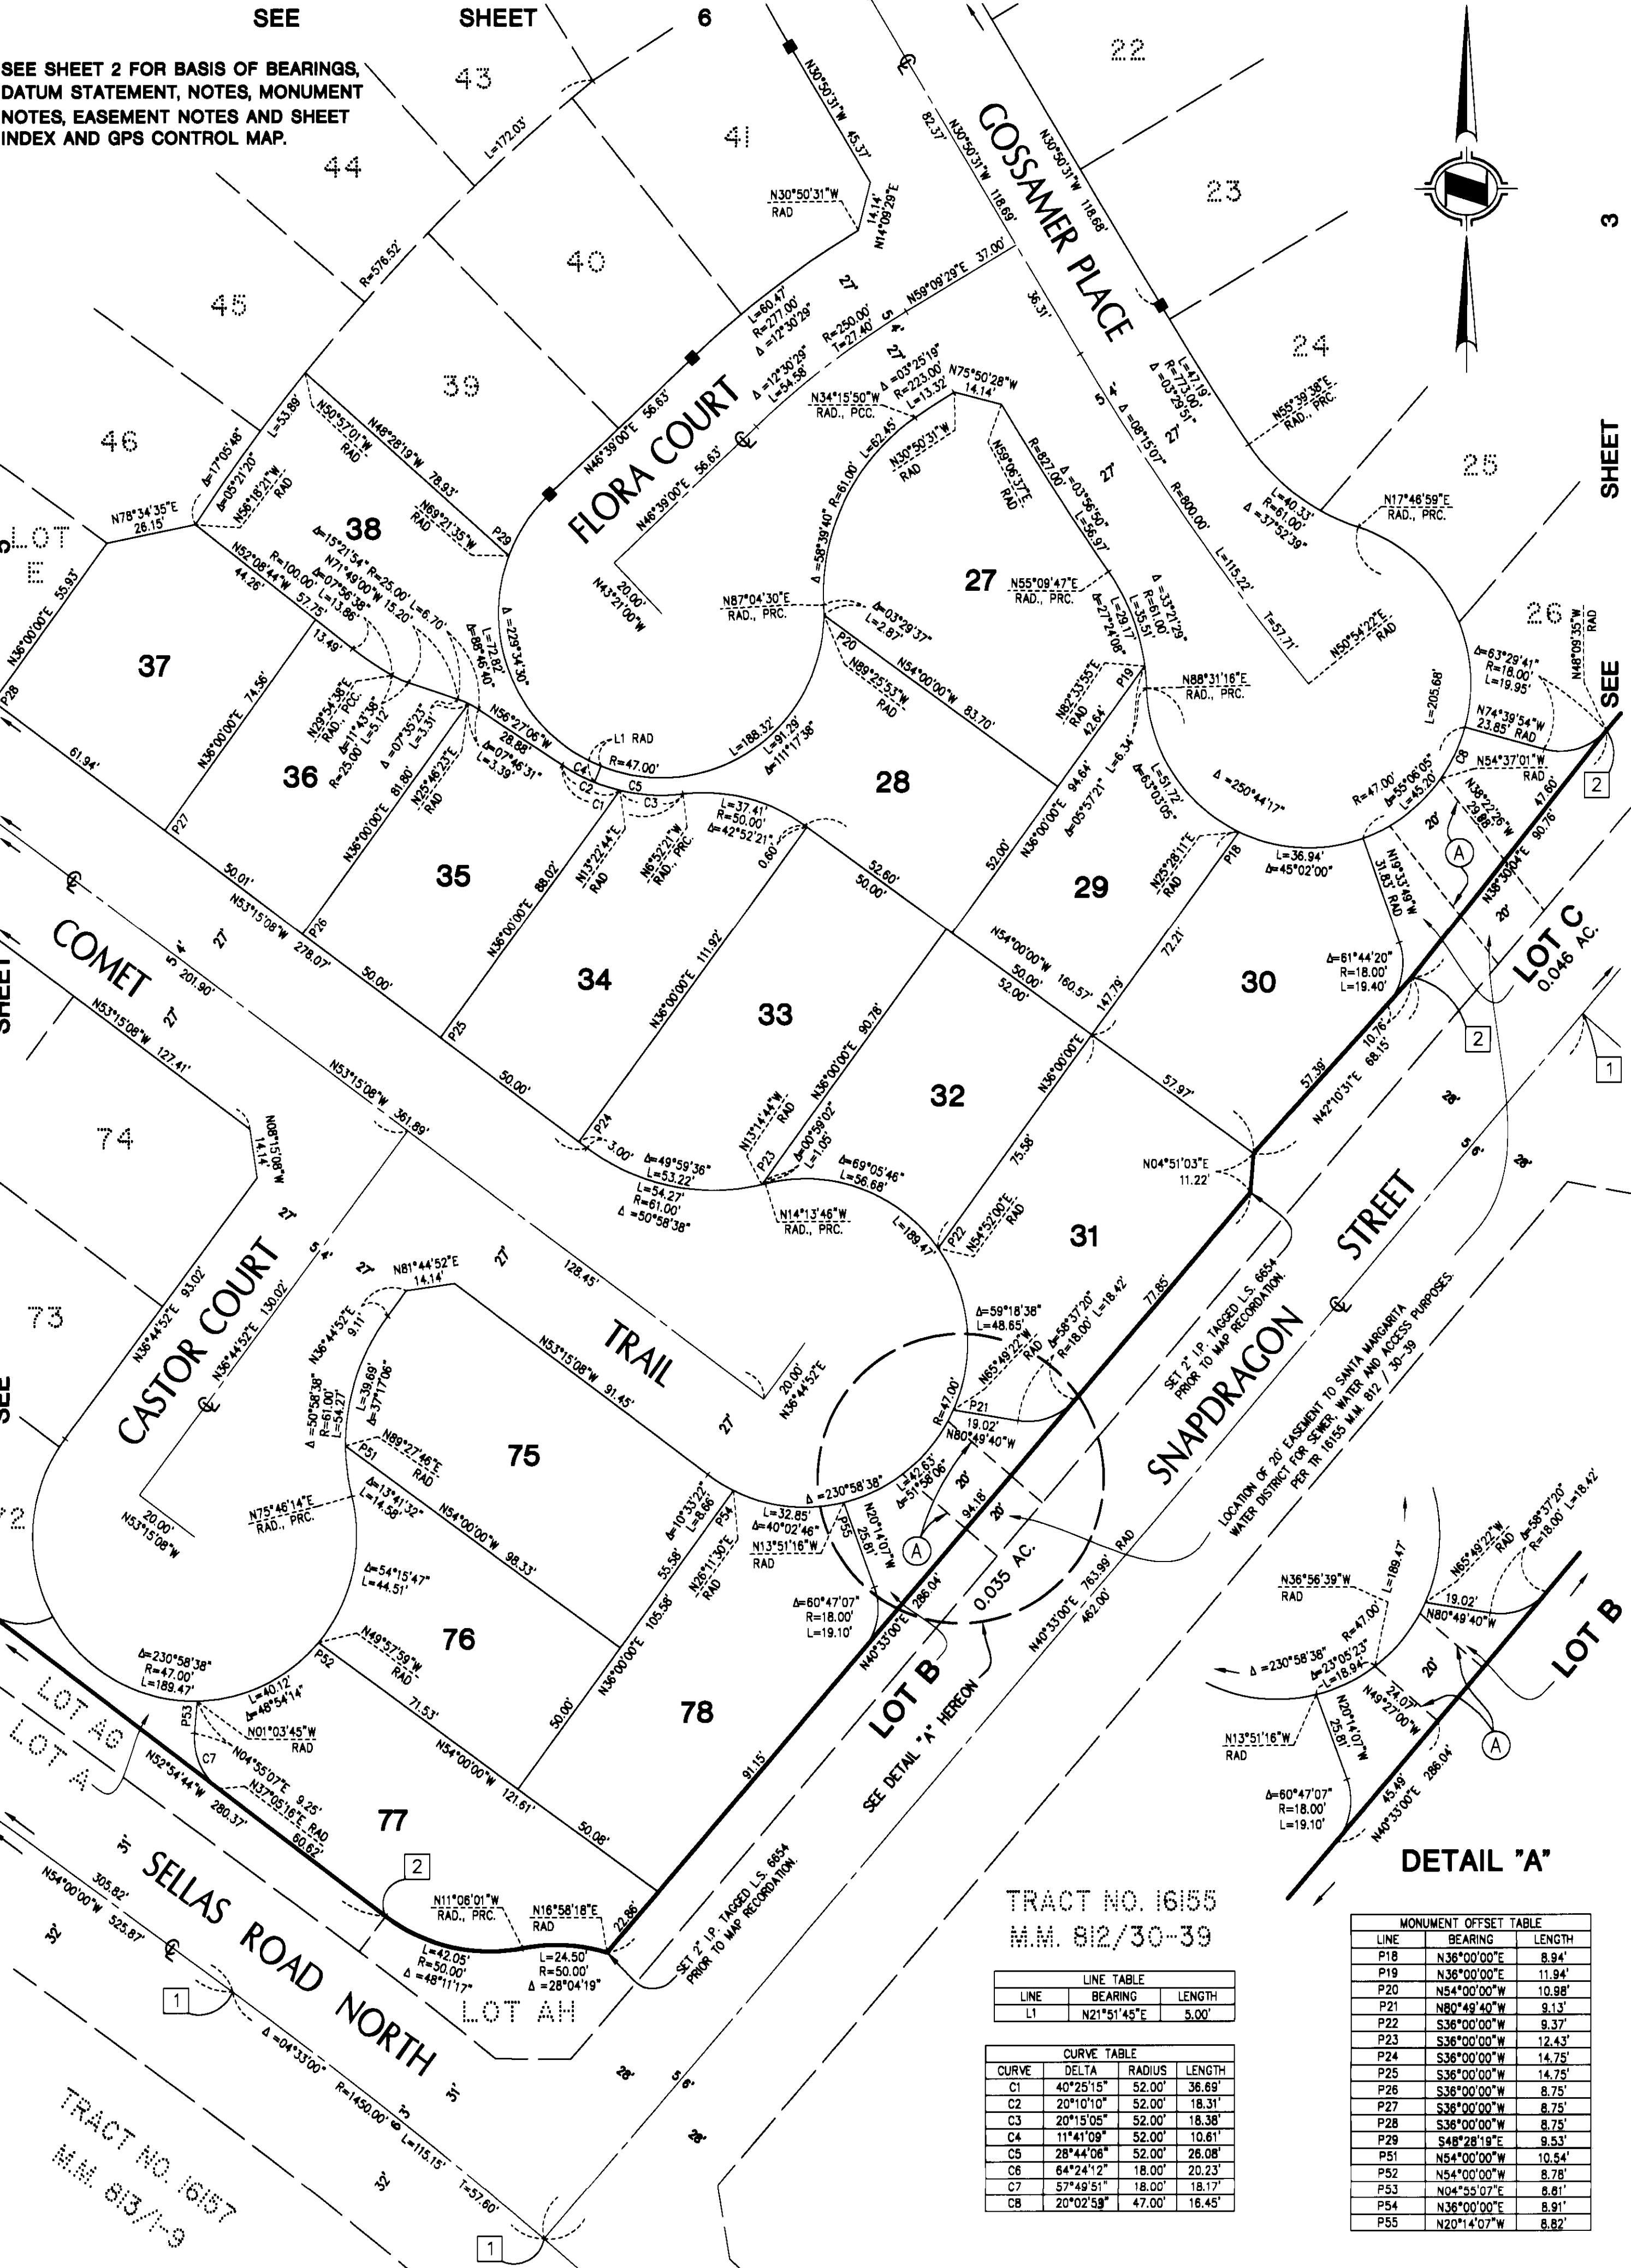

TRACT NO. 16155
M.M. 812/30-39

LINE TABLE		
LINE	BEARING	LENGTH
L1	N21°51'45"E	5.00'

CURVE TABLE			
CURVE	DELTA	RADIUS	LENGTH
C1	40°25'15"	52.00'	36.69'
C2	20°10'10"	52.00'	18.31'
C3	20°15'05"	52.00'	18.38'
C4	11°41'09"	52.00'	10.61'
C5	28°44'08"	52.00'	28.08'
C6	64°24'12"	18.00'	20.23'
C7	57°49'51"	18.00'	18.17'
C8	20°02'58"	47.00'	16.45'

MONUMENT OFFSET TABLE		
LINE	BEARING	LENGTH
P18	N36°00'00"E	8.94'
P19	N36°00'00"E	11.94'
P20	N54°00'00"W	10.98'
P21	N80°49'40"W	9.13'
P22	S36°00'00"W	9.37'
P23	S36°00'00"W	12.43'
P24	S36°00'00"W	14.75'
P25	S36°00'00"W	14.75'
P26	S36°00'00"W	8.75'
P27	S36°00'00"W	8.75'
P28	S36°00'00"W	8.75'
P29	S48°28'19"E	9.53'
P51	N54°00'00"W	10.54'
P52	N54°00'00"W	8.78'
P53	N04°55'07"E	8.81'
P54	N36°00'00"E	8.91'
P55	N20°14'07"W	8.82'

SHEET 5 OF 6 SHEETS
SCALE 1" = 30'
78 NUMBERED LOTS AND LOTS
A THROUGH F, INCLUSIVE
ACREAGE: 12,208 ACRES
(ALL OF TENTATIVE
TRACT NO. 16104)

TRACT NO. 16104

IN UNINCORPORATED TERRITORY OF THE COUNTY OF ORANGE,
STATE OF CALIFORNIA

HUNSAKER AND ASSOCIATES IRVINE, INC.

RORY S. WILLIAMS, L.S. 6654


DATE OF SURVEY: DECEMBER, 2000

SEE SHEET 2 FOR BASIS OF BEARINGS,
DATUM STATEMENT, NOTES, MONUMENT
NOTES, EASEMENT NOTES AND SHEET
INDEX AND GPS CONTROL MAP.

PORTION OF PCL. I

LLA LL 96-026,

INST. NO. 19960587414, O.R.

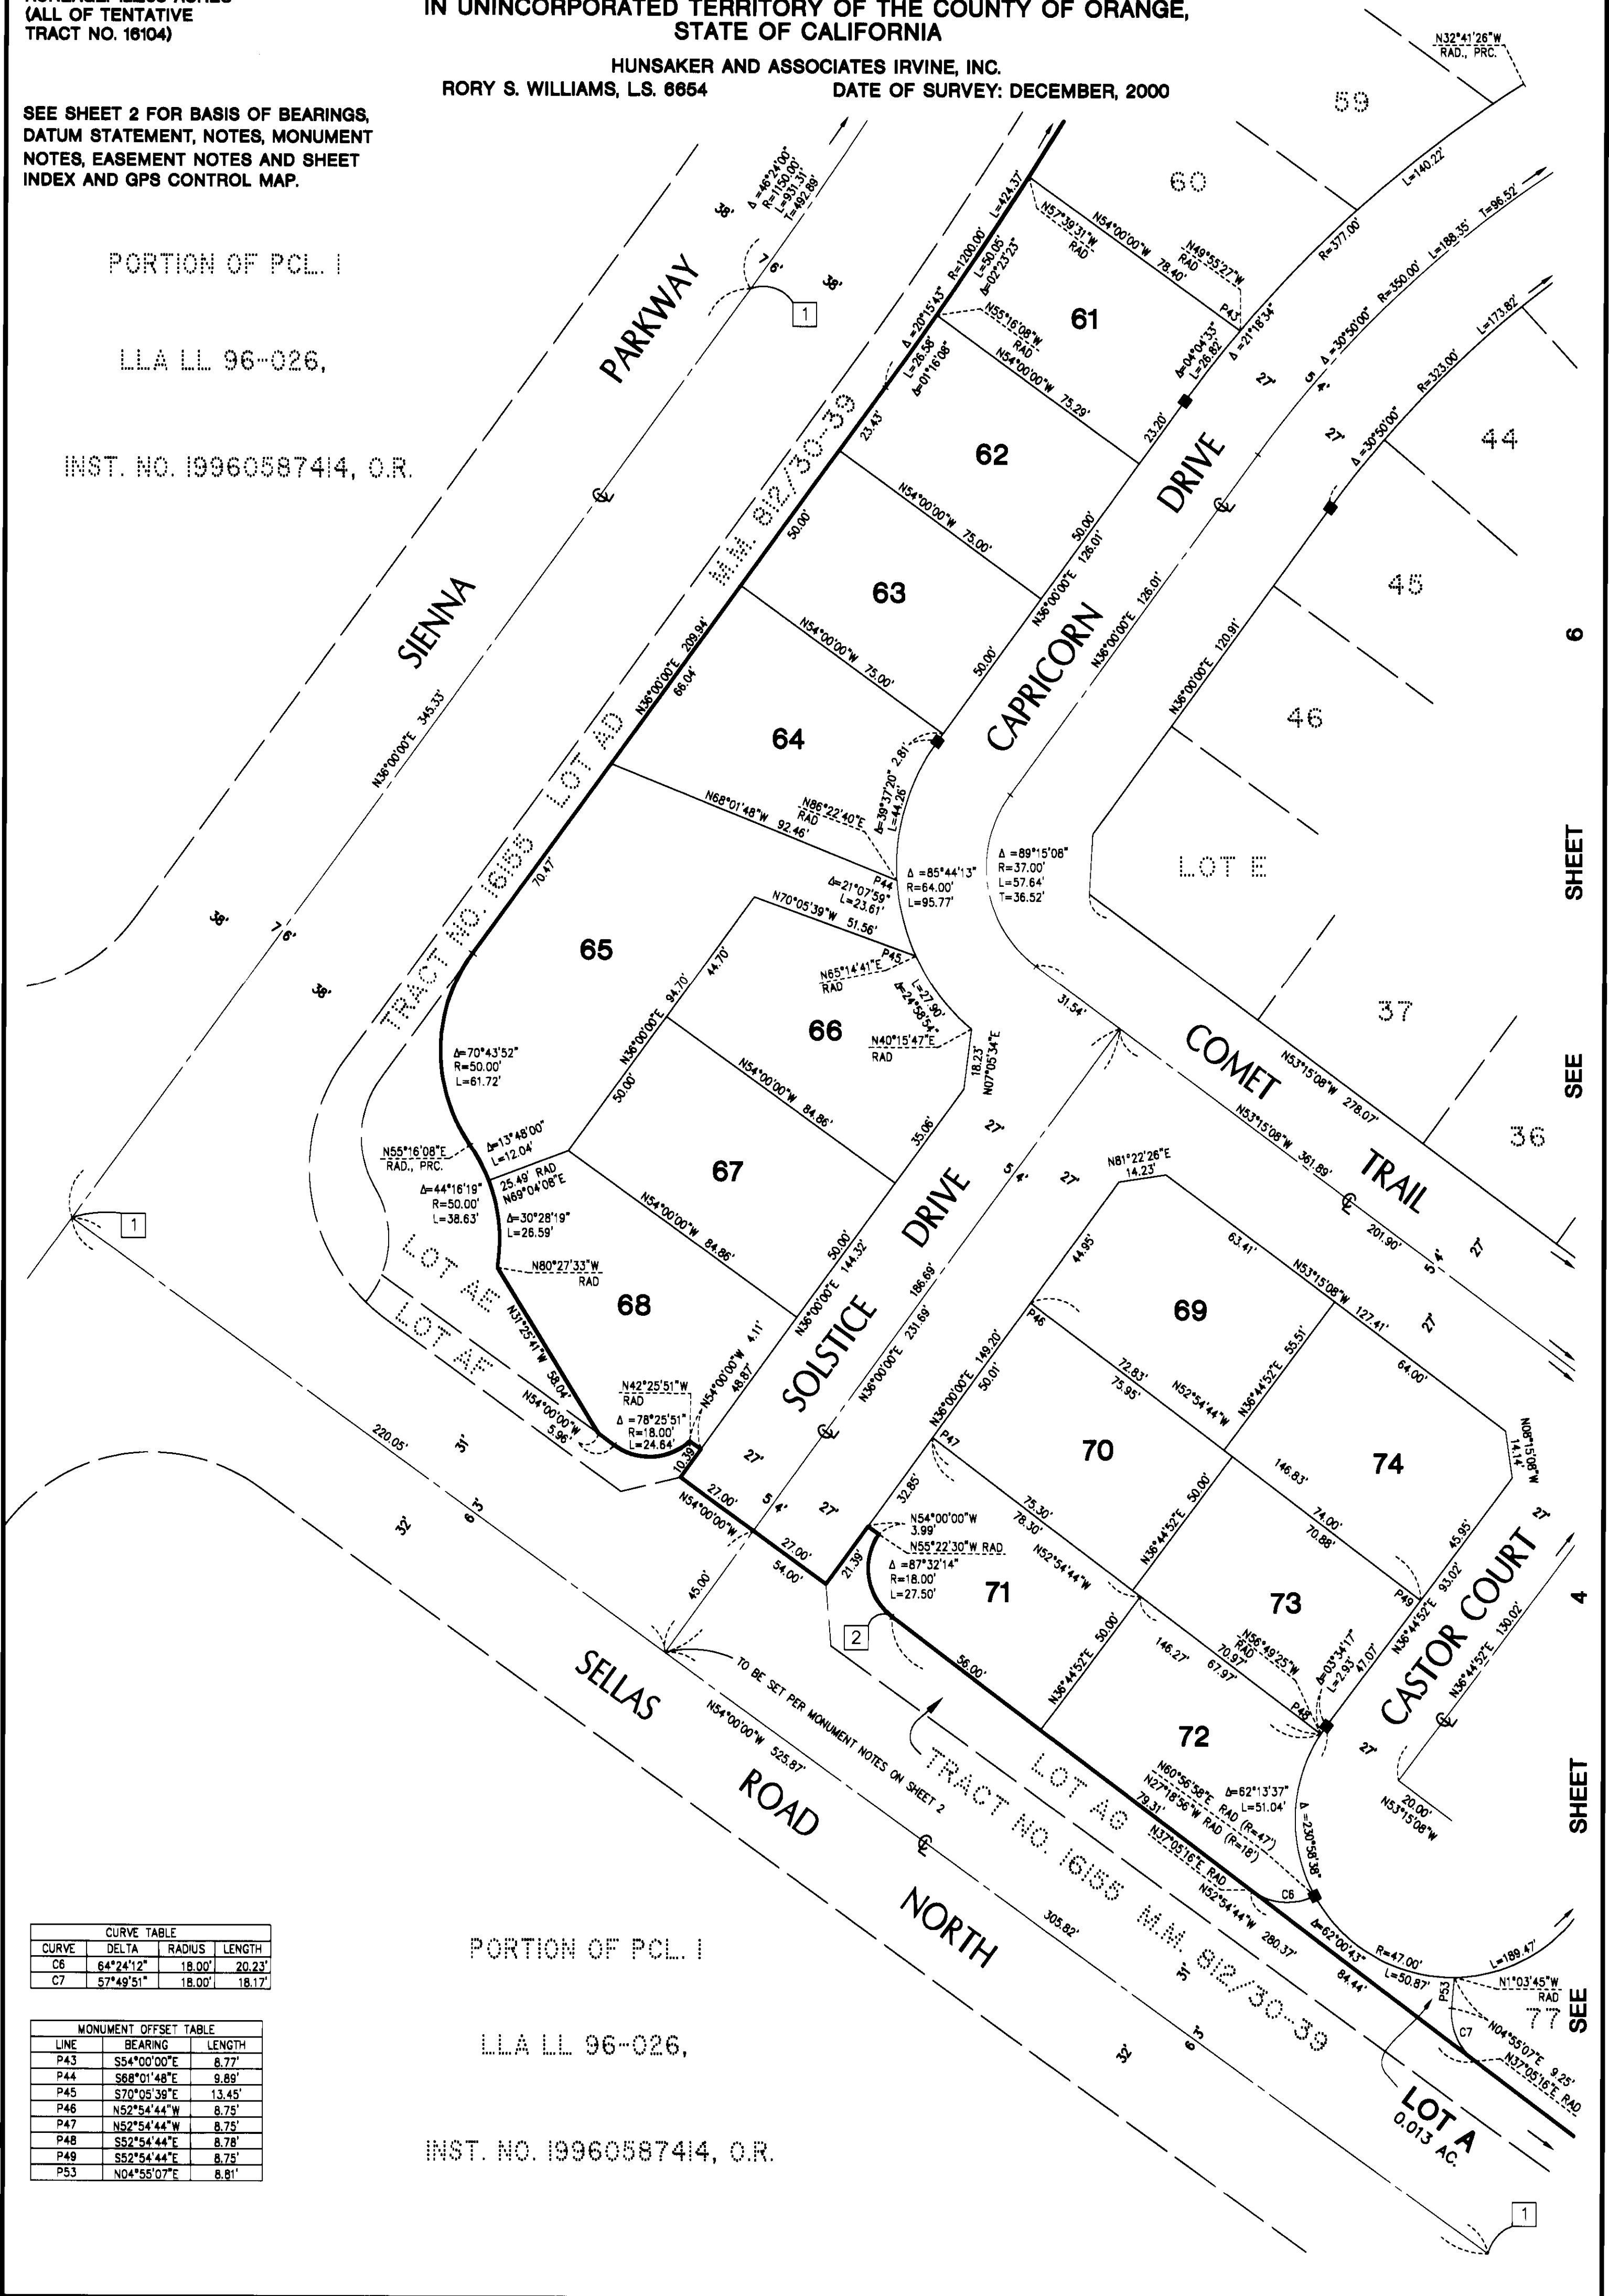

CURVE TABLE			
CURVE	DELTA	RADIUS	LENGTH
C6	64°24'12"	18.00'	20.23'
C7	57°49'51"	18.00'	18.17'

MONUMENT OFFSET TABLE		
LINE	BEARING	LENGTH
P43	S54°00'00"E	8.77'
P44	S68°01'48"E	9.89'
P45	S70°05'39"E	13.45'
P46	N52°54'44"W	8.75'
P47	N52°54'44"W	8.75'
P48	S52°54'44"E	8.78'
P49	S52°54'44"E	8.75'
P53	N04°55'07"E	8.81'

PORTION OF PCL. I

LLA LL 96-026,

INST. NO. 19960587414, O.R.

SHEET 5
SEE SHEET 4

821

39

SHEET 6 OF 6 SHEETS
SCALE 1" = 30'
78 NUMBERED LOTS AND LOTS
A THROUGH F, INCLUSIVE
ACREAGE: 12.208 ACRES
(ALL OF TENTATIVE
TRACT NO. 16104)

TRACT NO. 16104

IN UNINCORPORATED TERRITORY OF THE COUNTY OF ORANGE,
STATE OF CALIFORNIA

HUNSAKER AND ASSOCIATES IRVINE, INC.

RORY S. WILLIAMS, L.S. 6654

DATE OF SURVEY: DECEMBER, 2000

SEE SHEET 2 FOR BASIS OF BEARINGS,
DATUM STATEMENT, NOTES, MONUMENT
NOTES, EASEMENT NOTES AND SHEET
INDEX AND GPS CONTROL MAP.

TRACT NO. 16155

M.M. 812/30-39

LOT 3

MONUMENT OFFSET TABLE		
LINE	BEARING	LENGTH
P12	S59°09'29"W	8.76'
P13	S59°09'29"W	14.21'
P14	S59°09'29"W	14.75'
P28	S36°00'00"W	8.75'
P29	S48°28'19"E	9.53'
P30	S44°33'55"E	8.75'
P31	S38°11'25"E	8.75'
P32	N31°48'27"W	8.77'
P33	N42°12'43"W	8.76'
P34	N02°17'00"E	11.42'
P35	S18°36'33"E	8.78'
P36	S18°36'33"E	9.68'
P37	S18°36'33"E	14.02'
P38	S18°36'33"E	9.98'
P39	S30°33'08"E	8.90'
P40	S54°00'00"E	9.64'
P41	S54°00'00"E	9.31'
P42	S54°00'00"E	8.94'
P43	S54°00'00"E	8.77'

