

SHEET 1 OF 9 SHEETS

TRACT MAP NO. 16105

ALL OF TENTATIVE TRACT
MAP NO. 16105
TOTAL LOTS: 1-83 AND LOTS A-EE
TOTAL ACREAGE: 9.016 AC.
DATE OF SURVEY: APRIL, 2001

BLOCK 5057
MODULE 63

IN THE UNINCORPORATED TERRITORY OF THE COUNTY OF ORANGE,
STATE OF CALIFORNIA

BEING A SUBDIVISION OF PARCEL 1, AS SHOWN ON LOT LINE ADJUSTMENT
NO. LL 2001-013, PER INSTRUMENT NO. 20010651105, O.R. *
IN THE OFFICE OF THE COUNTY RECORDER OF SAID COUNTY, STATE OF CALIFORNIA

ADAMS - STREETER CIVIL ENGINEERING, INC. JAN A. ADAMS, R.C.E. 21687
DATE OF SURVEY: APRIL, 2001

ACCEPTED AND FILED AT THE
REQUEST OF

FIRST AMERICAN TITLE INSURANCE COMPANY

DATE OCTOBER 22, 2001TIME 1:14 P.M. FEE \$ 23.00INSTRUMENT # 20010743806BOOK 823 PAGE 18-26 M/MGARY L. GRANVILLE
COUNTY - CLERK RECORDERBY [Signature]
DEPUTY

OWNER'S CERTIFICATE:

WE, THE UNDERSIGNED, BEING ALL PARTIES HAVING ANY RECORD TITLE INTEREST IN THE LAND COVERED
BY THIS MAP, DO HEREBY CONSENT TO THE PREPARATION AND RECORDATION OF SAID MAP, AS SHOWN
WITHIN THE DISTINCTIVE BORDER LINE.

WE HEREBY DEDICATE TO THE PUBLIC FOR STREET PURPOSES: IRISH MOSS STREET & SKLAR STREET.

WE ALSO HEREBY DEDICATE TO THE COUNTY OF ORANGE:

~~AN EASEMENT FOR STORM DRAIN PURPOSES, AS SHOWN HEREON.~~
AN EASEMENT FOR EMERGENCY AND PUBLIC SERVICE VEHICULAR INGRESS-EGRESS AS SHOWN HEREON.

WE ALSO DEDICATE TO THE SANTA MARGARITA WATER DISTRICT, THE EASEMENTS FOR SEWER, WATER AND
AND ACCESS PURPOSES AS SHOWN ON SAID MAP, WHICH EASEMENTS SHALL BE SUBJECT TO THE
SAME TERMS AND CONDITIONS AS ARE SHOWN IN THAT CERTAIN EASEMENT RECORDED OCTOBER 6, 1980,
IN BOOK 13776, PAGE 341, OF OFFICIAL RECORDS, COUNTY OF ORANGE. THE SANTA MARGARITA WATER
DISTRICT SHALL RESTORE OTHER IMPROVEMENTS OR FACILITIES LOCATED WITHIN THE EASEMENT, IF IT
HAS CONSENTED TO THE LOCATION OF SUCH IMPROVEMENTS OR FACILITIES TO THE EXTENT THAT THE
EXERCISE OF ITS RIGHTS IN CONNECTION WITH THE EASEMENT IMPACTS OTHER IMPROVEMENTS OR FACILITIES
LOCATED WITHIN THE EASEMENT, HOWEVER, IN NO EVENT SHALL SANTA MARGARITA WATER DISTRICT BE
RESPONSIBLE FOR THE COST OF RELOCATING ITS FACILITIES IN THE EVENT OF CONFLICTS WITH SUCH
OTHER IMPROVEMENTS OR FACILITIES.

BARRATT-BAYWOOD I, LLC, A CALIFORNIA LIMITED LIABILITY COMPANY

[Signature]
G. Jack Becker
Senior Vice President

[Signature]
Stephen R. Reid
Vice President

DMB LADERA, LLC A DELAWARE LIMITED LIABILITY COMPANY AS BENEFICIARY UNDER A DEED
OF TRUST RECORDED FEBRUARY 13, 2001 AS INSTRUMENT NO. 20010079317, OF OFFICIAL RECORDS.
By: Rancho Mission Viejo, L.L.C., a Delaware Limited Liability Company,
as agent and/or manager

[Signature]
DONALD T. STRICKLAND
DIRECTOR OF COMMUNITY DEV.

[Signature]
STEPHEN C. SCHUBERT
EV. V.P.

GUARANTY BANK, A FEDERAL SAVINGS BANK AS BENEFICIARY UNDER A DEED OF TRUST
RECORDED FEBRUARY 13, 2001 AS INSTRUMENT NO. 20010079318, OF OFFICIAL RECORDS.

[Signature]
Scott C. Cox
Senior Vice President

[Signature]
JON M. LARSON
VICE PRESIDENT

STATE OF CALIFORNIA)
COUNTY OF San Diego)ss

ON THIS 26 DAY OF July, 2001, BEFORE ME, Stephanie C. Hagan A NOTARY,
PUBLIC IN AND FOR SAID STATE, PERSONALLY APPEARED Jack Becker AND Stephen R. Reid
PERSONALLY KNOWN TO ME (OR PROVED TO ME ON THE BASIS OF SATISFACTORY EVIDENCE) TO BE
THE PERSONS WHOSE NAMES ARE SUBSCRIBED TO THE WITHIN INSTRUMENT AND ACKNOWLEDGED TO ME
THAT THEY EXECUTED THE SAME IN THEIR AUTHORIZED CAPACITIES AND THAT BY THEIR SIGNATURES ON
THE INSTRUMENT THE PERSON OR THE ENTITY UPON BEHALF OF WHICH THE PERSONS ACTED, EXECUTED
THE INSTRUMENT.

WITNESS MY HAND:

[Signature]
NOTARY PUBLIC IN AND FOR SAID STATE

MY PRINCIPAL PLACE OF BUSINESS
IS IN San Diego COUNTY

Stephanie C. Hagan Commission #1254468 MY COMMISSION EXPIRES March 24, 2004
PRINT NAME

STATE OF CALIFORNIA)
COUNTY OF San Diego)ss

ON THIS 27th DAY OF July, 2001, BEFORE ME, Rosalinda I. Molina A NOTARY,
PUBLIC IN AND FOR SAID STATE, PERSONALLY APPEARED Scott C. Cox AND Jon M. Larson
PERSONALLY KNOWN TO ME (OR PROVED TO ME ON THE BASIS OF SATISFACTORY EVIDENCE) TO BE
THE PERSONS WHOSE NAMES ARE SUBSCRIBED TO THE WITHIN INSTRUMENT AND ACKNOWLEDGED TO ME
THAT THEY EXECUTED THE SAME IN THEIR AUTHORIZED CAPACITIES AND THAT BY THEIR SIGNATURES ON
THE INSTRUMENT THE PERSON OR THE ENTITY UPON BEHALF OF WHICH THE PERSONS ACTED, EXECUTED
THE INSTRUMENT.

WITNESS MY HAND:

[Signature]
NOTARY PUBLIC IN AND FOR SAID STATE

MY PRINCIPAL PLACE OF BUSINESS
IS IN San Diego COUNTY

Rosalinda I. Molina MY COMMISSION EXPIRES June 13, 2004
PRINT NAME

STATE OF CALIFORNIA)
COUNTY OF Orange)ss

ON THIS 9th DAY OF August, 2001, BEFORE ME, Jeanine Carta-Hanson A NOTARY,
PUBLIC IN AND FOR SAID STATE, PERSONALLY APPEARED Donald T. Strickland AND Stephen C. Schubert
PERSONALLY KNOWN TO ME (OR PROVED TO ME ON THE BASIS OF SATISFACTORY EVIDENCE) TO BE
THE PERSONS WHOSE NAMES ARE SUBSCRIBED TO THE WITHIN INSTRUMENT AND ACKNOWLEDGED TO ME
THAT THEY EXECUTED THE SAME IN THEIR AUTHORIZED CAPACITIES AND THAT BY THEIR SIGNATURES ON
THE INSTRUMENT THE PERSON OR THE ENTITY UPON BEHALF OF WHICH THE PERSONS ACTED, EXECUTED
THE INSTRUMENT.

WITNESS MY HAND:

[Signature]
NOTARY PUBLIC IN AND FOR SAID STATE

MY PRINCIPAL PLACE OF BUSINESS
IS IN _____ COUNTY

Jeanine CARTA-HANSON MY COMMISSION EXPIRES Feb. 25, 2003
PRINT NAME

SIGNATURE OMISSIONS

PURSUANT TO THE PROVISIONS OF SECTION 66436 (a)(3) OF THE SUBDIVISION MAP ACT, THE FOLLOWING
SIGNATURES HAVE BEEN OMITTED:

COUNTY OF ORANGE, HOLDER OF AN EASEMENT FOR STORM DRAIN PURPOSES, AS DEDICATED ON
TRACT MAP NO. 16155, BOOK 812, PAGES 30-39, OF OFFICIAL RECORDS.

DMB LADERA, LLC, HOLDER OF EASEMENTS FOR CONSTRUCTION, TELECOMMUNICATIONS, PUBLIC UTILITIES,
SURFACE RUNOFF, PUBLIC STREETS AND IRRIGATION PURPOSES, RECORDED FEBRUARY 13, 2001
PER INSTRUMENT NO. 20010079315, OF OFFICIAL RECORDS.

LADERA DEVELOPMENT COMPANY, LLC, HOLDER OF OIL, GAS AND MINERAL RIGHTS, RECORDED
DECEMBER 10, 1996 AS INSTRUMENT NO. 19960624029, OF OFFICIAL RECORDS.


SANTA MARGARITA WATER DISTRICT, HOLDER OF AN EASEMENT FOR SEWER AND WATER PURPOSES, AS
DEDICATED ON TRACT MAP NO. 16155, BOOK 812, PAGES 30-39, OF OFFICIAL RECORDS.

*together with a portion of
Irish Moss Street

ENGINEER'S STATEMENT

I HEREBY STATE THAT THIS MAP CONSISTING OF 9 SHEETS CORRECTLY REPRESENTS TRUE AND
COMPLETE SURVEY AS SHOWN MADE IN APRIL, 2001, WAS MADE BY ME OR UNDER MY DIRECTION;
THAT THE MONUMENTS ARE OF THE CHARACTER AND OCCUPY (OR WILL OCCUPY) THE POSITIONS
INDICATED BY SAID MAP; AND THAT SAID MONUMENTS ARE SUFFICIENT TO ENABLE THE SURVEY TO
BE RETRACED.

[Signature]
JAN A. ADAMS, R.C.E. 21687
EXPIRES: 9/30/01

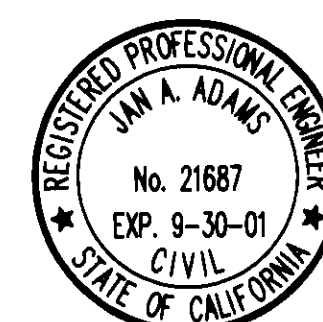


COUNTY SURVEYOR'S STATEMENT

I HEREBY STATE THAT I HAVE EXAMINED THIS MAP AND HAVE FOUND IT TO BE SUBSTANTIALLY IN
CONFORMANCE WITH THE TENTATIVE MAP AS FILED WITH, AMENDED AND APPROVED BY THE ORANGE
COUNTY SUBDIVISION COMMITTEE; THAT ALL PROVISIONS OF THE SUBDIVISION MAP ACT AND COUNTY
SUBDIVISION REGULATIONS HAVE BEEN COMPLIED WITH AND I AM SATISFIED SAID MAP IS TECHNICALLY
CORRECT.

DATED THIS 4TH DAY OF OCTOBER, 2001

[Signature]
JOHN CANAS, COUNTY SURVEYOR
LS 4408 EXPIRATION DATE: 9-30-05

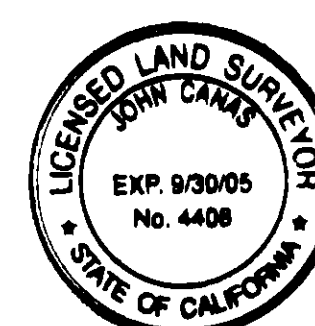

COUNTY TREASURER - TAX COLLECTOR'S CERTIFICATE

STATE OF CALIFORNIA)
COUNTY OF ORANGE)ss

I HEREBY CERTIFY THAT ACCORDING TO THE RECORDS OF MY OFFICE THERE ARE NO LIENS AGAINST THE
LAND COVERED BY THIS MAP OR ANY PART THEREOF FOR UNPAID STATE, COUNTY, MUNICIPAL OR LOCAL
TAXES OR SPECIAL ASSESSMENTS COLLECTED AS TAXES, EXCEPT TAXES OR SPECIAL ASSESSMENTS
COLLECTED AS TAXES NOT YET PAYABLE.

AND DO ALSO CERTIFY TO THE RECORDER OF ORANGE COUNTY THAT THE PROVISIONS OF THE
SUBDIVISION MAP ACT HAVE BEEN COMPLIED WITH REGARDING DEPOSITS TO SECURE THE PAYMENT OF
TAXES OR SPECIAL ASSESSMENTS COLLECTED AS TAXES ON THE LAND COVERED BY THIS MAP.

DATED THIS 17th DAY OF August, 2001

JOHN M. W. MOORLACH
COUNTY TREASURER - TAX COLLECTOR

BY [Signature]
DEPUTY TREASURER - TAX COLLECTOR

CLERK OF THE BOARD OF SUPERVISORS'S CERTIFICATE

STATE OF CALIFORNIA)
COUNTY OF ORANGE)ss

I HEREBY CERTIFY THAT THIS MAP PRESENTED FOR APPROVAL TO THE BOARD OF SUPERVISORS OF
ORANGE COUNTY AT A REGULAR MEETING THEREOF HELD ON THE 16th DAY OF October,
2001, AND THAT THEREUPON SAID BOARD DID, BY AN ORDER DULY PASSED AND ENTERED, APPROVE
SAID MAP AND DID ACCEPT ON BEHALF OF THE PUBLIC, SUBJECT TO IMPROVEMENTS; THE DEDICATION FOR
STREET PURPOSES OF: IRISH MOSS STREET & SKLAR STREET.

AND DID ACCEPT ON BEHALF OF THE COUNTY OF ORANGE:

~~THE EASEMENT FOR STORM DRAIN PURPOSES, AS DEDICATED.~~
THE EASEMENT FOR EMERGENCY AND PUBLIC SERVICE VEHICULAR INGRESS-EGRESS, AS DEDICATED.

WE ALSO HEREBY ABANDON, PURSUANT TO SECTION 66434 (g) OF THE SUBDIVISION MAP ACT,
THAT PORTION OF IRISH MOSS STREET WITHIN THE BOUNDARY OF THIS MAP WHICH WAS ACQUIRED BY THE
COUNTY OF ORANGE PER THE MAP OF TRACT NO. 16155 IN BOOK 812 PAGES 30 THROUGH 39, INCLUSIVE,
OF MISCELLANEOUS MAPS, RECORDS OF ORANGE COUNTY, CALIFORNIA, AS SHOWN ON THIS MAP.

AND DID ALSO APPROVE SUBJECT MAP PURSUANT TO THE PROVISIONS OF SECTION 66436 (a)(3)(A) OF
THE SUBDIVISION MAP ACT.

DATED THIS 16th DAY OF OCTOBER, 2001.

[Signature]
DARLENE J. BLOOM, CLERK OF THE BOARD OF SUPERVISORS



CERTIFICATE OF ACCEPTANCE

THE UNDERSIGNED, BEING THE DULY APPOINTED AGENT OF THE SANTA MARGARITA WATER DISTRICT,
A PUBLIC CORPORATION OF ORANGE COUNTY, CALIFORNIA, PURSUANT TO ITS RESOLUTION NO. 88-10-2,
DOES HEREBY ACCEPT ON BEHALF OF SAID DISTRICT THE EASEMENTS FOR SEWER, WATER AND ACCESS
PURPOSES, AS DEDICATED AND AS SHOWN ON THIS TRACT MAP, BY AND BETWEEN THE SANTA MARGARITA
WATER DISTRICT AND BARRATT-BAYWOOD, LLC, AND DOES HEREBY CERTIFY THAT THE GRANTEE CONSENTS
TO THE RECORDATION OF SAID TRACT.

BY: [Signature]
DANIEL R. FERONS, CHIEF ENGINEER
SANTA MARGARITA WATER DISTRICT

STATE OF CALIFORNIA)
COUNTY OF ORANGE)ss

ON THIS 10th DAY OF August, 2001, BEFORE ME, ANDREA M. EVANS, A NOTARY,
PUBLIC IN AND FOR SAID STATE, PERSONALLY APPEARED Daniel R. Ferons PERSONALLY KNOWN TO ME
(OR PROVED TO ME ON THE BASIS OF SATISFACTORY EVIDENCE) TO BE THE PERSON WHOSE NAME IS
SUBSCRIBED TO THE WITHIN INSTRUMENT AND ACKNOWLEDGED TO ME THAT HE EXECUTED THE SAME IN
HIS AUTHORIZED CAPACITY AND THAT BY HIS SIGNATURE ON THE INSTRUMENT THE PERSON, OR THE
ENTITY UPON BEHALF OF WHICH THE PERSON ACTED, EXECUTED THE INSTRUMENT.

WITNESS MY HAND:

[Signature]
NOTARY PUBLIC IN AND FOR SAID STATE

MY PRINCIPAL PLACE OF BUSINESS
IS IN ORANGE COUNTY

ANDREA M. EVANS
PRINT NAME

MY COMMISSION EXPIRES 04-08-04

PATH: M:\991289\mmaping\TM\
DWG NAME: TM1

DATE: 4/04/2001
TIME: 1:08 p.m.

* DMB LADERA, L.L.C., Holder of Easements, Covenants and Conditions, Recorded September 14, 2001, as Instrument No. 20010651107, Official Records.

023

18

SHEET 2 OF 9 SHEETS

ALL OF TENTATIVE TRACT
MAP NO. 16105
TOTAL LOTS: 1-83 AND LOTS A-EE
TOTAL ACREAGE: 9.016 AC.
DATE OF SURVEY: APRIL, 2001

TRACT MAP NO. 16105


IN THE UNINCORPORATED TERRITORY OF THE COUNTY OF ORANGE,
STATE OF CALIFORNIA

ADAMS - STREETER CIVIL ENGINEERING, INC. JAN A. ADAMS, R.C.E. 21687
DATE OF SURVEY: APRIL, 2001

LETTERED LOT INFORMATION

LOT	AREA	USE
A	0.380 AC	PRIVATE STREET
B	0.732 AC	PRIVATE STREET
C	0.163 AC	PRIVATE STREET
D	0.116 AC	PRIVATE STREET
E	0.164 AC	PRIVATE STREET
F	0.045 AC	PRIVATE STREET
G	0.143 AC	PRIVATE STREET
H	0.187 AC	PRIVATE STREET
I	0.094 AC	PRIVATE STREET
J	0.084 AC	PRIVATE STREET
K	0.137 AC	PRIVATE STREET
L	0.095 AC	OPEN SPACE
M	0.052 AC	OPEN SPACE
N	0.064 AC	OPEN SPACE
O	0.199 AC	OPEN SPACE
P	0.184 AC	OPEN SPACE
Q	0.081 AC	OPEN SPACE
R	0.062 AC	OPEN SPACE
S	0.067 AC	OPEN SPACE
T	0.090 AC	OPEN SPACE
U	0.004 AC	OPEN SPACE
V	0.099 AC	OPEN SPACE
W	0.114 AC	OPEN SPACE
X	0.115 AC	OPEN SPACE
Y	0.121 AC	OPEN SPACE
Z	0.006 AC	OPEN SPACE
AA	0.152 AC	OPEN SPACE
BB	0.007 AC	OPEN SPACE
CC	0.163 AC	OPEN SPACE
DD	0.008 AC	OPEN SPACE
EE	0.097 AC	OPEN SPACE

BOUNDARY CONTROL AND SHEET INDEX MAP

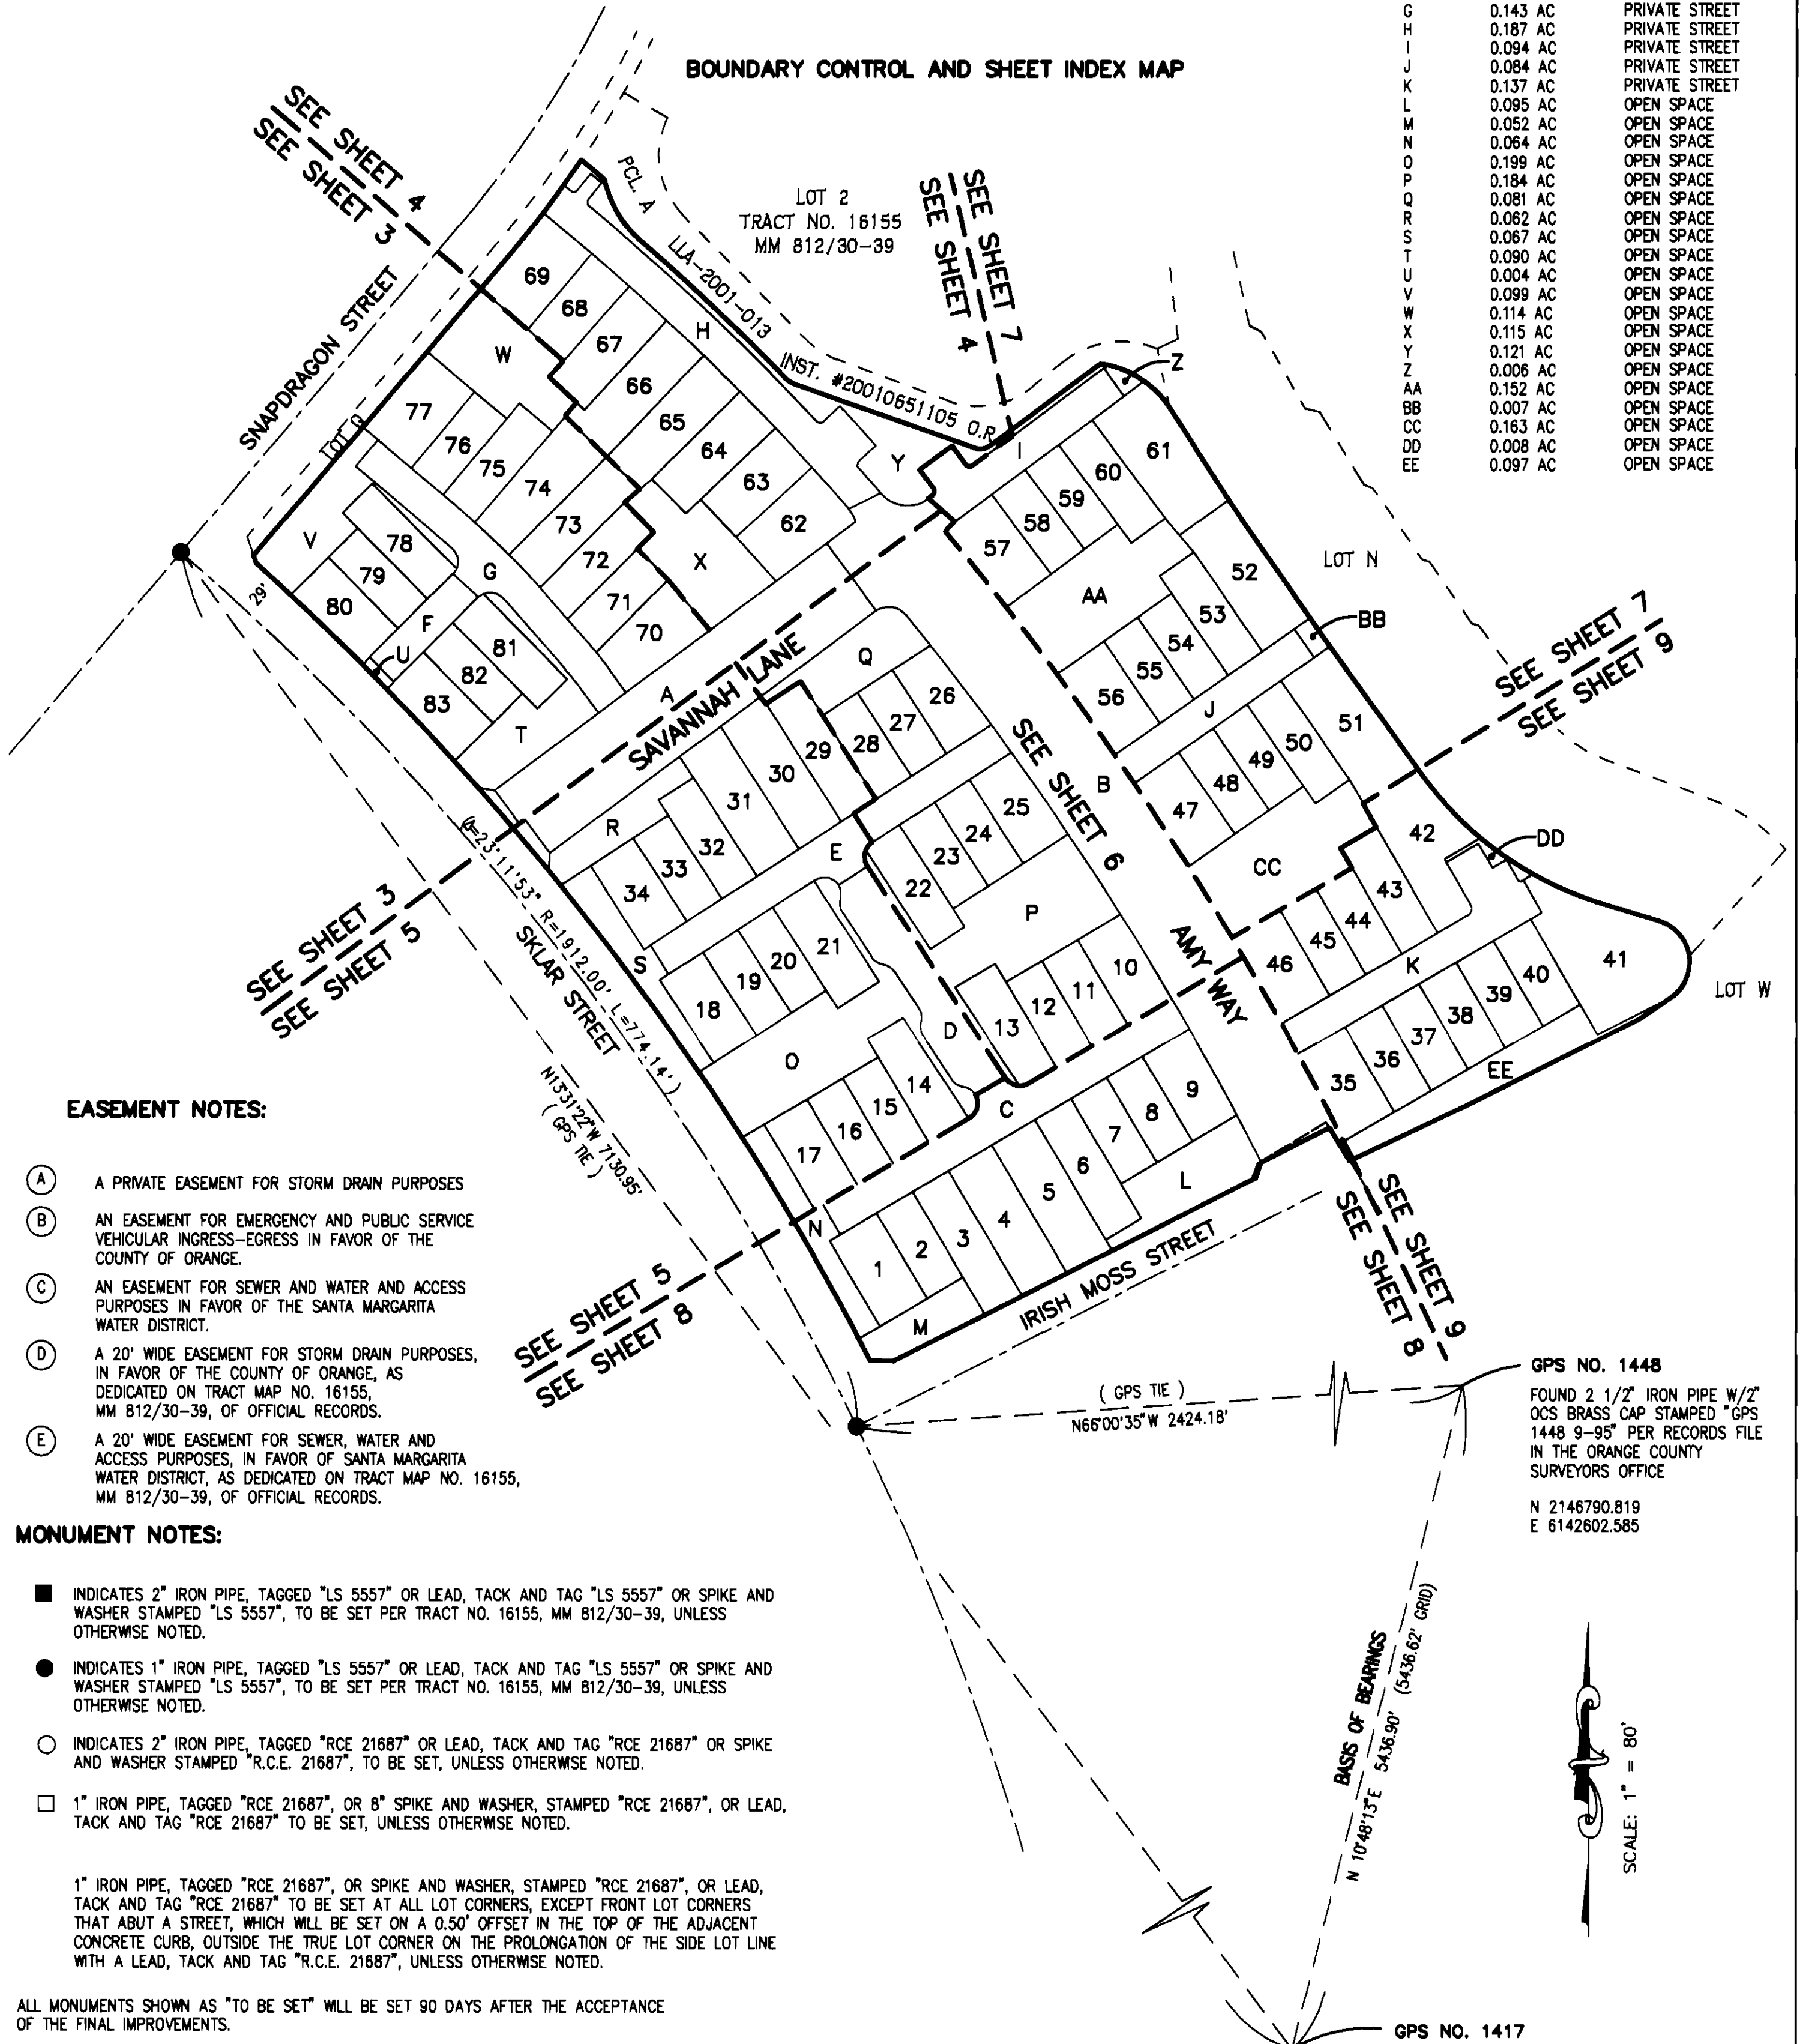

EASEMENT NOTES:

- (A) A PRIVATE EASEMENT FOR STORM DRAIN PURPOSES
- (B) AN EASEMENT FOR EMERGENCY AND PUBLIC SERVICE VEHICULAR INGRESS-EGRESS IN FAVOR OF THE COUNTY OF ORANGE.
- (C) AN EASEMENT FOR SEWER AND WATER AND ACCESS PURPOSES IN FAVOR OF THE SANTA MARGARITA WATER DISTRICT.
- (D) A 20' WIDE EASEMENT FOR STORM DRAIN PURPOSES, IN FAVOR OF THE COUNTY OF ORANGE, AS DEDICATED ON TRACT MAP NO. 16155, MM 812/30-39, OF OFFICIAL RECORDS.
- (E) A 20' WIDE EASEMENT FOR SEWER, WATER AND ACCESS PURPOSES, IN FAVOR OF SANTA MARGARITA WATER DISTRICT, AS DEDICATED ON TRACT MAP NO. 16155, MM 812/30-39, OF OFFICIAL RECORDS.

MONUMENT NOTES:

- INDICATES 2" IRON PIPE, TAGGED "LS 5557" OR LEAD, TACK AND TAG "LS 5557" OR SPIKE AND WASHER STAMPED "LS 5557", TO BE SET PER TRACT NO. 16155, MM 812/30-39, UNLESS OTHERWISE NOTED.
 - INDICATES 1" IRON PIPE, TAGGED "LS 5557" OR LEAD, TACK AND TAG "LS 5557" OR SPIKE AND WASHER STAMPED "LS 5557", TO BE SET PER TRACT NO. 16155, MM 812/30-39, UNLESS OTHERWISE NOTED.
 - INDICATES 2" IRON PIPE, TAGGED "RCE 21687" OR LEAD, TACK AND TAG "RCE 21687" OR SPIKE AND WASHER STAMPED "R.C.E. 21687", TO BE SET, UNLESS OTHERWISE NOTED.
 - 1" IRON PIPE, TAGGED "RCE 21687", OR 8" SPIKE AND WASHER, STAMPED "RCE 21687", OR LEAD, TACK AND TAG "R.C.E. 21687" TO BE SET, UNLESS OTHERWISE NOTED.
- 1" IRON PIPE, TAGGED "RCE 21687", OR SPIKE AND WASHER, STAMPED "RCE 21687", OR LEAD, TACK AND TAG "RCE 21687" TO BE SET AT ALL LOT CORNERS, EXCEPT FRONT LOT CORNERS THAT ADJ. A STREET, WHICH WILL BE SET ON A 0.50' OFFSET IN THE TOP OF THE ADJACENT CONCRETE CURB, OUTSIDE THE TRUE LOT CORNER ON THE PROLONGATION OF THE SIDE LOT LINE WITH A LEAD, TACK AND TAG "R.C.E. 21687", UNLESS OTHERWISE NOTED.

ALL MONUMENTS SHOWN AS "TO BE SET" WILL BE SET 90 DAYS AFTER THE ACCEPTANCE OF THE FINAL IMPROVEMENTS.

BASIS OF BEARINGS

THE BEARINGS SHOWN HEREON ARE BASED ON THE BEARING BETWEEN ORANGE COUNTY SURVEYOR'S HORIZONTAL CONTROL STATION "GPS NO. 1417" AND "GPS NO. 1448", BEING N. 10°48'13" E. PER RECORDS ON FILE IN THE OFFICE OF THE ORANGE COUNTY SURVEYOR.

DATUM STATEMENT

COORDINATES SHOWN HEREON ARE BASED IN THE CALIFORNIA COORDINATE SYSTEM (CCS83) ZONE VI, 1983 NAD (1991.35 EPOCH), O.C.S. GPS ADJUSTMENT. ALL DISTANCE SHOWN HEREON ARE GROUND, UNLESS OTHERWISE NOTED. TO OBTAIN GRID DISTANCE MULTIPLY THE GROUND DISTANCE BY 0.99993286.

AUTOMATIC FIRE SPRINKLER NOTE:

ALL STRUCTURES EXCEEDING FIRE DEPARTMENT ACCESS REQUIREMENTS SHALL BE PROTECTED BY AN AUTOMATIC FIRE SPRINKLER SYSTEM, IN A MANNER MEETING THE APPROVAL OF THE FIRE CHIEF.

SPECIAL FIRE PROTECTION NOTE:

PROPERTY IS TOTALLY EXCLUDED FROM A SPECIAL FIRE PROTECTION AREA.

HIGH FIRE HAZARD AREA NOTE:

THE LOTS SHOWN ON THIS MAP ARE IN A HIGH FIRE HAZARD AREA DUE TO WILD LAND EXPOSURE BASED ON STATE SRA MAPS.

NOTES:

LETTERED LOTS ARE NOT SEPARATE BUILDING SITES.

LOTS DESIGNATED AS OPEN SPACES ARE FOR LANDSCAPE PURPOSES AND WILL BE MAINTAINED BY THE HOMEOWNER'S ASSOCIATION.

THE PRIVATE STREETS CONSTRUCTED WITHIN THIS TRACT MAP SHALL BE OWNED, OPERATED AND MAINTAINED BY THE DEVELOPER, HIS SUCCESSORS OR ASSIGNS. THE COUNTY OF ORANGE SHALL HAVE NO RESPONSIBILITY THEREOF, UNLESS PURSUANT TO APPROPRIATE SECTIONS OF THE STREETS HAVE BEEN ACCEPTED INTO THE COUNTY ROAD SYSTEM BY APPROPRIATE RESOLUTION OF THE BOARD OF SUPERVISORS.

() INDICATES MEASURED AND RECORD PER TRACT MAP NO. 16155, MM 812/30-39

[] INDICATES MEASURED AND RECORD PER LOT LINE ADJUSTMENT NO. 2001-013 PER INSTRUMENT NO. 20010651105, O.R., SEPTEMBER 14, 2001.

GPS NO. 1448

FOUND 2 1/2" IRON PIPE W/2" OCS BRASS CAP STAMPED "GPS 1448 9-95" PER RECORDS FILE IN THE ORANGE COUNTY SURVEYORS OFFICE

N 2146790.819
E 6142602.585

GPS NO. 1417

FOUND 2 1/2" IRON PIPE W/2" OCS BRASS CAP STAMPED "GPS 1417 9-95" PER RECORDS ON FILE IN THE ORANGE COUNTY SURVEYORS OFFICE

N 2141450.558
E 6141583.535

SCALE: 1" = 80'

SHEET 3 OF 9 SHEETS

ALL OF TENTATIVE TRACT
 MAP NO. 16105
 TOTAL LOTS: 1-83 AND LOTS A-EE
 TOTAL ACREAGE: 9.016 AC.
 DATE OF SURVEY: APRIL, 2001



TRACT MAP NO. 16105

IN THE UNINCORPORATED TERRITORY OF THE COUNTY OF ORANGE,
 STATE OF CALIFORNIA

ADAMS - STREETER CIVIL ENGINEERING, INC. JAN A. ADAMS, R.C.E. 21687
 DATE OF SURVEY: APRIL, 2001

NOTES:

SEE SHEET 2 FOR EASEMENT NOTES, MONUMENT NOTES, BASIS OF BEARINGS AND
 DATUM STATEMENT, NOTES, LETTERED LOT INFORMATION, BOUNDARY AND GPS CONTROL
 AND SHEET INDEX.

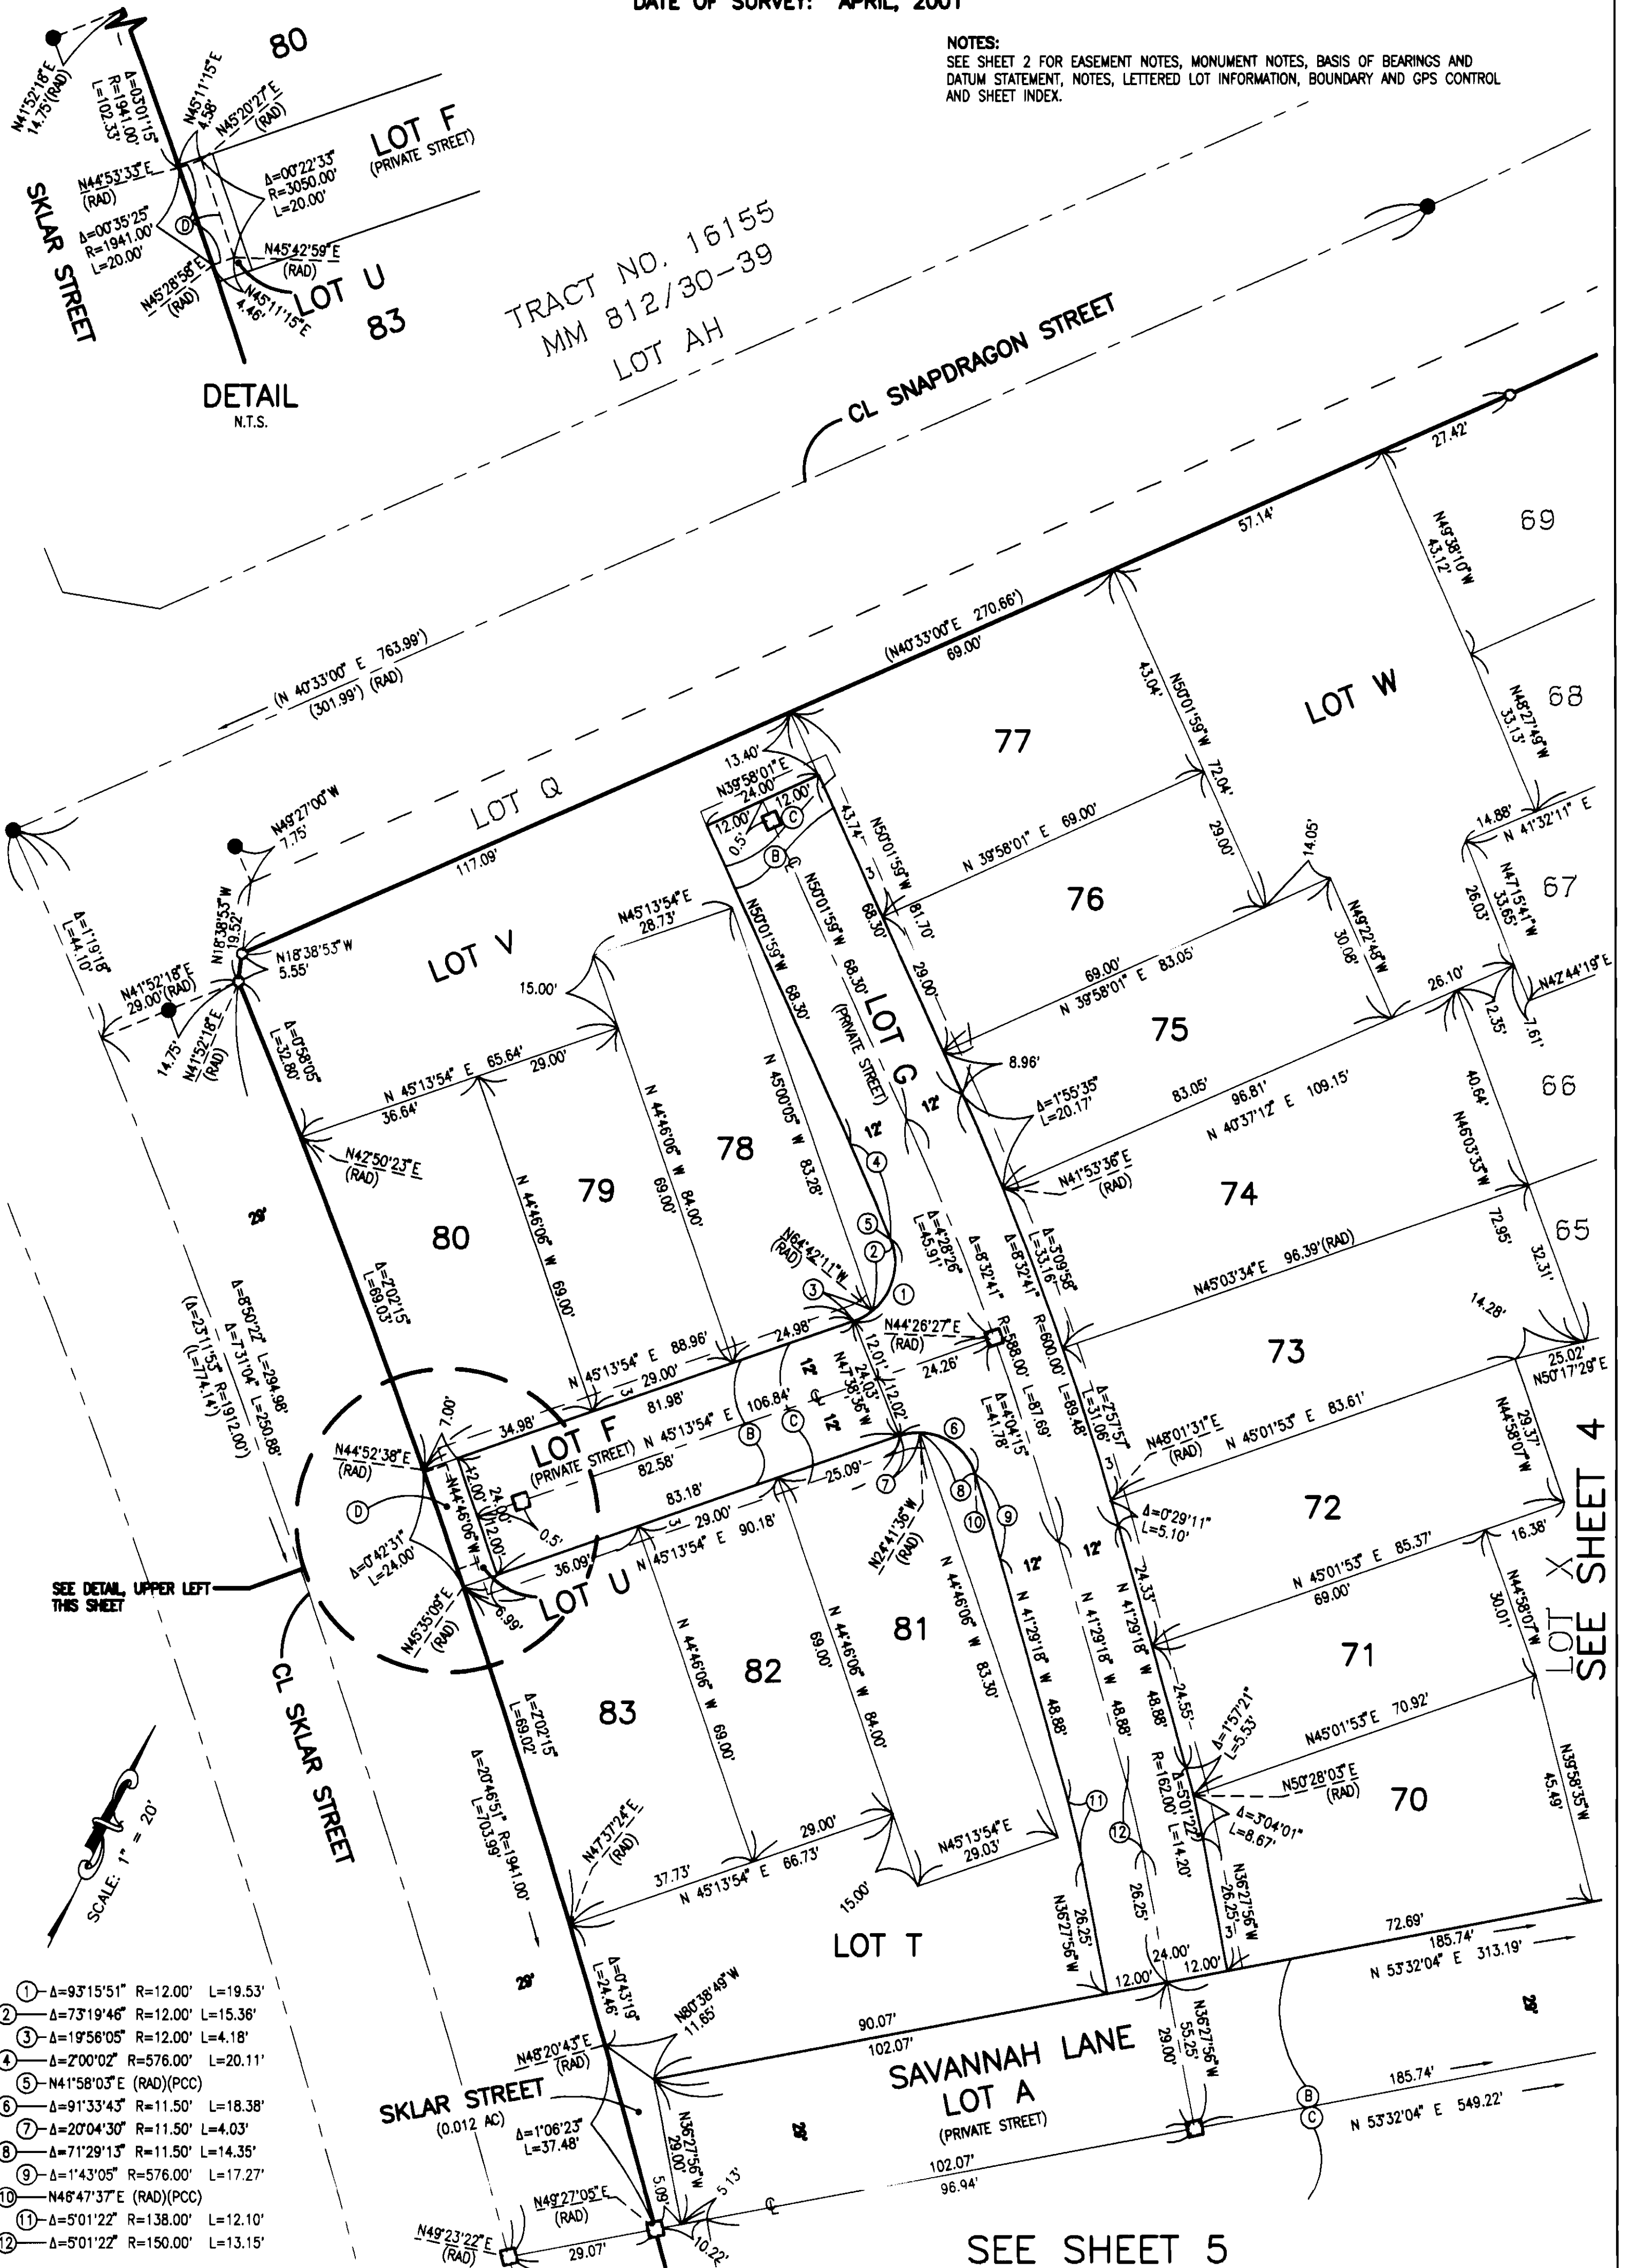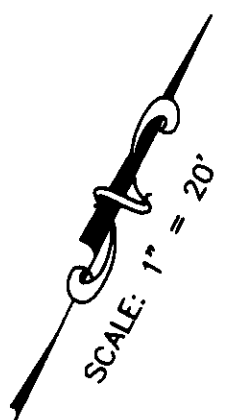SEE DETAIL, UPPER LEFT
THIS SHEET

- ① $\Delta=93^{\circ}15'51''$ $R=12.00'$ $L=19.53'$
- ② $\Delta=73^{\circ}19'46''$ $R=12.00'$ $L=15.36'$
- ③ $\Delta=19^{\circ}56'05''$ $R=12.00'$ $L=4.18'$
- ④ $\Delta=2^{\circ}00'02''$ $R=576.00'$ $L=20.11'$
- ⑤ $\Delta=1^{\circ}58'03''$ (RAD)(PCC)
- ⑥ $\Delta=91^{\circ}33'43''$ $R=11.50'$ $L=18.38'$
- ⑦ $\Delta=20^{\circ}04'30''$ $R=11.50'$ $L=4.03'$
- ⑧ $\Delta=71^{\circ}29'13''$ $R=11.50'$ $L=14.35'$
- ⑨ $\Delta=1^{\circ}43'05''$ $R=576.00'$ $L=17.27'$
- ⑩ $\Delta=48^{\circ}47'37''$ (RAD)(PCC)
- ⑪ $\Delta=5^{\circ}01'22''$ $R=138.00'$ $L=12.10'$
- ⑫ $\Delta=5^{\circ}01'22''$ $R=150.00'$ $L=13.15'$

SEE SHEET 5


SHEET 4 OF 9 SHEETS

ALL OF TENTATIVE TRACT
 MAP NO. 16105
 TOTAL LOTS: 1-83 AND LOTS A-E
 TOTAL ACREAGE: 9.016 AC.
 DATE OF SURVEY: APRIL, 2001

TRACT MAP NO. 16105


IN THE UNINCORPORATED TERRITORY OF THE COUNTY OF ORANGE,
 STATE OF CALIFORNIA

ADAMS - STREETER CIVIL ENGINEERING, INC. JAN A. ADAMS, R.C.E. 21687
 DATE OF SURVEY: APRIL, 2001

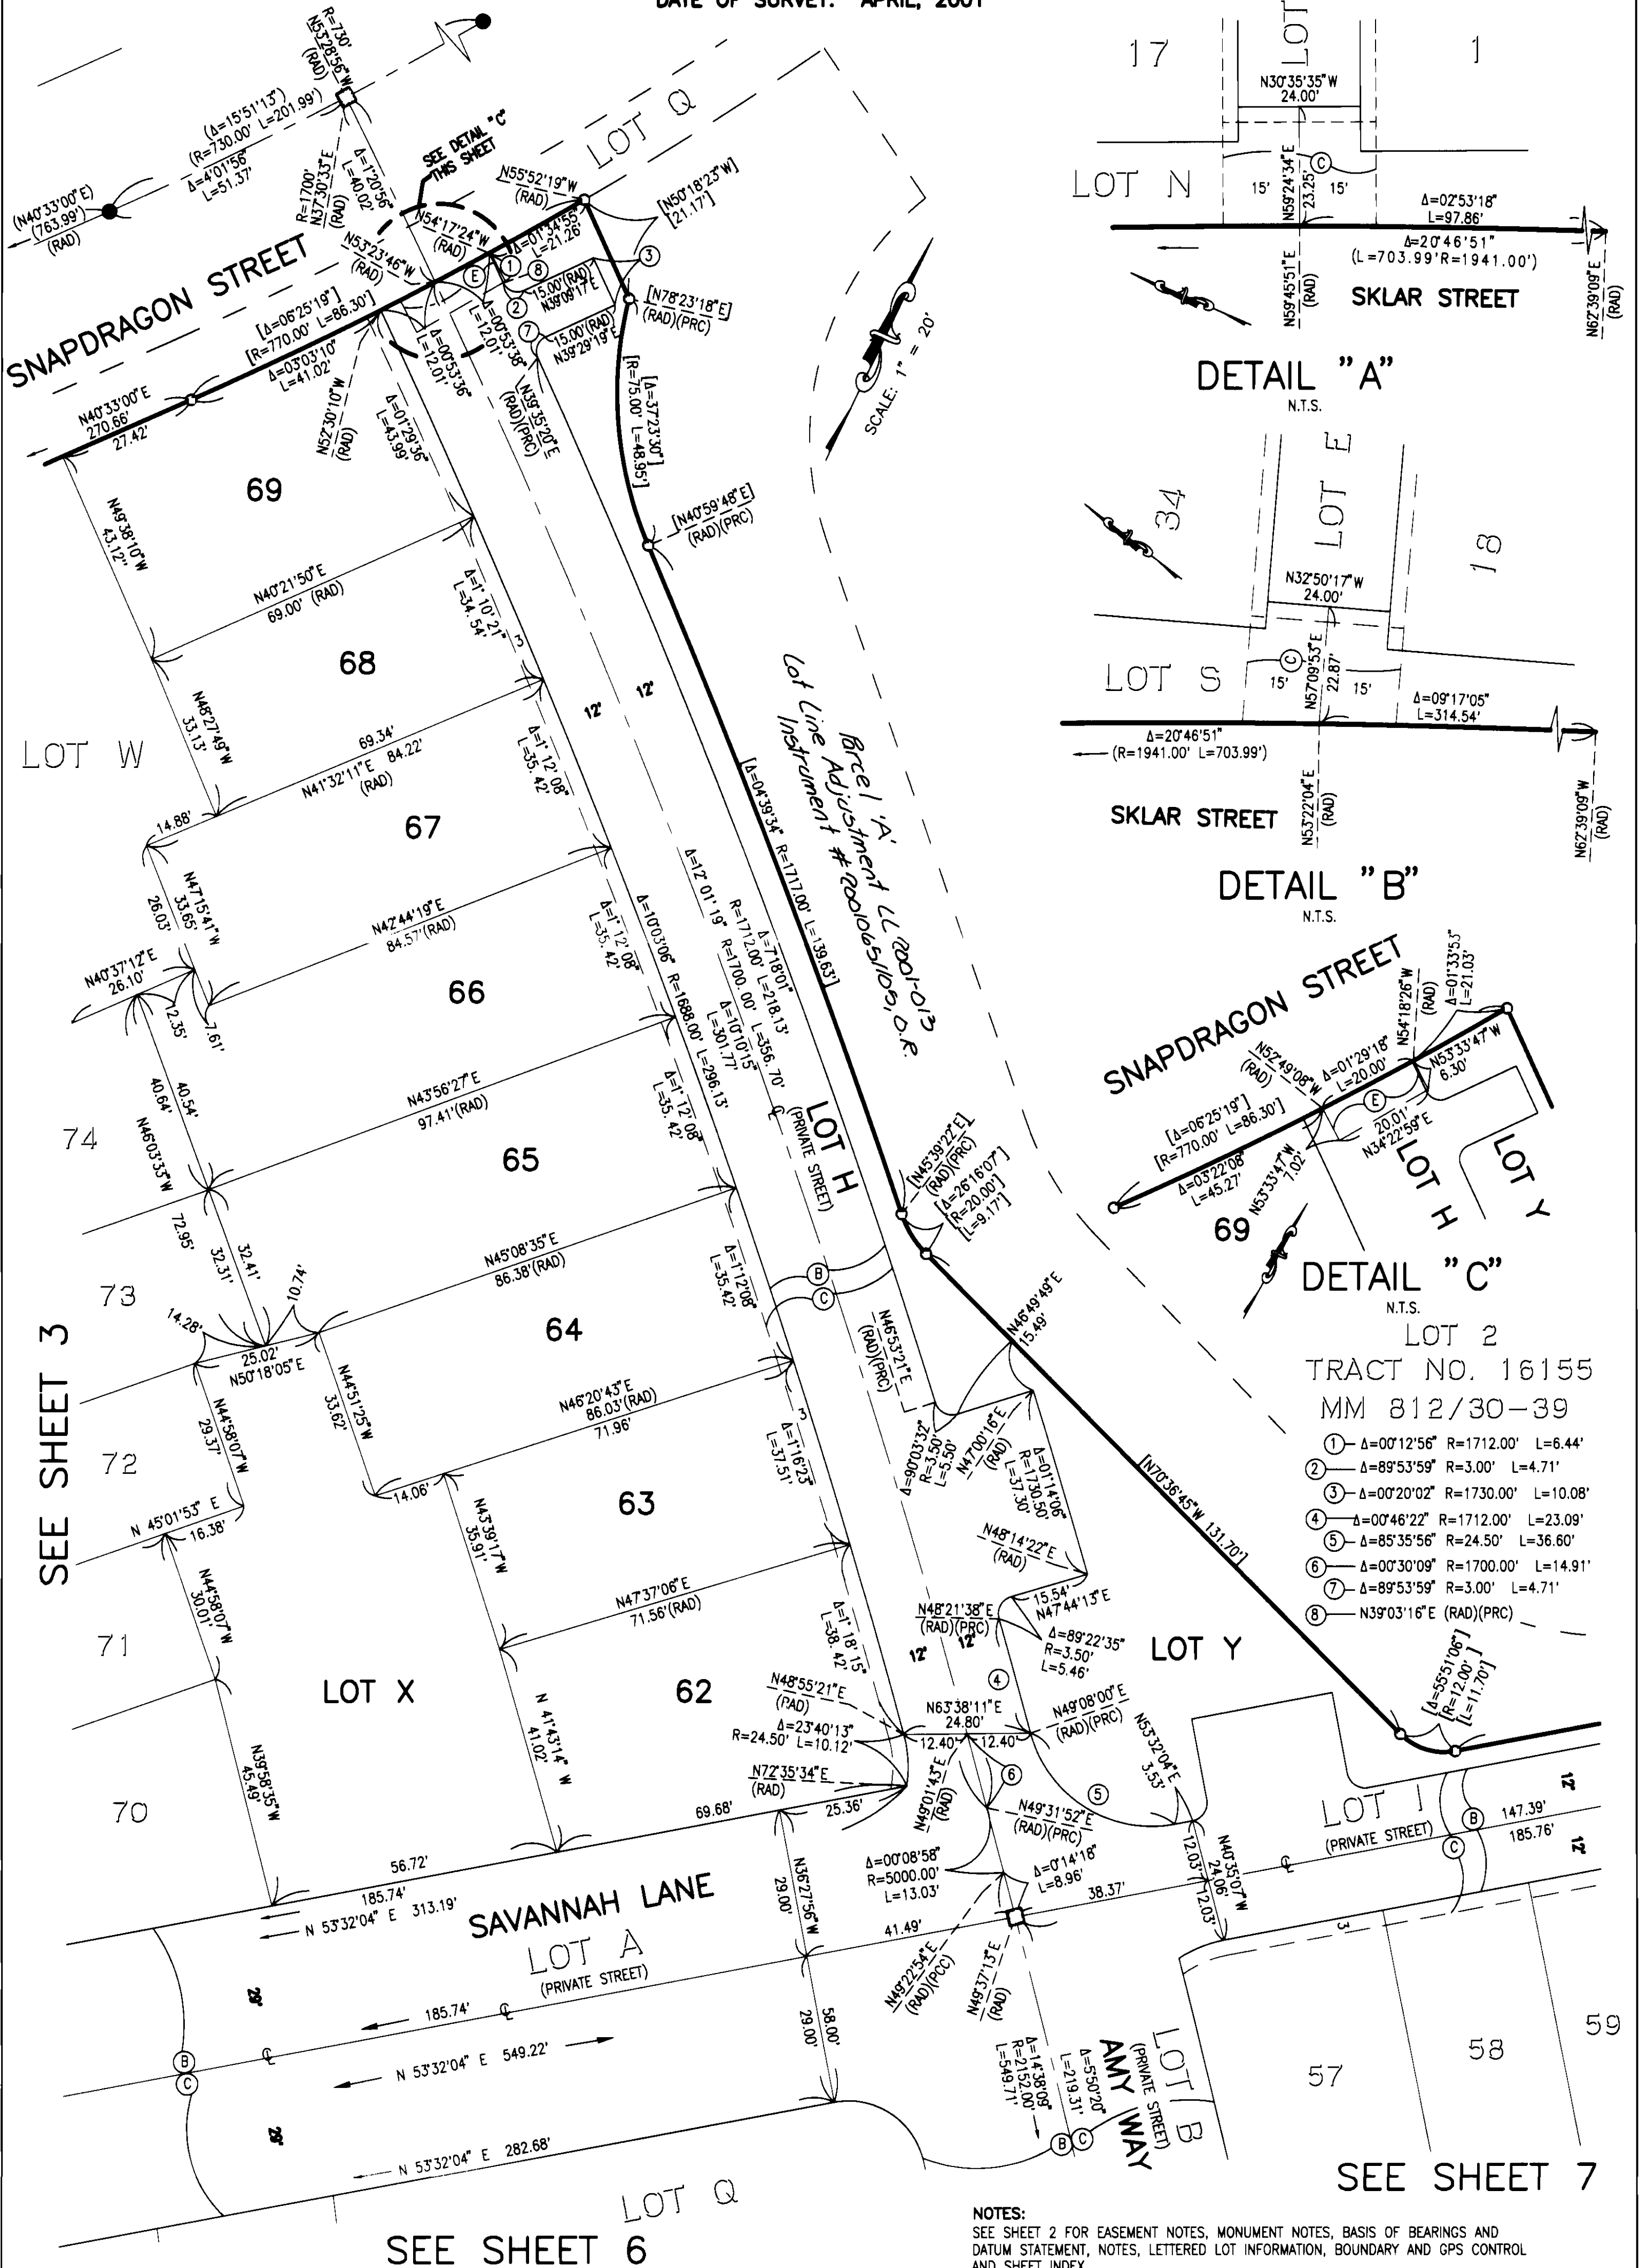

ADAMS - STREETER CIVIL ENGINEERING, INC. JAN A. ADAMS, R.C.E. 21687
DATE OF SURVEY: APRIL, 2001

SEE SHEET 3

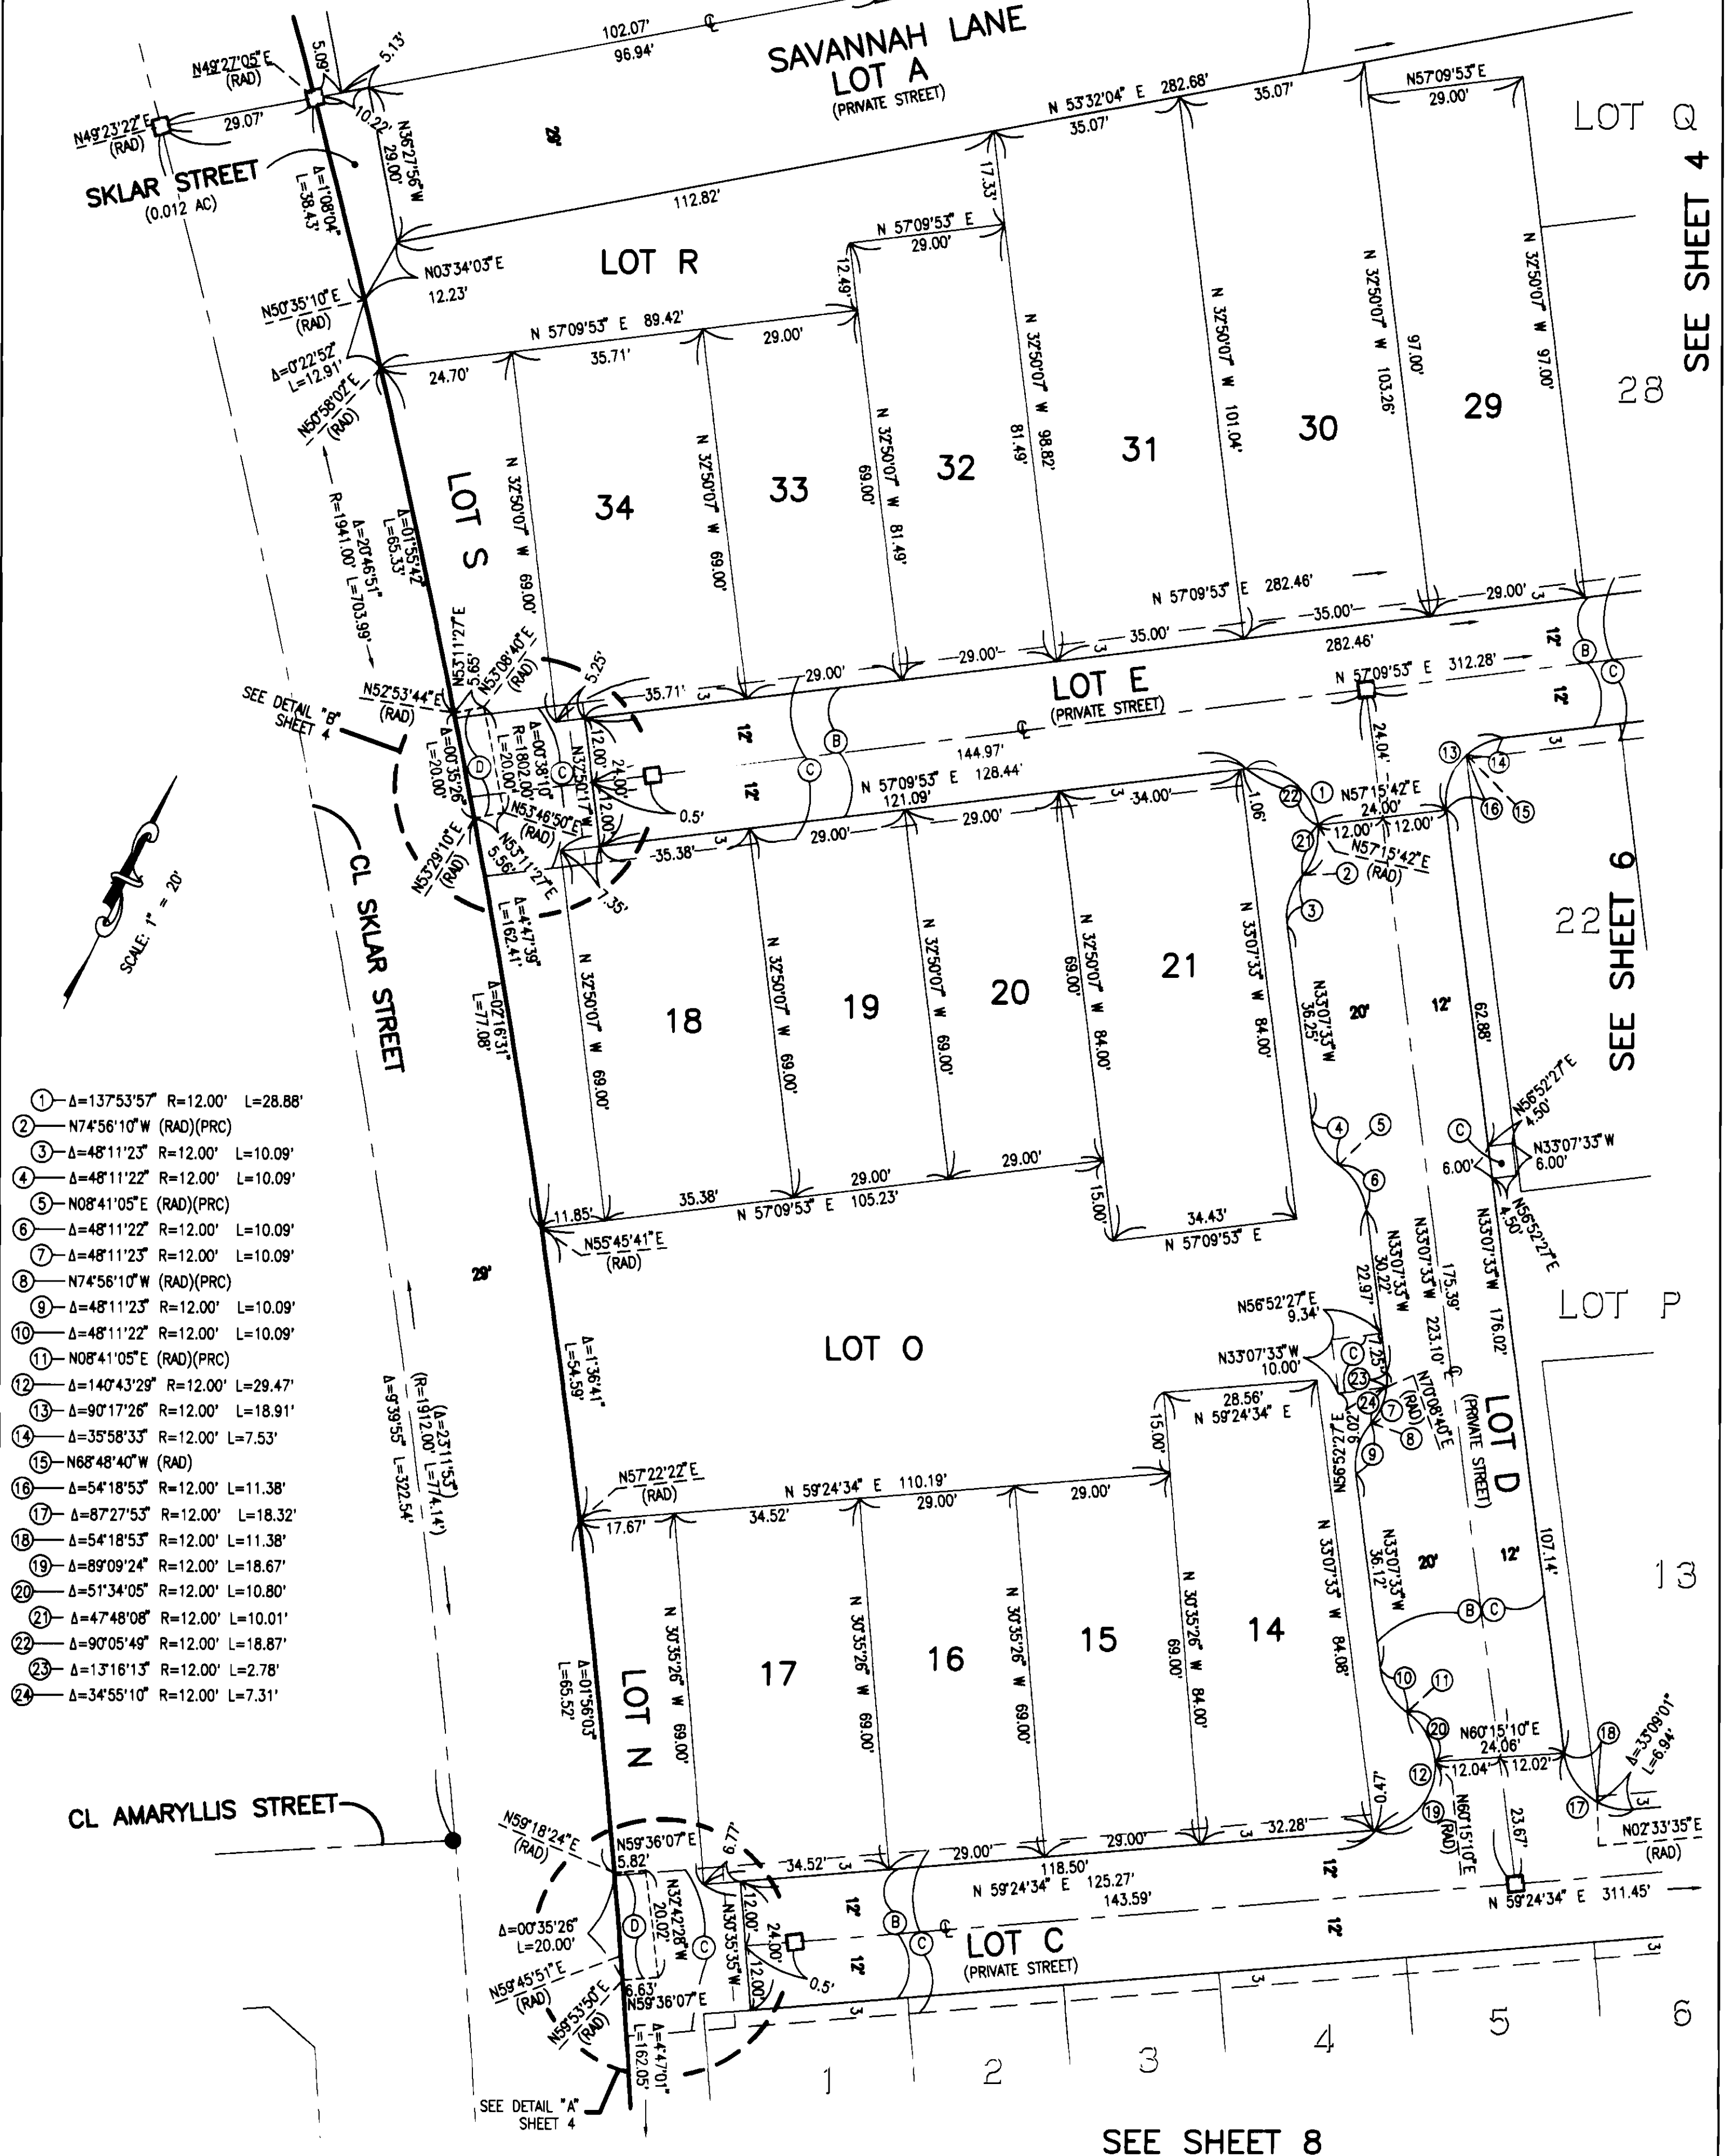

SHEET 6 OF 9 SHEETS

ALL OF TENTATIVE TRACT
MAP NO. 16105
TOTAL LOTS: 1-83 AND LOTS A-EE
TOTAL ACREAGE: 9.016 AC.
DATE OF SURVEY: APRIL, 2001

TRACT MAP NO. 16105

IN THE UNINCORPORATED TERRITORY OF THE COUNTY OF ORANGE,
STATE OF CALIFORNIA

ADAMS - STREETER CIVIL ENGINEERING, INC. JAN A. ADAMS, R.C.E. 21687
DATE OF SURVEY: APRIL, 2001

NOTES:

SEE SHEET 2 FOR EASEMENT NOTES, MONUMENT NOTES, BASIS OF BEARINGS AND
DATUM STATEMENT, NOTES, LETTERED LOT INFORMATION, BOUNDARY AND GPS CONTROL
AND SHEET INDEX.


SEE SHEET 5

SEE SHEET 5

SEE SHEET 7

SEE SHEET 9

SEE SHEET 8

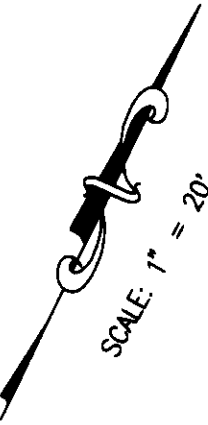

- ① $\Delta=90^{\circ}17'26''$ R=12.00' L=18.91'
- ② $\Delta=35^{\circ}58'33''$ R=12.00' L=7.53'
- ③ N68°48'40"W (RAD)
- ④ $\Delta=54^{\circ}18'53''$ R=12.00' L=11.38'
- ⑤ $\Delta=87^{\circ}27'53''$ R=12.00' L=18.32'
- ⑥ $\Delta=54^{\circ}18'52''$ R=12.00' L=11.38'




SHEET 7 OF 9 SHEETS

ALL OF TENTATIVE TRACT
MAP NO. 16105
TOTAL LOTS: 1-83 AND LOTS A-EE
TOTAL ACREAGE: 9.016 AC.
DATE OF SURVEY: APRIL, 2001

TRACT MAP NO. 16105

IN THE UNINCORPORATED TERRITORY OF THE COUNTY OF ORANGE,
STATE OF CALIFORNIA

ADAMS - STREETER CIVIL ENGINEERING, INC. JAN A. ADAMS, R.C.E. 21687
DATE OF SURVEY: APRIL, 2001

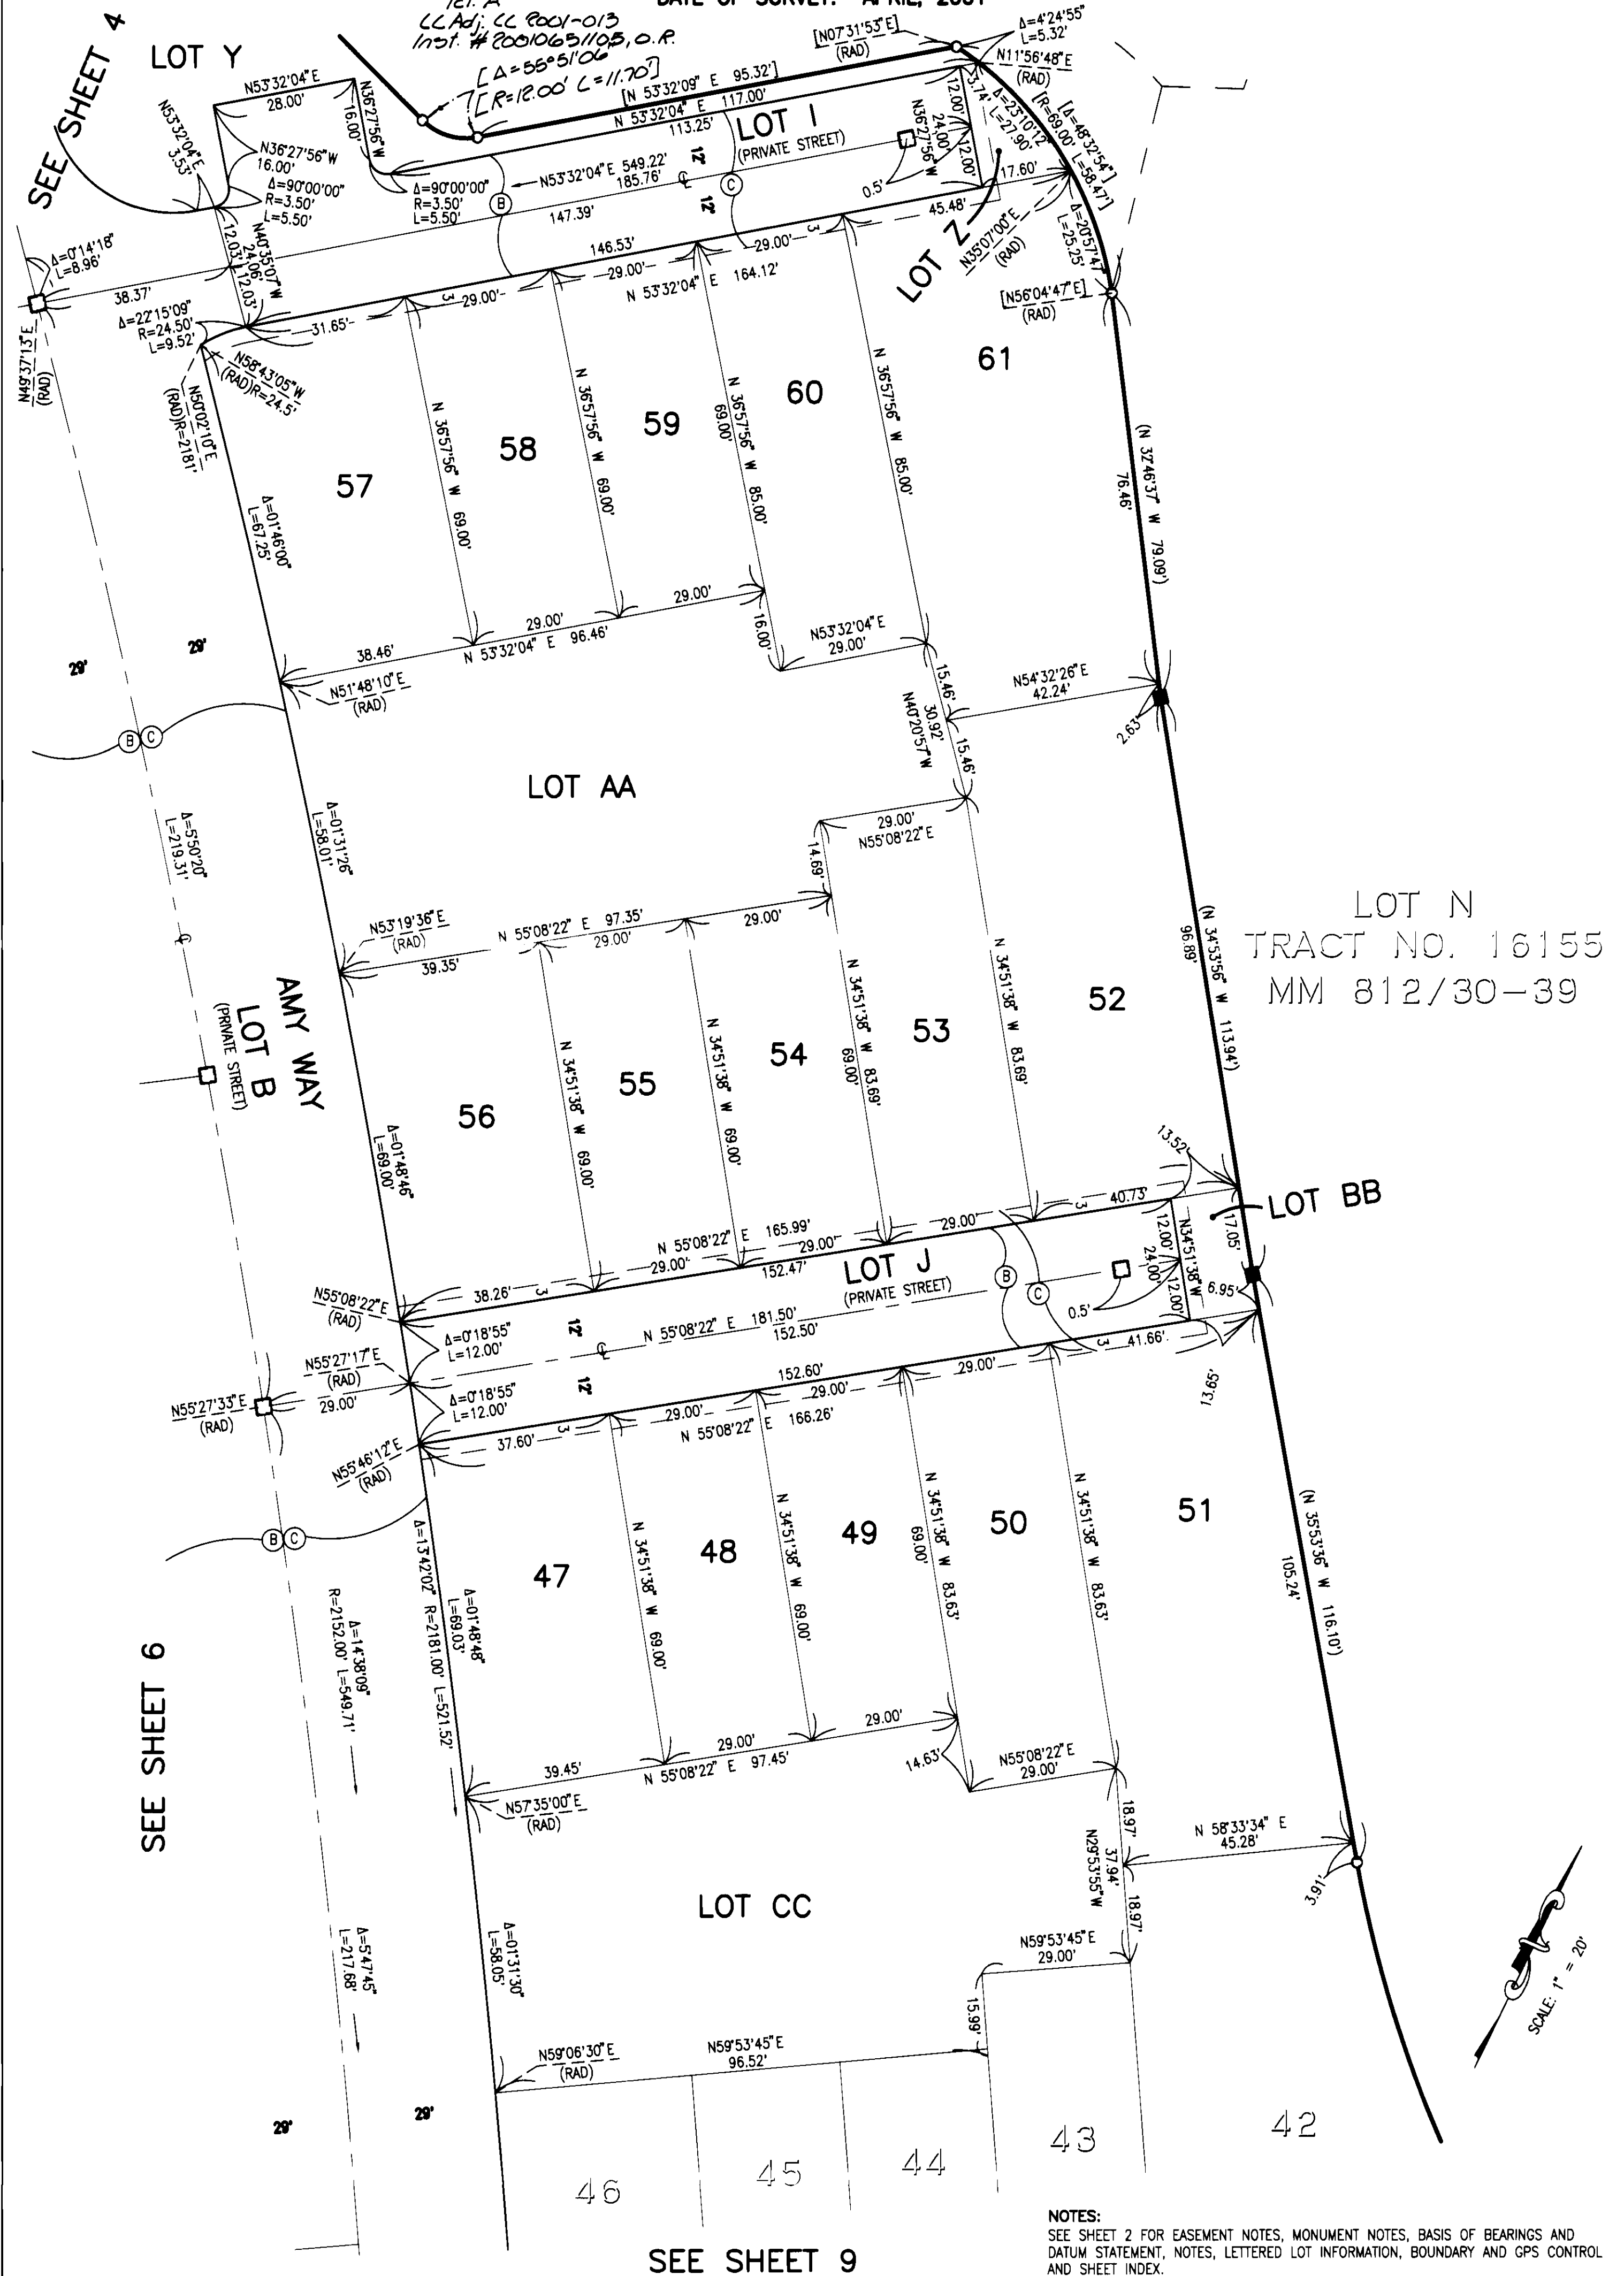

SEE SHEET 9

25

SHEET 9 OF 9 SHEETS

ALL OF TENTATIVE TRACT
MAP NO. 16105
TOTAL LOTS: 1-83 AND LOTS A-EE
TOTAL ACREAGE: 9.016 AC.
DATE OF SURVEY: APRIL, 2001

TRACT MAP NO. 16105

IN THE UNINCORPORATED TERRITORY OF THE COUNTY OF ORANGE,
STATE OF CALIFORNIA

ADAMS - STREETER CIVIL ENGINEERING, INC. JAN A. ADAMS, R.C.E. 21687
DATE OF SURVEY: APRIL, 2001

- ① $\Delta=00^{\circ}01'24''$ $R=2152.00'$ $L=0.87'$
② $N59^{\circ}53'45''E$ 8.80'
③ $N59^{\circ}53'45''E$ 8.30'

NOTES:

SEE SHEET 2 FOR EASEMENT NOTES, MONUMENT NOTES, BASIS OF BEARINGS AND
DATUM STATEMENT, NOTES, LETTERED LOT INFORMATION, BOUNDARY AND GPS CONTROL
AND SHEET INDEX.

