

SHEET 1 OF 4 SHEETS
34 NUMBERED LOTS AND LOTS
A THROUGH C, INCLUSIVE
ACREAGE: 5.901 ACRES
(ALL OF TENTATIVE
TRACT NO. 16114)

TRACT NO. 16114

IN UNINCORPORATED TERRITORY OF THE COUNTY OF ORANGE,
STATE OF CALIFORNIA

BEING A SUBDIVISION OF LOT 3 OF TRACT NO. 16025, AS SHOWN ON A MAP
FILED IN BOOK 812, PAGES 22 THROUGH 29, INCLUSIVE, OF MISCELLANEOUS
MAPS, IN THE OFFICE OF THE COUNTY RECORDER OF SAID COUNTY.

BLOCK: 5057
MODULES: 47 AND 48

HUNSAKER AND ASSOCIATES IRVINE, INC.
RORY S. WILLIAMS, L.S. 6654 DATE OF SURVEY: DECEMBER, 2000

ACCEPTED AND FILED AT THE
REQUEST OF
BENEFIT LAND TITLE INSURANCE COMPANY

DATE: JULY 31, 2001
TIME: 1:48 P.M. FEE: \$13.00
INSTRUMENT NO. 20010520750
BOOK 821 PAGE 41-44 M/M

GARY L. GRANVILLE
COUNTY CLERK - RECORDER
BY [Signature] DEPUTY

OWNERSHIP CERTIFICATE:

WE, THE UNDERSIGNED, BEING ALL PARTIES HAVING ANY RECORD TITLE INTEREST IN THE LAND COVERED BY THIS MAP, DO HEREBY CONSENT TO THE PREPARATION AND RECORDATION OF SAID MAP, AS SHOWN WITHIN THE DISTINCTIVE BORDER LINE.

WE HEREBY DEDICATE TO THE PUBLIC FOR STREET PURPOSES:

CANDLEWIND COURT, CELESTINE CIRCLE, LUNA COURT AND MERRIWEATHER PLACE.

WE ALSO HEREBY DEDICATE TO THE COUNTY OF ORANGE:

THE EASEMENT FOR STORM DRAIN PURPOSES AS SHOWN ON THIS MAP.

WE ALSO DO HEREBY DECLARE THAT THE LAND COVERED BY THIS MAP IS LOCATED IN A VERY HIGH FIRE HAZARD AREA DUE TO WILDLAND EXPOSURE BASED ON STATE SRA MAPS.

WE ALSO HEREBY DEDICATE TO THE SANTA MARGARITA WATER DISTRICT THE PIPELINE EASEMENT FOR WATER AND SEWER PURPOSES, AS SHOWN ON THIS TRACT MAP, WHICH EASEMENT SHALL BE SUBJECT TO THE SAME TERMS AND CONDITIONS AS SHOWN IN THAT CERTAIN EASEMENT RECORDED OCTOBER 6, 1980, IN BOOK 13776, PAGE 341 OF OFFICIAL RECORDS OF ORANGE COUNTY, CALIFORNIA.

THE SANTA MARGARITA WATER DISTRICT SHALL RESTORE OTHER IMPROVEMENTS OR FACILITIES LOCATED WITHIN THE EASEMENT, IF IT HAS CONSENTED TO THE LOCATION OF SUCH IMPROVEMENTS OR FACILITIES TO THE EXTENT THAT THE EXERCISE OF ITS RIGHTS IN CONNECTION WITH THE EASEMENT IMPACTS OTHER IMPROVEMENTS OR FACILITIES LOCATED WITHIN THE EASEMENT. HOWEVER, IN NO EVENT SHALL SANTA MARGARITA WATER DISTRICT BE RESPONSIBLE FOR THE COST OF RELOCATING ITS FACILITIES IN THE EVENT OF CONFLICTS WITH SUCH OTHER IMPROVEMENTS OR FACILITIES.

CENTEX HOMES, A NEVADA GENERAL PARTNERSHIP, OWNER.

BY: CENTEX REAL ESTATE CORPORATION, A NEVADA CORPORATION,
ITS MANAGING GENERAL PARTNER.

BY: [Signature] NAME: ROLAND OSGOOD TITLE: DIVISION PRESIDENT
BY: [Signature] NAME: Martin Juliusen TITLE: Controller/Assistant Secretary

DMB LADERA, LLC, A DELAWARE LIMITED LIABILITY COMPANY, BENEFICIARY UNDER DEED OF TRUST RECORDED APRIL 3, 2001, AS INSTRUMENT NO. 2001-095570 OF OFFICIAL RECORDS.

BY: RANCHO MISSION VIEJO, L.L.C., A DELAWARE LIMITED LIABILITY COMPANY, ITS AUTHORIZED AGENT AND MANAGER.

BY: [Signature] NAME: Stephen C. Schrant TITLE: Executive VP of Development
BY: [Signature] NAME: Paul Johnson TITLE: VP of Community Development

NOTARY ACKNOWLEDGMENTS:

STATE OF CALIFORNIA }
COUNTY OF ORANGE } SS

ON April 2, 2001 BEFORE ME, Rhonda Keiger Painter PERSONALLY
APPEARED Roland F. Osgood AND Martin Juliusen PERSONALLY
KNOWN TO ME (OR PROVED TO ME ON THE BASIS OF SATISFACTORY EVIDENCE) TO BE THE PERSON(S)
WHOSE NAME(S) IS/ARE SUBSCRIBED TO THE WITHIN INSTRUMENT AND ACKNOWLEDGED TO ME THAT
HE/SHE/THEY EXECUTED THE SAME IN HIS/HER/their AUTHORIZED CAPACITY(IES), AND THAT BY
HIS/HER/their SIGNATURE(S) ON THE INSTRUMENT THE PERSON(S), OR ENTITY UPON BEHALF OF
WHICH THE PERSON(S) ACTED, EXECUTED THE INSTRUMENT.

WITNESS MY HAND:

SIGNATURE [Signature] MY PRINCIPAL PLACE OF BUSINESS IS
NOTARY PUBLIC IN AND FOR SAID STATE IN Orange COUNTY.
Rhonda Keiger Painter MY COMMISSION EXPIRES: 12/9/03
(NAME PRINTED)

STATE OF CALIFORNIA }
COUNTY OF ORANGE } SS

ON April 9, 2001 BEFORE ME, Holly Broman PERSONALLY
APPEARED Stephen C. Schrant AND Paul Johnson PERSONALLY
KNOWN TO ME (OR PROVED TO ME ON THE BASIS OF SATISFACTORY EVIDENCE) TO BE THE PERSON(S)
WHOSE NAME(S) IS/ARE SUBSCRIBED TO THE WITHIN INSTRUMENT AND ACKNOWLEDGED TO ME THAT
HE/SHE/THEY EXECUTED THE SAME IN HIS/HER/their AUTHORIZED CAPACITY(IES), AND THAT BY
HIS/HER/their SIGNATURE(S) ON THE INSTRUMENT THE PERSON(S), OR ENTITY UPON BEHALF OF
WHICH THE PERSON(S) ACTED, EXECUTED THE INSTRUMENT.

WITNESS MY HAND:

SIGNATURE [Signature] MY PRINCIPAL PLACE OF BUSINESS IS
NOTARY PUBLIC IN AND FOR SAID STATE IN Orange COUNTY.
Holly Broman MY COMMISSION EXPIRES: 3/3/04
(NAME PRINTED)

SURVEYOR'S STATEMENT:

I HEREBY STATE THAT THIS MAP, CONSISTING OF 4 SHEETS, CORRECTLY REPRESENTS A TRUE AND COMPLETE SURVEY AS SHOWN MADE IN DECEMBER, 2000; WAS MADE BY ME OR UNDER MY DIRECTION; THAT THE MONUMENTS ARE OF THE CHARACTER AND OCCUPY (OR WILL OCCUPY) THE POSITIONS INDICATED BY SAID MAP; AND THAT SAID MONUMENTS ARE (OR WILL BE) SUFFICIENT TO ENABLE THE SURVEY TO BE RETRACED.

Rory S. Williams 3/29/01
RORY S. WILLIAMS, L.S. 6654 DATE
EXPIRATION DATE: 12/31/03



COUNTY SURVEYOR'S STATEMENT

I HEREBY STATE THAT I HAVE EXAMINED THIS MAP AND HAVE FOUND IT TO BE SUBSTANTIALLY IN CONFORMANCE WITH THE TENTATIVE MAP AS FILED WITH, AMENDED AND APPROVED BY THE ORANGE COUNTY SUBDIVISION COMMITTEE; THAT ALL PROVISIONS OF THE SUBDIVISION MAP ACT AND COUNTY SUBDIVISION REGULATIONS HAVE BEEN COMPLIED WITH AND I AM SATISFIED SAID MAP IS TECHNICALLY CORRECT.

DATED THIS 13TH DAY OF JULY, 2001.

Michael K. Sullivan
JOHN CANAS, COUNTY SURVEYOR
LS 4408, EXPIRATION DATE: 9-30-01 BY: MICHAEL K. SULLIVAN, DEPUTY
LS 6254 EXPIRES 6-30-02



COUNTY TREASURER-TAX COLLECTOR'S CERTIFICATE:

STATE OF CALIFORNIA }
COUNTY OF ORANGE } SS

I HEREBY CERTIFY THAT ACCORDING TO THE RECORDS OF MY OFFICE THERE ARE NO LIENS AGAINST THE LAND COVERED BY THIS MAP OR ANY PART THEREOF FOR UNPAID STATE, COUNTY, MUNICIPAL OR LOCAL TAXES OR SPECIAL ASSESSMENTS COLLECTED AS TAXES, EXCEPT TAXES OR SPECIAL ASSESSMENTS COLLECTED AS TAXES NOT YET PAYABLE.

AND DO ALSO CERTIFY TO THE RECORDER OF ORANGE COUNTY THAT THE PROVISIONS OF THE SUBDIVISION MAP ACT HAVE BEEN COMPLIED WITH REGARDING DEPOSITS TO SECURE PAYMENT OF TAXES OR SPECIAL ASSESSMENTS COLLECTED AS TAXES ON THE LAND COVERED BY THIS MAP.

DATED THIS 27th DAY OF June, 2001.

JOHN M.W. MOORLACH BY: Dixie Feronis
COUNTY TREASURER-TAX COLLECTOR DEPUTY TREASURER-TAX COLLECTOR

CLERK OF THE BOARD OF SUPERVISORS' CERTIFICATE:

STATE OF CALIFORNIA }
COUNTY OF ORANGE } SS

I HEREBY CERTIFY THAT THIS MAP WAS PRESENTED FOR APPROVAL TO THE BOARD OF SUPERVISORS OF THE COUNTY OF ORANGE AT REGULAR MEETING THEREOF HELD ON THE 24th DAY OF July, 2001, AND THAT THEREUPON SAID BOARD DID, BY AN ORDER DULY PASSED AND ENTERED, APPROVE SAID MAP AND DID ACCEPT ON BEHALF OF THE PUBLIC, SUBJECT TO IMPROVEMENTS, THE DEDICATION FOR STREET PURPOSES OF CANDLEWIND COURT, CELESTINE CIRCLE, LUNA COURT AND MERRIWEATHER PLACE.

AND DID ALSO ACCEPT ON BEHALF OF THE COUNTY OF ORANGE:
THE EASEMENT FOR STORM DRAIN PURPOSES, AS DEDICATED.

DATED THIS 24th DAY OF July, 2001.

[Signature]
CLERK OF THE BOARD OF SUPERVISORS
DARLENE J. BLOOM



CERTIFICATE OF ACCEPTANCE - SANTA MARGARITA WATER DISTRICT

THE UNDERSIGNED, BEING THE DULY APPOINTED AGENT OF THE SANTA MARGARITA WATER DISTRICT, A PUBLIC CORPORATION IN ORANGE COUNTY, CALIFORNIA, PURSUANT TO ITS RESOLUTION NO. 88-10-2, DOES HEREBY ACCEPT ON BEHALF OF SAID DISTRICT, THE PIPELINE EASEMENT FOR WATER AND SEWER PURPOSES AS DEDICATED AND SHOWN ON THIS TRACT MAP, BY AND BETWEEN THE SANTA MARGARITA WATER DISTRICT AND CENTEX HOMES, A NEVADA GENERAL PARTNERSHIP, AND DOES HEREBY CERTIFY THAT THE GRANTEE CONSENTS TO THE RECORDATION OF SAID TRACT MAP.

[Signature]
DANIEL R. FERONS, CHIEF ENGINEER
SANTA MARGARITA WATER DISTRICT

NOTARY ACKNOWLEDGMENT - SANTA MARGARITA WATER DISTRICT

STATE OF CALIFORNIA }
COUNTY OF ORANGE } SS

ON May 18, 2001 BEFORE ME, ANDREA M. EVANS PERSONALLY
APPEARED DANIEL R. FERONS, PERSONALLY
KNOWN TO ME (OR PROVED TO ME ON THE BASIS OF SATISFACTORY EVIDENCE) TO BE THE PERSON
WHOSE NAME IS SUBSCRIBED TO THE WITHIN INSTRUMENT AND ACKNOWLEDGED TO ME THAT
HE EXECUTED THE SAME IN HIS AUTHORIZED CAPACITY, AND THAT BY
HIS SIGNATURE ON THE INSTRUMENT THE PERSON, OR ENTITY UPON BEHALF OF
WHICH THE PERSON ACTED, EXECUTED THE INSTRUMENT.

WITNESS MY HAND:

SIGNATURE [Signature] MY PRINCIPAL PLACE OF BUSINESS IS
NOTARY PUBLIC IN AND FOR SAID STATE IN ORANGE COUNTY.
ANDREA M. EVANS MY COMMISSION EXPIRES: 4/08/02
(NAME PRINTED)

SIGNATURE OMISSIONS:

PURSUANT TO THE PROVISIONS OF SECTION 66436 (a)(3)(C) OF THE SUBDIVISION MAP ACT, THE FOLLOWING SIGNATURES HAVE BEEN OMITTED:

LADERA DEVELOPMENT COMPANY, L.L.C., HOLDER OF OIL, GAS AND MINERAL RIGHTS RECORDED AS INSTRUMENT NO. 19960624029 OF OFFICIAL RECORDS.

SHEET 2 OF 4 SHEETS
SCALE 1" = 80'
34 NUMBERED LOTS AND LOTS
A THROUGH C, INCLUSIVE
ACREAGE: 5.901 ACRES
(ALL OF TENTATIVE
TRACT NO. 16114)

TRACT NO. 16114

IN UNINCORPORATED TERRITORY OF THE COUNTY OF ORANGE,
STATE OF CALIFORNIA

HUNSAKER AND ASSOCIATES IRVINE, INC.
RORY S. WILLIAMS, L.S. 6654
DATE OF SURVEY: DECEMBER, 2000

3 INDICATES SHEET NUMBER

SHEET INDEX AND GPS CONTROL MAP

BASIS OF BEARINGS:

THE BEARINGS SHOWN HEREON ARE BASED ON THE BEARING BETWEEN
O.C.S. HORIZONTAL CONTROL STATION GPS NO. 1417 AND STATION
GPS NO. 1448 BEING N10°48'13"E PER RECORDS ON FILE IN THE
OFFICE OF THE ORANGE COUNTY SURVEYOR.

DATUM STATEMENT:

COORDINATES SHOWN ARE BASED ON THE CALIFORNIA COORDINATE
SYSTEM (CCS83), ZONE VI, 1983 NAD, (1991.35 EPOCH OCS GPS
ADJUSTMENT).

ALL DISTANCES SHOWN ARE GROUND, UNLESS OTHERWISE NOTED. TO
OBTAIN GRID DISTANCE MULTIPLY GROUND DISTANCE BY 0.99994850.

NOTES:

LOT A IS FOR OPEN SPACE PURPOSES.

LOTS B & C ARE FOR POCKET PARK PURPOSES.

THE PROPERTY IS IN A SPECIAL FIRE PROTECTION AREA. TOTAL EXCLUSION
GRANTED FOR THIS TRACT.

ALL R-3 STRUCTURES GREATER THAN 5,500 SQUARE FEET, OTHER
STRUCTURES GREATER THAN 6,000 SQUARE FEET OR IDENTIFIED BY THE FIRE
CHIEF, AND STRUCTURES OUT OF FIRE DEPARTMENT ACCESS OF 150 FEET
SHALL BE PROTECTED BY AN AUTOMATIC FIRE SPRINKLER SYSTEM, IN A
MANNER MEETING THE APPROVAL OF THE FIRE CHIEF.

EASEMENT NOTES:

(A) INDICATES A 32' WIDE EASEMENT FOR WATER LINE, SANITARY SEWER
AND ACCESS PURPOSES DEDICATED HEREON TO THE SANTA MARGARITA
WATER DISTRICT.

(B) INDICATES A 20' WIDE EASEMENT FOR STORM DRAIN PURPOSES
DEDICATED HEREON TO THE COUNTY OF ORANGE.

MONUMENT NOTES:

2" I.P. TAGGED L.S. 6654 OR LEAD, TACK & TAG L.S. 6654 OR NAIL & TAG L.S.
6654 OR 8" SAW STAMPED L.S. 6654 TO BE SET AT ALL TRACT BOUNDARY CORNERS
WITHIN 90 DAYS AFTER ACCEPTANCE OF IMPROVEMENTS, UNLESS OTHERWISE NOTED.

1" I.P. TAGGED L.S. 6654 OR LEAD, TACK & TAG L.S. 6654 OR NAIL & TAG L.S.
6654 OR 8" SAW STAMPED L.S. 6654 TO BE SET AT ALL LOT CORNERS, EXCEPT LOT
CORNERS THAT ARE THE INTERSECTION OF SIDE LOT LINES WITH STREET RIGHT OF
WAY, WITHIN 90 DAYS AFTER ACCEPTANCE OF IMPROVEMENTS, UNLESS OTHERWISE
NOTED.

LEAD, TACK & TAG L.S. 6654 TO BE SET IN TOP OF CURB ON ALL SIDE LOT LINES
PRODUCED OR CONTINUED, 8.75' FROM INTERSECTION WITH STREET RIGHT OF WAY
FOR ALL SIDE LOT LINES RADIAL OR PERPENDICULAR TO STREET RIGHT OF WAY.
WITHIN 90 DAYS AFTER ACCEPTANCE OF IMPROVEMENTS, UNLESS OTHERWISE NOTED.
FOR ALL SIDE LOT LINES NON-RADIAL OR NON-PERPENDICULAR TO STREET RIGHT OF
WAY, OR NOT AT AN 8.75' OFFSET, BEARING AND DISTANCE OF PRODUCTION IS AS
NOTED HEREON.

8" SAW STAMPED L.S. 6654 OR LEAD, TACK & TAG L.S. 6654 OR 1" I.P. TAGGED L.S.
6654 TO BE SET AT ALL STREET CENTERLINE POINTS OF CONTROL, WITHIN 90 DAYS
AFTER ACCEPTANCE OF IMPROVEMENTS, UNLESS OTHERWISE NOTED.

● INDICATES FOUND MONUMENT OR LOCATION OF MONUMENT SET OR TO BE SET,
AS NOTED.

■ INDICATES NOTHING TO BE SET.


P# INDICATES BEARING AND DISTANCE OF LOT LINE PRODUCTION FROM LOT CORNER
TO MONUMENT.

1 INDICATES LOCATION OF 1" I.P. TAGGED "P.L.S. 5557" OR SPIKE & WASHER STAMPED
"P.L.S. 5557" OR LEAD, TACK & TAG "P.L.S. 5557" TO BE SET PER TRACT NO.
16025, M.M. 812/22-29.

2 INDICATES LOCATION OF 1" I.P. TAGGED "P.L.S. 5557" OR SPIKE & WASHER STAMPED
"P.L.S. 5557" OR LEAD, TACK & TAG "P.L.S. 5557" TO BE SET PER TRACT NO.
16157, M.M. 813/1-9.

3 INDICATES LOCATION OF 2" I.P. TAGGED "P.L.S. 5557" OR SPIKE & WASHER STAMPED
"P.L.S. 5557" OR LEAD, TACK & TAG "P.L.S. 5557" TO BE SET PER TRACT NO.
16025, M.M. 812/22-29.

4 INDICATES SET 2" I.P. TAGGED L.S. 6654 PRIOR TO MAP RECORDATION.

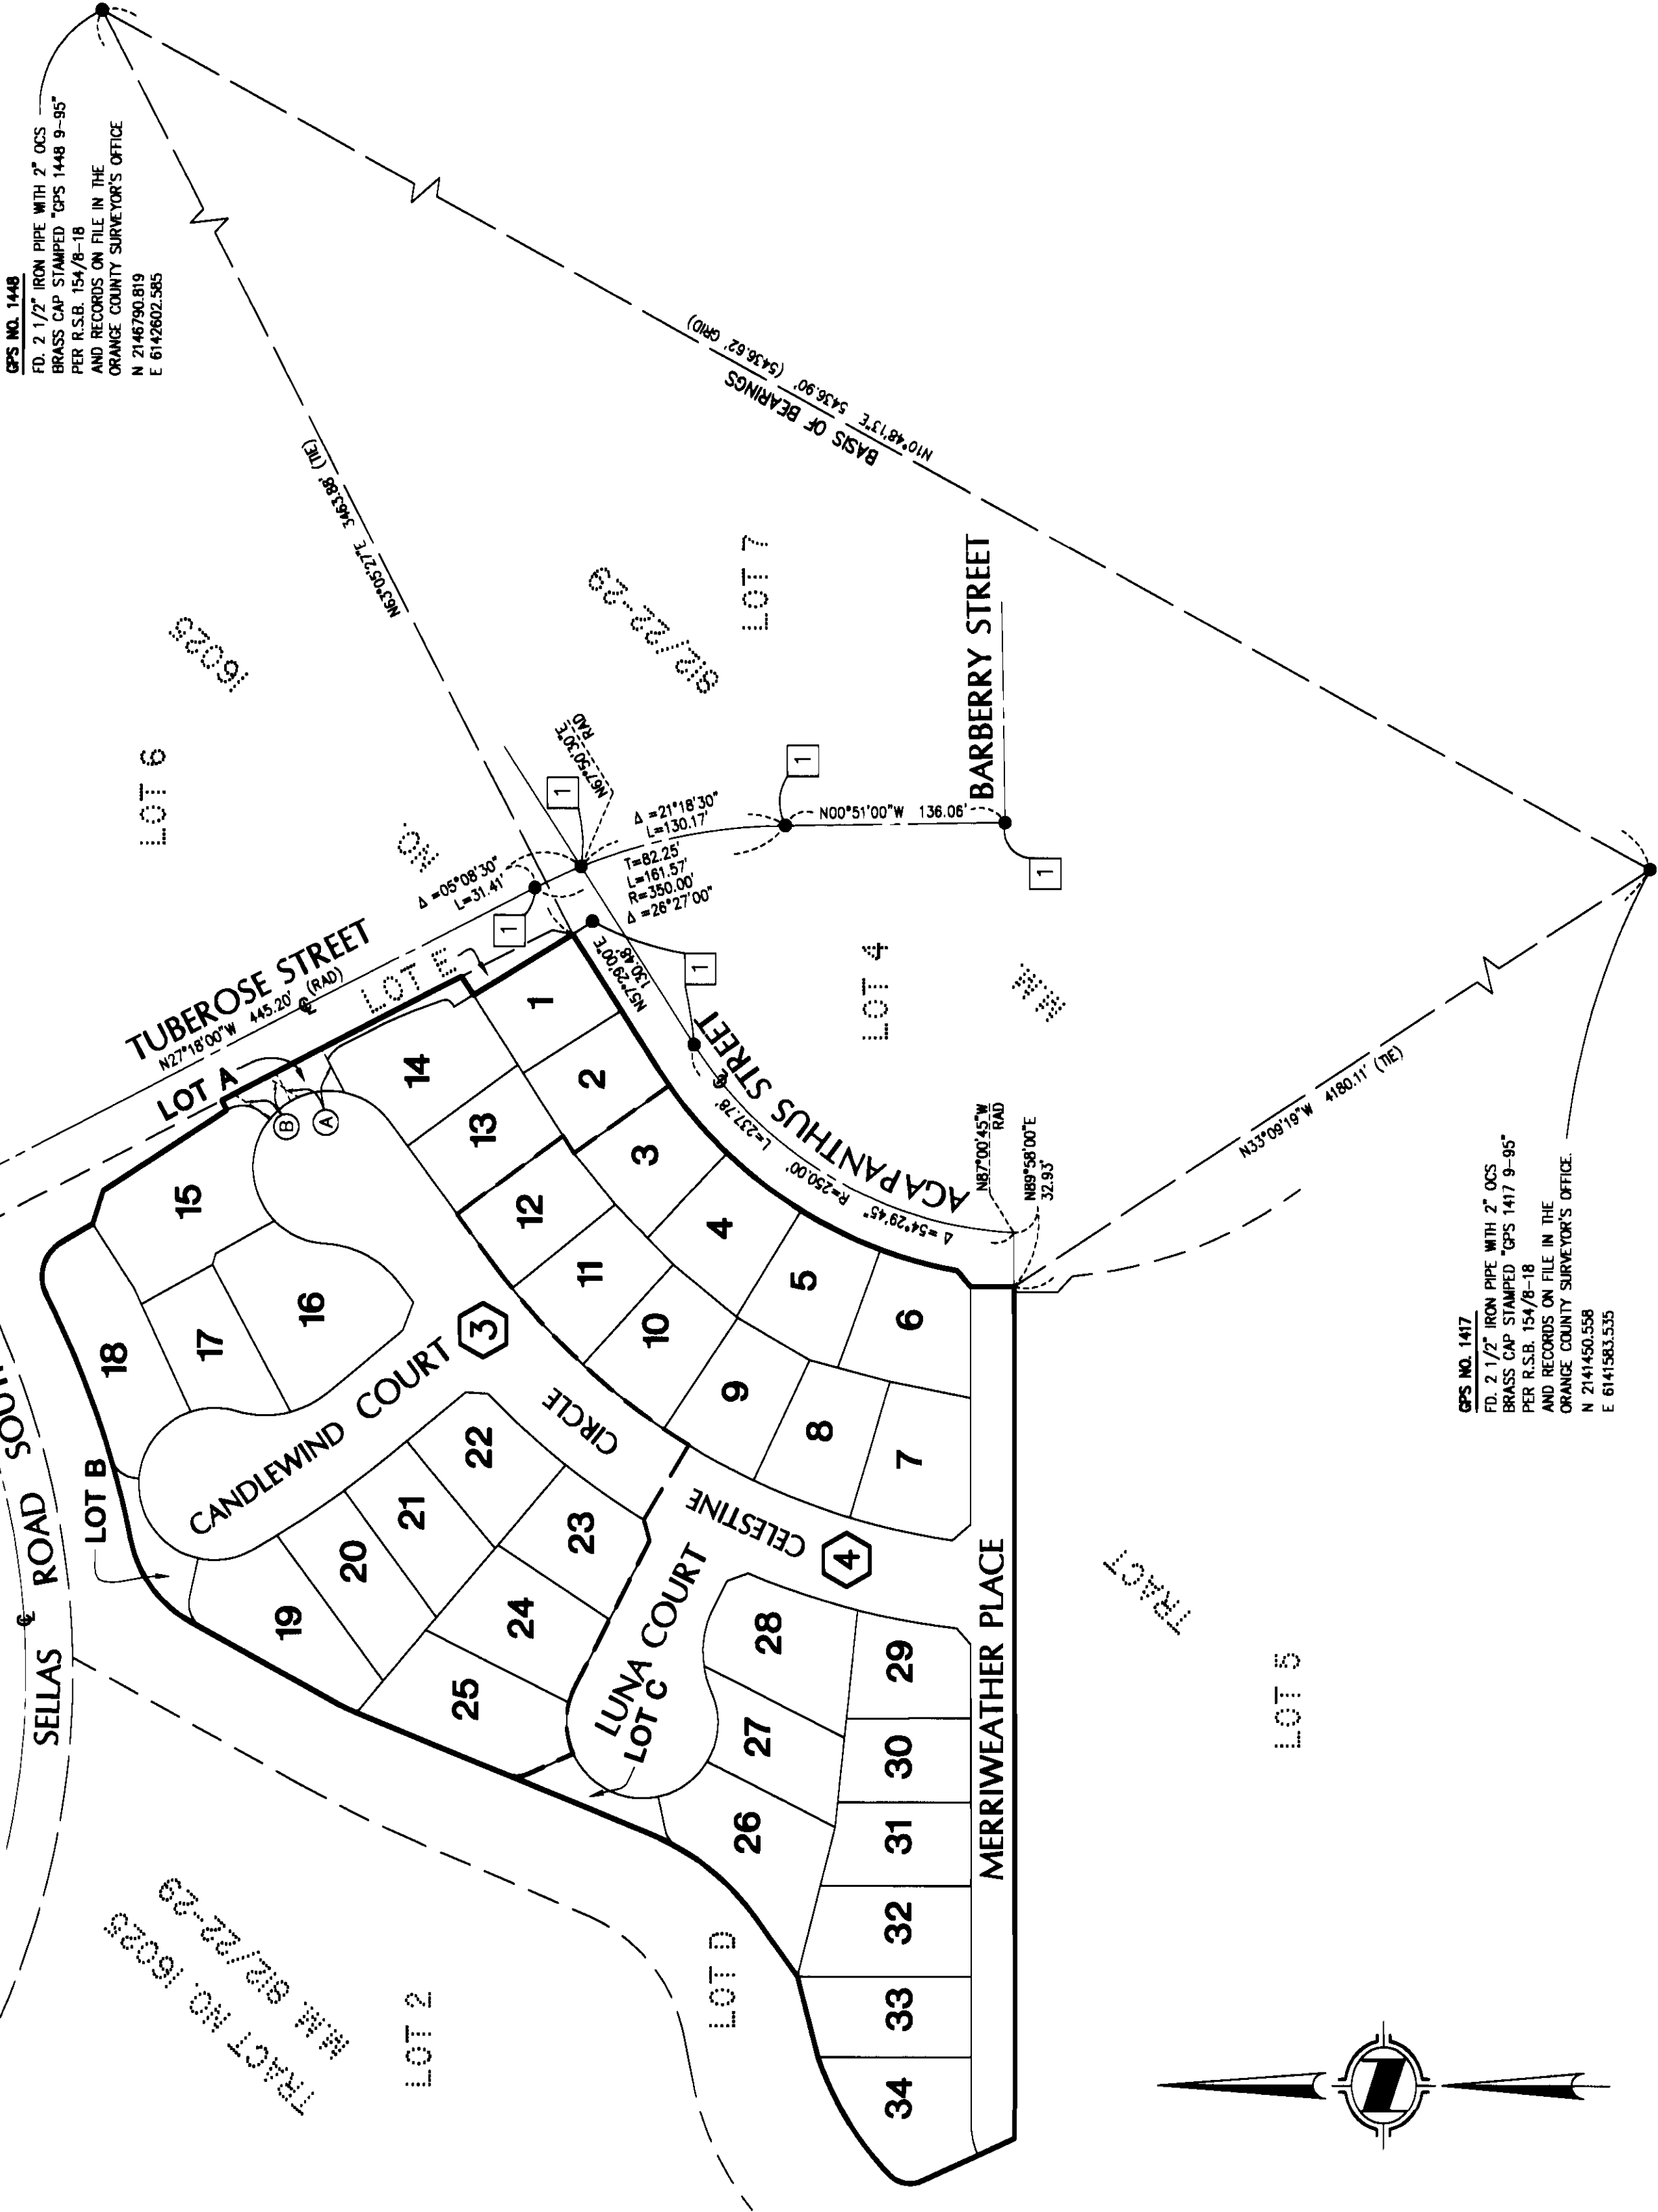

GPS NO. 1417
FD. 2 1/2" IRON PIPE WITH 2" OCS
BRASS CAP STAMPED "GPS 1417 9-95"
PER R.S.B. 154/9-18
AND RECORDS ON FILE IN THE
ORANGE COUNTY SURVEYOR'S OFFICE.
N 2141450.558
E 6141503.535

GPS NO. 1448
FD. 2 1/2" IRON PIPE WITH 2" OCS
BRASS CAP STAMPED "GPS 1448 9-95"
PER R.S.B. 154/9-18
AND RECORDS ON FILE IN THE
ORANGE COUNTY SURVEYOR'S OFFICE.
N 2146790.819
E 6142602.585

SHEET 3 OF 4 SHEETS
SCALE: T = 30'
34 NUMBERED LOTS AND LOTS
A THROUGH C, INCLUSIVE
ACREAGE: 5.901 ACRES
(ALL OF TENTATIVE
TRACT NO. 16114)

TRACT NO. 16114

IN UNINCORPORATED TERRITORY OF THE COUNTY OF ORANGE,
STATE OF CALIFORNIA

HUNSAKER AND ASSOCIATES IRVINE, INC.

RORY S. WILLIAMS, L.S. 6854

DATE OF SURVEY: DECEMBER, 2000

SELLAS ROAD SOUTH

SEE SHEET 2 FOR BASIS OF BEARINGS,
DATUM STATEMENT, NOTES, MONUMENT
NOTES, EASEMENT NOTES AND SHEET
INDEX AND GPS CONTROL MAP.


TRACT NO. 16025

M.M. 8/12/22-29

CURVE TABLE			
CURVE	DELTA	RADIUS	LENGTH
C1	01°15'48"	47.00'	1.04'

LINE TABLE		
LINE	BEARING	LENGTH
L1	N62°42'00"E	22.42'
L2	N32°23'34"E	27.34'
L3	N62°42'00"E	20.06'

MONUMENT OFFSET TABLE		
LINE	BEARING	LENGTH
P1	S28°48'57"E	9.16'
P2	S61°53'44"W	8.95'
P3	S65°07'32"W	8.82'
P4	N53°52'00"E	8.78'
P5	S33°44'47"W	8.81'
P6	S27°03'00"W	9.00'
P10	S32°31'00"E	14.75'
P15	S62°42'00"W	12.30'

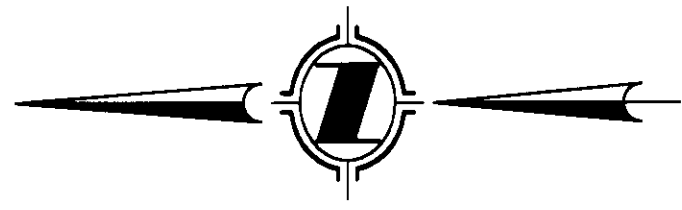

TRACT NO. 16025

M.M. 8/12/22-29

CANDLEWIND COURT

TUBEROSE STREET

CELESTINE STREET

ACAPANTHUS STREET

LUNA COURT

SHEET

SEE

SHEET 4 OF 4 SHEETS
SCALE: 1" = 30'
34 NUMBERED LOTS AND LOTS
A THROUGH C, INCLUSIVE
ACREAGE 5.901 ACRES
(ALL OF TENTATIVE
TRACT NO. 16114)


TRACT NO. 16114
IN UNINCORPORATED TERRITORY OF THE COUNTY OF ORANGE,
STATE OF CALIFORNIA

SEE SHEET 2 FOR BASIS OF BEARINGS,
DATUM STATEMENT, NOTES, MONUMENT
NOTES, EASEMENT NOTES AND SHEET
INDEX AND GPS CONTROL MAP.

RORY S. WILLIAMS, L.S. 6654

HUNSAKER AND ASSOCIATES IRVINE, INC.

DATE OF SURVEY: DECEMBER, 2000

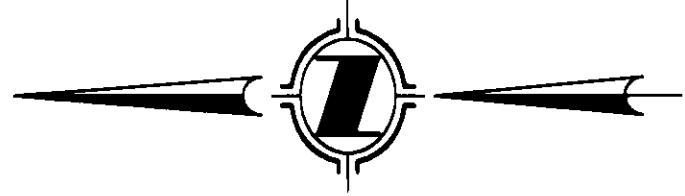

TRACT NO. 16025

M.M. 812/22-29

LOT 2

LOT C
0.038 AC.

MONUMENT OFFSET TABLE		
LINE	BEARING	LENGTH
P7	N27°03'00"E	8.77
P8	N27°03'00"E	10.38
P11	N64°42'32"W	14.75
P12	N38°55'32"W	14.75

CANDLEWIND
COURT

CIRCLE

LUNA COURT

LOT D

CELESTINE

ACAPANTHUS
STREET

MERRIWEATHER PLACE

TRACT NO. 16025

M.M. 812/22-29

LOT 5