

SHEET 1 OF 6 SHEETS

TRACT NO. 16115

ALL OF VESTING
TENTATIVE TRACT NO. 16115BLOCK MODULE
5157 25DATE OF SURVEY:
DECEMBER 2000IN UNINCORPORATED TERRITORY OF ORANGE COUNTY, CALIFORNIA
BEING A SUBDIVISION OF LOT 5 OF TRACT NO. 16025 FILED IN BOOK 812, PAGES 22
THROUGH 29 OF MISCELLANEOUS MAPS, RECORDS OF ORANGE COUNTY, CALIFORNIA.

APRIL 2001

JAMES F. GILLEN, L.S. 5557

HUITT-ZOLIARS

55 NUMBERED LOTS AND 4 LETTERED LOTS

9.147 ACRES

ACCEPTED AND FILED AT THE
REQUEST OF

FIRST AMERICAN TITLE INSURANCE COMPANY

DATE DECEMBER 26, 2001TIME 9:39 AM FEE \$ 17.00INSTRUMENT NO. 20010940037BOOK 825 PAGE 40-45 M/M

GARY L. GRANVILLE

COUNTY CLERK-RECORDER

BY [Signature]


DEPUTY

OWNERSHIP CERTIFICATE:

WE, THE UNDERSIGNED, BEING ALL PARTIES HAVING ANY RECORD TITLE INTEREST IN THE LAND COVERED BY THIS MAP, DO HEREBY CONSENT TO THE PREPARATION AND RECORDATION OF SAID MAP, AS SHOWN WITHIN THE DISTINCTIVE BORDER LINE. WE ALSO HEREBY DEDICATE TO THE PUBLIC FOR STREET PURPOSES: CELESTINE CIRCLE, MERRIWEATHER PLACE, PLUM STREET, OLIVE STREET, AND BEECHTREE STREET.

SURVEYOR'S STATEMENT:

I HEREBY STATE THAT THIS MAP CONSISTING OF 6 SHEETS, CORRECTLY REPRESENTS A TRUE AND COMPLETE SURVEY AS SHOWN MADE IN DECEMBER, 2000; WAS MADE BY ME OR UNDER MY DIRECTION; THAT THE MONUMENTS ARE OF THE CHARACTER AND OCCUPY OR WILL OCCUPY THE POSITIONS INDICATED BY SAID MAP; AND THAT SAID MONUMENTS WILL BE SUFFICIENT TO ENABLE THE SURVEY TO BE RETRACED.

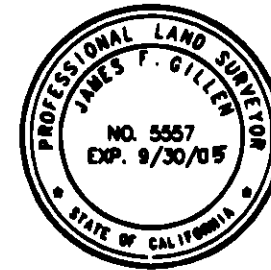

[Signature]
JAMES F. GILLEN
L.S. 5557
EXPIRATION DATE: 9/30/05

STANDARD PACIFIC CORP., A DELAWARE CORPORATION

BY: [Signature] BY: [Signature]
PRINT NAME: ANDREW H. PARNES PRINT NAME: JARI L. KARTOJAN
PRINT TITLE: CHIEF FINANCIAL OFFICER PRINT TITLE: VICE PRESIDENT

COUNTY SURVEYOR'S STATEMENT:

I HEREBY STATE THAT I HAVE EXAMINED THIS MAP AND HAVE FOUND IT TO BE SUBSTANTIALLY IN CONFORMANCE WITH THE TENTATIVE MAP AS FILED WITH, AMENDED AND APPROVED BY THE ORANGE COUNTY SUBDIVISION COMMITTEE; THAT ALL PROVISIONS OF THE SUBDIVISION MAP ACT AND COUNTY SUBDIVISION REGULATIONS HAVE BEEN COMPLIED WITH AND I AM SATISFIED SAID MAP IS TECHNICALLY CORRECT.

DATED THIS 5TH DAY OF DECEMBER, 2001.

[Signature]
JOHN CANAS, COUNTY SURVEYOR
LSL 408 EXPIRATION DATE: 09-30-05



DMB LADERA, L.L.C., A DELAWARE LIMITED LIABILITY COMPANY.
BENEFICIARY UNDER A DEED OF TRUST RECORDED FEBRUARY 15, 2001
AS INSTRUMENT NO. 20010084593 OF OFFICIAL RECORDS, AND HOLDER OF
A REPURCHASE OPTION RECORDED FEBRUARY 15, 2001 AS INSTRUMENT
NO. 20010084591 OF OFFICIAL RECORDS.

BY: RANCHO MISSION VIEJO, L.L.C., A DELAWARE LIMITED LIABILITY COMPANY,
AS AGENT AND/OR MANAGER.

BY: [Signature] BY: [Signature]
PRINT NAME: DENACOT STARKIN PRINT NAME: Stephen C. Schrank
PRINT TITLE: DIRECTOR OF COMMUNITY DEVELOPMENT PRINT TITLE: Executive Vice President

COUNTY TREASURER-TAX COLLECTOR'S CERTIFICATE:

STATE OF CALIFORNIA)
COUNTY OF ORANGE)

I HEREBY CERTIFY THAT ACCORDING TO THE RECORDS OF MY OFFICE THERE ARE NO LIENS AGAINST THE LAND COVERED BY THIS MAP OR ANY PART THEREOF FOR UNPAID STATE, COUNTY, MUNICIPAL OR LOCAL TAXES OR SPECIAL ASSESSMENTS COLLECTED AS TAXES, ~~EXCEPT TAXES OR SPECIAL ASSESSMENTS COLLECTED AS TAXES NOT YET PAYABLE.~~

~~AND DO ALSO HEREBY CERTIFY TO THE RECORDER OF ORANGE COUNTY THAT THE PROVISIONS OF THE SUBDIVISION MAP ACT HAVE BEEN COMPLIED WITH REGARDING DEPOSITS TO SECURE THE PAYMENT OF TAXES OR SPECIAL ASSESSMENTS COLLECTED AS TAXES ON THE LAND COVERED BY THIS MAP.~~

DATED THIS 16TH DAY OF October, 2001.

JOHN M.W. MOORLACH BY: [Signature]
COUNTY TREASURER-TAX COLLECTOR DEPUTY TREASURER-TAX COLLECTOR

CLERK OF THE BOARD OF SUPERVISORS' CERTIFICATE:

STATE OF CALIFORNIA)
COUNTY OF ORANGE)

I HEREBY CERTIFY THAT THIS MAP WAS PRESENTED FOR APPROVAL TO THE BOARD OF SUPERVISORS OF ORANGE COUNTY AT A REGULAR MEETING THEREOF HELD ON THE 18 DAY OF December, 2001, AND THAT THEREUPON SAID BOARD DID, BY AN ORDER DULY PASSED AND ENTERED, APPROVE SAID MAP AND DID ACCEPT ON BEHALF OF THE PUBLIC, SUBJECT TO IMPROVEMENTS; THE DEDICATION FOR STREET PURPOSES OF: CELESTINE CIRCLE, MERRIWEATHER PLACE, PLUM STREET, OLIVE STREET, AND BEECHTREE STREET.

DATED THIS 18 DAY OF December, 2001.

[Signature]
DARLENE J. BLOOM
CLERK OF THE BOARD OF SUPERVISORS



AUTOMATIC FIRE SPRINKLER NOTE:

ALL COMMERCIAL STRUCTURES GREATER THAN 6,000 SQUARE FEET; ALL MULTIFAMILY RESIDENTIAL STRUCTURES; ALL SINGLE-FAMILY STRUCTURES EXCEEDING 5,500 SQUARE FEET, AND ALL STRUCTURES EXCEEDING FIRE DEPARTMENT ACCESS REQUIREMENTS SHALL BE PROTECTED BY AN AUTOMATIC SPRINKLER SYSTEM. LOTS 23-26, 31-34, 40-44 AND 52-55 WILL REQUIRE AUTOMATIC FIRE SPRINKLER SYSTEM PER O.C.F.A.

HIGH FIRE HAZARD AREA NOTE:

THE LOTS SHOWN ON THIS MAP ARE IN A HIGH FIRE HAZARD AREA DUE TO WILD LAND EXPOSURE BASED ON STATE SRA MAPS.

THE PROPERTY SHOWN ON THIS MAP IS "TOTALLY EXCLUDED" FROM A "SPECIAL FIRE PROTECTION AREA." THERE ARE NO LOTS IN THIS TRACT THAT ARE SUBJECT TO CONSTRUCTION FEATURES OF THE ORANGE COUNTY ORDINANCE 3960.

NOTES:

PROPERTY MAY BE SUBJECT TO IMPACTS FROM THE FOOTHILL/EASTERN TRANSPORTATION CORRIDOR.

SEE SHEET 2 FOR NOTARY ACKNOWLEDGMENTS AND SIGNATURE OMISSIONS.

TRACT NO. 16115

ALL OF VESTING TENTATIVE
TRACT NO. 16115

IN UNINCORPORATED TERRITORY OF ORANGE COUNTY, CALIFORNIA

DATE OF SURVEY:
DECEMBER 2000

APRIL 2001

JAMES F. GILLEN, L.S. 5557

HUITT-ZOLIARS

55 NUMBERED LOTS AND 4 LETTERED LOTS

9.147 ACRES

STANDARD PACIFIC CORP.

STATE OF CALIFORNIA)
COUNTY OF ORANGE)SS

ON THIS 21ST DAY OF SEPTEMBER, 2001, BEFORE ME,
KATHLEEN M. VILLARI, A NOTARY PUBLIC IN AND FOR SAID STATE,
PERSONALLY APPEARED ANDREW H. FARNES AND
JARI L. KARLOZMAN, PERSONALLY KNOWN TO ME OR PROVED TO ME
~~ON THE BASIS OF SATISFACTORY EVIDENCE~~ TO BE THE PERSONS WHOSE NAMES
ARE SUBSCRIBED TO THE WITHIN INSTRUMENT AND ACKNOWLEDGED TO ME THAT
THEY EXECUTED THE SAME IN THEIR AUTHORIZED CAPACITIES, AND THAT BY THEIR
SIGNATURES ON THE INSTRUMENT THE PERSONS, OR THE ENTITY UPON BEHALF
OF WHICH THE PERSONS ACTED, EXECUTED THE INSTRUMENT.

WITNESS MY HAND: MY COMMISSION EXPIRES 8-10-2003
Kathleen M Villari MY PRINCIPAL PLACE OF BUSINESS
NOTARY PUBLIC IN AND FOR SAID STATE IS IN ORANGE COUNTY.
KATHLEEN M. VILLARI
PRINT NAME

DMB LADERA, L.L.C.

STATE OF CALIFORNIA)
COUNTY OF ORANGE)SS

ON THIS 1st DAY OF OCTOBER, 2001, BEFORE ME,
Tina T. Baker, A NOTARY PUBLIC IN AND FOR SAID STATE,
PERSONALLY APPEARED Donald T. Stahl AND
Stephen C. Schenk, PERSONALLY KNOWN TO ME OR PROVED TO ME
~~ON THE BASIS OF SATISFACTORY EVIDENCE~~ TO BE THE PERSONS WHOSE NAMES
ARE SUBSCRIBED TO THE WITHIN INSTRUMENT AND ACKNOWLEDGED TO ME THAT
THEY EXECUTED THE SAME IN THEIR AUTHORIZED CAPACITIES, AND THAT BY THEIR
SIGNATURES ON THE INSTRUMENT THE PERSONS, OR THE ENTITY UPON BEHALF
OF WHICH THE PERSONS ACTED, EXECUTED THE INSTRUMENT.

WITNESS MY HAND: MY COMMISSION EXPIRES 8-29-2004
Tina T. Baker MY PRINCIPAL PLACE OF BUSINESS
NOTARY PUBLIC IN AND FOR SAID STATE IS IN ORANGE COUNTY.
Tina T. Baker
PRINT NAME

SIGNATURE OMISSIONS:

IN ACCORDANCE WITH THE PROVISIONS OF SECTION 66436(o) (3) OF THE SUBDIVISION
MAP ACT, THE FOLLOWING SIGNATURE HAS BEEN OMITTED:

1. LADERA DEVELOPMENT COMPANY, L.L.C., HOLDER OF OIL, GAS, MINERAL, AND WATER RIGHTS
RECORDED DECEMBER 10, 1996 AS INSTRUMENT NO. 19960624029 OF OFFICIAL RECORDS.
2. DMB LADERA, L.L.C., A DELAWARE LIMITED LIABILITY COMPANY, HOLDER OF EASEMENTS
RECORDED FEBRUARY 15, 2001 AS INSTRUMENT NO. 20010084592 OF OFFICIAL RECORDS.


BASIS OF BEARINGS:

BEARINGS SHOWN HEREON ARE BASED ON THE SOUTHWESTERLY LINE OF LOT 5, BEING N48°53'37"W
AS SHOWN ON TRACT NO. 16025, FILED IN BOOK 812, PAGES 22 THROUGH 29 OF MISCELLANEOUS MAPS,
RECORDS OF ORANGE COUNTY, CALIFORNIA.

MONUMENT NOTES:

- ▲ INDICATES FOUND 2" I.P. TAGGED "P.L.S. 5557" PER TRACT NO. 16025, M.M. 812/22-29
- INDICATES LOCATION OF 1" I.P. TAGGED "P.L.S. 5557" OR SPIKE & WASHER
STAMPED "P.L.S. 5557" OR LEAD, TACK & TAG "P.L.S. 5557" TO BE SET PER
TRACT NO. 16025, M.M. 812/22-29.
- △ INDICATES LOCATION OF 2" I.P. TAGGED "P.L.S. 5557" OR SPIKE & WASHER
STAMPED "P.L.S. 5557" OR LEAD, TACK & TAG "P.L.S. 5557" TO BE SET PER
TRACT NO. 16025, M.M. 812/22-29.
- INDICATES LOCATION OF 1" I.P. TAGGED "P.L.S. 5557" OR SPIKE & WASHER
STAMPED "P.L.S. 5557" OR LEAD, TACK & TAG "P.L.S. 5557" TO BE SET WITHIN
90 DAYS AFTER ACCEPTANCE OF IMPROVEMENTS.
- 2" I.P. TAGGED "P.L.S. 5557" OR SPIKE & WASHER STAMPED "P.L.S. 5557" OR LEAD,
TACK AND TAG "P.L.S. 5557" TO BE SET AT ALL TRACT BOUNDARY CORNERS,
WITHIN 90 DAYS AFTER ACCEPTANCE OF IMPROVEMENTS, UNLESS OTHERWISE NOTED.
- 1" I.P. TAGGED "P.L.S. 5557" OR SPIKE & WASHER STAMPED "P.L.S. 5557" OR LEAD,
TACK AND TAG "P.L.S. 5557" TO BE SET AT ALL INTERIOR LOT CORNERS, EXCEPT LOT
CORNERS ABUTTING STREETS; LEAD, TACK & TAG "P.L.S. 5557" TO BE SET IN TOP OF
CURB OR SIDEWALK ON A 8.75' OR 14.75' OFFSET ON SIDE LOT LINES PRODUCED FOR LOT
CORNERS ABUTTING STREETS, WITHIN 90 DAYS AFTER ACCEPTANCE OF IMPROVEMENTS,
UNLESS OTHERWISE NOTED.

NO MONUMENTATION TO BE SET AT BC'S AND EC'S OF STREET RIGHT OF WAY LINES,
UNLESS OTHERWISE NOTED.

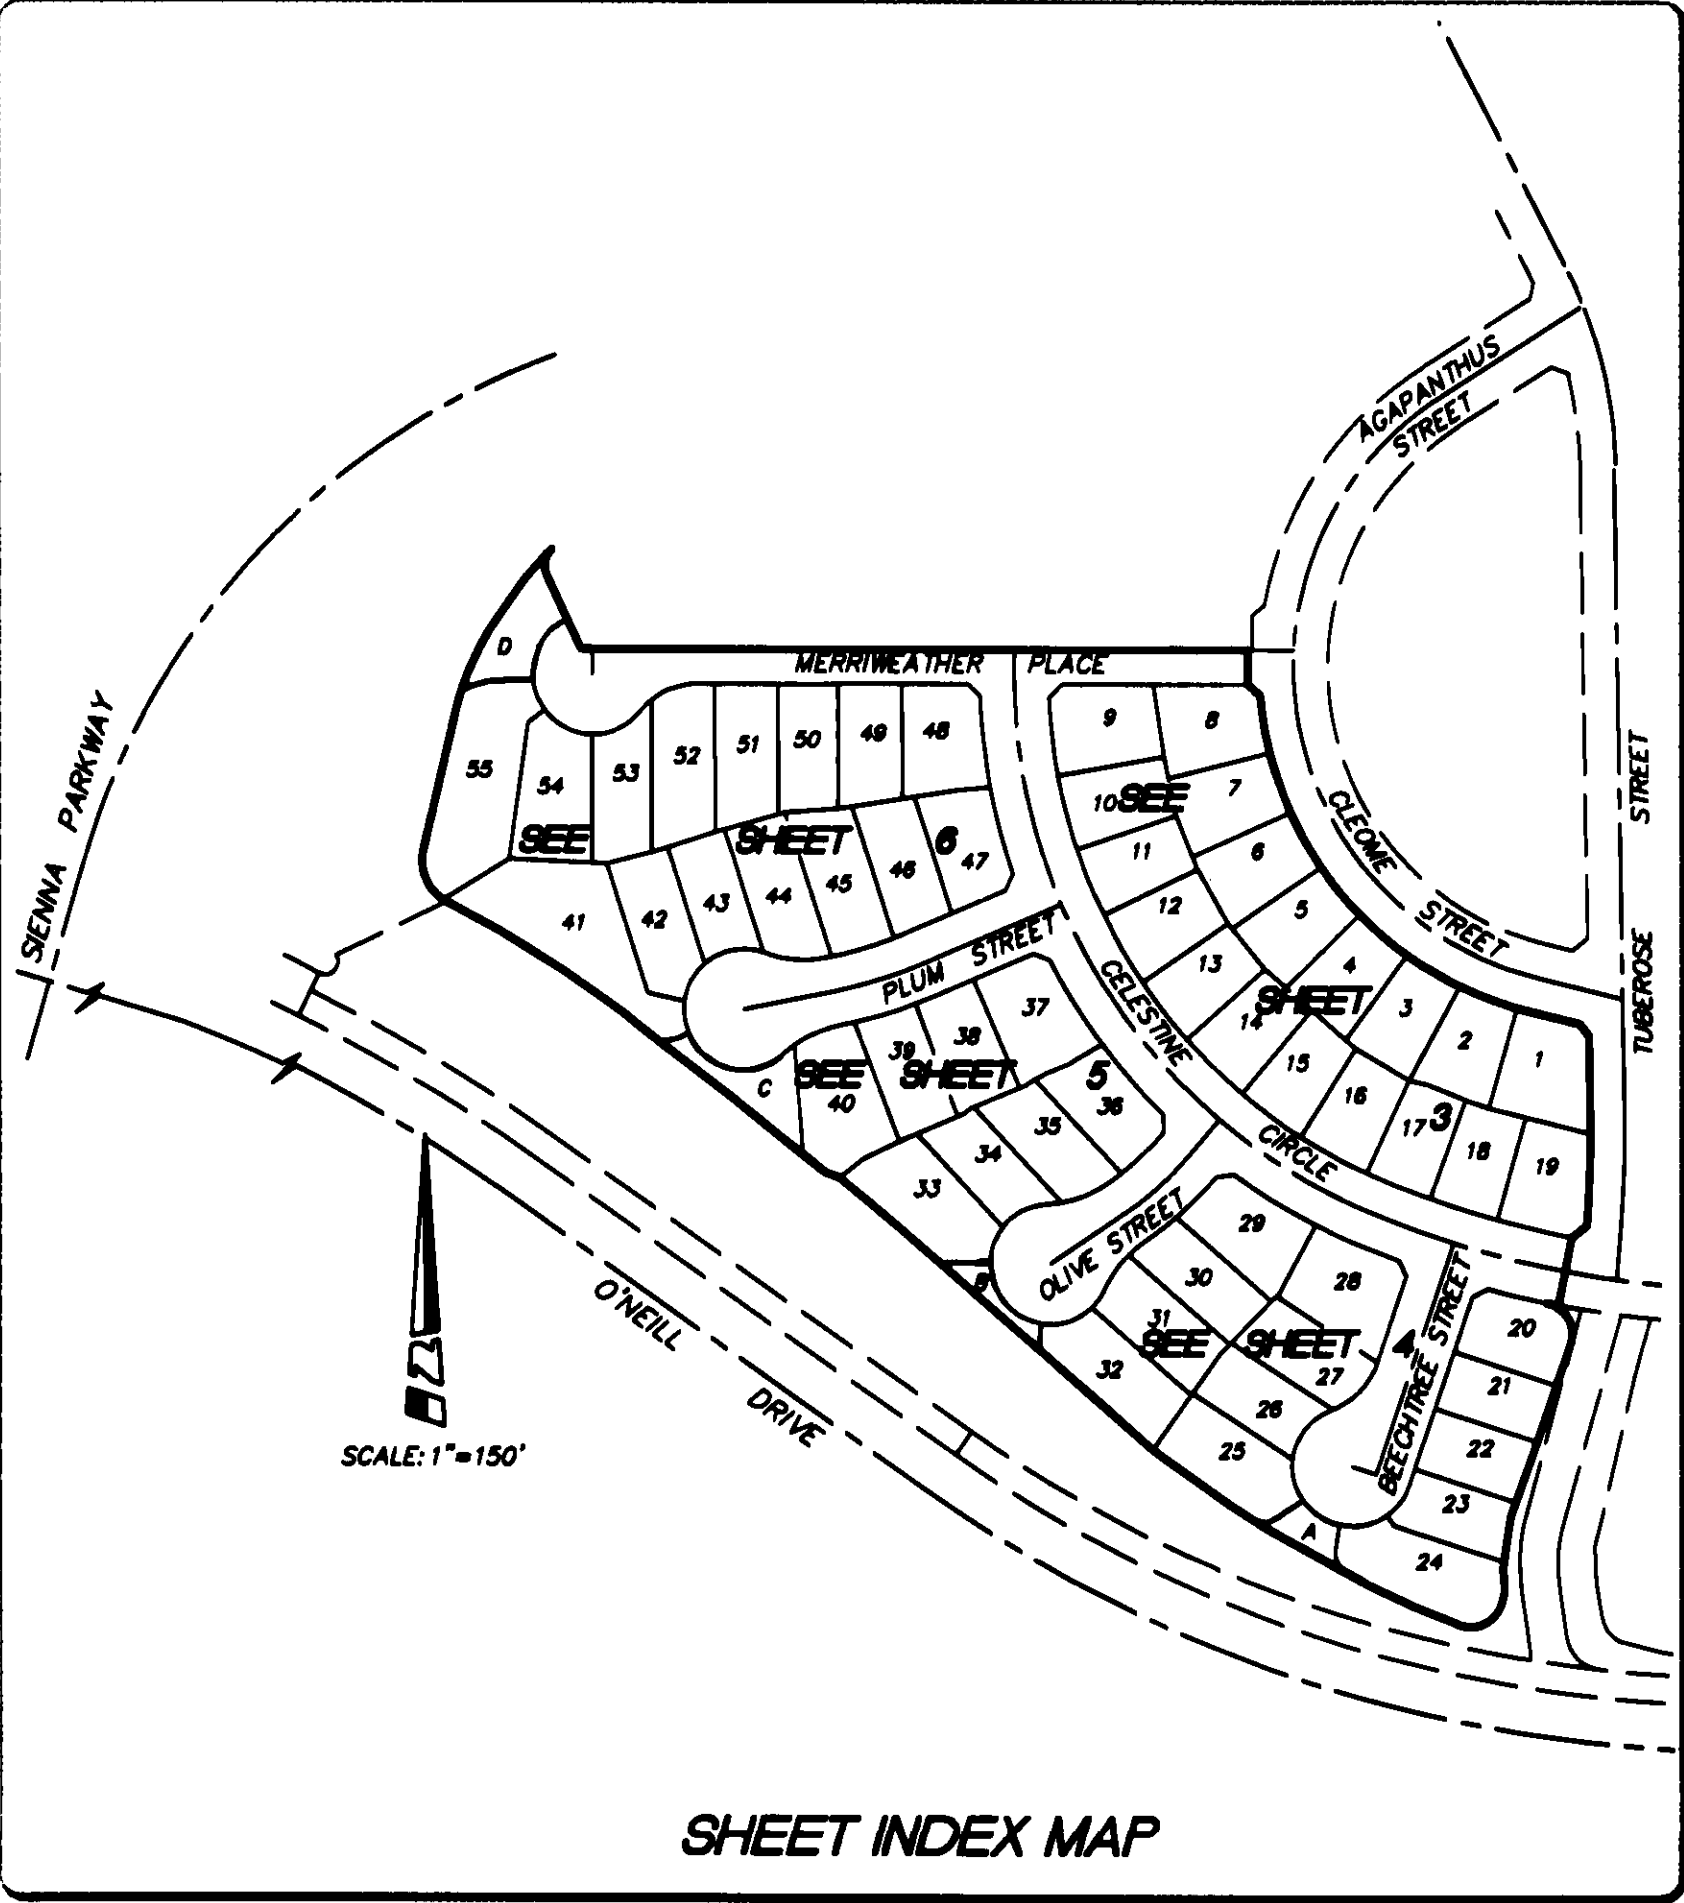

SHEET 3 OF 6 SHEETS

TRACT NO. 16115

ALL OF VESTING TENTATIVE
TRACT NO. 16115

IN UNINCORPORATED TERRITORY OF ORANGE COUNTY, CALIFORNIA

DATE OF SURVEY:
DECEMBER 2000



APRIL 2001

JAMES F. GILLEN, L.S. 5557

HUITT-ZOLIARS

55 NUMBERED LOTS AND 4 LETTERED LOTS

9.147 ACRES

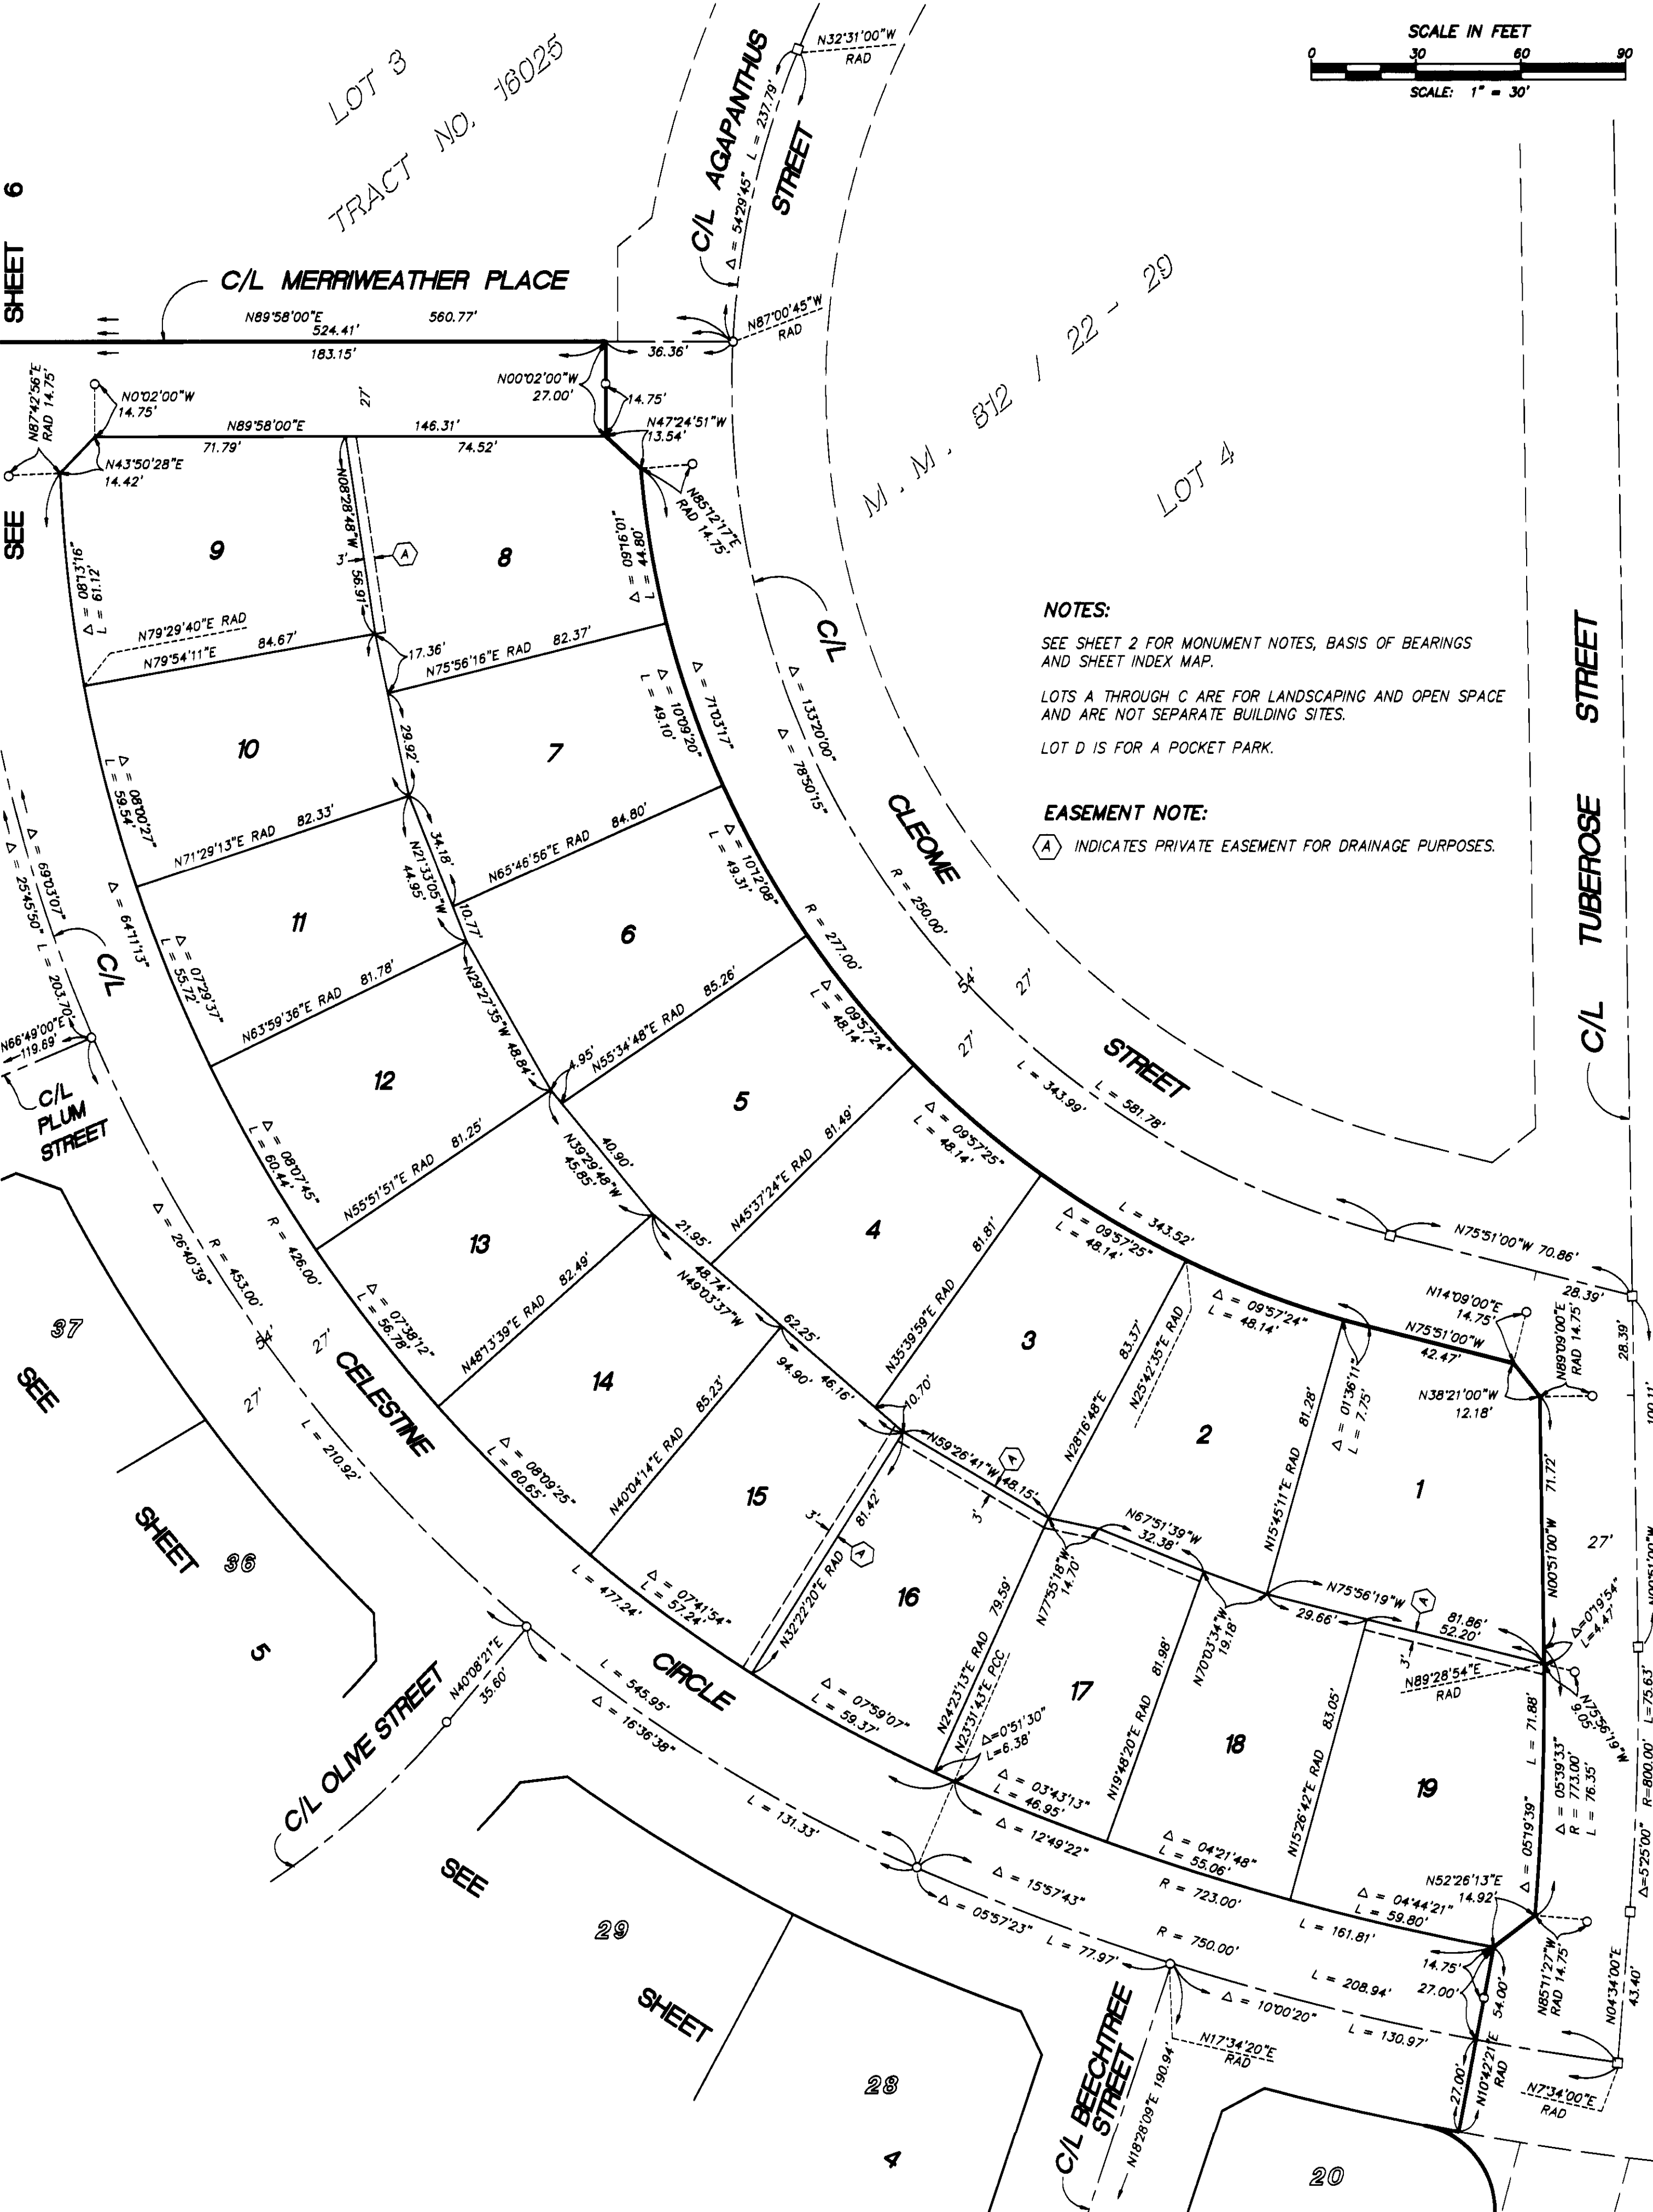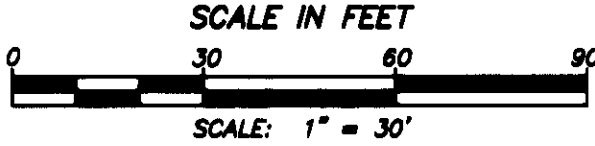

SHEET 4 OF 6 SHEETS

TRACT NO. 16115

ALL OF VESTING TENTATIVE
TRACT NO. 16115

IN UNINCORPORATED TERRITORY OF ORANGE COUNTY, CALIFORNIA

DATE OF SURVEY:
DECEMBER 2000



APRIL 2001

JAMES F. GILLEN, L.S. 5557

HUITT-ZOLIARS

55 NUMBERED LOTS AND 4 LETTERED LOTS

9.147 ACRES

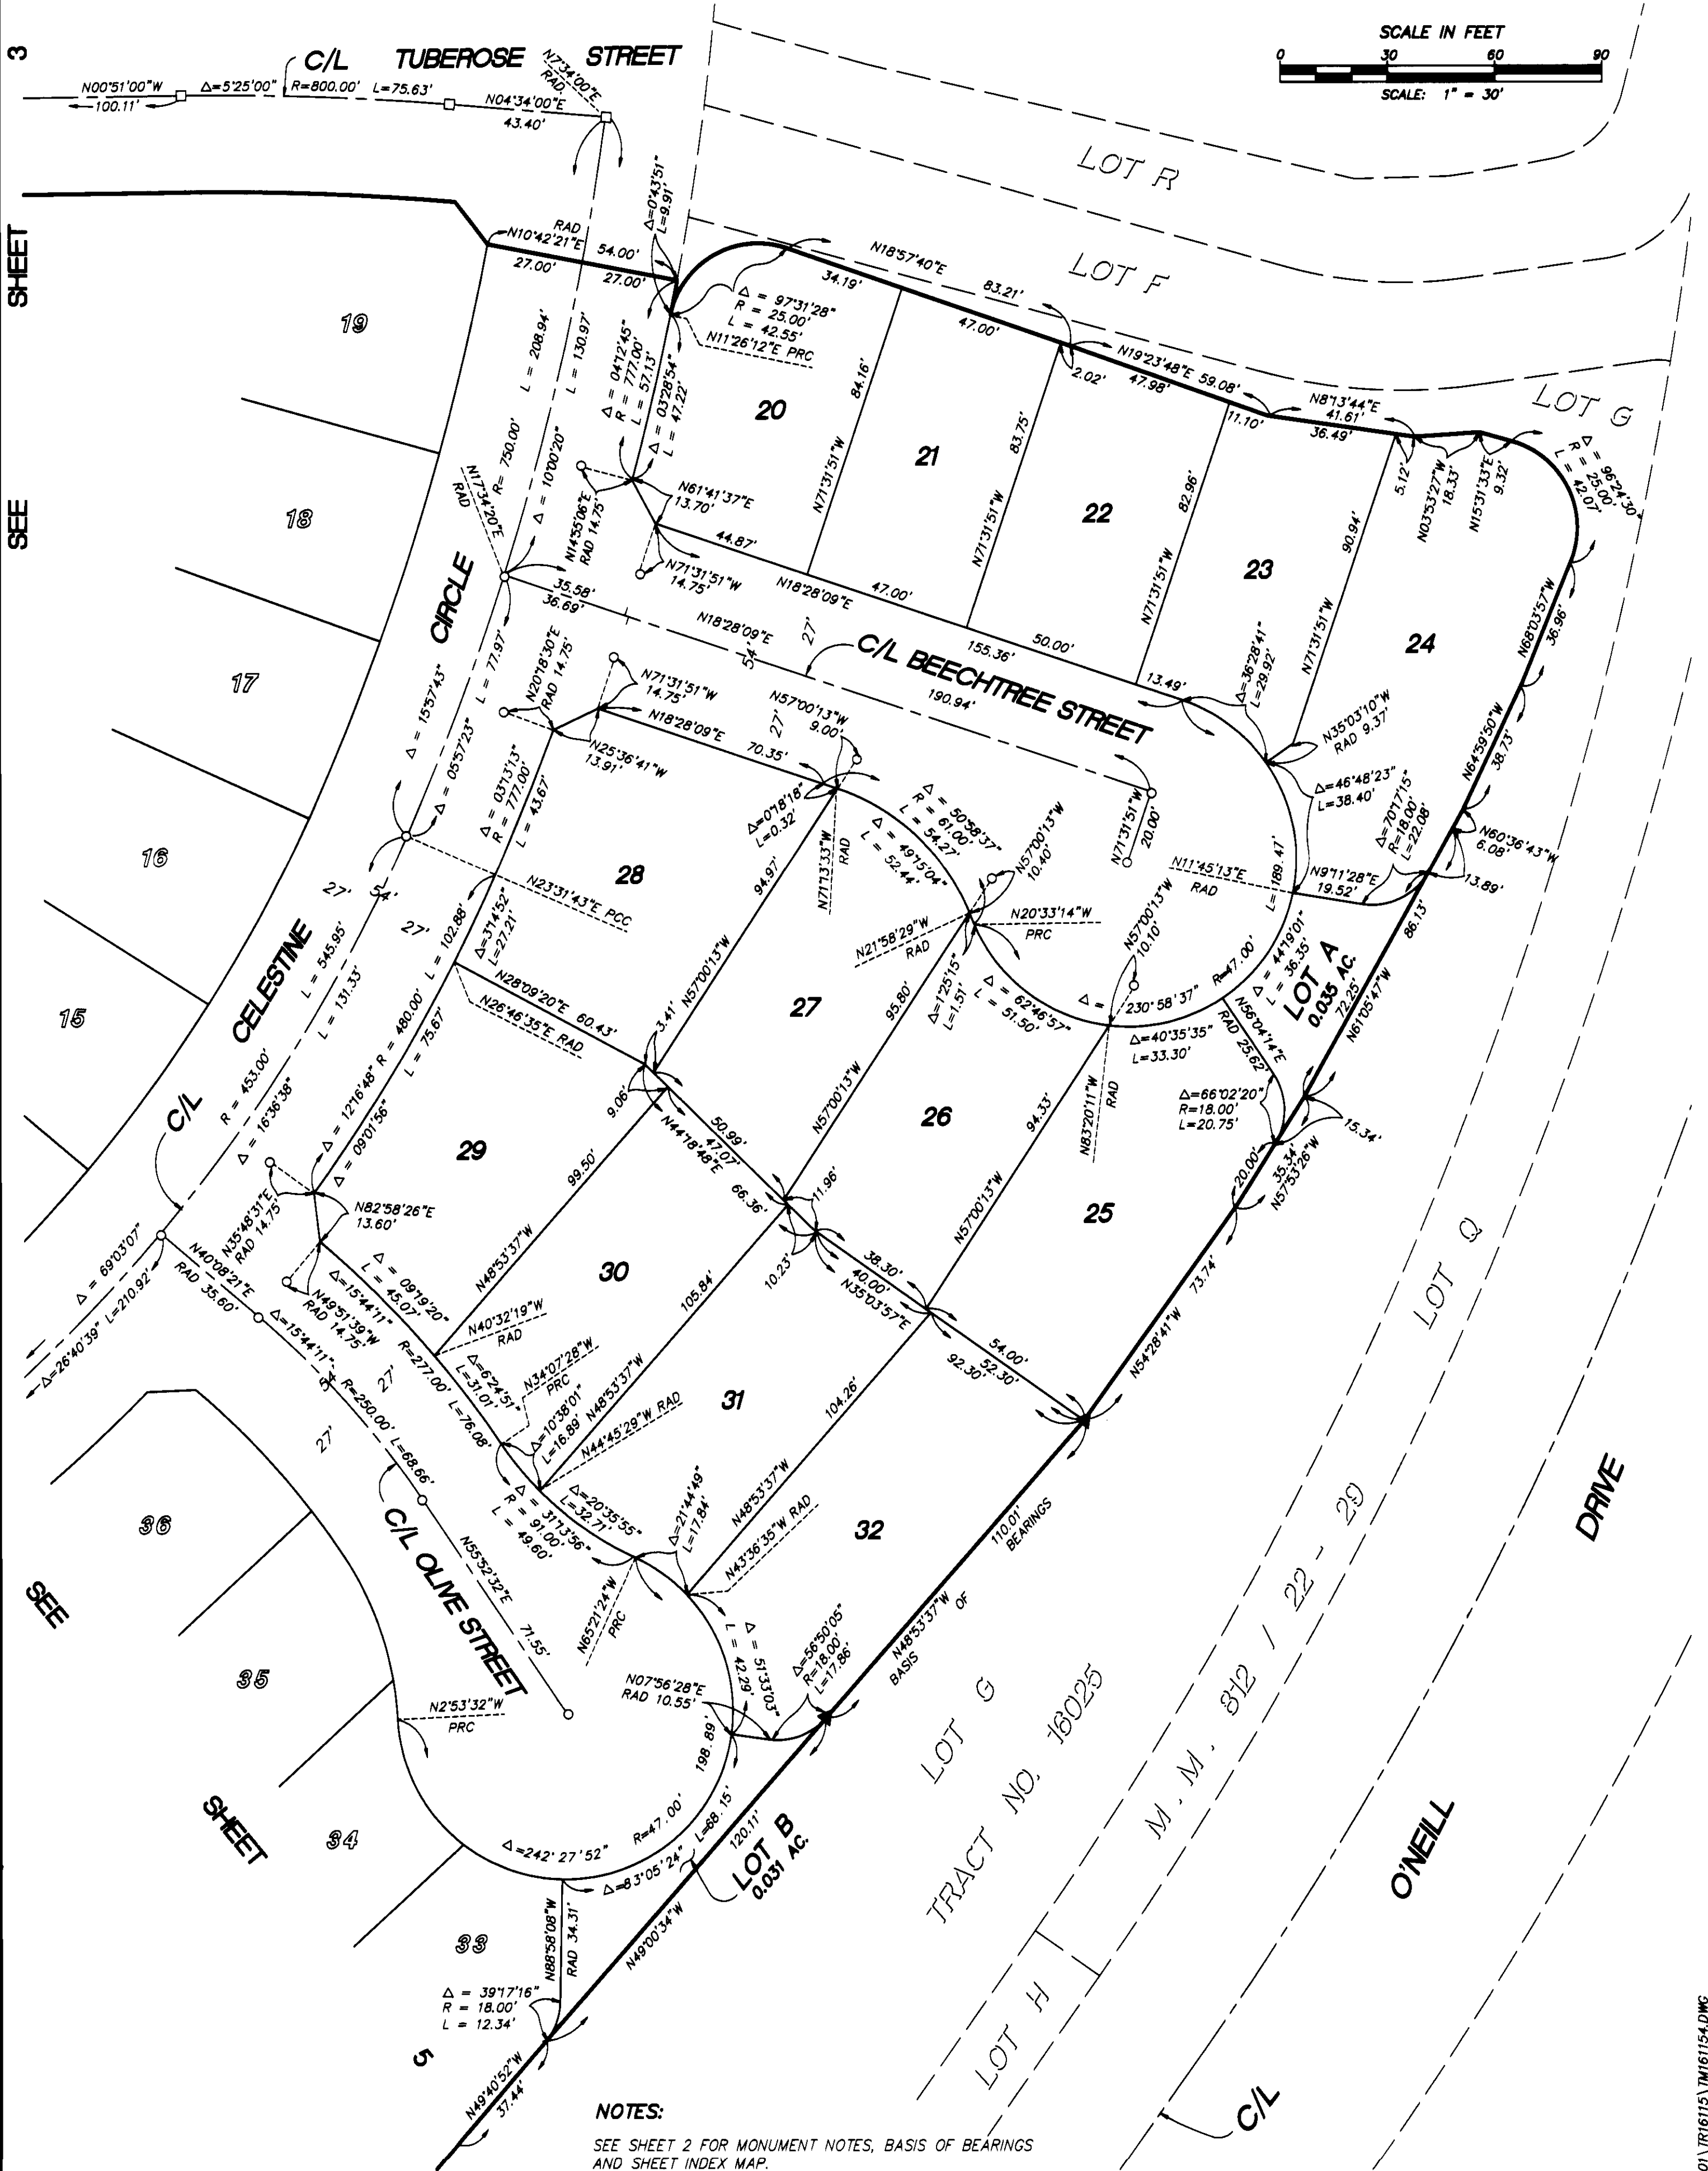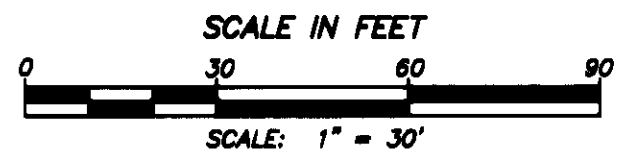

NOTES:

SEE SHEET 2 FOR MONUMENT NOTES, BASIS OF BEARINGS
AND SHEET INDEX MAP.

LOTS A THROUGH C ARE FOR LANDSCAPING AND OPEN SPACE
AND ARE NOT SEPARATE BUILDING SITES.

LOT D IS FOR A POCKET PARK.

SHEET 5 OF 6 SHEETS

TRACT NO. 16115

ALL OF VESTING TENTATIVE
TRACT NO. 16115

IN UNINCORPORATED TERRITORY OF ORANGE COUNTY, CALIFORNIA

DATE OF SURVEY:
DECEMBER 2000


APRIL 2001

JAMES F. GILLEN, L.S. 5557

HUITT-ZOLIARS

55 NUMBERED LOTS AND 4 LETTERED LOTS

9.147 ACRES

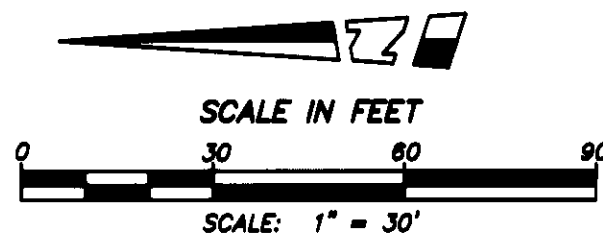


NOTES:

SEE SHEET 2 FOR MONUMENT NOTES, BASIS OF BEARINGS
AND SHEET INDEX MAP.

LOTS A THROUGH C ARE FOR LANDSCAPING AND OPEN SPACE
AND ARE NOT SEPARATE BUILDING SITES.

LOT D IS FOR A POCKET PARK.

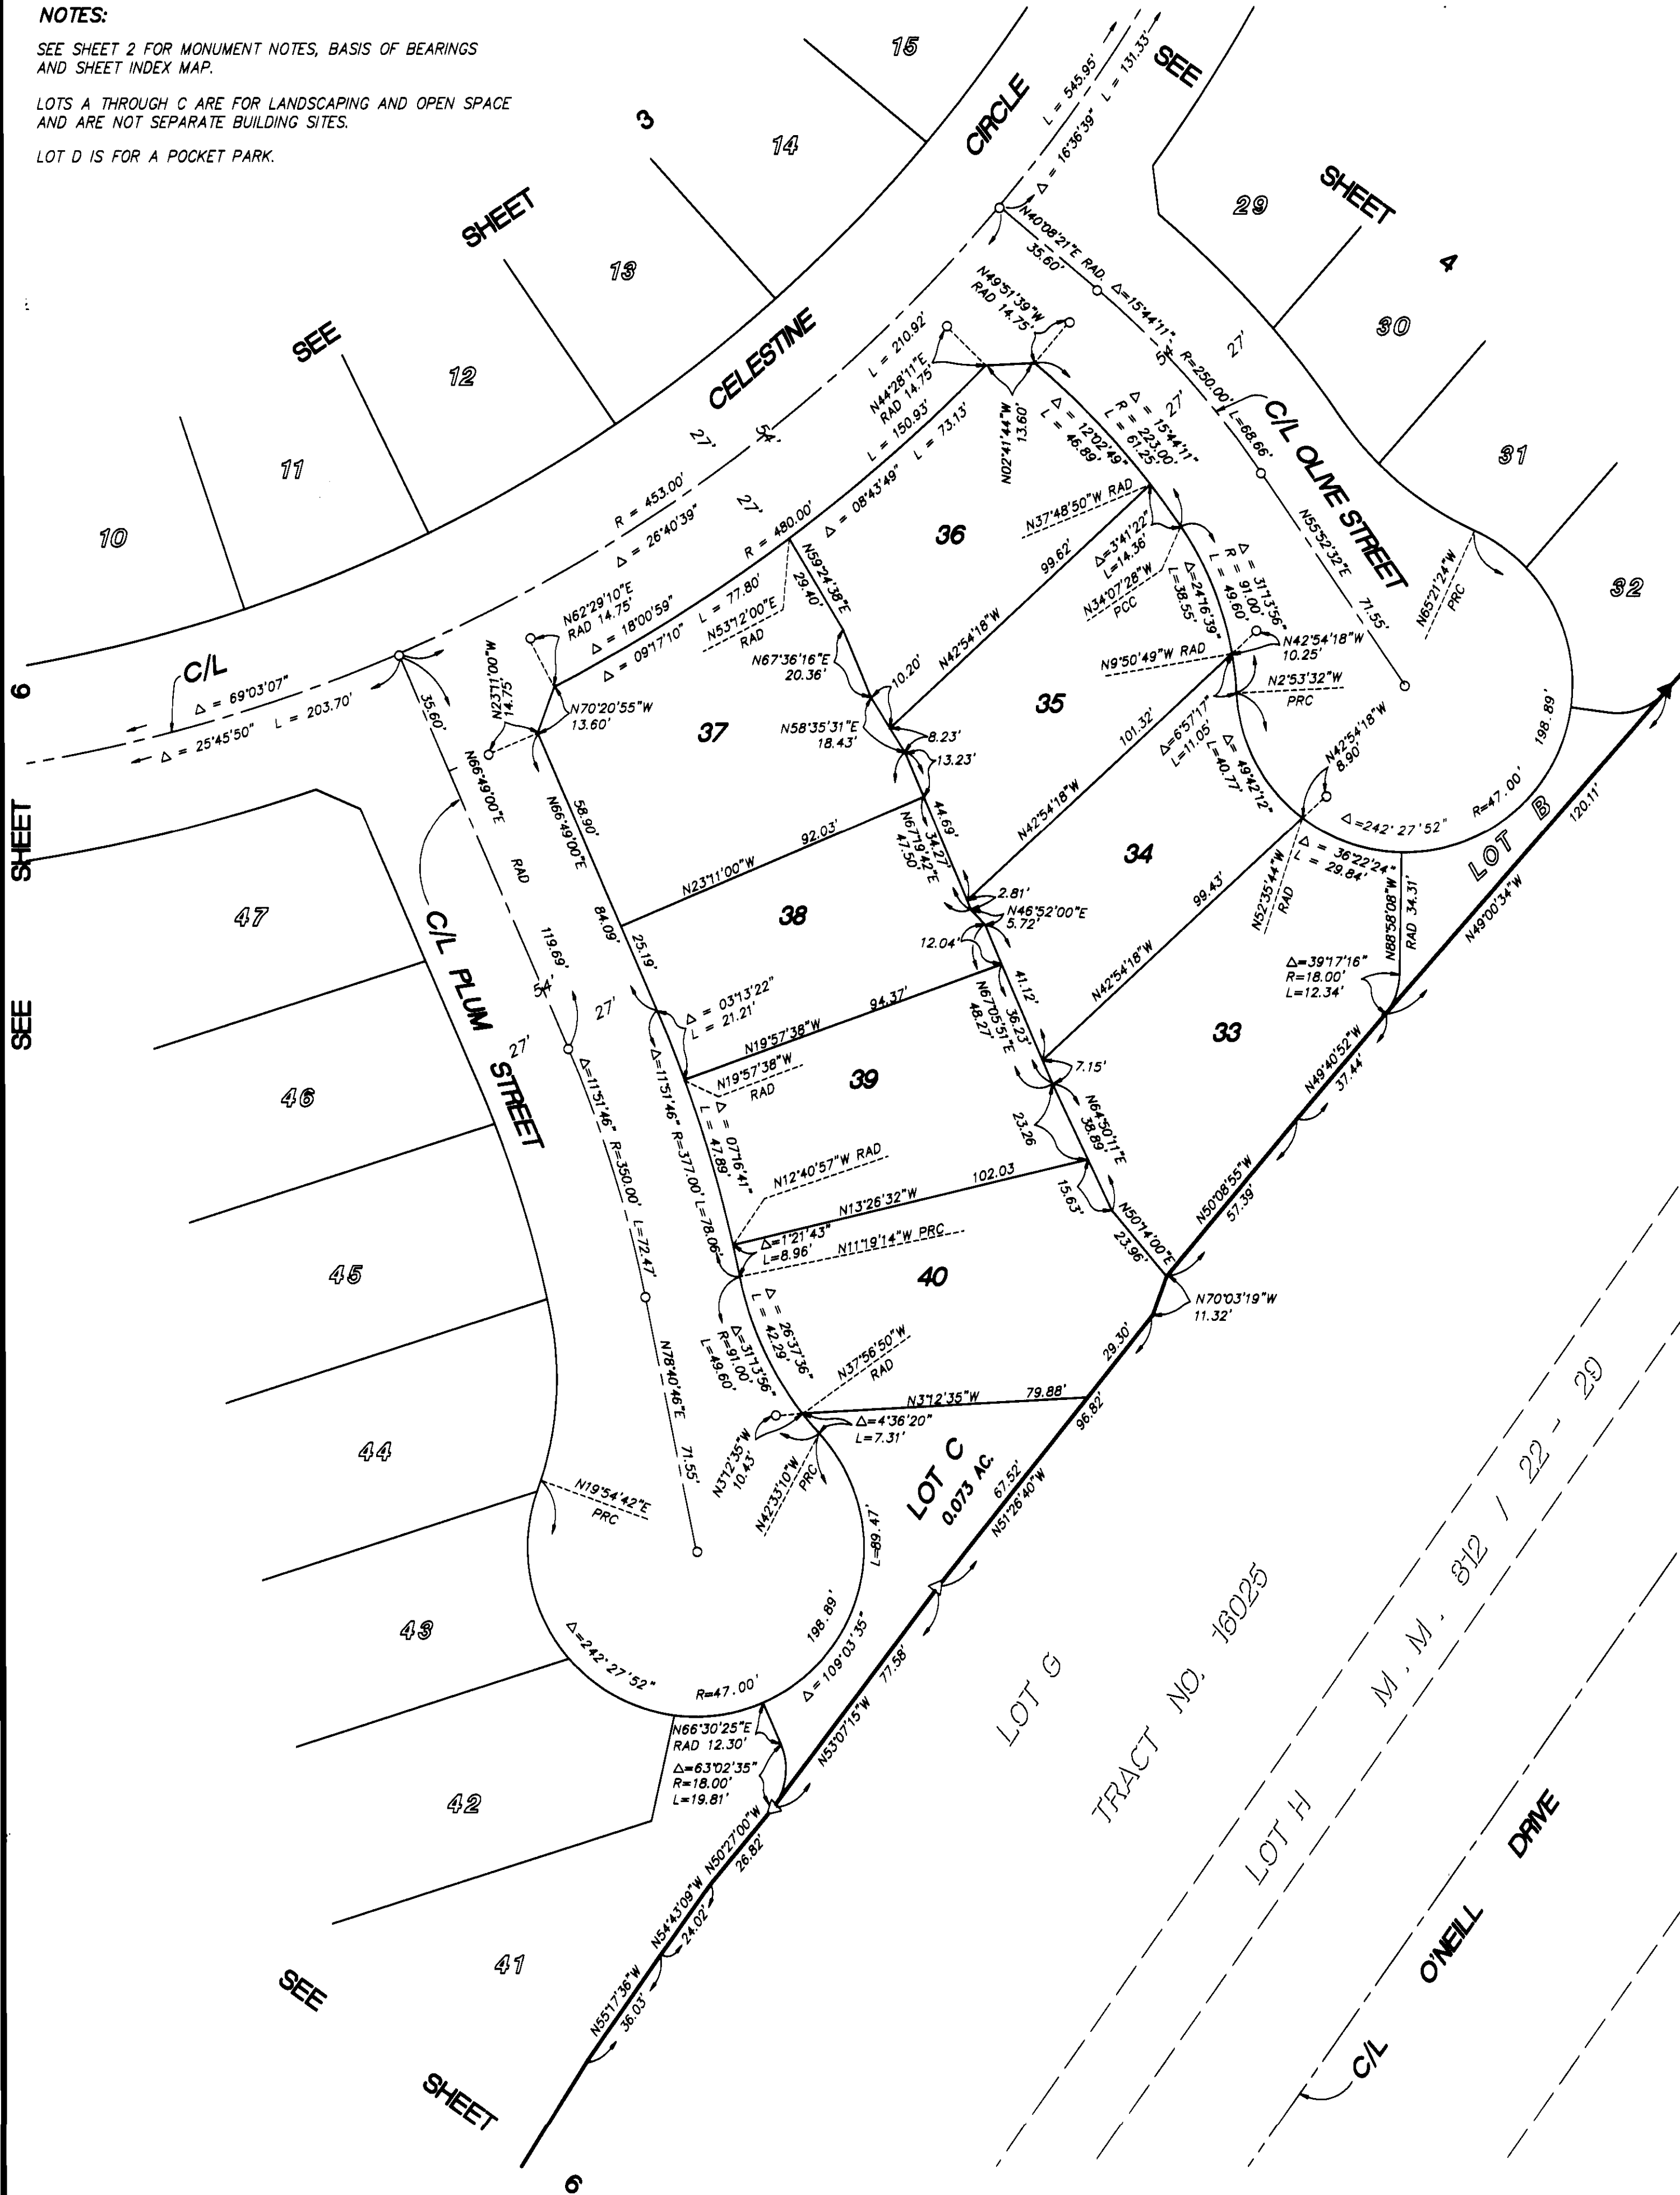

TRACT NO. 16115

IN UNINCORPORATED TERRITORY OF ORANGE COUNTY, CALIFORNIA


APRIL 2001

JAMES F. GILLEN, L.S. 5557

HUITT-ZOLIARS


55 NUMBERED LOTS AND 4 LETTERED LOTS

9.147 ACRES

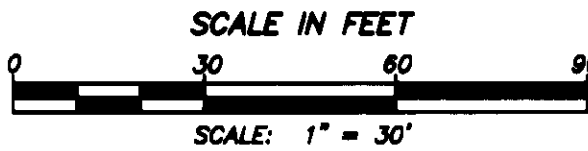

EASEMENT NOTE:

(A) INDICATES PRIVATE EASEMENT
FOR DRAINAGE PURPOSES.

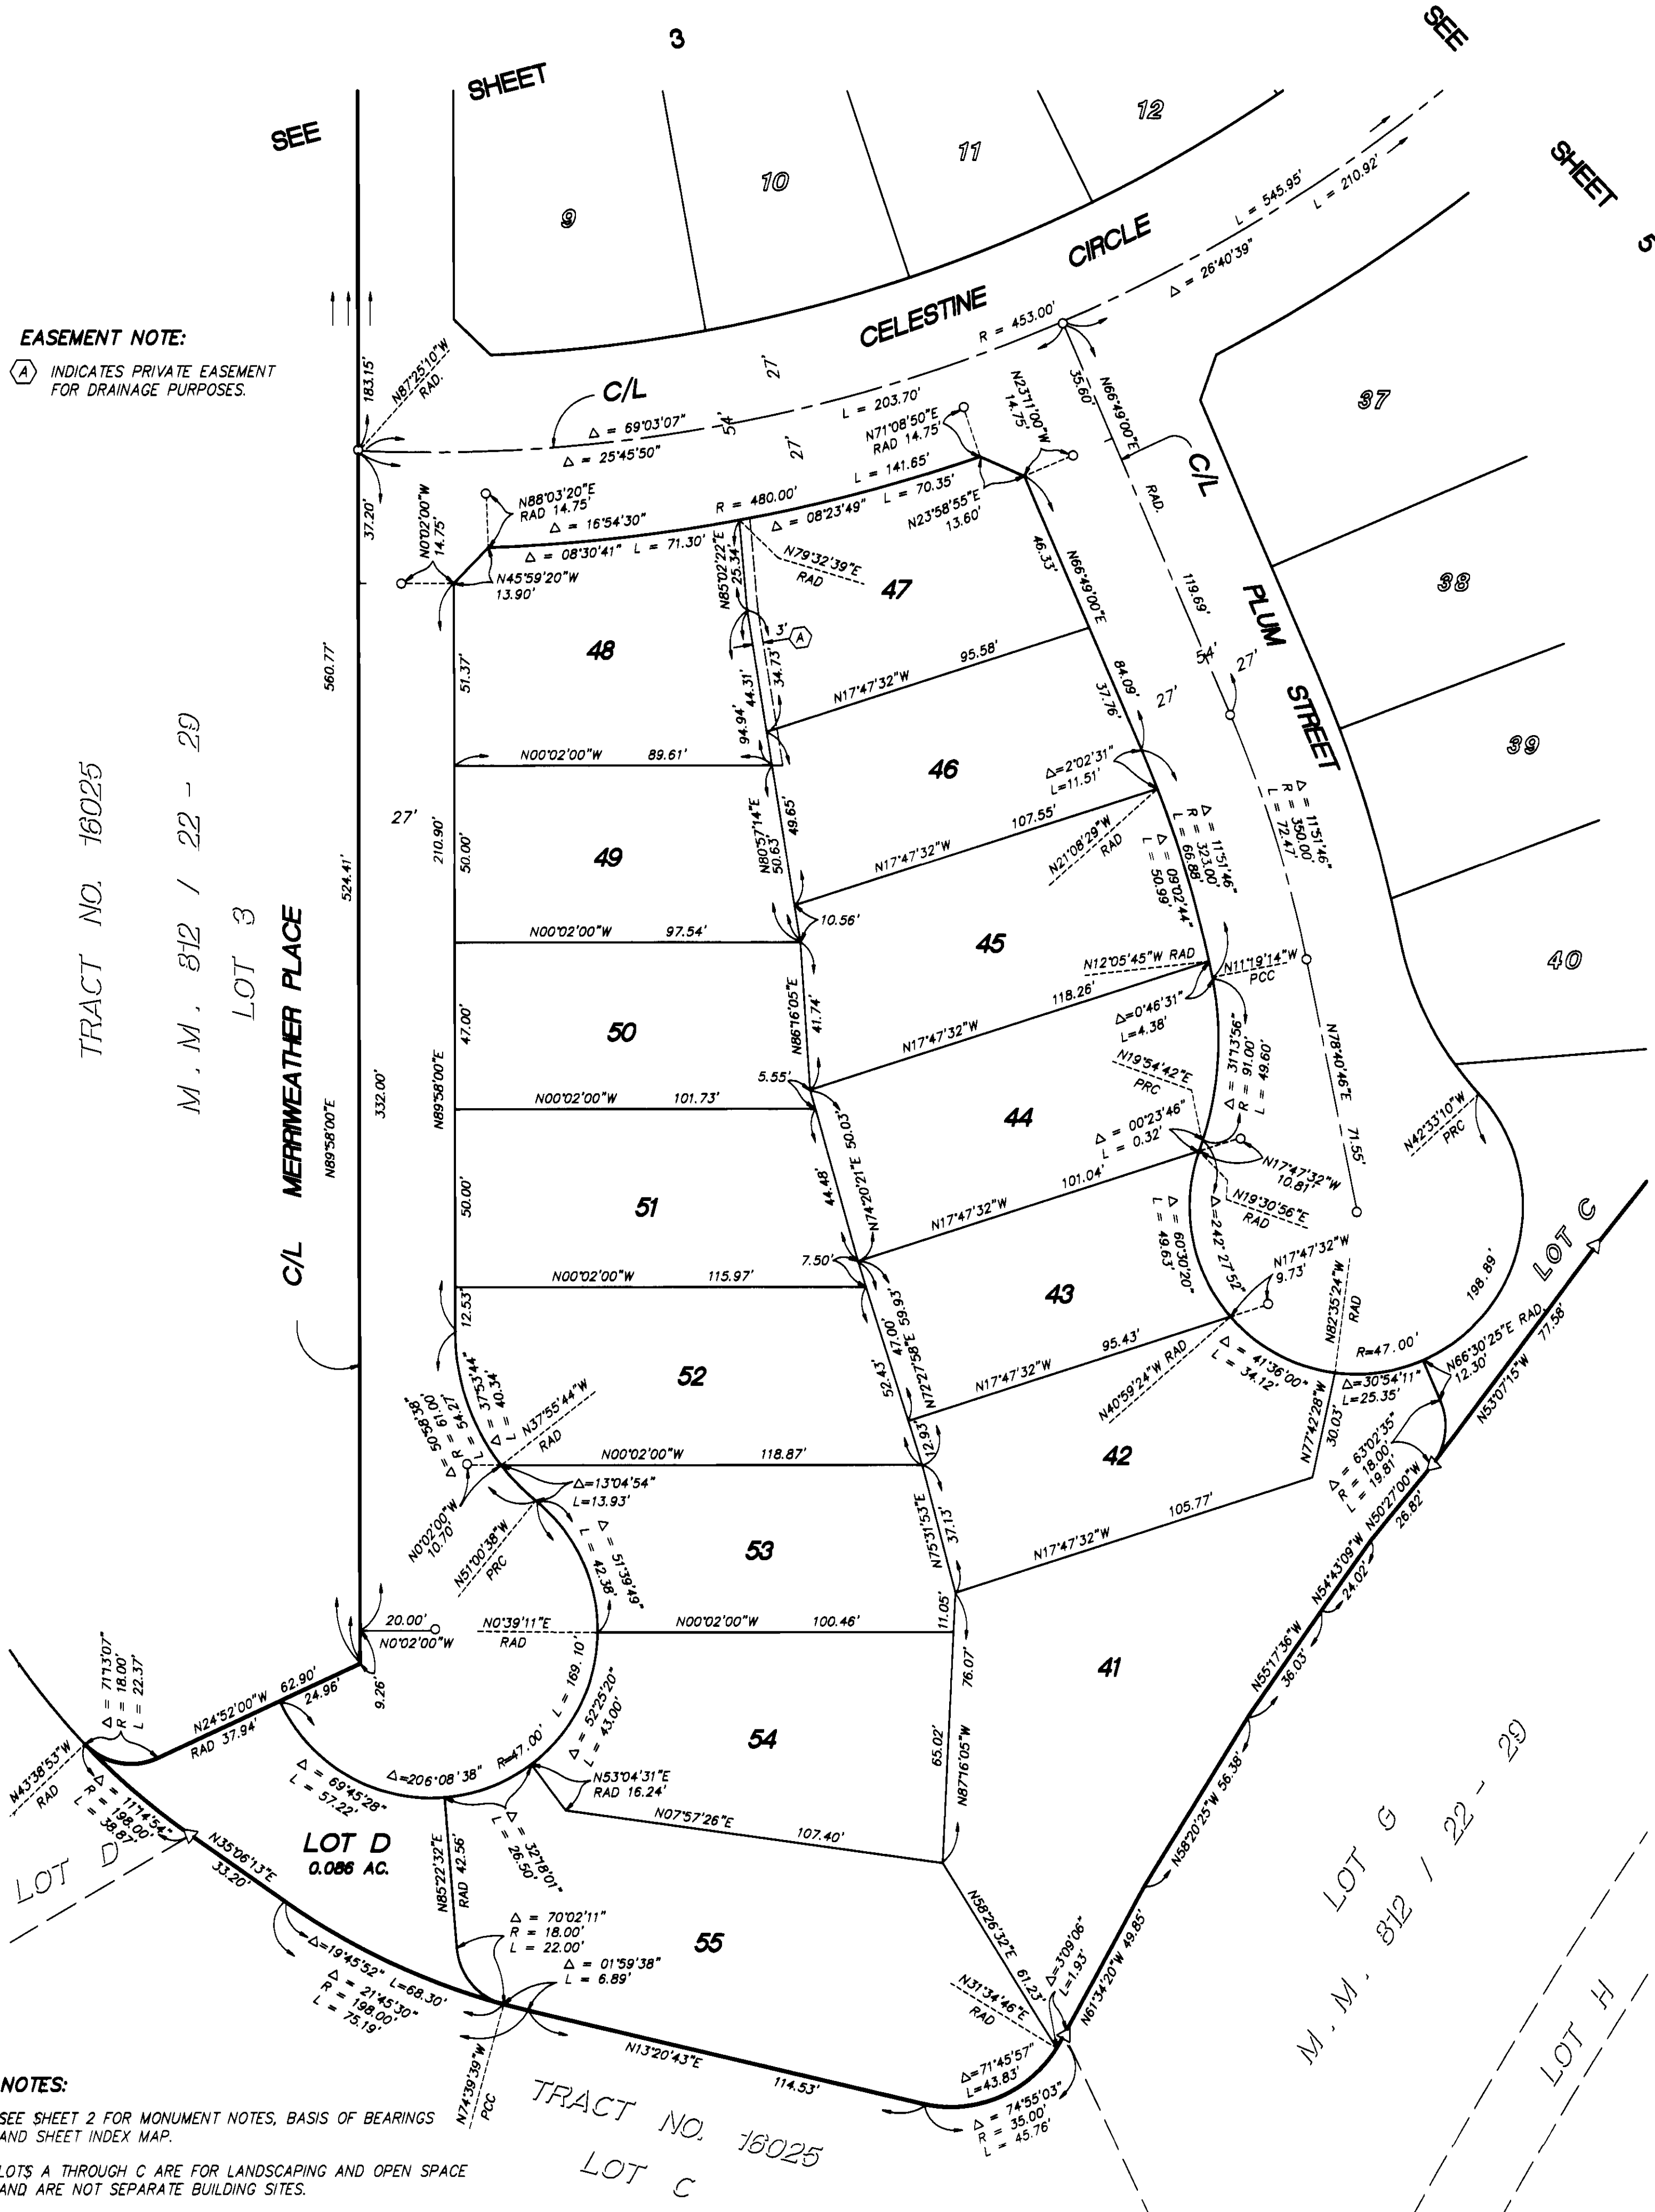

NOTES:

SEE SHEET 2 FOR MONUMENT NOTES, BASIS OF BEARINGS
AND SHEET INDEX MAP.

LOTS A THROUGH C ARE FOR LANDSCAPING AND OPEN SPACE
AND ARE NOT SEPARATE BUILDING SITES.

LOT D IS FOR A POCKET PARK.