

SHEET 1 OF 8 SHEETS
71 NUMBERED LOTS AND LOTS
A THROUGH H, INCLUSIVE
ACREAGE: 12.165 ACRES
(ALL OF TENTATIVE
TRACT NO. 16116)

TRACT NO. 16116

IN UNINCORPORATED TERRITORY OF THE COUNTY OF ORANGE,
STATE OF CALIFORNIA

BEING A SUBDIVISION OF LOT 8 AND LETTERED LOTS "L", "M", "N", "O", "P" AND
"R" OF TRACT NO. 16025, AS SHOWN ON A MAP FILED IN BOOK 812, PAGES
22 THROUGH 29, INCLUSIVE, OF MISCELLANEOUS MAPS, IN THE OFFICE OF
THE COUNTY RECORDER OF SAID COUNTY.

BLOCK: 5057
MODULES: 37

HUNSAKER AND ASSOCIATES IRVINE, INC.
RORY S. WILLIAMS, L.S. 6654 DATE OF SURVEY: AUGUST, 2001

ACCEPTED AND FILED AT THE
REQUEST OF

FIDELITY NATIONAL TITLE INSURANCE CO.

DATE: MAY 16, 2002

TIME: 08:09 AM FEE: \$ 17.00

INSTRUMENT NO. 2002 0411754

BOOK 830 PAGE 35-40 M/H
DARLENE J. BLOOM
INTERIM
COUNTY CLERK - RECORDER

BY  DEPUTY

OWNERSHIP CERTIFICATE:

WE, THE UNDERSIGNED, BEING ALL PARTIES HAVING ANY RECORD TITLE INTEREST IN THE LAND COVERED BY THIS MAP, DO HEREBY CONSENT TO THE PREPARATION AND RECORDATION OF SAID MAP, AS SHOWN WITHIN THE DISTINCTIVE BORDER LINE.

WE HEREBY DEDICATE TO THE PUBLIC FOR STREET PURPOSES: BLUEWING LANE, DUSKYWING COURT AND SACHEM WAY.

WE ALSO DO HEREBY DECLARE THAT THE LAND COVERED BY THIS MAP IS LOCATED IN A VERY HIGH FIRE HAZARD AREA DUE TO WILDLAND EXPOSURE BASED ON STATE SRA MAPS.


WE ALSO HEREBY DEDICATE TO THE SANTA MARGARITA WATER DISTRICT THE PIPELINE EASEMENT FOR SEWER, WATER AND ACCESS PURPOSES, AS SHOWN ON THIS TRACT MAP, WHICH EASEMENT SHALL BE SUBJECT TO THE SAME TERMS AND CONDITIONS AS SHOWN IN THAT CERTAIN EASEMENT RECORDED OCTOBER 6, 1980, IN BOOK 13776, PAGE 341 OF OFFICIAL RECORDS OF ORANGE COUNTY, CALIFORNIA.

WILLIAM LYON HOMES, INC., A CALIFORNIA CORPORATION, OWNER.


BY:  NAME: THOMAS J. MITCHELL
TITLE: SENIOR VICE PRESIDENT
BY:  NAME: THOMAS G. GRABLE
TITLE: ASSISTANT SECRETARY

DMB LADERA, L.L.C., A DELAWARE LIMITED LIABILITY COMPANY, OWNER AND HOLDER OF A REPURCHASE OPTION PER A MEMORANDUM OF REPURCHASE OPTION RECORDED JANUARY 4, 2002, AS INSTRUMENT NO. 2002008700 OF OFFICIAL RECORDS, AND BENEFICIARY UNDER DEED OF TRUST RECORDED JANUARY 4, 2002, AS INSTRUMENT NO. 20020008699 OF OFFICIAL RECORDS, AND HOLDER OF EASEMENTS RECORDED JANUARY 4, 2002, AS INSTRUMENT NO. 20020008697 OF OFFICIAL RECORDS.

BY: RANCHO MISSION VIEJO, L.L.C., A DELAWARE LIMITED LIABILITY COMPANY, ITS AUTHORIZED AGENT AND MANAGER.

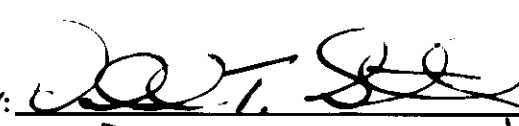BY:  NAME: DONALD T. STAHL
TITLE: DIRECTOR OF COMMUNITY DEV.
BY:  NAME: STEPHEN C. SCHRANK
TITLE: EXECUTIVE VICE PRESIDENT

GUARANTY BANK, A FEDERAL SAVINGS BANK, BENEFICIARY UNDER DEED OF TRUST RECORDED JANUARY 4, 2002, AS INSTRUMENT NO. 20020008698 OF OFFICIAL RECORDS.

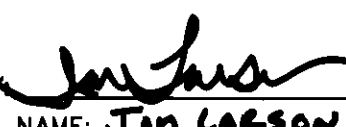BY:  NAME: JON LARSON
TITLE: SENIOR VICE PRESIDENT
BY:  NAME: SCOTT L. COX
TITLE: ASSISTANT SECRETARY

NOTARY ACKNOWLEDGMENTS:

STATE OF CALIFORNIA } SS
COUNTY OF ORANGE }

ON FEBRUARY 13, 2002 BEFORE ME, SUSAN E. MENARD, PERSONALLY APPEARED THOMAS J. MITCHELL AND THOMAS G. GRABLE, PERSONALLY KNOWN TO ME (OR PROVED TO ME ON THE BASIS OF SATISFACTORY EVIDENCE) TO BE THE PERSON(S) WHOSE NAME(S) IS/ARE SUBSCRIBED TO THE WITHIN INSTRUMENT AND ACKNOWLEDGED TO ME THAT HE/SHE/ THEY EXECUTED THE SAME IN HIS/HER/ THEIR AUTHORIZED CAPACITY(IES), AND THAT BY HIS/HER/ THEIR SIGNATURE(S) ON THE INSTRUMENT THE PERSON(S), OR ENTITY UPON BEHALF OF WHICH THE PERSON(S) ACTED, EXECUTED THE INSTRUMENT.

WITNESS MY HAND:

SIGNATURE  NOTARY PUBLIC IN AND FOR SAID STATE

MY PRINCIPAL PLACE OF BUSINESS IS IN ORANGE COUNTY.

SUSAN E. MENARD
(NAME PRINTED)

MY COMMISSION EXPIRES: SEPT. 5, 2003

STATE OF CALIFORNIA } SS
COUNTY OF ORANGE }

ON February 16, 2002, BEFORE ME, Tina T. Baker, Notary Public, PERSONALLY APPEARED Donald T. Stahl AND Stephen C. Schrank, PERSONALLY KNOWN TO ME (OR PROVED TO ME ON THE BASIS OF SATISFACTORY EVIDENCE) TO BE THE PERSON(S) WHOSE NAME(S) IS/ARE SUBSCRIBED TO THE WITHIN INSTRUMENT AND ACKNOWLEDGED TO ME THAT HE/SHE/ THEY EXECUTED THE SAME IN HIS/HER/ THEIR AUTHORIZED CAPACITY(IES), AND THAT BY HIS/HER/ THEIR SIGNATURE(S) ON THE INSTRUMENT THE PERSON(S), OR ENTITY UPON BEHALF OF WHICH THE PERSON(S) ACTED, EXECUTED THE INSTRUMENT.

WITNESS MY HAND:

SIGNATURE  NOTARY PUBLIC IN AND FOR SAID STATE

MY PRINCIPAL PLACE OF BUSINESS IS IN Orange COUNTY.


Tina T. Baker
(NAME PRINTED)

MY COMMISSION EXPIRES: 8-29-04

STATE OF CALIFORNIA } SS
COUNTY OF ORANGE }

ON 2-14-02, BEFORE ME, SUSAN T. STERLING, PERSONALLY APPEARED JON M. LARSON AND SCOTT L. COX, PERSONALLY KNOWN TO ME (OR PROVED TO ME ON THE BASIS OF SATISFACTORY EVIDENCE) TO BE THE PERSON(S) WHOSE NAME(S) IS/ARE SUBSCRIBED TO THE WITHIN INSTRUMENT AND ACKNOWLEDGED TO ME THAT HE/SHE/ THEY EXECUTED THE SAME IN HIS/HER/ THEIR AUTHORIZED CAPACITY(IES), AND THAT BY HIS/HER/ THEIR SIGNATURE(S) ON THE INSTRUMENT THE PERSON(S), OR ENTITY UPON BEHALF OF WHICH THE PERSON(S) ACTED, EXECUTED THE INSTRUMENT.

WITNESS MY HAND:

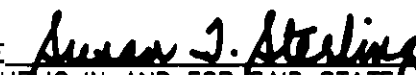SIGNATURE  NOTARY PUBLIC IN AND FOR SAID STATE

MY PRINCIPAL PLACE OF BUSINESS IS IN SAN DIEGO COUNTY.

SUSAN T. STERLING
(NAME PRINTED)

MY COMMISSION EXPIRES: 8-21-04
Commission # 1271852

SURVEYOR'S STATEMENT:

THIS MAP WAS PREPARED BY ME OR UNDER MY DIRECTION AND IS BASED UPON A FIELD SURVEY IN CONFORMANCE WITH THE REQUIREMENTS OF THE SUBDIVISION MAP ACT AND LOCAL ORDINANCE AT THE REQUEST OF WILLIAM LYON HOMES, INC., IN AUGUST, 2001. I HEREBY STATE THAT ALL MONUMENTS ARE OF THE CHARACTER AND OCCUPY THE POSITIONS INDICATED, OR THAT THEY WILL BE SET IN SUCH POSITIONS; AND THAT SAID MONUMENTS ARE SUFFICIENT TO ENABLE THE SURVEY TO BE RETRACED. I HEREBY STATE THAT THIS FINAL MAP SUBSTANTIALLY CONFORMS TO THE CONDITIONALLY APPROVED TENTATIVE MAP.

 2/27/02
RORY S. WILLIAMS, L.S. 6654 DATE
LICENSE EXPIRES: 12/31/03



COUNTY SURVEYOR'S STATEMENT

I HEREBY STATE THAT I HAVE EXAMINED THIS MAP AND HAVE FOUND IT TO BE SUBSTANTIALLY IN CONFORMANCE WITH THE TENTATIVE MAP AS FILED WITH, AMENDED AND APPROVED BY THE ORANGE COUNTY SUBDIVISION COMMITTEE; THAT ALL PROVISIONS OF THE SUBDIVISION MAP ACT AND COUNTY SUBDIVISION REGULATIONS HAVE BEEN COMPLIED WITH AND I AM SATISFIED SAID MAP IS TECHNICALLY CORRECT.

DATED THIS 19TH DAY OF APRIL, 2002.

 JOHN CANAS, COUNTY SURVEYOR
LS 4408, EXPIRATION DATE: 9-30-05
BY: MICHAEL K. SULLIVAN, DEPUTY
LS 6254 EXPIRES 6-30-02



COUNTY TREASURER-TAX COLLECTOR'S CERTIFICATE:

STATE OF CALIFORNIA } SS
COUNTY OF ORANGE }

I HEREBY CERTIFY THAT ACCORDING TO THE RECORDS OF MY OFFICE THERE ARE NO LIENS AGAINST THE LAND COVERED BY THIS MAP OR ANY PART THEREOF FOR UNPAID STATE, COUNTY, MUNICIPAL OR LOCAL TAXES OR SPECIAL ASSESSMENTS COLLECTED AS TAXES, EXCEPT TAXES OR SPECIAL ASSESSMENTS COLLECTED AS TAXES NOT YET PAYABLE.

AND DO CERTIFY TO THE RECORDER OF ORANGE COUNTY THAT THE PROVISIONS OF THE SUBDIVISION MAP ACT HAVE BEEN COMPLIED WITH REGARDING DEPOSITS TO SECURE PAYMENT OF TAXES OR SPECIAL ASSESSMENTS COLLECTED AS TAXES ON THE LAND COVERED BY THIS MAP.

DATED THIS 4th DAY OF April, 2002.

JOHN M.W. MOORLACH COUNTY TREASURER-TAX COLLECTOR
BY:  DEPUTY TREASURER-TAX COLLECTOR


CLERK OF THE BOARD OF SUPERVISORS' CERTIFICATE:

STATE OF CALIFORNIA } SS
COUNTY OF ORANGE }

I HEREBY CERTIFY THAT THIS MAP WAS PRESENTED FOR APPROVAL TO THE BOARD OF SUPERVISORS OF THE COUNTY OF ORANGE AT REGULAR MEETING THEREOF HELD ON THE 7th DAY OF May, 2002, AND THAT THEREUPON SAID BOARD DID, BY AN ORDER DULY PASSED AND ENTERED, APPROVE SAID MAP AND DID ACCEPT ON BEHALF OF THE PUBLIC, SUBJECT TO IMPROVEMENTS, THE DEDICATION FOR STREET PURPOSES OF: BLUEWING LANE, DUSKYWING COURT AND SACHEM WAY.

AND DID ALSO APPROVE SAID MAP PURSUANT TO THE PROVISIONS OF SECTION 66436 (c)(3)(A) OF THE SUBDIVISION MAP ACT.

DATED THIS 7th DAY OF May, 2002.

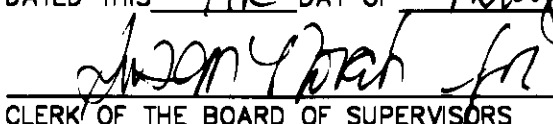 CLERK OF THE BOARD OF SUPERVISORS
DARLENE J. BLOOM



CERTIFICATE OF ACCEPTANCE - SANTA MARGARITA WATER DISTRICT

THE UNDERSIGNED, BEING THE DULY APPOINTED AGENT OF THE SANTA MARGARITA WATER DISTRICT, A PUBLIC CORPORATION IN ORANGE COUNTY, CALIFORNIA, PURSUANT TO ITS RESOLUTION NO. 88-10-2, DOES HEREBY ACCEPT ON BEHALF OF SAID DISTRICT, THE PIPELINE EASEMENT FOR WATER AND SEWER PURPOSES AS DEDICATED AND SHOWN ON THIS TRACT MAP, BY AND BETWEEN THE SANTA MARGARITA WATER DISTRICT AND WILLIAM LYON HOMES, INC., A CALIFORNIA CORPORATION, AND DOES HEREBY CERTIFY THAT THE GRANTEE CONSENTS TO THE RECORDATION OF SAID TRACT MAP.


 DANIEL R. FERONS, CHIEF ENGINEER
SANTA MARGARITA WATER DISTRICT

NOTARY ACKNOWLEDGMENT - SANTA MARGARITA WATER DISTRICT

STATE OF CALIFORNIA } SS
COUNTY OF ORANGE }

ON 3-11-02, BEFORE ME, ANDREA M. EVANS, NOTARY PUBLIC, PERSONALLY APPEARED DANIEL R. FERONS, PERSONALLY KNOWN TO ME (OR PROVED TO ME ON THE BASIS OF SATISFACTORY EVIDENCE) TO BE THE PERSON WHOSE NAME IS SUBSCRIBED TO THE WITHIN INSTRUMENT AND ACKNOWLEDGED TO ME THAT HE EXECUTED THE SAME IN HIS AUTHORIZED CAPACITY, AND THAT BY HIS SIGNATURE ON THE INSTRUMENT THE PERSON, OR ENTITY UPON BEHALF OF WHICH THE PERSON ACTED, EXECUTED THE INSTRUMENT.

WITNESS MY HAND:

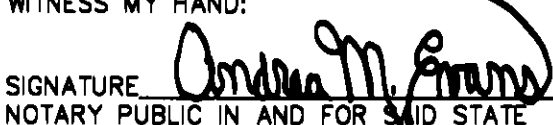SIGNATURE  NOTARY PUBLIC IN AND FOR SAID STATE
ANDREA M. EVANS
(NAME PRINTED)

MY PRINCIPAL PLACE OF BUSINESS IS IN ORANGE COUNTY.

MY COMMISSION EXPIRES: 4-08-04

SIGNATURE OMISSIONS:

PURSUANT TO THE PROVISIONS OF SECTION 66436 (c)(3) OF THE SUBDIVISION MAP ACT, THE FOLLOWING SIGNATURES HAVE BEEN OMITTED:

LADERA DEVELOPMENT COMPANY, L.L.C., HOLDER OF OIL, GAS AND MINERAL RIGHTS RECORDED AS INSTRUMENT NO. 19960624029 OF OFFICIAL RECORDS.

SANTA MARGARITA WATER DISTRICT HOLDER OF EASEMENT FOR WATER, SEWER AND ACCESS AS PER TRACT NO. 16025, AS SHOWN ON A MAP FILED IN BOOK 812, PAGES 22 THROUGH 29, INCLUSIVE, OF MISCELLANEOUS MAPS, RECORDS OF ORANGE COUNTY, CALIFORNIA.

DMB LADERA, L.L.C., HOLDERS OF EASEMENTS RECORDED JANUARY 4, 2002, AS INSTRUMENT NO. 20020008697 OF OFFICIAL RECORDS. (BLANKET IN NATURE).

SHEET 2 OF 6 SHEETS
SCALE: 1" = 100'
71 NUMBERED LOTS AND LOTS
A THROUGH H, INCLUSIVE
ACREAGE: 12.165 ACRES
(ALL OF TENTATIVE
TRACT NO. 16116)

TRACT NO. 16116

IN UNINCORPORATED TERRITORY OF THE COUNTY OF ORANGE,
STATE OF CALIFORNIA

HUNSAKER AND ASSOCIATES IRVINE, INC.
RORY S. WILLIAMS, L.S. 6654 DATE OF SURVEY: AUGUST, 2001

MONUMENT NOTES:

2" I.P. TAGGED L.S. 6654 OR LEAD, TACK & TAG L.S. 6654 OR NAIL & TAG L.S. 6654 OR
8" S&W STAMPED L.S. 6654 TO BE SET AT ALL TRACT BOUNDARY CORNERS WITHIN 90
DAYS AFTER ACCEPTANCE OF IMPROVEMENTS, UNLESS OTHERWISE NOTED.

1" I.P. TAGGED L.S. 6654 OR LEAD, TACK & TAG L.S. 6654 OR NAIL & TAG L.S. 6654 OR
8" S&W STAMPED L.S. 6654 TO BE SET AT ALL LOT CORNERS, EXCEPT LOT CORNERS
THAT ARE THE INTERSECTION OF SIDE LOT LINES WITH STREET RIGHT OF WAY, WITHIN 90
DAYS AFTER ACCEPTANCE OF IMPROVEMENTS, UNLESS OTHERWISE NOTED.

LEAD, TACK & TAG L.S. 6654 TO BE SET IN TOP OF CURB ON ALL SIDE LOT LINES
PRODUCED OR CONTINUED, 8.75' FROM INTERSECTION WITH STREET RIGHT OF WAY FOR ALL
SIDE LOT LINES RADIAL OR PERPENDICULAR TO STREET RIGHT OF WAY, WITHIN 90 DAYS
AFTER ACCEPTANCE OF IMPROVEMENTS, UNLESS OTHERWISE NOTED. FOR ALL SIDE LOT
LINES NON-RADIAL OR NON-PERPENDICULAR TO STREET RIGHT OF WAY, OR NOT AT AN
8.75' OFFSET, BEARING AND DISTANCE OF PRODUCTION IS AS NOTED HEREON.

8" S&W STAMPED L.S. 6654 OR LEAD, TACK & TAG L.S. 6654 OR 1" I.P. TAGGED L.S.
6654 TO BE SET AT ALL STREET CENTERLINE POINTS OF CONTROL, WITHIN 90 DAYS AFTER
ACCEPTANCE OF IMPROVEMENTS, UNLESS OTHERWISE NOTED.

● INDICATES FOUND MONUMENT OR LOCATION OF MONUMENT SET OR TO BE SET, AS
NOTED.

■ INDICATES NOTHING TO BE SET.

P# INDICATES BEARING AND DISTANCE OF LOT LINE PRODUCTION FROM LOT CORNER

NOTHING IS TO BE SET BY TRACT NO. 16025, M.M. 812/22-29, AT THE TRACT CORNERS
OF SUBJECT TRACT.

M1 INDICATES LOCATION OF 1" I.P. TAGGED P.L.S. 5557 OR S&W STAMPED P.L.S. 5557 OR
LEAD, TACK & TAG P.L.S. 5557 TO BE SET PER TRACT NO. 16025, M.M. 812/22-29,
UNLESS OTHERWISE NOTED.

M2 INDICATES LOCATION OF 1" I.P. TAGGED P.L.S. 5557 OR S&W STAMPED P.L.S. 5557 OR
LEAD, TACK & TAG P.L.S. 5557 TO BE SET PER TRACT NO. 16025, M.M. 812/22-29,
UNLESS OTHERWISE NOTED.

M3 INDICATES LOCATION OF 2" I.P. TAGGED P.L.S. 5557 OR S&W STAMPED P.L.S. 5557 OR
LEAD, TACK & TAG P.L.S. 5557 TO BE SET PER TRACT NO. 16025, M.M. 812/22-29,
UNLESS OTHERWISE NOTED.

M4 INDICATES LOCATION OF 2" I.P. TAGGED L.S. 5557 OR S&W STAMPED L.S. 5557 OR
LEAD, TACK & TAG L.S. 5557 TO BE SET PER TRACT NO. 16156, M.M. 812/40-48,
UNLESS OTHERWISE NOTED.

BASIS OF BEARINGS:

THE BEARINGS SHOWN HEREON ARE BASED ON THE BEARING BETWEEN
O.C.S. HORIZONTAL CONTROL STATION GPS NO. 1417 AND STATION GPS
NO. 1424 BEING N01°36'34"E PER RECORDS ON FILE IN THE OFFICE OF
THE ORANGE COUNTY SURVEYOR.

DATUM STATEMENT:

COORDINATES SHOWN ARE BASED ON THE CALIFORNIA COORDINATE
SYSTEM (CCS83), ZONE VI, 1983 NAD, (1991.35 EPOCH OCS GPS
ADJUSTMENT).

ALL DISTANCES SHOWN ARE GROUND, UNLESS OTHERWISE NOTED. TO
OBTAIN GRID DISTANCE MULTIPLY GROUND DISTANCE BY 0.99994800.

NOTES:

LOTS A THROUGH G, INCLUSIVE, ARE FOR SLOPE/OPEN SPACE PURPOSES.

LOT H ARE FOR RECREATION/POCKET PARK PURPOSES.

THE PROPERTY IS IN A SPECIAL FIRE PROTECTION AREA. TOTAL EXCLUSION
GRANTED FOR THIS TRACT.

ALL RESIDENTIAL STRUCTURES EXCEEDING 5,500 SQUARE FEET (PER AMENDMENT)
AND ALL STRUCTURES EXCEEDING FIRE DEPARTMENT ACCESS REQUIREMENTS SHALL
BE PROTECTED BY AN AUTOMATIC FIRE SPRINKLER SYSTEM IN A MANNER MEETING
THE APPROVAL OF THE FIRE CHIEF.

EASEMENT NOTES:

(A) INDICATES A 20' WIDE EASEMENT FOR SEWER LINE, WATER LINE AND ACCESS
PURPOSES DEDICATED HEREON TO THE SANTA MARGARITA WATER DISTRICT.

(B) INDICATES A 5' WIDE EASEMENT FOR PRIVATE STORM DRAIN PURPOSES RESERVED
HEREON FOR FUTURE GRANT TO THE HOMEOWNERS' ASSOCIATION BY SEPARATE
INSTRUMENT.


(C) INDICATES A 20' WIDE EASEMENT FOR SEWER, WATER AND ACCESS PURPOSES
DEDICATED BY TRACT NO. 16025, M.M. 812/22-29, TO THE SANTA MARGARITA
WATER DISTRICT.

GPS NO. 1424

FD. 2 1/2" IRON PIPE WITH 2" OCS
BRASS CAP STAMPED "GPS 1424 9-95"
PER R.S.B. 154/8-18
AND RECORDS ON FILE IN THE
ORANGE COUNTY SURVEYOR'S OFFICE.

N 2152873.842
E 6141904.527

3 INDICATES SHEET NUMBER

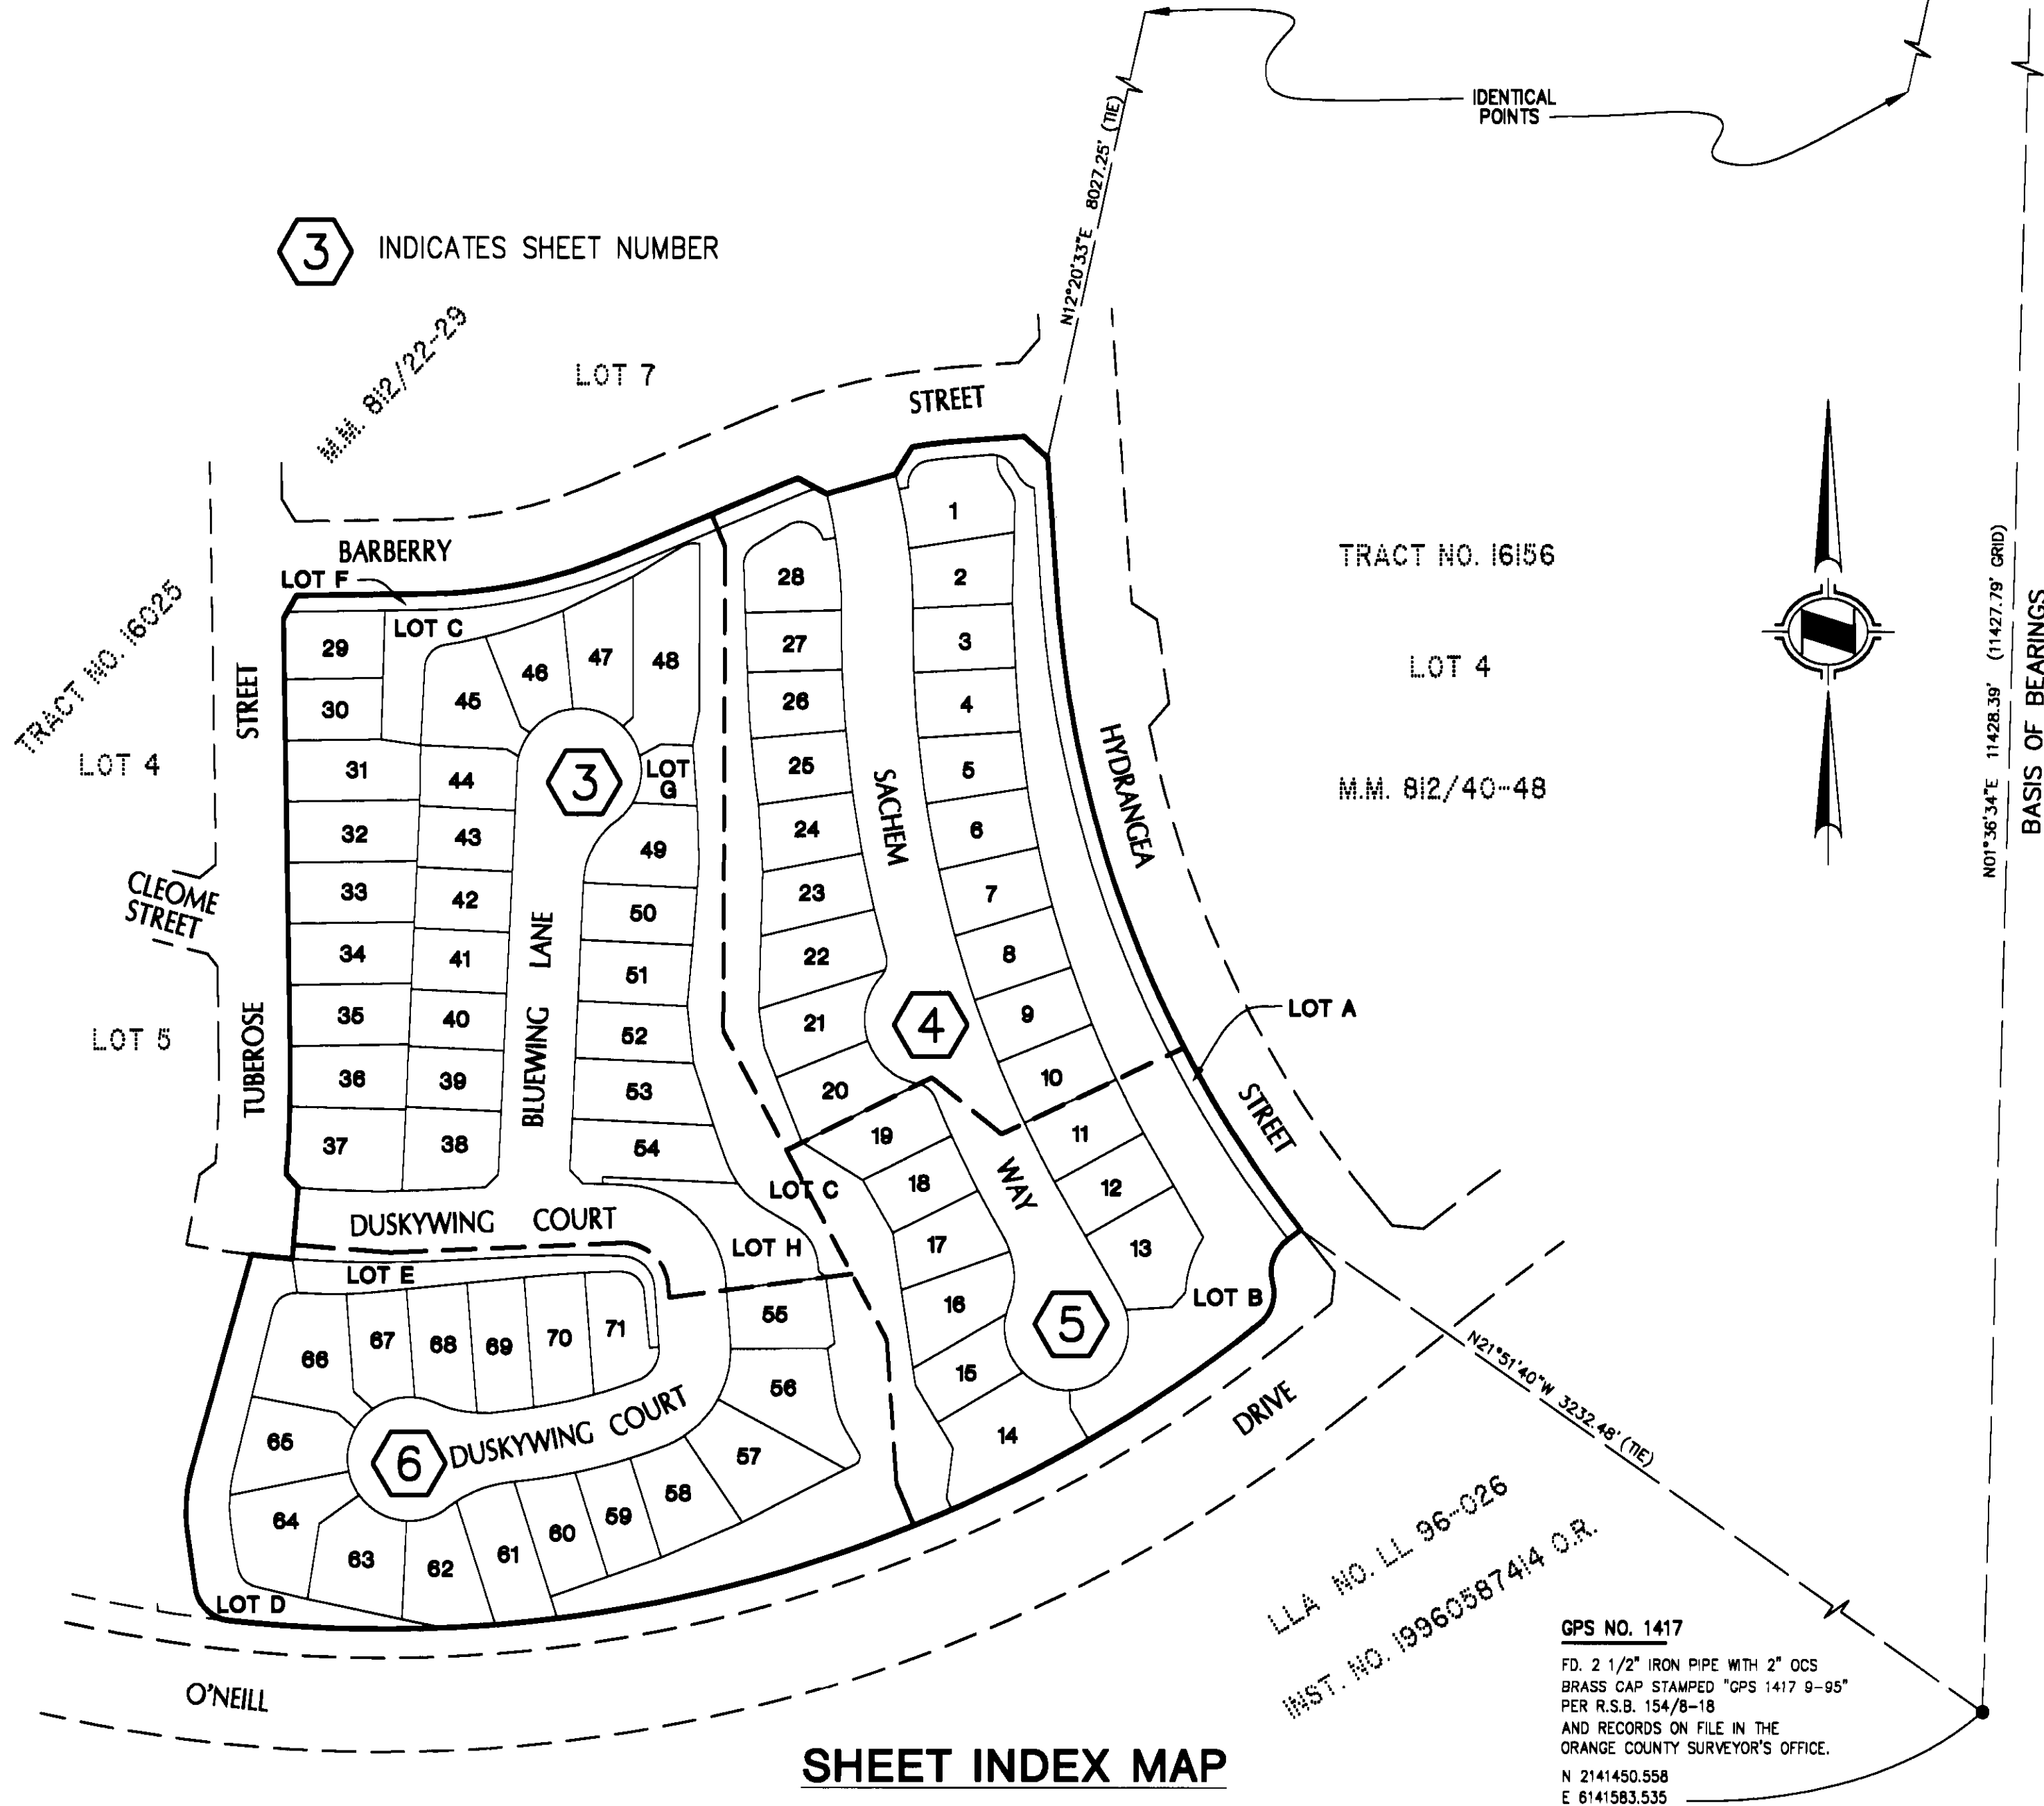

SHEET INDEX MAP

GPS NO. 1417

FD. 2 1/2" IRON PIPE WITH 2" OCS
BRASS CAP STAMPED "GPS 1417 9-95"
PER R.S.B. 154/8-18
AND RECORDS ON FILE IN THE
ORANGE COUNTY SURVEYOR'S OFFICE.
N 2141450.558
E 6141583.535

SHEET 3 OF 6 SHEETS
SCALE: 1" = 30'
71 NUMBERED LOTS AND LOTS
A THROUGH H, INCLUSIVE
ACREAGE: 12.165 ACRES
(ALL OF TENTATIVE
TRACT NO. 16116)

TRACT NO. 16116


IN UNINCORPORATED TERRITORY OF THE COUNTY OF ORANGE,
STATE OF CALIFORNIA

HUNSAKER AND ASSOCIATES IRVINE, INC.
RORY S. WILLIAMS, L.S. 6654 DATE OF SURVEY: AUGUST, 2001

TRACT NO. 16025
M.M. 812/22-29

MONUMENT OFFSET TABLE		
LINE	BEARING	LENGTH
P23	S66°45'38"E	9.28'
P24	S59°14'38"E	8.84'
P25	S62°02'09"W	9.08'
P26	N67°19'15"W	10.26'
P36	S89°09'00"W	14.75'
P37	S89°09'00"W	14.75'
P38	S89°09'00"W	14.75'
P41	S82°36'20"W	8.76'

SEE SHEET 2 FOR BASIS OF BEARINGS,
MONUMENT NOTES, EASEMENT NOTES,
GPS TIES, SHEET INDEX MAP, DATUM
STATEMENT AND NOTES.

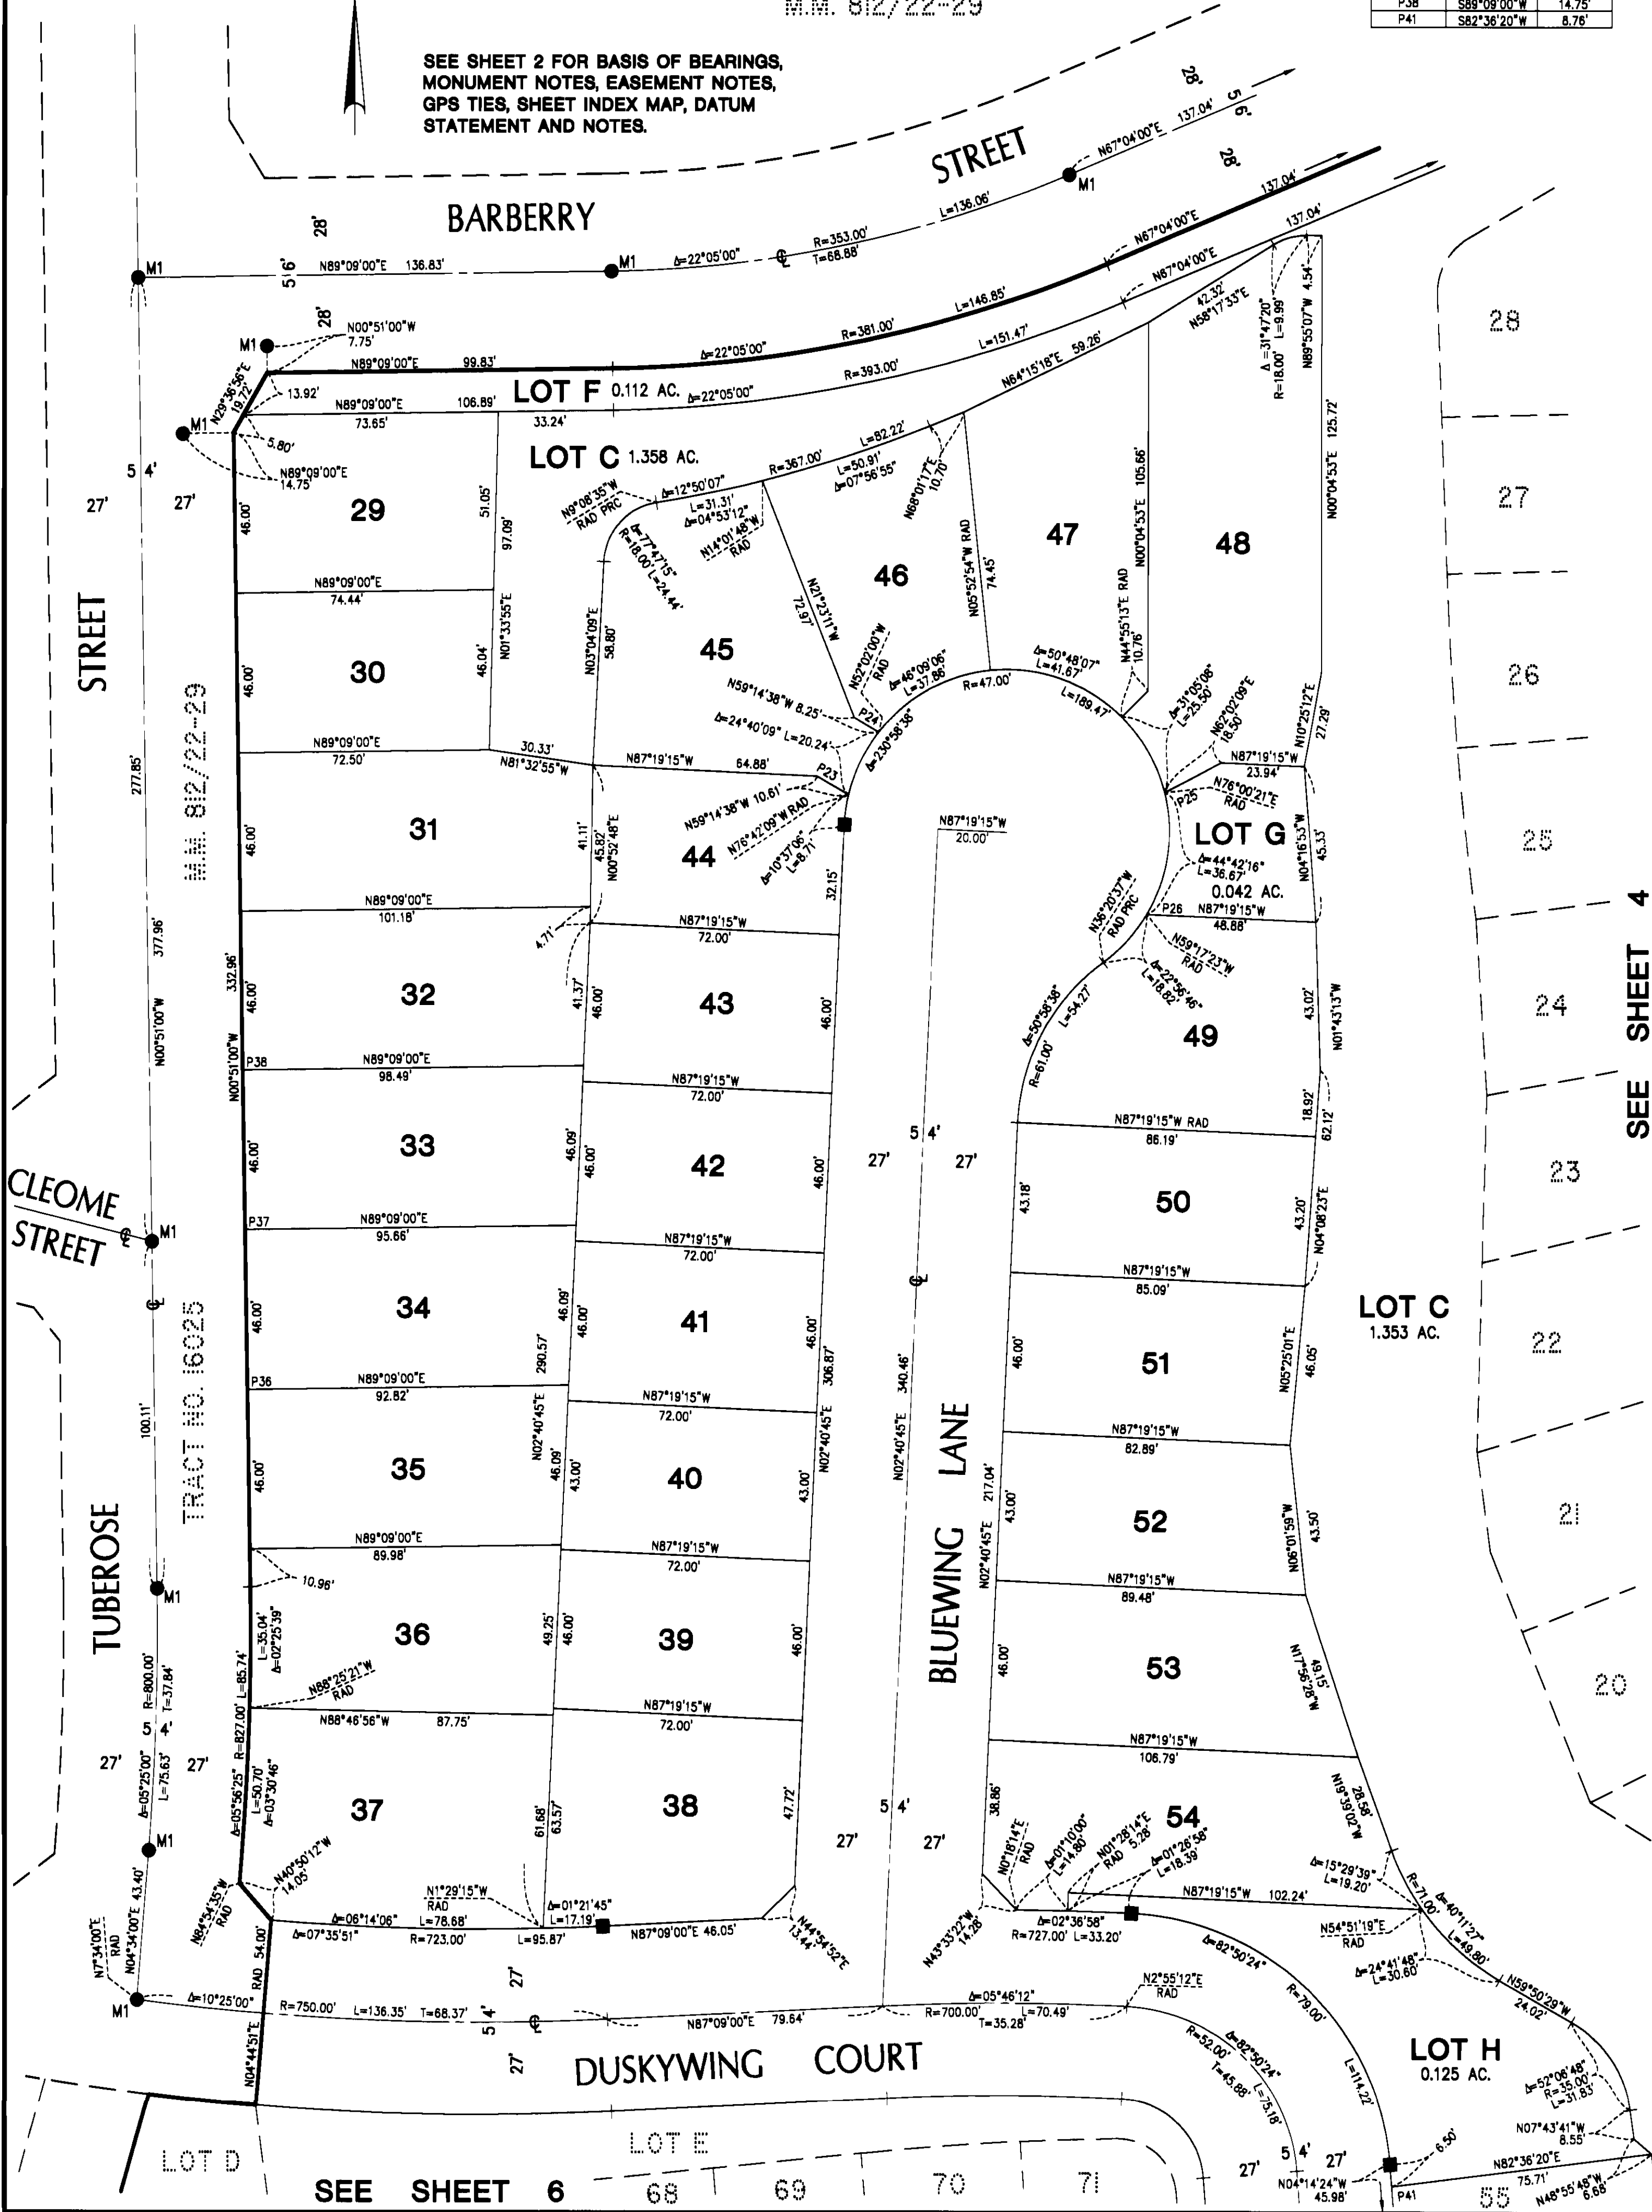

SHEET 4 OF 6 SHEETS
SCALE: 1" = 30'
71 NUMBERED LOTS AND LOTS
A THROUGH H, INCLUSIVE
ACREAGE: 12.165 ACRES
(ALL OF TENTATIVE
TRACT NO. 16116)




TRACT NO. 16116

IN UNINCORPORATED TERRITORY OF THE COUNTY OF ORANGE,
STATE OF CALIFORNIA

HUNSAKER AND ASSOCIATES IRVINE, INC.
RORY S. WILLIAMS, L.S. 6654
DATE OF SURVEY: AUGUST, 2001

SEE SHEET 2 FOR BASIS OF BEARINGS,
MONUMENT NOTES, EASEMENT NOTES,
GPS TIES, SHEET INDEX MAP, DATUM
STATEMENT AND NOTES.

TRACT NO. 16025
M.M. 812/22-29

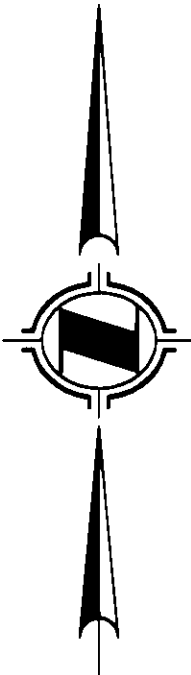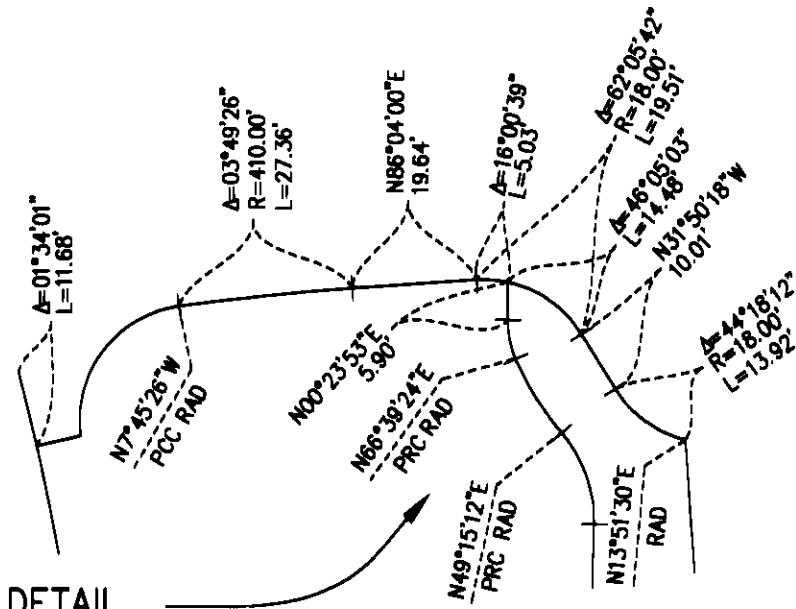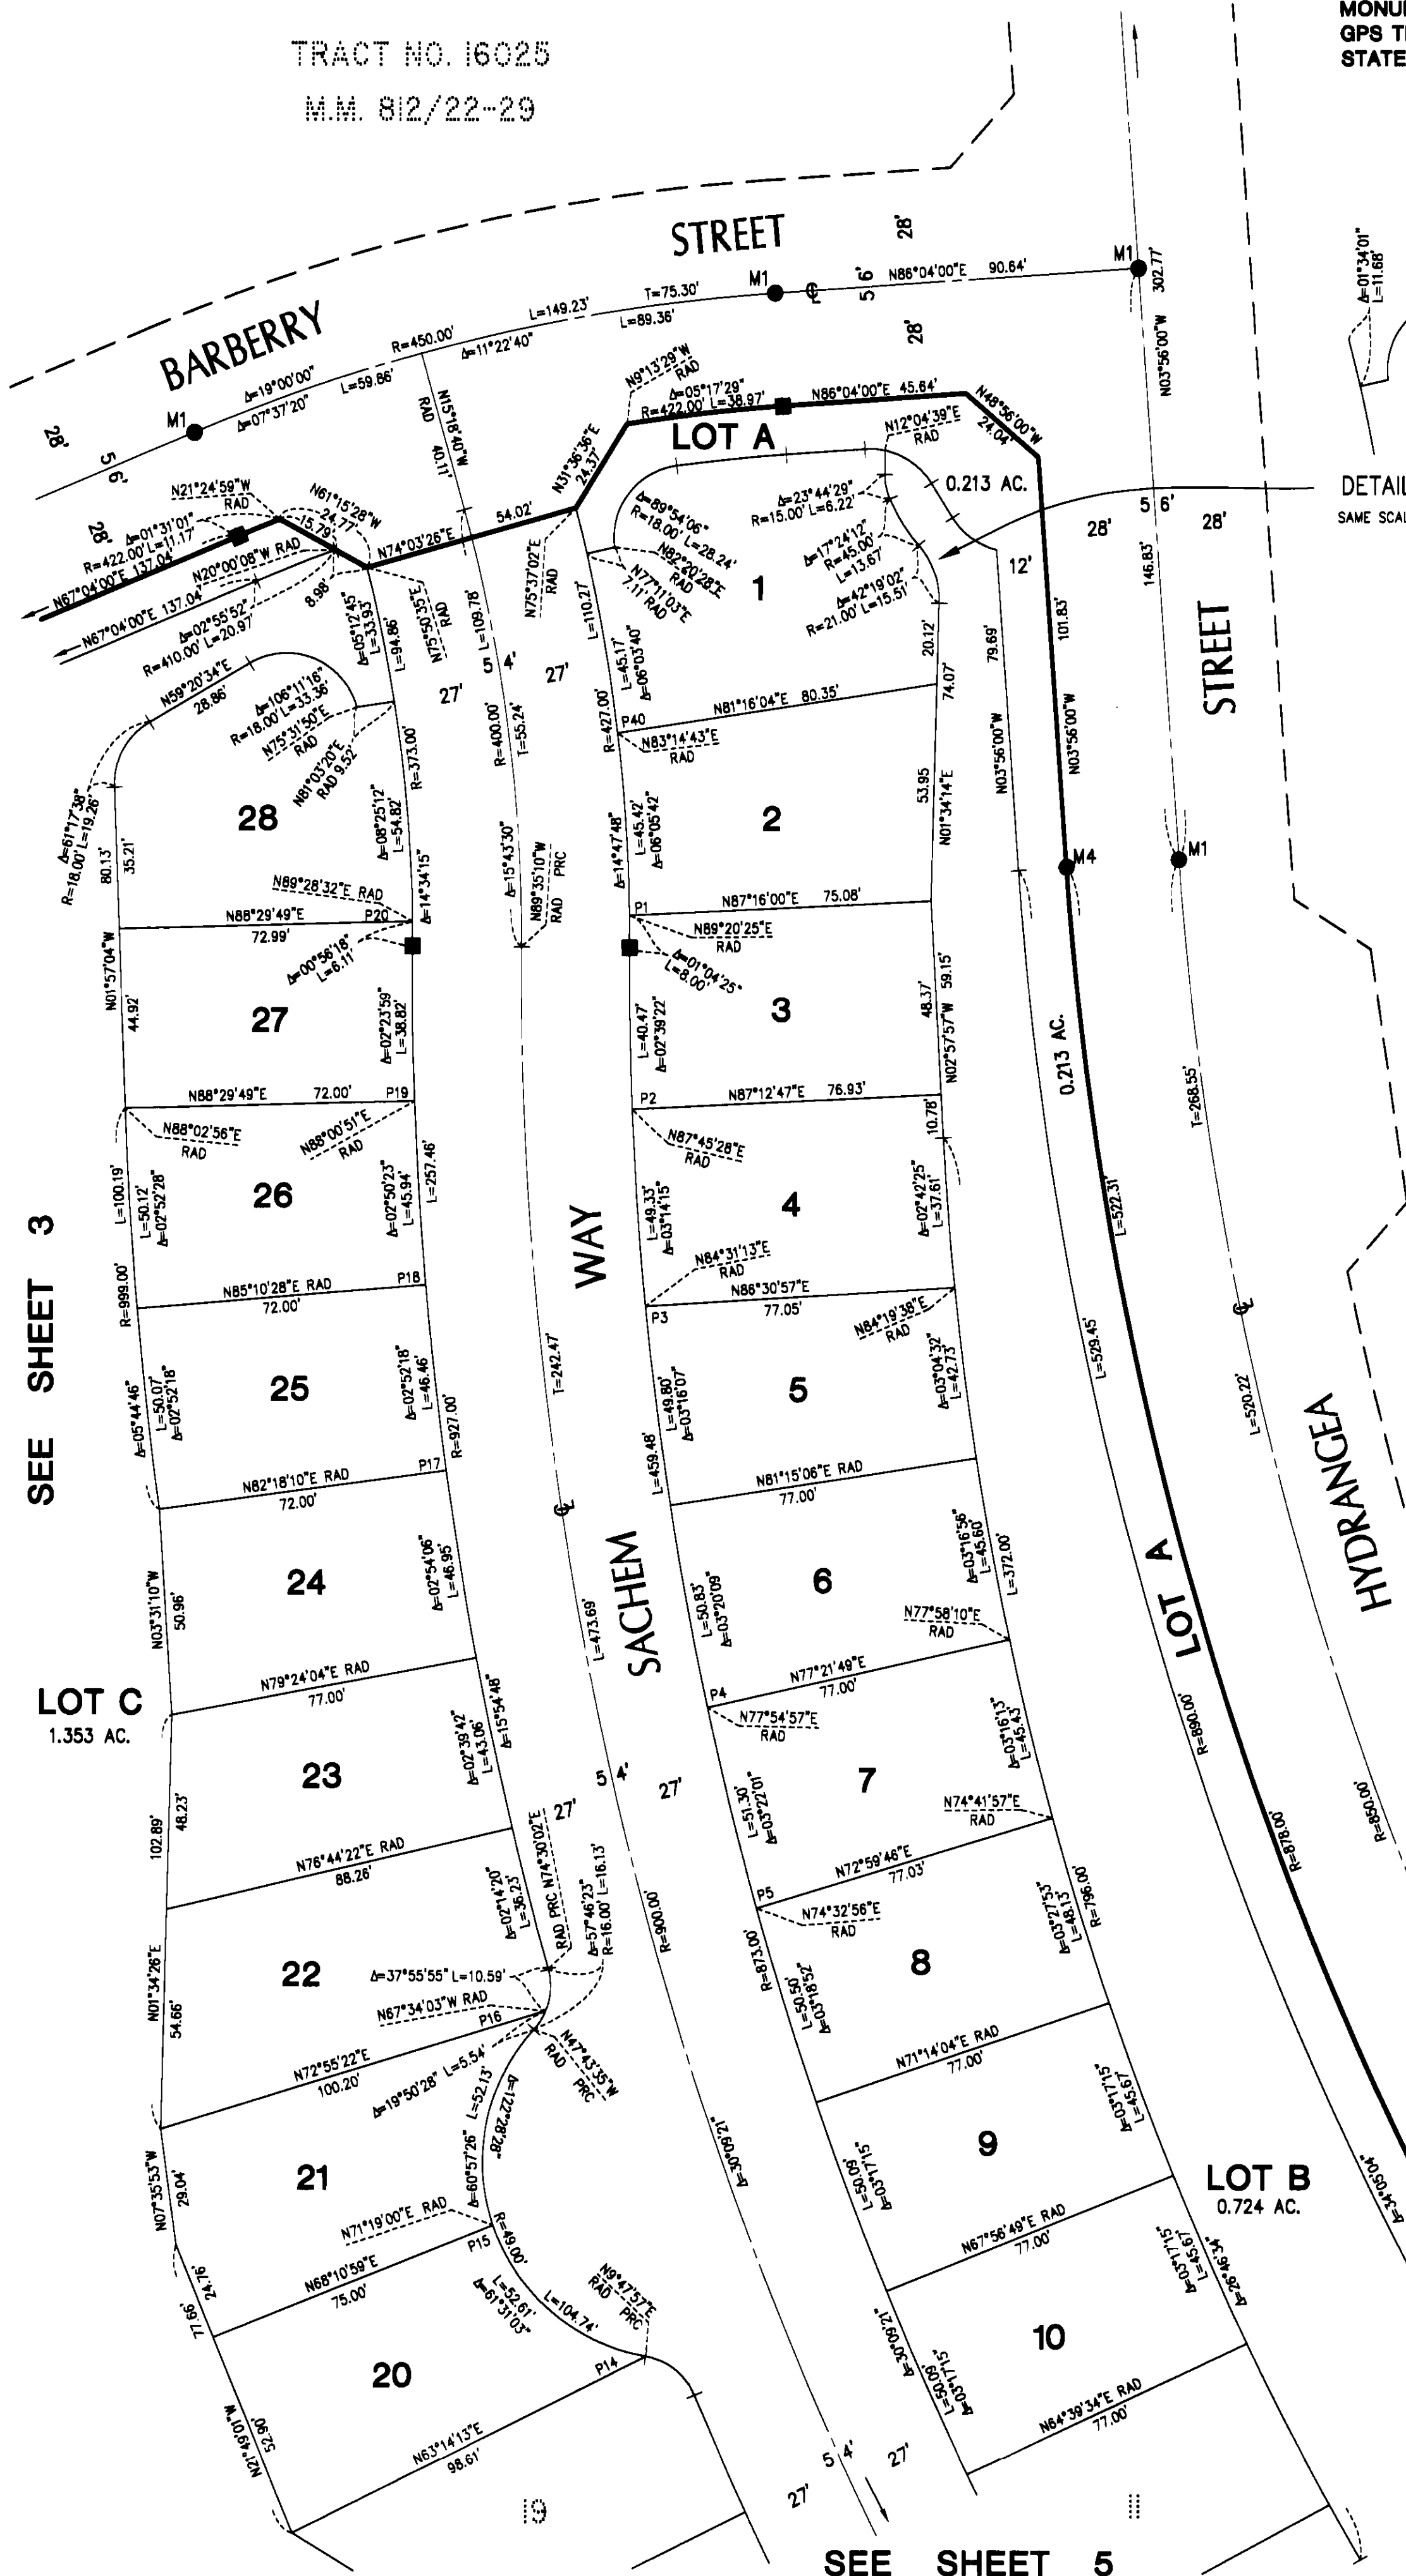

MONUMENT OFFSET TABLE		
LINE	BEARING	LENGTH
P1	S87°16'00\"W	8.76'
P2	S87°12'47\"W	8.75'
P3	S86°30'57\"W	14.76'
P4	S77°21'49\"W	8.75'
P5	S72°59'46\"W	8.75'
P14	N63°14'13\"E	11.82'
P15	N68°10'59\"E	8.77'
P16	N72°55'22\"E	10.22'
P17	N82°18'10\"E	8.77'
P18	N85°10'28\"E	14.75'
P19	N88°29'49\"E	8.75'
P20	N88°29'49\"E	8.75'
P40	S81°16'04\"W	8.76'

TRACT NO. 16156
M.M. 812/40-48


SEE SHEET 5

SHEET 6 OF 6 SHEETS
SCALE: 1" = 30'
71 NUMBERED LOTS AND LOTS
A THROUGH H, INCLUSIVE
ACREAGE: 12.165 ACRES
(ALL OF TENTATIVE
TRACT NO. 16116)

TRACT NO. 16116

IN UNINCORPORATED TERRITORY OF THE COUNTY OF ORANGE,
STATE OF CALIFORNIA


HUNSAKER AND ASSOCIATES IRVINE, INC.
RORY S. WILLIAMS, L.S. 6654 DATE OF SURVEY: AUGUST, 2001

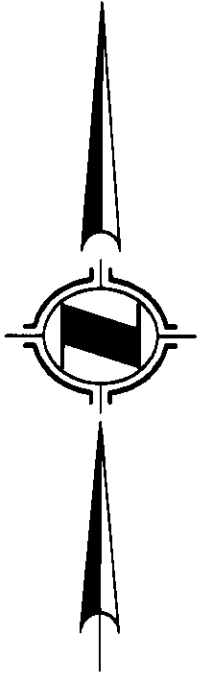

SEE SHEET 2 FOR BASIS OF BEARINGS,
MONUMENT NOTES, EASEMENT NOTES,
GPS TIES, SHEET INDEX MAP, DATUM
STATEMENT AND NOTES.

SEE SHEET 4

TRACT NO. 16156
M.M. 812/40-48

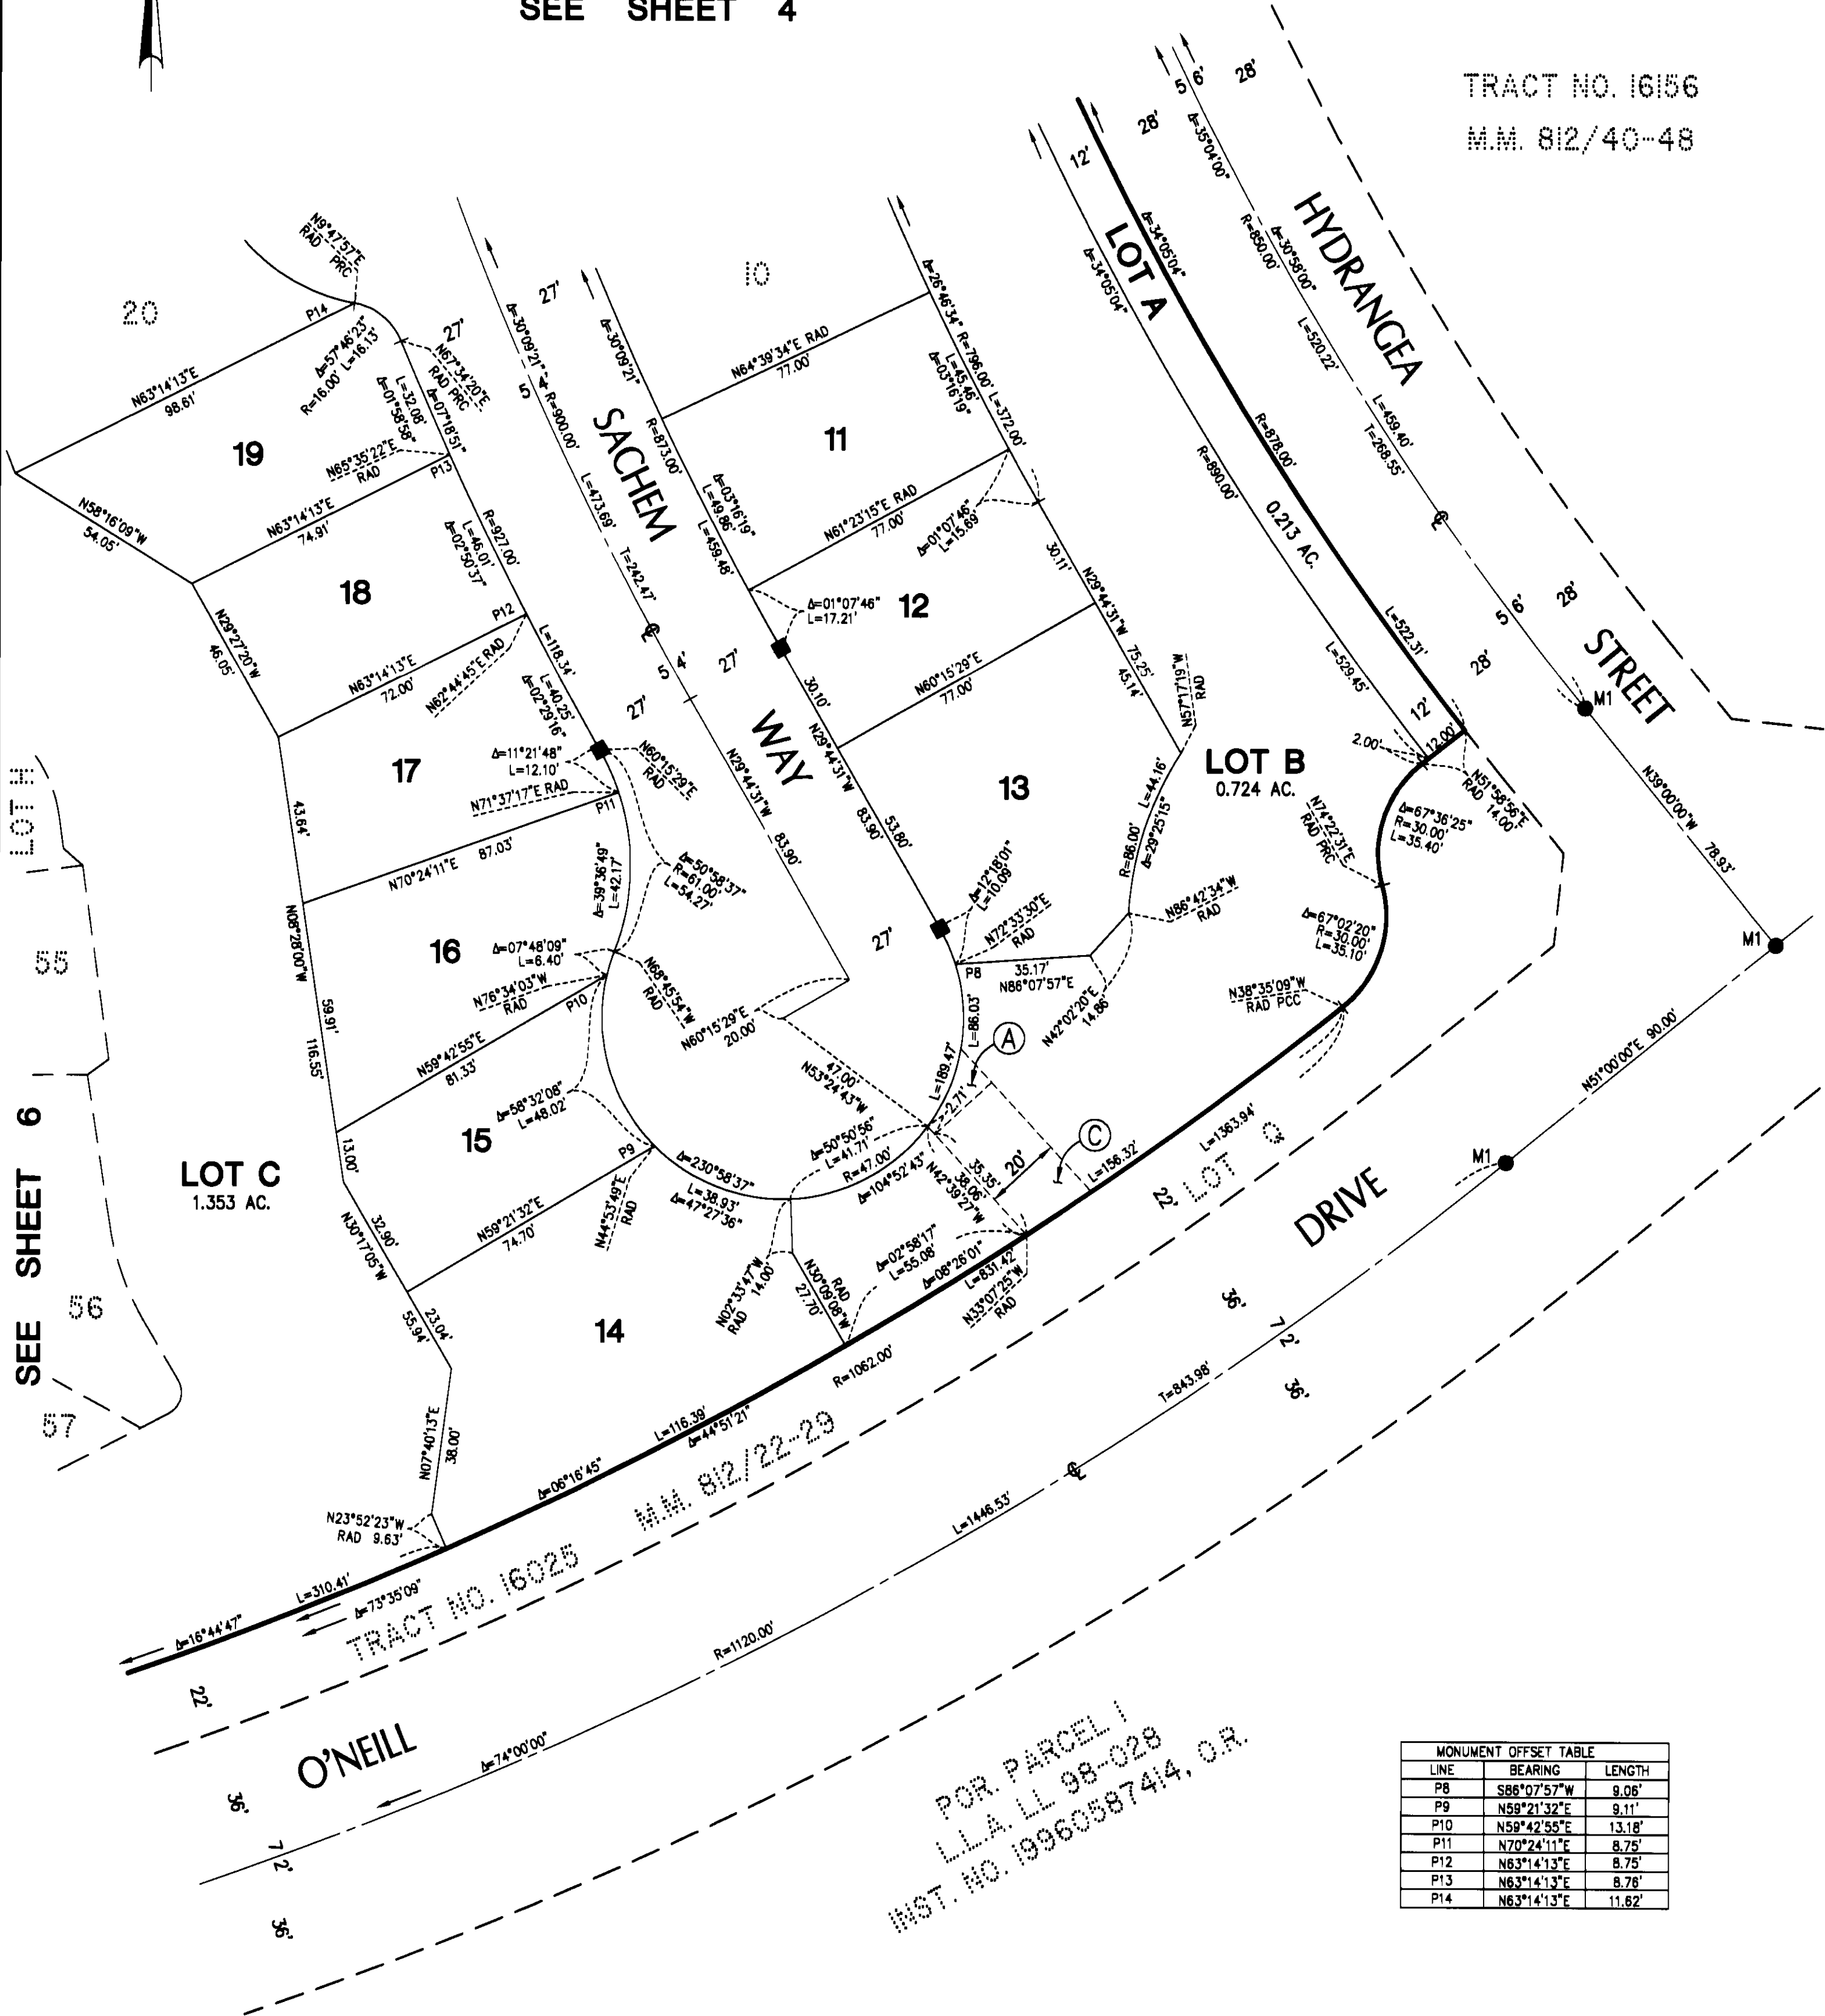

MONUMENT OFFSET TABLE		
LINE	BEARING	LENGTH
P8	S86°07'57"W	9.06'
P9	N59°21'32"E	9.11'
P10	N59°42'55"E	13.18'
P11	N70°24'11"E	8.75'
P12	N63°14'13"E	8.75'
P13	N63°14'13"E	8.78'
P14	N63°14'13"E	11.62'

FOR PARCEL I
L.A. LL 98-028
INST. NO. 19960587414, O.R.

830

**IN UNINCORPORATED TERRITORY OF THE COUNTY OF ORANGE,
STATE OF CALIFORNIA**


RORY S. WILLIAMS, L.S. 6654

DATE OF SURVEY: AUGUST, 2001

THE
JOURNAL
OF
THE
ROYAL
ANTHROPOLOGICAL
INSTITUTE

02/22-29

MONUMENT OFFERING TABLE		
LINE	BEARING	LENGTH
P29	S04°14'24"E	8.92'
P30	S04°14'24"E	8.77'
P31	S04°14'24"E	8.82'
P32	S04°14'24"E	8.88'
P33	N17°24'40"W	9.07'
P34	N17°24'40"W	8.98'
P35	N17°24'40"W	8.80'
P36	S46°16'43"E	8.83'
P41	S82°36'20"W	8.76'

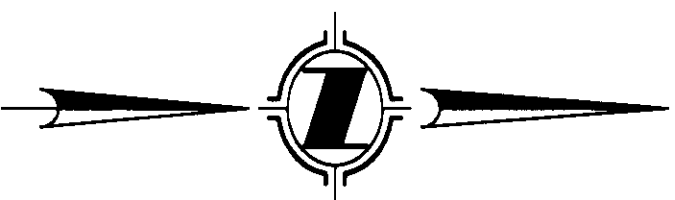

TRACT NO. 16025
M.M. 8/2/22-29

SET 2" I.P. TAGGED
L.S. 6654 PRIOR TO
RECORDATION

Lot 10

0.257 AC.

90.19' $\Delta = 13.40$
 182°45'56"E
 COURT

COURT

DUSKYWING

COURT

SET 2" I.P. TAGGED
L.S. 6654 PRIOR TO
RECORDATION

LOT E 0.122 AC

0.125 AC.

SEE SHEET 5

SEE SHEET 2 FOR BASIS OF BEARINGS
MONUMENT NOTES, EASEMENT NOTES,
GPS TIES, SHEET INDEX MAP, DATUM
STATEMENT AND NOTES.

B30

40