

## SHEET 1 OF 4 SHEETS

AREA: 8.870 ACRES GROSS  
(BEING ALL OF  
TENTATIVE TRACT NO. 16118  
NUMBERED LOTS: 48  
LETTERED LOTS: 9

BLOCK MODULE  
5057 59 AND 69  
5058 50 AND 60

## TRACT NO. 16118

IN THE UNINCORPORATED TERRITORY OF THE  
COUNTY OF ORANGE, STATE OF CALIFORNIA

BEING A SUBDIVISION OF LOT 3, TRACT NO. 16156 AS SHOWN ON A MAP FILED IN  
BOOK 812, PAGES 40 THROUGH 48 OF MISCELLANEOUS MAPS, IN THE OFFICE OF  
THE COUNTY RECORDER OF SAID ORANGE COUNTY.

JAMES R. CRAWFORD, L.S. 4965



DATE OF SURVEY: JANUARY, 2001

ACCEPTED AND FILED AT THE  
REQUEST OF  
FIRST AMERICAN TITLE INSURANCE CO.

DATE OCTOBER 26, 2001

TIME 1:12 P.M. FEE \$13.92

INSTRUMENT # 20010759369

BOOK 823 PAGE 30-33 M/M

GARY L. GRANVILLE  
COUNTY CLERK-RECORDER

BY DEPUTY

## OWNERSHIP CERTIFICATE:

WE THE UNDERSIGNED, BEING ALL PARTIES HAVING ANY RECORD TITLE INTEREST IN THE LAND COVERED BY THIS MAP, DO HEREBY CONSENT TO THE PREPARATION AND RECORDATION OF SAID MAP AS SHOWN WITHIN THE DISTINCTIVE BORDER LINE. WE ALSO HEREBY DEDICATE TO THE PUBLIC FOR STREET PURPOSES: SHIVELY ROAD, LANGFORD LANE AND CARLISLE COURT.

WE HEREBY ALSO DEDICATE TO THE COUNTY OF ORANGE:

- 1) THE EASEMENT FOR STORM DRAIN PURPOSES AS SHOWN HEREON.
- 2) THE EASEMENT FOR PEDESTRIAN ACCESS PURPOSES AS SHOWN ON SAID MAP.

WE ALSO HEREBY DEDICATE TO THE SANTA MARGARITA WATER DISTRICT THE EASEMENT FOR SEWER, WATER AND ACCESS PURPOSES AS SHOWN HEREON WHICH EASEMENT SHALL BE SUBJECT TO THE SAME TERMS AND CONDITIONS AS ARE SHOWN IN THAT CERTAIN EASEMENT RECORDED OCTOBER 6, 1980, IN BOOK 13776, PAGE 341 OF OFFICIAL RECORDS OF THE COUNTY OF ORANGE.

THE SANTA MARGARITA WATER DISTRICT SHALL RESTORE OTHER IMPROVEMENTS OR FACILITIES LOCATED WITHIN THE EASEMENT, IF IT HAS CONSENTED TO THE LOCATION OF SUCH IMPROVEMENTS OR FACILITIES TO THE EXTENT THAT THE EXERCISE OF ITS RIGHTS IN CONNECTION WITH THE EASEMENT IMPACTS OTHER IMPROVEMENTS OR FACILITIES LOCATED WITHIN THE EASEMENT, HOWEVER, IN NO EVENT SHALL SANTA MARGARITA WATER DISTRICT BE RESPONSIBLE FOR THE COST OF RELOCATING ITS FACILITIES IN THE EVENT OF CONFLICTS WITH SUCH OTHER IMPROVEMENTS OR FACILITIES.

WILLIAM LYON HOMES, INC., A CALIFORNIA CORPORATION,

PRINT NAME: THOMAS J. MITCHELL  
PRINT TITLE: SENIOR VICE PRESIDENT

PRINT NAME: WILLIAM H. LYON  
PRINT TITLE: ASSISTANT SECRETARY

DMB LADERA, L.L.C., A DELAWARE LIMITED LIABILITY COMPANY  
BENEFICIARY UNDER A DEED OF TRUST RECORDED FEBRUARY 28, 2001, AS INSTRUMENT NO. 20010110730 OF OFFICIAL RECORDS.

BY: RANCHO MISSION VIEJO, L.L.C., A DELAWARE LIMITED LIABILITY COMPANY  
AS AGENT OR MANAGER

PRINT NAME: Paul Johnson  
PRINT TITLE: VP-Community Development

PRINT NAME: Donald L. Vodra  
PRINT TITLE: Chief Operating Officer

RESIDENTIAL FUNDING CORPORATION, A DELAWARE CORPORATION,  
BENEFICIARY UNDER A DEED OF TRUST RECORDED FEBRUARY 28, 2001, AS INSTRUMENT NO. 20010110731 OF OFFICIAL RECORDS.

PRINT NAME: PETER FISCHER  
PRINT TITLE: DIRECTOR

PRINT NAME: Lance Franklin  
PRINT TITLE: Director

## NOTARY ACKNOWLEDGEMENT FOR WILLIAM LYON HOMES, INC.:

STATE OF CALIFORNIA } SS  
COUNTY OF ORANGE

ON JUNE 13, 2001, BEFORE ME, SUSAN E MENARD, A NOTARY PUBLIC IN AND FOR SAID STATE PERSONALLY APPEARED THOMAS J. MITCHELL AND WILLIAM H. LYON, PERSONALLY KNOWN TO ME (OR PROVED TO ME ON THE BASIS OF OF SATISFACTORY EVIDENCE) TO BE THE PERSONS WHOSE NAMES ARE SUBSCRIBED TO THE WITHIN INSTRUMENT AND ACKNOWLEDGED TO ME THAT THEY EXECUTED THE SAME IN THEIR AUTHORIZED CAPACITIES AND THAT BY THEIR SIGNATURES ON THE INSTRUMENT THE PERSONS, OR THE ENTITY UPON BEHALF OF WHICH THE PERSONS ACTED EXECUTED THE INSTRUMENT.

WITNESS MY HAND:

NOTARY PUBLIC IN AND FOR SAID STATE  
SUSAN E MENARD  
(NAME PRINTED)

MY PRINCIPAL PLACE OF BUSINESS IS  
IN NEWPORT BEACH  
MY COMMISSION EXPIRES: Sept 5, 2003

## NOTARY ACKNOWLEDGEMENT FOR DMB LADERA, LLC:

STATE OF California } SS  
COUNTY OF Orange

ON June 19, 2001, BEFORE ME, Tina T. Baker, A NOTARY PUBLIC IN AND FOR SAID STATE PERSONALLY APPEARED Paul Johnson AND Donald L. Vodra, PERSONALLY KNOWN TO ME (OR PROVED TO ME ON THE BASIS OF OF SATISFACTORY EVIDENCE) TO BE THE PERSONS WHOSE NAMES ARE SUBSCRIBED TO THE WITHIN INSTRUMENT AND ACKNOWLEDGED TO ME THAT THEY EXECUTED THE SAME IN THEIR AUTHORIZED CAPACITIES AND THAT BY THEIR SIGNATURES ON THE INSTRUMENT THE PERSONS, OR THE ENTITY UPON BEHALF OF WHICH THE PERSONS ACTED EXECUTED THE INSTRUMENT.

WITNESS MY HAND:

NOTARY PUBLIC IN AND FOR SAID STATE  
Tina T. Baker  
(NAME PRINTED)


MY PRINCIPAL PLACE OF BUSINESS IS  
IN San Juan Capistrano  
MY COMMISSION EXPIRES: 8-29-04

SEE SHEET 2 FOR SANTA MARGARITA WATER DISTRICT SIGNATURE AND ACKNOWLEDGEMENT,  
SIGNATURE OMISSIONS AND NOTES.

## SURVEYOR'S STATEMENT:

I HEREBY STATE THAT THIS MAP CONSISTING OF FOUR (4) SHEETS CORRECTLY REPRESENTS THE TRUE AND COMPLETE SURVEY AS SHOWN MADE IN JANUARY, 2001; WAS MADE BY ME OR UNDER MY DIRECTION; THAT THE MONUMENTS ARE OF THE CHARACTER AND OCCUPY OR WILL OCCUPY THE POSITIONS INDICATED BY SAID MAP; AND THAT SAID MONUMENTS ARE OR WILL BE SUFFICIENT TO ENABLE THE SURVEY TO BE RETRACED.

JAMES R. CRAWFORD, L.S. 4965  
MY LICENSE EXPIRES: DECEMBER 31, 2001

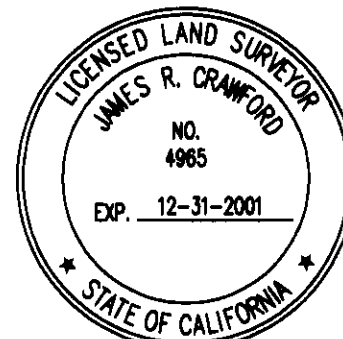


## COUNTY SURVEYOR'S STATEMENT:

I HEREBY STATE THAT I HAVE EXAMINED THIS MAP AND FOUND IT TO BE SUBSTANTIALLY IN CONFORMANCE WITH THE TENTATIVE MAP AS FILED WITH, AMENDED AND APPROVED BY THE ORANGE COUNTY SUBDIVISION COMMITTEE; THAT ALL PROVISIONS OF THE SUBDIVISION MAP ACT AND COUNTY SUBDIVISION REGULATIONS HAVE BEEN COMPLIED WITH AND I AM SATISFIED SAID MAP IS TECHNICALLY CORRECT.

DATED THIS 12th DAY OF October, 2001.

JOHN CANAS, COUNTY SURVEYOR  
L.S. 4408 EXPIRATION DATE: 09-30-2001  
Robert Jelinek, Deputy County Surveyor L.S. 6803 Exp. 9/30/04

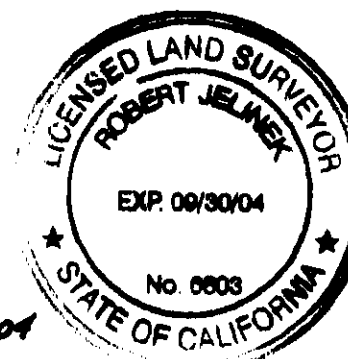

## CLERK OF THE BOARD OF SUPERVISORS' CERTIFICATE:

STATE OF CALIFORNIA }  
COUNTY OF ORANGE } SS

I HEREBY CERTIFY THAT THIS MAP WAS PRESENTED FOR APPROVAL TO THE BOARD OF SUPERVISORS OF ORANGE COUNTY AT A REGULAR MEETING THEREOF HELD ON THE 23rd DAY OF October, 2001, AND THAT THEREUPON SAID BOARD DID, BY AN ORDER DULY PASSED AND ENTERED, APPROVE SAID MAP AND DID ACCEPT ON BEHALF OF THE PUBLIC, SUBJECT TO IMPROVEMENTS; THE DEDICATION FOR STREET PURPOSES OF: SHIVELY ROAD, LANGFORD LANE AND CARLISLE COURT.

AND DID ALSO ACCEPT ON BEHALF OF THE COUNTY:

- 1) THE EASEMENT FOR STORM DRAIN PURPOSES AS DEDICATED, SUBJECT TO IMPROVEMENTS.
- 2) THE EASEMENT FOR PEDESTRIAN ACCESS PURPOSES AS DEDICATED.

AND DID ALSO APPROVE SUBJECT MAP PURSUANT TO THE PROVISIONS OF SECTION 66436(a)(3) OF THE SUBDIVISION MAP ACT.

DATED THIS 23rd DAY OF October, 2001.

DARLENE J. BLOOM  
CLERK OF THE BOARD OF SUPERVISORS



## COUNTY TREASURER-TAX COLLECTOR'S CERTIFICATE:

STATE OF CALIFORNIA }  
COUNTY OF ORANGE } SS

I HEREBY CERTIFY THAT ACCORDING TO THE RECORDS OF MY OFFICE, THERE ARE NO LIENS AGAINST THE LAND COVERED BY THIS MAP OR ANY PART THEREOF FOR UNPAID STATE, COUNTY, MUNICIPAL OR LOCAL TAXES OR SPECIAL ASSESSMENTS COLLECTED AS TAXES, EXCEPT TAXES OR SPECIAL ASSESSMENTS COLLECTED AS TAXES NOT YET PAYABLE.

AND DO CERTIFY TO THE RECORDER OF ORANGE COUNTY THAT THE PROVISIONS OF THE SUBDIVISION MAP ACT HAVE BEEN COMPLIED WITH REGARDING DEPOSITS TO SECURE THE PAYMENT OF TAXES OR SPECIAL ASSESSMENTS COLLECTED AS TAXES ON THE LAND COVERED BY THIS MAP.

DATED THIS 18th DAY OF September, 2001.

JOHN M. W. MOORLACH  
COUNTY TREASURER-TAX COLLECTOR

BY   
DEPUTY TREASURER-TAX COLLECTOR

## NOTARY ACKNOWLEDGEMENT FOR RESIDENTIAL FUNDING CORPORATION:

STATE OF California } SS  
COUNTY OF Los Angeles

ON June 18, 2001, BEFORE ME, Sonia B. Garcia, A NOTARY PUBLIC IN AND FOR SAID STATE PERSONALLY APPEARED Peter Fischer AND Lance Franklin, PERSONALLY KNOWN TO ME (OR PROVED TO ME ON THE BASIS OF OF SATISFACTORY EVIDENCE) TO BE THE PERSONS WHOSE NAMES ARE SUBSCRIBED TO THE WITHIN INSTRUMENT AND ACKNOWLEDGED TO ME THAT THEY EXECUTED THE SAME IN THEIR AUTHORIZED CAPACITIES AND THAT BY THEIR SIGNATURES ON THE INSTRUMENT THE PERSONS, OR THE ENTITY UPON BEHALF OF WHICH THE PERSONS ACTED EXECUTED THE INSTRUMENT.

WITNESS MY HAND:


NOTARY PUBLIC IN AND FOR SAID STATE  
SONIA E. GARCIA  
(NAME PRINTED)

MY PRINCIPAL PLACE OF BUSINESS IS  
IN Los Angeles County  
MY COMMISSION EXPIRES: May 9, 2003





DATE OF SURVEY: JANUARY, 2001

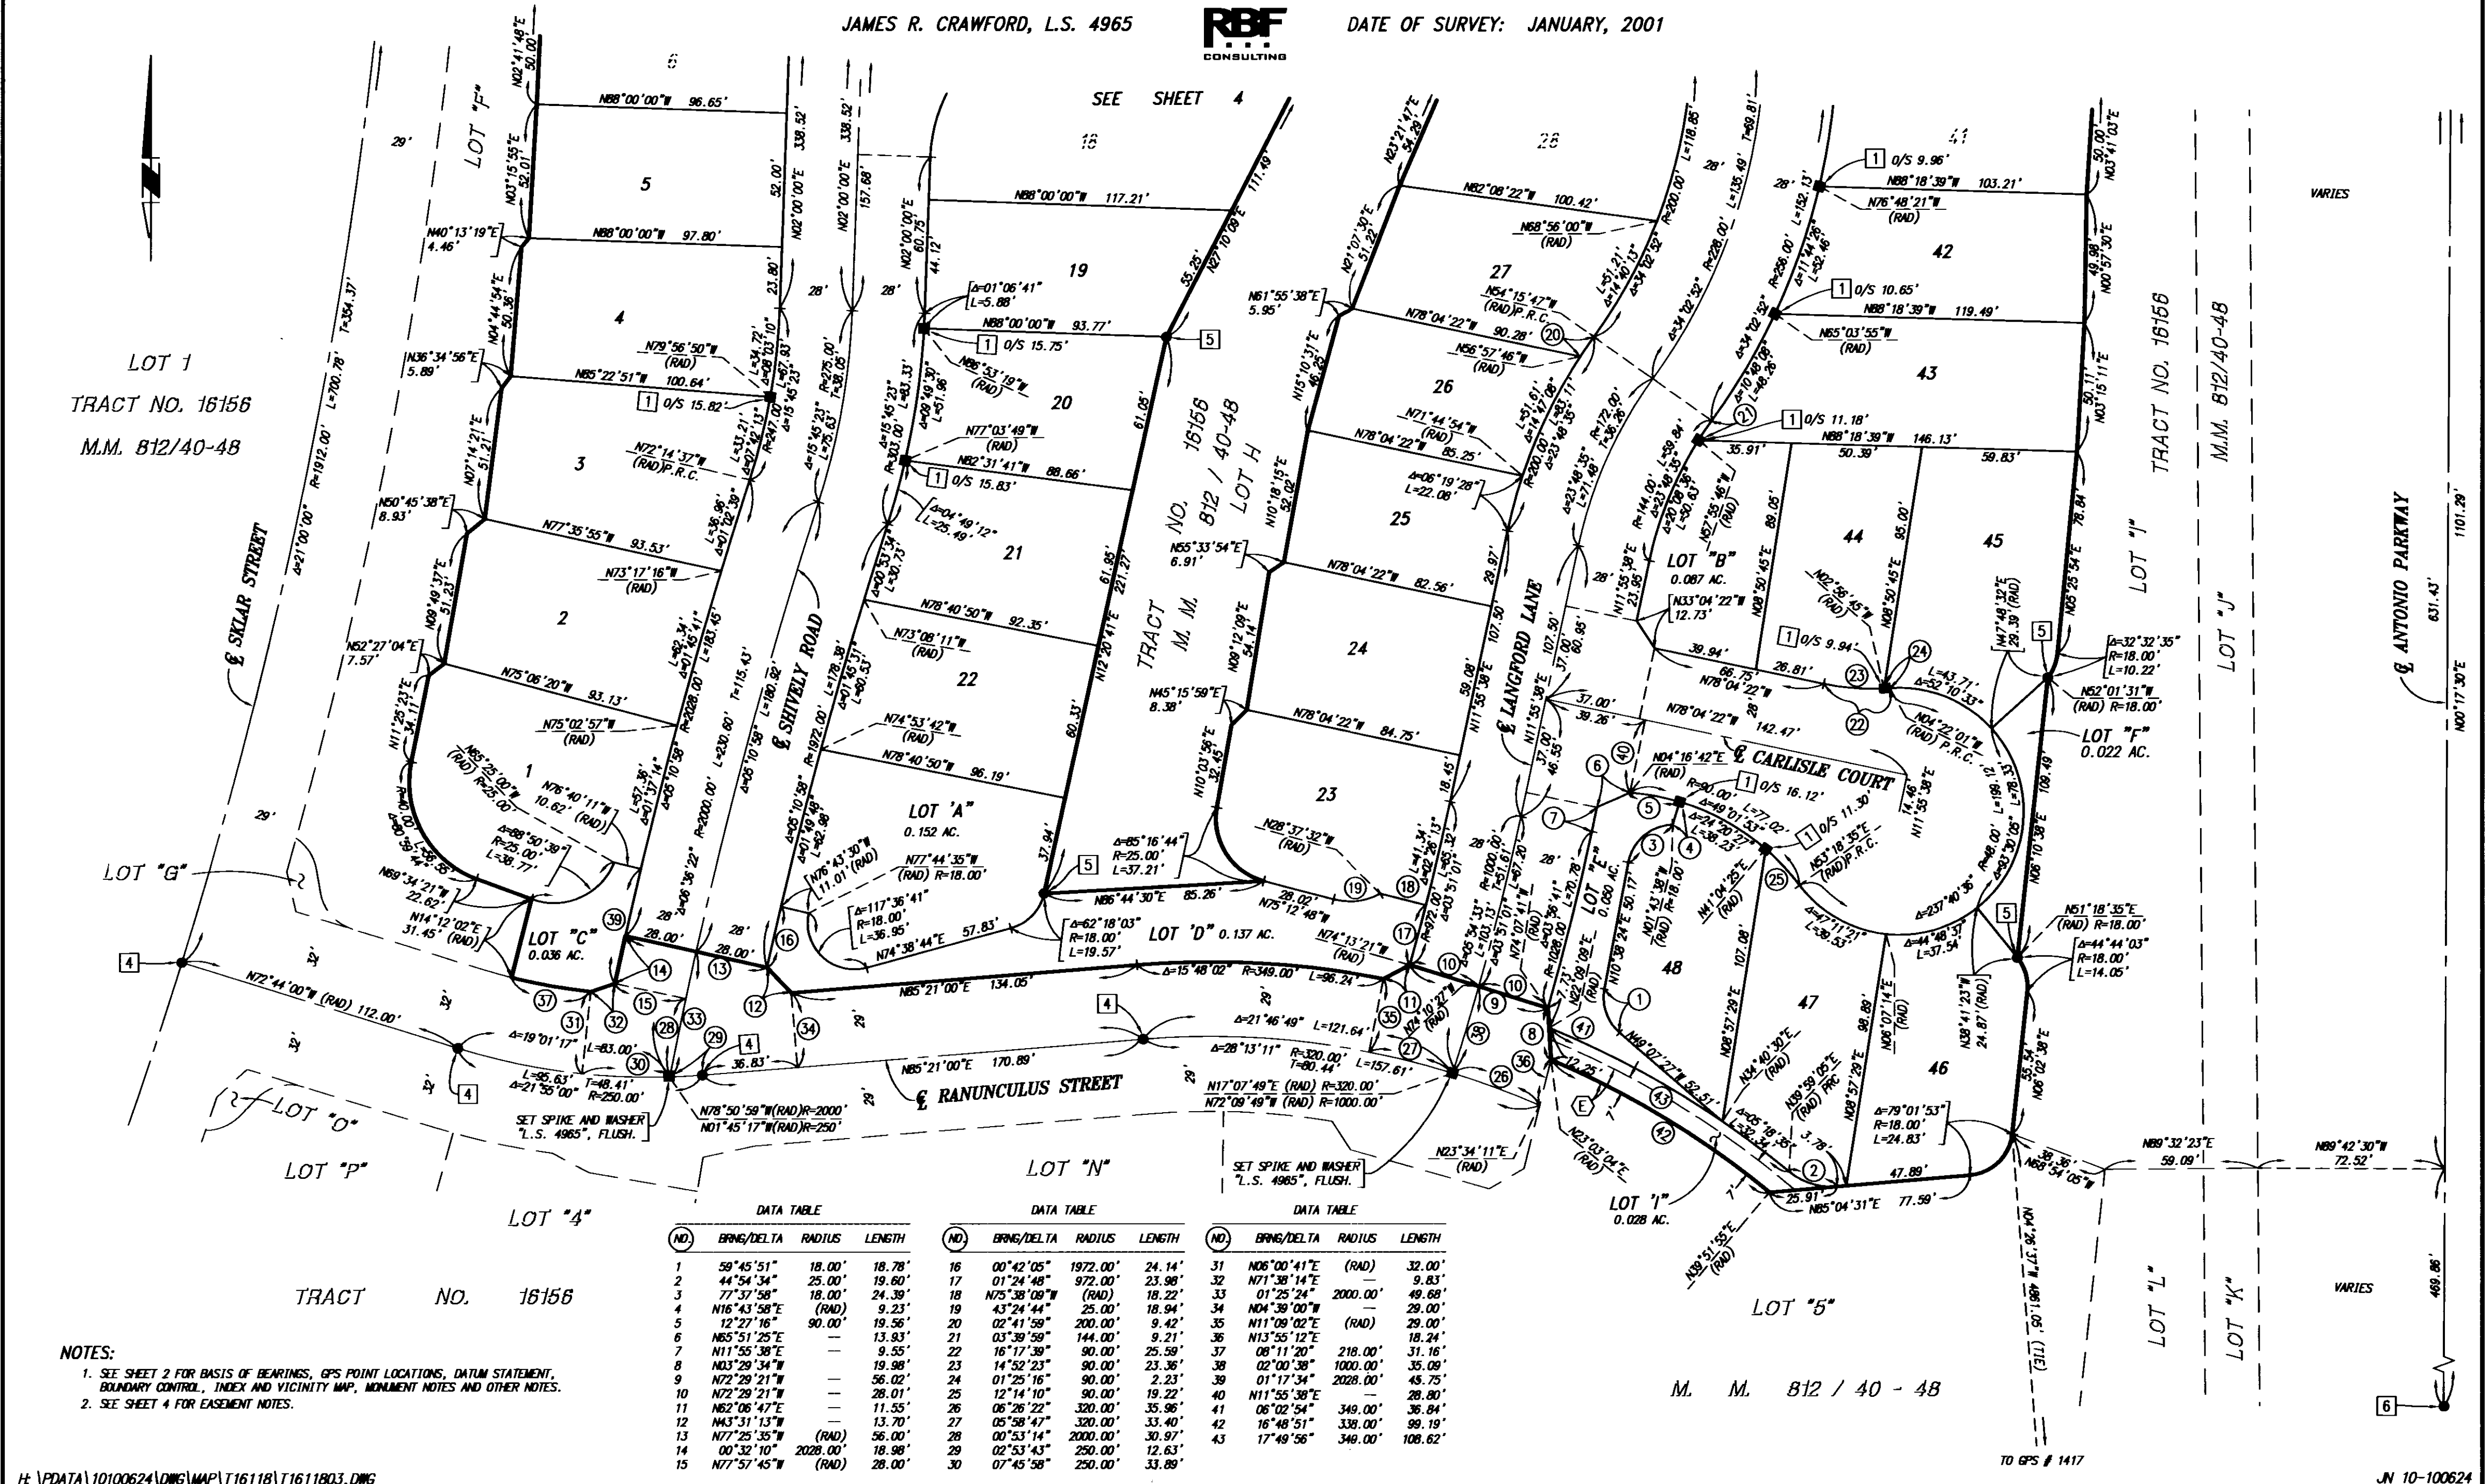



SHEET 4 OF 4 SHEETS  
AREA: 8.870 ACRES GROSS  
(BEING ALL OF  
TENTATIVE TRACT NO. 16118)  
NUMBERED LOTS: 48  
LETTERED LOTS: 9  
SCALE: 1" = 40'

# TRACT NO. 16118

IN THE UNINCORPORATED TERRITORY OF THE  
COUNTY OF ORANGE, STATE OF CALIFORNIA

JAMES R. CRAWFORD, L.S. 4965



DATE OF SURVEY: JANUARY, 2001

| DATA TABLE |               |          |        |
|------------|---------------|----------|--------|
| NO.        | BEARING/Delta | RADIUS   | LENGTH |
| 1          | N79°19'30"E   | —        | 65.08' |
| 2          | N86°16'00"E   | —        | 23.47' |
| 3          | 64°17'00"     | 18.00'   | 20.20' |
| 4          | 52°20'40"     | 48.00'   | 43.85' |
| 5          | 77°46'50"     | 25.00'   | 33.94' |
| 6          | N78°44'40"E   | —        | 62.83' |
| 7          | N78°44'40"E   | —        | 30.55' |
| 8          | N86°16'00"E   | —        | 32.10' |
| 9          | 49°18'41"     | 48.00'   | 41.31' |
| 10         | 00°36'46"     | 60.00'   | 0.64'  |
| 11         | 09°47'51"     | 60.00'   | 10.26' |
| 12         | 01°22'49"     | 200.00'  | 5.11'  |
| 13         | 12°02'53"     | 90.00'   | 18.93' |
| 14         | 13°34'18"     | 90.00'   | 21.32' |
| 15         | 00°14'38"     | 256.00'  | 1.09'  |
| 16         | 64°02'53"     | 30.00'   | 33.54' |
| 17         | 86°59'49"     | 15.00'   | 17.54' |
| 18         | 00°33'40"     | 2248.00' | 22.02' |
| 19         | 00°24'59"     | 2248.00' | 16.34' |


## EASEMENT NOTES:

- (A) DENOTES AN EASEMENT FOR STORM DRAIN PURPOSES IN FAVOR OF THE COUNTY OF ORANGE BEING DEDICATED HEREON.
- (B) DENOTES AN EASEMENT FOR SEWER, WATER AND ACCESS PURPOSES IN FAVOR OF THE SANTA MARGARITA WATER DISTRICT BEING DEDICATED HEREON.
- (C) DENOTES AN EASEMENT FOR STORM DRAIN PURPOSES IN FAVOR OF THE COUNTY OF ORANGE DEDICATED PER TRACT NO. 16156, M.M. 812/40-48.
- (D) DENOTES AN EASEMENT FOR SEWER, WATER AND ACCESS PURPOSES IN FAVOR OF THE SANTA MARGARITA WATER DISTRICT DEDICATED PER TRACT NO. 16156, M.M. 812/40-48.
- (E) DENOTES AN EASEMENT FOR PEDESTRIAN ACCESS PURPOSES IN FAVOR OF THE COUNTY OF ORANGE BEING DEDICATED HEREON.

TRACT NO. 16155  
M. M. 812 / 30 - 39

AVENDALE

BOULEVARD

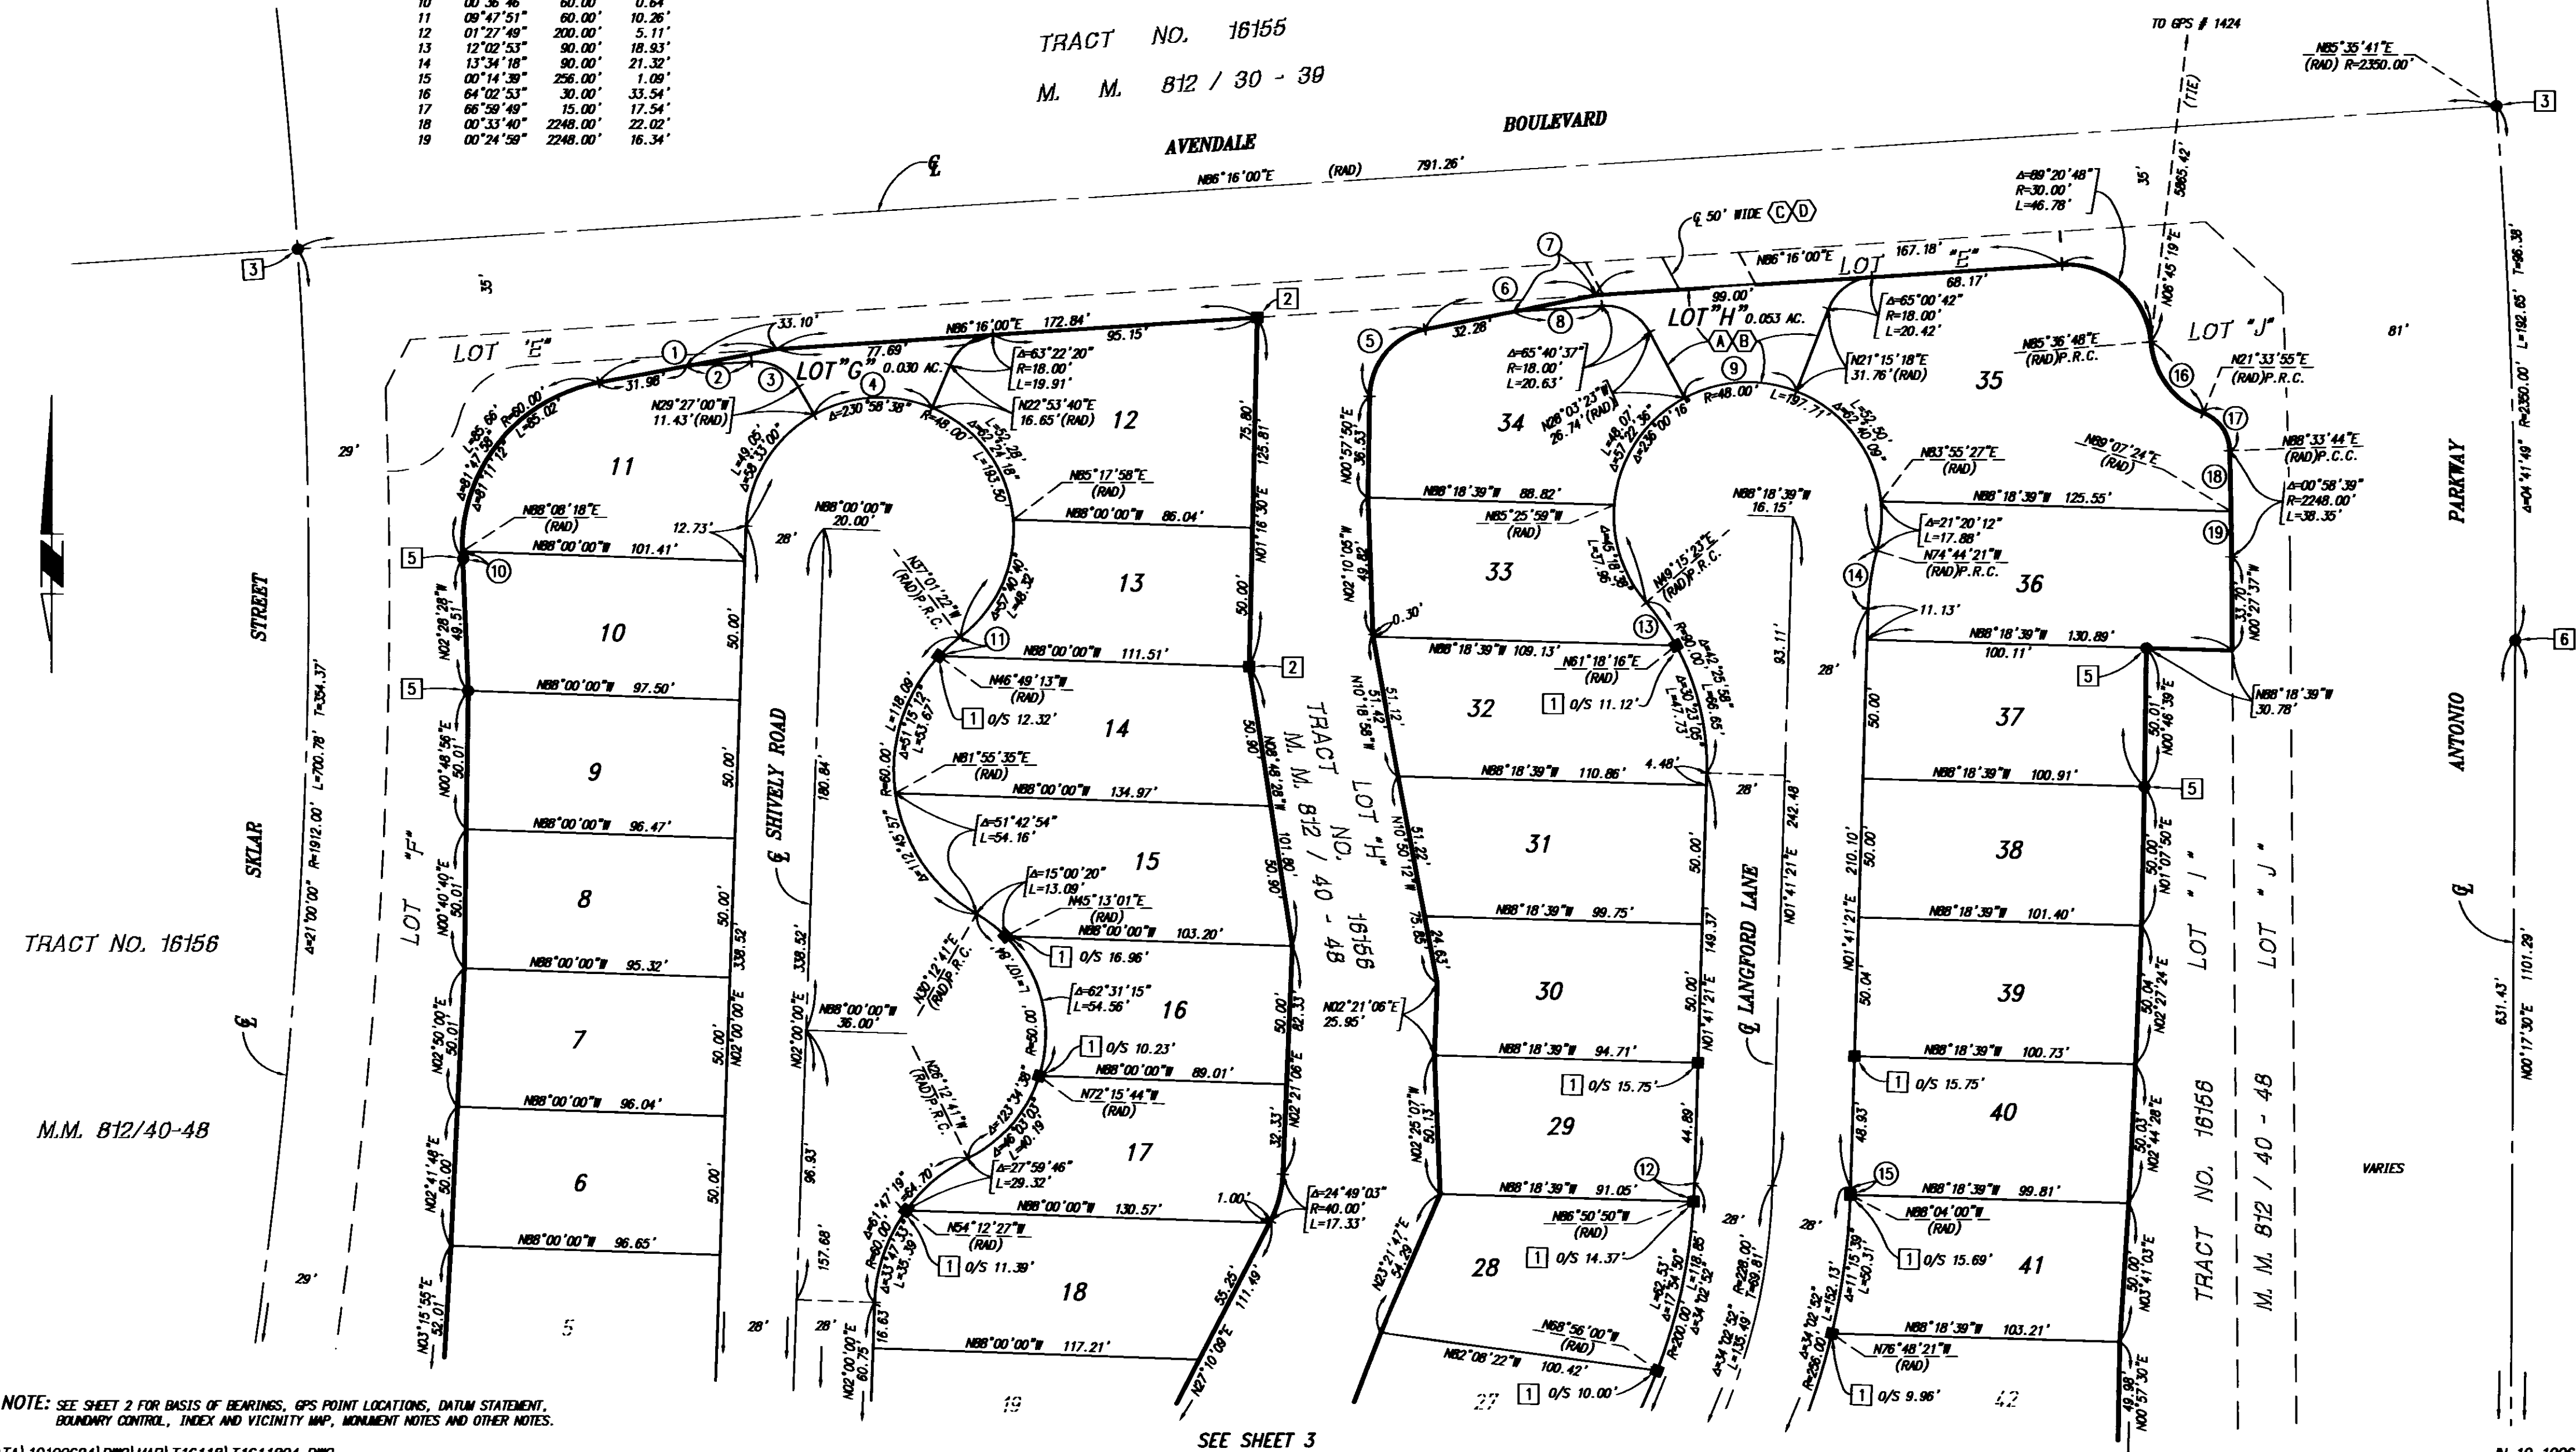

TRACT NO. 16156

M.M. 812/40-48

NOTE: SEE SHEET 2 FOR BASIS OF BEARINGS, GPS POINT LOCATIONS, DATUM STATEMENT, BOUNDARY CONTROL, INDEX AND VICINITY MAP, MONUMENT NOTES AND OTHER NOTES.

SEE SHEET 3