

TRACT NO. 16119

ALL OF VESTING  
TENTATIVE TRACT NO. 16119

BLOCK MODULE  
5157 19

DATE OF SURVEY:  
DECEMBER 2000

IN UNINCORPORATED TERRITORY OF ORANGE COUNTY, CALIFORNIA  
BEING A SUBDIVISION OF LOT 4 OF TRACT NO. 16156 FILED IN BOOK 812, PAGES 40  
THROUGH 48 OF MISCELLANEOUS MAPS, RECORDS OF ORANGE COUNTY, CALIFORNIA.

MARCH 2001

JAMES F. GILLEN, L.S. 5557

HUITT-ZOLIARS

12 NUMBERED LOTS AND LETTERED LOTS A, B, AND C 2.846 ACRES

ACCEPTED AND FILED AT THE  
REQUEST OF  
FIRST AMERICAN TITLE INSURANCE COMPANY

DATE DECEMBER 26, 2001  
TIME 10:52 AM FEE \$ 11.00  
INSTRUMENT NO. 20010940467  
BOOK 824 PAGE 48-50 M/M

GARY L. GRANVILLE  
COUNTY CLERK-RECORDER  
BY [Signature]  
DEPUTY

OWNERSHIP CERTIFICATE:

WE, THE UNDERSIGNED, BEING ALL PARTIES HAVING ANY RECORD TITLE INTEREST IN THE  
LAND COVERED BY THIS MAP, DO HEREBY CONSENT TO THE PREPARATION AND RECORDATION  
OF SAID MAP, AS SHOWN WITHIN THE DISTINCTIVE BORDER LINE. WE ALSO HEREBY DEDICATE  
TO THE PUBLIC FOR STREET PURPOSES: SHIVELY ROAD.

WE ALSO HEREBY DEDICATE TO THE COUNTY OF ORANGE:  
(1) THE EASEMENT FOR STORM DRAIN PURPOSES AS SHOWN ON SAID MAP.

WE ALSO HEREBY DEDICATE TO THE SANTA MARGARITA WATER DISTRICT THE EASEMENT FOR  
SEWER, WATER, AND ACCESS PURPOSES AS SHOWN ON SAID MAP, WHICH EASEMENT SHALL BE  
SUBJECT TO THE SAME TERMS AND CONDITIONS AS ARE SHOWN IN THAT CERTAIN EASEMENT  
RECORDED OCTOBER 6, 1980 IN BOOK 13776, PAGE 341, OF OFFICIAL RECORDS, COUNTY OF ORANGE.  
THE SANTA MARGARITA WATER DISTRICT SHALL RESTORE OTHER IMPROVEMENTS OR FACILITIES  
LOCATED WITHIN THE EASEMENT, IF IT HAS CONSENTED TO THE LOCATION OF SUCH IMPROVEMENTS  
OR FACILITIES TO THE EXTENT THAT THE EXERCISE OF ITS RIGHTS IN CONNECTION WITH THE EASEMENT  
IMPACTS OTHER IMPROVEMENTS OR FACILITIES LOCATED WITHIN THE EASEMENT, HOWEVER, IN NO EVENT  
SHALL SANTA MARGARITA WATER DISTRICT BE RESPONSIBLE FOR THE COST OF RELOCATING ITS FACILITIES  
IN THE EVENT OF CONFLICTS WITH SUCH OTHER IMPROVEMENTS OR FACILITIES.

STANDARD PACIFIC CORP., A DELAWARE CORPORATION

BY: [Signature] BY: [Signature]  
PRINT NAME: Andrew Barnes PRINT NAME: Jacil L. Kargozian  
PRINT TITLE: Chief Financial Officer PRINT TITLE: Vice President

DMB LADERA, L.L.C., A DELAWARE LIMITED LIABILITY COMPANY,  
BENEFICIARY UNDER A DEED OF TRUST RECORDED FEBRUARY 15, 2001 AS  
INSTRUMENT NO. 20010084587 OF OFFICIAL RECORDS, AND HOLDER OF A REPURCHASE  
OPTION RECORDED FEBRUARY 15, 2001 AS INSTRUMENT NO. 20010084585 OF  
OFFICIAL RECORDS.

BY: RANCHO MISSION VIEJO, L.L.C., A DELAWARE LIMITED LIABILITY COMPANY,  
AS AGENT AND/OR MANAGER.  
BY: [Signature] BY: [Signature]  
PRINT NAME: Paul Johnson PRINT NAME: Stephen C. Schrank  
PRINT TITLE: VP Community Development PRINT TITLE: Executive VP Development

CERTIFICATE OF ACCEPTANCE

THE UNDERSIGNED, BEING THE DULY APPOINTED AGENT OF THE SANTA MARGARITA WATER  
DISTRICT, A PUBLIC CORPORATION OF ORANGE COUNTY, CALIFORNIA, PURSUANT TO ITS  
RESOLUTION NO. 88-10-2, DOES HEREBY ACCEPT ON BEHALF OF SAID DISTRICT THE EASEMENT  
FOR SEWER, WATER AND ACCESS PURPOSES, AS DEDICATED AND AS SHOWN ON THIS TRACT MAP,  
BY AND BETWEEN THE SANTA MARGARITA WATER DISTRICT AND STANDARD PACIFIC CORP. AND  
DOES HEREBY CERTIFY THAT THE GRANTEE CONSENTS TO THE RECORDATION OF SAID TRACT.

[Signature]  
DANIEL R. FERONS, CHIEF ENGINEER  
SANTA MARGARITA WATER DISTRICT.

AUTOMATIC FIRE SPRINKLER NOTE:

ALL COMMERCIAL STRUCTURES GREATER THAN 6,000 SQUARE FEET; ALL MULTIFAMILY RESIDENTIAL  
STRUCTURES; ALL DETACHED SINGLE-FAMILY STRUCTURES EXCEEDING 5,500 SQUARE FEET, AND ALL  
STRUCTURES EXCEEDING FIRE AUTHORITY ACCESS REQUIREMENTS SHALL BE PROTECTED BY AN  
AUTOMATIC SPRINKLER SYSTEM. LOTS 10-12 WILL REQUIRE AUTOMATIC FIRE SPRINKLER  
SYSTEM PER OCCA.

HIGH FIRE HAZARD AREA NOTE:

THE LOTS SHOWN ON THIS MAP ARE IN A HIGH FIRE HAZARD AREA DUE TO  
WILD LAND EXPOSURE BASED ON STATE SRA MAPS.

THE PROPERTY SHOWN ON THIS MAP IS "TOTALLY EXCLUDED" FROM A "SPECIAL FIRE PROTECTION  
AREA." THERE ARE NO LOTS IN THIS TRACT THAT ARE SUBJECT TO CONSTRUCTION FEATURES OF  
THE ORANGE COUNTY ORDINANCE 3960.

NOTES:

PROPERTY MAY BE SUBJECT TO IMPACTS FROM THE FOOTHILL/EASTERN  
TRANSPORTATION CORRIDOR.

SEE SHEET 2 FOR NOTARY ACKNOWLEDGMENTS AND SIGNATURE OMISSIONS.

SURVEYOR'S STATEMENT:

I HEREBY STATE THAT THIS MAP CONSISTING OF 3 SHEETS, CORRECTLY REPRESENTS A TRUE AND  
COMPLETE SURVEY AS SHOWN MADE IN DECEMBER, 2000; WAS MADE BY ME OR UNDER MY DIRECTION;  
THAT THE MONUMENTS ARE OF THE CHARACTER AND OCCUPY OR WILL OCCUPY THE POSITIONS  
INDICATED BY SAID MAP; AND THAT SAID MONUMENTS WILL BE SUFFICIENT TO ENABLE THE  
SURVEY TO BE RETRACED.



[Signature]  
JAMES F. GILLEN  
L.S. 5557  
EXPIRATION DATE: 9/30/05

COUNTY SURVEYOR'S STATEMENT:

I HEREBY STATE THAT I HAVE EXAMINED THIS MAP AND HAVE FOUND IT TO BE  
SUBSTANTIALLY IN CONFORMANCE WITH THE TENTATIVE MAP AS FILED WITH, AMENDED AND  
APPROVED BY THE ORANGE COUNTY SUBDIVISION COMMITTEE; THAT ALL PROVISIONS OF THE  
SUBDIVISION MAP ACT AND COUNTY SUBDIVISION REGULATIONS HAVE BEEN COMPLIED WITH  
AND I AM SATISFIED SAID MAP IS TECHNICALLY CORRECT.

DATED THIS 5<sup>TH</sup> DAY OF DECEMBER, 2001.

[Signature]  
JOHN CANAS, COUNTY SURVEYOR  
US 4408 EXPIRATION DATE: 09-30-05



COUNTY TREASURER-TAX COLLECTOR'S CERTIFICATE:

STATE OF CALIFORNIA )  
COUNTY OF ORANGE )SS

I HEREBY CERTIFY THAT ACCORDING TO THE RECORDS OF MY OFFICE THERE ARE NO LIENS  
AGAINST THE LAND COVERED BY THIS MAP OR ANY PART THEREOF FOR UNPAID STATE,  
COUNTY, MUNICIPAL OR LOCAL TAXES OR SPECIAL ASSESSMENTS COLLECTED AS TAXES,  
~~EXCEPT TAXES OR SPECIAL ASSESSMENTS COLLECTED AS TAXES NOT YET PAYABLE.~~  
AND DO ALSO HEREBY CERTIFY TO THE RECORDER OF ORANGE COUNTY THAT THE PROVISIONS  
OF THE SUBDIVISION MAP ACT HAVE BEEN COMPLIED WITH REGARDING DEPOSITS TO SECURE  
THE PAYMENT OF TAXES OR SPECIAL ASSESSMENTS COLLECTED AS TAXES ON THE LAND  
COVERED BY THIS MAP.

DATED THIS 30<sup>TH</sup> DAY OF November, 2001.

JOHN M.W. MOORLACH BY: [Signature]  
COUNTY TREASURER-TAX COLLECTOR DEPUTY TREASURER-TAX COLLECTOR

CLERK OF THE BOARD OF SUPERVISORS' CERTIFICATE:

STATE OF CALIFORNIA )  
COUNTY OF ORANGE )SS

I HEREBY CERTIFY THAT THIS MAP WAS PRESENTED FOR APPROVAL TO THE BOARD OF  
SUPERVISORS OF ORANGE COUNTY AT A REGULAR MEETING THEREOF HELD ON THE 18 DAY  
OF December, 2001, AND THAT THEREUPON SAID BOARD DID, BY AN ORDER DULY PASSED  
AND ENTERED, APPROVE SAID MAP AND DID ACCEPT ON BEHALF OF THE PUBLIC, SUBJECT TO  
IMPROVEMENTS; THE DEDICATION FOR STREET PURPOSES OF : SHIVELY ROAD.

AND DID ALSO ACCEPT ON BEHALF OF THE COUNTY OF ORANGE:

1. THE EASEMENT FOR STORM DRAIN PURPOSES AS DEDICATED.

DATED THIS 18 DAY OF December, 2001.

[Signature]  
DARLENE J. BLOOM  
CLERK OF THE BOARD OF SUPERVISORS



SHEET 2 OF 3 SHEETS

## TRACT NO. 16119

ALL OF VESTING TENTATIVE  
TRACT NO. 16119

IN UNINCORPORATED TERRITORY OF ORANGE COUNTY, CALIFORNIA

DATE OF SURVEY:  
DECEMBER 2000

MARCH 2001

JAMES F. GILLEN, L.S. 5557

## HUITT-ZOLIARS

12 NUMBERED LOTS AND LETTERED LOTS A, B, AND C

2.846 ACRES

## STANDARD PACIFIC CORP.

STATE OF CALIFORNIA)  
COUNTY OF ORANGE )

ON THIS 20th DAY OF April, 2001, BEFORE ME,  
Kathleen M. Villari, A NOTARY PUBLIC IN AND FOR SAID STATE,  
PERSONALLY APPEARED Andrew Paine AND  
Gary Hernandez, PERSONALLY KNOWN TO ME OR PROVED TO ME  
ON THE BASIS OF SATISFACTORY EVIDENCE TO BE THE PERSONS WHOSE NAMES  
ARE SUBSCRIBED TO THE WITHIN INSTRUMENT AND ACKNOWLEDGED TO ME THAT  
THEY EXECUTED THE SAME IN THEIR AUTHORIZED CAPACITIES, AND THAT BY THEIR  
SIGNATURES ON THE INSTRUMENT THE PERSONS, OR THE ENTITY UPON BEHALF  
OF WHICH THE PERSONS ACTED, EXECUTED THE INSTRUMENT.

WITNESS MY HAND: MY COMMISSION EXPIRES 8-10-2003  
Kathleen M. Villari MY PRINCIPAL PLACE OF BUSINESS  
NOTARY PUBLIC IN AND FOR SAID STATE IS IN Orange COUNTY.

KATHLEEN M. VILLARI  
PRINT NAME

## DMB LADERA, L.L.C.

STATE OF CALIFORNIA)  
COUNTY OF ORANGE )

ON THIS 2nd DAY OF May, 2001, BEFORE ME,  
Tina T. Baker, A NOTARY PUBLIC IN AND FOR SAID STATE,  
PERSONALLY APPEARED Paul Johnson AND  
Stephen C. Schuch, PERSONALLY KNOWN TO ME OR PROVED TO ME  
ON THE BASIS OF SATISFACTORY EVIDENCE TO BE THE PERSONS WHOSE NAMES  
ARE SUBSCRIBED TO THE WITHIN INSTRUMENT AND ACKNOWLEDGED TO ME THAT  
THEY EXECUTED THE SAME IN THEIR AUTHORIZED CAPACITIES, AND THAT BY THEIR  
SIGNATURES ON THE INSTRUMENT THE PERSONS, OR THE ENTITY UPON BEHALF  
OF WHICH THE PERSONS ACTED, EXECUTED THE INSTRUMENT.

WITNESS MY HAND: MY COMMISSION EXPIRES 8-29-04  
Tina T. Baker MY PRINCIPAL PLACE OF BUSINESS  
NOTARY PUBLIC IN AND FOR SAID STATE IS IN Orange COUNTY.

Tina T. Baker  
PRINT NAME

## SANTA MARGARITA WATER DISTRICT

STATE OF CALIFORNIA)  
COUNTY OF ORANGE )

ON THIS 13th DAY OF SEPTEMBER, 2001, BEFORE ME,  
Andrea M. Evans, A NOTARY PUBLIC IN AND FOR SAID STATE,  
PERSONALLY APPEARED DANIEL R. FERONS PERSONALLY KNOWN TO ME  
OR PROVED TO ME ON THE BASIS OF SATISFACTORY EVIDENCE TO BE THE  
PERSON WHOSE NAME IS SUBSCRIBED TO THE WITHIN INSTRUMENT AND ACKNOWLEDGED  
TO ME THAT HE EXECUTED THE SAME IN HIS AUTHORIZED CAPACITY, AND THAT  
BY HIS SIGNATURE ON THE INSTRUMENT THE PERSON, OR THE ENTITY UPON BEHALF  
OF WHICH THE PERSON ACTED, EXECUTED THE INSTRUMENT.

WITNESS MY HAND: MY COMMISSION EXPIRES April 8, 2004  
Andrea M. Evans MY PRINCIPAL PLACE OF BUSINESS  
NOTARY PUBLIC IN AND FOR SAID STATE IS IN ORANGE COUNTY.

ANDREA M. EVANS  
PRINT NAME

## MONUMENT NOTES:

- ▲ INDICATES FOUND 2" I.P. TAGGED "P.L.S. 5557" PER TRACT NO. 16156, M.M. 812/40-48
- INDICATES LOCATION OF 1" I.P. TAGGED "P.L.S. 5557" OR SPIKE & WASHER  
STAMPED "P.L.S. 5557" OR LEAD, TACK & TAG "P.L.S. 5557" TO BE SET PER  
TRACT NO. 16156, M.M. 812/40-48.
- INDICATES LOCATION OF 1" I.P. TAGGED "P.L.S. 5557" OR SPIKE & WASHER  
STAMPED "P.L.S. 5557" OR LEAD, TACK & TAG "P.L.S. 5557" TO BE SET WITHIN  
90 DAYS AFTER ACCEPTANCE OF IMPROVEMENTS.
- 1" I.P. TAGGED "P.L.S. 5557" OR SPIKE & WASHER STAMPED "P.L.S. 5557" OR LEAD,  
TACK AND TAG "P.L.S. 5557" TO BE SET AT ALL INTERIOR LOT CORNERS, FOR LOTS 1  
THROUGH 12, EXCEPT LOT CORNERS ABUTTING STREETS; LEAD, TACK & TAG "P.L.S. 5557"  
TO BE SET IN TOP OF CURB OR SIDEWALK ON 9.75' OFFSET ON SIDE LOT LINES PRODUCED  
FOR LOT CORNERS ABUTTING STREETS, WITHIN 90 DAYS AFTER ACCEPTANCE OF IMPROVEMENTS,  
UNLESS OTHERWISE NOTED.

NO MONUMENTATION TO BE SET AT BC'S AND EC'S OF STREET RIGHT OF WAY LINES,  
UNLESS OTHERWISE NOTED.


## SIGNATURE OMISSIONS:

IN ACCORDANCE WITH THE PROVISIONS OF SECTION 66436(a) (3) OF THE SUBDIVISION  
MAP ACT, THE FOLLOWING SIGNATURE HAS BEEN OMITTED:

1. LADERA DEVELOPMENT COMPANY, L.L.C., HOLDER OF OIL, GAS, MINERAL, AND WATER RIGHTS  
RECORDED DECEMBER 10, 1996 AS INSTRUMENT NO. 19960624029 OF OFFICIAL RECORDS.
2. DMB LADERA, L.L.C., A DELAWARE LIMITED LIABILITY COMPANY, HOLDER OF EASEMENTS  
RECORDED FEBRUARY 15, 2001 AS INSTRUMENT NO. 20010084586 OF OFFICIAL RECORDS.

## BASIS OF BEARINGS:

BEARINGS SHOWN HEREON ARE BASED ON THE SOUTHERLY LINE OF LOT 4, BEING N78°13'23"E AS  
SHOWN ON TRACT NO. 16156, FILED IN BOOK 812, PAGES 40 THROUGH 48 OF MISCELLANEOUS MAPS,  
RECORDS OF ORANGE COUNTY, CALIFORNIA.

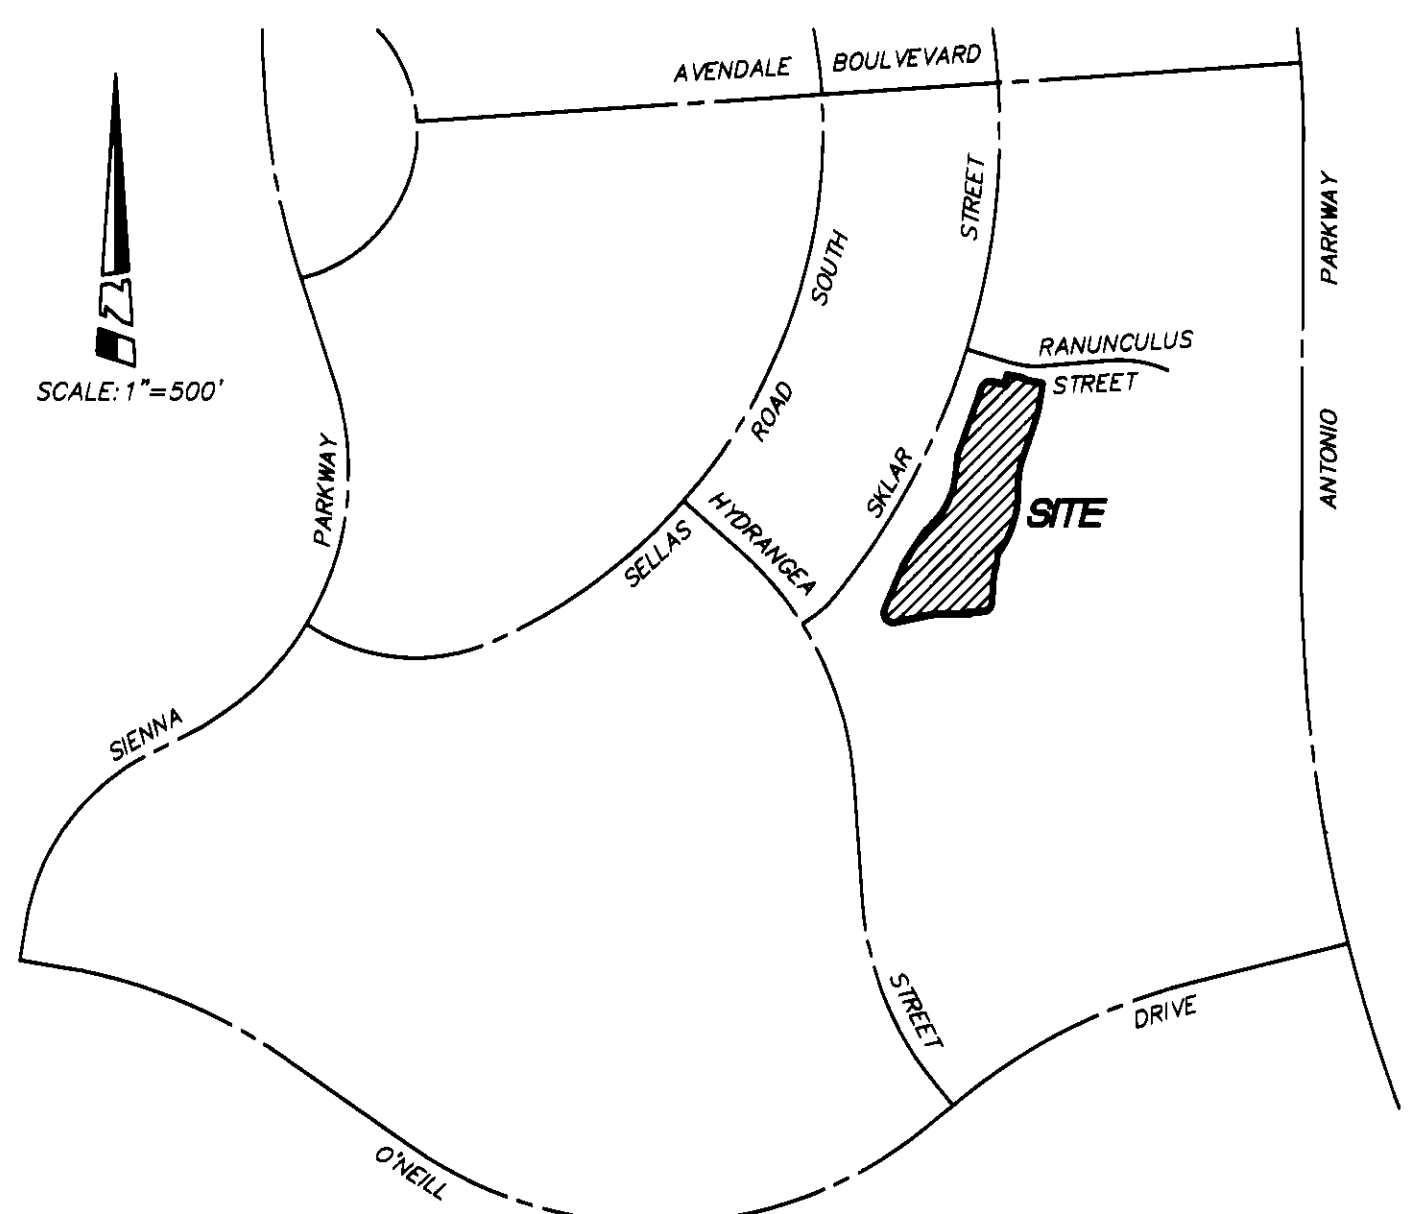

VICINITY MAP

SHEET 3 OF 3 SHEETS

# TRACT NO. 16119

ALL OF VESTING TENTATIVE  
TRACT NO. 16119

IN UNINCORPORATED TERRITORY OF ORANGE COUNTY, CALIFORNIA

DATE OF SURVEY:  
DECEMBER 2000


MARCH 2001

JAMES F. GILLEN, L.S. 5557

## HUITT-ZOLIARS

12 NUMBERED LOTS AND LOTS A, B AND C

2.846 ACRES

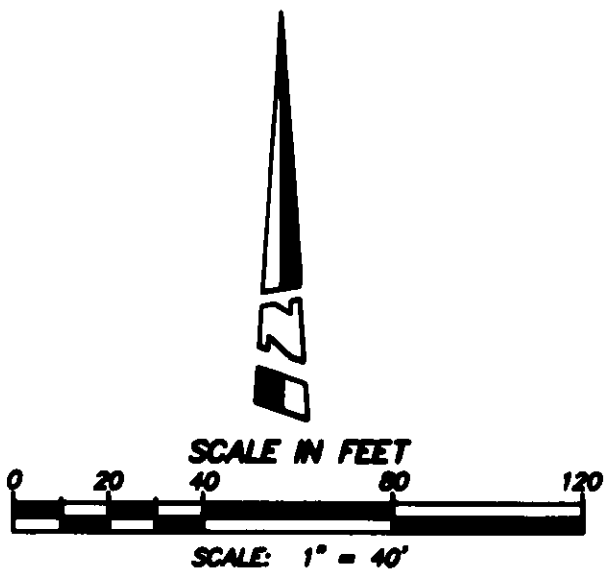

### EASEMENT NOTES:

- (A) INDICATES EASEMENT FOR STORM DRAIN PURPOSES DEDICATED TO THE COUNTY OF ORANGE.
- (B) INDICATES EASEMENT FOR SEWER, WATER, AND ACCESS PURPOSES DEDICATED TO THE SANTA MARGARITA WATER DISTRICT.

### NOTES:

SEE SHEET 2 FOR MONUMENT NOTES AND BASIS OF BEARINGS.

LOT A IS FOR POCKET PARK PURPOSES

LOTS B AND C ARE FOR LANDSCAPING AND OPEN SPACE AND ARE NOT SEPARATE BUILDING SITES.

### COURSE DATA

- 1 N62°00'38"W 15.99'
- 2 N27°35'08"E RAD 18.05'
- 3 N39°56'26"E RAD 19.39'
- 4 N34°55'22"W RAD 22.80'
- 5 N9°58'42"E 10.27'
- 6 N5°32'32"E RAD
- 7 N80°12'37"W 9.50'
- 8 N73°25'00"W 9.85'
- 9 N73°25'00"W 13.00'
- 10 N73°25'00"W 13.75'
- 11 N73°25'00"W 9.88'
- 12 N73°25'00"W 10.55'
- 13 N73°25'00"W 10.79'
- 14 N73°25'00"W 13.42'
- 15 N85°19'43"W 9.95'

### CURVE DATA

- 1 Δ = 09°07'21" R = 226.00' L = 35.98'
- 2 Δ = 06°08'24" R = 226.00' L = 24.22'
- 3 Δ = 02°58'57" R = 226.00' L = 11.76'
- 4 Δ = 82°22'21" R = 18.00' L = 25.88'
- 5 Δ = 00°47'35" R = 226.00' L = 3.13'
- 6 Δ = 04°51'40" R = 268.00' L = 22.73'
- 7 Δ = 51°38'21" R = 48.00' L = 43.26'
- 8 Δ = 74°51'48" R = 48.00' L = 62.72'
- 9 Δ = 38°16'57" R = 18.00' L = 12.03'
- 10 Δ = 34°23'54" R = 48.00' L = 28.82'
- 11 Δ = 9°40'51" R = 282.00' L = 47.65'
- 12 Δ = 1°37'19" R = 282.00' L = 7.99'
- 13 Δ = 8°03'32" R = 282.00' L = 39.66'

