

SHEET 1 OF 4 SHEETS  
29 NUMBERED LOTS AND 5  
LETTERED LOTS  
6.876 ACRES GROSS  
ALL OF T.T.M. 16120  
BLOCK 5157  
MODULE 19

# TRACT MAP NO. 16120

IN UNINCORPORATED TERRITORY OF ORANGE COUNTY  
STATE OF CALIFORNIA

BEING A SUBDIVISION OF LOT 5 OF TRACT NO. 16156 AS SHOWN ON A MAP THEREOF  
FILED IN BOOK 812 PAGES 40 THROUGH 48 OF MISCELLANEOUS MAPS, IN THE OFFICE  
OF THE COUNTY RECORDER OF SAID ORANGE COUNTY

DAVID EVANS AND ASSOCIATES, INC.  
CHARLES J. PRIOLO, R.C.E. #30790 FEBRUARY 2001

ACCEPTED AND FILED AT THE  
REQUEST OF

FIRST AMERICAN TITLE INSURANCE COMPANY

DATE OCTOBER 12, 2001  
TIME 11:08 A.M. FEES \$18.00  
INSTRUMENT #  
BOOK 822 PAGE 40-48 N/M

GARY L. GRANVILLE  
COUNTY CLERK-RECORDER

BY [Signature]  
DEPUTY

## OWNERSHIP CERTIFICATE:

WE, THE UNDERSIGNED, BEING ALL PARTIES HAVING ANY RECORD TITLE INTEREST IN  
THE LAND COVERED BY THIS MAP, DO HEREBY CONSENT TO THE PREPARATION  
AND RECORDATION OF SAID MAP, AS SHOWN WITHIN THE DISTINCTIVE BORDER LINE.

WE ALSO HEREBY DEDICATE TO THE PUBLIC FOR STREET PURPOSES RANUNCULUS  
STREET AND LANGFORD LANE.

WE ALSO HEREBY DEDICATE TO THE COUNTY OF ORANGE THE EASEMENT  
FOR STORM DRAIN PURPOSES AS SHOWN ON SAID MAP.

WE ALSO HEREBY DEDICATE TO THE SANTA MARGARITA WATER DISTRICT THE  
EASEMENTS FOR SEWER, WATER AND ACCESS PURPOSES AS SHOWN ON SAID MAP,  
WHICH EASEMENTS SHALL BE SUBJECT TO THE SAME TERMS AND CONDITIONS AS  
ARE SHOWN IN THAT CERTAIN EASEMENT RECORDED OCTOBER 6, 1980 IN BOOK  
13776, PAGE 341, OF OFFICIAL RECORDS, COUNTY OF ORANGE. THE SANTA  
MARGARITA WATER DISTRICT SHALL RESTORE OTHER IMPROVEMENTS OR FACILITIES  
LOCATED WITHIN THE EASEMENT, IF IT HAS CONSENTED TO THE LOCATION OF SUCH  
IMPROVEMENTS OR FACILITIES TO THE EXTENT THAT THE EXERCISE OF ITS RIGHTS  
IN CONNECTION WITH THE EASEMENT IMPACTS OTHER IMPROVEMENTS OR FACILITIES  
LOCATED WITHIN THE EASEMENT, HOWEVER, IN NO EVENT SHALL SANTA MARGARITA  
WATER DISTRICT BE RESPONSIBLE FOR THE COST OF RELOCATING ITS FACILITIES  
IN THE EVENT OF CONFLICTS WITH SUCH OTHER IMPROVEMENTS OR FACILITIES.

W. L. HOMES L.L.C. DBA JOHN LAING HOMES (CALIFORNIA), A DELAWARE LIMITED  
LIABILITY COMPANY.

BY: Wayne J. Stelmar  
PRINT NAME: WAYNE STELMAR  
PRINT TITLE: Division President

BY: [Signature]  
PRINT NAME: DAVID DIRIENZO  
PRINT TITLE: VICE PRESIDENT LAND DEVELOPMENT

DMB LADERA, L.L.C., A DELAWARE LIMITED LIABILITY COMPANY,  
BENEFICIARY UNDER DEEDS OF TRUSTS RECORDED MARCH 16, 2001 AS  
INSTRUMENT NO. 20010154668 AND RECORDED APRIL 12, 2001 AS INSTRUMENT  
NO. 20010220692, BOTH OF OFFICIAL RECORDS.

BY: [Signature]  
AS AGENT AND/OR MANAGER.

BY: [Signature]  
PRINT NAME: DONALD T. STALLIN  
PRINT TITLE: DIRECTOR OF COMMUNITY DEVELOPMENT

BY: [Signature]  
PRINT NAME: Stephen C. Schenk  
PRINT TITLE: Exec. Vice President Development

WASHINGTON MUTUAL BANK, FA, A FEDERAL ASSOCIATION,  
BENEFICIARY UNDER DEED OF TRUSTS RECORDED MARCH 16, 2001 AS  
INSTRUMENT NO. 20010154669, OF OFFICIAL RECORDS

BY: [Signature]  
PRINT NAME: TOM GRIFFIN  
PRINT TITLE: SENIOR VICE PRESIDENT

BY: [Signature]  
PRINT NAME: KRIS KLINGER  
PRINT TITLE: VICE PRESIDENT

## CERTIFICATE OF ACCEPTANCE:

THE UNDERSIGNED, BEING THE DULY APPOINTED AGENT OF THE SANTA MARGARITA  
WATER DISTRICT, A PUBLIC CORPORATION OF ORANGE COUNTY, CALIFORNIA,  
PURSUANT TO ITS RESOLUTION NO. 88-10-2, DOES HEREBY ACCEPT ON BEHALF  
OF SAID DISTRICT THE EASEMENTS FOR SEWER, WATER, AND ACCESS PURPOSES,  
AS DEDICATED AND AS SHOWN ON THIS TRACT MAP, BY AND BETWEEN THE SANTA  
MARGARITA WATER DISTRICT AND W. L. HOMES, L.L.C., AND DOES HEREBY CERTIFY  
THAT THE GRANTEE CONSENTS TO THE RECORDATION OF SAID TRACT.

[Signature]  
DANIEL R. FERONS, CHIEF ENGINEER  
SANTA MARGARITA WATER DISTRICT.

## AUTOMATIC FIRE SPRINKLER NOTE:

ALL COMMERCIAL STRUCTURES GREATER THAN 6,000 SQUARE FEET; ALL  
MULTIFAMILY RESIDENTIAL STRUCTURES; ALL SINGLE-FAMILY STRUCTURES EXCEEDING  
5,500 SQUARE FEET, AND ALL STRUCTURES EXCEEDING FIRE DEPARTMENT ACCESS  
REQUIREMENTS SHALL BE PROTECTED BY AN AUTOMATIC SPRINKLER SYSTEM.

## SPECIAL FIRE PROTECTION NOTE:

PROPERTY IS TOTALLY EXCLUDED FROM A SPECIAL FIRE PROTECTION AREA.

## HIGH FIRE HAZARD AREA NOTE:

THE LOTS SHOWN ON THIS MAP ARE IN A HIGH FIRE HAZARD AREA DUE TO WILD  
LAND EXPOSURE.

NOTE:  
SEE SHEET 2 FOR NOTARY ACKNOWLEDGEMENTS AND SIGNATURE OMISSIONS.

## ENGINEER'S STATEMENT

I HEREBY STATE THAT THIS MAP CONSISTING OF 4 SHEETS, CORRECTLY  
REPRESENTS TRUE AND COMPLETE SURVEY AS SHOWN MADE IN FEBRUARY, 2001;  
WAS MADE BY ME OR UNDER MY DIRECTION; THAT THE MONUMENTS ARE OF THE  
CHARACTER AND OCCUPY (OR WILL OCCUPY) THE POSITIONS INDICATED BY SAID  
MAP; AND THAT SAID MONUMENTS ARE SUFFICIENT TO ENABLE THE SURVEY TO BE  
RETRACED.

[Signature] 7/23/01  
CHARLES J. PRIOLO, R.C.E. #30790  
LICENSE EXPIRES: 3/31/2004



## COUNTY SURVEYOR'S STATEMENT

I HEREBY STATE THAT I HAVE EXAMINED THIS MAP AND HAVE FOUND IT TO BE  
SUBSTANTIALLY IN CONFORMANCE WITH THE TENTATIVE MAP AS FILED WITH,  
AMENDED AND APPROVED BY THE ORANGE COUNTY SUBDIVISION COMMITTEE; THAT  
ALL PROVISIONS OF THE SUBDIVISION MAP ACT AND COUNTY SUBDIVISION  
REGULATIONS HAVE BEEN COMPLIED WITH AND I AM SATISFIED SAID MAP IS  
TECHNICALLY CORRECT.

DATED THIS 20TH DAY OF SEP, 2001.

[Signature]  
JOHN CANAS, COUNTY SURVEYOR  
LE 4408 EXPIRATION DATE: 9-30-01



## COUNTY TREASURER-TAX COLLECTOR'S CERTIFICATE:

STATE OF CALIFORNIA )  
COUNTY OF ORANGE ) SS

I HEREBY CERTIFY THAT ACCORDING TO THE RECORDS OF MY OFFICE THERE ARE  
NO LIENS AGAINST THE LAND COVERED BY THIS MAP OR ANY PART THEREOF FOR  
UNPAID STATE COUNTY, MUNICIPAL OR LOCAL TAXES OR SPECIAL ASSESSMENTS  
COLLECTED AS TAXES, EXCEPT TAXES OR SPECIAL ASSESSMENTS COLLECTED AS  
TAXES NOT YET PAYABLE.  
AND DO CERTIFY TO THE RECORDER OF ORANGE COUNTY THAT THE PROVISIONS  
OF THE SUBDIVISION MAP ACT HAVE BEEN COMPLIED WITH REGARDING DEPOSITS  
TO SECURE PAYMENT OF TAXES OR SPECIAL ASSESSMENTS COLLECTED AS TAXES  
ON THE LAND COVERED BY THIS MAP.

DATED THIS 14TH DAY OF August, 2001.

JOHN M. W. MOORLACH BY: [Signature]  
COUNTY TREASURER-TAX COLLECTOR DEPUTY TREASURER-TAX COLLECTOR

## CLERK OF THE BOARD OF SUPERVISORS' CERTIFICATE

STATE OF CALIFORNIA )  
COUNTY OF ORANGE ) SS

I HEREBY CERTIFY THAT THIS MAP WAS PRESENTED FOR APPROVAL TO THE BOARD  
OF SUPERVISORS OF ORANGE COUNTY AT A REGULAR MEETING THEREOF HELD ON  
THE 2nd DAY OF October, 2001 AND THAT  
THEREUPON SAID BOARD DID, BY AN ORDER DULY PASSED AND ENTERED,  
APPROVE SAID MAP AND DID ACCEPT ON BEHALF OF THE PUBLIC, SUBJECT TO  
IMPROVEMENTS; THE DEDICATION FOR STREET PURPOSES OF RANUNCULUS STREET  
AND LANGFORD LANE.

AND DID ALSO ACCEPT ON BEHALF OF THE COUNTY OF ORANGE THE EASEMENT  
FOR STORM DRAIN PURPOSES AS DEDICATED.

AND DID ALSO APPROVE SUBJECT MAP PURSUANT TO THE PROVISIONS OF SECTION  
66436(a)(3)(A) OF THE SUBDIVISION MAP ACT.

DATED THIS 2nd DAY OF October, 2001.

[Signature]  
DARLENE J. BLOOM  
CLERK OF THE BOARD OF SUPERVISORS



SHEET 2 OF 4 SHEETS  
29 NUMBERED LOTS AND 5  
LETTERED LOTS  
6.876 ACRES GROSS  
ALL OF T.T.M. 16120

# TRACT MAP NO. 16120

IN UNINCORPORATED TERRITORY OF ORANGE COUNTY  
STATE OF CALIFORNIA  
DAVID EVANS AND ASSOCIATES, INC.  
CHARLES J. PRIOLO, R.C.E. #30790 FEBRUARY 2001

## NOTARY ACKNOWLEDGEMENT

W.L. HOMES, L.L.C.

STATE OF CALIFORNIA)  
PERSONALLY APPEARED )SS  
COUNTY OF ORANGE )

ON THIS 24<sup>th</sup> DAY OF July, 2001, BEFORE ME,  
KATHLEEN A. HOYT A NOTARY PUBLIC IN AND FOR SAID STATE,  
PERSONALLY APPEARED Wayne J. Stalmar AND  
PERSONALLY KNOWN TO ME (OR  
PROVED TO ME ON THE BASIS OF SATISFACTORY EVIDENCE) TO BE THE PERSONS  
WHOSE NAMES ARE SUBSCRIBED TO THE WITHIN INSTRUMENT AND ACKNOWLEDGED  
TO ME THAT HE/SHE/they EXECUTED THE SAME IN HIS/HER/their AUTHORIZED  
CAPACITIES, AND THAT BY HIS/HER/their SIGNATURES ON THE INSTRUMENT THE  
PERSONS, OR THE ENTITY UPON BEHALF OF WHICH THE PERSON ACTED, EXECUTED  
THE INSTRUMENT.

WITNESS MY HAND: MY COMMISSION EXPIRES: Aug 15, 2001

Kathleen A. Hoyt MY PRINCIPAL PLACE OF BUSINESS  
NOTARY PUBLIC IN AND FOR SAID STATE IS IN Orange COUNTY.  
KATHLEEN A. HOYT  
PRINT NAME

## NOTARY ACKNOWLEDGEMENT

W.L. HOMES, L.L.C.

STATE OF CALIFORNIA)  
PERSONALLY APPEARED )SS  
COUNTY OF ORANGE )

ON THIS 24<sup>th</sup> DAY OF July, 2001, BEFORE ME,  
Amy Day A NOTARY PUBLIC IN AND FOR SAID STATE,  
PERSONALLY APPEARED David Dierenz AND  
PERSONALLY KNOWN TO ME (OR  
PROVED TO ME ON THE BASIS OF SATISFACTORY EVIDENCE) TO BE THE PERSONS  
WHOSE NAMES ARE SUBSCRIBED TO THE WITHIN INSTRUMENT AND ACKNOWLEDGED  
TO ME THAT HE/SHE/they EXECUTED THE SAME IN HIS/HER/their AUTHORIZED  
CAPACITIES, AND THAT BY HIS/HER/their SIGNATURES ON THE INSTRUMENT THE  
PERSONS, OR THE ENTITY UPON BEHALF OF WHICH THE PERSON ACTED, EXECUTED  
THE INSTRUMENT.

WITNESS MY HAND: MY COMMISSION EXPIRES: 10-14-01

Amy Day MY PRINCIPAL PLACE OF BUSINESS  
NOTARY PUBLIC IN AND FOR SAID STATE IS IN Orange COUNTY.  
Amy Day  
PRINT NAME

## NOTARY ACKNOWLEDGEMENT

DMB LADERA, L.L.C.

STATE OF CALIFORNIA)  
PERSONALLY APPEARED )SS  
COUNTY OF ORANGE )

ON THIS \_\_\_\_\_ DAY OF \_\_\_\_\_, 2001, BEFORE ME,  
\_\_\_\_\_ A NOTARY PUBLIC IN AND FOR SAID STATE,  
PERSONALLY APPEARED \_\_\_\_\_ AND  
PERSONALLY KNOWN TO ME (OR  
PROVED TO ME ON THE BASIS OF SATISFACTORY EVIDENCE) TO BE THE PERSONS  
WHOSE NAMES ARE SUBSCRIBED TO THE WITHIN INSTRUMENT AND ACKNOWLEDGED  
TO ME THAT HE/SHE/they EXECUTED THE SAME IN HIS/HER/their AUTHORIZED  
CAPACITIES, AND THAT BY HIS/HER/their SIGNATURES ON THE INSTRUMENT THE  
PERSONS, OR THE ENTITY UPON BEHALF OF WHICH THE PERSON ACTED, EXECUTED  
THE INSTRUMENT.

WITNESS MY HAND: MY COMMISSION EXPIRES: \_\_\_\_\_

\_\_\_\_\_ MY PRINCIPAL PLACE OF BUSINESS  
NOTARY PUBLIC IN AND FOR SAID STATE IS IN \_\_\_\_\_ COUNTY.

PRINT NAME

## NOTARY ACKNOWLEDGEMENT

DMB LADERA, L.L.C.

STATE OF CALIFORNIA)  
PERSONALLY APPEARED )SS  
COUNTY OF ORANGE )

ON THIS 31<sup>st</sup> DAY OF July, 2001, BEFORE ME,  
Tina T. Baker A NOTARY PUBLIC IN AND FOR SAID STATE,  
PERSONALLY APPEARED Donald T. Stahl AND  
Stephen C. Schenk PERSONALLY KNOWN TO ME (OR  
PROVED TO ME ON THE BASIS OF SATISFACTORY EVIDENCE) TO BE THE PERSONS  
WHOSE NAMES ARE SUBSCRIBED TO THE WITHIN INSTRUMENT AND ACKNOWLEDGED  
TO ME THAT HE/SHE/they EXECUTED THE SAME IN HIS/HER/their AUTHORIZED  
CAPACITIES, AND THAT BY HIS/HER/their SIGNATURES ON THE INSTRUMENT THE  
PERSONS, OR THE ENTITY UPON BEHALF OF WHICH THE PERSON ACTED, EXECUTED  
THE INSTRUMENT.

WITNESS MY HAND: MY COMMISSION EXPIRES: 8/29/04

Tina T. Baker MY PRINCIPAL PLACE OF BUSINESS  
NOTARY PUBLIC IN AND FOR SAID STATE IS IN Orange COUNTY.  
Tina T. Baker  
PRINT NAME

## SIGNATURE OMISSIONS:

IN ACCORDANCE WITH THE PROVISIONS OF SECTION 66436(a)(3)(A) OF THE  
SUBDIVISION MAP ACT, THE FOLLOWING SIGNATURE HAS BEEN OMITTED:

1. LADERA DEVELOPMENT COMPANY, L.L.C., HOLDER OF OIL, GAS, MINERAL, AND  
WATER RIGHTS RECORDED DECEMBER 10, 1996 AS INSTRUMENT NO. 19960624029  
OF OFFICIAL RECORDS.

## NOTARY ACKNOWLEDGEMENT

WASHINGTON MUTUAL BANK

STATE OF CALIFORNIA)  
PERSONALLY APPEARED )SS  
COUNTY OF ORANGE )

ON THIS 2<sup>nd</sup> DAY OF August, 2001, BEFORE ME,  
Terri L. Castellanos A NOTARY PUBLIC IN AND FOR SAID STATE,  
PERSONALLY APPEARED Kris Ringer PERSONALLY KNOWN TO  
ME (OR PROVED TO ME ON THE BASIS OF SATISFACTORY EVIDENCE) TO BE THE  
PERSONS WHOSE NAMES ARE SUBSCRIBED TO THE WITHIN INSTRUMENT AND  
ACKNOWLEDGED TO ME THAT HE/SHE/they EXECUTED THE SAME IN  
HIS/HER/their AUTHORIZED CAPACITIES, AND THAT BY HIS/HER/their SIGNATURES  
ON THE INSTRUMENT THE PERSONS, OR THE ENTITY UPON BEHALF OF WHICH THE  
PERSON ACTED, EXECUTED THE INSTRUMENT.

WITNESS MY HAND: MY COMMISSION EXPIRES: 1-2-04

Terri L. Castellanos MY PRINCIPAL PLACE OF BUSINESS  
NOTARY PUBLIC IN AND FOR SAID STATE IS IN San Diego COUNTY.  
Terri L. Castellanos  
PRINT NAME

## NOTARY ACKNOWLEDGEMENT

WASHINGTON MUTUAL BANK

STATE OF CALIFORNIA)  
PERSONALLY APPEARED )SS  
COUNTY OF ORANGE )

ON THIS 6<sup>th</sup> DAY OF August, 2001, BEFORE ME,  
Terri L. Castellanos A NOTARY PUBLIC IN AND FOR SAID STATE,  
PERSONALLY APPEARED Tom Griffin PERSONALLY KNOWN TO  
ME (OR PROVED TO ME ON THE BASIS OF SATISFACTORY EVIDENCE) TO BE THE  
PERSONS WHOSE NAMES ARE SUBSCRIBED TO THE WITHIN INSTRUMENT AND  
ACKNOWLEDGED TO ME THAT HE/SHE/they EXECUTED THE SAME IN  
HIS/HER/their AUTHORIZED CAPACITIES, AND THAT BY HIS/HER/their SIGNATURES  
ON THE INSTRUMENT THE PERSONS, OR THE ENTITY UPON BEHALF OF WHICH THE  
PERSON ACTED, EXECUTED THE INSTRUMENT.

WITNESS MY HAND: MY COMMISSION EXPIRES: 1-2-04

Terri L. Castellanos MY PRINCIPAL PLACE OF BUSINESS  
NOTARY PUBLIC IN AND FOR SAID STATE IS IN San Diego COUNTY.  
Terri L. Castellanos  
PRINT NAME

## NOTARY ACKNOWLEDGEMENT

SANTA MARGARITA WATER DISTRICT

STATE OF CALIFORNIA)  
PERSONALLY APPEARED )SS  
COUNTY OF ORANGE )

ON THIS 10<sup>th</sup> DAY OF August, 2001, BEFORE ME,  
ANDREA M. EVANS A NOTARY PUBLIC IN AND FOR SAID STATE,  
PERSONALLY APPEARED DANIEL R. FERONS PERSONALLY KNOWN TO ME (OR  
PROVED TO ME ON THE BASIS OF SATISFACTORY EVIDENCE) TO BE THE PERSONS  
WHOSE NAMES ARE SUBSCRIBED TO THE WITHIN INSTRUMENT AND ACKNOWLEDGED  
TO ME THAT HE/SHE/they EXECUTED THE SAME IN HIS/HER/their AUTHORIZED  
CAPACITIES, AND THAT BY HIS/HER/their SIGNATURES ON THE INSTRUMENT THE  
PERSONS, OR THE ENTITY UPON BEHALF OF WHICH THE PERSON ACTED, EXECUTED  
THE INSTRUMENT.

WITNESS MY HAND: MY COMMISSION EXPIRES: 04-08-04

Andrea M. Evans MY PRINCIPAL PLACE OF BUSINESS  
NOTARY PUBLIC IN AND FOR SAID STATE IS IN ORANGE COUNTY.  
ANDREA M. EVANS  
PRINT NAME



SHEET 3 OF 4 SHEETS  
28 NUMBERED LOTS AND 5  
LETTERED LOTS  
6.876 ACRES GROSS  
ALL OF T.T.M. 16120

# TRACT MAP NO. 16120

IN UNINCORPORATED TERRITORY OF ORANGE COUNTY  
STATE OF CALIFORNIA

DAVID EVANS AND ASSOCIATES, INC.

CHARLES J. PRIOLO, R.C.E. #30790 FEBRUARY 2001

### GPS POINT LOCATION

GPS NO. 1417 2 1/2 IRON PIPE W/2" BRASS CAP STAMPED "GPS 1417  
N 2141450.558 9-95" PER TR. 16156 M.M. 812/40-48 AND RECORDS ON  
E 6141583.535 FILE IN THE ORANGE COUNTY SURVEYOR OFFICE

GPS NO. 1448 2 1/2 IRON PIPE W/2" OCS BRASS CAP STAMPED "GPS 1448  
N 2146790.819 9-95" PER TR. 16156 M.M. 812/40-48 AND RECORDS ON FILE  
E 6142602.585 IN THE ORANGE COUNTY SURVEYOR OFFICE

### BASIS OF BEARINGS

THE BEARINGS SHOWN HEREON ARE BASED UPON THE BEARING BETWEEN O.C.S.  
HORIZONTAL CONTROL STATION GPS NO. 1417 AND STATION GPS NO. 1448 BEING  
N10°48'13"E PER RECORDS ON FILE IN THE OFFICE OF THE ORANGE COUNTY RECORDER

### DATUM STATEMENT

COORDINATES SHOWN ARE BASED ON CALIFORNIA COORDINATE SYSTEM, (CCS83) ZONE  
VI, 1983 NAD, (1991.35 EPOCH OCS GPS ADJUSTMENT)

ALL DISTANCES SHOWN ARE GROUND, UNLESS OTHERWISE NOTED. TO OBTAIN GRID  
DISTANCES MULTIPLY GROUND DISTANCE BY 0.99993286

### MONUMENT NOTES


- ALL MONUMENTS SHOWN AS SET WILL BE SET WITHIN 90 DAYS AFTER THE ACCEPTANCE  
OF IMPROVEMENTS EXCEPT AS NOTED.
- TIES TO CENTERLINE MONUMENTS WILL BE MADE AND A COPY OF SAID TIES WILL BE  
FURNISHED TO THE COUNTY SURVEYOR.
- SET 1" IRON PIPE TAGGED "R.C.E. LS 30790" AT ALL LOT CORNERS EXCEPT LOT CORNERS  
THAT ABUT A STREET WHICH WILL BE MARKED ON AN 9.75' OR 10.75' OR 15.75' OFFSET  
INSIDE STREET RIGHT-OF-WAY IN CONCRETE CURB BY A LEAD, TACK AND TAG "R.C.E.  
30790" ON SIDELINES PRODUCED, UNLESS OTHERWISE NOTED. MONUMENTS FOR ALL LOT  
CORNERS THAT ABUT RANUNCULUS STREET WILL BE SET ON AN 10.75' OFFSET.  
MONUMENTS FOR ALL LOT CORNERS THAT ABUT LANGFORD LANE WILL BE SET ON AN  
9.75' OFFSET, EXCEPT COMMON CORNERS FOR LOTS 3, 4 AND 18, 19, WHICH WILL BE  
SET ON AN 15.75' OFFSET. (NO MONUMENTS WILL BE SET FOR ANGLE POINTS, CORNER  
CUTOFFS, B.C. E.C. P.C.C. OR P.R.C. THAT ABUT A STREET WHICH ARE NOT LOT CORNERS  
MARKING SIDELINES, UNLESS OTHERWISE NOTED).
- SET 2" IRON PIPE TAGGED "R.C.E. 30790" OR A SPIKE W/BRASS WASHER STAMPED  
"R.C.E. 30790" IN ASPHALT HAVING A THICKNESS OF 2" OR MORE AT ALL TRACT  
BOUNDARY CORNERS, EXCEPT BOUNDARY CORNERS THAT ABUT A STREET WHICH WILL BE  
MARKED ON AN OFFSET INSIDE THE STREET RIGHT-OF-WAY IN CONCRETE CURB BY A  
LEAD, TACK AND TAG "R.C.E. 30790" ON EITHER A RADIAL OR PERPENDICULAR LINE TO  
STREET CENTERLINE, UNLESS OTHERWISE NOTED. (NO MONUMENTS WILL BE SET FOR ANGLE  
POINTS, CORNER CUTOFF, B.C. E.C. P.C.C. OR P.R.C. THAT ABUT A STREET WHICH ARE  
NOT BOUNDARY CORNERS, UNLESS OTHERWISE NOTED).
- SET LEAD, TACK AND TAG "R.C.E. 30790" IN CONCRETE OR A SPIKE W/BRASS WASHER  
STAMPED "R.C.E. 30790" AT ALL STREET CENTERLINE POINTS OF CONTROL, UNLESS  
OTHERWISE NOTED.
- ▲ INDICATES FOUND MONUMENTS AS NOTED
- INDICATES 2" I.P. TAGGED "P.L.S. 5557" OR SPIKE & WASHER STAMPED  
"P.L.S. 5557" OR LEAD, TACK & TAG "P.L.S. 5557" TO BE SET PER  
TRACT NO. 16156, M.M. 812/40-48.
- INDICATES SPIKE & WASHER STAMPED "P.L.S. 5557" TO BE SET PER TRACT NO.  
16156, M.M. 812/40-48.
- INDICATES 2" I.P. WITH 3/8" BRASS DISK SET IN CONCRETE, STAMPED "R.C.E. 30790"  
PRIOR TO RECORDATION.

### EASEMENT NOTES:

- (A) INDICATES 40' WIDE EASEMENT FOR SEWER, WATER AND ACCESS  
PURPOSES DEDICATED HEREON TO THE SANTA MARGARITA WATER DISTRICT.
- (B) INDICATES 40' WIDE EASEMENT FOR STORM DRAIN  
PURPOSES DEDICATED HEREON TO THE COUNTY OF ORANGE.
- (C) INDICATES 40' WIDE EXISTING EASEMENT FOR SEWER, WATER AND ACCESS  
PURPOSES DEDICATED PER TRACT NO. 16156 TO THE SANTA MARGARITA  
WATER DISTRICT.
- (D) INDICATES 40' WIDE EXISTING EASEMENT FOR STORM DRAIN  
PURPOSES DEDICATED PER TRACT NO. 16156 TO THE COUNTY OF ORANGE.


### NOTES:

- LOTS "A" AND "B" ARE PROPOSED TO BE GRANTED IN FEE TO THE  
HOMEOWNERS ASSOCIATION FOR POCKET PARK PURPOSES.
- LOTS "C", "D" AND "E" ARE PROPOSED TO BE GRANTED IN FEE TO THE  
HOMEOWNERS ASSOCIATION FOR LANDSCAPE MAINTENANCE PURPOSES.
- LOTS "A" THROUGH "E" ARE NOT SEPARATE BUILDING SITES.

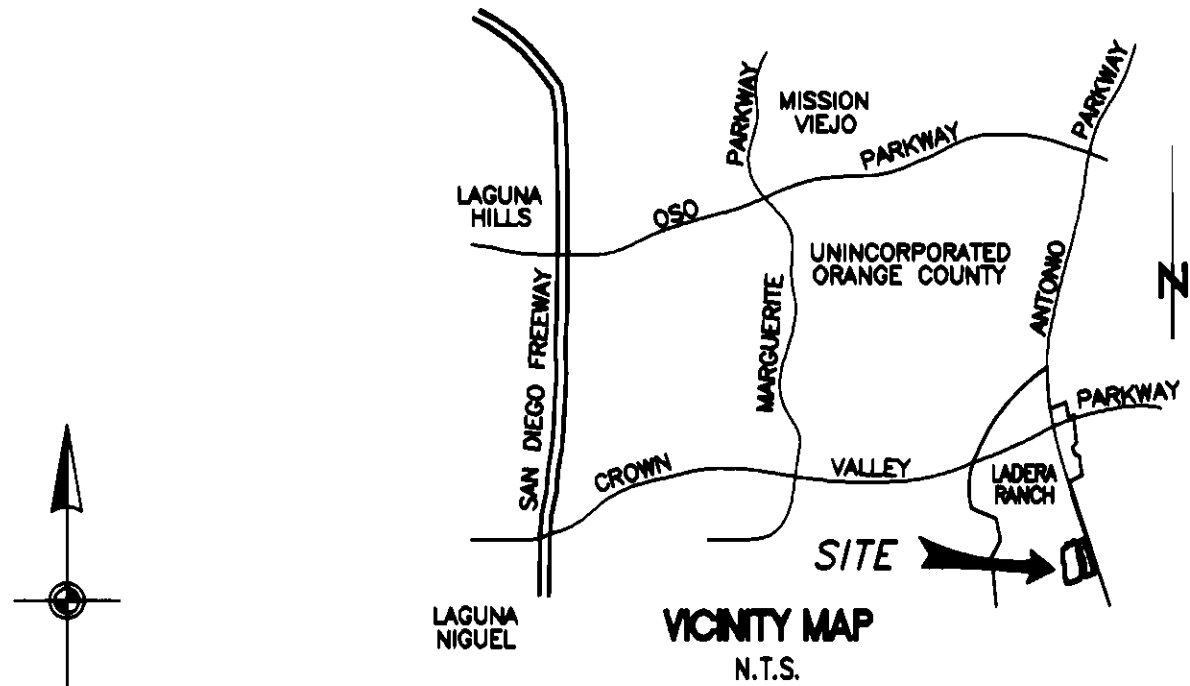

SCALE 1" = 120'

④ INDICATES SHEET NUMBER

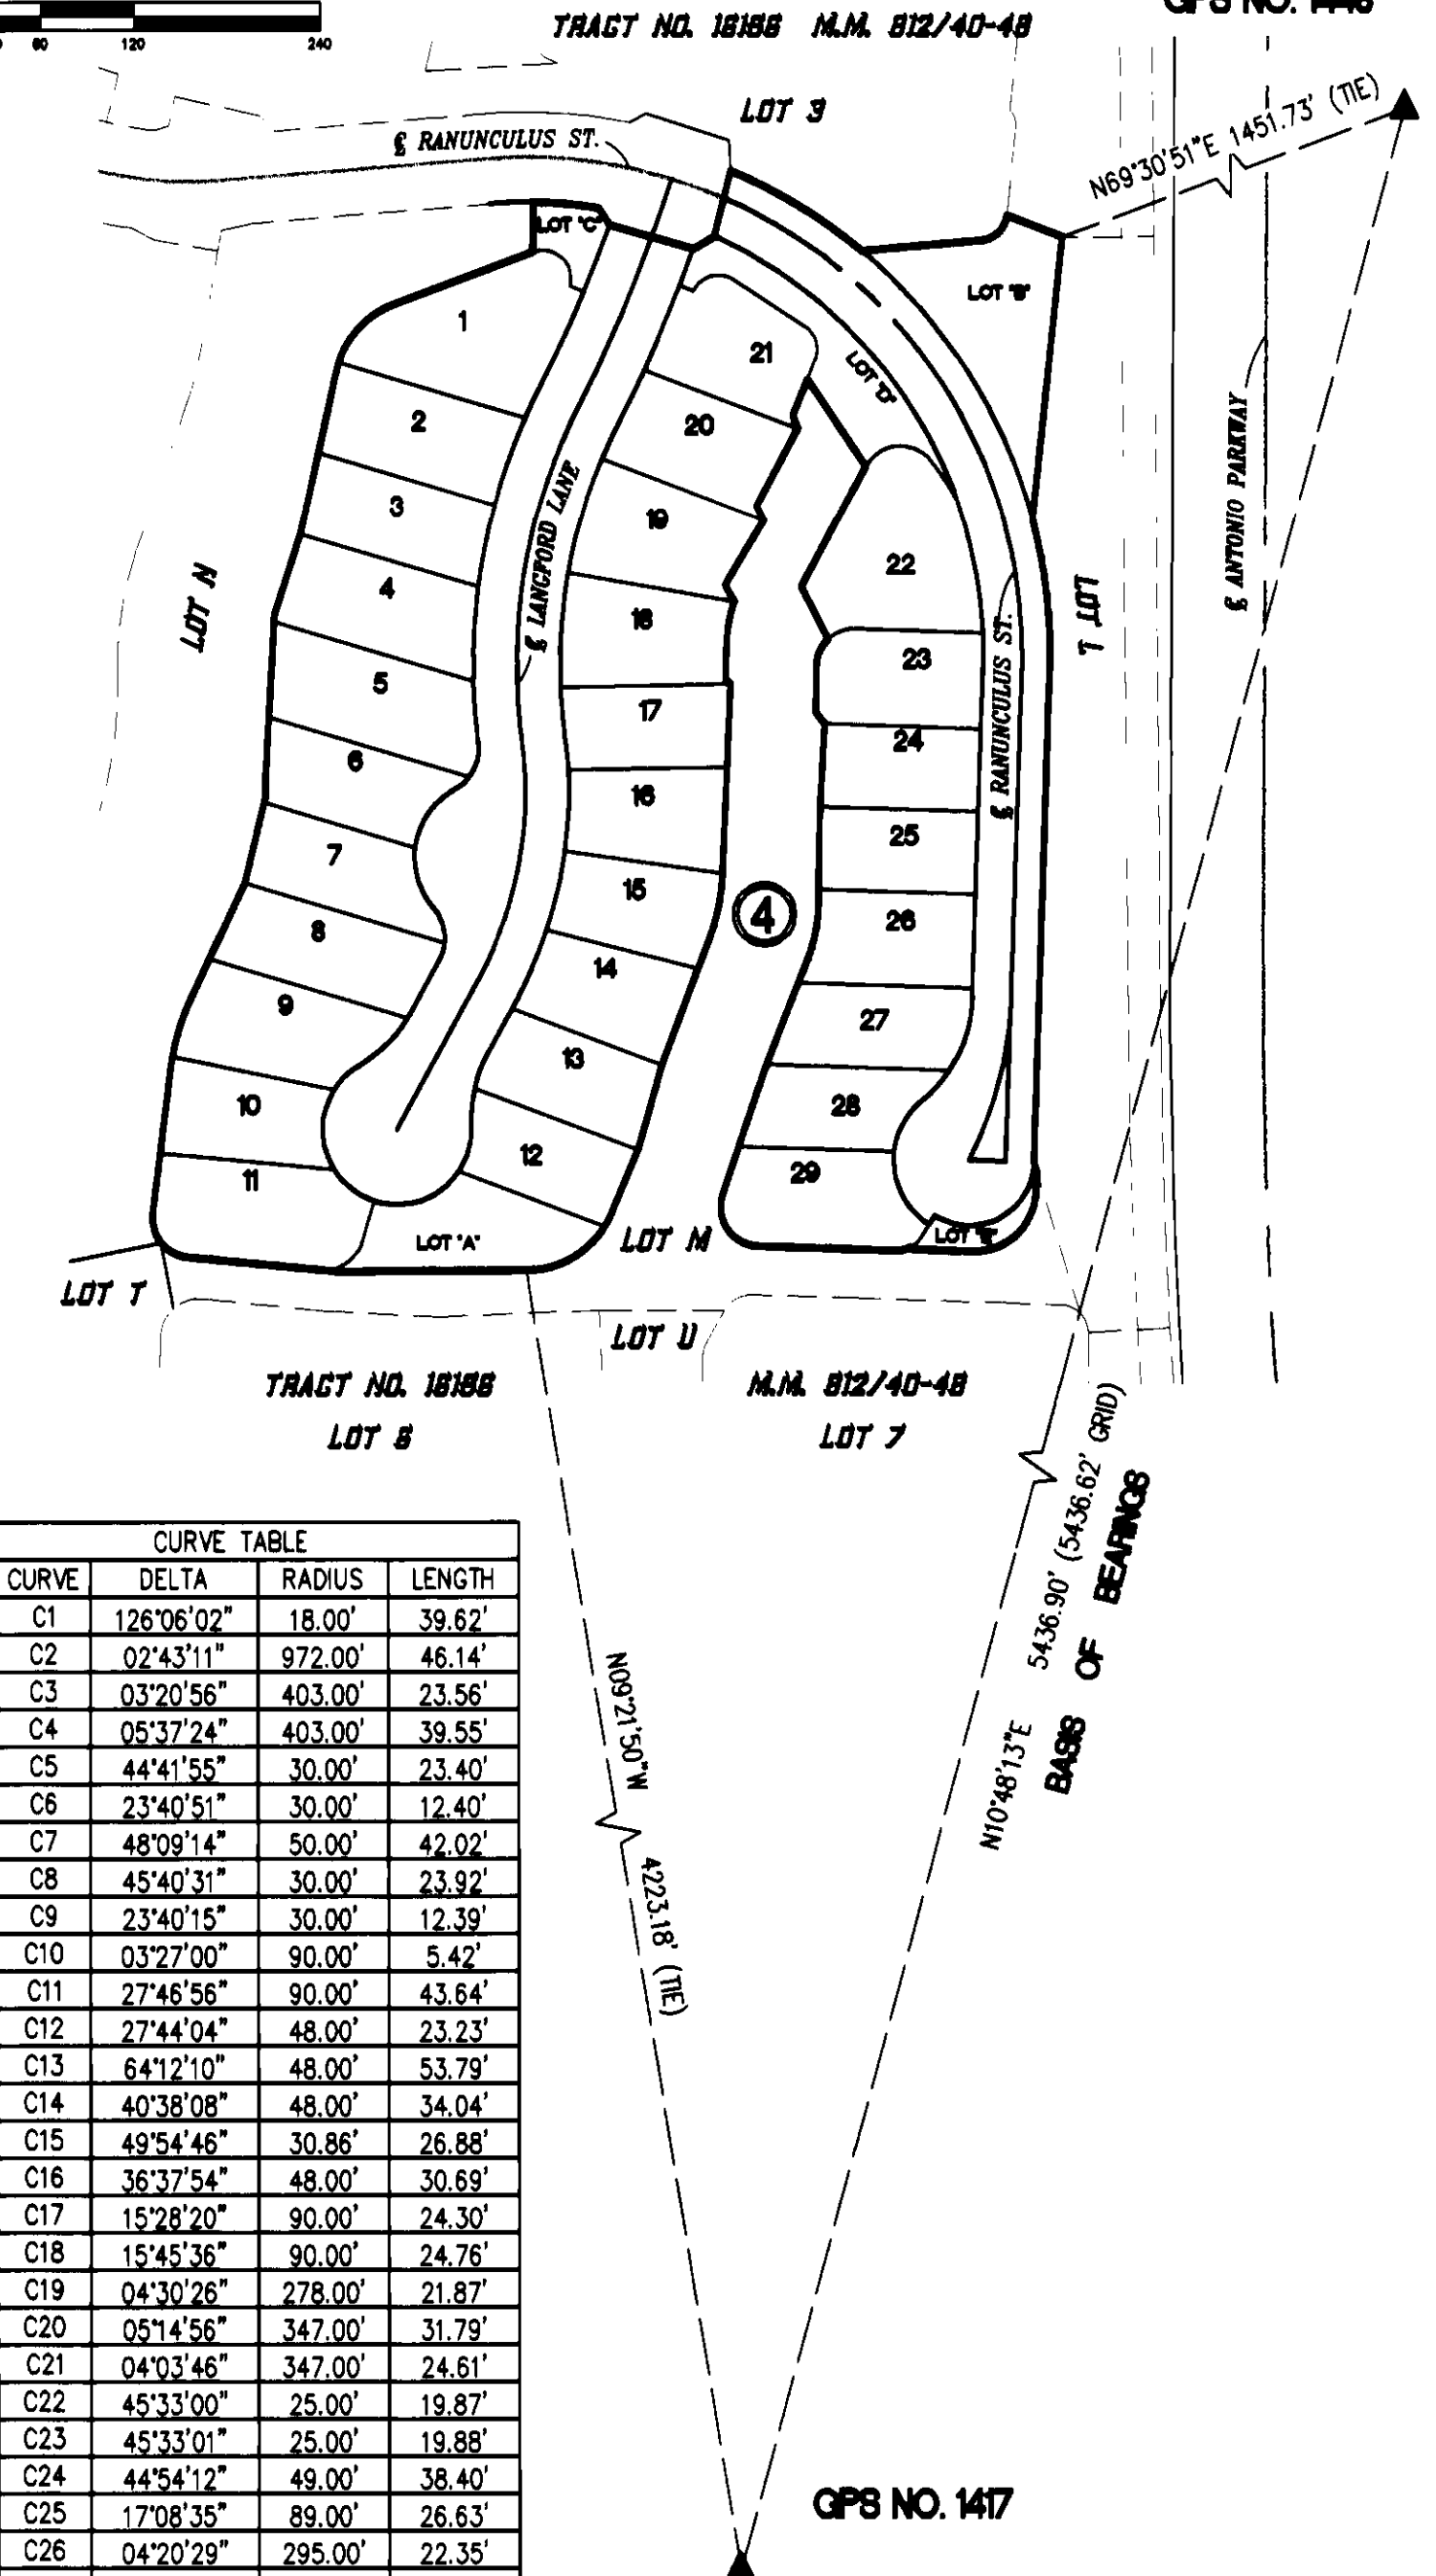

| CURVE TABLE |            |          |        |
|-------------|------------|----------|--------|
| CURVE       | DELTA      | RADIUS   | LENGTH |
| C1          | 126°06'02" | 18.00'   | 39.62' |
| C2          | 02°43'11"  | 972.00'  | 46.14' |
| C3          | 03°20'56"  | 403.00'  | 23.56' |
| C4          | 05°37'24"  | 403.00'  | 39.55' |
| C5          | 44°41'55"  | 30.00'   | 23.40' |
| C6          | 23°40'51"  | 30.00'   | 12.40' |
| C7          | 48°09'14"  | 50.00'   | 42.02' |
| C8          | 45°40'31"  | 30.00'   | 23.92' |
| C9          | 23°40'15"  | 30.00'   | 12.39' |
| C10         | 03°27'00"  | 90.00'   | 5.42'  |
| C11         | 27°46'56"  | 90.00'   | 43.64' |
| C12         | 27°44'04"  | 48.00'   | 23.23' |
| C13         | 64°12'10"  | 48.00'   | 53.79' |
| C14         | 40°38'08"  | 48.00'   | 34.04' |
| C15         | 49°54'46"  | 30.86'   | 26.88' |
| C16         | 36°37'54"  | 48.00'   | 30.69' |
| C17         | 15°28'20"  | 90.00'   | 24.30' |
| C18         | 15°45'36"  | 90.00'   | 24.76' |
| C19         | 04°30'26"  | 278.00'  | 21.87' |
| C20         | 05°14'56"  | 347.00'  | 31.79' |
| C21         | 04°03'46"  | 347.00'  | 24.61' |
| C22         | 45°33'00"  | 25.00'   | 19.87' |
| C23         | 45°33'01"  | 25.00'   | 19.88' |
| C24         | 44°54'12"  | 49.00'   | 38.40' |
| C25         | 17°08'35"  | 89.00'   | 26.63' |
| C26         | 04°20'29"  | 295.00'  | 22.35' |
| C27         | 05°46'59"  | 60.00'   | 6.06'  |
| C28         | 03°17'01"  | 150.00'  | 8.60'  |
| C29         | 14°43'35"  | 150.00'  | 38.55' |
| C30         | 09°33'33"  | 60.00'   | 10.01' |
| C31         | 31°47'18"  | 18.00'   | 9.99'  |
| C32         | 27°50'49"  | 18.00'   | 8.75'  |
| C33         | 02°15'44"  | 1000.00' | 39.48' |
| C34         | 06°26'21"  | 320.00'  | 35.96' |
| C35         | 01°24'53"  | 1028.00' | 25.38' |

| LINE TABLE |                  |          |
|------------|------------------|----------|
| LINE       | BEARING          | DISTANCE |
| L1         | N29°52'59"W(RAD) | 2.00'    |
| L2         | N32°16'13"E(RAD) | 16.72'   |
| L3         | N32°16'13"E(RAD) | 9.72'    |
| L4         | N32°16'13"E(RAD) | 7.00'    |
| L5         | N08°25'02"E      | 16.92'   |



DAVID EVANS AND ASSOCIATES, INC.  
CHARLES J. PRIOLO, R.C.E. #30790 FEBRUARY 2001

