

SHEET 1 OF 5 SHEETS

TRACT NO. 16121

ALL OF VESTING
TENTATIVE TRACT NO. 16121BLOCK MODULE
5157 19DATE OF SURVEY:
DECEMBER 2000IN UNINCORPORATED TERRITORY OF ORANGE COUNTY, CALIFORNIA
BEING A SUBDIVISION OF LOT 6 OF TRACT NO. 16156 FILED IN BOOK 812, PAGES 40
THROUGH 48 OF MISCELLANEOUS MAPS, RECORDS OF ORANGE COUNTY, CALIFORNIA.

APRIL 2001

JAMES F. GILLEN, L.S. 5557

HUITT-ZOLIARS

47 NUMBERED LOTS AND 6 LETTERED LOTS

10.301 ACRES

ACCEPTED AND FILED AT THE
REQUEST OF
FIRST AMERICAN TITLE INSURANCE COMPANYDATE DECEMBER 26, 2001TIME 11:08 A.M. FEE \$ 15.00INSTRUMENT NO. 20010940549BOOK 825 PAGE 46-50 M/MGARY L. GRANVILLE
COUNTY CLERK-RECORDERBY [Signature]
DEPUTY

OWNERSHIP CERTIFICATE:

WE, THE UNDERSIGNED, BEING ALL PARTIES HAVING ANY RECORD TITLE INTEREST IN THE LAND COVERED BY THIS MAP, DO HEREBY CONSENT TO THE PREPARATION AND RECORDATION OF SAID MAP, AS SHOWN WITHIN THE DISTINCTIVE BORDER LINE. WE ALSO HEREBY DEDICATE TO THE PUBLIC FOR STREET PURPOSES: SMOKE TREE DRIVE AND SCARLET MAPLE DRIVE.

WE ALSO HEREBY DEDICATE TO THE COUNTY OF ORANGE:

(1) THE EASEMENT FOR STORM DRAIN PURPOSES AS SHOWN ON SAID MAP.

WE ALSO HEREBY DEDICATE TO THE SANTA MARGARITA WATER DISTRICT THE EASEMENT FOR SEWER, WATER AND ACCESS PURPOSES AS SHOWN ON SAID MAP, WHICH EASEMENT SHALL BE SUBJECT TO THE SAME TERMS AND CONDITIONS AS ARE SHOWN IN THAT CERTAIN EASEMENT RECORDED OCTOBER 6, 1980 IN BOOK 13776, PAGE 341, OF OFFICIAL RECORDS, COUNTY OF ORANGE.

WE ALSO HEREBY DEDICATE TO THE SANTA MARGARITA WATER DISTRICT THE EASEMENTS FOR SEWER, WATER AND ACCESS PURPOSES AS SHOWN ON SAID MAP, WHICH EASEMENTS SHALL BE SUBJECT TO THE SAME TERMS AND CONDITIONS AS ARE SHOWN IN THAT CERTAIN EASEMENT RECORDED OCTOBER 6, 1980 IN BOOK 13776, PAGE 341, OF OFFICIAL RECORDS, COUNTY OF ORANGE. THE SANTA MARGARITA WATER DISTRICT SHALL RESTORE OTHER IMPROVEMENTS OR FACILITIES LOCATED WITHIN THE EASEMENT, IF IT HAS CONSENTED TO THE LOCATION OF SUCH IMPROVEMENTS OR FACILITIES TO THE EXTENT THAT THE EXERCISE OF ITS RIGHTS IN CONNECTION WITH THE EASEMENT IMPACTS OTHER IMPROVEMENTS OR FACILITIES LOCATED WITHIN THE EASEMENT, HOWEVER, IN NO EVENT SHALL SANTA MARGARITA WATER DISTRICT BE RESPONSIBLE FOR THE COST OF RELOCATING ITS FACILITIES IN THE EVENT OF CONFLICTS WITH SUCH OTHER IMPROVEMENTS OR FACILITIES.

STANDARD PACIFIC CORP., A DELAWARE CORPORATION

BY: [Signature]
PRINT NAME: Andrew Barnes
PRINT TITLE: Chief Financial Officer

BY: [Signature]
PRINT NAME: Jari L. Karibayan
PRINT TITLE: Vice President

DMB LADERA, L.L.C., A DELAWARE LIMITED LIABILITY COMPANY.
BENEFICIARY UNDER A DEED OF TRUST RECORDED FEBRUARY 15, 2001 AS INSTRUMENT NO. 20010084587 OF OFFICIAL RECORDS AND HOLDER OF A REPURCHASE OPTION RECORDED FEBRUARY 15, 2001 AS INSTRUMENT NO. 20010084585 OF OFFICIAL RECORDS.

BY: RANCHO MISSION VIEJO, L.L.C., A DELAWARE LIMITED LIABILITY COMPANY,
AS AGENT AND/OR MANAGER.

BY: [Signature]
PRINT NAME: Paul Johnson
PRINT TITLE: VP Community Development

BY: [Signature]
PRINT NAME: Stephen C. Schrank
PRINT TITLE: Executive VP Development

CERTIFICATE OF ACCEPTANCE

THE UNDERSIGNED, BEING THE DULY APPOINTED AGENT OF THE SANTA MARGARITA WATER DISTRICT, A PUBLIC CORPORATION OF ORANGE COUNTY, CALIFORNIA, PURSUANT TO ITS RESOLUTION NO. 88-10-2, DOES HEREBY ACCEPT ON BEHALF OF SAID DISTRICT THE EASEMENTS FOR SEWER, WATER AND ACCESS PURPOSES, AS DEDICATED AND AS SHOWN ON THIS TRACT MAP, BY AND BETWEEN THE SANTA MARGARITA WATER DISTRICT AND STANDARD PACIFIC CORP. AND DOES HEREBY CERTIFY THAT THE GRANTEE CONSENTS TO THE RECORDATION OF SAID TRACT.

[Signature]
DANIEL R. FERONS, CHIEF ENGINEER
SANTA MARGARITA WATER DISTRICT.

AUTOMATIC FIRE SPRINKLER NOTE:

ALL COMMERCIAL STRUCTURES GREATER THAN 6,000 SQUARE FEET; ALL MULTIFAMILY RESIDENTIAL STRUCTURES; ALL SINGLE-FAMILY STRUCTURES EXCEEDING 5,500 SQUARE FEET, AND ALL STRUCTURES EXCEEDING FIRE DEPARTMENT ACCESS REQUIREMENTS SHALL BE PROTECTED BY AN AUTOMATIC SPRINKLER SYSTEM. LOTS 2, 3, 11-14, 30-34 AND 41-47 WILL REQUIRE AUTOMATIC FIRE SPRINKLER SYSTEM PER OCCA.

HIGH FIRE HAZARD AREA NOTE:

THE LOTS SHOWN ON THIS MAP ARE IN A HIGH FIRE HAZARD AREA DUE TO WILD LAND EXPOSURE BASED ON STATE SRA MAPS.

THE PROPERTY SHOWN ON THIS MAP IS "TOTALLY EXCLUDED" FROM A "SPECIAL FIRE PROTECTION AREA." THERE ARE NO LOTS IN THIS TRACT THAT ARE SUBJECT TO CONSTRUCTION FEATURES OF THE ORANGE COUNTY ORDINANCE 3960.


NOTES:

PROPERTY MAY BE SUBJECT TO IMPACTS FROM THE FOOTHILL/EASTERN TRANSPORTATION CORRIDOR.

SEE SHEET 2 FOR NOTARY ACKNOWLEDGMENTS AND SIGNATURE OMISSIONS.

SURVEYOR'S STATEMENT:

I HEREBY STATE THAT THIS MAP CONSISTING OF 5 SHEETS, CORRECTLY REPRESENTS A TRUE AND COMPLETE SURVEY AS SHOWN MADE IN DECEMBER, 2000; WAS MADE BY ME OR UNDER MY DIRECTION; THAT THE MONUMENTS ARE OF THE CHARACTER AND OCCUPY OR WILL OCCUPY THE POSITIONS INDICATED BY SAID MAP; AND THAT SAID MONUMENTS WILL BE SUFFICIENT TO ENABLE THE SURVEY TO BE RETRACED.

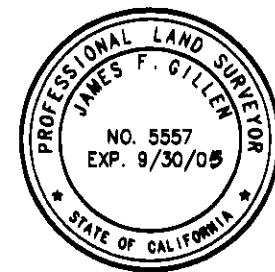


[Signature]
JAMES F. GILLEN
L.S. 5557
EXPIRATION DATE: 9/30/05

COUNTY SURVEYOR'S STATEMENT:

I HEREBY STATE THAT I HAVE EXAMINED THIS MAP AND HAVE FOUND IT TO BE SUBSTANTIALLY IN CONFORMANCE WITH THE TENTATIVE MAP AS FILED WITH, AMENDED AND APPROVED BY THE ORANGE COUNTY SUBDIVISION COMMITTEE; THAT ALL PROVISIONS OF THE SUBDIVISION MAP ACT AND COUNTY SUBDIVISION REGULATIONS HAVE BEEN COMPLIED WITH AND I AM SATISFIED SAID MAP IS TECHNICALLY CORRECT.

DATED THIS 5TH DAY OF DECEMBER, 2001.

[Signature]
JOHN CANAS, COUNTY SURVEYOR
L.S. 4408 EXPIRATION DATE: 09-30-05

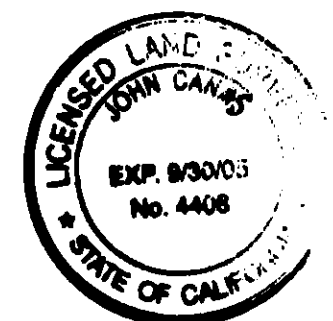

COUNTY TREASURER-TAX COLLECTOR'S CERTIFICATE:

STATE OF CALIFORNIA)
COUNTY OF ORANGE)SS

I HEREBY CERTIFY THAT ACCORDING TO THE RECORDS OF MY OFFICE THERE ARE NO LIENS AGAINST THE LAND COVERED BY THIS MAP OR ANY PART THEREOF FOR UNPAID STATE, COUNTY, MUNICIPAL OR LOCAL TAXES OR SPECIAL ASSESSMENTS COLLECTED AS TAXES, EXCEPT TAXES OR SPECIAL ASSESSMENTS COLLECTED AS TAXES NOT YET PAYABLE. AND DO ALSO HEREBY CERTIFY TO THE RECORDER OF ORANGE COUNTY THAT THE PROVISIONS OF THE SUBDIVISION MAP ACT HAVE BEEN COMPLIED WITH REGARDING DEPOSITS TO SECURE THE PAYMENT OF TAXES OR SPECIAL ASSESSMENTS COLLECTED AS TAXES ON THE LAND COVERED BY THIS MAP.

DATED THIS 20TH DAY OF November, 2001.

JOHN M.W. MOORLACH
COUNTY TREASURER-TAX COLLECTOR

BY: [Signature]
DEPUTY TREASURER-TAX COLLECTOR

CLERK OF THE BOARD OF SUPERVISORS' CERTIFICATE:

STATE OF CALIFORNIA)
COUNTY OF ORANGE)SS


I HEREBY CERTIFY THAT THIS MAP WAS PRESENTED FOR APPROVAL TO THE BOARD OF SUPERVISORS OF ORANGE COUNTY AT A REGULAR MEETING THEREOF HELD ON THE 18 DAY OF December, 2001, AND THAT THEREUPON SAID BOARD DID, BY AN ORDER DULY PASSED AND ENTERED, APPROVE SAID MAP AND DID ACCEPT ON BEHALF OF THE PUBLIC, SUBJECT TO IMPROVEMENTS: THE DEDICATION FOR STREET PURPOSES OF: SMOKE TREE DRIVE AND SCARLET MAPLE DRIVE.

AND DID ALSO ACCEPT ON BEHALF OF THE COUNTY OF ORANGE:

1. THE EASEMENT FOR STORM DRAIN PURPOSES AS DEDICATED.

DATED THIS 18 DAY OF December, 2001.

[Signature]
DARLENE J. BLOOM
CLERK OF THE BOARD OF SUPERVISORS

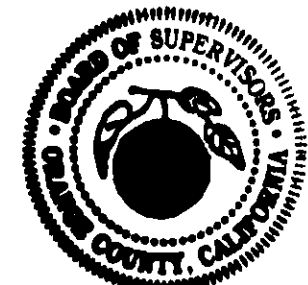

SHEET 2 OF 5 SHEETS

TRACT NO. 16121

ALL OF VESTING TENTATIVE
TRACT NO. 16121

IN UNINCORPORATED TERRITORY OF ORANGE COUNTY, CALIFORNIA

DATE OF SURVEY:
DECEMBER 2000

APRIL 2001

JAMES F. GILLEN, L.S. 5557

HUITT-ZOLIARS

47 NUMBERED LOTS AND 6 LETTERED LOTS

10.301 ACRES

STANDARD PACIFIC CORP.

STATE OF CALIFORNIA)
COUNTY OF ORANGE)

ON THIS 20th DAY OF April, 2001, BEFORE ME,
Kathleen M. Villari, A NOTARY PUBLIC IN AND FOR SAID STATE,
PERSONALLY APPEARED Andrew Johnson AND
Jane Santogian, PERSONALLY KNOWN TO ME OR PROVED TO ME
ON THE BASIS OF SATISFACTORY EVIDENCE TO BE THE PERSONS WHOSE NAMES
ARE SUBSCRIBED TO THE WITHIN INSTRUMENT AND ACKNOWLEDGED TO ME THAT
THEY EXECUTED THE SAME IN THEIR AUTHORIZED CAPACITIES, AND THAT BY THEIR
SIGNATURES ON THE INSTRUMENT THE PERSONS, OR THE ENTITY UPON BEHALF
OF WHICH THE PERSONS ACTED, EXECUTED THE INSTRUMENT.

WITNESS MY HAND: MY COMMISSION EXPIRES 8-10-2003
Kathleen M. Villari MY PRINCIPAL PLACE OF BUSINESS
NOTARY PUBLIC IN AND FOR SAID STATE IS IN Orange COUNTY.
KATHLEEN M. VILLARI
PRINT NAME

DMB LADERA, L.L.C.

STATE OF CALIFORNIA)
COUNTY OF ORANGE)

ON THIS 2nd DAY OF May, 2001, BEFORE ME,
Tina T. Baker, A NOTARY PUBLIC IN AND FOR SAID STATE,
PERSONALLY APPEARED Paul Johnson AND
Stephen C. Schenk, PERSONALLY KNOWN TO ME OR PROVED TO ME
ON THE BASIS OF SATISFACTORY EVIDENCE TO BE THE PERSONS WHOSE NAMES
ARE SUBSCRIBED TO THE WITHIN INSTRUMENT AND ACKNOWLEDGED TO ME THAT
THEY EXECUTED THE SAME IN THEIR AUTHORIZED CAPACITIES, AND THAT BY THEIR
SIGNATURES ON THE INSTRUMENT THE PERSONS, OR THE ENTITY UPON BEHALF
OF WHICH THE PERSONS ACTED, EXECUTED THE INSTRUMENT.

WITNESS MY HAND: MY COMMISSION EXPIRES 8-29-04
Tina T. Baker MY PRINCIPAL PLACE OF BUSINESS
NOTARY PUBLIC IN AND FOR SAID STATE IS IN Orange COUNTY.
Tina T. Baker
PRINT NAME

SANTA MARGARITA WATER DISTRICT

STATE OF CALIFORNIA)
COUNTY OF ORANGE)

ON THIS 13th DAY OF SEPTEMBER, 2001, BEFORE ME,
Andrea M. Evans, A NOTARY PUBLIC IN AND FOR SAID STATE,
PERSONALLY APPEARED DANIEL R. FERONS PERSONALLY KNOWN TO ME
OR PROVED TO ME ON THE BASIS OF SATISFACTORY EVIDENCE TO BE THE
PERSON WHOSE NAME IS SUBSCRIBED TO THE WITHIN INSTRUMENT AND ACKNOWLEDGED
TO ME THAT HE EXECUTED THE SAME IN HIS AUTHORIZED CAPACITY, AND THAT
BY HIS SIGNATURE ON THE INSTRUMENT THE PERSON, OR THE ENTITY UPON BEHALF
OF WHICH THE PERSON ACTED, EXECUTED THE INSTRUMENT.

WITNESS MY HAND: MY COMMISSION EXPIRES April 8, 2001
Andrea M. Evans MY PRINCIPAL PLACE OF BUSINESS
NOTARY PUBLIC IN AND FOR SAID STATE IS IN ORANGE COUNTY.
ANDREA M. EVANS
PRINT NAME

MONUMENT NOTES:

- ▲ INDICATES FOUND 2" I.P. TAGGED "P.L.S. 5557" PER TRACT NO. 16156, M.M. 812/40-48.
- INDICATES LOCATION OF 1" I.P. TAGGED "P.L.S. 5557" OR SPIKE & WASHER
STAMPED "P.L.S. 5557" OR LEAD, TACK & TAG "P.L.S. 5557" TO BE SET PER
TRACT NO. 16156, M.M. 812/40-48.
- △ INDICATES LOCATION OF 2" I.P. TAGGED "P.L.S. 5557" OR SPIKE & WASHER
STAMPED "P.L.S. 5557" OR LEAD, TACK & TAG "P.L.S. 5557" TO BE SET PER
TRACT NO. 16156, M.M. 812/40-48.
- INDICATES LOCATION OF 1" I.P. TAGGED "P.L.S. 5557" OR SPIKE & WASHER
STAMPED "P.L.S. 5557" OR LEAD, TACK & TAG "P.L.S. 5557" TO BE SET WITHIN
90 DAYS AFTER ACCEPTANCE OF IMPROVEMENTS.
- 1" I.P. TAGGED "P.L.S. 5557" OR SPIKE & WASHER STAMPED "P.L.S. 5557" OR LEAD,
TACK AND TAG "P.L.S. 5557" TO BE SET AT ALL INTERIOR LOT CORNERS, EXCEPT LOT
CORNERS ABUTTING STREETS; LEAD, TACK & TAG "P.L.S. 5557" TO BE SET IN TOP OF
CURB OR SIDEWALK ON 9.75' OFFSET ON SIDE LOT LINES PRODUCED FOR LOT CORNERS
ABUTTING STREETS, WITHIN 90 DAYS AFTER ACCEPTANCE OF IMPROVEMENTS,
UNLESS OTHERWISE NOTED.

NO MONUMENTATION TO BE SET AT BC'S AND EC'S OF STREET RIGHT OF WAY LINES,
UNLESS OTHERWISE NOTED.

SIGNATURE OMISSIONS:

IN ACCORDANCE WITH THE PROVISIONS OF SECTION 66436(a) (3) OF THE SUBDIVISION
MAP ACT, THE FOLLOWING SIGNATURE HAS BEEN OMITTED:


1. LADERA DEVELOPMENT COMPANY, L.L.C., HOLDER OF OIL, GAS, MINERAL, AND WATER RIGHTS
RECORDED DECEMBER 10, 1996 AS INSTRUMENT NO. 19960624029 OF OFFICIAL RECORDS.
2. DMB LADERA, L.L.C., A DELAWARE LIMITED LIABILITY COMPANY, HOLDER OF EASEMENTS
RECORDED FEBRUARY 15, 2001 AS INSTRUMENT NO. 20010084586 OF OFFICIAL RECORDS.

BASIS OF BEARINGS:

BEARINGS SHOWN HEREON ARE BASED ON THE WESTERLY LINE OF LOT T, BEING N31°19'04"W
AS SHOWN ON TRACT NO. 16156, FILED IN BOOK 812, PAGES 40 THROUGH 48 OF MISCELLANEOUS MAPS,
RECORDS OF ORANGE COUNTY, CALIFORNIA.

EASEMENT NOTES:

- A INDICATES EASEMENT FOR STORM DRAIN PURPOSES DEDICATED TO THE COUNTY OF ORNAGE.
- B INDICATES EASEMENT FOR SEWER, WATER, AND ACCESS PURPOSES DEDICATED TO THE
SANTA MARGARITA WATER DISTRICT.

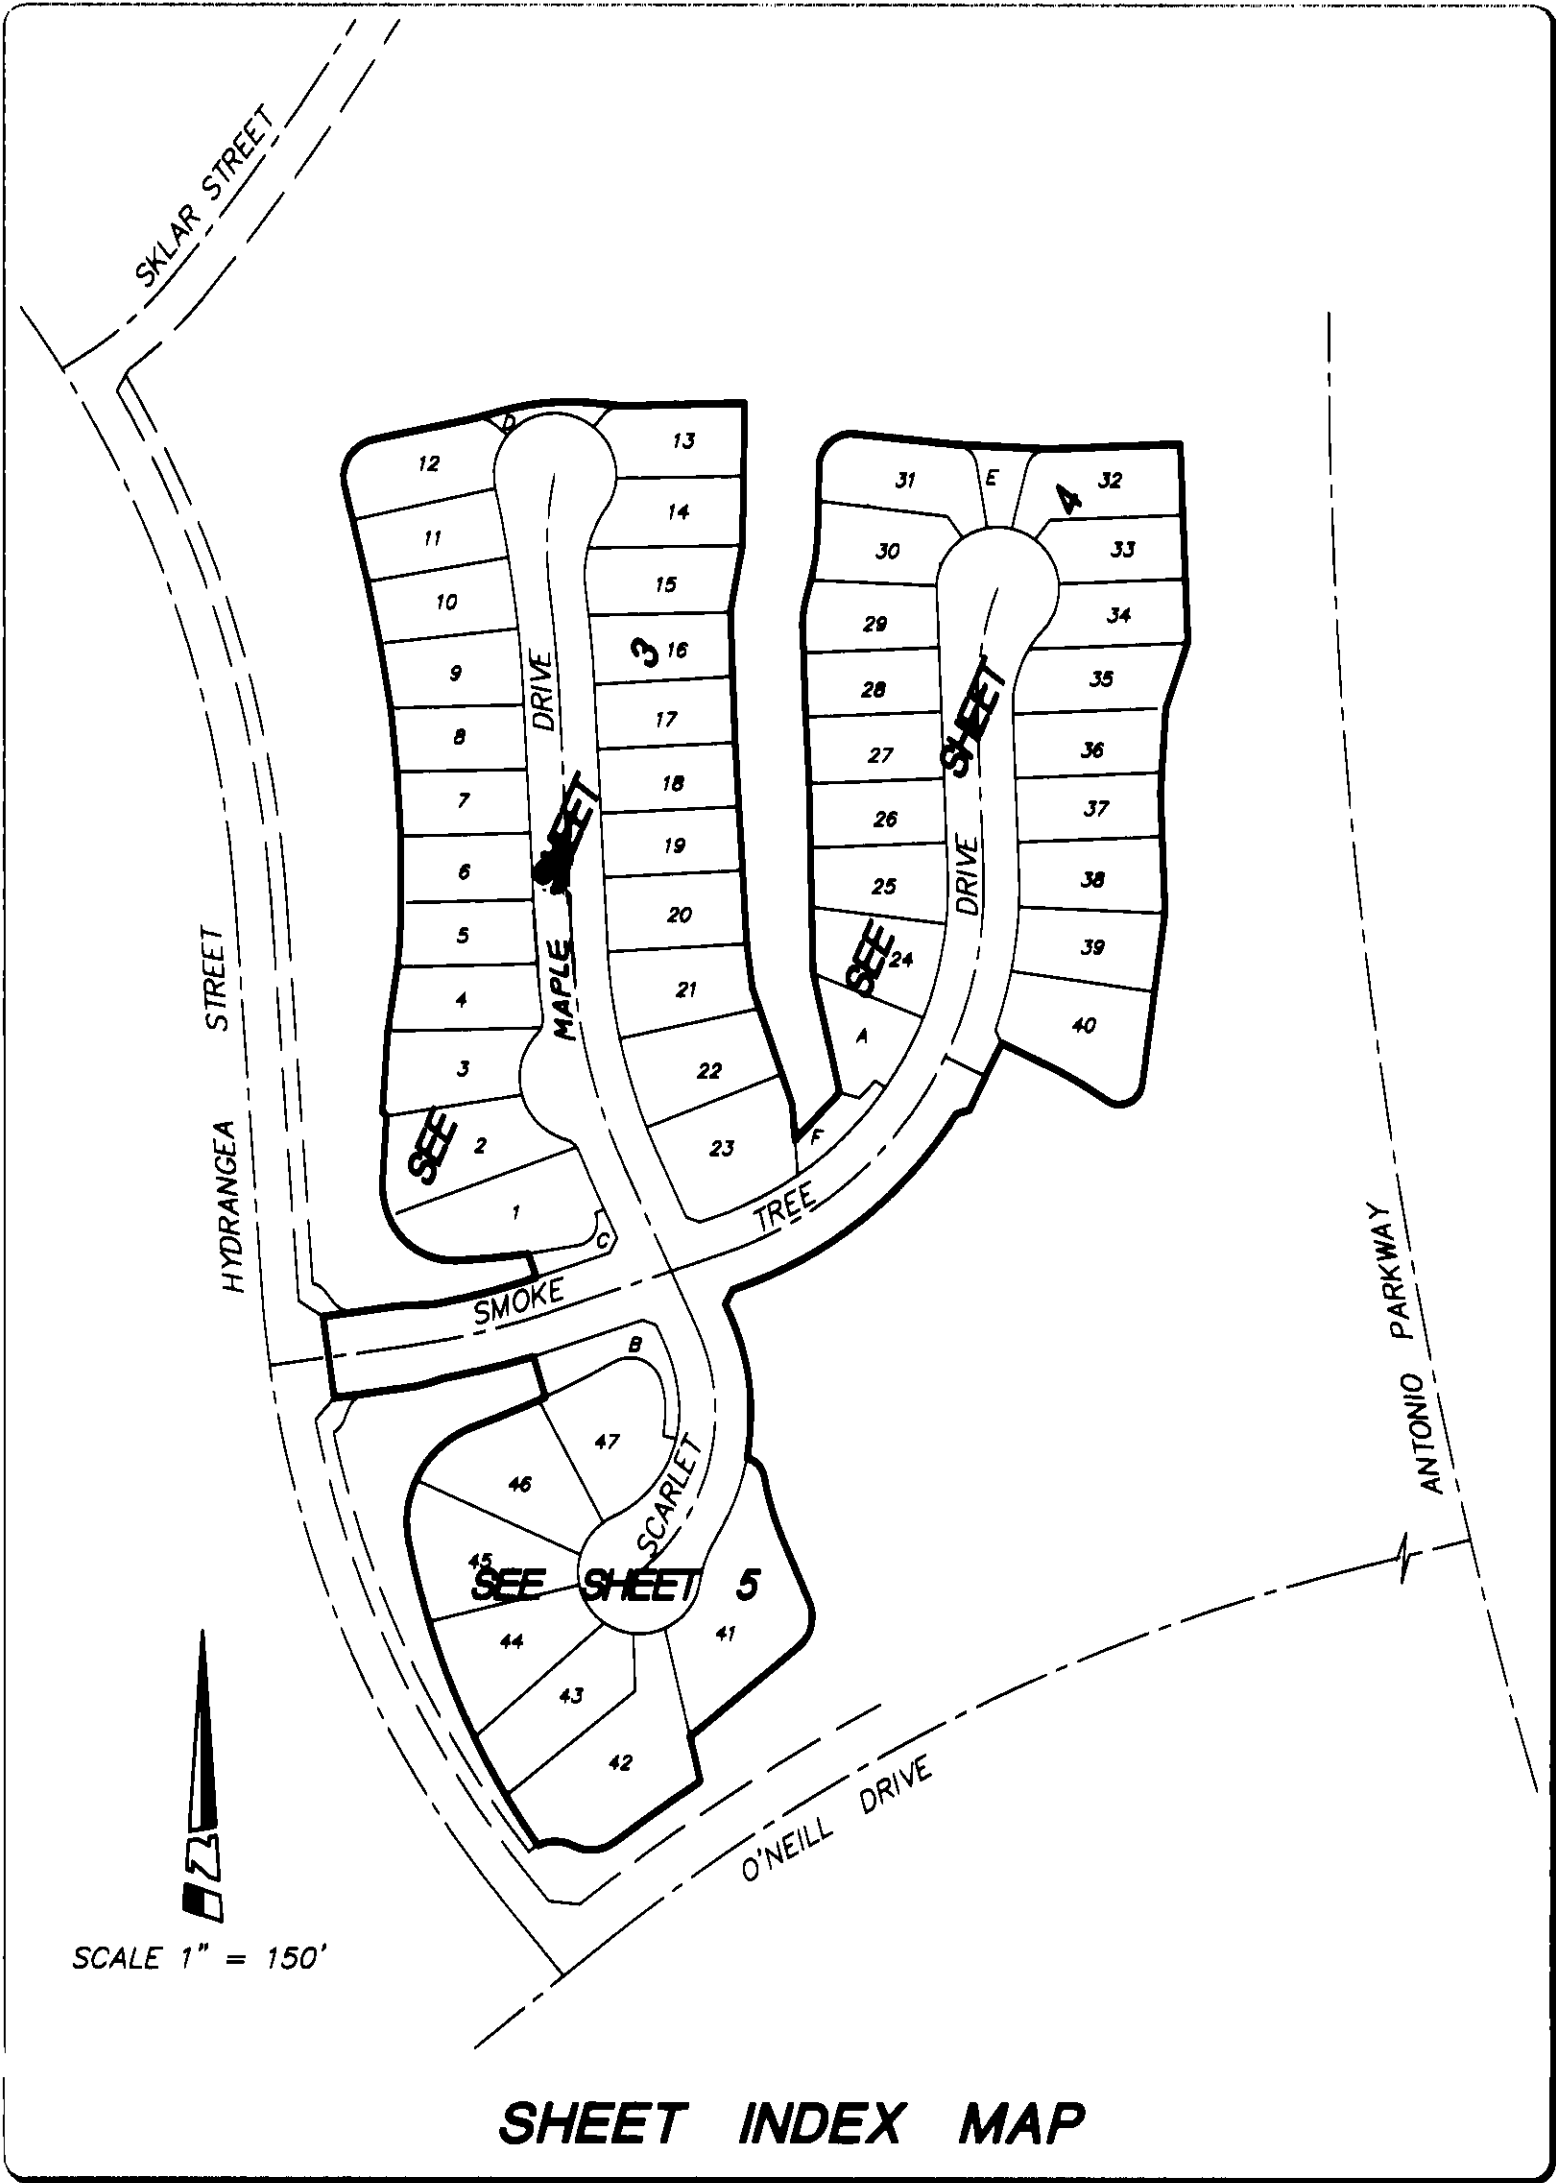

SHEET 3 OF 5 SHEETS

TRACT NO. 16121

ALL OF VESTING TENTATIVE
TRACT NO. 16121

IN UNINCORPORATED TERRITORY OF ORANGE COUNTY, CALIFORNIA

DATE OF SURVEY:
DECEMBER 2000


APRIL 2001

JAMES F. GILLEN, L.S. 5557

HUITT-ZOLIARS

47 NUMBERED LOTS AND 6 LETTERED LOTS

10.301 ACRES

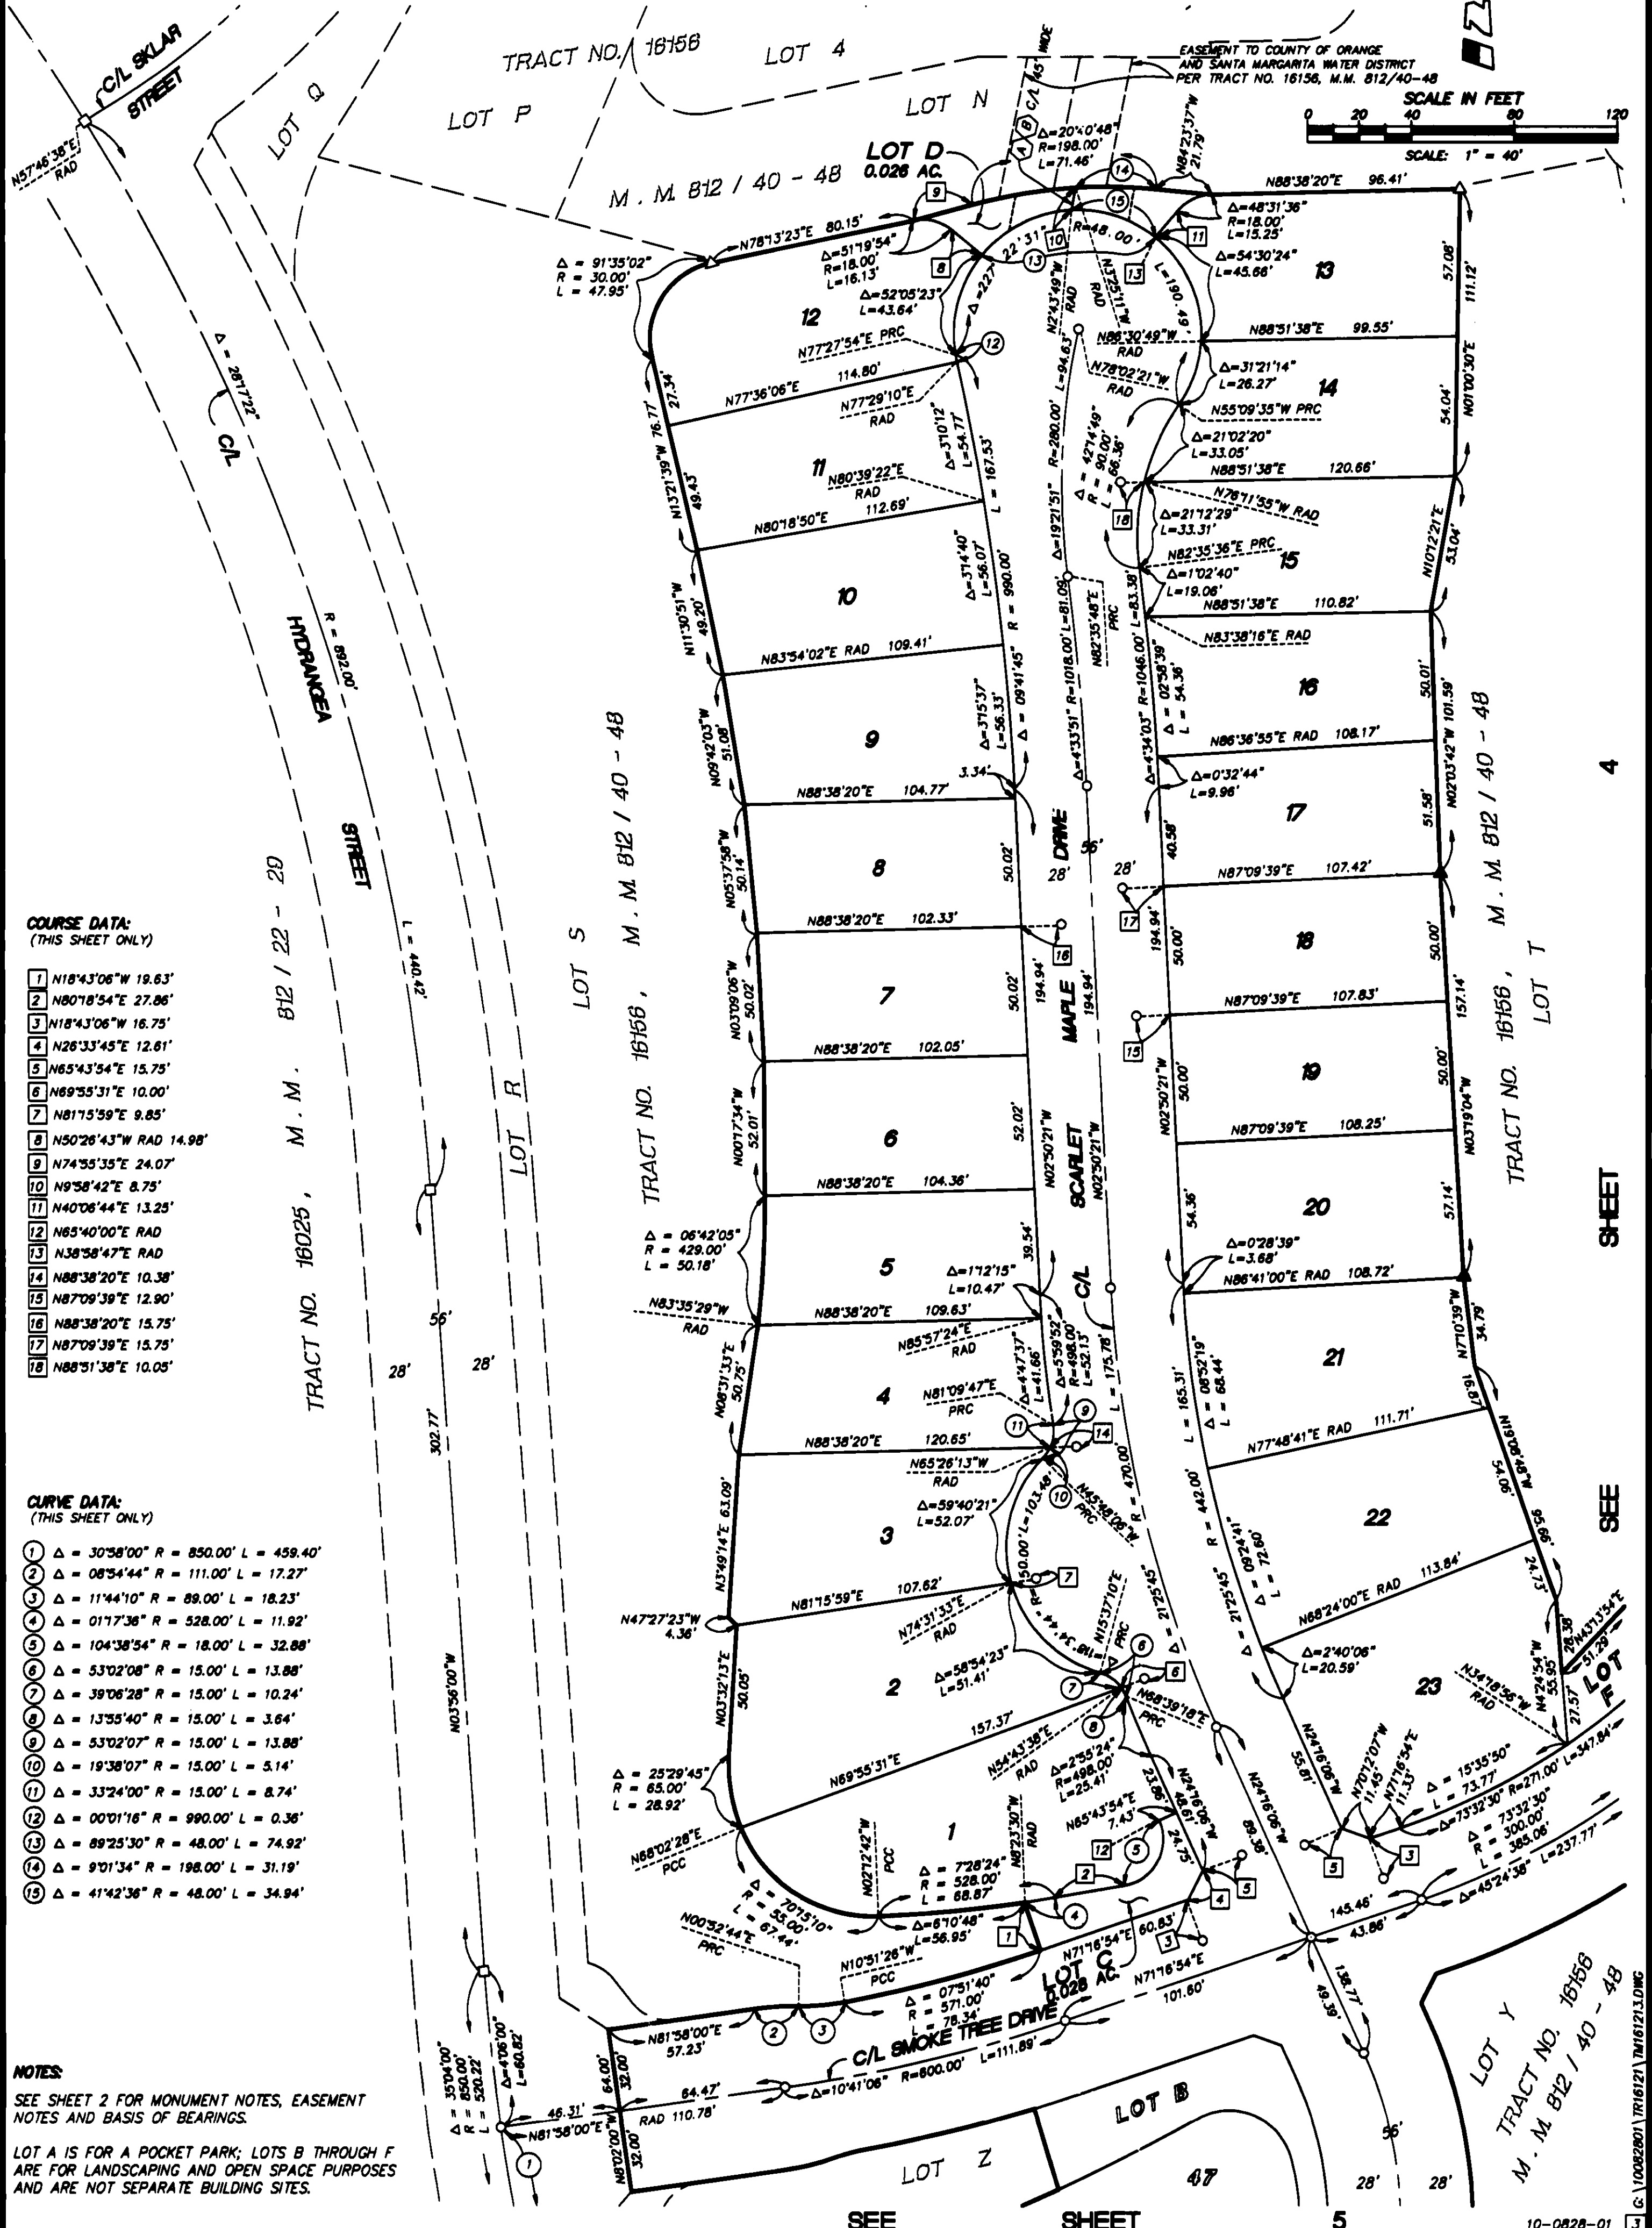

4

SHEET

SEE

825

48

10-0828-01

SHEET 4 OF 5 SHEETS

TRACT NO. 16121

ALL OF VESTING TENTATIVE
TRACT NO. 16121

IN UNINCORPORATED TERRITORY OF ORANGE COUNTY, CALIFORNIA

DATE OF SURVEY:
DECEMBER 2000

APRIL 2001

JAMES F. GILLEN, L.S. 5557

HUITT-ZOLIARS

47 NUMBERED LOTS AND 6 LETTERED LOTS



10.301 ACRES

TRACT NO. 16158 , M. M. 812 / 40 - 48

LOT 5

EASEMENT TO SANTA MARGARITA WATER DISTRICT
PER TRACT NO. 16156, M.M. 812/40-48

LOT M

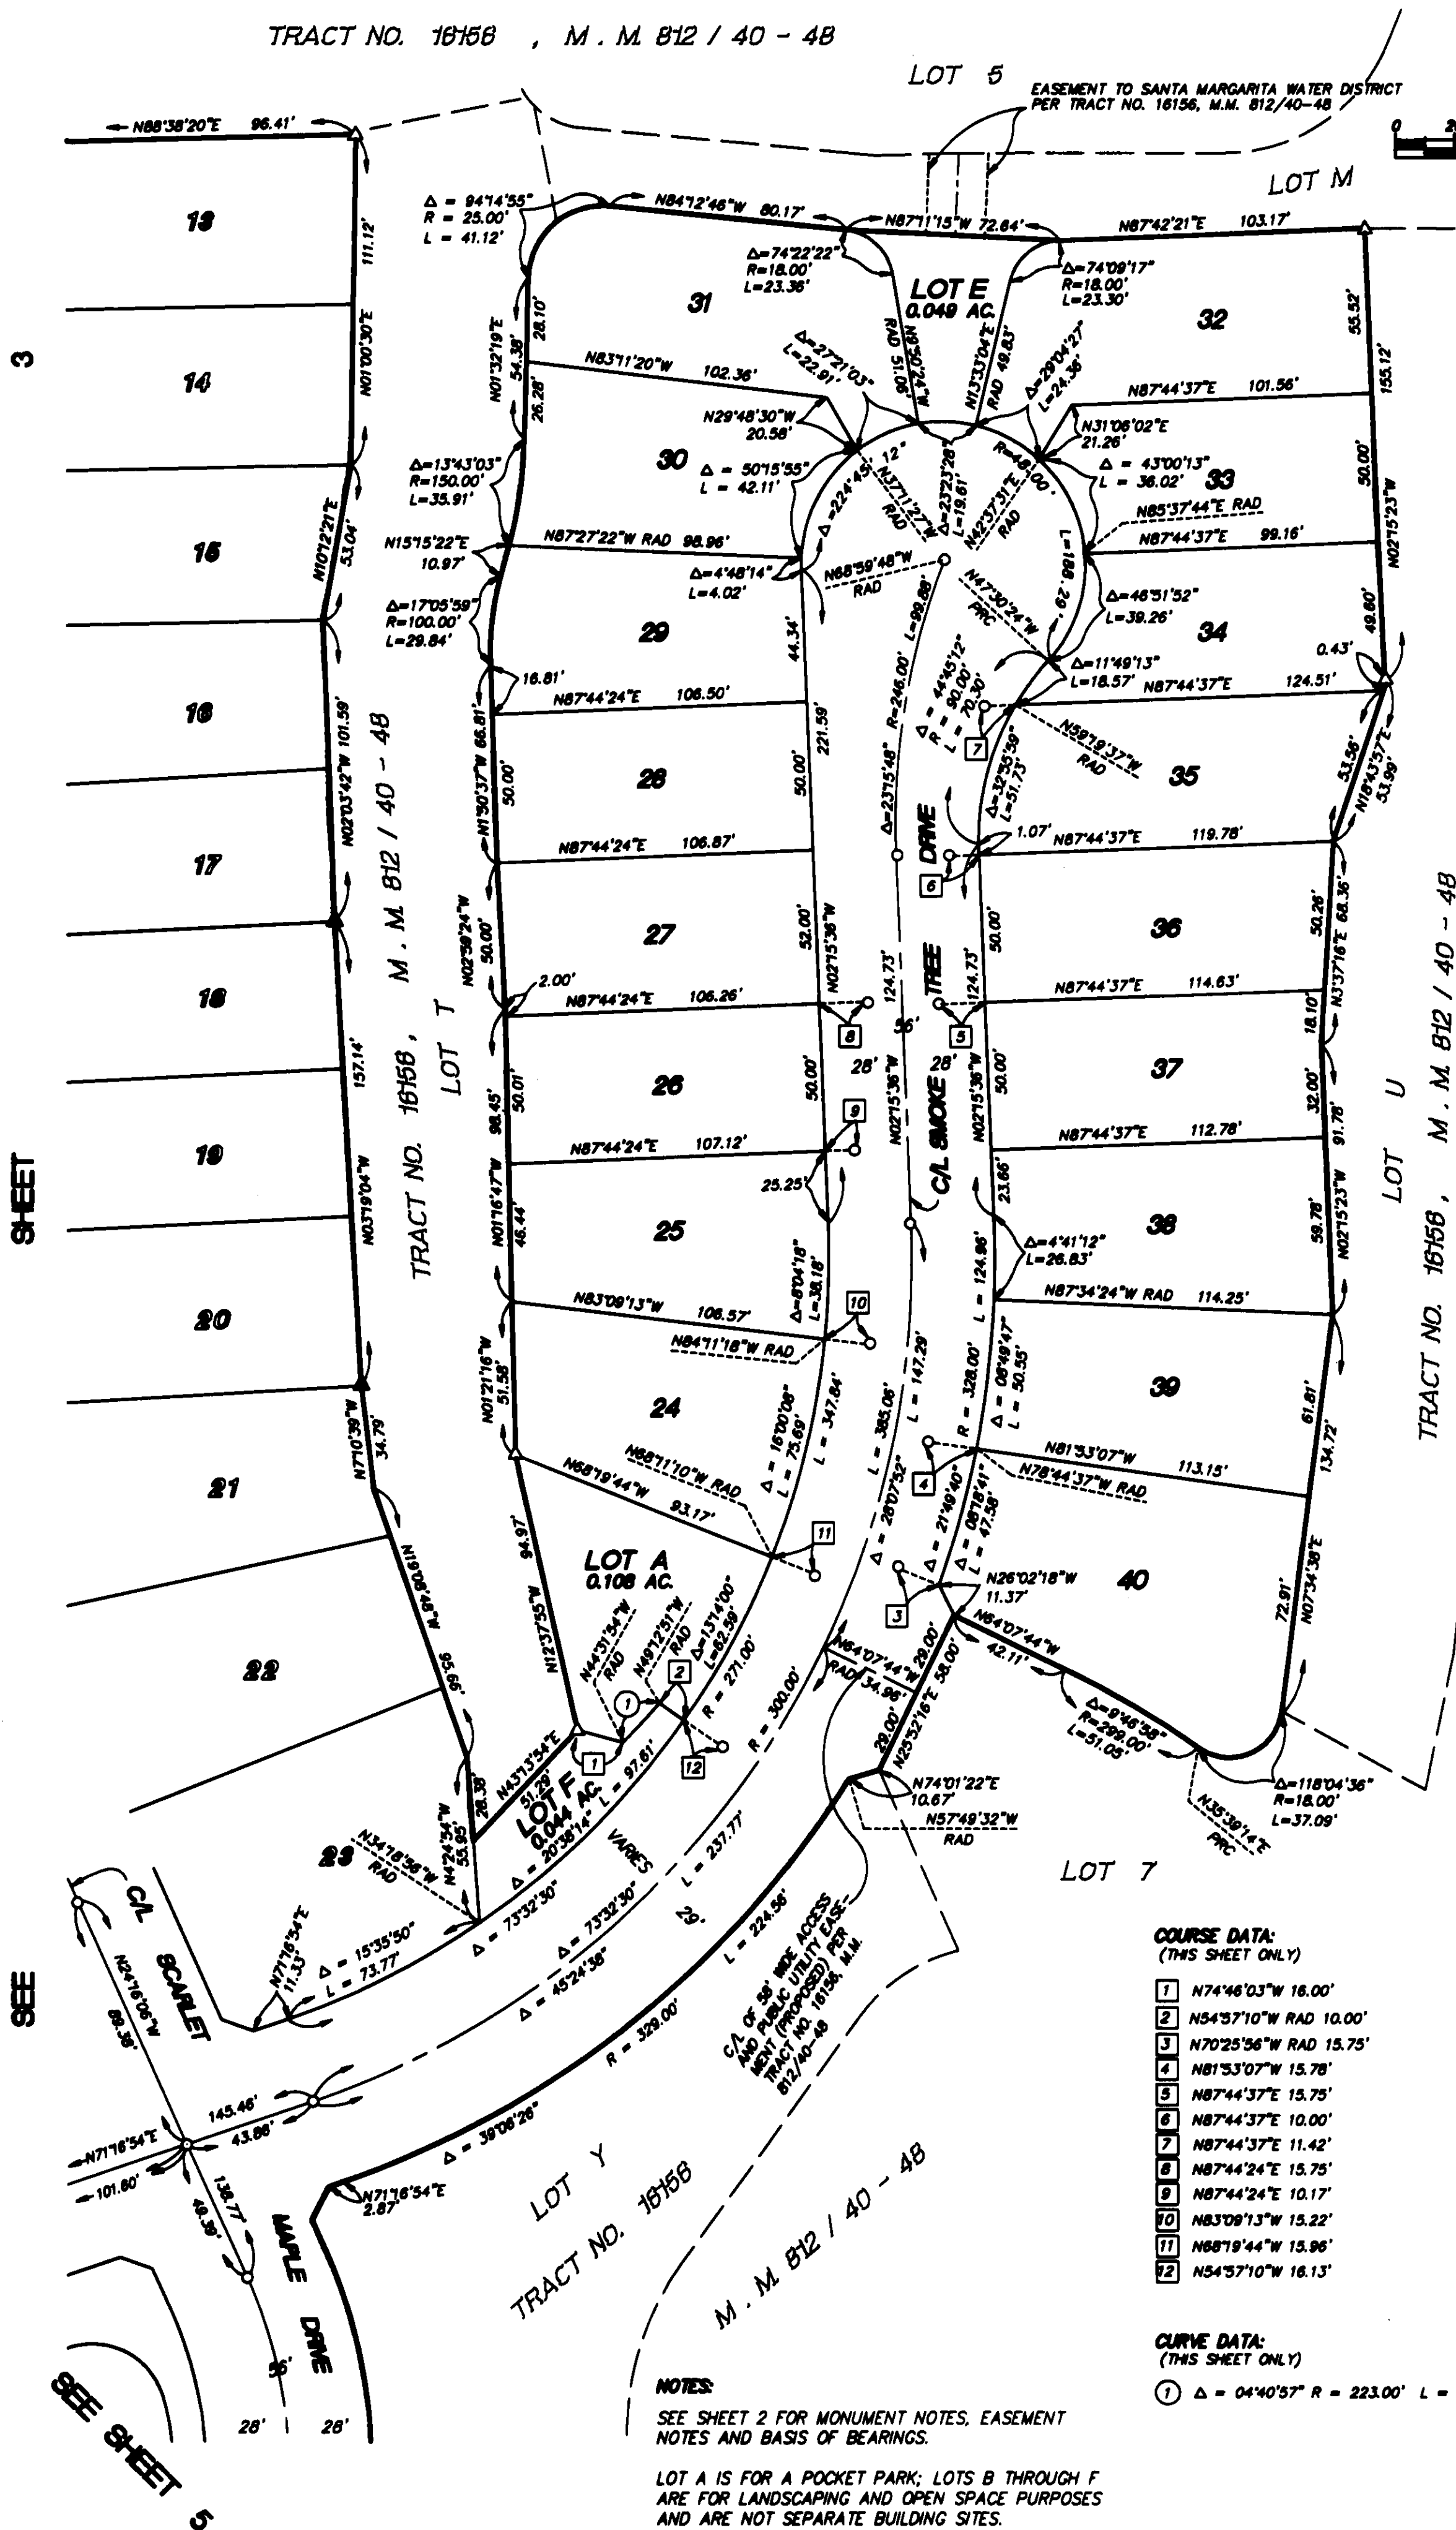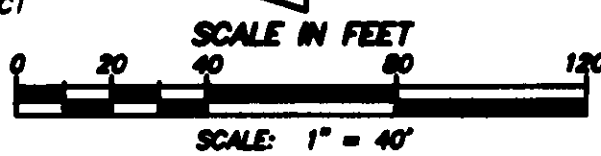

COURSE DATA: (THIS SHEET ONLY)

- 1 N74°46'03"W 18.00'
- 2 N54°57'10"W RAD 10.00'
- 3 N70°25'56"W RAD 15.75'
- 4 N81°53'07"W 15.78'
- 5 N87°44'37"E 15.75'
- 6 N87°44'37"E 10.00'
- 7 N87°44'37"E 11.42'
- 8 N87°44'24"E 15.75'
- 9 N87°44'24"E 10.17'
- 10 N83°08'13"W 15.22'
- 11 N88°19'44"W 13.96'
- 12 N54°57'10"W 18.13'

CURVE DATA: (THIS SHEET ONLY)

- ① Δ = 04°40'57" R = 223.00' L = 18.22'

NOTES:

SEE SHEET 2 FOR MONUMENT NOTES, EASEMENT
NOTES AND BASIS OF BEARINGS.

LOT A IS FOR A POCKET PARK; LOTS B THROUGH F
ARE FOR LANDSCAPING AND OPEN SPACE PURPOSES
AND ARE NOT SEPARATE BUILDING SITES.

SHEET 5 OF 5 SHEETS

TRACT NO. 16121

ALL OF VESTING TENTATIVE
TRACT NO. 16121

IN UNINCORPORATED TERRITORY OF ORANGE COUNTY, CALIFORNIA

APRIL 2001



JAMES F. GILLEN, L.S. 5557

DATE OF SURVEY:
DECEMBER 2000

HUITT-ZOLIARS

47 NUMBERED LOTS AND 6 LETTERED LOTS

10.301 ACRES

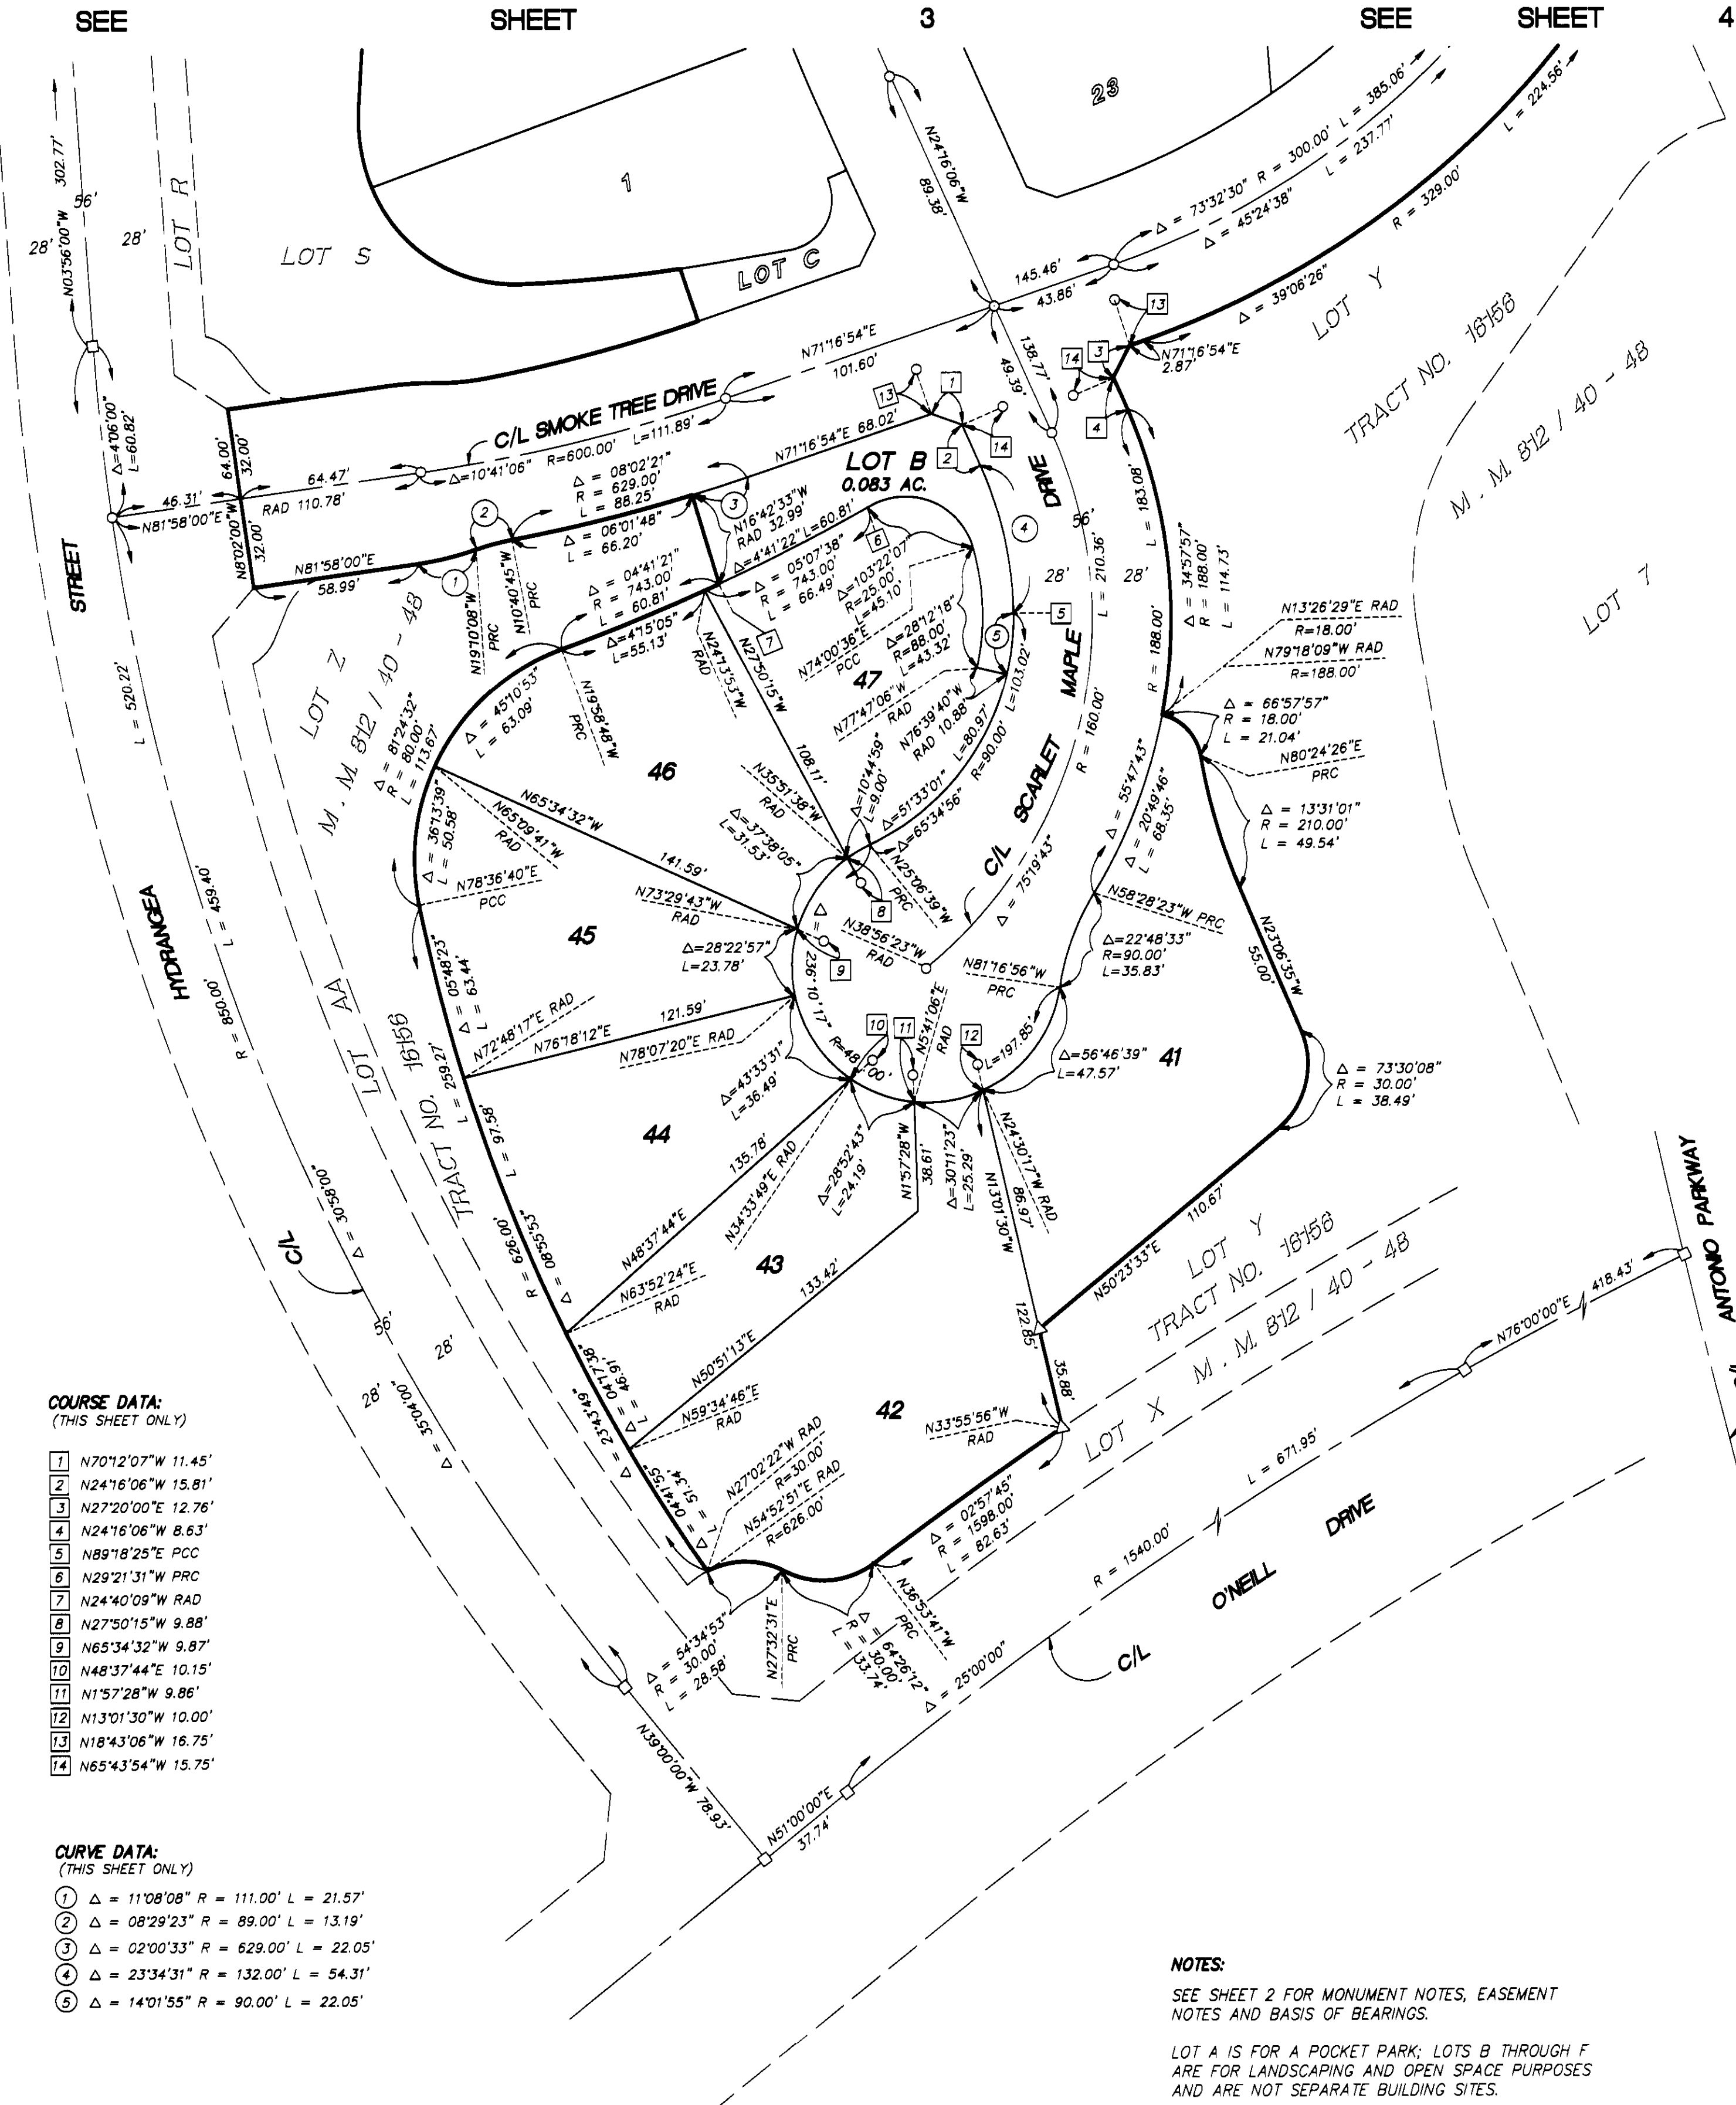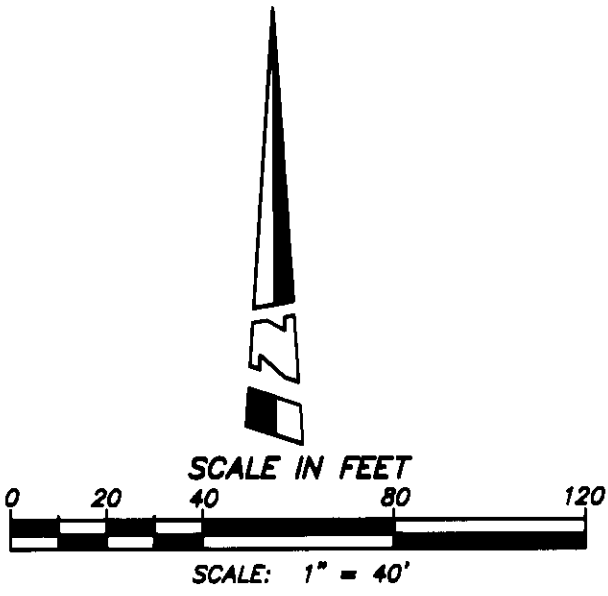

COURSE DATA:
(THIS SHEET ONLY)

- 1 N70°12'07"W 11.45'
- 2 N24°16'06"W 15.81'
- 3 N27°20'00"E 12.76'
- 4 N24°16'06"W 8.63'
- 5 N89°18'25"E PCC
- 6 N29°21'31"W PRC
- 7 N24°40'09"W RAD
- 8 N27°50'15"W 9.88'
- 9 N65°34'32"W 9.87'
- 10 N48°37'44"E 10.15'
- 11 N1°57'28"W 9.86'
- 12 N13°01'30"W 10.00'
- 13 N18°43'06"W 16.75'
- 14 N65°43'54"W 15.75'

CURVE DATA:
(THIS SHEET ONLY)

- 1 Δ = 11°08'08" R = 111.00' L = 21.57'
- 2 Δ = 08°29'23" R = 89.00' L = 13.19'
- 3 Δ = 02°00'33" R = 629.00' L = 22.05'
- 4 Δ = 23°34'31" R = 132.00' L = 54.31'
- 5 Δ = 14°01'55" R = 90.00' L = 22.05'

NOTES:

SEE SHEET 2 FOR MONUMENT NOTES, EASEMENT
NOTES AND BASIS OF BEARINGS.

LOT A IS FOR A POCKET PARK; LOTS B THROUGH F
ARE FOR LANDSCAPING AND OPEN SPACE PURPOSES
AND ARE NOT SEPARATE BUILDING SITES.