

SHEET 1 OF 5 SHEETS
29 NUMBERED LOTS AND 8
LETTERED LOTS
7.139 ACRES GROSS
ALL OF T.T.M. 16122
BLOCK 5157
MODULE 19

TRACT MAP NO. 16122

IN UNINCORPORATED TERRITORY OF ORANGE COUNTY
STATE OF CALIFORNIA

BEING A SUBDIVISION OF LOT 7 OF TRACT NO. 16156 AS SHOWN ON A MAP THEREOF
FILED IN BOOK 812 PAGES 40 THROUGH 48 OF MISCELLANEOUS MAPS, IN THE OFFICE
OF THE COUNTY RECORDER OF SAID ORANGE COUNTY

DAVID EVANS AND ASSOCIATES, INC.
CHARLES J. PRIOLO, R.C.E. #30790 FEBRUARY 2001

ACCEPTED AND FILED AT THE
REQUEST OF

FIRST AMERICAN TITLE INSURANCE CO.
DATE OCTOBER 26, 2001
TIME 1:41 P.M. FEES \$ 15.00
INSTRUMENT # 20010750424
BOOK 823 PAGE 34-38 N/M

GARY L. GRANVILLE
COUNTY CLERK-RECORDER
BY [Signature]
DEPUTY

OWNERSHIP CERTIFICATE:

WE, THE UNDERSIGNED, BEING ALL PARTIES HAVING ANY RECORD TITLE INTEREST IN
THE LAND COVERED BY THIS MAP, DO HEREBY CONSENT TO THE PREPARATION
AND RECORDATION OF SAID MAP, AS SHOWN WITHIN THE DISTINCTIVE BORDER LINE.

WE ALSO HEREBY DEDICATE TO THE PUBLIC FOR STREET PURPOSES CRAFTSBURY
PLACE AND STONEBRIER LANE.

WE ALSO HEREBY DEDICATE TO THE COUNTY OF ORANGE THE EASEMENT
FOR STORM DRAIN PURPOSES AS SHOWN ON SAID MAP.

WE ALSO HEREBY DEDICATE TO THE SANTA MARGARITA WATER DISTRICT THE
EASEMENTS FOR SEWER, WATER AND ACCESS PURPOSES AS SHOWN ON SAID MAP,
WHICH EASEMENTS SHALL BE SUBJECT TO THE SAME TERMS AND CONDITIONS AS
ARE SHOWN IN THAT CERTAIN EASEMENT RECORDED OCTOBER 6, 1980 IN BOOK
13776, PAGE 341, OF OFFICIAL RECORDS, COUNTY OF ORANGE. THE SANTA
MARGARITA WATER DISTRICT SHALL RESTORE OTHER IMPROVEMENTS OR FACILITIES
LOCATED WITHIN THE EASEMENT, IF IT HAS CONSENTED TO THE LOCATION OF SUCH
IMPROVEMENTS OR FACILITIES TO THE EXTENT THAT THE EXERCISE OF ITS RIGHTS
IN CONNECTION WITH THE EASEMENT IMPACTS OTHER IMPROVEMENTS OR FACILITIES
LOCATED WITHIN THE EASEMENT, HOWEVER, IN NO EVENT SHALL SANTA MARGARITA
WATER DISTRICT BE RESPONSIBLE FOR THE COST OF RELOCATING ITS FACILITIES
IN THE EVENT OF CONFLICTS WITH SUCH OTHER IMPROVEMENTS OR FACILITIES.

W. L. HOMES L.L.C. DBA JOHN LAING HOMES (CALIFORNIA), A DELAWARE LIMITED
LIABILITY COMPANY.

BY: Wayne Stelmor
PRINT NAME: WAYNE STELMAR
PRINT TITLE: CEO
DIVISION PRESIDENT

BY: [Signature]
PRINT NAME: DAVID DIRIENZO
PRINT TITLE: VICE PRESIDENT LAND DEVELOPMENT

DMB LADERA, L.L.C., A DELAWARE LIMITED LIABILITY COMPANY,
BENEFICIARY UNDER DEEDS OF TRUSTS RECORDED MARCH 16, 2001 AS
INSTRUMENT NO. 20010154668 AND RECORDED APRIL 12, 2001 AS INSTRUMENT
NO. 20010220692, BOTH OF OFFICIAL RECORDS.

BY: RANCHO MISSION VIEJO, L.L.C., A DELAWARE LIMITED LIABILITY COMPANY,
AS AGENT AND/OR MANAGER.

BY: Donalot Stahl
PRINT NAME: DONALOT STAHL
PRINT TITLE: DIRECTOR OF COMMUNITY DEVELOPMENT

BY: Stephen C. Schrank
PRINT NAME: Stephen C. Schrank
PRINT TITLE: Exec Vice President Development

WASHINGTON MUTUAL BANK, FA, A FEDERAL ASSOCIATION,
BENEFICIARY UNDER DEED OF TRUSTS RECORDED MARCH 16, 2001 AS
INSTRUMENT NO. 20010154669, OF OFFICIAL RECORDS

BY: Tom Griffin
PRINT NAME: TOM GRIFFIN
PRINT TITLE: SENIOR VICE PRESIDENT

BY: Kris Klinger
PRINT NAME: KRIS KLINGER
PRINT TITLE: VICE PRESIDENT

CERTIFICATE OF ACCEPTANCE:

THE UNDERSIGNED, BEING THE DULY APPOINTED AGENT OF THE SANTA MARGARITA
WATER DISTRICT, A PUBLIC CORPORATION OF ORANGE COUNTY, CALIFORNIA,
PURSUANT TO ITS RESOLUTION NO. 88-10-2, DOES HEREBY ACCEPT ON BEHALF
OF SAID DISTRICT THE EASEMENTS FOR SEWER, WATER, AND ACCESS PURPOSES,
AS DEDICATED AND AS SHOWN ON THIS TRACT MAP, BY AND BETWEEN THE SANTA
MARGARITA WATER DISTRICT AND W. L. HOMES, L.L.C., AND DOES HEREBY CERTIFY
THAT THE GRANTEE CONSENTS TO THE RECORDATION OF SAID TRACT.

[Signature]
DANIEL R. FERONS, CHIEF ENGINEER
SANTA MARGARITA WATER DISTRICT.

AUTOMATIC FIRE SPRINKLER NOTE:

ALL COMMERCIAL STRUCTURES GREATER THAN 6,000 SQUARE FEET; ALL
MULTIFAMILY RESIDENTIAL STRUCTURES; ALL SINGLE-FAMILY STRUCTURES EXCEEDING
5,500 SQUARE FEET, AND ALL STRUCTURES EXCEEDING FIRE DEPARTMENT ACCESS
REQUIREMENTS SHALL BE PROTECTED BY AN AUTOMATIC SPRINKLER SYSTEM.

SPECIAL FIRE PROTECTION NOTE:

PROPERTY IS TOTALLY EXCLUDED FROM A SPECIAL FIRE PROTECTION AREA.

HIGH FIRE HAZARD AREA NOTE:


THE LOTS SHOWN ON THIS MAP ARE IN A HIGH FIRE HAZARD AREA DUE TO WILD
LAND EXPOSURE.

NOTE:
SEE SHEET 2 FOR NOTARY ACKNOWLEDGEMENTS AND SIGNATURE OMISSIONS.

ENGINEER'S STATEMENT

I HEREBY STATE THAT THIS MAP CONSISTING OF 5 SHEETS, CORRECTLY
REPRESENTS TRUE AND COMPLETE SURVEY AS SHOWN MADE IN FEBRUARY, 2001;
WAS MADE BY ME OR UNDER MY DIRECTION; THAT THE MONUMENTS ARE OF THE
CHARACTER AND OCCUPY (OR WILL OCCUPY) THE POSITIONS INDICATED BY SAID
MAP; AND THAT SAID MONUMENTS ARE SUFFICIENT TO ENABLE THE SURVEY TO BE
RETRACTED.

Charles J. Priolo 7/23/01
CHARLES J. PRIOLO, R.C.E. #30790
LICENSE EXPIRES: 3/31/2004

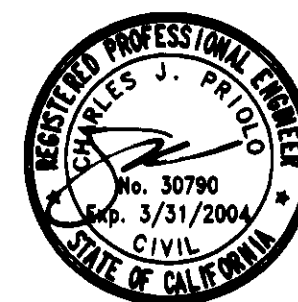

COUNTY SURVEYOR'S STATEMENT

I HEREBY STATE THAT I HAVE EXAMINED THIS MAP AND HAVE FOUND IT TO BE
SUBSTANTIALLY IN CONFORMANCE WITH THE TENTATIVE MAP AS FILED WITH,
AMENDED AND APPROVED BY THE ORANGE COUNTY SUBDIVISION COMMITTEE; THAT
ALL PROVISIONS OF THE SUBDIVISION MAP ACT AND COUNTY SUBDIVISION
REGULATIONS HAVE BEEN COMPLIED WITH AND I AM SATISFIED SAID MAP IS
TECHNICALLY CORRECT.

DATED THIS 20th DAY OF SEPT., 2001.

John Canas
JOHN CANAS, COUNTY SURVEYOR
LS 4408 EXPIRATION DATE: 9-30-01



COUNTY TREASURER-TAX COLLECTOR'S CERTIFICATE:

STATE OF CALIFORNIA)
COUNTY OF ORANGE) SS

I HEREBY CERTIFY THAT ACCORDING TO THE RECORDS OF MY OFFICE THERE ARE
NO LIENS AGAINST THE LAND COVERED BY THIS MAP OR ANY PART THEREOF FOR
UNPAID STATE COUNTY, MUNICIPAL OR LOCAL TAXES OR SPECIAL ASSESSMENTS
COLLECTED AS TAXES, EXCEPT TAXES OR SPECIAL ASSESSMENTS COLLECTED AS
TAXES NOT YET PAYABLE.
AND DO CERTIFY TO THE RECORDER OF ORANGE COUNTY THAT THE PROVISIONS
OF THE SUBDIVISION MAP ACT HAVE BEEN COMPLIED WITH REGARDING DEPOSITS
TO SECURE PAYMENT OF TAXES OR SPECIAL ASSESSMENTS COLLECTED AS TAXES
ON THE LAND COVERED BY THIS MAP.

DATED THIS 14th DAY OF August, 2001.

JOHN M. W. MOORLACH
COUNTY TREASURER-TAX COLLECTOR BY: Marja Jorgensen
DEPUTY TREASURER-TAX COLLECTOR

CLERK OF THE BOARD OF SUPERVISORS' CERTIFICATE

STATE OF CALIFORNIA)
COUNTY OF ORANGE) SS

I HEREBY CERTIFY THAT THIS MAP WAS PRESENTED FOR APPROVAL TO THE BOARD
OF SUPERVISORS OF ORANGE COUNTY AT A REGULAR MEETING THEREOF HELD ON
THE 23rd DAY OF October, 2001 AND THAT
THEREUPON SAID BOARD DID, BY AN ORDER DULY PASSED AND ENTERED,
APPROVE SAID MAP AND DID ACCEPT ON BEHALF OF THE PUBLIC, SUBJECT TO
IMPROVEMENTS; THE DEDICATION FOR STREET PURPOSES OF CRAFTSBURY PLACE
AND STONEBRIER LANE.

AND DID ALSO ACCEPT ON BEHALF OF THE COUNTY OF ORANGE THE EASEMENT
FOR STORM DRAIN PURPOSES AS DEDICATED.

AND DID ALSO APPROVE SUBJECT MAP PURSUANT TO THE PROVISIONS OF SECTION
66436(a)(3)(A) OF THE SUBDIVISION MAP ACT.

DATED THIS 23rd DAY OF October, 2001.

Darlene J. Bloom
DARLENE J. BLOOM
CLERK OF THE BOARD OF SUPERVISORS



SHEET 2 OF 5 SHEETS
29 NUMBERED LOTS AND 6
LETTERED LOTS
7.139 ACRES GROSS
ALL OF T.T.M. 16122

TRACT MAP NO. 16122

IN UNINCORPORATED TERRITORY OF ORANGE COUNTY
STATE OF CALIFORNIA

DAVID EVANS AND ASSOCIATES, INC.

CHARLES J. PRIOLO, R.C.E. #30790 FEBRUARY 2001

NOTARY ACKNOWLEDGEMENT

W. L. HOMES, L.L.C.

STATE OF CALIFORNIA)
)SS
COUNTY OF ORANGE)

ON THIS 24th DAY OF July, 2001, BEFORE ME,
KATHLEEN A. Hoyt A NOTARY PUBLIC IN AND FOR SAID STATE,
PERSONALLY APPEARED Wayne J. Stelmach AND
PERSONALLY KNOWN TO ME (OR
PROVED TO ME ON THE BASIS OF SATISFACTORY EVIDENCE) TO BE THE PERSONS
WHOSE NAMES ARE SUBSCRIBED TO THE WITHIN INSTRUMENT AND ACKNOWLEDGED
TO ME THAT HE/SHE/they EXECUTED THE SAME IN HIS/HER/their AUTHORIZED
CAPACITIES, AND THAT BY HIS/HER/their SIGNATURES ON THE INSTRUMENT THE
PERSONS, OR THE ENTITY UPON BEHALF OF WHICH THE PERSON ACTED, EXECUTED
THE INSTRUMENT.

WITNESS MY HAND:

MY COMMISSION EXPIRES: Aug 15, 2001

Kathleen A. Hoyt MY PRINCIPAL PLACE OF BUSINESS
NOTARY PUBLIC IN AND FOR SAID STATE IS IN Orange COUNTY.

KATHLEEN A. Hoyt
PRINT NAME

NOTARY ACKNOWLEDGEMENT

W. L. HOMES, L.L.C.

STATE OF CALIFORNIA)
)SS
COUNTY OF ORANGE)

ON THIS 24th DAY OF July, 2001, BEFORE ME,
David D. Dierckx A NOTARY PUBLIC IN AND FOR SAID STATE,
PERSONALLY APPEARED David Dierckx AND
PERSONALLY KNOWN TO ME (OR
PROVED TO ME ON THE BASIS OF SATISFACTORY EVIDENCE) TO BE THE PERSONS
WHOSE NAMES ARE SUBSCRIBED TO THE WITHIN INSTRUMENT AND ACKNOWLEDGED
TO ME THAT HE/SHE/they EXECUTED THE SAME IN HIS/HER/their AUTHORIZED
CAPACITIES, AND THAT BY HIS/HER/their SIGNATURES ON THE INSTRUMENT THE
PERSONS, OR THE ENTITY UPON BEHALF OF WHICH THE PERSON ACTED, EXECUTED
THE INSTRUMENT.

WITNESS MY HAND:

MY COMMISSION EXPIRES: 10-14-01

Amy Day MY PRINCIPAL PLACE OF BUSINESS
NOTARY PUBLIC IN AND FOR SAID STATE IS IN Orange COUNTY.

Amy Day
PRINT NAME

NOTARY ACKNOWLEDGEMENT

DMB LADERA, L.L.C.

STATE OF CALIFORNIA)
)SS
COUNTY OF ORANGE)

ON THIS 31st DAY OF July, 2001, BEFORE ME,
Tina T. Baker A NOTARY PUBLIC IN AND FOR SAID STATE,
PERSONALLY APPEARED Donald T. Stehlin AND
Stephen C. Schenk PERSONALLY KNOWN TO ME (OR
PROVED TO ME ON THE BASIS OF SATISFACTORY EVIDENCE) TO BE THE PERSONS
WHOSE NAMES ARE SUBSCRIBED TO THE WITHIN INSTRUMENT AND ACKNOWLEDGED
TO ME THAT HE/SHE/they EXECUTED THE SAME IN HIS/HER/their AUTHORIZED
CAPACITIES, AND THAT BY HIS/HER/their SIGNATURES ON THE INSTRUMENT THE
PERSONS, OR THE ENTITY UPON BEHALF OF WHICH THE PERSON ACTED, EXECUTED
THE INSTRUMENT.

WITNESS MY HAND:

MY COMMISSION EXPIRES: 8/29/04

Jana J. Baker MY PRINCIPAL PLACE OF BUSINESS
NOTARY PUBLIC IN AND FOR SAID STATE IS IN Orange COUNTY.

Tina T. Baker
PRINT NAME

NOTARY ACKNOWLEDGEMENT

DMB LADERA, L.L.C.

STATE OF CALIFORNIA)
)SS
COUNTY OF ORANGE)

ON THIS _____ DAY OF _____, 2001, BEFORE ME,
_____ A NOTARY PUBLIC IN AND FOR SAID STATE,
PERSONALLY APPEARED _____ AND
PERSONALLY KNOWN TO ME (OR
PROVED TO ME ON THE BASIS OF SATISFACTORY EVIDENCE) TO BE THE PERSONS
WHOSE NAMES ARE SUBSCRIBED TO THE WITHIN INSTRUMENT AND ACKNOWLEDGED
TO ME THAT HE/SHE/they EXECUTED THE SAME IN HIS/HER/their AUTHORIZED
CAPACITIES, AND THAT BY HIS/HER/their SIGNATURES ON THE INSTRUMENT THE
PERSONS, OR THE ENTITY UPON BEHALF OF WHICH THE PERSON ACTED, EXECUTED
THE INSTRUMENT.

WITNESS MY HAND:

MY COMMISSION EXPIRES: _____

_____ MY PRINCIPAL PLACE OF BUSINESS
NOTARY PUBLIC IN AND FOR SAID STATE IS IN _____ COUNTY.

PRINT NAME

SIGNATURE OMISSIONS:

IN ACCORDANCE WITH THE PROVISIONS OF SECTION 66436(a)(3)(A) OF THE
SUBDIVISION MAP ACT, THE FOLLOWING SIGNATURE HAS BEEN OMITTED:

1. LADERA DEVELOPMENT COMPANY, L.L.C., HOLDER OF OIL, GAS, MINERAL, AND
WATER RIGHTS RECORDED DECEMBER 10, 1996 AS INSTRUMENT NO. 19960624029
OF OFFICIAL RECORDS.

NOTARY ACKNOWLEDGEMENT

WASHINGTON MUTUAL BANK, FA.

STATE OF CALIFORNIA)
 San Diego)SS
COUNTY OF ORANGE)

ON THIS 2nd DAY OF August, 2001, BEFORE ME,
Terri L. Castellanos A NOTARY PUBLIC IN AND FOR SAID STATE,
PERSONALLY APPEARED Kris Klinger AND
PERSONALLY KNOWN TO ME (OR
PROVED TO ME ON THE BASIS OF SATISFACTORY EVIDENCE) TO BE THE PERSONS
WHOSE NAMES ARE SUBSCRIBED TO THE WITHIN INSTRUMENT AND ACKNOWLEDGED
TO ME THAT HE/SHE/they EXECUTED THE SAME IN HIS/HER/their AUTHORIZED
CAPACITIES, AND THAT BY HIS/HER/their SIGNATURES ON THE INSTRUMENT THE
PERSONS, OR THE ENTITY UPON BEHALF OF WHICH THE PERSON ACTED, EXECUTED
THE INSTRUMENT.

WITNESS MY HAND:

MY COMMISSION EXPIRES: 1-2-04

Terri L. Castellanos MY PRINCIPAL PLACE OF BUSINESS
NOTARY PUBLIC IN AND FOR SAID STATE IS IN San Diego COUNTY.

Terri L. Castellanos
PRINT NAME

NOTARY ACKNOWLEDGEMENT

WASHINGTON MUTUAL BANK, FA.

STATE OF CALIFORNIA)
 San Diego)SS
COUNTY OF ORANGE)

ON THIS 6th DAY OF August, 2001, BEFORE ME,
Terri L. Castellanos A NOTARY PUBLIC IN AND FOR SAID STATE,
PERSONALLY APPEARED Tom Griffin AND
PERSONALLY KNOWN TO ME (OR
PROVED TO ME ON THE BASIS OF SATISFACTORY EVIDENCE) TO BE THE PERSONS
WHOSE NAMES ARE SUBSCRIBED TO THE WITHIN INSTRUMENT AND ACKNOWLEDGED
TO ME THAT HE/SHE/they EXECUTED THE SAME IN HIS/HER/their AUTHORIZED
CAPACITIES, AND THAT BY HIS/HER/their SIGNATURES ON THE INSTRUMENT THE
PERSONS, OR THE ENTITY UPON BEHALF OF WHICH THE PERSON ACTED, EXECUTED
THE INSTRUMENT.

WITNESS MY HAND:

MY COMMISSION EXPIRES: 1-2-04

Terri L. Castellanos MY PRINCIPAL PLACE OF BUSINESS
NOTARY PUBLIC IN AND FOR SAID STATE IS IN San Diego COUNTY.

Terri L. Castellanos
PRINT NAME

NOTARY ACKNOWLEDGEMENT

SANTA MARGARITA WATER DISTRICT

STATE OF CALIFORNIA)
)SS
COUNTY OF ORANGE)

ON THIS 10th DAY OF August, 2001, BEFORE ME,
ANDREA M. EVANS A NOTARY PUBLIC IN AND FOR SAID STATE,
PERSONALLY APPEARED DANIEL R. FERONS AND

PERSONALLY KNOWN TO ME (OR
PROVED TO ME ON THE BASIS OF SATISFACTORY EVIDENCE) TO BE THE PERSONS
WHOSE NAMES ARE SUBSCRIBED TO THE WITHIN INSTRUMENT AND ACKNOWLEDGED
TO ME THAT HE/SHE/they EXECUTED THE SAME IN HIS/HER/their AUTHORIZED
CAPACITIES, AND THAT BY HIS/HER/their SIGNATURES ON THE INSTRUMENT THE
PERSONS, OR THE ENTITY UPON BEHALF OF WHICH THE PERSON ACTED, EXECUTED
THE INSTRUMENT.

WITNESS MY HAND:

MY COMMISSION EXPIRES: 04-08-04

Andrea M. Evans MY PRINCIPAL PLACE OF BUSINESS
NOTARY PUBLIC IN AND FOR SAID STATE IS IN ORANGE COUNTY.

ANDREA M. EVANS
PRINT NAME


**SHEET 3 OF 5 SHEETS
29 NUMBERED LOTS AND 6
LETTERED LOTS
7.139 ACRES GROSS
ALL OF T.T.M. 16122**

TRACT MAP NO. 16122

IN UNINCORPORATED TERRITORY OF ORANGE COUNTY
STATE OF CALIFORNIA

DAVID EVANS AND ASSOCIATES, INC.

CHARLES J. PRIOLO, R.C.E. #30790 FEBRUARY 2001

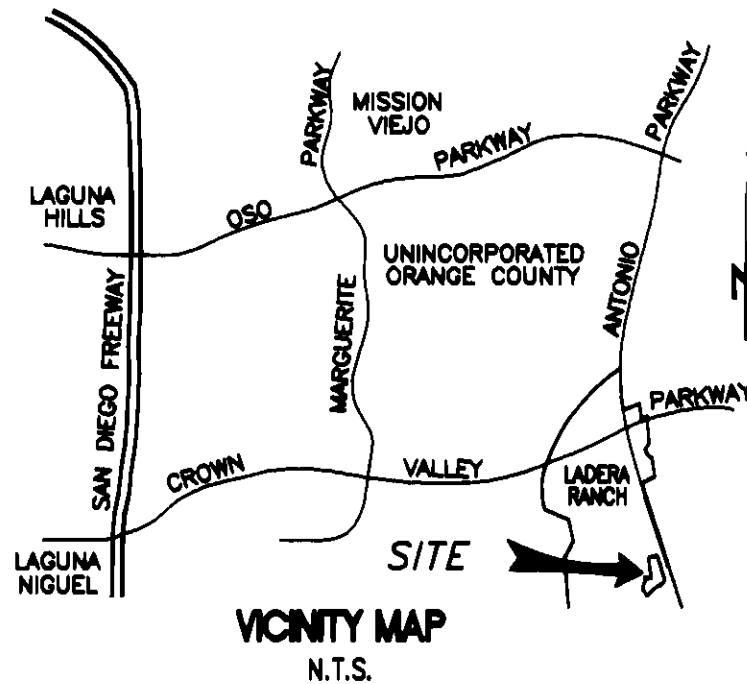

GPS POINT LOCATION

GPS NO. 1448 2 1/2 IRON PIPE W/2" OCS BRASS CAP STAMPED "GPS 1448
N 2146790.819 9-95" PER TR. 16156 M.M. 812/40-48 AND RECORDS ON FILE
E 6142602.585 IN THE ORANGE COUNTY SURVEYOR OFFICE

GPS NO. 1417 2 1/2 IRON PIPE W/2" BRASS CAP STAMPED "GPS 1417
N 2141450.558 9-95" PER TR. 16156 M.M. 812/40-48 AND RECORDS ON
E 6141583.535 FILE IN THE ORANGE COUNTY SURVEYOR OFFICE

BASIS OF BEARINGS

THE BEARINGS SHOWN HEREON ARE BASED UPON THE BEARING BETWEEN O.C.S.
HORIZONTAL CONTROL STATION GPS NO. 1417 AND STATION GPS NO. 1448 BEING
N10°48'13"E PER RECORDS ON FILE IN THE OFFICE OF THE ORANGE COUNTY RECORDER

DATUM STATEMENT

COORDINATES SHOWN ARE BASED ON CALIFORNIA COORDINATE SYSTEM, (CCS83) ZONE VI, 1983 NAD, (1991.35 EPOCH OCS GPS ADJUSTMENT)

ALL DISTANCES SHOWN ARE GROUND, UNLESS OTHERWISE NOTED. TO OBTAIN GRID DISTANCES MULTIPLY GROUND DISTANCE BY 0.99993286

MONUMENT NOTES


1. ALL MONUMENTS SHOWN AS SET WILL BE SET WITHIN 90 DAYS AFTER THE ACCEPTANCE OF IMPROVEMENTS EXCEPT AS NOTED.
2. TIES TO CENTERLINE MONUMENTS WILL BE MADE AND A COPY OF SAID TIES WILL BE FURNISHED TO THE COUNTY SURVEYOR.
3. SET 1" IRON PIPE TAGGED "R.C.E. 30790" AT ALL LOT CORNERS EXCEPT LOT CORNERS THAT ABOUT A STREET WHICH WILL BE MARKED ON AN 9.75' OFFSET INSIDE STREET RIGHT-OF-WAY IN CONCRETE CURB BY A LEAD, TACK AND TAG "R.C.E. 30790" ON SIDELINES PRODUCED, EXCEPT COMMON CORNERS FOR LOTS 5-6, 13-14, WHICH WILL BE SET ON AN 15.75' OFFSET, AND THE COMMON CORNER FOR LOTS 14-15, WHICH WILL BE SET ON AN 11.25' OFFSET, UNLESS OTHERWISE NOTED. (NO MONUMENTS WILL BE SET FOR ANGLE POINTS, CORNER CUTOFFS, B.C. E.C. P.C.C. OR P.R.C. THAT ABOUT A STREET WHICH ARE NOT LOT CORNERS MARKING SIDELINES, UNLESS OTHERWISE NOTED).
4. SET 2" IRON PIPE TAGGED "R.C.E. 30790" OR A SPIKE W/BRASS WASHER STAMPED "R.C.E. 30790" IN ASPHALT HAVING A THICKNESS OF 2" OR MORE AT ALL TRACT BOUNDARY CORNERS, EXCEPT BOUNDARY CORNERS THAT ABOUT A STREET WHICH WILL BE MARKED ON AN OFFSET INSIDE THE STREET RIGHT-OF-WAY IN CONCRETE CURB BY A LEAD, TACK AND TAG "R.C.E. 30790" ON EITHER A RADIAL OR PERPENDICULAR LINE TO STREET CENTERLINE, UNLESS OTHERWISE NOTED. (NO MONUMENTS WILL BE SET FOR ANGLE POINTS, CORNER CUTOFF, B.C. E.C. P.C.C. OR P.R.C. THAT ABOUT A STREET WHICH ARE NOT BOUNDARY CORNERS, UNLESS OTHERWISE NOTED)
5. SET LEAD, TACK AND TAG "R.C.E. 30790" IN CONCRETE OR A SPIKE W/BRASS WASHER STAMPED "R.C.E. 30790" AT ALL STREET CENTERLINE POINTS OF CONTROL, UNLESS OTHERWISE NOTED.
6. ▲ INDICATES FOUND MONUMENTS AS NOTED
7. ■ INDICATES 2" I.P. TAGGED "P.L.S. 5557" OR SPIKE & WASHER STAMPED "P.L.S. 5557" OR LEAD, TACK & TAG "P.L.S. 5557" TO BE SET PER TRACT NO. 16156, M.M. 812/40-48.
8. □ INDICATES 2" IP WITH 3/8" BRASS DISK (UNLESS NOTED OTHERWISE) SET IN CONCRETE, STAMPED "R.C.E. 30790" PRIOR TO RECORDATION.

EASEMENT NOTES:

- (A) INDICATES 20' WIDE EASEMENT FOR SEWER, WATER AND ACCESS PURPOSES DEDICATED HEREON TO THE SANTA MARGARITA WATER DISTRICT.
- (B) INDICATES 40' WIDE EASEMENT FOR SEWER, WATER AND ACCESS PURPOSES DEDICATED HEREON TO THE SANTA MARGARITA WATER DISTRICT.
- (C) INDICATES 40' WIDE EASEMENT FOR STORM DRAIN PURPOSES DEDICATED HEREON TO THE COUNTY OF ORANGE.
- (D) INDICATES 40' WIDE EXISTING EASEMENT FOR SEWER, WATER AND ACCESS PURPOSES DEDICATED PER TRACT 16156 TO THE SANTA MARGARITA WATER DISTRICT.
- (E) INDICATES 40' WIDE EXISTING EASEMENT FOR STORM DRAIN PURPOSES DEDICATED PER TRACT 16156 TO THE COUNTY OF ORANGE.
- (F) INDICATES 20' WIDE EXISTING EASEMENT FOR SEWER, WATER AND ACCESS PURPOSES DEDICATED PER TRACT 16156 TO THE SANTA MARGARITA WATER DISTRICT.

NOTES:



1. LOTS "A" AND "B" ARE PROPOSED TO BE GRANTED IN FEE TO THE HOMEOWNERS ASSOCIATION FOR POCKET PARK PURPOSES.
2. LOTS "C", "D", "E" AND "F" ARE PROPOSED TO BE GRANTED IN FEE TO THE HOMEOWNERS ASSOCIATION FOR LANDSCAPE MAINTENANCE PURPOSES.
3. LOTS "A" THROUGH "F" ARE NOT SEPARATE BUILDING SITES.

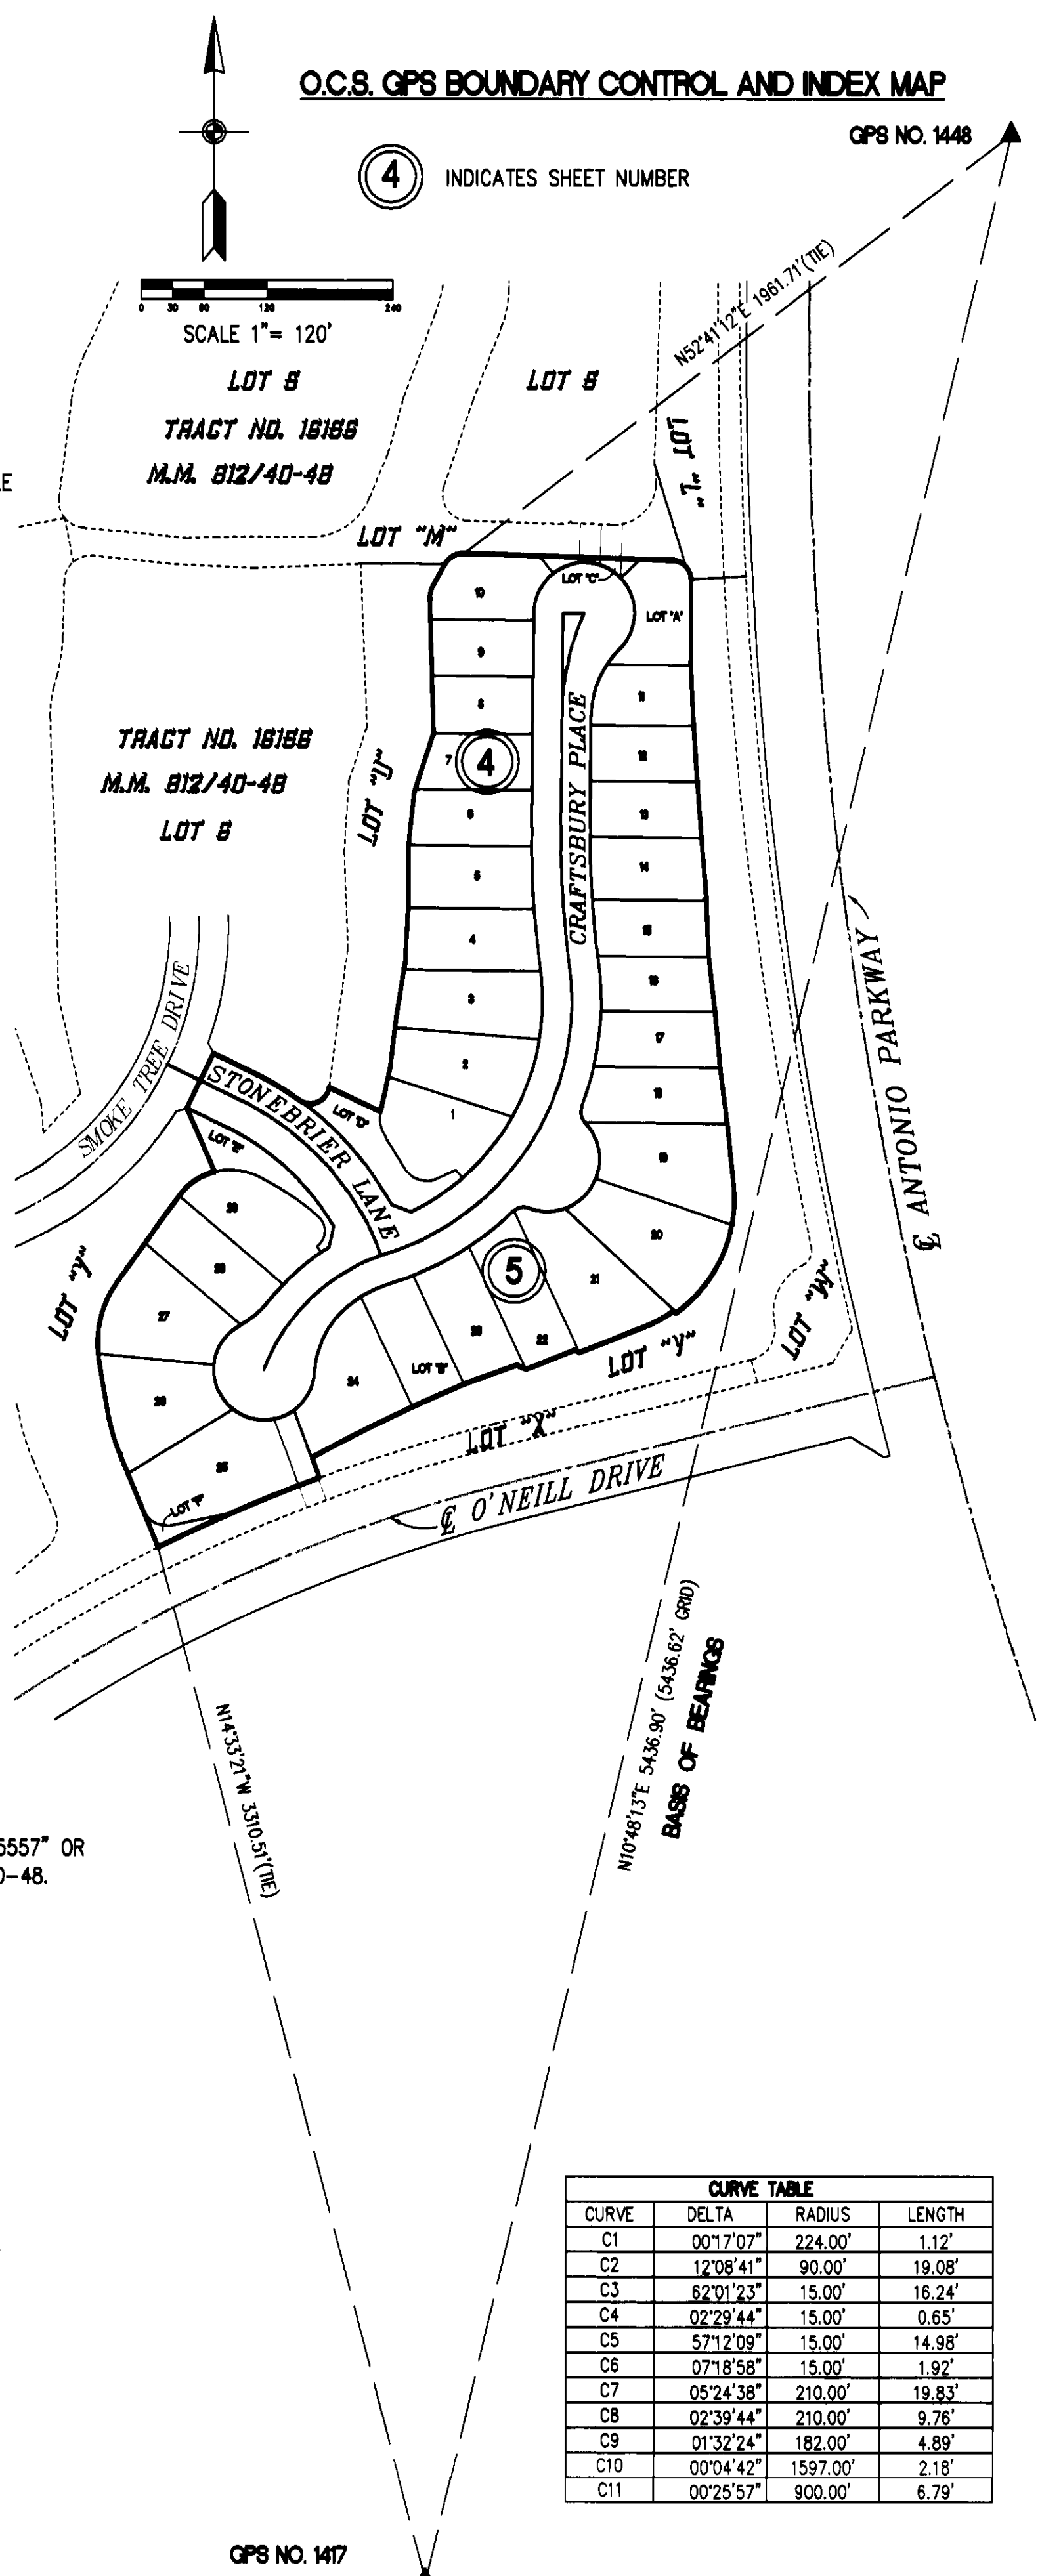

CURVE	DELTA	RADIUS	LENGTH
C1	00°17'07"	224.00'	1.12'
C2	12°08'41"	90.00'	19.08'
C3	62°01'23"	15.00'	16.24'
C4	02°29'44"	15.00'	0.65'
C5	57°12'09"	15.00'	14.98'
C6	07°18'58"	15.00'	1.92'
C7	05°24'38"	210.00'	19.83'
C8	02°39'44"	210.00'	9.76'
C9	01°32'24"	182.00'	4.89'
C10	00°04'42"	1597.00'	2.18'
C11	00°25'57"	990.00'	6.70'

DAVID EVANS AND ASSOCIATES, INC.
CHARLES J. PRIOLO, R.C.E. #30790 FEBRUARY 2001


NOTE:
SEE SHEET 3 FOR BASIS OF BEARINGS, DATUM
STATEMENT, GPS POINT LOCATION, MONUMENT AND
EASEMENT NOTES, CURVES AND LINES DATA
TABLES

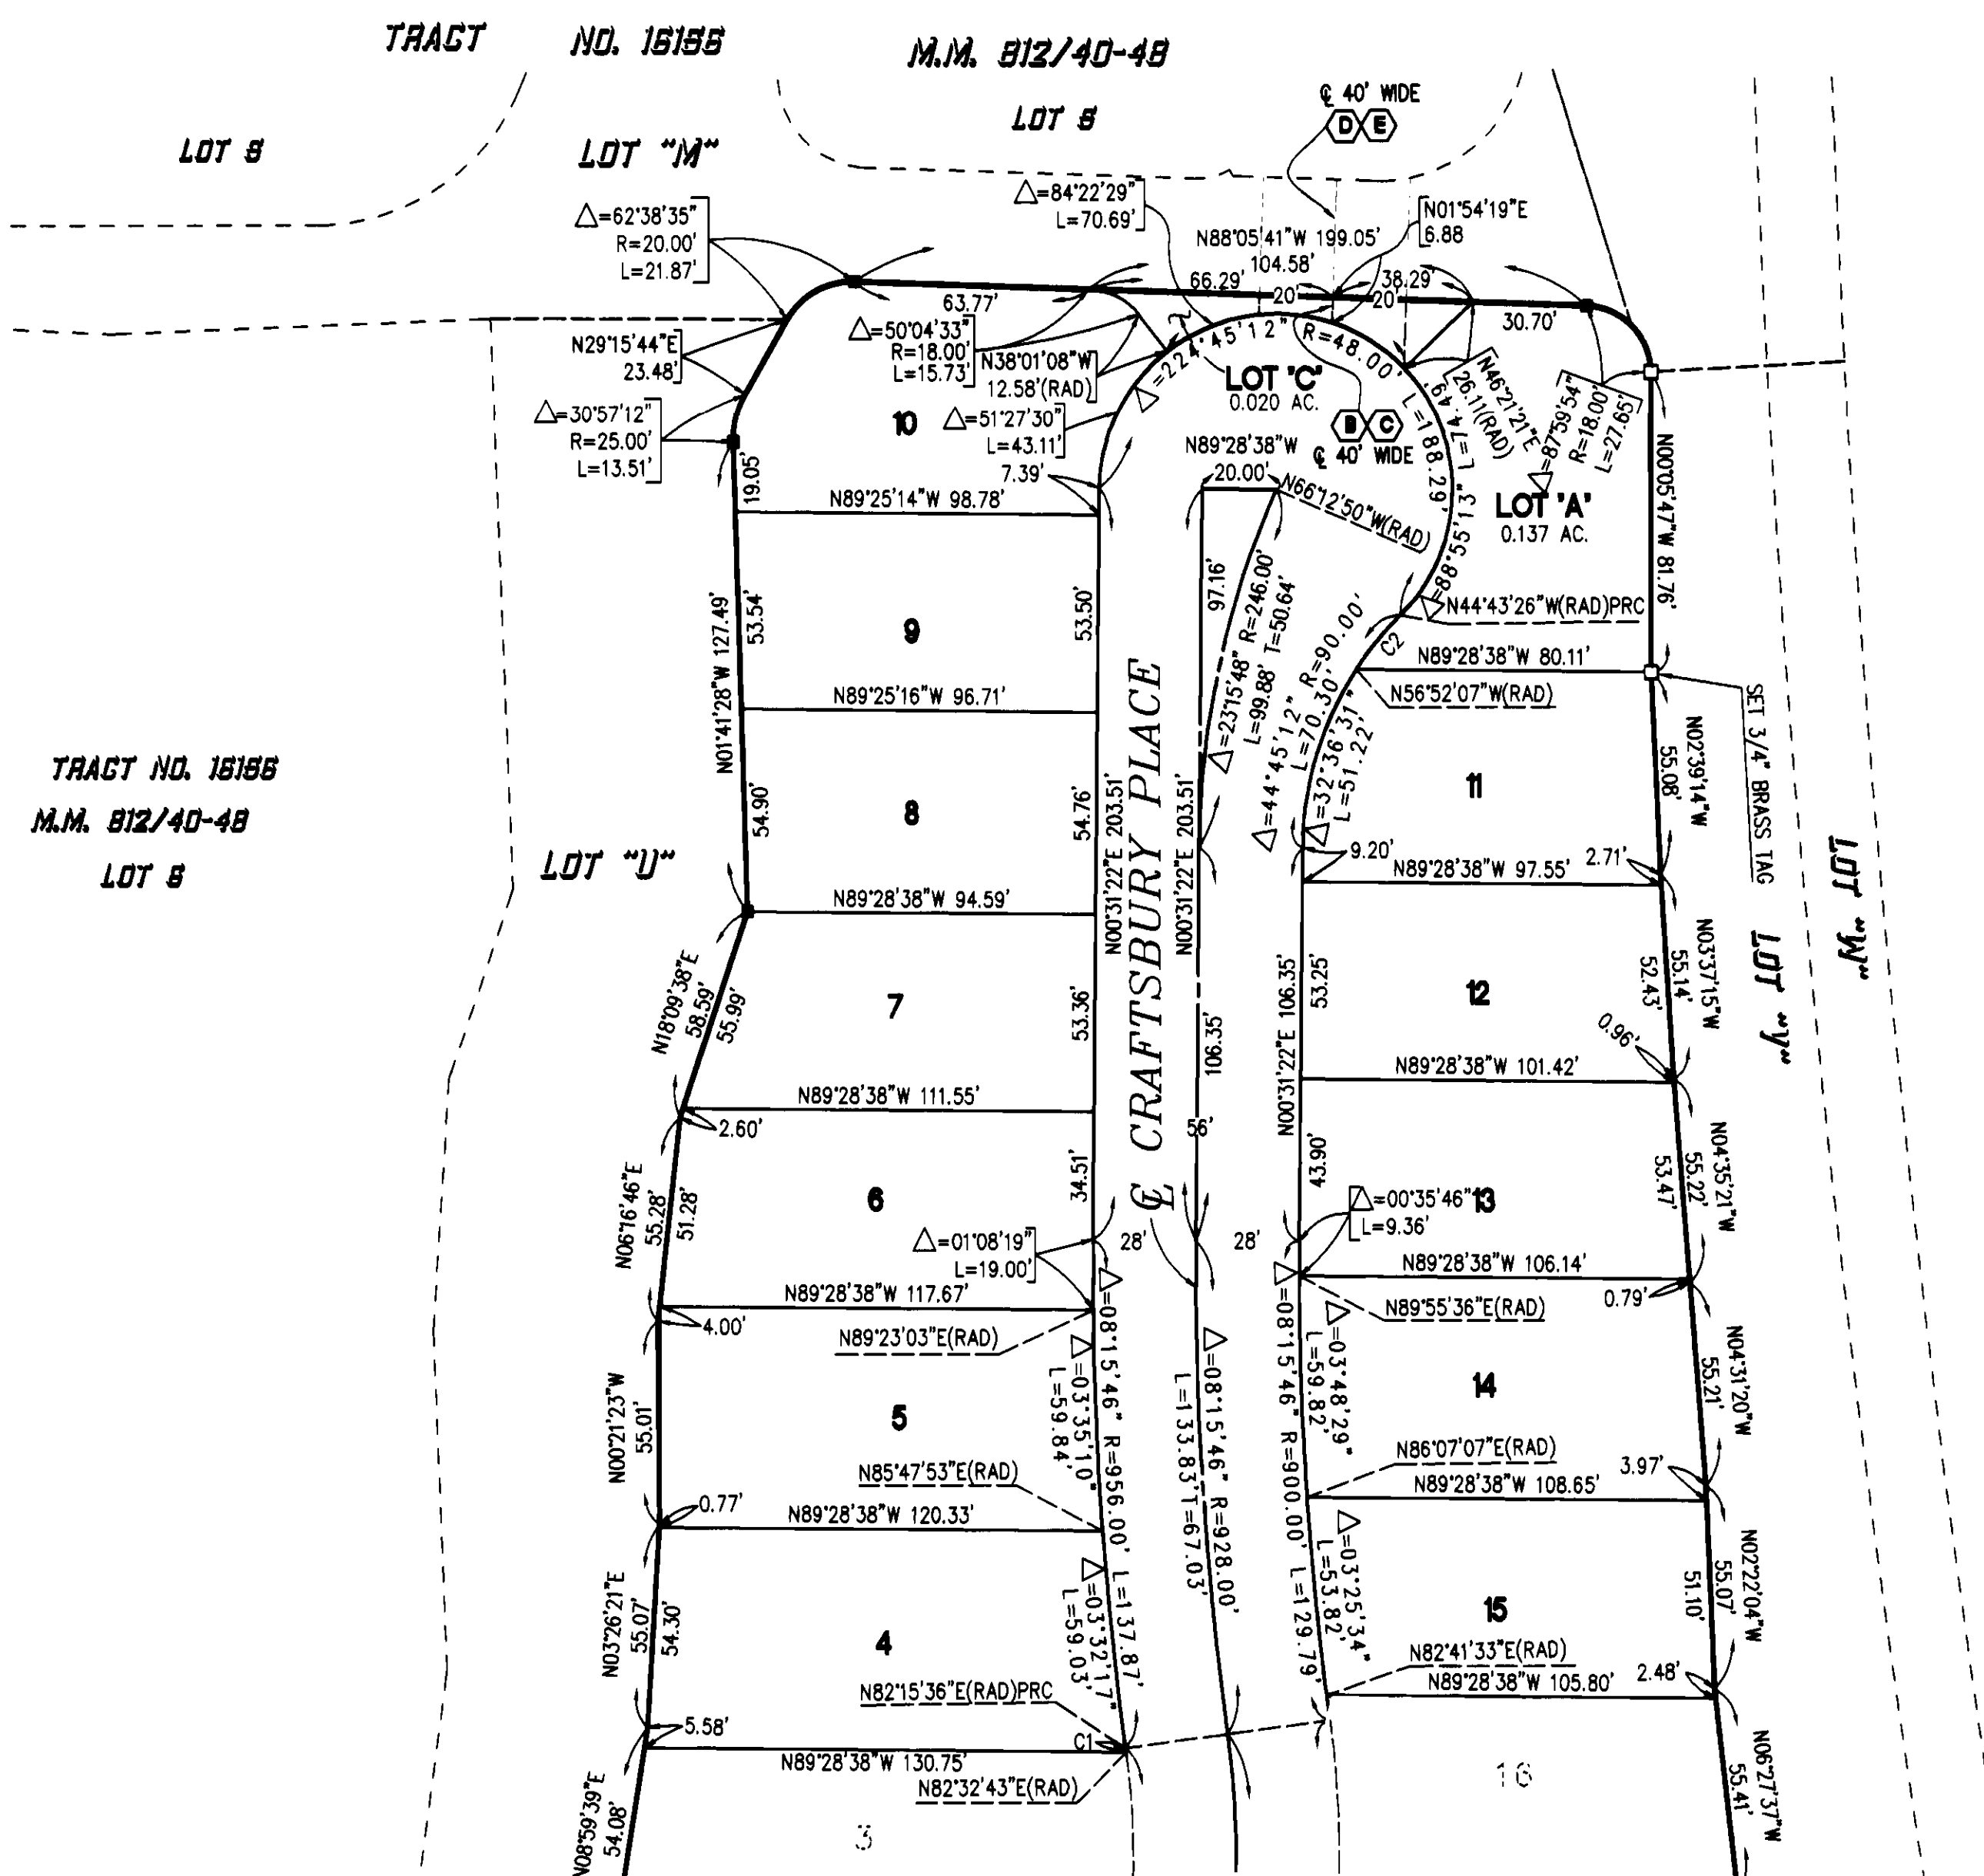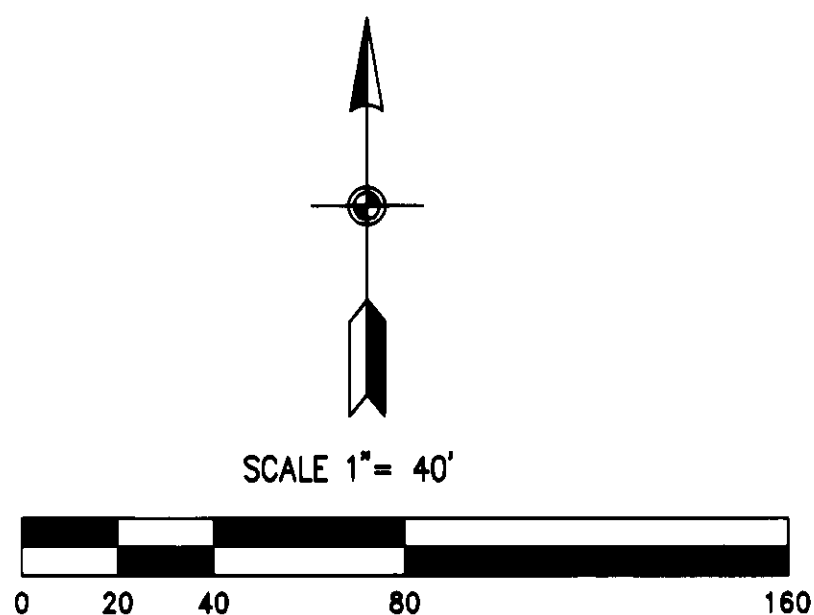


SEE SHEET 5

DAVID EVANS AND ASSOCIATES, INC.
CHARLES J. PRIOLO, R.C.E. #30790 FEBRUARY 2001


NOTE:
SEE SHEET 3 FOR BASIS OF BEARINGS, DATUM
STATEMENT, GPS POINT LOCATION, MONUMENT AND
EASEMENT NOTES, CURVES AND LINES DATA
TABLES

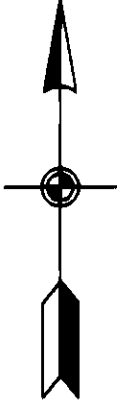

SCALE 1" = 40'

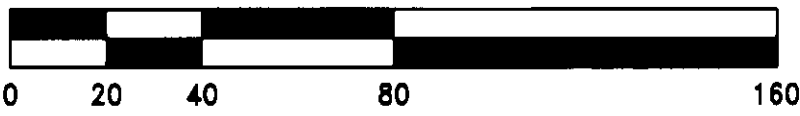

SEE SHEET 4

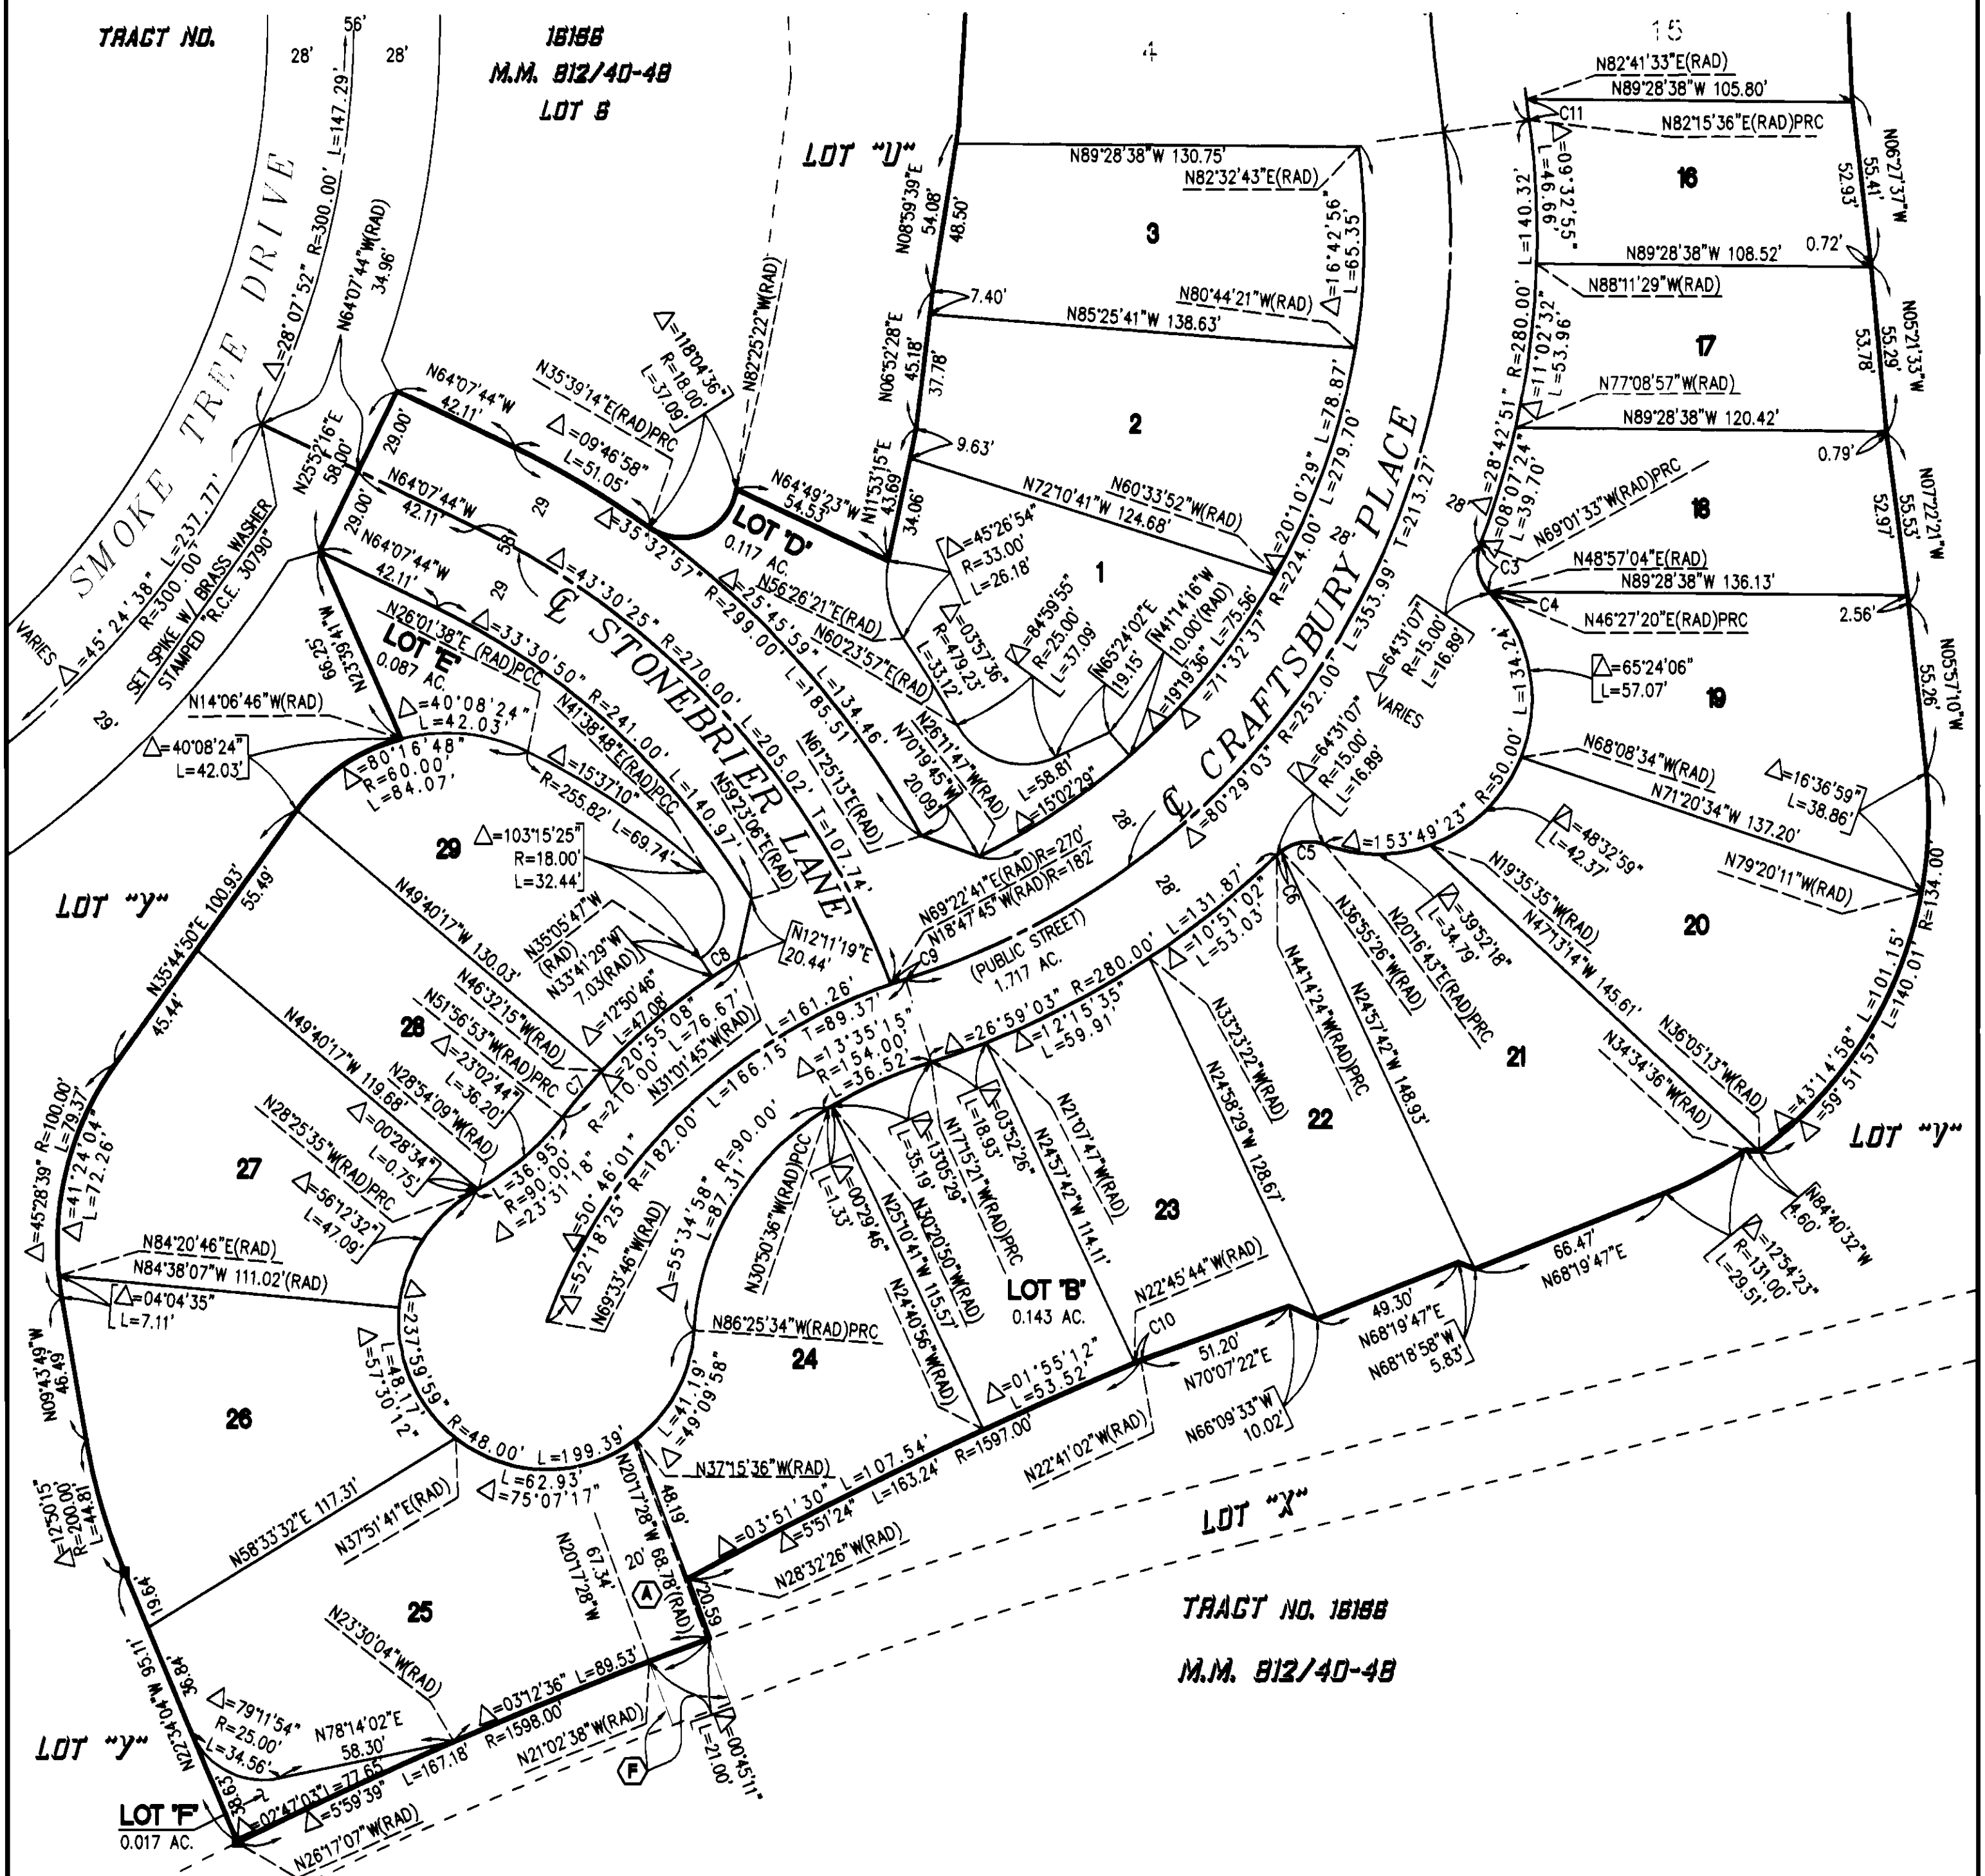

TRACT NO. 16155

M.M. 812/40-48

827

38