

SHEET 1 OF 6 SHEETS
64 NUMBERED LOTS AND LOTS
A THROUGH M, INCLUSIVE
ACREAGE: 6.021 ACRES
(ALL OF TENTATIVE
TRACT NO. 16126)

TRACT NO. 16126

IN UNINCORPORATED TERRITORY OF THE
COUNTY OF ORANGE, STATE OF CALIFORNIA.

BEING A SUBDIVISION OF LOTS 2, C AND D OF TRACT NO. 16156, AS SHOWN ON A MAP FILED IN
BOOK 812, PAGES 40 THROUGH 48, INCLUSIVE, OF MISCELLANEOUS MAPS, IN THE OFFICE OF
THE COUNTY RECORDER OF SAID COUNTY OF ORANGE.

BLOCK: 5157
MODULES: 16 & 17

HUNSAKER AND ASSOCIATES IRVINE, INC.
RORY S. WILLIAMS, L.S. 6654 DATE OF SURVEY: DECEMBER, 2000

ACCEPTED AND FILED AT THE
REQUEST OF

FIRST AMERICAN TITLE INSURANCE CO.

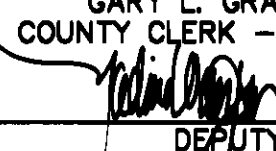
DATE: NOVEMBER 8, 2001

TIME: 8:45 A.M. FEE: \$17.00

INSTRUMENT NO. 20010799594

BOOK 824 PAGE 15-20 M/M

GARY L. GRANVILLE
COUNTY CLERK - RECORDER

BY  DEPUTY

OWNERSHIP CERTIFICATE:

WE, THE UNDERSIGNED, BEING ALL PARTIES HAVING ANY RECORD TITLE INTEREST IN THE LAND COVERED BY THIS MAP, DO HEREBY CONSENT TO THE PREPARATION AND RECORDATION OF SAID MAP, AS SHOWN WITHIN THE DISTINCTIVE BORDER LINE.

WE HEREBY DEDICATE TO THE COUNTY OF ORANGE:

AN EASEMENT FOR INGRESS AND EGRESS OF EMERGENCY AND PUBLIC SERVICE VEHICLES OVER LOT D, AS SHOWN ON THIS MAP.

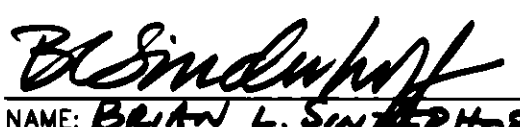
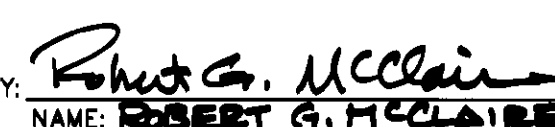
WE RESERVE TO OURSELVES, OUR SUCCESSORS AND ASSIGNS THE PUBLIC UTILITY EASEMENTS SHOWN ON THIS MAP, FOR THE USE AND BENEFIT OF THE VARIOUS UTILITY COMPANIES AUTHORIZED TO PROVIDE SERVICE TO THE LOTS SHOWN HEREON.

WE ALSO DO HEREBY DECLARE THAT THE LAND COVERED BY THIS MAP IS LOCATED IN A HIGH FIRE HAZARD AREA DUE TO WILDLAND EXPOSURE BASED ON STATE SRA MAPS.

WE ALSO HEREBY DEDICATE TO THE SANTA MARGARITA WATER DISTRICT THE PIPELINE EASEMENTS FOR WATER, SEWER AND ACCESS PURPOSES, ALL AS SHOWN ON THIS TRACT MAP, WHICH EASEMENTS SHALL BE SUBJECT TO THE SAME TERMS AND CONDITIONS AS SHOWN IN THAT CERTAIN EASEMENT RECORDED OCTOBER 6, 1980, IN BOOK 13776, PAGE 341 OF OFFICIAL RECORDS OF ORANGE COUNTY, CALIFORNIA.

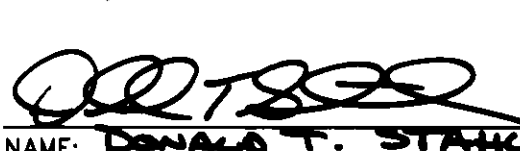
WARMINGTON LDR ASSOCIATES III, L.P., A CALIFORNIA LIMITED PARTNERSHIP, OWNER.

BY: WARMINGTON HOMES CALIFORNIA, ITS GENERAL PARTNER.

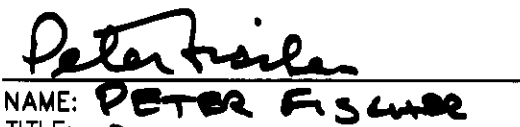
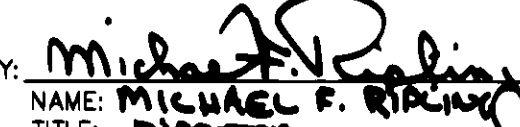
BY:  NAME: BRIAN L. SINTERHOFF TITLE: President, So. Cal. Division
BY:  NAME: ROBERT G. MCCLAIRE TITLE: VP PROJECT DEVELOPMENT

DMB LADERA, L.L.C., A DELAWARE LIMITED LIABILITY COMPANY, BENEFICIARY UNDER A DEED OF TRUST RECORDED AS INSTRUMENT NO. 20010110195 OF OFFICIAL RECORDS.

BY: RANCHO MISSION VIEJO, L.L.C., A DELAWARE LIMITED LIABILITY COMPANY, AS AGENT AND/OR MANAGER.

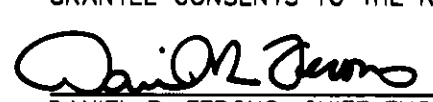
BY:  NAME: DONALD T. STANKIN TITLE: DIRECTOR OF COMMUNITY DEVELOPMENT
BY:  NAME: STEPHEN C. SCHRANK TITLE: EXECUTIVE VICE PRES.

RFC CONSTRUCTION FUNDING CORP., A DELAWARE CORPORATION, BENEFICIARY UNDER A DEED OF TRUST RECORDED AS INSTRUMENT NO. 20010110196 OF OFFICIAL RECORDS.

BY:  NAME: PETER F. FISHER TITLE: DIRECTOR
BY:  NAME: MICHAEL F. RIPLEY TITLE: DIRECTOR

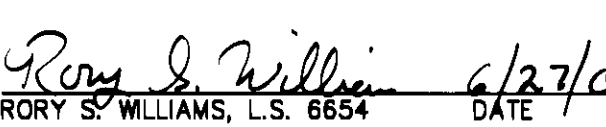
CERTIFICATE OF ACCEPTANCE - SANTA MARGARITA WATER DISTRICT

THE UNDERSIGNED, BEING THE DULY APPOINTED AGENT OF THE SANTA MARGARITA WATER DISTRICT, A PUBLIC CORPORATION IN ORANGE COUNTY, CALIFORNIA, PURSUANT TO ITS RESOLUTION NO. 88-10-2, DOES HEREBY ACCEPT ON BEHALF OF SAID DISTRICT THE PIPELINE EASEMENTS FOR WATER, SEWER AND ACCESS PURPOSES, AS DEDICATED AND SHOWN ON THIS TRACT MAP, BY AND BETWEEN THE SANTA MARGARITA WATER DISTRICT AND WARMINGTON LDR ASSOCIATES III, L.P., A CALIFORNIA LIMITED PARTNERSHIP, AND DOES HEREBY CERTIFY THAT THE GRANTEE CONSENTS TO THE RECORDATION OF SAID TRACT MAP.


DANIEL R. FERONS, CHIEF ENGINEER
SANTA MARGARITA WATER DISTRICT

SURVEYOR'S STATEMENT:

I HEREBY STATE THAT THIS MAP, CONSISTING OF 6 SHEETS, CORRECTLY REPRESENTS A TRUE AND COMPLETE SURVEY AS SHOWN MADE IN DECEMBER, 2000; WAS MADE BY ME OR UNDER MY DIRECTION; THAT THE MONUMENTS ARE OF THE CHARACTER AND OCCUPY (OR WILL OCCUPY) THE POSITIONS INDICATED BY SAID MAP; AND THAT SAID MONUMENTS ARE (OR WILL BE) SUFFICIENT TO ENABLE THE SURVEY TO BE RETRACED.

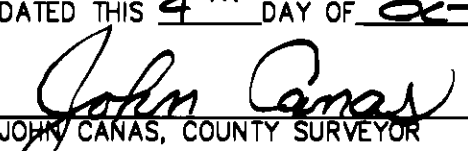
 6/27/01
RORY S. WILLIAMS, L.S. 6654 DATE
EXPIRATION DATE: 12/31/03

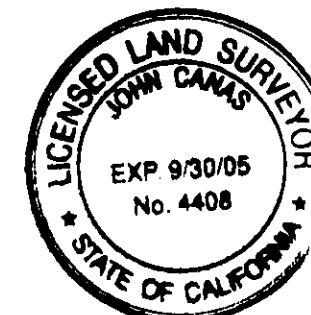


COUNTY SURVEYOR'S STATEMENT

I HEREBY STATE THAT I HAVE EXAMINED THIS MAP AND HAVE FOUND IT TO BE SUBSTANTIALLY IN CONFORMANCE WITH THE TENTATIVE MAP AS FILED WITH, AMENDED AND APPROVED BY THE ORANGE COUNTY SUBDIVISION COMMITTEE; THAT ALL PROVISIONS OF THE SUBDIVISION MAP ACT AND COUNTY SUBDIVISION REGULATIONS HAVE BEEN COMPLIED WITH AND I AM SATISFIED SAID MAP IS TECHNICALLY CORRECT.

DATED THIS 4TH DAY OF OCTOBER, 2001.


JOHN CANAS, COUNTY SURVEYOR
L.S. 4408, EXPIRATION DATE: 9-30-05



COUNTY TREASURER-TAX COLLECTOR'S CERTIFICATE:

STATE OF CALIFORNIA }
COUNTY OF ORANGE } SS

I HEREBY CERTIFY THAT ACCORDING TO THE RECORDS OF MY OFFICE THERE ARE NO LIENS AGAINST THE LAND COVERED BY THIS MAP OR ANY PART THEREOF FOR UNPAID STATE, COUNTY, MUNICIPAL OR LOCAL TAXES OR SPECIAL ASSESSMENTS COLLECTED AS TAXES, EXCEPT TAXES OR SPECIAL ASSESSMENTS COLLECTED AS TAXES NOT YET PAYABLE.

AND DO CERTIFY TO THE RECORDER OF ORANGE COUNTY THAT THE PROVISIONS OF THE SUBDIVISION MAP ACT HAVE BEEN COMPLIED WITH REGARDING DEPOSITS TO SECURE PAYMENT OF TAXES OR SPECIAL ASSESSMENTS COLLECTED AS TAXES ON THE LAND COVERED BY THIS MAP.

DATED THIS 26TH DAY OF September, 2001.

JOHN M.W. MOORLACH
COUNTY TREASURER-TAX COLLECTOR

BY:  DEPUTY TREASURER-TAX COLLECTOR

CLERK OF THE BOARD OF SUPERVISORS' CERTIFICATE:

STATE OF CALIFORNIA }
COUNTY OF ORANGE } SS

I HEREBY CERTIFY THAT THIS MAP WAS PRESENTED FOR APPROVAL TO THE BOARD OF SUPERVISORS OF THE COUNTY OF ORANGE AT A REGULAR MEETING THEREOF HELD ON THE 16TH DAY OF October, 2001, AND THAT THEREUPON SAID BOARD DID, BY AN ORDER DULY PASSED AND ENTERED, APPROVE SAID MAP.

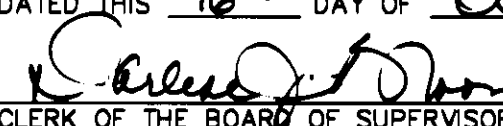
AND DID ACCEPT ON BEHALF OF THE COUNTY OF ORANGE:

THE EASEMENT FOR INGRESS AND EGRESS OF EMERGENCY AND PUBLIC SERVICE VEHICLES OVER LOT D, AS DEDICATED.

WE ALSO HEREBY ABANDON, PURSUANT TO SECTION 44920.1 OF THE SUBDIVISION MAP ACT, THAT CERTAIN EASEMENT FOR STORM DRAIN PURPOSES WITHIN THE BOUNDARY OF THIS MAP, WHICH WAS ACQUIRED BY THE COUNTY OF ORANGE PER TRACT NO. 16156, AS PER MAP FILED IN BOOK 812, PAGES 40 THROUGH 48, INCLUSIVE, OF MISCELLANEOUS MAPS, RECORDS OF ORANGE COUNTY, NOT SHOWN ON THIS MAP.

AND DID ALSO APPROVE SUBJECT MAP PURSUANT TO THE PROVISIONS OF SECTION 66436(a)(3)(A) OF THE SUBDIVISION MAP ACT.

DATED THIS 16TH DAY OF October, 2001.


CLERK OF THE BOARD OF SUPERVISORS
DARLENE J. BLOOM



NOTE:

THE PRIVATE STREETS CONSTRUCTED WITHIN THIS MAP SHALL BE OWNED, OPERATED AND MAINTAINED BY THE DEVELOPER, SUCCESSORS OR ASSIGNS. THE COUNTY OF ORANGE SHALL HAVE NO RESPONSIBILITY THEREFOR, UNLESS PURSUANT TO APPROPRIATE SECTIONS OF THE STREET AND HIGHWAYS CODE OF THE STATE OF CALIFORNIA, THE SAID PRIVATE STREETS HAVE BEEN ACCEPTED INTO THE COUNTY ROAD SYSTEM BY APPROPRIATE RESOLUTION OF THE ORANGE COUNTY BOARD OF SUPERVISORS.

NOTE:

SEE SHEET 2 FOR NOTARY ACKNOWLEDGMENTS AND SIGNATURE OMISSIONS.

SHEET 2 OF 6 SHEETS
54 NUMBERED LOTS AND LOTS
A THROUGH M, INCLUSIVE
ACREAGE: 6.021 ACRES
(ALL OF TENTATIVE
TRACT NO. 16126)

TRACT NO. 16126

IN UNINCORPORATED TERRITORY OF THE
COUNTY OF ORANGE, STATE OF CALIFORNIA.

HUNSAKER AND ASSOCIATES IRVINE, INC.
RORY S. WILLIAMS, LS. 6654 DATE OF SURVEY: DECEMBER, 2000

NOTARY ACKNOWLEDGMENTS:

STATE OF CALIFORNIA }
COUNTY OF ORANGE } SS
ON July 31, 2001 BEFORE ME, Tina T. Baker, Notary Public, PERSONALLY
APPEARED Donna T. Stahl AND Stephen C. Schmitt PERSONALLY
KNOWN TO ME (OR PROVED TO ME ON THE BASIS OF SATISFACTORY EVIDENCE) TO BE THE PERSON(S)
WHOSE NAME(S) IS/ARE SUBSCRIBED TO THE WITHIN INSTRUMENT AND ACKNOWLEDGED TO ME THAT
HE/SHE/THEY EXECUTED THE SAME IN HIS/HER/THEIR AUTHORIZED CAPACITY(IES), AND THAT BY
HIS/HER/THEIR SIGNATURE(S) ON THE INSTRUMENT THE PERSON(S), OR ENTITY UPON BEHALF OF
WHICH THE PERSON(S) ACTED, EXECUTED THE INSTRUMENT.

WITNESS MY HAND:

SIGNATURE Tina T. Baker
NOTARY PUBLIC IN AND FOR SAID STATE
Tina T. Baker
(NAME PRINTED)

MY PRINCIPAL PLACE OF BUSINESS IS
IN Orange COUNTY.
MY COMMISSION EXPIRES: 8/29/2004

STATE OF CALIFORNIA }
COUNTY OF ORANGE } SS
ON July 9, 2001 BEFORE ME, Betty Jo Poston, PERSONALLY
APPEARED B. J. Lindberg AND Robert S. McClure PERSONALLY
KNOWN TO ME (OR PROVED TO ME ON THE BASIS OF SATISFACTORY EVIDENCE) TO BE THE PERSON(S)
WHOSE NAME(S) IS/ARE SUBSCRIBED TO THE WITHIN INSTRUMENT AND ACKNOWLEDGED TO ME THAT
HE/SHE/THEY EXECUTED THE SAME IN HIS/HER/THEIR AUTHORIZED CAPACITY(IES), AND THAT BY
HIS/HER/THEIR SIGNATURE(S) ON THE INSTRUMENT THE PERSON(S), OR ENTITY UPON BEHALF OF
WHICH THE PERSON(S) ACTED, EXECUTED THE INSTRUMENT.

WITNESS MY HAND:

SIGNATURE Betty Jo Poston
NOTARY PUBLIC IN AND FOR SAID STATE
Betty Jo Poston
(NAME PRINTED)

MY PRINCIPAL PLACE OF BUSINESS IS
IN Orange COUNTY.
MY COMMISSION EXPIRES: 3/17/05

STATE OF CALIFORNIA }
COUNTY OF Los Angeles } SS
ON July 5, 2001 BEFORE ME, Sonia G. Garcia, PERSONALLY
APPEARED Peter Fischer AND Michael F. Ripling PERSONALLY
KNOWN TO ME (OR PROVED TO ME ON THE BASIS OF SATISFACTORY EVIDENCE) TO BE THE PERSON(S)
WHOSE NAME(S) IS/ARE SUBSCRIBED TO THE WITHIN INSTRUMENT AND ACKNOWLEDGED TO ME THAT
HE/SHE/THEY EXECUTED THE SAME IN HIS/HER/THEIR AUTHORIZED CAPACITY(IES), AND THAT BY
HIS/HER/THEIR SIGNATURE(S) ON THE INSTRUMENT THE PERSON(S), OR ENTITY UPON BEHALF OF
WHICH THE PERSON(S) ACTED, EXECUTED THE INSTRUMENT.

WITNESS MY HAND:

SIGNATURE Sonia G. Garcia
NOTARY PUBLIC IN AND FOR SAID STATE
SONIA E. GARCIA
(NAME PRINTED)

MY PRINCIPAL PLACE OF BUSINESS IS
IN Los Angeles COUNTY.
MY COMMISSION EXPIRES: May 9, 2003

NOTARY ACKNOWLEDGMENT - SANTA MARGARITA WATER DISTRICT

STATE OF CALIFORNIA }
COUNTY OF ORANGE } SS
ON 9-24-01 BEFORE ME, ANDREA M. EVANS, PERSONALLY
APPEARED DANIEL R. FERONS, PERSONALLY
KNOWN TO ME (OR PROVED TO ME ON THE BASIS OF SATISFACTORY EVIDENCE) TO BE THE PERSON
WHOSE NAME IS SUBSCRIBED TO THE WITHIN INSTRUMENT AND ACKNOWLEDGED TO ME THAT
HE EXECUTED THE SAME IN HIS AUTHORIZED CAPACITY, AND THAT BY
HIS SIGNATURE ON THE INSTRUMENT THE PERSON, OR ENTITY UPON BEHALF OF
WHICH THE PERSON ACTED, EXECUTED THE INSTRUMENT.

WITNESS MY HAND:

SIGNATURE Andrea M. Evans
NOTARY PUBLIC IN AND FOR SAID STATE
ANDREA M. EVANS
(NAME PRINTED)

MY PRINCIPAL PLACE OF BUSINESS IS
IN Orange COUNTY.
MY COMMISSION EXPIRES: 4-8-04

SIGNATURE OMISSIONS:
PURSUANT TO THE PROVISIONS OF SECTION 66436 (a)(3)(C) OF THE SUBDIVISION MAP ACT, THE
FOLLOWING SIGNATURES HAVE BEEN OMITTED:

DMB LADERA, LLC, HOLDER OF EASEMENTS RECORDED AS INSTRUMENT NO. 20010110194 OF
OFFICIAL RECORDS.
LADERA DEVELOPMENT COMPANY, L.L.C., HOLDER OF OIL, GAS AND MINERAL RIGHTS RECORDED
AS INSTRUMENT NO. 19960624029 OF OFFICIAL RECORDS.
THE COUNTY OF ORANGE, HOLDER OF EASEMENT DEDICATED ON THE MAP OF TRACT NO. 16156.

SHEET 3 OF 6 SHEETS
SCALE: 1" = 60'
54 NUMBERED LOTS AND LOTS
A THROUGH M, INCLUSIVE
ACREAGE: 6.021 ACRES
(ALL OF TENTATIVE
TRACT NO. 16126)

TRACT NO. 16126

IN UNINCORPORATED TERRITORY OF THE COUNTY OF ORANGE,
STATE OF CALIFORNIA
HUNSAKER AND ASSOCIATES IRVINE, INC.
RORY S. WILLIAMS, L.S. 6654 DATE OF SURVEY: DECEMBER, 2000

SHEET INDEX AND GPS CONTROL MAP

BASIS OF BEARINGS:

THE BEARINGS SHOWN HEREON ARE BASED ON THE BEARING BETWEEN
O.C.S. HORIZONTAL CONTROL STATION GPS NO. 1448 AND STATION
GPS NO. 1417 BEING N10°48'13"E PER RECORDS ON FILE IN THE
OFFICE OF THE ORANGE COUNTY SURVEYOR.

DATUM STATEMENT:

COORDINATES SHOWN ARE BASED ON THE CALIFORNIA COORDINATE
SYSTEM (OCS83), ZONE VI, 1983 NAD, (1991.35 EPOCH OCS GPS
ADJUSTMENT).

ALL DISTANCES SHOWN ARE GROUND UNLESS OTHERWISE NOTED. TO
OBTAIN GRID DISTANCE MULTIPLY GROUND DISTANCE BY 0.99994850.

NOTES:

LOTS A & B ARE FOR PRIVATE PARK PURPOSES.

LOT C IS FOR OPEN SPACE PURPOSES.

LOT D IS FOR PRIVATE STREET AND PRIVATE ALLEY PURPOSES.

LOTS E THROUGH M, INCLUSIVE, ARE FOR LANDSCAPE PURPOSES AND ARE
NOT SEPARATE BUILDING SITES.

THIS PROPERTY IS IN A SPECIAL FIRE PROTECTION AREA. TOTAL EXCLUSION
GRANTED FOR THIS TRACT.

ALL COMMERCIAL STRUCTURES OVER 6,000 SQUARE FEET, ALL RESIDENTIAL
STRUCTURES OVER 5,500 SQUARE FEET, ALL STRUCTURES EXCEEDING FIRE
DEPARTMENT ACCESS REQUIREMENTS SHALL BE PROTECTED BY AN
AUTOMATIC FIRE SPRINKLER SYSTEM, IN A MANNER MEETING THE APPROVAL
OF THE FIRE CHIEF.

EASEMENT NOTES:

- (A) INDICATES AN EASEMENT FOR SEWER, WATER AND ACCESS PURPOSES
DEDICATED HEREON TO THE SANTA MARGARITA WATER DISTRICT.
- (B) INDICATES AN EASEMENT FOR INGRESS AND EGRESS OF EMERGENCY
AND PUBLIC SERVICE VEHICLES DEDICATED HEREON TO THE COUNTY
OF ORANGE.
- (C) INDICATES AN EASEMENT FOR PUBLIC UTILITY PURPOSES
RESERVED HEREON FOR FUTURE GRANT.

MONUMENT NOTES:

LEAD, TACK & TAG L.S. 6654 TO BE SET IN TOP OF CURB AT AN OFFSET OF 10.75' ALONG
FRONT SIDE LOT LINES PRODUCED FOR LOTS 1 THROUGH 18, INCLUSIVE, AND LOTS 36
THROUGH 38, INCLUSIVE, AND AT AN OFFSET OF 9.75' ON SIDE LOT LINES PRODUCED FOR
LOTS 19 THROUGH 30, INCLUSIVE, AND LOTS 39 THROUGH 54, INCLUSIVE, WITHIN 90 DAYS
AFTER ACCEPTANCE OF IMPROVEMENTS, UNLESS OTHERWISE NOTED. FOR ALL SIDE LOT LINES
NON-RADIAL OR NON-PERPENDICULAR TO STREET RIGHT OF WAY, OR NOT AT AN OFFSET OF
9.75' OR 10.75', BEARING AND DISTANCE OF PRODUCTION IS AS NOTED HEREON.

LEAD, TACK & TAG L.S. 6654 TO BE SET IN TOP OF CURB ON ALL REAR SIDE LOT LINES AT
A 0.50' OFFSET INSIDE THE LOT CORNER FROM INTERSECTION WITH 24.00' WIDE PRIVATE
ALLEY RIGHTS OF WAY, IN LIEU OF AT LOT CORNERS, WITHIN 90 DAYS AFTER ACCEPTANCE
OF IMPROVEMENTS. (THE REARS OF ALL LOTS FACE THE PRIVATE ALLEYS.)

8" S&W STAMPED L.S. 6654 OR LEAD, TACK & TAG L.S. 6654 OR 1" I.P. TAGGED L.S. 6654
IN MEDIAN TO BE SET AT ALL STREET CENTERLINE POINTS OF CONTROL, WITHIN 90 DAYS
AFTER ACCEPTANCE OF IMPROVEMENTS, UNLESS OTHERWISE NOTED.

1" I.P. TAGGED L.S. 6654 TO BE SET AT THE FRONT CORNERS OF LOTS 31 THROUGH 35,
INCLUSIVE, FACING LOT A, WITHIN 90 DAYS AFTER ACCEPTANCE OF IMPROVEMENTS, UNLESS
OTHERWISE NOTED.

- INDICATES FOUND MONUMENT AS NOTED OR LOCATION
OF MONUMENT TO BE SET AS NOTED.

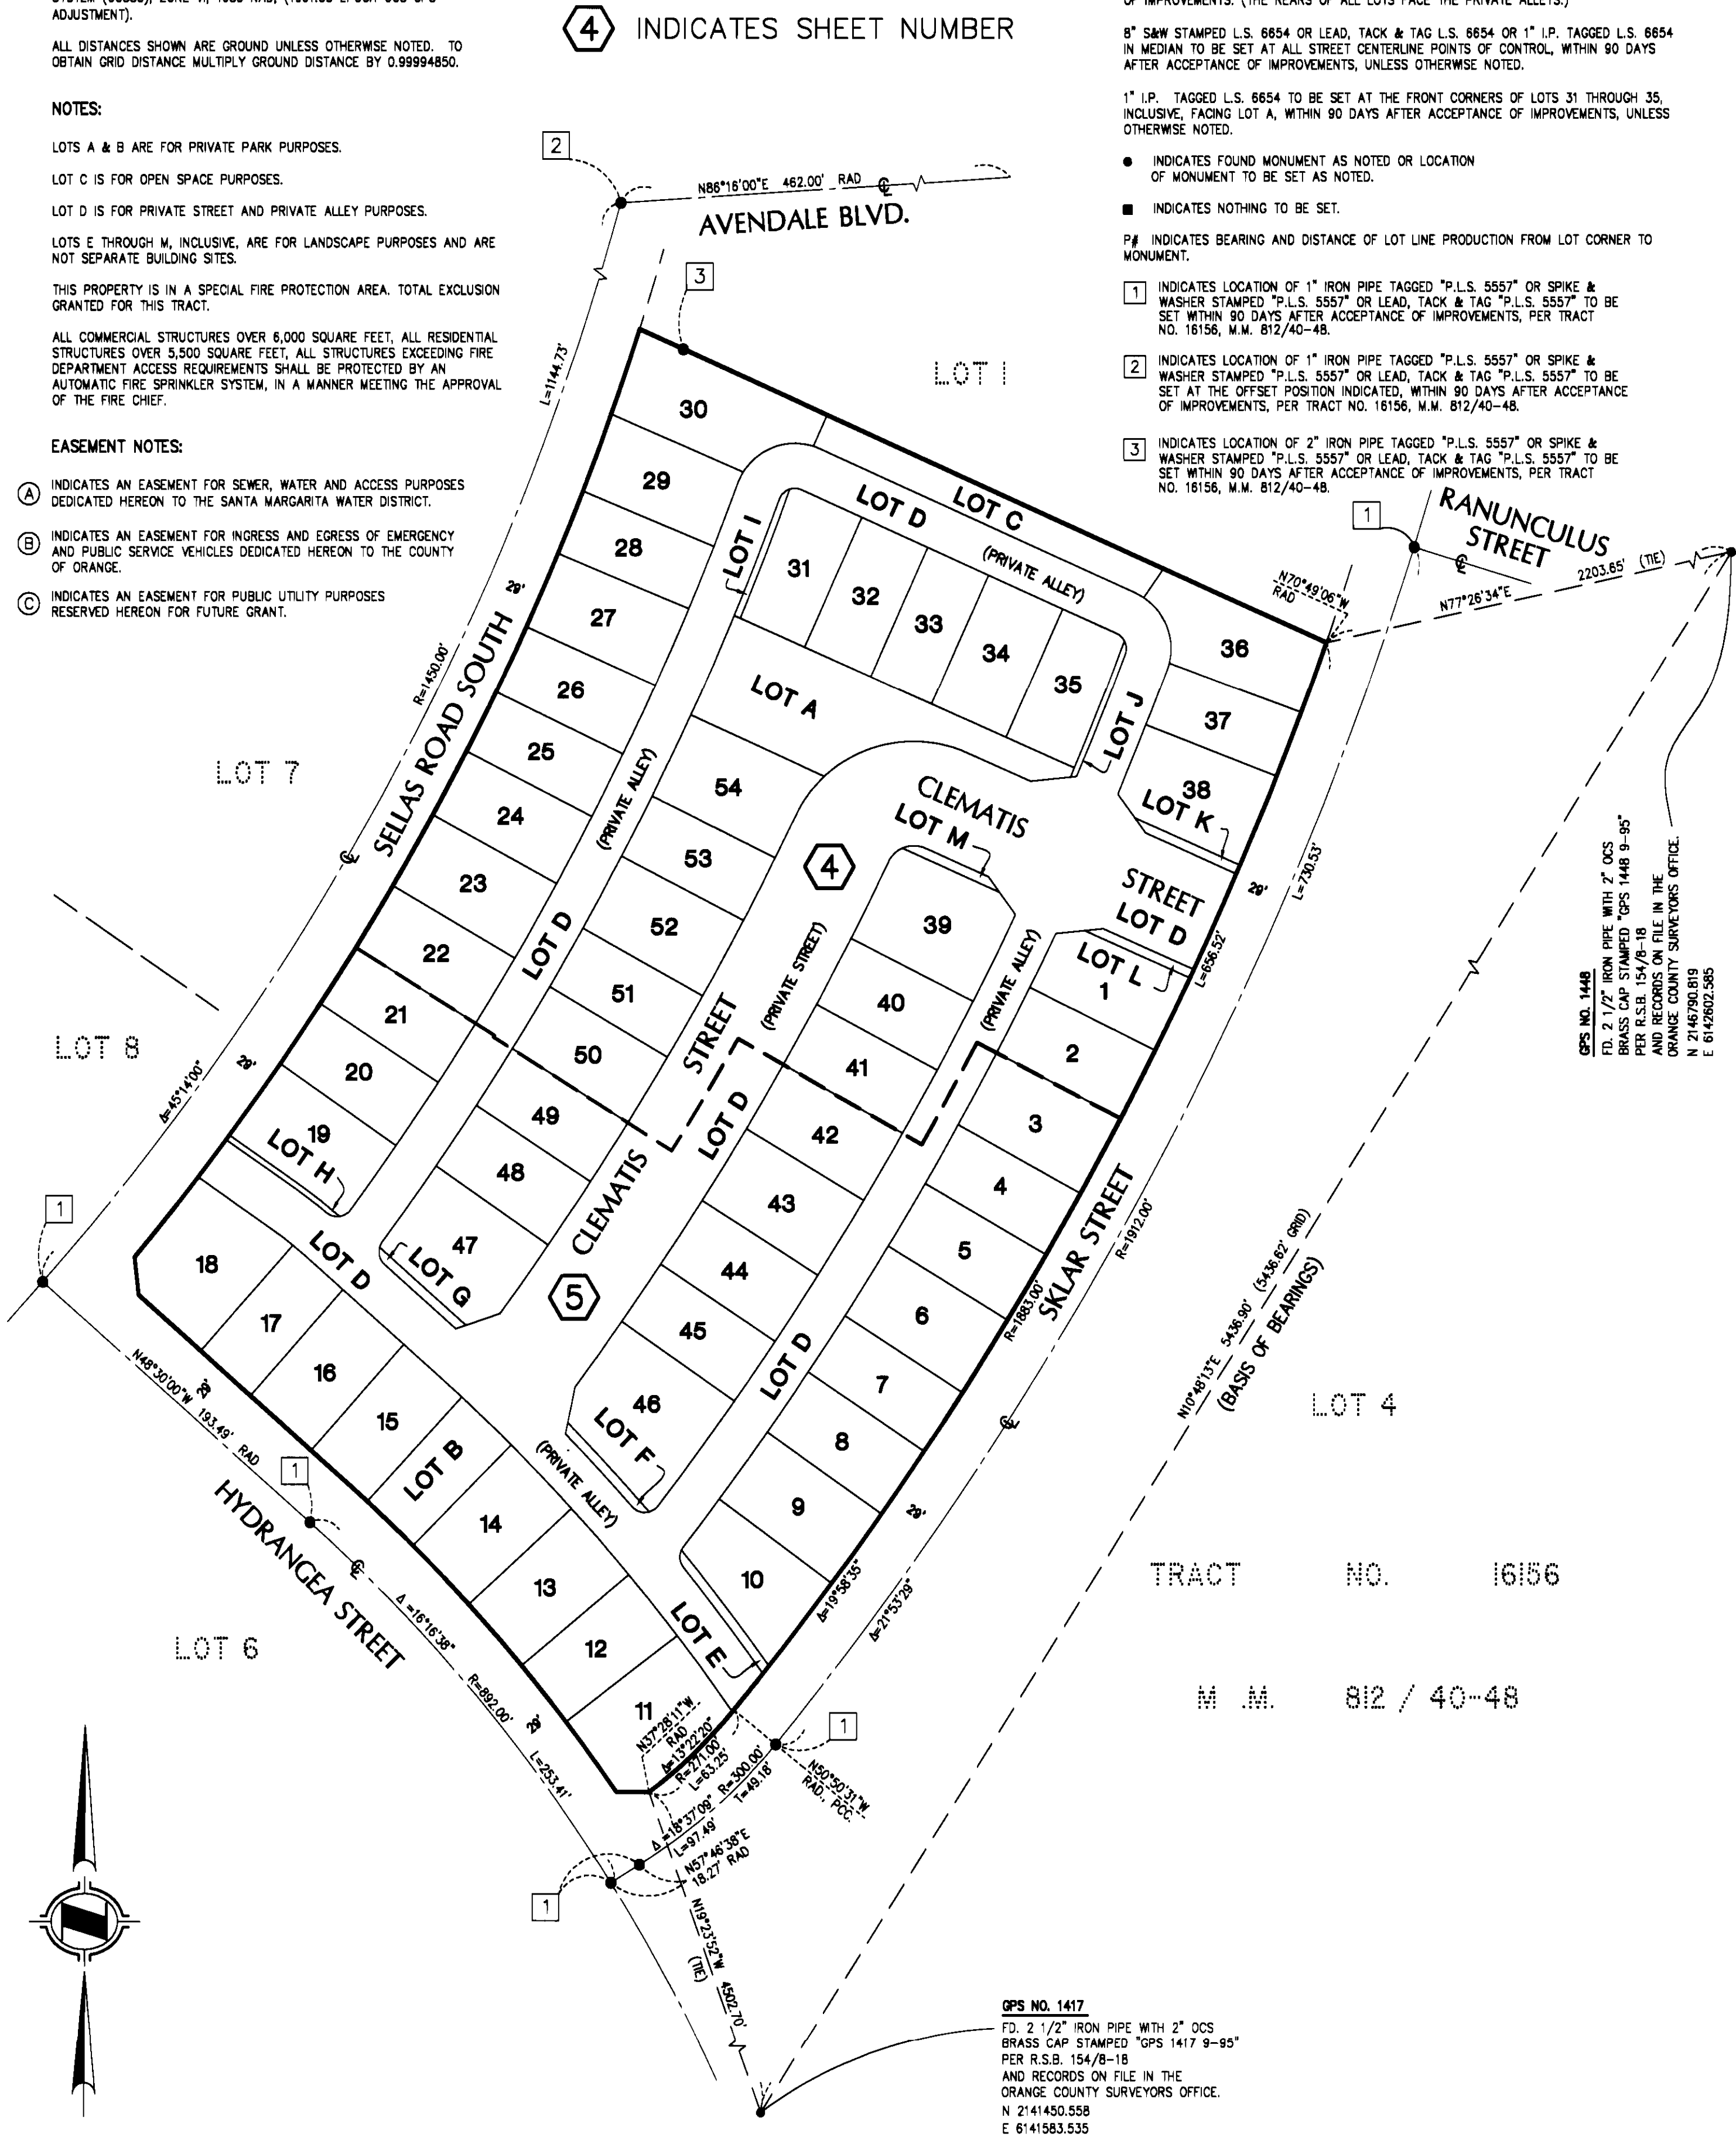
- INDICATES NOTHING TO BE SET.

P# INDICATES BEARING AND DISTANCE OF LOT LINE PRODUCTION FROM LOT CORNER TO
MONUMENT.

1 INDICATES LOCATION OF 1" IRON PIPE TAGGED "P.L.S. 5557" OR SPIKE &
WASHER STAMPED "P.L.S. 5557" OR LEAD, TACK & TAG "P.L.S. 5557" TO BE
SET WITHIN 90 DAYS AFTER ACCEPTANCE OF IMPROVEMENTS, PER TRACT
NO. 16156, M.M. 812/40-48.

2 INDICATES LOCATION OF 1" IRON PIPE TAGGED "P.L.S. 5557" OR SPIKE &
WASHER STAMPED "P.L.S. 5557" OR LEAD, TACK & TAG "P.L.S. 5557" TO BE
SET AT THE OFFSET POSITION INDICATED, WITHIN 90 DAYS AFTER ACCEPTANCE
OF IMPROVEMENTS, PER TRACT NO. 16156, M.M. 812/40-48.

3 INDICATES LOCATION OF 2" IRON PIPE TAGGED "P.L.S. 5557" OR SPIKE &
WASHER STAMPED "P.L.S. 5557" OR LEAD, TACK & TAG "P.L.S. 5557" TO BE
SET WITHIN 90 DAYS AFTER ACCEPTANCE OF IMPROVEMENTS, PER TRACT
NO. 16156, M.M. 812/40-48.



GPS NO. 1448
FD. 2 1/2" IRON PIPE WITH 2" OCS
BRASS CAP STAMPED "GPS 1448 9-95"
PER R.S.B. 154/8-18
AND RECORDS ON FILE IN THE
ORANGE COUNTY SURVEYORS OFFICE.
N 2146790.819
E 6142602.565

GPS NO. 1417
FD. 2 1/2" IRON PIPE WITH 2" OCS
BRASS CAP STAMPED "GPS 1417 9-95"
PER R.S.B. 154/8-18
AND RECORDS ON FILE IN THE
ORANGE COUNTY SURVEYORS OFFICE.
N 2141450.558
E 6141583.535

SHEET 4 OF 6 SHEETS
SCALE: 1" = 30'
54 NUMBERED LOTS AND LOTS
A THROUGH M, INCLUSIVE
ACREAGE: 8.021 ACRES
(ALL OF TENTATIVE
TRACT NO. 16126)

TRACT NO. 16126

IN UNINCORPORATED TERRITORY OF THE COUNTY OF ORANGE,
STATE OF CALIFORNIA

HUNSAKER AND ASSOCIATES IRVINE, INC.

RORY S. WILLIAMS, L.S. 6654

DATE OF SURVEY: DECEMBER, 2000

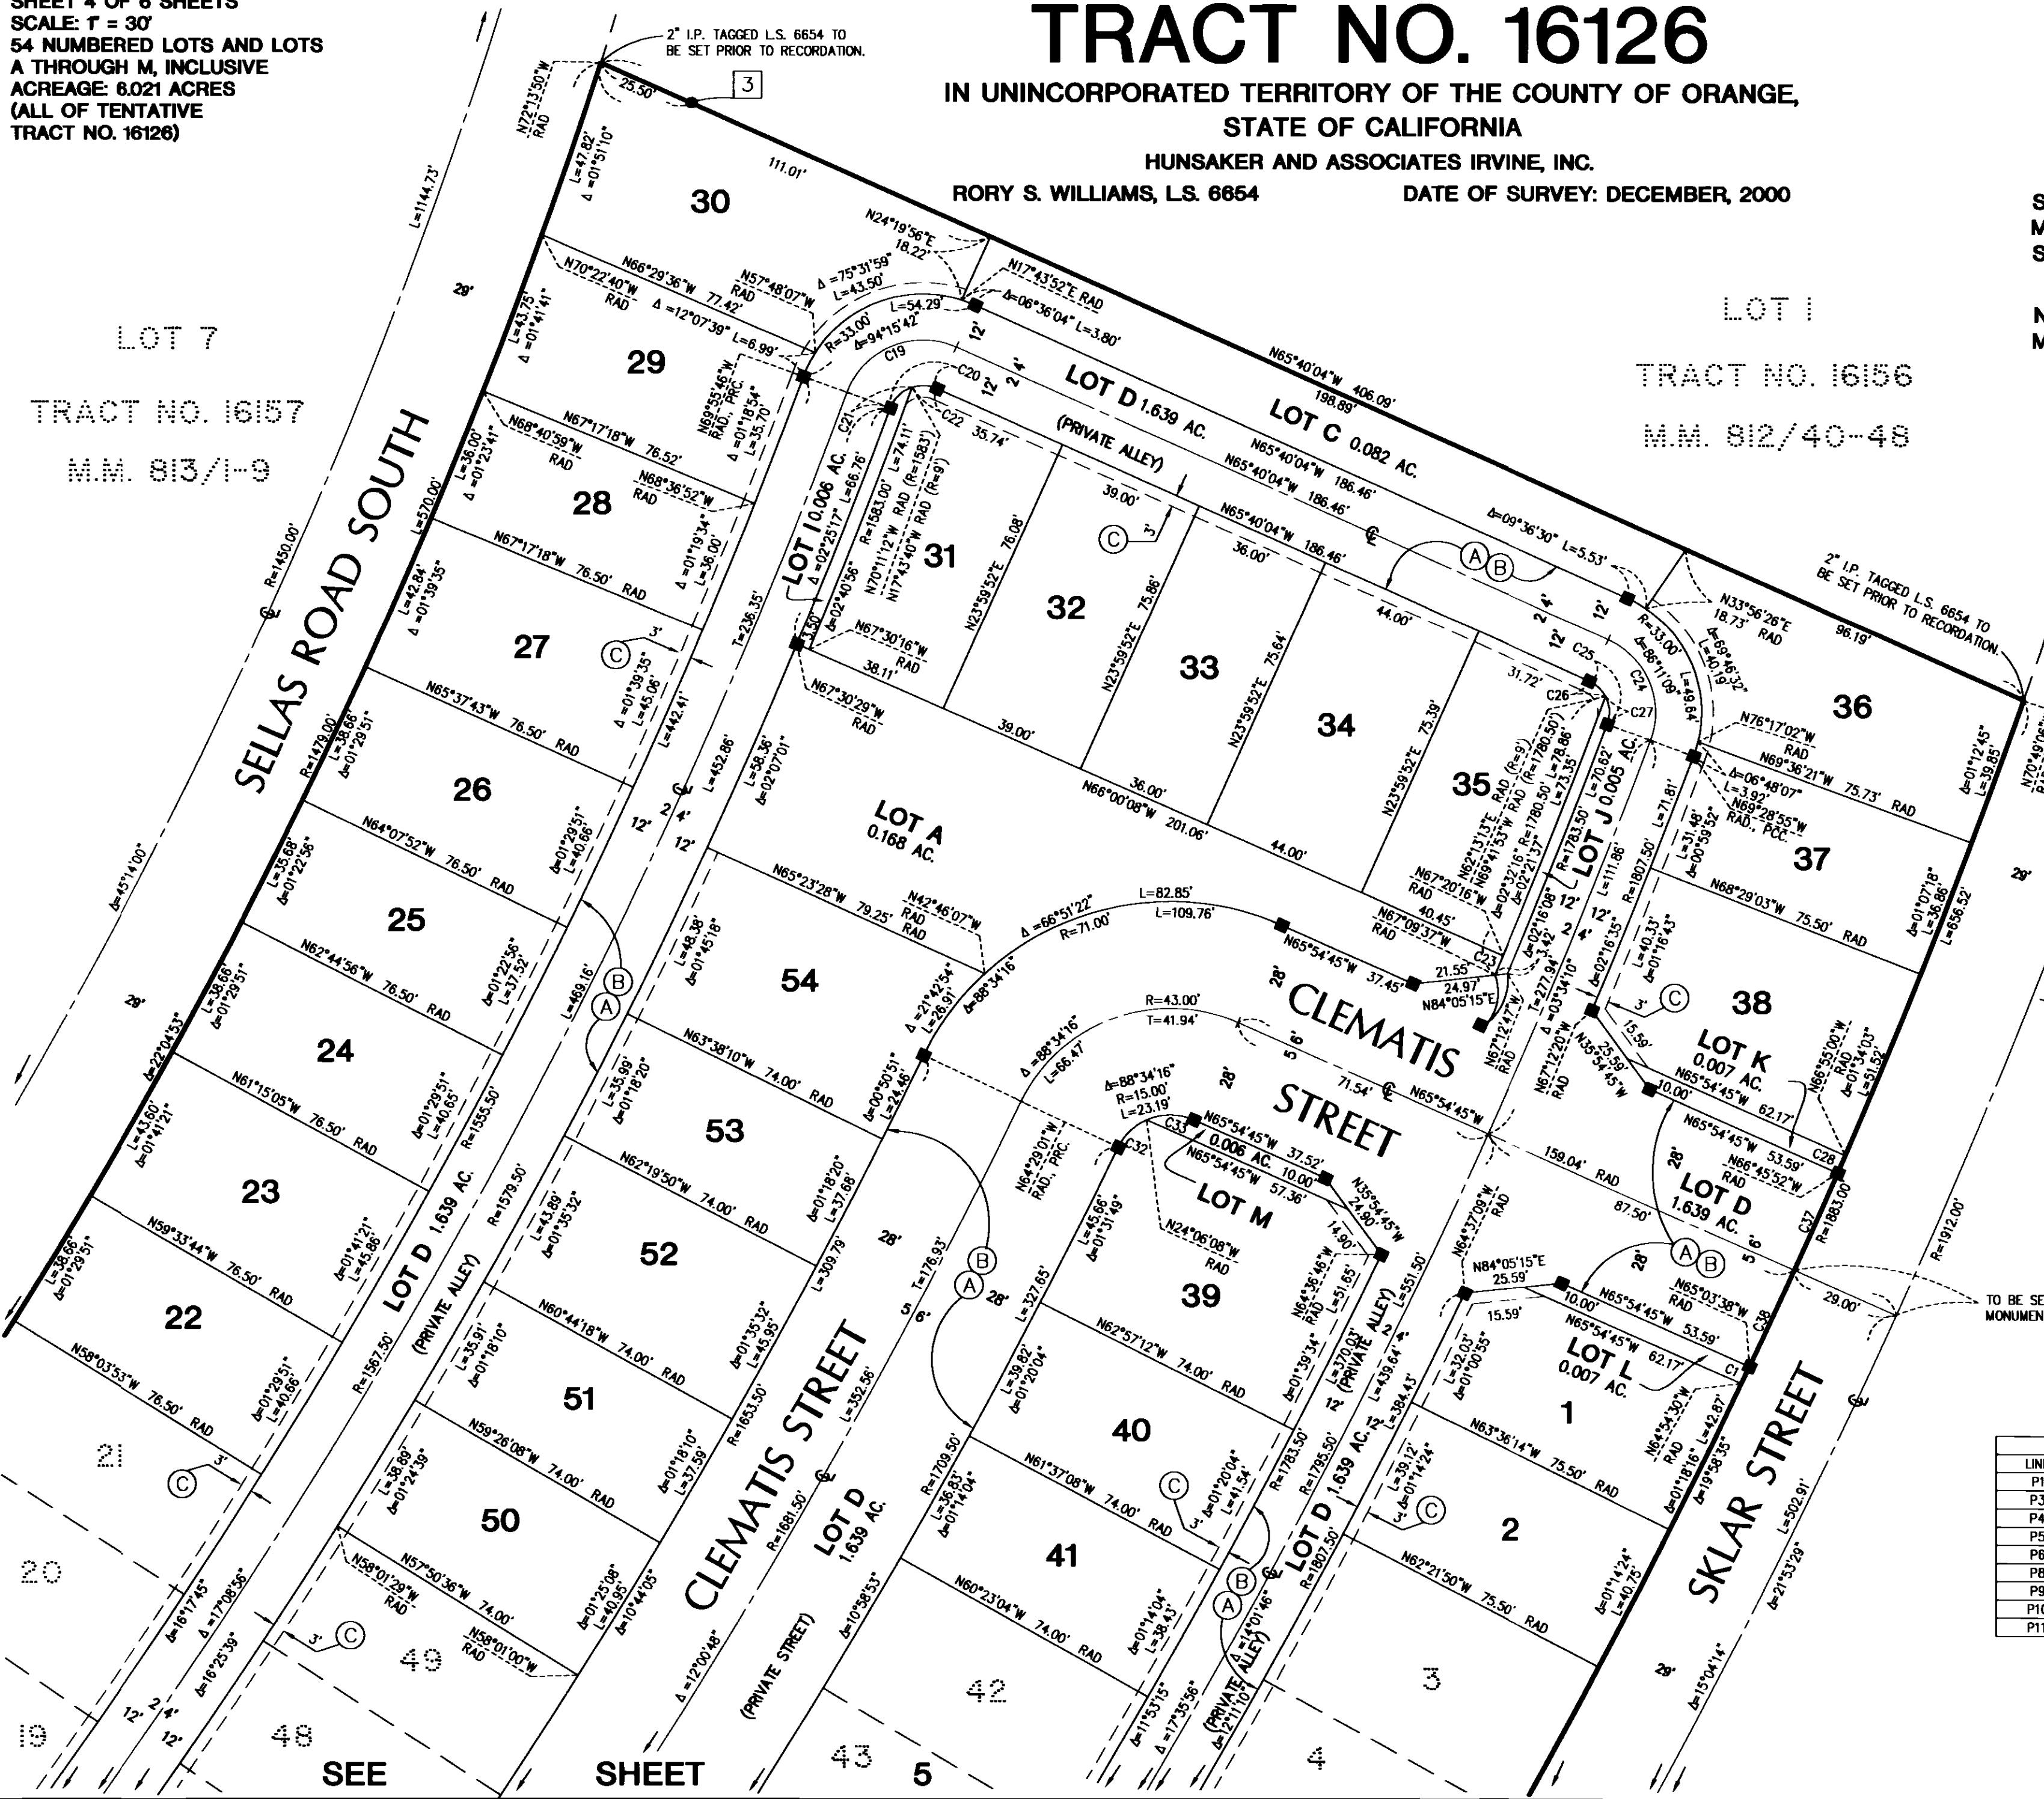
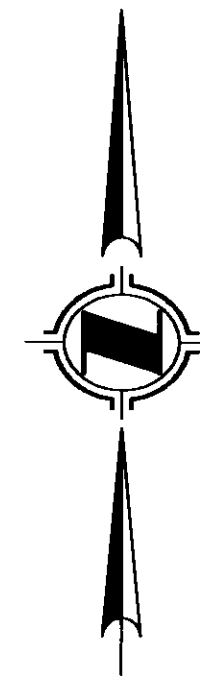
SEE SHEET 2 FOR SHEET INDEX AND GPS CONTROL
MAP, MONUMENT NOTES, BASIS OF BEARINGS, DATUM
STATEMENT, EASEMENT NOTES AND NOTES.

NOTE: SEE SHEET 6 FOR ADDITIONAL SANTA
MARGARITA WATER DISTRICT EASEMENTS.

LOT 7
TRACT NO. 16157
M.M. 813/1-9

LOT 1
TRACT NO. 16156
M.M. 812/40-48

LOT 4
TRACT NO. 16156
M.M. 812/40-48



MONUMENT OFFSET TABLE		
LINE	BEARING	LENGTH
P1	N65°54'45"W	10.75'
P3	N67°17'18"W	9.75'
P4	N66°29'36"W	9.77'
P5	N65°54'45"W	10.75'
P6	N65°54'45"W	11.46'
P8	N57°50'36"W	9.75'
P9	N65°23'28"W	10.71'
P10	N65°54'45"W	11.90'
P11	N65°54'45"W	12.34'

CURVE TABLE				
CURVE	DELTA	RADIUS	LENGTH	TANGENT
C1	00°09'08"	1883.00'	5.00'	2.50'
C19	94°15'42"	21.00'	34.55'	22.62'
C20	94°15'42"	9.00'	14.81'	9.70'
C21	52°12'06"	9.00'	8.20'	4.41'
C22	42°03'36"	9.00'	6.61'	3.46'
C23	00°10'39"	1780.50'	5.51'	2.76'
C24	86°11'09"	21.00'	31.59'	19.65'
C25	86°11'09"	9.00'	13.54'	8.42'
C26	37°53'17"	9.00'	5.95'	3.09'
C27	48°17'52"	9.00'	7.59'	4.04'
C28	00°09'08"	1883.00'	5.00'	2.50'
C32	40°22'53"	15.00'	10.57'	5.52'
C33	48°11'23"	15.00'	12.62'	6.71'
C37	00°51'07"	1883.00'	28.00'	14.00'
C38	00°51'07"	1883.00'	28.00'	14.00'

SHEET 5 OF 6 SHEETS
SCALE: 1" = 30'
54 NUMBERED LOTS AND LOTS
A THROUGH M, INCLUSIVE
ACREAGE: 6.021 ACRES
(ALL OF TENTATIVE
TRACT NO. 16126)

TRACT NO. 16126

IN UNINCORPORATED TERRITORY OF THE COUNTY OF ORANGE,
STATE OF CALIFORNIA

HUNSAKER AND ASSOCIATES IRVINE, INC.

RORY S. WILLIAMS, L.S. 6654

DATE OF SURVEY: DECEMBER, 2000

SEE

SHEET

LOT 8
TRACT NO. 16157
M.M. 813/1-9

MONUMENT OFFSET TABLE		
LINE	BEARING	LENGTH
P2	N55°11'06"W	9.75'
P7	N48°30'00"W	20.53'
P8	N57°50'36"W	9.75'

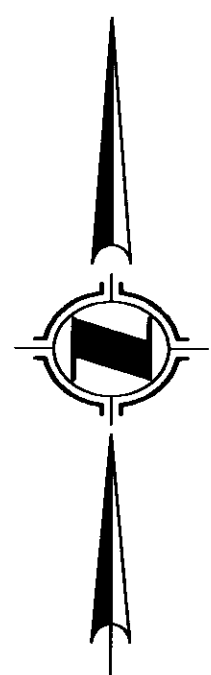
CURVE TABLE				
CURVE	DELTA	RADIUS	LENGTH	TANGENT
C2	76°38'35"	9.00'	12.04'	7.11'
C3	63°23'16"	9.00'	9.96'	5.56'
C4	13°15'19"	9.00'	2.08'	1.05'
C5	00°09'31"	1883.00'	5.21'	2.61'
C6	00°23'47"	1883.00'	13.03'	6.52'
C7	00°21'26"	1883.00'	11.74'	5.87'
C8	00°16'14"	271.00'	1.28'	0.64'
C9	06°41'06"	207.50'	24.21'	12.12'
C10	00°29'05"	1479.00'	12.51'	6.26'
C11	00°29'05"	1479.00'	12.51'	6.25'
C12	00°06'58"	1479.00'	3.00'	1.50'
C13	06°41'06"	220.00'	25.67'	12.85'
C14	04°51'57"	232.50'	19.75'	9.88'
C15	06°34'52"	228.00'	26.19'	13.11'
C16	63°18'52"	9.00'	14.66'	9.54'
C17	47°23'56"	9.00'	7.45'	3.95'
C29	84°59'53"	9.00'	13.35'	8.25'
C30	63°36'44"	9.00'	9.99'	5.58'
C31	21°23'09"	9.00'	3.36'	1.70'
C34	101°15'32"	9.00'	15.91'	10.97'
C35	63°23'16"	9.00'	9.96'	5.56'
C36	37°52'16"	9.00'	5.95'	3.09'

TRACT NO. 16025

M.M. 812/22-29

TRACT NO. 16156

M.M. 812/40-48



SEE SHEET 2 FOR SHEET INDEX AND GPS CONTROL
MAP, MONUMENT NOTES, BASIS OF BEARINGS, DATUM
STATEMENT, EASEMENT NOTES AND NOTES.

NOTE: SEE SHEET 6 FOR ADDITIONAL SANTA
MARGARITA WATER DISTRICT EASEMENTS.

SHEET 6 OF 6 SHEETS
SCALE: 1" = 60'
54 NUMBERED LOTS AND LOTS
A THROUGH M, INCLUSIVE
ACREAGE: 6.021 ACRES
(ALL OF TENTATIVE
TRACT NO. 16126)

TRACT NO. 16126

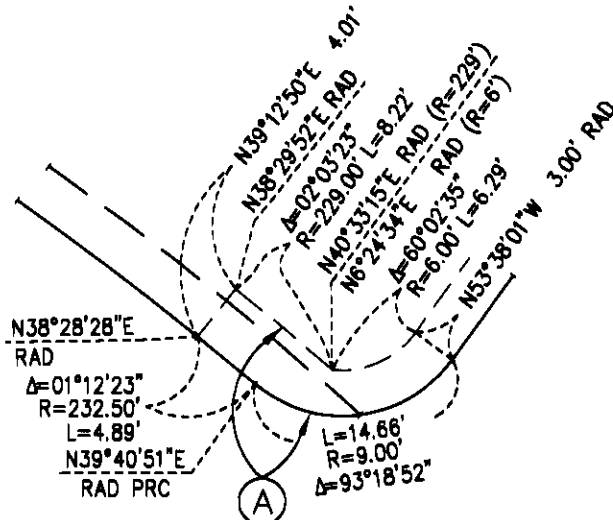
IN UNINCORPORATED TERRITORY OF THE COUNTY OF ORANGE,
STATE OF CALIFORNIA
HUNSAKER AND ASSOCIATES IRVINE, INC.
RORY S. WILLIAMS, LS. 6654 DATE OF SURVEY: DECEMBER, 2000

SANTA MARGARITA WATER DISTRICT EASEMENT DETAIL SHEET

SEE SHEET 3 FOR SHEET INDEX AND GPS CONTROL
MAP, MONUMENT NOTES, BASIS OF BEARINGS, DATUM
STATEMENT, EASEMENT NOTES AND NOTES.

EASEMENT NOTE:

(A) INDICATES AN EASEMENT FOR WATER LINE PURPOSES
DEDICATED HEREON TO THE SANTA MARGARITA WATER DISTRICT.



DETAIL
N.T.S.

