

SHEET 1 OF 6 SHEETS
45 NUMBERED LOTS AND LOTS
A THROUGH L, INCLUSIVE
ACREAGE: 4.956 ACRES
(ALL OF TENTATIVE
TRACT NO. 16127)

TRACT NO. 16127

IN UNINCORPORATED TERRITORY OF THE
COUNTY OF ORANGE, STATE OF CALIFORNIA

BEING A SUBDIVISION OF LOTS 7, AI, AJ, AK AND AL OF TRACT NO. 16155, AS SHOWN ON A MAP
FILED IN BOOK 812, PAGES 30 THROUGH 39, INCLUSIVE, OF MISCELLANEOUS MAPS, IN THE
OFFICE OF THE COUNTY RECORDER OF SAID COUNTY OF ORANGE

BLOCK: 5057
MODULE: 78

HUNSAKER AND ASSOCIATES IRVINE, INC.
RORY S. WILLIAMS, L.S. 6654 DATE OF SURVEY: DECEMBER, 2000

ACCEPTED AND FILED AT THE
REQUEST OF

FIRST AMERICAN TITLE INSURANCE COMPANY


DATE: JULY 30, 2001

TIME: 1:37 P.M. FEE: \$17.00

INSTRUMENT NO. 20010515435

BOOK 821 PAGE 29-34 M/M

GARY L. GRANVILLE
COUNTY CLERK - RECORDER

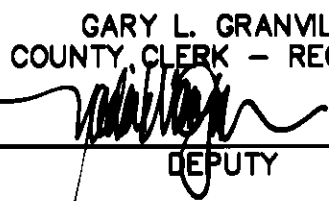BY  DEPUTY

OWNERSHIP CERTIFICATE:

WE, THE UNDERSIGNED, BEING ALL PARTIES HAVING ANY RECORD TITLE INTEREST IN THE LAND COVERED BY THIS MAP, DO HEREBY CONSENT TO THE PREPARATION AND RECORDATION OF SAID MAP, AS SHOWN WITHIN THE DISTINCTIVE BORDER LINE.

WE HEREBY DEDICATE TO THE COUNTY OF ORANGE:

AN EASEMENT FOR INGRESS AND EGRESS OF EMERGENCY AND PUBLIC SERVICE VEHICLES OVER LOT B, AS SHOWN ON THIS MAP.

WE RESERVE TO OURSELVES, OUR SUCCESSORS AND ASSIGNS THE PUBLIC UTILITY EASEMENTS SHOWN ON THIS MAP, FOR THE USE AND BENEFIT OF THE VARIOUS UTILITY COMPANIES AUTHORIZED TO PROVIDE SERVICE TO THE LOTS SHOWN HEREON.

WE ALSO DO HEREBY DECLARE THAT THE LAND COVERED BY THIS MAP IS LOCATED IN A HIGH FIRE HAZARD AREA DUE TO WILDLAND EXPOSURE BASED ON STATE SRA MAPS.


WE ALSO HEREBY DEDICATE TO THE SANTA MARGARITA WATER DISTRICT THE PIPELINE EASEMENTS FOR WATER, SEWER AND ACCESS PURPOSES

ALL AS SHOWN ON THIS TRACT MAP, WHICH EASEMENTS SHALL BE SUBJECT TO THE SAME TERMS AND CONDITIONS AS SHOWN IN THAT CERTAIN EASEMENT, RECORDED OCTOBER 6, 1980, IN BOOK 13776, PAGE 341 OF OFFICIAL RECORDS OF ORANGE COUNTY, CALIFORNIA.

WARMINGTON LDR ASSOCIATES III, L.P., A CALIFORNIA LIMITED PARTNERSHIP, OWNER.

BY: WARMINGTON HOMES CALIFORNIA, ITS GENERAL PARTNER.


BY:  NAME: BRIAN L. SINDERHOFF
TITLE: PRESIDENT, So. CAL. DIV.

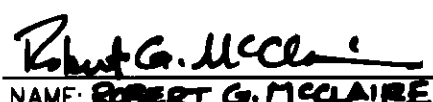BY:  NAME: ROBERT G. MCCLAIRE
TITLE: VP PROJECT DEVELOPMENT


DMB LADERA, L.L.C., A DELAWARE LIMITED LIABILITY COMPANY, BENEFICIARY UNDER A DEED OF TRUST RECORDED AS INSTRUMENT NO. 20010110195 OF OFFICIAL RECORDS.


BY: RANCHO MISSION VIEJO, L.L.C., A DELAWARE LIMITED LIABILITY COMPANY, AS AGENT AND/OR MANAGER.

BY:  NAME: Paul Johnson
TITLE: VP Community Development

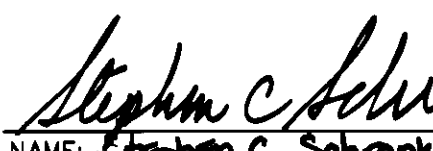BY:  NAME: Stephen C. Schrank
TITLE: Executive VP Development


RESIDENTIAL FUNDING CORPORATION, A DELAWARE CORPORATION, BENEFICIARY UNDER A DEED OF TRUST RECORDED AS INSTRUMENT NO. 20010110196 OF OFFICIAL RECORDS.

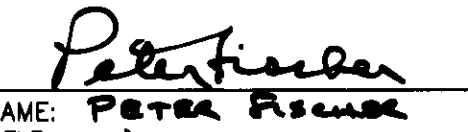BY:  NAME: Peter Ferson
TITLE: Director

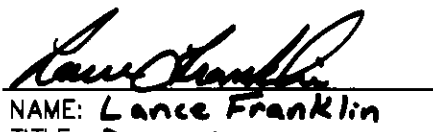BY:  NAME: Lance Franklin
TITLE: Director


CERTIFICATE OF ACCEPTANCE - SANTA MARGARITA WATER DISTRICT


THE UNDERSIGNED, BEING THE DULY APPOINTED AGENT OF THE SANTA MARGARITA WATER DISTRICT, A PUBLIC CORPORATION IN ORANGE COUNTY, CALIFORNIA, PURSUANT TO ITS RESOLUTION NO. 88-10-2, DOES HEREBY ACCEPT ON BEHALF OF SAID DISTRICT THE PIPELINE EASEMENTS FOR WATER, SEWER AND ACCESS PURPOSES, AS DEDICATED AND SHOWN ON THIS TRACT MAP, BY AND BETWEEN THE SANTA MARGARITA WATER DISTRICT AND WARMINGTON LDR ASSOCIATES III, L.P., A CALIFORNIA LIMITED PARTNERSHIP, AND DOES HEREBY CERTIFY THAT THE GRANTEE CONSENTS TO THE RECORDATION OF SAID TRACT MAP.

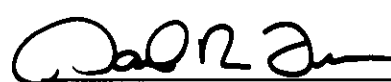
DANIEL R. FERONS, CHIEF ENGINEER
SANTA MARGARITA WATER DISTRICT

SURVEYOR'S STATEMENT:

I HEREBY STATE THAT THIS MAP, CONSISTING OF 6 SHEETS, CORRECTLY REPRESENTS A TRUE AND COMPLETE SURVEY AS SHOWN MADE IN DECEMBER, 2000; WAS MADE BY ME OR UNDER MY DIRECTION; THAT THE MONUMENTS ARE OF THE CHARACTER AND OCCUPY (OR WILL OCCUPY) THE POSITIONS INDICATED BY SAID MAP; AND THAT SAID MONUMENTS ARE (OR WILL BE) SUFFICIENT TO ENABLE THE SURVEY TO BE RETRACED.

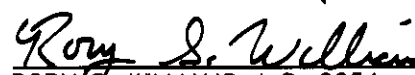 4/17/01
RORY S. WILLIAMS, L.S. 6654 DATE
EXPIRATION DATE: 12/31/03

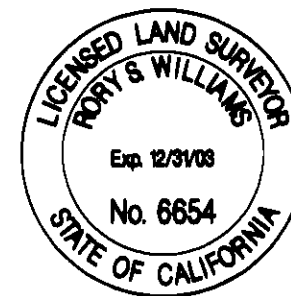


COUNTY SURVEYOR'S STATEMENT

I HEREBY STATE THAT I HAVE EXAMINED THIS MAP AND HAVE FOUND IT TO BE SUBSTANTIALLY IN CONFORMANCE WITH THE TENTATIVE MAP AS FILED WITH, AMENDED AND APPROVED BY THE ORANGE COUNTY SUBDIVISION COMMITTEE; THAT ALL PROVISIONS OF THE SUBDIVISION MAP ACT AND COUNTY SUBDIVISION REGULATIONS HAVE BEEN COMPLIED WITH AND I AM SATISFIED SAID MAP IS TECHNICALLY CORRECT.

DATED THIS 13TH DAY OF JULY, 2001.


JOHN CANAS, COUNTY SURVEYOR
L.S. 4408, EXPIRATION DATE: 9-30-01

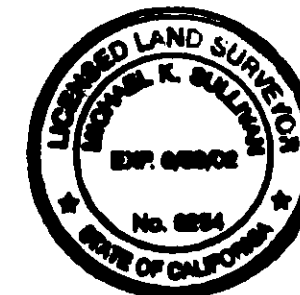

BY: MICHAEL K. SULLIVAN, DEPUTY
L.S. 6254 EXPIRES 6-30-02

COUNTY TREASURER-TAX COLLECTOR'S CERTIFICATE:

STATE OF CALIFORNIA }
COUNTY OF ORANGE } SS

I HEREBY CERTIFY THAT ACCORDING TO THE RECORDS OF MY OFFICE THERE ARE NO LIENS AGAINST THE LAND COVERED BY THIS MAP OR ANY PART THEREOF FOR UNPAID STATE, COUNTY, MUNICIPAL OR LOCAL TAXES OR SPECIAL ASSESSMENTS COLLECTED AS TAXES, EXCEPT TAXES OR SPECIAL ASSESSMENTS COLLECTED AS TAXES NOT YET PAYABLE.

AND DO CERTIFY TO THE RECORDER OF ORANGE COUNTY THAT THE PROVISIONS OF THE SUBDIVISION MAP ACT HAVE BEEN COMPLIED WITH REGARDING DEPOSITS TO SECURE PAYMENT OF TAXES OR SPECIAL ASSESSMENTS COLLECTED AS TAXES ON THE LAND COVERED BY THIS MAP.

DATED THIS 14TH DAY OF JUNE, 2001.

JOHN M.W. MOORLACH
COUNTY TREASURER-TAX COLLECTOR

BY:  DEPUTY TREASURER-TAX COLLECTOR

CLERK OF THE BOARD OF SUPERVISORS' CERTIFICATE:

STATE OF CALIFORNIA }
COUNTY OF ORANGE } SS

I HEREBY CERTIFY THAT THIS MAP WAS PRESENTED FOR APPROVAL TO THE BOARD OF SUPERVISORS OF THE COUNTY OF ORANGE AT A REGULAR MEETING THEREOF HELD ON THE 24TH DAY OF JULY, 2001, AND THAT THEREUPON SAID BOARD DID, BY AN ORDER DULY PASSED AND ENTERED, APPROVE SAID MAP.

AND DID ACCEPT ON BEHALF OF THE COUNTY OF ORANGE:

THE EASEMENT FOR INGRESS AND EGRESS OF EMERGENCY AND PUBLIC SERVICE VEHICLES OVER LOT B, AS DEDICATED.

WE ALSO HEREBY ABANDON, PURSUANT TO SECTION 66499.2(a) OF THE SUBDIVISION MAP ACT, THOSE EASEMENTS FOR STORM DRAIN PURPOSES WITHIN THE BOUNDARY OF THIS MAP, WHICH WERE ACQUIRED BY THE COUNTY OF ORANGE PER TRACT NO. 16155, AS PER MAP FILED IN BOOK 812, PAGES 30 THROUGH 39, INCLUSIVE, OF MISCELLANEOUS MAPS, RECORDS OF ORANGE COUNTY, NOT SHOWN ON THIS MAP.

AND DID ALSO APPROVE SUBJECT MAP PURSUANT TO THE PROVISIONS OF SECTION 66436(a)(3)(A) OF THE SUBDIVISION MAP ACT.

DATED THIS 24TH DAY OF JULY, 2001.


CLERK OF THE BOARD OF SUPERVISORS
DARLENE J. BLOOM



NOTE:

THE PRIVATE STREETS CONSTRUCTED WITHIN THIS MAP SHALL BE OWNED, OPERATED AND MAINTAINED BY THE DEVELOPER, SUCCESSORS OR ASSIGNS. THE COUNTY OF ORANGE SHALL HAVE NO RESPONSIBILITY THEREFOR, UNLESS PURSUANT TO APPROPRIATE SECTIONS OF THE STREET AND HIGHWAYS CODE OF THE STATE OF CALIFORNIA, THE SAID PRIVATE STREETS HAVE BEEN ACCEPTED INTO THE COUNTY ROAD SYSTEM BY APPROPRIATE RESOLUTION OF THE ORANGE COUNTY BOARD OF SUPERVISORS.

NOTE:

SEE SHEET 2 FOR NOTARY ACKNOWLEDGMENTS AND SIGNATURE OMISSIONS.

SHEET 2 OF 6 SHEETS
45 NUMBERED LOTS AND LOTS
A THROUGH L, INCLUSIVE
ACREAGE: 4.956 ACRES
(ALL OF TENTATIVE
TRACT NO. 16127)

TRACT NO. 16127

IN UNINCORPORATED TERRITORY OF THE
COUNTY OF ORANGE, STATE OF CALIFORNIA.

HUNSAKER AND ASSOCIATES IRVINE, INC.
RORY S. WILLIAMS, LS. 6654 DATE OF SURVEY: DECEMBER, 2000

NOTARY ACKNOWLEDGMENTS:

STATE OF CALIFORNIA }
COUNTY OF ORANGE } SS
ON 4/18/01, BEFORE ME, Betty Jo Poston, PERSONALLY
APPEARED B. K. Sinderhoff AND Robert H. McClane PERSONALLY
KNOWN TO ME (OR PROVED TO ME ON THE BASIS OF SATISFACTORY EVIDENCE) TO BE THE PERSON(S)
WHOSE NAME(S) IS/ARE SUBSCRIBED TO THE WITHIN INSTRUMENT AND ACKNOWLEDGED TO ME THAT
HE/SHE/THEY EXECUTED THE SAME IN HIS/HER/THEIR AUTHORIZED CAPACITY(IES), AND THAT BY
HIS/HER/THEIR SIGNATURE(S) ON THE INSTRUMENT THE PERSON(S), OR ENTITY UPON BEHALF OF
WHICH THE PERSON(S) ACTED, EXECUTED THE INSTRUMENT.
WITNESS MY HAND:
SIGNATURE Betty Jo Poston MY PRINCIPAL PLACE OF BUSINESS IS
NOTARY PUBLIC IN AND FOR SAID STATE IN Orange COUNTY.
Betty Jo Poston MY COMMISSION EXPIRES: 3/17/2005
(NAME PRINTED)

STATE OF CALIFORNIA }
COUNTY OF ORANGE } SS
ON 5/2/01, BEFORE ME, Tina T. Baker, Notary Public PERSONALLY
APPEARED Paul Johnson AND Stephen C. Schrank PERSONALLY
KNOWN TO ME (OR PROVED TO ME ON THE BASIS OF SATISFACTORY EVIDENCE) TO BE THE PERSON(S)
WHOSE NAME(S) IS/ARE SUBSCRIBED TO THE WITHIN INSTRUMENT AND ACKNOWLEDGED TO ME THAT
HE/SHE/THEY EXECUTED THE SAME IN HIS/HER/THEIR AUTHORIZED CAPACITY(IES), AND THAT BY
HIS/HER/THEIR SIGNATURE(S) ON THE INSTRUMENT THE PERSON(S), OR ENTITY UPON BEHALF OF
WHICH THE PERSON(S) ACTED, EXECUTED THE INSTRUMENT.
WITNESS MY HAND:
SIGNATURE Tina T. Baker MY PRINCIPAL PLACE OF BUSINESS IS
NOTARY PUBLIC IN AND FOR SAID STATE IN Orange COUNTY.
Tina T. Baker MY COMMISSION EXPIRES: 8-28-04
(NAME PRINTED)

STATE OF CALIFORNIA }
COUNTY OF ORANGE } Los Angeles
ON 4/19/01, BEFORE ME, Gonia C. Garcia PERSONALLY
APPEARED Ruben Fischer AND Larisa Franklin PERSONALLY
KNOWN TO ME (OR PROVED TO ME ON THE BASIS OF SATISFACTORY EVIDENCE) TO BE THE PERSON(S)
WHOSE NAME(S) IS/ARE SUBSCRIBED TO THE WITHIN INSTRUMENT AND ACKNOWLEDGED TO ME THAT
HE/SHE/THEY EXECUTED THE SAME IN HIS/HER/THEIR AUTHORIZED CAPACITY(IES), AND THAT BY
HIS/HER/THEIR SIGNATURE(S) ON THE INSTRUMENT THE PERSON(S), OR ENTITY UPON BEHALF OF
WHICH THE PERSON(S) ACTED, EXECUTED THE INSTRUMENT.
WITNESS MY HAND:
SIGNATURE Gonia C. Garcia MY PRINCIPAL PLACE OF BUSINESS IS
NOTARY PUBLIC IN AND FOR SAID STATE IN Los Angeles COUNTY.
SONIA E. GARCIA MY COMMISSION EXPIRES: May 9, 2003
(NAME PRINTED)

NOTARY ACKNOWLEDGMENT - SANTA MARGARITA WATER DISTRICT

STATE OF CALIFORNIA }
COUNTY OF ORANGE } SS
ON 6-12-01, BEFORE ME, Cindy R. Lane, Notary Public PERSONALLY
APPEARED DANIEL R. FERONS, PERSONALLY
KNOWN TO ME (OR PROVED TO ME ON THE BASIS OF SATISFACTORY EVIDENCE) TO BE THE PERSON
WHOSE NAME IS SUBSCRIBED TO THE WITHIN INSTRUMENT AND ACKNOWLEDGED TO ME THAT
HE EXECUTED THE SAME IN HIS AUTHORIZED CAPACITY, AND THAT BY
HIS SIGNATURE ON THE INSTRUMENT THE PERSON, OR ENTITY UPON BEHALF OF
WHICH THE PERSON ACTED, EXECUTED THE INSTRUMENT.
WITNESS MY HAND:
SIGNATURE Cindy R. Lane MY PRINCIPAL PLACE OF BUSINESS IS
NOTARY PUBLIC IN AND FOR SAID STATE IN Orange COUNTY.
CINDY R. LANE MY COMMISSION EXPIRES: 7-20-2005
(NAME PRINTED)

SIGNATURE OMISSIONS:
PURSUANT TO THE PROVISIONS OF SECTION 66436 (a)(3)(C) OF THE SUBDIVISION MAP ACT, THE
FOLLOWING SIGNATURES HAVE BEEN OMITTED:
SANTA MARGARITA WATER DISTRICT, HOLDER OF AN EASEMENT DEDICATED ON THE MAP OF
TRACT NO. 16155.
DMB LADERA, LLC, HOLDER OF EASEMENTS RECORDED AS INSTRUMENT NO. 20010110193 OF
OFFICIAL RECORDS.
LADERA DEVELOPMENT COMPANY, L.L.C., HOLDER OF OIL, GAS AND MINERAL RIGHTS RECORDED
AS INSTRUMENT NO. 19960624029 OF OFFICIAL RECORDS.
THE COUNTY OF ORANGE, HOLDER OF EASEMENTS DEDICATED ON THE MAP OF TRACT NO.
16155.

SHEET 3 OF 6 SHEETS
SCALE: 1" = 60'
45 NUMBERED LOTS AND LOTS
A THROUGH L, INCLUSIVE
ACREAGE: 4.956 ACRES
(ALL OF TENTATIVE
TRACT NO. 16127)

TRACT NO. 16127

IN UNINCORPORATED TERRITORY OF THE COUNTY OF ORANGE,
STATE OF CALIFORNIA

HUNSAKER AND ASSOCIATES IRVINE, INC.
RORY S. WILLIAMS, L.S. 6654 DATE OF SURVEY: DECEMBER, 2000

SHEET INDEX AND GPS CONTROL MAP

BASIS OF BEARINGS:

THE BEARINGS SHOWN HEREON ARE BASED ON THE BEARING BETWEEN
O.C.S. HORIZONTAL CONTROL STATION GPS NO. 1417 AND STATION
GPS NO. 1448 BEING N10°48'13"E PER RECORDS ON FILE IN THE
OFFICE OF THE ORANGE COUNTY SURVEYOR.

DATUM STATEMENT:

COORDINATES SHOWN ARE BASED ON THE CALIFORNIA COORDINATE
SYSTEM (CCS83), ZONE VI, 1983 NAD, (1991.35 EPOCH OCS GPS
ADJUSTMENT).

ALL DISTANCES SHOWN ARE GROUND, UNLESS OTHERWISE NOTED. TO
OBTAIN GRID DISTANCE MULTIPLY GROUND DISTANCE BY 0.999948295.

NOTES:

LOT A IS FOR PRIVATE PARK PURPOSES.

LOT B IS FOR PRIVATE STREET AND PRIVATE ALLEY PURPOSES.

LOTS C THROUGH L, INCLUSIVE, ARE FOR LANDSCAPE PURPOSES AND ARE
NOT SEPARATE BUILDING SITES.

THE PROPERTY IS IN A SPECIAL FIRE PROTECTION AREA. TOTAL
EXCLUSION GRANTED FOR THIS TRACT.

EASEMENT NOTES:

- (A) INDICATES AN EASEMENT FOR WATER, SEWER AND ACCESS PURPOSES
DEDICATED HEREON TO THE SANTA MARGARITA WATER DISTRICT.
- (B) INDICATES AN EASEMENT FOR INGRESS AND EGRESS OF EMERGENCY
AND PUBLIC SERVICE VEHICLES DEDICATED HEREON TO THE COUNTY
OF ORANGE.
- (C) INDICATES AN EASEMENT FOR PUBLIC UTILITY PURPOSES RESERVED
HEREON FOR FUTURE GRANT.
- (D) INDICATES AN EASEMENT FOR SEWER, WATER AND ACCESS PURPOSES
DEDICATED TO THE SANTA MARGARITA WATER DISTRICT PER TRACT
NO. 16155, M.M. 812/30-39.
- (E) INDICATES AN EASEMENT FOR SIDEWALK PURPOSES DEDICATED TO
THE COUNTY OF ORANGE PER TRACT NO. 16155, M.M. 812/30-39.
- (F) INDICATES AN EASEMENT FOR INGRESS AND EGRESS PURPOSES
RESERVED HEREON FOR THE BENEFIT OF LOT 5.
- (G) INDICATES AN EASEMENT FOR INGRESS AND EGRESS PURPOSES
RESERVED HEREON FOR THE BENEFIT OF LOT 6.

MONUMENT NOTES:

LEAD, TACK & TAG L.S. 6654 TO BE SET IN TOP OF CURB AT AN OFFSET OF 19.75' ALONG
FRONT SIDE LOT LINES PRODUCED FOR LOTS 16 THROUGH 23, INCLUSIVE, IN LIEU OF AT
FRONT LOT CORNERS, WITHIN 90 DAYS AFTER ACCEPTANCE OF IMPROVEMENTS, UNLESS
OTHERWISE NOTED.

LEAD, TACK & TAG L.S. 6654 TO BE SET IN TOP OF CURB AT AN OFFSET OF 9.75' ALONG
FRONT SIDE LOT LINES PRODUCED FOR LOTS 35 THROUGH 45, INCLUSIVE, IN LIEU OF AT
FRONT LOT CORNERS, WITHIN 90 DAYS AFTER ACCEPTANCE OF IMPROVEMENTS, UNLESS
OTHERWISE NOTED. FOR ALL SIDE LOT LINES NON-RADIAL OR NON-PERPENDICULAR TO
STREET RIGHT OF WAY, OR NOT AT AN OFFSET OF 9.75', BEARING AND DISTANCE OF
PRODUCTION IS AS NOTED HEREON.

LEAD, TACK & TAG L.S. 6654 TO BE SET IN TOP OF CURB AT AN OFFSET OF 10.75' ALONG
FRONT SIDE LOT LINES PRODUCED FOR LOTS 6 THROUGH 15, INCLUSIVE, IN LIEU OF AT
FRONT LOT CORNERS, WITHIN 90 DAYS AFTER ACCEPTANCE OF IMPROVEMENTS, UNLESS
OTHERWISE NOTED. FOR ALL SIDE LOT LINES NON-RADIAL OR NON-PERPENDICULAR TO
STREET RIGHT OF WAY, BEARING AND DISTANCE OF PRODUCTION IS AS NOTED HEREON.

LEAD, TACK & TAG L.S. 6654 TO BE SET IN TOP OF CURB AT AN OFFSET AS INDICATED IN
THE MONUMENT OFFSET TABLES SHOWN HEREON ALONG FRONT SIDE LOT LINES PRODUCED
FOR ALL OTHER LOTS, IN LIEU OF AT FRONT LOT CORNERS, WITHIN 90 DAYS AFTER
ACCEPTANCE OF IMPROVEMENTS, UNLESS OTHERWISE NOTED.

LEAD, TACK & TAG L.S. 6654 TO BE SET IN TOP OF CURB ON ALL REAR SIDE LOT LINES AT
A 0.50' OFFSET INSIDE THE LOT CORNER FROM INTERSECTION WITH 24.00' WIDE PRIVATE
ALLEY RIGHTS OF WAY, IN LIEU OF AT REAR LOT CORNERS, WITHIN 90 DAYS AFTER
ACCEPTANCE OF IMPROVEMENTS. (THE REARS OF ALL LOTS FACE THE PRIVATE ALLEYS.)

8" S&W STAMPED L.S. 6654 OR LEAD, TACK & TAG L.S. 6654 OR 1" I.P. TAGGED L.S. 6654
IN MEDIAN TO BE SET AT ALL STREET CENTERLINE POINTS OF CONTROL, WITHIN 90 DAYS
AFTER ACCEPTANCE OF IMPROVEMENTS, UNLESS OTHERWISE NOTED.

● INDICATES FOUND MONUMENT OR LOCATION OF MONUMENT TO BE SET, AS NOTED.

■ INDICATES NOTHING TO BE SET.

P# INDICATES BEARING AND DISTANCE OF LOT LINE PRODUCTION FROM LOT
CORNER TO MONUMENT.

1 INDICATES LOCATION OF 1" IRON PIPE TAGGED "L.S. 5557" OR SPIKE &
WASHER STAMPED "L.S. 5557" OR LEAD, TACK & TAG "L.S. 5557" TO BE
SET WITHIN 90 DAYS AFTER ACCEPTANCE OF IMPROVEMENTS, PER TRACT
NO. 16155, M.M. 812/30-39.

2 INDICATES LOCATION OF 1" IRON PIPE TAGGED "L.S. 5557" OR SPIKE &
WASHER STAMPED "L.S. 5557" OR LEAD, TACK & TAG "L.S. 5557" TO BE
SET AT THE OFFSET POSITION INDICATED, WITHIN 90 DAYS AFTER ACCEPTANCE
OF IMPROVEMENTS, PER TRACT NO. 16155, M.M. 812/30-39.

3 INDICATES LOCATION OF 1" IRON PIPE TAGGED "L.S. 6654" OR SPIKE &
WASHER STAMPED "L.S. 6654" OR LEAD, TACK & TAG "L.S. 6654" TO BE
SET WITHIN 90 DAYS AFTER ACCEPTANCE OF IMPROVEMENTS.

TRACT NO. 16155

M.M. 812 / 30 - 39



LOT 6

GPS NO. 1448
FD. 2 1/2" IRON PIPE WITH 2" OCS
BRASS CAP STAMPED "GPS 1448 9-95"
PER R.S.B. 154/8-18
AND RECORDS ON FILE IN THE
ORANGE COUNTY SURVEYOR'S OFFICE
N 2146790.819
E 6142602.585

GPS NO. 1417
FD. 2 1/2" IRON PIPE WITH 2" OCS
BRASS CAP STAMPED "GPS 1417 9-95"
PER R.S.B. 154/8-18
AND RECORDS ON FILE IN THE
ORANGE COUNTY SURVEYOR'S OFFICE.
N 2141450.558
E 6141583.535

4

INDICATES SHEET NUMBER

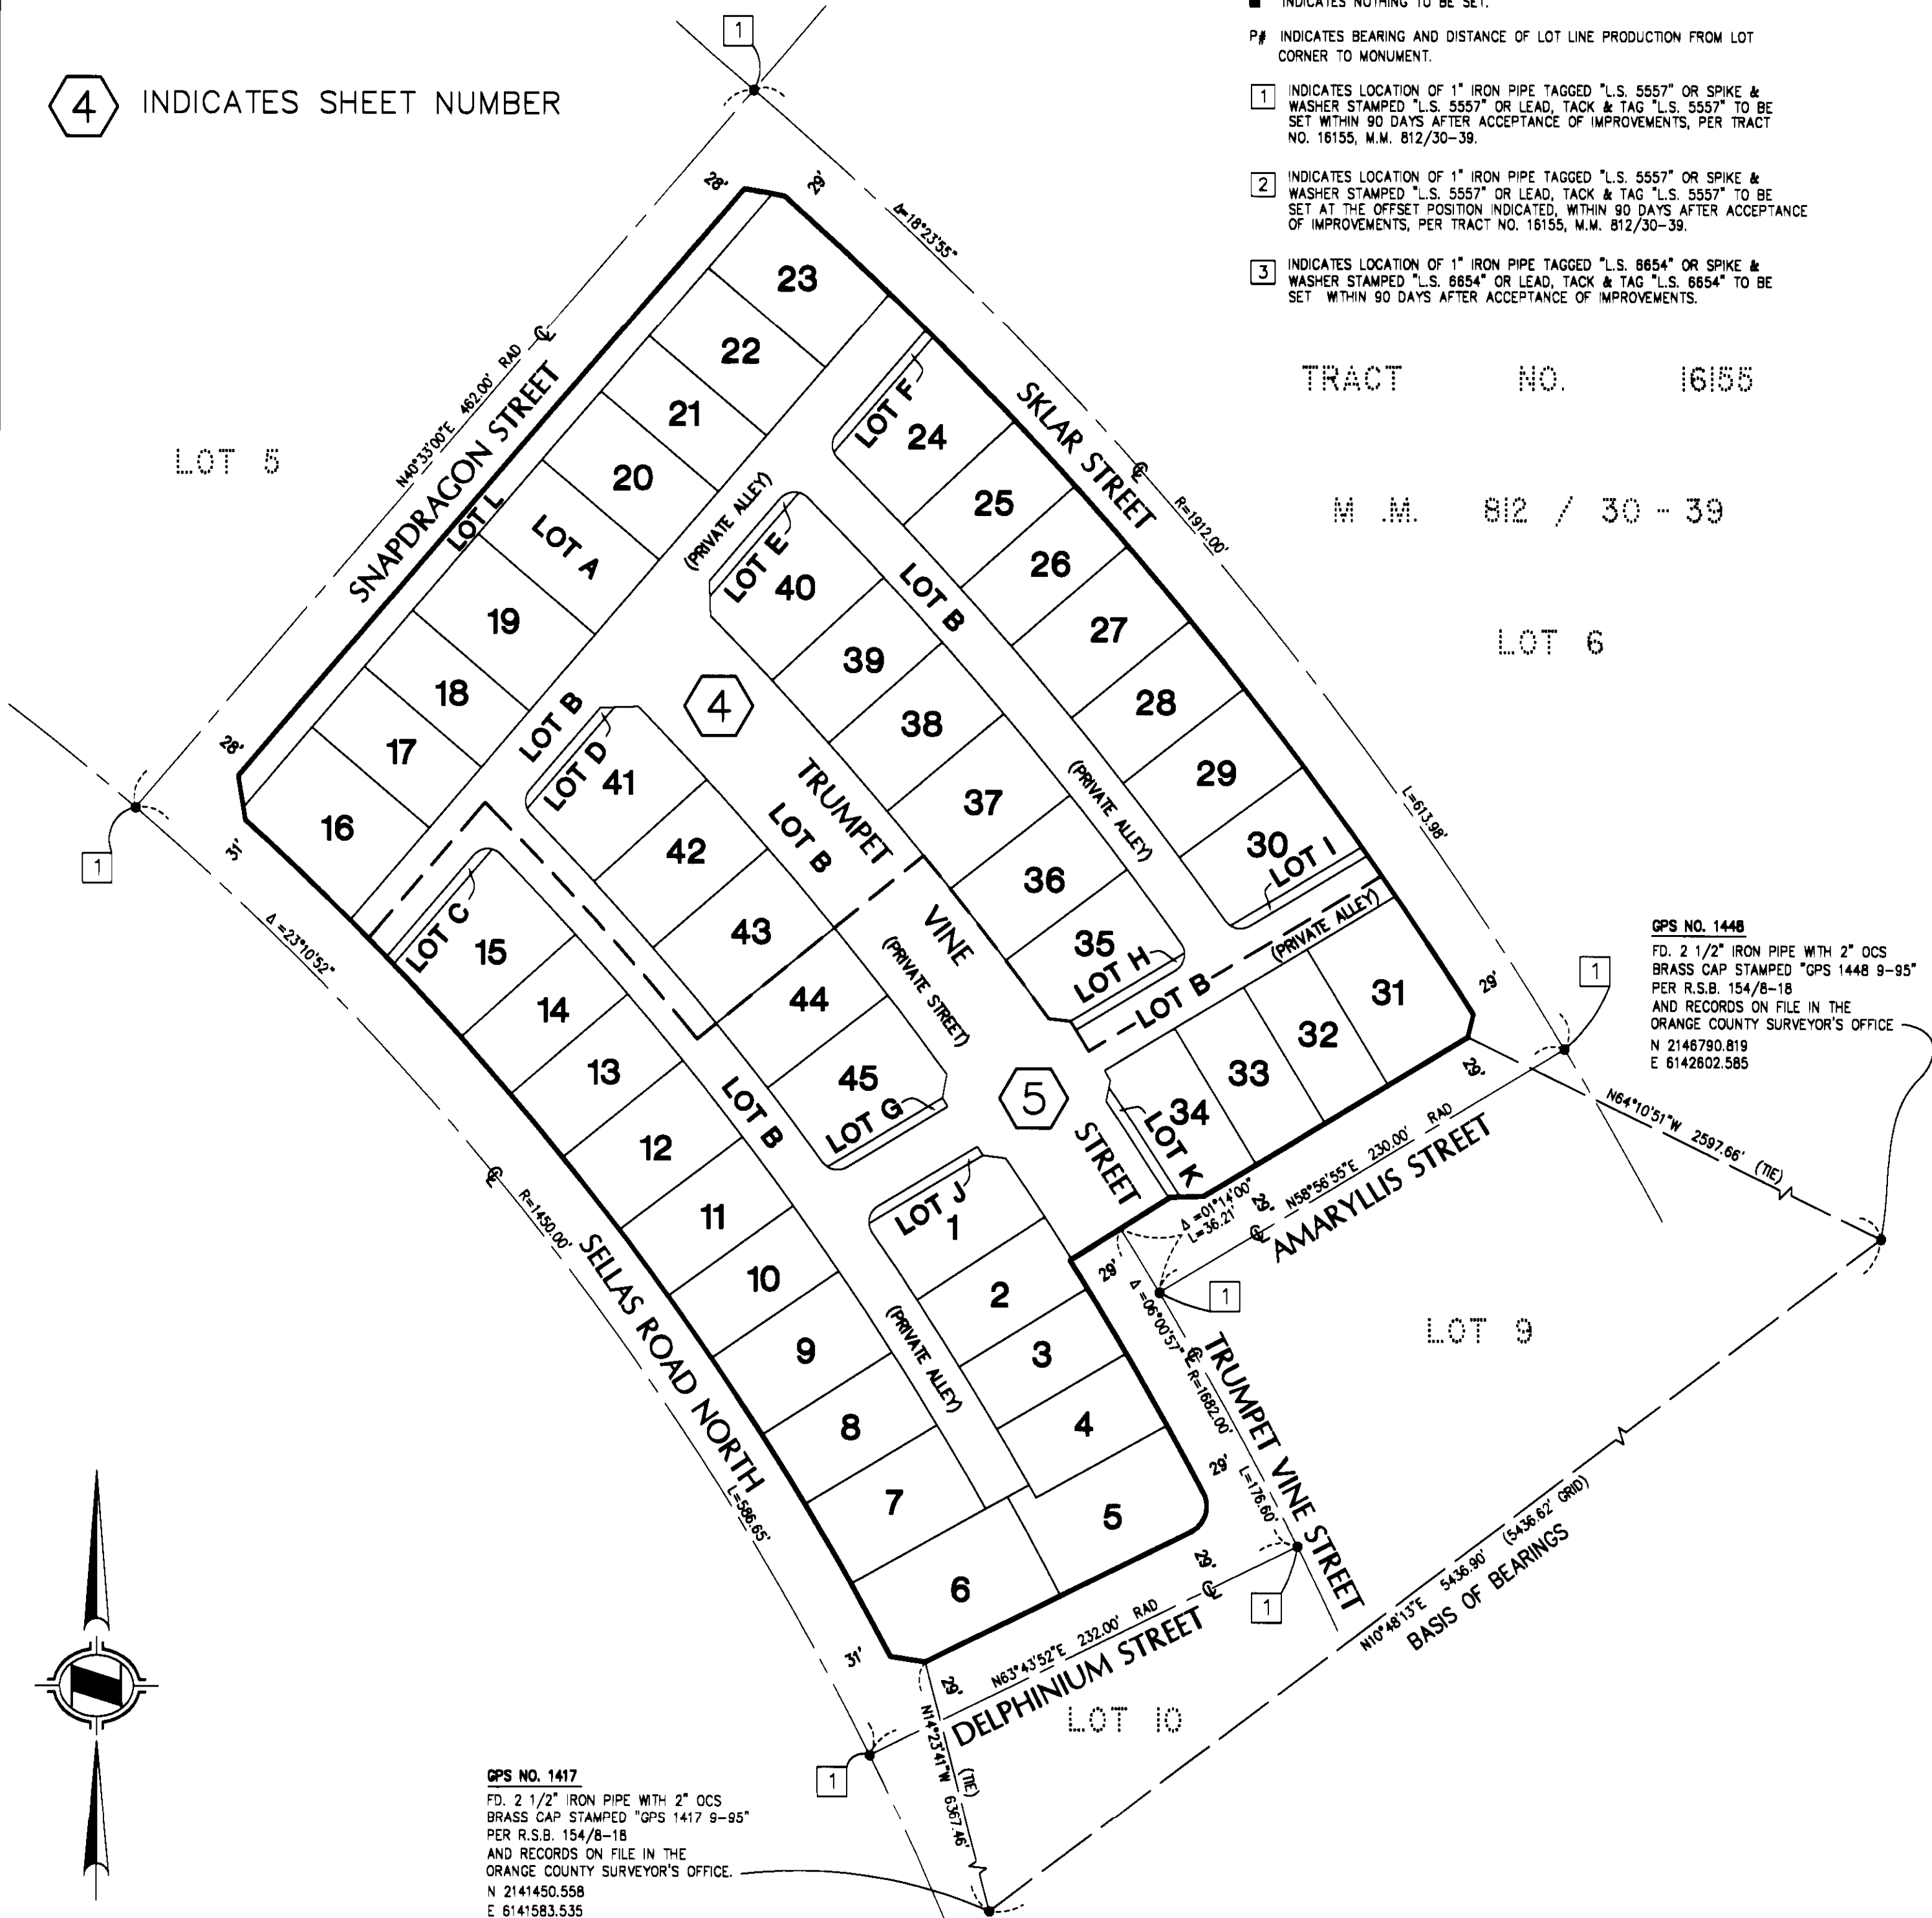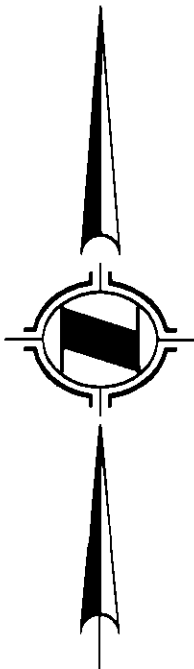

SHEET 4 OF 8 SHEETS
SCALE: 1" = 30'
45 NUMBERED LOTS AND LOTS
A THROUGH L, INCLUSIVE
ACREAGE: 4.958 ACRES
(ALL OF TENTATIVE
TRACT NO. 16127)


TRACT NO. 16127

IN UNINCORPORATED TERRITORY OF THE COUNTY OF ORANGE,
STATE OF CALIFORNIA

RORY S. WILLIAMS, L.S. 8654
HUNSAKER AND ASSOCIATES IRVINE, INC.
DATE OF SURVEY: DECEMBER, 2000

SEE SHEET 3 FOR SHEET INDEX AND GPS CONTROL
MAP, MONUMENT NOTES, BASIS OF BEARINGS, DATUM
STATEMENT, EASEMENT NOTES AND NOTES.

NOTE: ALL SANTA MARGARITA EASEMENTS
ARE SHOWN ON SHEET 6.

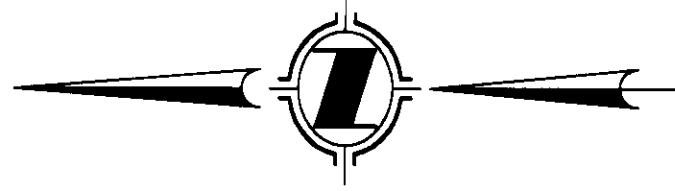

CURVE TABLE			
CURVE	DELTA	RADIUS	LENGTH
C7	95°31'37"	9.00'	15.00'
C8	00°29'08"	1481.00'	12.55'
C9	00°29'07"	1481.00'	12.54'
C10	00°58'15"	1481.00'	25.09'
C11	00°22'53"	1883.00'	12.53'
C12	00°22'52"	1883.00'	12.53'
C13	00°45'45"	1883.00'	25.06'
C14	00°09'09"	1883.00'	5.01'
C15	21°41'03"	9.00'	3.41'
C16	63°36'44"	9.00'	9.99'
C17	85°17'47"	9.00'	13.40'
C18	63°36'44"	9.00'	9.99'
C19	22°00'01"	9.00'	3.46'
C20	85°36'45"	9.00'	13.45'
C21	00°21'57"	1883.00'	12.03'
C22	00°21'57"	1883.00'	12.03'
C23	00°09'09"	1883.00'	5.01'
C24	00°43'54"	1883.00'	24.05'
C25	63°36'44"	9.00'	9.99'
C26	30°52'45"	9.00'	4.85'
C27	94°29'29"	9.00'	14.84'
C28	63°36'44"	9.00'	9.99'
C29	31°12'11"	9.00'	4.90'
C30	94°48'55"	9.00'	14.89'
C31	63°36'44"	9.00'	9.99'
C32	21°00'26"	9.00'	3.30'
C33	84°37'10"	9.00'	13.29'

MONUMENT OFFSET TABLE		
LINE	BEARING	LENGTH
P7	N40°33'00"E	10.78'
P8	N45°41'59"E	10.75'
P9	N48°00'42"E	16.75'
P10	N49°11'44"E	16.75'
P11	N50°38'16"E	16.75'
P12	N51°55'07"E	10.75'
P13	N53°21'39"E	10.75'
P14	N58°56'55"E	10.78'
P20	S58°56'55"W	14.29'
P21	S40°33'00"W	18.10'
P22	N40°33'00"E	18.37'

LOT 6
TRACT NO. 16155
M.M. 812/30-39

LOT 5
TRACT NO. 16155
M.M. 812/30-39

LOT 2
TRACT NO. 16157
M.M. 813/1-9

SEE

SHEET

32

5

SHEET 5 OF 6 SHEETS
SCALE: T = 30'
45 NUMBERED LOTS AND LOTS
A THROUGH L INCLUSIVE
ACREAGE: 4.956 ACRES
(ALL OF TENTATIVE
TRACT NO. 16127)

TRACT NO. 16127
IN UNINCORPORATED TERRITORY OF THE COUNTY OF ORANGE,
STATE OF CALIFORNIA

HUNSAKER AND ASSOCIATES IRVINE, INC.
RORY S. WILLIAMS, L.S. 8654
DATE OF SURVEY: DECEMBER, 2000
SHEET

SEE

LOT 6
TRACT NO. 16155
M.M. 812/30-39


LINE	BEARING	LENGTH
P1	N58°56'55"E	13.63'
P2	N58°52'19"E	9.75'
P3	N58°15'47"E	16.75'
P4	N58°32'36"E	16.75'
P5	N60°56'04"E	15.53'
P6	S40°33'00"W	10.80'
P15	S31°03'05"E	10.75'
P16	S31°03'05"E	10.75'
P17	S31°03'05"E	10.75'
P18	R=1715.00'	22.05'
P19	R=1715.00'	6.81'
P20	S58°56'55"W	14.29'
P23	N58°56'55"E	11.11'

CURVE	DELTA	RADIUS	LENGTH
C1	63°36'44"	9.00'	9.99'
C2	28°53'15"	9.00'	4.70'
C3	93°20'58"	9.00'	14.69'
C4	63°36'44"	9.00'	9.99'
C5	31°54'53"	9.00'	5.07'
C6	95°31'37"	1481.00'	15.00'
C7	95°31'37"	9.00'	15.00'
C8	00°29'08"	1481.00'	12.54'
C9	00°29'07"	1481.00'	12.54'
C10	00°58'15"	1481.00'	25.08'
C21	00°21'57"	1883.00'	12.03'
C22	00°21'57"	1883.00'	12.03'
C24	00°43'54"	1883.00'	24.05'
C27	94°29'29"	9.00'	14.84'
C34	63°36'44"	9.00'	9.99'
C35	21°22'10"	9.00'	3.36'
C36	84°58'54"	9.00'	13.35'



SEE SHEET 3 FOR SHEET INDEX AND GPS CONTROL
MAP, MONUMENT NOTES, BASIS OF BEARINGS, DATUM
STATEMENT, EASEMENT NOTES AND NOTES.

NOTE: ALL SANTA MARGARITA EASEMENTS
ARE SHOWN ON SHEET 6.

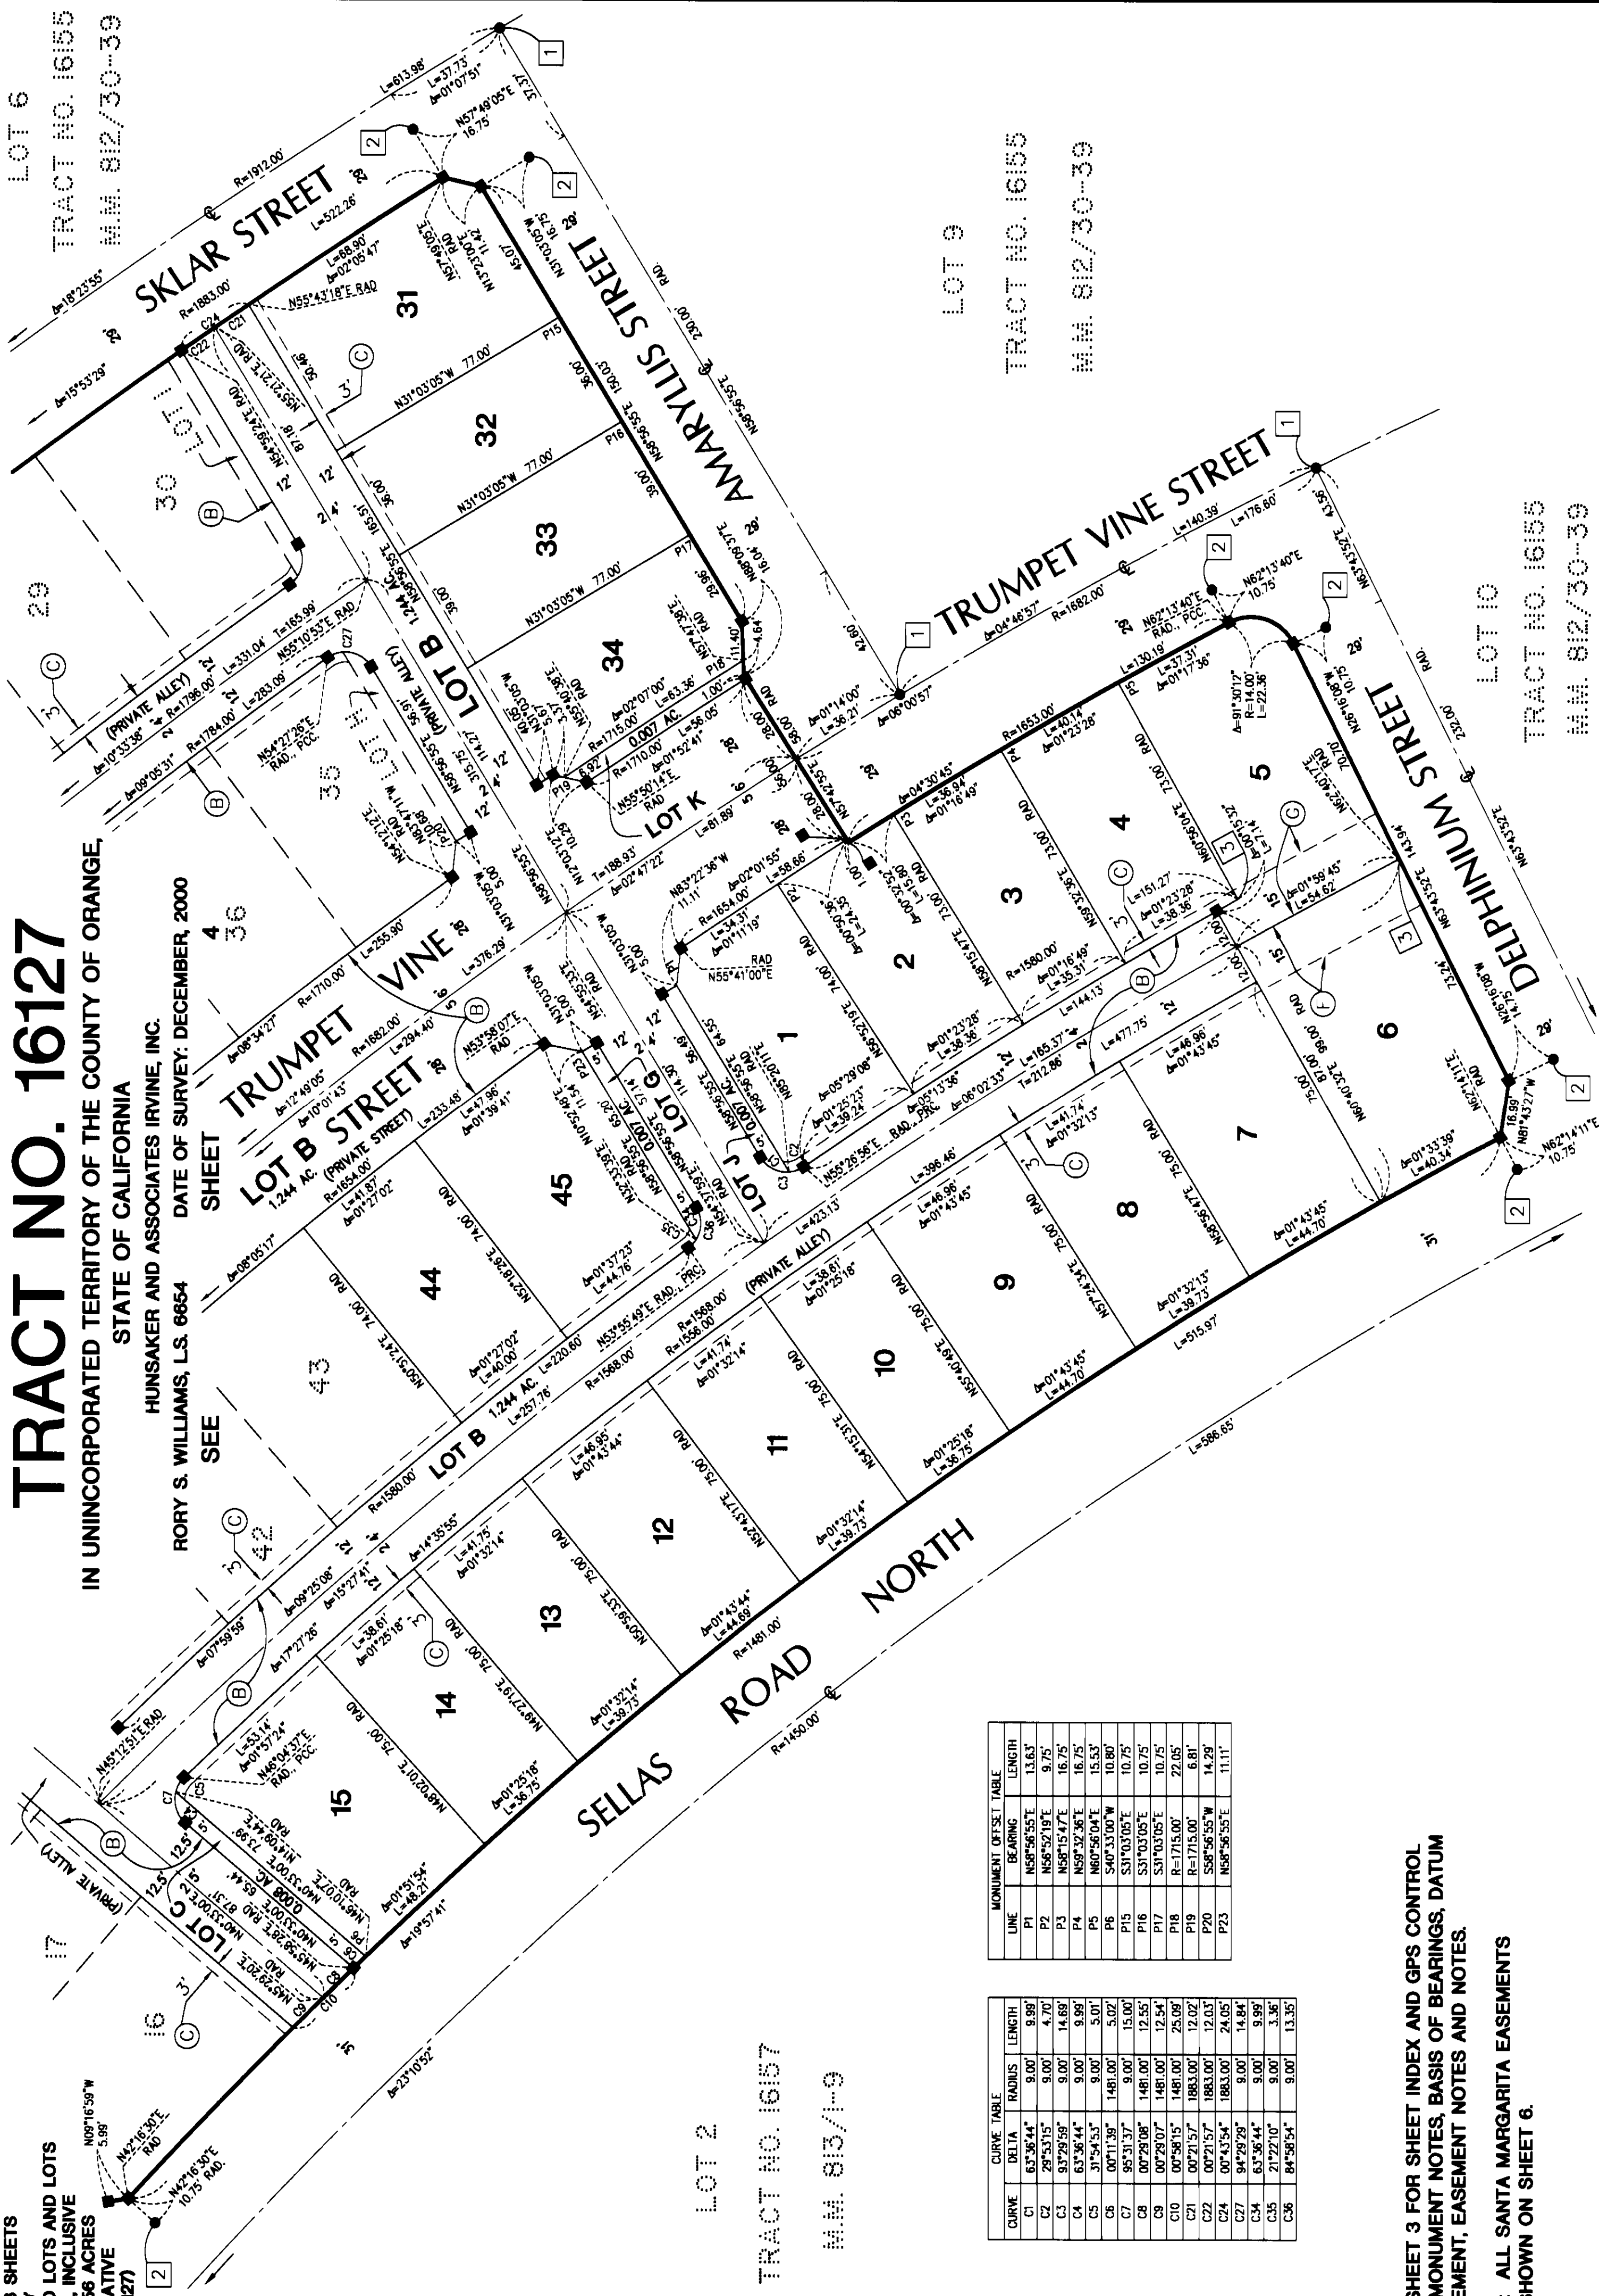

LOT 9
TRACT NO. 16155
M.M. 812/30-39

LOT 10
TRACT NO. 16155
M.M. 812/30-39

LOT 2
TRACT NO. 16157
M.M. 813/1-3


SHEET 6 OF 6 SHEETS
SCALE 1" = 40'
45 NUMBERED LOTS AND LOTS
A THROUGH L, INCLUSIVE
ACREAGE: 4.958 ACRES
(ALL OF TENTATIVE
TRACT NO. 16127)

TRACT NO. 16127

IN UNINCORPORATED TERRITORY OF THE COUNTY OF ORANGE,
STATE OF CALIFORNIA



HUNSAKER AND ASSOCIATES IRVINE, INC.
RORY S. WILLIAMS, L.S. 6654 DATE OF SURVEY: DECEMBER, 2000

SANTA MARGARITA WATER DISTRICT EASEMENT DETAIL SHEET

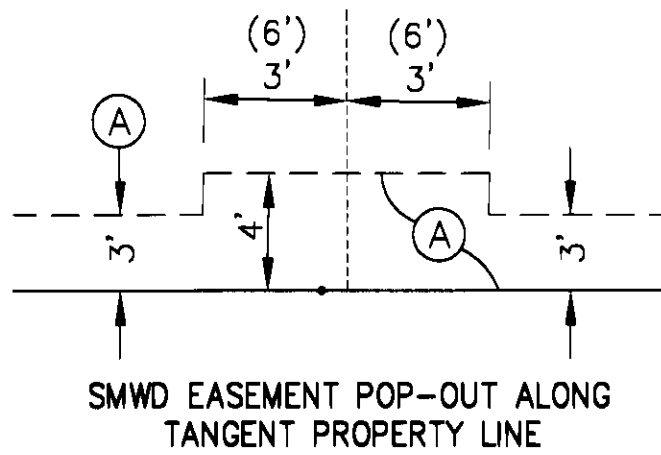

CURVE TABLE			
CURVE	DELTA	RADIUS	LENGTH
C1	00°43'49"	1337.00'	17.04'
C2	00°43'52"	1337.00'	17.08'
C3	00°39'38"	1481.00'	17.08'
C4	00°39'35"	1481.00'	17.08'

LINE TABLE		
LINE	BEARING	LENGTH
L1	N40°33'00"E	11.78'
L2	N40°33'00"E	11.38'
L3	N40°33'00"E	11.59'

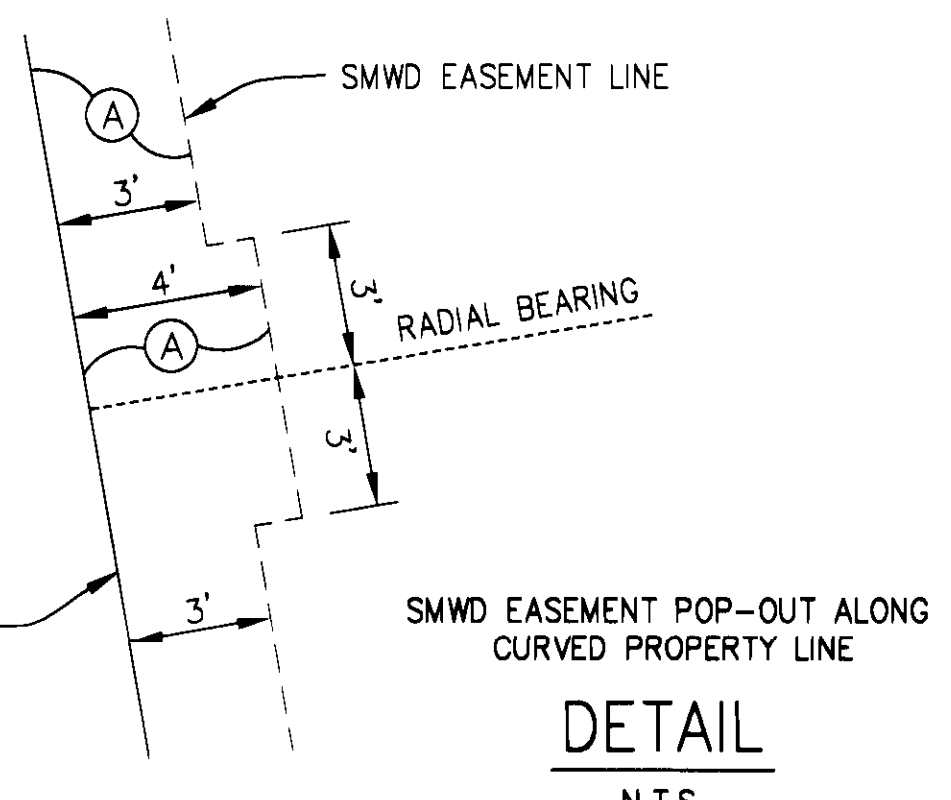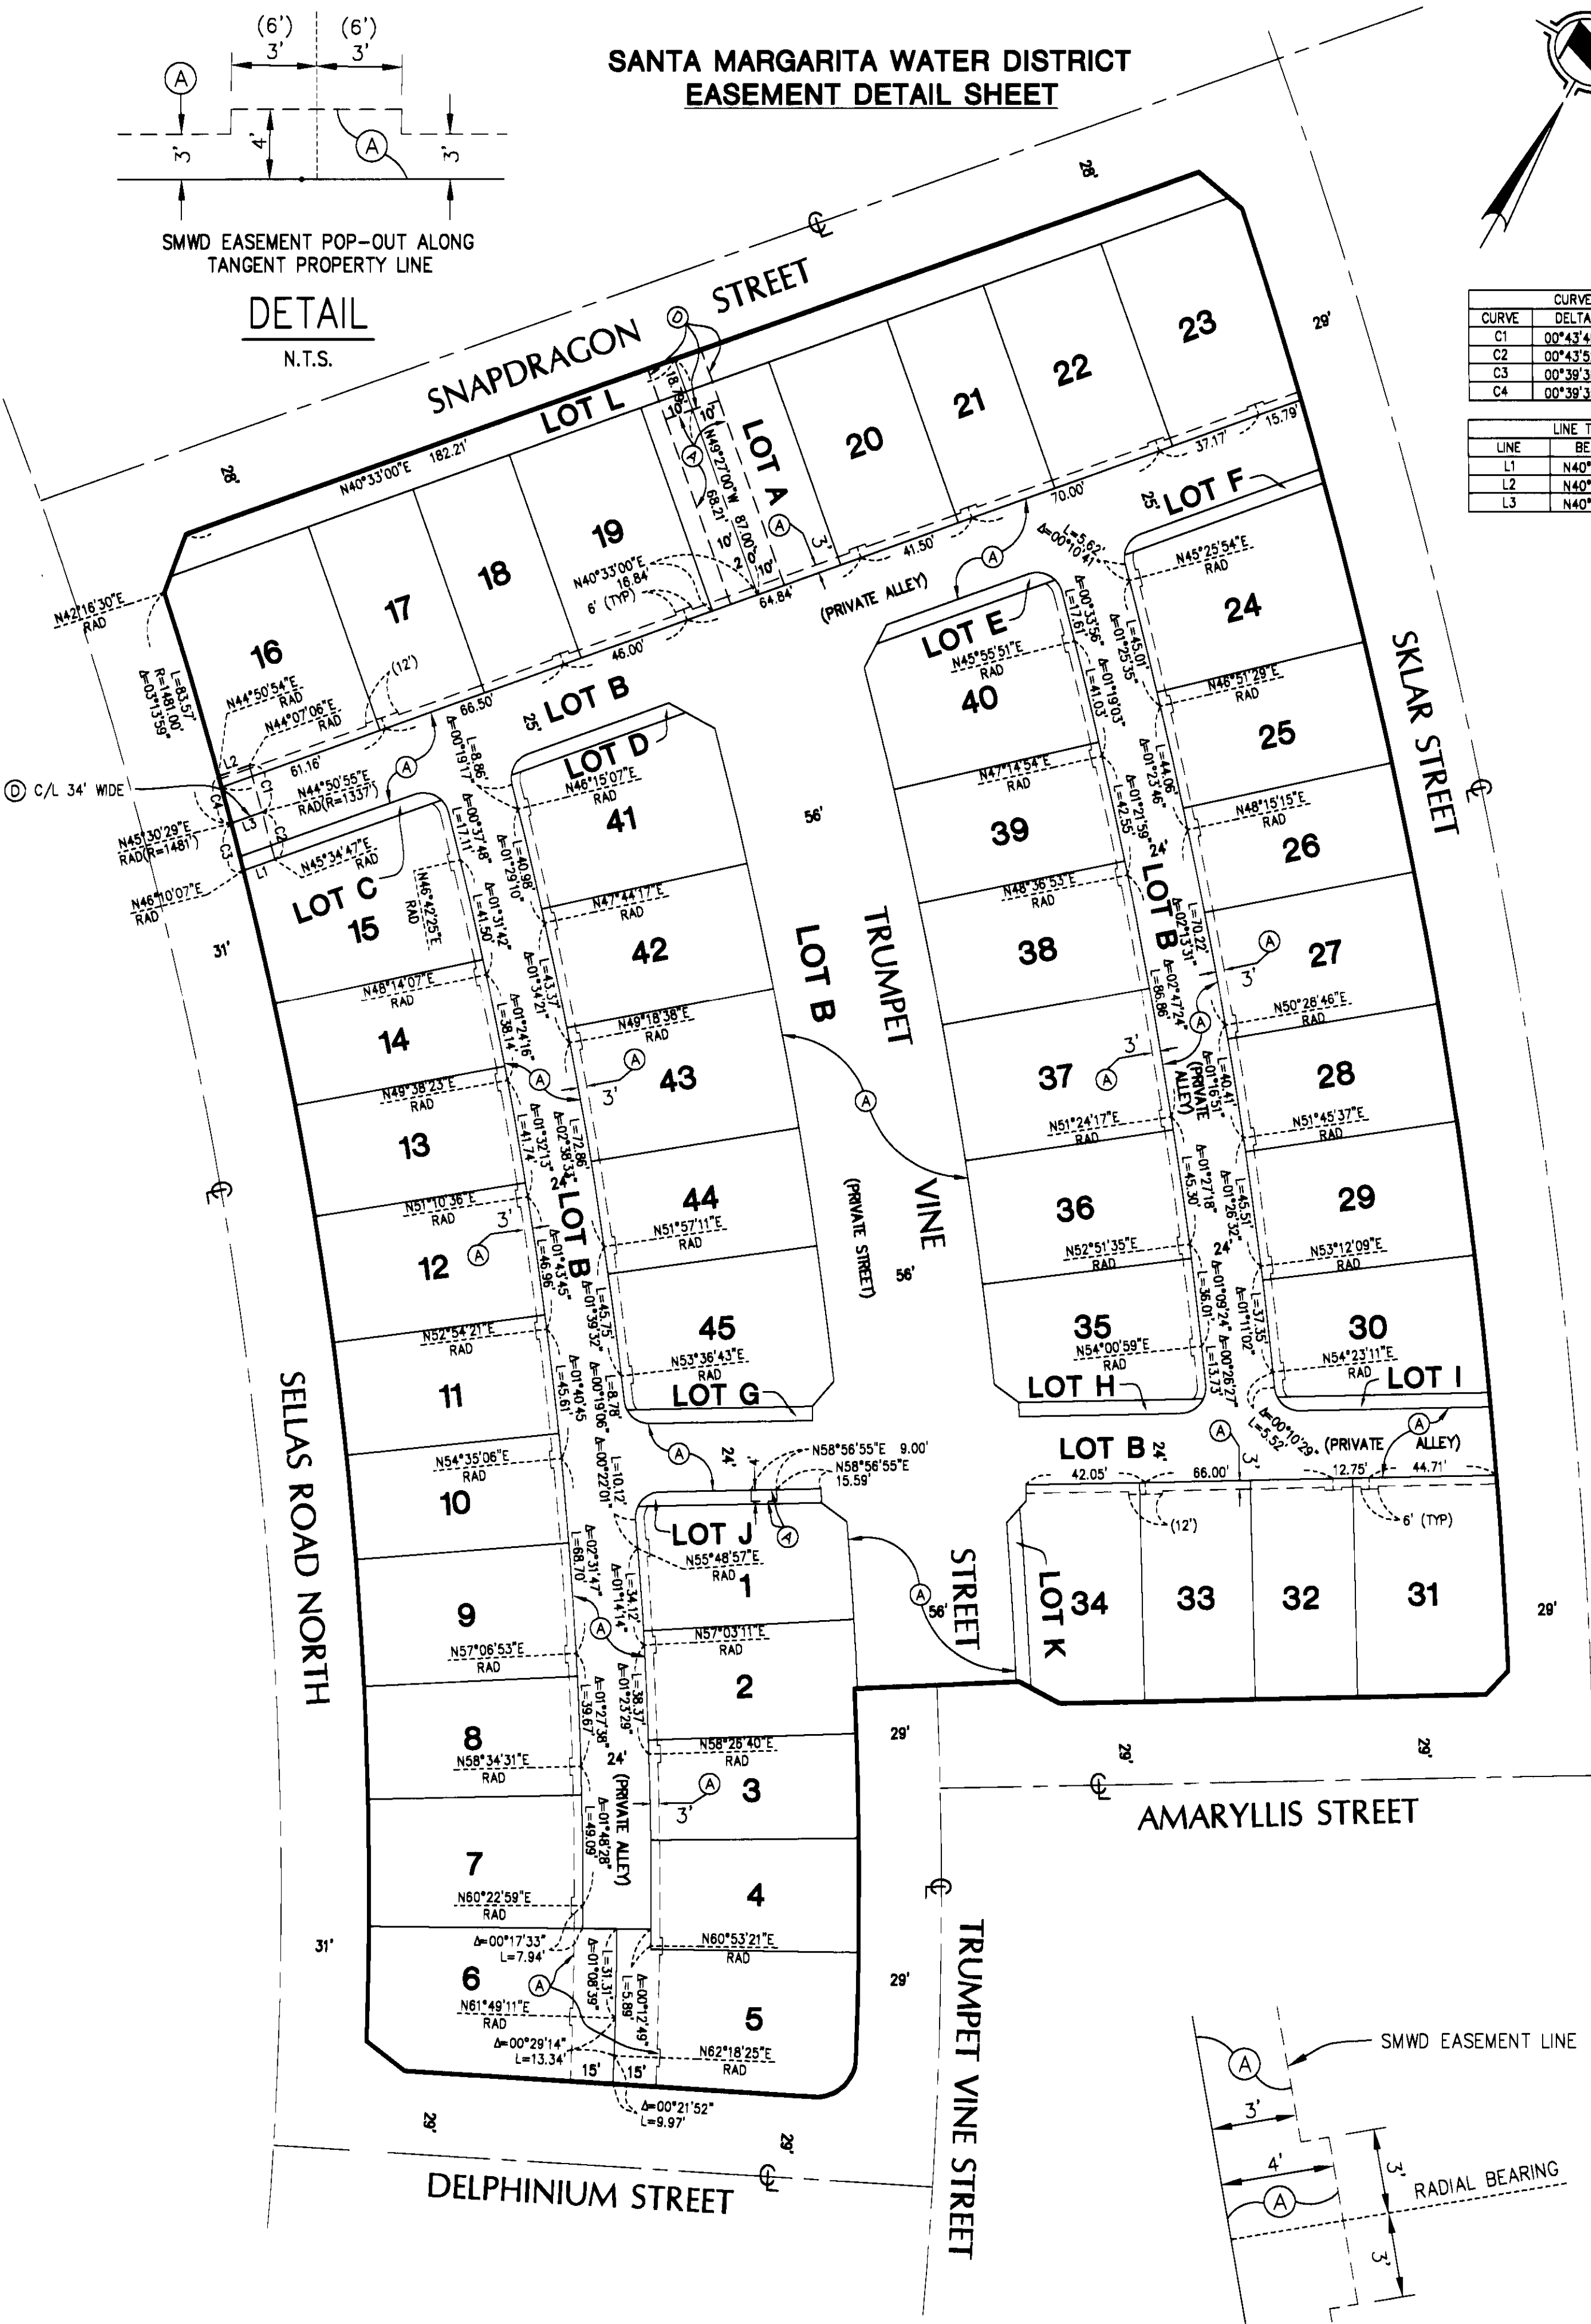

SEE SHEET 3 FOR SHEET INDEX AND GPS CONTROL
MAP, MONUMENT NOTES, BASIS OF BEARINGS, DATUM
STATEMENT, EASEMENT NOTES AND NOTES.

DETAIL
N.T.S.