

SHEET 1 OF 10 SHEETS

TRACT NO. 16155

A PORTION OF VESTING
TENTATIVE TRACT NO. 16025BLOCK 5057-5058 MODULES
60, 68, 69, 70, 78, 79
88, 89, 98 & 99DATE OF SURVEY:
JANUARY 1999IN UNINCORPORATED TERRITORY OF ORANGE COUNTY, CALIFORNIA
BEING A SUBDIVISION OF A PORTION OF PARCEL 1 OF LOT LINE ADJUSTMENT NO. LL 96-026
AS SHOWN ON EXHIBIT "B" ATTACHED TO THAT CERTAIN DOCUMENT RECORDED NOVEMBER 21,
1996 AS INSTRUMENT NO. 19960587414 OF OFFICIAL RECORDS, RECORDS OF ORANGE COUNTY,
CALIFORNIA.

OCTOBER 2000

JAMES F. GILLEN, L.S. 5557

HUITT-ZOLIARS

10 NUMBERED LOTS AND 40 LETTERED LOTS

100.789 ACRES

ACCEPTED AND FILED AT THE
REQUEST OF

FIRST AMERICAN TITLE INSURANCE CO.

DATE JANUARY 26, 2001

TIME 3:55 P.M. FEE \$25.00

INSTRUMENT NO. 20010047444

BOOK 812 PAGE 30-39 M/M

GARY L. GRANVILLE
COUNTY CLERK-RECORDERBY *[Signature]*
DEPUTY

OWNERSHIP CERTIFICATE:

WE, THE UNDERSIGNED, BEING ALL PARTIES HAVING ANY RECORD TITLE INTEREST IN THE LAND COVERED BY THIS MAP, DO HEREBY CONSENT TO THE PREPARATION AND RECORDATION OF SAID MAP, AS SHOWN WITHIN THE DISTINCTIVE BORDER LINE. WE ALSO HEREBY DEDICATE TO THE PUBLIC FOR STREET PURPOSES: ANTONIO PARKWAY, SIENNA PARKWAY, SELLAS ROAD NORTH, SNAPDRAGON STREET, SKLAR STREET, AVENDALE BOULEVARD, IRISH MOSS STREET, DELPHINIUM STREET, AMARYLLIS STREET, TRUMPET VINE STREET, GLOXINIA STREET, AND SWEET PEA STREET, AND BELLFLOWER STREET.

WE ALSO HEREBY DEDICATE TO THE COUNTY OF ORANGE:

- (1) THE EASEMENTS FOR SIDEWALK PURPOSES AS SHOWN ON SAID MAP.
- (2) THE EASEMENTS FOR STORM DRAIN PURPOSES AS SHOWN ON SAID MAP.

- (3) THE SCENIC PRESERVATION EASEMENTS AS SHOWN ON SAID MAP FOR THE PURPOSES AND SUBJECT TO THE SAME CONDITIONS AND LIMITATIONS AS SHOWN IN THAT CERTAIN EASEMENT RECORDED MARCH 10, 1989 AS DOCUMENT 89-125032, OF OFFICIAL RECORDS.

WE ALSO HEREBY RELEASE AND RELINQUISH TO THE COUNTY OF ORANGE ALL VEHICULAR ACCESS RIGHTS TO SIENNA PARKWAY AND ANTONIO PARKWAY, EXCEPT AT APPROVED ACCESS LOCATIONS.

PURSUANT TO SECTION 7050 OF THE GOVERNMENT CODE, WE HEREBY IRREVOCABLY OFFER TO DEDICATE TO THE COUNTY OF ORANGE LOT 4 IN FEE SIMPLE FOR LOCAL PARK PURPOSES, TOGETHER WITH THE RIGHT TO GRANT EASEMENTS FOR PUBLIC UTILITIES OR OTHER ESSENTIAL PURPOSES.

WE ALSO HEREBY DEDICATE TO THE SANTA MARGARITA WATER DISTRICT THE EASEMENTS FOR SEWER, WATER AND ACCESS PURPOSES AS SHOWN ON SAID MAP, WHICH EASEMENTS SHALL BE SUBJECT TO THE SAME TERMS AND CONDITIONS AS ARE SHOWN IN THAT CERTAIN EASEMENT RECORDED OCTOBER 6, 1980 IN BOOK 13776, PAGE 341, OF OFFICIAL RECORDS, COUNTY OF ORANGE. THE SANTA MARGARITA WATER DISTRICT SHALL RESTORE OTHER IMPROVEMENTS OR FACILITIES LOCATED WITHIN THE EASEMENT, IF IT HAS CONSENTED TO THE LOCATION OF SUCH IMPROVEMENTS OR FACILITIES TO THE EXTENT THAT THE EXERCISE OF ITS RIGHTS IN CONNECTION WITH THE EASEMENT IMPACTS OTHER IMPROVEMENTS OR FACILITIES LOCATED WITHIN THE EASEMENT, HOWEVER, IN NO EVENT SHALL SANTA MARGARITA WATER DISTRICT BE RESPONSIBLE FOR THE COST OF RELOCATING ITS FACILITIES IN THE EVENT OF CONFLICTS WITH SUCH OTHER IMPROVEMENTS OR FACILITIES.

DMB LADERA, L.L.C., A DELAWARE LIMITED LIABILITY COMPANY.

BY: RANCHO MISSION VIEJO, L.L.C., A DELAWARE LIMITED LIABILITY COMPANY,
AS AGENT AND/OR MANAGER.BY: *[Signature]*
PRINT NAME: MIC JOHNSON
PRINT TITLE: K.P. COMMUNITY DEV.BY: *[Signature]*
PRINT NAME: Stephen C. Schrank
PRINT TITLE: EXECUTIVE VICE PRESIDENTDMB CONSOLIDATED HOLDINGS, L.L.C., AN ARIZONA LIMITED LIABILITY COMPANY,
BENEFICIARY UNDER DEEDS OF TRUSTS RECORDED DECEMBER 10, 1996 AS INSTRUMENT
NO. 19960624030, AND RECORDED APRIL 20, 1999 AS INSTRUMENT NO. 19990288616,
BOTH OF OFFICIAL RECORDS.BY: DMB ASSOCIATES, INC., AN ARIZONA CORPORATION,
AS MANAGER.BY: *[Signature]*
PRINT NAME: TERRY D. RUSSELL
PRINT TITLE: VICE PRESIDENTBY: *[Signature]*
PRINT NAME: Timothy A. Kasper
PRINT TITLE: EXECUTIVE VICE PRESIDENT

CERTIFICATE OF ACCEPTANCE

THE UNDERSIGNED, BEING THE DULY APPOINTED AGENT OF THE SANTA MARGARITA WATER DISTRICT, A PUBLIC CORPORATION OF ORANGE COUNTY, CALIFORNIA, PURSUANT TO ITS RESOLUTION NO. 88-10-2, DOES HEREBY ACCEPT ON BEHALF OF SAID DISTRICT THE EASEMENTS FOR SEWER, WATER AND ACCESS PURPOSES, AS DEDICATED AND AS SHOWN ON THIS TRACT MAP, BY AND BETWEEN THE SANTA MARGARITA WATER DISTRICT AND DMB LADERA, L.L.C., AND DOES HEREBY CERTIFY THAT THE GRANTEE CONSENTS TO THE RECORDATION OF SAID TRACT.

[Signature]
DANIEL R. FERONS, CHIEF ENGINEER
SANTA MARGARITA WATER DISTRICT.

AUTOMATIC FIRE SPRINKLER NOTE:

ALL COMMERCIAL STRUCTURES GREATER THAN 6,000 SQUARE FEET; ALL MULTIFAMILY RESIDENTIAL STRUCTURES; ALL SINGLE-FAMILY STRUCTURES EXCEEDING 5,500 SQUARE FEET, AND ALL STRUCTURES EXCEEDING FIRE DEPARTMENT ACCESS REQUIREMENTS SHALL BE PROTECTED BY AN AUTOMATIC SPRINKLER SYSTEM.

SPECIAL FIRE PROTECTION NOTE:

PROPERTY IS IN A SPECIAL FIRE PROTECTION AREA AND MUST MEET ALL REQUIREMENTS FOR DEVELOPMENT WITHIN THE AREA.

PROPERTY IS TOTALLY EXCLUDED FROM A SPECIAL FIRE PROTECTION AREA.

HIGH FIRE HAZARD AREA NOTE:

THE LOTS SHOWN ON THIS MAP ARE IN A HIGH FIRE HAZARD AREA DUE TO WILD LAND EXPOSURE.

NOTE:

SEE SHEET 2 FOR NOTARY ACKNOWLEDGMENTS AND SIGNATURE OMISSIONS.

SURVEYOR'S STATEMENT:

I HEREBY STATE THAT THIS MAP CONSISTING OF 10 SHEETS, CORRECTLY REPRESENTS A TRUE AND COMPLETE SURVEY AS SHOWN MADE IN JANUARY, 1999; WAS MADE BY ME OR UNDER MY DIRECTION; THAT THE MONUMENTS ARE OF THE CHARACTER AND OCCUPY OR WILL OCCUPY THE POSITIONS INDICATED BY SAID MAP; AND THAT SAID MONUMENTS WILL BE SUFFICIENT TO ENABLE THE SURVEY TO BE RETRACED.



[Signature]
JAMES F. GILLEN
L.S. 5557
EXPIRATION DATE: 9/30/01

COUNTY SURVEYOR'S STATEMENT:

I HEREBY STATE THAT I HAVE EXAMINED THIS MAP AND HAVE FOUND IT TO BE SUBSTANTIALLY IN CONFORMANCE WITH THE TENTATIVE MAP AS FILED WITH, AMENDED AND APPROVED BY THE ORANGE COUNTY SUBDIVISION COMMITTEE; THAT ALL PROVISIONS OF THE SUBDIVISION MAP ACT AND COUNTY SUBDIVISION REGULATIONS HAVE BEEN COMPLIED WITH AND I AM SATISFIED SAID MAP IS TECHNICALLY CORRECT.

DATED THIS 17TH DAY OF JANUARY, 2001.

[Signature]
JOHN CANAS, COUNTY SURVEYOR
LS 4408 EXPIRATION DATE: 09-30-01

BY: MICHAEL K. SULLIVAN, DEPUTY
LS. 6254 EXPIRES 6-30-02



COUNTY TREASURER-TAX COLLECTOR'S CERTIFICATE:

STATE OF CALIFORNIA)
COUNTY OF ORANGE)

I HEREBY CERTIFY THAT ACCORDING TO THE RECORDS OF MY OFFICE THERE ARE NO LIENS AGAINST THE LAND COVERED BY THIS MAP OR ANY PART THEREOF FOR UNPAID STATE, COUNTY, MUNICIPAL OR LOCAL TAXES OR SPECIAL ASSESSMENTS COLLECTED AS TAXES, EXCEPT TAXES OR SPECIAL ASSESSMENTS COLLECTED AS TAXES NOT YET PAYABLE.

AND DO ALSO HEREBY CERTIFY TO THE RECORDER OF ORANGE COUNTY THAT THE PROVISIONS OF THE SUBDIVISION MAP ACT HAVE BEEN COMPLIED WITH REGARDING DEPOSITS TO SECURE THE PAYMENT OF TAXES OR SPECIAL ASSESSMENTS COLLECTED AS TAXES ON THE LAND COVERED BY THIS MAP.

DATED THIS 12 DAY OF JANUARY, 2001

JOHN M.W. MOORLACH
COUNTY TREASURER-TAX COLLECTOR

BY: *[Signature]*
DEPUTY TREASURER-TAX COLLECTOR

CLERK OF THE BOARD OF SUPERVISORS' CERTIFICATE:

STATE OF CALIFORNIA)
COUNTY OF ORANGE)

I HEREBY CERTIFY THAT THIS MAP WAS PRESENTED FOR APPROVAL TO THE BOARD OF SUPERVISORS OF ORANGE COUNTY AT A REGULAR MEETING THEREOF HELD ON THE 23RD DAY OF JANUARY, 2001, AND THAT THEREUPON SAID BOARD DID, BY AN ORDER DULY PASSED AND ENTERED, APPROVE SAID MAP AND DID ACCEPT ON BEHALF OF THE PUBLIC, SUBJECT TO IMPROVEMENTS: THE DEDICATION FOR STREET PURPOSES OF: ANTONIO PARKWAY, SIENNA PARKWAY, SELLAS ROAD NORTH, SNAPDRAGON STREET, SKLAR STREET, AVENDALE BOULEVARD, IRISH MOSS STREET, DELPHINIUM STREET, AMARYLLIS STREET, TRUMPET VINE STREET, GLOXINIA STREET, SWEET PEA STREET, AND BELLFLOWER STREET.


AND DID ALSO ACCEPT ON BEHALF OF THE COUNTY OF ORANGE:

1. THE EASEMENTS FOR SIDEWALK PURPOSES AS DEDICATED.
2. THE EASEMENTS FOR STORM DRAIN PURPOSES AS DEDICATED.
3. THE EASEMENTS FOR SCENIC PRESERVATION PURPOSES AS DEDICATED.
4. THE VEHICULAR ACCESS RIGHTS TO SIENNA PARKWAY AND ANTONIO PARKWAY AS RELEASED AND RELINQUISHED.

AND DID NOT ACCEPT THE IRREVOCABLE OFFER OF: LOT 4 FOR LOCAL PARK PURPOSES AS DEDICATED.
AND DID ALSO APPROVE SUBJECT MAP PURSUANT TO THE PROVISIONS OF SECTION 66436 (a)(3) OF SUBDIVISION MAP ACT.

DATED THIS 23RD DAY OF January, 2001.

[Signature]
DARLENE J. BLOOM
CLERK OF THE BOARD OF SUPERVISORS

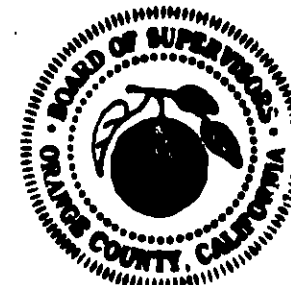

SHEET 2 OF 10 SHEETS

TRACT NO. 16155

A PORTION OF VESTING
TENTATIVE TRACT NO. 16025

IN UNINCORPORATED TERRITORY OF ORANGE COUNTY, CALIFORNIA

OCTOBER 2000

JAMES F. GILLEN, L.S. 5557

DATE OF SURVEY:
JANUARY 1999

HUITT-ZOLIARS

10 NUMBERED LOTS AND 40 LETTERED LOTS

100.789 ACRES

DMB LADERA, L.L.C.

STATE OF CALIFORNIA)
COUNTY OF ORANGE)

ON THIS 7th DAY OF December, 2000, BEFORE ME,
~~JEANNINE CARTA HANSON~~ A NOTARY PUBLIC IN AND FOR SAID STATE,
 PERSONALLY APPEARED PAUL JOHNSON AND
Stephen C. Schrank, PERSONALLY KNOWN TO ME OR PROVED TO ME
 ON THE BASIS OF SATISFACTORY EVIDENCE TO BE THE PERSONS WHOSE NAMES
 ARE SUBSCRIBED TO THE WITHIN INSTRUMENT AND ACKNOWLEDGED TO ME THAT
 THEY EXECUTED THE SAME IN THEIR AUTHORIZED CAPACITIES, AND THAT BY THEIR
 SIGNATURES ON THE INSTRUMENT THE PERSONS, OR THE ENTITY UPON BEHALF
 OF WHICH THE PERSONS ACTED, EXECUTED THE INSTRUMENT.

WITNESS MY HAND:

MY COMMISSION EXPIRES Feb. 25, 2003

Jeannine Carta Hanson MY PRINCIPAL PLACE OF BUSINESS
 NOTARY PUBLIC IN AND FOR SAID STATE IS IN ORANGE COUNTY.

JEANNINE CARTA HANSON
 PRINT NAME

DMB CONSOLIDATED HOLDINGS, L.L.C.

STATE OF CALIFORNIA)
COUNTY OF ORANGE)

ON THIS 7th DAY OF December, 2000, BEFORE ME,
~~JEANNINE CARTA HANSON~~ A NOTARY PUBLIC IN AND FOR SAID STATE,
 PERSONALLY APPEARED TERRY D. RANDALL PERSONALLY KNOWN TO ME
 OR PROVED TO ME ON THE BASIS OF SATISFACTORY EVIDENCE TO BE THE
 PERSON WHOSE NAME IS SUBSCRIBED TO THE WITHIN INSTRUMENT AND ACKNOWLEDGED
 TO ME THAT HE EXECUTED THE SAME IN HIS AUTHORIZED CAPACITY, AND THAT
 BY HIS SIGNATURE ON THE INSTRUMENT THE PERSON, OR THE ENTITY UPON BEHALF
 OF WHICH THE PERSON ACTED, EXECUTED THE INSTRUMENT, AS BENEFICIARY.

WITNESS MY HAND:

MY COMMISSION EXPIRES Feb. 25, 2003

Jeannine Carta Hanson MY PRINCIPAL PLACE OF BUSINESS
 NOTARY PUBLIC IN AND FOR SAID STATE IS IN ORANGE COUNTY.

JEANNINE CARTA HANSON
 PRINT NAME

SANTA MARGARITA WATER DISTRICT

STATE OF CALIFORNIA)
COUNTY OF ORANGE)

ON THIS 22nd DAY OF December, 2000, BEFORE ME,
Lupe Martinez, A NOTARY PUBLIC IN AND FOR SAID STATE,
 PERSONALLY APPEARED DANIEL R. FERONS PERSONALLY KNOWN TO ME
 OR PROVED TO ME ON THE BASIS OF SATISFACTORY EVIDENCE TO BE THE
 PERSON WHOSE NAME IS SUBSCRIBED TO THE WITHIN INSTRUMENT AND ACKNOWLEDGED
 TO ME THAT HE EXECUTED THE SAME IN HIS AUTHORIZED CAPACITY, AND THAT
 BY HIS SIGNATURE ON THE INSTRUMENT THE PERSON, OR THE ENTITY UPON BEHALF
 OF WHICH THE PERSON ACTED, EXECUTED THE INSTRUMENT.

WITNESS MY HAND:

MY COMMISSION EXPIRES 8-13-2002

Lupe Martinez MY PRINCIPAL PLACE OF BUSINESS
 NOTARY PUBLIC IN AND FOR SAID STATE IS IN Orange COUNTY.

Lupe Martinez
 PRINT NAME

SIGNATURE OMISSIONS:

IN ACCORDANCE WITH THE PROVISIONS OF SECTION 66436(a) (3) OF THE SUBDIVISION
 MAP ACT, THE FOLLOWING SIGNATURE HAS BEEN OMITTED:

1. LADERA DEVELOPMENT COMPANY, L.L.C., HOLDER OF OIL, GAS, MINERAL, AND WATER RIGHTS
 RECORDED DECEMBER 10, 1996 AS INSTRUMENT NO. 19960624029 OF OFFICIAL RECORDS.
2. ~~SAN DIEGO GAS & ELECTRIC COMPANY, HOLDER OF A UTILITY EASEMENT RECORDED FEBRUARY 10,
 1993 AS INSTRUMENT NO. 93-001210 OF OFFICIAL RECORDS.~~

EASEMENT NOTES:

- (A) INDICATES EASEMENT FOR SCENIC PRESERVATION PURPOSES DEDICATED TO THE COUNTY OF ORANGE.
- (B) INDICATES SIDEWALK EASEMENT DEDICATED TO THE COUNTY OF ORANGE.
- (C) INDICATES A UTILITY EASEMENT TO SAN DIEGO GAS AND ELECTRIC COMPANY PER INSTRUMENT
 NO. 20010014945, O.R.
- (D) INDICATES EASEMENT FOR SEWER, WATER AND ACCESS PURPOSES DEDICATED TO THE SANTA MARGARITA
 WATER DISTRICT.
- (E) INDICATES STORM DRAIN EASEMENT DEDICATED TO THE COUNTY OF ORANGE.

DMB CONSOLIDATED HOLDINGS, L.L.C.

STATE OF Arizona)
COUNTY OF Maricopa)


ON THIS 26th DAY OF December, 2000, BEFORE ME,
Carolynn Sneddon A NOTARY PUBLIC IN AND FOR SAID STATE,
 PERSONALLY APPEARED Timothy A. Kachr PERSONALLY
 KNOWN TO ME OR PROVED TO ME ON THE BASIS OF SATISFACTORY
 EVIDENCE TO BE THE PERSON WHOSE NAME IS SUBSCRIBED TO THE WITHIN
 INSTRUMENT AND ACKNOWLEDGED TO ME THAT HE EXECUTED THE SAME
 IN HIS AUTHORIZED CAPACITY, AND THAT BY HIS SIGNATURE ON THE
 INSTRUMENT THE PERSON, OR THE ENTITY UPON BEHALF OF WHICH THE
 PERSON ACTED, EXECUTED THE INSTRUMENT, AS BENEFICIARY.

WITNESS MY HAND:

MY COMMISSION EXPIRES 07-14-02

Carolynn Sneddon MY PRINCIPAL PLACE OF BUSINESS
 NOTARY PUBLIC IN AND FOR SAID STATE IS IN Maricopa COUNTY.

Carolynn Sneddon
 PRINT NAME

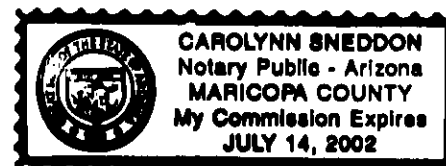

TRACT NO. 16155

IN UNINCORPORATED TERRITORY OF ORANGE COUNTY, CALIFORNIA

OCTOBER 2000

JAMES F. GILLEN, L.S. 5557


HUITT-ZOLIARS

10 NUMBERED LOTS AND 40 LETTERED LOTS

100.789 ACRES

A PORTION VESTING TENTATIVE
TRACT NO. 16025

DATE OF SURVEY:
JANUARY 1999

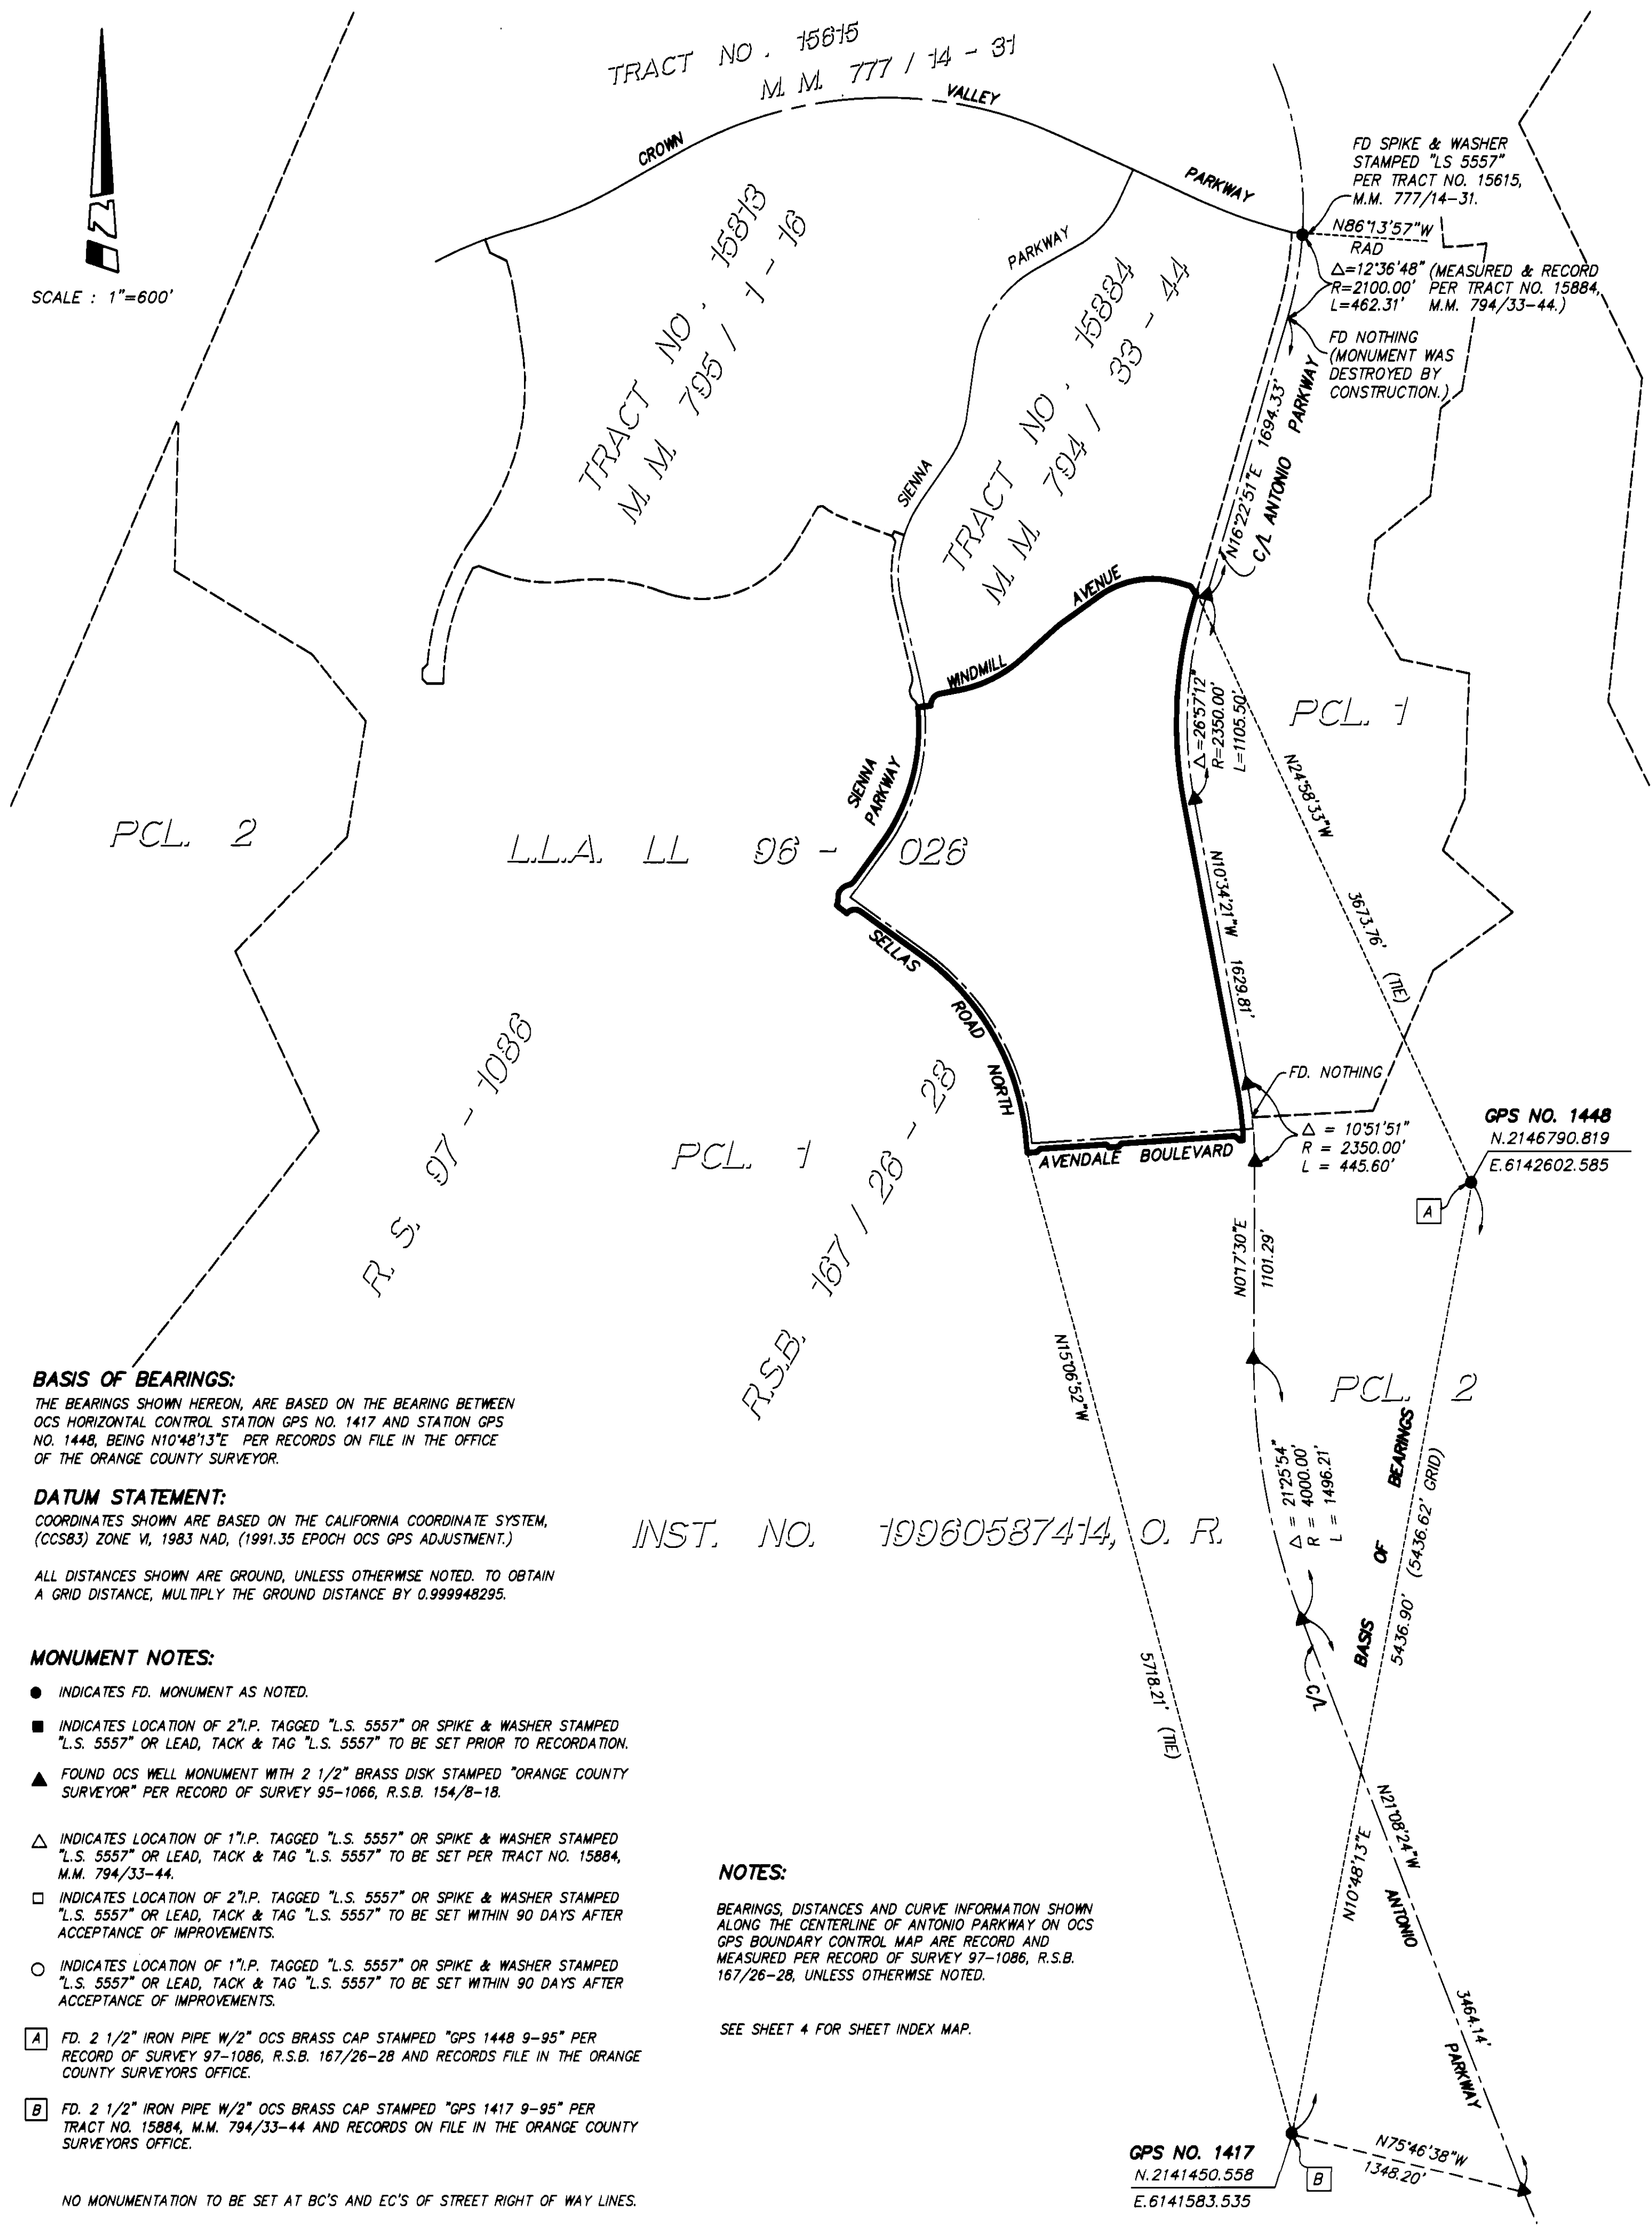

BASIS OF BEARINGS:
THE BEARINGS SHOWN HEREON, ARE BASED ON THE BEARING BETWEEN
OCS HORIZONTAL CONTROL STATION GPS NO. 1417 AND STATION GPS
NO. 1448, BEING N10°48'13"E PER RECORDS ON FILE IN THE OFFICE
OF THE ORANGE COUNTY SURVEYOR.

DATUM STATEMENT:
COORDINATES SHOWN ARE BASED ON THE CALIFORNIA COORDINATE SYSTEM,
(CCS83) ZONE VI, 1983 NAD, (1991.35 EPOCH OCS GPS ADJUSTMENT.)

ALL DISTANCES SHOWN ARE GROUND, UNLESS OTHERWISE NOTED. TO OBTAIN
A GRID DISTANCE, MULTIPLY THE GROUND DISTANCE BY 0.999948295.

MONUMENT NOTES:

- INDICATES FD. MONUMENT AS NOTED.
- INDICATES LOCATION OF 2" I.P. TAGGED "L.S. 5557" OR SPIKE & WASHER STAMPED "L.S. 5557" OR LEAD, TACK & TAG "L.S. 5557" TO BE SET PRIOR TO RECORDATION.
- ▲ FOUND OCS WELL MONUMENT WITH 2 1/2" BRASS DISK STAMPED "ORANGE COUNTY SURVEYOR" PER RECORD OF SURVEY 95-1066, R.S.B. 154/B-18.
- △ INDICATES LOCATION OF 1" I.P. TAGGED "L.S. 5557" OR SPIKE & WASHER STAMPED "L.S. 5557" OR LEAD, TACK & TAG "L.S. 5557" TO BE SET PER TRACT NO. 15884, M.M. 794/33-44.
- INDICATES LOCATION OF 2" I.P. TAGGED "L.S. 5557" OR SPIKE & WASHER STAMPED "L.S. 5557" OR LEAD, TACK & TAG "L.S. 5557" TO BE SET WITHIN 90 DAYS AFTER ACCEPTANCE OF IMPROVEMENTS.
- INDICATES LOCATION OF 1" I.P. TAGGED "L.S. 5557" OR SPIKE & WASHER STAMPED "L.S. 5557" OR LEAD, TACK & TAG "L.S. 5557" TO BE SET WITHIN 90 DAYS AFTER ACCEPTANCE OF IMPROVEMENTS.
- [A] FD. 2 1/2" IRON PIPE W/2" OCS BRASS CAP STAMPED "GPS 1448 9-95" PER RECORD OF SURVEY 97-1086, R.S.B. 167/26-28 AND RECORDS FILE IN THE ORANGE COUNTY SURVEYORS OFFICE.
- [B] FD. 2 1/2" IRON PIPE W/2" OCS BRASS CAP STAMPED "GPS 1417 9-95" PER TRACT NO. 15884, M.M. 794/33-44 AND RECORDS ON FILE IN THE ORANGE COUNTY SURVEYORS OFFICE.

NO MONUMENTATION TO BE SET AT BC'S AND EC'S OF STREET RIGHT OF WAY LINES.

NOTES:

BEARINGS, DISTANCES AND CURVE INFORMATION SHOWN
ALONG THE CENTERLINE OF ANTONIO PARKWAY ON OCS
GPS BOUNDARY CONTROL MAP ARE RECORD AND
MEASURED PER RECORD OF SURVEY 97-1086, R.S.B.
167/26-28, UNLESS OTHERWISE NOTED.

SEE SHEET 4 FOR SHEET INDEX MAP.



OCS GPS BOUNDARY CONTROL MAP

SHEET 4 OF 10 SHEETS

A PORTION OF VESTING TENTATIVE
TRACT NO. 18025

DATE OF SURVEY:
JANUARY 1999

TRACT NO. 16155
IN UNINCORPORATED TERRITORY OF ORANGE COUNTY, CALIFORNIA
OCTOBER 2000 JAMES F. GILLEN, L.S. 5557
HUITT-ZOLIARS
10 NUMBERED LOTS AND 40 LETTERED LOTS 100.789 ACRES

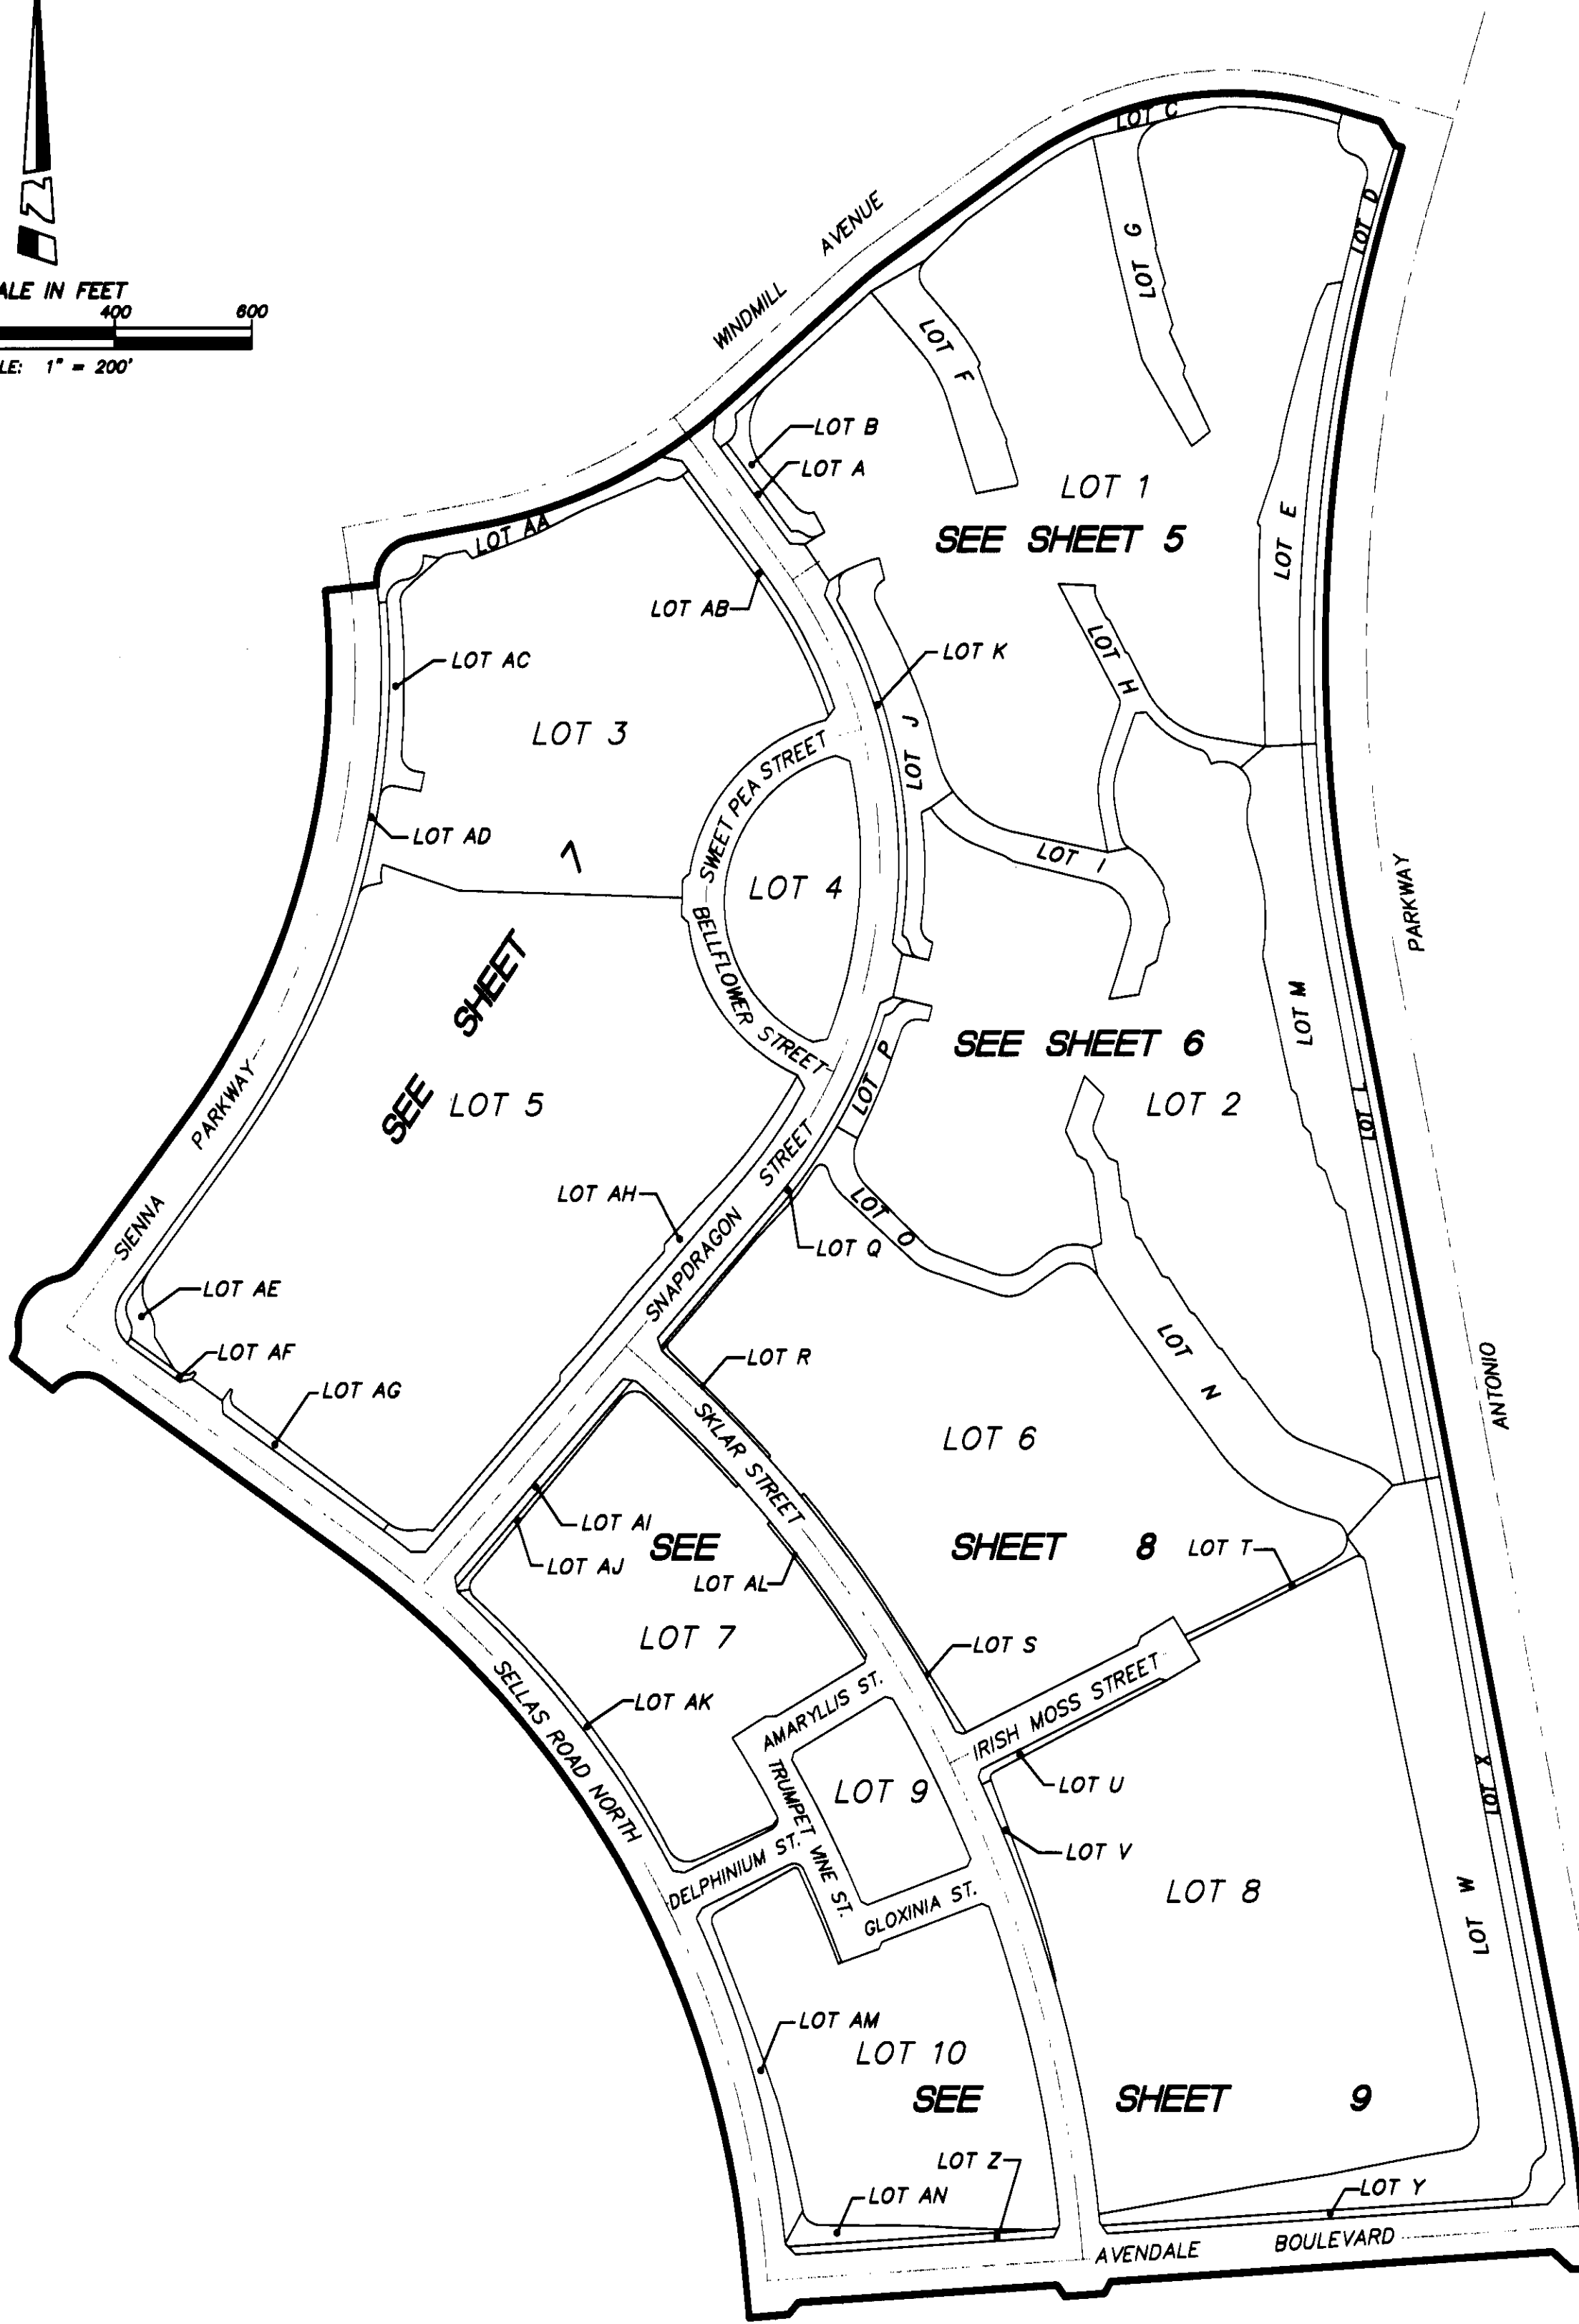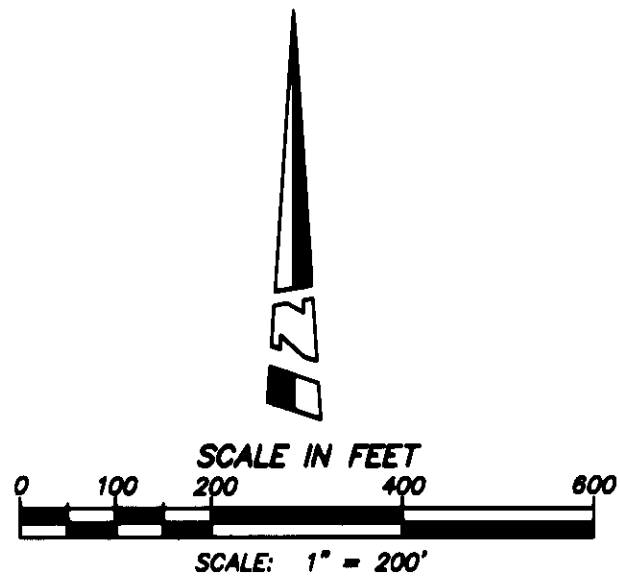

SHEET INDEX MAP

SHEET 5 OF 10 SHEETS

A PORTION OF VESTING
TENTATIVE TRACT NO. 16025DATE OF SURVEY:
JANUARY 1999

TRACT NO. 16155

IN UNINCORPORATED TERRITORY OF ORANGE COUNTY, CALIFORNIA


OCTOBER 2000

JAMES F. GILLEN, L.S. 5557

HUITT-ZOLLARS

10 NUMBERED LOTS AND 40 LETTERED LOTS

100.789 ACRES

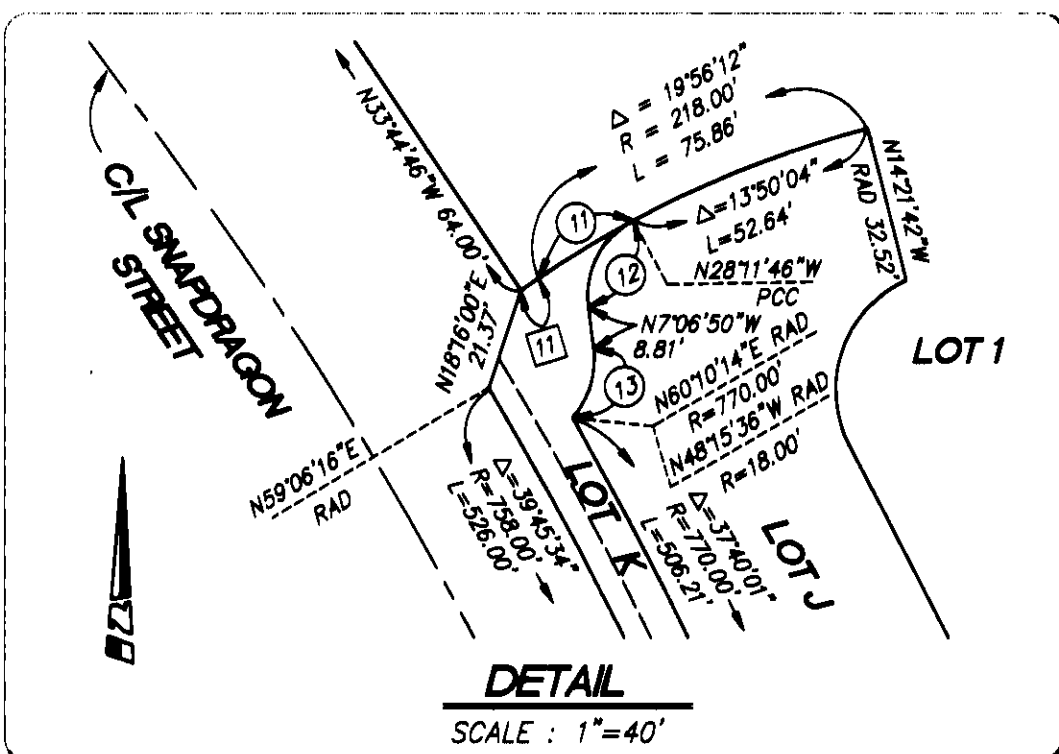


CURVE DATA (THIS SHEET ONLY)

- ① $\Delta = 79^{\circ}14'38''$ R = 15.00' L = 20.75'
- ② $\Delta = 79^{\circ}44'21''$ R = 30.00' L = 41.75'
- ③ $\Delta = 90^{\circ}00'00''$ R = 30.00' L = 47.12'
- ④ $\Delta = 04^{\circ}47'18''$ R = 80.00' L = 6.69'
- ⑤ $\Delta = 61^{\circ}19'21''$ R = 42.00' L = 44.95'
- ⑥ $\Delta = 52^{\circ}27'54''$ R = 18.00' L = 16.48'
- ⑦ $\Delta = 65^{\circ}20'57''$ R = 25.00' L = 28.51'
- ⑧ $\Delta = 00^{\circ}54'49''$ R = 496.00' L = 7.91'
- ⑨ $\Delta = 06^{\circ}01'00''$ R = 516.00' L = 54.19'
- ⑩ $\Delta = 87^{\circ}27'35''$ R = 30.00' L = 45.79'
- ⑪ $\Delta = 06^{\circ}06'08''$ R = 218.00' L = 23.22'
- ⑫ $\Delta = 68^{\circ}55'04''$ R = 18.00' L = 21.65'
- ⑬ $\Delta = 48^{\circ}51'14''$ R = 18.00' L = 15.35'
- ⑭ $\Delta = 53^{\circ}34'48''$ R = 789.00' L = 76.61'

COURSE DATA (THIS SHEET ONLY)

- 1 N73°22'13"W 4.27'
- 2 N16°23'00"E 20.02'
- 3 N73°37'00"W 4.27'
- 4 N16°23'00"E 7.75'
- 5 N16°22'51"E 22.91'
- 6 N73°37'09"W 12.00'
- 7 N22°17'35"W RAD 11.08'
- 8 N15°14'31"E PRC
- 9 N84°53'23"E 16.00'
- 10 N55°42'06"E 3.86'
- 11 N55°42'06"E 4.47'
- 12 N27°32'18"W 43.04'
- 13 N16°22'51"E 52.77'
- 14 N16°23'00"E RAD
- 15 N16°52'34"E RAD

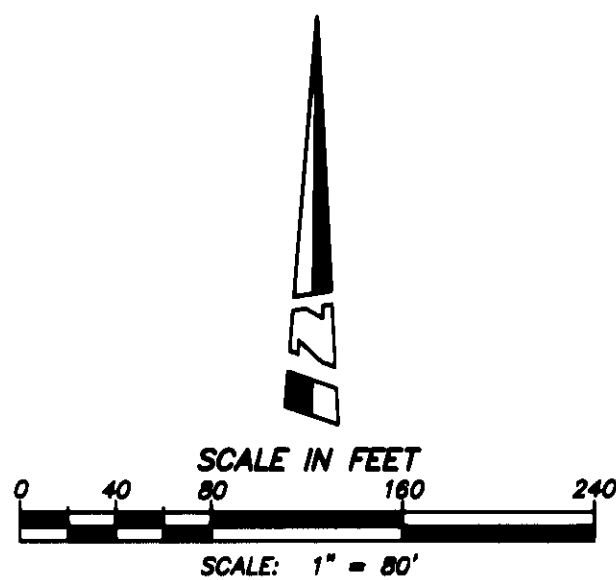


NOTES:

SEE SHEET 2 FOR EASEMENT NOTES.

SEE SHEET 3 FOR BASIS OF BEARINGS, DATUM STATEMENT,
MONUMENT NOTES AND OCS GPS BOUNDARY CONTROL MAP.

SEE SHEET 4 FOR SHEET INDEX MAP.

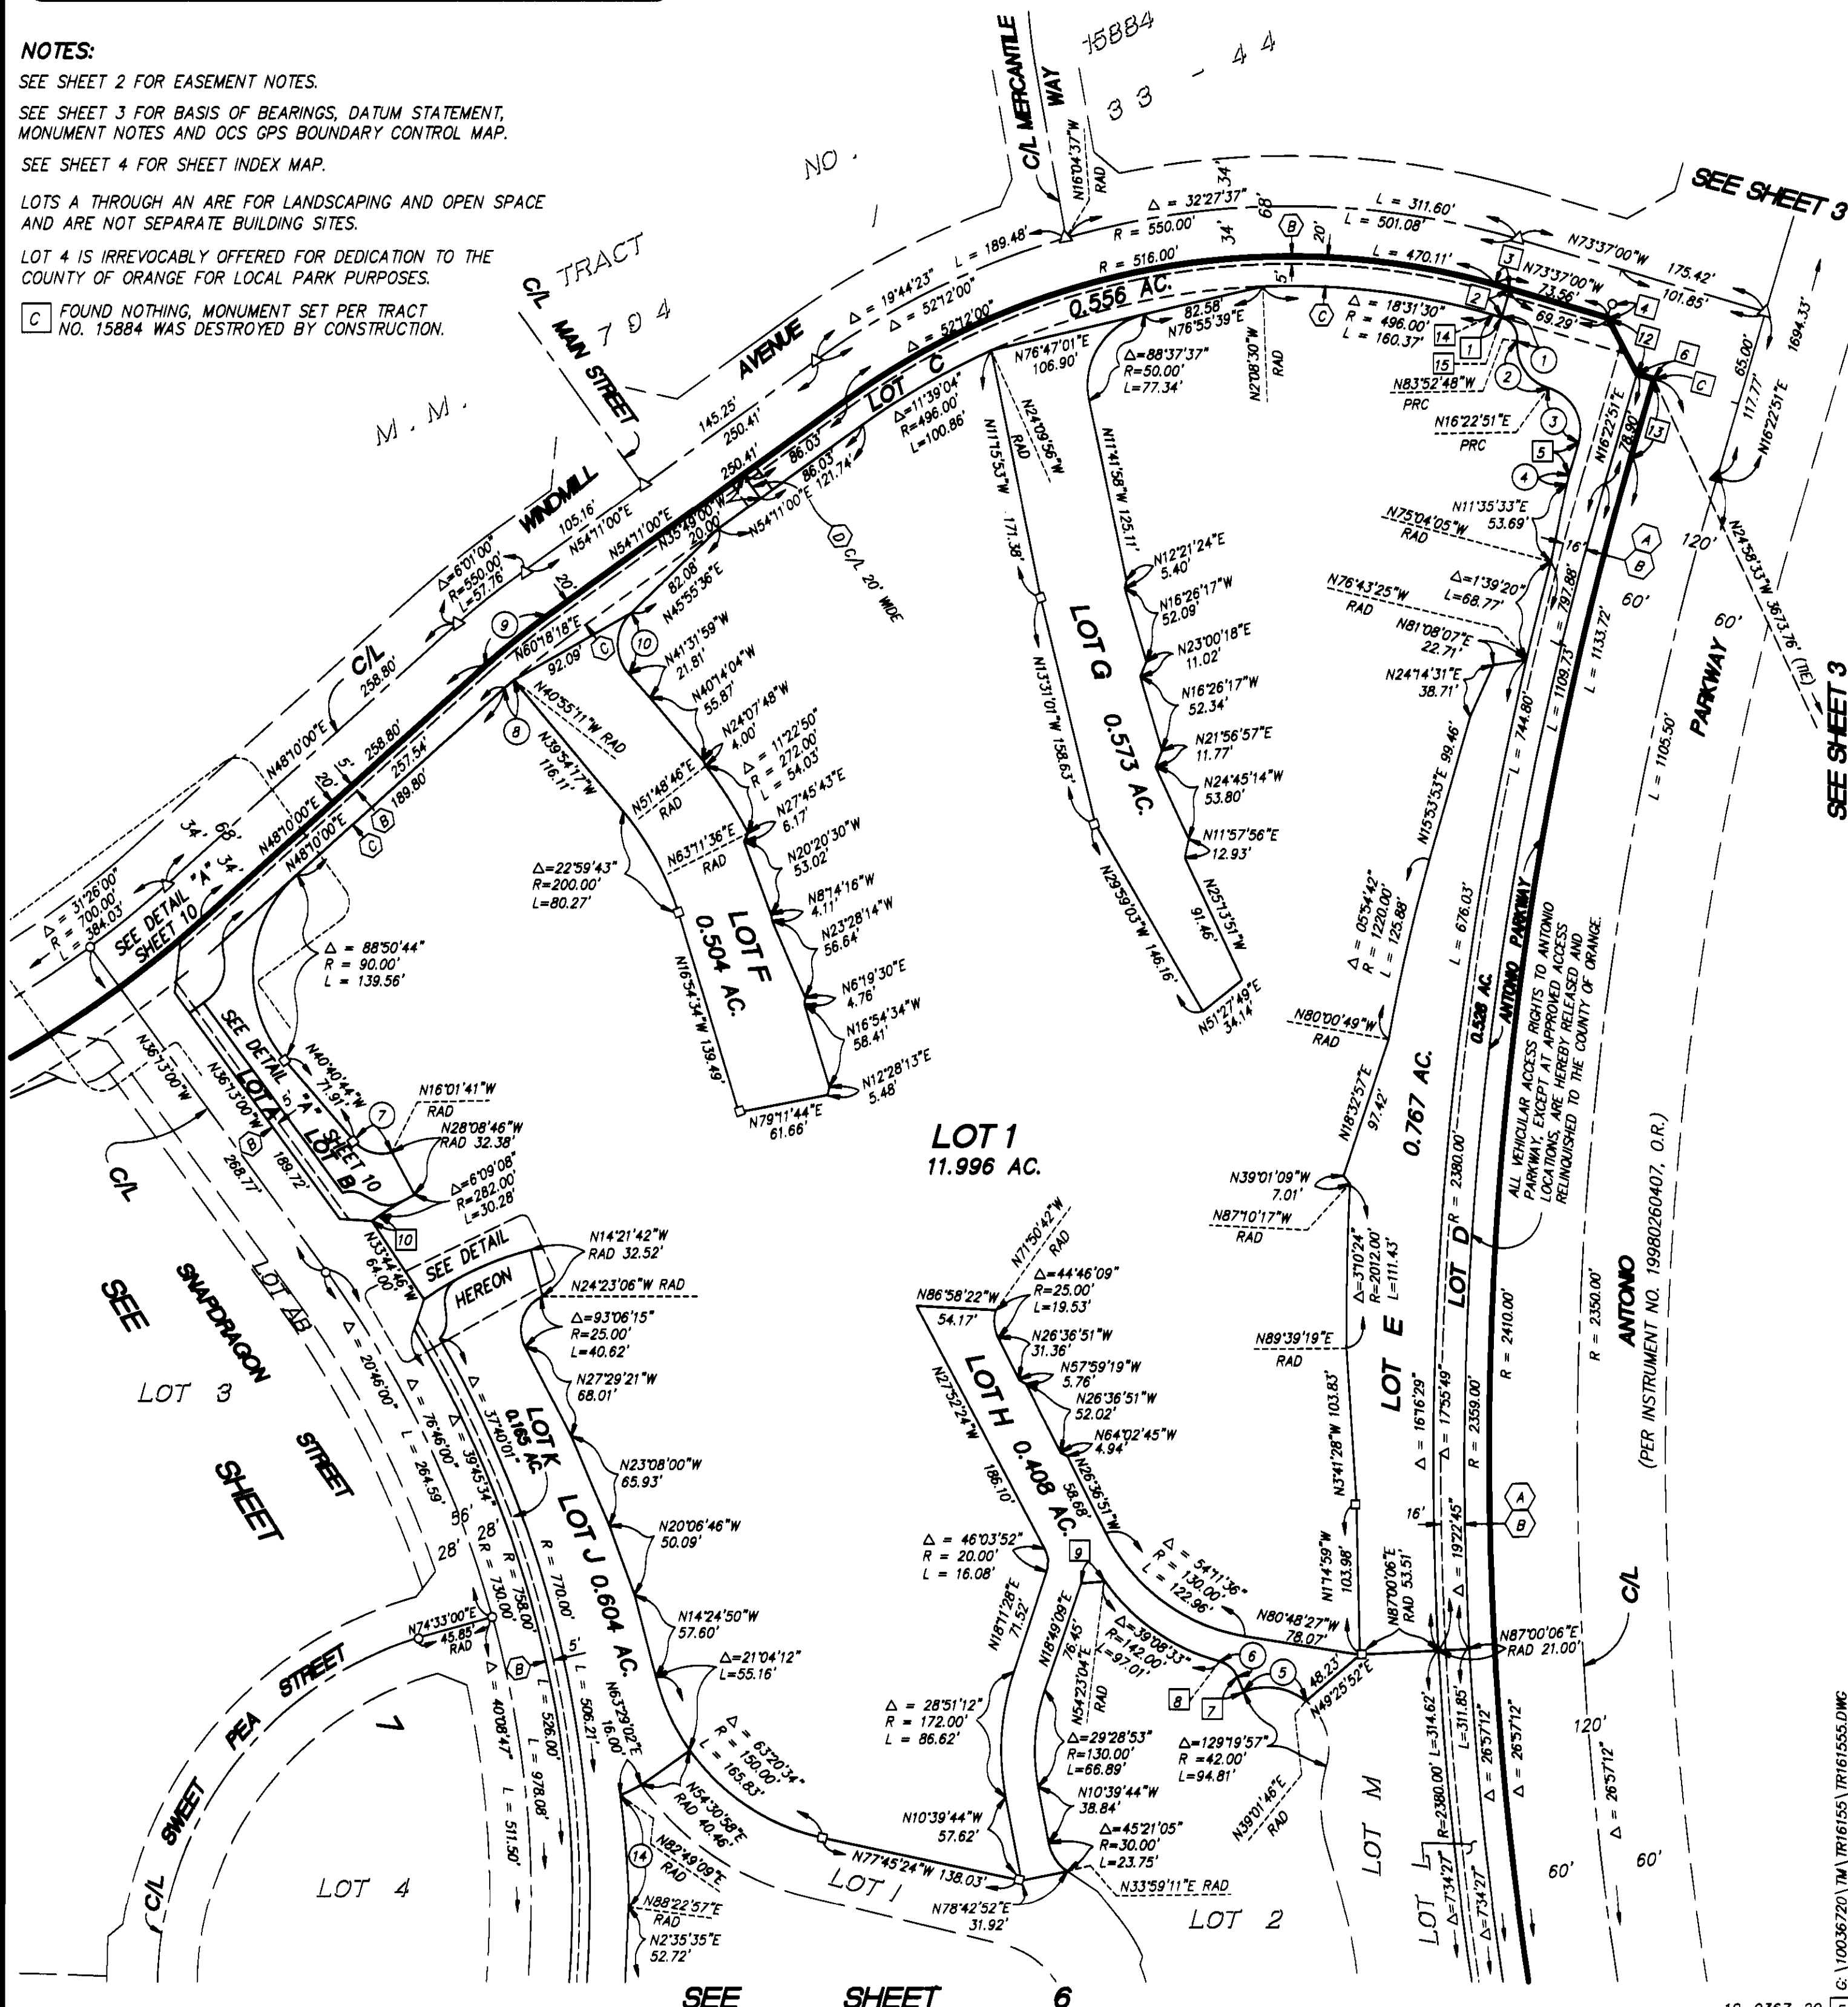LOTS A THROUGH AN ARE FOR LANDSCAPING AND OPEN SPACE
AND ARE NOT SEPARATE BUILDING SITES.LOT 4 IS IRREVOCABLY OFFERED FOR DEDICATION TO THE
COUNTY OF ORANGE FOR LOCAL PARK PURPOSES.C FOUND NOTHING, MONUMENT SET PER TRACT
NO. 15884 WAS DESTROYED BY CONSTRUCTION.

SEE SHEET 3

SHEET 6 OF 10 SHEETS

TRACT NO. 16155

IN UNINCORPORATED TERRITORY OF ORANGE COUNTY, CALIFORNIA

OCTOBER 2000

JAMES F. GILLEN, L.S. 5557

HUITT-ZOLLARS


10 NUMBERED LOTS AND 40 LETTERED LOTS

100.789 ACRES

A PORTION OF VESTING
TENTATIVE TRACT NO. 16025

DATE OF SURVEY:
JANUARY 1999

SEE SHEET 5

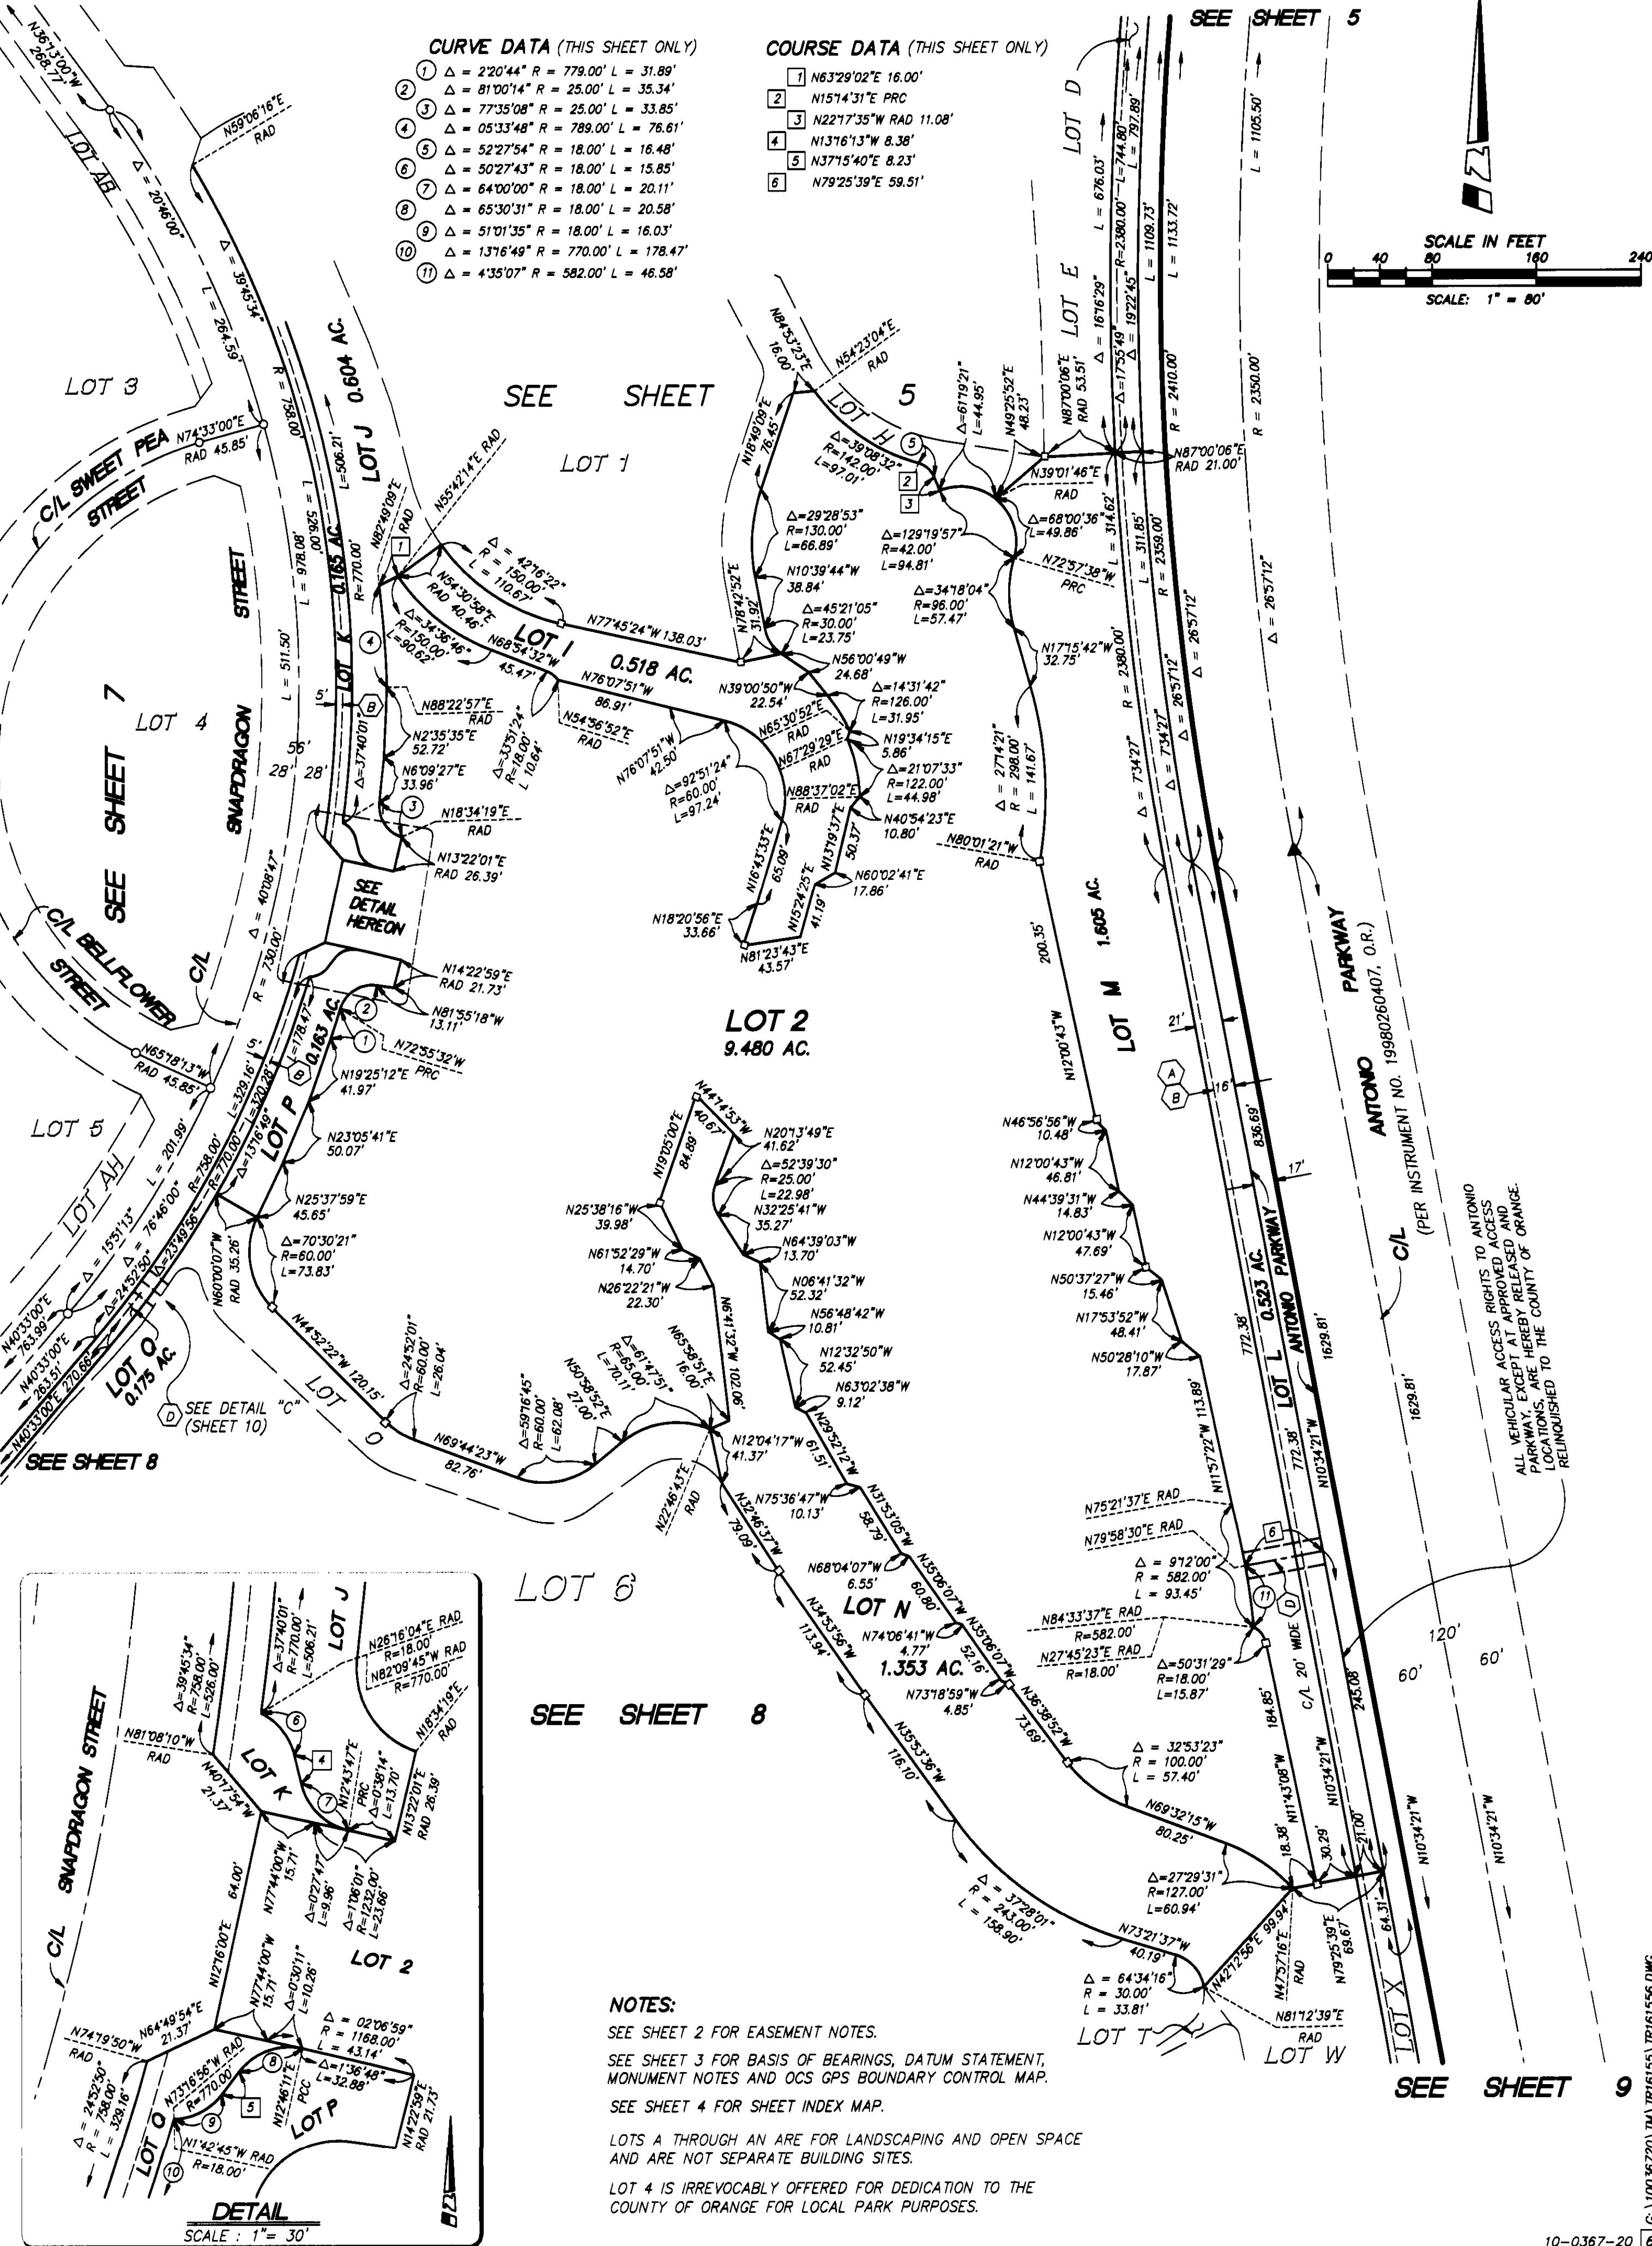

SHEET 7 OF 10 SHEETS


TRACT NO. 16155

IN UNINCORPORATED TERRITORY OF ORANGE COUNTY, CALIFORNIA
OCTOBER 2000 JAMES F. GILLEN, L.S. 5557

HUITT-ZOLIARS

10 NUMBERED LOTS AND 40 LETTERED LOTS

100.789 ACRES

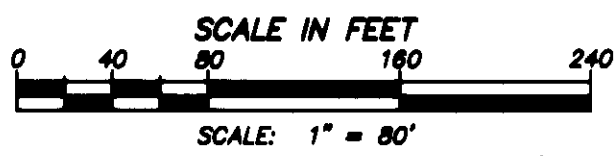A PORTION OF VESTING
TENTATIVE TRACT NO. 16025DATE OF SURVEY:
JANUARY 1999

NOTES:

SEE SHEET 2 FOR EASEMENT NOTES.

SEE SHEET 3 FOR BASIS OF BEARINGS, DATUM STATEMENT,
MONUMENT NOTES AND OCS GPS BOUNDARY CONTROL MAP.

SEE SHEET 4 FOR SHEET INDEX MAP.

LOTS A THROUGH AN ARE FOR LANDSCAPING AND OPEN SPACE
AND ARE NOT SEPARATE BUILDING SITES.LOT 4 IS IRREVOCABLY OFFERED FOR DEDICATION TO THE
COUNTY OF ORANGE FOR LOCAL PARK PURPOSES.

CURVE DATA (THIS SHEET ONLY)

- 1 $\Delta = 85^{\circ}35'43''$ R = 62.00' L = 92.62'
- 2 $\Delta = 01^{\circ}14'27''$ R = 1188.00' L = 25.73'
- 3 $\Delta = 88^{\circ}39'42''$ R = 30.00' L = 46.42'
- 4 $\Delta = 94^{\circ}31'23''$ R = 30.00' L = 49.49'
- 5 $\Delta = 30^{\circ}16'42''$ R = 25.00' L = 13.21'
- 6 $\Delta = 08^{\circ}17'20''$ R = 734.00' L = 106.19'
- 7 $\Delta = 12^{\circ}35'24''$ R = 702.00' L = 154.26'
- 8 $\Delta = 28^{\circ}04'20''$ R = 50.00' L = 24.50'
- 9 $\Delta = 48^{\circ}11'17''$ R = 50.00' L = 42.05'
- 10 $\Delta = 1^{\circ}56'13''$ R = 1481.00' L = 50.07'
- 11 $\Delta = 04^{\circ}33'00''$ R = 1450.00' L = 115.15'
- 12 $\Delta = 02^{\circ}49'30''$ R = 1481.00' L = 73.02'
- 13 $\Delta = 00^{\circ}53'17''$ R = 1481.00' L = 22.95'
- 14 $\Delta = 90^{\circ}00'00''$ R = 56.00' L = 87.96'
- 15 $\Delta = 70^{\circ}43'52''$ R = 50.00' L = 61.72'
- 16 $\Delta = 2^{\circ}49'53''$ R = 1130.00' L = 55.84'
- 17 $\Delta = 60^{\circ}46'21''$ R = 18.00' L = 19.09'
- 18 $\Delta = 85^{\circ}26'28''$ R = 18.00' L = 26.84'
- 19 $\Delta = 78^{\circ}25'51''$ R = 18.00' L = 24.64'
- 20 $\Delta = 44^{\circ}16'19''$ R = 50.00' L = 38.63'
- 21 $\Delta = 4^{\circ}50'24''$ R = 1188.00' L = 100.36'

COURSE DATA (THIS SHEET ONLY)

- 1 N85°14'44"E RAD 12.00'
- 2 N06°05'34"W PRC
- 3 N79°51'32"W 24.70'
- 4 N71°17'10"E RAD 7.75'
- 5 N37°09'02"E 14.56'
- 6 N37°09'02"E 21.35'
- 7 N37°09'02"E 6.79'
- 8 N74°33'00"E RAD 45.85'
- 9 N68°05'33"W 21.37'
- 10 N77°20'19"E 21.37'
- 11 N65°18'13"W RAD 45.85'
- 12 N27°54'15"W 21.35'
- 13 N89°37'01"W 21.69'
- 14 N38°49'30"E RAD 10.75'
- 15 N76°36'05"E 18.44'
- 16 N79°23'03"E RAD
- 17 N10°24'00"W RAD 7.75'
- 18 N49°27'00"W 7.75'
- 19 N84°00'17"E PRC 7.75'
- 20 N15°30'07"W RAD 12.75'
- 21 N15°31'16"W RAD 12.75'
- 22 N77°48'50"E RAD 7.75'
- 23 N24°46'03"E RAD 12.75'
- 24 N24°44'54"E RAD 12.75'
- 25 N68°34'03"W RAD 7.75'
- 26 N82°02'24"W RAD 7.75'
- 27 N38°22'26"W 18.13'
- 28 N31°25'41"W 58.04'
- 29 N54°00'00"W 5.96'
- 30 N89°54'52"W RAD 32.87'
- 31 N84°51'23"W 12.15'
- 32 N75°58'27"W RAD
- 33 N75°53'01"W RAD
- 34 N54°00'00"W 80.28'

PORTION OF PCL. 1

L L A LL 98-026, INST. NO. 19980587414, O.R.

ALL VEHICULAR ACCESS RIGHTS TO SIENNA
PARKWAY, EXCEPT AT APPROVED ACCESS
LOCATIONS, ARE HEREBY RELEASED AND
RELINQUISHED TO THE COUNTY OF ORANGE.

SEE DETAIL "B"

SHEET 10

LOT AE

0.068 AC.

LOT 5
12.208 AC.

LOT AH

0.376 AC.

LOT AG

0.108 AC.

LOT AF

0.025 AC.

PORTION OF PCL. 1

L L A LL 98-026, INST. NO. 19980587414, O.R.

10-0367-20 7

812

36

SHEET 8 OF 10 SHEETS

TRACT NO. 16155

IN UNINCORPORATED TERRITORY OF ORANGE COUNTY, CALIFORNIA


OCTOBER 2000

JAMES F. GILLEN, L.S. 5557

HUITT-ZOLLARS

10 NUMBERED LOTS AND 40 LETTERED LOTS

100.789 ACRES

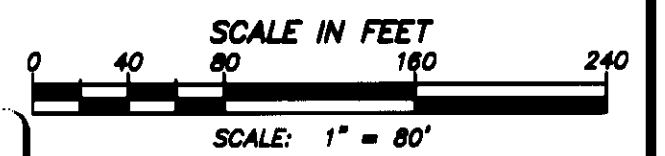A PORTION OF VESTING
TENTATIVE TRACT NO. 16025DATE OF SURVEY:
JANUARY 1999

COURSE DATA (THIS SHEET ONLY)

- 1 N76°35'59"E PRC
- 2 N87°27'30"W 16.05'
- 3 N13°23'00"E 7.38'
- 4 N13°23'00"E 11.42'
- 5 N13°23'00"E 4.04'
- 6 N88°09'37"E 16.04'
- 7 N81°43'27"W 16.99'
- 8 N41°52'18"E RAD 14.75'
- 9 N41°55'36"E RAD
- 10 N42°16'30"E RAD 10.75'
- 11 N49°27'00"W 7.75'
- 12 N62°14'11"E RAD 10.75'
- 13 N26°16'08"W 14.75'
- 14 N31°03'05"W 16.75'
- 15 N57°49'05"E RAD 16.75'
- 16 N26°45'32"W 16.75'
- 17 N62°39'09"E RAD 10.75'
- 18 N65°18'13"W RAD 45.85'

CURVE DATA (THIS SHEET ONLY)

- ① $\Delta = 132°13'00"$ R = 10.00' L = 23.08'
- ② $\Delta = 10°33'07"$ R = 770.00' L = 141.81'
- ③ $\Delta = 33°36'30"$ R = 75.00' L = 43.99'
- ④ $\Delta = 129°08'31"$ R = 30.00' L = 67.62'
- ⑤ $\Delta = 64°34'15"$ R = 30.00' L = 33.81'
- ⑥ $\Delta = 2°09'40"$ R = 1883.00' L = 71.02'
- ⑦ $\Delta = 02°32'48"$ R = 1337.00' L = 59.43'
- ⑧ $\Delta = 03°13'59"$ R = 1481.00' L = 83.57'

NOTES:






SEE SHEET 2 FOR EASEMENT NOTES.

SEE SHEET 3 FOR BASIS OF BEARINGS, DATUM STATEMENT,
MONUMENT NOTES AND OCS GPS BOUNDARY CONTROL MAP.

SEE SHEET 4 FOR SHEET INDEX MAP.

LOTS A THROUGH AN ARE FOR LANDSCAPING AND OPEN SPACE
AND ARE NOT SEPARATE BUILDING SITES.LOT 4 IS IRREVOCABLY OFFERED FOR DEDICATION TO THE
COUNTY OF ORANGE FOR LOCAL PARK PURPOSES.

PORTION OF PCL 1
L.L.A. LL 96 - 026
INST. NO. 19960587414, O.R.

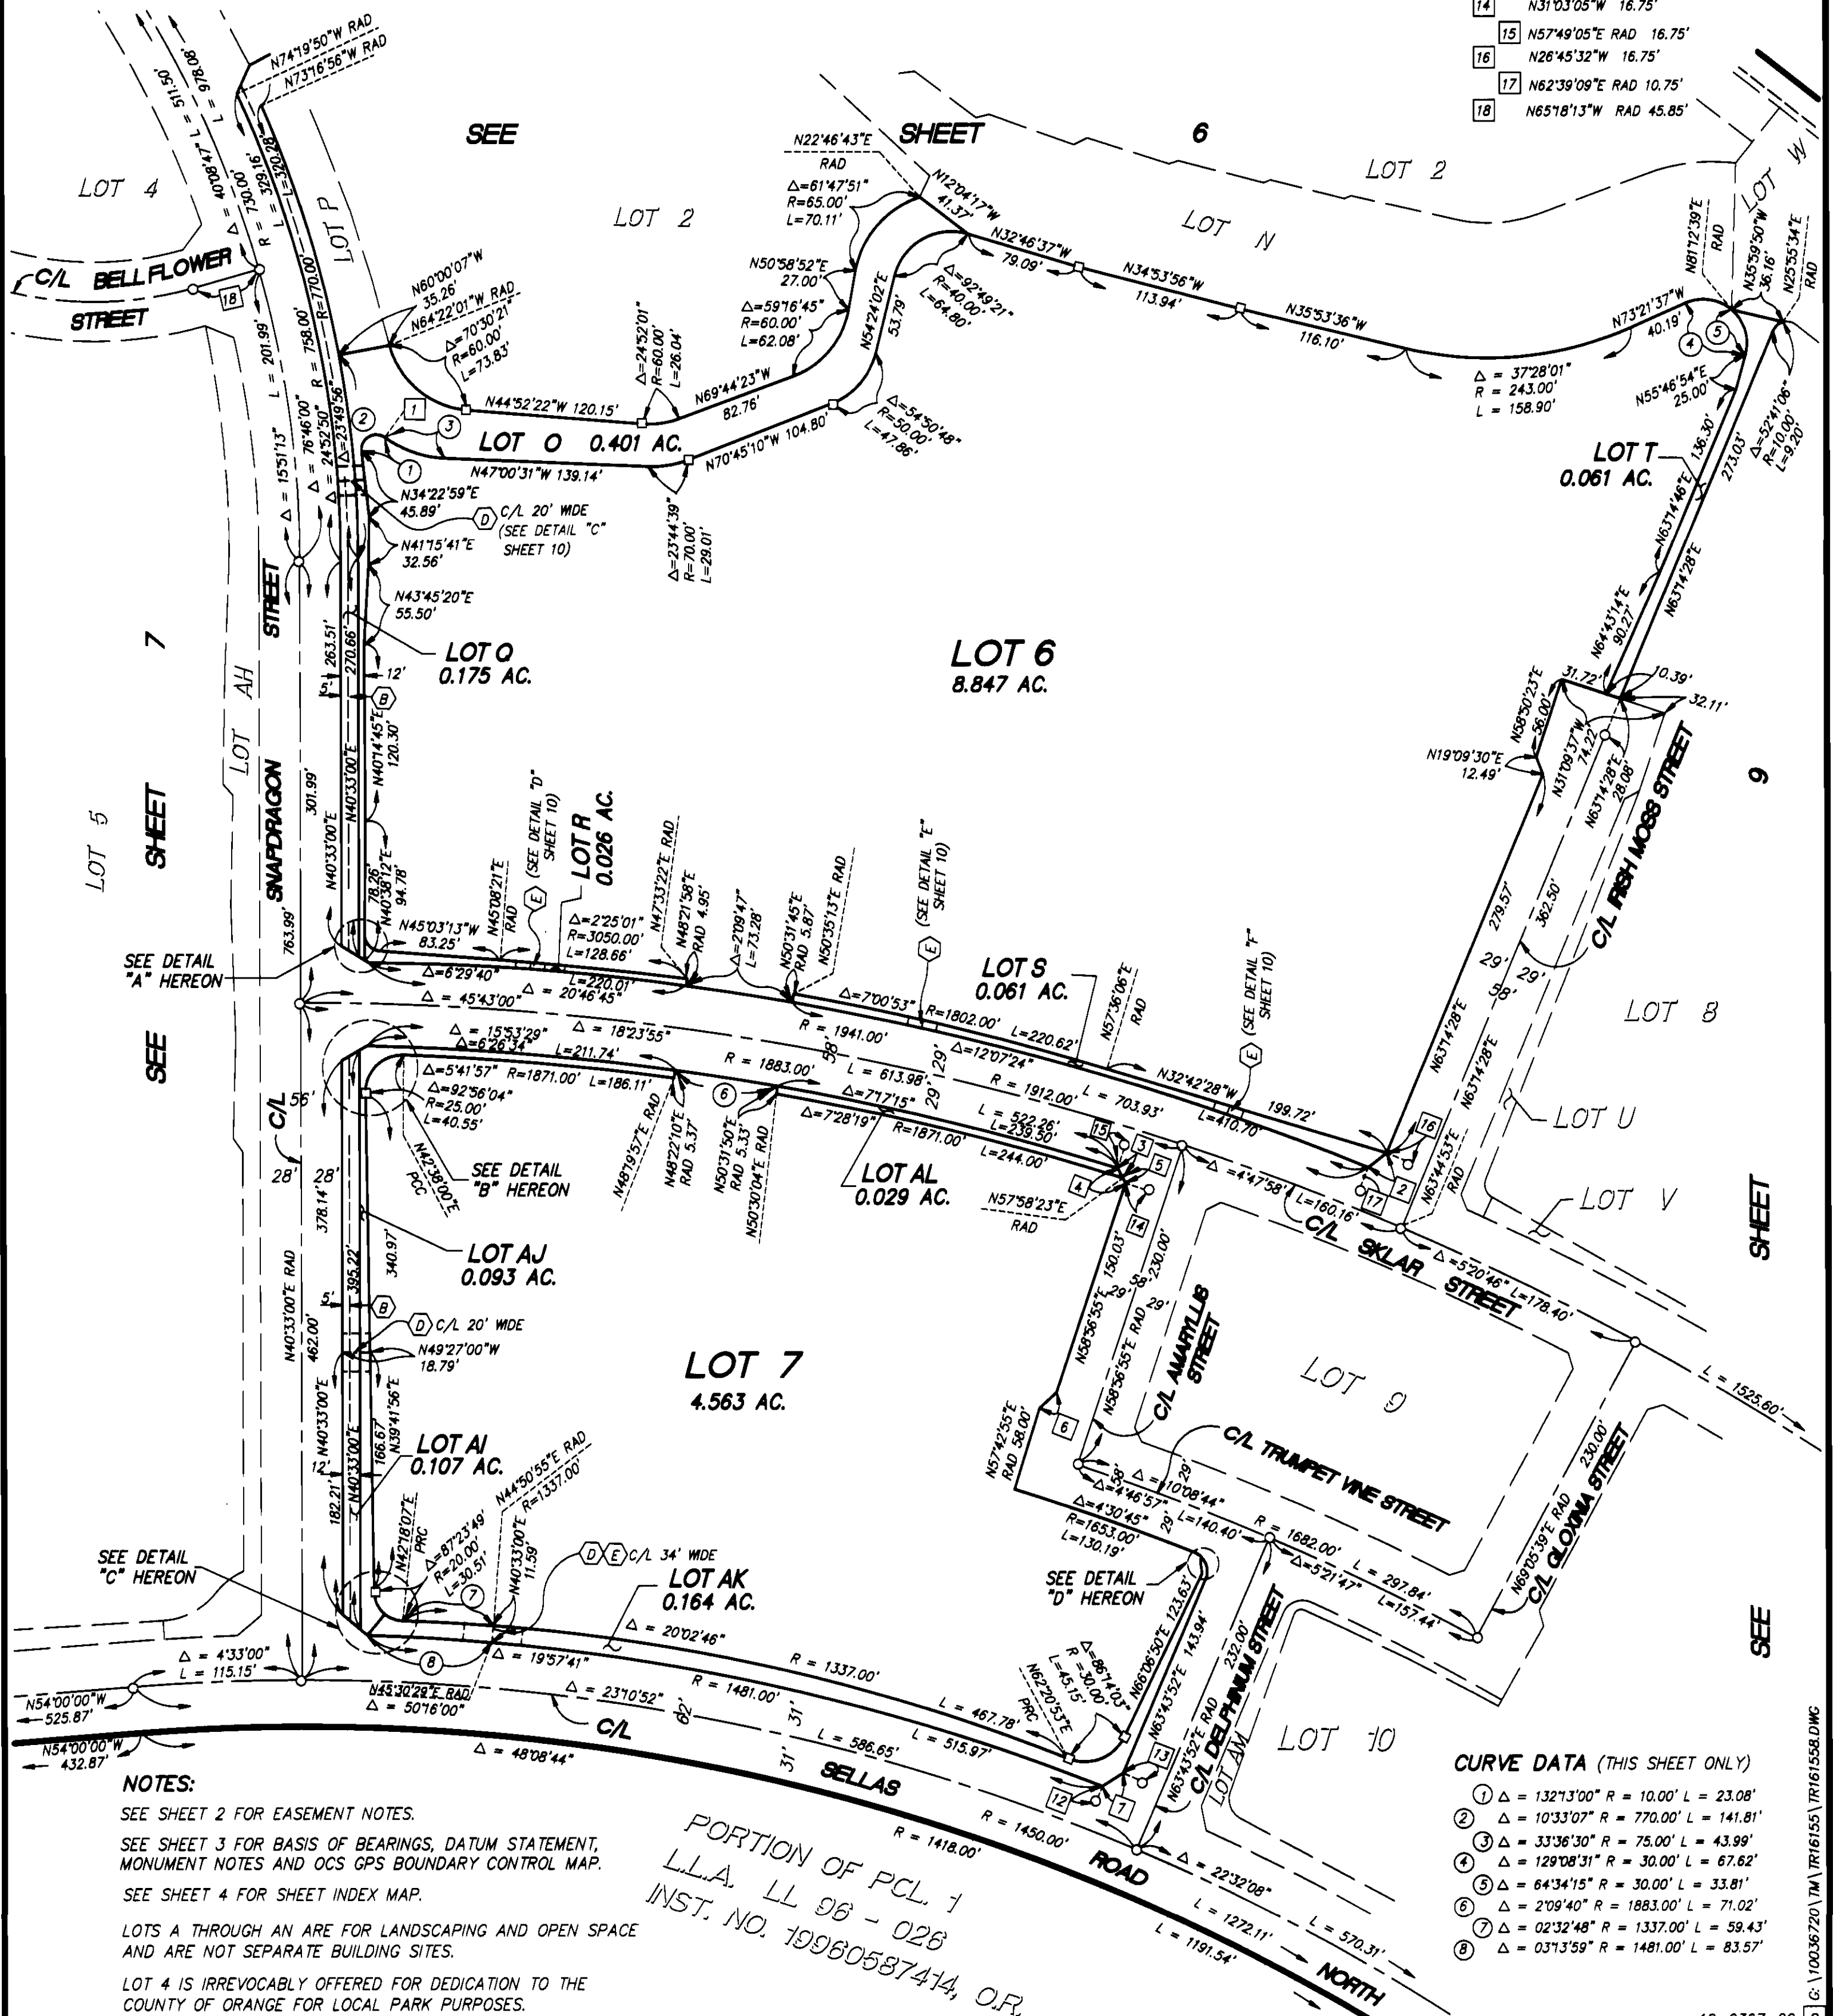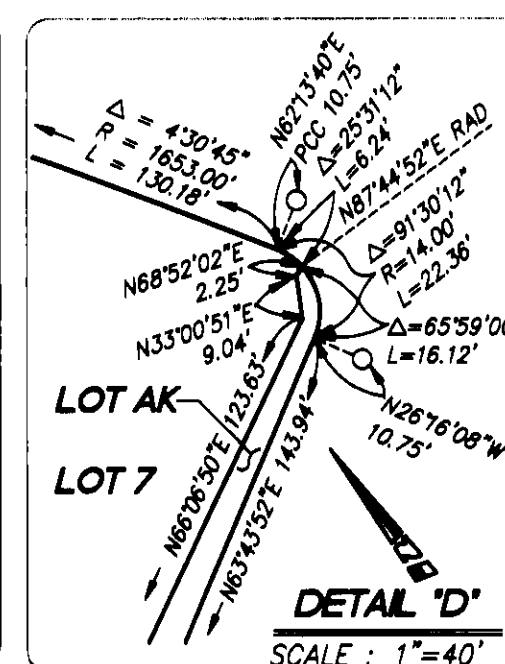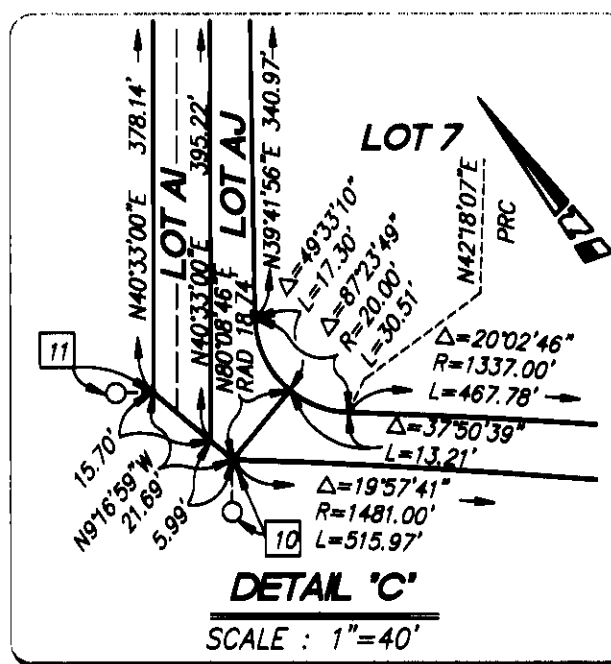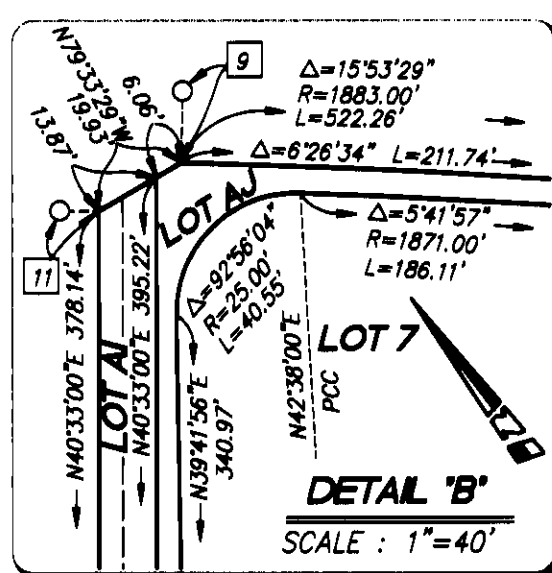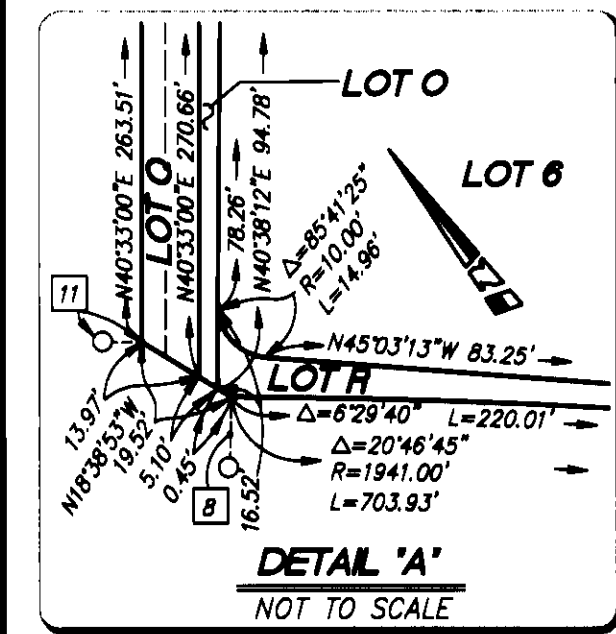

SHEET 9 OF 10 SHEETS

TRACT NO. 16155

IN UNINCORPORATED TERRITORY OF ORANGE COUNTY, CALIFORNIA



OCTOBER 2000

JAMES F. GILLEN, L.S. 5557

HUITT-ZOLLARS

10 NUMBERED LOTS AND 40 LETTERED LOTS

100.789 ACRES

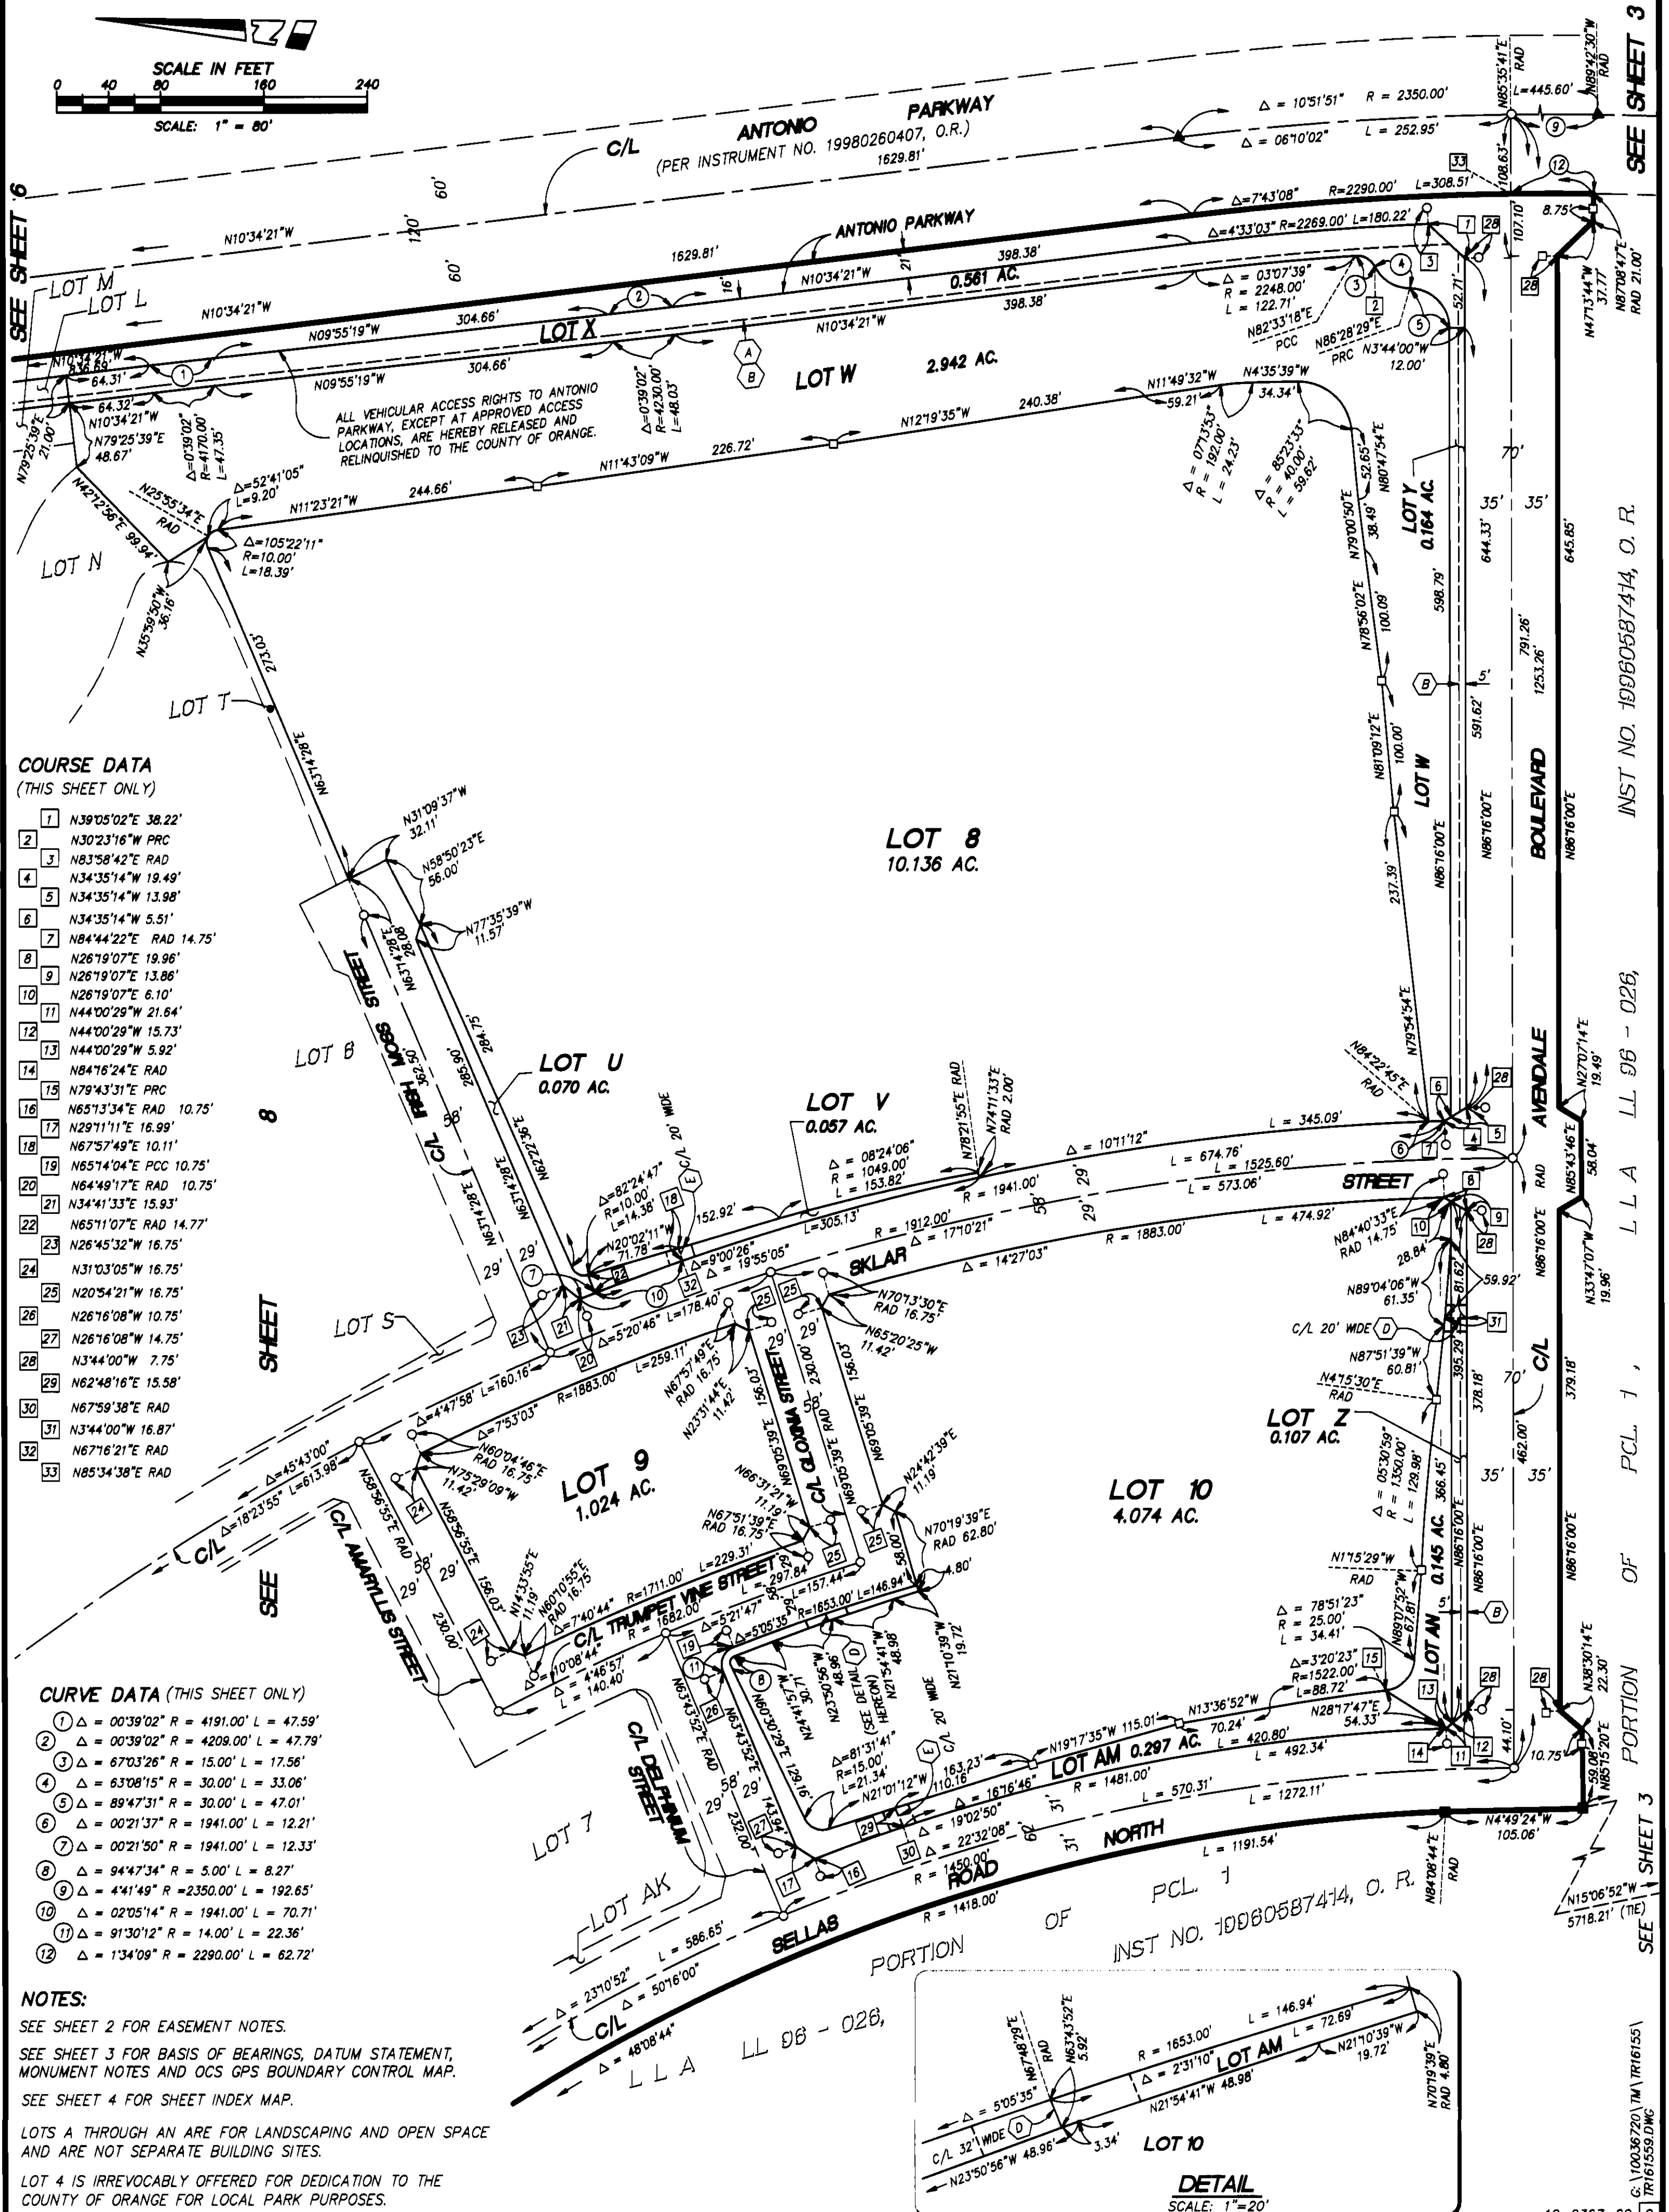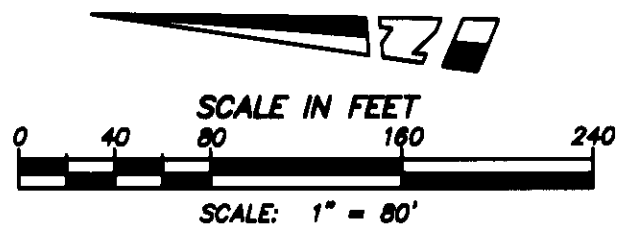A PORTION OF VESTING
TENTATIVE TRACT NO. 16025DATE OF SURVEY:
JANUARY 1999

SEE SHEET 3

INST NO. 19960587414, O. R.

PCL 1, LL 96 - 026,

PORTION OF

SEE SHEET 3

812

38

G:\10036720\TM\16155\16155.DWG

10-0367-20 9

SHEET 10 OF 10 SHEETS

TRACT NO. 16155

A PORTION OF VESTING
TENTATIVE TRACT NO. 16025

IN UNINCORPORATED TERRITORY OF ORANGE COUNTY, CALIFORNIA

OCTOBER 2000






JAMES F. GILLEN, L.S. 5557

DATE OF SURVEY:
JANUARY 1999

HUITT-ZOLLARS

10 NUMBERED LOTS AND 40 LETTERED LOTS

100.789 ACRES

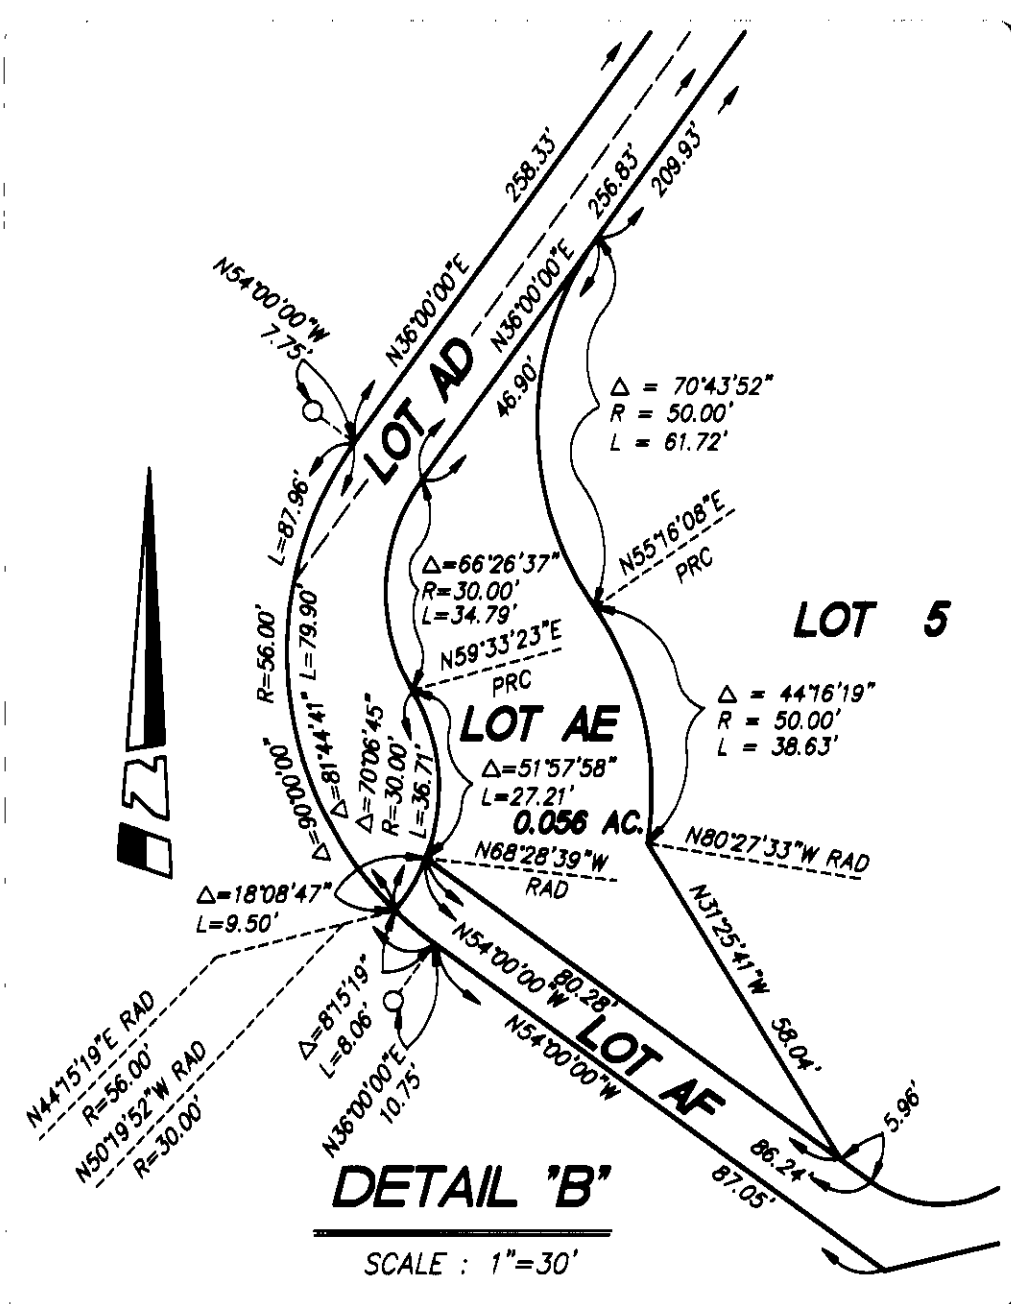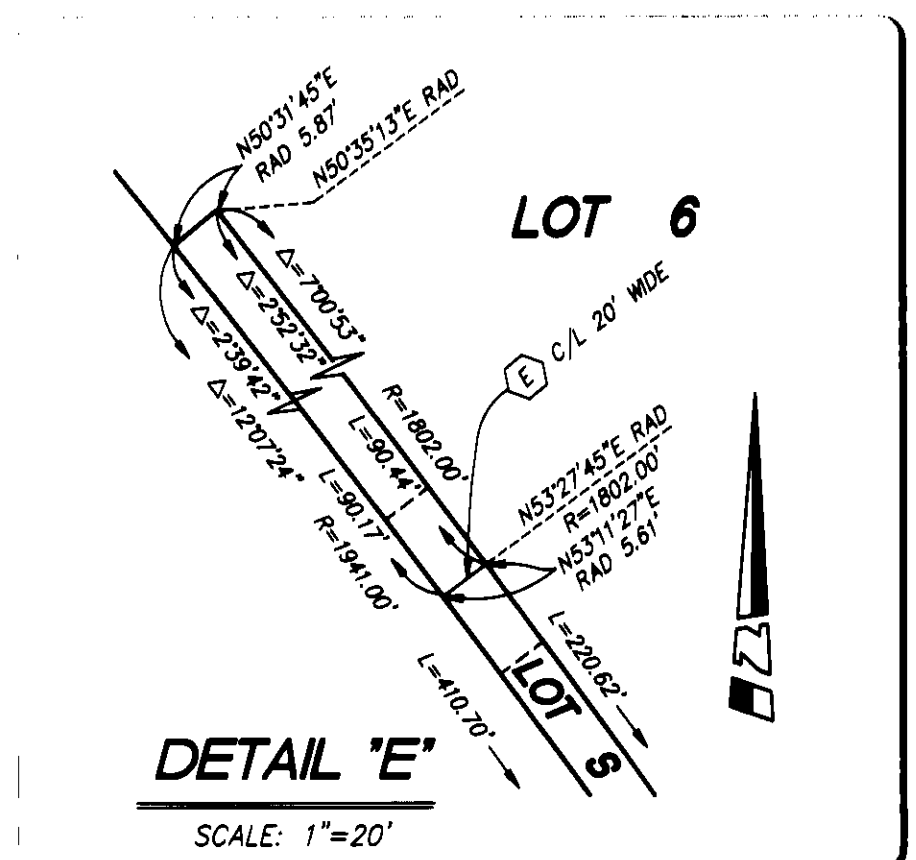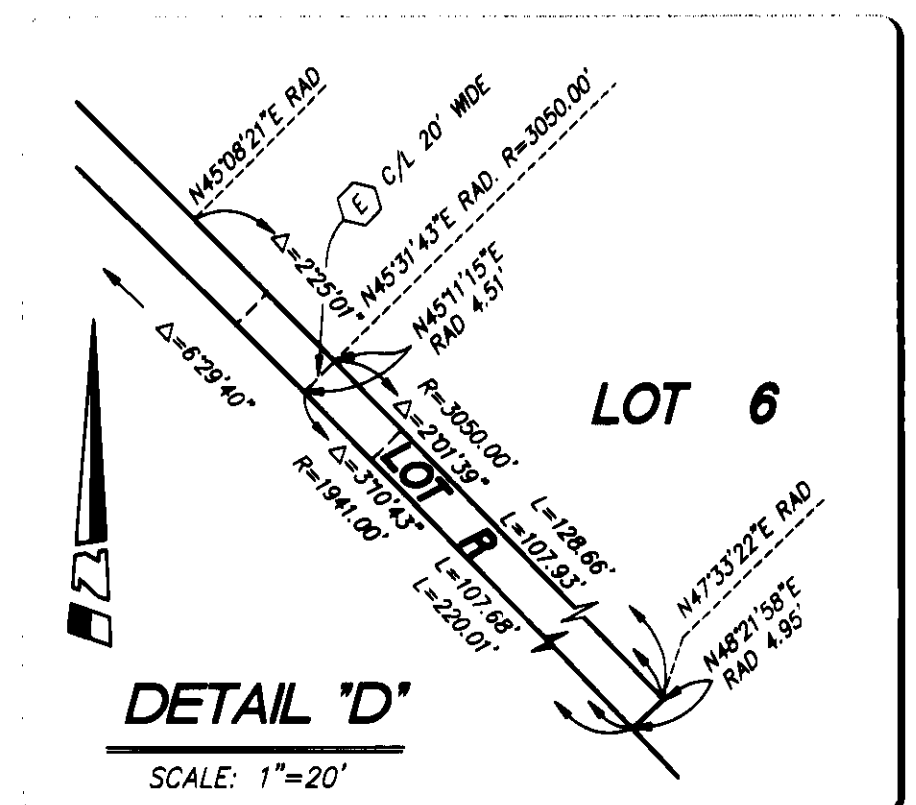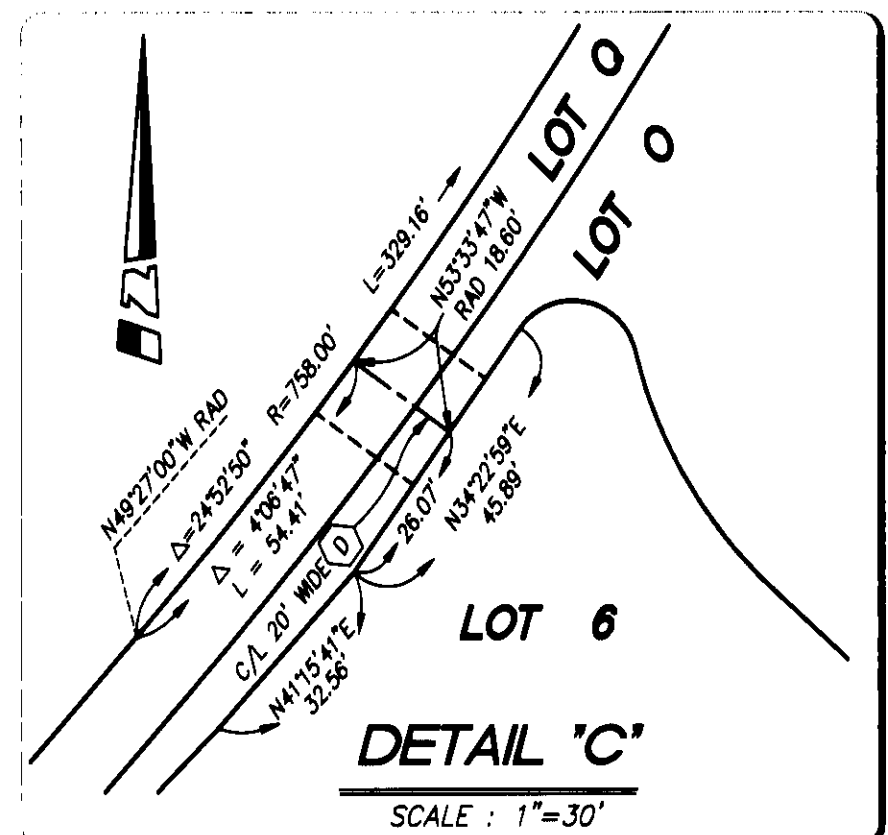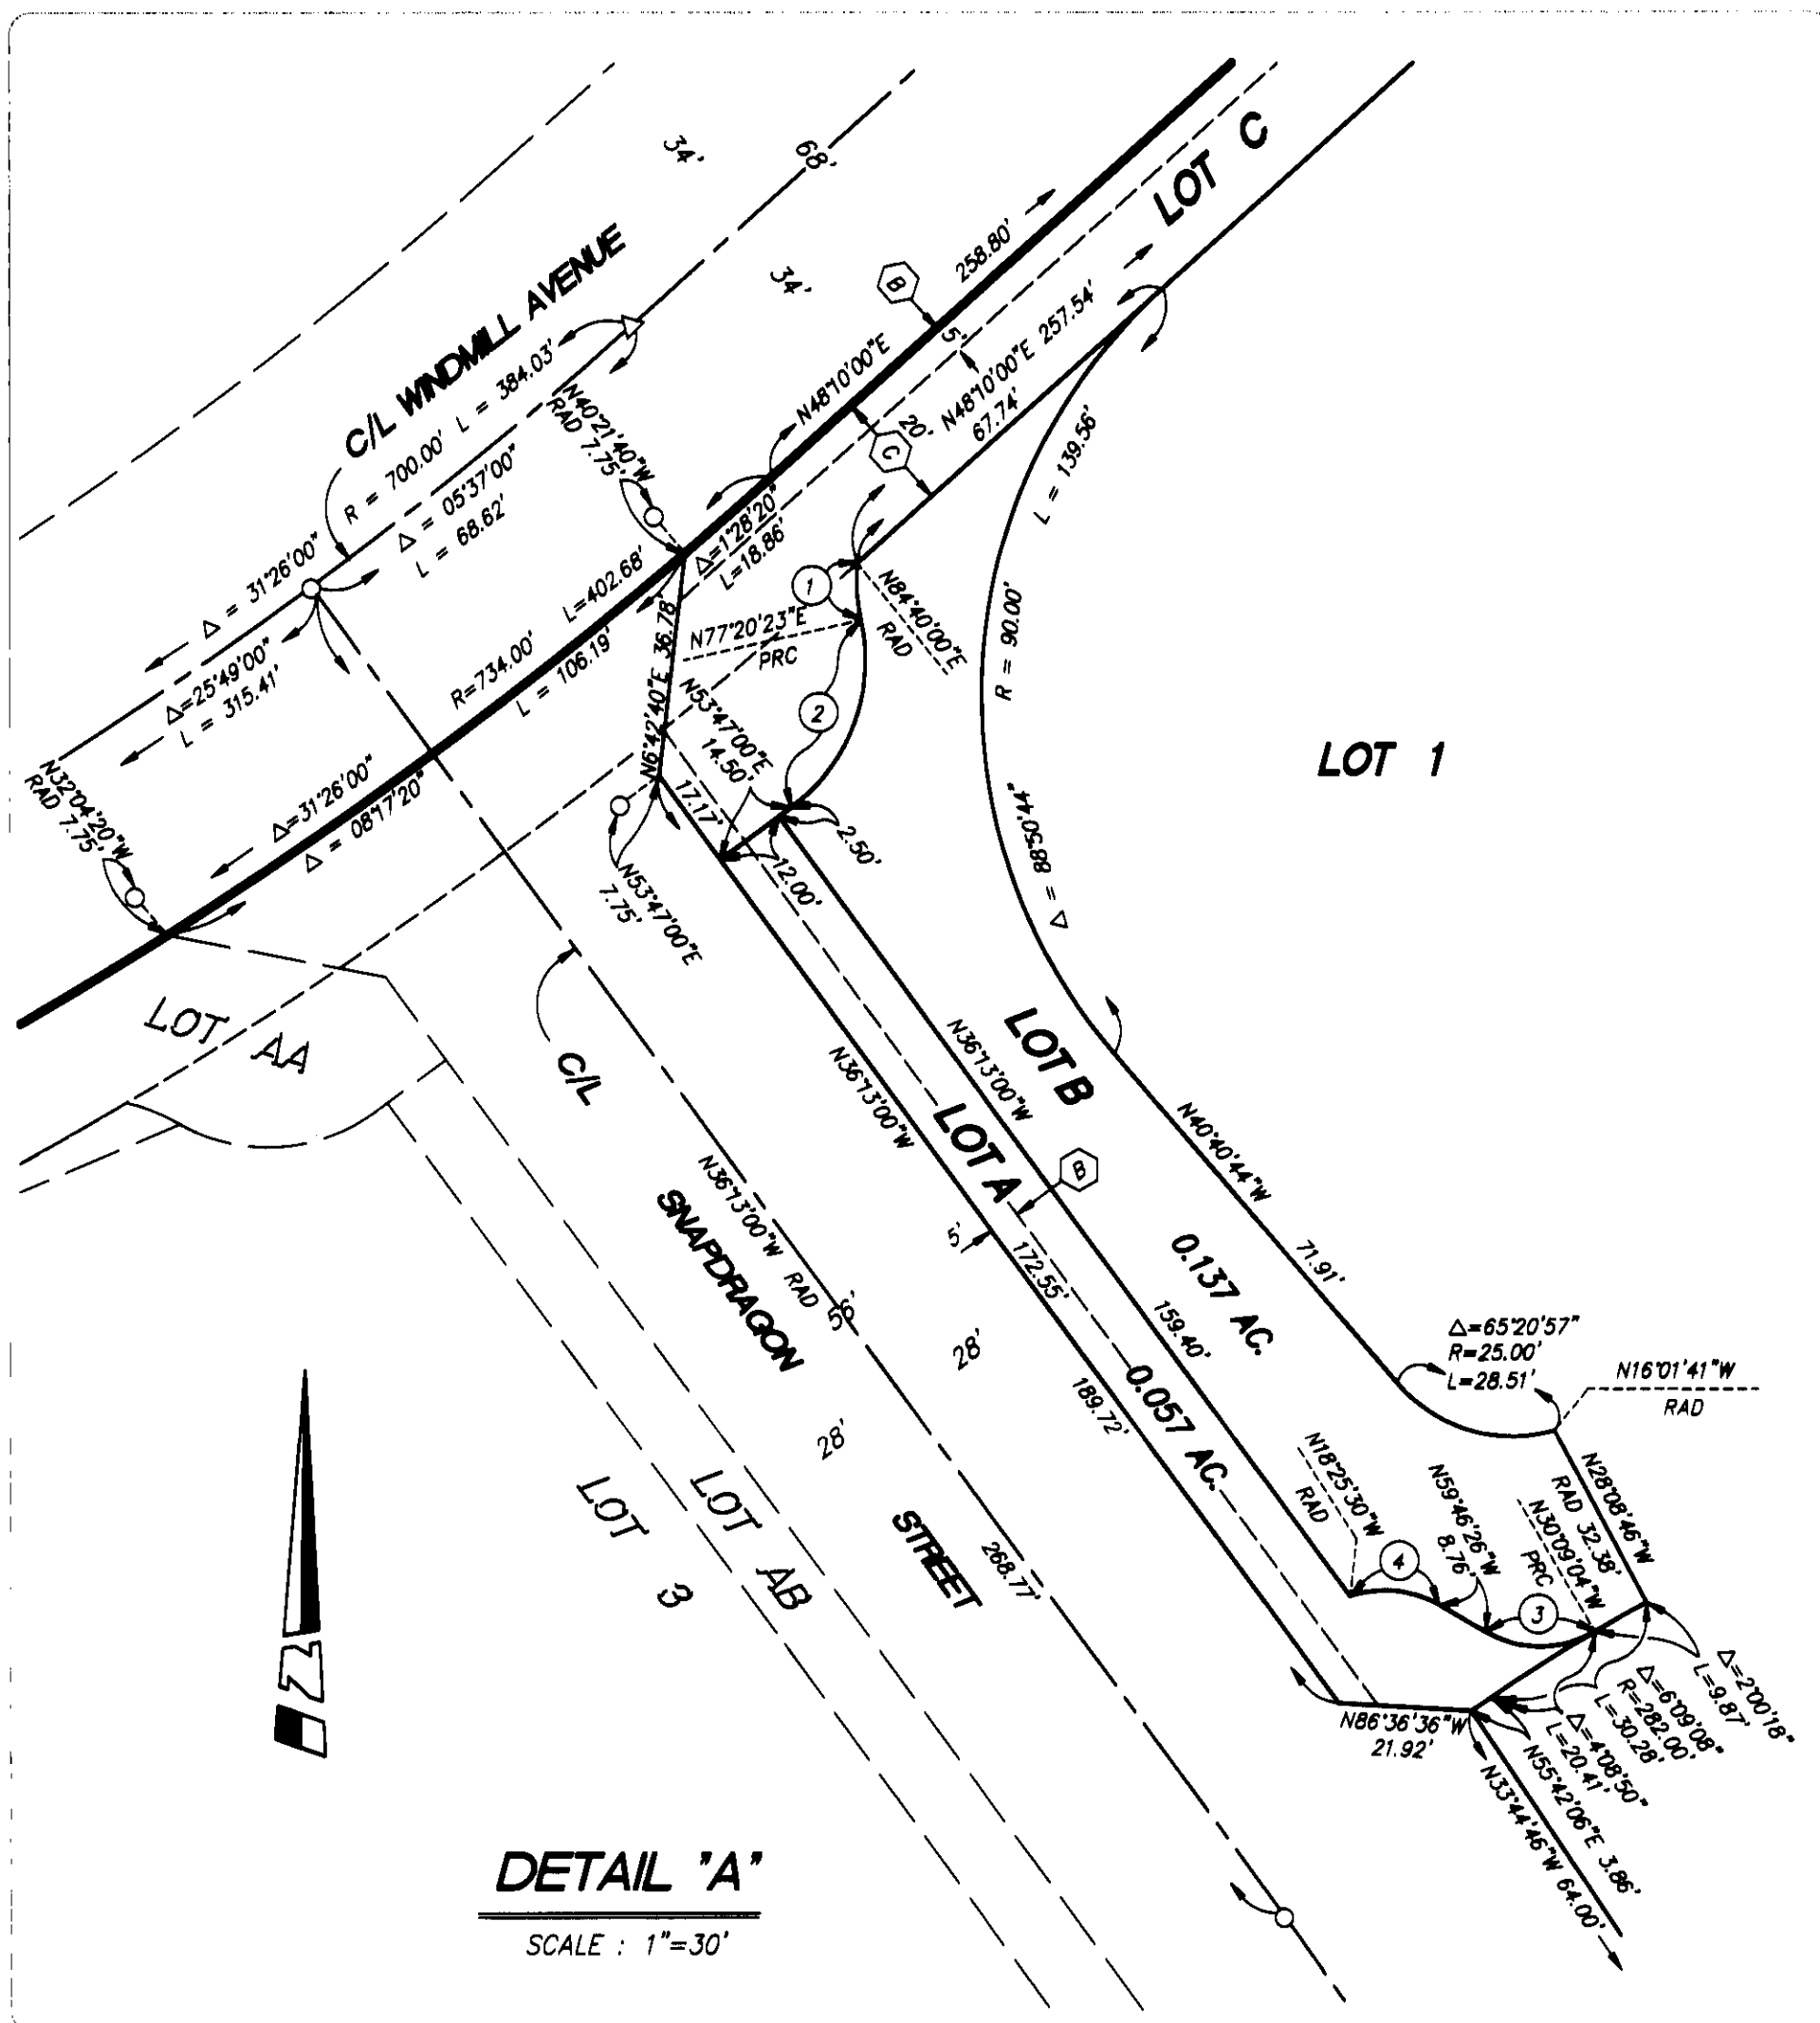

CURVE DATA (THIS SHEET ONLY)

- ① $\Delta = 17^{\circ}59'37''$ R = 30.00' L = 9.42'
- ② $\Delta = 66^{\circ}26'37''$ R = 30.00' L = 34.79'
- ③ $\Delta = 60^{\circ}22'38''$ R = 18.00' L = 18.97'
- ④ $\Delta = 48^{\circ}39'04''$ R = 18.00' L = 15.28'

NOTES:

SEE SHEET 2 FOR EASEMENT NOTES.

SEE SHEET 3 FOR BASIS OF BEARINGS, DATUM STATEMENT,
MONUMENT NOTES AND OCS GPS BOUNDARY CONTROL MAP.

SEE SHEET 4 FOR SHEET INDEX MAP.

LOTS A THROUGH AN ARE FOR LANDSCAPING AND OPEN SPACE
AND ARE NOT SEPARATE BUILDING SITES.LOT 4 IS IRREVOCABLY OFFERED FOR DEDICATION TO THE
COUNTY OF ORANGE FOR LOCAL PARK PURPOSES.