

SHEET 1 OF 9 SHEETS

TRACT NO. 16156

A PORTION OF VESTING
TENTATIVE TRACT NO. 16025BLOCK MODULE
5157 19DATE OF SURVEY:
JANUARY 1999

IN UNINCORPORATED TERRITORY OF ORANGE COUNTY, CALIFORNIA

BEING A SUBDIVISION OF A PORTION OF PARCEL 1 OF LOT LINE ADJUSTMENT NO. LL 96-026
AS SHOWN ON EXHIBIT "B" ATTACHED TO THAT CERTAIN DOCUMENT RECORDED NOVEMBER 21,
1996 AS INSTRUMENT NO. 19960587414 OF OFFICIAL RECORDS, RECORDS OF ORANGE COUNTY,
CALIFORNIA.

DECEMBER 2000

JAMES F. GILLEN, L.S. 5557

HUITT-ZOLIARS

7 NUMBERED LOTS AND 27 LETTERED LOTS

71.991 ACRES

ACCEPTED AND FILED AT THE
REQUEST OF


FIRST AMERICAN TITLE INSURANCE CO.

DATE JANUARY 26, 2001

TIME 3:55 PM FEE \$23.00

INSTRUMENT NO. 20010047445

BOOK 812 PAGE 40-48 M/M

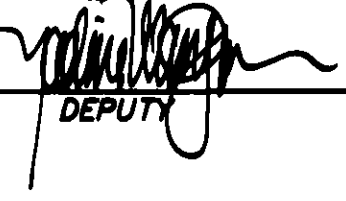GARY L. GRANVILLE
COUNTY CLERK-RECORDERBY 
DEPUTY

OWNERSHIP CERTIFICATE:

WE, THE UNDERSIGNED, BEING ALL PARTIES HAVING ANY RECORD TITLE INTEREST IN THE
LAND COVERED BY THIS MAP, DO HEREBY CONSENT TO THE PREPARATION AND RECORDATION
OF SAID MAP, AS SHOWN WITHIN THE DISTINCTIVE BORDER LINE. WE ALSO HEREBY DEDICATE
TO THE PUBLIC FOR STREET PURPOSES: ANTONIO PARKWAY, SELLAS ROAD SOUTH, HYDRANGEA
STREET, SKLAR STREET, O'NEILL DRIVE AND RANUNCULUS STREET.

WE ALSO HEREBY DEDICATE TO THE COUNTY OF ORANGE:


- (1) THE EASEMENTS FOR SIDEWALK PURPOSES AS SHOWN ON SAID MAP.
- (2) THE EASEMENTS FOR STORM DRAIN PURPOSES AS SHOWN ON SAID MAP.
- (3) THE SCENIC PRESERVATION EASEMENT AS SHOWN ON SAID MAP FOR THE PURPOSES
AND SUBJECT TO THE SAME CONDITIONS AND LIMITATIONS AS SHOWN IN THAT CERTAIN
EASEMENT RECORDED MARCH 10, 1989 AS DOCUMENT 89-125032, OF OFFICIAL RECORDS.

WE ALSO HEREBY RELEASE AND RELINQUISH TO THE COUNTY OF ORANGE ALL VEHICULAR
ACCESS RIGHTS TO ANTONIO PARKWAY, EXCEPT AT APPROVED ACCESS LOCATIONS.

WE ALSO HEREBY DEDICATE TO THE SANTA MARGARITA WATER DISTRICT THE EASEMENTS FOR
SEWER AND WATER PURPOSES AS SHOWN ON SAID MAP, WHICH EASEMENTS SHALL BE
SUBJECT TO THE SAME TERMS AND CONDITIONS AS ARE SHOWN IN THAT CERTAIN EASEMENT
RECORDED OCTOBER 6, 1980 IN BOOK 13778, PAGE 341, OF OFFICIAL RECORDS, COUNTY OF ORANGE.
THE SANTA MARGARITA WATER DISTRICT SHALL RESTORE OTHER IMPROVEMENTS OR FACILITIES
LOCATED WITHIN THE EASEMENT, IF IT HAS CONSENTED TO THE LOCATION OF SUCH IMPROVEMENTS
OR FACILITIES TO THE EXTENT THAT THE EXERCISE OF ITS RIGHTS IN CONNECTION WITH THE EASEMENT
IMPACTS OTHER IMPROVEMENTS OR FACILITIES LOCATED WITHIN THE EASEMENT, HOWEVER, IN NO EVENT
SHALL SANTA MARGARITA WATER DISTRICT BE RESPONSIBLE FOR THE COST OF RELOCATING ITS FACILITIES
IN THE EVENT OF CONFLICTS WITH SUCH OTHER IMPROVEMENTS OR FACILITIES.

DMB LADERA, L.L.C., A DELAWARE LIMITED LIABILITY COMPANY.

BY: RANCHO MISSION VIEJO, L.L.C., A DELAWARE LIMITED LIABILITY COMPANY,
AS AGENT AND/OR MANAGER.

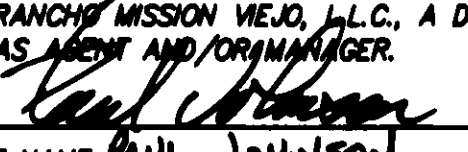BY: 
PRINT NAME: PAUL JOHNSON
PRINT TITLE: V.P. COMMUNITY DEVELOPMENT

BY: 
PRINT NAME: STEPHEN C. SUMANEK
PRINT TITLE: ENG. VICE PRES.

DMB CONSOLIDATED HOLDINGS, L.L.C., AN ARIZONA LIMITED LIABILITY COMPANY,
BENEFICIARY UNDER DEEDS OF TRUSTS RECORDED DECEMBER 10, 1996 AS INSTRUMENT
NO. 19960624030, AND RECORDED APRIL 20, 1999 AS INSTRUMENT NO. 19990289616,
BOTH OF OFFICIAL RECORDS.


BY: DMB ASSOCIATES, INC., AN ARIZONA CORPORATION,
AS MANAGER.

BY: 
PRINT NAME: TERRY D. RANDALL
PRINT TITLE: VICE PRESIDENT

BY: 
PRINT NAME: TIMOTHY A. HAEFFLER
PRINT TITLE: Executive Vice President

CERTIFICATE OF ACCEPTANCE

THE UNDERSIGNED, BEING THE DULY APPOINTED AGENT OF THE SANTA MARGARITA WATER
DISTRICT, A PUBLIC CORPORATION OF ORANGE COUNTY, CALIFORNIA, PURSUANT TO ITS
RESOLUTION NO. 88-10-2, DOES HEREBY ACCEPT ON BEHALF OF SAID DISTRICT THE EASEMENTS
FOR SEWER, WATER, AND ACCESS PURPOSES, AS DEDICATED AND AS SHOWN ON THIS TRACT MAP,
BY AND BETWEEN THE SANTA MARGARITA WATER DISTRICT AND DMB LADERA, L.L.C., AND
DOES HEREBY CERTIFY THAT THE GRANTEE CONSENTS TO THE RECORDATION OF SAID TRACT.

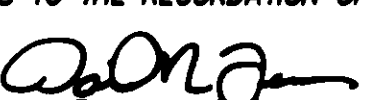
DANIEL R. FERONS, CHIEF ENGINEER
SANTA MARGARITA WATER DISTRICT.

AUTOMATIC FIRE SPRINKLER NOTE:

ALL COMMERCIAL STRUCTURES GREATER THAN 6,000 SQUARE FEET; ALL MULTIFAMILY RESIDENTIAL
STRUCTURES; ALL SINGLE-FAMILY STRUCTURES EXCEEDING 5,500 SQUARE FEET, AND ALL STRUCTURES
EXCEEDING FIRE DEPARTMENT ACCESS REQUIREMENTS SHALL BE PROTECTED BY AN AUTOMATIC
SPRINKLER SYSTEM.

SPECIAL FIRE PROTECTION NOTE:

~~PROPERTY IS TOTALLY EXCLUDED FROM A SPECIAL FIRE PROTECTION AREA.~~
PROPERTY IS TOTALLY EXCLUDED FROM A SPECIAL FIRE PROTECTION AREA.

HIGH FIRE HAZARD AREA NOTE:

THE LOTS SHOWN ON THIS MAP ARE IN A HIGH FIRE HAZARD AREA DUE TO
WILD LAND EXPOSURE.

NOTE:

SEE SHEET 2 FOR NOTARY ACKNOWLEDGMENTS AND SIGNATURE OMISSIONS.

SURVEYOR'S STATEMENT:

I HEREBY STATE THAT THIS MAP CONSISTING OF 9 SHEETS, CORRECTLY REPRESENTS A TRUE AND
COMPLETE SURVEY AS SHOWN MADE IN JANUARY, 1999; WAS MADE BY ME OR UNDER MY DIRECTION;
THAT THE MONUMENTS ARE OF THE CHARACTER AND OCCUPY OR WILL OCCUPY THE POSITIONS
INDICATED BY SAID MAP; AND THAT SAID MONUMENTS WILL BE SUFFICIENT TO ENABLE THE
SURVEY TO BE RETRACED.




JAMES F. GILLEN
L.S. 5557
EXPIRATION DATE: 9/30/01

COUNTY SURVEYOR'S STATEMENT:

I HEREBY STATE THAT I HAVE EXAMINED THIS MAP AND HAVE FOUND IT TO BE
SUBSTANTIALLY IN CONFORMANCE WITH THE TENTATIVE MAP AS FILED WITH, AMENDED AND
APPROVED BY THE ORANGE COUNTY SUBDIVISION COMMITTEE; THAT ALL PROVISIONS OF THE
SUBDIVISION MAP ACT AND COUNTY SUBDIVISION REGULATIONS HAVE BEEN COMPLIED WITH
AND I AM SATISFIED SAID MAP IS TECHNICALLY CORRECT.

DATED THIS 17TH DAY OF JANUARY, 2001.


JOHN CANAS, COUNTY SURVEYOR
L.S. 4408, EXPIRATION DATE: 9-30-01

BY: MICHAEL K. SULLIVAN, DEPUTY
L.S. 8254 EXPIRES 6-30-02

COUNTY TREASURER-TAX COLLECTOR'S CERTIFICATE:

STATE OF CALIFORNIA)
COUNTY OF ORANGE)

I HEREBY CERTIFY THAT ACCORDING TO THE RECORDS OF MY OFFICE THERE ARE NO LIENS
AGAINST THE LAND COVERED BY THIS MAP OR ANY PART THEREOF FOR UNPAID STATE,
COUNTY, MUNICIPAL OR LOCAL TAXES OR SPECIAL ASSESSMENTS COLLECTED AS TAXES,
EXCEPT TAXES OR SPECIAL ASSESSMENTS COLLECTED AS TAXES NOT YET PAYABLE.

AND DO ALSO HEREBY CERTIFY TO THE RECORDER OF ORANGE COUNTY THAT THE PROVISIONS
OF THE SUBDIVISION MAP ACT HAVE BEEN COMPLIED WITH REGARDING DEPOSITS TO SECURE
THE PAYMENT OF TAXES OR SPECIAL ASSESSMENTS COLLECTED AS TAXES ON THE LAND
COVERED BY THIS MAP.

DATED THIS 18TH DAY OF JANUARY, 2001.

JOHN M.W. MOORLACH
COUNTY TREASURER-TAX COLLECTOR

BY: 
DEPUTY TREASURER-TAX COLLECTOR

CLERK OF THE BOARD OF SUPERVISORS' CERTIFICATE:


STATE OF CALIFORNIA)
COUNTY OF ORANGE)

I HEREBY CERTIFY THAT THIS MAP WAS PRESENTED FOR APPROVAL TO THE BOARD OF
SUPERVISORS OF ORANGE COUNTY AT A REGULAR MEETING THEREOF HELD ON THE 23RD DAY
OF JANUARY, 2001, AND THAT THEREUPON SAID BOARD DID, BY AN ORDER DULY PASSED
AND ENTERED, APPROVE SAID MAP AND DID ACCEPT ON BEHALF OF THE PUBLIC, SUBJECT TO
IMPROVEMENTS: THE DEDICATION FOR STREET PURPOSES OF: ANTONIO PARKWAY, SELLAS ROAD SOUTH
HYDRANGEA STREET, SKLAR STREET, O'NEILL DRIVE AND RANUNCULUS STREET.

AND DID ALSO ACCEPT ON BEHALF OF THE COUNTY OF ORANGE:

1. THE EASEMENTS FOR SIDEWALK PURPOSES AS DEDICATED.
2. THE EASEMENTS FOR STORM DRAIN PURPOSES AS DEDICATED.
3. THE EASEMENT FOR SCENIC PRESERVATION PURPOSES AS DEDICATED.
4. THE VEHICULAR ACCESS RIGHTS TO ANTONIO PARKWAY AS RELEASED AND RELINQUISHED.

DATED THIS 23RD DAY OF JANUARY, 2001.

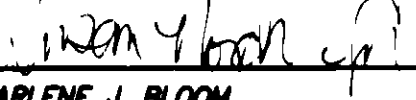
DARLENE J. BLOOM
CLERK OF THE BOARD OF SUPERVISORS



SHEET 2 OF 9 SHEETS

TRACT NO. 16156

A PORTION OF VESTING
TENTATIVE TRACT NO. 18025

IN UNINCORPORATED TERRITORY OF ORANGE COUNTY, CALIFORNIA

DATE OF SURVEY:
JANUARY 1999

DECEMBER 2000

JAMES F. GILLEN, L.S. 5557

HUITT-ZOLIARS

7 NUMBERED LOTS AND 27 LETTERED LOTS

71.991 ACRES

DMB LADERA, L.L.C.

STATE OF CALIFORNIA)
COUNTY OF ORANGE)SS

ON THIS 21st DAY OF December, 2000, BEFORE ME,
JEANNINE CARTA HANSON A NOTARY PUBLIC IN AND FOR SAID STATE,
 PERSONALLY APPEARED Stephen C. Schrank AND
Paul Johnson, PERSONALLY KNOWN TO ME OR PROVED TO ME
 ON THE BASIS OF SATISFACTORY EVIDENCE TO BE THE PERSONS WHOSE NAMES
 ARE SUBSCRIBED TO THE WITHIN INSTRUMENT AND ACKNOWLEDGED TO ME THAT
 THEY EXECUTED THE SAME IN THEIR AUTHORIZED CAPACITIES, AND THAT BY THEIR
 SIGNATURES ON THE INSTRUMENT THE PERSONS, OR THE ENTITY UPON BEHALF
 OF WHICH THE PERSONS ACTED, EXECUTED THE INSTRUMENT.

WITNESS MY HAND:

MY COMMISSION EXPIRES Feb. 25, 2003

JEANNINE CARTA HANSON MY PRINCIPAL PLACE OF BUSINESS
 NOTARY PUBLIC IN AND FOR SAID STATE IS IN ORANGE COUNTY.

JEANNINE CARTA HANSON
 PRINT NAME

DMB CONSOLIDATED HOLDINGS, L.L.C.

STATE OF Arizona)
COUNTY OF Maricopa)SS


ON THIS 26th DAY OF December, 2000, BEFORE ME,
Carolynn Sneddon, A NOTARY PUBLIC IN AND FOR SAID STATE,
 PERSONALLY APPEARED Terry D. Randall PERSONALLY KNOWN TO ME
 OR PROVED TO ME ON THE BASIS OF SATISFACTORY EVIDENCE TO BE THE
 PERSON WHOSE NAME IS SUBSCRIBED TO THE WITHIN INSTRUMENT AND ACKNOWLEDGED
 TO ME THAT HE EXECUTED THE SAME IN HIS AUTHORIZED CAPACITY, AND THAT
 BY HIS SIGNATURE ON THE INSTRUMENT THE PERSON, OR THE ENTITY UPON BEHALF
 OF WHICH THE PERSON ACTED, EXECUTED THE INSTRUMENT, AS BENEFICIARY.

WITNESS MY HAND:

MY COMMISSION EXPIRES 07-14-02

Carolynn Sneddon MY PRINCIPAL PLACE OF BUSINESS
 NOTARY PUBLIC IN AND FOR SAID STATE IS IN Maricopa COUNTY.

Carolynn Sneddon
 PRINT NAME

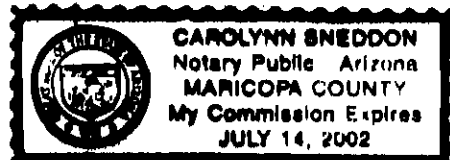

SIGNATURE OMISSIONS:

IN ACCORDANCE WITH THE PROVISIONS OF SECTION 66436(a) (3) OF THE SUBDIVISION
 MAP ACT, THE FOLLOWING SIGNATURE HAS BEEN OMITTED:

1. LADERA DEVELOPMENT COMPANY, L.L.C., HOLDER OF OIL, GAS, MINERAL, AND WATER RIGHTS
 RECORDED DECEMBER 10, 1998 AS INSTRUMENT NO. 19980624029 OF OFFICIAL RECORDS.

EASEMENT NOTES:

- (A) INDICATES EASEMENT FOR SCENIC PRESERVATION PURPOSES DEDICATED TO THE COUNTY OF ORANGE.
 (B) INDICATES SIDEWALK EASEMENT DEDICATED TO THE COUNTY OF ORANGE.
 (C) INDICATES EASEMENT FOR STORM DRAIN PURPOSES DEDICATED TO THE COUNTY OF ORANGE.
 (D) INDICATES EASEMENT FOR SEWER, WATER, AND ACCESS PURPOSES DEDICATED TO THE SANTA MARGARITA
 WATER DISTRICT.

DMB CONSOLIDATED HOLDINGS, L.L.C.

STATE OF Arizona)
COUNTY OF Maricopa)SS

ON THIS 26th DAY OF December, 2000, BEFORE ME,
Carolynn Sneddon, A NOTARY PUBLIC IN AND FOR SAID STATE
 PERSONALLY APPEARED Timothy A. Kachr PERSONALLY KNOWN TO ME
 OR PROVED TO ME ON THE BASIS OF SATISFACTORY EVIDENCE TO BE THE PERSON
 WHOSE NAME IS SUBSCRIBED TO THE WITHIN INSTRUMENT AND ACKNOWLEDGED
 TO ME THAT HE EXECUTED THE SAME IN HIS AUTHORIZED CAPACITY, AND THAT
 BY HIS SIGNATURE ON THE INSTRUMENT THE PERSON, OR THE ENTITY UPON BEHALF
 OF WHICH THE PERSON ACTED, EXECUTED THE INSTRUMENT, AS BENEFICIARY.


WITNESS MY HAND:

MY COMMISSION EXPIRES 07-14-02

Carolynn Sneddon
 NOTARY PUBLIC IN AND FOR SAID STATE

MY PRINCIPAL PLACE OF BUSINESS
 IS IN Maricopa COUNTY.

Carolynn Sneddon
 PRINT NAME

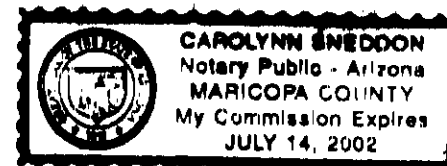

SANTA MARGARITA WATER DISTRICT

STATE OF CALIFORNIA)
COUNTY OF ORANGE)SS

ON THIS 21st DAY OF December, 2000, BEFORE ME,
Lupe Martinez, A NOTARY PUBLIC IN AND FOR SAID STATE,
 PERSONALLY APPEARED DANIEL R. FERONS PERSONALLY KNOWN TO ME
 OR PROVED TO ME ON THE BASIS OF SATISFACTORY EVIDENCE TO BE THE
 PERSON WHOSE NAME IS SUBSCRIBED TO THE WITHIN INSTRUMENT AND ACKNOWLEDGED
 TO ME THAT HE EXECUTED THE SAME IN HIS AUTHORIZED CAPACITY, AND THAT
 BY HIS SIGNATURE ON THE INSTRUMENT THE PERSON, OR THE ENTITY UPON BEHALF
 OF WHICH THE PERSON ACTED, EXECUTED THE INSTRUMENT.

WITNESS MY HAND:

MY COMMISSION EXPIRES 8-13-2001

Lupe Martinez MY PRINCIPAL PLACE OF BUSINESS
 NOTARY PUBLIC IN AND FOR SAID STATE IS IN Orange COUNTY.

Lupe Martinez
 PRINT NAME

TRACT NO. 16156

IN UNINCORPORATED TERRITORY OF ORANGE COUNTY, CALIFORNIA

DECEMBER 2000

JAMES F. GILLEN, L.S. 5557



HUITT-ZOLLARS

7 NUMBERED LOTS AND 27 LETTERED LOTS

71.991 ACRES

A PORTION VESTING TENTATIVE
TRACT NO. 16025

DATE OF SURVEY:
JANUARY 1999

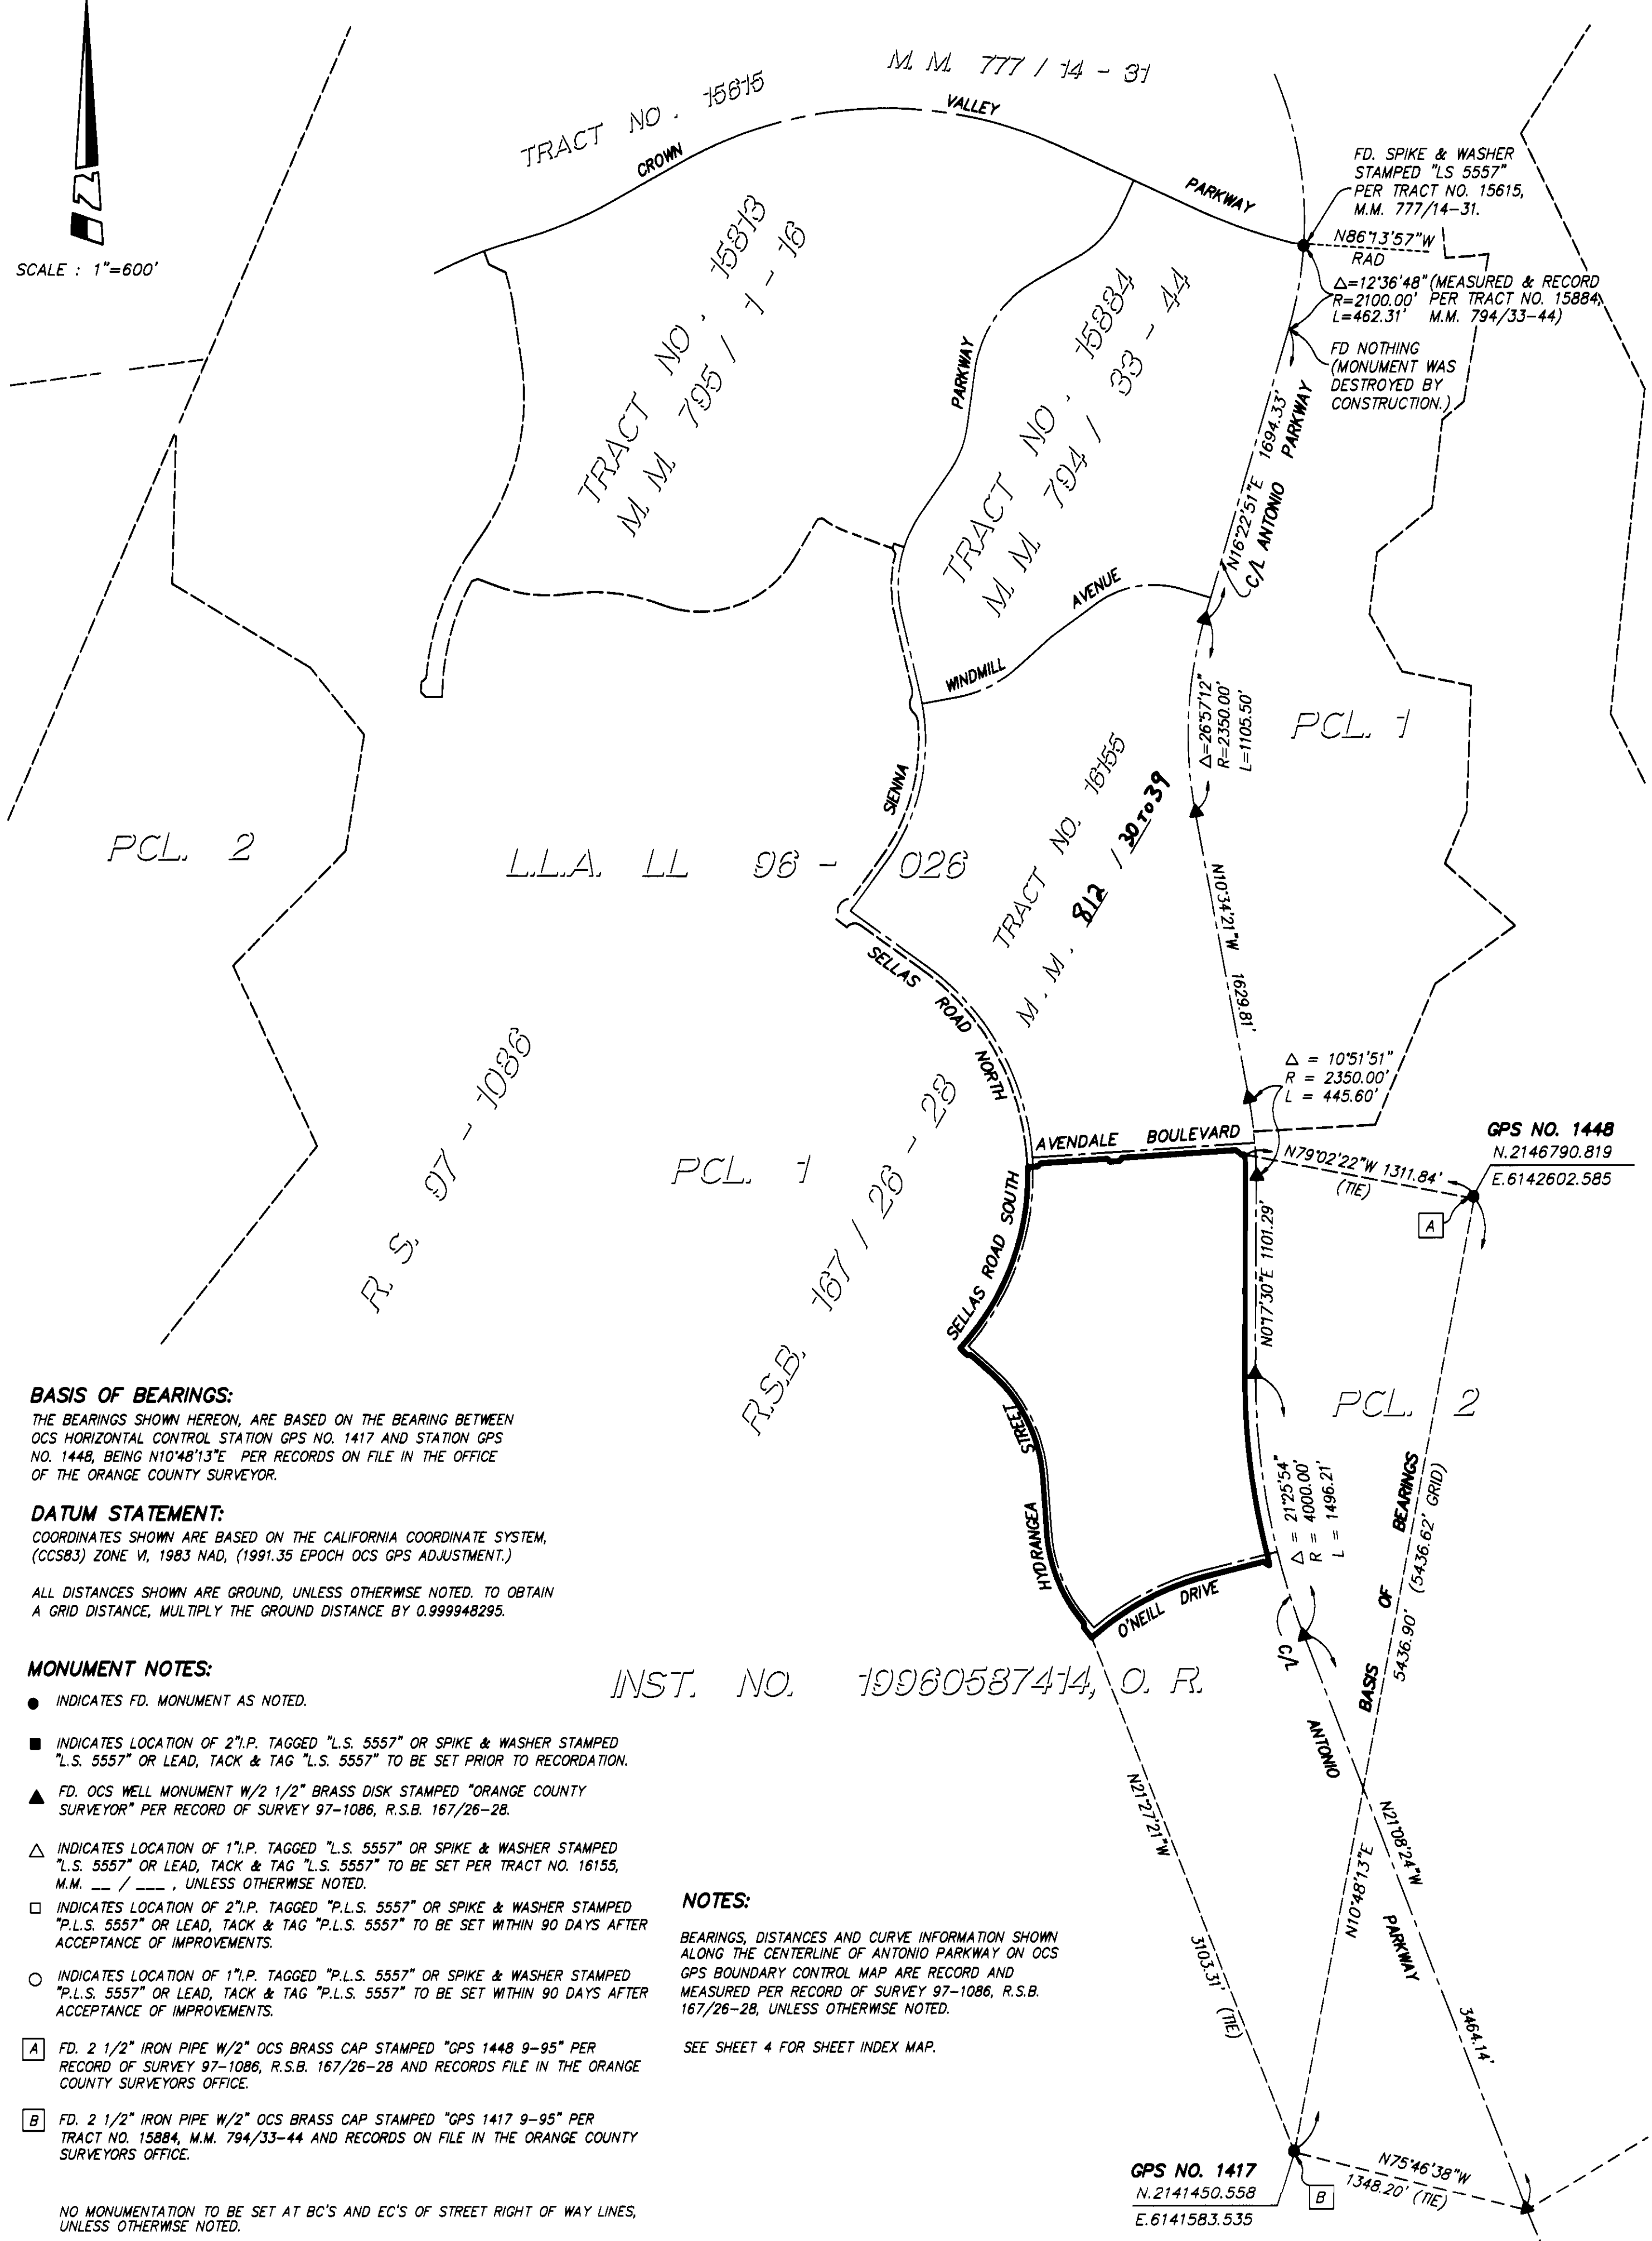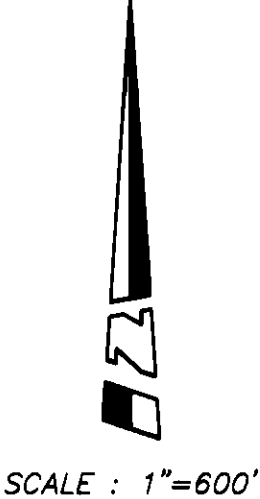

BASIS OF BEARINGS:
THE BEARINGS SHOWN HEREON, ARE BASED ON THE BEARING BETWEEN
OCS HORIZONTAL CONTROL STATION GPS NO. 1417 AND STATION GPS
NO. 1448, BEING N10°48'13"E PER RECORDS ON FILE IN THE OFFICE
OF THE ORANGE COUNTY SURVEYOR.

DATUM STATEMENT:
COORDINATES SHOWN ARE BASED ON THE CALIFORNIA COORDINATE SYSTEM,
(CCS83) ZONE VI, 1983 NAD, (1991.35 EPOCH OCS GPS ADJUSTMENT.)

ALL DISTANCES SHOWN ARE GROUND, UNLESS OTHERWISE NOTED. TO OBTAIN
A GRID DISTANCE, MULTIPLY THE GROUND DISTANCE BY 0.999948295.

MONUMENT NOTES:

- INDICATES FD. MONUMENT AS NOTED.
- INDICATES LOCATION OF 2" I.P. TAGGED "L.S. 5557" OR SPIKE & WASHER STAMPED "L.S. 5557" OR LEAD, TACK & TAG "L.S. 5557" TO BE SET PRIOR TO RECORDATION.
- ▲ FD. OCS WELL MONUMENT W/2 1/2" BRASS DISK STAMPED "ORANGE COUNTY SURVEYOR" PER RECORD OF SURVEY 97-1086, R.S.B. 167/26-28.
- △ INDICATES LOCATION OF 1" I.P. TAGGED "L.S. 5557" OR SPIKE & WASHER STAMPED "L.S. 5557" OR LEAD, TACK & TAG "L.S. 5557" TO BE SET PER TRACT NO. 16155, M.M. ___ / ___, UNLESS OTHERWISE NOTED.
- INDICATES LOCATION OF 2" I.P. TAGGED "P.L.S. 5557" OR SPIKE & WASHER STAMPED "P.L.S. 5557" OR LEAD, TACK & TAG "P.L.S. 5557" TO BE SET WITHIN 90 DAYS AFTER ACCEPTANCE OF IMPROVEMENTS.
- INDICATES LOCATION OF 1" I.P. TAGGED "P.L.S. 5557" OR SPIKE & WASHER STAMPED "P.L.S. 5557" OR LEAD, TACK & TAG "P.L.S. 5557" TO BE SET WITHIN 90 DAYS AFTER ACCEPTANCE OF IMPROVEMENTS.
- [A] FD. 2 1/2" IRON PIPE W/2" OCS BRASS CAP STAMPED "GPS 1448 9-95" PER RECORD OF SURVEY 97-1086, R.S.B. 167/26-28 AND RECORDS FILE IN THE ORANGE COUNTY SURVEYORS OFFICE.
- [B] FD. 2 1/2" IRON PIPE W/2" OCS BRASS CAP STAMPED "GPS 1417 9-95" PER TRACT NO. 15884, M.M. 794/33-44 AND RECORDS ON FILE IN THE ORANGE COUNTY SURVEYORS OFFICE.

NO MONUMENTATION TO BE SET AT BC'S AND EC'S OF STREET RIGHT OF WAY LINES,
UNLESS OTHERWISE NOTED.

INST. NO. 19960587414, O. R.

NOTES:

BEARINGS, DISTANCES AND CURVE INFORMATION SHOWN
ALONG THE CENTERLINE OF ANTONIO PARKWAY ON OCS
GPS BOUNDARY CONTROL MAP ARE RECORD AND
MEASURED PER RECORD OF SURVEY 97-1086, R.S.B.
167/26-28, UNLESS OTHERWISE NOTED.

SEE SHEET 4 FOR SHEET INDEX MAP.



OCS GPS BOUNDARY CONTROL MAP

SHEET 4 OF 9 SHEETS

A PORTION OF VESTING TENTATIVE
TRACT NO. 16025

DATE OF SURVEY:
JANUARY 1999

TRACT NO. 16156
IN UNINCORPORATED TERRITORY OF ORANGE COUNTY, CALIFORNIA
DECEMBER 2000 JAMES F. GILLEN, L.S. 5557
HUITT-ZOLLARS
7 NUMBERED LOTS AND 27 LETTERED LOTS 71.991 ACRES

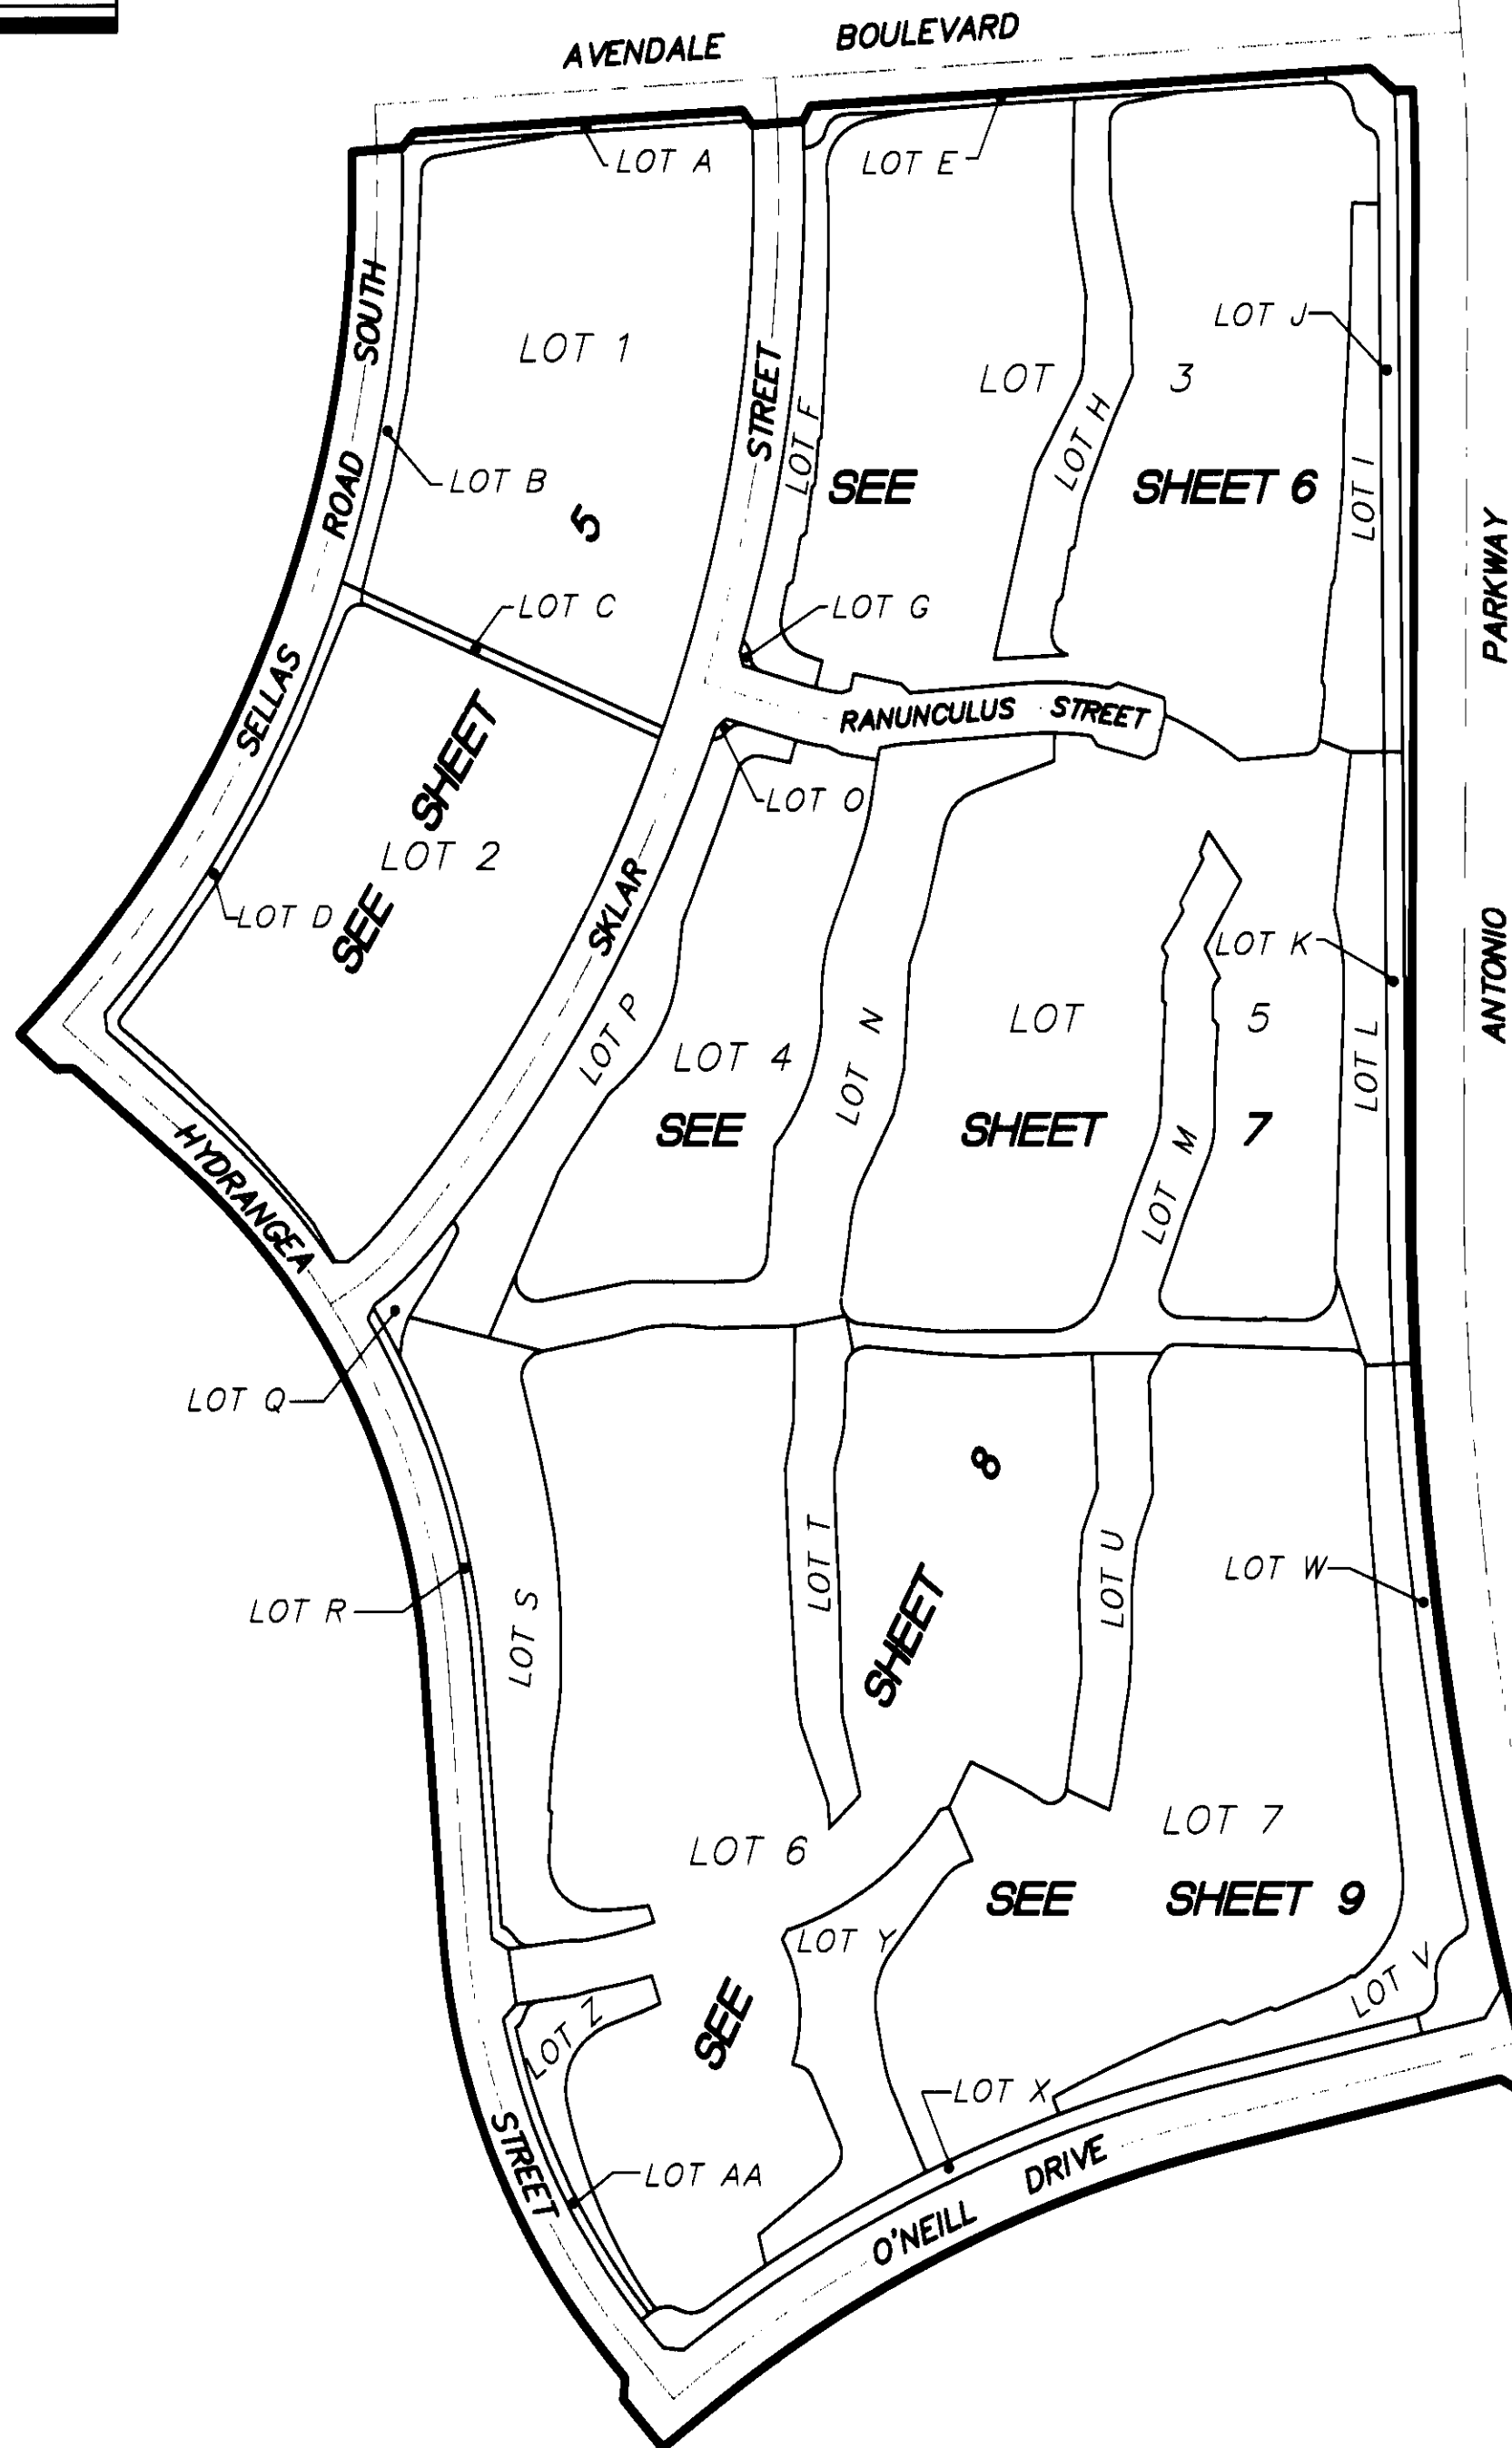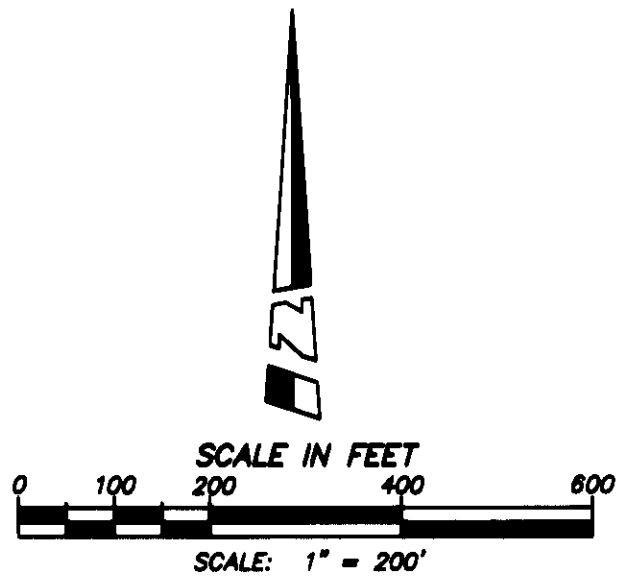

SHEET INDEX MAP

SHEET 5 OF 9 SHEETS

A PORTION OF VESTING
TENTATIVE TRACT NO. 16025DATE OF SURVEY:
JANUARY 1999

TRACT NO. 16156

IN UNINCORPORATED TERRITORY OF ORANGE COUNTY, CALIFORNIA


DECEMBER 2000

JAMES F. GILLEN, L.S. 5557

HUITT-ZOLLARS

7 NUMBERED LOTS AND 27 LETTERED LOTS

71.991 ACRES

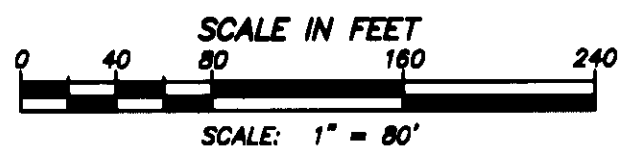

CURVE DATA (THIS SHEET ONLY)

- ① $\Delta = 87^{\circ}25'09''$ R = 10.00' L = 15.26'
- ② $\Delta = 92^{\circ}09'43''$ R = 20.00' L = 32.17'
- ③ $\Delta = 77^{\circ}26'54''$ R = 20.00' L = 27.03'
- ④ $\Delta = 0^{\circ}23'05''$ R = 1883.00' L = 12.64'
- ⑤ $\Delta = 18^{\circ}37'09''$ R = 300.00' L = 97.49'
- ⑥ $\Delta = 13^{\circ}22'20''$ R = 271.00' L = 63.25'
- ⑦ $\Delta = 28^{\circ}17'22''$ R = 892.00' L = 440.42'
- ⑧ $\Delta = 03^{\circ}02'20''$ R = 1479.00' L = 78.44'
- ⑨ $\Delta = 02^{\circ}53'51''$ R = 1479.00' L = 74.79'
- ⑩ $\Delta = 2^{\circ}03'22''$ R = 1450.00' L = 52.03'

COURSE DATA (THIS SHEET ONLY)

- 1 N38°30'14"E 22.30'
- 2 N38°30'14"E 16.21'
- 3 N38°30'14"E 6.09'
- 4 N33°47'07"W 19.96'
- 5 N33°47'07"W 13.86'
- 6 N33°47'07"W 6.10'
- 7 N57°46'38"E RAD 18.27'
- 8 N6°21'26"W 20.22'
- 9 N50°08'57"W RAD 9.75'
- 10 N65°40'04"W 25.50'
- 11 N41°30'00"E 10.75'
- 12 N03°44'00"W 7.75'
- 13 N27°07'14"E 19.49'
- 14 N52°56'28"W RAD 15.54'
- 15 N88°15'45"E RAD
- 16 N88°19'22"E RAD

NOTES:


SEE SHEET 2 FOR EASEMENT NOTES.

SEE SHEET 3 FOR BASIS OF BEARINGS, DATUM STATEMENT,
MONUMENT NOTES AND OCS GPS BOUNDARY CONTROL MAP.

SEE SHEET 4 FOR SHEET INDEX MAP.

LOTS A THROUGH AA ARE FOR LANDSCAPING AND OPEN SPACE
AND ARE NOT SEPARATE BUILDING SITES.

SEE SHEET 8

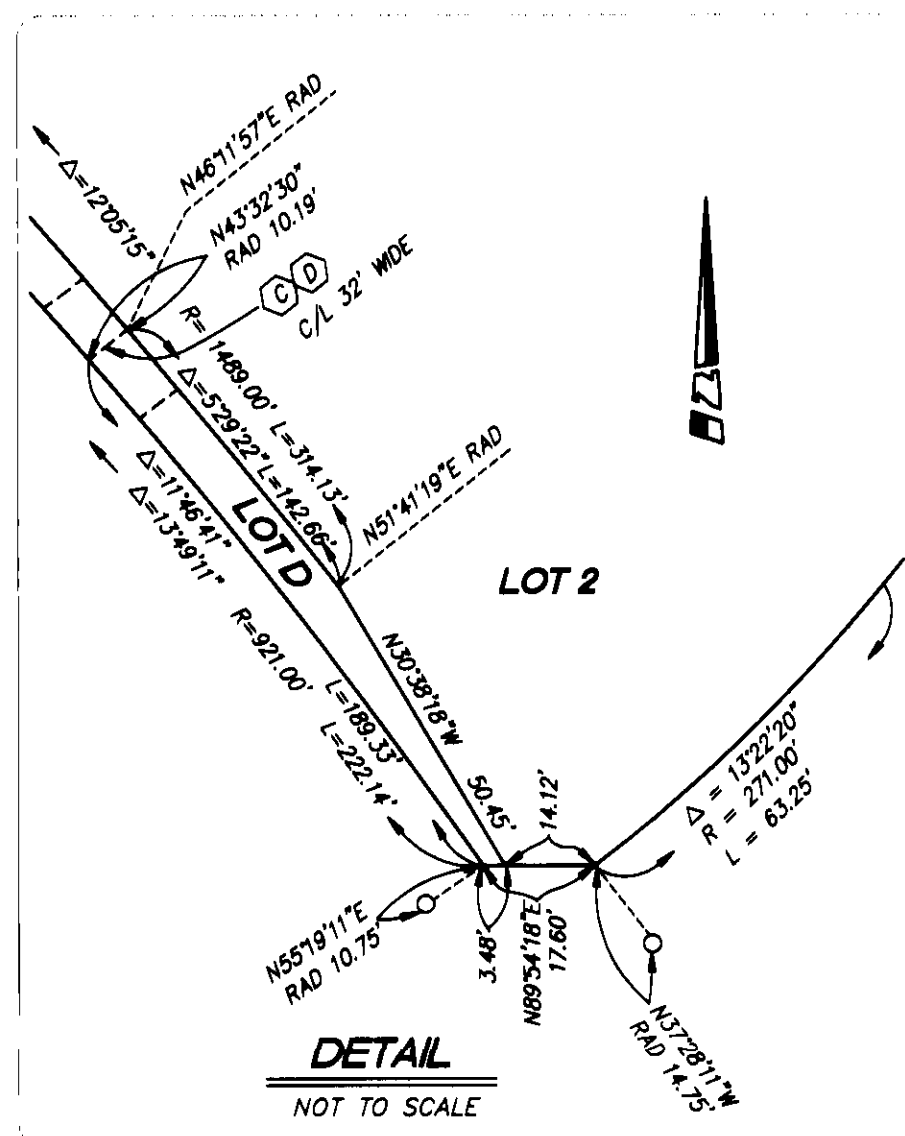

SHEET 6 OF 9 SHEETS

TRACT NO. 16156

IN UNINCORPORATED TERRITORY OF ORANGE COUNTY, CALIFORNIA

DECEMBER 2000

JAMES F. GILLEN, L.S. 5557

HUITT-ZOLLARS

7 NUMBERED LOTS AND 27 LETTERED LOTS

71.991 ACRES

A PORTION OF VESTING
TENTATIVE TRACT NO. 16025

DATE OF SURVEY:
JANUARY 1999

CURVE DATA (THIS SHEET ONLY)

- 1 $\Delta = 00^{\circ}24'06''$ R = 1941.00' L = 13.61'
- 2 $\Delta = 46^{\circ}44'12''$ R = 18.00' L = 14.68'
- 3 $\Delta = 63^{\circ}01'53''$ R = 18.00' L = 19.80'
- 4 $\Delta = 11^{\circ}15'19''$ R = 218.00' L = 42.82'
- 5 $\Delta = 03^{\circ}03'58''$ R = 218.00' L = 11.66'
- 6 $\Delta = 08^{\circ}11'21''$ R = 218.00' L = 31.16'
- 7 $\Delta = 00^{\circ}32'10''$ R = 2028.00' L = 18.98'
- 8 $\Delta = 79^{\circ}10'47''$ R = 25.00' L = 34.55'
- 9 $\Delta = 72^{\circ}32'33''$ R = 25.00' L = 31.65'
- 10 $\Delta = 00^{\circ}53'21''$ R = 1941.00' L = 30.12'
- 11 $\Delta = 77^{\circ}46'50''$ R = 25.00' L = 33.94'
- 12
- 13
- 14
- 15 $\Delta = 64^{\circ}02'53''$ R = 30.00' L = 33.54'
- 16 $\Delta = 66^{\circ}59'49''$ R = 15.00' L = 17.54'
- 17 $\Delta = 89^{\circ}20'48''$ R = 30.00' L = 46.78'
- 18 $\Delta = 00^{\circ}58'39''$ R = 2248.00' L = 38.35'
- 19 $\Delta = 1^{\circ}33'06''$ R = 2350.00' L = 63.64'

COURSE DATA (THIS SHEET ONLY)

- 1 N71°38'14"E 9.83'
- 2 N06°00'41"E RAD
- 3 N72°44'00"W 16.91'
- 4 N28°24'27"W 19.56'
- 5 N74°04'54"W RAD 10.75'
- 6 N74°28'00"W RAD (R=1941.00')
- 7 N33°33'41"E RAD (R=18.00')
- 8 N8°42'07"W 9.34'
- 9 N2°54'14"E RAD (R=25.00')
- 10 N88°40'59"E RAD (R=1941.00')
- 11 N76°16'33"W PRC
- 12 N27°07'14"E 19.49'
- 13 N03°44'00"W 12.00'
- 14 N21°33'55"E PRC
- 15 N85°36'48"E PRC
- 16 N88°33'44"E PRC
- 17 N17°16'00"E 10.75'
- 18 N3°44'00"W 7.75'
- 19 N87°08'47"E RAD 81.00'


NOTES:

SEE SHEET 2 FOR EASEMENT NOTES.


SEE SHEET 3 FOR BASIS OF BEARINGS, DATUM STATEMENT,
MONUMENT NOTES AND OCS GPS BOUNDARY CONTROL MAP.

SEE SHEET 4 FOR SHEET INDEX MAP.

LOTS A THROUGH AA ARE FOR LANDSCAPING AND OPEN SPACE
AND ARE NOT SEPARATE BUILDING SITES.

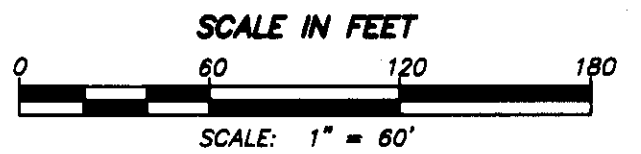

TRACT NO. 16155, M.M. 812 / 30 to 39

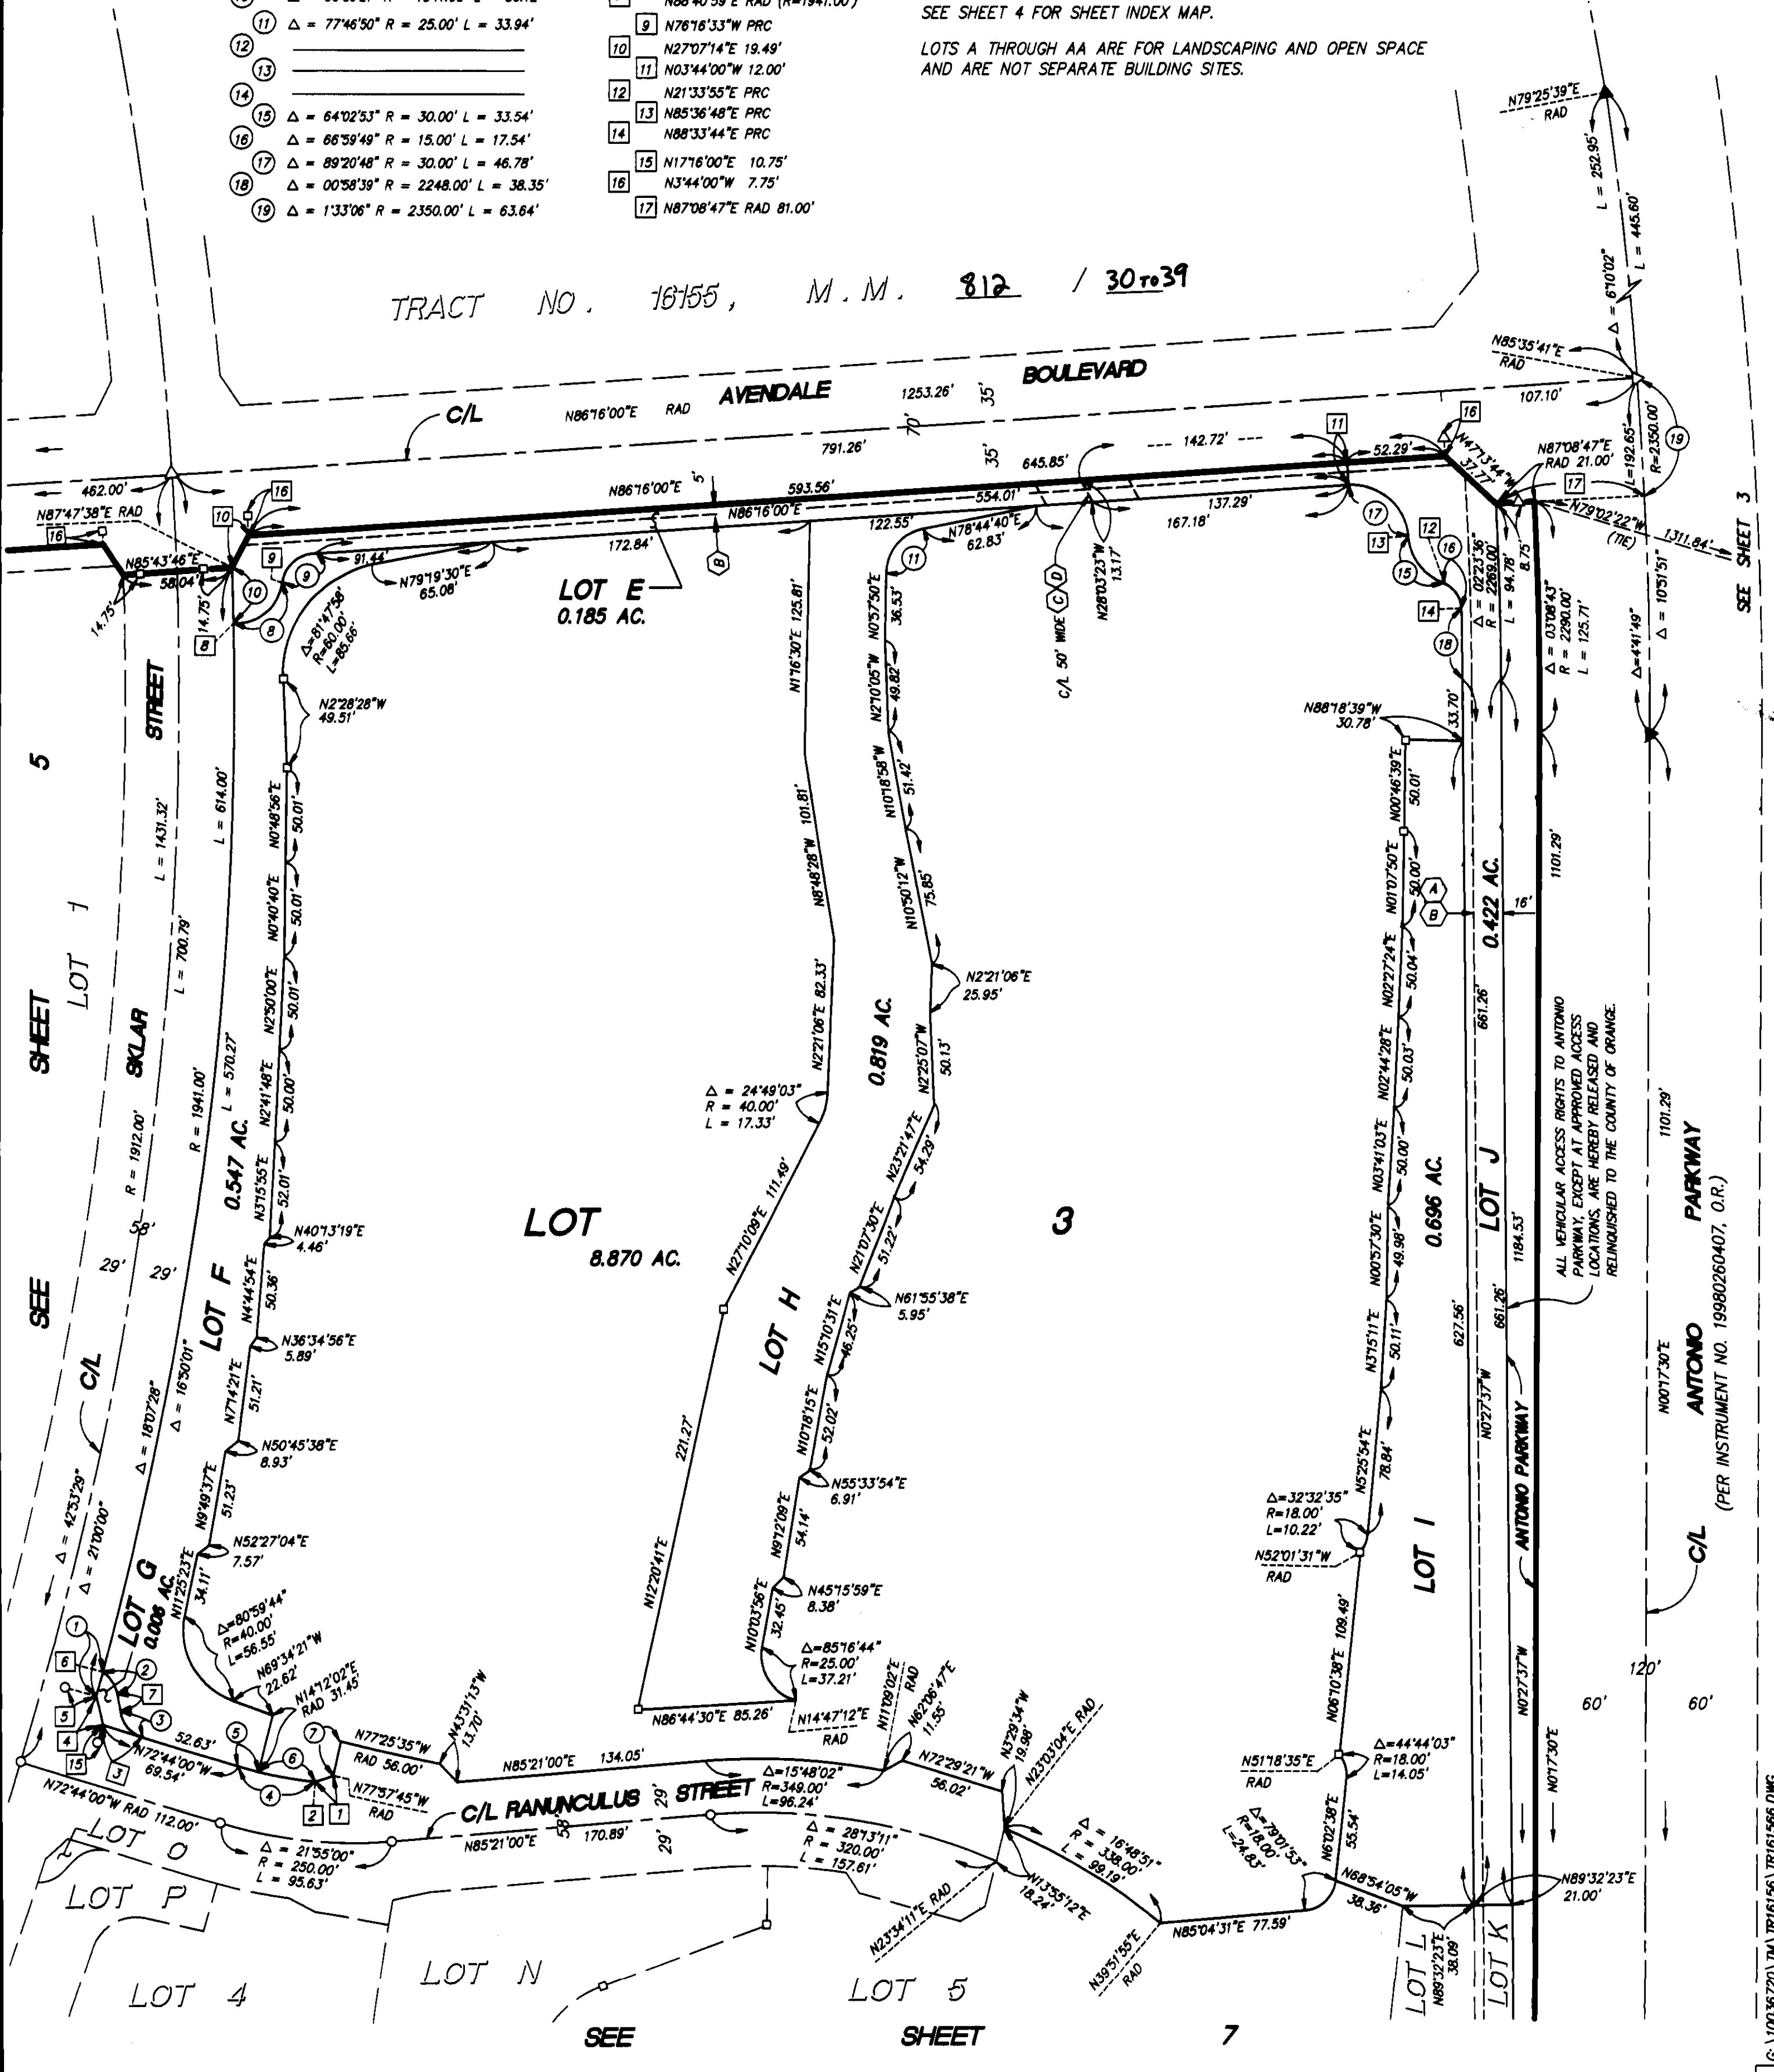

G:\10036\20\1M\1R16156\1R16156\1.DWG

SHEET 8 OF 9 SHEETS

TRACT NO. 16156

IN UNINCORPORATED TERRITORY OF ORANGE COUNTY, CALIFORNIA

DECEMBER 2000

JAMES F. GILLEN, L.S. 5557

A PORTION OF VESTING
TENTATIVE TRACT NO. 16025DATE OF SURVEY:
JANUARY 1999



HUITT-ZOLLARS

7 NUMBERED LOTS AND 27 LETTERED LOTS

71.991 ACRES

SEE SHEET 5

SEE SHEET 7

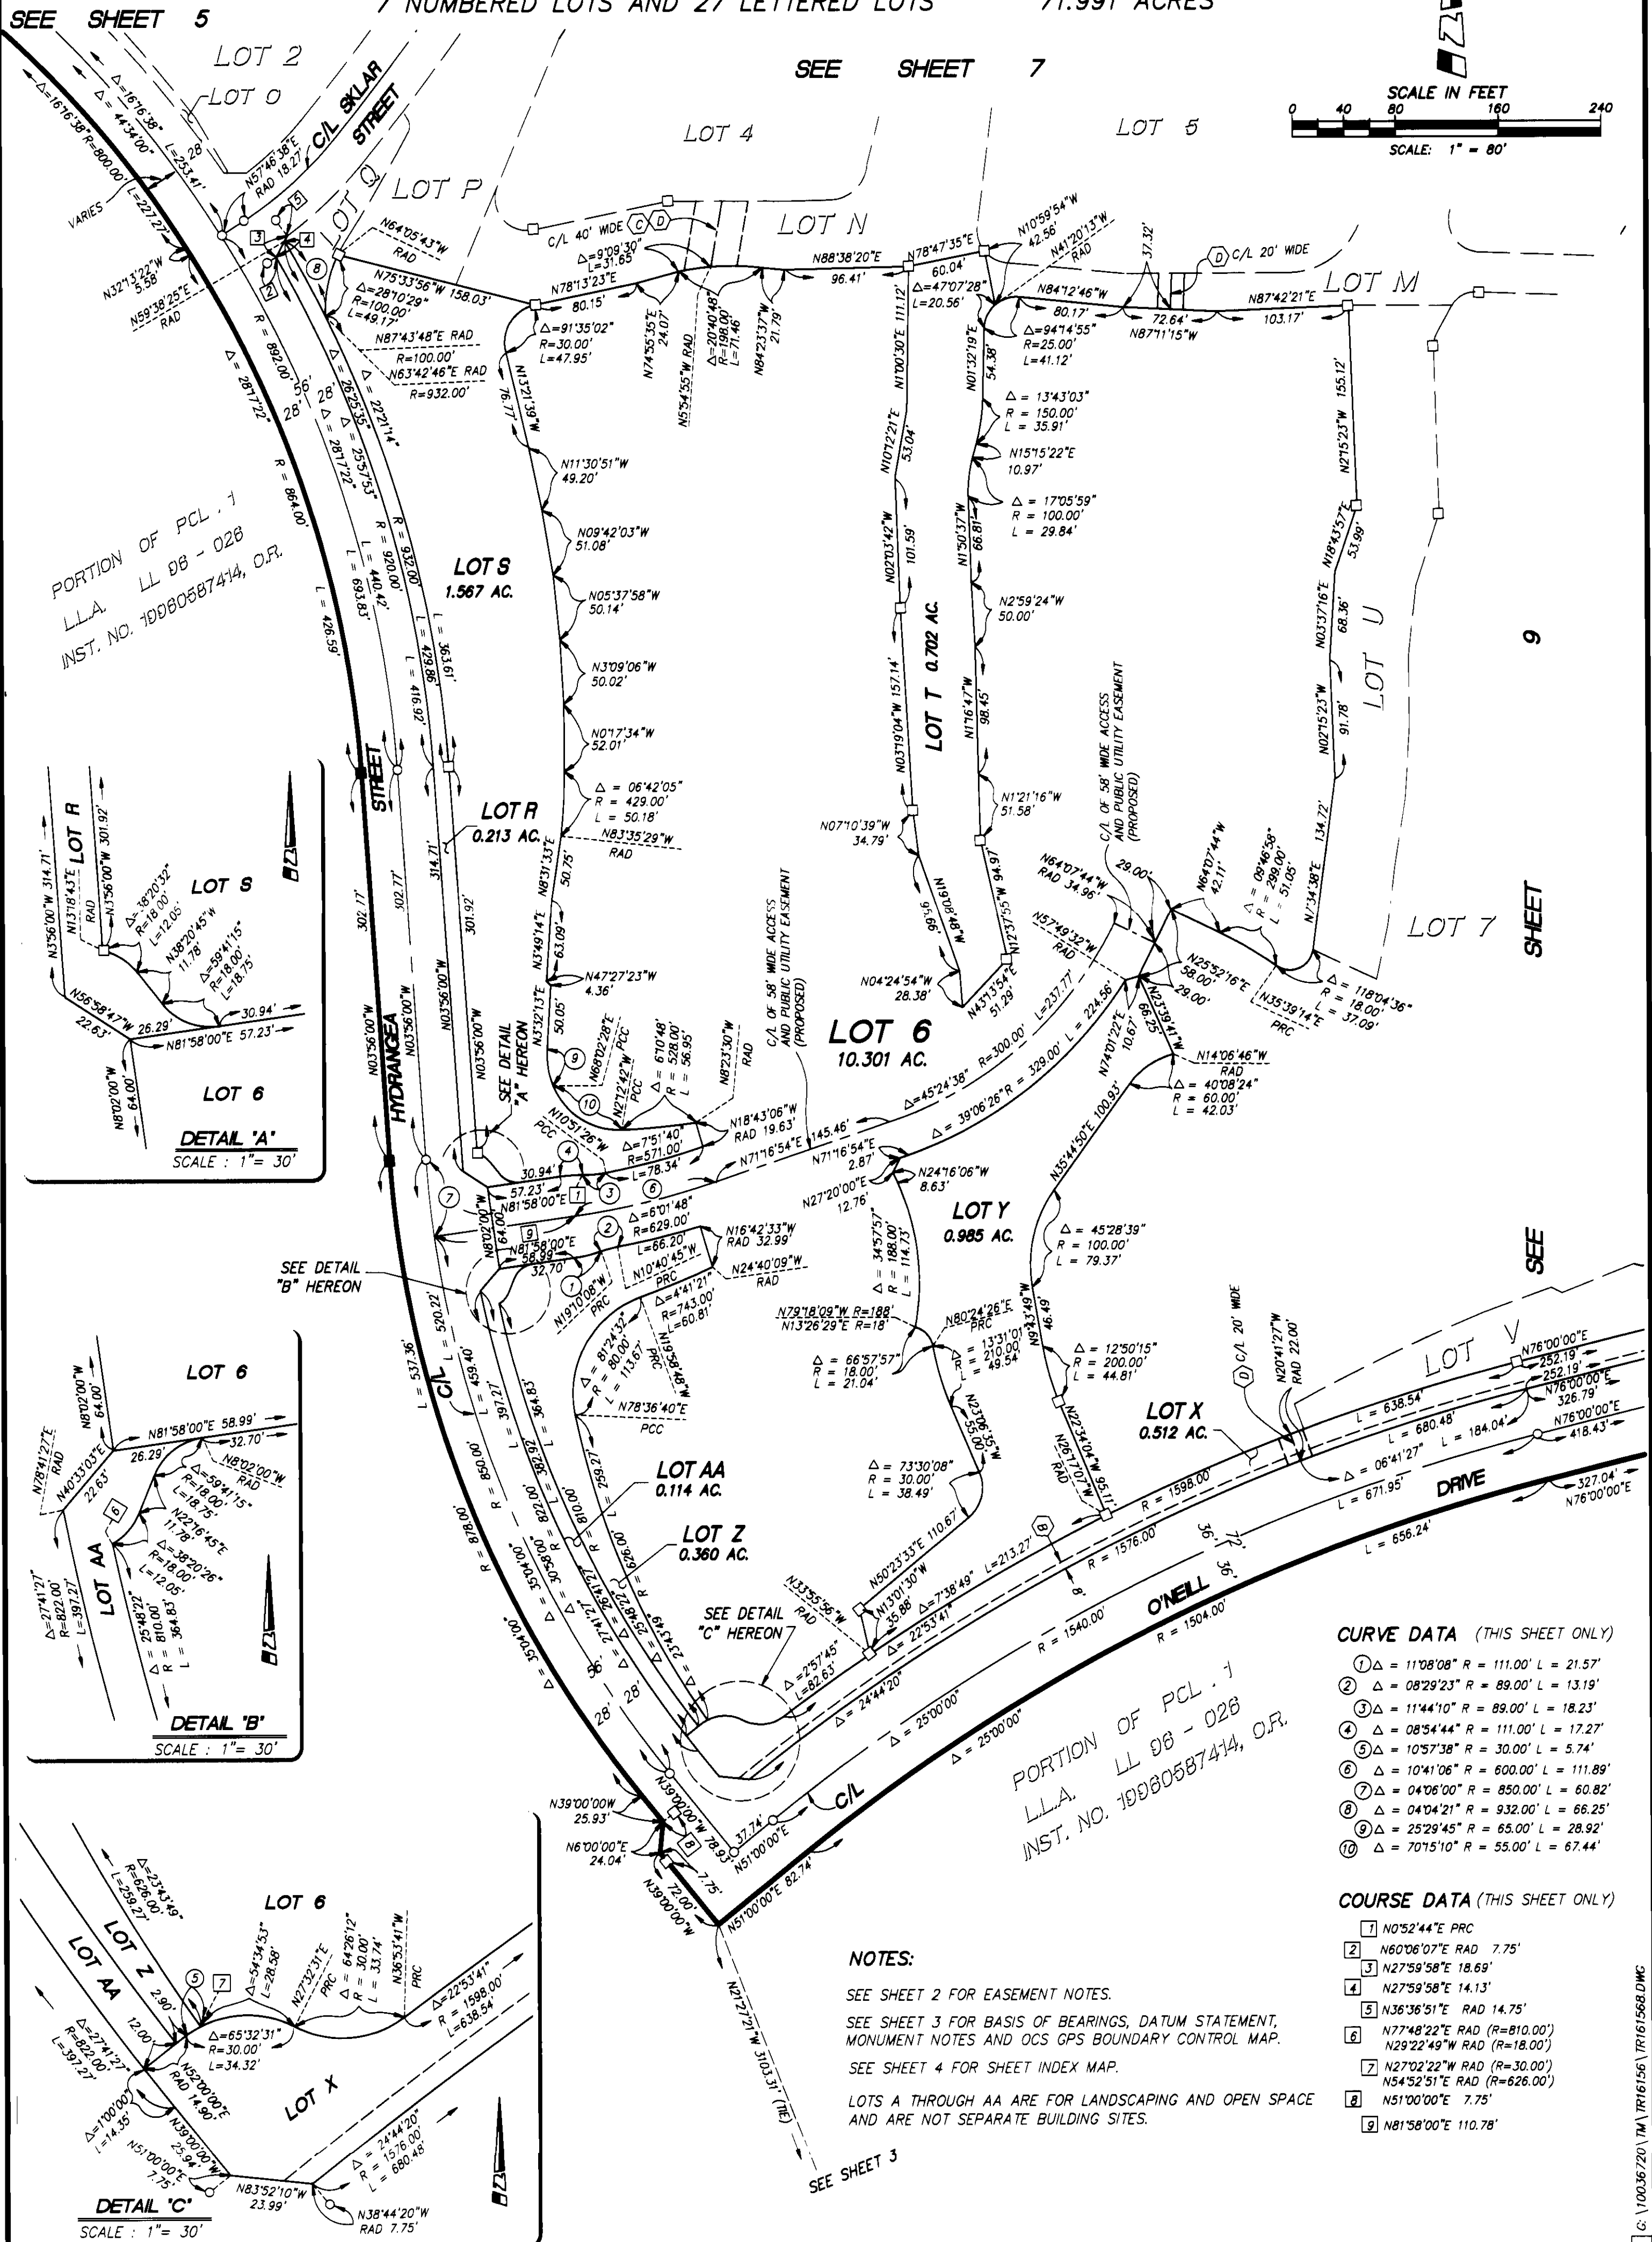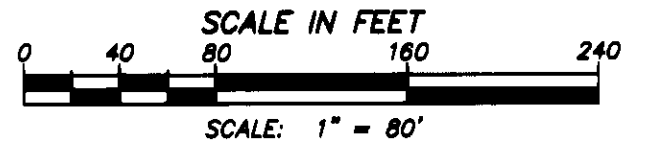

CURVE DATA (THIS SHEET ONLY)

- ① $\Delta = 111^{\circ}08'08''$ R = 111.00' L = 21.57'
- ② $\Delta = 08^{\circ}29'23''$ R = 89.00' L = 13.19'
- ③ $\Delta = 11^{\circ}44'10''$ R = 89.00' L = 18.23'
- ④ $\Delta = 08^{\circ}54'44''$ R = 111.00' L = 17.27'
- ⑤ $\Delta = 10^{\circ}57'38''$ R = 30.00' L = 5.74'
- ⑥ $\Delta = 10^{\circ}41'06''$ R = 600.00' L = 111.89'
- ⑦ $\Delta = 04^{\circ}06'00''$ R = 850.00' L = 60.82'
- ⑧ $\Delta = 04^{\circ}04'21''$ R = 932.00' L = 66.25'
- ⑨ $\Delta = 25^{\circ}28'45''$ R = 65.00' L = 28.92'
- ⑩ $\Delta = 70^{\circ}15'10''$ R = 55.00' L = 67.44'

COURSE DATA (THIS SHEET ONLY)

- ① N052'44"E PRC
- ② N60'06'07"E RAD 7.75'
- ③ N27'59'58"E 18.69'
- ④ N27'59'58"E 14.13'
- ⑤ N36'36'51"E RAD 14.75'
- ⑥ N77'48'22"E RAD (R=810.00')
- ⑦ N29'22'49"W RAD (R=18.00')
- ⑧ N27'02'22"W RAD (R=30.00')
- ⑨ N54'52'51"E RAD (R=626.00')
- ⑩ N51'00'00"E 7.75'
- ⑪ N81'58'00"E 110.78'

NOTES:

SEE SHEET 2 FOR EASEMENT NOTES.

SEE SHEET 3 FOR BASIS OF BEARINGS, DATUM STATEMENT,
MONUMENT NOTES AND OCS GPS BOUNDARY CONTROL MAP.

SEE SHEET 4 FOR SHEET INDEX MAP.

LOTS A THROUGH AA ARE FOR LANDSCAPING AND OPEN SPACE
AND ARE NOT SEPARATE BUILDING SITES.

SEE SHEET 3

PORTION OF PCL. 1
LLA. LL 98 - 028
INST. NO. 19980587414, O.R.

SHEET 9 OF 9 SHEETS

TRACT NO. 16156

IN UNINCORPORATED TERRITORY OF ORANGE COUNTY, CALIFORNIA



DECEMBER 2000

JAMES F. GILLEN, L.S. 5557

HUITT-ZOLIARS

7 NUMBERED LOTS AND 27 LETTERED LOTS

71.991 ACRES

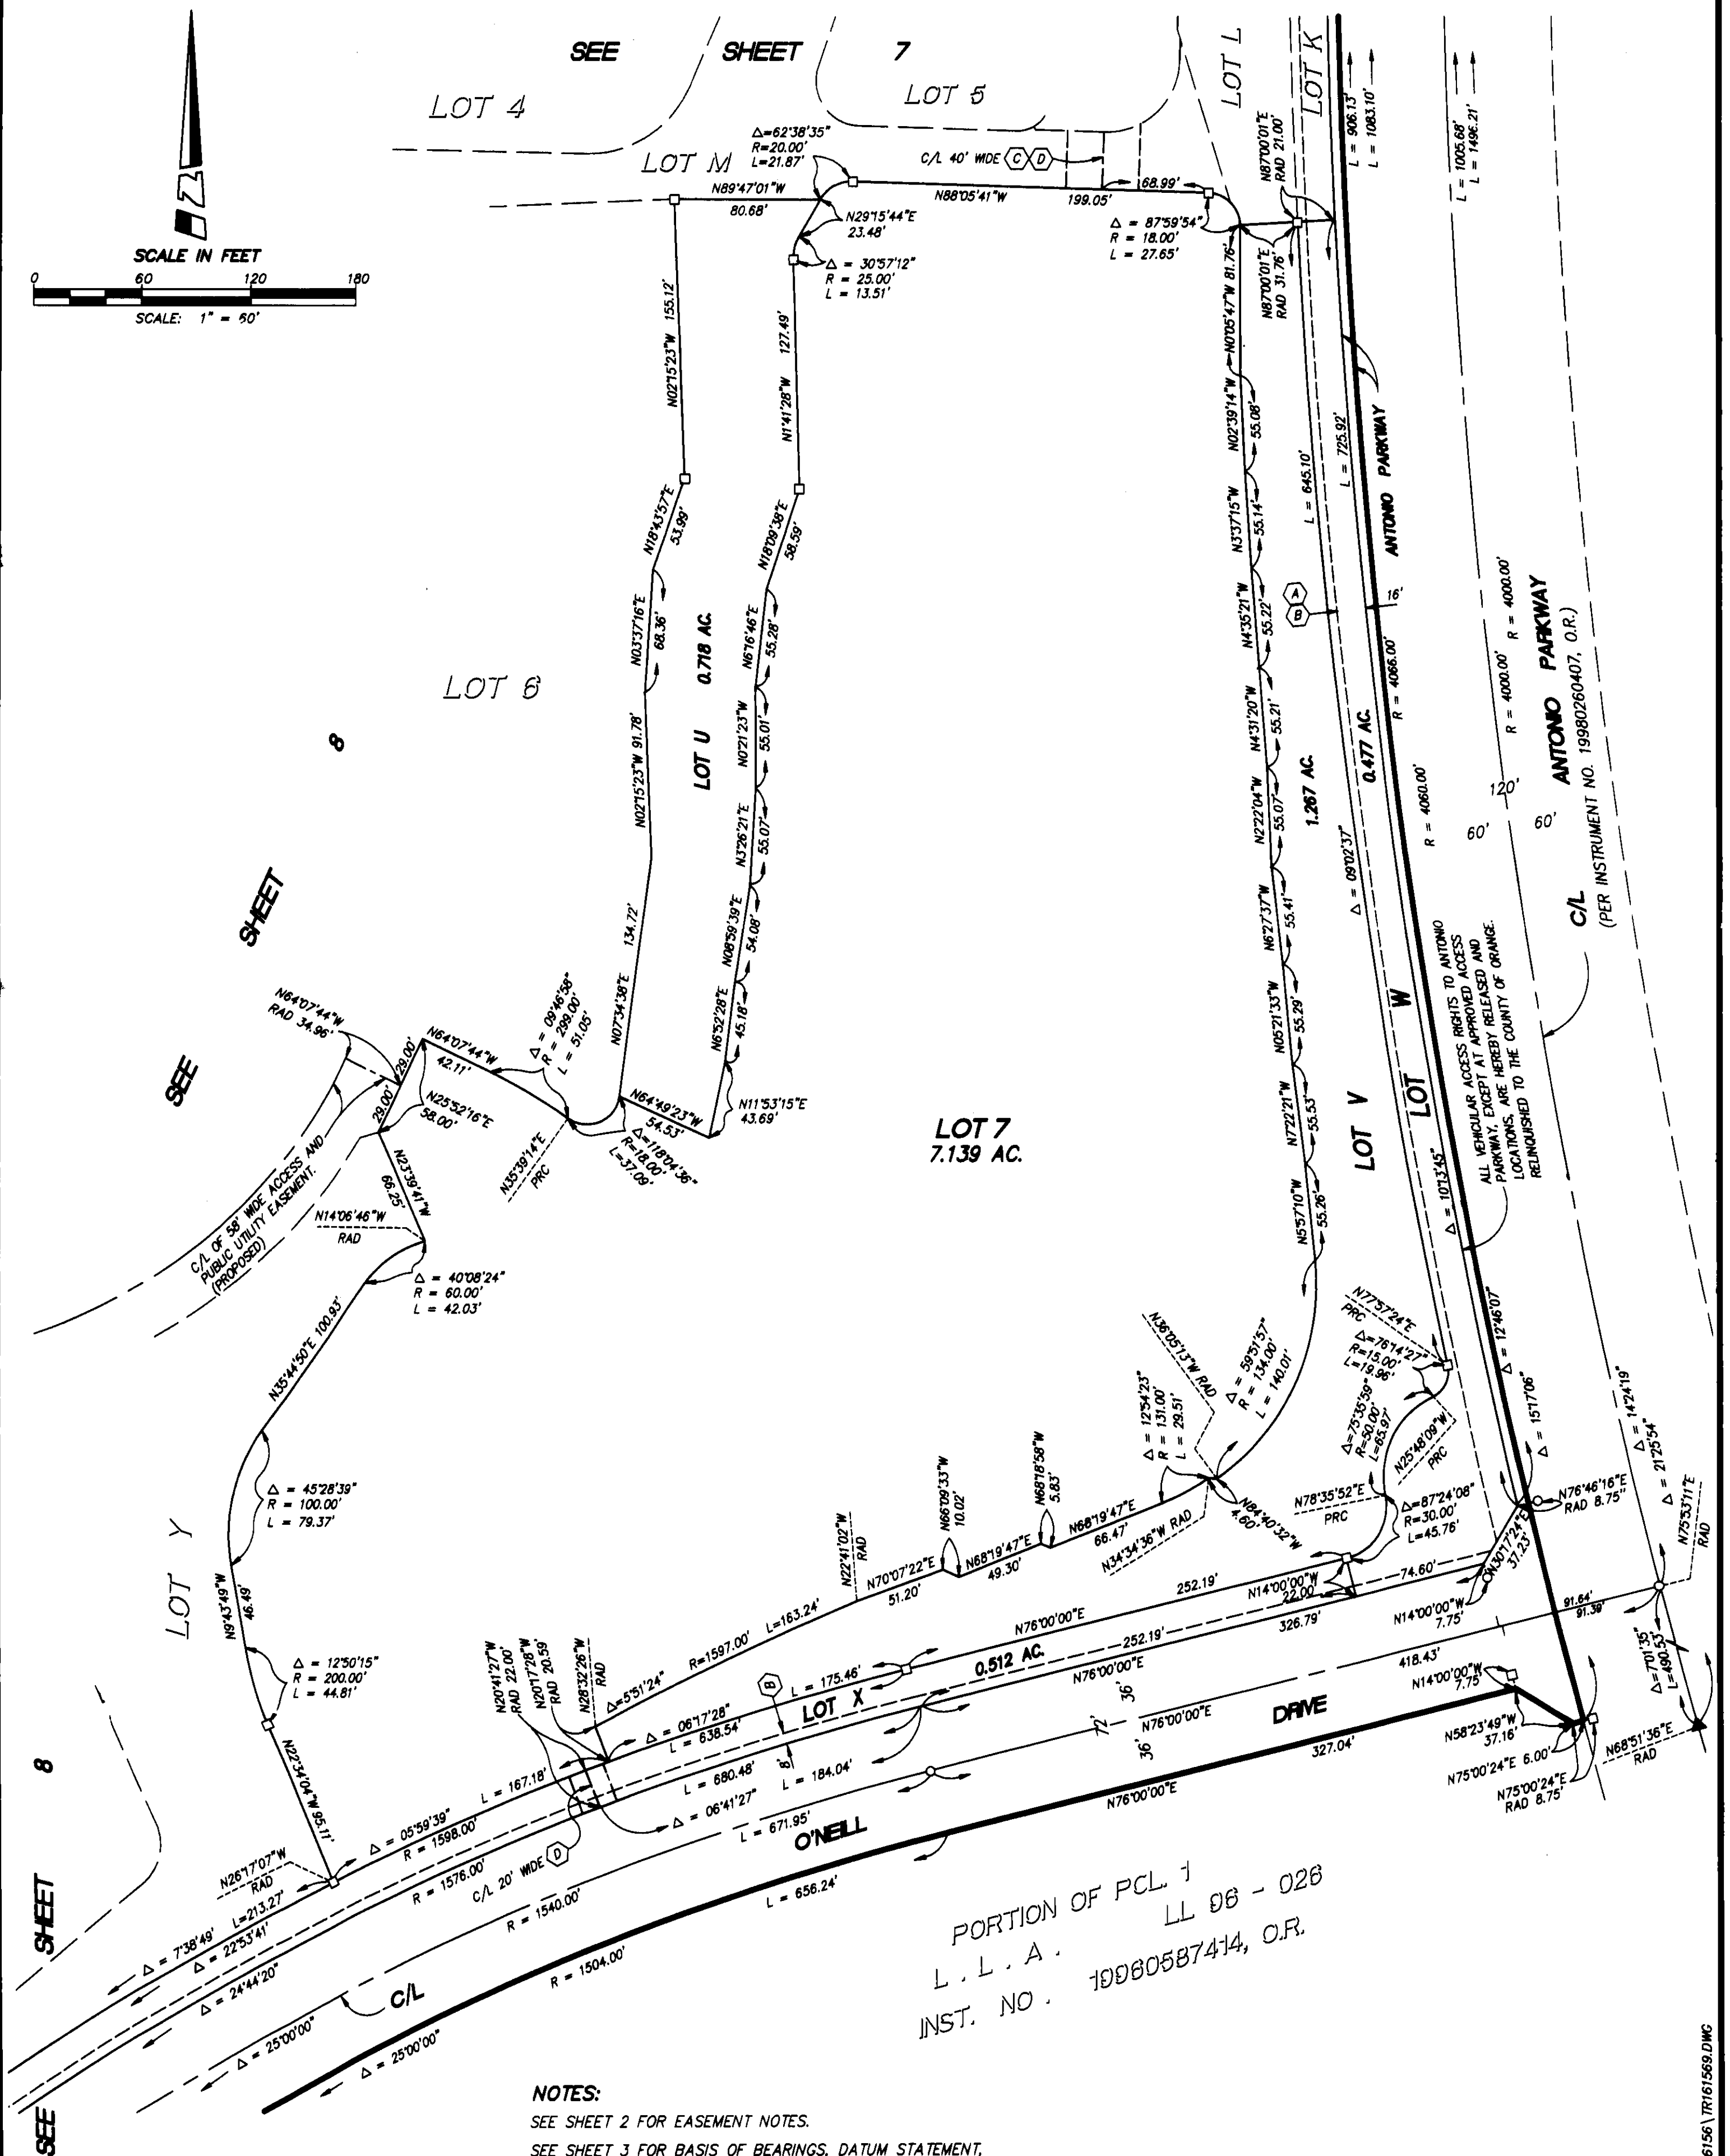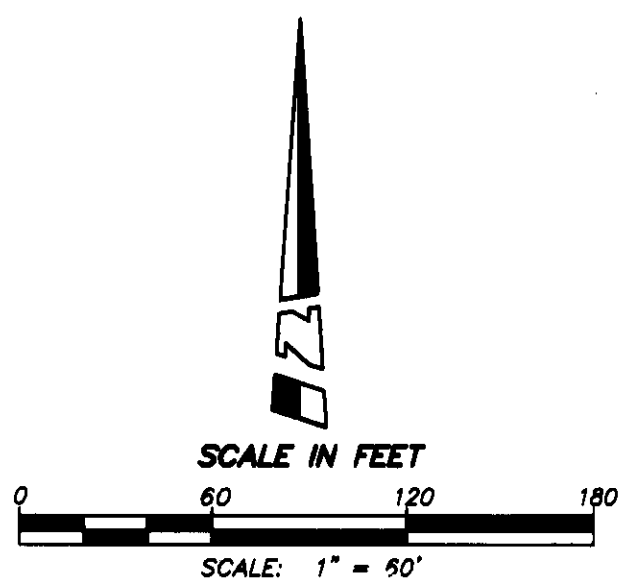A PORTION OF VESTING
TENTATIVE TRACT NO. 16025DATE OF SURVEY:
JANUARY 1999

NOTES:

SEE SHEET 2 FOR EASEMENT NOTES.

SEE SHEET 3 FOR BASIS OF BEARINGS, DATUM STATEMENT,
MONUMENT NOTES AND OCS GPS BOUNDARY CONTROL MAP.

SEE SHEET 4 FOR SHEET INDEX MAP.

LOTS A THROUGH AA ARE FOR LANDSCAPING AND OPEN SPACE
AND ARE NOT SEPARATE BUILDING SITES.

PORTION OF PCL 1
L.L.A.
INST. NO. 19960587414, O.R.
LL 06 - 026