

SHEET 1 OF 9 SHEETS

TRACT NO. 16157

A PORTION OF VESTING
TENTATIVE TRACT NO. 16025BLOCK MODULE
5157 19DATE OF SURVEY:
JANUARY 1999

IN UNINCORPORATED TERRITORY OF ORANGE COUNTY, CALIFORNIA
BEING A SUBDIVISION OF A PORTION OF PARCEL 1 OF LOT LINE ADJUSTMENT NO. LL 96-026
AS SHOWN ON EXHIBIT "B" ATTACHED TO THAT CERTAIN DOCUMENT RECORDED NOVEMBER 21,
1996 AS INSTRUMENT NO. 19960587414 OF OFFICIAL RECORDS, RECORDS OF ORANGE COUNTY,
CALIFORNIA.

OCTOBER 2000

JAMES F. GILLEN, L.S. 5557

HUITT-ZOLLARS

9 NUMBERED LOTS AND 15 LETTERED LOTS

69.655 ACRES

ACCEPTED AND FILED AT THE
REQUEST OF

FIRST AMERICAN TITLE INSURANCE CO.

DATE JANUARY 26, 2001

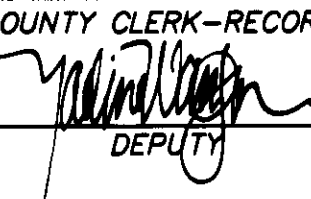
TIME 3:55 PM FEE \$ 23.00

INSTRUMENT NO. 20010047446

BOOK 813 PAGE 1-9 M/M

GARY L. GRANVILLE

COUNTY CLERK-RECORDER

BY  DEPUTY

OWNERSHIP CERTIFICATE:

WE, THE UNDERSIGNED, BEING ALL PARTIES HAVING ANY RECORD TITLE INTEREST IN THE
LAND COVERED BY THIS MAP, DO HEREBY CONSENT TO THE PREPARATION AND RECORDATION
OF SAID MAP, AS SHOWN WITHIN THE DISTINCTIVE BORDER LINE. WE ALSO HEREBY DEDICATE
TO THE PUBLIC FOR STREET PURPOSES: SIENNA PARKWAY, AVENDALE BOULEVARD, DAISY STREET NORTH,
GILLYFLOWER STREET, ZINNIA STREET, STRAWFLOWER STREET, ABELIA STREET, TRISTANIA STREET,
~~SELLAS ROAD NORTH, SELLAS ROAD SOUTH, AND DAISY STREET SOUTH.~~

WE ALSO HEREBY DEDICATE TO THE COUNTY OF ORANGE:

- (1) THE EASEMENTS FOR SIDEWALK PURPOSES AS SHOWN ON SAID MAP.
- (2) THE EASEMENTS FOR STORM DRAIN PURPOSES AS SHOWN ON SAID MAP.

WE ALSO HEREBY RELEASE AND RELINQUISH TO THE COUNTY OF ORANGE ALL VEHICULAR
ACCESS RIGHTS TO SIENNA PARKWAY, EXCEPT AT APPROVED ACCESS LOCATIONS.

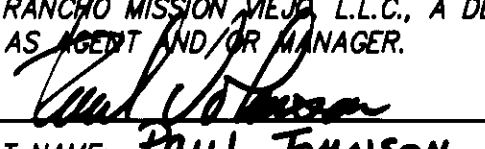
~~PURSUANT TO SECTION 7050 OF THE GOVERNMENT CODE, WE HEREBY IRREVOCABLY~~
~~OFFER TO DEDICATE TO THE COUNTY OF ORANGE AN EASEMENT OVER LOT 4 FOR~~
PRIVATE LOCAL PARK PURPOSES, SUBJECT TO THE SAME TERMS AND CONDITIONS AS
THAT CERTAIN DOCUMENT RECORDED OCTOBER 7, 1987 AS INSTRUMENT NO. 87-563594,
OF OFFICIAL RECORDS, COUNTY OF ORANGE.

PURSUANT TO SECTION 7050 OF THE GOVERNMENT CODE, WE HEREBY IRREVOCABLY
OFFER TO DEDICATE TO THE COUNTY OF ORANGE LOT 3 IN FEE SIMPLE FOR ~~REGIONAL~~ LOCAL
PARK PURPOSES, TOGETHER WITH THE RIGHT TO GRANT EASEMENTS FOR PUBLIC UTILITIES
OR OTHER ESSENTIAL PURPOSES.

WE ALSO HEREBY DEDICATE TO THE SANTA MARGARITA WATER DISTRICT THE EASEMENTS FOR
SEWER, WATER AND ACCESS PURPOSES AS SHOWN ON SAID MAP, WHICH EASEMENTS SHALL BE
SUBJECT TO THE SAME TERMS AND CONDITIONS AS ARE SHOWN IN THAT CERTAIN EASEMENT
RECORDED OCTOBER 6, 1980 IN BOOK 13776, PAGE 341, OF OFFICIAL RECORDS, COUNTY OF ORANGE.
THE SANTA MARGARITA WATER DISTRICT SHALL RESTORE OTHER IMPROVEMENTS OR FACILITIES
LOCATED WITHIN THE EASEMENT, IF IT HAS CONSENTED TO THE LOCATION OF SUCH IMPROVEMENTS
OR FACILITIES TO THE EXTENT THAT THE EXERCISE OF ITS RIGHTS IN CONNECTION WITH THE EASEMENT
IMPACTS OTHER IMPROVEMENTS OR FACILITIES LOCATED WITHIN THE EASEMENT, HOWEVER, IN NO EVENT
SHALL SANTA MARGARITA WATER DISTRICT BE RESPONSIBLE FOR THE COST OF RELOCATING ITS FACILITIES
IN THE EVENT OF CONFLICTS WITH SUCH OTHER IMPROVEMENTS OR FACILITIES.

DMB LADERA, L.L.C., A DELAWARE LIMITED LIABILITY COMPANY.

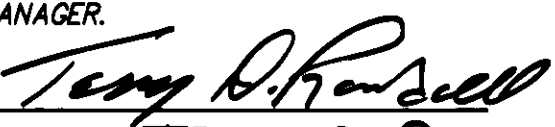
BY: RANCHO MISSION MEJO, L.L.C., A DELAWARE LIMITED LIABILITY COMPANY,
AS AGENT AND/OR MANAGER.

BY: 
PRINT NAME: PAUL JOHNSON
PRINT TITLE: VP. COMMUNITY DEV.

BY: 
PRINT NAME: Stephen C. Schrank
PRINT TITLE: EXECUTIVE VICE PRESIDENT

DMB CONSOLIDATED HOLDINGS, L.L.C., AN ARIZONA LIMITED LIABILITY COMPANY,
BENEFICIARY UNDER DEEDS OF TRUSTS RECORDED DECEMBER 10, 1996 AS INSTRUMENT
NO. 19960624030, AND RECORDED APRIL 20, 1999 AS INSTRUMENT NO. 19990288616,
BOTH OF OFFICIAL RECORDS.

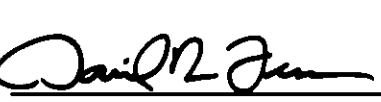
BY: DMB ASSOCIATES, INC., AN ARIZONA CORPORATION,
AS MANAGER.

BY: 
PRINT NAME: TERRY P. RANDALL
PRINT TITLE: VICE PRESIDENT

BY: 
PRINT NAME: Timothy A. Kraemer
PRINT TITLE: President / C.E.O.

CERTIFICATE OF ACCEPTANCE

THE UNDERSIGNED, BEING THE DULY APPOINTED AGENT OF THE SANTA MARGARITA WATER
DISTRICT, A PUBLIC CORPORATION OF ORANGE COUNTY, CALIFORNIA, PURSUANT TO ITS
RESOLUTION NO. 88-10-2, DOES HEREBY ACCEPT ON BEHALF OF SAID DISTRICT THE EASEMENTS
FOR SEWER, WATER AND ACCESS PURPOSES, AS DEDICATED AND AS SHOWN ON THIS TRACT MAP,
BY AND BETWEEN THE SANTA MARGARITA WATER DISTRICT AND DMB LADERA, L.L.C., AND
DOES HEREBY CERTIFY THAT THE GRANTEE CONSENTS TO THE RECORDATION OF SAID TRACT.


DANIEL R. FERONS, CHIEF ENGINEER
SANTA MARGARITA WATER DISTRICT.

AUTOMATIC FIRE SPRINKLER NOTE:

ALL COMMERCIAL STRUCTURES GREATER THAN 6,000 SQUARE FEET; ALL MULTIFAMILY RESIDENTIAL
STRUCTURES; ALL SINGLE-FAMILY STRUCTURES EXCEEDING 5,500 SQUARE FEET, AND ALL STRUCTURES
EXCEEDING FIRE DEPARTMENT ACCESS REQUIREMENTS SHALL BE PROTECTED BY AN AUTOMATIC
SPRINKLER SYSTEM.

SPECIAL FIRE PROTECTION NOTE:

~~PROPOSED DEVELOPMENT IS EXCLUDED FROM A SPECIAL FIRE PROTECTION AREA AND MUST MEET ALL REQUIREMENTS~~
~~FOR DEVELOPMENT WITHIN THE AREA.~~
PROPERTY IS TOTALLY EXCLUDED FROM A SPECIAL FIRE PROTECTION AREA.

HIGH FIRE HAZARD AREA NOTE:

THE LOTS SHOWN ON THIS MAP ARE IN A HIGH FIRE HAZARD AREA DUE TO
WILD LAND EXPOSURE.

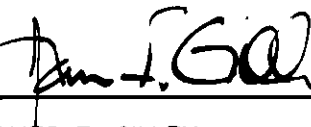
NOTE:

SEE SHEET 2 FOR NOTARY ACKNOWLEDGMENTS AND SIGNATURE OMISSIONS.

SURVEYOR'S STATEMENT:

I HEREBY STATE THAT THIS MAP CONSISTING OF 9 SHEETS, CORRECTLY REPRESENTS A TRUE AND
COMPLETE SURVEY AS SHOWN MADE IN JANUARY, 1999; WAS MADE BY ME OR UNDER MY DIRECTION;
THAT THE MONUMENTS ARE OF THE CHARACTER AND OCCUPY OR WILL OCCUPY THE POSITIONS
INDICATED BY SAID MAP; AND THAT SAID MONUMENTS WILL BE SUFFICIENT TO ENABLE THE
SURVEY TO BE RETRACED.

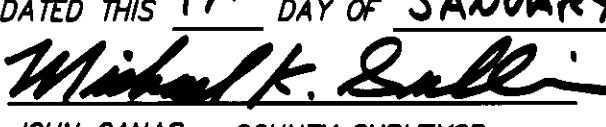


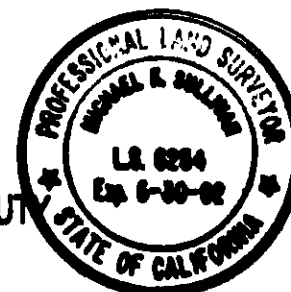

JAMES F. GILLEN
L.S. 5557
EXPIRATION DATE: 9/30/01

COUNTY SURVEYOR'S STATEMENT:

I HEREBY STATE THAT I HAVE EXAMINED THIS MAP AND HAVE FOUND IT TO BE
SUBSTANTIALLY IN CONFORMANCE WITH THE TENTATIVE MAP AS FILED WITH, AMENDED AND
APPROVED BY THE ORANGE COUNTY SUBDIVISION COMMITTEE; THAT ALL PROVISIONS OF THE
SUBDIVISION MAP ACT AND COUNTY SUBDIVISION REGULATIONS HAVE BEEN COMPLIED WITH
AND I AM SATISFIED SAID MAP IS TECHNICALLY CORRECT.

DATED THIS 17TH DAY OF JANUARY, 2001.


JOHN CANAS, COUNTY SURVEYOR
PLS 4408, EXPIRATION DATE: 9/30/01

BY: MICHAEL K. SULLIVAN, DEPUTY
L.S. 6254 EXPIRES 6-30-02

COUNTY TREASURER-TAX COLLECTOR'S CERTIFICATE:

STATE OF CALIFORNIA)
COUNTY OF ORANGE)

I HEREBY CERTIFY THAT ACCORDING TO THE RECORDS OF MY OFFICE THERE ARE NO LIENS
AGAINST THE LAND COVERED BY THIS MAP OR ANY PART THEREOF FOR UNPAID STATE,
COUNTY, MUNICIPAL OR LOCAL TAXES OR SPECIAL ASSESSMENTS COLLECTED AS TAXES,
EXCEPT TAXES OR SPECIAL ASSESSMENTS COLLECTED AS TAXES NOT YET PAYABLE.

AND DO ALSO HEREBY CERTIFY TO THE RECORDER OF ORANGE COUNTY THAT THE PROVISIONS
OF THE SUBDIVISION MAP ACT HAVE BEEN COMPLIED WITH REGARDING DEPOSITS TO SECURE
THE PAYMENT OF TAXES OR SPECIAL ASSESSMENTS COLLECTED AS TAXES ON THE LAND
COVERED BY THIS MAP.

DATED THIS 12 DAY OF JANUARY, 2001

JOHN M.W. MOORLACH
COUNTY TREASURER-TAX COLLECTOR

BY: 
DEPUTY TREASURER-TAX COLLECTOR

CLERK OF THE BOARD OF SUPERVISORS' CERTIFICATE:

STATE OF CALIFORNIA)
COUNTY OF ORANGE)

I HEREBY CERTIFY THAT THIS MAP WAS PRESENTED FOR APPROVAL TO THE BOARD OF
SUPERVISORS OF ORANGE COUNTY AT A REGULAR MEETING THEREOF HELD ON THE 3rd DAY
OF January, 2001, AND THAT THEREUPON SAID BOARD DID, BY AN ORDER DULY PASSED
AND ENTERED, APPROVE SAID MAP AND DID ACCEPT ON BEHALF OF THE PUBLIC, SUBJECT TO
IMPROVEMENTS: THE DEDICATION FOR STREET PURPOSES OF: SIENNA PARKWAY, AVENDALE BOULEVARD,
DAISY STREET NORTH, GILLYFLOWER STREET, ZINNIA STREET, STRAWFLOWER STREET, ABELIA STREET, TRISTANIA
STREET, ~~AND SELLAS ROAD NORTH, SELLAS ROAD SOUTH, DAISY STREET NORTH, AND~~
DAISY STREET SOUTH.

AND DID ALSO ACCEPT ON BEHALF OF THE COUNTY OF ORANGE:

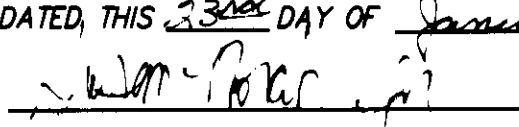
1. THE EASEMENTS FOR SIDEWALK PURPOSES AS DEDICATED.
2. THE EASEMENTS FOR STORM DRAIN PURPOSES AS DEDICATED.
3. THE VEHICULAR ACCESS RIGHTS TO SIENNA PARKWAY AS RELEASED AND RELINQUISHED.

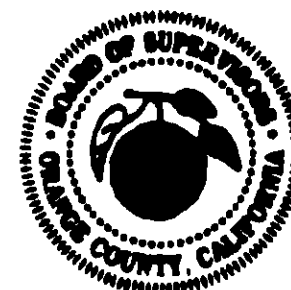
AND DID ~~NOT~~ ACCEPT THE IRREVOCABLE OFFER OF AN EASEMENT OVER LOT 4 FOR PRIVATE LOCAL
PARK PURPOSES AS DEDICATED.

AND DID NOT ACCEPT THE IRREVOCABLE OFFER OF: LOT 3 FOR LOCAL PARK PURPOSES
AS DEDICATED.

AND DID ALSO APPROVE SUBJECT MAP PURSUANT TO THE PROVISIONS OF SECTION
66436 (a)(3) OF SUBDIVISION MAP ACT.

DATED, THIS 23rd DAY OF January, 2001.


DARLENE J. BLOOM
CLERK OF THE BOARD OF SUPERVISORS



SHEET 2 OF 9 SHEETS

TRACT NO. 16157

A PORTION OF VESTING
TENTATIVE TRACT NO. 16025

IN UNINCORPORATED TERRITORY OF ORANGE COUNTY, CALIFORNIA

DATE OF SURVEY:
JANUARY 1999

OCTOBER 2000

JAMES F. GILLEN, L.S. 5557

HUITT-ZOLIARS

9 NUMBERED LOTS AND 15 LETTERED LOTS

69.655 ACRES

DMB LADERA, L.L.C.

STATE OF CALIFORNIA)
COUNTY OF ORANGE)SS

ON THIS 7th DAY OF December, 2000, BEFORE ME,
JEANNINE CARTA HANSON, A NOTARY PUBLIC IN AND FOR SAID STATE,
 PERSONALLY APPEARED TERREY D. RANDALL AND PAUL JOHNSON
STEVE C. Schrank, PERSONALLY KNOWN TO ME OR PROVED TO ME
 ON THE BASIS OF SATISFACTORY EVIDENCE TO BE THE PERSONS WHOSE NAMES
 ARE SUBSCRIBED TO THE WITHIN INSTRUMENT AND ACKNOWLEDGED TO ME THAT
 THEY EXECUTED THE SAME IN THEIR AUTHORIZED CAPACITIES, AND THAT BY THEIR
 SIGNATURES ON THE INSTRUMENT THE PERSONS, OR THE ENTITY UPON BEHALF
 OF WHICH THE PERSONS ACTED, EXECUTED THE INSTRUMENT.

WITNESS MY HAND: MY COMMISSION EXPIRES Feb. 25, 2003
Jeannine Carta Hanson MY PRINCIPAL PLACE OF BUSINESS
 NOTARY PUBLIC IN AND FOR SAID STATE IS IN ORANGE COUNTY.

JEANNINE CARTA HANSON
 PRINT NAME

DMB CONSOLIDATED HOLDINGS, L.L.C.

STATE OF CALIFORNIA)
COUNTY OF ORANGE)SS

ON THIS 7th DAY OF December, 2000, BEFORE ME,
Jeannine Carta Hanson, A NOTARY PUBLIC IN AND FOR SAID STATE,
 PERSONALLY APPEARED Terry D. Randall PERSONALLY KNOWN TO ME
 OR PROVED TO ME ON THE BASIS OF SATISFACTORY EVIDENCE TO BE THE
 PERSON WHOSE NAME IS SUBSCRIBED TO THE WITHIN INSTRUMENT AND ACKNOWLEDGED
 TO ME THAT HE EXECUTED THE SAME IN HIS AUTHORIZED CAPACITY, AND THAT
 BY HIS SIGNATURE ON THE INSTRUMENT THE PERSON, OR THE ENTITY UPON BEHALF
 OF WHICH THE PERSON ACTED, EXECUTED THE INSTRUMENT, AS BENEFICIARY.

WITNESS MY HAND: MY COMMISSION EXPIRES Feb. 25, 2003
Jeannine Carta Hanson MY PRINCIPAL PLACE OF BUSINESS
 NOTARY PUBLIC IN AND FOR SAID STATE IS IN ORANGE COUNTY.

JEANNINE CARTA HANSON
 PRINT NAME

SANTA MARGARITA WATER DISTRICT

STATE OF CALIFORNIA)
COUNTY OF ORANGE)SS

ON THIS 22nd DAY OF December, 2000, BEFORE ME,
Lupe Martinez, A NOTARY PUBLIC IN AND FOR SAID STATE,
 PERSONALLY APPEARED DANIEL R. FERONS PERSONALLY KNOWN TO ME
 OR PROVED TO ME ON THE BASIS OF SATISFACTORY EVIDENCE TO BE THE
 PERSON WHOSE NAME IS SUBSCRIBED TO THE WITHIN INSTRUMENT AND ACKNOWLEDGED
 TO ME THAT HE EXECUTED THE SAME IN HIS AUTHORIZED CAPACITY, AND THAT
 BY HIS SIGNATURE ON THE INSTRUMENT THE PERSON, OR THE ENTITY UPON BEHALF
 OF WHICH THE PERSON ACTED, EXECUTED THE INSTRUMENT.

WITNESS MY HAND: MY COMMISSION EXPIRES 9-13-2002
Lupe Martinez MY PRINCIPAL PLACE OF BUSINESS
 NOTARY PUBLIC IN AND FOR SAID STATE IS IN Orange COUNTY.

Lupe Martinez
 PRINT NAME

SIGNATURE OMISSIONS:

IN ACCORDANCE WITH THE PROVISIONS OF SECTION 66436(a) (3) OF THE SUBDIVISION
MAP ACT, THE FOLLOWING SIGNATURE HAS BEEN OMITTED:

1. LADERA DEVELOPMENT COMPANY, L.L.C., HOLDER OF OIL, GAS, MINERAL, AND WATER RIGHTS
RECORDED DECEMBER 10, 1996 AS INSTRUMENT NO. 19960624029 OF OFFICIAL RECORDS.
2. SAN DIEGO GAS & ELECTRIC COMPANY, HOLDER OF A UTILITY EASEMENT RECORDED FEBRUARY 10,
1993 AS INSTRUMENT NO. 93-091210 OF OFFICIAL RECORDS. (TO BE ABANDONED PRIOR TO RECORDATION)

EASEMENT NOTES:

- (A) PRIVATE LOCAL PARK EASEMENT DEDICATED TO THE COUNTY OF ORANGE.
 (B) INDICATES SIDEWALK EASEMENT DEDICATED TO THE COUNTY OF ORANGE.
 (C) INDICATES EASEMENT FOR SEWER, WATER AND ACCESS PURPOSES DEDICATED TO THE
SANTA MARGARITA WATER DISTRICT.
 (D) INDICATES STORM DRAIN EASEMENT DEDICATED TO THE COUNTY OF ORANGE.

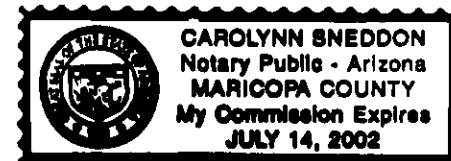
DMB CONSOLIDATED HOLDINGS, L.L.C.

STATE OF Arizona)SS
COUNTY OF Maricopa

ON THIS 26th DAY OF December, 2000, BEFORE ME
Carolynn Sneddon, A NOTARY PUBLIC IN AND FOR SAID
 STATE, PERSONALLY APPEARED Timothy A. Kaehr PERSONALLY
 KNOWN TO ME OR PROVED TO ME ON THE BASIS OF SATISFACTORY
 EVIDENCE TO BE THE PERSON WHOSE NAME IS SUBSCRIBED TO THE
 WITHIN INSTRUMENT AND ACKNOWLEDGED TO ME THAT HE EXECUTED
 THE SAME IN HIS AUTHORIZED CAPACITY, AND THAT BY HIS SIGNATURE ON
 THE INSTRUMENT THE PERSON, OR THE ENTITY UPON BEHALF OF WHICH
 THE PERSON ACTED, EXECUTED THE INSTRUMENT, AS BENEFICIARY.

WITNESS MY HAND: MY COMMISSION EXPIRES 07-14-02
Carolynn Sneddon MY PRINCIPAL PLACE OF BUSINESS
 NOTARY PUBLIC IN AND FOR SAID STATE IS IN Maricopa COUNTY.

Carolynn Sneddon
 PRINT NAME



TRACT NO. 16157

IN UNINCORPORATED TERRITORY OF ORANGE COUNTY, CALIFORNIA

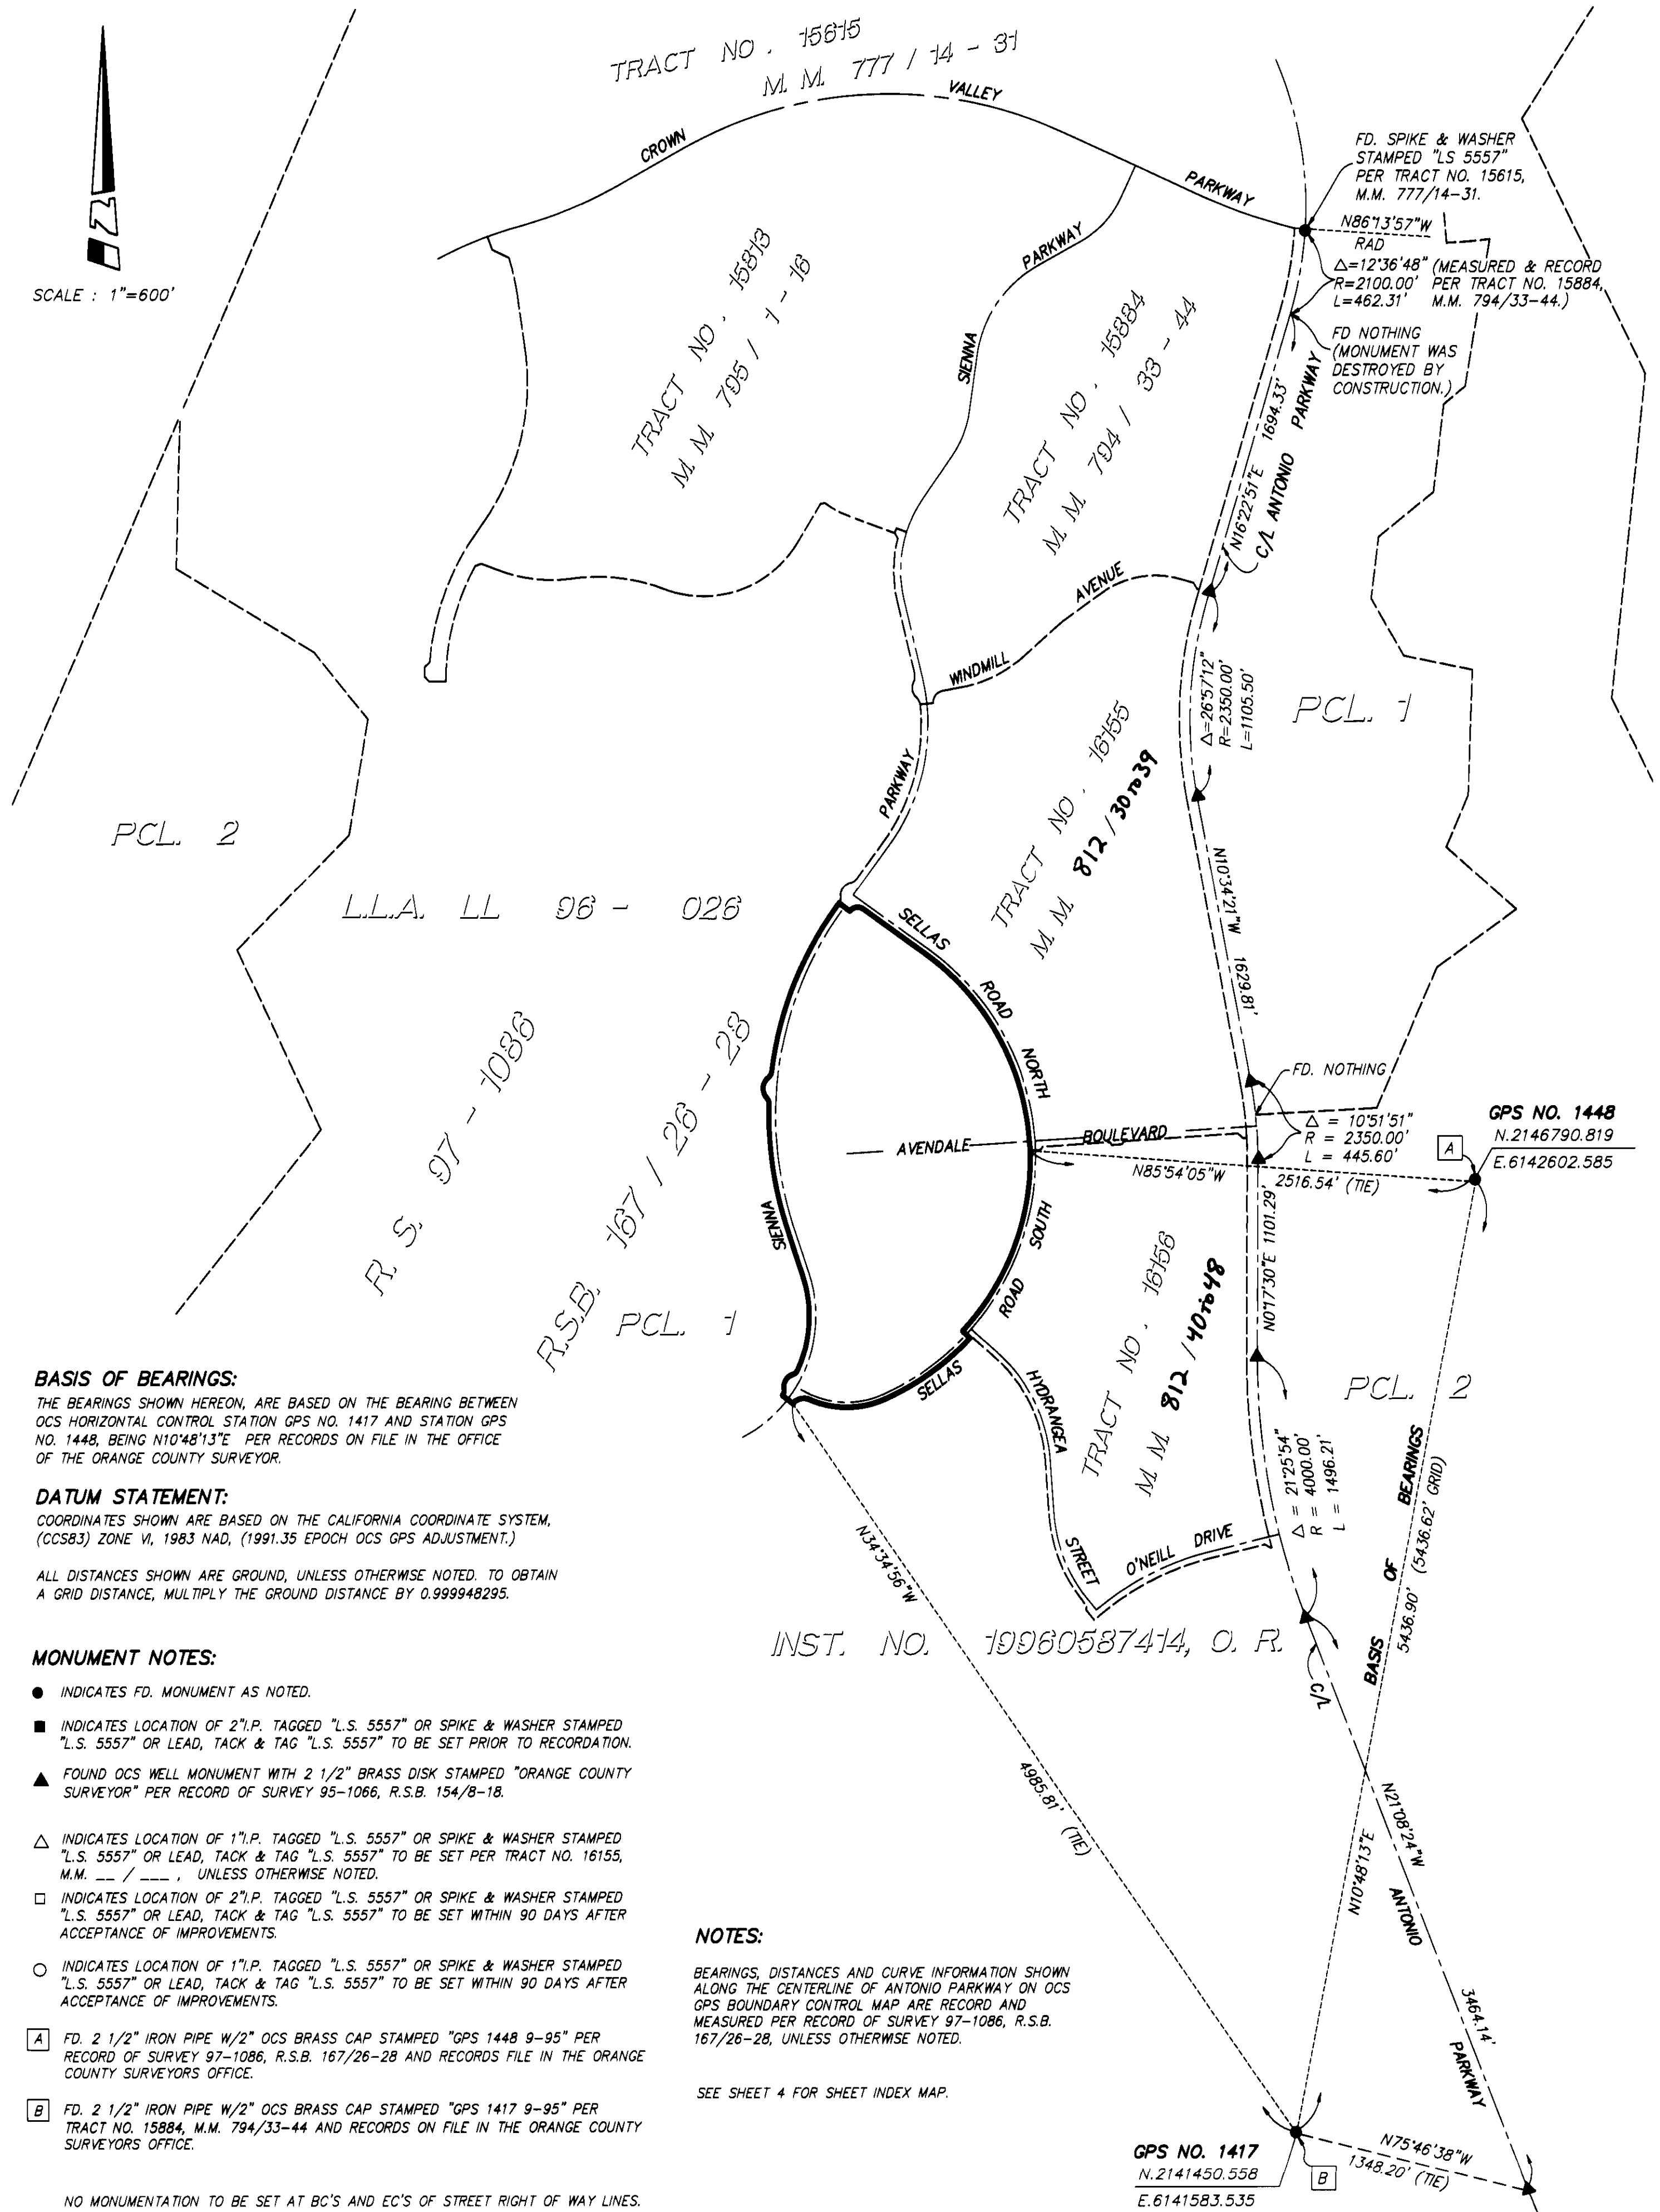
OCTOBER 2000

JAMES F. GILLEN, L.S. 5557

HUITT-ZOLIARS

9 NUMBERED LOTS AND 15 LETTERED LOTS

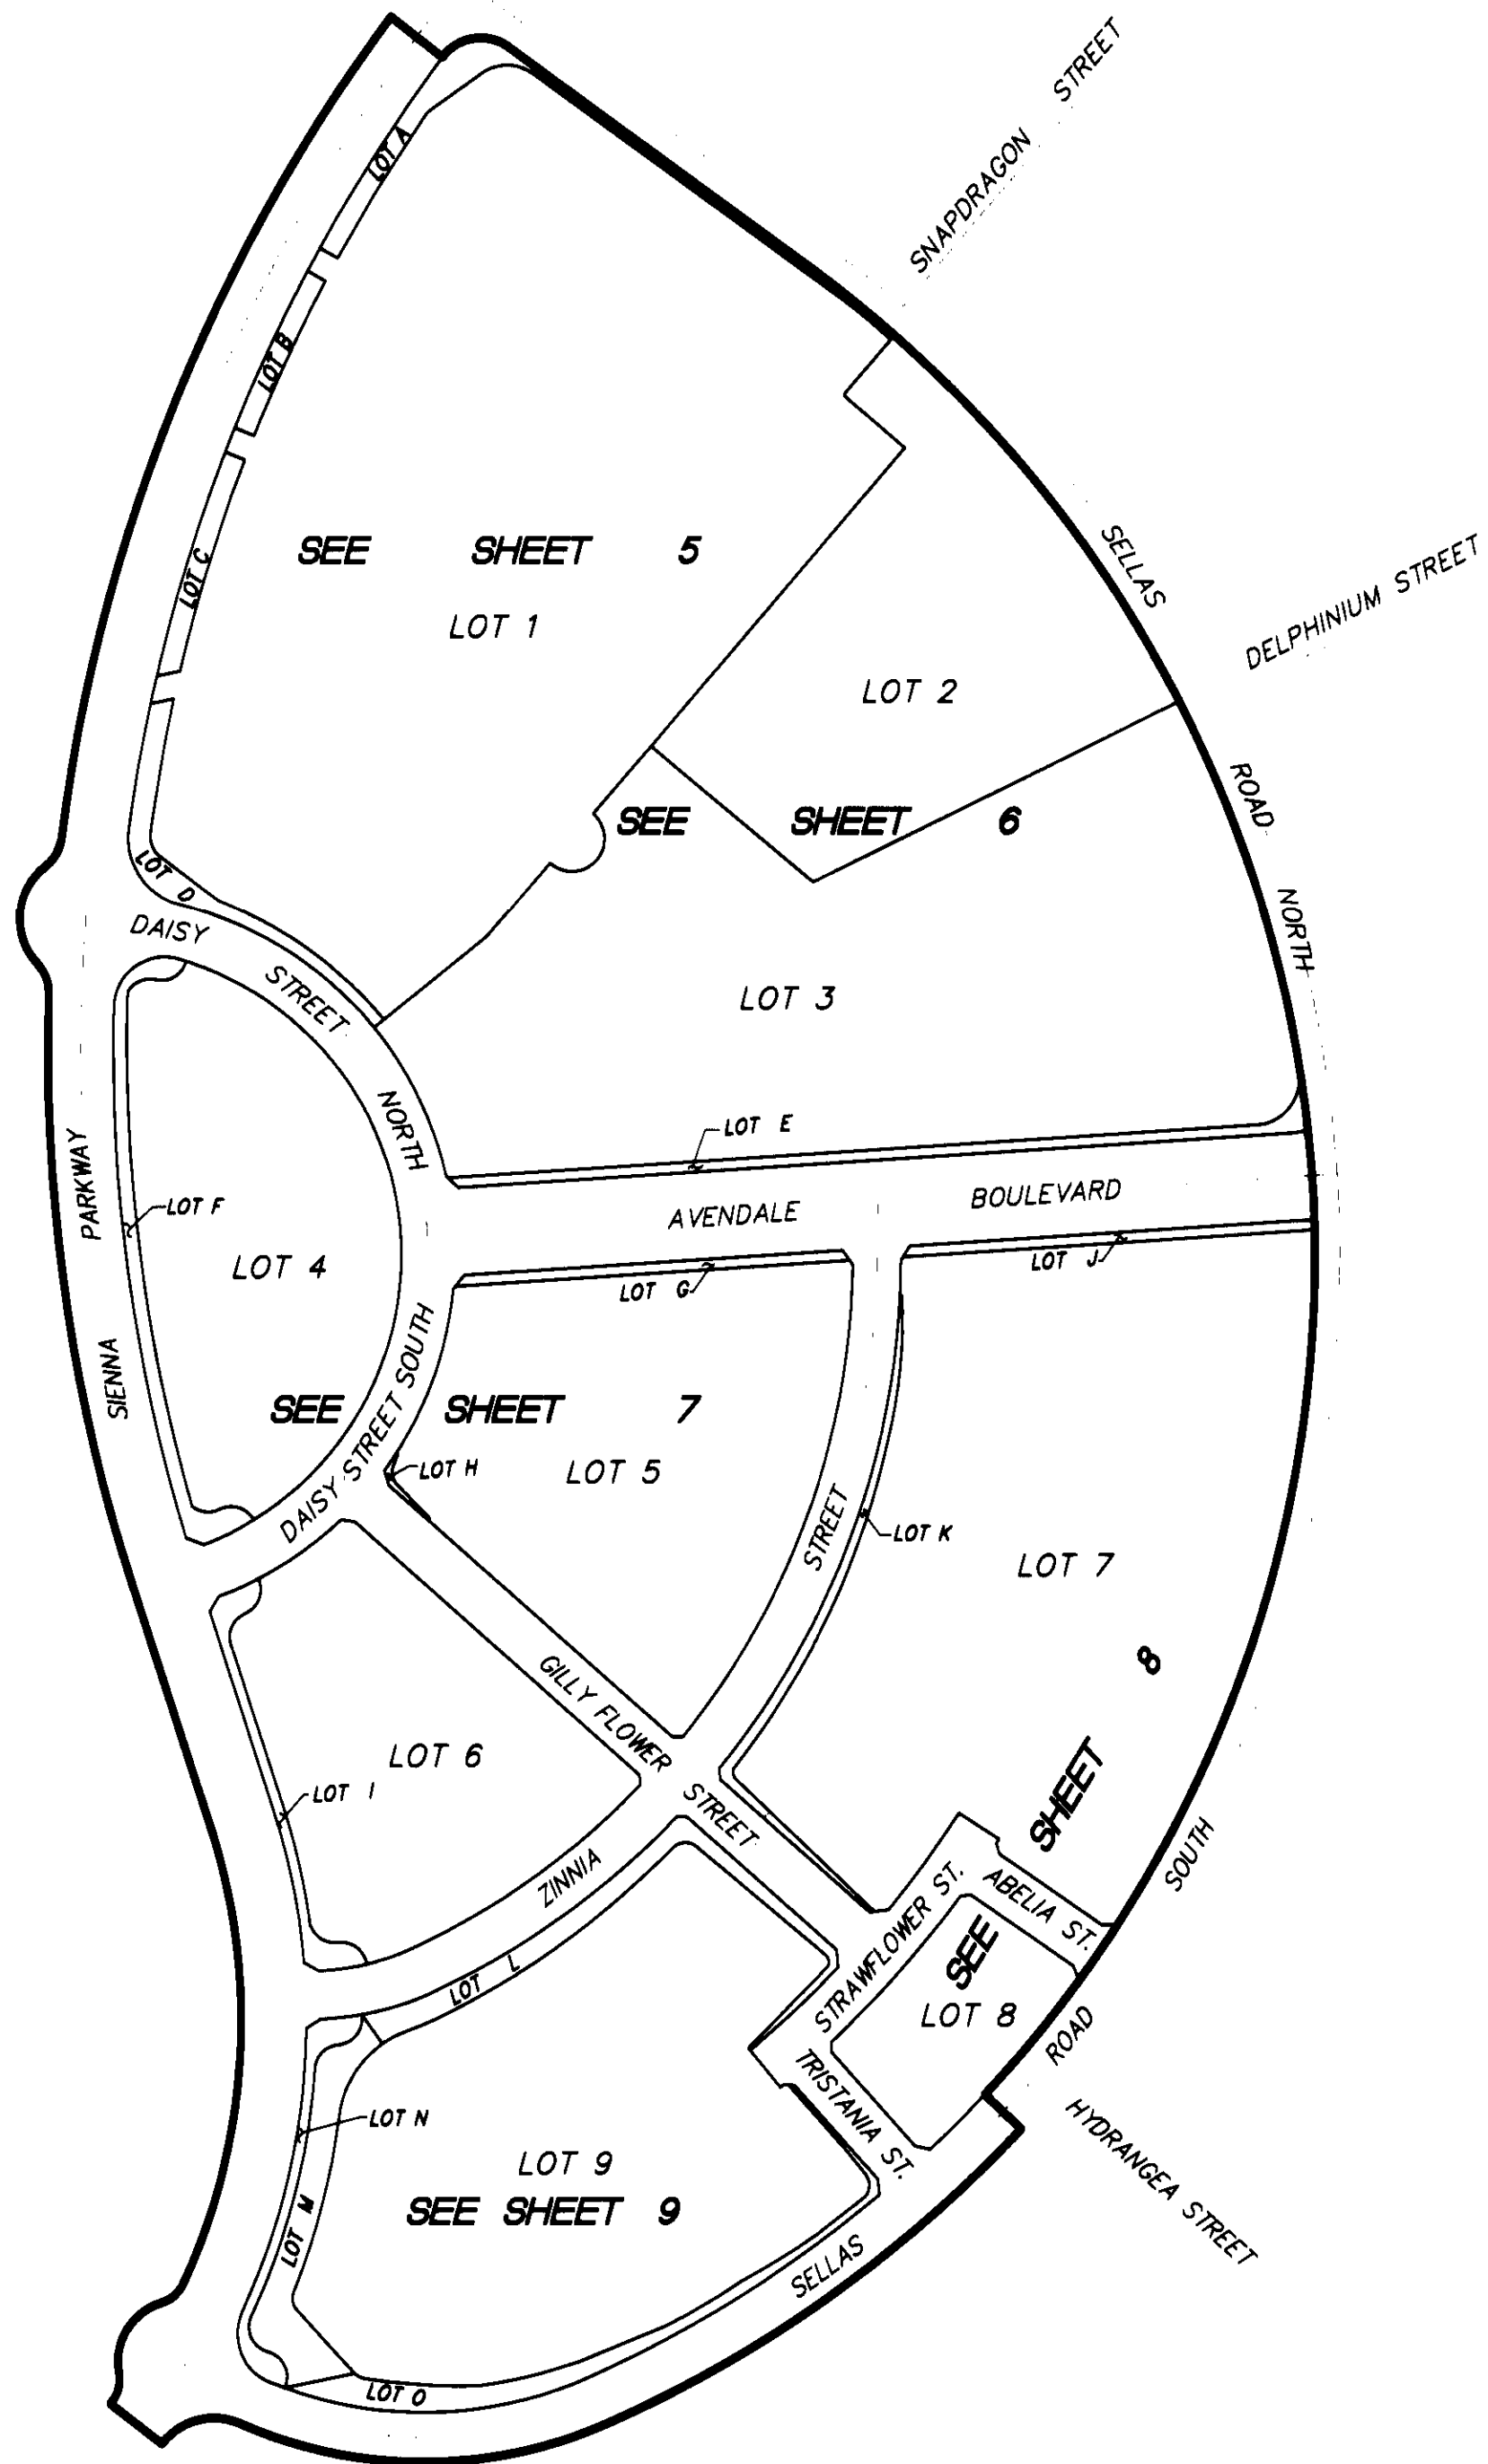
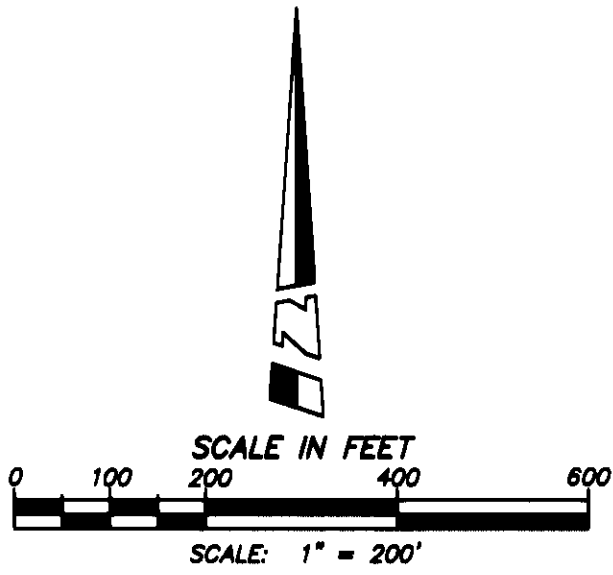
69.655 ACRES



SHEET 4 OF 9 SHEETS

A PORTION OF VESTING
TENTATIVE TRACT NO. 16025DATE OF SURVEY:
JANUARY 1999

TRACT NO. 16157
IN UNINCORPORATED TERRITORY OF ORANGE COUNTY, CALIFORNIA
OCTOBER 2000 JAMES F. GILLEN, L.S. 5557
HUITT-ZOLLARS
9 NUMBERED LOTS AND 15 LETTERED LOTS 69.655 ACRES

**SHEET INDEX MAP**

SHEET 5 OF 9 SHEETS

A PORTION OF VESTING
TENTATIVE TRACT NO. 16025DATE OF SURVEY:
JANUARY 1999

TRACT NO. 16157

IN UNINCORPORATED TERRITORY OF ORANGE COUNTY, CALIFORNIA

OCTOBER 2000

JAMES F. GILLEN, L.S. 5557

HUITT-ZOLLARS

9 NUMBERED LOTS AND 15 LETTERED LOTS

69.655 ACRES

TRACT

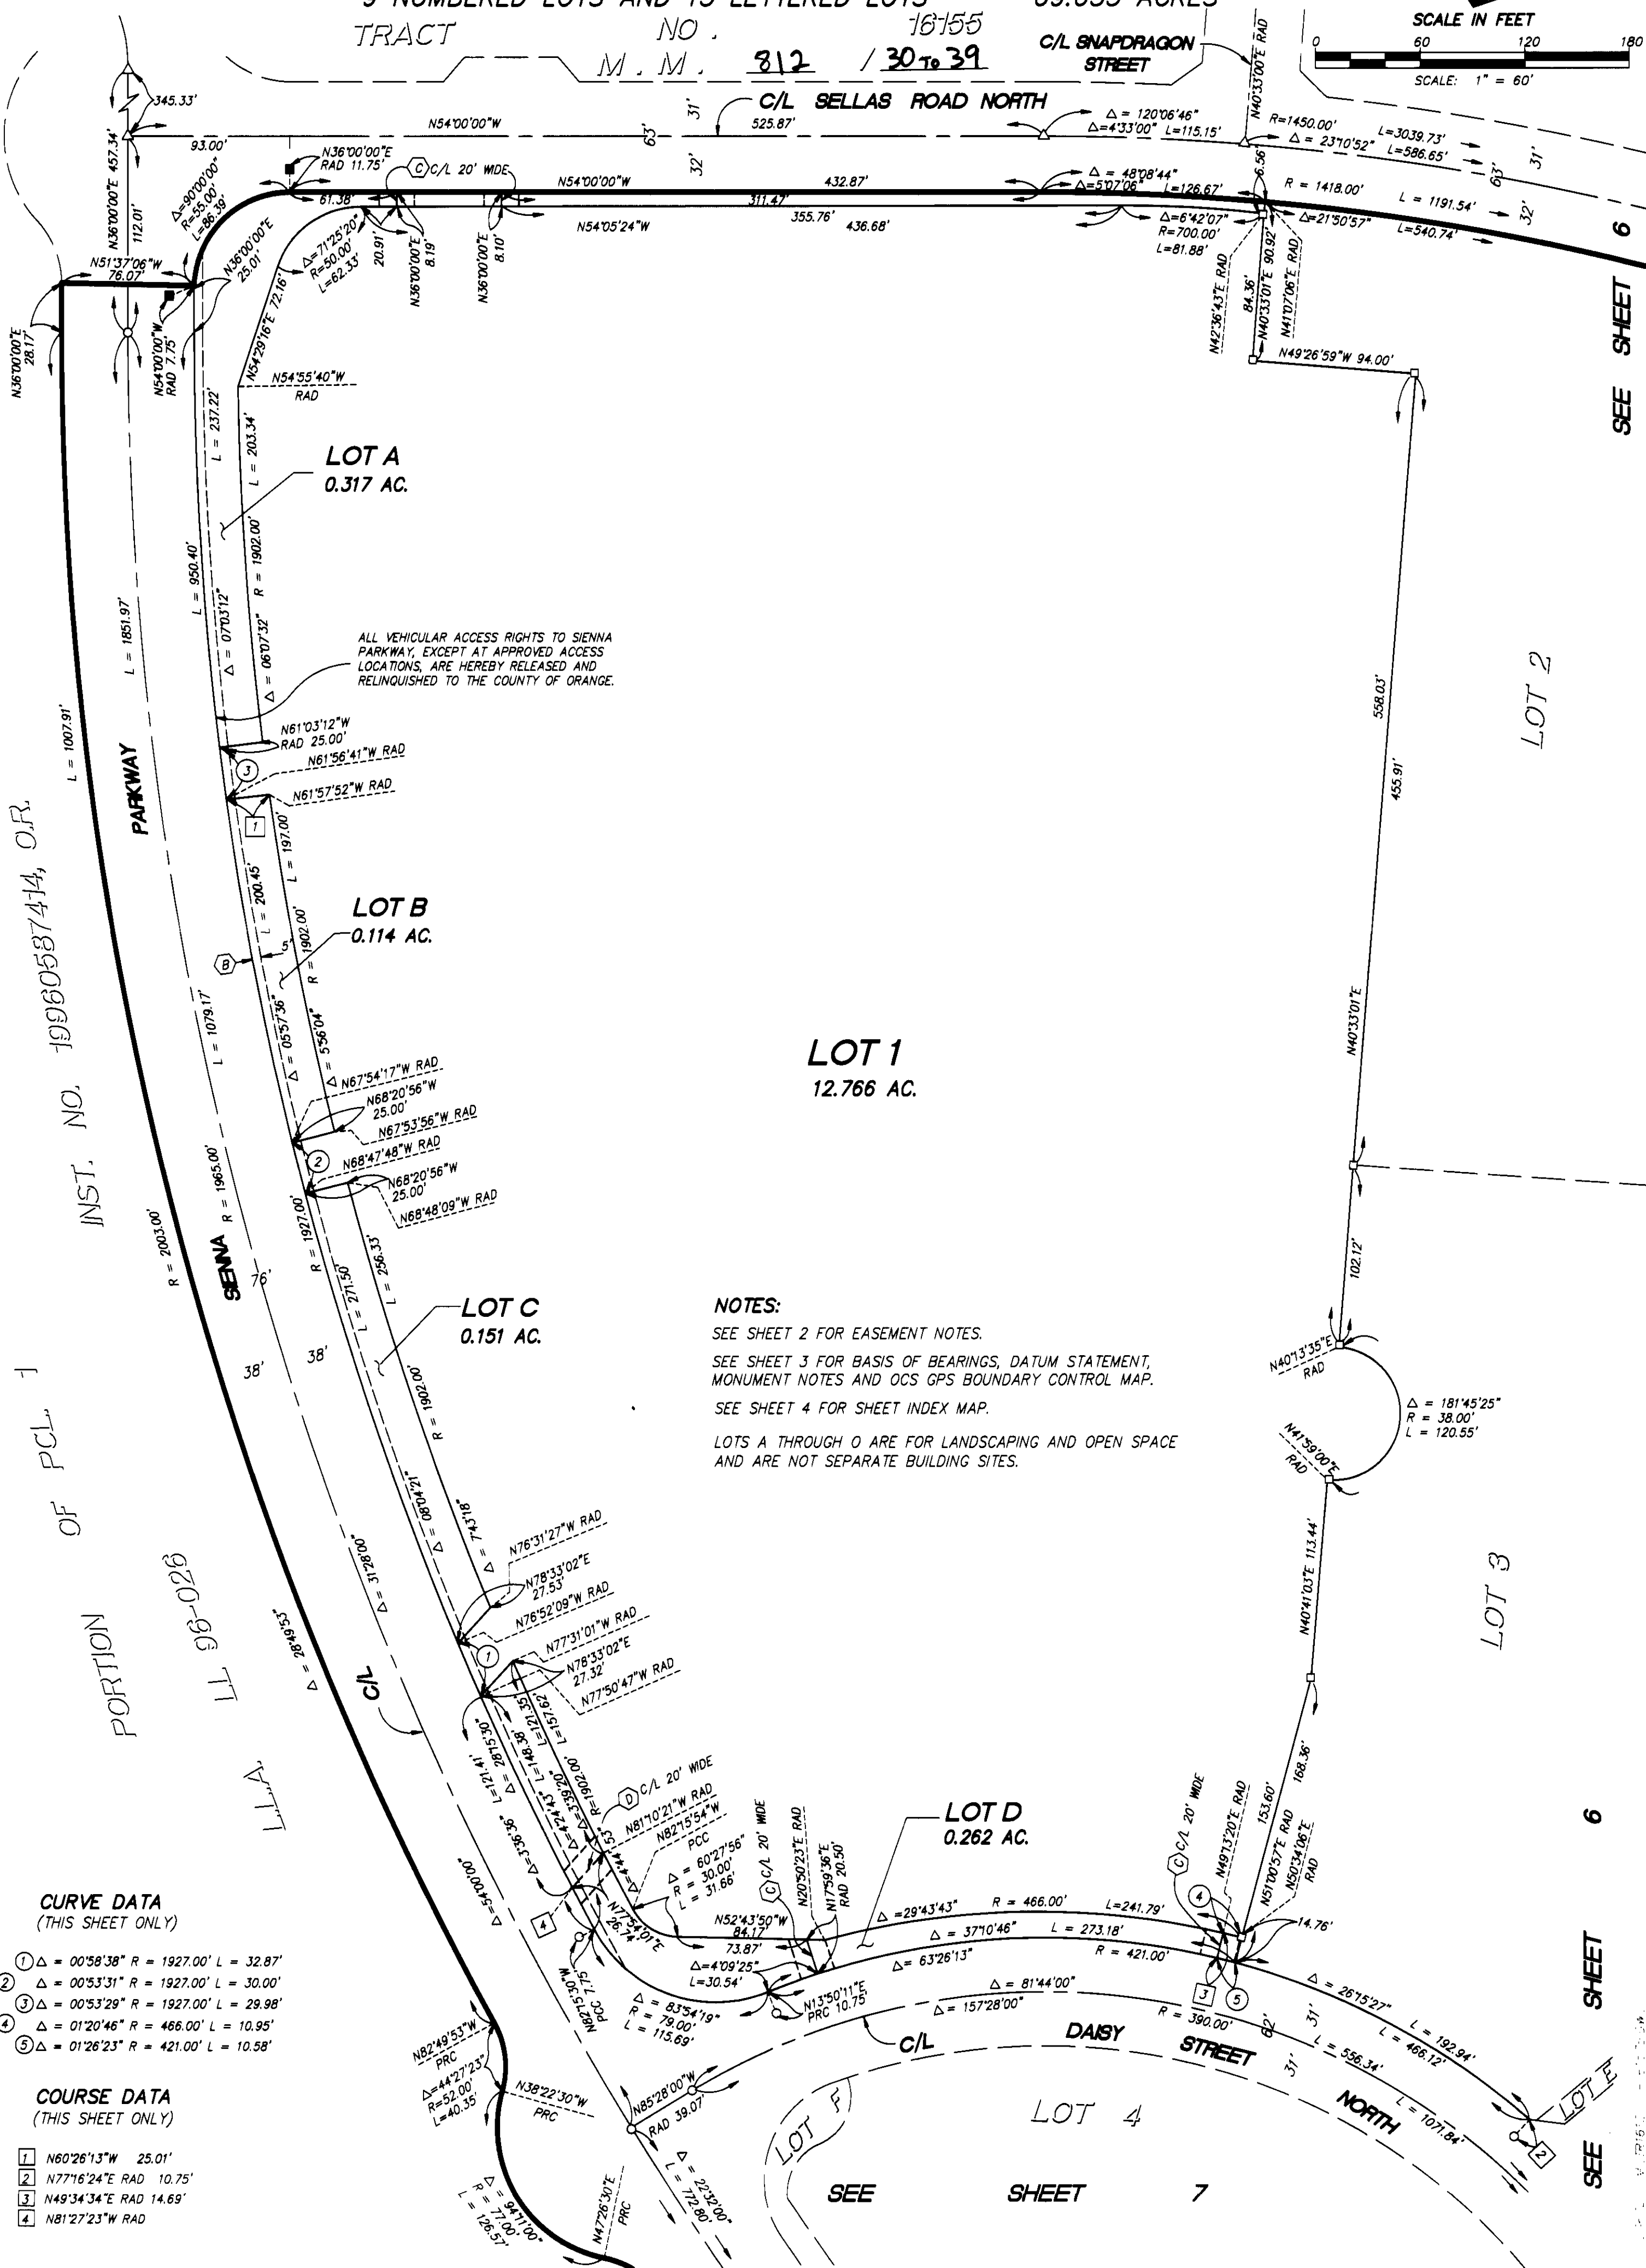
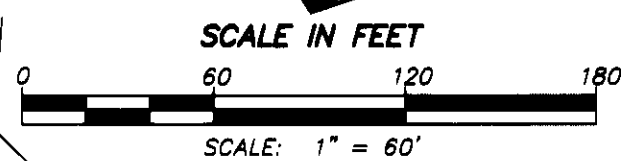
NO.

16155

M. M.

812

/ 30 TO 39

C/L SNAPDRAGON
STREETLOT A
0.317 AC.LOT B
0.114 AC.LOT 1
12.766 AC.LOT C
0.151 AC.LOT D
0.262 AC.

NOTES:

SEE SHEET 2 FOR EASEMENT NOTES.

SEE SHEET 3 FOR BASIS OF BEARINGS, DATUM STATEMENT,
MONUMENT NOTES AND OCS GPS BOUNDARY CONTROL MAP.

SEE SHEET 4 FOR SHEET INDEX MAP.

LOTS A THROUGH O ARE FOR LANDSCAPING AND OPEN SPACE
AND ARE NOT SEPARATE BUILDING SITES.CURVE DATA
(THIS SHEET ONLY)

- ① $\Delta = 00^{\circ}58'38''$ $R = 1927.00'$ $L = 32.87'$
- ② $\Delta = 00^{\circ}53'31''$ $R = 1927.00'$ $L = 30.00'$
- ③ $\Delta = 00^{\circ}53'29''$ $R = 1927.00'$ $L = 29.98'$
- ④ $\Delta = 01^{\circ}20'46''$ $R = 466.00'$ $L = 10.95'$
- ⑤ $\Delta = 01^{\circ}26'23''$ $R = 421.00'$ $L = 10.58'$

COURSE DATA
(THIS SHEET ONLY)

- 1 $N60^{\circ}26'13''W$ 25.01'
- 2 $N77^{\circ}16'24''E$ RAD 10.75'
- 3 $N49^{\circ}34'34''E$ RAD 14.69'
- 4 $N81^{\circ}27'23''W$ RAD

SEE SHEET 6

LOT 2

LOT 3

6

SHEET

SEE

SHEET

7

813

5

SHEET 6 OF 9 SHEETS

TRACT NO. 16157

IN UNINCORPORATED TERRITORY OF ORANGE COUNTY, CALIFORNIA

OCTOBER 2000

JAMES F. GILLEN, L.S. 5557

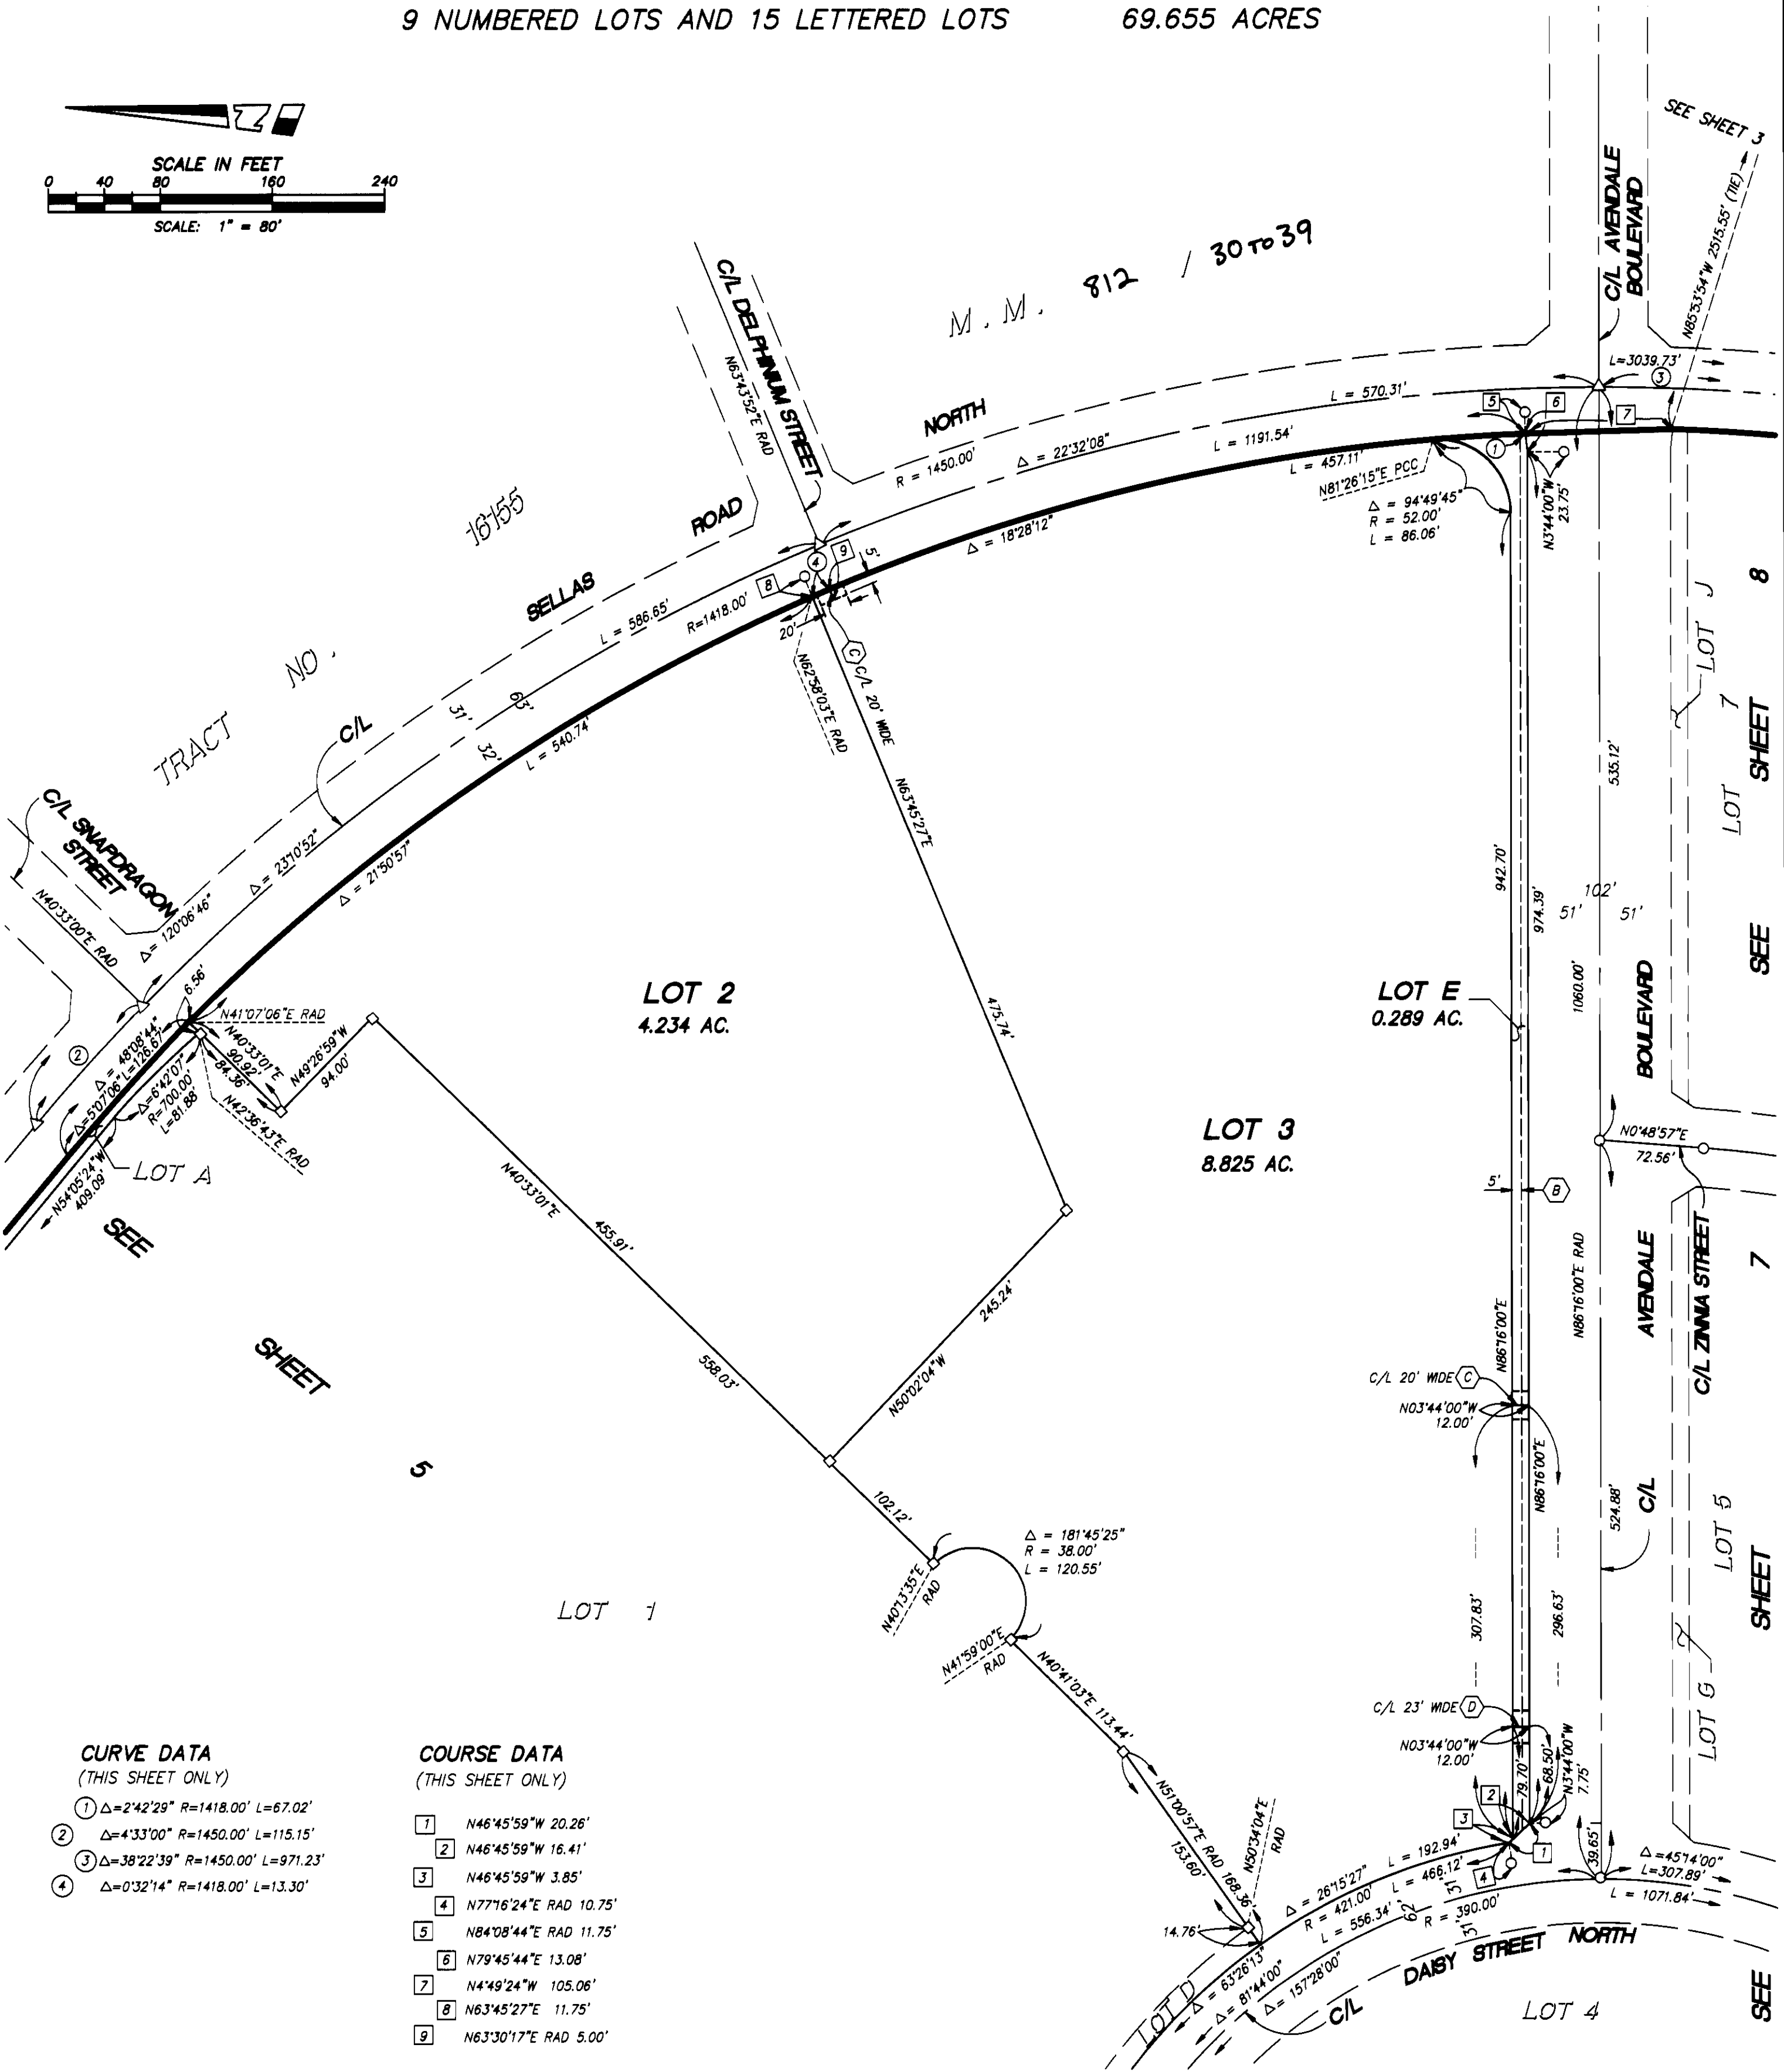
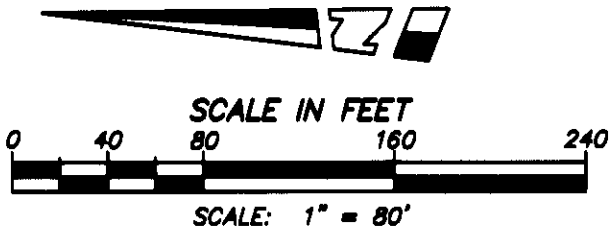
A PORTION OF VESTING
TENTATIVE TRACT NO. 16025

DATE OF SURVEY:
JANUARY 1999

HUITT-ZOLLARS

9 NUMBERED LOTS AND 15 LETTERED LOTS

69.655 ACRES



CURVE DATA
(THIS SHEET ONLY)

- ① $\Delta = 2^\circ 42' 29''$ $R = 1418.00'$ $L = 67.02'$
- ② $\Delta = 4^\circ 33' 00''$ $R = 1450.00'$ $L = 115.15'$
- ③ $\Delta = 38^\circ 22' 39''$ $R = 1450.00'$ $L = 971.23'$
- ④ $\Delta = 0^\circ 32' 14''$ $R = 1418.00'$ $L = 13.30'$

COURSE DATA
(THIS SHEET ONLY)

- ① $N46^\circ 45' 59'' W$ 20.26'
- ② $N46^\circ 45' 59'' W$ 16.41'
- ③ $N46^\circ 45' 59'' W$ 3.85'
- ④ $N77^\circ 16' 24'' E$ RAD 10.75'
- ⑤ $N84^\circ 08' 44'' E$ RAD 11.75'
- ⑥ $N79^\circ 45' 44'' E$ 13.08'
- ⑦ $N4^\circ 49' 24'' W$ 105.06'
- ⑧ $N63^\circ 45' 27'' E$ 11.75'
- ⑨ $N63^\circ 30' 17'' E$ RAD 5.00'

NOTES:

SEE SHEET 2 FOR EASEMENT NOTES.

SEE SHEET 3 FOR BASIS OF BEARINGS, DATUM STATEMENT,
MONUMENT NOTES AND OCS GPS BOUNDARY CONTROL MAP.

SEE SHEET 4 FOR SHEET INDEX MAP.

LOTS A THROUGH O ARE FOR LANDSCAPING AND OPEN SPACE
AND ARE NOT SEPARATE BUILDING SITES.

SEE SHEET 5

SHEET 7 OF 9 SHEETS

TRACT NO. 16157

IN UNINCORPORATED TERRITORY OF ORANGE COUNTY, CALIFORNIA

OCTOBER 2000

JAMES F. GILLEN, L.S. 5557

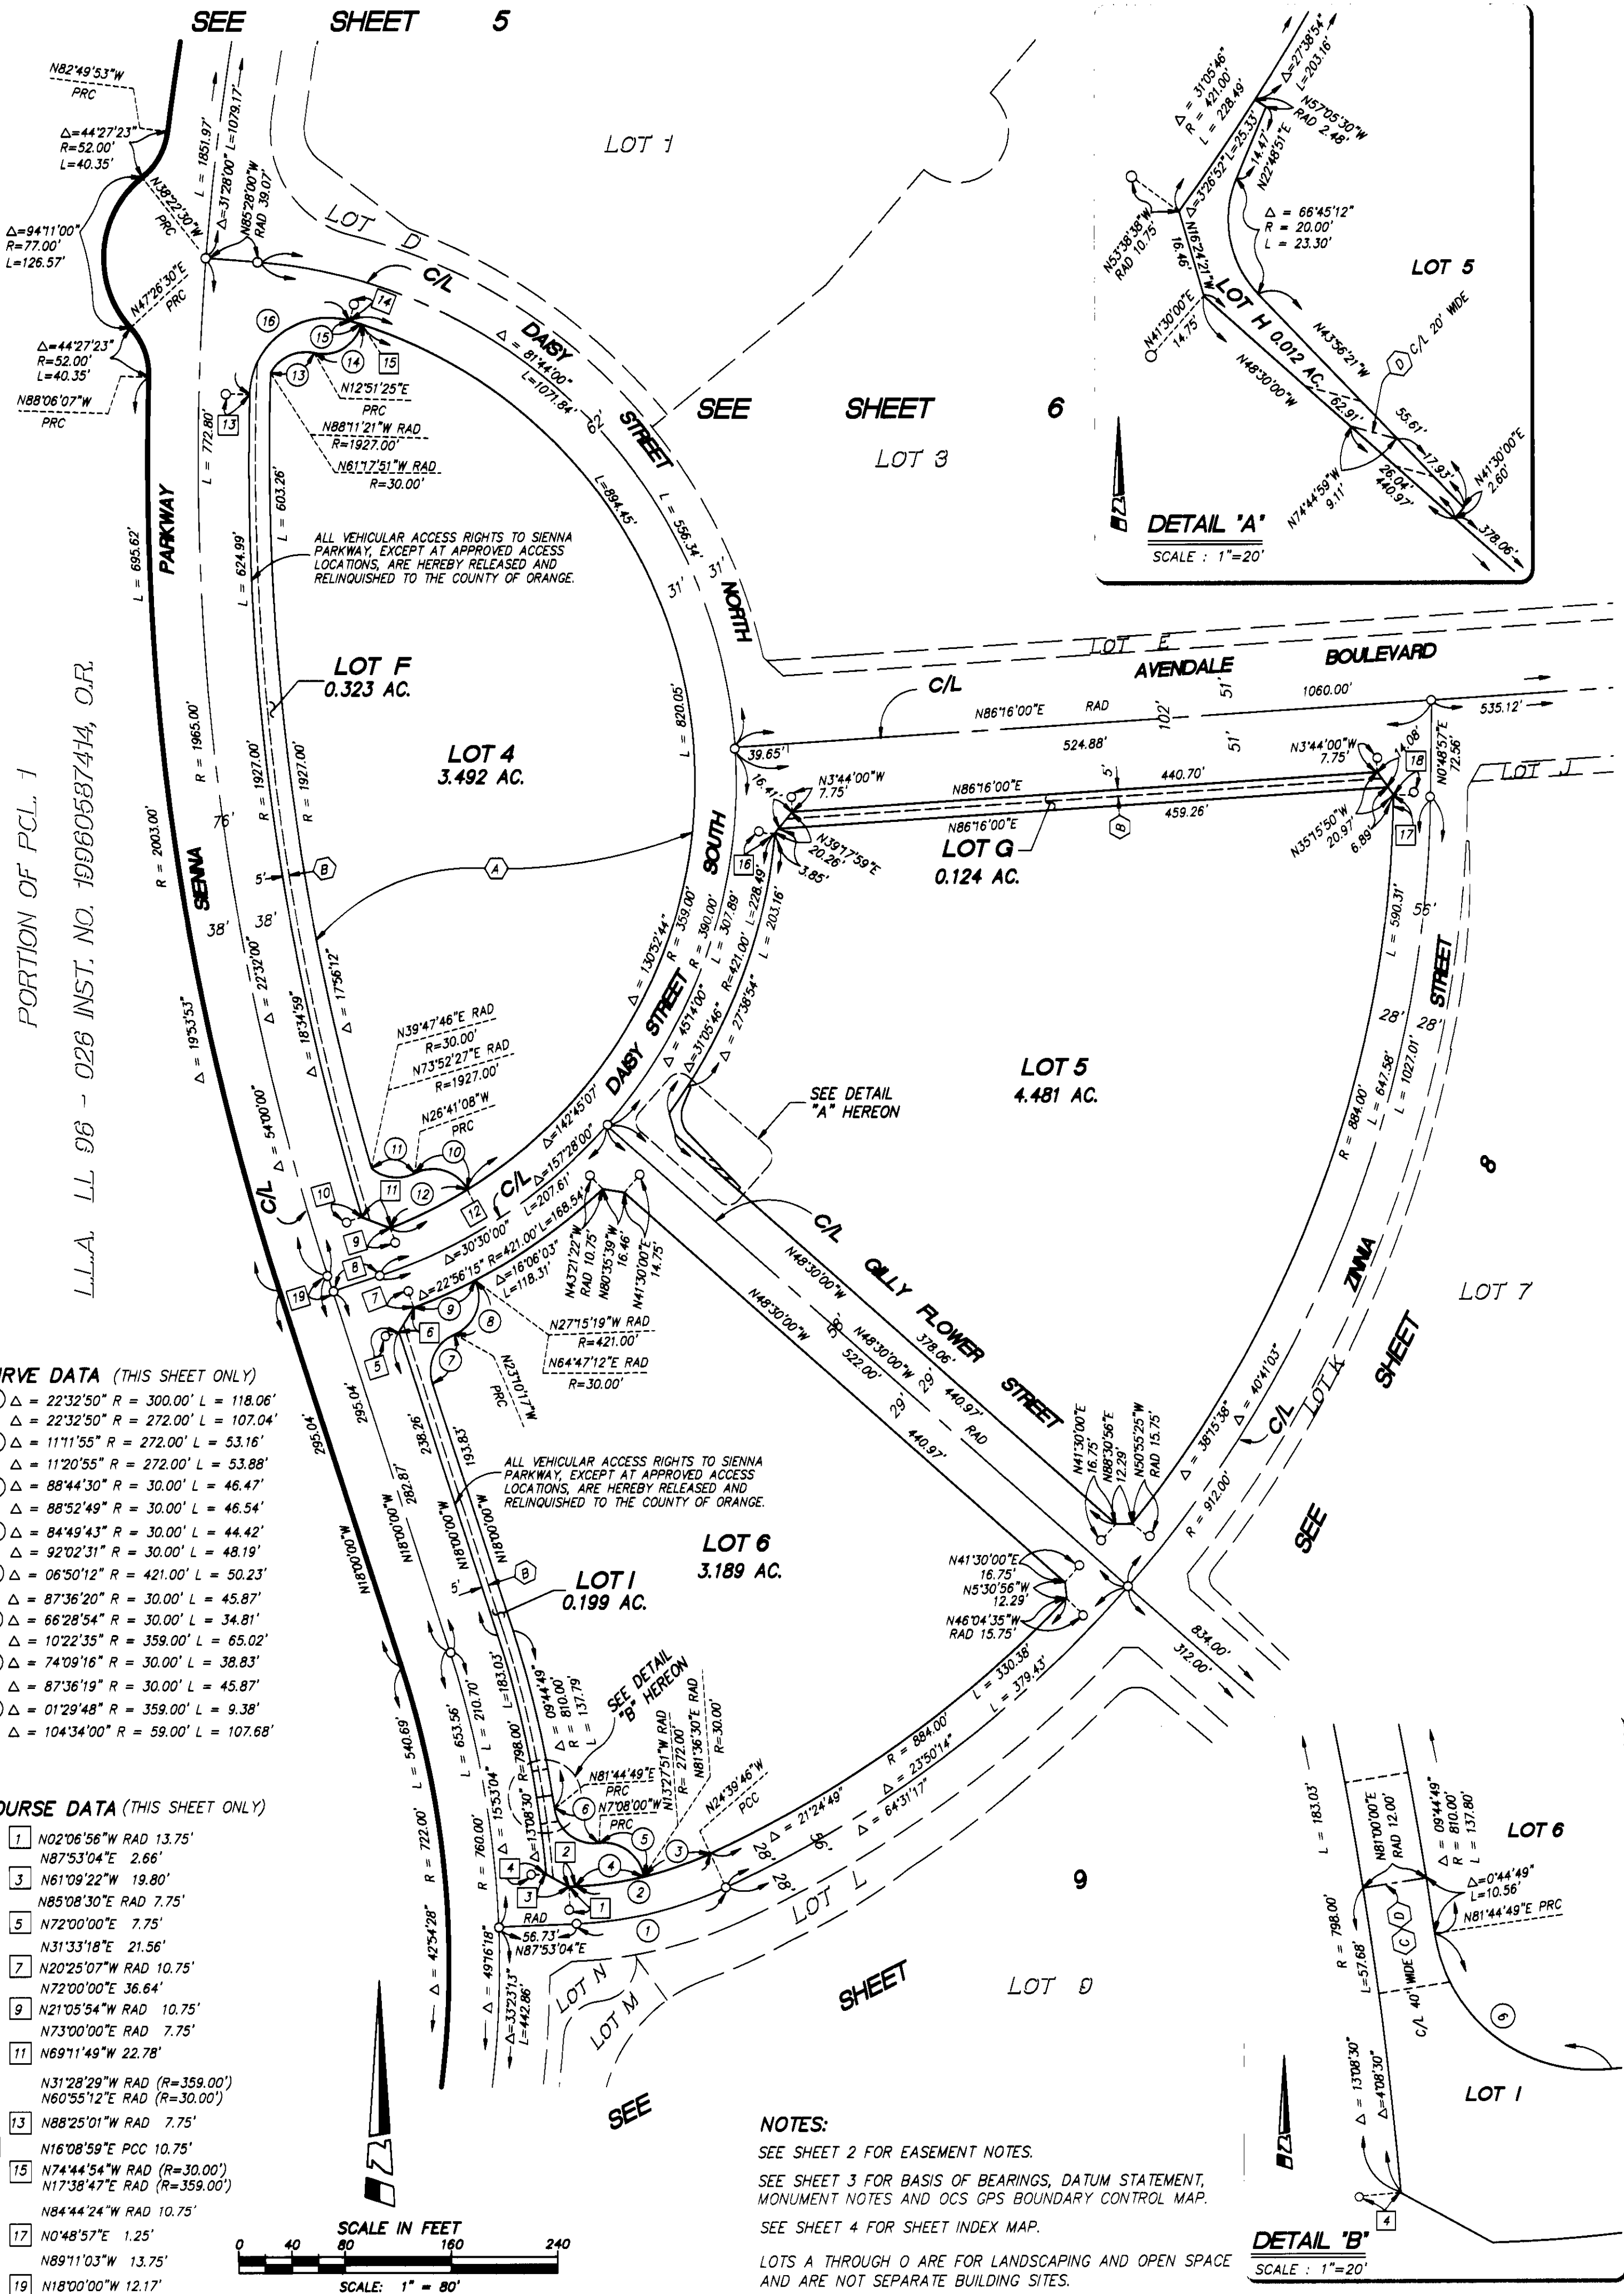
A PORTION OF VESTING
TENTATIVE TRACT NO. 16025DATE OF SURVEY:
JANUARY 1999

HUITT-ZOLLARS

9 NUMBERED LOTS AND 15 LETTERED LOTS

69.655 ACRES

SEE SHEET 5



SHEET 8 OF 9 SHEETS

TRACT NO. 16157

A PORTION OF VESTING
TENTATIVE TRACT NO. 16025

IN UNINCORPORATED TERRITORY OF ORANGE COUNTY, CALIFORNIA

OCTOBER 2000

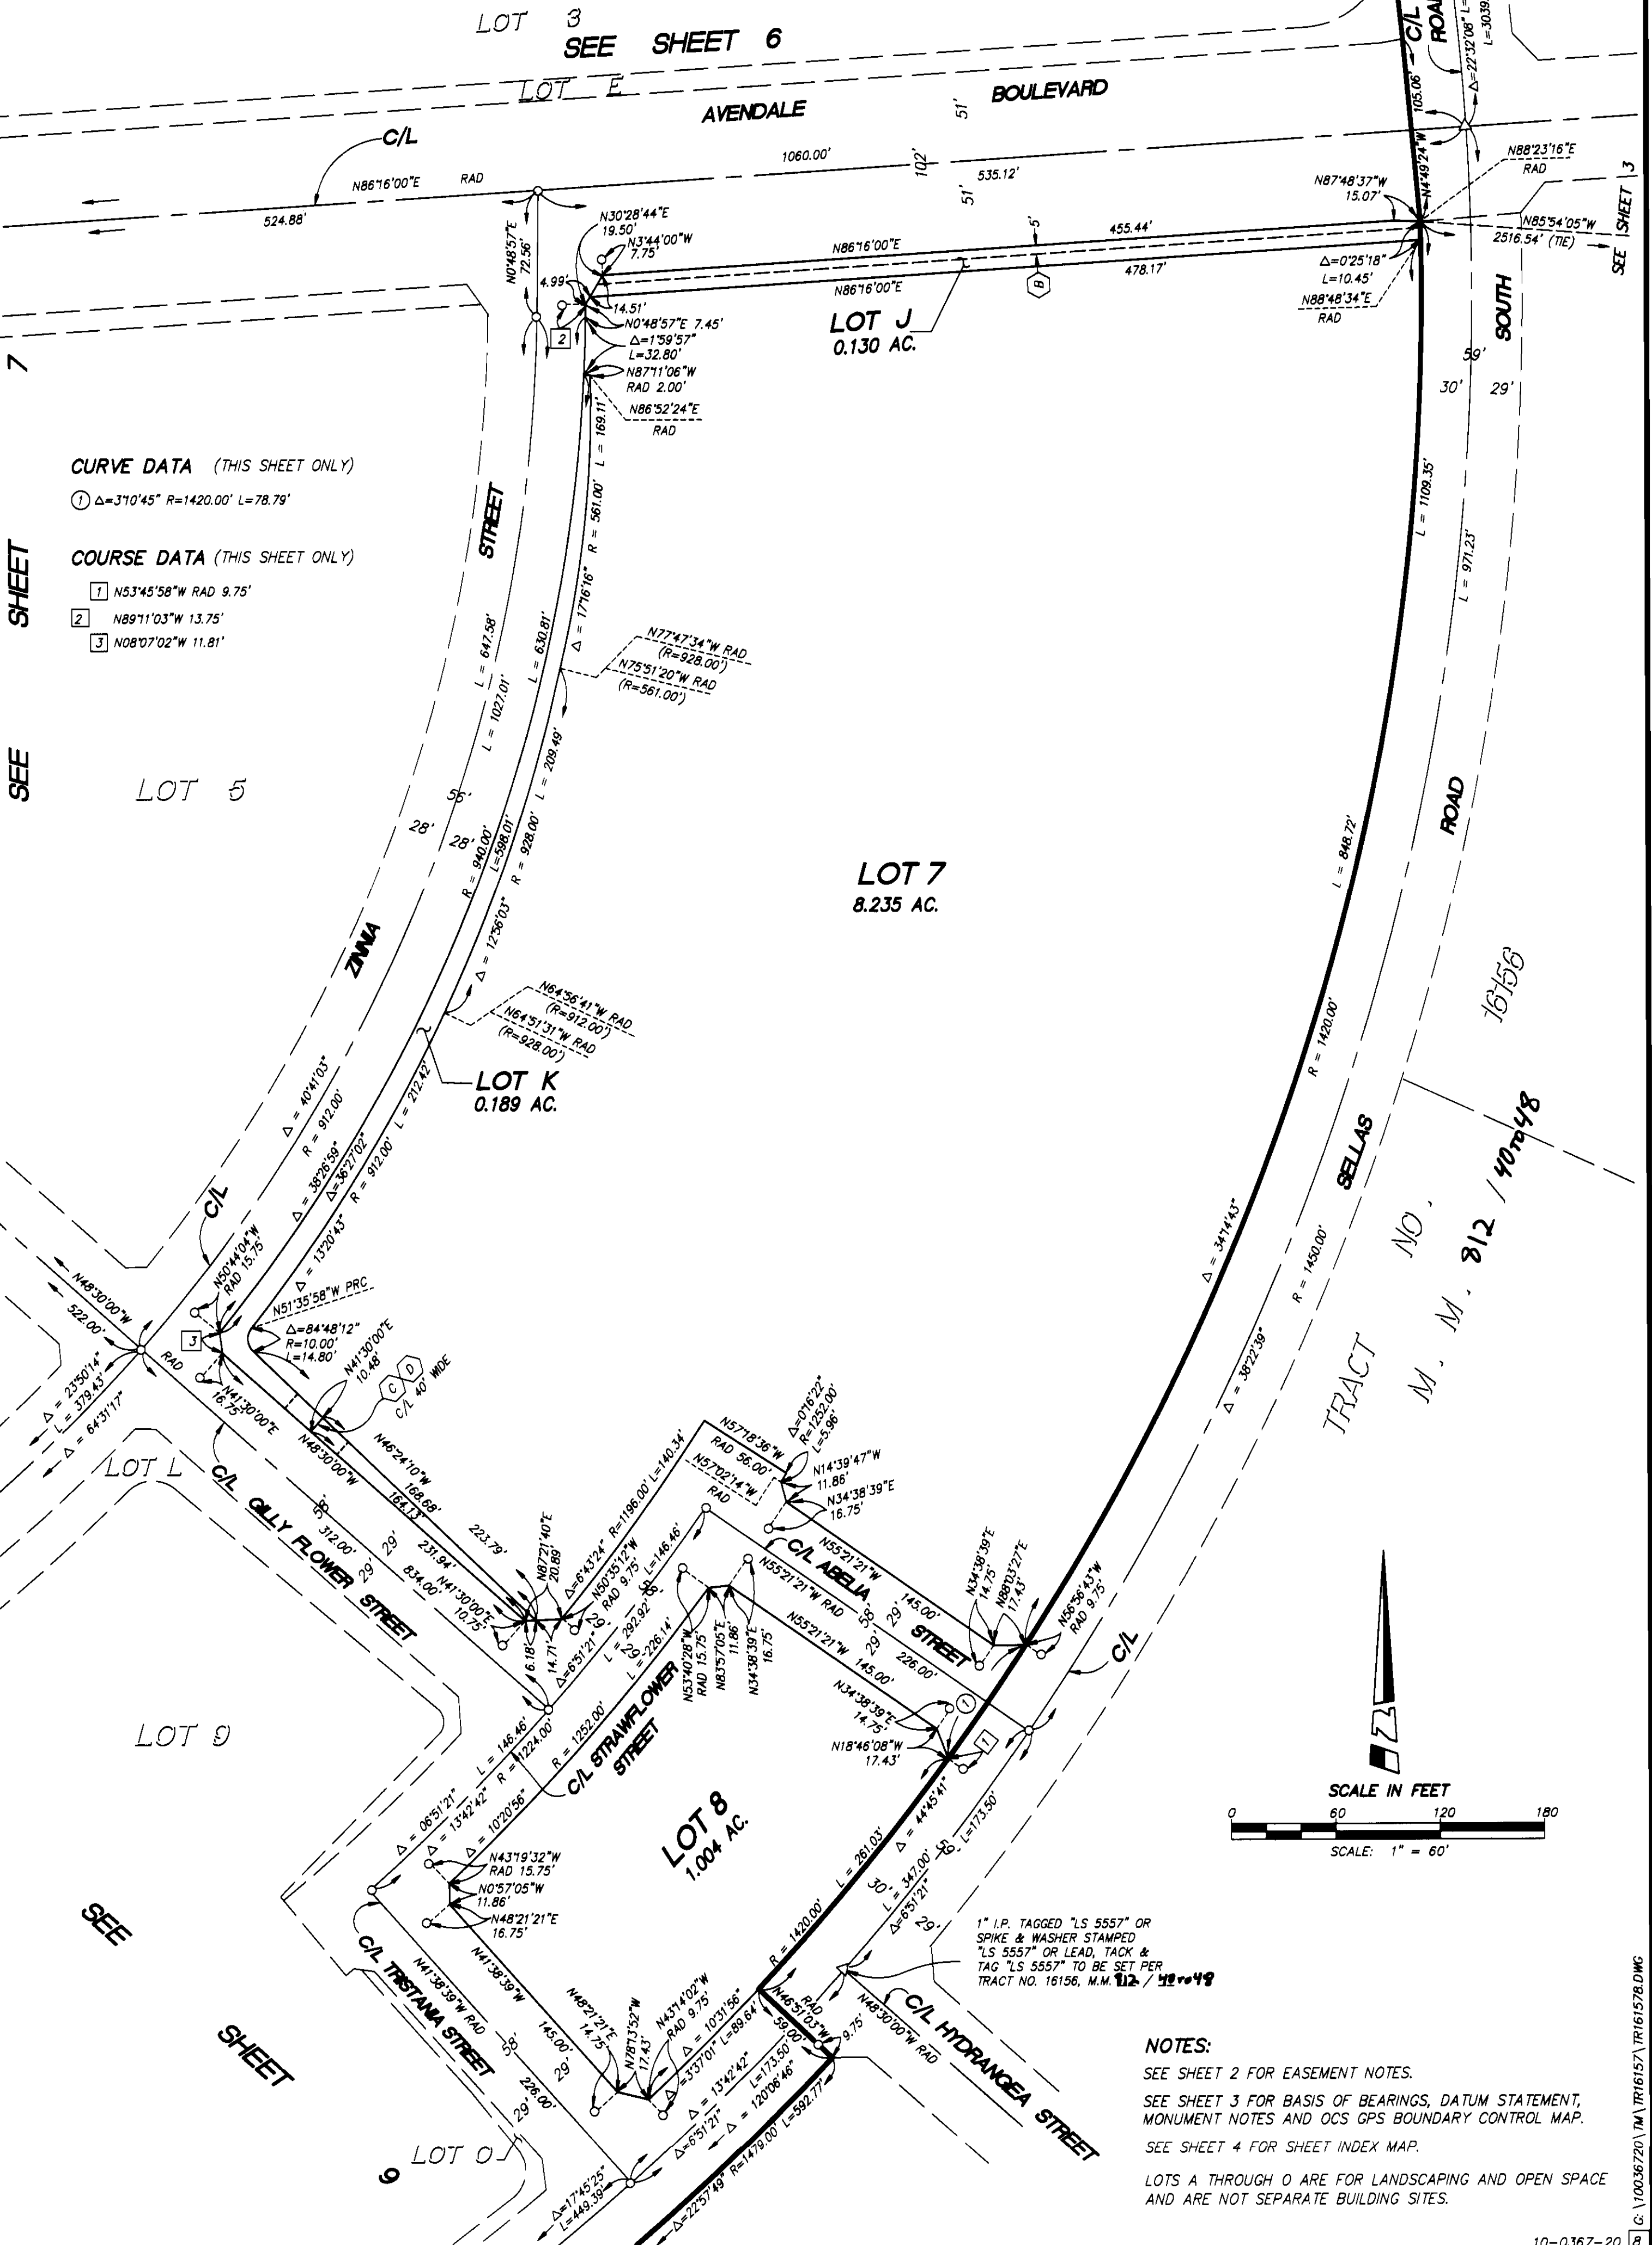
JAMES F. GILLEN, L.S. 5557

DATE OF SURVEY:
JANUARY 1999

HUITT-ZOLLARS

9 NUMBERED LOTS AND 15 LETTERED LOTS

69.655 ACRES



SHEET 9 OF 9 SHEETS

TRACT NO. 16157

IN UNINCORPORATED TERRITORY OF ORANGE COUNTY, CALIFORNIA

OCTOBER 2000

JAMES F. GILLEN, L.S. 5557

HUITT-ZOLLARS

9 NUMBERED LOTS AND 15 LETTERED LOTS

69.655 ACRES

A PORTION OF VESTING
TENTATIVE TRACT NO. 16025DATE OF SURVEY:
JANUARY 1999

NOTES:

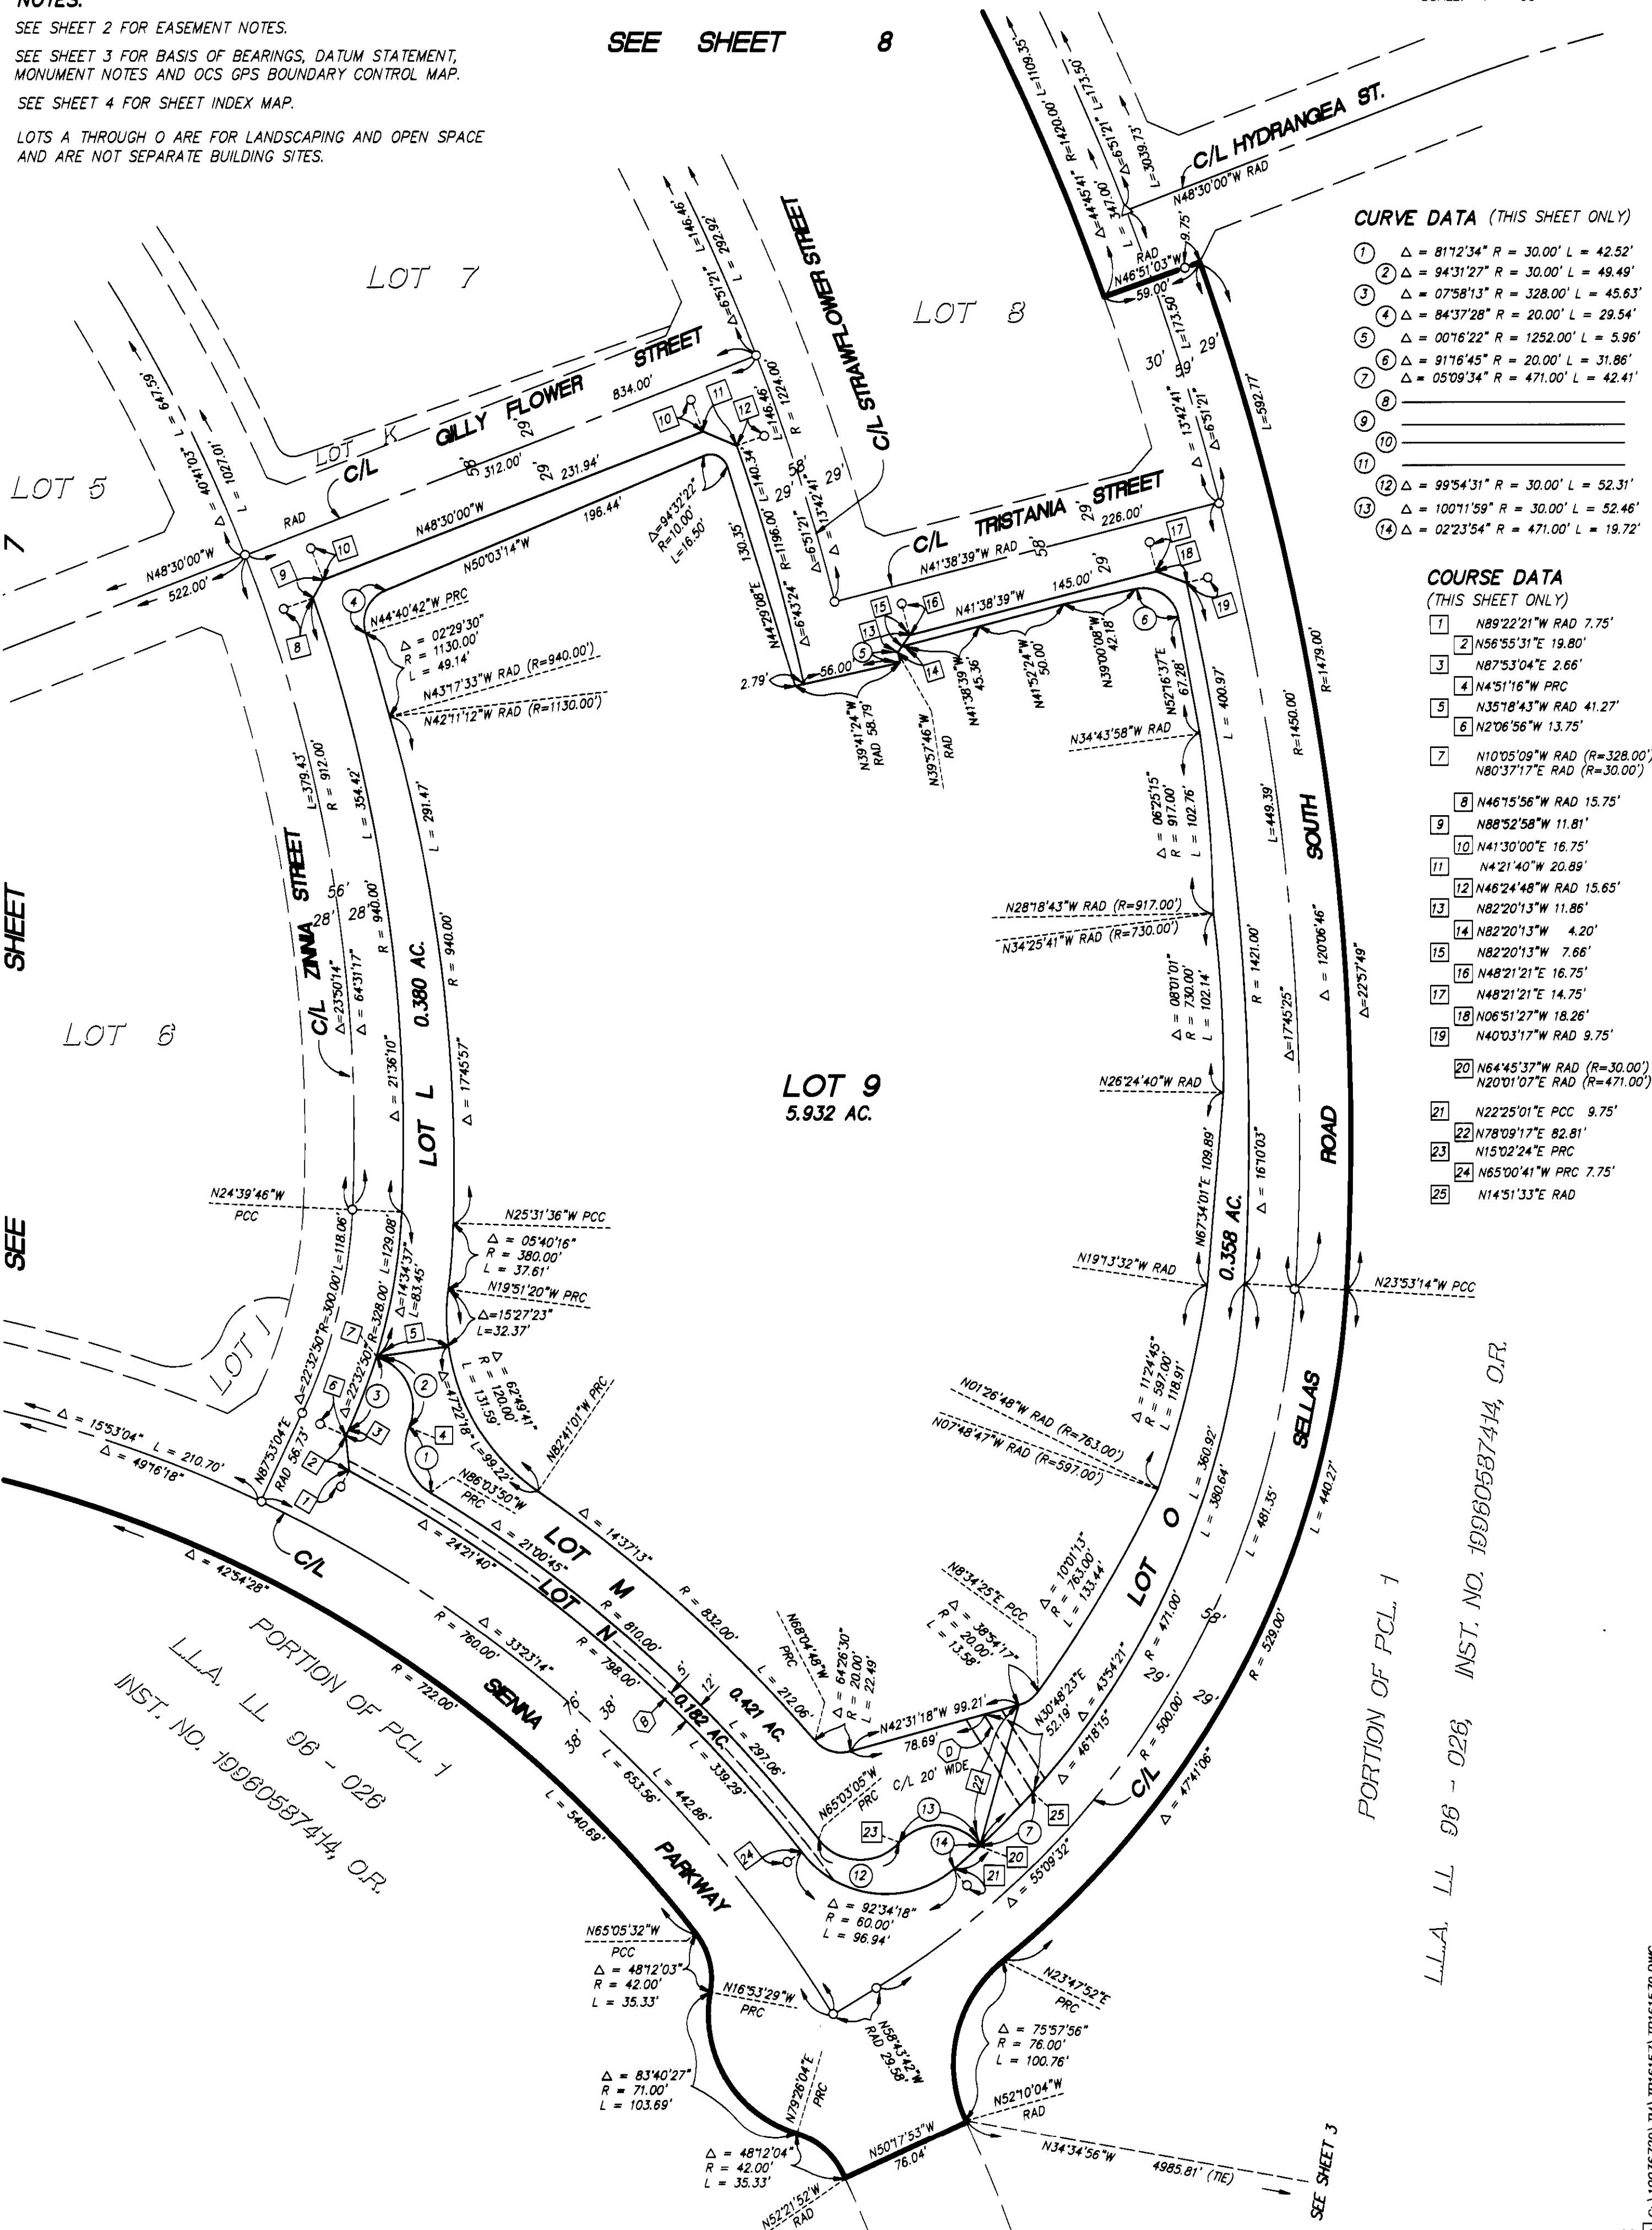
SEE SHEET 2 FOR EASEMENT NOTES.

SEE SHEET 3 FOR BASIS OF BEARINGS, DATUM STATEMENT,
MONUMENT NOTES AND OCS GPS BOUNDARY CONTROL MAP.

SEE SHEET 4 FOR SHEET INDEX MAP.

LOTS A THROUGH O ARE FOR LANDSCAPING AND OPEN SPACE
AND ARE NOT SEPARATE BUILDING SITES.

SEE SHEET 8



L.L.A. LL 96 - 026, INST. NO. 19960587414, O.R.

PORTION OF PCL 1

SEE SHEET 3