

SHEET 1 OF 13 SHEETS

TRACT NO. 16203

FINAL UNIT OF VESTING
TENTATIVE TRACT NO. 16203BLOCK MODULES
5157 03-05DATE OF SURVEY:
JANUARY 1999

IN THE UNINCORPORATED TERRITORY OF ORANGE COUNTY, CALIFORNIA
BEING A SUBDIVISION OF A PORTION OF PARCEL 1 OF LOT LINE ADJUSTMENT NO. LL 96-026
AS SHOWN ON EXHIBIT "B" ATTACHED TO THAT CERTAIN DOCUMENT RECORDED NOVEMBER 21,
1996 AS INSTRUMENT NO. 19960587414 OF OFFICIAL RECORDS, RECORDS OF ORANGE COUNTY,
CALIFORNIA.

OCTOBER 2001

HUITT-ZOLIARS

13 NUMBERED LOTS AND 24 LETTERED LOTS

JAMES F. GILLEN, L.S. 5557

142.159 ACRES

ACCEPTED AND FILED AT THE
REQUEST OF
FIRST AMERICAN TITLE INSURANCE COMPANY

DATE JANUARY 24, 2002
TIME 2:13 P.M. FEE \$ 31.00
INSTRUMENT NO. 20020063220
BOOK 826 PAGE 8-20 M/M

GARY L. GRANVILLE
COUNTY CLERK-RECORDER
BY [Signature]
DEPUTY

OWNERSHIP CERTIFICATE:

WE, THE UNDERSIGNED, BEING ALL PARTIES HAVING ANY RECORD TITLE INTEREST IN THE
LAND COVERED BY THIS MAP, DO HEREBY CONSENT TO THE PREPARATION AND RECORDATION
OF SAID MAP, AS SHOWN WITHIN THE DISTINCTIVE BORDER LINE. WE HEREBY DEDICATE
TO THE PUBLIC FOR STREET PURPOSES: DORRANCE DRIVE, CREIGHTON PLACE, UNIVERSITY AVENUE,
ETON PLACE, AND O'NEILL DRIVE.

WE ALSO HEREBY DEDICATE TO THE COUNTY OF ORANGE:

(1) THE EASEMENTS FOR SIDEWALK PURPOSES AS SHOWN ON SAID MAP.

(2) THE EASEMENTS FOR STORM DRAIN PURPOSES AS SHOWN ON SAID MAP.

(3) THE SCENIC PRESERVATION EASEMENT OVER ALL OF LOT O, AS SHOWN ON SAID MAP FOR
THE PURPOSES AND SUBJECT TO THE SAME CONDITIONS AND LIMITATIONS AS SHOWN IN THAT
CERTAIN EASEMENT RECORDED SEPTEMBER 19, 1999 AS DOCUMENT 91-511820 OF OFFICIAL RECORDS.

WE ALSO HEREBY RELEASE AND RELINQUISH TO THE COUNTY OF ORANGE ALL VEHICULAR
ACCESS RIGHTS TO O'NEILL DRIVE, EXCEPT AT APPROVED ACCESS LOCATIONS.

PURSUANT TO SECTION 7050 OF THE GOVERNMENT CODE, WE HEREBY IRREVOCABLY OFFER
TO DEDICATE TO THE COUNTY OF ORANGE LOTS 2, 3, 6, AND 10 IN FEE SIMPLE FOR LOCAL
PARK PURPOSES, TOGETHER WITH THE RIGHT TO GRANT EASEMENTS FOR PUBLIC UTILITIES
OR OTHER ESSENTIAL PURPOSES.

DMB LADERA, L.L.C., A DELAWARE LIMITED LIABILITY COMPANY.

BY: RANCHO MISSION VIEJO, L.L.C., A DELAWARE LIMITED LIABILITY COMPANY,
AS AGENT AND/OR MANAGER.

BY: [Signature]
PRINT NAME: DONALD T. STARKIN
PRINT TITLE: Director of Community Development

BY: [Signature]
PRINT NAME: Stephen C. Schraak
PRINT TITLE: Exec. VP - Development

DMB CONSOLIDATED HOLDINGS, L.L.C., AN ARIZONA LIMITED LIABILITY COMPANY,
BENEFICIARY UNDER DEEDS OF TRUSTS RECORDED DECEMBER 10, 1996 AS INSTRUMENT
NO. 19960624030, AND RECORDED APRIL 20, 1999 AS INSTRUMENT NO. 19990288616,
BOTH OF OFFICIAL RECORDS.

BY: DMB ASSOCIATES, INC., AN ARIZONA CORPORATION,
AS MANAGER.

BY: [Signature]
PRINT NAME: TERRY D. RANZALL
PRINT TITLE: Vice President

BY: [Signature]
PRINT NAME: TERRY A. KRAMER
PRINT TITLE: Exec. VP - CFO

AUTOMATIC FIRE SPRINKLER NOTE:

ALL COMMERCIAL STRUCTURES GREATER THAN 6,000 SQUARE FEET; ALL MULTIFAMILY RESIDENTIAL
STRUCTURES; ALL SINGLE-FAMILY STRUCTURES EXCEEDING 5,500 SQUARE FEET, AND ALL STRUCTURES
EXCEEDING FIRE DEPARTMENT ACCESS REQUIREMENTS SHALL BE PROTECTED BY AN AUTOMATIC
SPRINKLER SYSTEM.

SPECIAL FIRE PROTECTION NOTE:

PROPERTY IS IN A SPECIAL FIRE PROTECTION AREA AND MUST MEET ALL REQUIREMENTS
FOR DEVELOPMENT WITHIN THE AREA.

HIGH FIRE HAZARD AREA NOTE:

THE LOTS SHOWN ON THIS MAP ARE IN A HIGH FIRE HAZARD AREA DUE TO
WLD LAND EXPOSURE.

NOTE:

SEE SHEET 2 FOR NOTARY ACKNOWLEDGMENTS AND SIGNATURE OMISSIONS.

SURVEYOR'S STATEMENT:

I HEREBY STATE THAT THIS MAP CONSISTING OF 13 SHEETS, CORRECTLY REPRESENTS A TRUE AND
COMPLETE SURVEY AS SHOWN MADE IN JANUARY, 1999; WAS MADE BY ME OR UNDER MY DIRECTION;
THAT THE MONUMENTS ARE OF THE CHARACTER AND OCCUPY OR WILL OCCUPY THE POSITIONS
INDICATED BY SAID MAP; AND THAT SAID MONUMENTS WILL BE SUFFICIENT TO ENABLE THE
SURVEY TO BE RETRACED.




[Signature]
JAMES F. GILLEN
L.S. 5557
EXPIRATION DATE: 9/30/05

COUNTY SURVEYOR'S STATEMENT:

I HEREBY STATE THAT I HAVE EXAMINED THIS MAP AND HAVE FOUND IT TO BE
SUBSTANTIALLY IN CONFORMANCE WITH THE TENTATIVE MAP AS FILED WITH, AMENDED AND
APPROVED BY THE ORANGE COUNTY SUBDIVISION COMMITTEE; THAT ALL PROVISIONS OF THE
SUBDIVISION MAP ACT AND COUNTY SUBDIVISION REGULATIONS HAVE BEEN COMPLIED WITH
AND I AM SATISFIED SAID MAP IS TECHNICALLY CORRECT.

DATED THIS 28TH DAY OF DECEMBER, 2002.

[Signature]
JOHN CANAS, COUNTY SURVEYOR
L.S. 4408 EXPIRATION DATE: 09-30-05

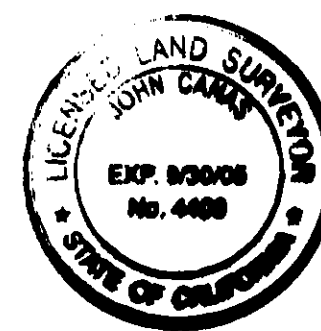

COUNTY TREASURER-TAX COLLECTOR'S CERTIFICATE:

STATE OF CALIFORNIA))
COUNTY OF ORANGE)

I HEREBY CERTIFY THAT ACCORDING TO THE RECORDS OF MY OFFICE THERE ARE NO LIENS
AGAINST THE LAND COVERED BY THIS MAP OR ANY PART THEREOF FOR UNPAID STATE,
COUNTY, MUNICIPAL OR LOCAL TAXES OR SPECIAL ASSESSMENTS COLLECTED AS TAXES,
EXCEPT TAXES OR SPECIAL ASSESSMENTS COLLECTED AS TAXES NOT YET PAYABLE.

AND DO ALSO HEREBY CERTIFY TO THE RECORDER OF ORANGE COUNTY THAT THE PROVISIONS
OF THE SUBDIVISION MAP ACT HAVE BEEN COMPLIED WITH REGARDING DEPOSITS TO SECURE
THE PAYMENT OF TAXES OR SPECIAL ASSESSMENTS COLLECTED AS TAXES ON THE LAND
COVERED BY THIS MAP.

DATED THIS 2nd DAY OF January, 2002.

[Signature]
JOHN M.W. MOORLACH
COUNTY TREASURER-TAX COLLECTOR

BY: [Signature]
DEPUTY TREASURER-TAX COLLECTOR

CLERK OF THE BOARD OF SUPERVISORS' CERTIFICATE:

STATE OF CALIFORNIA))
COUNTY OF ORANGE)

I HEREBY CERTIFY THAT THIS MAP WAS PRESENTED FOR APPROVAL TO THE BOARD OF
SUPERVISORS OF ORANGE COUNTY AT A REGULAR MEETING THEREOF HELD ON THE 16TH DAY
OF January, 2002, AND THAT THEREUPON SAID BOARD DID, BY AN ORDER DULY PASSED
AND ENTERED, APPROVE SAID MAP AND DID ACCEPT ON BEHALF OF THE PUBLIC, SUBJECT TO
IMPROVEMENTS: THE DEDICATION FOR STREET PURPOSES OF : DORRANCE DRIVE, CREIGHTON PLACE,
UNIVERSITY AVENUE, ETON PLACE, AND O'NEILL DRIVE.

AND DID ALSO ACCEPT ON BEHALF OF THE COUNTY OF ORANGE:

1. THE EASEMENTS FOR SIDEWALK PURPOSES AS DEDICATED.
2. THE EASEMENTS FOR STORM DRAIN PURPOSES AS DEDICATED.
3. THE EASEMENT FOR SCENIC PRESERVATION PURPOSES AS DEDICATED.

4. THE VEHICULAR ACCESS RIGHTS TO O'NEILL DRIVE AS RELEASED AND RELINQUISHED.

AND DID NOT ACCEPT THE IRREVOCABLE OFFER OF LOTS 2, 3, 6, AND 10 FOR LOCAL PARK
PURPOSES AS DEDICATED.

AND DID ALSO APPROVE SUBJECT MAP PURSUANT TO THE PROVISIONS
OF SECTION 66436(b)(3) OF THE SUBDIVISION MAP ACT.

DATED THIS 16TH DAY OF January, 2002.

[Signature]
DARLENE J. BLOOM
CLERK OF THE BOARD OF SUPERVISORS



SHEET 2 OF 13 SHEETS

TRACT NO. 16203

FINAL UNIT OF VESTING
TENTATIVE TRACT NO. 16203

IN THE UNINCORPORATED TERRITORY OF ORANGE COUNTY, CALIFORNIA

DATE OF SURVEY:
JANUARY 1999

OCTOBER 2001

JAMES F. GILLEN, L.S. 5557

HUITT-ZOLIARS

13 NUMBERED LOTS AND 24 LETTERED LOTS

142.159 ACRES

DMB LADERA, L.L.C.

STATE OF CALIFORNIA)
COUNTY OF ORANGE)

ON THIS 12th DAY OF November, 2001, BEFORE ME,
Tina T. Baker, A NOTARY PUBLIC IN AND FOR SAID STATE,
 PERSONALLY APPEARED Donald T. Stahl AND
Stephen C. Schmal, PERSONALLY KNOWN TO ME OR PROVED TO ME
 ON THE BASIS OF SATISFACTORY EVIDENCE TO BE THE PERSONS WHOSE NAMES
 ARE SUBSCRIBED TO THE WITHIN INSTRUMENT AND ACKNOWLEDGED TO ME THAT
 THEY EXECUTED THE SAME IN THEIR AUTHORIZED CAPACITIES, AND THAT BY THEIR
 SIGNATURES ON THE INSTRUMENT THE PERSONS, OR THE ENTITY UPON BEHALF
 OF WHICH THE PERSONS ACTED, EXECUTED THE INSTRUMENT.

WITNESS MY HAND:

MY COMMISSION EXPIRES

8/28/04

Tina T. Baker
 NOTARY PUBLIC IN AND FOR SAID STATE

MY PRINCIPAL PLACE OF BUSINESS
 IS IN Orange COUNTY.

Tina T. Baker
 PRINT NAME

DMB CONSOLIDATED HOLDINGS, L.L.C.

STATE OF Arizona)
COUNTY OF Maricopa)

ON THIS 18th DAY OF November, 2001, BEFORE ME,
Carolynn Snedden, A NOTARY PUBLIC IN AND FOR SAID STATE,
 PERSONALLY APPEARED Terry D. Randall AND
Timothy A. Koeber, PERSONALLY KNOWN TO ME OR PROVED TO ME
 ON THE BASIS OF SATISFACTORY EVIDENCE TO BE THE PERSONS WHOSE NAMES
 ARE SUBSCRIBED TO THE WITHIN INSTRUMENT AND ACKNOWLEDGED TO ME THAT
 THEY EXECUTED THE SAME IN THEIR AUTHORIZED CAPACITIES, AND THAT BY THEIR
 SIGNATURES ON THE INSTRUMENT THE PERSONS, OR THE ENTITY UPON BEHALF
 OF WHICH THE PERSONS ACTED, EXECUTED THE INSTRUMENT.

WITNESS MY HAND:

MY COMMISSION EXPIRES

07/14/02

Carolynn Snedden
 NOTARY PUBLIC IN AND FOR SAID STATE

MY PRINCIPAL PLACE OF BUSINESS
 IS IN Maricopa COUNTY.

Carolynn Snedden
 PRINT NAME

SIGNATURE OMISSIONS:

IN ACCORDANCE WITH THE PROVISIONS OF SECTION 664.36(a) (3) OF THE SUBDIVISION
 MAP ACT, THE FOLLOWING SIGNATURES HAVE BEEN OMITTED:

1. SOUTHERN CALIFORNIA EDISON COMPANY, HOLDER OF EASEMENTS FOR PUBLIC UTILITIES AND INCIDENTAL PURPOSES RECORDED APRIL 16, 1965 IN BOOK 7485, PAGE 714, AND RECORDED JUNE 16, 1966 IN BOOK 7962, PAGE 126, BOTH OF OFFICIAL RECORDS.
2. SFPP, L.P., HOLDER OF AN EASEMENT FOR PUBLIC UTILITIES AND INCIDENTAL PURPOSES RECORDED DECEMBER 6, 1999 AS INSTRUMENT NO. 19990831017 AS AMENDED BY A DOCUMENT RECORDED NOVEMBER 5, 2001 AS INSTRUMENT NO. 20010787529, BOTH OF OFFICIAL RECORDS.
3. SAN DIEGO GAS & ELECTRIC COMPANY, HOLDER OF UTILITY EASEMENTS RECORDED FEBRUARY 10, 1993 AS INSTRUMENT NO. 93-091210, RECORDED JANUARY 4, 2001 AS INSTRUMENT NO. 20010004357, AND RECORDED JANUARY 9, 2001 AS INSTRUMENT NO. 20010014545, ALL OF OFFICIAL RECORDS.
4. LADERA DEVELOPMENT COMPANY, L.L.C., HOLDER OF OIL, GAS, MINERAL, AND WATER RIGHTS RECORDED DECEMBER 10, 1996 AS INSTRUMENT NO. 19960624029 OF OFFICIAL RECORDS.

EASEMENT NOTES:

- (A) INDICATES EASEMENT FOR SCENIC PRESERVATION PURPOSES DEDICATED TO THE COUNTY OF ORANGE.
- (B) INDICATES SIDEWALK EASEMENT DEDICATED TO THE COUNTY OF ORANGE.
- (C) INDICATES A UTILITY EASEMENT TO SAN DIEGO GAS AND ELECTRIC COMPANY PER INSTRUMENT NO. 20010014545, O.R.
- (D) INDICATES STORM DRAIN EASEMENT DEDICATED TO THE COUNTY OF ORANGE.
- (E) INDICATES A UTILITY EASEMENT TO SOUTHERN CALIFORNIA EDISON COMPANY PER BOOK 7962, PAGE 126, O.R.
- (F) INDICATES A UTILITY EASEMENT DEDICATED TO SAN DIEGO GAS & ELECTRIC COMPANY PER INSTRUMENT NO. 93-091210, O.R.
- (G) INDICATES A UTILITY EASEMENT DEDICATED TO SAN DIEGO GAS & ELECTRIC COMPANY PER INSTRUMENT NO. 20010004357, O.R.
- (H) INDICATES A UTILITY EASEMENT DEDICATED TO SFPP, L.P., PER INSTRUMENT NO. 20010787529.

SHEET 3 OF 13 SHEETS

TRACT NO. 16203

IN THE UNINCORPORATED TERRITORY OF ORANGE COUNTY, CALIFORNIA

OCTOBER 2001


JAMES F. GILLEN, L.S. 5557

DATE OF SURVEY:
JANUARY 1999

HUITT-ZOLIARS

13 NUMBERED LOTS AND 24 LETTERED LOTS

142.159 ACRES

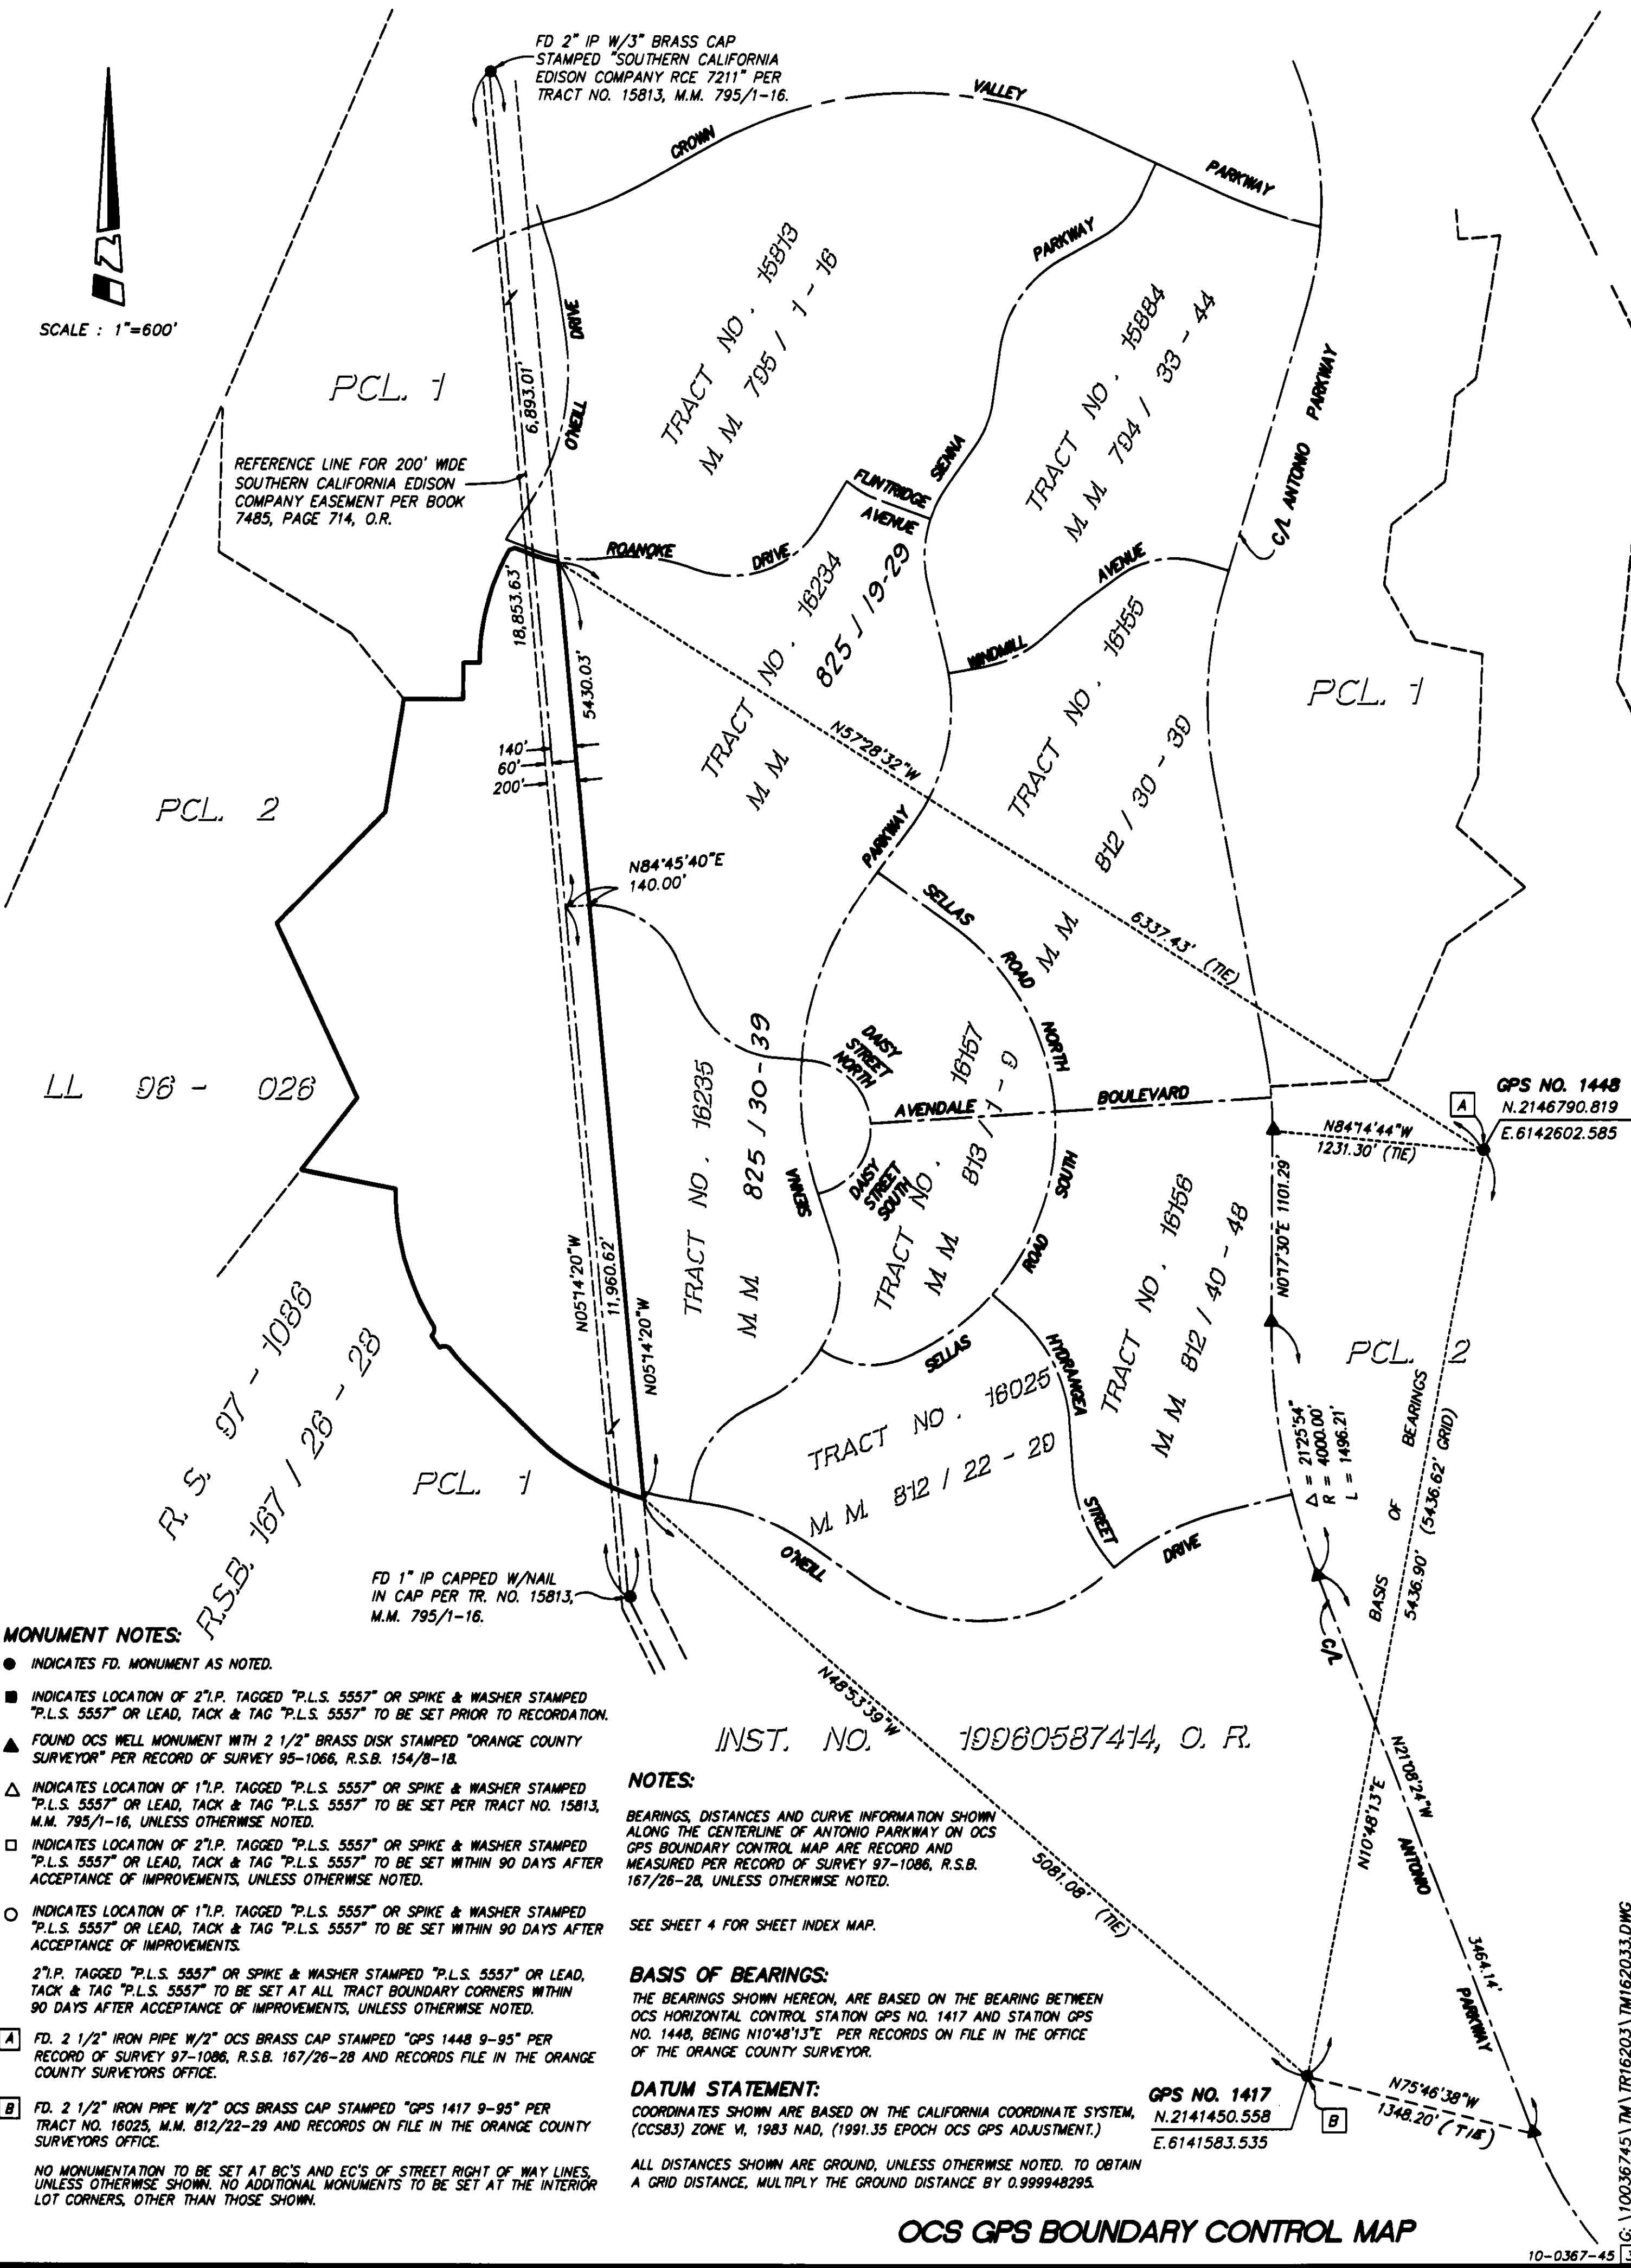

MONUMENT NOTES:

- INDICATES FD. MONUMENT AS NOTED.
- INDICATES LOCATION OF 2" I.P. TAGGED "P.L.S. 5557" OR SPIKE & WASHER STAMPED "P.L.S. 5557" OR LEAD, TACK & TAG "P.L.S. 5557" TO BE SET PRIOR TO RECORDATION.
- ▲ FOUND OCS WELL MONUMENT WITH 2 1/2" BRASS DISK STAMPED "ORANGE COUNTY SURVEYOR" PER RECORD OF SURVEY 95-1066, R.S.B. 154/B-18.
- △ INDICATES LOCATION OF 1" I.P. TAGGED "P.L.S. 5557" OR SPIKE & WASHER STAMPED "P.L.S. 5557" OR LEAD, TACK & TAG "P.L.S. 5557" TO BE SET PER TRACT NO. 15813, M.M. 795/1-16, UNLESS OTHERWISE NOTED.
- INDICATES LOCATION OF 2" I.P. TAGGED "P.L.S. 5557" OR SPIKE & WASHER STAMPED "P.L.S. 5557" OR LEAD, TACK & TAG "P.L.S. 5557" TO BE SET WITHIN 90 DAYS AFTER ACCEPTANCE OF IMPROVEMENTS, UNLESS OTHERWISE NOTED.
- INDICATES LOCATION OF 1" I.P. TAGGED "P.L.S. 5557" OR SPIKE & WASHER STAMPED "P.L.S. 5557" OR LEAD, TACK & TAG "P.L.S. 5557" TO BE SET WITHIN 90 DAYS AFTER ACCEPTANCE OF IMPROVEMENTS.
- 2" I.P. TAGGED "P.L.S. 5557" OR SPIKE & WASHER STAMPED "P.L.S. 5557" OR LEAD, TACK & TAG "P.L.S. 5557" TO BE SET AT ALL TRACT BOUNDARY CORNERS WITHIN 90 DAYS AFTER ACCEPTANCE OF IMPROVEMENTS, UNLESS OTHERWISE NOTED.
- [A] FD. 2 1/2" IRON PIPE W/2" OCS BRASS CAP STAMPED "GPS 1448 9-95" PER RECORD OF SURVEY 97-1086, R.S.B. 167/26-28 AND RECORDS FILE IN THE ORANGE COUNTY SURVEYORS OFFICE.
- [B] FD. 2 1/2" IRON PIPE W/2" OCS BRASS CAP STAMPED "GPS 1417 9-95" PER TRACT NO. 16025, M.M. 812/22-29 AND RECORDS ON FILE IN THE ORANGE COUNTY SURVEYORS OFFICE.

NO MONUMENTATION TO BE SET AT BC'S AND EC'S OF STREET RIGHT OF WAY LINES, UNLESS OTHERWISE SHOWN. NO ADDITIONAL MONUMENTS TO BE SET AT THE INTERIOR LOT CORNERS, OTHER THAN THOSE SHOWN.

NOTES:

BEARINGS, DISTANCES AND CURVE INFORMATION SHOWN ALONG THE CENTERLINE OF ANTONIO PARKWAY ON OCS GPS BOUNDARY CONTROL MAP ARE RECORD AND MEASURED PER RECORD OF SURVEY 97-1086, R.S.B. 167/26-28, UNLESS OTHERWISE NOTED.

SEE SHEET 4 FOR SHEET INDEX MAP.

BASIS OF BEARINGS:

THE BEARINGS SHOWN HEREON, ARE BASED ON THE BEARING BETWEEN OCS HORIZONTAL CONTROL STATION GPS NO. 1417 AND STATION GPS NO. 1448, BEING N10°48'13"E PER RECORDS ON FILE IN THE OFFICE OF THE ORANGE COUNTY SURVEYOR.

DATUM STATEMENT:

COORDINATES SHOWN ARE BASED ON THE CALIFORNIA COORDINATE SYSTEM, (CCS83) ZONE VI, 1983 NAD, (1991.35 EPOCH OCS GPS ADJUSTMENT.)

ALL DISTANCES SHOWN ARE GROUND, UNLESS OTHERWISE NOTED. TO OBTAIN A GRID DISTANCE, MULTIPLY THE GROUND DISTANCE BY 0.999948295.

GPS NO. 1417
N.2141450.558
E.6141583.535

GPS NO. 1448
N.2146790.819
E.6142602.585

OCS GPS BOUNDARY CONTROL MAP

SHEET 4 OF 13 SHEETS

A FINAL UNIT OF VESTING
TENTATIVE TRACT NO. 16203DATE OF SURVEY:
JANUARY 1999**TRACT NO. 16203**

IN THE UNINCORPORATED TERRITORY OF ORANGE COUNTY, CALIFORNIA



OCTOBER 2001

JAMES F. GILLEN, L.S. 5557

HUITT-ZOLIARS

13 NUMBERED LOTS AND 24 LETTERED LOTS

142.159 ACRES

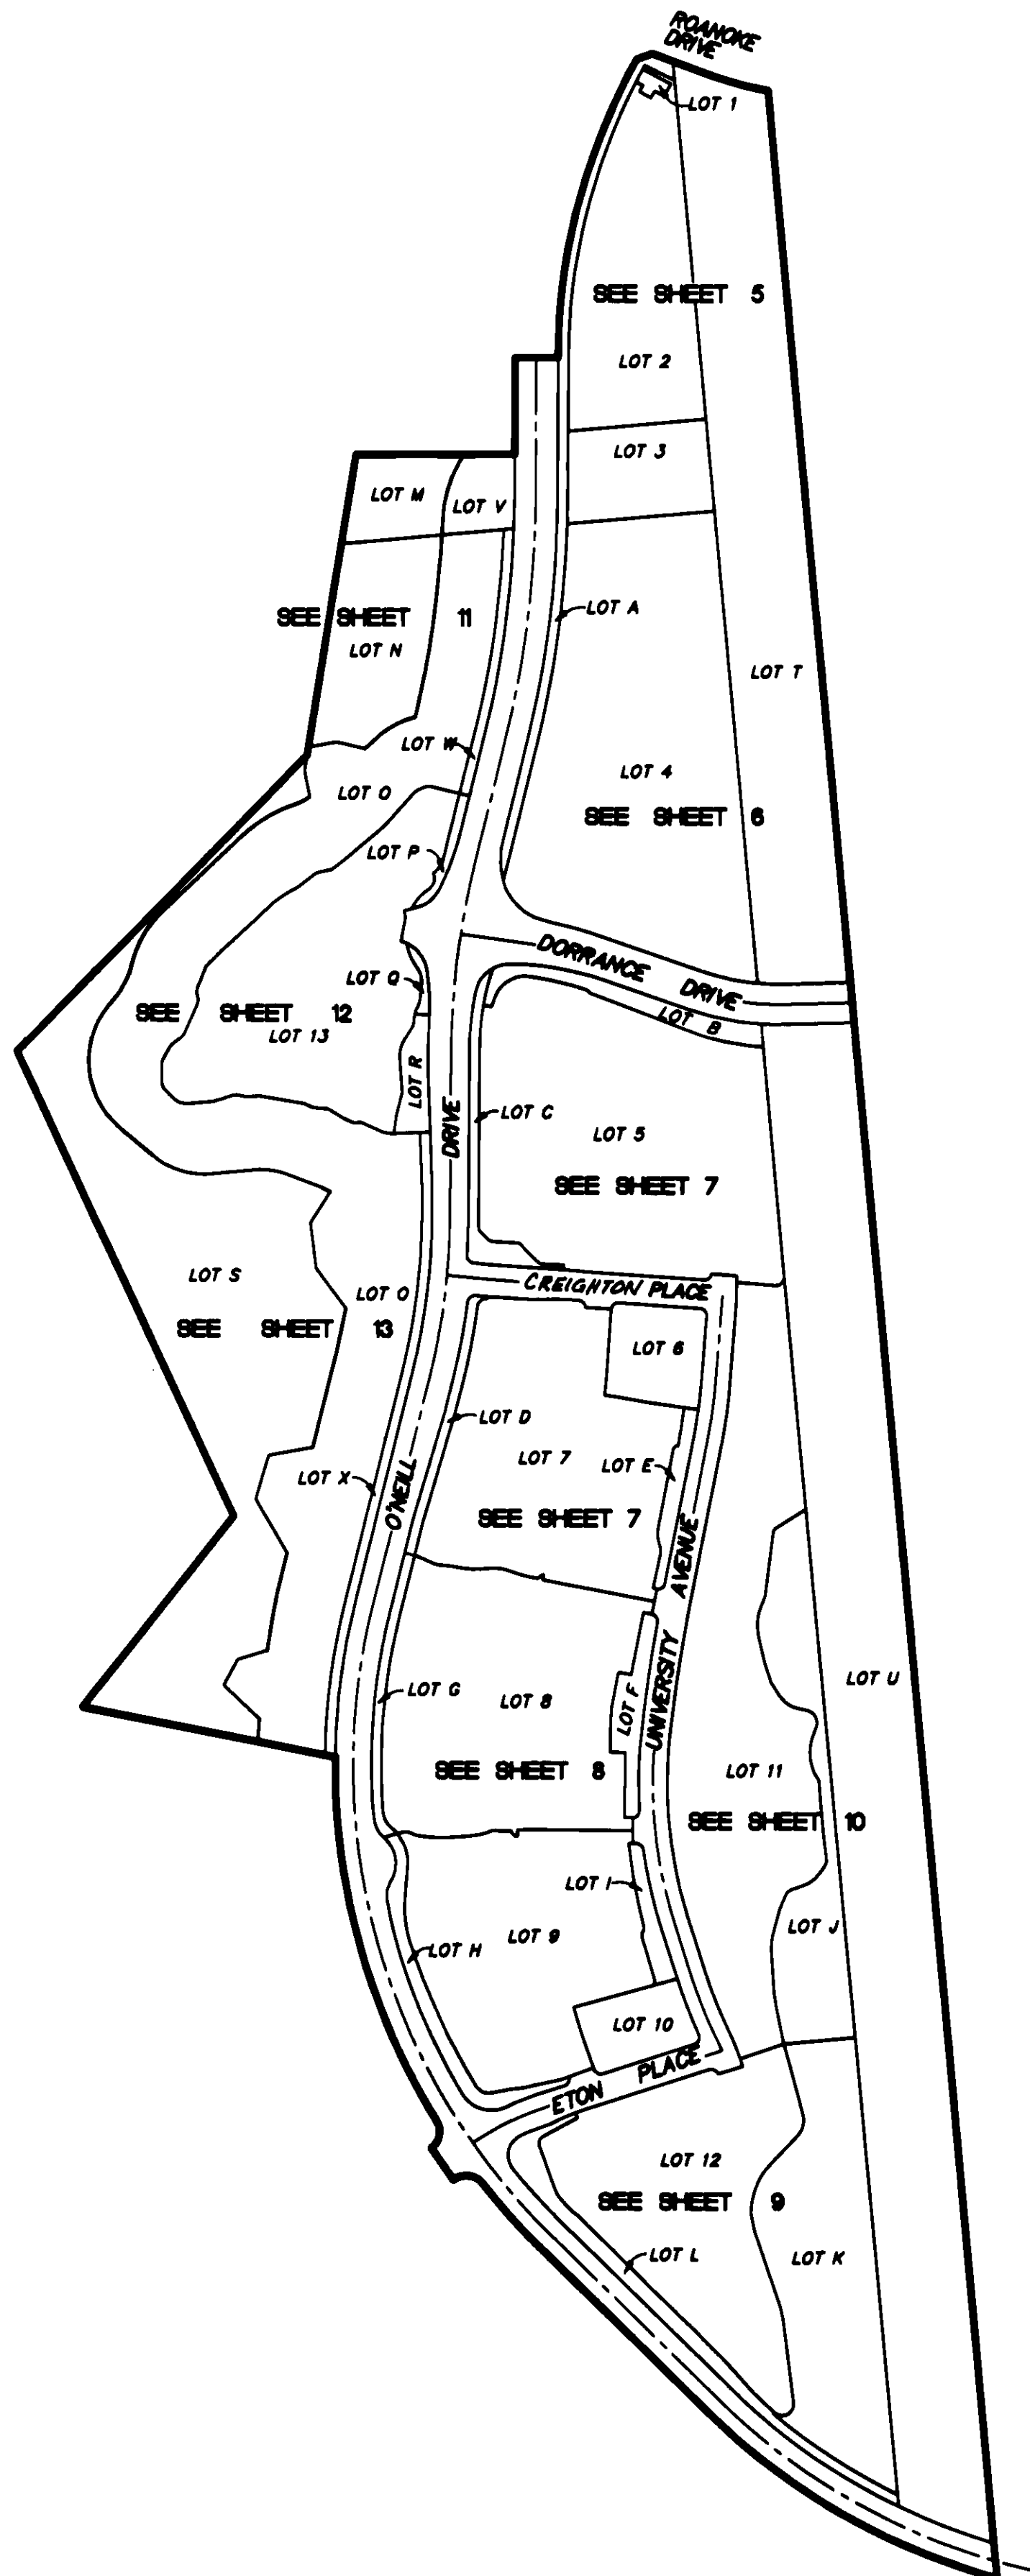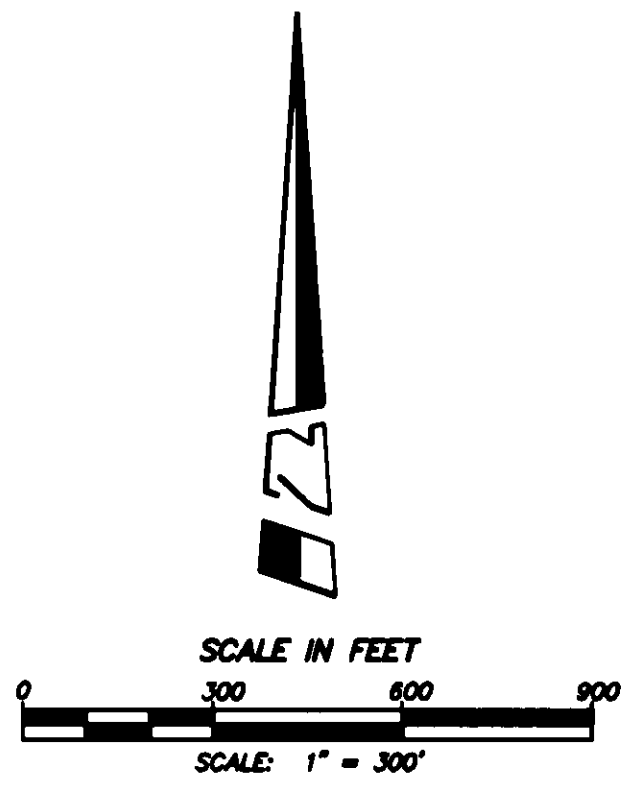**SHEET INDEX MAP**

SHEET 6 OF 13 SHEETS

TRACT NO. 16203

FINAL UNIT OF VESTING
TENTATIVE TRACT NO. 16203

IN THE UNINCORPORATED TERRITORY OF ORANGE COUNTY, CALIFORNIA

OCTOBER 2001



JAMES F. GILLEN, L.S. 5557

DATE OF SURVEY:
JANUARY 1999

HUITT-ZOLIARS

13 NUMBERED LOTS AND 24 LETTERED LOTS

142.159 ACRES

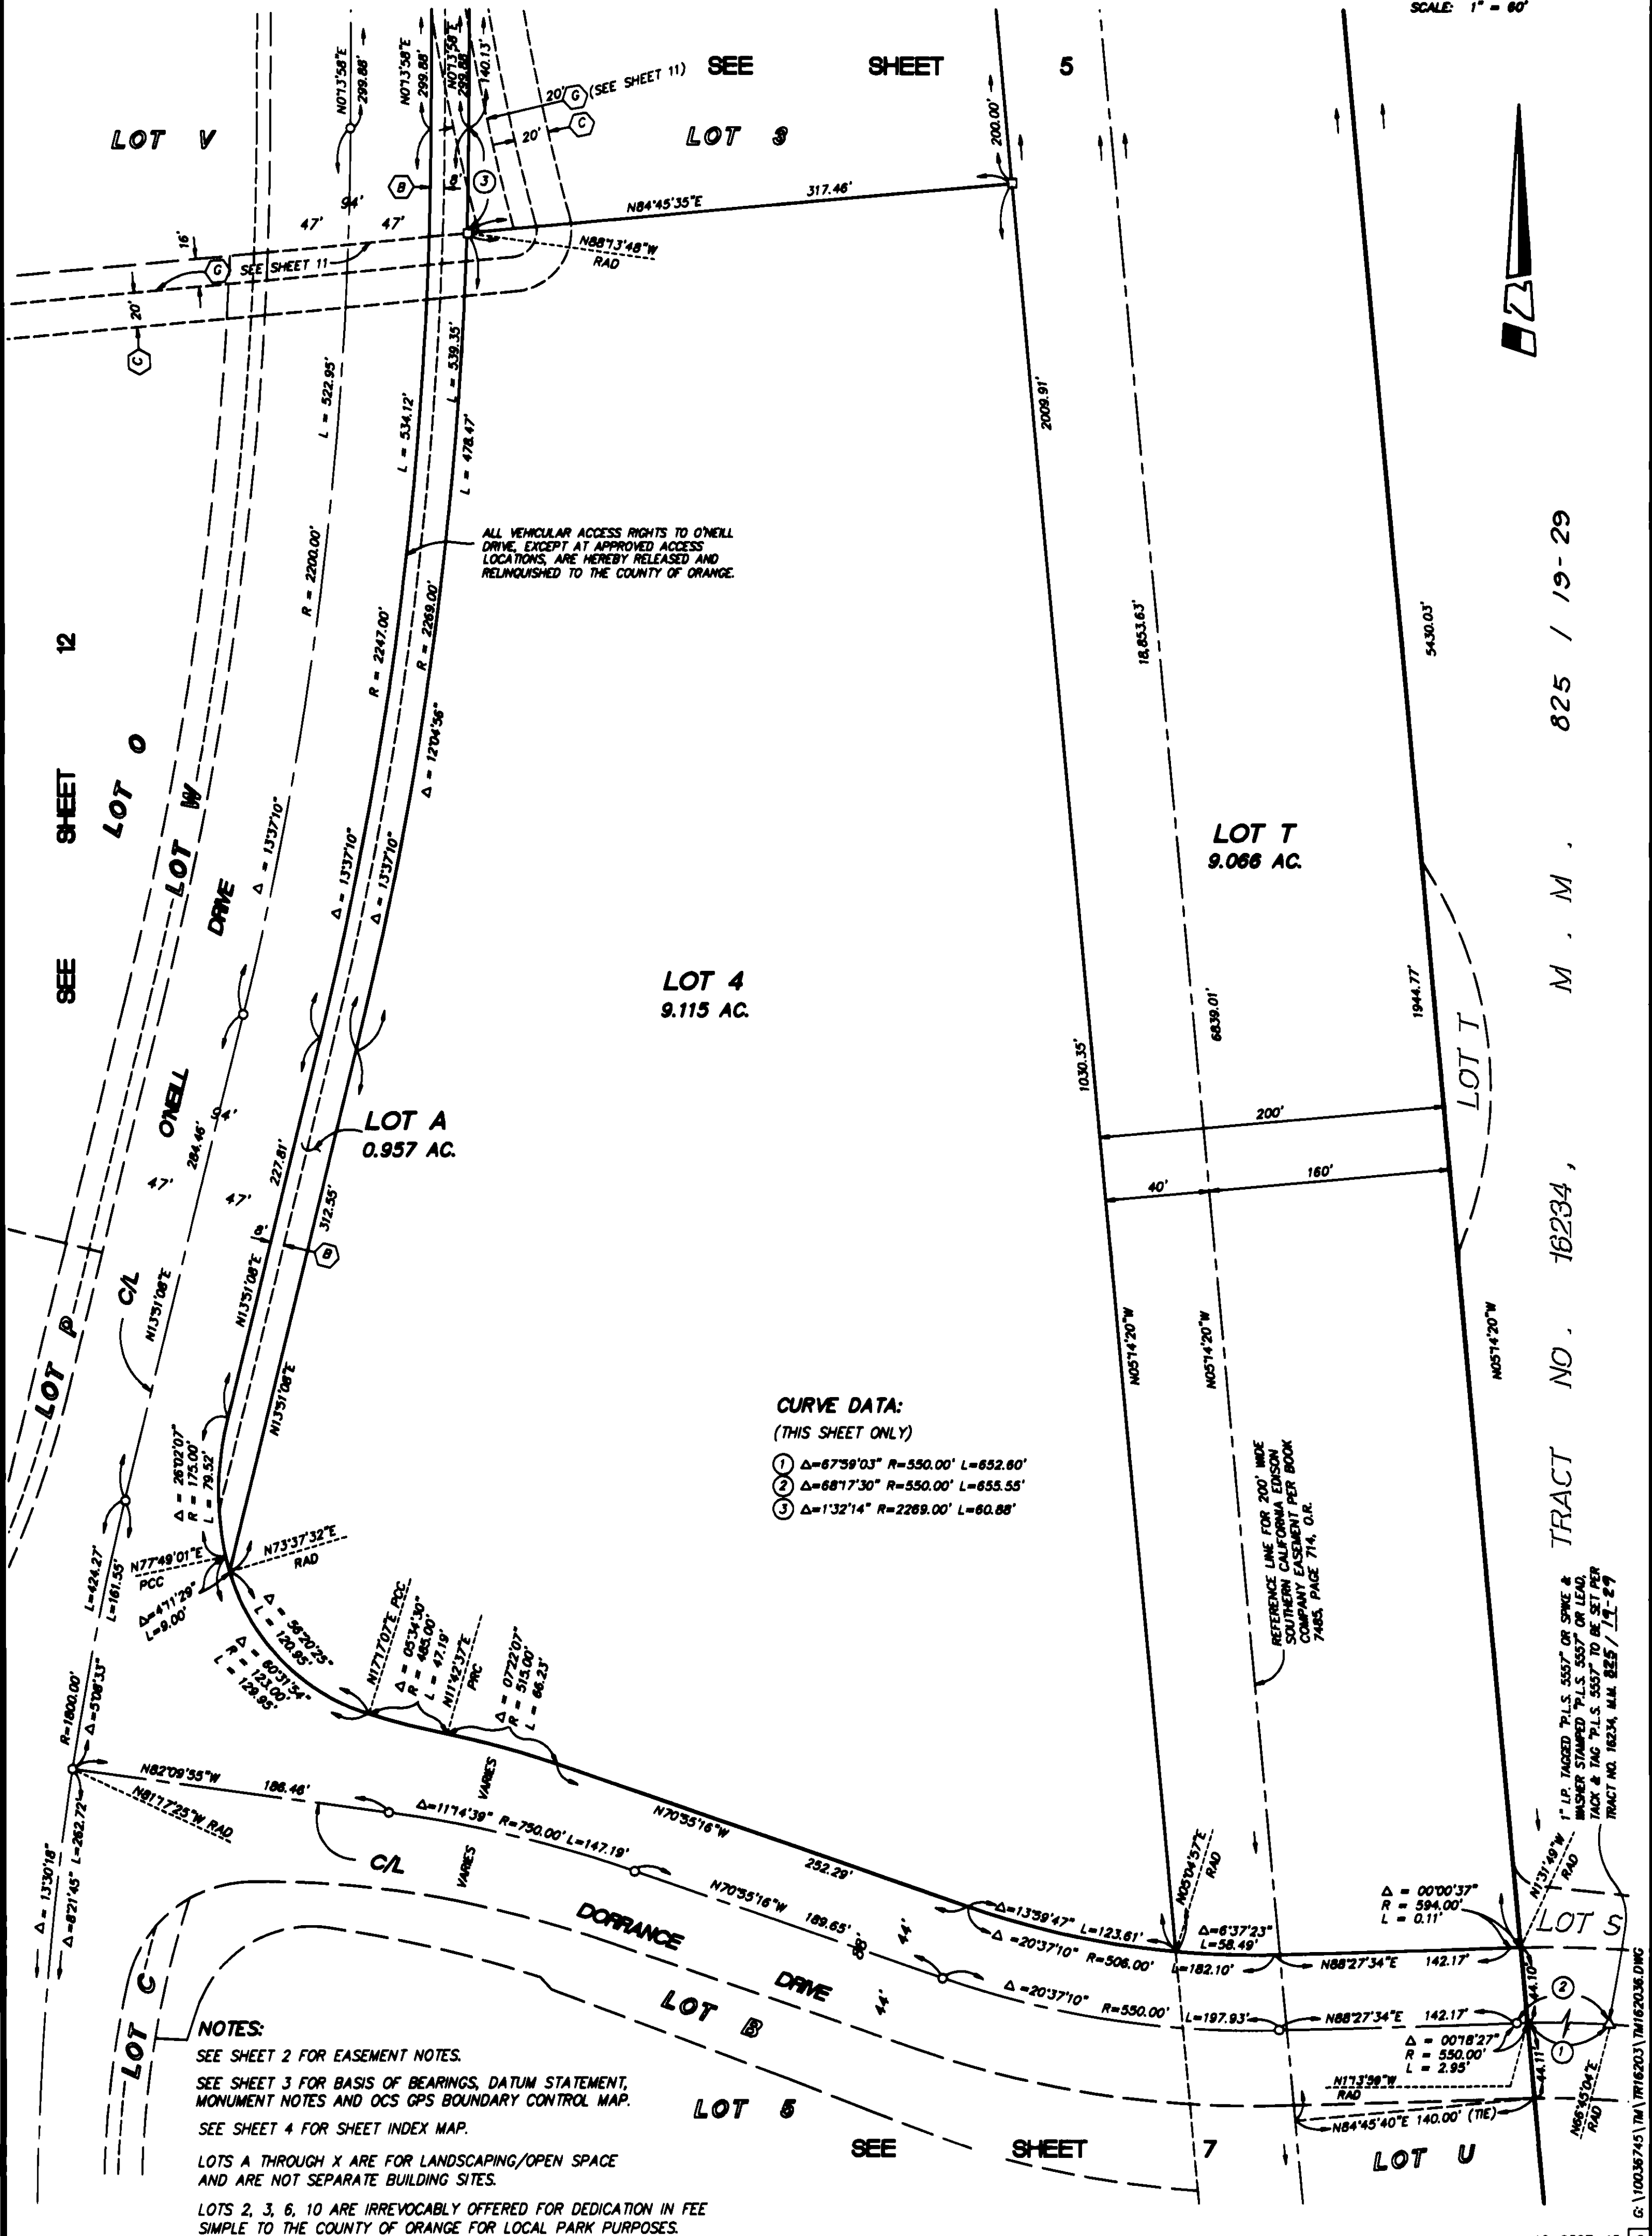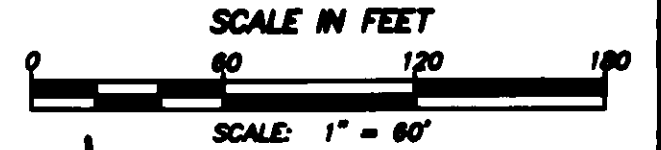

825 / 19-29

M. M.

TRACT NO. 16234,

16234,

1" IP TAPPED TO L.S. 5557 OR SWKE & WALKER STAMPED "P.L.S. 5557" OR LEAD TACK & TAG "P.L.S. 5557" TO BE SET PER TRACT NO. 16203, M.M. 825 / 12-29

SHEET 7 OF 13 SHEETS

TRACT NO. 16203

IN THE UNINCORPORATED TERRITORY OF ORANGE COUNTY, CALIFORNIA

OCTOBER 2001



JAMES F. GILLEN, L.S. 5557

DATE OF SURVEY:
JANUARY 1999

HUITT-ZOLLARS

13 NUMBERED LOTS AND 24 LETTERED LOTS

142.159 ACRES

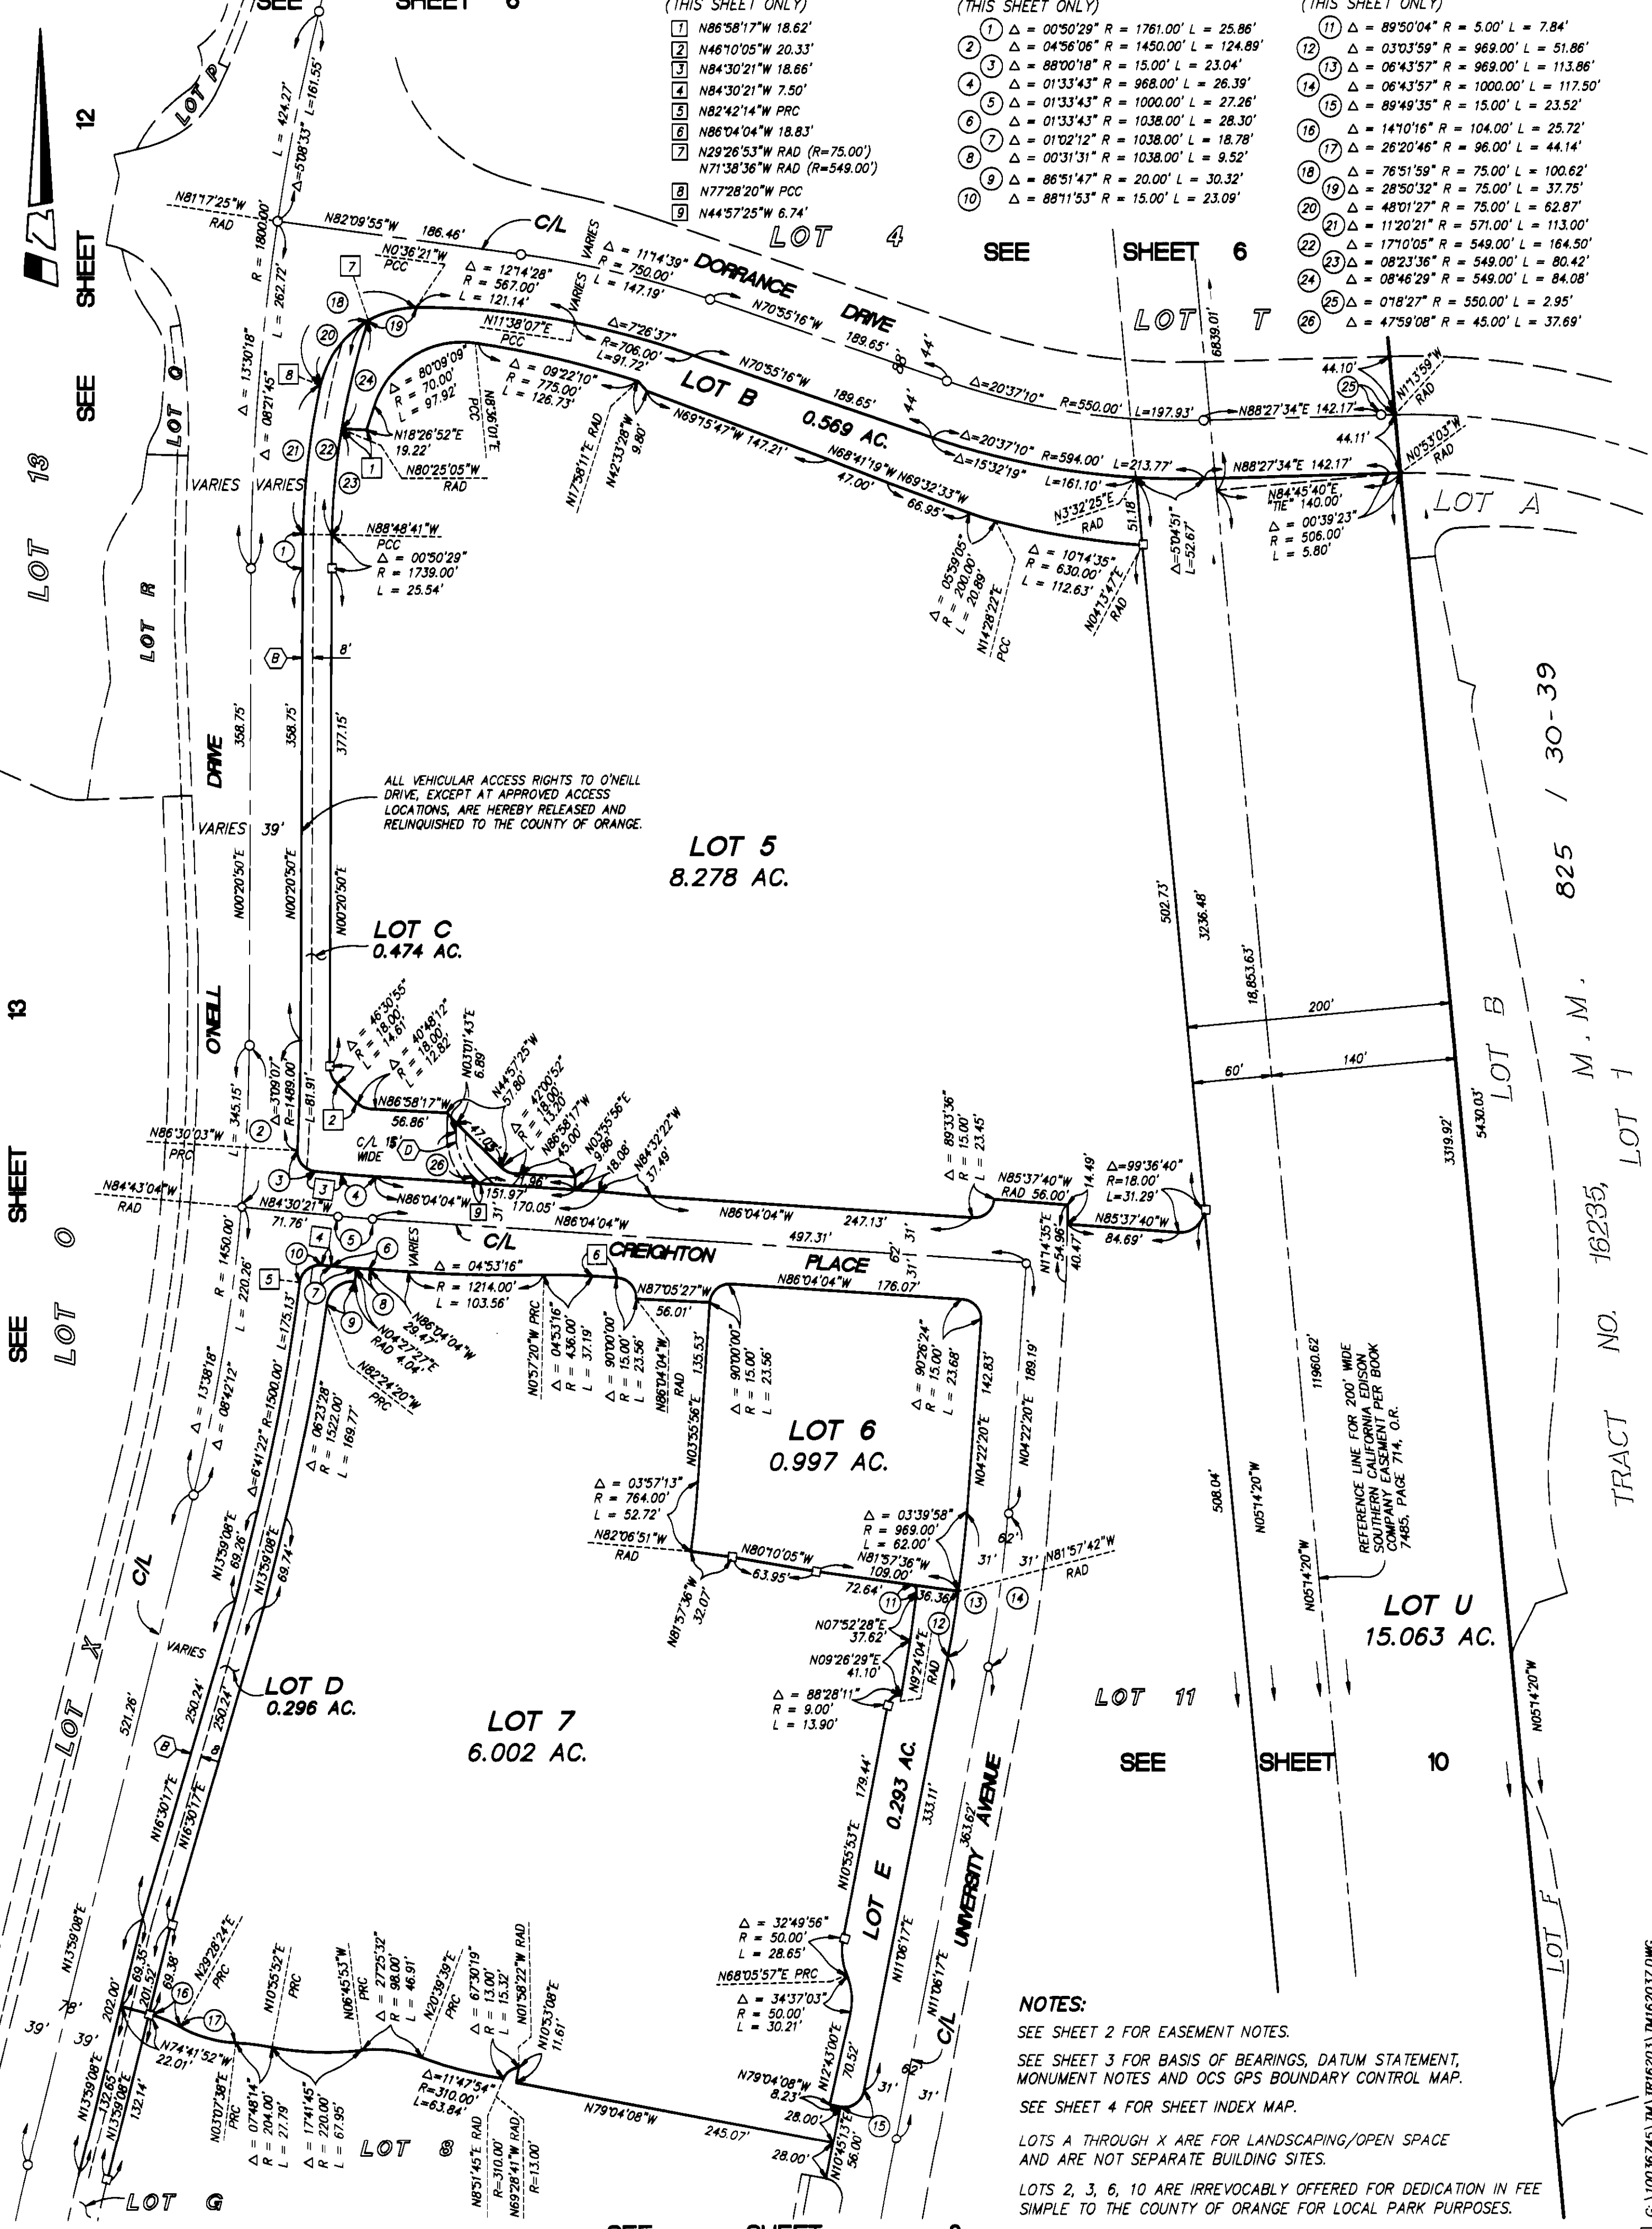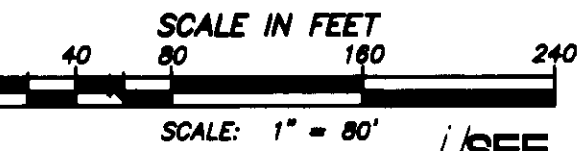

COURSE DATA:
(THIS SHEET ONLY)

- 1 N86°58'17"W 18.62'
- 2 N46°10'05"W 20.33'
- 3 N84°30'21"W 18.66'
- 4 N84°30'21"W 7.50'
- 5 N82°42'14"W PRC
- 6 N86°04'04"W 18.83'
- 7 N29°26'53"W RAD (R=75.00')
- 8 N71°38'36"W RAD (R=549.00')
- 9 N77°28'20"W PCC
- 10 N44°57'25"W 6.74'

CURVE DATA:
(THIS SHEET ONLY)

- 1 Δ = 00°50'29" R = 1761.00' L = 25.86'
- 2 Δ = 04°56'06" R = 1450.00' L = 124.89'
- 3 Δ = 88°00'18" R = 15.00' L = 23.04'
- 4 Δ = 01°33'43" R = 968.00' L = 26.39'
- 5 Δ = 01°33'43" R = 1000.00' L = 27.26'
- 6 Δ = 01°33'43" R = 1038.00' L = 28.30'
- 7 Δ = 01°02'12" R = 1038.00' L = 18.78'
- 8 Δ = 00°31'31" R = 1038.00' L = 9.52'
- 9 Δ = 86°51'47" R = 20.00' L = 30.32'
- 10 Δ = 88°11'53" R = 15.00' L = 23.09'

CURVE DATA:
(THIS SHEET ONLY)

- 11 Δ = 89°50'04" R = 5.00' L = 7.84'
- 12 Δ = 03°03'59" R = 969.00' L = 51.86'
- 13 Δ = 06°43'57" R = 969.00' L = 113.86'
- 14 Δ = 06°43'57" R = 1000.00' L = 117.50'
- 15 Δ = 89°49'35" R = 15.00' L = 23.52'
- 16 Δ = 14°10'16" R = 104.00' L = 25.72'
- 17 Δ = 26°20'46" R = 96.00' L = 44.14'
- 18 Δ = 76°51'59" R = 75.00' L = 100.62'
- 19 Δ = 28°50'32" R = 75.00' L = 37.75'
- 20 Δ = 48°01'27" R = 75.00' L = 62.87'
- 21 Δ = 11°20'21" R = 571.00' L = 113.00'
- 22 Δ = 17°10'05" R = 549.00' L = 164.50'
- 23 Δ = 08°23'36" R = 549.00' L = 80.42'
- 24 Δ = 08°46'29" R = 549.00' L = 84.08'
- 25 Δ = 01°18'27" R = 550.00' L = 2.95'
- 26 Δ = 47°59'08" R = 45.00' L = 37.69'

ALL VEHICULAR ACCESS RIGHTS TO O'NEILL DRIVE, EXCEPT AT APPROVED ACCESS LOCATIONS, ARE HEREBY RELEASED AND RELINQUISHED TO THE COUNTY OF ORANGE.

NOTES:

- SEE SHEET 2 FOR EASEMENT NOTES.
- SEE SHEET 3 FOR BASIS OF BEARINGS, DATUM STATEMENT, MONUMENT NOTES AND OCS GPS BOUNDARY CONTROL MAP.
- SEE SHEET 4 FOR SHEET INDEX MAP.
- LOTS A THROUGH X ARE FOR LANDSCAPING/OPEN SPACE AND ARE NOT SEPARATE BUILDING SITES.
- LOTS 2, 3, 6, 10 ARE IRREVOCABLY OFFERED FOR DEDICATION IN FEE SIMPLE TO THE COUNTY OF ORANGE FOR LOCAL PARK PURPOSES.

G:\10036745\TM\16203\TM16203.DWG

EE SHEET 9

SHEET 9 OF 13 SHEETS

TRACT NO. 16203

IN THE UNINCORPORATED TERRITORY OF ORANGE COUNTY, CALIFORNIA

FINAL UNIT OF VESTING
TENTATIVE TRACT NO. 16203DATE OF SURVEY:
JANUARY 1999



OCTOBER 2001

JAMES F. GILLEN, L.S. 5557

HUITT-ZOLLARS

13 NUMBERED LOTS AND 24 LETTERED LOTS

142.159 ACRES

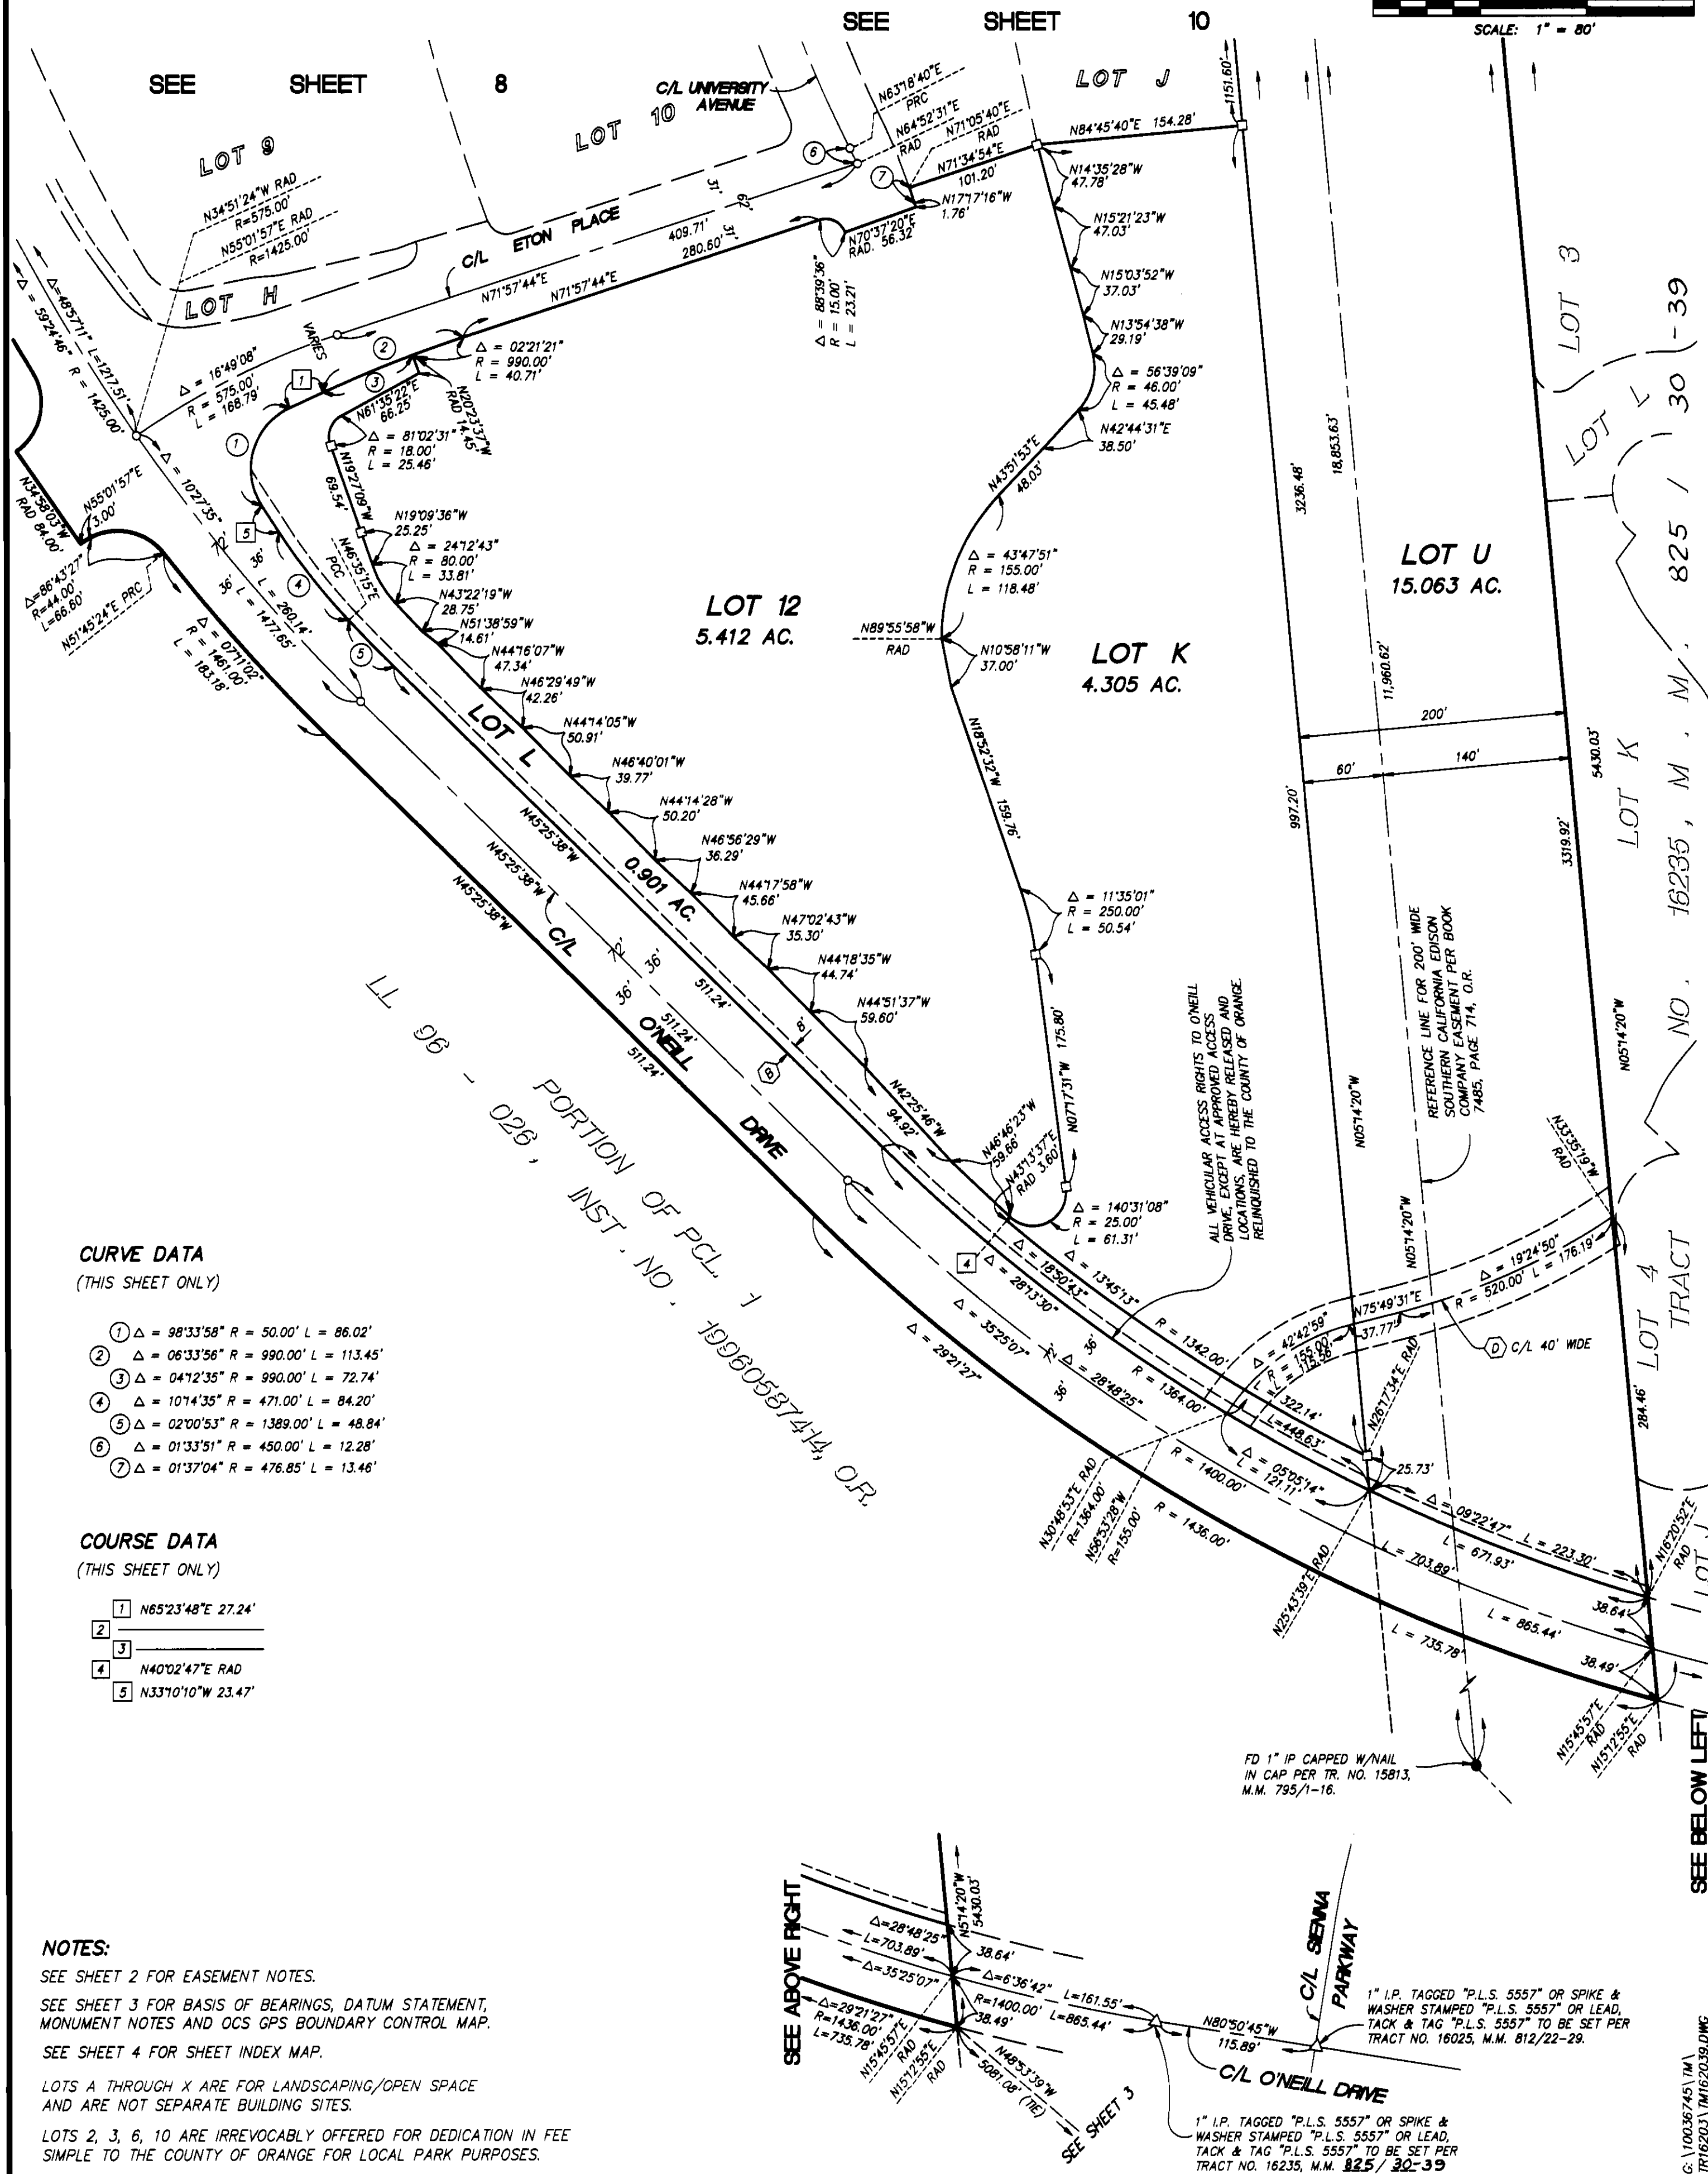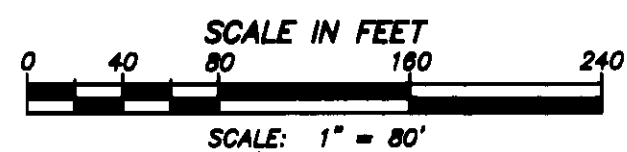

SHEET 10 OF 13 SHEETS

FINAL UNIT OF VESTING
TENTATIVE TRACT NO. 16203DATE OF SURVEY:
JANUARY 1999

TRACT NO. 16203

IN THE UNINCORPORATED TERRITORY OF ORANGE COUNTY, CALIFORNIA


OCTOBER 2001

JAMES F. GILLEN, L.S. 5557

HUITT-ZOLIARS

13 NUMBERED LOTS AND 24 LETTERED LOTS

142.159 ACRES

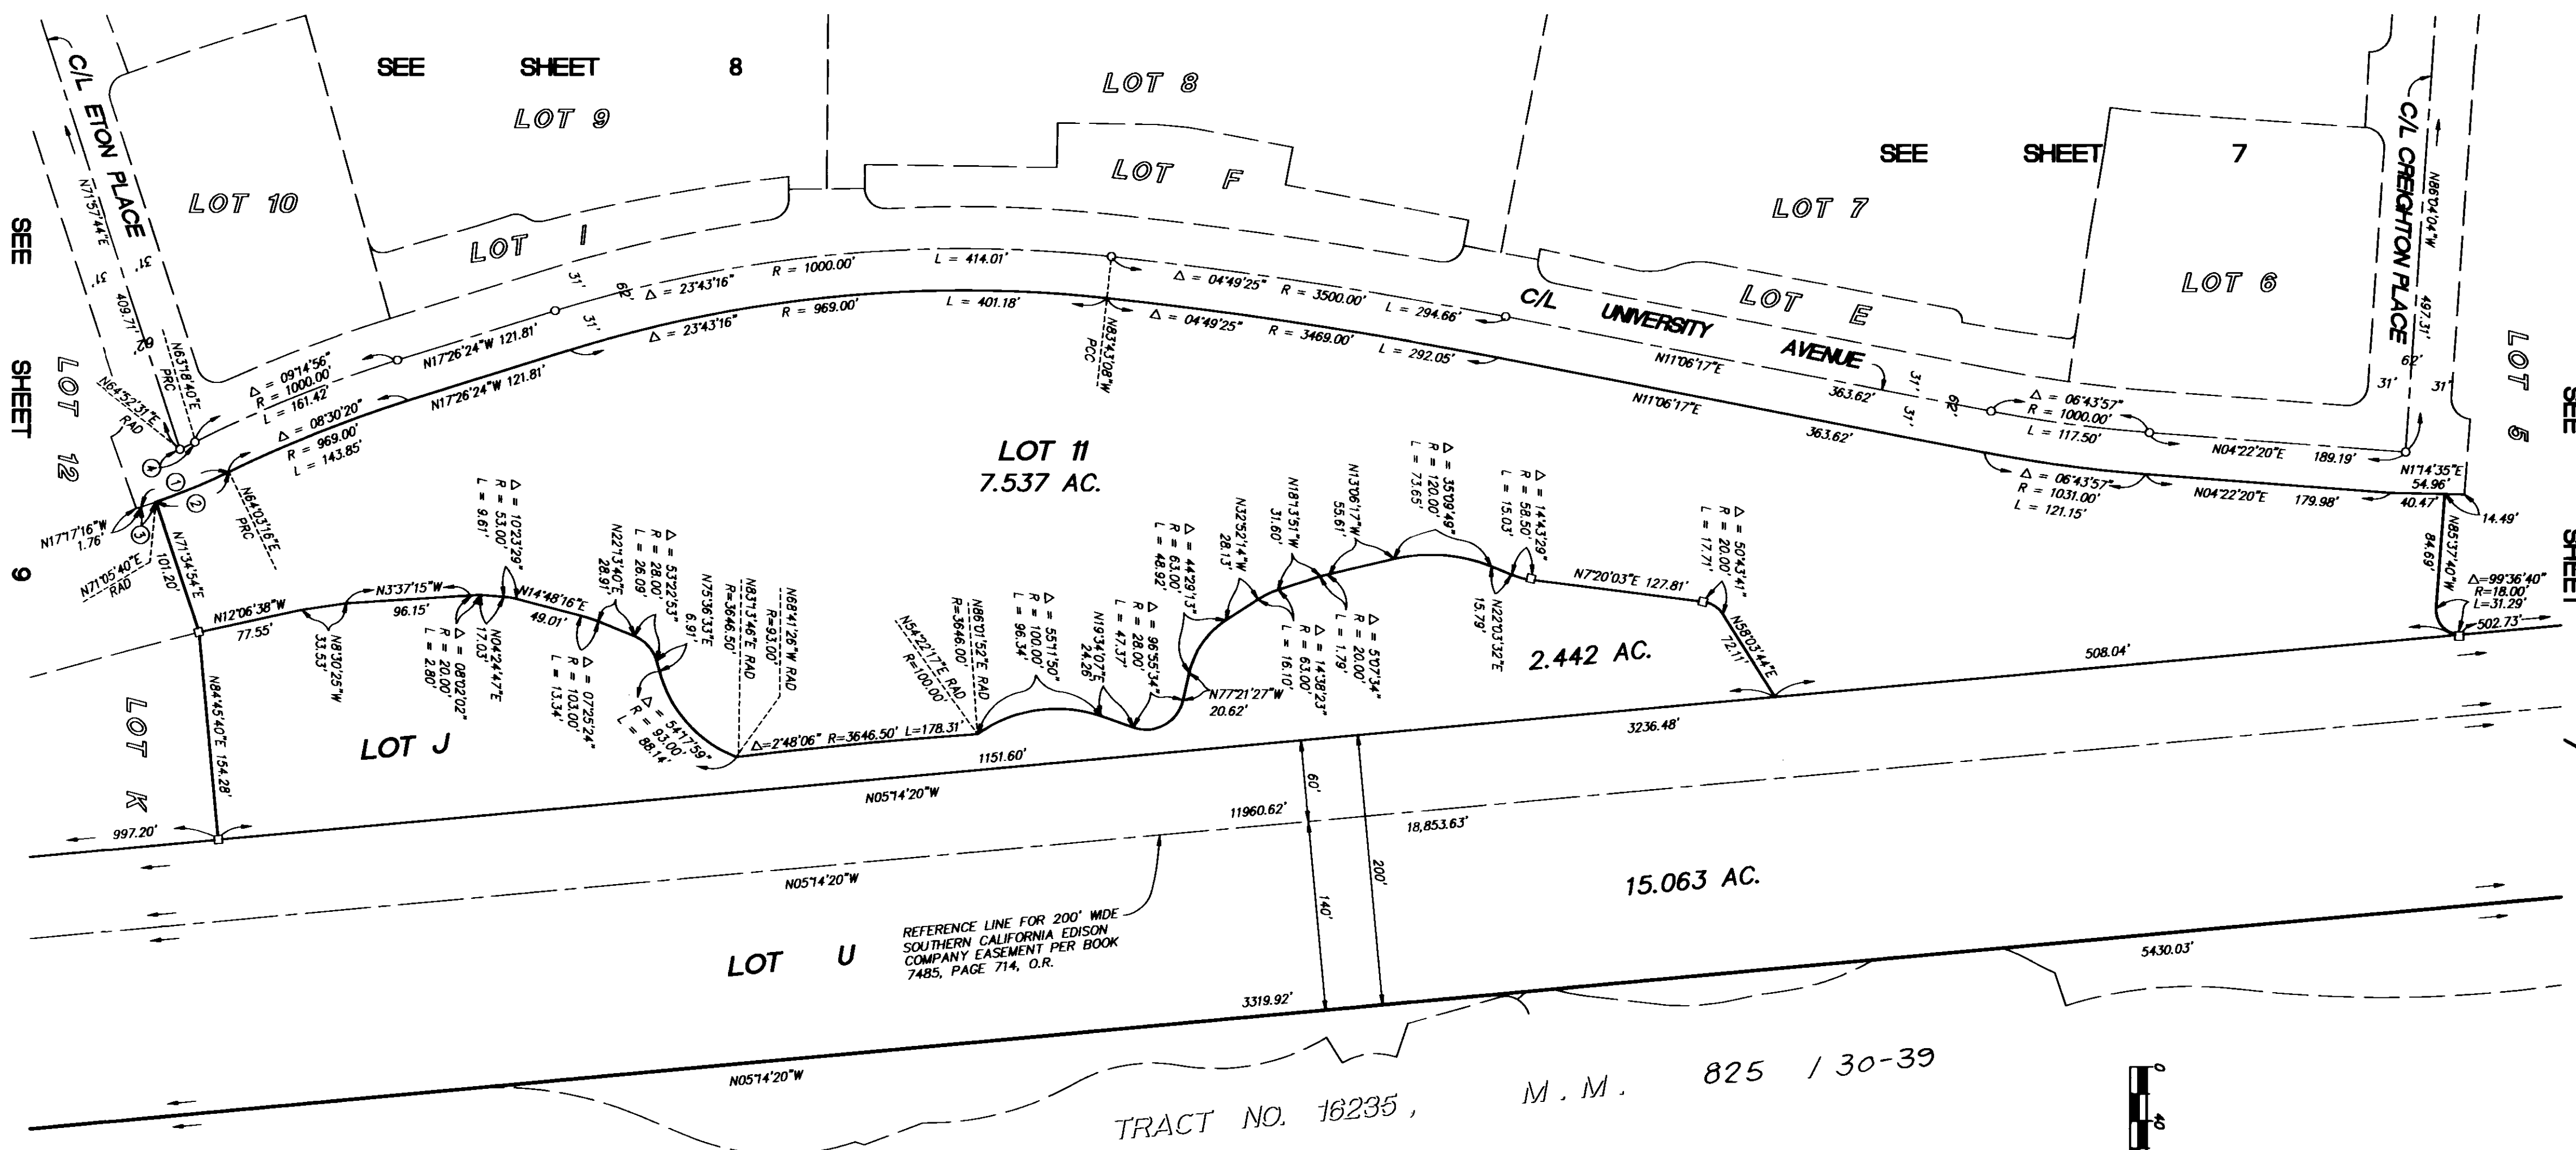

NOTES:

SEE SHEET 2 FOR EASEMENT NOTES.

SEE SHEET 3 FOR BASIS OF BEARINGS, DATUM STATEMENT,
MONUMENT NOTES AND OCS GPS BOUNDARY CONTROL MAP.


SEE SHEET 4 FOR SHEET INDEX MAP.

LOTS A THROUGH X ARE FOR LANDSCAPING/OPEN SPACE
AND ARE NOT SEPARATE BUILDING SITES.LOTS 2, 3, 6, 10 ARE IRREVOCABLY OFFERED FOR DEDICATION IN FEE
SIMPLE TO THE COUNTY OF ORANGE FOR LOCAL PARK PURPOSES.

CURVE DATA

(THIS SHEET ONLY)

- ① $\Delta = 08^{\circ}39'28''$ $R = 476.85'$ $L = 72.06'$
- ② $\Delta = 07^{\circ}02'24''$ $R = 476.85'$ $L = 58.60'$
- ③ $\Delta = 01^{\circ}37'04''$ $R = 476.85'$ $L = 13.46'$
- ④ $\Delta = 01^{\circ}33'51''$ $R = 450.00'$ $L = 12.28'$

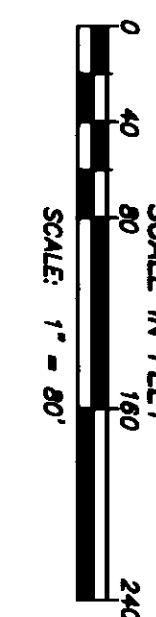

SHEET 11 OF 13 SHEETS

TRACT NO. 16203

IN THE UNINCORPORATED TERRITORY OF ORANGE COUNTY, CALIFORNIA

OCTOBER 2001

JAMES F. GILLEN, L.S. 5557


FINAL UNIT OF VESTING
TENTATIVE TRACT NO. 16203

DATE OF SURVEY:
JANUARY 1999


HUITT-ZOLIARS

13 NUMBERED LOTS AND 24 LETTERED LOTS

142.159 ACRES

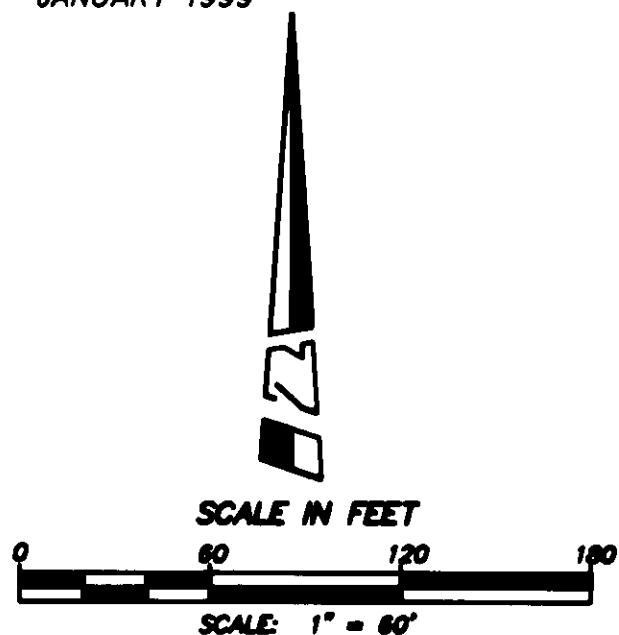

PORTION OF PCL. 2
LL 06 - 026, INST. NO. 10060587414, O.R.

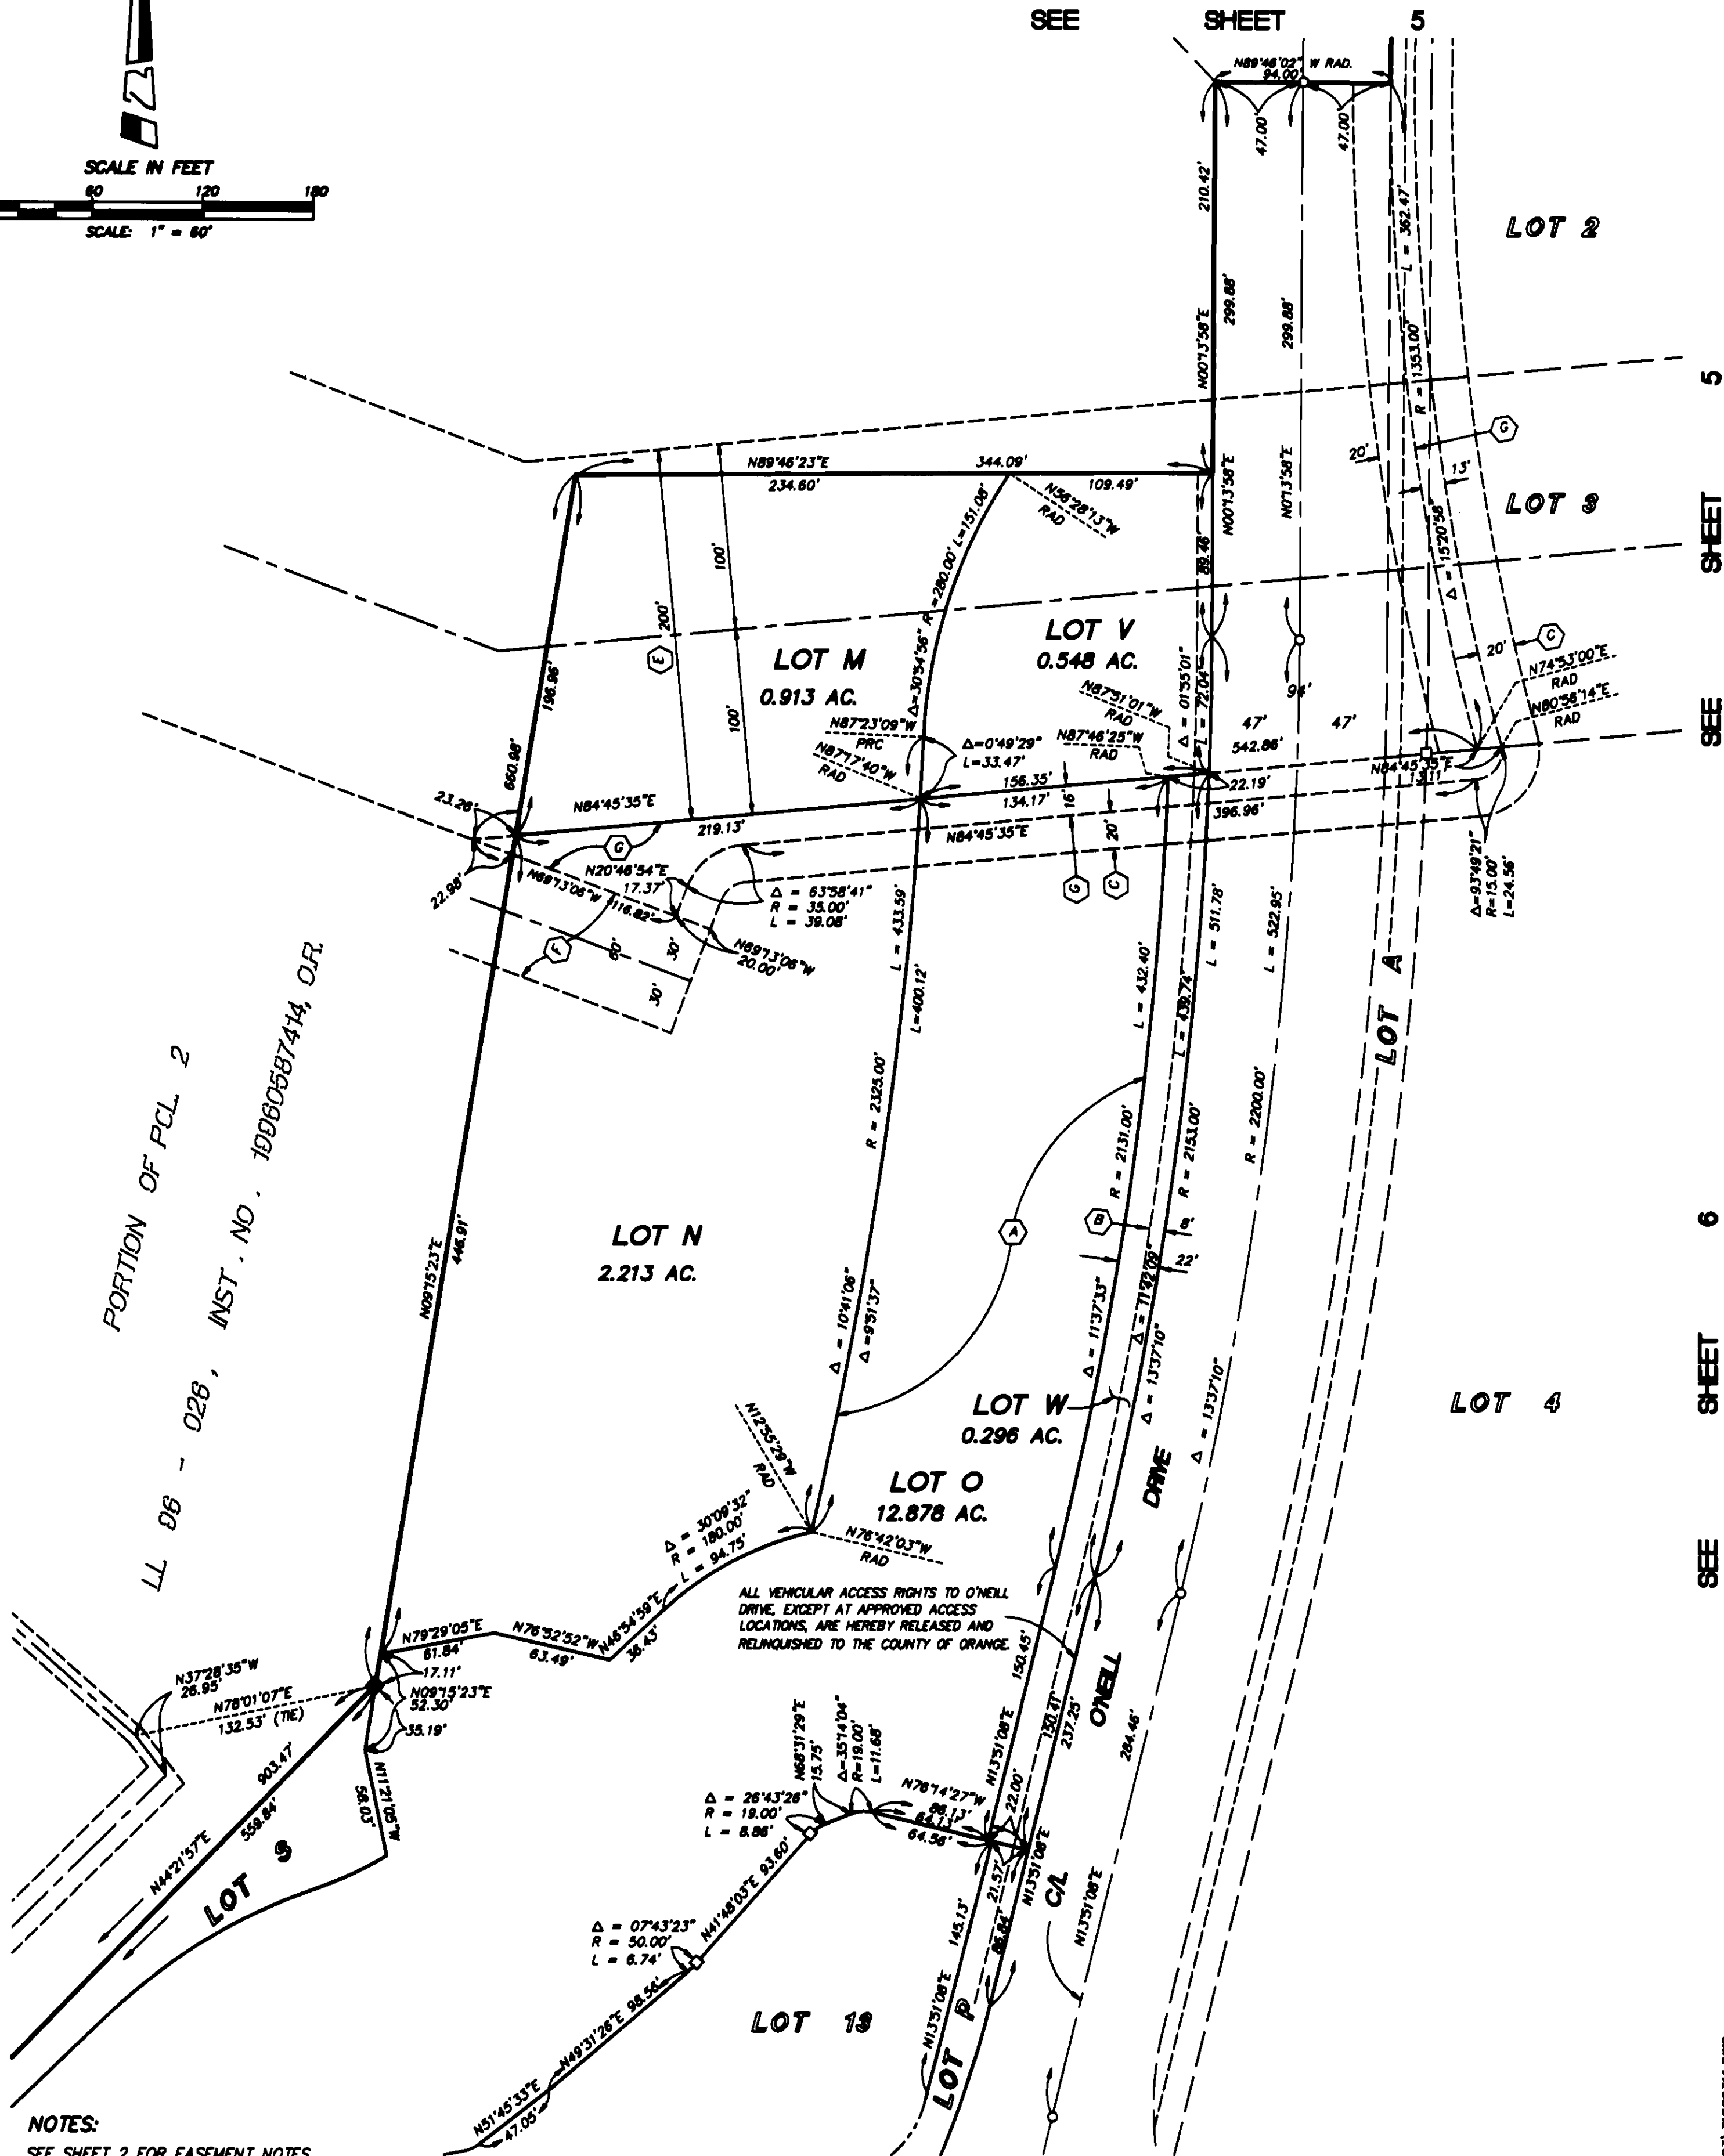

NOTES:

SEE SHEET 2 FOR EASEMENT NOTES.

SEE SHEET 3 FOR BASIS OF BEARINGS, DATUM STATEMENT, MONUMENT NOTES AND OCS GPS BOUNDARY CONTROL MAP.

SEE SHEET 4 FOR SHEET INDEX MAP.

LOTS A THROUGH X ARE FOR LANDSCAPING/OPEN SPACE AND ARE NOT SEPARATE BUILDING SITES.

LOTS 2, 3, 6, 10 ARE IRREVOCABLY OFFERED FOR DEDICATION IN FEE SIMPLE TO THE COUNTY OF ORANGE FOR LOCAL PARK PURPOSES.

SHEET 12 OF 13 SHEETS

FINAL UNIT OF VESTING
TENTATIVE TRACT NO. 16203DATE OF SURVEY:
JANUARY 1999

TRACT NO. 16203

IN THE UNINCORPORATED TERRITORY OF ORANGE COUNTY, CALIFORNIA

OCTOBER 2001

JAMES F. GILLEN, L.S. 5557

HUITT-ZOLIARS

13 NUMBERED LOTS AND 24 LETTERED LOTS


142.159 ACRES

NOTES:

SEE SHEET 2 FOR EASEMENT NOTES.

SEE SHEET 3 FOR BASIS OF BEARINGS, DATUM STATEMENT,
MONUMENT NOTES AND OCS GPS BOUNDARY CONTROL MAP.


SEE SHEET 4 FOR SHEET INDEX MAP.

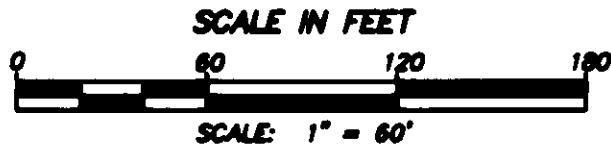LOTS A THROUGH X ARE FOR LANDSCAPING/OPEN SPACE
AND ARE NOT SEPARATE BUILDING SITES.LOTS 2, 3, 6, 10 ARE IRREVOCABLY OFFERED FOR DEDICATION IN FEE
SIMPLE TO THE COUNTY OF ORANGE FOR LOCAL PARK PURPOSES.CURVE DATA:
(THIS SHEET ONLY)

- ① $\Delta = 84^{\circ}34'07''$ R = 25.00' L = 36.90'
- ② $\Delta = 10^{\circ}32'36''$ R = 112.00' L = 20.62'
- ③ $\Delta = 01^{\circ}03'39''$ R = 1872.00' L = 34.66'
- ④ $\Delta = 27^{\circ}55'34''$ R = 40.00' L = 19.50'
- ⑤ $\Delta = 23^{\circ}34'57''$ R = 40.00' L = 16.46'
- ⑥ $\Delta = 16^{\circ}28'40''$ R = 54.00' L = 15.53'
- ⑦ $\Delta = 10^{\circ}07'06''$ R = 560.00' L = 98.90'
- ⑧ $\Delta = 00^{\circ}56'45''$ R = 560.00' L = 9.24'
- ⑨ $\Delta = 03^{\circ}31'44''$ R = 54.00' L = 3.33'
- ⑩ $\Delta = 12^{\circ}56'56''$ R = 54.00' L = 12.20'

COURSE DATA:
(THIS SHEET ONLY)

- 1 N88°15'35"W RAD
- 2 N80°00'45"E RAD (R=120.00')
- N22°13'27"E RAD (R=54.00')

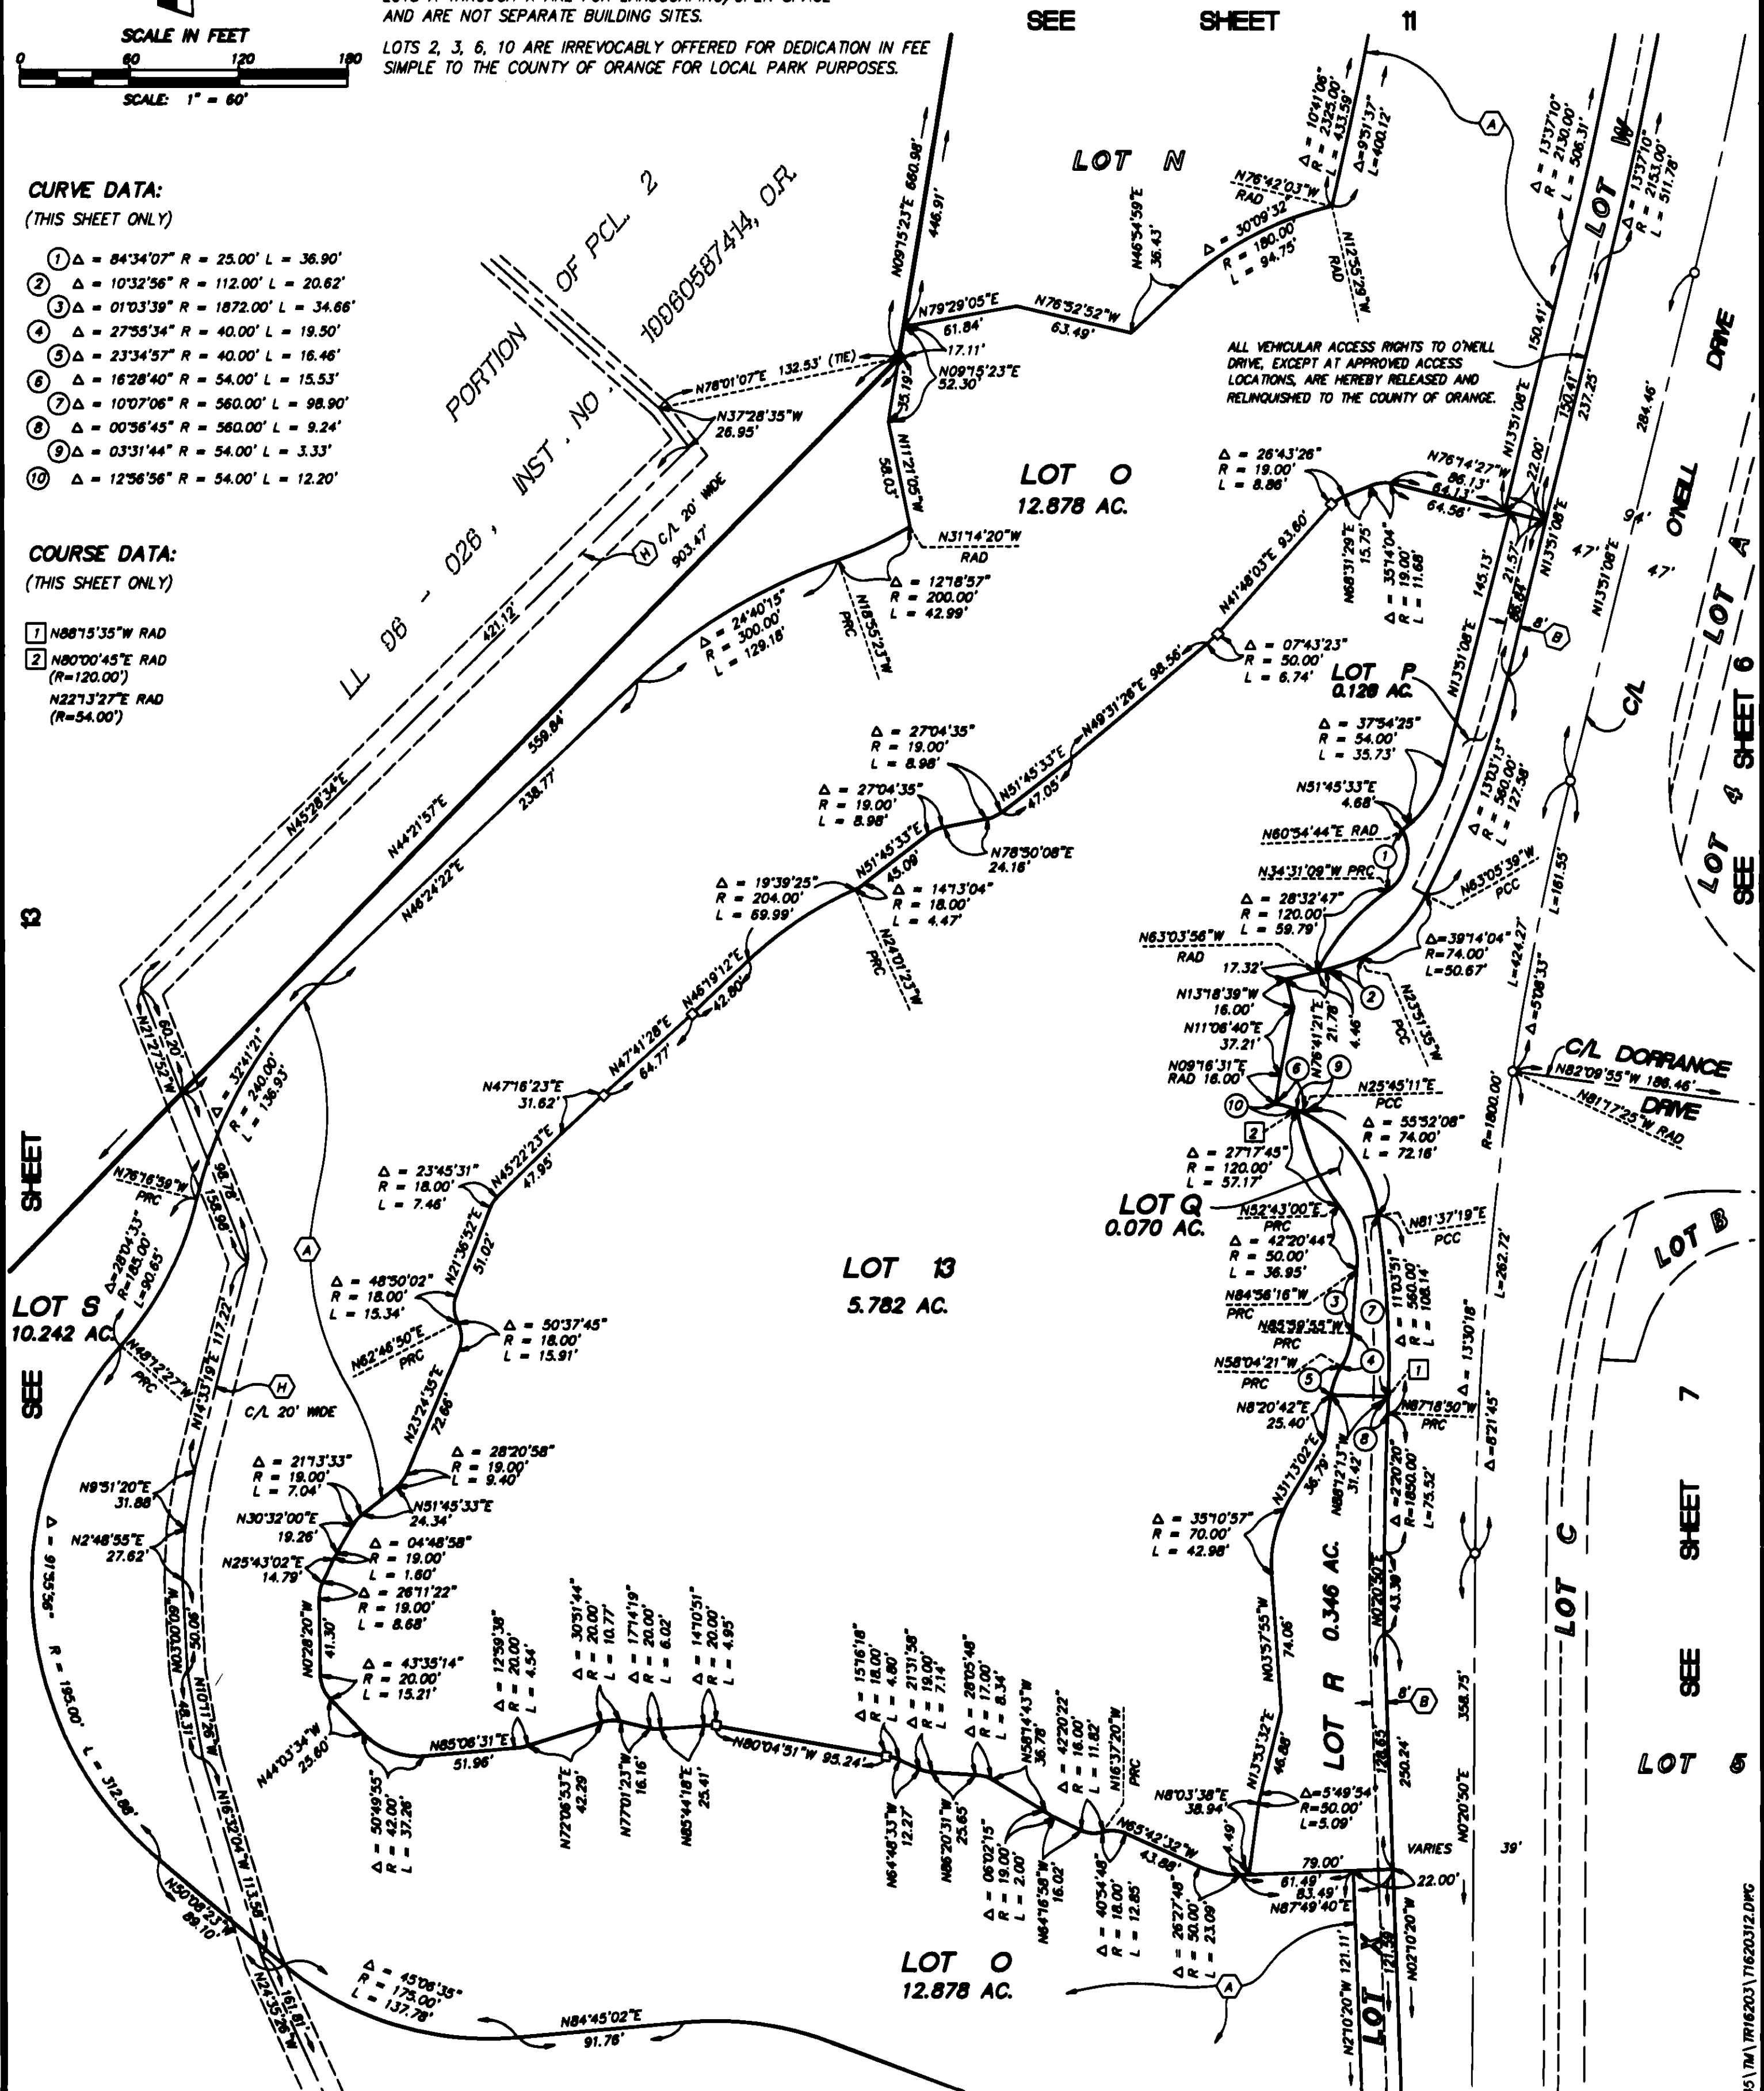

SEE SHEET 13

