

835

17

SHEET 1 OF 4 SHEETS

(ALL OF VESTING TENTATIVE
TRACT NO. 16237)TOTAL ACRES: 9.834 AC.
NUMBERED LOTS: 44
LETTERED LOTS: 1
DATE OF SURVEY: DECEMBER 2001.BLOCK: 5157
MODULE: 26

TRACT NO. 16237

IN THE UNINCORPORATED TERRITORY OF ORANGE COUNTY, STATE OF CALIFORNIA

BEING A SUBDIVISION OF LOT 2 OF TRACT NO. 16234 IN THE UNINCORPORATED TERRITORY OF THE
COUNTY OF ORANGE, STATE OF CALIFORNIA, AS SHOWN ON A MAP FILED IN BOOK
825, PAGES 19-29 OF MISCELLANEOUS MAPS IN THE OFFICE OF THE
COUNTY RECORDER OF ORANGE COUNTY, CALIFORNIA.DOUGLAS BENDER AND ASSOCIATES DOUGLAS W. BENDER R.C.E. 28946
DECEMBER, 2001ACCEPTED AND FILED AT THE
REQUEST OF
FIRST AMERICAN TITLE INSURANCE COMPANY
DATE August 14, 2002
TIME 4:00 pm FEE \$ 13.00
INSTRUMENT # 2002-681280 M/M
BOOK 835 PAGE 17-20
DARLENE J. BLOOM
INTERIM-COUNTY CLERK-RECORDER
BY Jill Skores
DEPUTY

OWNERSHIP CERTIFICATE:

WE, THE UNDERSIGNED, BEING ALL PARTIES HAVING ANY RECORD TITLE
INTEREST IN THE LAND COVERED BY THIS MAP, DO HEREBY CONSENT TO
THE PREPARATION AND RECORDATION OF SAID MAP, AS SHOWN WITHIN
THE DISTINCTIVE BORDER LINE.WE ALSO HEREBY DEDICATE TO THE PUBLIC FOR STREET PURPOSES
CHARDONNAY DRIVE, SAUVIGNON DRIVE, VINEYARD DRIVE AND
DOWNING STREET.

SHEA HOMES LIMITED PARTNERSHIP

A CALIFORNIA LIMITED PARTNERSHIP
J.F. SHEA CO., INC. NEVADA CORPORATION,
ITS GENERAL PARTNERBY: [Signature]PRINT NAME: Robert J. YoderPRINT TITLE: Division Vice PresidentBY: [Signature]PRINT NAME: John C. DanversPRINT TITLE: Asst Secretary


SHEA HOMES LIMITED PARTNERSHIP

STATE OF CALIFORNIA)
COUNTY OF ORANGE) SSON THIS April 19, 2002, BEFORE ME, Beth A. Hutchinson,

A NOTARY PUBLIC IN AND FOR SAID STATE, PERSONALLY APPEARED

Robert J. Yoder and John C. Danvers
PERSONALLY KNOWN TO ME (OR PROVED TO ME ON THE BASIS OF SATISFACTORY EVIDENCE)
TO BE THE PERSON (S) WHOSE NAME (S) IS/ARE SUBSCRIBED TO THE WITHIN INSTRUMENT
AND ACKNOWLEDGED TO ME THAT HE/SHE/they EXECUTED THE SAME IN THE/their
AUTHORIZED CAPACITY (IES), AND THAT BY HIS/HER/their SIGNATURE (S) ON THE
INSTRUMENT THE PERSON (S), OR THE ENTITY UPON BEHALF OF WHICH THE PERSON (S)
ACTED, EXECUTED THE INSTRUMENT.

WITNESS MY HAND:

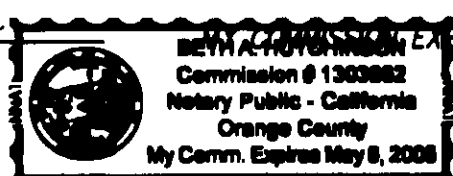SIGNATURE Beth A. Hutchinson MY PRINCIPAL PLACE OF BUSINESS IS
NOTARY PUBLIC IN AND FOR SAID STATE IN Orange COUNTY.Beth A. Hutchinson
(NAME PRINTED)

DMB LADERA, L.L.C.

A DELAWARE LIMITED LIABILITY COMPANY, BENEFICIARY UNDER A DEED OF TRUST
RECORDED JANUARY 30, 2002 AS INSTRUMENT NO. 20020080172 OF OFFICIAL
RECORDS.BY: [Signature] RANCHO MISSION VIEJO, L.L.C., A DELAWARE LIMITED LIABILITY COMPANY,
AS AGENT AND OR MANAGER.BY: [Signature]PRINT NAME: Donald T. StahlPRINT TITLE: Dir. of Comm. DevBY: [Signature]PRINT NAME: Stephen C. SchrankPRINT TITLE: Executive Vice President

DMB LADERA, L.L.C.

STATE OF CALIFORNIA)
COUNTY OF ORANGE) SSON THIS May 16, 2002, BEFORE ME, Tina T. Baker,

A NOTARY PUBLIC IN AND FOR SAID STATE, PERSONALLY APPEARED

Donald T. Stahl and Stephen C. Schrank
PERSONALLY KNOWN TO ME (OR PROVED TO ME ON THE BASIS OF SATISFACTORY EVIDENCE)
TO BE THE PERSON (S) WHOSE NAME (S) IS/ARE SUBSCRIBED TO THE WITHIN INSTRUMENT
AND ACKNOWLEDGED TO ME THAT HE/SHE/they EXECUTED THE SAME IN HIS/HER/their
AUTHORIZED CAPACITY (IES), AND THAT BY HIS/HER/their SIGNATURE (S) ON THE
INSTRUMENT THE PERSON (S), OR THE ENTITY UPON BEHALF OF WHICH THE PERSON (S)
ACTED, EXECUTED THE INSTRUMENT.

WITNESS MY HAND:

SIGNATURE Tina T. Baker MY PRINCIPAL PLACE OF BUSINESS IS
NOTARY PUBLIC IN AND FOR SAID STATE IN Orange COUNTY.TINA T. BAKER
(NAME PRINTED)MY COMMISSION EXPIRES 8/29/04

ENGINEER'S STATEMENT:

I HEREBY STATE THAT THIS MAP CONSISTING OF 4 SHEETS, CORRECTLY REPRESENTS
A TRUE AND COMPLETE SURVEY AS SHOWN MADE IN DECEMBER 2001; WAS MADE BY
ME OR UNDER MY DIRECTION; THAT THE MONUMENTS ARE OF CHARACTER AND
OCCUPY (OR WILL OCCUPY) THE POSITIONS INDICATED BY SAID MAP; AND THAT
SAID MONUMENTS ARE (OR WILL BE) SUFFICIENT TO ENABLE THE SURVEY
TO BE RETRACED.DOUGLAS W. BENDER, R.C.E. 28946
MY REGISTRATION EXPIRES MARCH 31, 2003.

COUNTY SURVEYOR'S STATEMENT:

I HEREBY STATE THAT I HAVE EXAMINED THIS MAP AND HAVE FOUND IT TO BE
SUBSTANTIALLY IN CONFORMANCE WITH THE TENTATIVE MAP AS FILED WITH, AMENDED
AND APPROVED BY THE ORANGE COUNTY SUBDIVISION COMMITTEE, THAT ALL
PROVISIONS OF THE SUBDIVISION MAP ACT AND COUNTY SUBDIVISION REGULATIONS
HAVE BEEN COMPLIED WITH AND I AM SATISFIED SAID MAP IS TECHNICALLY CORRECT.DATED THIS 1ST DAY OF July, 2002.Michael K. Sullivan

JOHN CANAS, COUNTY SURVEYOR

L.S. 4408 EXPIRATION DATE 9-30-05

BY: Michael K. Sullivan, DEPUTY
L.S. 6284 EXPIRES 6-30-04

CLERK OF THE BOARD OF SUPERVISOR'S CERTIFICATE:

STATE OF CALIFORNIA)
COUNTY OF ORANGE) SSI HEREBY CERTIFY THAT THIS MAP WAS PRESENTED FOR APPROVAL TO THE BOARD OF
SUPERVISORS OF ORANGE COUNTY AT A REGULAR MEETING THEREOF HELD ON THE 6th
DAY OF August, 2002, AND THAT THEREUPON SAID BOARD DID, BY AN ORDER
DULY PASSED AND ENTERED, APPROVE SAID MAP AND DID ACCEPT ON BEHALF OF THE
PUBLIC, SUBJECT TO IMPROVEMENTS, THE DEDICATION FOR STREET PURPOSES:
CHARDONNAY DRIVE, SAUVIGNON DRIVE, VINEYARD DRIVE AND
DOWNING STREET.*AND DID ALSO APPROVE SUBJECT MAP PURSUANT TO THE PROVISIONS OF
SECTION 66436(a)(3) OF THE SUBDIVISION MAP ACT.DATED THIS 6th DAY OF August, 2002.[Signature]
DARLENE J. BLOOM
CLERK OF THE BOARD OF SUPERVISORS

COUNTY TREASURER-TAX COLLECTOR'S CERTIFICATE:

STATE OF CALIFORNIA)
COUNTY OF ORANGE) SSI HEREBY CERTIFY THAT ACCORDING TO THE RECORDS OF MY OFFICE THERE ARE NO
LIENS AGAINST THE LAND COVERED BY THIS MAP OR ANY PART THEREOF FOR UNPAID
STATE, COUNTY, MUNICIPAL OR LOCAL TAXES OR SPECIAL ASSESSMENTS COLLECTED
AS TAXES, EXCEPT TAXES OR SPECIAL ASSESSMENTS COLLECTED AS TAXES NOT YET
PAYABLE.AND DO CERTIFY TO THE RECORDER OF ORANGE COUNTY THAT THE PROVISIONS OF
SUBDIVISION MAP ACT HAVE BEEN COMPLIED WITH REGARDING DEPOSITS TO
SECURE THE PAYMENT OF TAXES OR SPECIAL ASSESSMENTS COLLECTED AS TAXES ON
THE LAND COVERED BY THIS MAP.DATED THIS 26th DAY OF June, 2002.JOHN M.W. MOORLACH
COUNTY TREASURER-TAX COLLECTORBY: Tina T. Baker
DEPUTY TREASURER-TAX COLLECTOR

AUTOMATIC FIRE SPRINKLER NOTE:

ALL COMMERCIAL STRUCTURES OVER 6,000 SQUARE FEET; ALL MULTIFAMILY
RESIDENTIAL STRUCTURES; ALL DETACHED, SINGLE-FAMILY STRUCTURES EXCEEDING
5,500 SQUARE FEET; AND ALL STRUCTURES EXCEEDING FIRE AUTHORITY ACCESS
REQUIREMENTS SHALL BE PROTECTED BY AN AUTOMATIC SPRINKLER SYSTEM, IN A
MANNER MEETING THE APPROVAL OF THE FIRE CHIEF.

SPECIAL FIRE PROTECTION NOTE:

PROPERTY HAS TOTAL EXCLUSION FROM A SPECIAL FIRE PROTECTION AREA
AND MUST MEET ALL REQUIREMENTS OF THE EXCLUSION FOR DEVELOPMENT
WITHIN THE AREA.

HIGH FIRE HAZARD AREA NOTE:

THE LOTS SHOWN ON THIS MAP ARE IN A HIGH FIRE HAZARD AREA DUE TO
WILDLAND EXPOSURE.

NOTES:

PROPERTY MAY BE SUBJECT TO IMPACTS FROM THE FOOTHILL/EASTERN
TRANSPORTATION CORRIDOR.

SIGNATURE OMISSION

PURSUANT TO SECTION 66436 (a) (3) OF THE SUBDIVISION MAP ACT, THE FOLLOWING
SIGNATURES HAVE BEEN OMITTED:

1. LADERA DEVELOPMENT COMPANY, L.L.C., HOLDER OF OIL, GAS MINERAL AND WATER RIGHTS
RECORDED AS INSTRUMENT NO. 19960624029 OF OFFICIAL RECORDS.

835

17

TOTAL ACREAGE: 9.834 AC.
NUMBERED LOTS: 44
LETTERED LOTS: 1
DATE OF SURVEY: SEPTEMBER 2001

TRACT NO. 16237

IN THE UNINCORPORATED TERRITORY OF THE COUNTY OF ORANGE, STATE OF CALIFORNIA
DOUGLAS BENDER AND ASSOCIATES DOUGLAS W. BENDER R.C.E. 28946
DECEMBER, 2001

BOUNDARY AND INDEX MAP

MONUMENT NOTES

- INDICATES FOUND O.C.S. G.P.S. MONUMENTS AS NOTED.
- INDICATES MONUMENT TO BE SET AS NOTED.
- 1 INDICATES 2" I.P. TAGGED "P.L.S. 5557" OR SPIKE & WASHER STAMPED "P.L.S. 5557" OR LEAD, TACK & TAG "P.L.S. 5557" TO BE SET WITHIN 90 DAYS OF ACCEPTANCE OF IMPROVEMENTS UNLESS OTHERWISE NOTED PER TRACT NO. 16234 M.M. 825/19-29.
- 2 INDICATES 1" I.P. TAGGED "P.L.S. 5557" OR SPIKE & WASHER STAMPED "P.L.S. 5557" OR LEAD, TACK & TAG "P.L.S. 5557" TO BE SET WITHIN 90 DAYS OF ACCEPTANCE OF IMPROVEMENTS UNLESS OTHERWISE NOTED PER TRACT NO. 16234 M.M. 825/19-29.
- 3 INDICATES 1" I.P. TAGGED "P.L.S. 5557" OR SPIKE & WASHER STAMPED "P.L.S. 5557" OR LEAD, TACK & TAG "P.L.S. 5557" TO BE SET WITHIN 90 DAYS OF ACCEPTANCE OF IMPROVEMENTS UNLESS OTHERWISE NOTED PER TRACT NO. 15813 M.M. 795/1-16.
- INDICATES 2" I.P. TAGGED "RCE 28946" TO BE SET PRIOR TO RECDIFICATION.

BASIS OF BEARINGS

BEARINGS SHOWN HEREON ARE BASED ON THE LINE
BETWEEN O.C.S. HORIZONTAL CONTROL STATION G.P.S.
NO. 1417 AND STATION NO. 1448 BEING N10°48'13"E
PER RECORDS ON FILE IN THE OFFICE OF THE
ORANGE COUNTY SURVEYOR.

DATUM STATEMENT

COORDINATES SHOWN HEREON ARE BASED UPON THE CALIFORNIA COORDINATE SYSTEM (CCS83) ZONE VI 1983 NAD (1991.35 EPOCH O.C.S. GPS ADJUSTMENT). ALL DISTANCES SHOWN ARE GROUND DISTANCES UNLESS OTHERWISE NOTED. TO OBTAIN GRID DISTANCES, MULTIPLY GROUND DISTANCES BY 0.999948295.

LINE TABLE

	BEARING	DISTANCE
1	N01°25'51"W	19.37'
2	N51°57'48"E	4.01'
3	N14°07'49"E	22.99'
4	N57°21'59"E	6.06'
5	N42°42'09"E(R)	56.00'
6	N80°19'40"W	13.90'
7	N44°26'03"W	15.00'
8	N5°06'10"E	28.30'
9	N53°05'11"W	5.66'
10	N51°40'24"W	6.07'
11	N52°18'12"W	6.66'
12	N87°35'25"E(R)	56.00'
13	N86°54'49"W	51.07'
14	N33°21'23"W	25.22'
15	N76°15'51"E(R)	28.00'
16	N65°50'19"E	28.58'
17	(N07°34'28"E(R)	101.10' (R1

CURVE TABLE

	DELTA	RADIUS	LENGTH
A	06°43'32"	210.00'	31.98'
B	06°01'33"	207.00'	21.77'
C	15°5'28"	220.00'	58.59'
D	01°11'26"	622.00'	12.92'
E	85°11'23"	18.00'	26.76'
F	30°38'17"	90.00'	48.13'
G	00°39'09"	590.00'	6.72'
H	97°25'31"	18.00'	30.61'
I	90°32'33"	15.00'	23.70'
J	08°34'09"	328.00'	49.06'
K	78°16'52"	15.00'	20.49'

MONUMENT NOTES (CONT.)

2" IRON PIPE TAGGED "R.C.E. 28946" OR SPIKE AND WASHER STAMPED "R.C.E. 28946" OR LEAD AND TACK TAGGED "R.C.E. 28946" TO BE SET AT ALL TRACT CORNERS UNLESS OTHERWISE NOTED, WITHIN 90 DAYS AFTER ACCEPTANCE OF IMPROVEMENTS.

8" SPIKE & WASHER STAMPED "R.C.E. 28946" IN ASPHALT PAVING OR LEAD & TAG "R.C.E. 28946" IN CONCRETE TO BE SET AT ALL CENTERLINE INTERSECTIONS, B.C.'S, E.C.'S AND ALL OTHER CENTERLINE POINTS OF CONTROL, UNLESS OTHERWISE NOTED, WITHIN 90 DAYS AFTER ACCEPTANCE OF IMPROVEMENTS.


1" IRON PIPE TAGGED "R.C.E. 28946" OR SPIKE AND WASHER STAMPED "R.C.E. 28946" OR LEAD AND TACK TAGGED "R.C.E. 28946" TO BE SET AT ALL LOT CORNERS, EXCEPT B.C.'S, E.C.'S, P.R.C.'S AND P.C.'S THAT ABUT A STREET AND ARE NOT LOT CORNERS MARKING SIDE LOT LINES, UNLESS OTHERWISE NOTED, WITHIN 90 DAYS AFTER ACCEPTANCE OF IMPROVEMENTS.

NOTES

LOT A IS NOT A SEPARATE BUILDING SITE
LOT A IS FOR PRIVATE PARK PURPOSES.

REFERENCE

()R1= TRACT NO. 16234 M.M. 825/19-29.

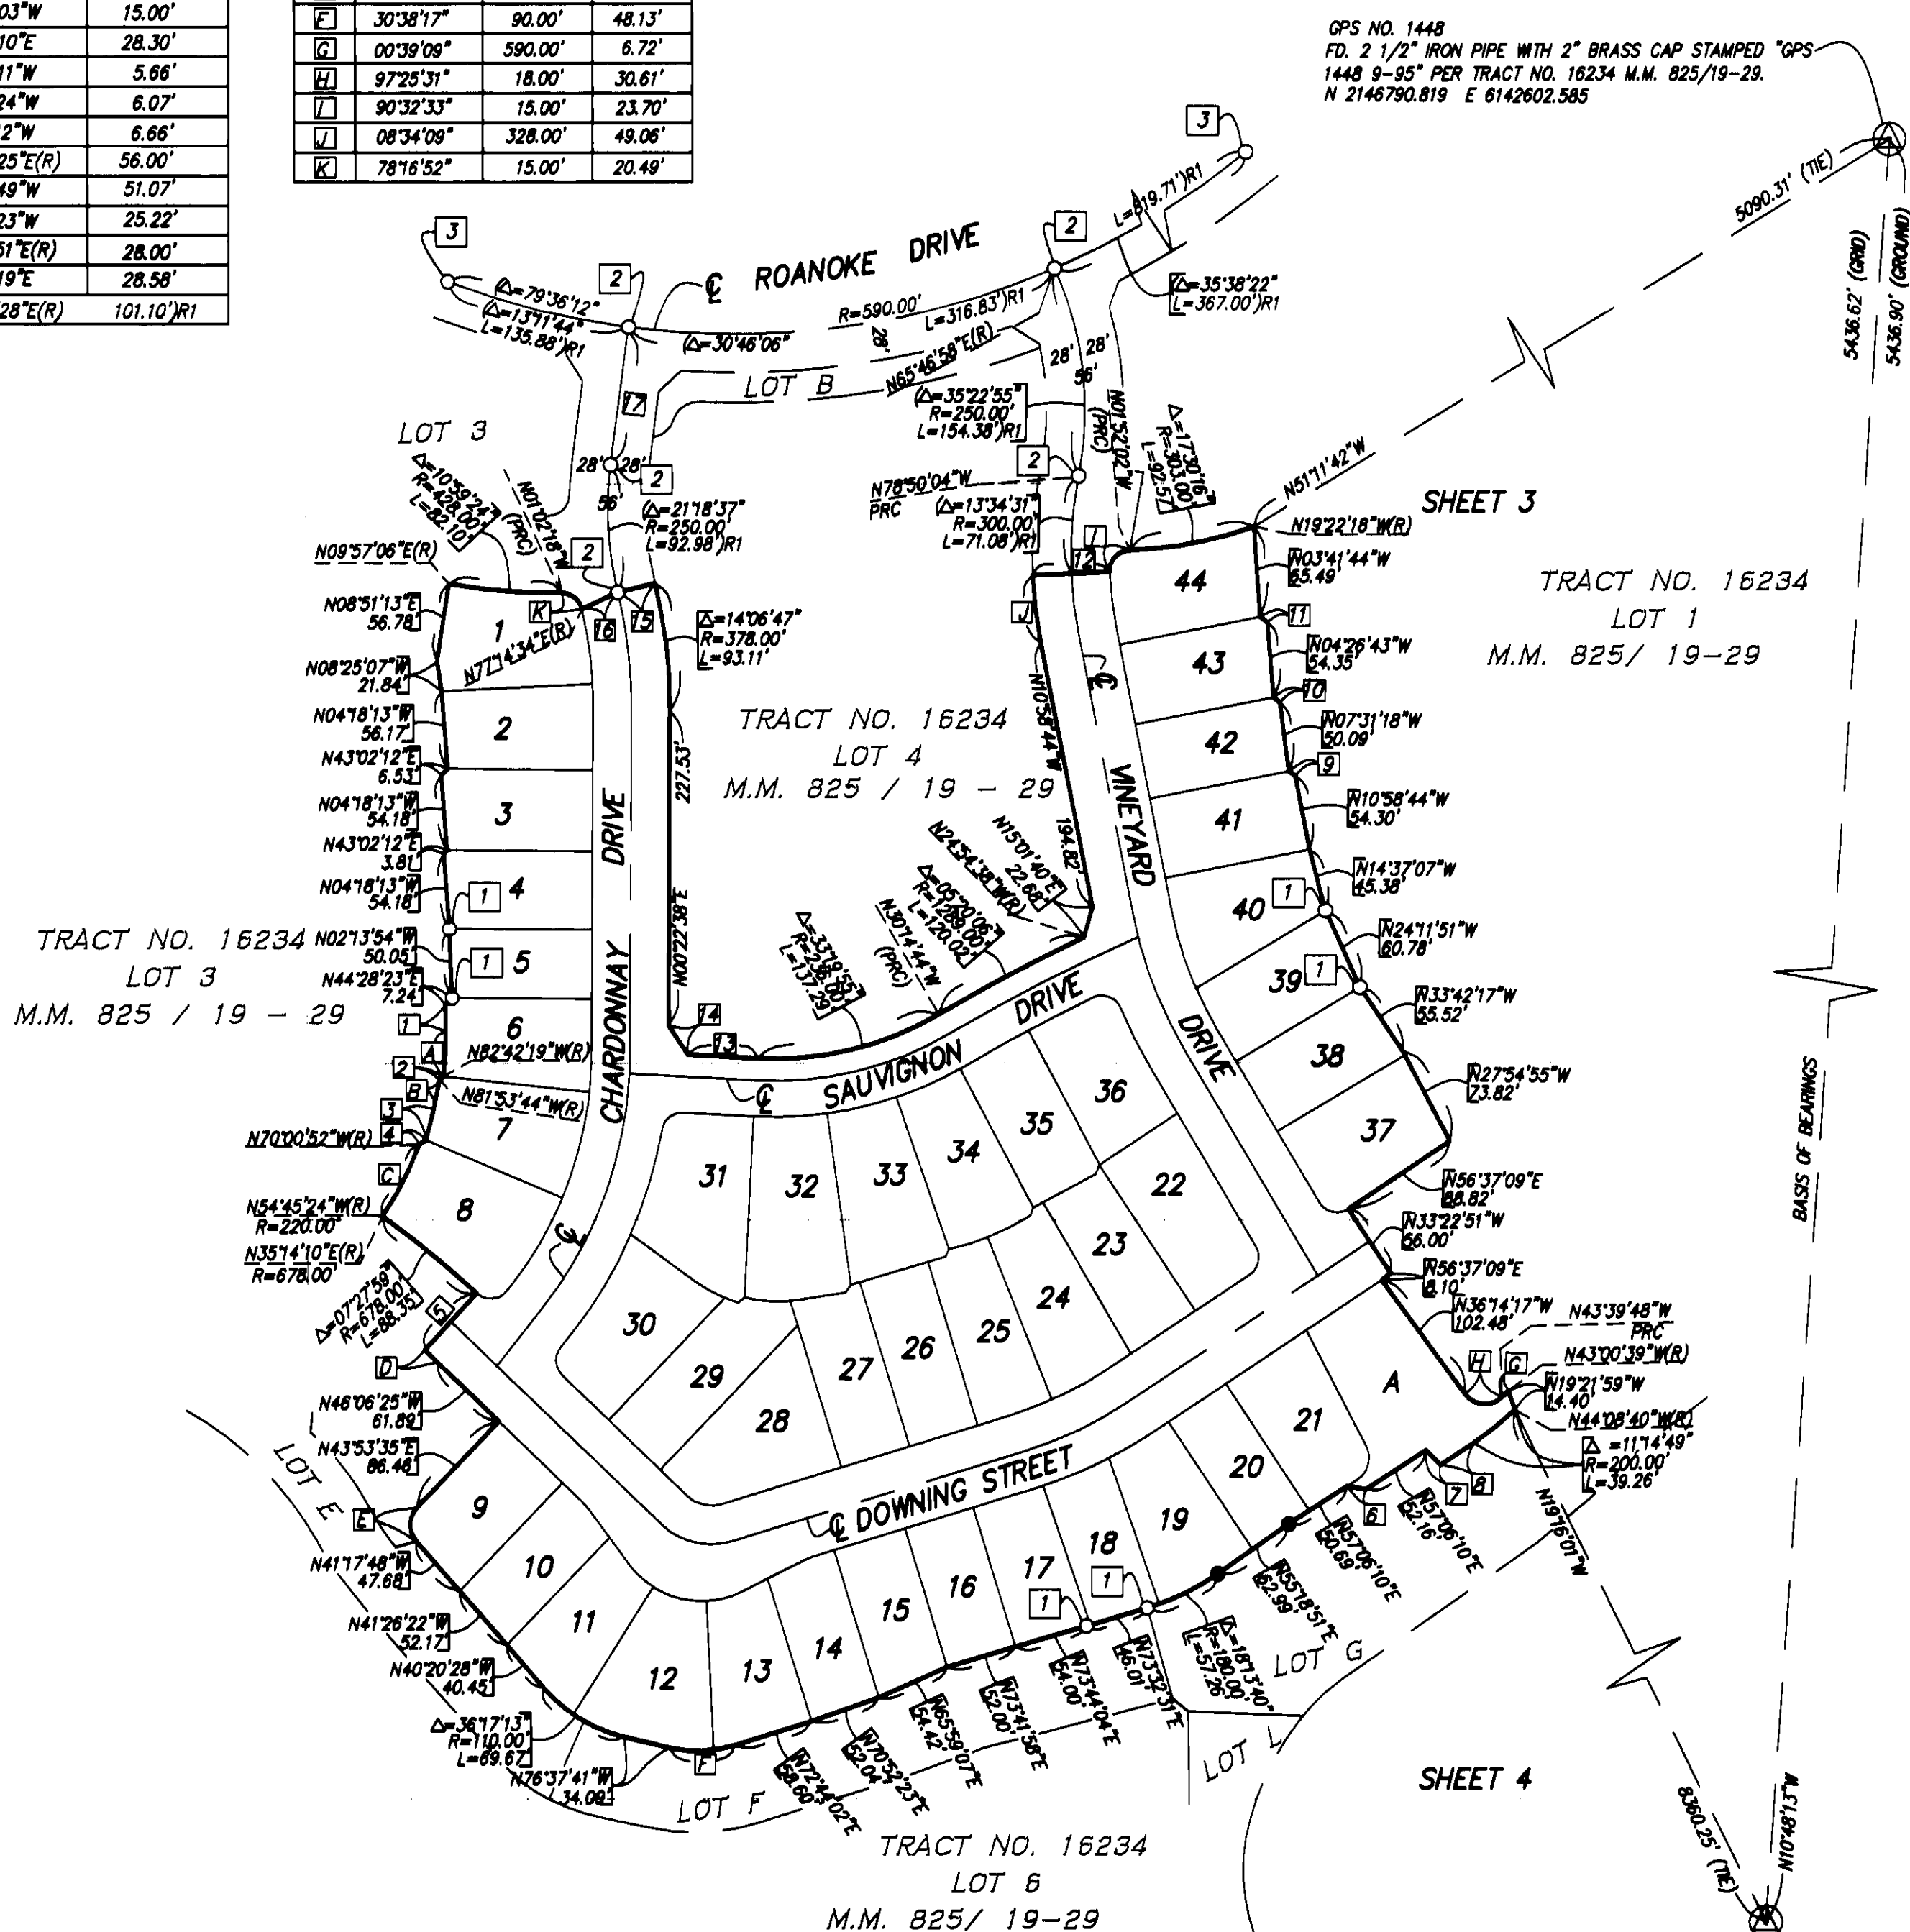

GPS NO. 1417
FD. 2 1/2" IRON PIPE WITH 2" BRASS CAP STAMPED "GPS
1417 9-95" PER TRACT NO. 16234 M.M. 825/19-29.
N 2141450.558 E 6141583.535

SHEET 3 OF 4 SHEETS
(ALL OF TENTATIVE TRACT NO. 16237)

TOTAL ACRES: 9.834 AC.
NUMBERED LOTS: 44
LETTERED LOTS: 1
DATE OF SURVEY: SEPTEMBER 2001

TRACT NO. 16237

IN THE UNINCORPORATED TERRITORY OF THE COUNTY OF ORANGE, STATE OF CALIFORNIA
DOUGLAS BENDER AND ASSOCIATES DOUGLAS W. BENDER R.C.E. 28946
SEPTEMBER, 2001

NOTES

LOT A IS NOT A SEPARATE BUILDING SITE
LOT A IS FOR PRIVATE PARK PURPOSES.
FOR BASIS OF BEARINGS, DATUM STATEMENT,
AND MONUMENT NOTES SEE SHEET 2.

SCALE: 1" = 40'

TRACT NO. 16234

LOT 1

M.M. 825 / 19 - 29


TRACT NO. 16234

LOT 4

M.M. 825 / 19 - 29

CURVE TABLE

DELTA	RADIUS	LENGTH
08°34'09"	300.00'	44.87'
08°34'09"	272.00'	40.68'
90°32'33"	15.00'	23.70'
92°45'30"	15.00'	24.28'
93°19'29"	15.00'	24.43'
08°26'56"	328.00'	48.37'
02°59'19"	300.00'	15.65'

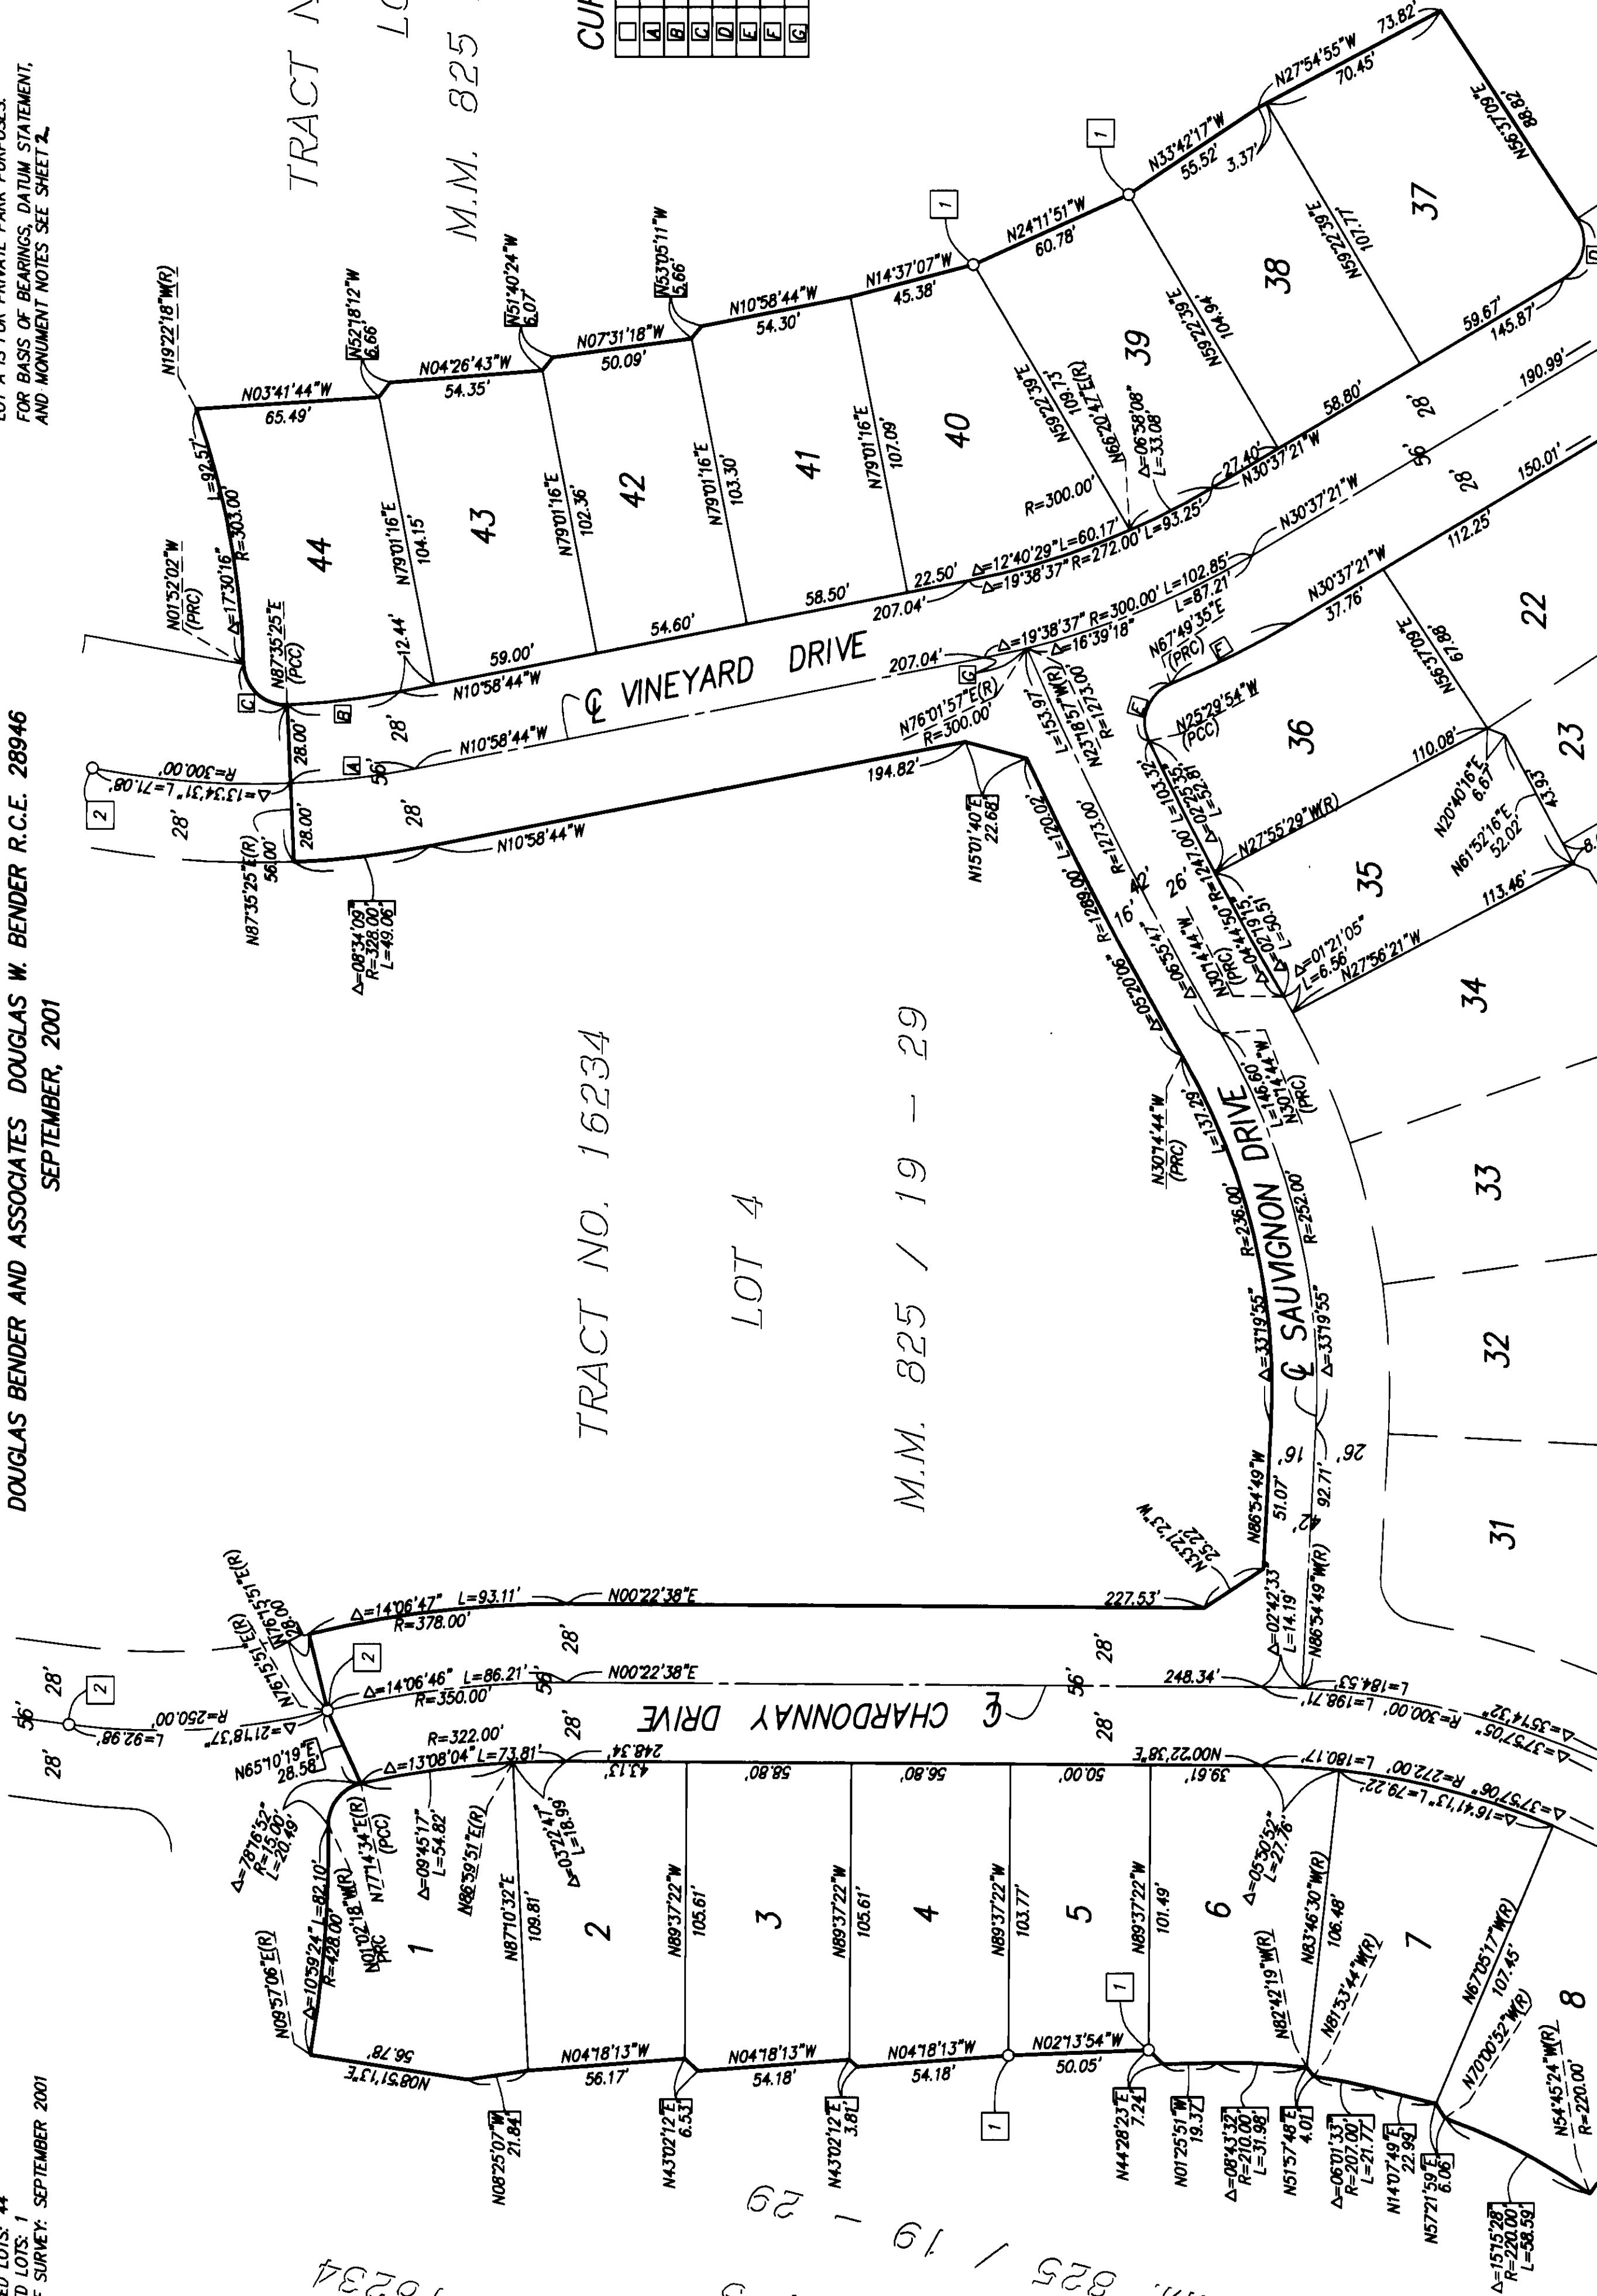

SEE


SHEET

4

TRACT NO. 16237
IN THE UNINCORPORATED TERRITORY OF THE COUNTY OF ORANGE, STATE OF CALIFORNIA
DOUGLAS BENDER AND ASSOCIATES DOUGLAS W. BENDER R.C.E. 28946
SEPTEMBER, 2001

SHEET 4 OF 4 SHEETS
(ALL OF TENTATIVE TRACT NO. 16237)
TOTAL ACREAGE: 9.834 AC.
NUMBERED LOTS: 44
LETTERED LOTS: 1
DATE OF SURVEY: SEPTEMBER 2001

NOTES
LOT A IS NOT A SEPARATE BUILDING SITE
LOT A IS FOR PRIVATE PARK PURPOSES.
FOR BASIS OF BEARINGS, DATUM STATEMENT,
AND MONUMENT NOTES SEE SHEET 2.

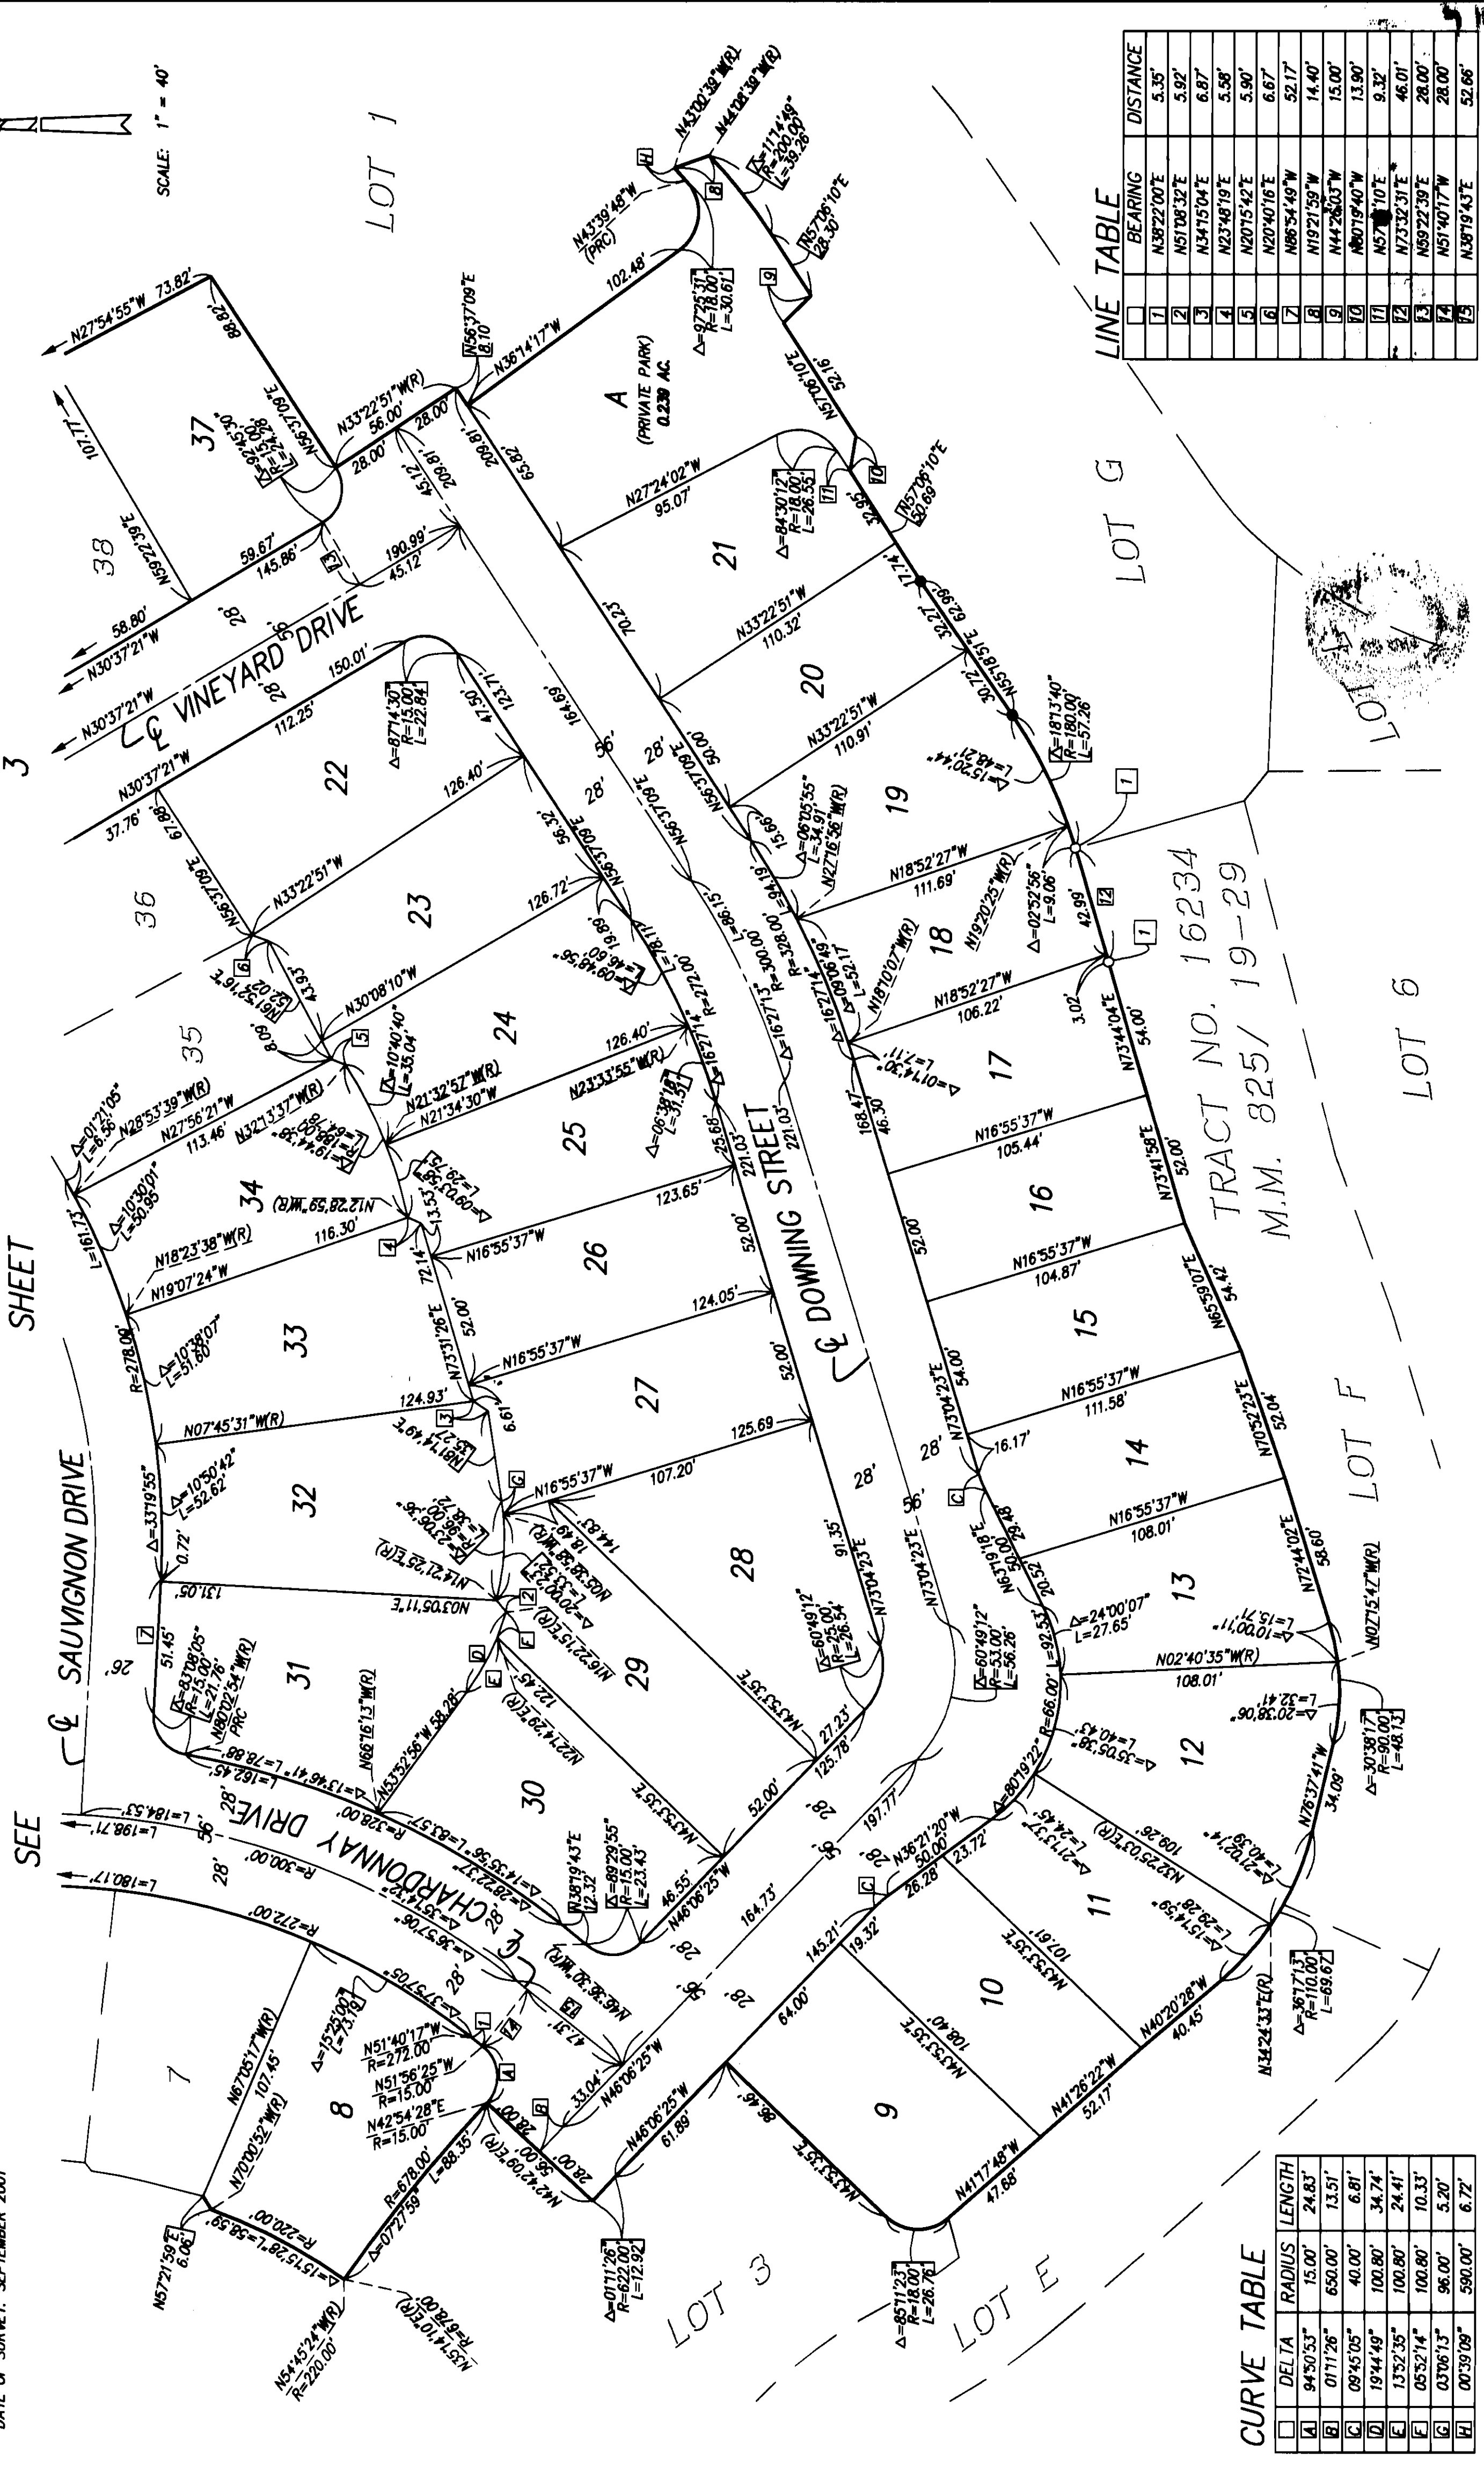

CURVE TABLE

DELTA	RADIUS	LENGTH
94°50'53"	15.00'	24.83'
01°11'26"	650.00'	13.51'
09°45'05"	40.00'	6.81'
19°44'49"	100.80'	34.74'
13°52'35"	100.80'	24.41'
05°52'14"	100.80'	10.33'
03°06'13"	96.00'	5.20'
00°59'08"	590.00'	6.72'

LINE TABLE

BEARING	DISTANCE
N38°22'00"E	5.35'
N51°08'32"E	5.92'
N34°15'04"E	6.87'
N23°48'19"E	5.58'
N20°15'42"E	5.90'
N20°40'16"E	6.67'
N86°54'48"W	52.17'
N19°21'59"W	14.40'
N44°26'03"W	15.00'
N80°19'40"W	13.90'
N57°10'10"E	9.32'
N73°32'31"E	46.01'
N59°22'39"E	28.00'
N51°40'17"W	28.00'
N38°19'43"E	52.66'