

835

21

SHEET 1 OF 5 SHEETS

TRACT NO. 16238

ALL OF VESTING
TENTATIVE TRACT NO. 16238BLOCK MODULE
5157 26DATE OF SURVEY:
DECEMBER 2001IN THE UNINCORPORATED TERRITORY OF ORANGE COUNTY, CALIFORNIA
BEING A SUBDIVISION OF LOT 1 OF TRACT NO. 16234 FILED IN BOOK 825, PAGES 19
THROUGH 29 OF MISCELLANEOUS MAPS, RECORDS OF ORANGE COUNTY, CALIFORNIA.

JANUARY 2002

JAMES F. GILLEN, L.S. 5557

HUITT-ZOLLARS

54 NUMBERED LOTS AND LETTERED LOTS A, B, C AND D 12.530 ACRES

ACCEPTED AND FILED AT THE
REQUEST OF
FIRST AMERICAN TITLE INSURANCE COMPANYDATE August 21, 2002
TIME 9:24 AM FEE \$ 15.00
INSTRUMENT NO. 2002-701182 M/M
BOOK 835 PAGE 21-25
DARLENE J. BLOOM
INTERIM
COUNTY CLERK-RECORDER
BY Jan Florn
DEPUTY

OWNERSHIP CERTIFICATE:

WE, THE UNDERSIGNED, BEING ALL PARTIES HAVING ANY RECORD TITLE INTEREST IN THE LAND COVERED BY THIS MAP, DO HEREBY CONSENT TO THE PREPARATION AND RECORDATION OF SAID MAP, AS SHOWN WITHIN THE DISTINCTIVE BORDER LINE. WE ALSO HEREBY DEDICATE TO THE PUBLIC FOR STREET PURPOSES: FALKNER DRIVE, DOWNING STREET, CALDWELL LANE, AND MARKHAM LANE.

WE ALSO HEREBY DEDICATE TO THE COUNTY OF ORANGE:
(1.) THE EASEMENT FOR STORM DRAIN PURPOSES AS SHOWN ON SAID MAP.

SURVEYOR'S STATEMENT:

I HEREBY STATE THAT THIS MAP CONSISTING OF 5 SHEETS, CORRECTLY REPRESENTS A TRUE AND COMPLETE SURVEY AS SHOWN MADE IN DECEMBER, 2001; WAS MADE BY ME OR UNDER MY DIRECTION; THAT THE MONUMENTS ARE OF THE CHARACTER AND OCCUPY OR WILL OCCUPY THE POSITIONS INDICATED BY SAID MAP; AND THAT SAID MONUMENTS WILL BE SUFFICIENT TO ENABLE THE SURVEY TO BE RETRACED.



James F. Gillen
JAMES F. GILLEN
L.S. 5557
EXPIRATION DATE: 9/30/05

STANDARD PACIFIC CORP., A DELAWARE CORPORATION.

BY: Andrew Parnes
PRINT NAME: Andrew Parnes
PRINT TITLE: Sr. V.P. of CFO.

BY: Jori L. Kordonian
PRINT NAME: Jori L. Kordonian
PRINT TITLE: Vice President

DMB LADERA, L.L.C., A DELAWARE LIMITED LIABILITY COMPANY, BENEFICIARY UNDER A DEED OF TRUST RECORDED APRIL 1, 2002 AS INSTRUMENT NO. 20020271761 OF OFFICIAL RECORDS.

BY: RANCHO MISSION VIEJO, L.L.C., A DELAWARE LIMITED LIABILITY COMPANY,
AS AGENT AND/OR MANAGER.

BY: Douglas J. Strawn
PRINT NAME: Douglas J. Strawn
PRINT TITLE: Director

BY: Stephen C. Schrank
PRINT NAME: Stephen C. Schrank
PRINT TITLE: Executive Vice President

COUNTY SURVEYOR'S STATEMENT:

I HEREBY STATE THAT I HAVE EXAMINED THIS MAP AND HAVE FOUND IT TO BE SUBSTANTIALLY IN CONFORMANCE WITH THE TENTATIVE MAP AS FILED WITH, AMENDED AND APPROVED BY THE ORANGE COUNTY SUBDIVISION COMMITTEE; THAT ALL PROVISIONS OF THE SUBDIVISION MAP ACT AND COUNTY SUBDIVISION REGULATIONS HAVE BEEN COMPLIED WITH AND I AM SATISFIED SAID MAP IS TECHNICALLY CORRECT.

DATED THIS 25TH DAY OF JULY, 2002.

Michael K. Sullivan
JOHN CANAS, COUNTY SURVEYOR
LS 4408 EXPIRATION DATE: 09-30-05

BY: MICHAEL K. SULLIVAN, DEPUTY
LS 6254 EXPIRES 6/30/06



COUNTY TREASURER-TAX COLLECTOR'S CERTIFICATE:

STATE OF CALIFORNIA)
COUNTY OF ORANGE)SS

I HEREBY CERTIFY THAT ACCORDING TO THE RECORDS OF MY OFFICE THERE ARE NO LIENS AGAINST THE LAND COVERED BY THIS MAP OR ANY PART THEREOF FOR UNPAID STATE, COUNTY, MUNICIPAL OR LOCAL TAXES OR SPECIAL ASSESSMENTS COLLECTED AS TAXES, EXCEPT TAXES OR SPECIAL ASSESSMENTS COLLECTED AS TAXES NOT YET PAYABLE.

AND DO ALSO HEREBY CERTIFY TO THE RECORDER OF ORANGE COUNTY THAT THE PROVISIONS OF THE SUBDIVISION MAP ACT HAVE BEEN COMPLIED WITH REGARDING DEPOSITS TO SECURE THE PAYMENT OF TAXES OR SPECIAL ASSESSMENTS COLLECTED AS TAXES ON THE LAND COVERED BY THIS MAP.

DATED THIS 9th DAY OF July, 2002.

JOHN M.W. MOORLACH
COUNTY TREASURER-TAX COLLECTOR

BY: MacJorgensen
DEPUTY TREASURER-TAX COLLECTOR

CLERK OF THE BOARD OF SUPERVISORS' CERTIFICATE:

STATE OF CALIFORNIA)
COUNTY OF ORANGE)SS

I HEREBY CERTIFY THAT THIS MAP WAS PRESENTED FOR APPROVAL TO THE BOARD OF SUPERVISORS OF ORANGE COUNTY AT A REGULAR MEETING THEREOF HELD ON THE 13th DAY OF AUGUST 2002, AND THAT THEREUPON SAID BOARD DID, BY AN ORDER DULY PASSED AND ENTERED, APPROVE SAID MAP AND DID ACCEPT ON BEHALF OF THE PUBLIC, SUBJECT TO IMPROVEMENTS: THE DEDICATION FOR STREET PURPOSES OF : FALKNER DRIVE, DOWNING STREET, CALDWELL LANE, AND MARKHAM LANE.

AND DID ALSO ACCEPT ON BEHALF OF THE COUNTY OF ORANGE:
(1.) THE EASEMENT FOR STORM DRAIN PURPOSES AS DEDICATED.

DATED THIS 13th DAY OF AUGUST, 2002.

Darlene J. Bloom
DARLENE J. BLOOM
CLERK OF THE BOARD OF SUPERVISORS

AUTOMATIC FIRE SPRINKLER NOTE:

ALL COMMERCIAL STRUCTURES GREATER THAN 6,000 SQUARE FEET; ALL MULTIFAMILY RESIDENTIAL STRUCTURES; ALL SINGLE-FAMILY STRUCTURES EXCEEDING 5,500 SQUARE FEET; AND ALL STRUCTURES EXCEEDING FIRE DEPARTMENT ACCESS REQUIREMENTS SHALL BE PROTECTED BY AN AUTOMATIC SPRINKLER SYSTEM. LOTS 1, 2, 53, AND 54 WILL REQUIRE AUTOMATIC FIRE SPRINKLER SYSTEMS PER OCFA.

HIGH FIRE HAZARD AREA NOTE:


THE LOTS SHOWN ON THIS MAP ARE IN A HIGH FIRE HAZARD AREA DUE TO WILD LAND EXPOSURE BASED ON STATE SRA MAPS.

THE PROPERTY SHOWN ON THIS MAP IS "TOTALLY EXCLUDED" FROM A "SPECIAL FIRE PROTECTION AREA." THERE ARE NO LOTS IN THIS TRACT THAT ARE SUBJECT TO CONSTRUCTION FEATURES OF THE ORANGE COUNTY ORDINANCE 3960.

NOTES:

PROPERTY MAY BE SUBJECT TO IMPACTS FROM THE FOOTHILL/EASTERN TRANSPORTATION CORRIDOR.

SEE SHEET 2 FOR NOTARY ACKNOWLEDGMENTS AND SIGNATURE OMISSIONS.

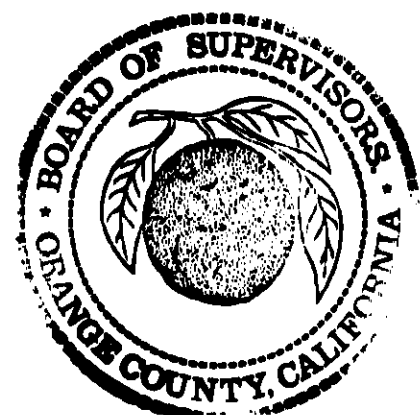

SHEET 2 OF 5 SHEETS

TRACT NO. 16238

ALL OF VESTING TENTATIVE
TRACT NO. 16238

IN THE UNINCORPORATED TERRITORY OF ORANGE COUNTY, CALIFORNIA

DATE OF SURVEY:
DECEMBER 2001

JANUARY 2002

JAMES F. GILLEN, L.S. 5557

HUITT-ZOLIARS

54 NUMBERED LOTS AND LETTERED LOTS A, B, C AND D 12.530 ACRES

STATE OF CALIFORNIA)
COUNTY OF ORANGE)SS

ON THIS 24th DAY OF April, 2002, BEFORE ME,
Kathleen M. Villari, A NOTARY PUBLIC IN AND FOR SAID STATE,
PERSONALLY APPEARED James F. Gillen AND
James F. Gillen, PERSONALLY KNOWN TO ME OR PROVED TO ME
ON THE BASIS OF SATISFACTORY EVIDENCE TO BE THE PERSONS WHOSE NAMES
ARE SUBSCRIBED TO THE WITHIN INSTRUMENT AND ACKNOWLEDGED TO ME THAT
THEY EXECUTED THE SAME IN THEIR AUTHORIZED CAPACITIES, AND THAT BY THEIR
SIGNATURES ON THE INSTRUMENT THE PERSONS, OR THE ENTITY UPON BEHALF
OF WHICH THE PERSONS ACTED, EXECUTED THE INSTRUMENT.

WITNESS MY HAND: MY COMMISSION EXPIRES 8-10-2003
Kathleen M. Villari MY PRINCIPAL PLACE OF BUSINESS
NOTARY PUBLIC IN AND FOR SAID STATE IS IN Orange COUNTY.
KATHLEEN M. VILLARI
PRINT NAME

STATE OF CALIFORNIA)
COUNTY OF ORANGE)SS

ON THIS 2nd DAY OF May, 2002, BEFORE ME,
Tina T. Baker, A NOTARY PUBLIC IN AND FOR SAID STATE,
PERSONALLY APPEARED Donald T. Steffen AND
Stephen C. Schrand, PERSONALLY KNOWN TO ME OR PROVED TO ME
ON THE BASIS OF SATISFACTORY EVIDENCE TO BE THE PERSONS WHOSE NAMES
ARE SUBSCRIBED TO THE WITHIN INSTRUMENT AND ACKNOWLEDGED TO ME THAT
THEY EXECUTED THE SAME IN THEIR AUTHORIZED CAPACITIES, AND THAT BY THEIR
SIGNATURES ON THE INSTRUMENT THE PERSONS, OR THE ENTITY UPON BEHALF
OF WHICH THE PERSONS ACTED, EXECUTED THE INSTRUMENT.

WITNESS MY HAND: MY COMMISSION EXPIRES 8/29/04
Tina T. Baker MY PRINCIPAL PLACE OF BUSINESS
NOTARY PUBLIC IN AND FOR SAID STATE IS IN Orange COUNTY.
TINA T. BAKER
PRINT NAME

MONUMENT NOTES:

- INDICATES FOUND 2" I.P. TAGGED "P.L.S. 5557" PER TRACT NO. 16234, M.M. 825 / 19-29.
- INDICATES LOCATION OF 2" I.P. TAGGED "P.L.S. 5557" OR SPIKE & WASHER
STAMPED "P.L.S. 5557" OR LEAD, TACK & TAG "P.L.S. 5557" TO BE SET PER
TRACT NO. 16234, M.M. 825 / 19-29.
- △ INDICATES LOCATION OF 1" I.P. TAGGED "L.S. 5557" OR SPIKE & WASHER
STAMPED "L.S. 5557" OR LEAD, TACK & TAG "L.S. 5557" TO BE SET PER
TRACT NO. 15884, M.M. 794/33-44, UNLESS OTHERWISE NOTED.
- INDICATES LOCATION OF 1" I.P. TAGGED "P.L.S. 5557" OR SPIKE & WASHER
STAMPED "P.L.S. 5557" OR LEAD, TACK & TAG "P.L.S. 5557" TO BE SET WITHIN
90 DAYS AFTER ACCEPTANCE OF IMPROVEMENTS.
- 2" I.P. TAGGED "P.L.S. 5557" OR SPIKE & WASHER STAMPED "P.L.S. 5557" OR LEAD,
TACK AND TAG "P.L.S. 5557" TO BE SET AT ALL TRACT BOUNDARY CORNERS, WITHIN
90 DAYS AFTER ACCEPTANCE OF IMPROVEMENTS, UNLESS OTHERWISE NOTED.
- 1" I.P. TAGGED "P.L.S. 5557" OR SPIKE & WASHER STAMPED "P.L.S. 5557" OR LEAD,
TACK AND TAG "P.L.S. 5557" TO BE SET AT ALL INTERIOR LOT CORNERS, EXCEPT LOT
CORNERS ABUTTING STREETS; LEAD, TACK & TAG "P.L.S. 5557" TO BE SET IN TOP OF
CURB OR SIDEWALK ON A 9.75' OFFSET OR A 15.75' OFFSET ON SIDE LOT LINES PRODUCED
FOR LOT CORNERS ABUTTING STREETS, WITHIN 90 DAYS AFTER ACCEPTANCE OF IMPROVEMENTS,
UNLESS OTHERWISE NOTED.
- △ INDICATES LOCATION OF 1" I.P. TAGGED "L.S. 5557" OR SPIKE & WASHER
STAMPED "L.S. 5557" OR LEAD, TACK & TAG "L.S. 5557" TO BE SET PER
TRACT NO. 15813, M.M. 795/1-16.
- INDICATES LOCATION OF 1" I.P. TAGGED "P.L.S. 5557" OR SPIKE & WASHER
STAMPED "P.L.S. 5557" OR LEAD, TACK & TAG "P.L.S. 5557" TO BE SET PER
TRACT NO. 16234, M.M. 825/19-29.

NO MONUMENTATION TO BE SET AT BC'S AND EC'S OF STREET RIGHT OF WAY LINES,
UNLESS OTHERWISE NOTED.


SIGNATURE OMISSIONS:

IN ACCORDANCE WITH THE PROVISIONS OF SECTION 66436(a) (3) OF THE SUBDIVISION
MAP ACT, THE FOLLOWING SIGNATURE HAS BEEN OMITTED:

1. LADERA DEVELOPMENT COMPANY, L.L.C., HOLDER OF OIL, GAS, MINERAL, AND WATER RIGHTS
RECORDED DECEMBER 10, 1996 AS INSTRUMENT NO. 19960624029 OF OFFICIAL RECORDS.

BASIS OF BEARINGS:

BEARINGS SHOWN HEREON ARE BASED ON THE EASTERLY LINE OF LOT 1 BEING N11°37'12"E
AS SHOWN ON TRACT NO. 16234, FILED IN BOOK 825, PAGES 19 THROUGH 29 OF MISCELLANEOUS MAPS,
RECORDS OF ORANGE COUNTY, CALIFORNIA.

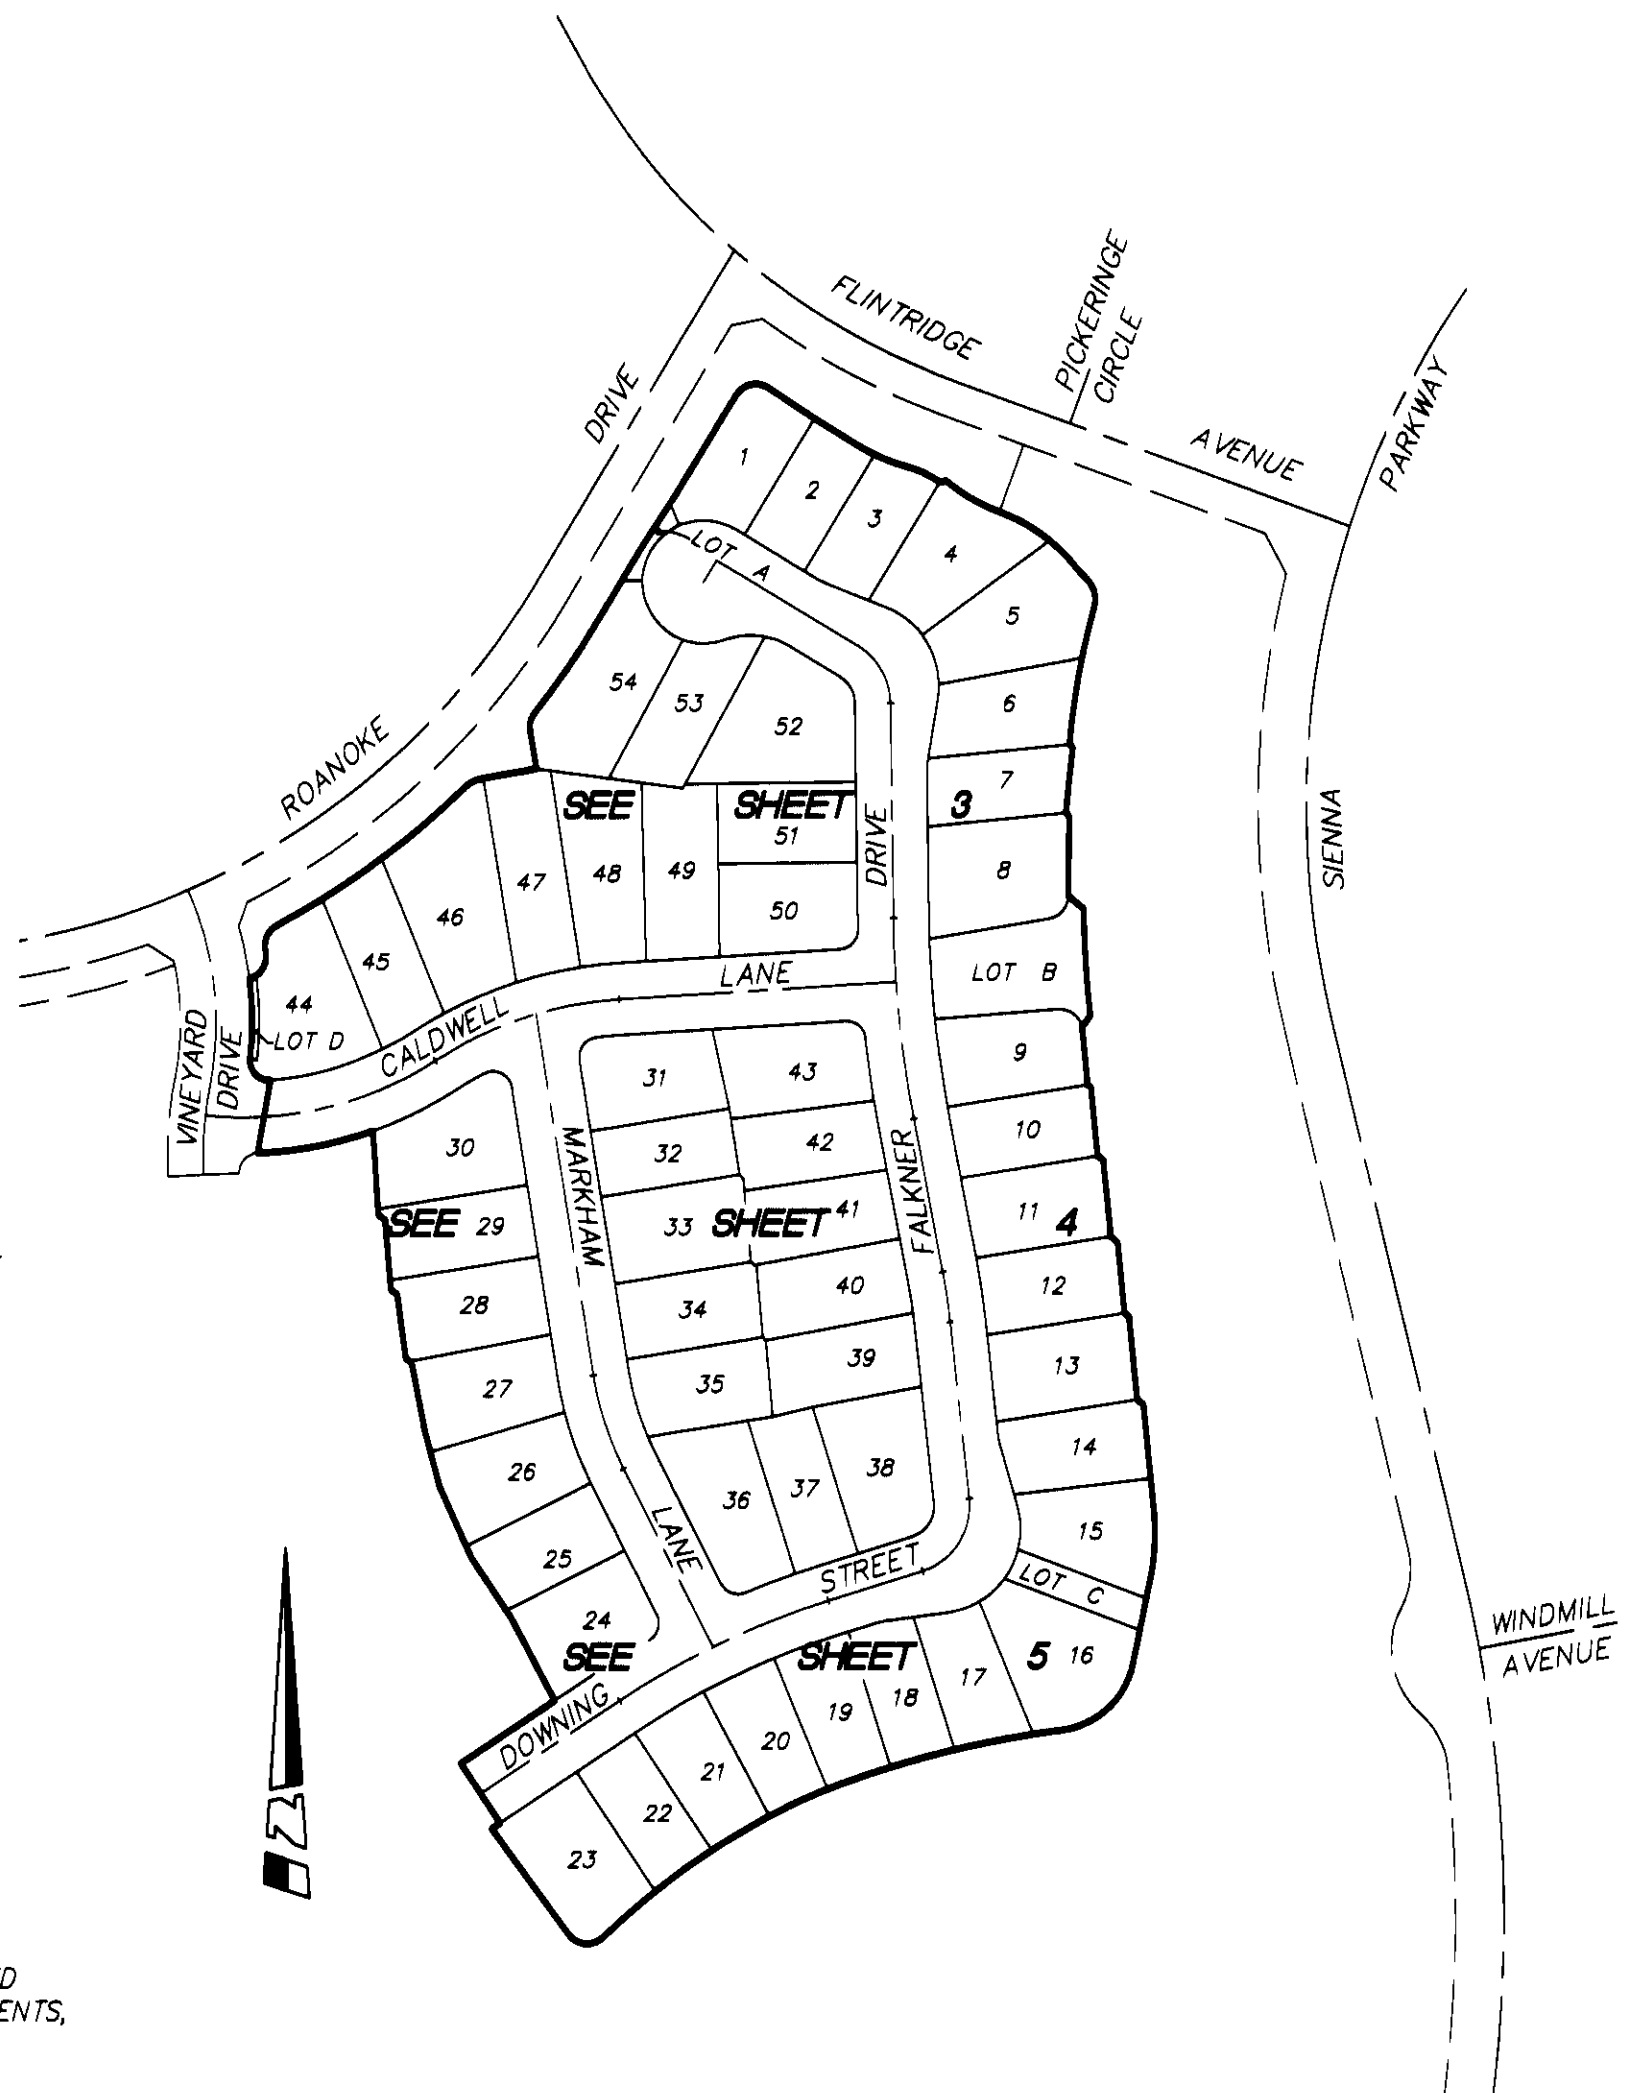

SHEET INDEX MAP

1"=150'



NOTES:
SEE SHEET 2 FOR MONUMENT NOTES,
BASIS OF BEARINGS.

LOTS A, C AND D ARE FOR LANDSCAPING AND OPEN
SPACE AND ARE NOT SEPARATE BUILDING SITES.
LOT B IS FOR A POCKET PARK.


[] INDICATES MEASURED AND RECORD PER
TRACT NO. 15907, M.M. 805/26-28.

CURVE DATA: (THIS SHEET ONLY)

- ① $\Delta = 66^{\circ}05'35''$ $R = 48.00'$ $L = 55.37'$
② $\Delta = 71^{\circ}32'28''$ $R = 48.00'$ $L = 59.93'$

COURSE DATA: (THIS SHEET ONLY)

- ① $N31^{\circ}22'38''E$ 9.90'
② $N79^{\circ}46'43''E$ 9.90'

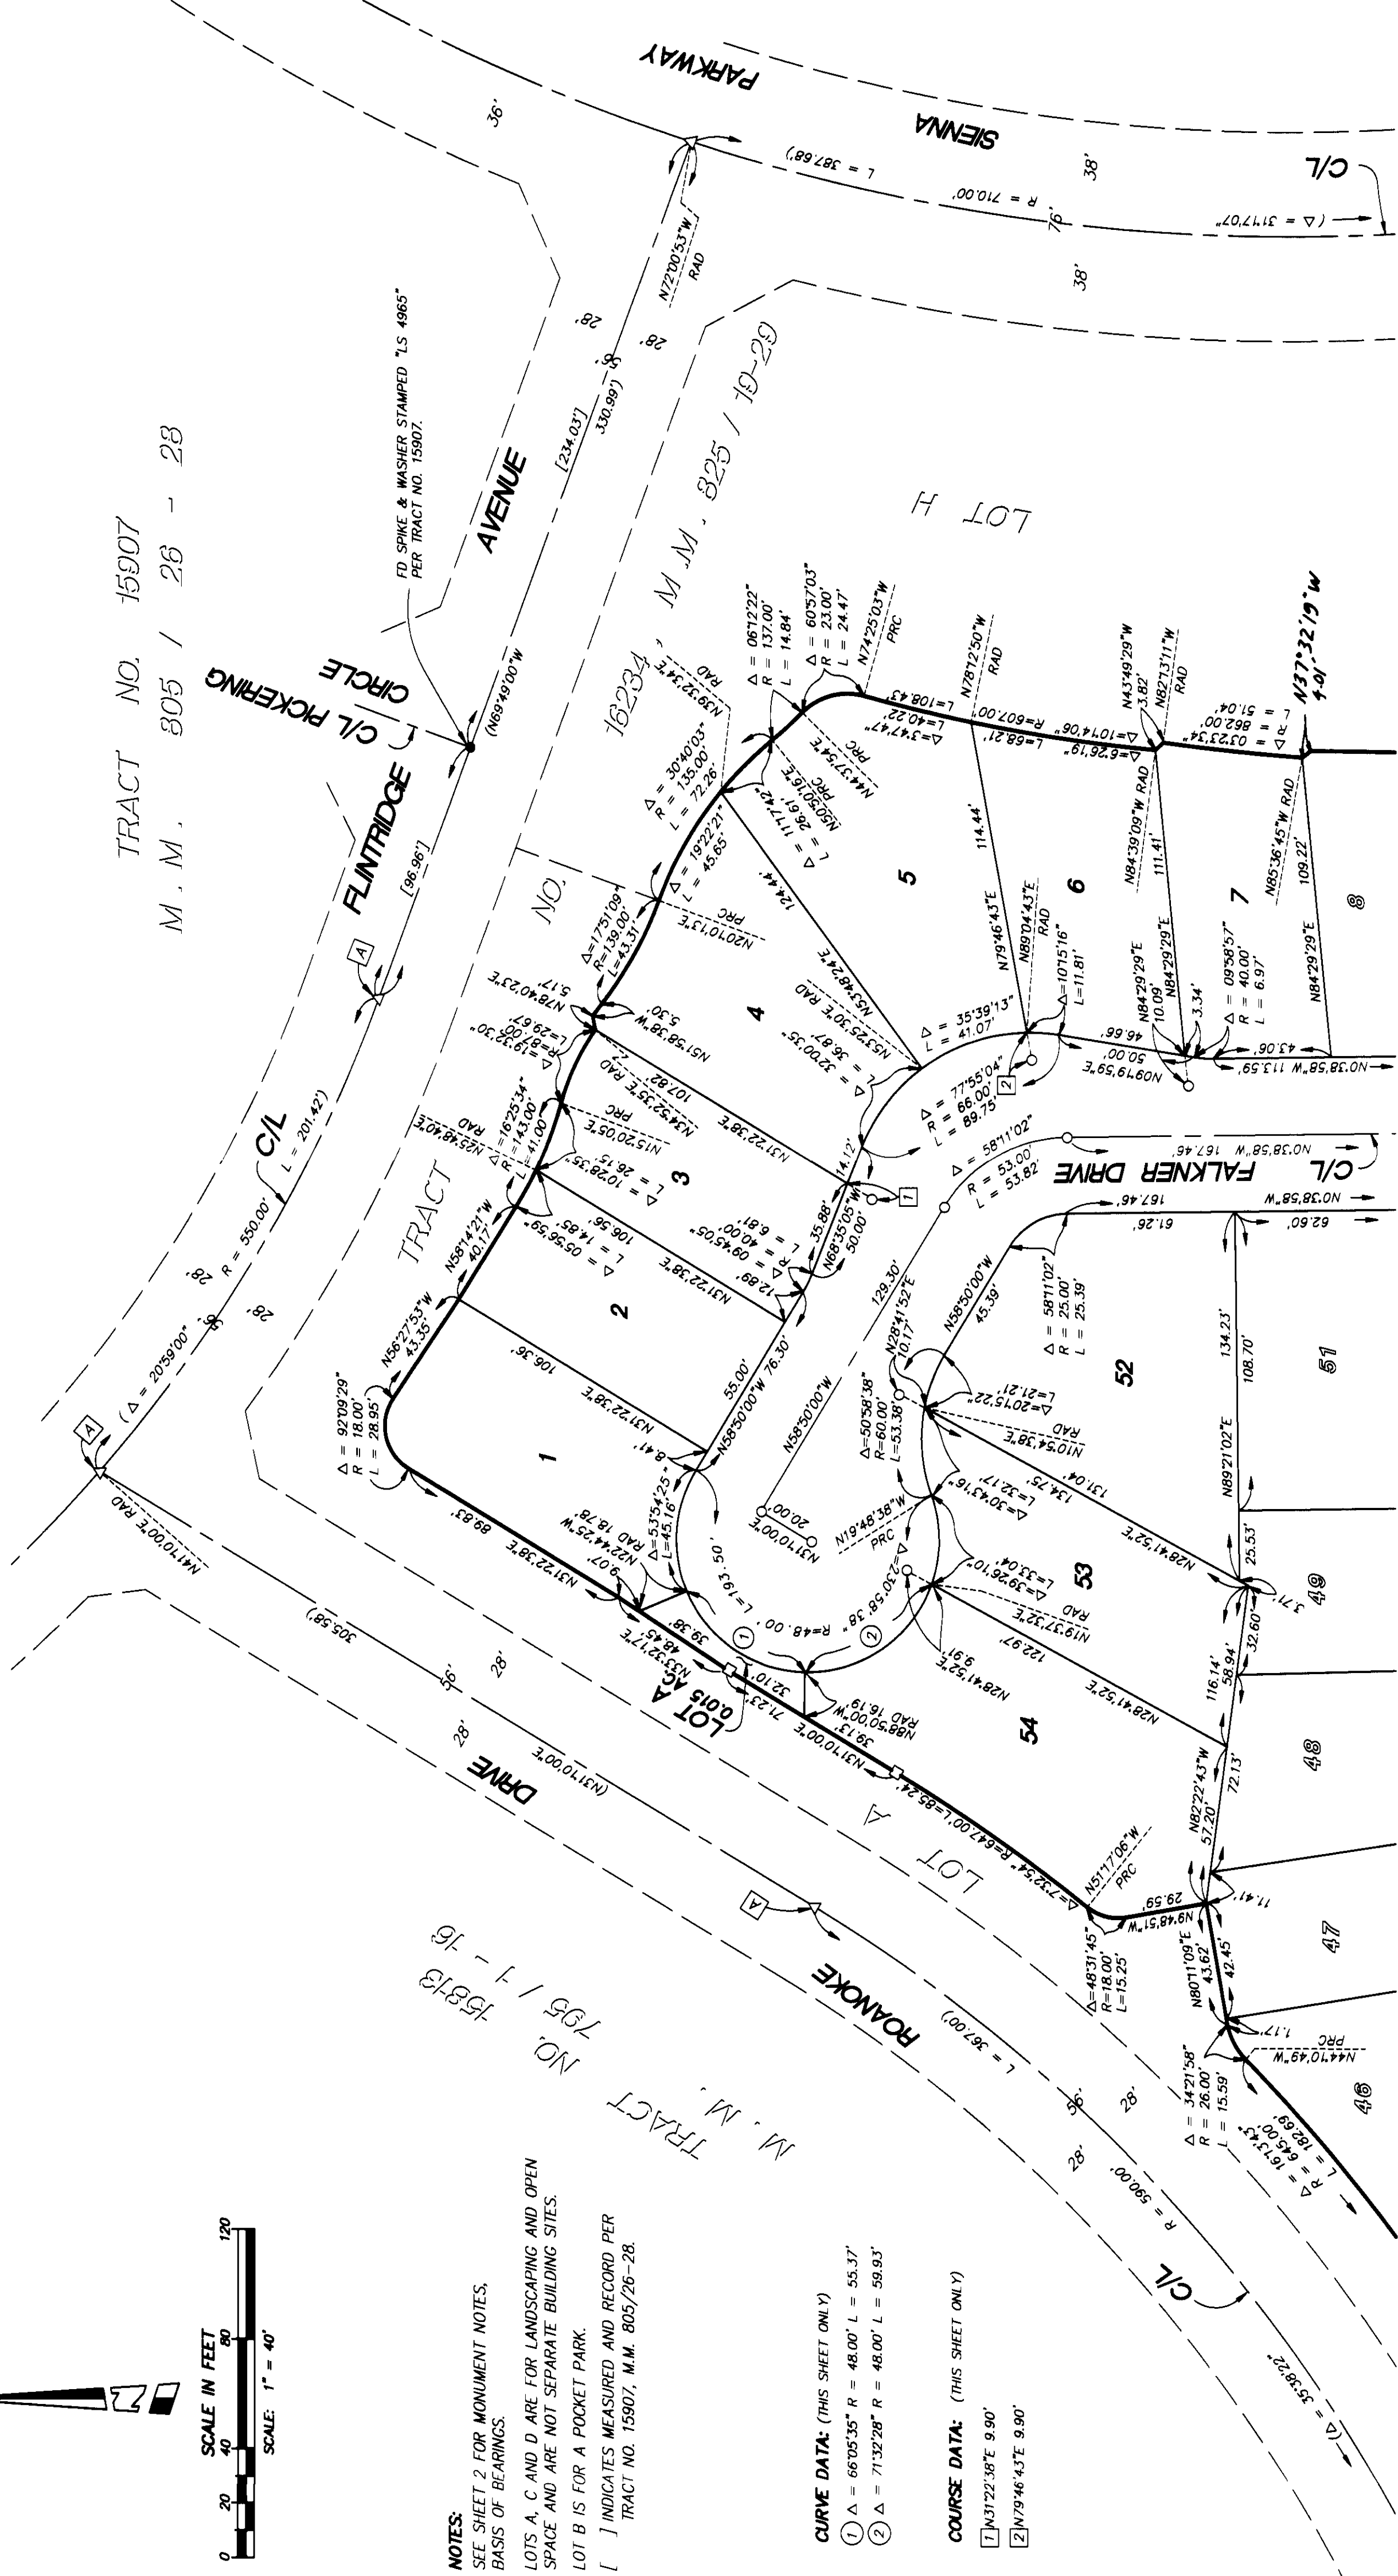

TRACT NO. 16238


IN THE UNINCORPORATED TERRITORY OF ORANGE COUNTY, CALIFORNIA

JANUARY 2002

JAMES F. GILLEN, L.S. 5557

HUITT-ZOLIARS

54 NUMBERED LOTS AND LETTERED LOTS A, B, C AND D 12.530 ACRES

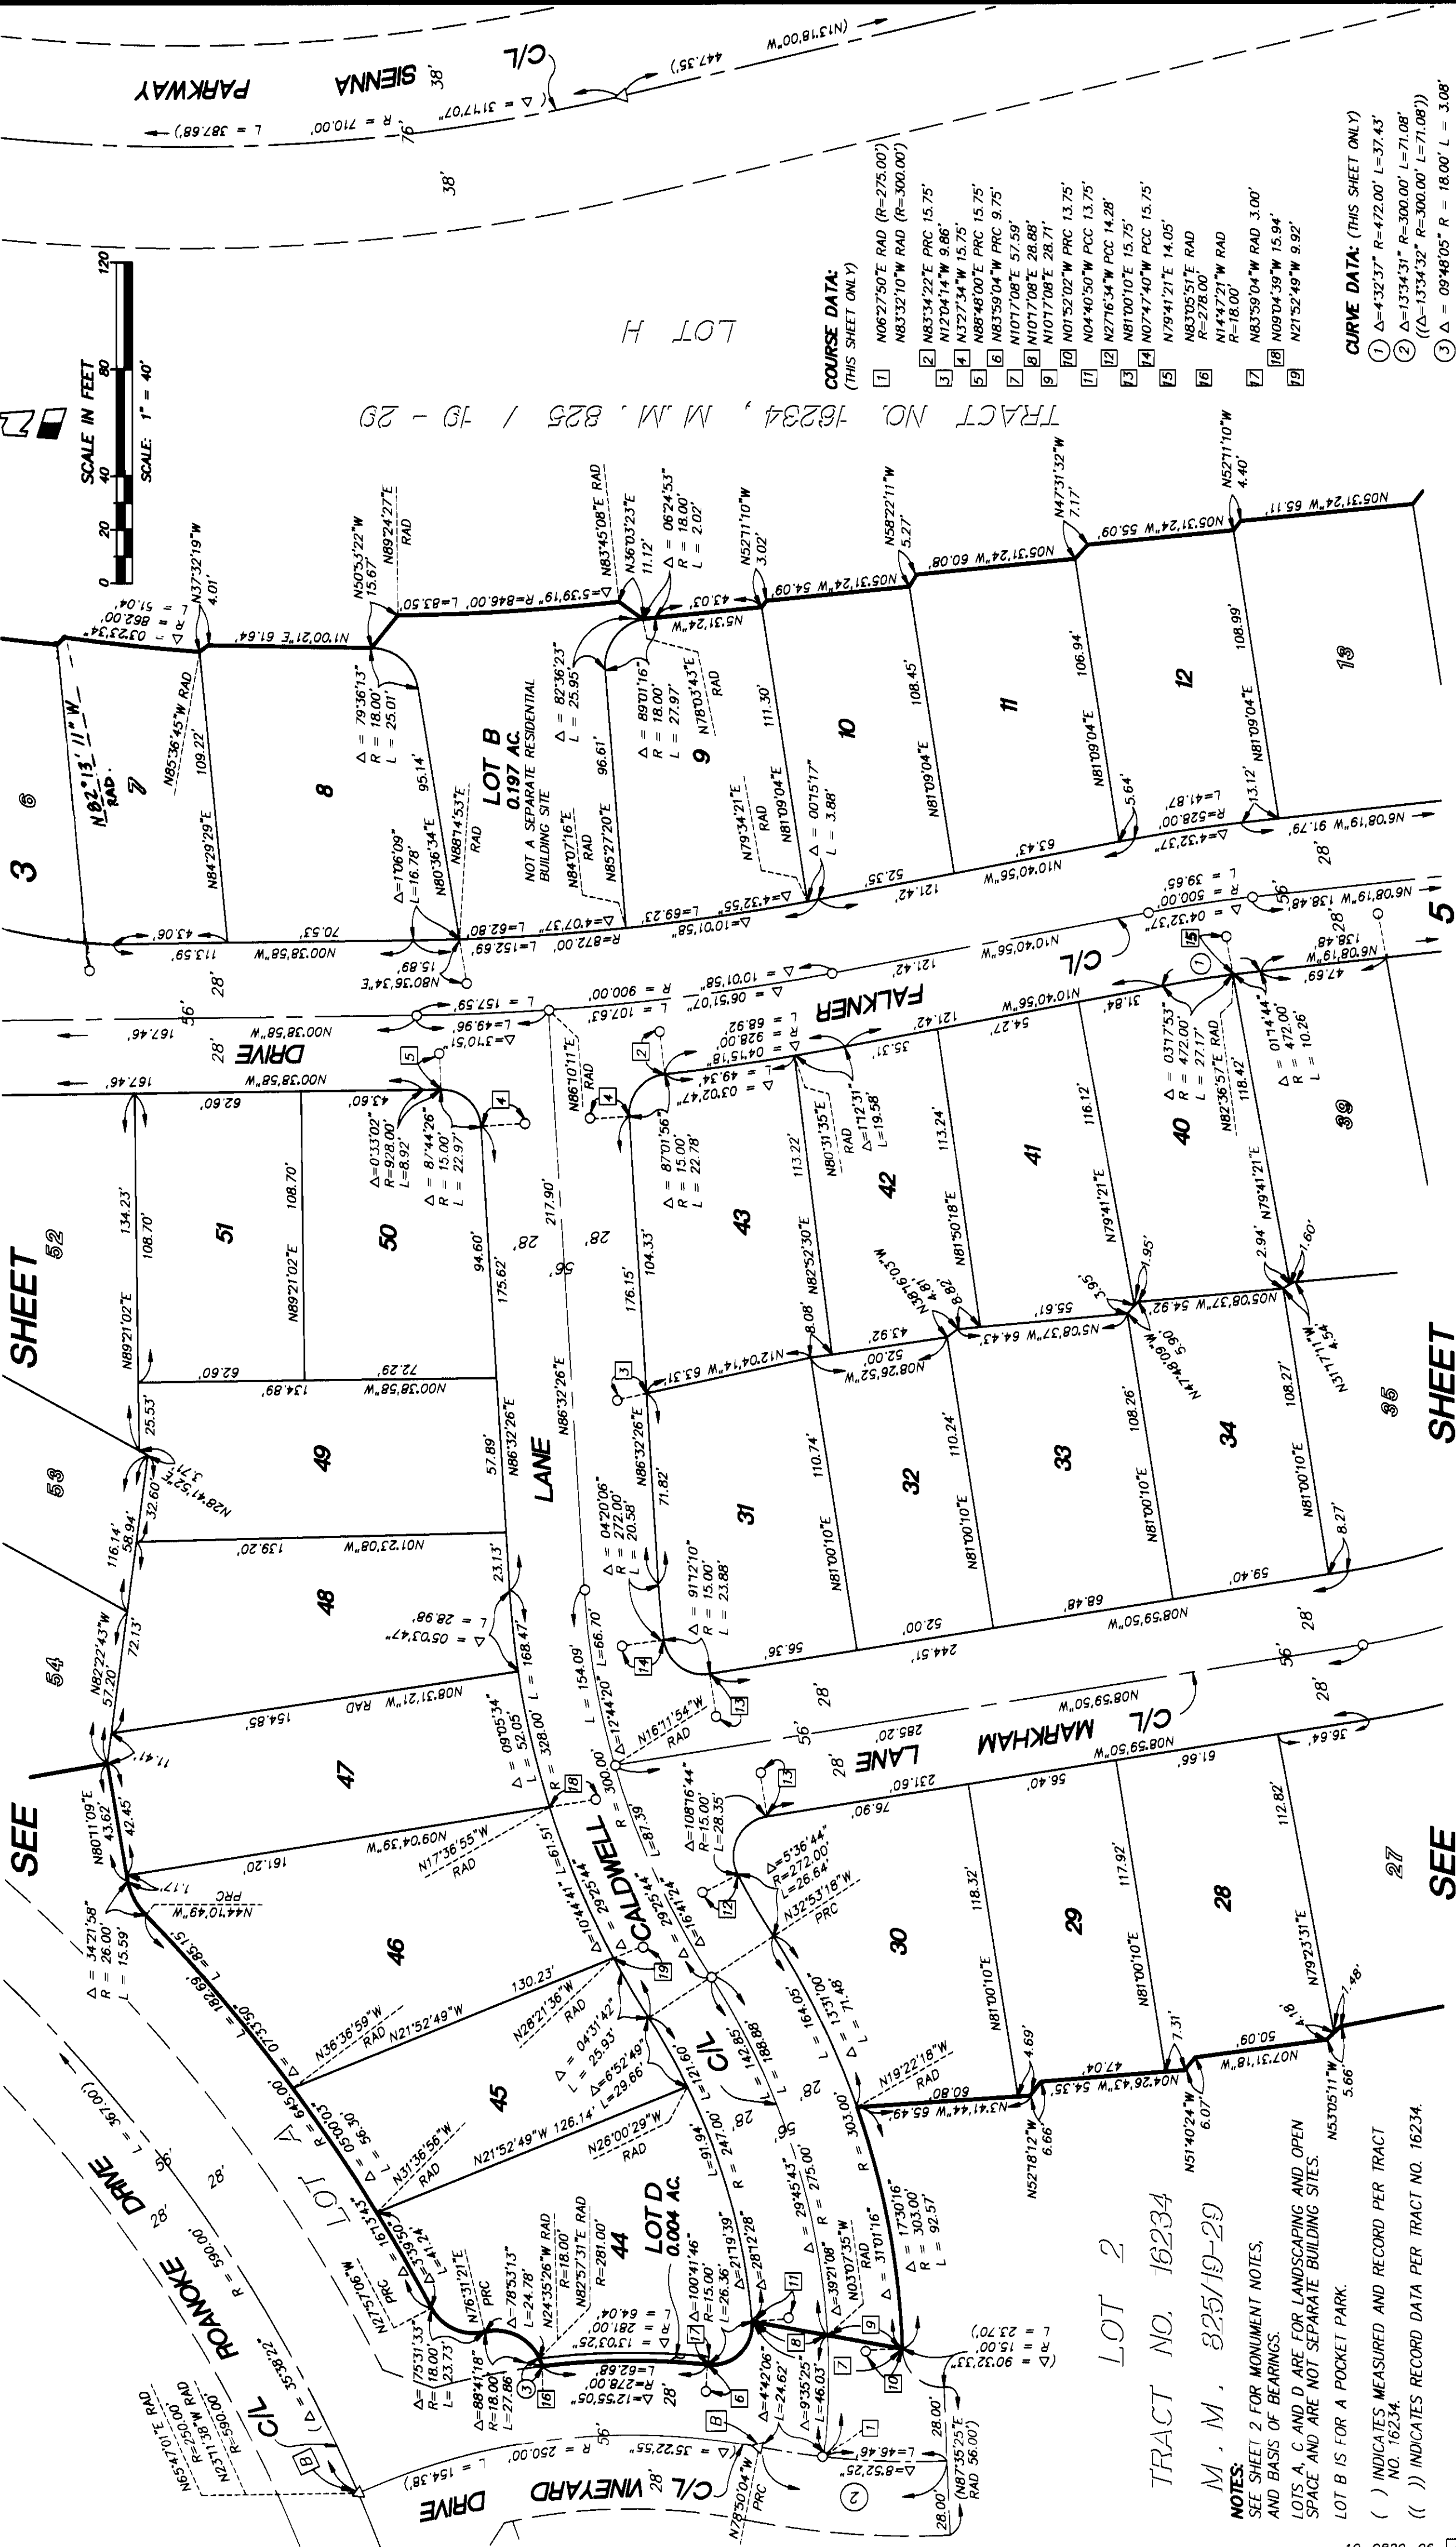

CURVE DATA: (THIS SHEET ONLY)

- ① $\Delta = 432.37^\circ$ $R = 472.00'$ $L = 37.43'$
- ② $\Delta = 1334.31^\circ$ $R = 300.00'$ $L = 71.08'$
(($\Delta = 1334.32^\circ$ $R = 300.00'$ $L = 71.08'$))
- ③ $\Delta = 0948.05^\circ$ $R = 18.00'$ $L = 3.08'$

NOTES:

SEE SHEET 2 FOR MONUMENT NOTES,
AND BASIS OF BEARINGS.

LOTS A, C AND D ARE FOR LANDSCAPING AND OPEN
SPACE AND ARE NOT SEPARATE BUILDING SITES.

LOT B IS FOR A POCKET PARK.

() INDICATES MEASURED AND RECORD PER TRACT
NO. 16234.

(()) INDICATES RECORD DATA PER TRACT NO. 16234.

TRACT NO. 16234

LOT 2



TRACT NO. 16238

IN THE UNINCORPORATED TERRITORY OF ORANGE COUNTY, CALIFORNIA
JAMES F. GILLEN, L.S. 5557

HUITT-ZOLIARS

54 NUMBERED LOTS AND LETTERED LOTS A, B, C AND D 12.530 ACRES

SHEET 4

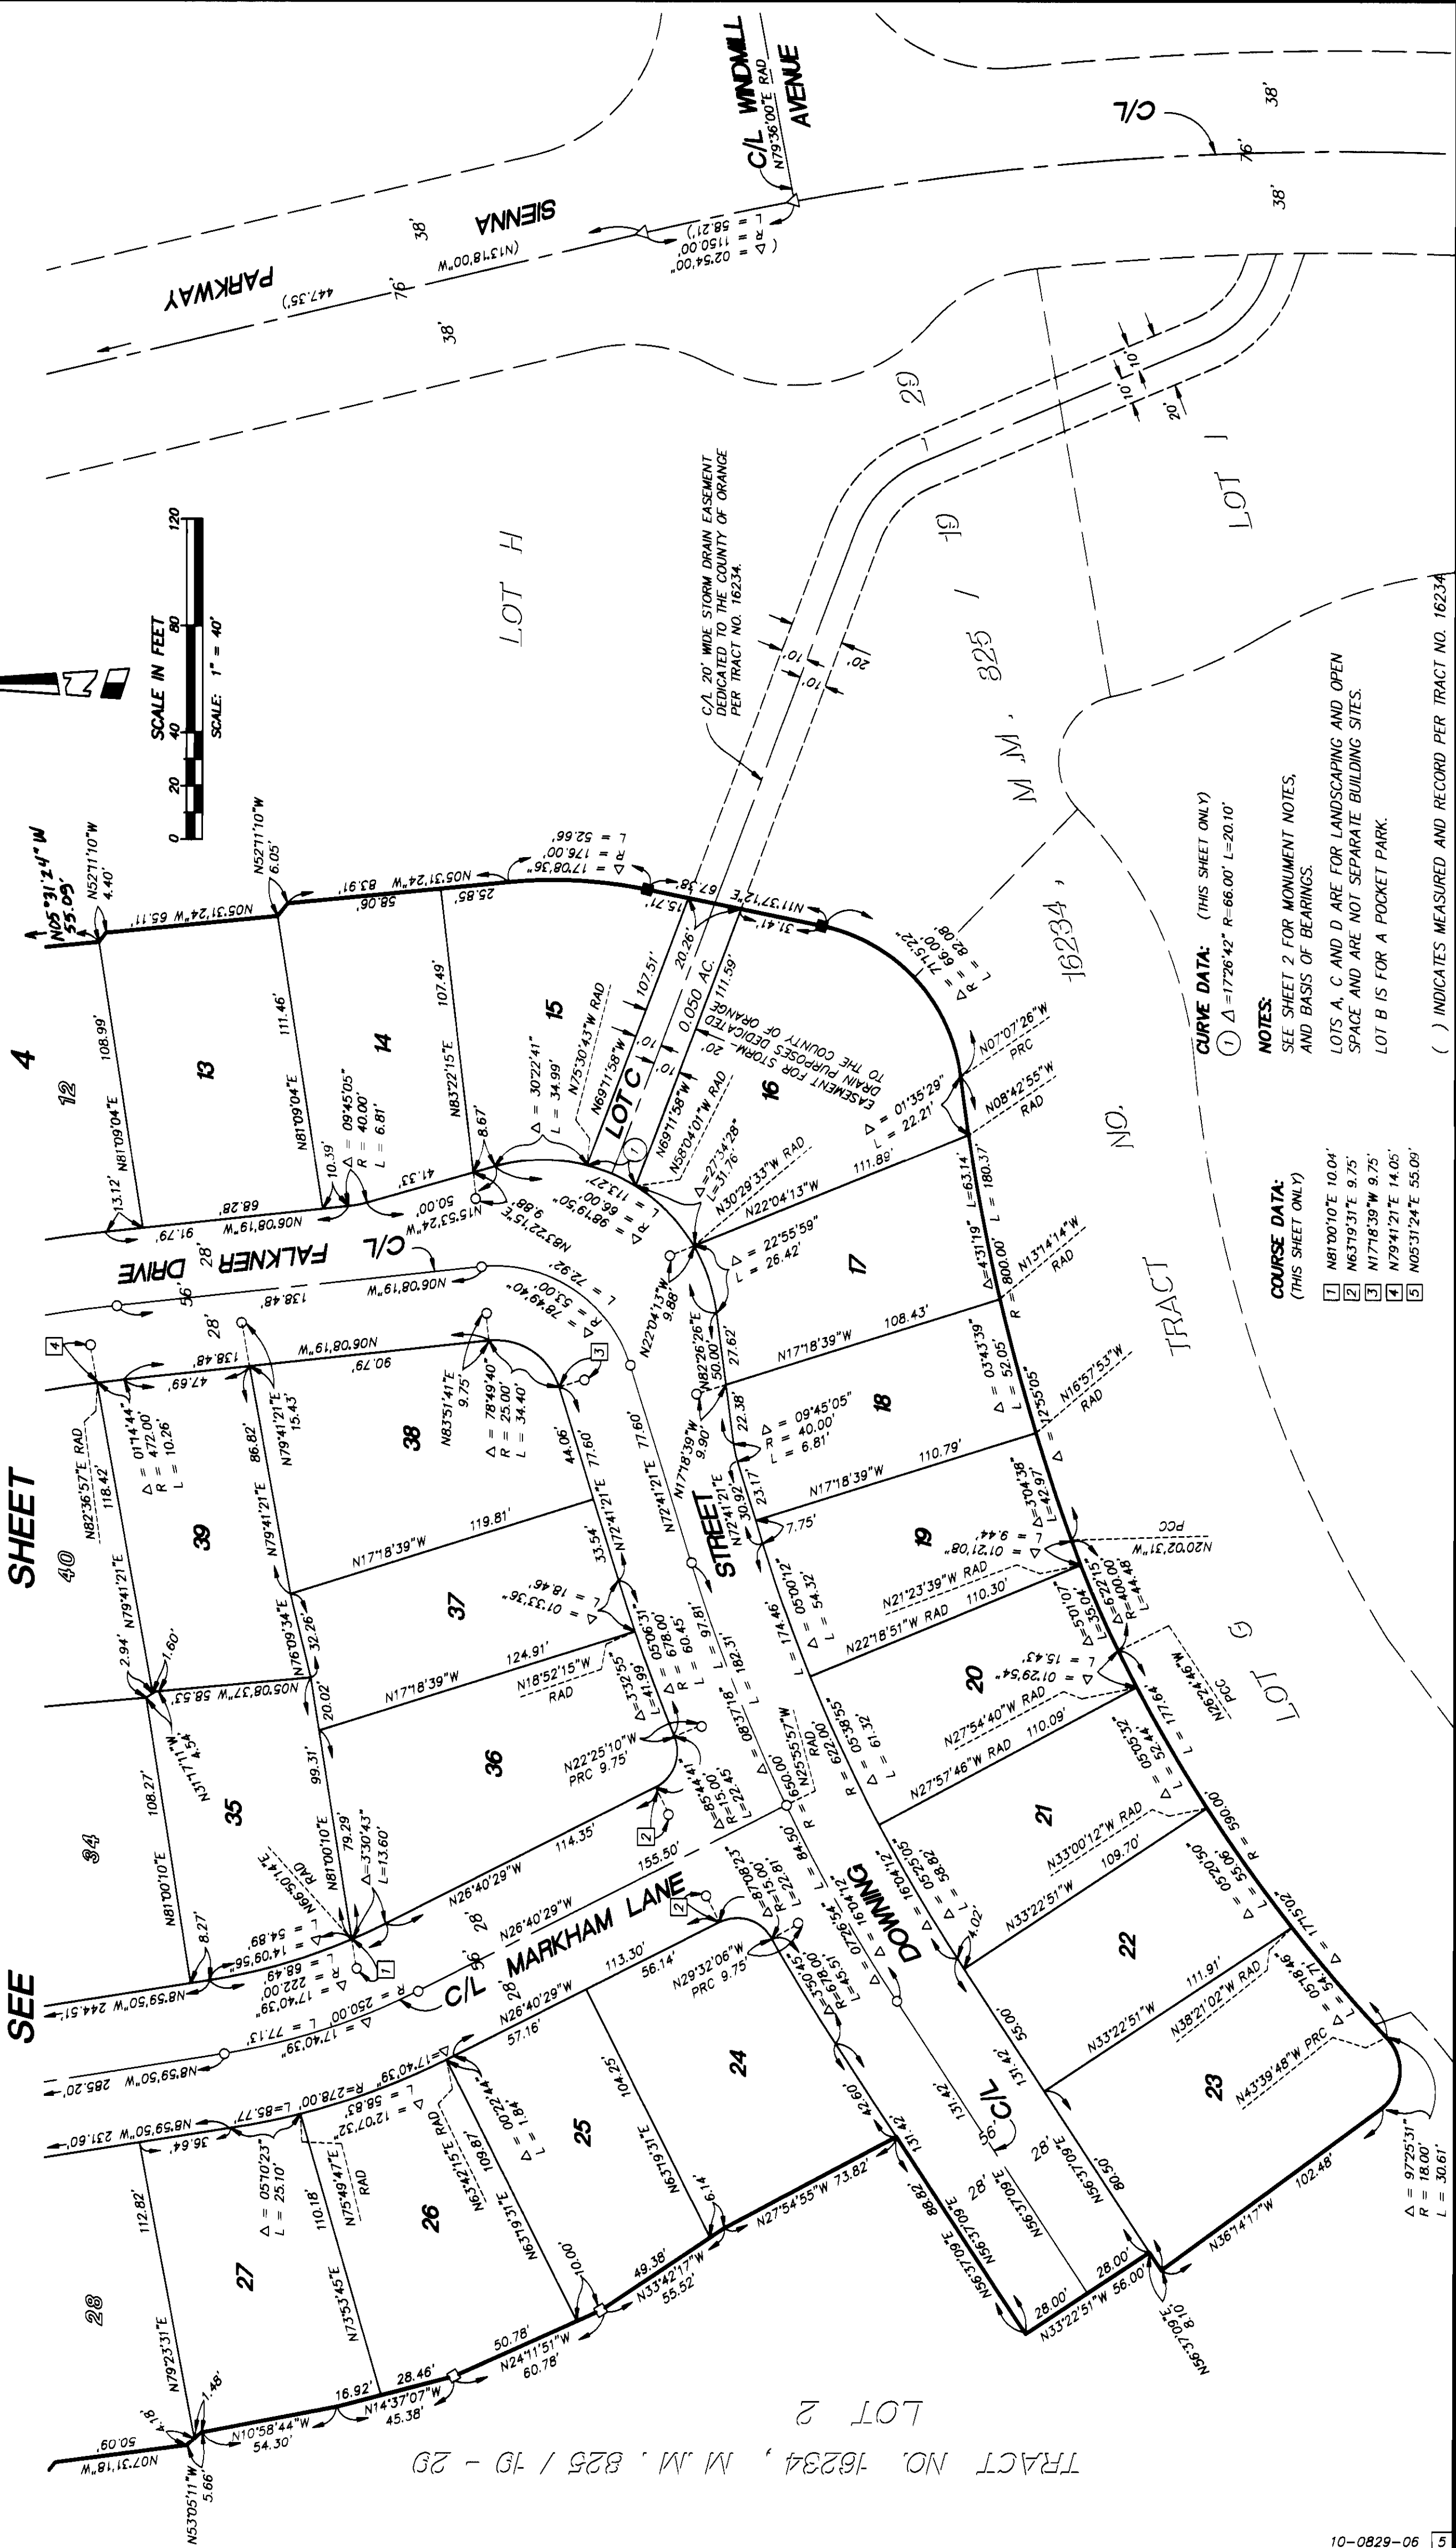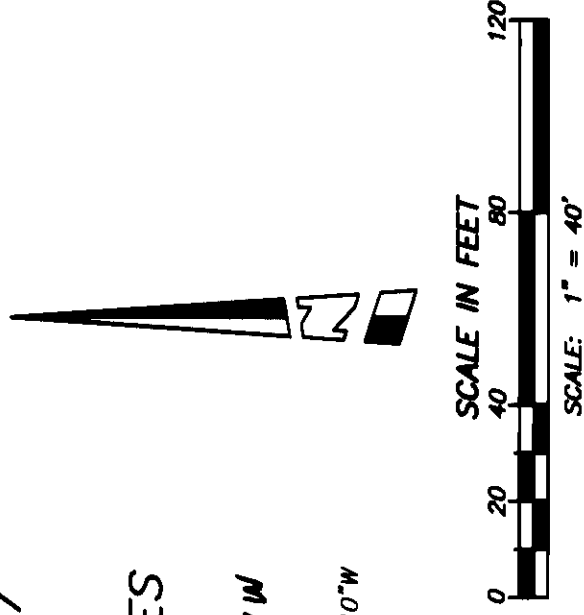

COURSE DATA:
(THIS SHEET ONLY)

- 1 N81°00'10"E 10.04'
- 2 N63°19'31"E 9.75'
- 3 N17°18'39"W 9.75'
- 4 N79°41'21"E 14.05'
- 5 N05°31'24"E 55.09'

NOTES:

SEE SHEET 2 FOR MONUMENT NOTES,
AND BASIS OF BEARINGS.

LOTS A, C AND D ARE FOR LANDSCAPING AND OPEN
SPACE AND ARE NOT SEPARATE BUILDING SITES.
LOT B IS FOR A POCKET PARK.

CURVE DATA: (THIS SHEET ONLY)
① $\Delta = 1726'42''$ R=66.00' L=20.10'

() INDICATES MEASURED AND RECORD PER TRACT NO. 16234