

SHEET 1 OF 7 SHEETS
13.419 ACRES
4 LOTS AND LOTS "A" THROUGH "F"
BEING ALL OF TENTATIVE TRACT 16239
BLOCK 5157 MODULE 26

TRACT NO. 16239

IN THE UNINCORPORATED TERRITORY OF THE
COUNTY OF ORANGE, STATE OF CALIFORNIA

BEING A SUBDIVISION OF LOT 5 OF TRACT NO. 16234, PER MAP FILED
IN BOOK 825, PAGES 19 THROUGH 29, INCLUSIVE, OF MISCELLANEOUS
MAPS, RECORDS OF ORANGE COUNTY.

WAGNER HALLADAY, INC.

ROBERT N. MIM MACK L.S. 5314 DATE OF SURVEY: JANUARY, 2002

ACCEPTED AND FILED AT THE
REQUEST OF
FIRST AMERICAN TITLE INSURANCE CO.

DATE JUNE 26, 2002
TIME 08:15 AM FEE \$ 19.00
INSTRUMENT # 20020533421
BOOK 834 PAGE 9-15 m/m
BY DARLENE J. BLOOM
INTERIM COUNTY CLERK-RECORDER
DEPUTY

OWNERSHIP CERTIFICATE

WE, THE UNDERSIGNED, BEING ALL PARTIES HAVING ANY RECORD TITLE INTEREST IN THE LAND COVERED
BY THIS MAP, DO HEREBY CONSENT TO THE PREPARATION AND RECORDATION OF SAID MAP, AS SHOWN
WITHIN THE DISTINCTIVE BORDER LINE.

WE HEREBY DEDICATE TO THE COUNTY OF ORANGE: THE EASEMENTS FOR EMERGENCY AND PUBLIC SERVICE
INGRESS AND EGRESS PURPOSES AS SHOWN ON THIS MAP.

WE ALSO HEREBY DEDICATE TO THE SANTA MARGARITA WATER DISTRICT THE EASEMENTS FOR SEWER AND
WATER PURPOSES AS SHOWN ON THIS MAP, WHICH EASEMENTS SHALL BE SUBJECT TO THE SAME TERMS AND
CONDITIONS AS ARE SHOWN IN THAT CERTAIN EASEMENT RECORDED OCTOBER 6, 1980, IN BOOK 13776,
PAGE 341, OF OFFICIAL RECORDS OF ORANGE COUNTY.

WL HOMES LLC, A DELAWARE LIMITED LIABILITY COMPANY
DBA JOHN LAING HOMES

BY: STEVE KABEL
PRINT NAME PRINT TITLE
STEVE KABEL PRESIDENT

BY: Wayne J. Stelmar
PRINT NAME PRINT TITLE
Wayne J. Stelmar CFO

RESIDENTIAL FUNDING CORPORATION, A DELAWARE CORPORATION, AS BENEFICIARY UNDER DEED OF TRUST
RECORDED FEBRUARY 6, 2002, AS INSTRUMENT NO. 20020101722, OFFICIAL RECORDS OF ORANGE COUNTY.

BY: MICHAEL F. RIPLEY
PRINT NAME PRINT TITLE
MICHAEL F. RIPLEY DIRECTOR

BY: Lance Franklin
PRINT NAME PRINT TITLE
Lance Franklin Director

DMB LADERA, L.L.C., A DELAWARE LIMITED LIABILITY COMPANY, BENEFICIARY UNDER A DEED OF
TRUST RECORDED FEBRUARY 6, 2002, AS INSTRUMENT NO. 20020101721 OF OFFICIAL RECORDS
OF ORANGE COUNTY.

BY: RANCHO MISSION VIEJO, L.L.C., A DELAWARE LIMITED LIABILITY COMPANY,
AS AGENT AND OR MANAGER

BY: DONALD T. STAHLIN
PRINT NAME PRINT TITLE
DONALD T. STAHLIN DIRECTOR

BY: Stephen C. Schrank
PRINT NAME PRINT TITLE
Stephen C. Schrank Executive Vice President

NOTARY ACKNOWLEDGMENT

STATE OF CALIFORNIA)
COUNTY OF ORANGE) SS

ON THIS 19th DAY OF March, 2002, BEFORE ME Serelle M. Adams
Notary Public, PERSONALLY APPEARED Steve Kabel AND
Wayne J. Stelmar PERSONALLY KNOWN TO ME OR PROVED TO ME ON THE BASIS
OF SATISFACTORY EVIDENCE TO BE THE PERSONS WHOSE NAMES ARE SUBSCRIBED TO THE WITHIN INSTRUMENT
AND ACKNOWLEDGED TO ME THAT THEY EXECUTED THE SAME IN THEIR AUTHORIZED CAPACITIES, AND THAT BY
THEIR SIGNATURES ON THE INSTRUMENT THE PERSONS, OR THE ENTITY UPON BEHALF OF WHICH THE PERSONS
ACTED, EXECUTED THE INSTRUMENT.

WITNESS MY HAND:

MY PRINCIPAL PLACE OF BUSINESS IS IN
Orange COUNTY.

MY COMMISSION EXPIRES: Dec 10, 2005

Serelle M. Adams
NOTARY PUBLIC IN AND FOR SAID STATE
Serelle M. Adams
(PRINT NAME)

SURVEYOR'S STATEMENT

I HEREBY STATE THAT THIS MAP CONSISTING OF 7 SHEETS, CORRECTLY REPRESENTS A TRUE AND COMPLETE
SURVEY AS SHOWN MADE IN JANUARY, 2002; WAS MADE BY ME OR UNDER MY DIRECTION; THAT THE MONU-
MENTS ARE OF THE CHARACTER AND OCCUPY (OR WILL OCCUPY) THE POSITIONS INDICATED BY SAID MAP; AND
THAT SAID MONUMENTS ARE (OR WILL BE) SUFFICIENT TO ENABLE THE SURVEY TO BE RETRACED.



Robert N. Mim Mack
ROBERT N. MIM MACK L.S. 5314
MY LICENSE EXPIRES: 12/31/03

COUNTY SURVEYOR'S STATEMENT

I HEREBY STATE THAT I HAVE EXAMINED THIS MAP AND HAVE FOUND IT TO BE SUBSTANTIALLY IN CONFORMANCE
WITH THE TENTATIVE MAP AS FILED WITH, AMENDED AND APPROVED BY THE ORANGE COUNTY SUBDIVISION COMMIT-
TEE; THAT ALL THE PROVISIONS OF THE SUBDIVISION MAP ACT AND COUNTY SUBDIVISION REGULATIONS HAVE
BEEN COMPLIED WITH AND I AM SATISFIED THAT SAID MAP IS TECHNICALLY CORRECT.

DATED THIS 6TH DAY OF JUNE, 2002.

Michael K. Sullivan
JOHN CANAS, COUNTY SURVEYOR
L.S. 4408, EXPIRATION 9/30/05

BY: MICHAEL K. SULLIVAN, DEPUTY
L.S. 6254 EXPIRES 6-30-02



COUNTY TREASURER-TAX COLLECTOR'S CERTIFICATE

STATE OF CALIFORNIA)
COUNTY OF ORANGE) SS

I HEREBY CERTIFY THAT ACCORDING TO THE RECORDS OF MY OFFICE THERE ARE NO LIENS AGAINST THE LAND
COVERED BY THIS MAP OR ANY PART THEREOF FOR UNPAID STATE, COUNTY, MUNICIPAL OR LOCAL TAXES OR
SPECIAL ASSESSMENTS COLLECTED AS TAXES, EXCEPT TAXES OR SPECIAL ASSESSMENTS COLLECTED AS TAXES
NOT YET PAYABLE.

AND DO ALSO HEREBY CERTIFY TO THE RECORDER OF ORANGE COUNTY THAT THE PROVISIONS OF THE SUBDIVISION
MAP ACT HAVE BEEN COMPLIED WITH REGARDING DEPOSITS TO SECURE THE PAYMENT OF TAXES OR SPECIAL
ASSESSMENTS COLLECTED AS TAXES ON THE LAND COVERED BY THIS MAP.

DATED THIS 29th DAY OF May, 2002.

JOHN M. W. MOORLACH
COUNTY TREASURER-TAX COLLECTOR

BY: Mac Worsman
DEPUTY TREASURER-TAX COLLECTOR

CLERK OF THE BOARD OF SUPERVISORS' CERTIFICATE

STATE OF CALIFORNIA)
COUNTY OF ORANGE) SS

I HEREBY CERTIFY THAT THIS MAP WAS PRESENTED FOR APPROVAL TO THE BOARD OF SUPERVISORS OF ORANGE
COUNTY AT A REGULAR MEETING THEREOF HELD ON THE 18th DAY OF June, 2002,
AND THAT THEREUPON SAID BOARD DID, BY AN ORDER DULY PASSED AND ENTERED, APPROVE SAID MAP,

AND DID ACCEPT ON BEHALF OF THE COUNTY OF ORANGE:

(1) THE EASEMENTS FOR EMERGENCY AND PUBLIC SERVICE INGRESS AND EGRESS PURPOSES AS DEDICATED HEREON.

AND DID ALSO APPROVE SUBJECT MAP PURSUANT TO THE PROVISIONS OF SECTION 66436 (a)(3)
OF THE SUBDIVISION MAP ACT.

DATED THIS 19th DAY OF June, 2002.

Darlene J. Bloom
CLERK OF THE BOARD OF SUPERVISORS
OF ORANGE COUNTY, CALIFORNIA



SEE SHEET 2 FOR ADDITIONAL NOTARY ACKNOWLEDGMENTS, SIGNATURE
OMISSIONS, ADDITIONAL DECLARATIONS AND SANTA MARGARITA WATER
DISTRICT ACCEPTANCE CERTIFICATE AND NOTARY ACKNOWLEDGMENT.

SHEET 2 OF 7 SHEETS
13.419 ACRES
4 LOTS AND LOTS "A" THROUGH "F"

TRACT NO. 16239

IN THE UNINCORPORATED TERRITORY OF THE
COUNTY OF ORANGE, STATE OF CALIFORNIA

WAGNER HALLADAY, INC.

ROBERT N. MIM MACK L.S. 5314 DATE OF SURVEY: JANUARY, 2002

SIGNATURE OMISSIONS

PURSUANT TO SECTION 66436 (a)(3) OF THE SUBDIVISION MAP ACT, THE SIGNATURES OF THE FOLLOWING HAVE BEEN OMITTED:

1. LADERA DEVELOPMENT COMPANY, L.L.C., HOLDER OF OIL, GAS, MINERAL AND WATER RIGHTS PER DOCUMENT RECORDED DECEMBER 10, 1996, AS INSTRUMENT NO. 19960824029 OF OFFICIAL RECORDS.

FIRE HAZARD NOTIFICATION NOTE

THIS PROJECT IS LOCATED IN STATE RESPONSIBILITY AREA BASED ON MAPPING BY THE STATE OF CALIFORNIA, HOWEVER THIS PROJECT DOES NOT HAVE ANY EXPOSURE TO WILD LAND AREAS BASED UPON OC FIRE AUTHORITY LETTER DATED FEBRUARY 9, 2001 PER ORDINANCE 3959-3960 OF THE COUNTY OF ORANGE.

FIRE PROTECTION AREA NOTE

A TOTAL EXCLUSION FROM THE SPECIAL FIRE PROTECTION AREA HAS BEEN GRANTED BY THE OC FIRE AUTHORITY PER LETTER DATED FEBRUARY 9, 2001 FROM THE OC FIRE AUTHORITY AND THEREFORE, THIS PROJECT IS NO LONGER IN A SPECIAL FIRE PROTECTION AREA PER ORDINANCE 3959-3960 OF THE COUNTY OF ORANGE.

NOTE

PROPERTY MAY BE SUBJECT TO IMPACTS FROM THE PROPOSED FOOTHILL/EASTERN TRANSPORTATION CORRIDORS.

FOOTHILL CIRCULATION PHASING PLAN NOTE

BUILDING PERMIT ISSUANCE SHALL BE PHASED IN ACCORDANCE WITH THE FOOTHILL CIRCULATION PHASING PLAN (FCPP) DEVELOPMENT PHASING PLAN, AND SHALL ALSO BE SUBJECT TO ANY OTHER BOARD OF SUPERVISORS APPROVED GROWTH MANAGEMENT PHASING PLAN PERTAINING TO THE TIMELY PROVISION OF PUBLIC SERVICES AND FACILITIES.

EASEMENT NOTES

- INDICATES AN EASEMENT TO THE COUNTY OF ORANGE FOR EMERGENCY AND PUBLIC SERVICE INGRESS AND EGRESS PURPOSES AS DEDICATED HEREON.
- INDICATES A 30' WIDE EASEMENT TO THE SANTA MARGARITA WATER DISTRICT FOR WATER AND SEWER LINE PURPOSES AS DEDICATED HEREON.
- INDICATES A 20' WIDE EASEMENT TO SANTA MARGARITA WATER DISTRICT FOR WATER LINE PURPOSES AS DEDICATED HEREON.
- INDICATES AN EASEMENT TO SANTA MARGARITA WATER DISTRICT FOR WATER AND SEWER LINE PURPOSES AS DEDICATED HEREON.
- INDICATES AN EASEMENT FOR PUBLIC UTILITY PURPOSES AS RESERVED HEREON.

AUTOMATIC FIRE SPRINKLER SYSTEMS

ALL RESIDENTIAL STRUCTURES EXCEEDING 5,500 SQUARE FEET (PER AMENDMENT) AND ALL STRUCTURES EXCEEDING FIRE DEPARTMENT ACCESS REQUIREMENTS SHALL BE PROTECTED BY AN AUTOMATIC FIRE SPRINKLER SYSTEM IN A MANNER MEETING THE APPROVAL OF THE FIRE CHIEF.

PRIVATE STREET NOTIFICATION

THE PRIVATE STREETS CONSTRUCTED WITHIN THIS MAP SHALL BE OWNED, OPERATED, AND MAINTAINED BY THE DEVELOPER, SUCCESSORS OR ASSIGNS. THE COUNTY OF ORANGE SHALL HAVE NO RESPONSIBILITY THEREFORE UNLESS PURSUANT TO APPROPRIATE SECTIONS OF THE STREETS AND HIGHWAYS CODE OF THE STATE OF CALIFORNIA, THE SAID PRIVATE STREETS HAVE BEEN ACCEPTED INTO THE COUNTY ROAD SYSTEM BY APPROPRIATE RESOLUTION OF THE ORANGE COUNTY BOARD OF SUPERVISORS.

SANTA MARGARITA WATER DISTRICT CERTIFICATE OF ACCEPTANCE

THE UNDERSIGNED, BEING THE DULY APPOINTED AGENT OF THE SANTA MARGARITA WATER DISTRICT, A PUBLIC CORPORATION IN ORANGE COUNTY, CALIFORNIA, PURSUANT TO ITS RESOLUTION NO. 88-10-2, DOES HEREBY ACCEPT ON BEHALF OF SAID DISTRICT, THE EASEMENTS FOR WATER AND SEWER PURPOSES, AS DEDICATED AND AS SHOWN ON THIS TRACT MAP, AND DOES HEREBY ACCEPT ON BEHALF OF SAID DISTRICT ALL WATER AND WATER RIGHTS, AS DEDICATED ON THIS TRACT MAP, BY AND BETWEEN THE SANTA MARGARITA WATER DISTRICT AND WL HOMES, LLC, AND DOES HEREBY CERTIFY THAT THE GRANTEE CONSENTS TO THE RECORDATION OF SAID TRACT.

BY: Daniel R. Feron
DANIEL R. FERONS - CHIEF ENGINEER
SANTA MARGARITA WATER DISTRICT

NOTARY ACKNOWLEDGMENT

SANTA MARGARITA WATER DISTRICT

STATE OF CALIFORNIA)
COUNTY OF ORANGE) SS

ON THIS 4th DAY OF APRIL, 2002, BEFORE ME ANDREA M. EVANS, Notary Public, PERSONALLY APPEARED DANIEL R. FERONS, PERSONALLY KNOWN TO ME OR PROVED TO ME ON THE BASIS OF SATISFACTORY EVIDENCE TO BE THE PERSON WHOSE NAME IS SUBSCRIBED TO THE WITHIN INSTRUMENT AND ACKNOWLEDGED TO ME THAT HE EXECUTED THE SAME IN HIS AUTHORIZED CAPACITY, AND THAT BY HIS SIGNATURE ON THE INSTRUMENT THE PERSON, OR THE ENTITY UPON BEHALF OF WHICH THE PERSON ACTED, EXECUTED THE INSTRUMENT.

WITNESS MY HAND:
Andrea M. Evans
NOTARY PUBLIC IN AND FOR SAID STATE
ANDREA M. EVANS
(PRINT NAME)

MY PRINCIPAL PLACE OF BUSINESS IS IN
ORANGE COUNTY

MY COMMISSION EXPIRES: 4/8/04

NOTARY ACKNOWLEDGMENT

STATE OF CALIFORNIA)
COUNTY OF Los Angeles) SS

ON THIS 20th DAY OF March, 2002, BEFORE ME Sonia E. Garcia, Notary Public, PERSONALLY APPEARED Michael F. Ripling AND Lance Franklin PERSONALLY KNOWN TO ME OR PROVED TO ME ON THE BASIS OF SATISFACTORY EVIDENCE TO BE THE PERSONS WHOSE NAMES ARE SUBSCRIBED TO THE WITHIN INSTRUMENT AND ACKNOWLEDGED TO ME THAT THEY EXECUTED THE SAME IN THEIR AUTHORIZED CAPACITIES, AND THAT BY THEIR SIGNATURES ON THE INSTRUMENT THE PERSONS, OR THE ENTITY UPON BEHALF OF WHICH THE PERSONS ACTED, EXECUTED THE INSTRUMENT.

MY PRINCIPAL PLACE OF BUSINESS IS IN
Los Angeles COUNTY.
MY COMMISSION EXPIRES: May 9, 2003

WITNESS MY HAND:
Sonia E. Garcia
NOTARY PUBLIC IN AND FOR SAID STATE
SONIA E. GARCIA
(PRINT NAME)

NOTARY ACKNOWLEDGMENT

STATE OF CALIFORNIA)
COUNTY OF ORANGE) SS

ON THIS 29th DAY OF March, 2002, BEFORE ME Tina T. Balen, Notary Public, PERSONALLY APPEARED Donald T. Stahl AND Stephen C. Schenck PERSONALLY KNOWN TO ME OR PROVED TO ME ON THE BASIS OF SATISFACTORY EVIDENCE TO BE THE PERSONS WHOSE NAMES ARE SUBSCRIBED TO THE WITHIN INSTRUMENT AND ACKNOWLEDGED TO ME THAT THEY EXECUTED THE SAME IN THEIR AUTHORIZED CAPACITIES, AND THAT BY THEIR SIGNATURES ON THE INSTRUMENT THE PERSONS, OR THE ENTITY UPON BEHALF OF WHICH THE PERSONS ACTED, EXECUTED THE INSTRUMENT.

MY PRINCIPAL PLACE OF BUSINESS IS IN
Orange COUNTY.
MY COMMISSION EXPIRES: 8/29/04

WITNESS MY HAND:
Tina T. Balen
NOTARY PUBLIC IN AND FOR SAID STATE
Tina T. Balen
(PRINT NAME)

SHEET 3 OF 7 SHEETS
13.419 ACRES
4 LOTS AND LOTS "A" THROUGH "F"

TRACT NO. 16239

IN THE UNINCORPORATED TERRITORY
OF THE COUNTY OF ORANGE, STATE OF CALIFORNIA

SCALE: 1" = 80'


WAGNER HALLADAY, INC.
ROBERT N. MIM MACK L.S. 5314 DATE OF SURVEY: JANUARY, 2002
FOR CONDOMINIUM PURPOSES
LOCATION AND INDEX MAP

EASEMENT NOTES:

- (A) INDICATES AN EASEMENT TO THE COUNTY OF ORANGE FOR EMERGENCY AND PUBLIC SERVICE INGRESS AND EGRESS PURPOSES AS DEDICATED HEREON.
- (B) INDICATES A 30' WIDE EASEMENT TO SANTA MARGARITA WATER DISTRICT FOR WATER AND SEWER LINE PURPOSES AS DEDICATED HEREON.
- (C) INDICATES A 20' WIDE EASEMENT TO SANTA MARGARITA WATER DISTRICT FOR WATER LINE PURPOSES AS DEDICATED HEREON.
- (D) INDICATES AN EASEMENT TO SANTA MARGARITA WATER DISTRICT FOR WATER AND SEWER LINE PURPOSES AS DEDICATED HEREON.
- (E) INDICATES AN EASEMENT FOR PUBLIC UTILITY PURPOSES AS RESERVED HEREON.

NOTES:

- INDICATES FOUND 2" I.P. TAGGED L.S. 5557 PER TRACT NO. 16234/ MM 825/19-29.
 - A 1" I.P. TAGGED "LS 5314" OR SPIKE & WASHER STAMPED "LS 5314" OR LEAD, TACK & TAG "LS. 5314" WILL BE SET AT ALL LOT CORNERS WITHIN 90 DAYS AFTER ACCEPTANCE OF IMPROVEMENTS.
 - A 2" I.P. TAGGED "LS 5314" OR SPIKE & WASHER STAMPED "LS 5314" OR LEAD, TACK & TAG "LS. 5314" WILL BE SET AT ALL TRACT ANGLE PTS., B.C.'s AND E.C.'s WITHIN 90 DAYS AFTER ACCEPTANCE OF IMPROVEMENTS.
 - LETTERED LOTS ARE FOR OPEN SPACE OR LANDSCAPING PURPOSES AND ARE NOT SEPARATE BUILDING SITES.
- BASIS OF BEARINGS:**
O.C.S. BENCHMARK DESIGNATION 388-36-88
AT THE SOUTHWEST CORNER OF THE INTERSECTION OF CROWN VALLEY PKWY. AND MARGUERITE PKWY.; 48 FT. WESTERLY OF THE CENTERLINE OF MARGUERITE PKWY.; 82 FT. SOUTHERLY OF THE CENTERLINE OF CROWN VALLEY PKWY. SET AT THE TOP OF THE NORTHWEST CORNER OF A 3 FT. BY 3 FT. CONCRETE BASE FOR THE TRAFFIC SIGNAL LIGHT POLE.

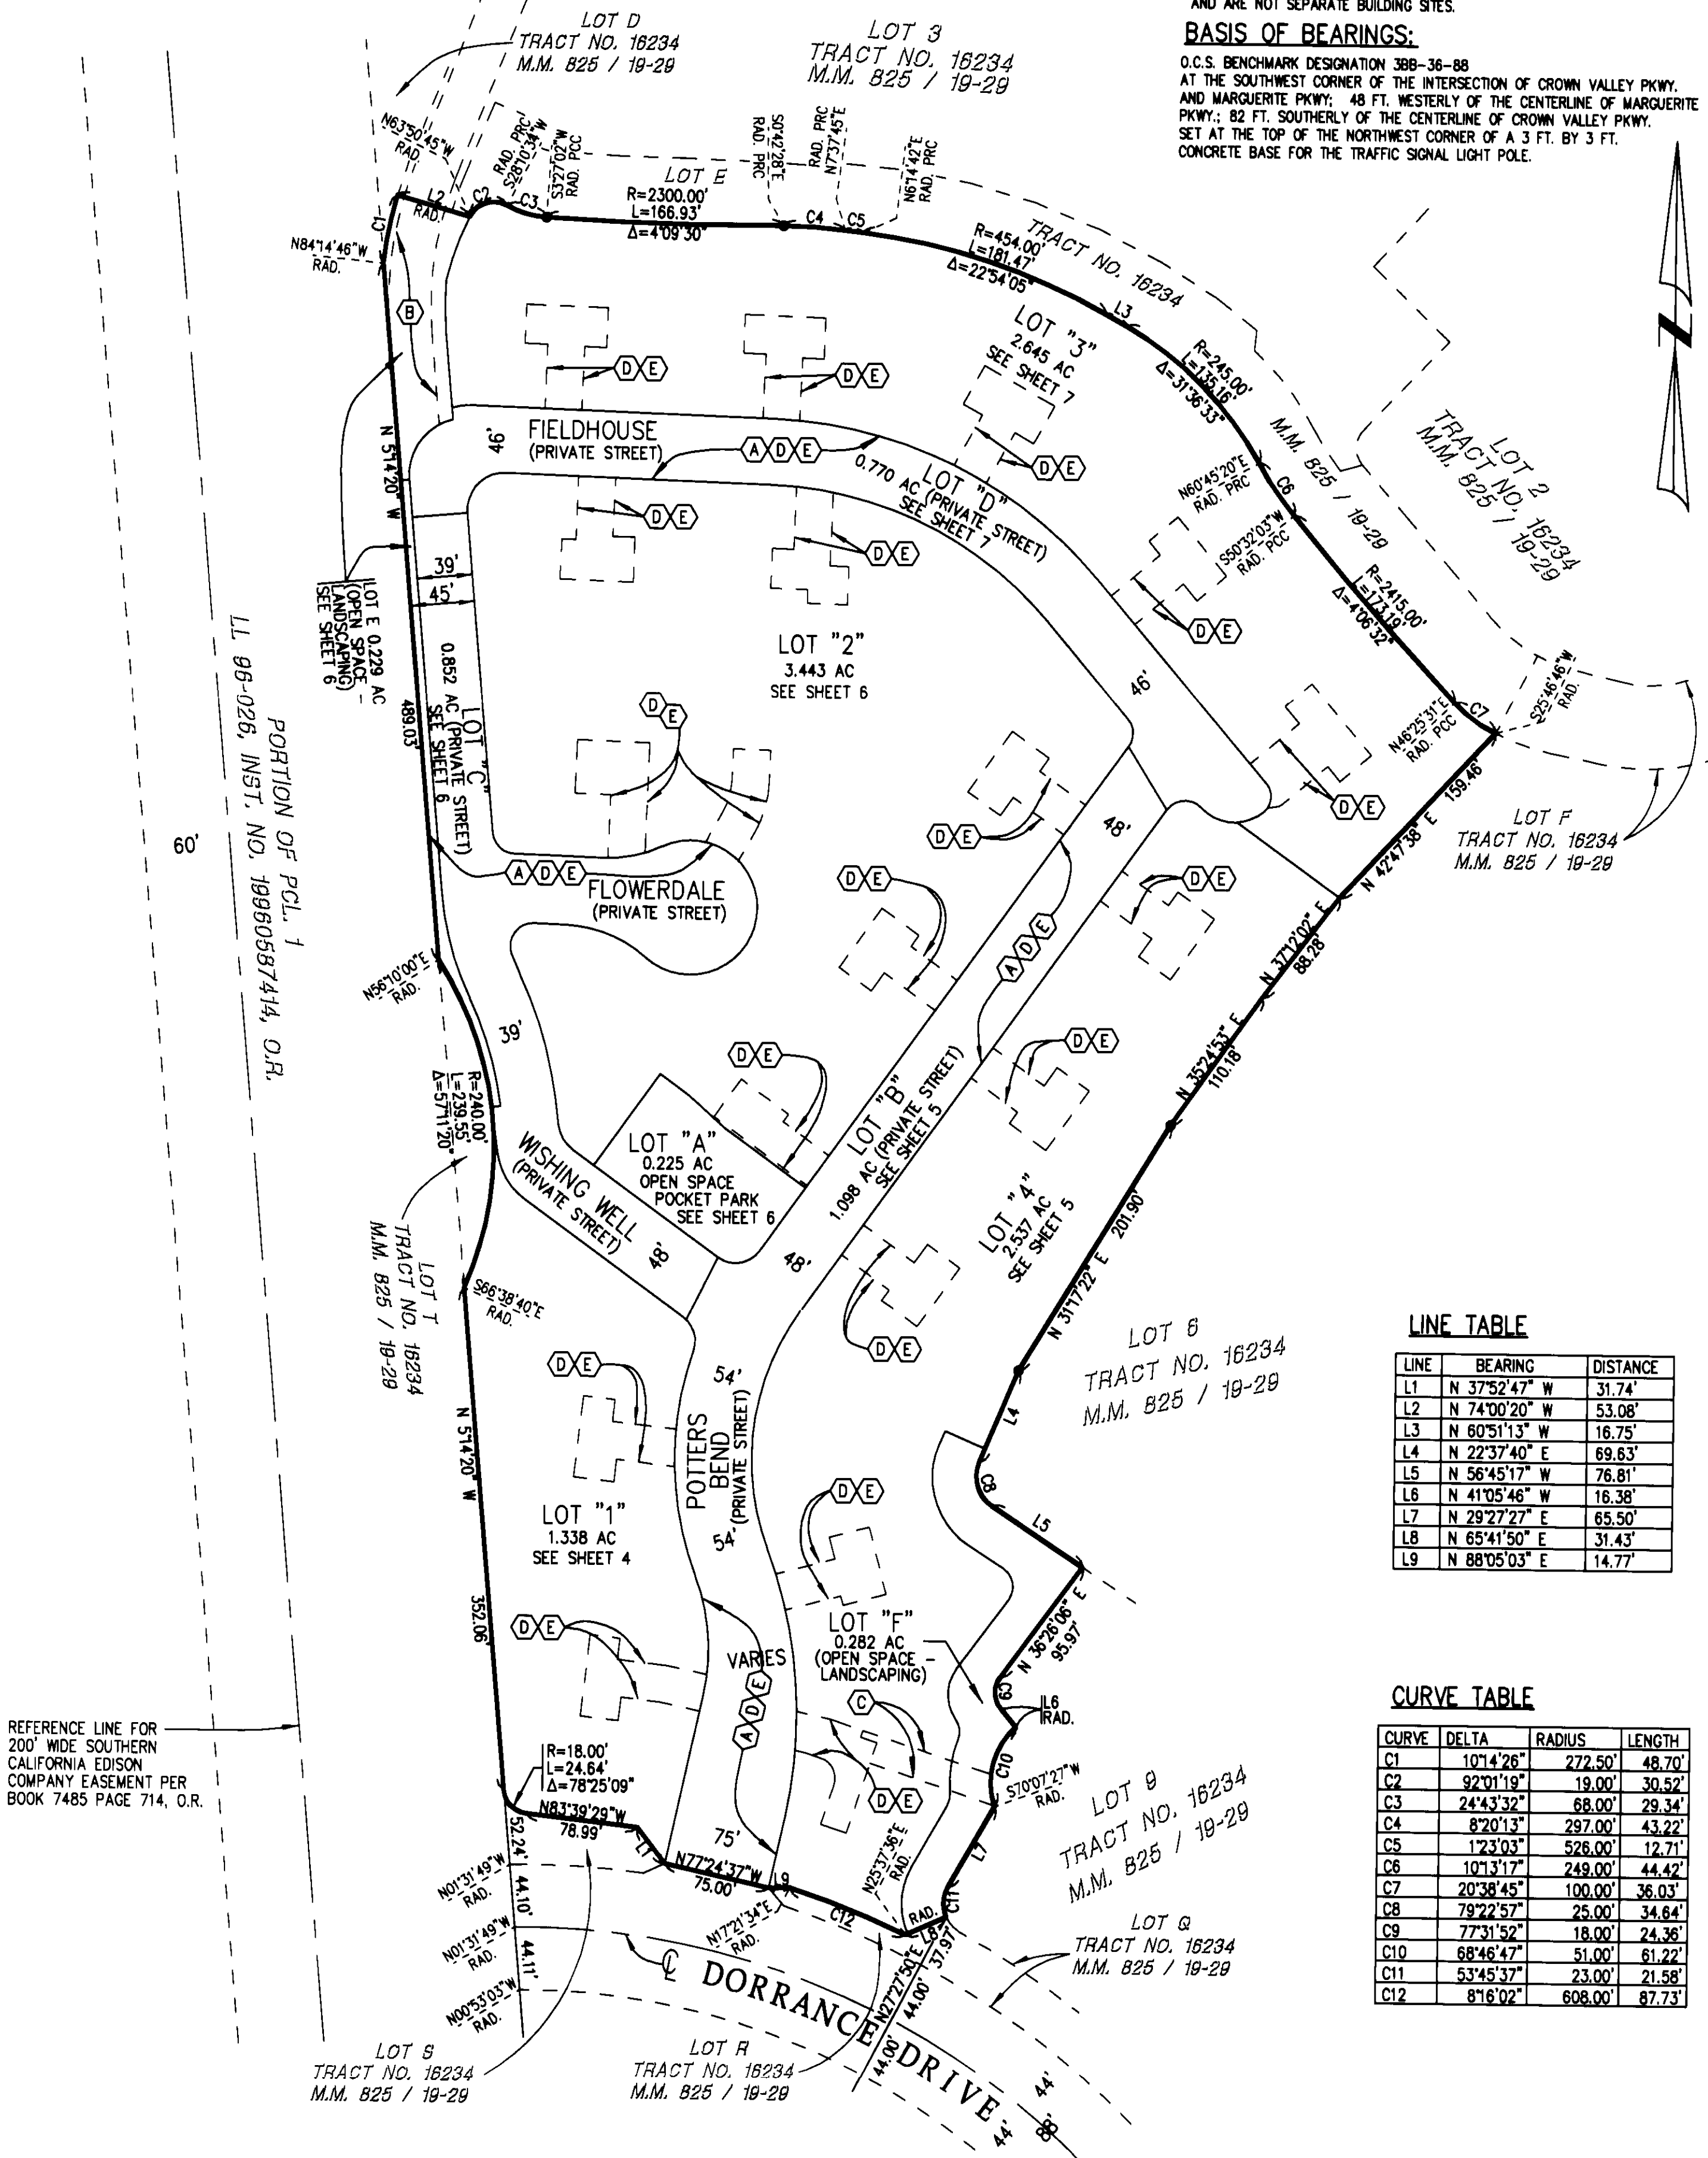

LINE TABLE

LINE	BEARING	DISTANCE
L1	N 37°52'47" W	31.74'
L2	N 74°00'20" W	53.08'
L3	N 60°51'13" W	16.75'
L4	N 22°37'40" E	69.63'
L5	N 56°45'17" W	76.81'
L6	N 41°05'46" W	16.38'
L7	N 29°27'27" E	65.50'
L8	N 65°41'50" E	31.43'
L9	N 88°05'03" E	14.77'

CURVE TABLE

CURVE	DELTA	RADIUS	LENGTH
C1	10°14'26"	272.50'	48.70'
C2	92°01'19"	19.00'	30.52'
C3	24°43'32"	68.00'	29.34'
C4	8°20'13"	297.00'	43.22'
C5	1°23'03"	526.00'	12.71'
C6	10°13'17"	249.00'	44.42'
C7	20°38'45"	100.00'	36.03'
C8	79°22'57"	25.00'	34.84'
C9	77°31'52"	18.00'	24.36'
C10	68°46'47"	51.00'	61.22'
C11	53°45'37"	23.00'	21.58'
C12	8°16'02"	608.00'	87.73'

REFERENCE LINE FOR
200' WIDE SOUTHERN
CALIFORNIA EDISON
COMPANY EASEMENT PER
BOOK 7485 PAGE 714, O.R.

SHEET 4 OF 7 SHEETS
13.419 ACRES
4 LOTS AND LOTS "A" THROUGH "F"

TRACT NO. 16239
IN THE UNINCORPORATED TERRITORY
OF THE COUNTY OF ORANGE, STATE OF CALIFORNIA


SCALE: 1" = 40'

WAGNER HALLADAY, INC.
ROBERT N. MIM MACK L.S. 5314 DATE OF SURVEY: JANUARY, 2002
FOR CONDOMINIUM PURPOSES

EASEMENT NOTES:

- (A) INDICATES AN EASEMENT TO THE COUNTY OF ORANGE FOR EMERGENCY AND PUBLIC SERVICE INGRESS AND EGRESS PURPOSES AS DEDICATED HEREON.
- (B) INDICATES A 30' WIDE EASEMENT TO SANTA MARGARITA WATER DISTRICT FOR WATER AND SEWER LINE PURPOSES AS DEDICATED HEREON.
- (C) INDICATES A 20' WIDE EASEMENT TO SANTA MARGARITA WATER DISTRICT FOR WATER LINE PURPOSES AS DEDICATED HEREON.
- (D) INDICATES AN EASEMENT TO SANTA MARGARITA WATER DISTRICT FOR WATER AND SEWER LINE PURPOSES AS DEDICATED HEREON.
- (E) INDICATES AN EASEMENT FOR PUBLIC UTILITY PURPOSES AS DEDICATED HEREON.

SEE SHEET 3 FOR
MONUMENT NOTES.

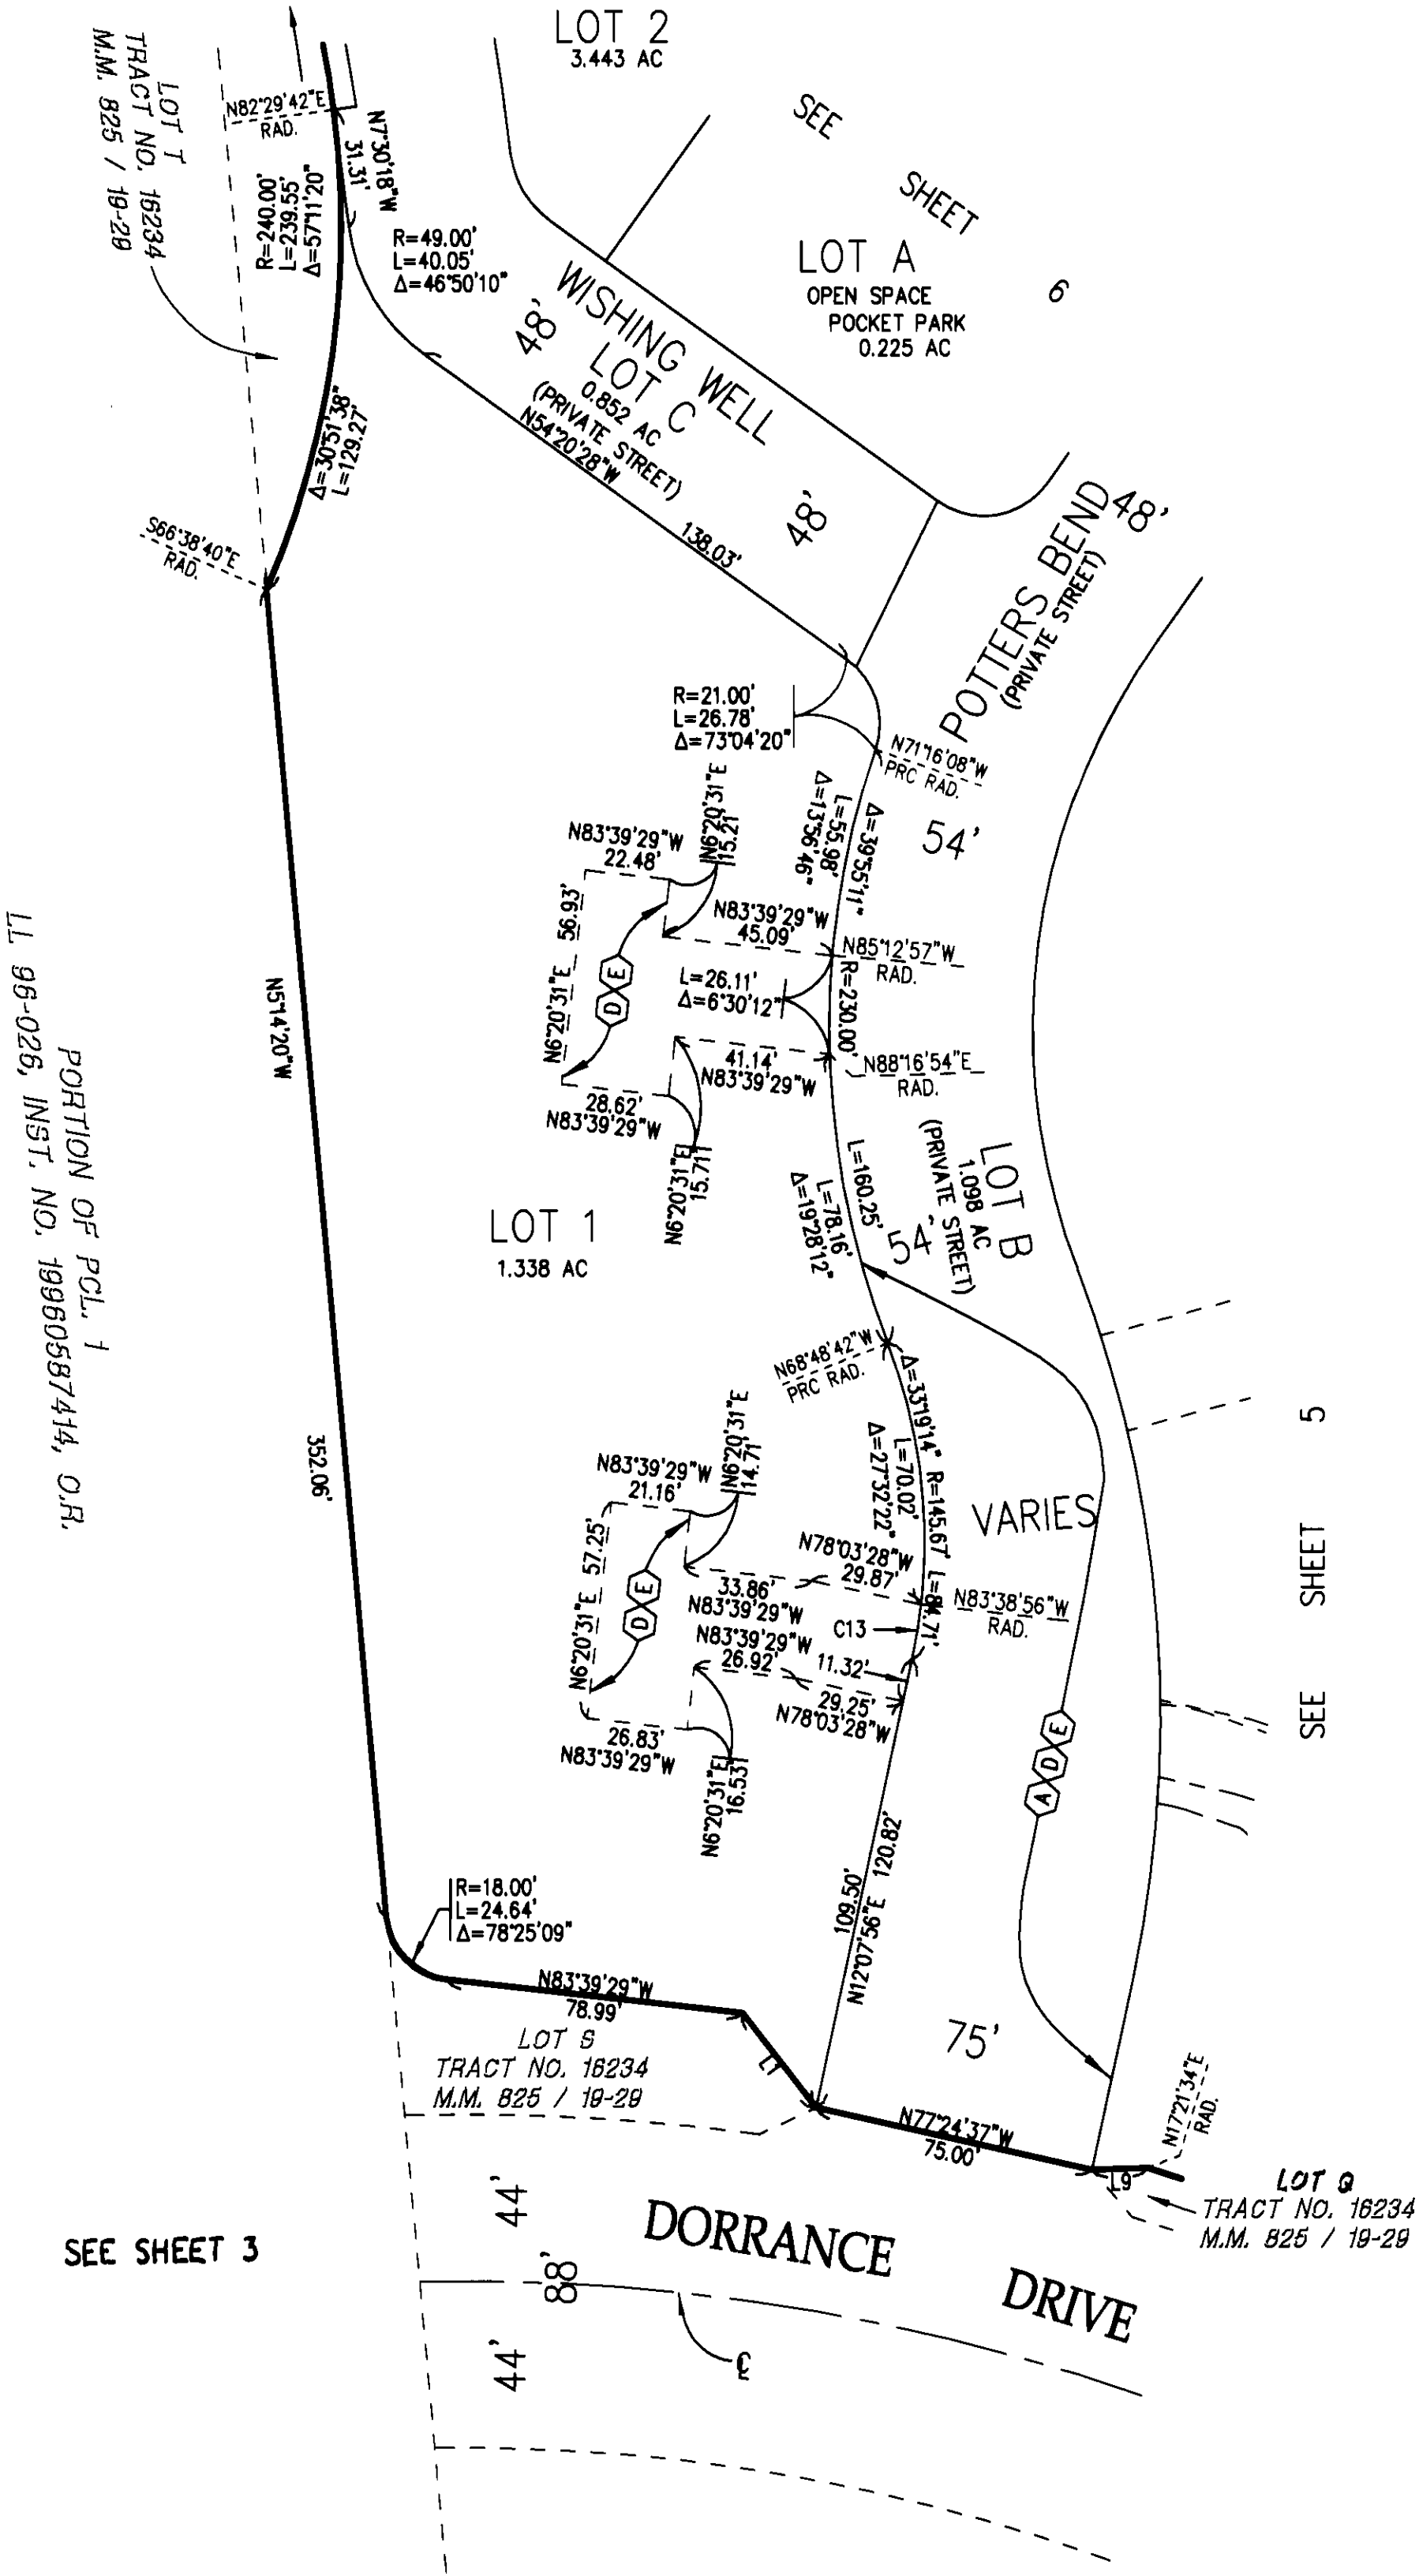

LINE TABLE

LINE	BEARING	DISTANCE
L1	N 37°52'47" W	31.74'
L9	N 88°05'03" E	14.77'

CURVE TABLE

CURVE	DELTA	RADIUS	LENGTH
C13	5°46'52"	145.67'	14.70'

SHEET 5 OF 7 SHEETS
13.419 ACRES
4 LOTS AND LOTS "A" THROUGH "F"

TRACT NO. 16239

IN THE UNINCORPORATED TERRITORY
OF THE COUNTY OF ORANGE, STATE OF CALIFORNIA


WAGNER HALLADAY, INC.
ROBERT N. MIM MACK L.S. 5314 DATE OF SURVEY: JANUARY, 2002
FOR CONDOMINIUM PURPOSES

SCALE: 1" = 40'

EASEMENT NOTES:

- (A) INDICATES AN EASEMENT TO THE COUNTY OF ORANGE FOR EMERGENCY AND PUBLIC SERVICE INGRESS AND EGRESS PURPOSES AS DEDICATED HEREON.
- (B) INDICATES A 30' WIDE EASEMENT TO SANTA MARGARITA WATER DISTRICT FOR WATER AND SEWER LINE PURPOSES AS DEDICATED HEREON.
- (C) INDICATES A 20' WIDE EASEMENT TO SANTA MARGARITA WATER DISTRICT FOR WATER LINE PURPOSES AS DEDICATED HEREON.
- (D) INDICATES AN EASEMENT TO SANTA MARGARITA WATER DISTRICT FOR WATER AND SEWER LINE PURPOSES AS DEDICATED HEREON.
- (E) INDICATES AN EASEMENT FOR PUBLIC UTILITY PURPOSES AS DEDICATED HEREON.

SEE SHEET 3 FOR
MONUMENT NOTES.

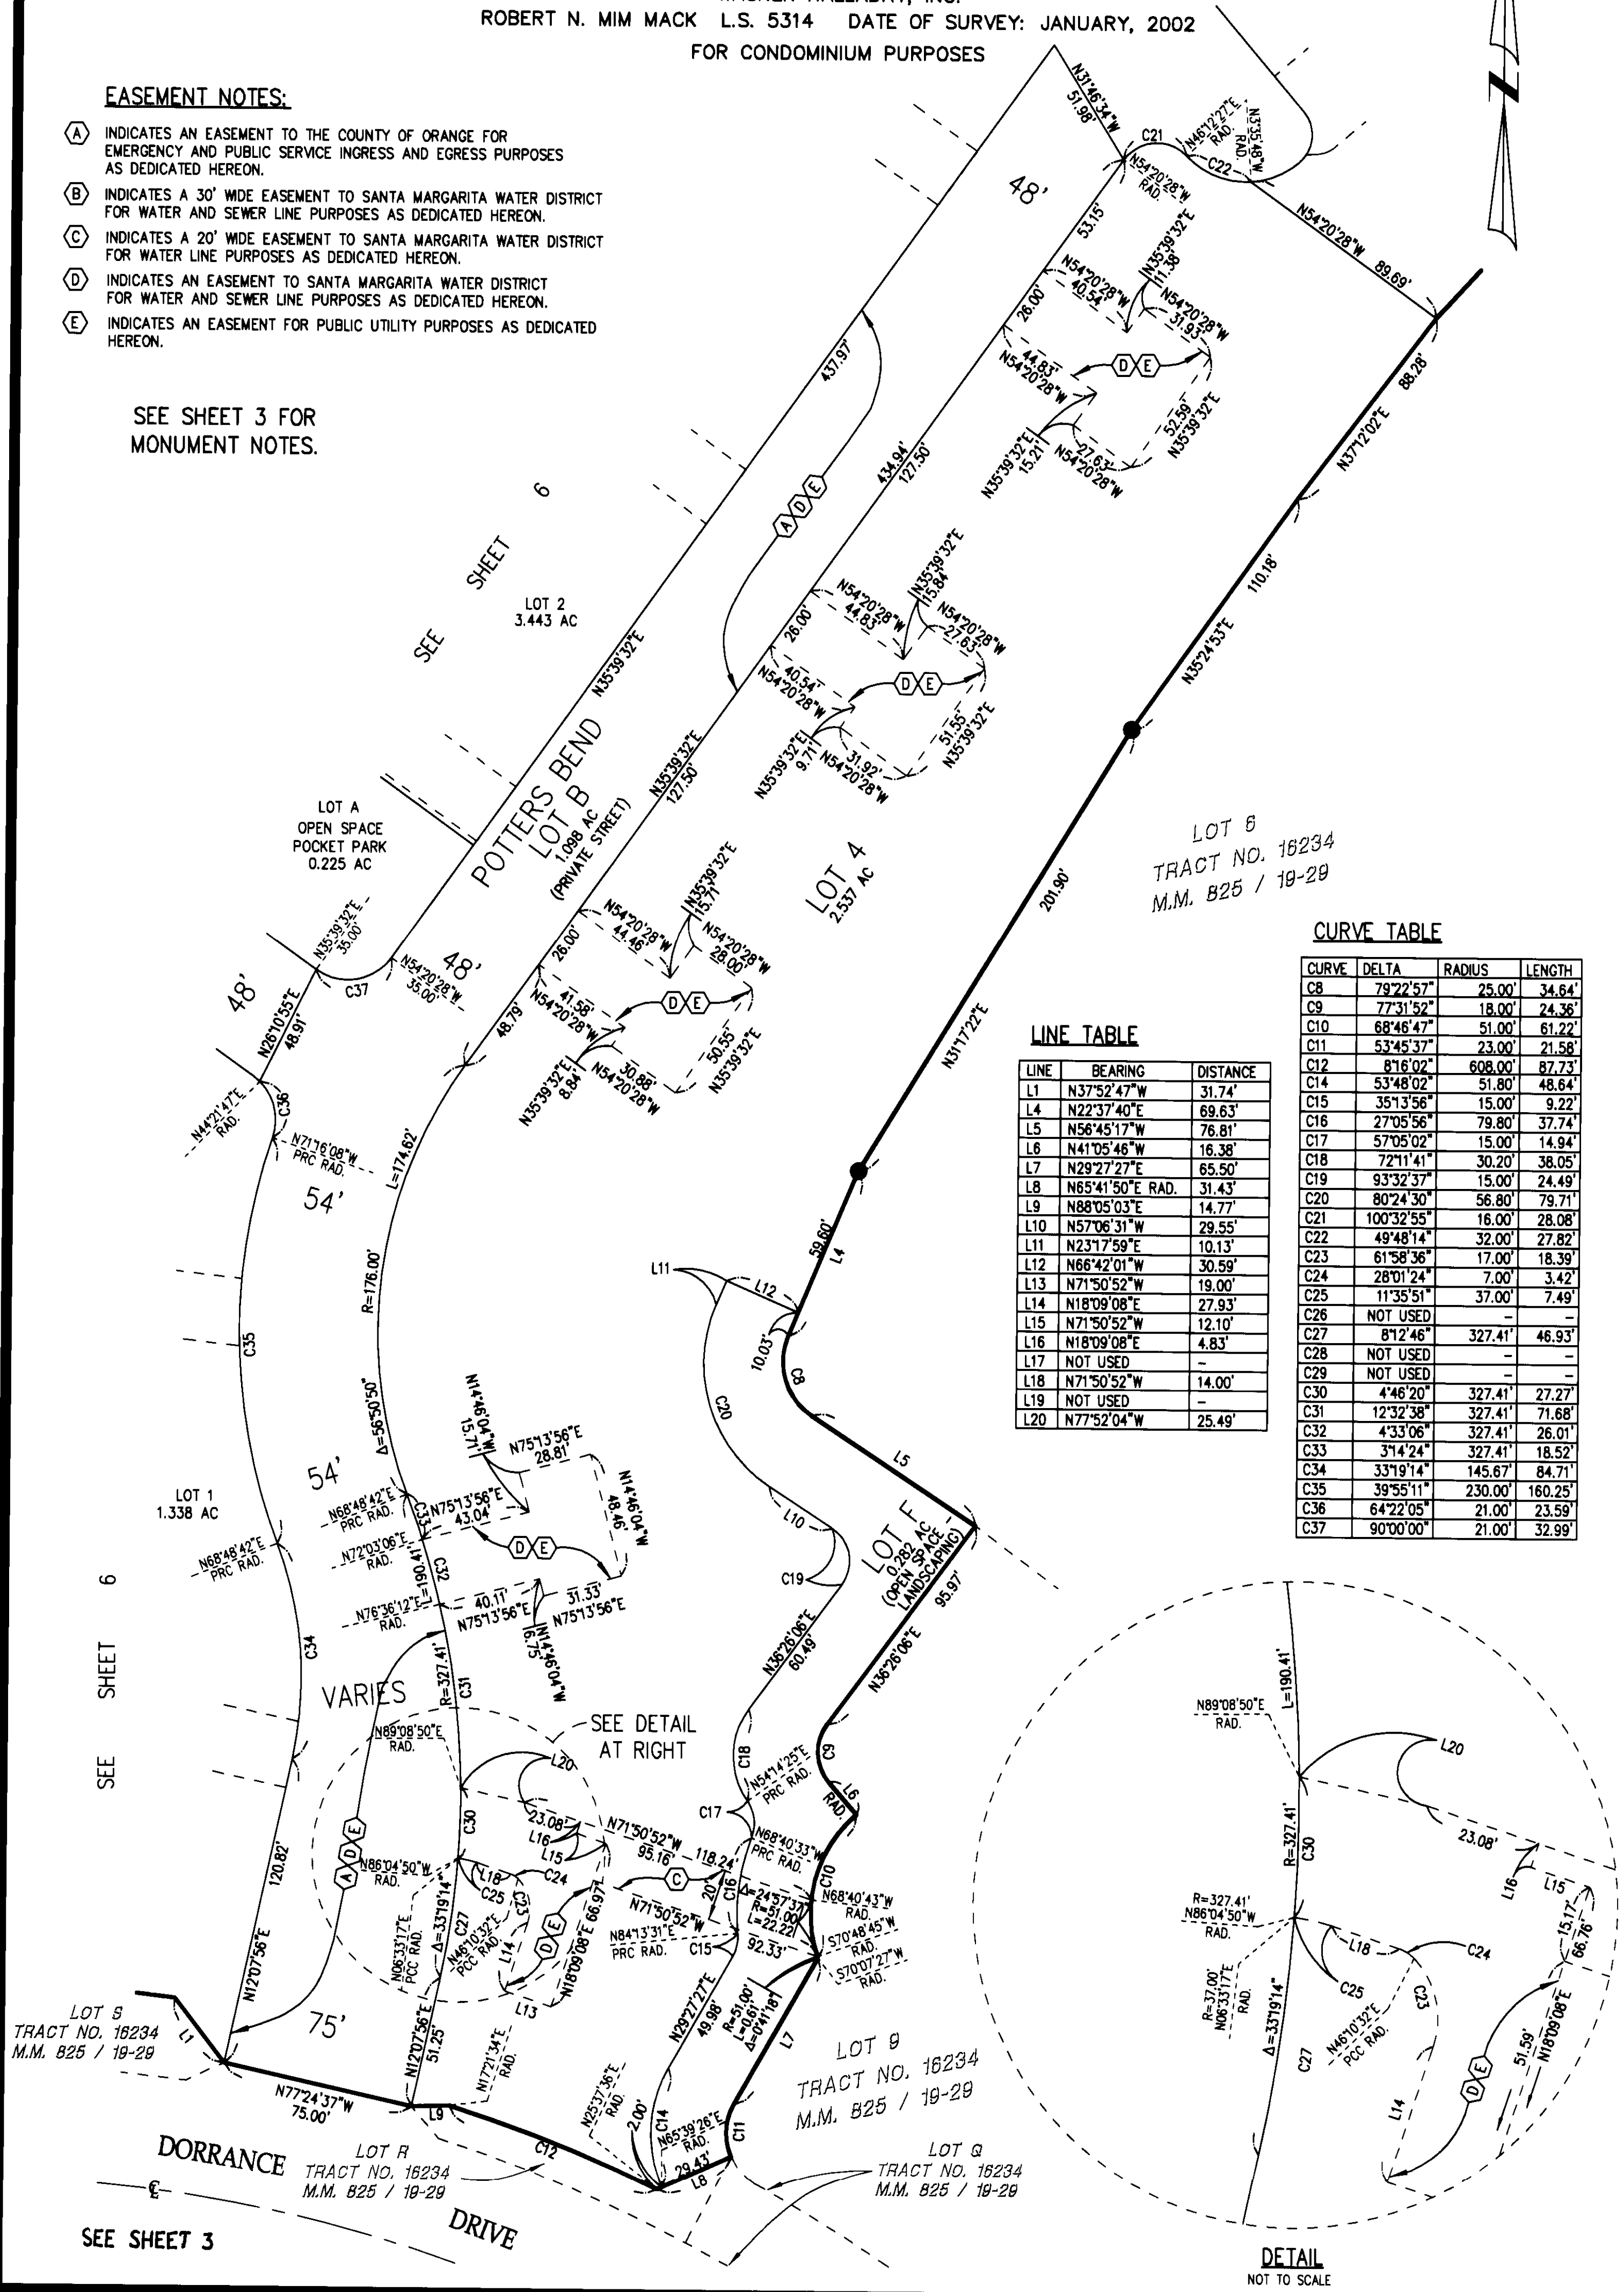

LINE TABLE

LINE	BEARING	DISTANCE
L1	N37°52'47\"W	31.74'
L4	N22°37'40\"E	69.63'
L5	N56°45'17\"W	76.81'
L6	N41°05'46\"W	16.38'
L7	N29°27'27\"E	65.50'
L8	N65°41'50\"E RAD.	31.43'
L9	N88°05'03\"E	14.77'
L10	N57°06'31\"W	29.55'
L11	N23°17'59\"E	10.13'
L12	N66°42'01\"W	30.59'
L13	N71°50'52\"W	19.00'
L14	N18°09'08\"E	27.93'
L15	N71°50'52\"W	12.10'
L16	N18°09'08\"E	4.83'
L17	NOT USED	-
L18	N71°50'52\"W	14.00'
L19	NOT USED	-
L20	N77°52'04\"W	25.49'

CURVE TABLE

CURVE	DELTA	RADIUS	LENGTH
C8	79°22'57\"	25.00'	34.64'
C9	77°31'52\"	18.00'	24.36'
C10	68°46'47\"	51.00'	61.22'
C11	53°45'37\"	23.00'	21.58'
C12	81°6'02\"	608.00'	87.73'
C14	53°48'02\"	51.80'	48.64'
C15	35°13'56\"	15.00'	9.22'
C16	27°05'56\"	79.80'	37.74'
C17	57°05'02\"	15.00'	14.94'
C18	72°11'41\"	30.20'	38.05'
C19	93°32'37\"	15.00'	24.49'
C20	80°24'30\"	56.80'	79.71'
C21	100°32'55\"	16.00'	28.08'
C22	49°48'14\"	32.00'	27.82'
C23	61°58'36\"	17.00'	18.39'
C24	28°01'24\"	7.00'	3.42'
C25	11°35'51\"	37.00'	7.49'
C26	NOT USED	-	-
C27	81°2'46\"	327.41'	46.93'
C28	NOT USED	-	-
C29	NOT USED	-	-
C30	4°46'20\"	327.41'	27.27'
C31	12°32'38\"	327.41'	71.68'
C32	4°33'06\"	327.41'	26.01'
C33	3°14'24\"	327.41'	18.52'
C34	33°19'14\"	145.67'	84.71'
C35	39°55'11\"	230.00'	160.25'
C36	64°22'05\"	21.00'	23.59'
C37	90°00'00\"	21.00'	32.99'

DETAIL
NOT TO SCALE

SHEET 6 OF 7 SHEETS
13.419 ACRES
4 LOTS AND LOTS "A" THROUGH "F"

TRACT NO. 16239

IN THE UNINCORPORATED TERRITORY
OF THE COUNTY OF ORANGE, STATE OF CALIFORNIA

SCALE: 1" = 40'

WAGNER HALLADAY, INC.
ROBERT N. MIM MACK L.S. 5314 DATE OF SURVEY: JANUARY, 2002
FOR CONDOMINIUM PURPOSES

CURVE TABLE

CURVE	DELTA	RADIUS	LENGTH
C38	90°00'00"	21.00'	32.99'
C39	76°00'00"	16.00'	21.22'
C40	5°36'54"	267.00'	26.17'
C41	3°32'18"	267.00'	16.49'
C42	97°07'13"	26.00'	44.07'
C43	82°52'47"	16.00'	23.14'
C44	26°57'45"	91.00'	42.82'
C45	39°09'44"	91.00'	62.20'
C46	112°31'28"	16.00'	31.42'
C47	5°07'26"	176.00'	15.74'
C48	46°50'10"	26.00'	21.25'
C49	8°42'15"	21.00'	3.19'
C50	46°50'10"	49.00'	40.05'
C51	18°15'42"	246.00'	78.41'
C52	20°31'40"	215.00'	77.03'
C53	81°22'23"	40.00'	56.81'
C54	9°12'36"	227.50'	36.57'
C55	12°28'29"	217.00'	47.25'
C56	10°14'26"	272.50'	48.70'
C57	1°56'15"	91.00'	3.08'
C58	16°41'48"	91.00'	26.52'
C59	8°19'42"	91.00'	13.23'
C60	37°31'28"	47.00'	30.78'
C61	27°11'40"	47.00'	22.31'
C62	27°11'40"	73.00'	34.65'
C63	32°41'23"	47.00'	26.82'

EASEMENT NOTES:

- (A) INDICATES AN EASEMENT TO THE COUNTY OF ORANGE FOR EMERGENCY AND PUBLIC SERVICE INGRESS AND EGRESS PURPOSES AS DEDICATED HEREON.
- (B) INDICATES A 30' WIDE EASEMENT TO SANTA MARGARITA WATER DISTRICT FOR WATER AND SEWER LINE PURPOSES AS DEDICATED HEREON.
- (C) INDICATES A 20' WIDE EASEMENT TO SANTA MARGARITA WATER DISTRICT FOR WATER LINE PURPOSES AS DEDICATED HEREON.
- (D) INDICATES AN EASEMENT TO SANTA MARGARITA WATER DISTRICT FOR WATER AND SEWER LINE PURPOSES AS DEDICATED HEREON.
- (E) INDICATES AN EASEMENT FOR PUBLIC UTILITY PURPOSES AS DEDICATED HEREON.

SEE SHEET 3 FOR
MONUMENT NOTES.

SEE SHEET 7

LOT 3
2.645 AC

LOT 2
3.443 AC

FIELDHOUSE
LOT D
0.770 AC
(PRIVATE STREET)
R=267.00'

FLOWERDALE
(PRIVATE STREET)

WISHING WELL
(PRIVATE STREET)

POTTERS BEND
LOT B
1.088 AC
(PRIVATE STREET)

LOT A
OPEN SPACE
POCKET PARK
0.225 AC

LOT 4
2.337 AC

SEE SHEET 4

SEE SHEET 5

SHEET 7 OF 7 SHEETS
13.419 ACRES
4 LOTS AND LOTS "A" THROUGH "F"

TRACT NO. 16239
IN THE UNINCORPORATED TERRITORY
OF THE COUNTY OF ORANGE, STATE OF CALIFORNIA



SCALE: 1" = 40'

WAGNER HALLADAY, INC.
ROBERT N. MIM MACK L.S. 5314 DATE OF SURVEY: JANUARY, 2002
FOR CONDOMINIUM PURPOSES

EASEMENT NOTES:

- (A) INDICATES AN EASEMENT TO THE COUNTY OF ORANGE FOR EMERGENCY AND PUBLIC SERVICE INGRESS AND EGRESS PURPOSES AS DEDICATED HEREON.
- (B) INDICATES A 30' WIDE EASEMENT TO SANTA MARGARITA WATER DISTRICT FOR WATER AND SEWER LINE PURPOSES AS DEDICATED HEREON.
- (C) INDICATES A 20' WIDE EASEMENT TO SANTA MARGARITA WATER DISTRICT FOR WATER LINE PURPOSES AS DEDICATED HEREON.
- (D) INDICATES AN EASEMENT TO SANTA MARGARITA WATER DISTRICT FOR WATER AND SEWER LINE PURPOSES AS DEDICATED HEREON.
- (E) INDICATES AN EASEMENT FOR PUBLIC UTILITY PURPOSES AS DEDICATED HEREON.
- (F) INDICATES PRIVATE EASEMENT FOR STORM DRAIN PURPOSES RESERVED HEREON.

SEE SHEET 3 FOR
MONUMENT NOTES.

LOT 3
TRACT NO. 16234
M.M. B25 / 19-29

LOT 6
TRACT NO. 16234
M.M. B25 / 19-29

LOT 4
2.537 AC

LOT B
1.098 AC
(PRIVATE STREET)

LOT 2
3.443 AC

LOT D
0.770 AC
(PRIVATE STREET)

LOT E
(OPEN SPACE -
LANDSCAPING)
0.229 AC

LOT D
TRACT NO. 16234
M.M. B25 / 19-29

PORTION OF PCL. 1
LL 96-026, INST. NO. 19960587414, O.R.

LINE TABLE

LINE	BEARING	DISTANCE
L3	N 60°51'13" W	16.75'

CURVE TABLE

CURVE	DELTA	RADIUS	LENGTH
C2	92°01'19"	19.00'	30.52'
C3	24°43'32"	68.00'	29.34'
C4	8°20'13"	297.00'	43.22'
C5	1°23'03"	526.00'	12.71'
C6	10°13'17"	249.00'	44.42'
C7	20°38'45"	100.00'	36.03'
C21	100°32'54"	16.00'	28.08'
C22	49°48'14"	32.00'	27.82'
C39	76°00'00"	16.00'	21.22'
C42	97°07'13"	26.00'	44.07'
C53	81°22'23"	40.00'	56.81'
C54	9°12'36"	227.50'	36.57'
C55	12°28'29"	217.00'	47.25'
C64	14°09'13"	49.00'	12.10'
C65	89°43'22"	14.00'	21.92'
C66	86°49'32"	32.00'	48.49'
C67	3°02'27"	313.00'	16.61'
C68	4°45'42"	313.00'	26.01'
C69	73°22'56"	14.00'	17.93'
C70	36°52'12"	10.33'	6.85'
C71	16°20'26"	14.00'	3.99'
C72	37°01'18"	32.00'	20.68'
C73	2°19'15"	249.00'	10.08'