

SHEET 1 OF 4 SHEETS

8.365 ACRES
88 NUMBERED LOTS AND
LETTERED LOTS "A" THROUGH "C"
DATE OF SURVEY: NOVEMBER 2001
(ALL OF TENTATIVE TRACT No. 16240)

TRACT NO. 16240

IN THE UNINCORPORATED TERRITORY OF THE COUNTY OF ORANGE, STATE OF CALIFORNIA.

BEING A SUBDIVISION OF LOT 6 OF TRACT No. 16234, AS SHOWN ON THE MAP THEREOF
FILED IN BOOK 825 AT PAGES 19 THROUGH 29, INCLUSIVE, OF MISCELLANEOUS MAPS,
IN THE OFFICE OF THE COUNTY RECORDER OF ORANGE COUNTY, CALIFORNIA.

BLOCK MODULE
5157 28

NOVEMBER 2001
JERRY L. USELTON, L.S. 5347 FUSCOE ENGINEERING, INC.

ACCEPTED AND FILED AT THE REQUEST OF

FIRST AMERICAN TITLE INS. CO.

DATE JUNE 28, 2002
TIME 11:28 AM FEE \$ 13.00
INSTRUMENT # 2002054675
BOOK 834 PAGE 22-25 A/A

GARY L. GRANVILLE
COUNTY CLERK-RECORDER

BY: [Signature]
DEPUTY

OWNERSHIP CERTIFICATE:

WE THE UNDERSIGNED, BEING ALL PARTIES HAVING ANY RECORD TITLE INTEREST IN THE LAND COVERED BY THIS MAP, DO HEREBY CONSENT TO THE PREPARATION AND RECORDATION OF SAID MAP, AS SHOWN WITHIN THE DISTINCTIVE BORDER LINE.

WE HEREBY DEDICATE TO THE PUBLIC FOR STREET PURPOSES: SYLVANOAK WAY; MARSTON LANE; WHIDBEY DRIVE; BAINBRIDGE AVENUE; AND ROYCROFT COURT.

WE ALSO HEREBY DEDICATE TO THE COUNTY OF ORANGE:

1. THE EASEMENT FOR STORM DRAIN PURPOSES AS SHOWN ON SAID MAP

MBK HOMES LTD., A CALIFORNIA LIMITED PARTNERSHIP, OWNER
BY: MBK RESIDENTIAL, INC., A CALIFORNIA CORPORATION
GENERAL PARTNER

BY: [Signature]
NAME Stephen Markowitz
TITLE President

BY: [Signature]
NAME Shinji Higuchi
TITLE Sen. V.P.

DMB LADERA, LLC, A DELAWARE LIMITED LIABILITY COMPANY,
BENEFICIARY UNDER DEED OF TRUST RECORDED AS INSTRUMENT No. 20020051783,
OF OFFICIAL RECORDS OF ORANGE COUNTY, CALIFORNIA
BY: RANCHO MISSION VIEJO, LLC, A DELAWARE LIMITED LIABILITY COMPANY, AS AGENT AND MANAGER

BY: [Signature]
NAME Donald T. Spaulin
TITLE Dir. of Community Dev.

BY: [Signature]
NAME Stephen C. Schrank
TITLE Executive Vice President

BANK OF AMERICA, N.A. A NATIONAL BANKING ASSOCIATION,
BENEFICIARY UNDER A DEED OF TRUST RECORDED AS INSTRUMENT No. 200251782,
OF OFFICIAL RECORDS OF ORANGE COUNTY, CALIFORNIA

BY: [Signature]
NAME Parash Patel
TITLE VP

STATE OF CALIFORNIA }
COUNTY OF ORANGE } SS

ON THIS 17th DAY OF May, 2002, BEFORE ME, Michelle M. Farina, Notary Public,
PERSONALLY APPEARED Stephen Markowitz & Shinji Higuchi
PERSONALLY KNOWN TO ME (OR PROVED TO ME ON THE BASIS OF SATISFACTORY EVIDENCE) TO BE THE
PERSON(S) WHOSE NAME(S) IS/ARE SUBSCRIBED TO THE WITHIN INSTRUMENT AND ACKNOWLEDGED TO ME THAT
HE/SHE/THEY EXECUTED THE SAME IN HIS/HER/THEIR AUTHORIZED CAPACITY(IES), AND THAT BY
HIS/HER/THEIR SIGNATURE(S) ON THE INSTRUMENT THE PERSON(S), OR THE ENTITY UPON BEHALF OF WHICH
THE PERSON(S) ACTED, EXECUTED THE INSTRUMENT.

MY PRINCIPAL PLACE OF BUSINESS
IS IN Orange COUNTY.

MY COMMISSION EXPIRES: 5-22-03

WITNESS MY HAND:

[Signature]
(SIGNATURE)
NOTARY PUBLIC IN AND FOR SAID STATE
Michelle M. Farina
(PRINT NAME)

STATE OF CALIFORNIA }
COUNTY OF ORANGE } SS

ON THIS 23rd DAY OF April, 2002, BEFORE ME, Carylan Offenhauer
PERSONALLY APPEARED Parash Patel
PERSONALLY KNOWN TO ME (OR PROVED TO ME ON THE BASIS OF SATISFACTORY EVIDENCE) TO BE THE
PERSON(S) WHOSE NAME(S) IS/ARE SUBSCRIBED TO THE WITHIN INSTRUMENT AND ACKNOWLEDGED TO ME THAT
HE/SHE/THEY EXECUTED THE SAME IN HIS/HER/THEIR AUTHORIZED CAPACITY(IES), AND THAT BY
HIS/HER/THEIR SIGNATURE(S) ON THE INSTRUMENT THE PERSON(S), OR THE ENTITY UPON BEHALF OF WHICH
THE PERSON(S) ACTED, EXECUTED THE INSTRUMENT.

MY PRINCIPAL PLACE OF BUSINESS
IS IN Orange COUNTY.

MY COMMISSION EXPIRES: 5-13-05

WITNESS MY HAND:

[Signature]
(SIGNATURE)
NOTARY PUBLIC IN AND FOR SAID STATE
Carylan Offenhauer
(PRINT NAME)

STATE OF CALIFORNIA }
COUNTY OF ORANGE } SS

ON THIS 14th DAY OF May, 2002, BEFORE ME, Tina T. Baker, Notary Public
PERSONALLY APPEARED Donald T. Spaulin and Stephen C. Schrank
PERSONALLY KNOWN TO ME (OR PROVED TO ME ON THE BASIS OF SATISFACTORY EVIDENCE) TO BE THE
PERSON(S) WHOSE NAME(S) IS/ARE SUBSCRIBED TO THE WITHIN INSTRUMENT AND ACKNOWLEDGED TO ME THAT
HE/SHE/THEY EXECUTED THE SAME IN HIS/HER/THEIR AUTHORIZED CAPACITY(IES), AND THAT BY
HIS/HER/THEIR SIGNATURE(S) ON THE INSTRUMENT THE PERSON(S), OR THE ENTITY UPON BEHALF OF WHICH
THE PERSON(S) ACTED, EXECUTED THE INSTRUMENT.

MY PRINCIPAL PLACE OF BUSINESS
IS IN Orange COUNTY.

MY COMMISSION EXPIRES: 8/29/04

WITNESS MY HAND:

[Signature]
(SIGNATURE)
NOTARY PUBLIC IN AND FOR SAID STATE
Tina T. Baker
(PRINT NAME)

SIGNATURE OMISSION NOTES:


IN ACCORDANCE WITH THE PROVISIONS OF SECTION 66436(a)(3)(A) OF THE
SUBDIVISION MAP ACT, THE FOLLOWING SIGNATURES HAVE BEEN OMITTED:

- 1.) LADERA DEVELOPMENT COMPANY, L.L.C. HOLDER OF OIL, GAS, MINERAL, AND
WATER RIGHTS RECORDED DECEMBER 10, 1996 AS INSTRUMENT NO.
19960624029 OF OFFICIAL RECORDS.

SURVEYOR'S STATEMENT:

I HEREBY STATE THAT THIS MAP CONSISTING OF 4 SHEETS, CORRECTLY
REPRESENTS A TRUE AND COMPLETE SURVEY AS SHOWN MADE IN NOVEMBER 2001;
WAS MADE BY ME OR UNDER MY DIRECTION; THAT THE MONUMENTS ARE OF THE
CHARACTER AND OCCUPY (OR WILL OCCUPY) THE POSITIONS INDICATED BY SAID
MAP; AND THAT SAID MONUMENTS ARE (OR WILL BE) SUFFICIENT TO ENABLE THE
SURVEY TO BE RETRACED.

[Signature]
JERRY L. USELTON, L.S. 5347
LICENSE EXPIRES 12/31/03

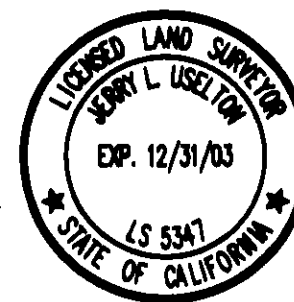


COUNTY SURVEYOR'S STATEMENT:

I HEREBY STATE THAT I HAVE EXAMINED THIS MAP AND FOUND IT TO BE
SUBSTANTIALLY IN CONFORMANCE WITH THE TENTATIVE MAP, AS FILED WITH,
AMENDED AND APPROVED BY THE ORANGE COUNTY SUBDIVISION COMMITTEE;
THAT ALL PROVISIONS OF THE SUBDIVISION MAP ACT AND COUNTY SUBDIVISION
REGULATIONS HAVE BEEN COMPLIED WITH AND I AM SATISFIED SAID MAP IS
TECHNICALLY CORRECT.

DATED THIS 13TH DAY OF JUNE, 2002.

[Signature]
JOHN CANAS, COUNTY SURVEYOR
U.S. 4408, EXPIRATION DATE: 9/30/05

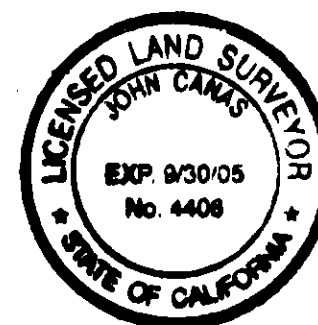

COUNTY TREASURER-TAX COLLECTOR'S CERTIFICATE:

STATE OF CALIFORNIA }
COUNTY OF ORANGE } SS

I HEREBY CERTIFY THAT ACCORDING TO THE RECORDS OF MY OFFICE THERE ARE
NO LIENS AGAINST THE LAND COVERED BY THIS MAP OR ANY PART THEREOF FOR
UNPAID STATE, COUNTY, MUNICIPAL OR LOCAL TAXES OR SPECIAL ASSESSMENTS
COLLECTED AS TAXES, EXCEPT TAXES OR SPECIAL ASSESSMENTS COLLECTED AS
TAXES NOT YET PAYABLE.

AND DO CERTIFY TO THE RECORDER OF ORANGE COUNTY THAT THE PROVISIONS
OF THE SUBDIVISION MAP ACT HAVE BEEN COMPLIED WITH REGARDING DEPOSITS
TO SECURE PAYMENT OF TAXES OR SPECIAL ASSESSMENTS COLLECTED AS TAXES
ON THE LAND COVERED BY THIS MAP

DATED THIS 5th DAY OF June, 2002

JOHN M. W. MOORLACH
COUNTY TREASURER-TAX COLLECTOR

[Signature]
DEPUTY TREASURER-TAX COLLECTOR

CLERK OF THE BOARD OF SUPERVISOR'S CERTIFICATE:

STATE OF CALIFORNIA }
COUNTY OF ORANGE } SS


I HEREBY CERTIFY THAT THIS MAP WAS PRESENTED FOR APPROVAL TO THE
BOARD OF SUPERVISORS OF ORANGE COUNTY AT A REGULAR MEETING
THEREOF HELD ON THE 25 DAY OF JUNE, 2002,
AND THAT THEREUPON SAID BOARD DID, BY AN ORDER DULY PASSED AND ENTERED,
APPROVE SAID MAP AND DID ACCEPT ON BEHALF OF THE PUBLIC, SUBJECT TO
IMPROVEMENTS THE DEDICATION FOR STREET PURPOSES OF: SYLVANOAK WAY;
MARSTON LANE; WHIDBEY DRIVE; BAINBRIDGE AVENUE; AND ROYCROFT COURT.

AND DID ALSO ACCEPT ON BEHALF OF THE COUNTY OF ORANGE THE EASEMENT FOR
STORM DRAIN PURPOSES AS DEDICATED.

AND DID ALSO APPROVE SAID MAP PURSUANT TO THE PROVISIONS OF SECTION
66436(a)(3)(A) OF THE SUBDIVISION MAP ACT

DATED THIS 25 DAY OF June, 2002.

[Signature]
DARLENE J. BLOOM
CLERK OF THE BOARD OF SUPERVISORS
OF ORANGE COUNTY, CALIFORNIA

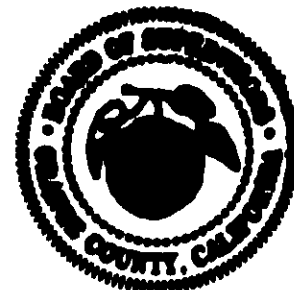

SHEET 2 OF 4 SHEETS
9.365 ACRES
69 NUMBERED LOTS AND
LETTERED LOTS "A" THROUGH "C"
DATE OF SURVEY: NOVEMBER 2001
(ALL OF TENTATIVE TRACT No. 16240)

TRACT NO. 16240

IN THE UNINCORPORATED TERRITORY OF THE COUNTY OF ORANGE, STATE OF CALIFORNIA.
NOVEMBER 2001
JERRY L. USELTON, L.S. 5347 FUSCOE ENGINEERING, INC.

MONUMENT NOTES:

- ▲ INDICATES LOCATION OF OCS GPS CONTROL POINT AS NOTED.
- INDICATES LOCATION OF 2" I.P. TAGGED "P.L.S. 5557" OR SPIKE AND WASHER STAMPED "P.L.S. 5557" OR LEAD TACK AND TAG "P.L.S. 5557" TO BE SET WITHIN 90 DAYS AFTER ACCEPTANCE OF IMPROVEMENTS PER TRACT 16234, M.M. 825/19-29
- INDICATES 1" I.P. TAGGED "L.S. 5557" OR SPIKE AND WASHER STAMPED "L.S. 5557" OR LEAD AND TAG "L.S. 5557" TO BE SET PER TRACT 16234, M.M. 825/19-29
- 2" I.P. TAGGED "L.S. 5347" OR SPIKE AND WASHER STAMPED "L.S. 5347" OR LEAD AND TAG "L.S. 5347" OR NAIL AND TAG "L.S. 5347" TO BE SET AT LOT CORNERS (UNLESS OTHERWISE NOTED) WITHIN 90 DAYS AFTER ACCEPTANCE OF IMPROVEMENTS.
- 1" I.P. TAGGED "L.S. 5347" OR SPIKE AND WASHER STAMPED "L.S. 5347" OR LEAD AND TAG "L.S. 5347" OR NAIL AND TAG "L.S. 5347" TO BE SET AT LOT CORNERS (UNLESS OTHERWISE NOTED) WITHIN 90 DAYS AFTER ACCEPTANCE OF IMPROVEMENTS.
- NO MONUMENTATION WILL BE SET AT BC's, EC's, PCC's, OR PRC's OF DEDICATED PUBLIC STREET SIDE LINES NOT MARKING LOT SIDELINES, UNLESS OTHERWISE NOTED.
- SPIKE AND WASHER STAMPED "L.S. 5347" OR LEAD AND TAG "L.S. 5347" TO BE SET AT DEDICATED PUBLIC STREET CENTERLINE POINTS OF CONTROL (UNLESS OTHERWISE NOTED) WITHIN 90 DAYS AFTER ACCEPTANCE OF IMPROVEMENTS.

- 1 INDICATES LOCATION OF 2" I.P. TAGGED "L.S. 5347" TO BE SET PRIOR TO RECORDATION.

SURVEYOR'S NOTES:

ALL LETTERED LOTS SHOWN HEREON ARE NOT SEPARATE BUILDING SITES. LOTS "A" AND "B" ARE FOR LANDSCAPE PURPOSES AND ARE TO BE CONVEYED TO THE APPROPRIATE HOMEOWNERS ASSOCIATION. LOT "C" IS FOR PRIVATE PARK PURPOSES AND IS TO BE CONVEYED TO THE APPROPRIATE HOMEOWNERS ASSOCIATION.

NOTE:

ALL COMMERCIAL STRUCTURES OVER 6,000 SQUARE FEET; ALL MULTIFAMILY RESIDENTIAL STRUCTURES; ALL DETACHED, SINGLE-FAMILY STRUCTURES EXCEEDING 5,500 SQUARE FEET, AND, ALL STRUCTURES EXCEEDING FIRE AUTHORITY ACCESS REQUIREMENTS SHALL BE PROTECTED BY AN AUTOMATIC SPRINKLER SYSTEM, IN A MANNER MEETING THE APPROVAL OF THE FIRE CHIEF.

NOTE:

THE PROPERTY IS "TOTALLY EXCLUDED" FROM A "SPECIAL FIRE PROTECTION AREA"

HIGH FIRE HAZARD AREA NOTE:

THE LOTS SHOWN ON THIS MAP ARE IN A HIGH FIRE HAZARD AREA DUE TO WILDLAND EXPOSURE.

EASEMENT NOTES:

- ▲ DENOTES THE EASEMENT FOR STORM DRAIN PURPOSES DEDICATED TO THE COUNTY OF ORANGE HEREON


BASIS OF BEARINGS:

THE BEARINGS SHOWN HEREON ARE BASED ON THE BEARING BETWEEN OCS HORIZONTAL CONTROL STATION GPS No. 1417 AND STATION GPS No. 1448 BEING N10°48'13"E PER RECORDS ON FILE IN THE OFFICE OF THE ORANGE COUNTY SURVEYOR.

DATUM STATEMENT:

COORDINATES SHOWN HEREON ARE BASED ON THE CALIFORNIA COORDINATE SYSTEM, (CCS83) ZONE VI, 1983 NAD, (1991.35 EPOCH OCS GPS ADJUSTMENT).

ALL DISTANCES SHOWN ARE GROUND, UNLESS NOTED OTHERWISE. TO OBTAIN GRID DISTANCES MULTIPLY THE GROUND DISTANCE SHOWN BY 0.999948295.

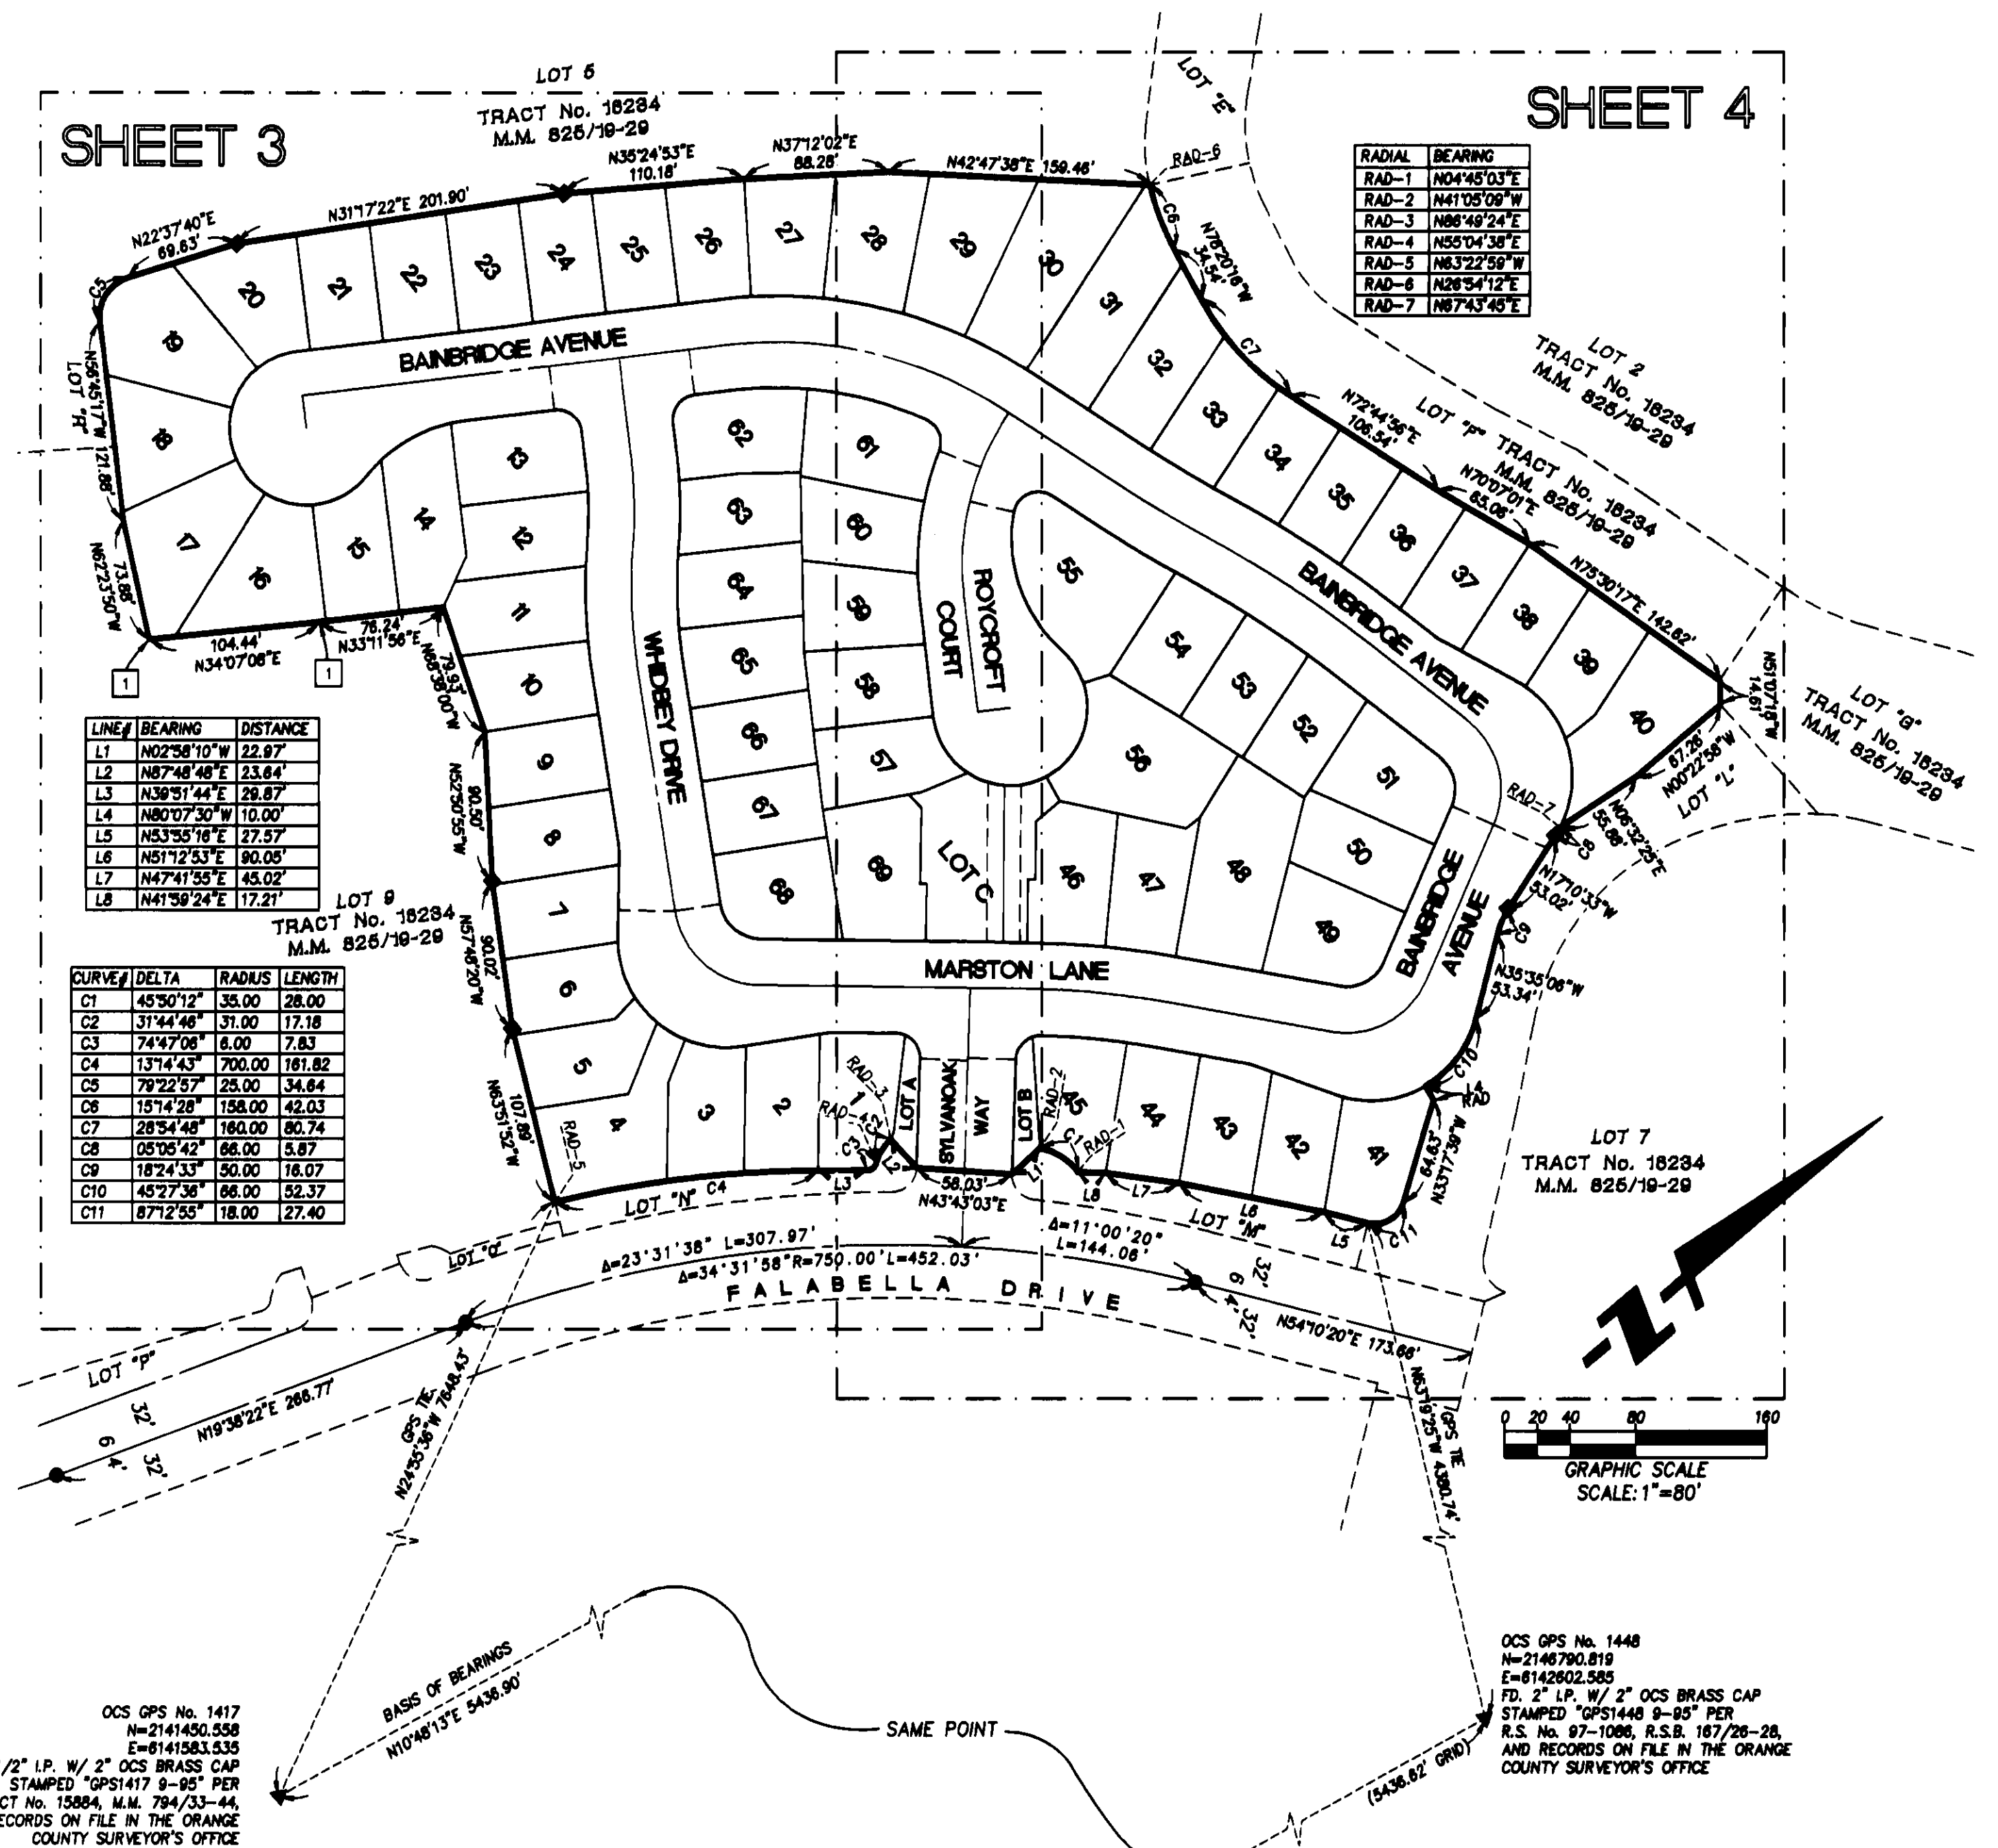

NOTE:

ALL DATA SHOWN ON THIS SHEET ARE MEASURED AND RECORD PER TRACT No. 16234, M.M. 825/19-29.

ALL ADJOINING LOT REFERENCES SHOWN ON THIS SHEET ARE PER TRACT No. 16234, M.M. 825/19-29.



BOUNDARY ESTABLISHMENT / SHEET INDEX MAP

SHEET 3 OF 4 SHEETS
9.365 ACRES
69 NUMBERED LOTS AND
LETTERED LOTS "A" THROUGH "C"
DATE OF SURVEY: NOVEMBER 2001
(ALL OF TENTATIVE TRACT No. 16240)


TRACT NO. 16240

IN THE UNINCORPORATED TERRITORY OF THE COUNTY OF ORANGE, STATE OF CALIFORNIA.

NOVEMBER 2001
JERRY L. USELTON, L.S. 5347 FUSCOE ENGINEERING, INC.

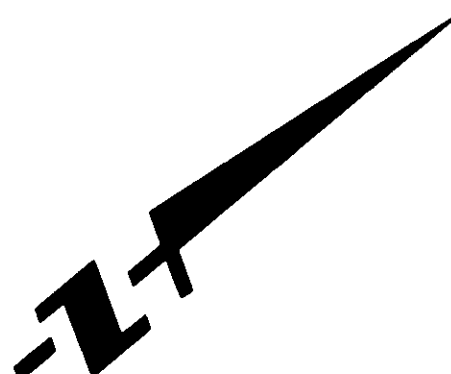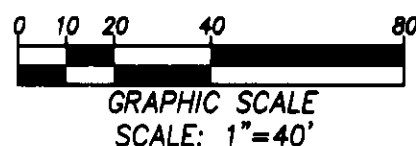

LOT 6
TRACT No. 16234
M.M. 826/10-20

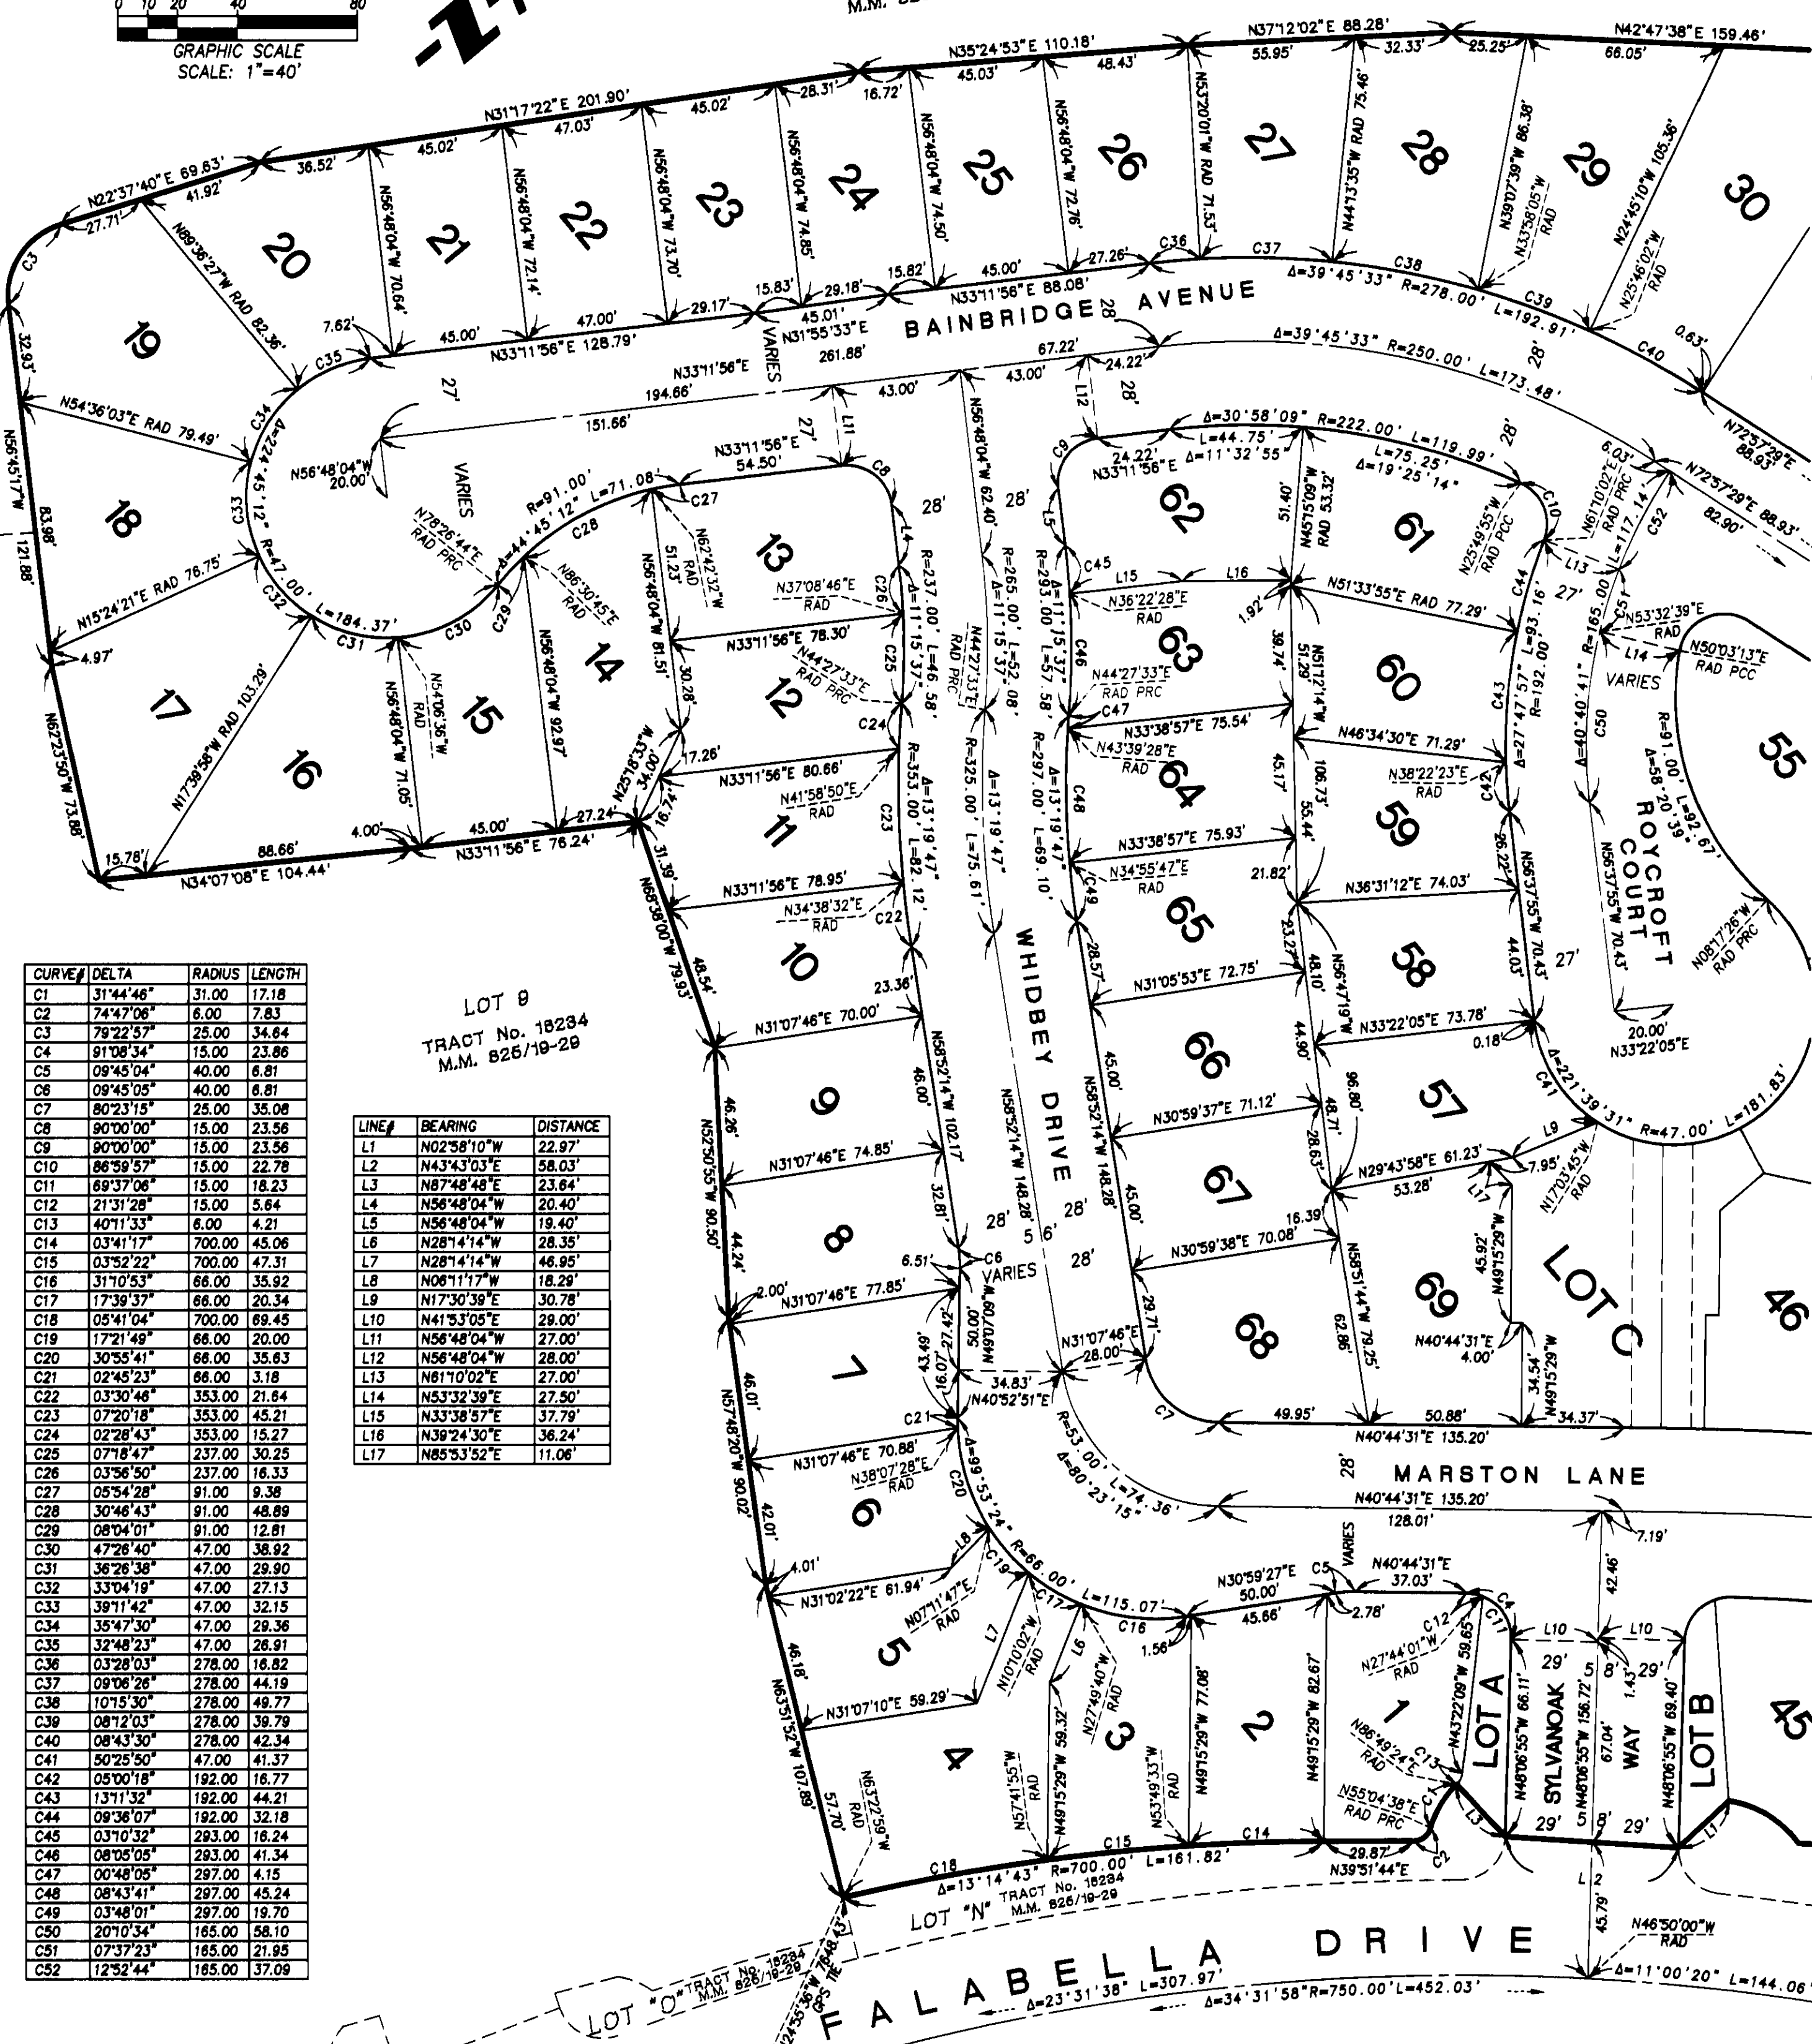

CURVE#	DELTA	RADIUS	LENGTH
C1	31°44'46"	31.00	17.18
C2	74°47'06"	6.00	7.83
C3	79°22'57"	25.00	34.64
C4	91°08'34"	15.00	23.86
C5	09°45'04"	40.00	6.81
C6	09°45'05"	40.00	6.81
C7	80°23'15"	25.00	35.08
C8	90°00'00"	15.00	23.56
C9	90°00'00"	15.00	23.56
C10	86°59'57"	15.00	22.78
C11	69°37'08"	15.00	18.23
C12	21°31'28"	15.00	5.64
C13	40°11'33"	6.00	4.21
C14	03°41'17"	700.00	45.06
C15	03°52'22"	700.00	47.31
C16	31°10'53"	66.00	35.92
C17	17°39'37"	66.00	20.34
C18	05°41'04"	700.00	69.45
C19	17°21'49"	66.00	20.00
C20	30°55'41"	66.00	35.63
C21	02°45'23"	66.00	3.18
C22	03°30'48"	353.00	21.64
C23	07°20'18"	353.00	45.21
C24	02°28'43"	353.00	15.27
C25	07°18'47"	237.00	30.25
C26	03°56'50"	237.00	16.33
C27	05°54'28"	91.00	9.38
C28	30°46'43"	91.00	48.89
C29	08°04'01"	91.00	12.81
C30	47°26'40"	47.00	36.92
C31	36°26'38"	47.00	29.90
C32	33°04'19"	47.00	27.13
C33	39°11'42"	47.00	32.15
C34	35°47'30"	47.00	29.36
C35	32°48'23"	47.00	26.91
C36	03°28'03"	278.00	16.82
C37	09°06'28"	278.00	44.19
C38	10°15'30"	278.00	49.77
C39	08°12'03"	278.00	39.79
C40	08°43'30"	278.00	42.34
C41	50°25'50"	47.00	41.37
C42	05°00'18"	192.00	16.77
C43	13°11'32"	192.00	44.21
C44	09°36'07"	192.00	32.18
C45	03°10'32"	293.00	16.24
C46	08°05'05"	293.00	41.34
C47	00°48'05"	297.00	4.15
C48	08°43'41"	297.00	45.24
C49	03°48'01"	297.00	19.70
C50	20°10'34"	165.00	58.10
C51	07°37'23"	165.00	21.95
C52	12°52'44"	165.00	37.09

LOT 9
TRACT No. 16234
M.M. 826/10-20

LINE#	BEARING	DISTANCE
L1	N02°58'10"W	22.97'
L2	N43°43'03"E	58.03'
L3	N87°48'48"E	23.84'
L4	N56°48'04"W	20.40'
L5	N56°48'04"W	19.40'
L6	N28°14'14"W	28.35'
L7	N28°14'14"W	46.95'
L8	N08°11'17"W	18.28'
L9	N17°30'39"E	30.78'
L10	N41°53'05"E	29.00'
L11	N56°48'04"W	27.00'
L12	N56°48'04"W	28.00'
L13	N61°10'02"E	27.00'
L14	N53°32'39"E	27.50'
L15	N33°38'57"E	37.79'
L16	N38°24'30"E	36.24'
L17	N85°53'52"E	11.06'

SEE SHEET 2 FOR BASIS OF BEARINGS, MONUMENT NOTES, EASEMENT NOTES, SURVEYOR'S NOTES, AND BOUNDARY ESTABLISHMENT/ SHEET INDEX MAP.

