

SHEET 1 OF 5 SHEETS

(ALL OF VESTING TENTATIVE
TRACT NO. 16241)TOTAL ACRES: 8.940 AC.
NUMBERED LOTS: 43
LETTERED LOTS: 2
DATE OF SURVEY: DECEMBER 2001.**TRACT NO. 16241**

IN THE UNINCORPORATED TERRITORY OF ORANGE COUNTY, STATE OF CALIFORNIA


BEING LOT 7 OF TRACT NO. 16234 IN THE UNINCORPORATED TERRITORY OF THE
COUNTY OF ORANGE, STATE OF CALIFORNIA, AS SHOWN ON A MAP FILED IN BOOK
825, PAGES 19-29 OF MISCELLANEOUS MAPS, RECORDS IN THE OFFICE OF THE
COUNTY RECORDER OF ORANGE COUNTY, CALIFORNIA.DOUGLAS BENDER AND ASSOCIATES DOUGLAS W. BENDER R.C.E. 28946
DECEMBER, 2001ACCEPTED AND FILED AT THE
FIRST AMERICAN REQUEST OF
~~CHICAGO~~ TITLE INSURANCE COMPANYDATE FEBRUARY 25, 2003TIME 04:25 PM FEE \$ 15.00INSTRUMENT # 2003000208446BOOK 840 PAGE 32-36 m/mTOM DALY
COUNTY CLERK-RECORDERBY *Randy*
DEPUTY**OWNERSHIP CERTIFICATE:**WE, THE UNDERSIGNED, BEING ALL PARTIES HAVING ANY RECORD TITLE
INTEREST IN THE LAND COVERED BY THIS MAP, DO HEREBY CONSENT TO
THE PREPARATION AND RECORDATION OF SAID MAP, AS SHOWN WITHIN
THE DISTINCTIVE BORDER LINE.WE ALSO HEREBY DEDICATE TO THE PUBLIC FOR STREET PURPOSES
ARDENNES DRIVE, HANOVERIAN WAY AND FALABELLA DRIVE.

WE ALSO HEREBY DEDICATE TO THE COUNTY OF ORANGE:

1. AN EASEMENT FOR STORM DRAIN PURPOSES AS SHOWN ON THIS
MAP.


WE ALSO HEREBY DEDICATE TO SANTA MARGARITA WATER DISTRICT, THE EASEMENTS FOR WATER AND
SEWER PIPELINES, AND ACCESS PURPOSES AS SHOWN ON THIS MAP, SAID EASEMENTS
SHALL BE SUBJECT TO THE SAME TERMS AND CONDITIONS AS ARE SHOWN IN THAT CERTAIN EASEMENT
RECORDED OCTOBER 6, 1980 IN BOOK 13776, PAGE 341 OF OFFICIAL RECORDS, COUNTY OF ORANGE.**CERTIFICATE OF ACCEPTANCE - SANTA MARGARITA WATER DISTRICT**THE UNDERSIGNED, BEING THE DULY APPOINTED AGENT OF THE SANTA MARGARITA WATER DISTRICT, A
PUBLIC CORPORATION OF ORANGE COUNTY, CALIFORNIA, PURSUANT TO ITS RESOLUTION NO. 88-10-2 DOES
HEREBY ACCEPT ON BEHALF OF SAID DISTRICT, THE PIPELINE EASEMENTS FOR WATER, SEWER & ACCESS
PURPOSES, AS DEDICATED AND SHOWN ON THIS TRACT MAP, AS DEDICATED, BY AND BETWEEN
THE SANTA MARGARITA WATER DISTRICT AND SHEA HOMES, AND DOES HEREBY CERTIFY
THAT THE GRANTEE CONSENTS TO THE RECORDATION OF SAID TRACT.BY *Daniel R. Ferons*
DANIEL R. FERONS, CHIEF ENGINEER
SANTA MARGARITA WATER DISTRICT**SHEA HOMES LIMITED PARTNERSHIP**A CALIFORNIA LIMITED PARTNERSHIP
J.F. SHEA CO., INC. NEVADA CORPORATION,
ITS GENERAL PARTNERBY *John C. Donnes*
PRINT NAME: John C. Donnes
PRINT TITLE: ASST. SECRETARYBY *Marion P. Marcum*
PRINT NAME: MARION P. MARCUM
PRINT TITLE: ASSISTANT SECRETARY**DMB LADERA, L.L.C.**A DELAWARE LIMITED LIABILITY COMPANY, BENEFICIARY UNDER A DEED OF TRUST
RECORDED JANUARY 30, 2002 AS INSTRUMENT NO. 20020080172 OF OFFICIAL
RECORDS.BY: RANCHO MISSION VIEJO, L.L.C., A DELAWARE LIMITED LIABILITY COMPANY,
AS AGENT AND OR MANAGER.BY *Donald T. Stark*
PRINT NAME: Donald T. Stark
PRINT TITLE: DIRECTORBY *Stephen C. Schrank*
PRINT NAME: Stephen C. Schrank
PRINT TITLE: Executive Vice President**SIGNATURE OMISSION**PURSUANT TO SECTION 66436 (a) (3) OF THE SUBDIVISION MAP ACT, THE FOLLOWING
SIGNATURES HAVE BEEN OMITTED:

1. LADERA DEVELOPMENT COMPANY, L.L.C., HOLDER OF OIL, GAS AND MINERAL RIGHTS
RECORDED AS INSTRUMENT NO. 19960624029 OF OFFICIAL RECORDS.
2. COUNTY OF ORANGE HOLDER OF STORM DRAIN EASEMENTS AS SHOWN ON TRACT NO. 16234
M.M. 825/19-29.
3. DMB LADERA, L.L.C. A DELAWARE LIMITED LIABILITY COMPANY, HOLDER OF EASEMENTS
RESERVED IN THE DEED RECORDED JANUARY 30, 2002 AS INSTRUMENT NO.
20020080171 OF OFFICIAL RECORDS. (NOT PLOTTABLE)

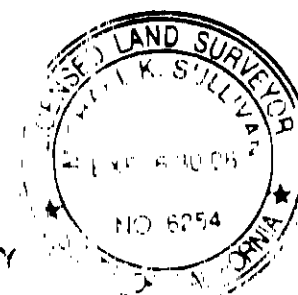ENGINEER'S STATEMENT:THIS MAP WAS PREPARED BY ME OR UNDER MY DIRECTION AND IS BASED UPON A
FIELD SURVEY IN CONFORMANCE WITH THE REQUIREMENTS OF THE SUBDIVISION
MAP ACT AND LOCAL ORDINANCE AT THE REQUEST OF SHEA HOMES ON
DECEMBER 2001. I HEREBY STATE THAT ALL MONUMENTS ARE OF THE CHARACTER
AND OCCUPY THE POSITIONS INDICATED OR THAT THEY WILL BE SET IN SUCH
POSITIONS; AND THAT SAID MONUMENTS ARE SUFFICIENT TO ENABLE THE SURVEY
TO BE RETRACED. I HEREBY STATE THAT THIS FINAL MAP SUBSTANTIALLY
CONFORMS TO THE CONDITIONALLY APPROVED TENTATIVE MAP.*Douglas W. Bender*
DOUGLAS W. BENDER, R.C.E. 28946
MY REGISTRATION EXPIRES MARCH 31, 2003.**COUNTY SURVEYOR'S STATEMENT:**I HEREBY STATE THAT I HAVE EXAMINED THIS MAP AND HAVE FOUND IT TO BE
SUBSTANTIALLY IN CONFORMANCE WITH THE TENTATIVE MAP AS FILED WITH, AMENDED
AND APPROVED BY THE ORANGE COUNTY SUBDIVISION COMMITTEE; THAT ALL
PROVISIONS OF THE SUBDIVISION MAP ACT AND COUNTY SUBDIVISION REGULATIONS
HAVE BEEN COMPLIED WITH AND I AM SATISFIED SAID MAP IS TECHNICALLY CORRECT.DATED THIS 24TH DAY OF JANUARY, 2003*Michael K. Sullivan*
JOHN CANAS, COUNTY SURVEYOR
LS 4408 EXPIRATION DATE: 9-30-05BY: MICHAEL K. SULLIVAN, DEPUTY
LS 6254 EXPIRES 6/30/06**CLERK OF THE BOARD OF SUPERVISOR'S CERTIFICATE:**STATE OF CALIFORNIA)
COUNTY OF ORANGE)I HEREBY CERTIFY THAT THIS MAP WAS PRESENTED FOR APPROVAL TO THE BOARD OF
SUPERVISORS OF ORANGE COUNTY AT A REGULAR MEETING THEREOF HELD ON THE 11th
DAY OF FEBRUARY, 2003, AND THAT THEREUPON SAID BOARD DID, BY AN ORDER
DULY PASSED AND ENTERED, APPROVE SAID MAP AND DID ACCEPT ON BEHALF OF THE
PUBLIC, SUBJECT TO IMPROVEMENTS, THE DEDICATION FOR STREET PURPOSES:
ARDENNES DRIVE, HANOVERIAN WAY AND FALABELLA DRIVE.

AND DID ALSO ACCEPT ON BEHALF OF THE COUNTY OF ORANGE:

1. AN EASEMENT FOR STORM DRAIN PURPOSES AS SHOWN ON THIS
MAP.
AND DID ALSO APPROVE SAID MAP SUBJECT TO SECTION 66436 (a)(3)(A)
OF THE SUBDIVISION MAP ACT.

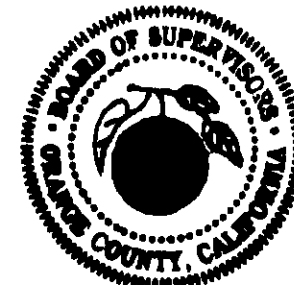DATED THIS 11th DAY OF FEBRUARY, 2003*Darlene J. Bloom*
DARLENE J. BLOOM
CLERK OF THE BOARD OF SUPERVISORS**COUNTY TREASURER-TAX COLLECTOR'S CERTIFICATE:**STATE OF CALIFORNIA)
COUNTY OF ORANGE)I HEREBY CERTIFY THAT ACCORDING TO THE RECORDS OF MY OFFICE THERE ARE NO
LIENS AGAINST THE LAND COVERED BY THIS MAP OR ANY PART THEREOF FOR UNPAID
STATE, COUNTY, MUNICIPAL OR LOCAL TAXES OR SPECIAL ASSESSMENTS COLLECTED
AS TAXES, EXCEPT TAXES OR SPECIAL ASSESSMENTS COLLECTED AS TAXES NOT YET
PAYABLE.AND DO ALSO CERTIFY TO THE RECORDER OF ORANGE COUNTY THAT THE PROVISIONS OF
THE SUBDIVISION MAP ACT HAVE BEEN COMPLIED WITH REGARDING DEPOSITS TO
SECURE THE PAYMENT OF TAXES OR SPECIAL ASSESSMENTS COLLECTED AS TAXES ON
THE LAND COVERED BY THIS MAP.DATED THIS 22nd DAY OF January, 2003*John M.W. Moorlach*
JOHN M.W. MOORLACH
COUNTY TREASURER-TAX COLLECTORBY: *Ms. Jorgensen*
DEPUTY TREASURER-TAX COLLECTOR**AUTOMATIC FIRE SPRINKLER NOTE:**ALL COMMERCIAL STRUCTURES OVER 6,000 SQUARE FEET; ALL MULTIFAMILY
RESIDENTIAL STRUCTURES; ALL DETACHED, SINGLE-FAMILY STRUCTURES EXCEEDING
5,500 SQUARE FEET, AND ALL STRUCTURES EXCEEDING FIRE AUTHORITY ACCESS
REQUIREMENTS SHALL BE PROTECTED BY AN AUTOMATIC SPRINKLER SYSTEM, IN A
MANNER MEETING THE APPROVAL OF THE FIRE CHIEF.**SPECIAL FIRE PROTECTION NOTE:**PROPERTY HAS TOTAL EXCLUSION FROM A SPECIAL FIRE PROTECTION AREA AND MUST
MEET ALL REQUIREMENTS OF THE EXCLUSION FOR DEVELOPMENT WITHIN THE AREA.**HIGH FIRE HAZARD AREA NOTE:**THE LOTS SHOWN ON THIS MAP ARE IN A HIGH FIRE HAZARD AREA DUE TO
WILDLAND EXPOSURE.**NOTES:**PROPERTY MAY BE SUBJECT TO IMPACTS FROM THE FOOTHILL/EASTERN
TRANSPORTATION CORRIDOR.

SHEET 2 OF 5 SHEETS

(ALL OF VESTING TENTATIVE
TRACT NO. 16241)TOTAL ACRES: 8.940 AC.
NUMBERED LOTS: 43
LETTERED LOTS: 2
DATE OF SURVEY: DECEMBER 2001.

TRACT NO. 16241

IN THE UNINCORPORATED TERRITORY OF ORANGE COUNTY, STATE OF CALIFORNIA

DOUGLAS BENDER AND ASSOCIATES DOUGLAS W. BENDER R.C.E. 28946
DECEMBER, 2001SHEA HOMES LIMITED PARTNERSHIPSTATE OF CALIFORNIA)
COUNTY OF ORANGE) SS

ON THIS July 11, 2002, BEFORE ME, Beth A. Hutchinson
A NOTARY PUBLIC IN AND FOR SAID STATE, PERSONALLY APPEARED
John C. Danvers and Marion P. Marcum
PERSONALLY KNOWN TO ME (OR PROVED TO ME ON THE BASIS OF SATISFACTORY EVIDENCE)
TO BE THE PERSON (S) WHOSE NAME (S) IS/ARE SUBSCRIBED TO THE WITHIN INSTRUMENT
AND ACKNOWLEDGED TO ME THAT HE/SHE/THEY EXECUTED THE SAME IN HIS/HER/THEIR
AUTHORIZED CAPACITY (IES), AND THAT BY HIS/HER/THEIR SIGNATURE (S) ON THE
INSTRUMENT THE PERSON (S), OR THE ENTITY UPON BEHALF OF WHICH THE PERSON (S)
ACTED, EXECUTED THE INSTRUMENT.

WITNESS MY HAND:

SIGNATURE Beth A. Hutchinson MY PRINCIPAL PLACE OF BUSINESS IS
NOTARY PUBLIC IN AND FOR SAID STATE IN Orange COUNTY.

Beth A. Hutchinson
(NAME PRINTED)

MY COMMISSION EXPIRES May 8, 2005DMB LADERA, L.L.C.STATE OF CALIFORNIA)
COUNTY OF ORANGE) SS

ON THIS 24th day of July 2002, BEFORE ME, Tina T. Baker
A NOTARY PUBLIC IN AND FOR SAID STATE, PERSONALLY APPEARED
Donald T. Stahl and Stephen C. Schaefer
PERSONALLY KNOWN TO ME (OR PROVED TO ME ON THE BASIS OF SATISFACTORY EVIDENCE)
TO BE THE PERSON (S) WHOSE NAME (S) IS/ARE SUBSCRIBED TO THE WITHIN INSTRUMENT
AND ACKNOWLEDGED TO ME THAT HE/SHE/THEY EXECUTED THE SAME IN HIS/HER/THEIR
AUTHORIZED CAPACITY (IES), AND THAT BY HIS/HER/THEIR SIGNATURE (S) ON THE
INSTRUMENT THE PERSON (S), OR THE ENTITY UPON BEHALF OF WHICH THE PERSON (S)
ACTED, EXECUTED THE INSTRUMENT.

WITNESS MY HAND:

SIGNATURE Tina T. Baker MY PRINCIPAL PLACE OF BUSINESS IS
NOTARY PUBLIC IN AND FOR SAID STATE IN Orange COUNTY.

Tina T. Baker
(NAME PRINTED)

MY COMMISSION EXPIRES 8-29-04SANTA MARGARITA WATER DISTRICTSTATE OF CALIFORNIA)
COUNTY OF ORANGE) SS

ON THIS August 13, 2002, BEFORE ME, ANDREA M. EVANS
A NOTARY PUBLIC IN AND FOR SAID STATE, PERSONALLY APPEARED
DANIEL R. FERONS
PERSONALLY KNOWN TO ME (OR PROVED TO ME ON THE BASIS OF SATISFACTORY EVIDENCE)
TO BE THE PERSON (S) WHOSE NAME (S) IS/ARE SUBSCRIBED TO THE WITHIN INSTRUMENT
AND ACKNOWLEDGED TO ME THAT HE/SHE/THEY EXECUTED THE SAME IN HIS/HER/THEIR
AUTHORIZED CAPACITY (IES), AND THAT BY HIS/HER/THEIR SIGNATURE (S) ON THE
INSTRUMENT THE PERSON (S), OR THE ENTITY UPON BEHALF OF WHICH THE PERSON (S)
ACTED, EXECUTED THE INSTRUMENT.

WITNESS MY HAND:

SIGNATURE Andrea M. Evans MY PRINCIPAL PLACE OF BUSINESS IS
NOTARY PUBLIC IN AND FOR SAID STATE IN Orange COUNTY.

ANDREA M. EVANS
(NAME PRINTED)

MY COMMISSION EXPIRES 4-8-04

SHEET 3 OF 5 SHEETS
(ALL OF TENTATIVE TRACT NO. 16241)

TRACT NO. 16241

IN THE UNINCORPORATED TERRITORY OF THE COUNTY OF ORANGE, STATE OF CALIFORNIA
DOUGLAS BENDER AND ASSOCIATES DOUGLAS W. BENDER R.C.E. 28946
DECEMBER, 2001

TOTAL ACREAGE: 8.940 AC.
NUMBERED LOTS: 43
LETTERED LOTS: 2
DATE OF SURVEY: DECEMBER 2001

BOUNDARY AND INDEX MAP

BASIS OF BEARINGS

BEARINGS SHOWN HEREON ARE BASED ON THE LINE BETWEEN O.C.S. HORIZONTAL CONTROL STATION G.P.S. NO. 1417 AND STATION NO. 1448 BEING N10°48'13"E PER RECORDS ON FILE IN THE OFFICE OF THE ORANGE COUNTY SURVEYOR.

DATUM STATEMENT

COORDINATES SHOWN HEREON ARE BASED UPON THE CALIFORNIA COORDINATE SYSTEM (CCS83) ZONE VI 1983 NAD (1991.35 EPOCH O.C.S. GPS ADJUSTMENT). ALL DISTANCES SHOWN ARE GROUND DISTANCES UNLESS OTHERWISE NOTED. TO OBTAIN GRID DISTANCES, MULTIPLY GROUND DISTANCES BY 0.999948295.

EASEMENT NOTES

- ① INDICATES AN EASEMENT FOR WATER, SEWER & ACCESS PURPOSES DEDICATED TO THE SANTA MARGARITA WATER DISTRICT AS SHOWN ON THIS MAP.
- ② INDICATES AN EASEMENT DEDICATED TO THE COUNTY OF ORANGE FOR STORM DRAIN PURPOSES PER TRACT 16234 M.M. 825/19-29.
- ③ INDICATES AN EASEMENT DEDICATED TO THE COUNTY OF ORANGE FOR STORM DRAIN PURPOSES AS SHOWN ON THIS MAP.

MONUMENT NOTES

- △ INDICATES FOUND O.C.S. G.P.S. MONUMENTS AS NOTED.
 - INDICATES MONUMENT TO BE SET AS NOTED.
 - 1 INDICATES 2" I.P. TAGGED "P.L.S. 5557" OR SPIKE & WASHER STAMPED "P.L.S. 5557" OR LEAD, TACK & TAG "P.L.S. 5557" TO BE SET WITHIN 90 DAYS OF ACCEPTANCE OF IMPROVEMENTS UNLESS OTHERWISE NOTED PER TRACT NO. 16234 M.M. 825/19-29.
 - 2 INDICATES 1" I.P. TAGGED "P.L.S. 5557" OR SPIKE & WASHER STAMPED "P.L.S. 5557" OR LEAD, TACK & TAG "P.L.S. 5557" TO BE SET WITHIN 90 DAYS OF ACCEPTANCE OF IMPROVEMENTS UNLESS OTHERWISE NOTED PER TRACT NO. 16234 M.M. 825/19-29.
 - INDICATES 2" I.P. TAGGED R.C.E. 28946 TO BE SET PRIOR TO RECORDATION.
- NOTES
LOT A IS FOR PRIVATE PARK PURPOSES.
LOT B IS FOR LANDSCAPE PURPOSES.
LOTS A AND B ARE NOT SEPARATE BUILDING SITES.

MONUMENT NOTES (CONT.)

- 2" IRON PIPE TAGGED "R.C.E. 28946" OR SPIKE AND WASHER STAMPED "R.C.E. 28946" OR LEAD AND TACK TAGGED "R.C.E. 28946" TO BE SET AT ALL TRACT CORNERS UNLESS OTHERWISE NOTED, WITHIN 90 DAYS AFTER ACCEPTANCE OF IMPROVEMENTS.
- 8" SPIKE & WASHER STAMPED "R.C.E. 28946" IN ASPHALT PAVING OR LEAD & TAG "R.C.E. 28946" IN CONCRETE TO BE SET AT ALL CENTERLINE INTERSECTIONS, B.C.'S, E.C.'S AND ALL OTHER CENTERLINE POINTS OF CONTROL, UNLESS OTHERWISE NOTED, WITHIN 90 DAYS AFTER ACCEPTANCE OF IMPROVEMENTS.
- 1" IRON PIPE TAGGED "R.C.E. 28946" OR SPIKE AND WASHER STAMPED "R.C.E. 28946" OR LEAD AND TACK TAGGED "R.C.E. 28946" TO BE SET AT ALL LOT CORNERS, EXCEPT B.C.'S, E.C.'S, P.R.C.'S AND P.C.C.'S THAT ABUT A STREET AND ARE NOT LOT CORNERS MARKING SIDE LOT LINES, UNLESS OTHERWISE NOTED, WITHIN 90 DAYS AFTER ACCEPTANCE OF IMPROVEMENTS.

SCALE: 1" = 100'


LINE TABLE

	BEARING	DISTANCE
1	N16°06'25"E	14.03'
2	N35°49'40"W	68.00'
3	N35°49'40"W	32.00'
4	N35°49'40"W	36.00'
5	N54°10'20"E	51.20'
6	N09°15'25"E	33.06'

CURVE TABLE

	DELTA	RADIUS	LENGTH
1	84°34'56"	20.00'	29.52'
2	02°13'15"	1705.00'	66.09'

GPS NO. 1448
FD. 2 1/2" IRON PIPE WITH 2" BRASS CAP STAMPED "GPS
1448 9-95" PER TRACT NO. 16234 M.M. 825/19-29.
N 2146790.819 E 6142602.585

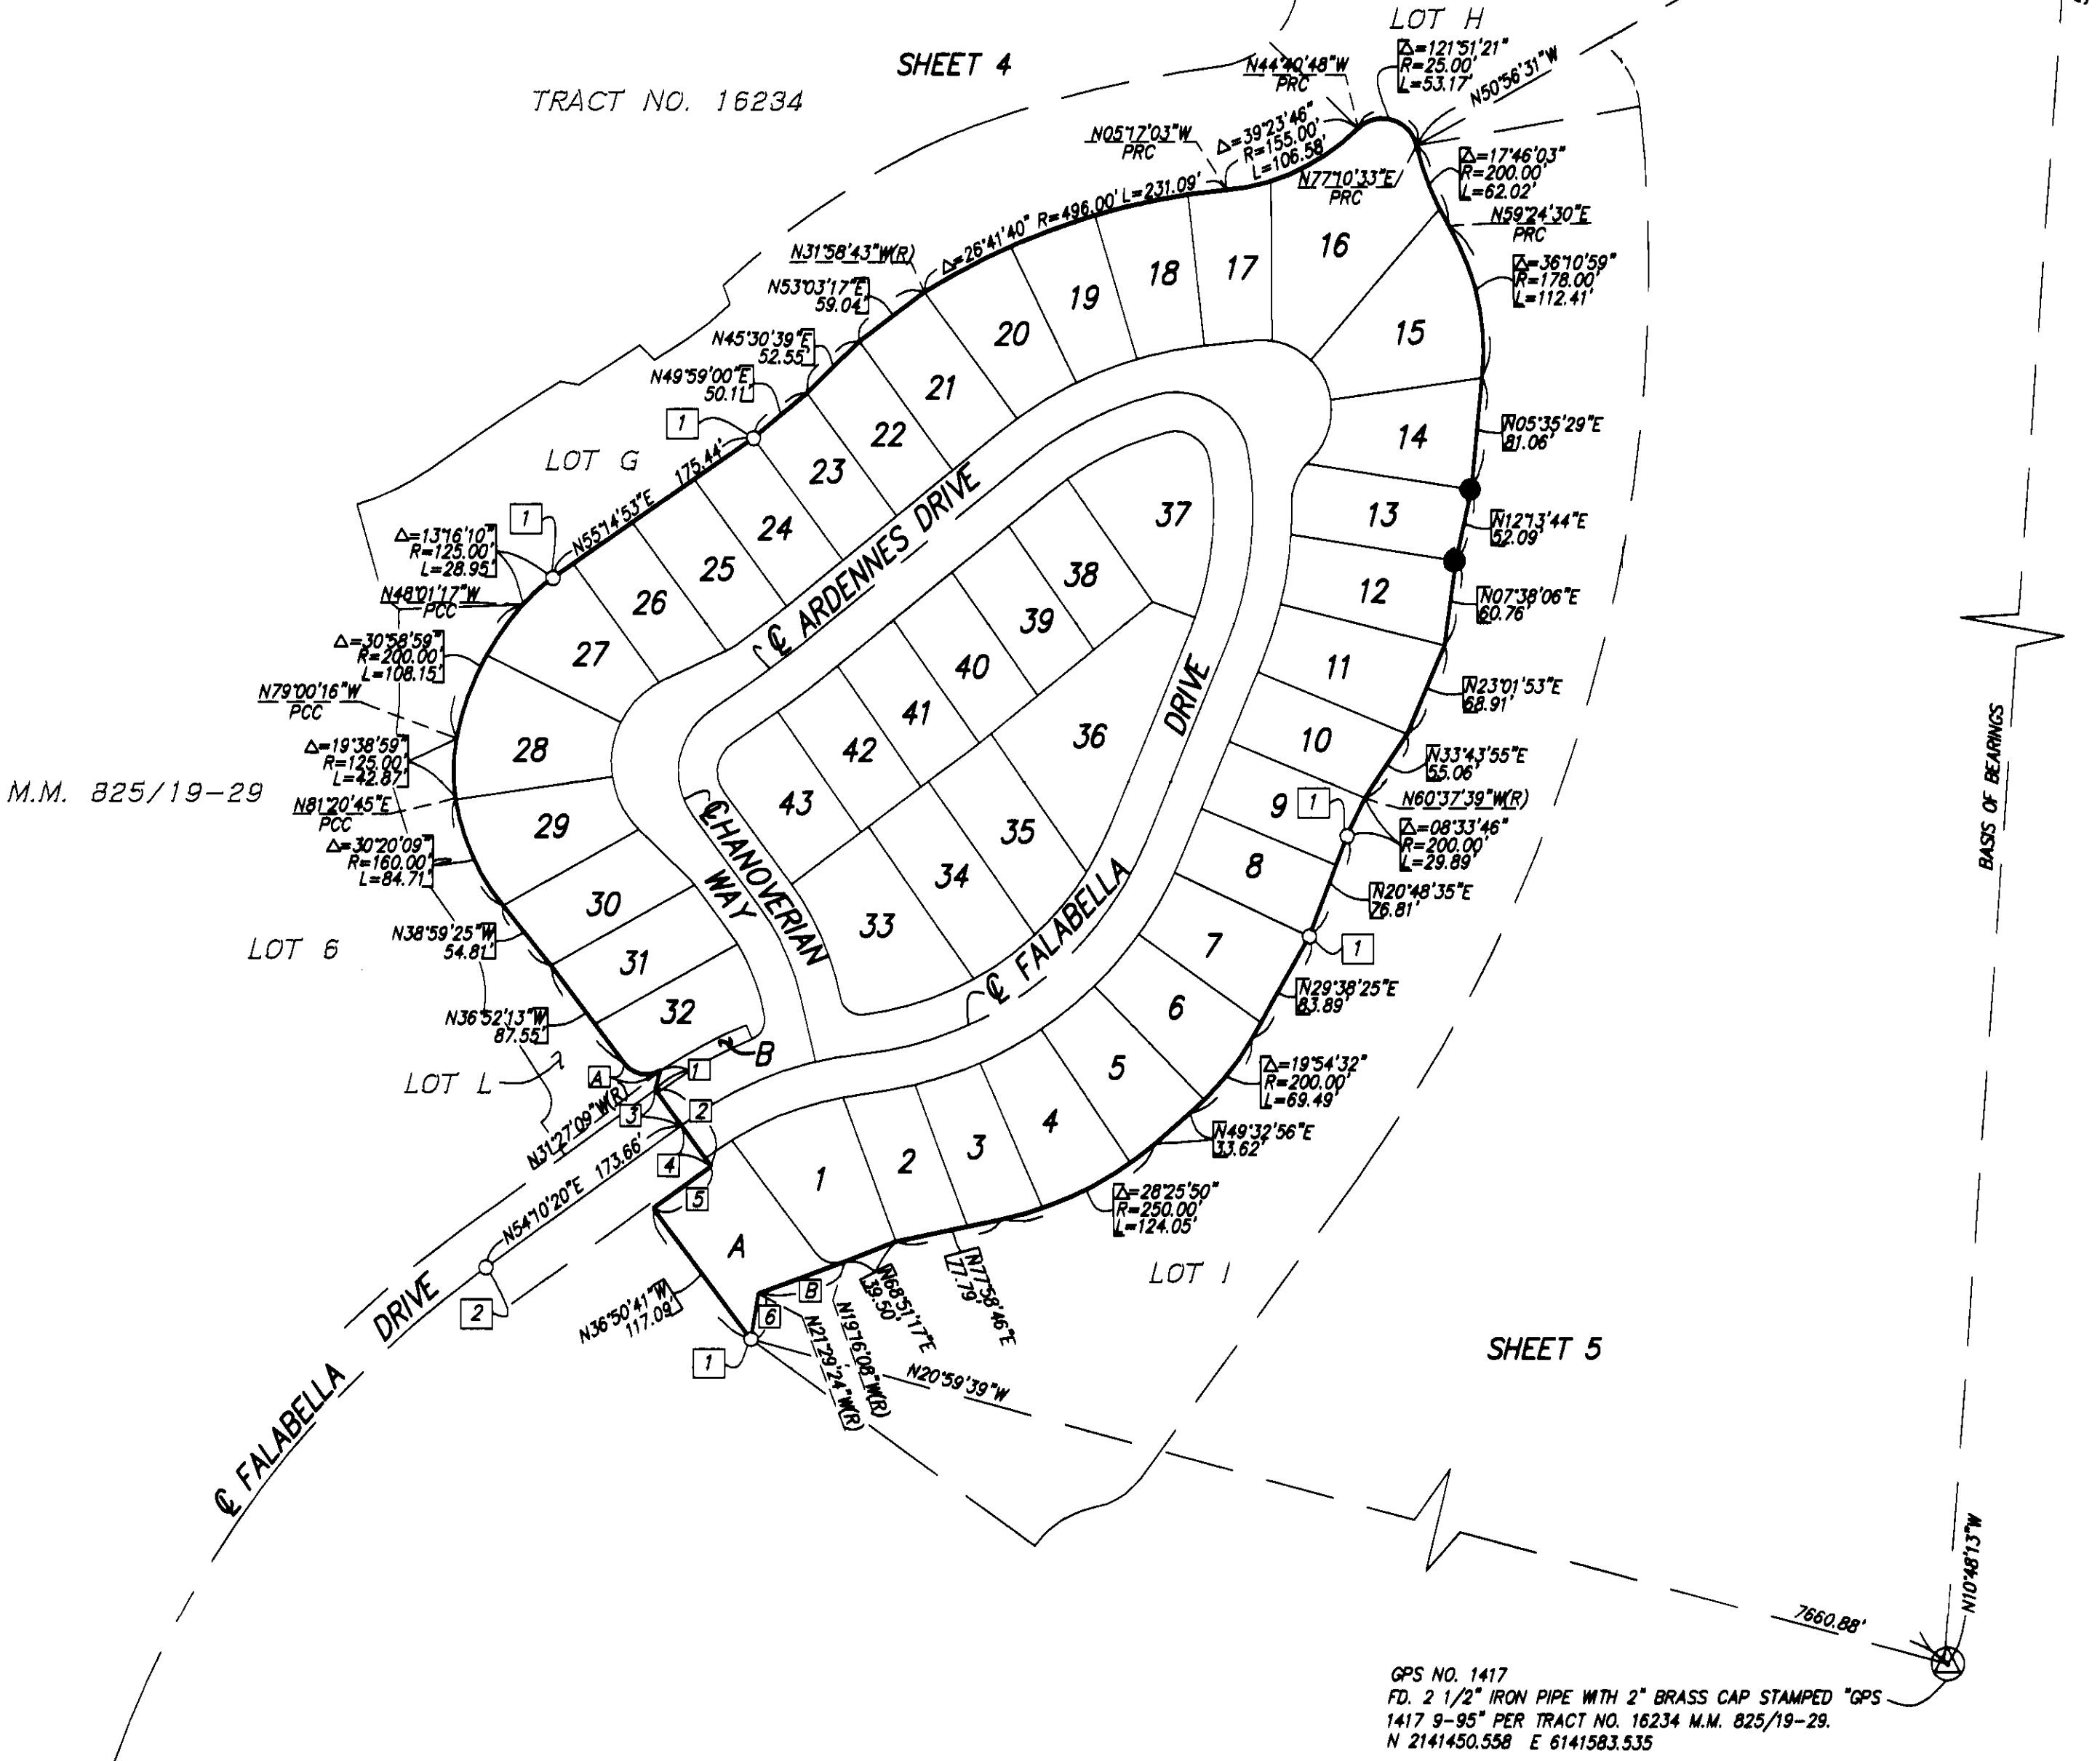

SHEET 4 OF 5 SHEETS
(ALL OF TENTATIVE TRACT NO. 16241)

TOTAL ACRES: 8.940 AC.
NUMBERED LOTS: 43
LETTERED LOTS: 2
DATE OF SURVEY: DECEMBER 2001

TRACT NO. 16241
IN THE UNINCORPORATED TERRITORY OF THE COUNTY OF ORANGE, STATE OF CALIFORNIA
DOUGLAS BENDER AND ASSOCIATES DOUGLAS W. BENDER R.C.E. 28946
DECEMBER, 2001

LINE TABLE

	BEARING	DISTANCE
1	N64°54'25"E	50.00'
2	N83°30'46"E	38.03'
3	N55°09'21"E	46.00'
4	N55°09'21"E	4.42'

CURVE TABLE

	DELTA	RADIUS	LENGTH
A	04°18'34"	472.00'	35.50'
B	09°45'05"	40.00'	6.81'
C	49°03'48"	40.00'	33.55'
D	04°18'34"	528.00'	39.71'
E	04°18'34"	500.00'	37.61'
F	02°03'41"	278.00'	10.00'
G	36°22'09"	50.00'	31.74'
H	23°55'34"	50.00'	20.30'
I	36°48'09"	50.00'	32.12'
J	07°29'38"	200.00'	26.16'
K	06°22'33"	200.00'	22.26'
L	03°53'51"	200.00'	13.60'

NOTES

LOT A IS FOR PRIVATE PARK PURPOSES.
LOT B IS FOR LANDSCAPE PURPOSES.
LOTS A AND B ARE NOT SEPARATE BUILDING SITES.
SEE SHEET 3 FOR MONUMENT NOTES, BASIS OF
BEARINGS, DATUM STATEMENT AND EASEMENT NOTES.

TRACT NO. 16234

M.M. 825/19-29

LOT H

LOT G

LOT I


SEE SHEET

5

TRACT NO. 16241

IN THE UNINCORPORATED TERRITORY OF THE COUNTY OF ORANGE, STATE OF CALIFORNIA
DOUGLAS BENDER AND ASSOCIATES DOUGLAS W. BENDER R.C.E. 28946
DECEMBER, 2001

SHEET 5 OF 5 SHEETS
(ALL OF TENTATIVE TRACT NO. 16241)
TOTAL ACREAGE: 8.940 AC.
NUMBERED LOTS: 43
LETTERED LOTS: 2
DATE OF SURVEY: DECEMBER 2001

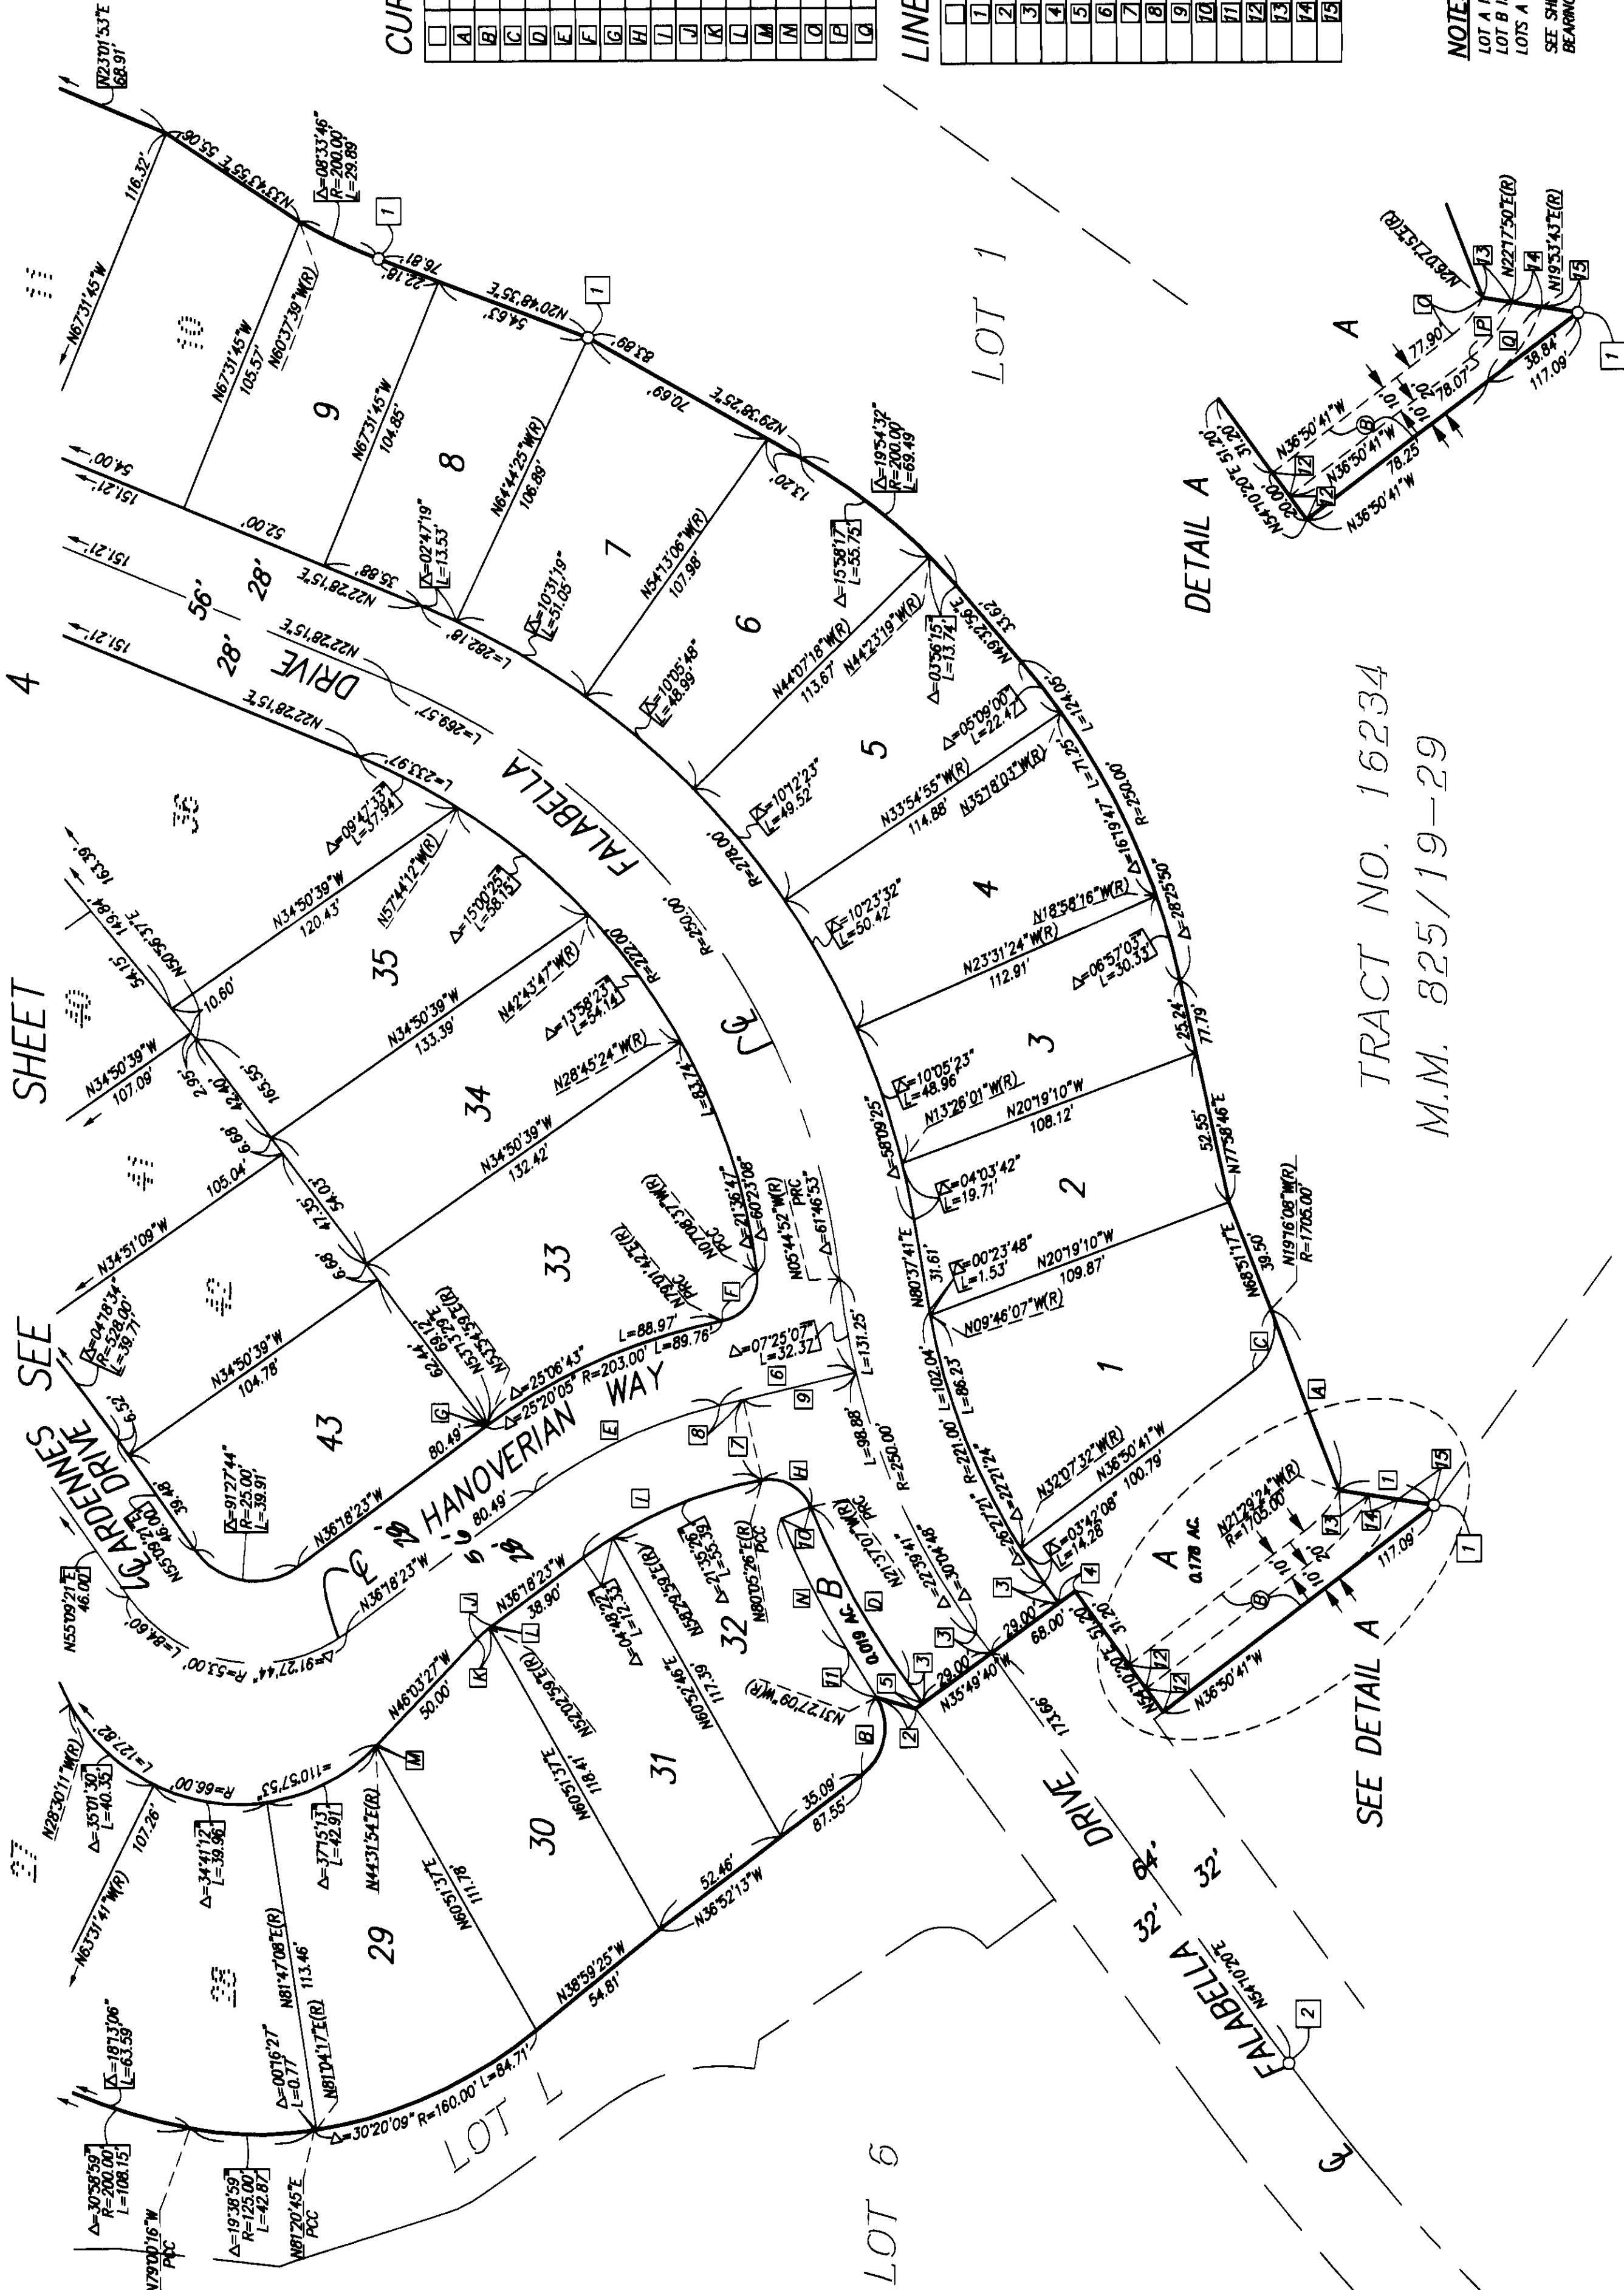

CURVE TABLE

	DELTA	RADIUS	LENGTH
A	02°13'15"	1765.00'	66.10'
B	84°34'56"	20.00'	29.52'
C	74°18'02"	18.00'	23.34'
D	14°12'33"	279.00'	69.19'
E	23°08'24"	175.00'	70.88'
F	86°10'19"	15.00'	22.56'
G	00°13'22"	203.00'	0.79'
H	78°17'28"	15.00'	20.50'
I	26°23'48"	147.00'	67.72'
J	09°45'05"	40.00'	6.81'
K	08°06'26"	40.00'	5.66'
L	01°38'38"	40.00'	1.15'
M	00°35'22"	66.00'	0.68'
N	09°50'03"	290.00'	49.77'
O	27°02'03"	35.00'	16.51'
P	30°51'29"	45.00'	24.24'
Q	33°15'35"	55.00'	31.93'

LINE TABLE

	BEARING	DISTANCE
1	N09°15'25"E	33.08'
2	N16°06'25"E	14.03'
3	N54°10'20"E	8.50'
4	N35°49'40"W	7.00'
5	N35°49'40"W	3.00'
6	N13°09'59"W(R)	48.31'
7	N76°50'01"E	28.24'
8	N13°09'59"W(R)	8.35'
9	N13°09'59"W(R)	39.98'
10	N21°37'07"W(R)	11.00'
11	N58°32'51"E	19.63'
12	N54°10'20"E	10.00'
13	N09°15'25"E	10.34'
14	N09°15'25"E	10.22'
15	N09°15'25"E	12.50'

NOTES

LOT A IS FOR PRIVATE PARK PURPOSES.
LOT B IS FOR LANDSCAPE PURPOSES.
LOTS A AND B ARE NOT SEPARATE BUILDING SITES.
SEE SHEET 3 FOR MONUMENT NOTES, BASIS OF BEARINGS, DATUM STATEMENT AND EASEMENT NOTES.

TRACT NO. 16234
M.M. 825/19-29