

SHEET 1 OF 4 SHEETS

ALL OF TENTATIVE TRACT
MAP NO. 16242
TOTAL LOTS: 1-37 AND LOTS A-F
TOTAL ACREAGE: 5.549 AC.
DATE OF SURVEY: NOVEMBER, 2001
BLOCK 5057 MODULE 25

TRACT MAP NO. 16242

IN THE UNINCORPORATED TERRITORY OF THE COUNTY OF ORANGE,
STATE OF CALIFORNIA

BEING A SUBDIVISION OF LOT 9, AS SHOWN ON TRACT MAP NO. 16234
FILED IN BOOK 825, PAGES 19 THROUGH 29 INCLUSIVE OF MISCELLANEOUS MAPS
IN THE OFFICE OF THE COUNTY RECORDER OF SAID COUNTY, STATE OF CALIFORNIA
ADAMS - STREETER CIVIL ENGINEERING, INC. JAN A. ADAMS, R.C.E. 21687
DATE OF SURVEY: NOVEMBER, 2001

ACCEPTED AND FILED AT THE
REQUEST OF

FIDELITY NATIONAL TITLE COMPANY

DATE JUNE 18, 2002
TIME 08:54 AM FEE \$ 13.00
INSTRUMENT # 20020508504
BOOK 833 PAGE 24-27 N/M
DARLENE J. BLOOM
INTERIM COUNTY CLERK-RECORDER
BY [Signature]
DEPUTY

OWNERSHIP CERTIFICATE:

WE, THE UNDERSIGNED, BEING ALL PARTIES HAVING ANY RECORD TITLE INTEREST IN THE LAND COVERED BY THIS MAP, DO HEREBY CONSENT TO THE PREPARATION AND RECORDATION OF SAID MAP, AS SHOWN WITHIN THE DISTINCTIVE BORDER LINE.

WE HEREBY DEDICATE TO THE PUBLIC FOR STREET PURPOSES: DE LEON LANE AND BAUDIN CIRCLE

WE ALSO DEDICATE TO THE SANTA MARGARITA WATER DISTRICT, THE EASEMENTS FOR SEWER, WATER AND ACCESS PURPOSES AS SHOWN ON SAID MAP, WHICH EASEMENTS SHALL BE SUBJECT TO THE SAME TERMS AND CONDITIONS AS ARE SHOWN IN THAT CERTAIN EASEMENT RECORDED OCTOBER 6, 1980, IN BOOK 13776, PAGE 341, OF OFFICIAL RECORDS, COUNTY OF ORANGE.

DMB LADERA, LLC, A DELAWARE LIMITED LIABILITY COMPANY.

BY: RANCHO MISSION VIEJO, LLC, A DELAWARE LIMITED LIABILITY COMPANY, AS AGENT AND/OR MANAGER.

[Signature]
DIRECTOR COMMUNITY DEV.
DONALD T. STAHLIN

[Signature]
EXECUTIVE VICE PRESIDENT
STEPHEN C. SCHIRANK

~~DMB CONSOLIDATED HOLDINGS, LLC, AN ARIZONA LIMITED LIABILITY COMPANY,
BENEFICIARY UNDER DEED OF TRUSTS RECORDED DECEMBER 10, 1996 AS INSTRUMENT
NO. 19960624030, AND RECORDED APRIL 20, 1999 AS INSTRUMENT NO. 19990288616,
BOTH OF OFFICIAL RECORDS.~~

BY: DMB ASSOCIATES, INC, AN ARIZONA CORPORATION, AS MANAGER.

[Signature]
TERRY D. RANDALL
VICE PRESIDENT

[Signature]
TIMOTHY A. KAEHR
EXECUTIVE VICE PRESIDENT

ENGINEER'S STATEMENT

THIS MAP WAS PREPARED BY ME OR UNDER MY DIRECTION AND IS BASED UPON A FIELD SURVEY IN CONFORMANCE WITH THE REQUIREMENTS OF THE SUBDIVISION MAP ACT AND LOCAL ORDINANCE AT THE REQUEST OF DMB LADERA, LLC, IN NOVEMBER, 2001. I HEREBY STATE THAT ALL MONUMENTS ARE OF THE CHARACTER AND OCCUPY THE POSITIONS INDICATED, OR THAT THEY WILL BE SET IN SUCH POSITIONS; AND THAT SAID MONUMENTS ARE SUFFICIENT TO ENABLE THE SURVEY TO BE RETRACED. I HEREBY STATE THAT THIS FINAL MAP SUBSTANTIALLY CONFORMS TO THE CONDITIONALLY APPROVED TENTATIVE MAP.

[Signature]
JAN A. ADAMS, R.C.E. 21687
EXPIRES: 9/30/05




COUNTY SURVEYOR'S STATEMENT

I HEREBY STATE THAT I HAVE EXAMINED THIS MAP AND HAVE FOUND IT TO BE SUBSTANTIALLY IN CONFORMANCE WITH THE TENTATIVE MAP AS FILED WITH, AMENDED AND APPROVED BY THE ORANGE COUNTY SUBDIVISION COMMITTEE; THAT ALL PROVISIONS OF THE SUBDIVISION MAP ACT AND COUNTY SUBDIVISION REGULATIONS HAVE BEEN COMPLIED WITH AND I AM SATISFIED SAID MAP IS TECHNICALLY CORRECT.

DATED THIS 29TH DAY OF MAY, 2002

[Signature]
JOHN CANAS, COUNTY SURVEYOR
LS 4408 EXPIRATION DATE: 9-30-05

BY: MICHAEL K. SULLIVAN, DEPUTY
LS 6284 EXPIRES 6-30-02

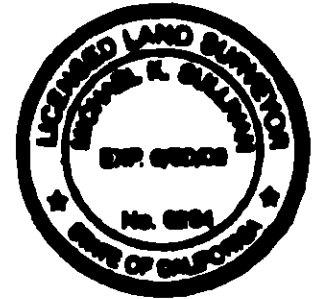

COUNTY TREASURER - TAX COLLECTOR'S CERTIFICATE

STATE OF CALIFORNIA }
COUNTY OF ORANGE } ss

I HEREBY CERTIFY THAT ACCORDING TO THE RECORDS OF MY OFFICE, THERE ARE NO LIENS AGAINST THE LAND COVERED BY THIS MAP OR ANY PART THEREOF FOR UNPAID STATE, COUNTY, MUNICIPAL OR LOCAL TAXES OR SPECIAL ASSESSMENTS COLLECTED AS TAXES, EXCEPT TAXES OR SPECIAL ASSESSMENTS COLLECTED AS TAXES NOT YET PAYABLE.

AND DO ALSO CERTIFY TO THE RECORDER OF ORANGE COUNTY THAT THE PROVISIONS OF THE SUBDIVISION MAP ACT HAVE BEEN COMPLIED WITH REGARDING DEPOSITS TO SECURE PAYMENT OF TAXES OR SPECIAL ASSESSMENTS COLLECTED AS TAXES ON THE LAND COVERED BY THIS MAP.

DATED THIS 9th DAY OF May, 2002

JOHN M. W. MOORLACH
COUNTY TREASURER - TAX COLLECTOR

BY [Signature]
DEPUTY TREASURER - TAX COLLECTOR

CLERK OF THE BOARD OF SUPERVISORS CERTIFICATE

STATE OF CALIFORNIA }
COUNTY OF ORANGE } ss

I HEREBY CERTIFY THAT THIS MAP WAS PRESENTED FOR APPROVAL TO THE BOARD OF SUPERVISORS OF ORANGE COUNTY AT A REGULAR MEETING THEREOF HELD ON THE 11th DAY OF June, 2002, AND THAT THEREUPON SAID BOARD DID, BY AN ORDER DULY PASSED AND ENTERED, APPROVE SAID MAP AND DID ACCEPT ON BEHALF OF THE PUBLIC, SUBJECT TO IMPROVEMENTS, THE DEDICATION FOR STREET PURPOSES OF: DE LEON LANE AND BAUDIN CIRCLE

DATED THIS 11th DAY OF June, 2002.

[Signature]
DARLENE J. BLOOM, CLERK OF THE BOARD OF SUPERVISORS



CERTIFICATE OF ACCEPTANCE

THE UNDERSIGNED, BEING THE DULY APPOINTED AGENT OF THE SANTA MARGARITA WATER DISTRICT, A PUBLIC CORPORATION OF ORANGE COUNTY, CALIFORNIA, PURSUANT TO ITS RESOLUTION NO. 88-10-2, DOES HEREBY ACCEPT ON BEHALF OF SAID DISTRICT THE EASEMENTS FOR SEWER, WATER AND ACCESS PURPOSES, AS DEDICATED AND AS SHOWN ON THIS TRACT MAP, BY AND BETWEEN THE SANTA MARGARITA WATER DISTRICT AND DMB LADERA, LLC, AND DOES HEREBY CERTIFY THAT THE GRANTEE CONSENTS TO THE RECORDATION OF SAID TRACT.

BY: [Signature]
DANIEL R. FERONS, CHIEF ENGINEER
SANTA MARGARITA WATER DISTRICT

STATE OF CALIFORNIA }
COUNTY OF ORANGE } ss

ON THIS 9th DAY OF APRIL, 2002, BEFORE ME, ANDREA M. EVANS, A NOTARY PUBLIC IN AND FOR SAID STATE, PERSONALLY APPEARED DANIEL FERONS, PERSONALLY KNOWN TO ME (OR PROVED TO ME ON THE BASIS OF SATISFACTORY EVIDENCE) TO BE THE PERSON WHOSE NAME IS SUBSCRIBED TO THE WITHIN INSTRUMENT AND ACKNOWLEDGED TO ME THAT SHE EXECUTED THE SAME IN HER AUTHORIZED CAPACITY AND THAT BY HER SIGNATURE ON THE INSTRUMENT THE PERSON, OR THE ENTITY UPON BEHALF OF WHICH THE PERSON ACTED, EXECUTED THE INSTRUMENT.

WITNESS MY HAND:

[Signature]
NOTARY PUBLIC IN AND FOR SAID STATE
ANDREA M. EVANS
PRINT NAME

MY PRINCIPAL PLACE OF BUSINESS
IS IN ORANGE COUNTY

MY COMMISSION EXPIRES 4/8/04

STATE OF CALIFORNIA)

COUNTY OF Orange

ON THIS 29th DAY OF March, 2002, BEFORE ME, Tina T. Baker, A NOTARY PUBLIC IN AND FOR SAID STATE, PERSONALLY APPEARED Donald T. Stahlin AND Stephen C. Schirank PERSONALLY KNOWN TO ME (OR PROVED TO ME ON THE BASIS OF SATISFACTORY EVIDENCE) TO BE THE PERSONS WHOSE NAMES ARE SUBSCRIBED TO THE WITHIN INSTRUMENT AND ACKNOWLEDGED TO ME THAT THEY EXECUTED THE SAME IN THEIR AUTHORIZED CAPACITIES AND THAT BY THEIR SIGNATURES ON THE INSTRUMENT THE PERSON OR THE ENTITY UPON BEHALF OF WHICH THE PERSONS ACTED, EXECUTED THE INSTRUMENT.

WITNESS MY HAND:

[Signature]
NOTARY PUBLIC IN AND FOR SAID STATE
Tina T. Baker
PRINT NAME

MY PRINCIPAL PLACE OF BUSINESS
IS IN Orange COUNTY

MY COMMISSION EXPIRES 8/29/04

STATE OF Arizona

COUNTY OF Maricopa

ON THIS 2nd DAY OF April, 2002, BEFORE ME, Carolynn Sneddon A NOTARY PUBLIC IN AND FOR SAID STATE, PERSONALLY APPEARED Terry D. Randall AND Timothy A. Kaeher PERSONALLY KNOWN TO ME (OR PROVED TO ME ON THE BASIS OF SATISFACTORY EVIDENCE) TO BE THE PERSONS WHOSE NAMES ARE SUBSCRIBED TO THE WITHIN INSTRUMENT AND ACKNOWLEDGED TO ME THAT THEY EXECUTED THE SAME IN THEIR AUTHORIZED CAPACITIES AND THAT BY THEIR SIGNATURES ON THE INSTRUMENT THE PERSON OR THE ENTITY UPON BEHALF OF WHICH THE PERSONS ACTED, EXECUTED THE INSTRUMENT.

WITNESS MY HAND:

[Signature]
NOTARY PUBLIC IN AND FOR SAID STATE
Carolynn Sneddon
PRINT NAME

MY PRINCIPAL PLACE OF BUSINESS
IS IN Maricopa COUNTY

MY COMMISSION EXPIRES 07/14/02

SIGNATURE OMISSIONS

PURSUANT TO THE PROVISIONS OF SECTION 66436 (3) OF THE SUBDIVISION MAP ACT, THE FOLLOWING SIGNATURES HAVE BEEN OMITTED:

LADERA DEVELOPMENT COMPANY, LLC, HOLDER OF OIL, GAS AND MINERAL RIGHTS RECORDED DECEMBER 10, 1996 AS INSTRUMENT NO. 19960624029 OF OFFICIAL RECORDS.


SHEET 3 OF 4 SHEETS
ALL OF TENTATIVE TRACT
MAP NO. 16242
TOTAL LOTS: 1-37 AND LOTS A-F
TOTAL ACREAGE: 5.549 AC.
DATE OF SURVEY: NOVEMBER, 2001

TRACT MAP NO. 16242

IN THE UNINCORPORATED TERRITORY OF THE COUNTY OF ORANGE,
STATE OF CALIFORNIA

ADAMS - STREETER CIVIL ENGINEERING, INC. JAN A. ADAMS, R.C.E. 21687
DATE OF SURVEY: NOVEMBER, 2001


LOT 6

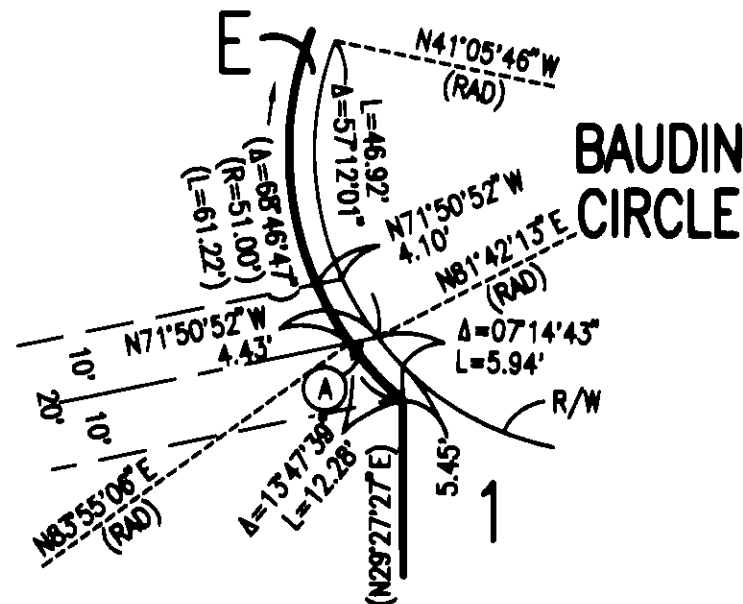

DETAIL 'A'
N.T.S.

LOT 6
TRACT NO. 16234
MM 825/19-29

SCALE: 1"=30'

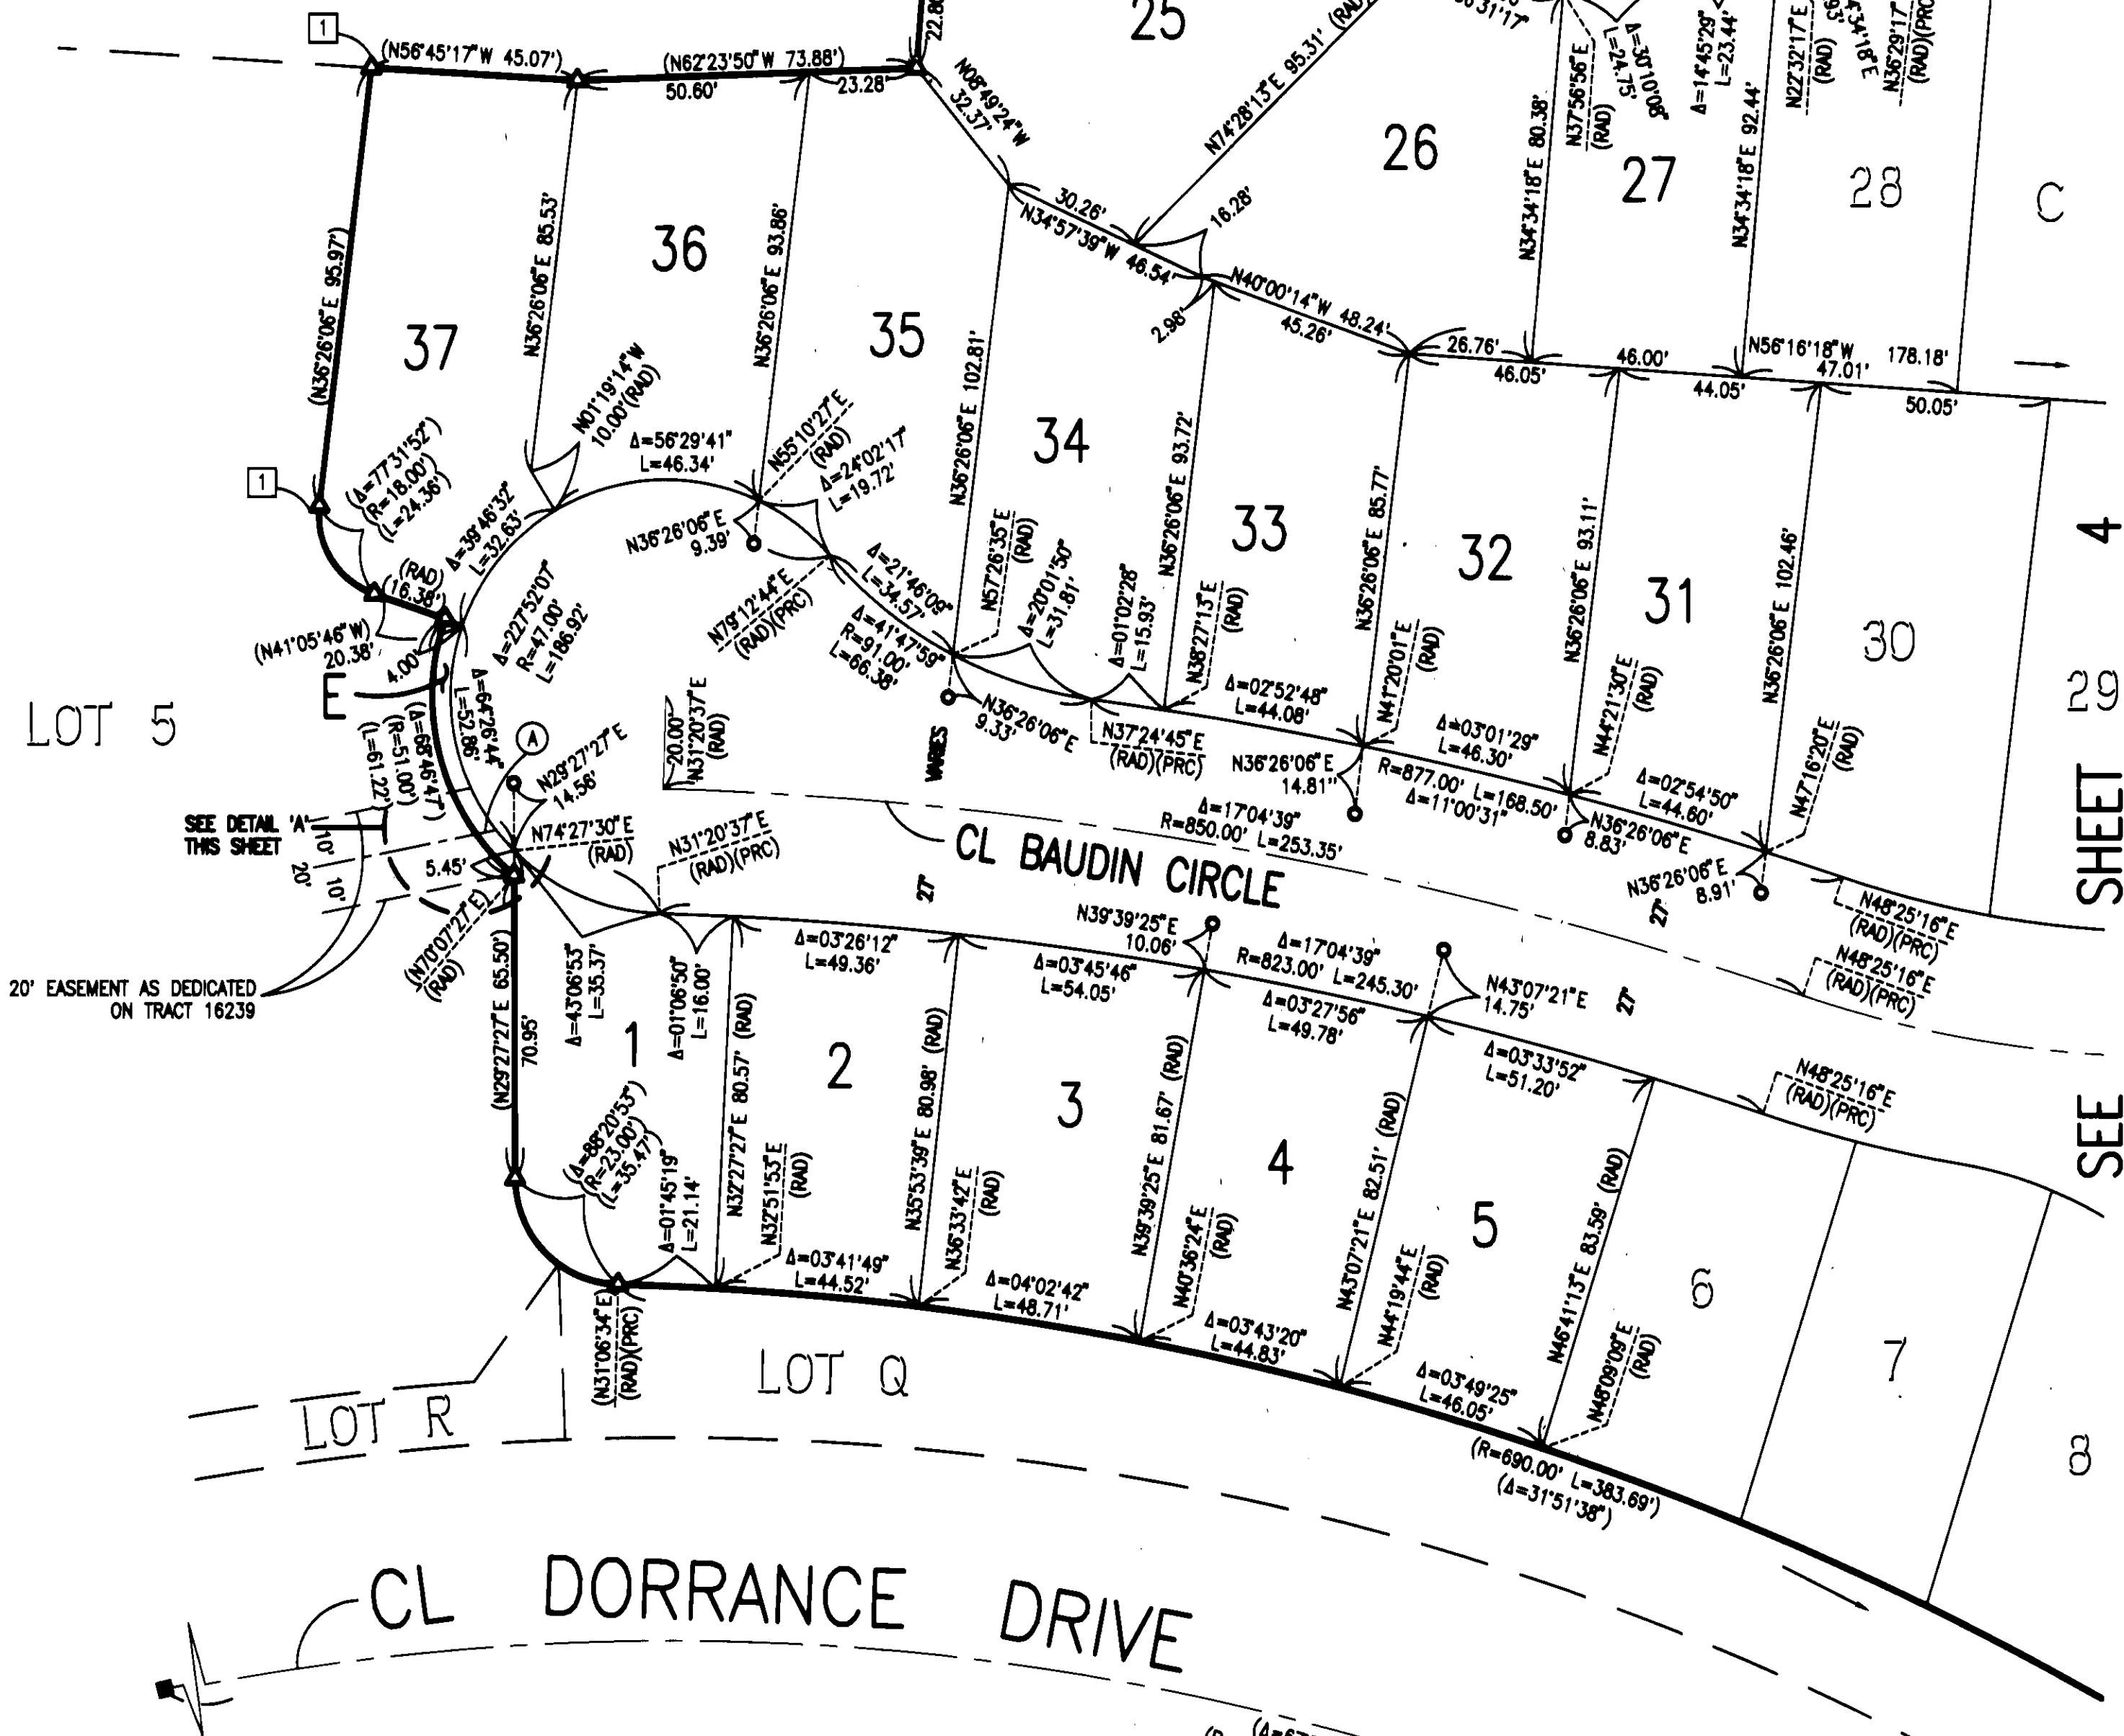

NOTES:

LETTERED LOTS ARE NOT SEPARATE BUILDING SITES.
LOTS DESIGNATED AS OPEN SPACES ARE FOR LANDSCAPE PURPOSES
AND WILL BE MAINTAINED BY THE HOMEOWNER'S ASSOCIATION.
SEE SHEET 2 FOR EASEMENT NOTES, BASIS OF BEARINGS, AND MONUMENT NOTES.

SHEET 4 OF 4 SHEETS

ALL OF TENTATIVE TRACT
MAP NO. 16242
TOTAL LOTS: 1-37 AND LOTS A-F
TOTAL ACRES: 5.540 AC.
DATE OF SURVEY: NOVEMBER, 2001

TRACT MAP NO. 16242

IN THE UNINCORPORATED TERRITORY OF THE COUNTY OF ORANGE,
STATE OF CALIFORNIA

ADAMS - STREETER CIVIL ENGINEERING, INC. JAN A. ADAMS, R.C.E. 21687
DATE OF SURVEY: NOVEMBER, 2001

