

SHEET 1 OF 6 SHEETS
64 NUMBERED LOTS AND
LOTS A, B AND C
ACREAGE: 9.905 ACRES
(ALL OF TENTATIVE
TRACT NO. 16243)

TRACT NO. 16243

IN UNINCORPORATED TERRITORY OF THE COUNTY OF ORANGE,
STATE OF CALIFORNIA

BEING A SUBDIVISION OF LOT 1 OF TRACT NO. 16235, AS SHOWN
ON A MAP FILED IN BOOK 825, PAGES 30 THROUGH 39,
INCLUSIVE, OF MISCELLANEOUS MAPS, IN THE OFFICE OF THE
COUNTY RECORDER OF SAID COUNTY.

HUNSAKER AND ASSOCIATES IRVINE, INC.

RORY S. WILLIAMS, L.S. 6654 DATE OF SURVEY: NOVEMBER, 2001

ACCEPTED AND FILED AT THE
REQUEST OF

COMMERCE TITLE COMPANY

DATE: AUGUST 30, 2002

TIME: 09:43 AM FEE: \$ 17.00

INSTRUMENT NO. 20020735193

BOOK 835 PAGE 34-39 m/n

DARLENE J. BLOOM
INTERIM COUNTY CLERK - RECORDER

BY  DEPUTY

BLOCK: 5157
MODULE: 26

OWNERSHIP CERTIFICATE:

WE, THE UNDERSIGNED, BEING ALL PARTIES HAVING ANY RECORD TITLE INTEREST IN THE LAND COVERED BY THIS MAP, DO HEREBY CONSENT TO THE PREPARATION AND RECORDATION OF SAID MAP, AS SHOWN WITHIN THE DISTINCTIVE BORDER LINE.

WE HEREBY DEDICATE TO THE PUBLIC FOR STREET PURPOSES: ST. BRIDE WAY, ST. GILES COURT, ST. IVES WAY, ST. JUST AVENUE AND ST. STEVEN COURT.

WE ALSO DO HEREBY DECLARE THAT THE LAND COVERED BY THIS MAP IS LOCATED IN A VERY HIGH FIRE HAZARD AREA DUE TO WILDLAND EXPOSURE BASED ON STATE SRA MAPS.

WE ALSO HEREBY DEDICATE TO THE SANTA MARGARITA WATER DISTRICT THE PIPELINE EASEMENT FOR WATER, SEWER AND ACCESS PURPOSES, AS SHOWN ON THIS TRACT MAP, WHICH EASEMENT SHALL BE SUBJECT TO THE SAME TERMS AND CONDITIONS AS SHOWN IN THAT CERTAIN EASEMENT RECORDED OCTOBER 6, 1980, IN BOOK 13776, PAGE 341 OF OFFICIAL RECORDS OF ORANGE COUNTY, CALIFORNIA.

CENTEX HOMES, A NEVADA GENERAL PARTNERSHIP, OWNER.

BY: CENTEX REAL ESTATE CORPORATION, A NEVADA CORPORATION,
ITS MANAGING GENERAL PARTNER.

BY:  NAME: Roland F. Osgood
TITLE: President - South Coast
BY:  NAME: Martin Juliusen
TITLE: Controller - South Coast

DMB LADERA, LLC, A DELAWARE LIMITED LIABILITY COMPANY, AS BENEFICIARY
UNDER DEED OF TRUST RECORDED AS INSTRUMENT NO.
200 OF OFFICIAL RECORDS.

BY: RANCHO MISSION VIEJO, L.L.C., A DELAWARE LIMITED LIABILITY COMPANY, ITS
AUTHORIZED AGENT AND MANAGER.

BY:  NAME: Donald T. Stahlin
TITLE: Director of Com. Dev.
BY:  NAME: Stephen C. Schmeck
TITLE: Exec Vice President - Development

NOTARY ACKNOWLEDGMENTS:

STATE OF CALIFORNIA } SS
COUNTY OF ORANGE }

ON March 12, 2002, BEFORE ME, Rhonda Keiger Painter, PERSONALLY
APPEARED Roland F. Osgood AND Martin Juliusen, PERSONALLY
KNOWN TO ME (OR PROVED TO ME ON THE BASIS OF SATISFACTORY EVIDENCE) TO BE THE PERSON(S)
WHOSE NAME(S) IS/ARE SUBSCRIBED TO THE WITHIN INSTRUMENT AND ACKNOWLEDGED TO ME THAT
HE/SHE/ THEY EXECUTED THE SAME IN HIS/HER/ THEIR AUTHORIZED CAPACITY(IES), AND THAT BY
HIS/HER/ THEIR SIGNATURE(S) ON THE INSTRUMENT, THE PERSON(S), OR ENTITY UPON BEHALF OF
WHICH THE PERSON(S) ACTED, EXECUTED THE INSTRUMENT.

WITNESS MY HAND:

SIGNATURE  MY PRINCIPAL PLACE OF BUSINESS IS
NOTARY PUBLIC IN AND FOR SAID STATE IN Orange COUNTY.
Rhonda Keiger Painter MY COMMISSION EXPIRES: 12/9/03
(NAME PRINTED)



STATE OF CALIFORNIA } SS
COUNTY OF ORANGE }


ON March 15, 2002, BEFORE ME, Tina T. Baker, Notary Public, PERSONALLY
APPEARED Donald T. Stahlin AND Stephen C. Schmeck, PERSONALLY
KNOWN TO ME (OR PROVED TO ME ON THE BASIS OF SATISFACTORY EVIDENCE) TO BE THE PERSON(S)
WHOSE NAME(S) IS/ARE SUBSCRIBED TO THE WITHIN INSTRUMENT AND ACKNOWLEDGED TO ME THAT
HE/SHE/ THEY EXECUTED THE SAME IN HIS/HER/ THEIR AUTHORIZED CAPACITY(IES), AND THAT BY
HIS/HER/ THEIR SIGNATURE(S) ON THE INSTRUMENT, THE PERSON(S), OR ENTITY UPON BEHALF OF
WHICH THE PERSON(S) ACTED, EXECUTED THE INSTRUMENT.

WITNESS MY HAND:

SIGNATURE  MY PRINCIPAL PLACE OF BUSINESS IS
NOTARY PUBLIC IN AND FOR SAID STATE IN Orange COUNTY.
Tina T. Baker MY COMMISSION EXPIRES: 4/29/2014
(NAME PRINTED)

SURVEYOR'S STATEMENT:

THIS MAP WAS PREPARED BY ME OR UNDER MY DIRECTION AND IS BASED UPON A FIELD SURVEY IN CONFORMANCE WITH THE REQUIREMENTS OF THE SUBDIVISION MAP ACT AND LOCAL ORDINANCE AT THE REQUEST OF CENTEX HOMES IN NOVEMBER, 2001. I HEREBY STATE THAT ALL MONUMENTS ARE OF THE CHARACTER AND OCCUPY THE POSITIONS INDICATED, OR THAT THEY WILL BE SET IN SUCH POSITIONS; AND THAT SAID MONUMENTS ARE SUFFICIENT TO ENABLE THE SURVEY TO BE RETRACED. I HEREBY STATE THAT THIS FINAL MAP SUBSTANTIALLY CONFORMS TO THE CONDITIONALLY APPROVED TENTATIVE MAP.

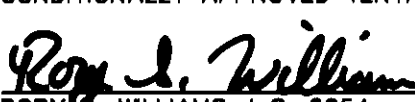
 3/12/02
RORY S. WILLIAMS, L.S. 6654 DATE
LICENSE EXPIRES: 12/31/03



COUNTY SURVEYOR'S STATEMENT

I HEREBY STATE THAT I HAVE EXAMINED THIS MAP AND HAVE FOUND IT TO BE SUBSTANTIALLY IN CONFORMANCE WITH THE TENTATIVE MAP AS FILED WITH, AMENDED AND APPROVED BY THE ORANGE COUNTY SUBDIVISION COMMITTEE; THAT ALL PROVISIONS OF THE SUBDIVISION MAP ACT AND COUNTY SUBDIVISION REGULATIONS HAVE BEEN COMPLIED WITH AND I AM SATISFIED SAID MAP IS TECHNICALLY CORRECT.

DATED THIS 7TH DAY OF August, 2002.

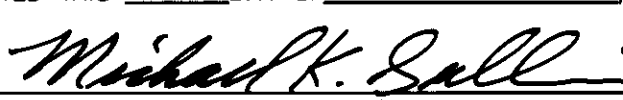
JOHN CANAS, COUNTY SURVEYOR
LS 4408, EXPIRATION DATE: 9-30-05 BY: MICHAEL K. SULLIVAN, DEPUTY
LS 6254 EXPIRES 6/30/06



COUNTY TREASURER-TAX COLLECTOR'S CERTIFICATE:

STATE OF CALIFORNIA } SS
COUNTY OF ORANGE }

I HEREBY CERTIFY THAT ACCORDING TO THE RECORDS OF MY OFFICE THERE ARE NO LIENS AGAINST THE LAND COVERED BY THIS MAP OR ANY PART THEREOF FOR UNPAID STATE, COUNTY, MUNICIPAL OR LOCAL TAXES OR SPECIAL ASSESSMENTS COLLECTED AS TAXES, EXCEPT TAXES OR SPECIAL ASSESSMENTS COLLECTED AS TAXES NOT YET PAYABLE.

AND DO CERTIFY TO THE RECORDER OF ORANGE COUNTY THAT THE PROVISIONS OF THE SUBDIVISION MAP ACT HAVE BEEN COMPLIED WITH REGARDING DEPOSITS TO SECURE PAYMENT OF TAXES OR SPECIAL ASSESSMENTS COLLECTED AS TAXES ON THE LAND COVERED BY THIS MAP.

DATED THIS 22nd DAY OF July, 2002.

JOHN M.W. MOORLACH BY: 
COUNTY TREASURER-TAX COLLECTOR DEPUTY TREASURER-TAX COLLECTOR


CLERK OF THE BOARD OF SUPERVISORS' CERTIFICATE:

STATE OF CALIFORNIA } SS
COUNTY OF ORANGE }

I HEREBY CERTIFY THAT THIS MAP WAS PRESENTED FOR APPROVAL TO THE BOARD OF SUPERVISORS OF THE COUNTY OF ORANGE AT REGULAR MEETING THEREOF HELD ON THE 7th DAY OF August, 2002, AND THAT THEREUPON SAID BOARD DID, BY AN ORDER DULY PASSED AND ENTERED, APPROVE SAID MAP AND DID ACCEPT ON BEHALF OF THE PUBLIC, SUBJECT TO IMPROVEMENTS, THE DEDICATION FOR STREET PURPOSES: ST. BRIDE WAY, ST. GILES COURT, ST. IVES WAY, ST. JUST AVENUE AND ST. STEVEN COURT.


AND DID ALSO APPROVE SAID MAP PURSUANT TO THE PROVISIONS OF SECTION 66436 (a)(3)(A) OF THE SUBDIVISION MAP ACT.

DATED THIS 20th DAY OF August, 2002.

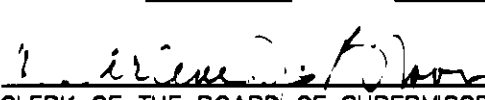
CLERK OF THE BOARD OF SUPERVISORS
DARLENE J. BLOOM

CERTIFICATE OF ACCEPTANCE - SANTA MARGARITA WATER DISTRICT

THE UNDERSIGNED, BEING THE DULY APPOINTED AGENT OF THE SANTA MARGARITA WATER DISTRICT, A PUBLIC CORPORATION IN ORANGE COUNTY, CALIFORNIA, PURSUANT TO ITS RESOLUTION NO. 88-10-2, DOES HEREBY ACCEPT ON BEHALF OF SAID DISTRICT, THE PIPELINE EASEMENT FOR WATER, SEWER AND ACCESS PURPOSES AS DEDICATED AND SHOWN ON THIS TRACT MAP, BY AND BETWEEN THE SANTA MARGARITA WATER DISTRICT AND CENTEX HOMES, A NEVADA GENERAL PARTNERSHIP, AND DOES HEREBY CERTIFY THAT THE GRANTEE CONSENTS TO THE RECORDATION OF SAID TRACT MAP.

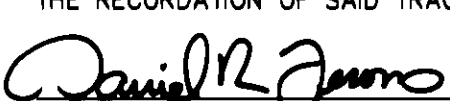
DANIEL R. FERONS, CHIEF ENGINEER
SANTA MARGARITA WATER DISTRICT

NOTARY ACKNOWLEDGMENT - SANTA MARGARITA WATER DISTRICT

STATE OF CALIFORNIA } SS
COUNTY OF ORANGE }

ON April 9, 2002, BEFORE ME, ANDREA M. EVANS, Notary Public, PERSONALLY
APPEARED DANIEL R. FERONS, PERSONALLY KNOWN TO ME (OR PROVED TO ME ON THE BASIS
OF SATISFACTORY EVIDENCE) TO BE THE PERSON WHOSE NAME IS SUBSCRIBED TO THE WITHIN
INSTRUMENT AND ACKNOWLEDGED TO ME THAT HE EXECUTED THE SAME IN HIS AUTHORIZED
CAPACITY, AND THAT BY HIS SIGNATURE ON THE INSTRUMENT THE PERSON, OR ENTITY UPON
BEHALF OF WHICH THE PERSON ACTED, EXECUTED THE INSTRUMENT.

WITNESS MY HAND:

SIGNATURE  MY PRINCIPAL PLACE OF BUSINESS IS
NOTARY PUBLIC IN AND FOR SAID STATE IN Orange COUNTY.
ANDREA M. EVANS MY COMMISSION EXPIRES: 4/8/04
(NAME PRINTED)

SIGNATURE OMISSIONS:

PURSUANT TO THE PROVISIONS OF SECTION 66436 (a)(3)(C) OF THE SUBDIVISION MAP ACT, THE FOLLOWING SIGNATURES HAVE BEEN OMITTED:

LADERA DEVELOPMENT COMPANY, L.L.C., HOLDER OF OIL, GAS AND MINERAL RIGHTS RECORDED AS INSTRUMENT NO. 19960624029 OF OFFICIAL RECORDS.

DMB LADERA, LLC, HOLDER OF EASEMENTS FOR PUBLIC UTILITIES, SURFACE RUNOFF, ROADS STREETS AND TRAILS, RECORDED AS INSTRUMENT NO. 20020666740 OF OFFICIAL RECORDS. (THE EXACT LOCATION AND EXTENT OF SAID EASEMENT IS NOT DISCLOSED OF RECORD.)

SHEET 2 OF 6 SHEETS
SCALE: 1" = 100'
54 NUMBERED LOTS AND
LOTS A, B AND C
ACREAGE: 9.906 ACRES
(ALL OF TENTATIVE
TRACT NO. 16243)

BASIS OF BEARINGS:

THE BEARINGS SHOWN HEREON ARE BASED ON THE BEARING BETWEEN
O.C.S. HORIZONTAL CONTROL STATION GPS NO. 1417 AND STATION
GPS NO. 1448 BEING N10°48'13"E PER RECORDS ON FILE IN THE
OFFICE OF THE ORANGE COUNTY SURVEYOR.

DATUM STATEMENT:

COORDINATES SHOWN ARE BASED ON THE CALIFORNIA COORDINATE SYSTEM (CCS83). ZONE
11N, 1983 NAD, (1981.35 EPOCH OCS GPS ADJUSTMENT). ALL DISTANCES SHOWN ARE GROUND,
UNLESS OTHERWISE NOTED. TO OBTAIN GRID DISTANCE, MULTIPLY GROUND DISTANCE BY
0.999944295.

NOTES:

LOTS B AND C ARE FOR LANDSCAPING PURPOSES.

LOT A IS FOR RECREATION & POCKET PARK PURPOSES.

THIS PROPERTY IS IN A SPECIAL FIRE PROTECTION AREA. TOTAL EXCLUSION GRANTED FOR THIS
TRACT.

ALL RESIDENTIAL STRUCTURES EXCEEDING 5,500 SQUARE FEET (PER AMENDMENT) AND ALL
STRUCTURES EXCEEDING FIRE DEPARTMENT ACCESS REQUIREMENTS SHALL BE PROTECTED BY
AN AUTOMATIC FIRE SPRINKLER SYSTEM IN A MANNER MEETING THE APPROVAL OF THE FIRE
CHIEF.

EASEMENT NOTE:

Ⓐ INDICATES A PIPELINE EASEMENT FOR WATER, SEWER AND ACCESS
PURPOSES DEDICATED HEREON TO THE SANTA MARGARITA WATER
DISTRICT.

MONUMENT NOTES:

2" I.P. TAGGED L.S. 6654 OR LEAD, TACK & TAG L.S. 6654 OR NAIL & TAG L.S. 6654 OR
R" SAW STAMPED L.S. 6654 TO BE SET AT ALL TRACT BOUNDARY CORNERS WITHIN 90
DAYS AFTER ACCEPTANCE OF IMPROVEMENTS, UNLESS OTHERWISE NOTED.

1" I.P. TAGGED L.S. 6654 OR LEAD, TACK & TAG L.S. 6654 OR NAIL & TAG L.S. 6654 OR
R" SAW STAMPED L.S. 6654 TO BE SET AT ALL LOT CORNERS, EXCEPT LOT CORNERS
THAT ARE THE INTERSECTION OF STRAIGHT SIDE LOT LINES WITH STREET RIGHT OF WAY,
WITHIN 90 DAYS AFTER ACCEPTANCE OF IMPROVEMENTS, UNLESS OTHERWISE NOTED.

R" SAW STAMPED L.S. 6654 OR LEAD, TACK & TAG L.S. 6654 OR 1" I.P. TAGGED L.S.
6654 TO BE SET AT ALL STREET CENTERLINE POINTS OF CONTROL, WITHIN 90 DAYS AFTER
ACCEPTANCE OF IMPROVEMENTS, UNLESS OTHERWISE NOTED.

LEAD, TACK & TAG L.S. 6654 TO BE SET IN TOP OF CURB AT AN OFFSET ALONG FRONT
SIDE LOT LINES PRODUCED, IN LIEU OF AT FRONT LOT CORNERS, WITHIN 90 DAYS AFTER
ACCEPTANCE OF IMPROVEMENTS, UNLESS OTHERWISE NOTED. BEARING AND DISTANCE OF
PRODUCTION IS AS NOTED HEREON.

● INDICATES FOUND MONUMENT OR LOCATION OF MONUMENT TO BE SET, AS NOTED.

■ INDICATES NOTHING TO BE SET.

Pg. INDICATES BEARING AND DISTANCE OF LOT LINE PRODUCTION FROM LOT CORNER TO
MONUMENT.

1 INDICATES LOCATION OF 2" I.P. TAGGED "P.L.S. 5557" OR SPIKE & WASHER STAMPED
"P.L.S. 5557" OR LEAD, TACK & TAG "P.L.S. 5557" TO BE SET PER TRACT NO. 16235,
M.M. 825/30-39.

2 INDICATES LOCATION OF 1" I.P. TAGGED "P.L.S. 5557" OR SPIKE & WASHER STAMPED
"P.L.S. 5557" OR LEAD, TACK & TAG "P.L.S. 5557" TO BE SET PER TRACT NO. 16234,
M.M. 825/19-29.

3 INDICATES LOCATION OF 1" I.P. TAGGED "P.L.S. 5557" OR SPIKE & WASHER STAMPED
"P.L.S. 5557" OR LEAD, TACK & TAG "P.L.S. 5557" TO BE SET PER TRACT NO. 16235,
M.M. 825/30-39.


4 INDICATES SET 2" I.P. TAGGED L.S. 6654 PRIOR TO MAP RECORDED.

TRACT NO. 16243
IN UNINCORPORATED TERRITORY OF THE COUNTY OF ORANGE,
STATE OF CALIFORNIA

HUNSAKER AND ASSOCIATES IRVINE, INC.

RORY S. WILLIAMS, L.S. 6654

DATE OF SURVEY: NOVEMBER, 2001

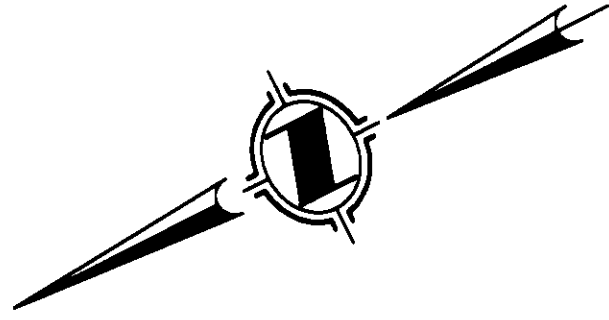

SHEET INDEX AND GPS CONTROL MAP

⬡ INDICATES SHEET NUMBER


SHEET 3 OF 6 SHEETS
SCALE: T = 30'
54 NUMBERED LOTS AND
LOTS A, B AND C
ACREAGE: 9.906 ACRES
(ALL OF TENTATIVE
TRACT NO. 16243)

TRACT NO. 16243

IN UNINCORPORATED TERRITORY OF THE COUNTY OF ORANGE,
STATE OF CALIFORNIA

HUNSAKER AND ASSOCIATES IRVINE, INC.
RORY S. WILLIAMS, L.S. 8854
DATE OF SURVEY: NOVEMBER, 2001
SEE SHEET 39

SEE SHEET 2 FOR BASIS OF BEARINGS, DATUM
STATEMENT, MONUMENT NOTES, EASEMENT NOTES,
NOTES AND SHEET INDEX AND GPS CONTROL MAP.

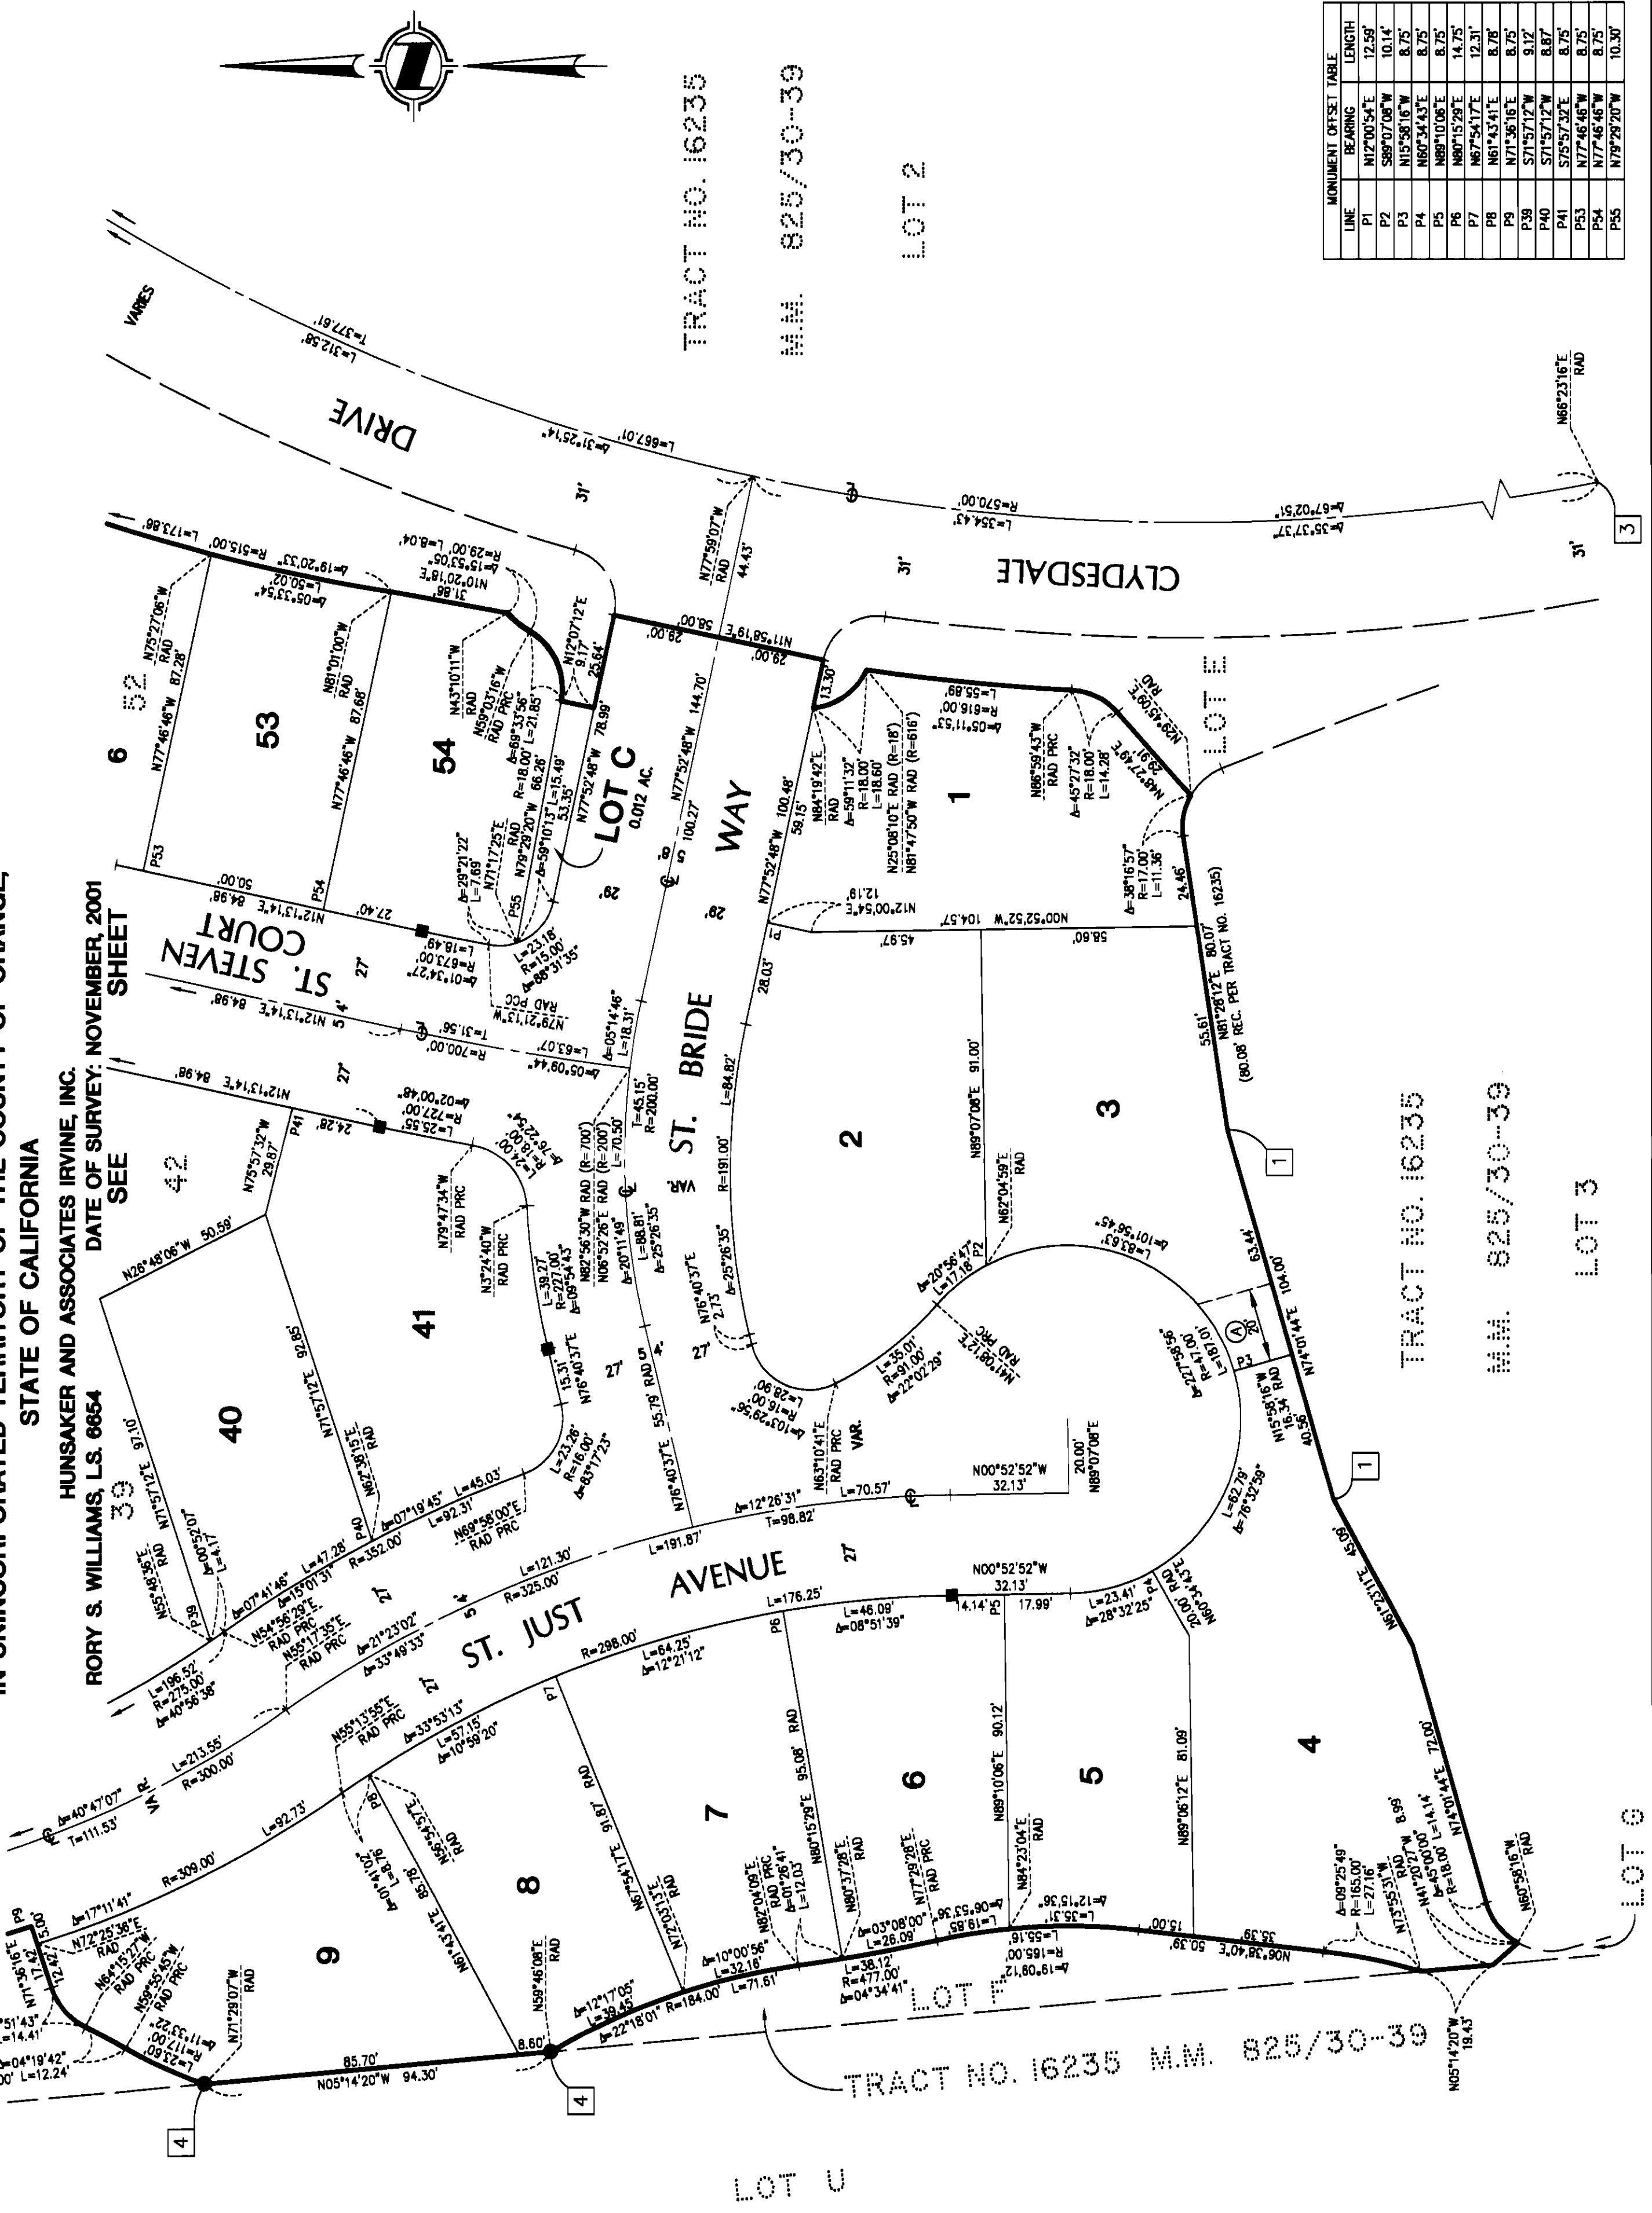

LINE	BEARING	LENGTH
P1	N12°00'54"E	12.59'
P2	S89°07'08"W	10.14'
P3	N15°58'16"W	8.75'
P4	N60°34'43"E	8.75'
P5	N89°10'08"E	8.75'
P6	N80°15'29"E	14.25'
P7	N87°54'17"E	12.31'
P8	N61°43'41"E	8.78'
P9	N71°36'16"E	8.75'
P38	S71°57'12"W	9.12'
P40	S71°57'12"W	8.87'
P41	S75°57'32"E	8.75'
P53	N77°46'46"W	8.75'
P54	N77°46'46"W	8.75'
P55	N79°29'20"W	10.50'

TRACT NO. 16203

M.M. 826/8-20

TRACT NO. 16235

M.M. 825/30-39

LOT 3

LOT 2

TRACT NO. 16235

M.M. 825/30-39


SHEET 4 OF 6 SHEETS
SCALE: 1" = 30'
54 NUMBERED LOTS AND
LOTS A, B AND C
ACREAGE: 9.906 ACRES
(ALL OF TENTATIVE
TRACT NO. 16243)

TRACT NO. 16243

IN UNINCORPORATED TERRITORY OF THE COUNTY OF ORANGE,
STATE OF CALIFORNIA

HUNSAKER AND ASSOCIATES IRVINE, INC.
RORY S. WILLIAMS, L.S. 8654 DATE OF SURVEY: NOVEMBER, 2001

SEE SHEET 2 FOR BASIS OF BEARINGS, DATUM
STATEMENT, MONUMENT NOTES, EASEMENT NOTES,
NOTES AND SHEET INDEX AND GPS CONTROL MAP.

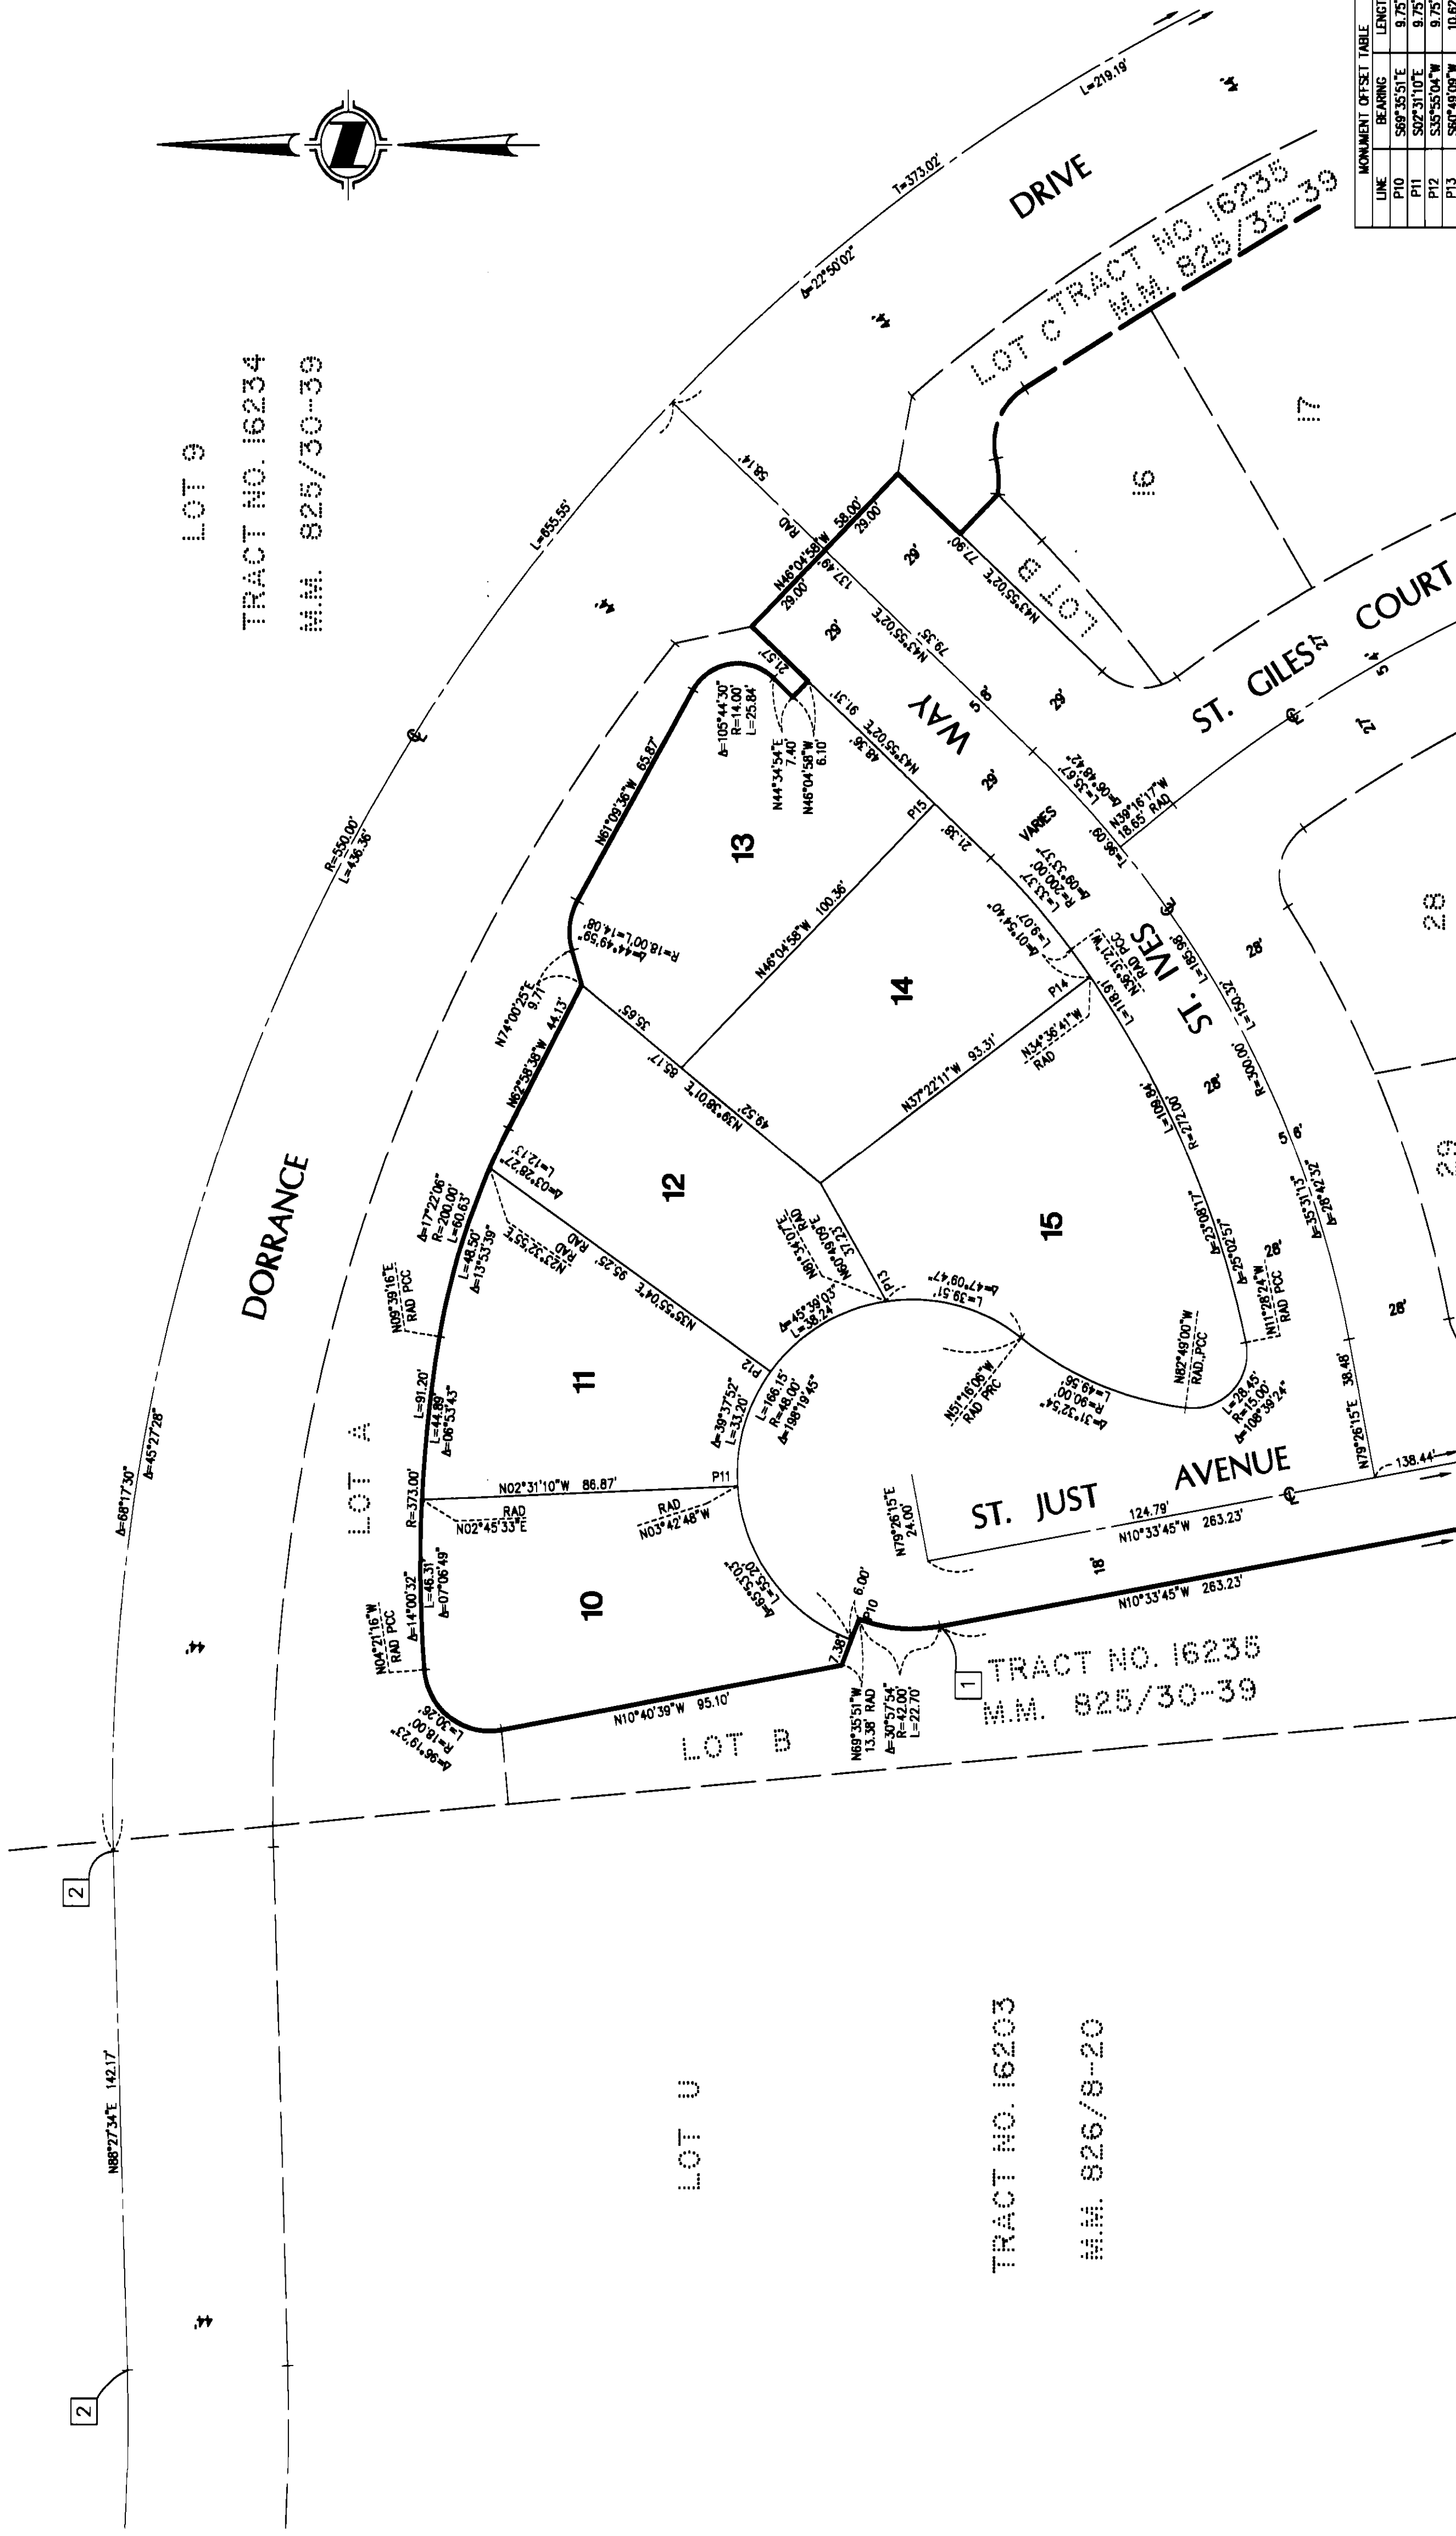

MONUMENT OFFSET TABLE		
LINE	BEARING	LENGTH
P10	S89°35'51"E	9.75'
P11	S02°31'10"E	9.75'
P12	S35°55'04"W	9.75'
P13	S80°49'09"W	10.62'
P14	S37°22'11"E	9.76'
P15	S46°04'56"E	9.75'

TRACT NO. 16203

M.M. 826/8-20

TRACT NO. 16235
M.M. 825/30-39

SEE SHEET 29

SEE SHEET 28


SHEET 5 OF 6 SHEETS
SCALE: T = 30'
54 NUMBERED LOTS AND
LOTS A, B AND C
ACREAGE: 9.905 ACRES
(ALL OF TENTATIVE
TRACT NO. 16243)

TRACT NO. 16243

IN UNINCORPORATED TERRITORY OF THE COUNTY OF ORANGE,
STATE OF CALIFORNIA

HUNSAKER AND ASSOCIATES IRVINE, INC.
RORY S. WILLIAMS, L.S. 8654
DATE OF SURVEY: NOVEMBER, 2001

LINE	BEARING	LENGTH
P16	S89°45'16"W	8.75'
P17	S86°19'28"W	8.75'
P18	S72°53'59"W	8.75'
P19	S72°53'59"W	8.75'
P20	S72°53'59"W	9.29'
P21	N72°01'21"W	8.75'
P22	N63°28'50"W	8.99'
P24	N71°13'19"E	10.89'
P25	N71°13'19"E	10.89'
P26	N71°13'19"E	8.84'
P27	N71°13'19"E	8.75'
P28	N71°13'19"E	8.84'

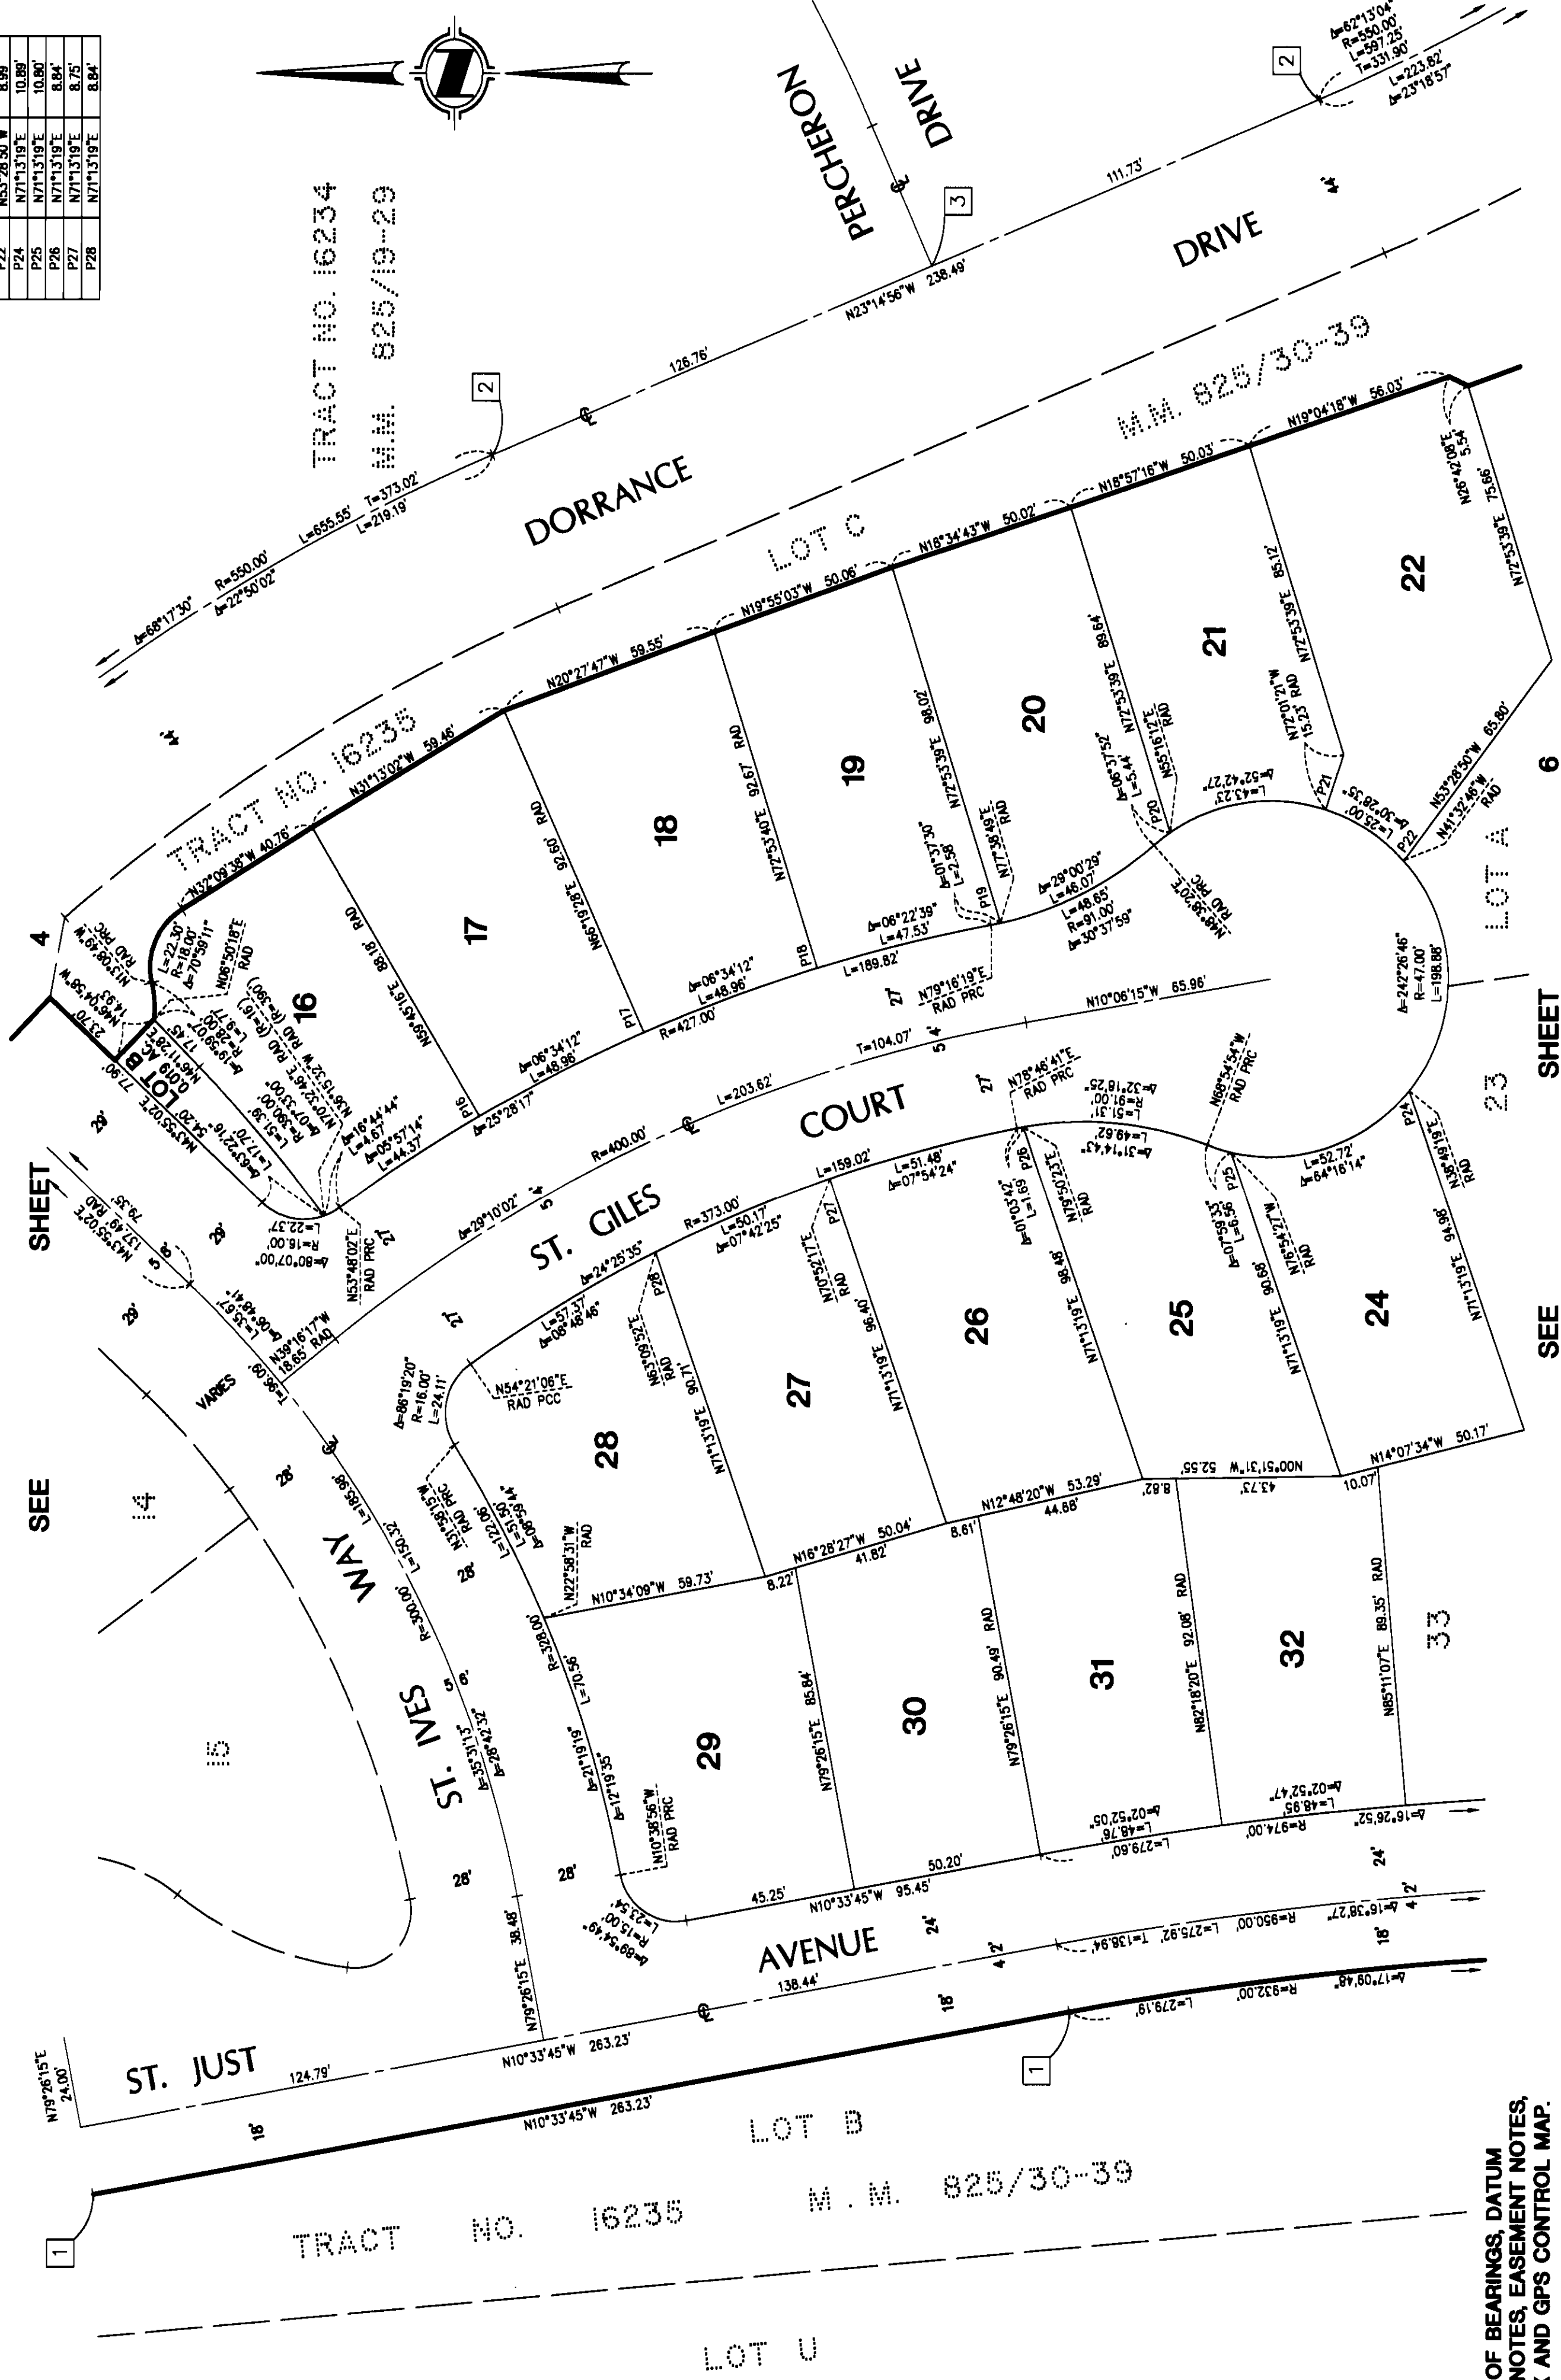


SEE SHEET 2 FOR BASIS OF BEARINGS, DATUM
STATEMENT, MONUMENT NOTES, EASEMENT NOTES,
NOTES AND SHEET INDEX AND GPS CONTROL MAP.

SHEET 6 OF 6 SHEETS
SCALE: T = 30'
54 NUMBERED LOTS AND
LOTS A, B AND C
ACREAGE: 9.906 ACRES
(ALL OF TENTATIVE
TRACT NO. 16243)

TRACT NO. 16243

IN UNINCORPORATED TERRITORY OF THE COUNTY OF ORANGE,
STATE OF CALIFORNIA

HUNSAKER AND ASSOCIATES IRVINE, INC.
RORY S. WILLIAMS, L.S. 8654 DATE OF SURVEY: NOVEMBER, 2001

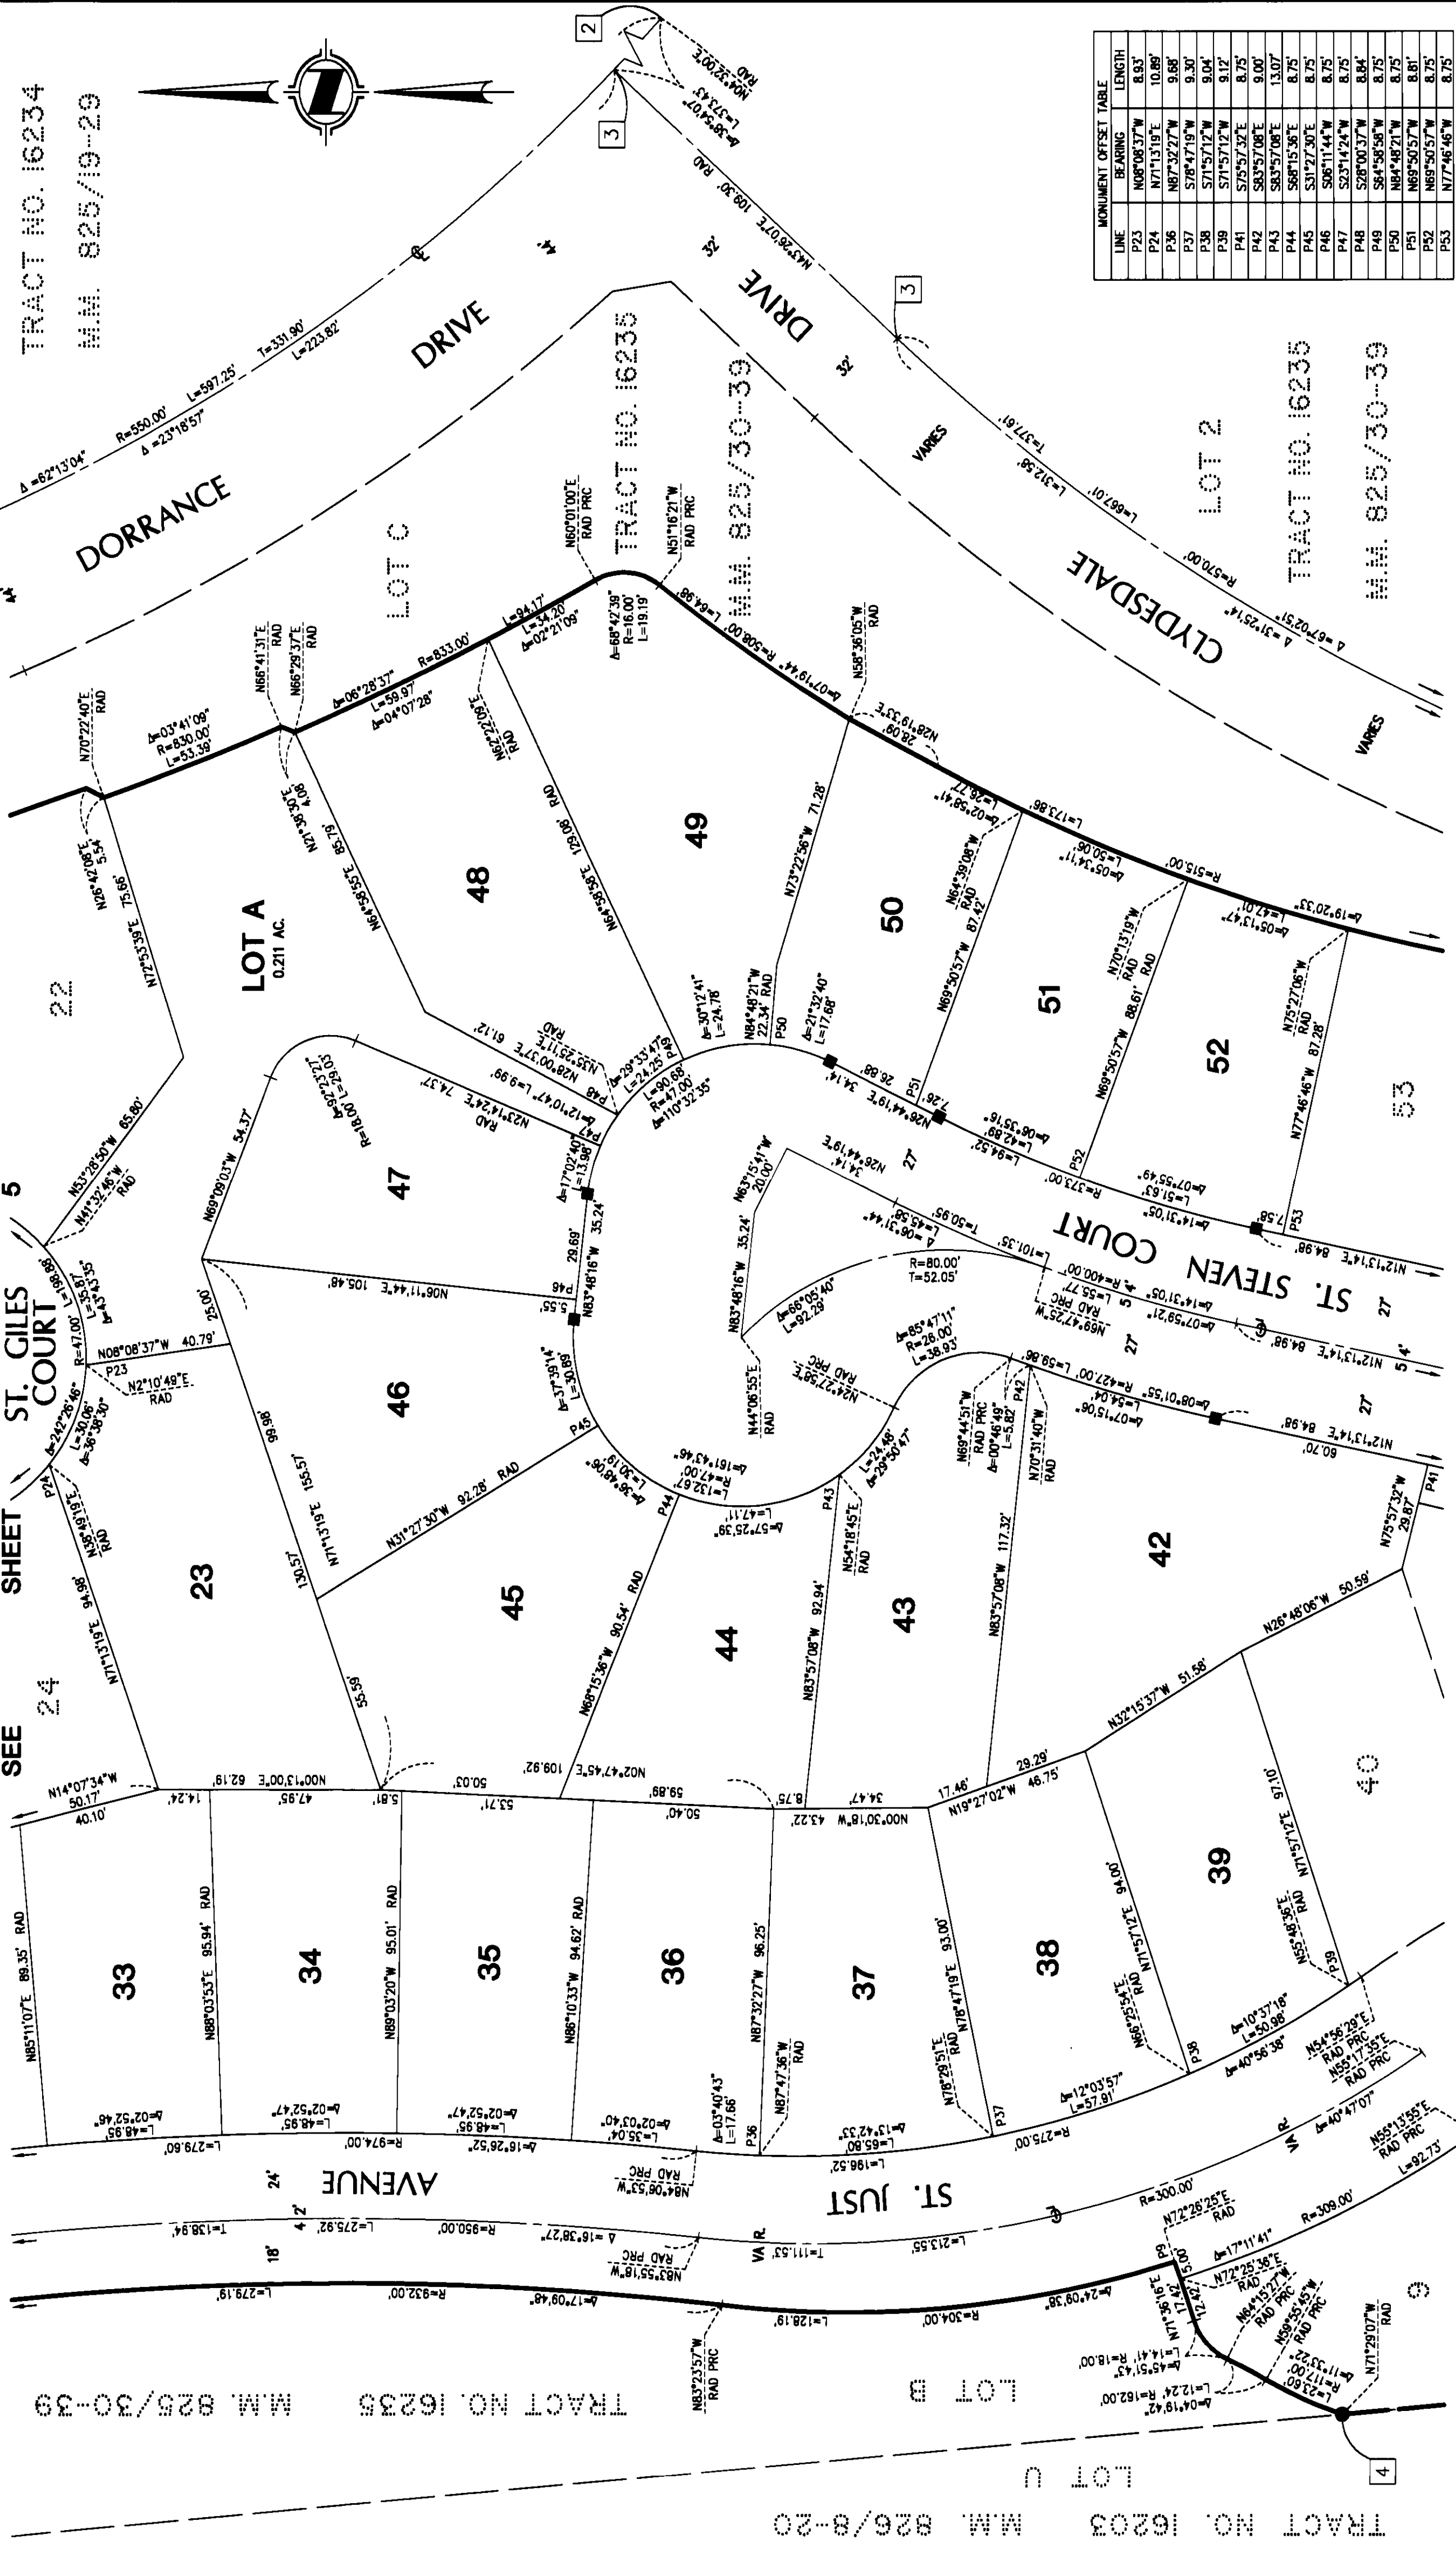

LINE	BEARING	LENGTH
P23	N08°08'37"W	8.93'
P24	N71°13'19"E	10.89'
P36	N87°32'27"W	9.68'
P37	S78°47'19"W	8.30'
P38	S71°57'12"W	9.04'
P39	S71°57'12"W	9.12'
P41	S75°57'32"E	8.75'
P42	S83°57'08"E	9.00'
P43	S83°57'08"E	13.07'
P44	S88°15'36"E	8.75'
P45	S31°27'30"E	8.75'
P46	S06°11'44"W	8.75'
P47	S23°14'24"W	8.75'
P48	S84°58'58"W	8.84'
P50	N84°48'21"W	8.75'
P51	N69°50'57"W	8.81'
P52	N69°50'57"W	8.75'
P53	N77°46'46"W	8.75'