

842 45

SHEET 1 OF 5 SHEETS

TRACT NO. 16246

ALL OF VESTING
TENTATIVE TRACT NO. 16246

IN THE UNINCORPORATED TERRITORY OF ORANGE COUNTY, CALIFORNIA
BEING A SUBDIVISION OF LOT 4 OF TRACT NO. 16235 FILED IN BOOK 825, PAGES 30
THROUGH 39 OF MISCELLANEOUS MAPS, RECORDS OF ORANGE COUNTY, CALIFORNIA.

DATE OF SURVEY:
DECEMBER 2001

FEBRUARY 2002

JAMES F. GILLEN, L.S. 5557

HUITT-ZOLIARS

64 NUMBERED LOTS AND 5 LETTERED LOTS

15.928 ACRES

ACCEPTED AND FILED AT THE
REQUEST OF
FIRST AMERICAN TITLE INSURANCE CO.

DATE MAY 2, 2003
TIME 01:16 PM FEE \$ 15.00
INSTRUMENT NO. 200300499728
BOOK 842 PAGE 45-49 m/m
TOM DALY
COUNTY CLERK-RECORDER

BY [Signature]
DEPUTY

OWNERSHIP CERTIFICATE:

WE, THE UNDERSIGNED, BEING ALL PARTIES HAVING ANY RECORD TITLE INTEREST IN THE LAND COVERED BY THIS MAP, DO HEREBY CONSENT TO THE PREPARATION AND RECORDATION OF SAID MAP, AS SHOWN WITHIN THE DISTINCTIVE BORDER LINE. WE ALSO HEREBY DEDICATE TO THE PUBLIC FOR STREET PURPOSES: HALLOCREST DRIVE, CURTIS LANE, TALBOTT COURT, CLYDESDALE DRIVE, AND BRYANT COURT.

WE ALSO HEREBY DEDICATE TO THE SANTA MARGARITA WATER DISTRICT THE EASEMENTS FOR SEWER, WATER AND ACCESS PURPOSES AS SHOWN ON SAID MAP, WHICH EASEMENT SHALL BE SUBJECT TO THE SAME TERMS AND CONDITIONS AS ARE SHOWN IN THAT CERTAIN EASEMENT RECORDED OCTOBER 6, 1980 IN BOOK 13776, PAGE 341, OF OFFICIAL RECORDS, COUNTY OF ORANGE.

STANDARD PACIFIC CORP., A DELAWARE CORPORATION.

BY: [Signature]
PRINT NAME: Andrew Parnes
PRINT TITLE: SVP

BY: [Signature]
PRINT NAME: Lloyd McKibbin
PRINT TITLE: Treasurer

DMB LADERA, L.L.C. A DELAWARE LIMITED LIABILITY COMPANY, BENEFICIARY UNDER A DEED OF TRUST RECORDED APRIL 1, 2002 AS INSTRUMENT NO. 20020271761 OF OFFICIAL RECORDS.

BY: RANCHO MISSION VIEJO, L.L.C., A DELAWARE LIMITED LIABILITY COMPANY, ITS AUTHORIZED AGENT AND MANAGER.

BY: [Signature]
PRINT NAME: DONALD T. STRAHLEN
PRINT TITLE: DIRECTOR

BY: [Signature]
PRINT NAME: Donald L. Votra
PRINT TITLE: Chief Operating Officer

CERTIFICATE OF ACCEPTANCE

THE UNDERSIGNED, BEING THE DULY APPOINTED AGENT OF THE SANTA MARGARITA WATER DISTRICT, A PUBLIC CORPORATION OF ORANGE COUNTY, CALIFORNIA, PURSUANT TO ITS RESOLUTION NO. 88-10-2, DOES HEREBY ACCEPT ON BEHALF OF SAID DISTRICT THE EASEMENTS FOR SEWER, WATER AND ACCESS PURPOSES, AS DEDICATED AND AS SHOWN ON THIS TRACT MAP, BY AND BETWEEN THE SANTA MARGARITA WATER DISTRICT AND STANDARD PACIFIC CORP. AND DOES HEREBY CERTIFY THAT THE GRANTEE CONSENTS TO THE RECORDATION OF SAID TRACT.

[Signature]
DANIEL R. FERONS, CHIEF ENGINEER
SANTA MARGARITA WATER DISTRICT.

AUTOMATIC FIRE SPRINKLER NOTE:

ALL COMMERCIAL STRUCTURES GREATER THAN 6,000 SQUARE FEET; ALL MULTIFAMILY RESIDENTIAL STRUCTURES; ALL SINGLE-FAMILY STRUCTURES EXCEEDING 5,500 SQUARE FEET, AND ALL STRUCTURES EXCEEDING FIRE DEPARTMENT ACCESS REQUIREMENTS SHALL BE PROTECTED BY AN AUTOMATIC SPRINKLER SYSTEM. LOTS 1, 2, 19, 24-29, **37-42, 44, 45, AND 52 WILL REQUIRE AUTOMATIC FIRE SPRINKLER SYSTEMS PER OCA.**

HIGH FIRE HAZARD AREA NOTE:

THE LOTS SHOWN ON THIS MAP ARE IN A HIGH FIRE HAZARD AREA DUE TO WILD LAND EXPOSURE BASED ON STATE SRA MAPS.

THE PROPERTY SHOWN ON THIS MAP IS "TOTALLY EXCLUDED" FROM A "SPECIAL FIRE PROTECTION AREA." THERE ARE NO LOTS IN THIS TRACT THAT ARE SUBJECT TO CONSTRUCTION FEATURES OF THE ORANGE COUNTY ORDINANCE 3960.

NOTES:

PROPERTY MAY BE SUBJECT TO IMPACTS FROM THE FOOTHILL/EASTERN TRANSPORTATION CORRIDOR.

SEE SHEET 2 FOR NOTARY ACKNOWLEDGMENTS AND SIGNATURE OMISSIONS.

SURVEYOR'S STATEMENT:

THIS MAP WAS PREPARED BY ME OR UNDER MY DIRECTION AND IS BASED UPON A FIELD SURVEY IN CONFORMANCE WITH THE REQUIREMENTS OF THE SUBDIVISION MAP ACT AND LOCAL ORDINANCE AT THE REQUEST OF STANDARD PACIFIC CORP., ON DECEMBER 2001. I HEREBY STATE THAT ALL MONUMENTS ARE OF THE CHARACTER AND OCCUPY THE POSITIONS INDICATED, OR THAT THEY WILL BE SET IN SUCH POSITIONS; AND THAT SAID MONUMENTS ARE SUFFICIENT TO ENABLE THE SURVEY TO BE RETRACED. I HEREBY STATE THAT THIS FINAL MAP SUBSTANTIALLY CONFORMS TO THE CONDITIONALLY APPROVED TENTATIVE MAP.



[Signature]
JAMES F. GILLEN
L.S. 5557
EXPIRATION DATE: 9/30/05

COUNTY SURVEYOR'S STATEMENT:

I HEREBY STATE THAT I HAVE EXAMINED THIS MAP AND HAVE FOUND IT TO BE SUBSTANTIALLY IN CONFORMANCE WITH THE TENTATIVE MAP AS FILED WITH, AMENDED AND APPROVED BY THE ORANGE COUNTY SUBDIVISION COMMITTEE; THAT ALL PROVISIONS OF THE SUBDIVISION MAP ACT AND COUNTY SUBDIVISION REGULATIONS HAVE BEEN COMPLIED WITH AND I AM SATISFIED SAID MAP IS TECHNICALLY CORRECT.

DATED THIS 10TH DAY OF APRIL, 2003

[Signature]
JOHN CANAS, COUNTY SURVEYOR
LS 4408 EXPIRATION DATE: 09-30-05

BY: MICHAEL K. SULLIVAN, DEPUTY
LS 6254 EXPIRES 6/30/06



COUNTY TREASURER-TAX COLLECTOR'S CERTIFICATE:

STATE OF CALIFORNIA)
COUNTY OF ORANGE)

I HEREBY CERTIFY THAT ACCORDING TO THE RECORDS OF MY OFFICE THERE ARE NO LIENS AGAINST THE LAND COVERED BY THIS MAP OR ANY PART THEREOF FOR UNPAID STATE, COUNTY, MUNICIPAL OR LOCAL TAXES OR SPECIAL ASSESSMENTS COLLECTED AS TAXES, EXCEPT TAXES OR SPECIAL ASSESSMENTS COLLECTED AS TAXES NOT YET PAYABLE.

AND DO ALSO HEREBY CERTIFY TO THE RECORDER OF ORANGE COUNTY THAT THE PROVISIONS OF THE SUBDIVISION MAP ACT HAVE BEEN COMPLIED WITH REGARDING DEPOSITS TO SECURE THE PAYMENT OF TAXES OR SPECIAL ASSESSMENTS COLLECTED AS TAXES ON THE LAND COVERED BY THIS MAP.

DATED THIS 7TH DAY OF March, 2003

JOHN M.W. MOORLACH
COUNTY TREASURER-TAX COLLECTOR

BY: [Signature]
DEPUTY TREASURER-TAX COLLECTOR


CLERK OF THE BOARD OF SUPERVISORS' CERTIFICATE:

STATE OF CALIFORNIA)
COUNTY OF ORANGE)

I HEREBY CERTIFY THAT THIS MAP WAS PRESENTED FOR APPROVAL TO THE BOARD OF SUPERVISORS OF ORANGE COUNTY AT A REGULAR MEETING THEREOF HELD ON THE 29TH DAY OF April, 2003, AND THAT THEREUPON SAID BOARD DID, BY AN ORDER DULY PASSED AND ENTERED, APPROVE SAID MAP AND DID ACCEPT ON BEHALF OF THE PUBLIC, SUBJECT TO IMPROVEMENTS: THE DEDICATION FOR STREET PURPOSES OF: HALLOCREST DRIVE, CURTIS LANE, TALBOTT COURT, CLYDESDALE DRIVE, AND BRYANT COURT.

DATED THIS 29TH DAY OF April, 2003

[Signature]
DARLENE J. BLOOM
CLERK OF THE BOARD OF SUPERVISORS

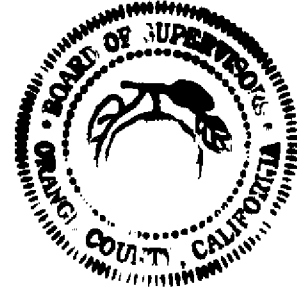

842 45

842 46

SHEET 2 OF 5 SHEETS

TRACT NO. 16246

ALL OF VESTING TENTATIVE
TRACT NO. 16246

IN THE UNINCORPORATED TERRITORY OF ORANGE COUNTY, CALIFORNIA

DATE OF SURVEY:
DECEMBER 2001

FEBRUARY 2002

JAMES F. GILLEN, L.S. 5557

HUITT-ZOLIARS

64 NUMBERED LOTS AND 5 LETTERED LOTS

15.928 ACRES

STATE OF CALIFORNIA)
COUNTY OF ORANGE)

ON THIS 27th DAY OF August, 2002, BEFORE ME,
Kathleen M. Villari, A NOTARY PUBLIC IN AND FOR SAID STATE,
PERSONALLY APPEARED James F. Gillen AND
James F. Gillen, PERSONALLY KNOWN TO ME OR PROVED TO ME
ON THE BASIS OF SATISFACTORY EVIDENCE TO BE THE PERSONS WHOSE NAMES
ARE SUBSCRIBED TO THE WITHIN INSTRUMENT AND ACKNOWLEDGED TO ME THAT
THEY EXECUTED THE SAME IN THEIR AUTHORIZED CAPACITIES, AND THAT BY THEIR
SIGNATURES ON THE INSTRUMENT THE PERSONS, OR THE ENTITY UPON BEHALF
OF WHICH THE PERSONS ACTED, EXECUTED THE INSTRUMENT.

WITNESS MY HAND: MY COMMISSION EXPIRES 8/10/2003
Kathleen M. Villari MY PRINCIPAL PLACE OF BUSINESS
NOTARY PUBLIC IN AND FOR SAID STATE IS IN Orange COUNTY.
KATHLEEN M. VILLARI
PRINT NAME

STATE OF CALIFORNIA)
COUNTY OF ORANGE)

ON THIS 27th DAY OF February, 2003, BEFORE ME,
Diana L. Binks, A NOTARY PUBLIC IN AND FOR SAID STATE,
PERSONALLY APPEARED Donald T. Stahl AND
Donald L. Vodra, PERSONALLY KNOWN TO ME OR PROVED TO ME
ON THE BASIS OF SATISFACTORY EVIDENCE TO BE THE PERSONS WHOSE NAMES
ARE SUBSCRIBED TO THE WITHIN INSTRUMENT AND ACKNOWLEDGED TO ME THAT
THEY EXECUTED THE SAME IN THEIR AUTHORIZED CAPACITIES, AND THAT BY THEIR
SIGNATURES ON THE INSTRUMENT THE PERSONS, OR THE ENTITY UPON BEHALF
OF WHICH THE PERSONS ACTED, EXECUTED THE INSTRUMENT.

WITNESS MY HAND: MY COMMISSION EXPIRES 12/12/06
Diana L. Binks MY PRINCIPAL PLACE OF BUSINESS
NOTARY PUBLIC IN AND FOR SAID STATE IS IN Orange COUNTY.
Diana L. Binks
PRINT NAME

SANTA MARGARITA WATER DISTRICT

STATE OF CALIFORNIA)
COUNTY OF ORANGE)

ON THIS 29th DAY OF AUGUST, 2002, BEFORE ME,
Andrea M. Evans, A NOTARY PUBLIC IN AND FOR SAID STATE,
PERSONALLY APPEARED Daniel R. Ferons PERSONALLY KNOWN TO ME
OR PROVED TO ME ON THE BASIS OF SATISFACTORY EVIDENCE TO BE THE
PERSON WHOSE NAME IS SUBSCRIBED TO THE WITHIN INSTRUMENT AND ACKNOWLEDGED
TO ME THAT HE EXECUTED THE SAME IN HIS AUTHORIZED CAPACITY, AND THAT
BY HIS SIGNATURE ON THE INSTRUMENT THE PERSON, OR THE ENTITY UPON BEHALF
OF WHICH THE PERSON ACTED, EXECUTED THE INSTRUMENT.

WITNESS MY HAND: MY COMMISSION EXPIRES 4/8/04
Andrea M. Evans MY PRINCIPAL PLACE OF BUSINESS
NOTARY PUBLIC IN AND FOR SAID STATE IS IN ORANGE COUNTY.
ANDREA M. EVANS
PRINT NAME

MONUMENT NOTES:

- INDICATES FOUND MONUMENT AS NOTED.
 - INDICATES FOUND 2" I.P. TAGGED "P.L.S. 5557" PER TRACT NO. 16235, M.M. 825 / 30-39.
 - INDICATES LOCATION OF 2" I.P. TAGGED "P.L.S. 5557" OR SPIKE & WASHER STAMPED "P.L.S. 5557" OR LEAD, TACK & TAG "P.L.S. 5557" TO BE SET PER TRACT NO. 16235, M.M. 825 / 30-39.
 - △ INDICATES LOCATION OF 1" I.P. TAGGED "P.L.S. 5557" OR SPIKE & WASHER STAMPED "P.L.S. 5557" OR LEAD, TACK & TAG "P.L.S. 5557" TO BE SET PER TRACT NO. 16235, M.M. 825/30-39.
 - INDICATES LOCATION OF 1" I.P. TAGGED "P.L.S. 5557" OR SPIKE & WASHER STAMPED "P.L.S. 5557" OR LEAD, TACK & TAG "P.L.S. 5557" TO BE SET WITHIN 90 DAYS AFTER ACCEPTANCE OF IMPROVEMENTS.
- 2" I.P. TAGGED "P.L.S. 5557" OR SPIKE & WASHER STAMPED "P.L.S. 5557" OR LEAD, TACK AND TAG "P.L.S. 5557" TO BE SET AT ALL TRACT BOUNDARY CORNERS, WITHIN 90 DAYS AFTER ACCEPTANCE OF IMPROVEMENTS, UNLESS OTHERWISE NOTED.
- 1" I.P. TAGGED "P.L.S. 5557" OR SPIKE & WASHER STAMPED "P.L.S. 5557" OR LEAD, TACK AND TAG "P.L.S. 5557" TO BE SET AT ALL INTERIOR LOT CORNERS, EXCEPT LOT CORNERS ABUTTING STREETS; LEAD, TACK & TAG "P.L.S. 5557" TO BE SET IN TOP OF CURB OR SIDEWALK ON A 8.75' OFFSET OR A 14.75' OFFSET ON SIDE LOT LINES PRODUCED FOR LOT CORNERS ABUTTING STREETS, WITHIN 90 DAYS AFTER ACCEPTANCE OF IMPROVEMENTS, UNLESS OTHERWISE NOTED.

NO MONUMENTATION TO BE SET AT BC'S AND EC'S OF STREET RIGHT OF WAY LINES, UNLESS OTHERWISE NOTED.

SIGNATURE OMISSIONS:

IN ACCORDANCE WITH THE PROVISIONS OF SECTION 66436(a) (3) OF THE SUBDIVISION MAP ACT, THE FOLLOWING SIGNATURE HAS BEEN OMITTED:


1. LADERA DEVELOPMENT COMPANY, L.L.C., HOLDER OF OIL, GAS, MINERAL, AND WATER RIGHTS RECORDED DECEMBER 10, 1996 AS INSTRUMENT NO. 19960624029 OF OFFICIAL RECORDS.
2. DMB LADERA, L.L.C., A DELAWARE LIMITED LIABILITY COMPANY, HOLDER OF EASEMENTS, RESERVED IN THE DEED RECORDED FEBRUARY 7, 2003 AS INSTRUMENT NO. 2003000149351 OF OFFICIAL RECORDS.

BASIS OF BEARINGS:

BEARINGS SHOWN HEREON ARE BASED ON THE SOUTHEASTERLY LINE OF LOT 4 BEING N35°57'41"E AS SHOWN ON TRACT NO. 16235, FILED IN BOOK 825, PAGES 30 THROUGH 39 OF MISCELLANEOUS MAPS, RECORDS OF ORANGE COUNTY, CALIFORNIA.

EASEMENT NOTE:

△ INDICATES EASEMENT FOR SEWER, WATER AND ACCESS PURPOSES DEDICATED TO THE SANTA MARGARITA WATER DISTRICT HEREON.

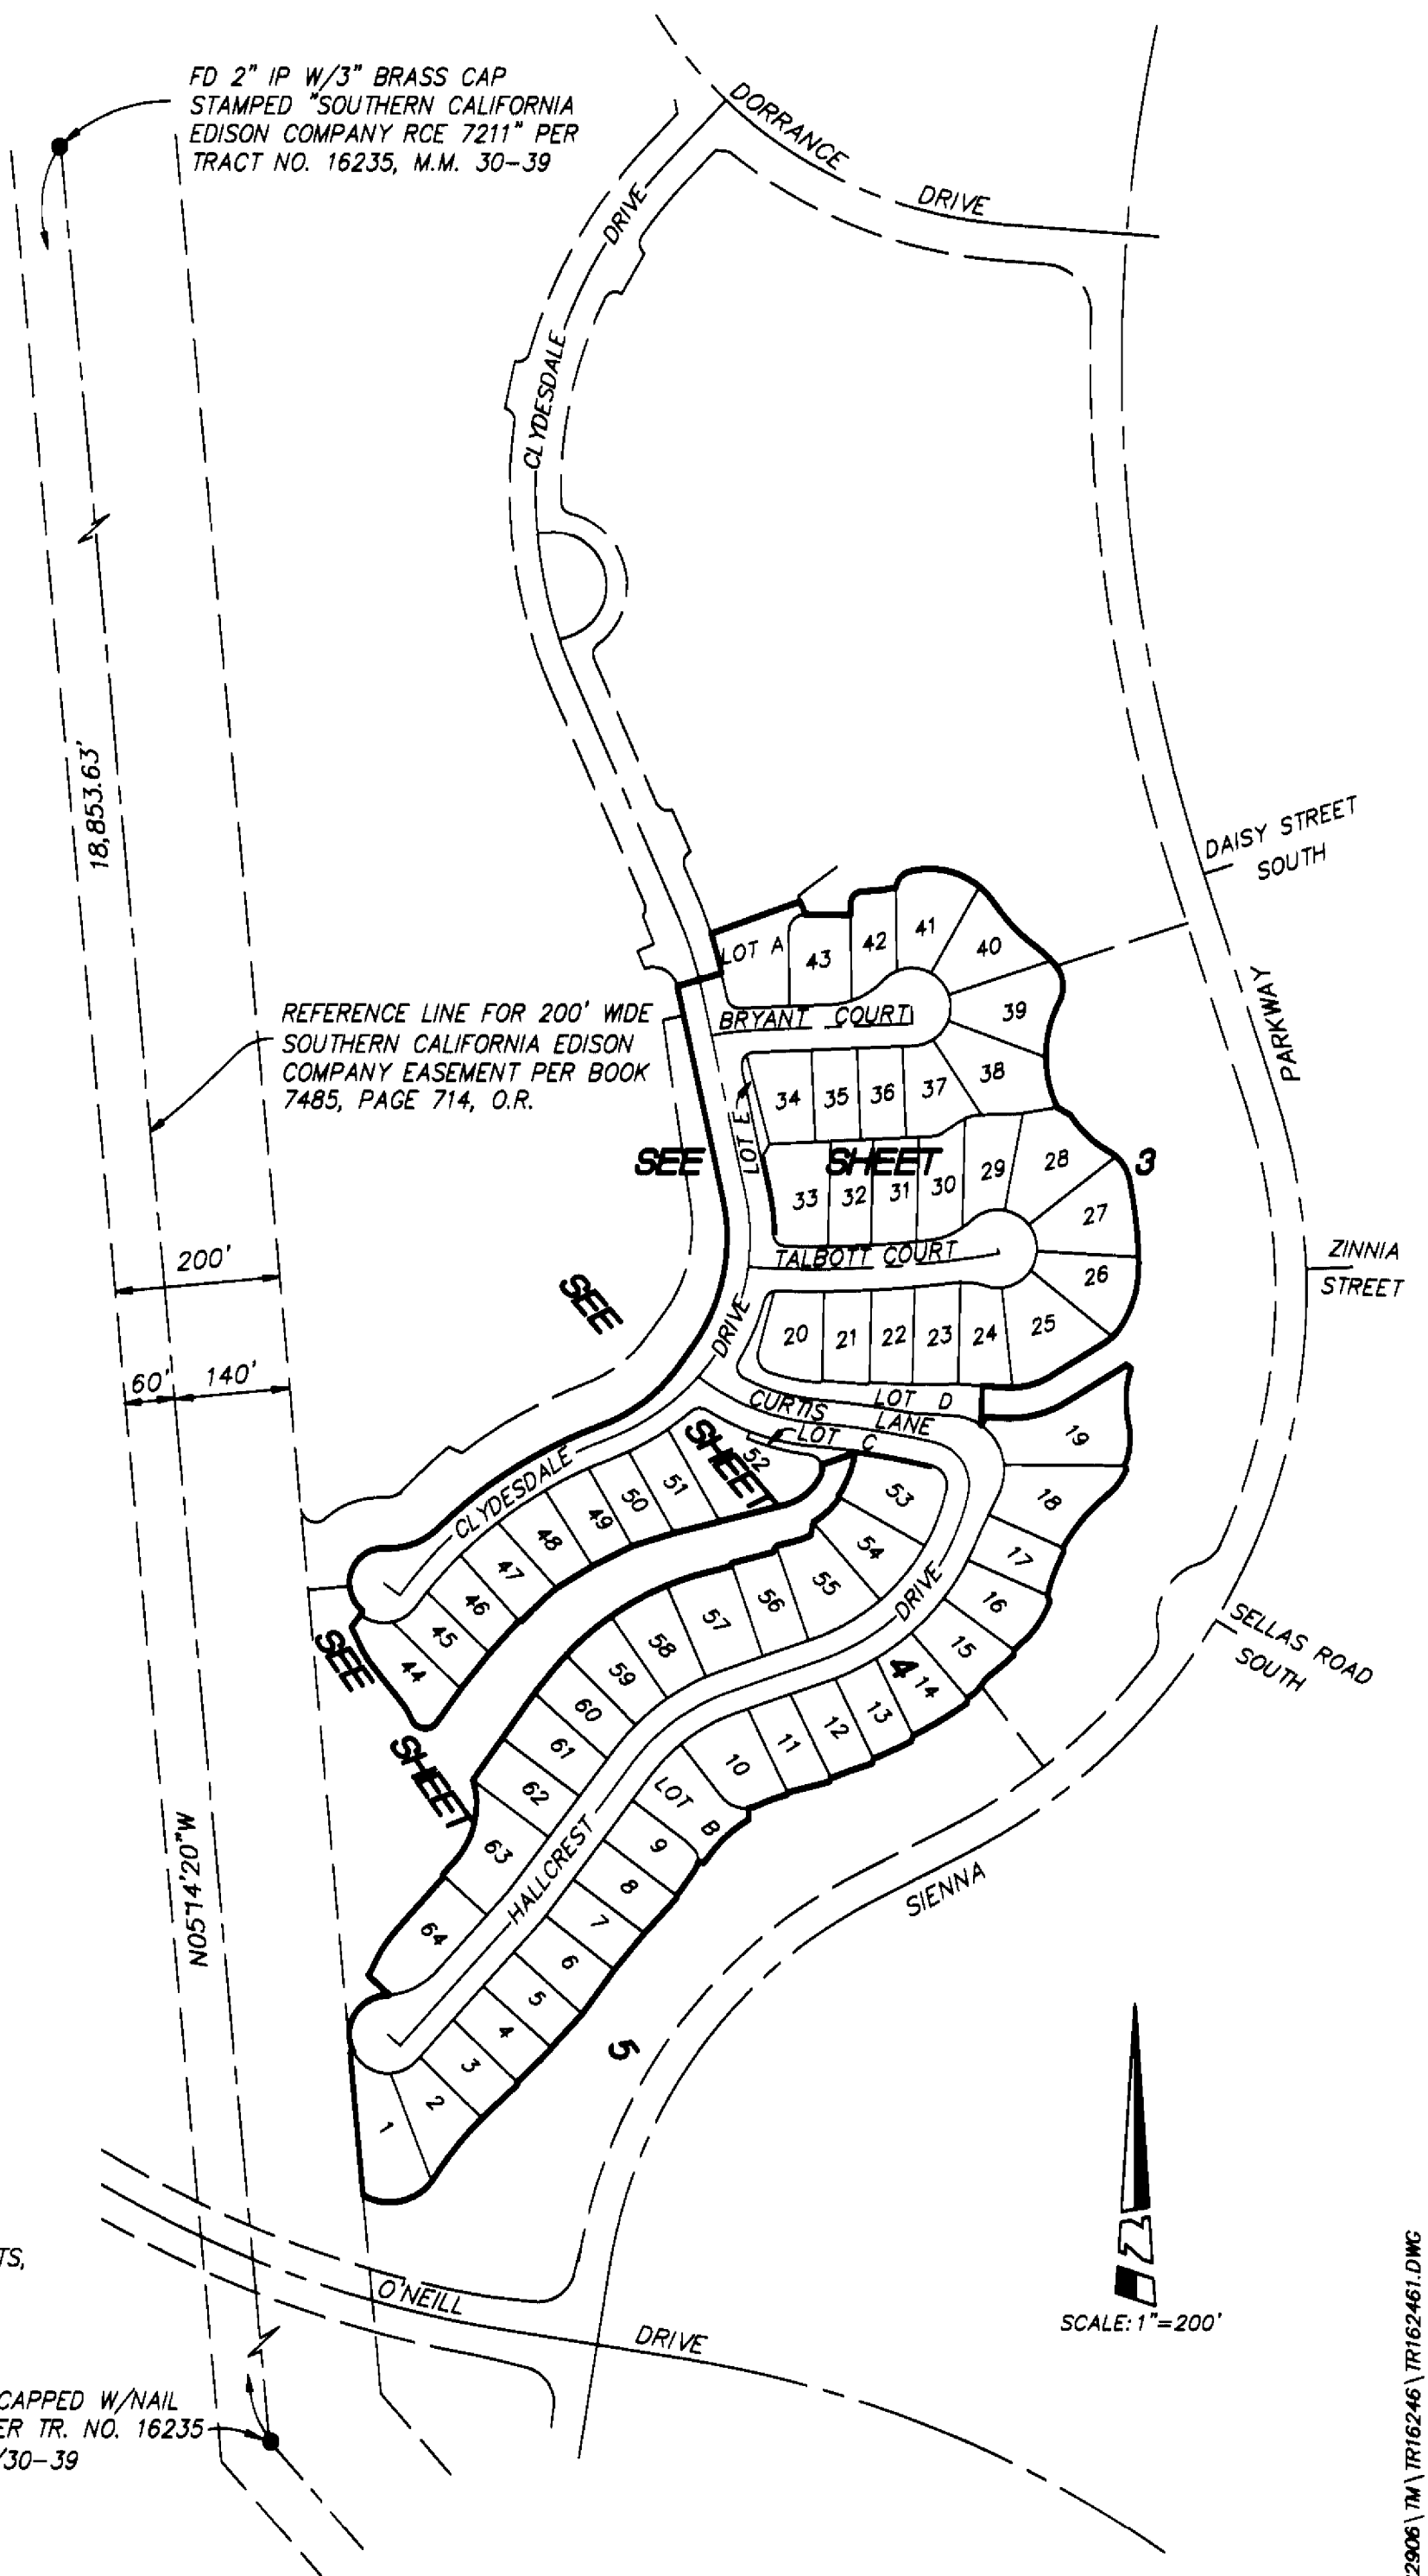

SHEET INDEX MAP

842 46

842 47

SHEET 3 OF 5 SHEETS

TRACT NO. 16246

ALL OF VESTING TENTATIVE
TRACT NO. 16246

IN THE UNINCORPORATED TERRITORY OF ORANGE COUNTY, CALIFORNIA

DATE OF SURVEY:
DECEMBER 2001



FEBRUARY 2002

JAMES F. GILLEN, L.S. 5557

HUITT-ZOLIARS

64 NUMBERED LOTS AND 5 LETTERED LOTS

15.928 ACRES

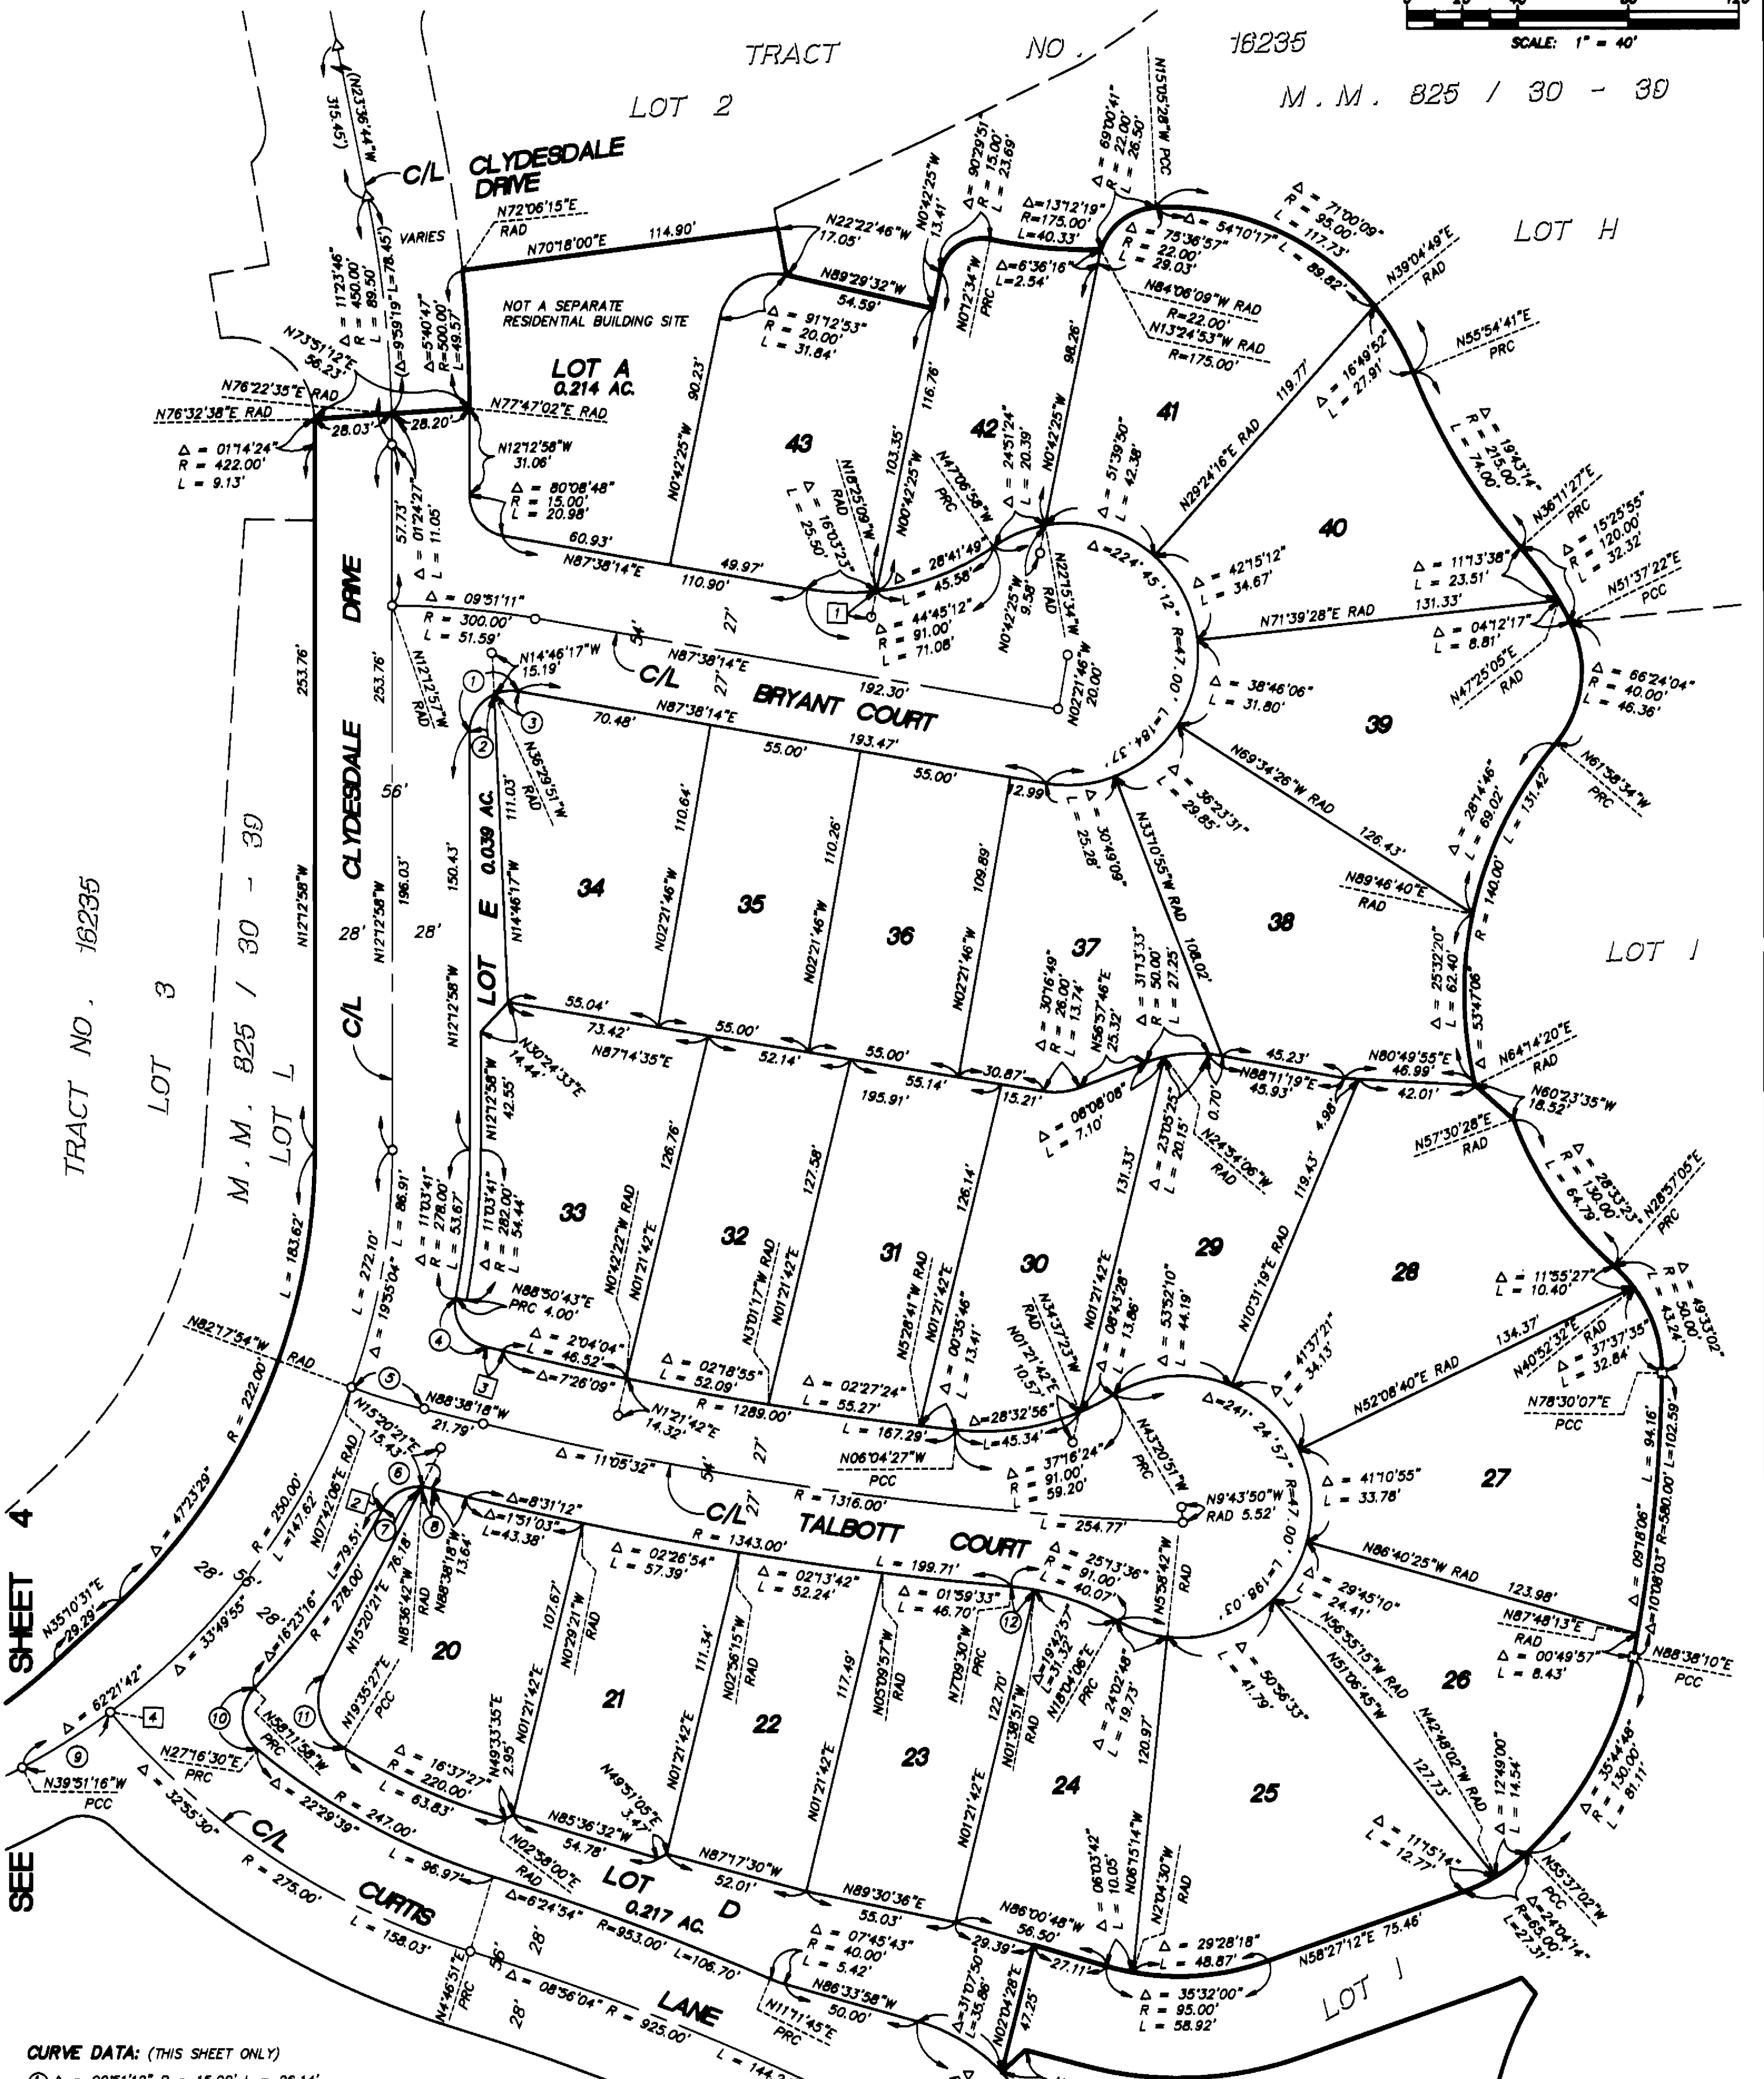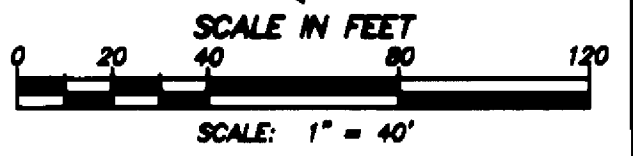

CURVE DATA: (THIS SHEET ONLY)

- ① $\Delta = 99^{\circ}51'12''$ R = 15.00' L = 26.14'
- ② $\Delta = 65^{\circ}43'07''$ R = 15.00' L = 17.20'
- ③ $\Delta = 34^{\circ}08'05''$ R = 15.00' L = 8.94'
- ④ $\Delta = 87^{\circ}29'01''$ R = 15.00' L = 22.90'
- ⑤ $\Delta = 06^{\circ}20'24''$ R = 250.00' L = 27.66'
- ⑥ $\Delta = 75^{\circ}56'56''$ R = 15.00' L = 19.88'
- ⑦ $\Delta = 65^{\circ}58'32''$ R = 15.00' L = 17.27'
- ⑧ $\Delta = 09^{\circ}58'24''$ R = 15.00' L = 2.61'
- ⑨ $\Delta = 08^{\circ}36'43''$ R = 250.00' L = 37.57'
- ⑩ $\Delta = 94^{\circ}31'32''$ R = 15.00' L = 24.75'
- ⑪ $\Delta = 85^{\circ}44'54''$ R = 20.00' L = 29.93'
- ⑫ $\Delta = 05^{\circ}30'39''$ R = 91.00' L = 8.75'
- ⑬ $\Delta = 89^{\circ}12'12''$ R = 53.00' L = 82.52'

**COURSE DATA:
(THIS SHEET ONLY)**

- ① N00°42'25"W 9.14'
- ② N74°35'14"W PRC
- ③ N88°38'18"W 5.15'
- ④ N48°27'59"W RAD (R=250.00')
- ⑤ N37°42'21"E RAD (R=275.00')

NOTES:

SEE SHEET 2 FOR MONUMENT NOTES,
EASEMENT NOTES AND BASIS OF BEARINGS.
LOTS A AND B ARE FOR POCKET PARKS.
LOTS C, D, AND E ARE FOR LANDSCAPING AND OPEN
SPACE AND ARE NOT SEPARATE BUILDING SITES.
ALL EXTERIOR TRACT BOUNDARY DIMENSIONS ARE MEASURED
AND RECORD PER TRACT NO. 16235, M.M. 825/30-39.
() INDICATES MEASURED AND RECORD PER
TRACT NO. 16235

10-0829-06

G:\10082906\TM\TR16246\TR162462.DWG

842 47

842 48

SHEET 4 OF 5 SHEETS

TRACT NO. 16246

ALL OF VESTING TENTATIVE
TRACT NO. 16246

IN THE UNINCORPORATED TERRITORY OF ORANGE COUNTY, CALIFORNIA

DATE OF SURVEY:
DECEMBER 2001


FEBRUARY 2002

JAMES F. GILLEN, L.S. 5557

HUITT-ZOLIARS

64 NUMBERED LOTS AND 5 LETTERED LOTS

15.928 ACRES

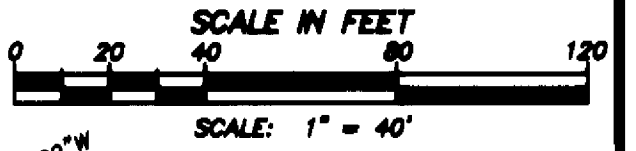

CURVE DATA: (THIS SHEET ONLY)

- 1 $\Delta = 08^{\circ}36'43''$ R = 250.00' L = 37.57'
- 2 $\Delta = 72^{\circ}3'45''$ R = 15.00' L = 18.91'
- 3 $\Delta = 03^{\circ}21'15''$ R = 282.00' L = 18.51'
- 4 $\Delta = 110^{\circ}23'49''$ R = 18.00' L = 34.68'
- 5 $\Delta = 64^{\circ}5'06''$ R = 18.00' L = 20.18'
- 6 $\Delta = 46^{\circ}08'43''$ R = 18.00' L = 14.50'
- 7 $\Delta = 48^{\circ}22'56''$ R = 68.00' L = 57.42'
- 8 $\Delta = 11^{\circ}24'31''$ R = 113.00' L = 22.50'
- 9 $\Delta = 23^{\circ}37'34''$ R = 101.00' L = 41.65'
- 10 $\Delta = 25^{\circ}49'08''$ R = 125.00' L = 56.33'
- 11 $\Delta = 03^{\circ}22'35''$ R = 631.00' L = 37.18'
- 12 $\Delta = 18^{\circ}20'32''$ R = 53.00' L = 16.97'
- 13 $\Delta = 27^{\circ}07'01''$ R = 48.00' L = 22.72'
- 14 $\Delta = 89^{\circ}08'29''$ R = 25.00' L = 38.90'
- 15 $\Delta = 14^{\circ}01'48''$ R = 223.00' L = 54.61'

COURSE DATA: (THIS SHEET ONLY)

- 1 N37°42'21"E RAD (R=275.00')
N48°27'59"W RAD (R=250.00')
- 2 N31°37'19"E PRC
- 3 N12°50'45"W 2.97'
- 4 N10°27'42"E 16.11'


NOTES:

SEE SHEET 2 FOR MONUMENT NOTES,
EASEMENT NOTES, AND BASIS OF BEARINGS.

LOTS A AND B ARE FOR POCKET PARKS.

LOTS C, D, AND E ARE FOR LANDSCAPING AND
OPEN SPACE AND ARE NOT SEPARATE BUILDING SITES.

ALL EXTERIOR TRACT BOUNDARY DIMENSIONS ARE
MEASURED AND RECORD PER TRACT NO. 16235,
M.M. 825/30-39.

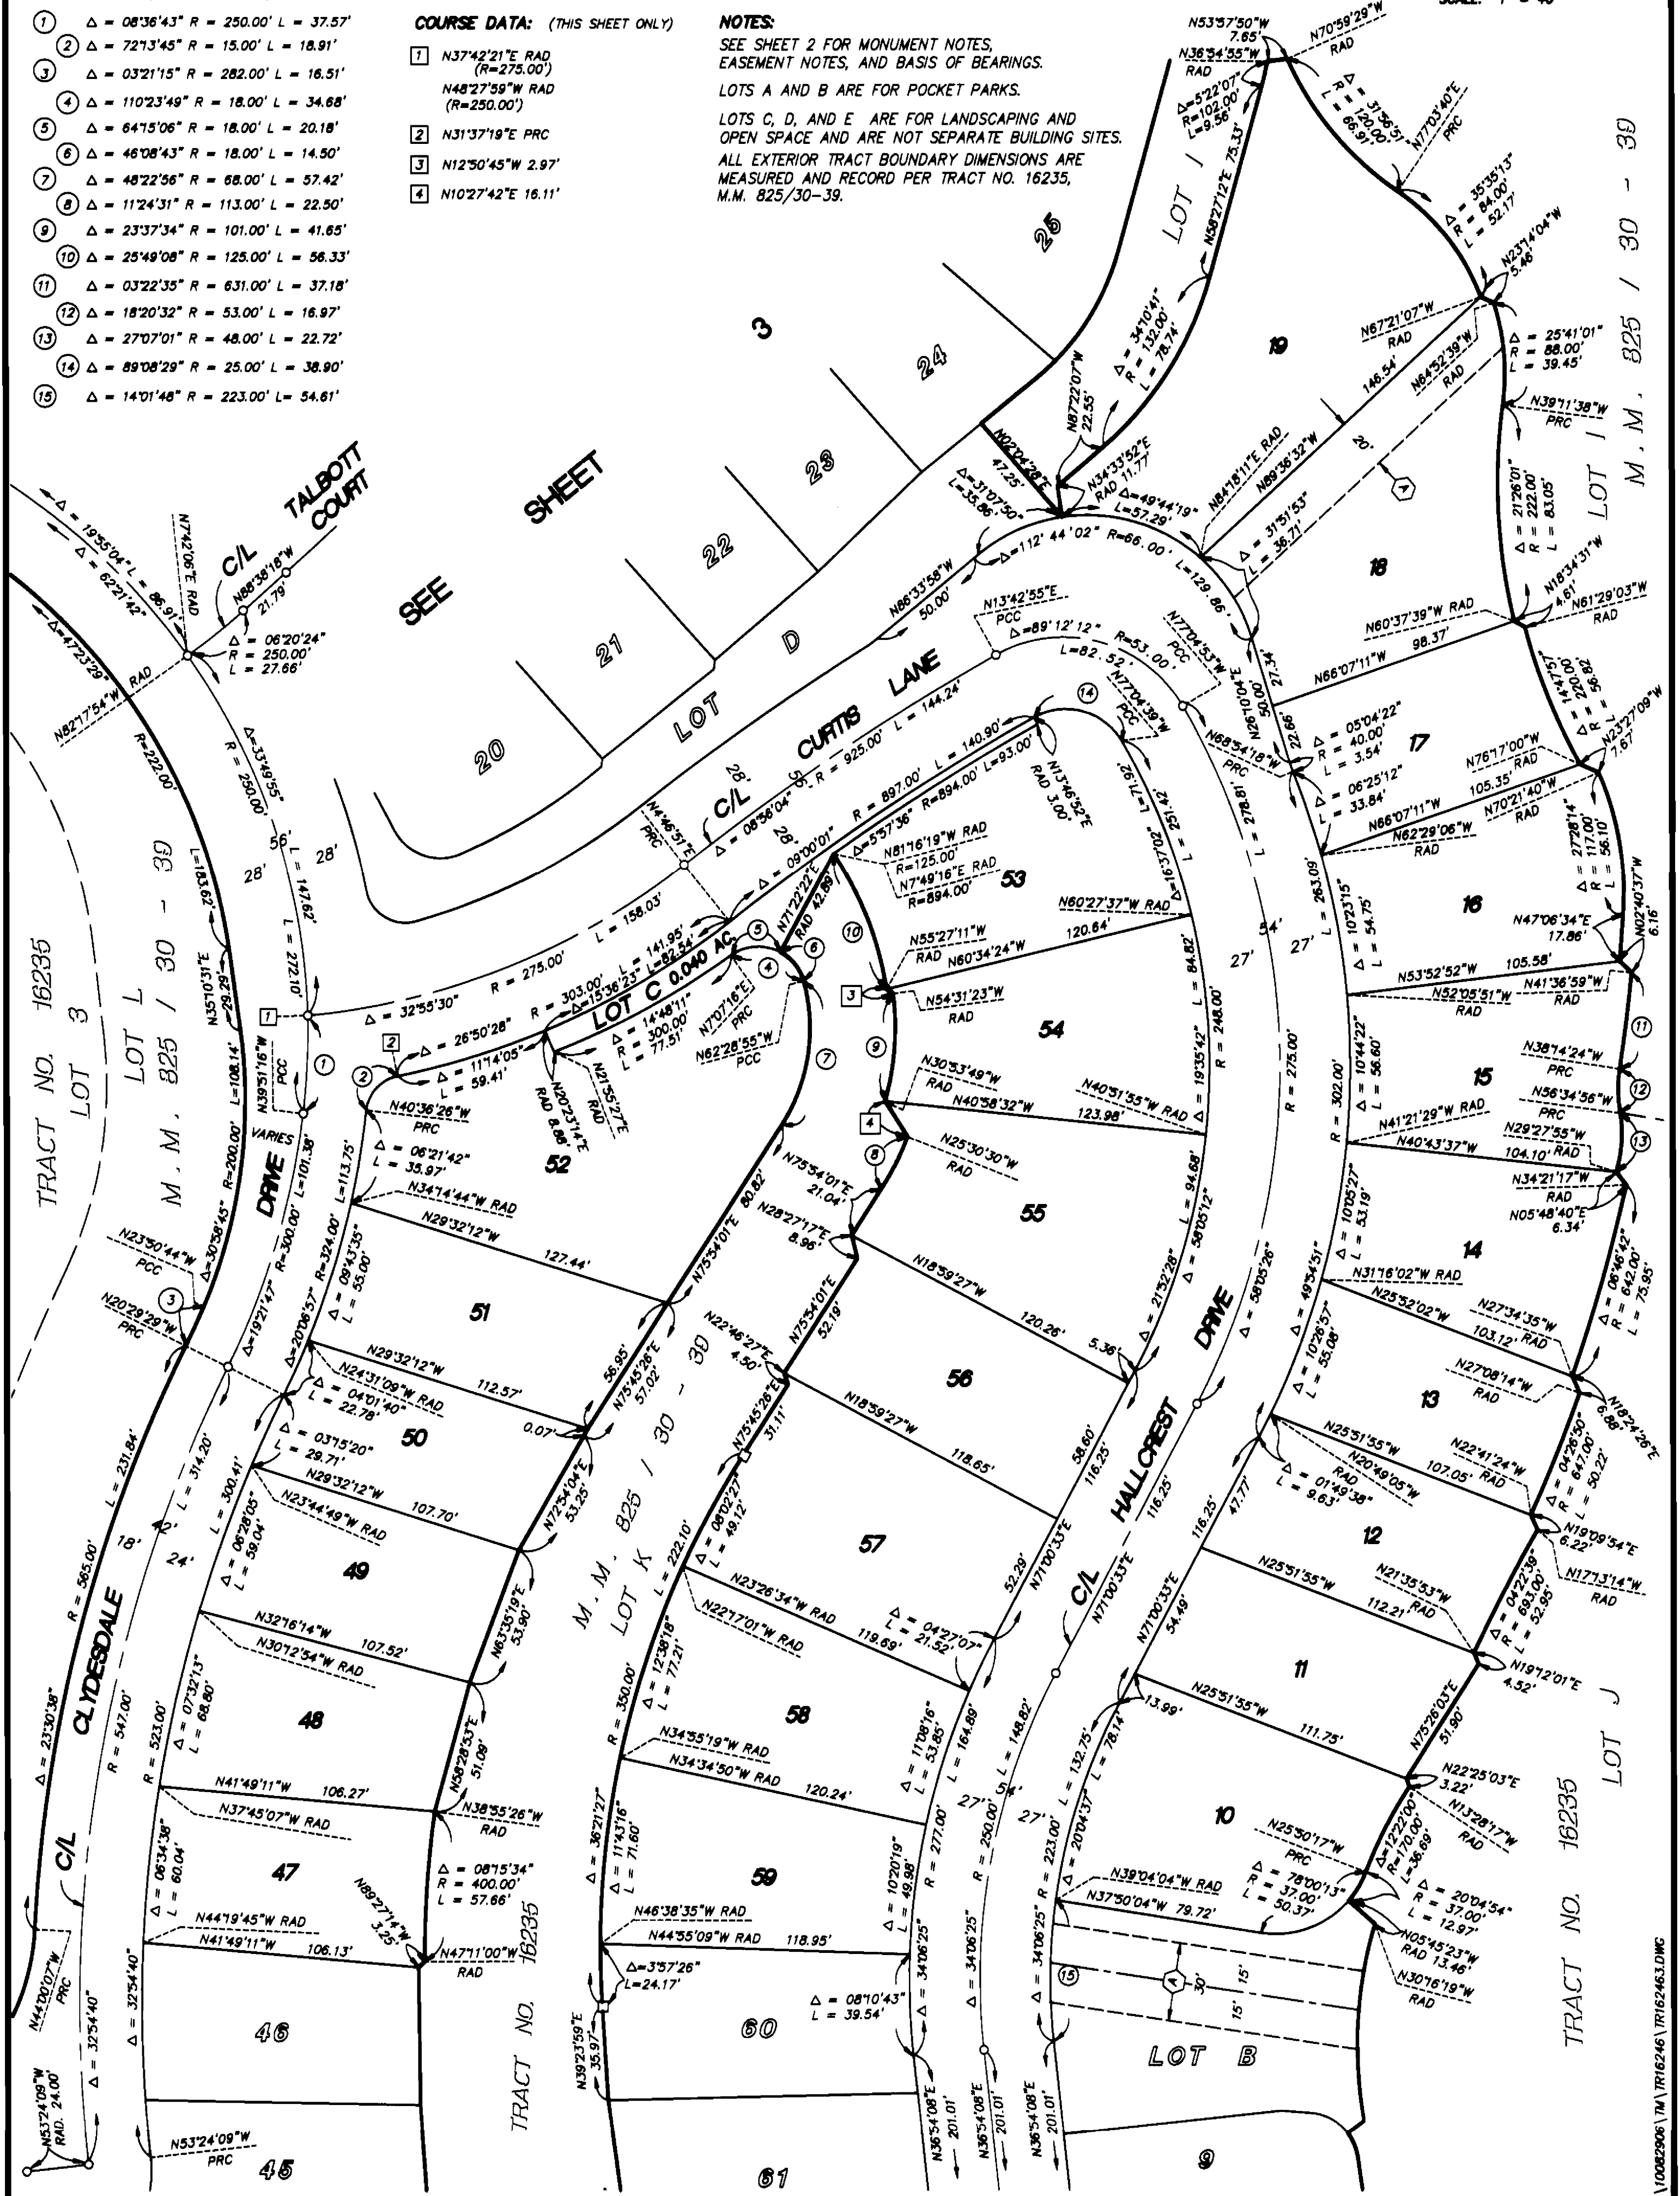

M.M. 825 / 30 - 39

TRACT NO. 16235

TRACT NO. 16245

G:\10082906\7M\16246\16246.DWG

842 48

TRACT NO. 16246

ALL OF VESTING TENTATIVE
TRACT NO. 16246

IN THE UNINCORPORATED TERRITORY OF ORANGE COUNTY, CALIFORNIA

DATE OF SURVEY:
DECEMBER 2001



FEBRUARY 2002

JAMES F. GILLEN, L.S. 5557

HUITT-ZOLIARS

64 NUMBERED LOTS AND 5 LETTERED LOTS

15.928 ACRES

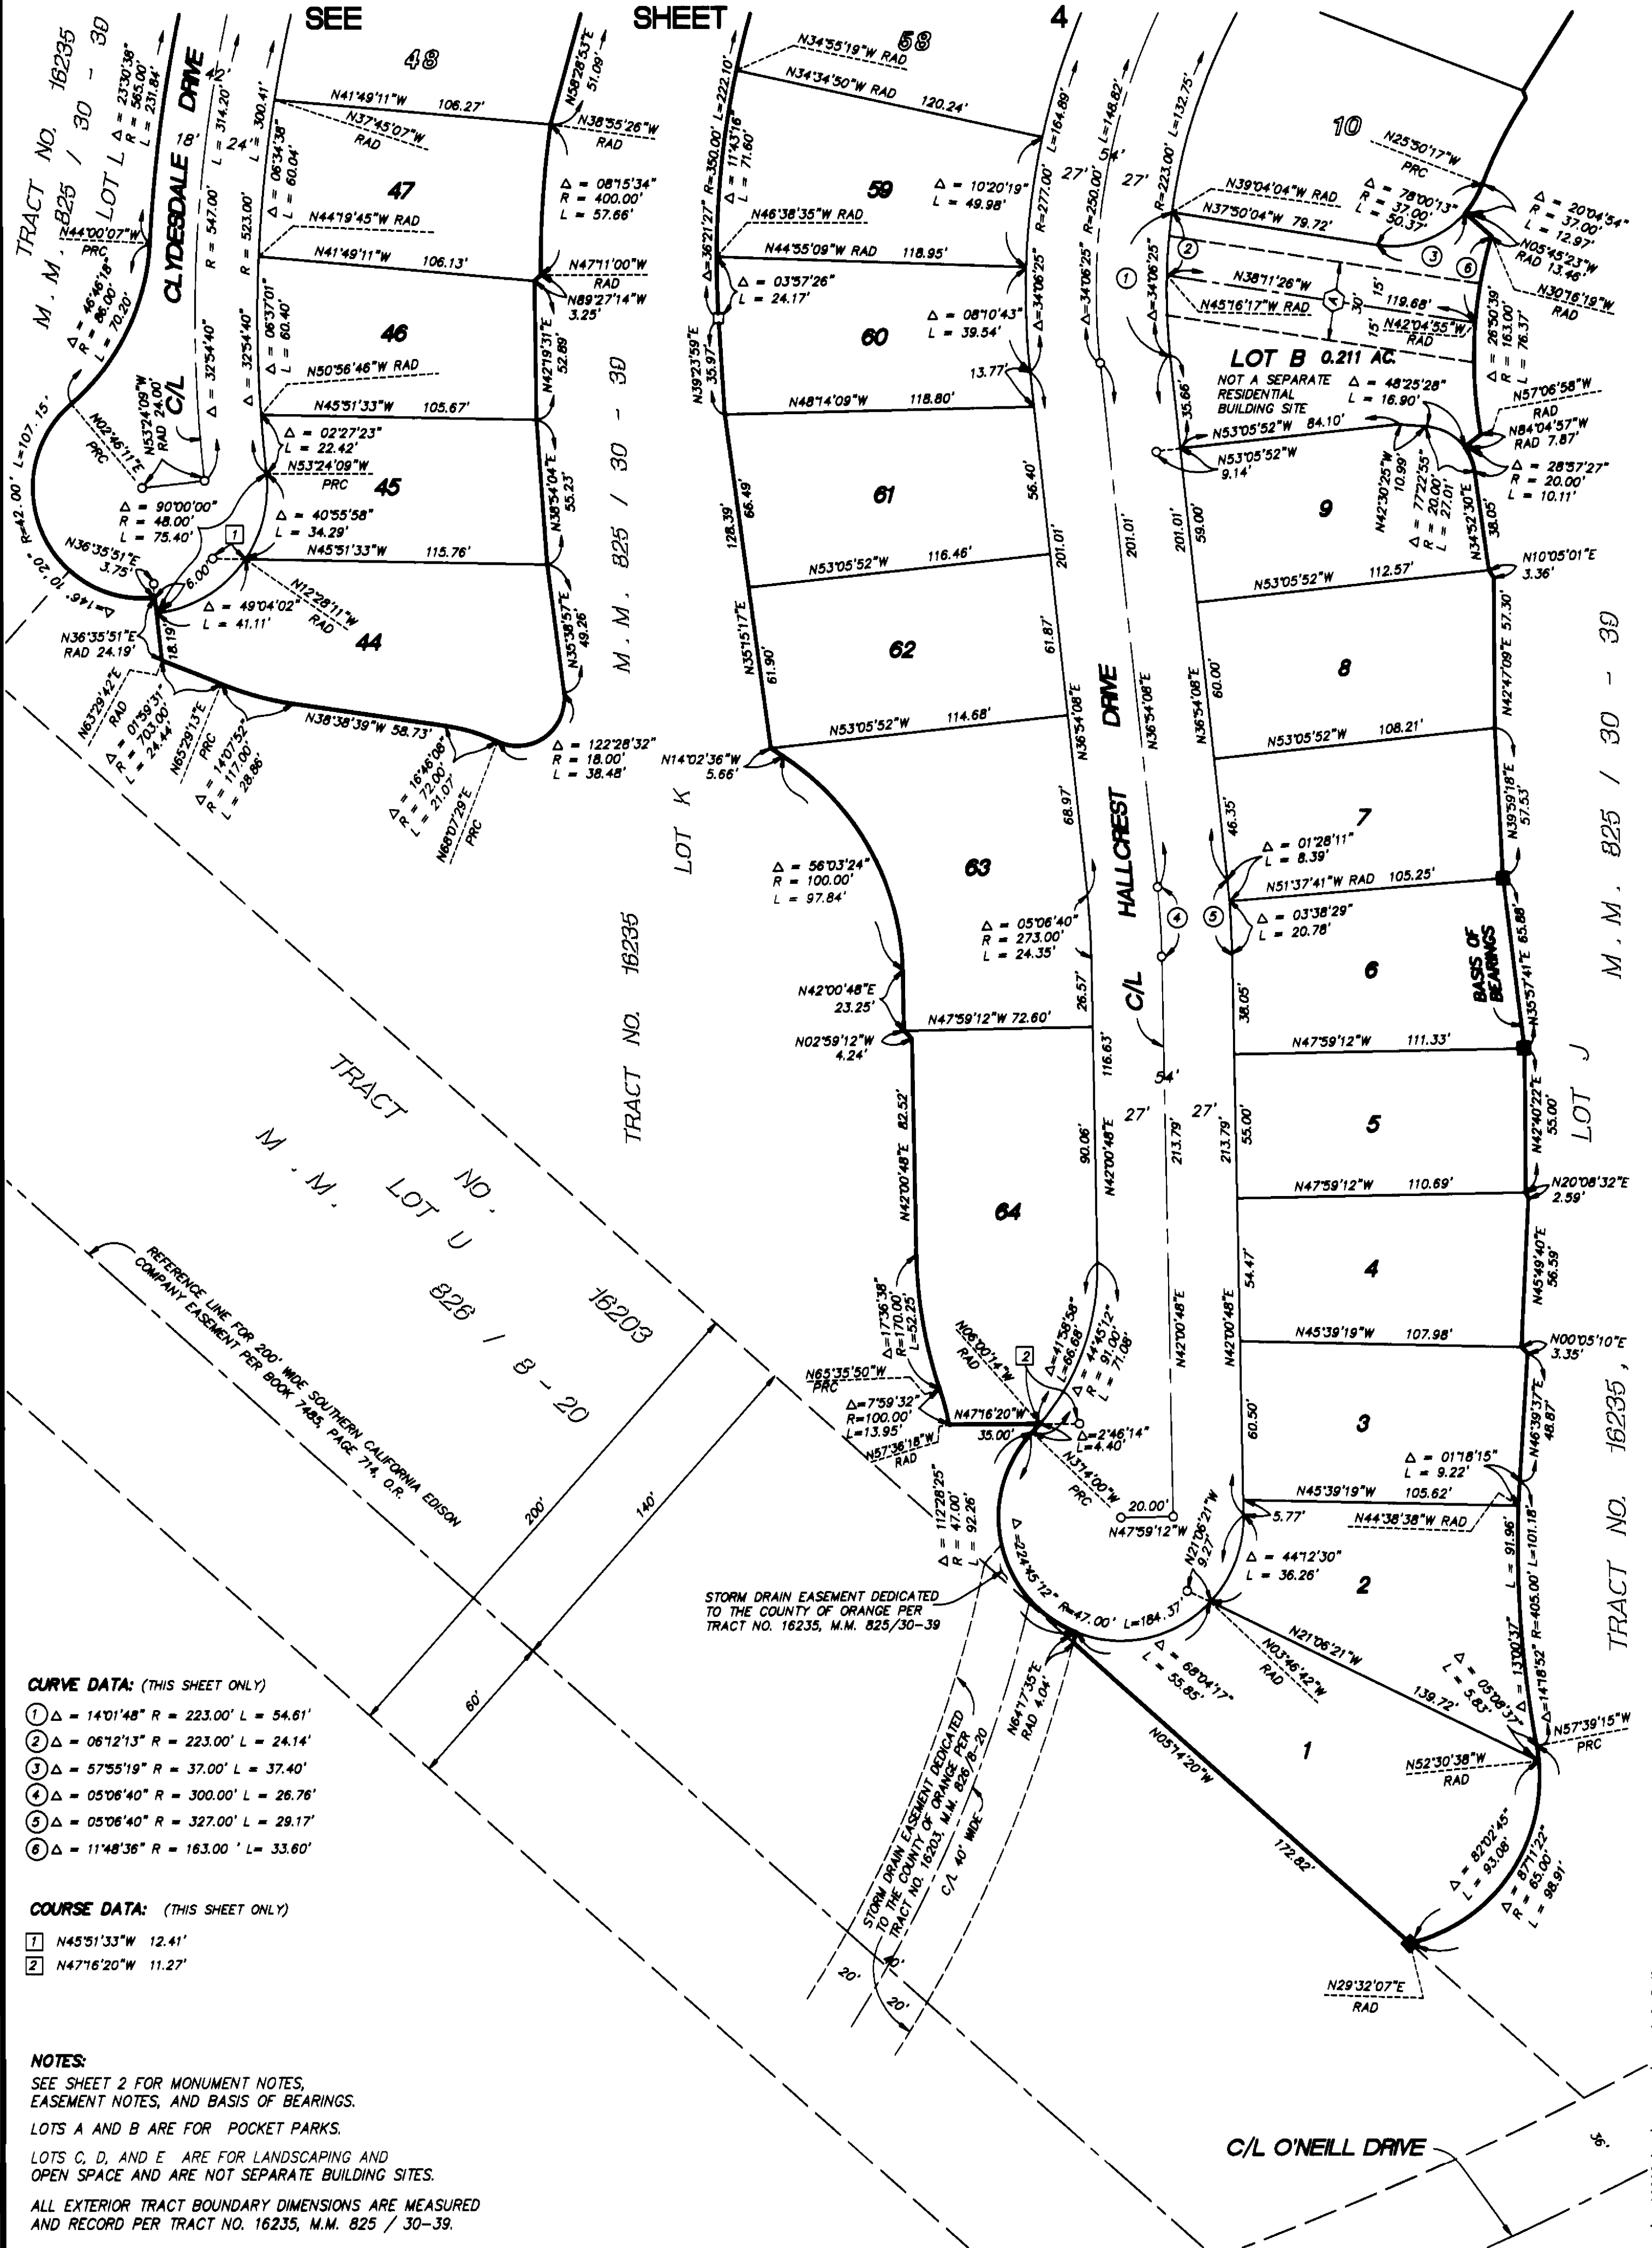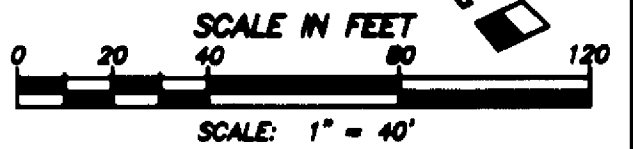

CURVE DATA: (THIS SHEET ONLY)

- ① $\Delta = 140'48''$ R = 223.00' L = 54.61'
- ② $\Delta = 06'12'13''$ R = 223.00' L = 24.14'
- ③ $\Delta = 57'55'19''$ R = 37.00' L = 37.40'
- ④ $\Delta = 05'06'40''$ R = 300.00' L = 26.76'
- ⑤ $\Delta = 05'06'40''$ R = 327.00' L = 29.17'
- ⑥ $\Delta = 11'48'36''$ R = 163.00' L = 33.60'

COURSE DATA: (THIS SHEET ONLY)

- ① N45°31'33"W 12.41'
- ② N47°16'20"W 11.27'

NOTES:

SEE SHEET 2 FOR MONUMENT NOTES,
EASEMENT NOTES, AND BASIS OF BEARINGS.

LOTS A AND B ARE FOR POCKET PARKS.

LOTS C, D, AND E ARE FOR LANDSCAPING AND
OPEN SPACE AND ARE NOT SEPARATE BUILDING SITES.

ALL EXTERIOR TRACT BOUNDARY DIMENSIONS ARE MEASURED
AND RECORD PER TRACT NO. 16235, M.M. 825 / 30-39.