

SHEET 1 OF 4 SHEETS

ALL OF TENTATIVE TRACT
MAP NO. 16247
TOTAL LOTS: 1-37 AND LOTS A-C
TOTAL ACREAGE: 5.412 AC.
DATE OF SURVEY: OCTOBER, 2001

BLOCK 5057
MODULE 25

TRACT MAP NO. 16247

IN THE UNINCORPORATED TERRITORY OF THE COUNTY OF ORANGE,
STATE OF CALIFORNIA

BEING A SUBDIVISION OF LOT 12, AS SHOWN ON TRACT MAP NO. 16203
FILED IN BOOK 826, PAGES 8 THROUGH 20, INCLUSIVE OF MISCELLANEOUS MAPS,
IN THE OFFICE OF THE COUNTY RECORDER OF SAID COUNTY, STATE OF CALIFORNIA

ADAMS - STREETER CML ENGINEERING, INC. JAN A. ADAMS, R.C.E. 21687
DATE OF SURVEY: OCTOBER, 2001

ACCEPTED AND FILED AT THE
REQUEST OF

FIRST AMERICAN TITLE INSURANCE COMPANY

DATE MAY 24, 2002
TIME 10:49 AM FEE \$ 13.00
INSTRUMENT # 2002 0440072
BOOK 832 PAGE 16-19 4/4

DARLENE J. BLOOM
INTERIM COUNTY CLERK-RECORDER

BY [Signature]
DEPUTY

OWNER'S CERTIFICATE:

WE, THE UNDERSIGNED, BEING ALL PARTIES HAVING ANY RECORD TITLE INTEREST IN THE LAND COVERED
BY THIS MAP, DO HEREBY CONSENT TO THE PREPARATION AND RECORDATION OF SAID MAP, AS SHOWN
WITHIN THE DISTINCTIVE BORDER LINE.

WE HEREBY DEDICATE TO THE PUBLIC FOR STREET PURPOSES: CERNER COURT, ELLISTON DRIVE AND
UNIVERSITY ~~AVENUE~~.

WE ALSO HEREBY DEDICATE TO THE COUNTY OF ORANGE:

1. AN EASEMENT FOR STORM DRAIN PURPOSES, AS SHOWN HEREON.
2. AN EASEMENT FOR PUBLIC UTILITY PURPOSES, AS SHOWN HEREON.

WE ALSO DEDICATE TO THE SANTA MARGARITA WATER DISTRICT, THE EASEMENTS FOR SEWER, WATER AND
AND ACCESS PURPOSES AS SHOWN ON SAID MAP, WHICH EASEMENTS SHALL BE SUBJECT TO THE
SAME TERMS AND CONDITIONS AS ARE SHOWN IN THAT CERTAIN EASEMENT RECORDED OCTOBER 6, 1980,
IN BOOK 13776, PAGE 341, OF OFFICIAL RECORDS, COUNTY OF ORANGE.

RICHMOND AMERICAN HOMES OF CALIFORNIA, INC., A COLORADO CORPORATION

[Signature]
ROBERT T. SHIOTA
PRESIDENT

[Signature]
JON H. SASAKI
ASSISTANT SECRETARY

DMB LADERA, LLC A DELAWARE LIMITED LIABILITY COMPANY AS
BENEFICIARY UNDER A DEED OF TRUST RECORDED FEBRUARY 19, 2002
AS INSTRUMENT NO. 20020140035, AND HOLDER OF EASEMENTS RECORDED
FEBRUARY 19, 2002 AS INSTRUMENT NO. 20020140033, BOTH OF
OFFICIAL RECORDS.

BY: RANCHO MISSION VIEJO, L.L.C., A DELAWARE LIMITED LIABILITY
COMPANY AS AGENT AND/OR MANAGER.

[Signature]
DONALD F. SHIOTA
DEPUTY COUNTY CLERK

[Signature]
STEPHEN C. SCHIRANK
EXECUTIVE VICE PRESIDENT

STATE OF CALIFORNIA }
COUNTY OF Orange } ss

ON THIS 20th DAY OF March, 2002, BEFORE ME, Valerie Holmes, A NOTARY
PUBLIC IN AND FOR SAID STATE, PERSONALLY APPEARED Robert T. Shiota and Jon H. Sasaki
PERSONALLY KNOWN TO ME (OR PROVED TO ME ON THE BASIS OF SATISFACTORY EVIDENCE) TO BE
THE PERSONS WHOSE NAMES ARE SUBSCRIBED TO THE WITHIN INSTRUMENT AND ACKNOWLEDGED TO ME
THAT THEY EXECUTED THE SAME IN THEIR AUTHORIZED CAPACITIES AND THAT BY THEIR SIGNATURES ON
THE INSTRUMENT THE PERSON OR THE ENTITY UPON BEHALF OF WHICH THE PERSONS ACTED, EXECUTED
THE INSTRUMENT.

WITNESS MY HAND:

Valerie Holmes
NOTARY PUBLIC IN AND FOR SAID STATE

MY PRINCIPAL PLACE OF BUSINESS
IS IN Orange COUNTY

Valerie Holmes
PRINT NAME

MY COMMISSION EXPIRES 5/24/05

STATE OF CALIFORNIA }
COUNTY OF Orange } ss

ON THIS 2nd DAY OF April, 2002, BEFORE ME, Tina T. Baker, A NOTARY
PUBLIC IN AND FOR SAID STATE, PERSONALLY APPEARED Donald F. Shiota and Stephen C. Schirank
PERSONALLY KNOWN TO ME (OR PROVED TO ME ON THE BASIS OF SATISFACTORY EVIDENCE) TO BE
THE PERSONS WHOSE NAMES ARE SUBSCRIBED TO THE WITHIN INSTRUMENT AND ACKNOWLEDGED TO ME
THAT THEY EXECUTED THE SAME IN THEIR AUTHORIZED CAPACITIES AND THAT BY THEIR SIGNATURES ON
THE INSTRUMENT THE PERSON OR THE ENTITY UPON BEHALF OF WHICH THE PERSONS ACTED, EXECUTED
THE INSTRUMENT.

WITNESS MY HAND:

Tina T. Baker
NOTARY PUBLIC IN AND FOR SAID STATE

MY PRINCIPAL PLACE OF BUSINESS
IS IN Orange COUNTY

Tina T. Baker
PRINT NAME

MY COMMISSION EXPIRES 8-29-04

SIGNATURE OMISSIONS

PURSUANT TO THE PROVISIONS OF SECTION 66436 (a)(3) OF THE SUBDIVISION MAP ACT, THE FOLLOWING
SIGNATURES HAVE BEEN OMITTED:

LADERA DEVELOPMENT COMPANY, LLC, HOLDER OF OIL, GAS AND MINERAL RIGHTS RECORDED AS
INSTRUMENT NO. 19960624029 OF OFFICIAL RECORDS.

ENGINEER'S STATEMENT

I HEREBY STATE THAT THIS MAP CONSISTING OF 4 SHEETS CORRECTLY REPRESENTS A TRUE AND
COMPLETE SURVEY AS SHOWN MADE IN OCTOBER, 2001, WAS MADE BY ME OR UNDER MY DIRECTION;
THAT THE MONUMENTS ARE OF THE CHARACTER AND OCCUPY (OR WILL OCCUPY) THE POSITIONS
INDICATED BY SAID MAP; AND THAT SAID MONUMENTS ARE SUFFICIENT TO ENABLE THE SURVEY TO
BE RETRACED.

[Signature]
JAN A. ADAMS, R.C.E. 21687
EXPIRES: 9/30/05



COUNTY SURVEYOR'S STATEMENT

I HEREBY STATE THAT I HAVE EXAMINED THIS MAP AND HAVE FOUND IT TO BE SUBSTANTIALLY IN
CONFORMANCE WITH THE TENTATIVE MAP AS FILED WITH, AMENDED AND APPROVED BY THE ORANGE
COUNTY SUBDIVISION COMMITTEE; THAT ALL PROVISIONS OF THE SUBDIVISION MAP ACT AND COUNTY
SUBDIVISION REGULATIONS HAVE BEEN COMPLIED WITH AND I AM SATISFIED SAID MAP IS TECHNICALLY
CORRECT.

DATED THIS 3RD DAY OF MAY, 2002

[Signature]
JOHN CANAS, COUNTY SURVEYOR
LS 4408 EXPIRATION DATE: 9-30-05

BY: MICHAEL K. SULLIVAN, DEPUTY
LS. 6254 EXPIRES 6-30-02



COUNTY TREASURER - TAX COLLECTOR'S CERTIFICATE

STATE OF CALIFORNIA }
COUNTY OF ORANGE } ss

I HEREBY CERTIFY THAT ACCORDING TO THE RECORDS OF MY OFFICE THERE ARE NO LIENS AGAINST THE
LAND COVERED BY THIS MAP OR ANY PART THEREOF FOR UNPAID STATE, COUNTY, MUNICIPAL OR LOCAL
TAXES OR SPECIAL ASSESSMENTS COLLECTED AS TAXES, EXCEPT TAXES OR SPECIAL ASSESSMENTS
COLLECTED AS TAXES NOT YET PAYABLE.

AND DO ALSO CERTIFY TO THE RECORDER OF ORANGE COUNTY THAT THE PROVISIONS OF THE
SUBDIVISION MAP ACT HAVE BEEN COMPLIED WITH REGARDING DEPOSITS TO SECURE THE PAYMENT OF
TAXES OR SPECIAL ASSESSMENTS COLLECTED AS TAXES ON THE LAND COVERED BY THIS MAP.

DATED THIS 11th DAY OF April, 2002

JOHN M. W. MOORLACH
COUNTY TREASURER - TAX COLLECTOR

BY: [Signature]
DEPUTY TREASURER - TAX COLLECTOR

CLERK OF THE BOARD OF SUPERVISOR'S CERTIFICATE

STATE OF CALIFORNIA }
COUNTY OF ORANGE } ss

I HEREBY CERTIFY THAT THIS MAP PRESENTED FOR APPROVAL TO THE BOARD OF SUPERVISORS OF
ORANGE COUNTY AT A REGULAR MEETING THEREOF HELD ON THE 21 DAY OF May,
2002, AND THAT THEREUPON SAID BOARD DID, BY AN ORDER DULY PASSED AND ENTERED, APPROVE
SAID MAP AND DID ACCEPT ON BEHALF OF THE PUBLIC, SUBJECT TO IMPROVEMENTS; THE DEDICATION FOR
STREET PURPOSES OF: CERNER COURT, ELLISTON DRIVE AND UNIVERSITY ~~AVENUE~~

AND DID ACCEPT ON BEHALF OF THE COUNTY OF ORANGE:

1. THE EASEMENT FOR STORM DRAIN PURPOSES, AS DEDICATED.
2. THE EASEMENT FOR PUBLIC UTILITY PURPOSES, AS DEDICATED.

AND DID ALSO APPROVE SUBJECT MAP PURSUANT TO THE PROVISIONS OF SECTION 66436 (a)(3)(A) OF
THE SUBDIVISION MAP ACT.

DATED THIS 21 DAY OF May, 2002.

[Signature]
DARLENE J. BLOOM, CLERK OF THE BOARD OF SUPERVISORS



CERTIFICATE OF ACCEPTANCE

THE UNDERSIGNED, BEING THE DULY APPOINTED AGENT OF THE SANTA MARGARITA WATER DISTRICT,
A PUBLIC CORPORATION OF ORANGE COUNTY, CALIFORNIA, PURSUANT TO ITS RESOLUTION NO. 88-10-2,
DOES HEREBY ACCEPT ON BEHALF OF SAID DISTRICT THE EASEMENTS FOR SEWER, WATER AND ACCESS
PURPOSES, AS DEDICATED AND AS SHOWN ON THIS TRACT MAP, BY AND BETWEEN THE SANTA MARGARITA
WATER DISTRICT AND RICHMOND AMERICAN HOMES OF CALIFORNIA, INC. DOES HEREBY CERTIFY THAT THE
GRANTEE CONSENTS TO THE RECORDATION OF SAID TRACT.

BY: [Signature]
DANIEL R. FERONS, CHIEF ENGINEER
SANTA MARGARITA WATER DISTRICT

STATE OF CALIFORNIA }
COUNTY OF ORANGE } ss

ON THIS 22nd DAY OF March, 2002, BEFORE ME, ANDREA M. EVANS, A NOTARY
PUBLIC IN AND FOR SAID STATE, PERSONALLY APPEARED DANIEL FERONS, PERSONALLY KNOWN TO ME
(OR PROVED TO ME ON THE BASIS OF SATISFACTORY EVIDENCE) TO BE THE PERSON WHOSE NAME IS
SUBSCRIBED TO THE WITHIN INSTRUMENT AND ACKNOWLEDGED TO ME THAT HE EXECUTED THE SAME IN
HIS AUTHORIZED CAPACITY AND THAT BY HIS SIGNATURE ON THE INSTRUMENT THE PERSON, OR THE
ENTITY UPON BEHALF OF WHICH THE PERSON ACTED, EXECUTED THE INSTRUMENT.

WITNESS MY HAND:

[Signature]
NOTARY PUBLIC IN AND FOR SAID STATE

MY PRINCIPAL PLACE OF BUSINESS
IS IN ORANGE COUNTY

ANDREA M. EVANS
PRINT NAME

MY COMMISSION EXPIRES 4-8-04

ALL OF TENTATIVE TRACT
MAP NO. 16247

TOTAL LOTS: 1-37 AND LOTS A-C

TOTAL ACREAGE: 5.412 AC.

DATE OF SURVEY: OCTOBER, 2001

TRACT MAP NO. 16247

IN THE UNINCORPORATED TERRITORY OF THE COUNTY OF ORANGE,
STATE OF CALIFORNIAADAMS - STREETER CIVIL ENGINEERING, INC. JAN A. ADAMS, R.C.E. 21687
DATE OF SURVEY: OCTOBER, 2001

BASIS OF BEARINGS

THE BEARINGS SHOWN HEREON ARE BASED ON THE BEARING BETWEEN ORANGE COUNTY SURVEYOR'S HORIZONTAL CONTROL STATION "GPS NO. 1417" AND "GPS NO. 1448", BEING N. 10°48'13" E., PER RECORDS ON FILE IN THE OFFICE OF THE ORANGE COUNTY SURVEYOR.

DATUM STATEMENT

COORDINATES SHOWN HEREON ARE BASED IN THE CALIFORNIA COORDINATE SYSTEM (CCS83) ZONE VI, 1983 NAD (1991.35 EPOCH), O.C.S. GPS ADJUSTMENT. ALL DISTANCE SHOWN HEREON ARE GROUND, UNLESS OTHERWISE NOTED. TO OBTAIN GRID DISTANCE MULTIPLY GROUND DISTANCE BY 0.99993286.

MONUMENT NOTES:

- INDICATES FOUND MONUMENT AS NOTED.
- △ 2" IRON PIPE, TAGGED "R.C.E. 21687", OR LEAD, TACK AND TAG "R.C.E. 21687" IN CONCRETE OR 8" SPIKE AND WASHER STAMPED "RCE 21687" IN ASPHALT PAVING TO BE SET AT ALL TRACT CORNERS, UNLESS OTHERWISE NOTED.
- △ 2" IRON PIPE, TAGGED "R.C.E. 21687" TO BE SET PRIOR TO RECORDATION.
- 1" IRON PIPE, TAGGED "R.C.E. 21687", OR SPIKE AND WASHER, STAMPED "R.C.E. 21687", OR LEAD, TACK AND TAG "R.C.E. 21687" TO BE SET AT ALL LOT CORNERS, EXCEPT AT LOT CORNERS THAT ADJUT A STREET, WHICH WILL BE SET ON A 9.75' OFFSET OUTSIDE THE TRUE LOT CORNER ON A PROLONGATION OF THE SIDE LOT LINE BY A LEAD, TACK AND TAG "R.C.E. 21687" IN THE TOP OF ADJACENT CONCRETE CURB, UNLESS OTHERWISE NOTED.
- LEAD, TACK AND TAG "R.C.E. 21687" TO BE SET ON AN OFFSET SHOWN HEREON OUTSIDE THE TRUE LOT CORNER IN THE TOP OF ADJACENT CONCRETE CURB, UNLESS OTHERWISE NOTED.
- 1" IRON PIPE, TAGGED "PLS 5557", OR SPIKE AND WASHER, STAMPED "PLS 5557", OR LEAD, TACK AND TAG "PLS 5557" TO BE SET PER TRACT NO. 16203, MM 826/8-20, UNLESS OTHERWISE NOTED.
- 2" IRON PIPE, TAGGED "PLS 5557", OR SPIKE AND WASHER, STAMPED "PLS 5557", OR LEAD, TACK AND TAG "PLS 5557" TO BE SET PER TRACT NO. 16203, MM 826/8-20, UNLESS OTHERWISE NOTED.
- 1" IRON PIPE, TAGGED "PLS 5557", OR SPIKE AND WASHER, STAMPED "PLS 5557", OR LEAD, TACK AND TAG "PLS 5557" TO BE SET PER TRACT NO. 15813, MM 795/1-16, UNLESS OTHERWISE NOTED.
- 8" SPIKE AND WASHER STAMPED "RCE 21687" IN ASPHALT PAVING OR LEAD, TACK AND TAG "R.C.E. 21687" IN CONCRETE OR 1" IRON PIPE, TAGGED "RCE 21687" TO BE SET AT ALL CENTERLINE INTERSECTIONS, B.C.'S, E.C.'S AND ALL OTHER CENTERLINE POINTS OF CONTROL, UNLESS OTHERWISE NOTED.
- ALL MONUMENTS SHOWN AS "TO BE SET" WILL BE SET 90 DAYS AFTER THE ACCEPTANCE OF THE FINAL IMPROVEMENTS.
- NO MONUMENTS TO BE SET AT B.C.'S AND E.C.'S OF STREET RIGHT OF WAY LINES.

EASEMENT NOTES:

- AN EASEMENT FOR SEWER AND WATER PIPELINE AND ACCESS PURPOSES IN FAVOR OF THE SANTA MARGARITA WATER DISTRICT.
- AN EASEMENT FOR STORM DRAIN PURPOSES IN FAVOR OF THE COUNTY OF ORANGE.
- A RESERVATION OF A PRIVATE EASEMENT FOR ACCESS AND DRAINAGE PURPOSES.
- AN EASEMENT FOR PUBLIC UTILITY PURPOSES IN FAVOR OF THE COUNTY OF ORANGE.

NOTES:

LETTERED LOTS ARE NOT SEPARATE BUILDING SITES.

LOTS DESIGNATED AS OPEN SPACES ARE FOR LANDSCAPE PURPOSES AND WILL BE MAINTAINED BY THE HOMEOWNER'S ASSOCIATION.

(X) - INDICATES SHEET NUMBER.

REFERENCES:

() INDICATES MEASURED AND RECORD PER TRACT MAP NO. 16203, M.M. 26/8-20.

[] INDICATES MEASURED AND RECORD PER TRACT MAP NO. 15813, M.M. 795/1-16.

LETTERED LOT INFORMATION

LOT	AREA	USE
A	0.118 AC	OPEN SPACE
B	0.137 AC	OPEN SPACE
C	0.015 AC	OPEN SPACE

AUTOMATIC FIRE SPRINKLER NOTE:

ALL RESIDENTIAL STRUCTURES EXCEEDING 5,500 SQUARE FEET AND ALL STRUCTURES EXCEEDING FIRE DEPARTMENT ACCESS REQUIREMENTS SHALL BE PROTECTED BY AN AUTOMATIC FIRE SPRINKLER SYSTEM, IN A MANNER MEETING THE APPROVAL OF THE FIRE CHIEF.


SPECIAL FIRE PROTECTION NOTE:

PROPERTY IS **TOTALY** EXCLUDED FROM A SPECIAL FIRE PROTECTION AREA.

ALL REQUIREMENTS FOR DEVELOPMENT AND CONSTRUCTION WITHIN A "SPECIAL FIRE PROTECTION AREA" INCLUDING INCREASED STREET WIDTHS AND CLASS A ROOF ASSEMBLIES WILL BE MET.

SIDEYARD EASEMENT NOTE:

CERTAIN LOTS WILL BE BENEFITED AND/OR BURDENED BY EASEMENTS FOR SIDEYARD AND/OR INGRESS/EGRESS PURPOSES. SUCH EASEMENTS WILL BE MORE PARTICULARLY SET FORTH IN SEPARATE DOCUMENTS TO BE RECORDED LATER. LOT 2 WILL BE BENEFITED BY AN EASEMENT FOR INGRESS/EGRESS PURPOSES SO THAT VEHICLES AND PEDESTRIANS WILL ENJOY A MINIMUM CONTINUOUS WIDTH OF TWENTY FEET. SUCH EASEMENT WILL BE MORE PARTICULARLY SET FORTH IN A SEPARATE DOCUMENT TO BE RECORDED LATER.

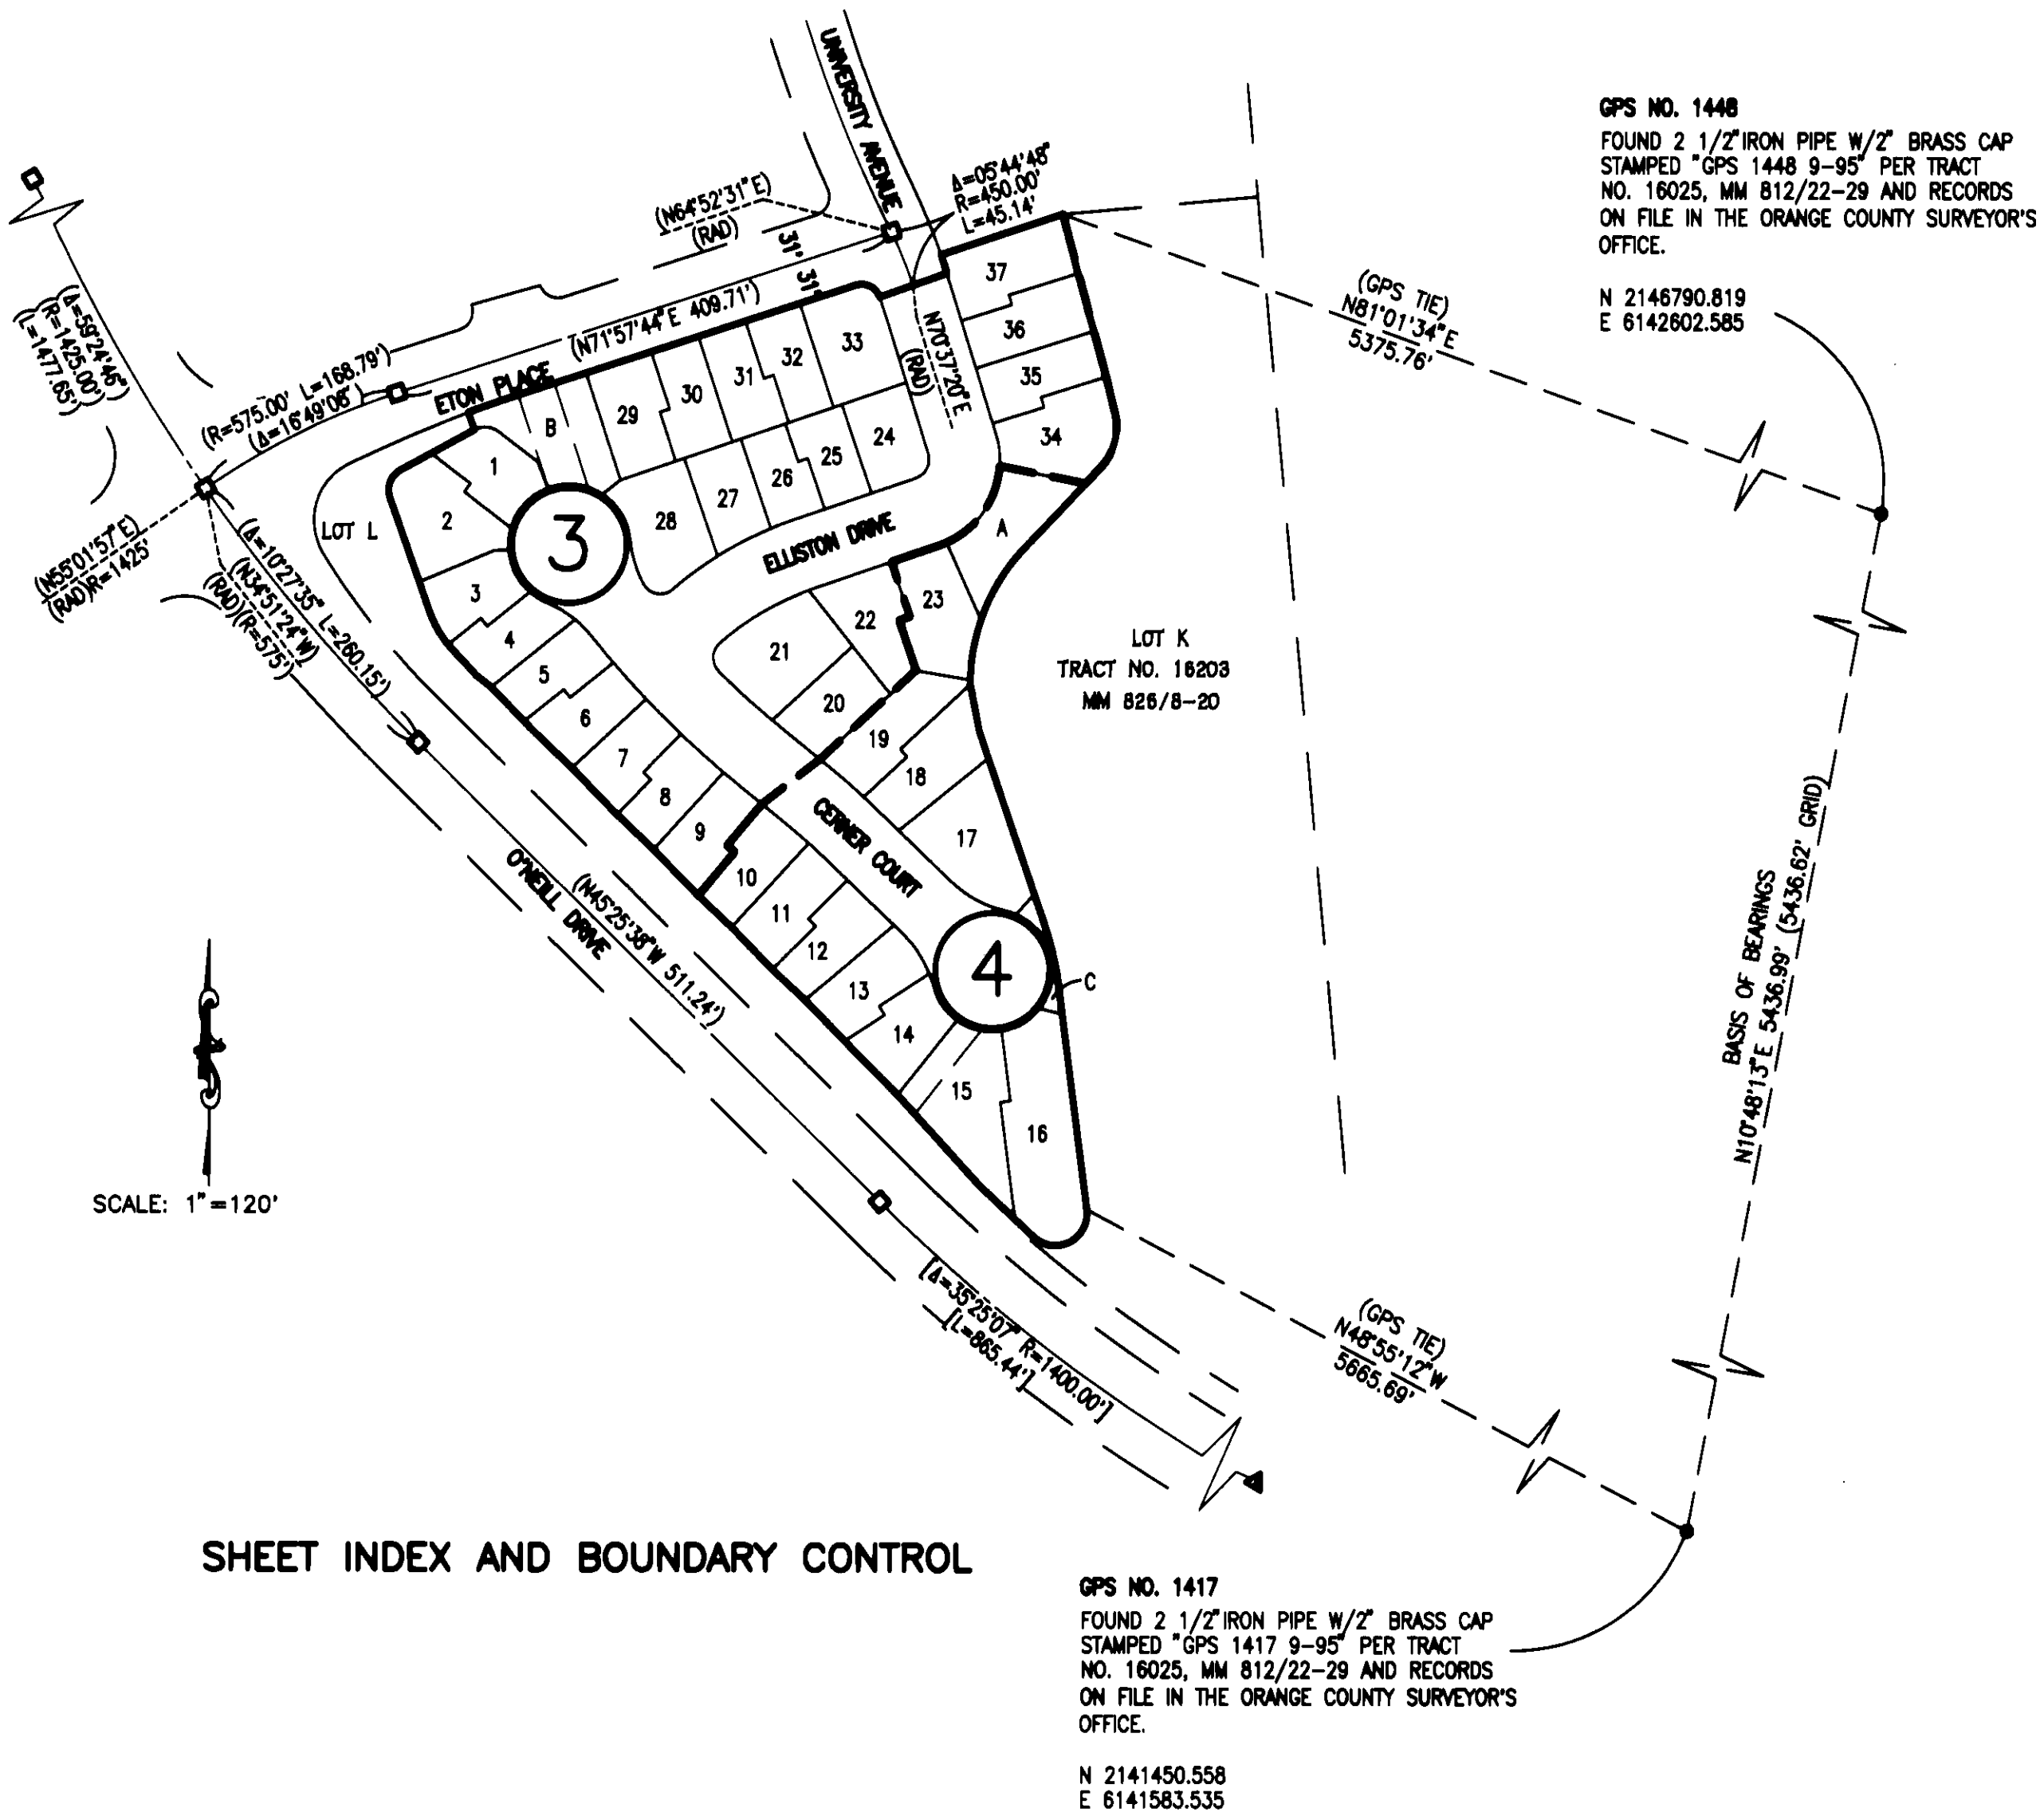

SHEET 3 OF 4 SHEETS

ALL OF TENTATIVE TRACT
MAP NO. 16247
TOTAL LOTS: 1-37 AND LOTS A-C
TOTAL ACREAGE: 5.412 AC.
DATE OF SURVEY: OCTOBER, 2001


TRACT MAP NO. 16247

IN THE UNINCORPORATED TERRITORY OF THE COUNTY OF ORANGE,
STATE OF CALIFORNIA

ADAMS - STREETER CIVIL ENGINEERING, INC. JAN A. ADAMS, R.C.E. 21687
DATE OF SURVEY: OCTOBER, 2001

NOTES:

- SEE SHEET 2 FOR BOUNDARY CONTROL SHEET INDEX,
MONUMENT NOTES, EASEMENT NOTES, LOT INFORMATION
DATUM STATEMENT AND BASIS OF BEARINGS.

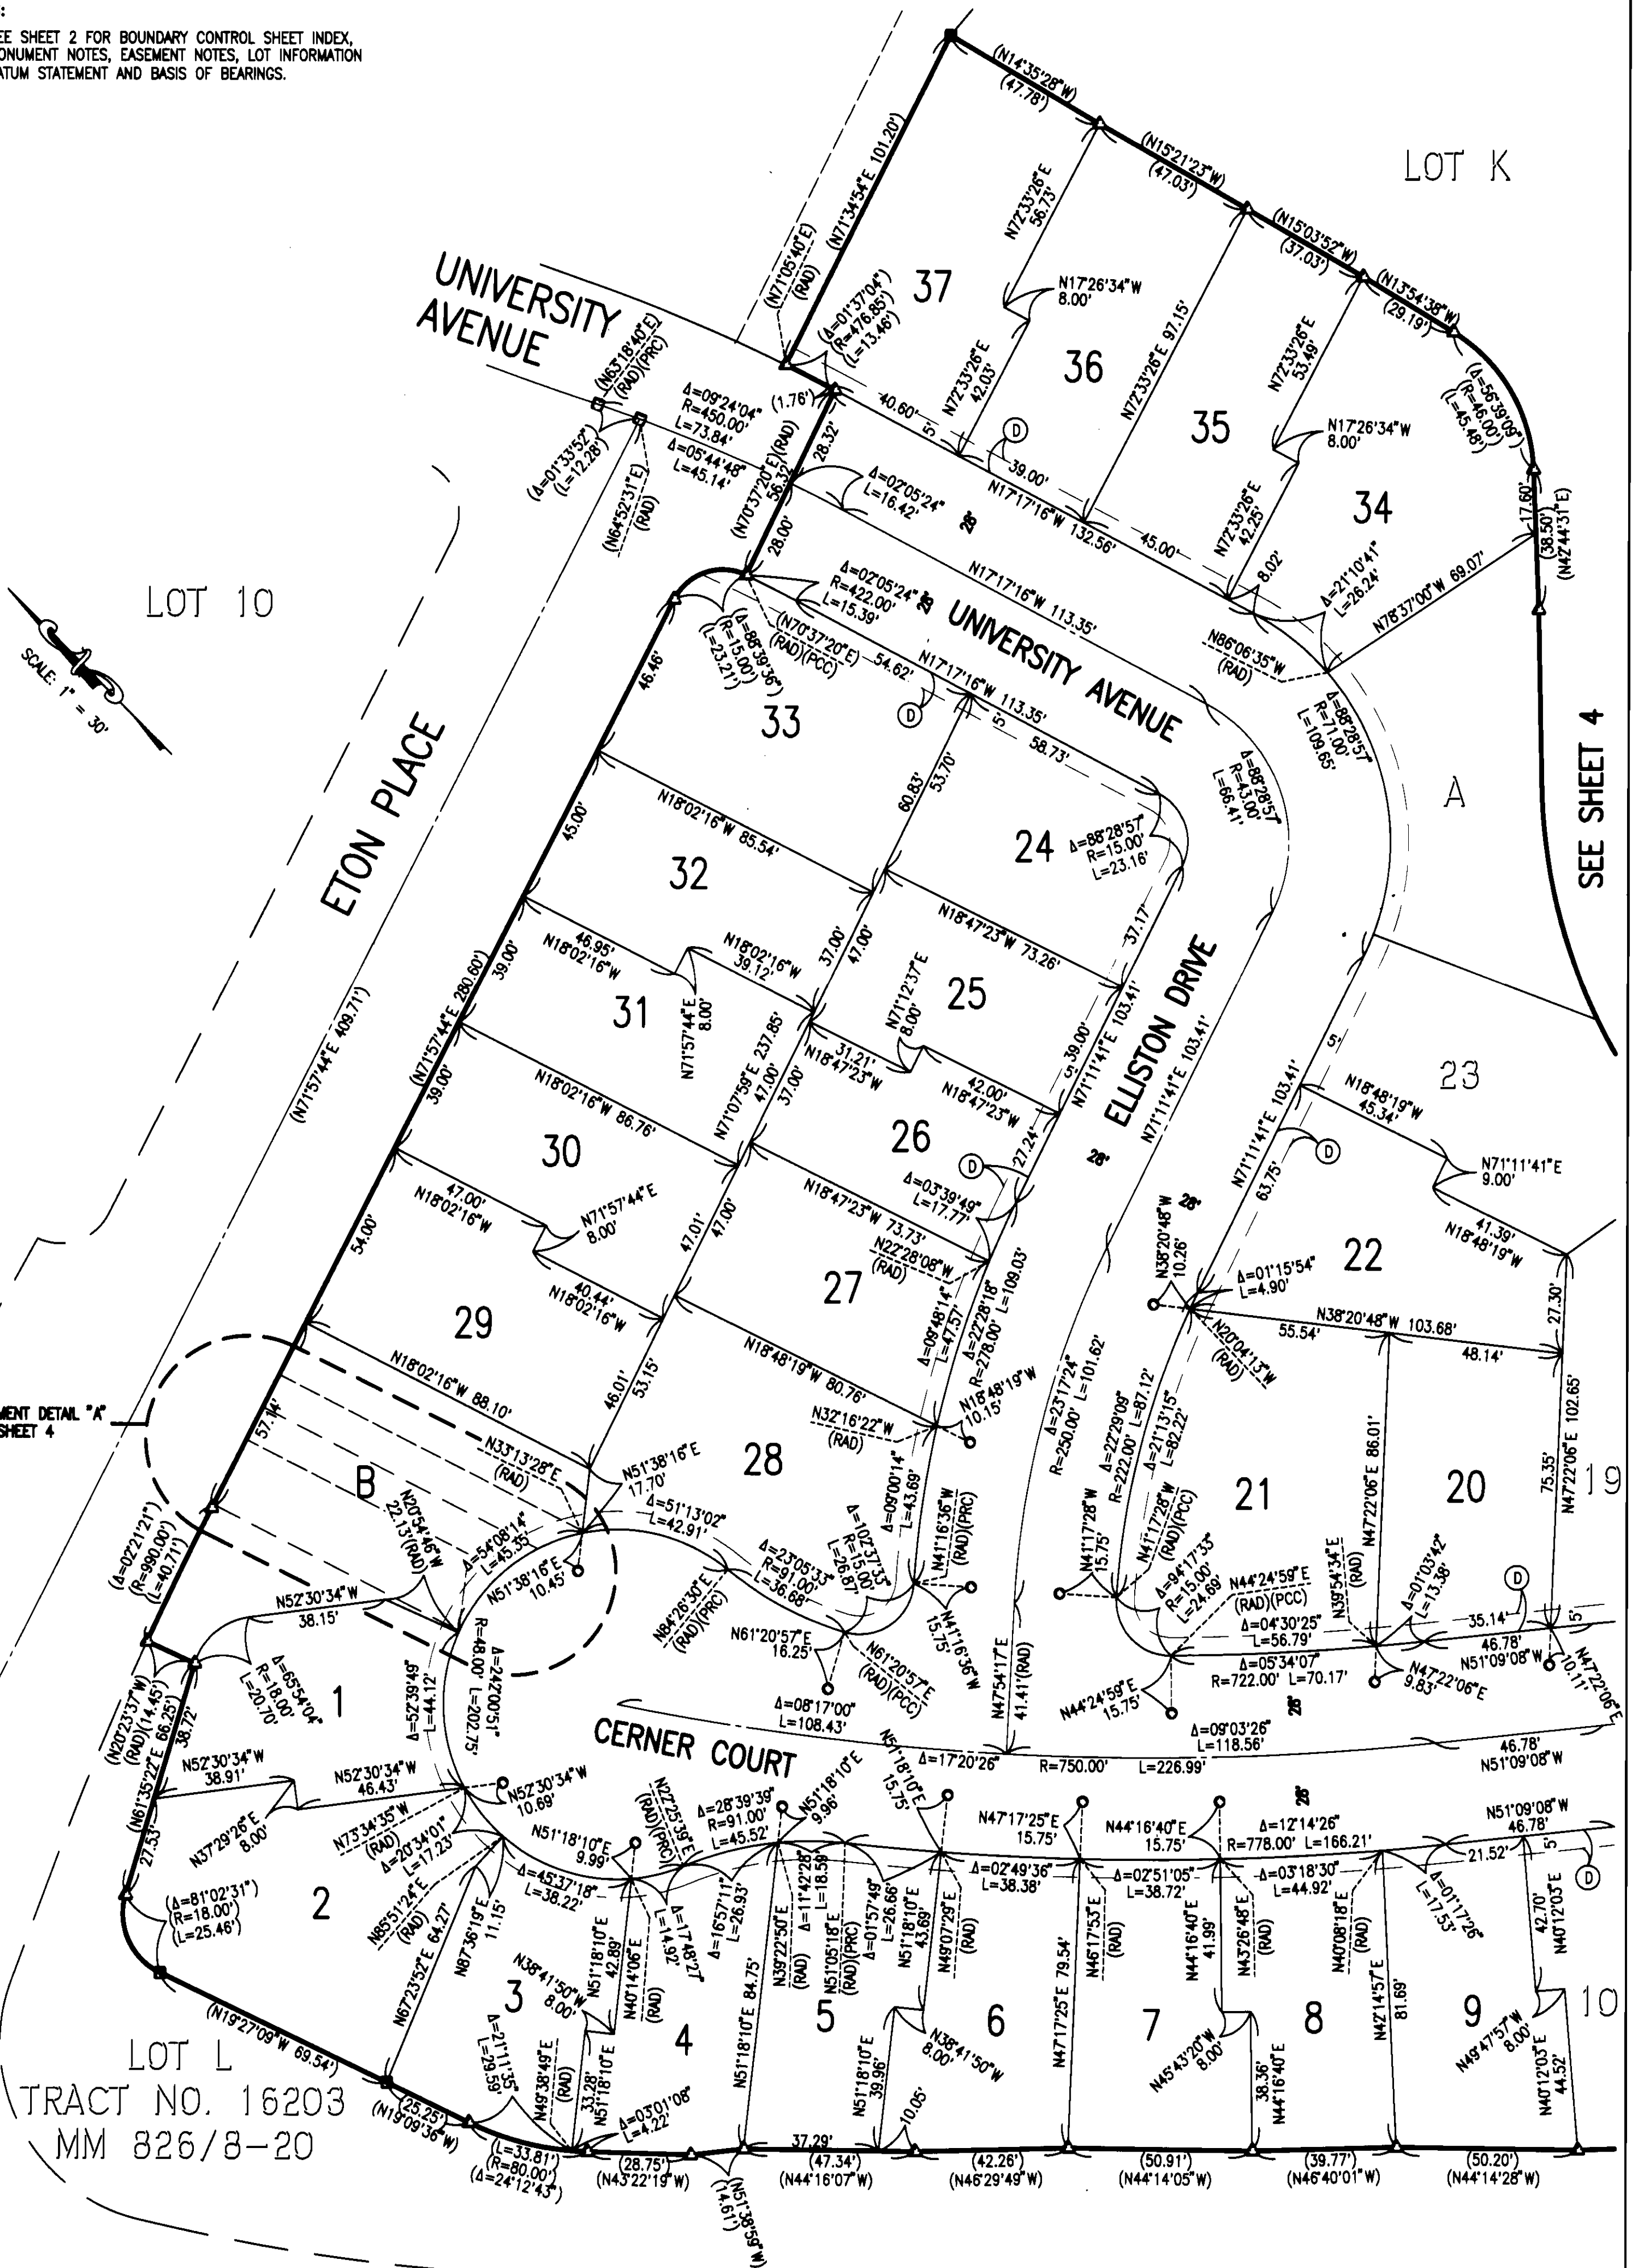

LOT L
TRACT NO. 16203
MM 826/8-20

SEE SHEET 4

SHEET 4 OF 4 SHEETS

ALL OF TENTATIVE TRACT
MAP NO. 16247
TOTAL LOTS: 1-37 AND LOTS A-C
TOTAL ACREAGE: 5.412 AC.
DATE OF SURVEY: OCTOBER, 2001

TRACT MAP NO. 16247

IN THE UNINCORPORATED TERRITORY OF THE COUNTY OF ORANGE,
STATE OF CALIFORNIA
ADAMS - STREETER CIVIL ENGINEERING, INC. JAN A. ADAMS, R.C.E. 21687
DATE OF SURVEY: OCTOBER, 2001

NOTES:

- SEE SHEET 2 FOR BOUNDARY CONTROL SHEET INDEX,
MONUMENT NOTES, EASEMENT NOTES, LOT INFORMATION
DATUM STATEMENT AND BASIS OF BEARINGS.

