

SHEET 1 OF 7 SHEETS

FINAL UNIT OF VESTING TENTATIVE
TRACT MAP NO. 16248
TOTAL LOTS: NUMBERED LOTS 1-55
AND LETTERED LOTS A-Y INCLUSIVE
TOTAL ACREAGE: 6.963 AC.
DATE OF SURVEY: MARCH, 2002

TRACT MAP NO. 16248

IN THE UNINCORPORATED TERRITORY OF THE COUNTY OF ORANGE,
STATE OF CALIFORNIA

BEING A SUBDIVISION OF PARCEL 8 OF LOT LINE ADJUSTMENT NO. LL 2002-011
RECORDED 11-20-02 AS INSTRUMENT NO. 2002001048546 IN THE OFFICE OF
THE COUNTY RECORDER OF SAID COUNTY, STATE OF CALIFORNIA

ADAMS - STREETER CIVIL ENGINEERING, INC. JAN A. ADAMS, R.C.E. 21687
DATE OF SURVEY: MARCH, 2002

ACCEPTED AND FILED AT THE
REQUEST OF

FIRST AMERICAN TITLE COMPANY

DATE JANUARY 17, 2003
TIME 04:22 PM FEE \$ 19.00
INSTRUMENT # 200300068152
BOOK 839 PAGE 27-33 M/A
TOM DALY
COUNTY CLERK - RECORDER
BY [Signature]
DEPUTY

OWNER'S CERTIFICATE:

WE, THE UNDERSIGNED, BEING ALL PARTIES HAVING ANY RECORD TITLE INTEREST IN THE LAND COVERED
BY THIS MAP, DO HEREBY CONSENT TO THE PREPARATION AND RECORDATION OF SAID MAP, AS SHOWN
WITHIN THE DISTINCTIVE BORDER LINE.

WE HEREBY DEDICATE TO THE COUNTY OF ORANGE:

1. AN EASEMENT FOR EMERGENCY AND PUBLIC SERVICE VEHICULAR INGRESS-EGRESS PURPOSES
AS SHOWN ON THIS MAP.

WE ALSO DEDICATE TO THE SANTA MARGARITA WATER DISTRICT, THE EASEMENTS FOR SEWER, WATER
AND ACCESS PURPOSES AS SHOWN ON SAID MAP, WHICH EASEMENTS SHALL BE SUBJECT TO THE
SAME TERMS AND CONDITIONS AS ARE SHOWN IN THAT CERTAIN EASEMENT RECORDED OCTOBER 6, 1980,
IN BOOK 13776, PAGE 341, OF OFFICIAL RECORDS, COUNTY OF ORANGE.

BARRATT-BAYWOOD II, LLC, A CALIFORNIA LIMITED LIABILITY COMPANY

[Signature]
PRINT NAME S. R. REID
PRINT TITLE MANAGING MEMBER

[Signature]
PRINT NAME R. W. LAING
PRINT TITLE MANAGING MEMBER

DMB LADERA, LLC A DELAWARE LIMITED LIABILITY COMPANY AS BENEFICIARY UNDER A DEED
OF TRUST RECORDED FEBRUARY 19, 2002 AS INSTRUMENT NO. 20020140148 OF OFFICIAL RECORDS.

BY: RANCHO MISSION VIEJO, LLC, A DELAWARE LIMITED LIABILITY COMPANY, AS AGENT AND/OR MANAGER.

[Signature]
PRINT NAME Donald T. Stahl
PRINT TITLE Director of Community Development

[Signature]
PRINT NAME Stephen C. Schrank
PRINT TITLE Exec Vice Pres

BANK OF AMERICA, A NATIONAL BANKING ASSOCIATION AS BENEFICIARY UNDER A DEED OF
TRUST RECORDED FEBRUARY 19, 2002 AS INSTRUMENT NO. 20020140149 OF OFFICIAL RECORDS.

[Signature]
PRINT NAME CATHERYN OLIVER
PRINT TITLE VICE PRESIDENT

[Signature]
PRINT NAME Carla A. Wells
PRINT TITLE Vice President

STATE OF CALIFORNIA)
COUNTY OF San Diego)ss

ON THIS 21st DAY OF MAY, 2002, BEFORE ME, Stephanie C. Hagan A NOTARY
PUBLIC IN AND FOR SAID STATE, PERSONALLY APPEARED Donald T. Stahl AND Robert W. Laing
PERSONALLY KNOWN TO ME (OR PROVED TO ME ON THE BASIS OF SATISFACTORY EVIDENCE) TO BE
THE PERSONS WHOSE NAMES ARE SUBSCRIBED TO THE WITHIN INSTRUMENT AND ACKNOWLEDGED TO ME
THAT THEY EXECUTED THE SAME IN THEIR AUTHORIZED CAPACITIES AND THAT BY THEIR SIGNATURES ON
THE INSTRUMENT THE PERSON OR THE ENTITY UPON BEHALF OF WHICH THE PERSONS ACTED, EXECUTED
THE INSTRUMENT.

WITNESS MY HAND:

[Signature]
NOTARY PUBLIC IN AND FOR SAID STATE
Stephanie C. Hagan
PRINT NAME

MY PRINCIPAL PLACE OF BUSINESS
IS IN San Diego COUNTY

MY COMMISSION EXPIRES March 24, 2004
MY COMMISSION # 1254668

STATE OF CALIFORNIA)
COUNTY OF ORANGE)ss

ON THIS 3rd DAY OF June, 2002, BEFORE ME, Tina T. Baker, A NOTARY
PUBLIC IN AND FOR SAID STATE, PERSONALLY APPEARED Donald T. Stahl AND Stephen C. Schrank
PERSONALLY KNOWN TO ME (OR PROVED TO ME ON THE BASIS OF SATISFACTORY EVIDENCE) TO BE
THE PERSONS WHOSE NAMES ARE SUBSCRIBED TO THE WITHIN INSTRUMENT AND ACKNOWLEDGED TO ME
THAT THEY EXECUTED THE SAME IN THEIR AUTHORIZED CAPACITIES AND THAT BY THEIR SIGNATURES ON
THE INSTRUMENT THE PERSON OR THE ENTITY UPON BEHALF OF WHICH THE PERSONS ACTED, EXECUTED
THE INSTRUMENT.

WITNESS MY HAND:

[Signature]
NOTARY PUBLIC IN AND FOR SAID STATE
Tina T. Baker
PRINT NAME

MY PRINCIPAL PLACE OF BUSINESS
IS IN Orange COUNTY

MY COMMISSION EXPIRES 8-29-04

STATE OF CALIFORNIA)
COUNTY OF San Diego)ss

ON THIS 24th DAY OF May, 2002, BEFORE ME, Peggy J. French, A NOTARY
PUBLIC IN AND FOR SAID STATE, PERSONALLY APPEARED Donald T. Stahl AND Carla A. Wells
PERSONALLY KNOWN TO ME (OR PROVED TO ME ON THE BASIS OF SATISFACTORY EVIDENCE) TO BE
THE PERSONS WHOSE NAMES ARE SUBSCRIBED TO THE WITHIN INSTRUMENT AND ACKNOWLEDGED TO ME
THAT THEY EXECUTED THE SAME IN THEIR AUTHORIZED CAPACITIES AND THAT BY THEIR SIGNATURES ON
THE INSTRUMENT THE PERSON OR THE ENTITY UPON BEHALF OF WHICH THE PERSONS ACTED, EXECUTED
THE INSTRUMENT.

WITNESS MY HAND:

[Signature]
NOTARY PUBLIC IN AND FOR SAID STATE
PEGGY J. FRENCH
PRINT NAME

MY PRINCIPAL PLACE OF BUSINESS
IS IN San Diego COUNTY

MY COMMISSION EXPIRES January 8, 2003
Commission # 1207169

SIGNATURE OMISSIONS

PURSUANT TO THE PROVISIONS OF SECTION 66436 (a)(3) (c) OF THE SUBDIVISION MAP ACT, THE FOLLOWING
SIGNATURES HAVE BEEN OMITTED:

LADERA DEVELOPMENT COMPANY, LLC, HOLDER OF OIL, GAS AND MINERAL RIGHTS RECORDED DECEMBER 10, 1996
AS INSTRUMENT NO. 19960624029 OF OFFICIAL RECORDS.

DMB LADERA, LLC, HOLDER OF EASEMENTS FOR CONSTRUCTION, TELECOMMUNICATIONS,
PUBLIC UTILITIES, SURFACE RUNOFF, PUBLIC STREETS AND IRRIGATION PURPOSES,
RECORDED FEBRUARY 19, 2002 PER INSTRUMENT NOS. 20020140146 AND 20020140027,
BOTH OF OFFICIAL RECORDS.

ENGINEER'S STATEMENT

THIS MAP WAS PREPARED BY ME OR UNDER MY DIRECTION AND IS BASED UPON A FIELD SURVEY IN
CONFORMANCE WITH THE REQUIREMENTS OF THE SUBDIVISION MAP ACT AND LOCAL ORDINANCE AT
THE REQUEST OF BARRATT-BAYWOOD II, LLC IN MARCH, 2002. I HEREBY STATE THAT ALL MONUMENTS
ARE OF THE CHARACTER AND OCCUPY THE POSITIONS INDICATED, OR THAT THEY WILL BE SET IN
SUCH POSITIONS; AND THAT SAID MONUMENTS ARE SUFFICIENT TO ENABLE THE SURVEY TO BE RETRACED.
I HEREBY STATE THAT THIS FINAL MAP SUBSTANTIALLY CONFORMS TO THE CONDITIONALLY APPROVED
TENTATIVE MAP.

JAN A. ADAMS, R.C.E. 21687
EXPIRES: 9/30/05



COUNTY SURVEYOR'S STATEMENT

I HEREBY STATE THAT I HAVE EXAMINED THIS MAP AND HAVE FOUND IT TO BE SUBSTANTIALLY IN
CONFORMANCE WITH THE TENTATIVE MAP AS FILED WITH, AMENDED AND APPROVED BY THE ORANGE
COUNTY SUBDIVISION COMMITTEE; THAT ALL PROVISIONS OF THE SUBDIVISION MAP ACT AND COUNTY
SUBDIVISION REGULATIONS HAVE BEEN COMPLIED WITH AND I AM SATISFIED SAID MAP IS TECHNICALLY
CORRECT.

DATED THIS 6th DAY OF JANUARY, 2003

[Signature]
JOHN CANAS, COUNTY SURVEYOR
EXP. 9-30-05



COUNTY TREASURER - TAX COLLECTOR'S CERTIFICATE

STATE OF CALIFORNIA)
COUNTY OF ORANGE)ss

I HEREBY CERTIFY THAT ACCORDING TO THE RECORDS OF MY OFFICE, THERE ARE NO LIENS AGAINST THE
LAND COVERED BY THIS MAP OR ANY PART THEREOF FOR UNPAID STATE, COUNTY, MUNICIPAL OR LOCAL
TAXES OR SPECIAL ASSESSMENTS COLLECTED AS TAXES.

EXCEPT TAXES OR SPECIAL ASSESSMENTS
COLLECTED AS TAXES NOT YET PAYABLE
AND DO ALSO CERTIFY TO THE RECORDER OF ORANGE COUNTY THAT THE PROVISIONS OF THE
SUBDIVISION MAP ACT HAVE BEEN COMPLIED WITH REGARDING DEPOSITS TO SECURE PAYMENT OF
TAXES OR SPECIAL ASSESSMENTS COLLECTED AS TAXES ON THE LAND COVERED BY THIS MAP

DATED THIS 27th DAY OF December, 2002

JOHN M. W. MOORLACH
COUNTY TREASURER - TAX COLLECTOR

BY [Signature]
DEPUTY TREASURER - TAX COLLECTOR

CLERK OF THE BOARD OF SUPERVISORS CERTIFICATE

STATE OF CALIFORNIA)
COUNTY OF ORANGE)ss

I HEREBY CERTIFY THAT THIS MAP WAS PRESENTED FOR APPROVAL TO THE BOARD OF SUPERVISORS OF
ORANGE COUNTY AT A REGULAR MEETING THEREOF HELD ON THE 14th DAY OF January,
2003, AND THAT THEREUPON SAID BOARD DID, BY AN ORDER DULY PASSED AND ENTERED, APPROVE
SAID MAP.

AND DID ACCEPT ON BEHALF OF THE COUNTY OF ORANGE:

1. THE EASEMENT FOR EMERGENCY AND PUBLIC SERVICE VEHICULAR INGRESS-EGRESS, AS DEDICATED.

DATED THIS 14th DAY OF JANUARY, 2003

[Signature]
DARLENE J. BLOOM, CLERK OF THE BOARD OF SUPERVISORS



CERTIFICATE OF ACCEPTANCE

THE UNDERSIGNED, BEING THE DULY APPOINTED AGENT OF THE SANTA MARGARITA WATER DISTRICT,
A PUBLIC CORPORATION OF ORANGE COUNTY, CALIFORNIA, PURSUANT TO ITS RESOLUTION NO. 88-10-2,
DOES HEREBY ACCEPT ON BEHALF OF SAID DISTRICT THE EASEMENTS FOR SEWER, WATER AND ACCESS
PURPOSES, AS DEDICATED AND AS SHOWN ON THIS TRACT MAP, BY AND BETWEEN THE SANTA MARGARITA
WATER DISTRICT AND DMB LADERA, LLC, AND DOES HEREBY CERTIFY THAT THE GRANTEE CONSENTS
TO THE RECORDATION OF SAID TRACT.

BY [Signature]
DANIEL R. FERONS, CHIEF ENGINEER
SANTA MARGARITA WATER DISTRICT

STATE OF CALIFORNIA)
COUNTY OF ORANGE)ss

ON THIS 4th DAY OF June, 2002, BEFORE ME, ANDREA EVANS A NOTARY
PUBLIC IN AND FOR SAID STATE, PERSONALLY APPEARED Daniel R. Ferons
PERSONALLY KNOWN TO ME (OR PROVED TO ME ON THE BASIS OF SATISFACTORY EVIDENCE) TO BE
THE PERSON WHOSE NAME IS SUBSCRIBED TO THE WITHIN INSTRUMENT AND ACKNOWLEDGED TO ME
THAT HE EXECUTED THE SAME IN HIS AUTHORIZED CAPACITY AND THAT BY HIS SIGNATURE ON
THE INSTRUMENT THE PERSON OR THE ENTITY UPON BEHALF OF WHICH THE PERSON ACTED, EXECUTED
THE INSTRUMENT.

WITNESS MY HAND:

[Signature]
NOTARY PUBLIC IN AND FOR SAID STATE
ANDREA M. EVANS
PRINT NAME

MY PRINCIPAL PLACE OF BUSINESS
IS IN Orange COUNTY

MY COMMISSION EXPIRES April 8, 2004

SHEET 2 OF 7 SHEETS

FINAL UNIT OF VESTING TENTATIVE
TRACT MAP NO. 16248
TOTAL LOTS: NUMBERED LOTS 1-55
AND LETTERED LOTS A-Y INCLUSIVE
TOTAL ACREAGE: 6.963 AC.
DATE OF SURVEY: MARCH, 2002

TRACT MAP NO. 16248

IN THE UNINCORPORATED TERRITORY OF THE COUNTY OF ORANGE,
STATE OF CALIFORNIA

ADAMS - STREETER CIVIL ENGINEERING, INC. JAN A. ADAMS, R.C.E. 21687
DATE OF SURVEY: MARCH, 2002

MONUMENT NOTES:

- INDICATES FOUND MONUMENT AS NOTED.
- △ INDICATES 2" IRON PIPE, TAGGED "R.C.E. 21687", OR LEAD, TACK AND TAG "R.C.E. 21687" IN CONCRETE, OR 8" SPIKE AND WASHER STAMPED "RCE 21687" IN ASPHALT PAVING TO BE SET, UNLESS OTHERWISE NOTED.
- △ INDICATES 2" IRON PIPE, TAGGED "R.C.E. 21687" TO BE SET PRIOR TO RECORDATION.
- INDICATES LEAD, TACK AND TAG "R.C.E. 21687" TO BE SET ON AN OFFSET SHOWN HEREON OUTSIDE THE TRUE LOT CORNER IN THE TOP OF ADJACENT CONCRETE CURB, UNLESS OTHERWISE NOTED.
- INDICATES LOCATION OF 1" IRON PIPE, TAGGED "LS 5557", OR SPIKE AND WASHER, STAMPED "LS 5557", OR LEAD, TACK AND TAG "LS 5557" TO BE SET PER TRACT NO. 16203, MM 826/8-20, UNLESS OTHERWISE NOTED.
- INDICATES LOCATION OF 2" IRON PIPE, TAGGED "LS 5557", OR SPIKE AND WASHER, STAMPED "LS 5557", OR LEAD, TACK AND TAG "LS 5557" TO BE SET PER TRACT NO. 16203, MM 826/8-20, UNLESS OTHERWISE NOTED.
- 1" IRON PIPE TAGGED "R.C.E. 21687", OR SPIKE AND WASHER STAMPED "R.C.E. 21687", OR LEAD, TACK AND TAG STAMPED "R.C.E. 21687" TO BE SET AT ALL LOT CORNERS, EXCEPT AT THOSE LOT CORNERS THAT ABUT A STREET, IN WHICH CASE A LEAD, TACK AND TAG STAMPED "RCE 21687" WILL BE SET ON THE PROLONGATION OF THE SIDE LOT LINE, 0.50 FEET FROM THE TRUE LOT CORNER, IN THE TOP OF ADJACENT CONCRETE CURB, UNLESS OTHERWISE NOTED.
- 8" SPIKE AND WASHER STAMPED "RCE 21687" IN ASPHALT PAVING, OR LEAD, TACK AND TAG "R.C.E. 21687" IN CONCRETE, OR 1" IRON PIPE, TAGGED "RCE 21687" TO BE SET AT ALL CENTERLINE INTERSECTIONS, B.C.'S, E.C.'S AND ALL OTHER CENTERLINE POINTS OF CONTROL, UNLESS OTHERWISE NOTED.
- ALL MONUMENTS SHOWN AS "TO BE SET" WILL BE SET WITHIN 90 DAYS AFTER THE ACCEPTANCE OF THE FINAL IMPROVEMENTS.
- NO MONUMENTS ARE TO BE SET AT BC'S AND EC'S OF STREET RIGHT OF WAY LINES.

LETTERED LOT INFORMATION

LOT	AREA	USE	LOT	AREA	USE
A	0.034 AC.	OPEN SPACE	N	0.359 AC.	PRIVATE STREET
B	0.031 AC.	OPEN SPACE	O	0.356 AC.	PRIVATE STREET
C	0.436 AC.	OPEN SPACE	P	0.255 AC.	PRIVATE STREET
D	0.080 AC.	OPEN SPACE	Q	0.107 AC.	PRIVATE STREET
E	0.080 AC.	OPEN SPACE	R	0.014 AC.	OPEN SPACE
F	0.459 AC.	OPEN SPACE	S	0.009 AC.	OPEN SPACE
G	0.072 AC.	OPEN SPACE	T	0.101 AC.	PRIVATE STREET
H	0.022 AC.	OPEN SPACE	U	0.086 AC.	PRIVATE STREET
I	0.076 AC.	OPEN SPACE	V	0.180 AC.	PRIVATE STREET
J	0.021 AC.	OPEN SPACE	W	0.173 AC.	PRIVATE STREET
K	0.125 AC.	OPEN SPACE	X	0.172 AC.	PRIVATE STREET
L	0.198 AC.	OPEN SPACE	Y	0.253 AC.	PRIVATE STREET
M	0.011 AC.	OPEN SPACE			

EASEMENT NOTES:

- (A) AN EASEMENT FOR EMERGENCY AND PUBLIC SERVICE VEHICULAR INGRESS-EGRESS DEDICATED TO THE COUNTY OF ORANGE.
- (B) AN EASEMENT FOR SEWER AND WATER PIPELINE AND ACCESS PURPOSES DEDICATED TO THE SANTA MARGARITA WATER DISTRICT.

BASIS OF BEARINGS

THE BEARINGS SHOWN HEREON ARE BASED ON THE BEARING BETWEEN ORANGE COUNTY SURVEYOR'S HORIZONTAL CONTROL STATION "GPS NO. 1417" AND "GPS NO. 1448", BEING N 10°48'13" E, AS SHOWN ON THE MAP OF TRACT NO. 16025 FILED IN BOOK 812, PAGES 22 THROUGH 29 OF MISCELLANEOUS MAPS, RECORDS OF ORANGE COUNTY, CALIFORNIA.

DATUM STATEMENT

COORDINATES SHOWN HEREON ARE BASED IN THE CALIFORNIA COORDINATE SYSTEM (CCS83) ZONE VI, 1983 NAD (1991.35 EPOCH, O.C.S. GPS ADJUSTMENT). ALL DISTANCE SHOWN HEREON ARE GROUND, UNLESS OTHERWISE NOTED. TO OBTAIN GRID DISTANCE MULTIPLY GROUND DISTANCE BY 0.99993286.

AUTOMATIC FIRE SPRINKLER NOTE:

ALL RESIDENTIAL STRUCTURES EXCEEDING 5,500 SQUARE FEET AND ALL STRUCTURES EXCEEDING FIRE DEPARTMENT ACCESS REQUIREMENTS SHALL BE PROTECTED BY AN AUTOMATIC FIRE SPRINKLER SYSTEM, IN A MANNER MEETING THE APPROVAL OF THE FIRE CHIEF.

SPECIAL FIRE PROTECTION NOTE:

PROPERTY IS CONDITIONALLY EXCLUDED FROM A SPECIAL FIRE PROTECTION AREA.

ALL REQUIREMENTS FOR DEVELOPMENT AND CONSTRUCTION WITHIN A "SPECIAL FIRE PROTECTION AREA" INCLUDING INCREASED STREET WIDTHS AND CLASS A ROOF ASSEMBLIES WILL BE MET.

PROPERTY IS IN A "(HIGH/VERY HIGH) FIRE HAZARD AREA" DUE TO WILDLAND EXPOSURE BASED ON STATE SRA MAPS.

REFERENCES:

() INDICATES MEASURED AND RECORD PER TRACT MAP NO. 16203, M.M. 826/8-20.


NOTES:

LETTERED LOTS ARE NOT SEPARATE BUILDING SITES.

LOTS DESIGNATED AS OPEN SPACES ARE FOR LANDSCAPE PURPOSES AND WILL BE MAINTAINED BY THE HOMEOWNER'S ASSOCIATION.

(X) - INDICATES SHEET NUMBER.

SHEET INDEX AND BOUNDARY CONTROL

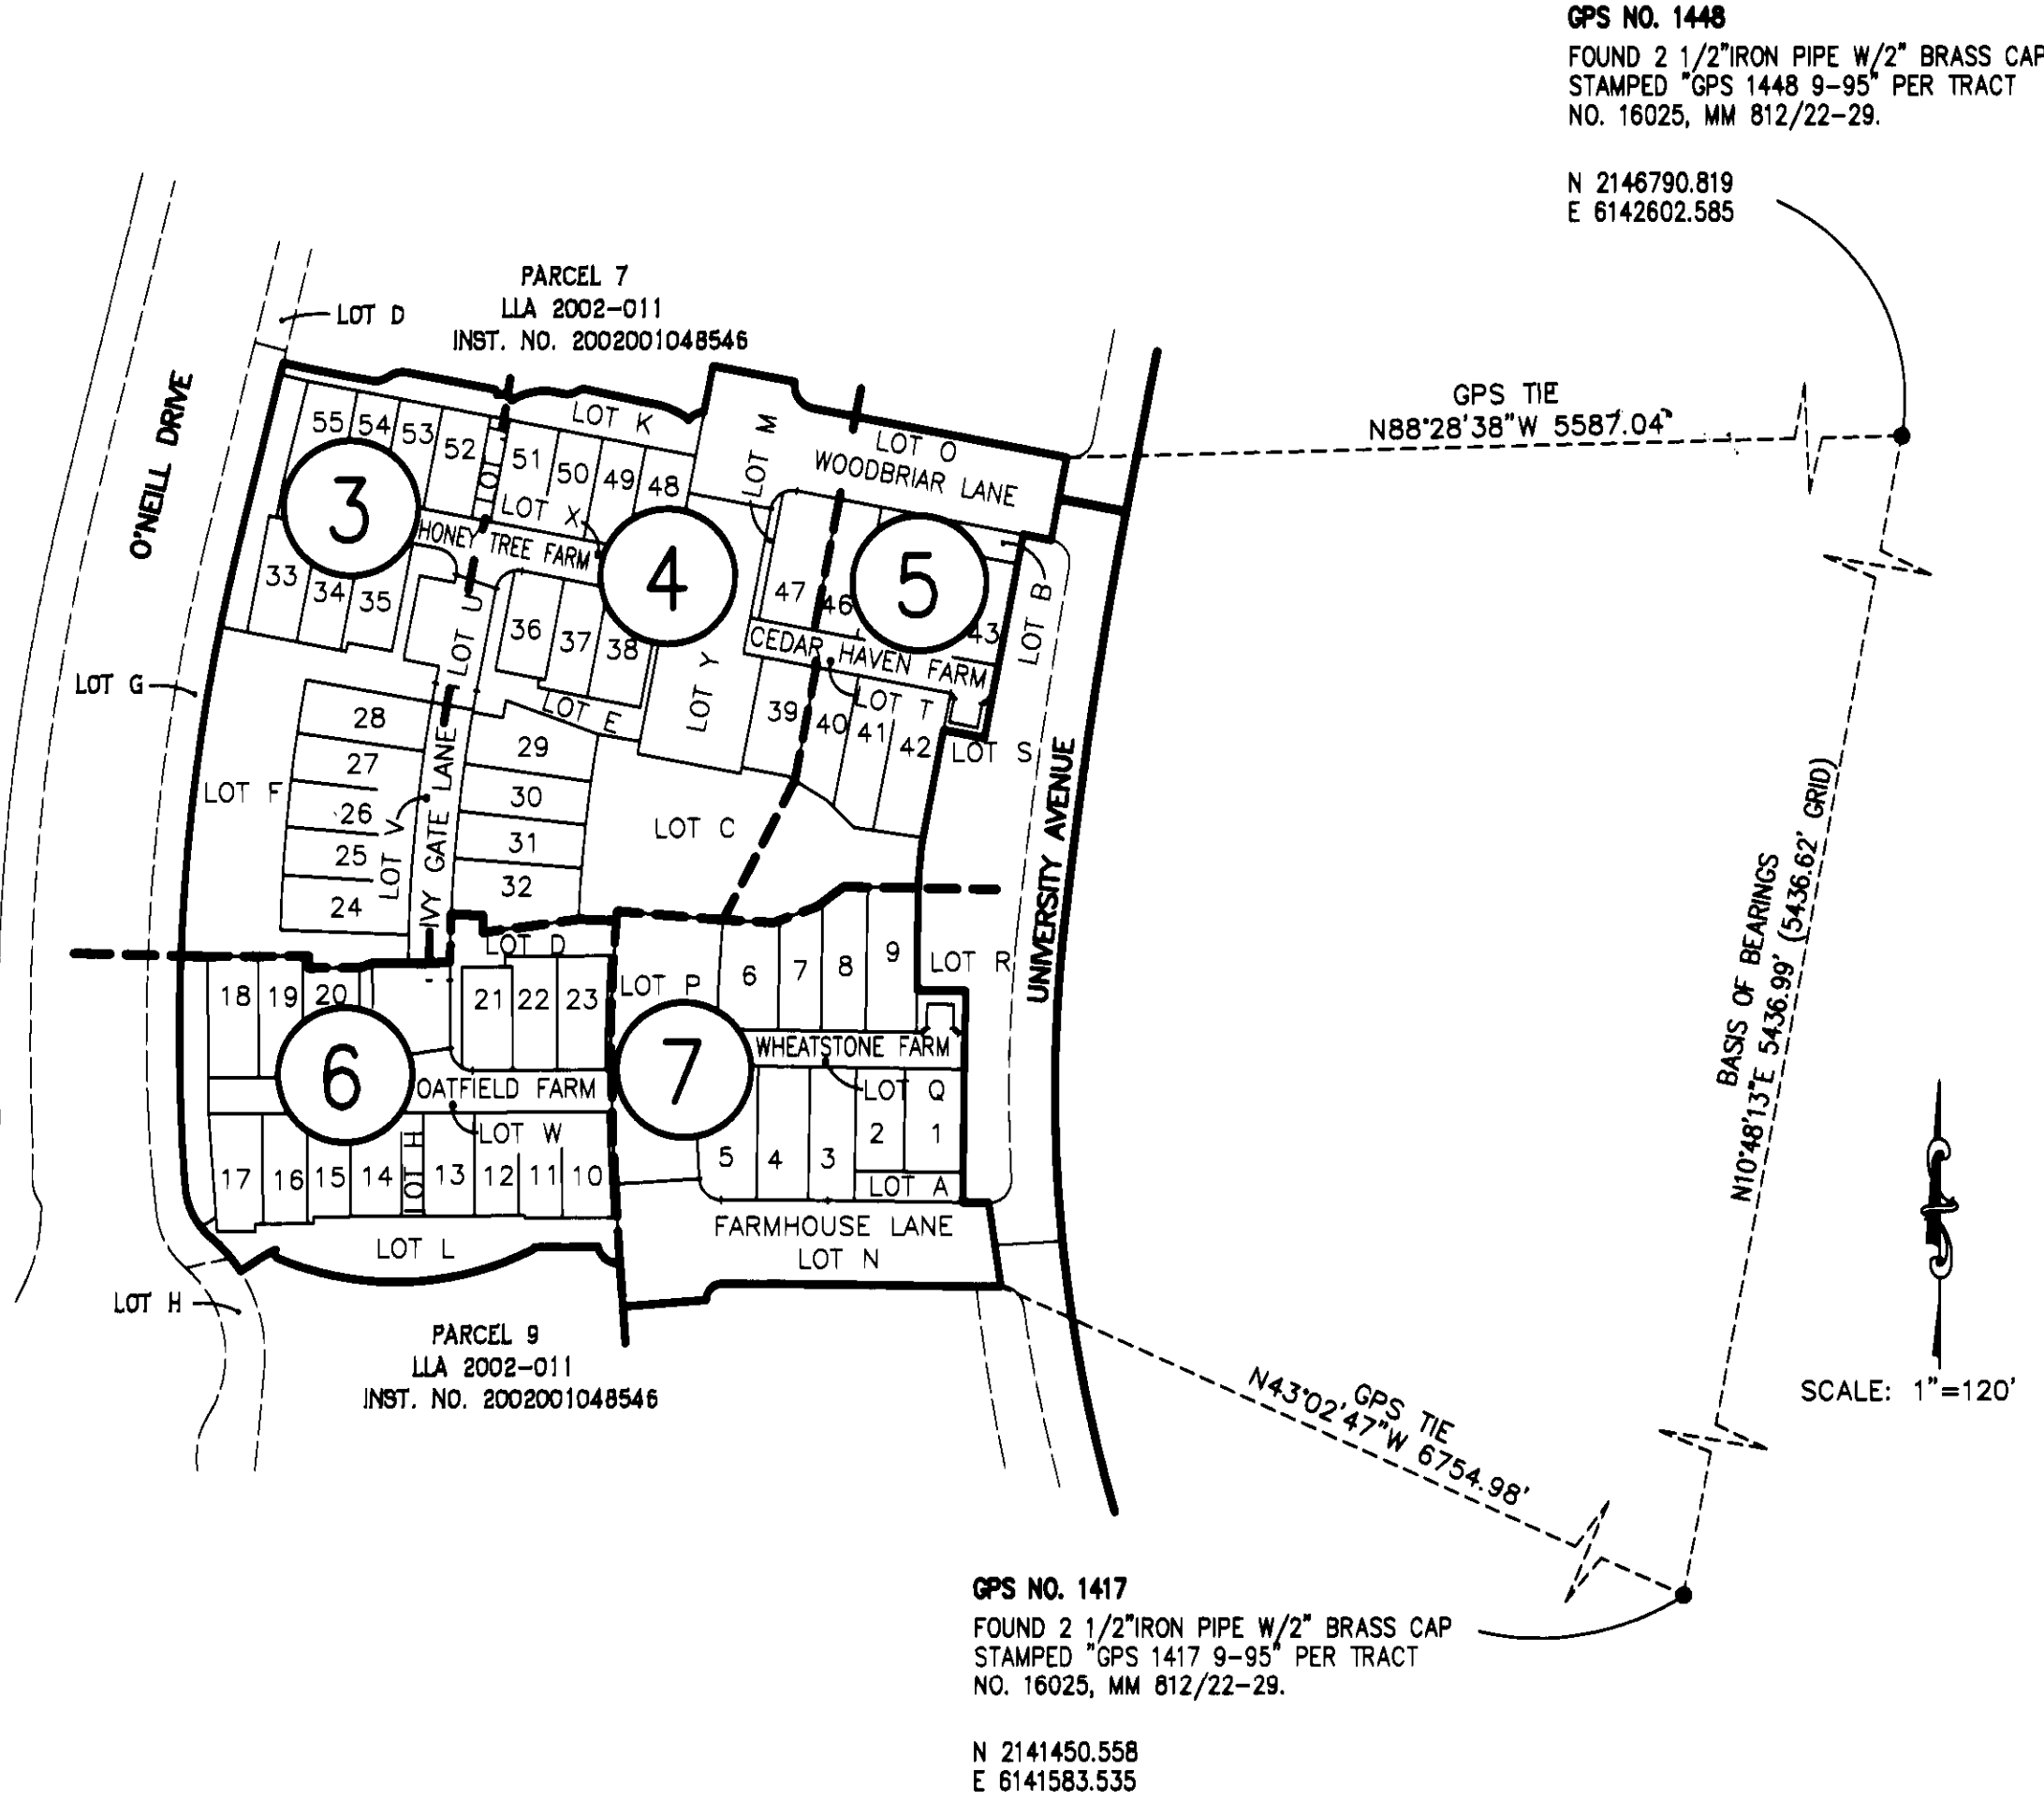

SHEET 3 OF 7 SHEETS

FINAL UNIT OF VESTING TENTATIVE
TRACT MAP NO. 16248
TOTAL LOTS: NUMBERED LOTS 1-55
AND LETTERED LOTS A-Y INCLUSIVE
TOTAL ACREAGE: 6.963 AC.
DATE OF SURVEY: MARCH, 2002

TRACT MAP NO. 16248

IN THE UNINCORPORATED TERRITORY OF THE COUNTY OF ORANGE,
STATE OF CALIFORNIA

ADAMS - STREETER CIVIL ENGINEERING, INC. JAN A. ADAMS, R.C.E. 21687
DATE OF SURVEY: MARCH, 2002

PARCEL 7
LLA 2002-011
INST. NO. 2002001048546

CL O'NEILL DRIVE

(A=48°57'11" R=1425.00' L=1217.51')

LOT G
TRACT NO. 16203
MM 826/8-20

LOT F

SEE SHEET 6

HONEY TREE FARM
(PVT. ST.)

LOT X

LOT U

LOT E

MY GATE LANE
(PVT. ST.)

LOT V

LOT D

SEE SHEET 4

SCALE: 1"=20'

SHEET 4 OF 7 SHEETS

TRACT MAP NO. 16248

IN THE UNINCORPORATED TERRITORY OF THE COUNTY OF ORANGE,
STATE OF CALIFORNIA


FINAL UNIT OF VESTING TENTATIVE
TRACT MAP NO. 16248
TOTAL LOTS: NUMBERED LOTS 1-55
AND LETTERED LOTS A-Y INCLUSIVE
TOTAL ACREAGE: 6.963 AC.
DATE OF SURVEY: MARCH, 2002

ADAMS - STREETER CIVIL ENGINEERING, INC. JAN A. ADAMS, R.C.E. 21687
DATE OF SURVEY: MARCH, 2002

SEE SHEET 3

LOT V

SEE SHEET 5

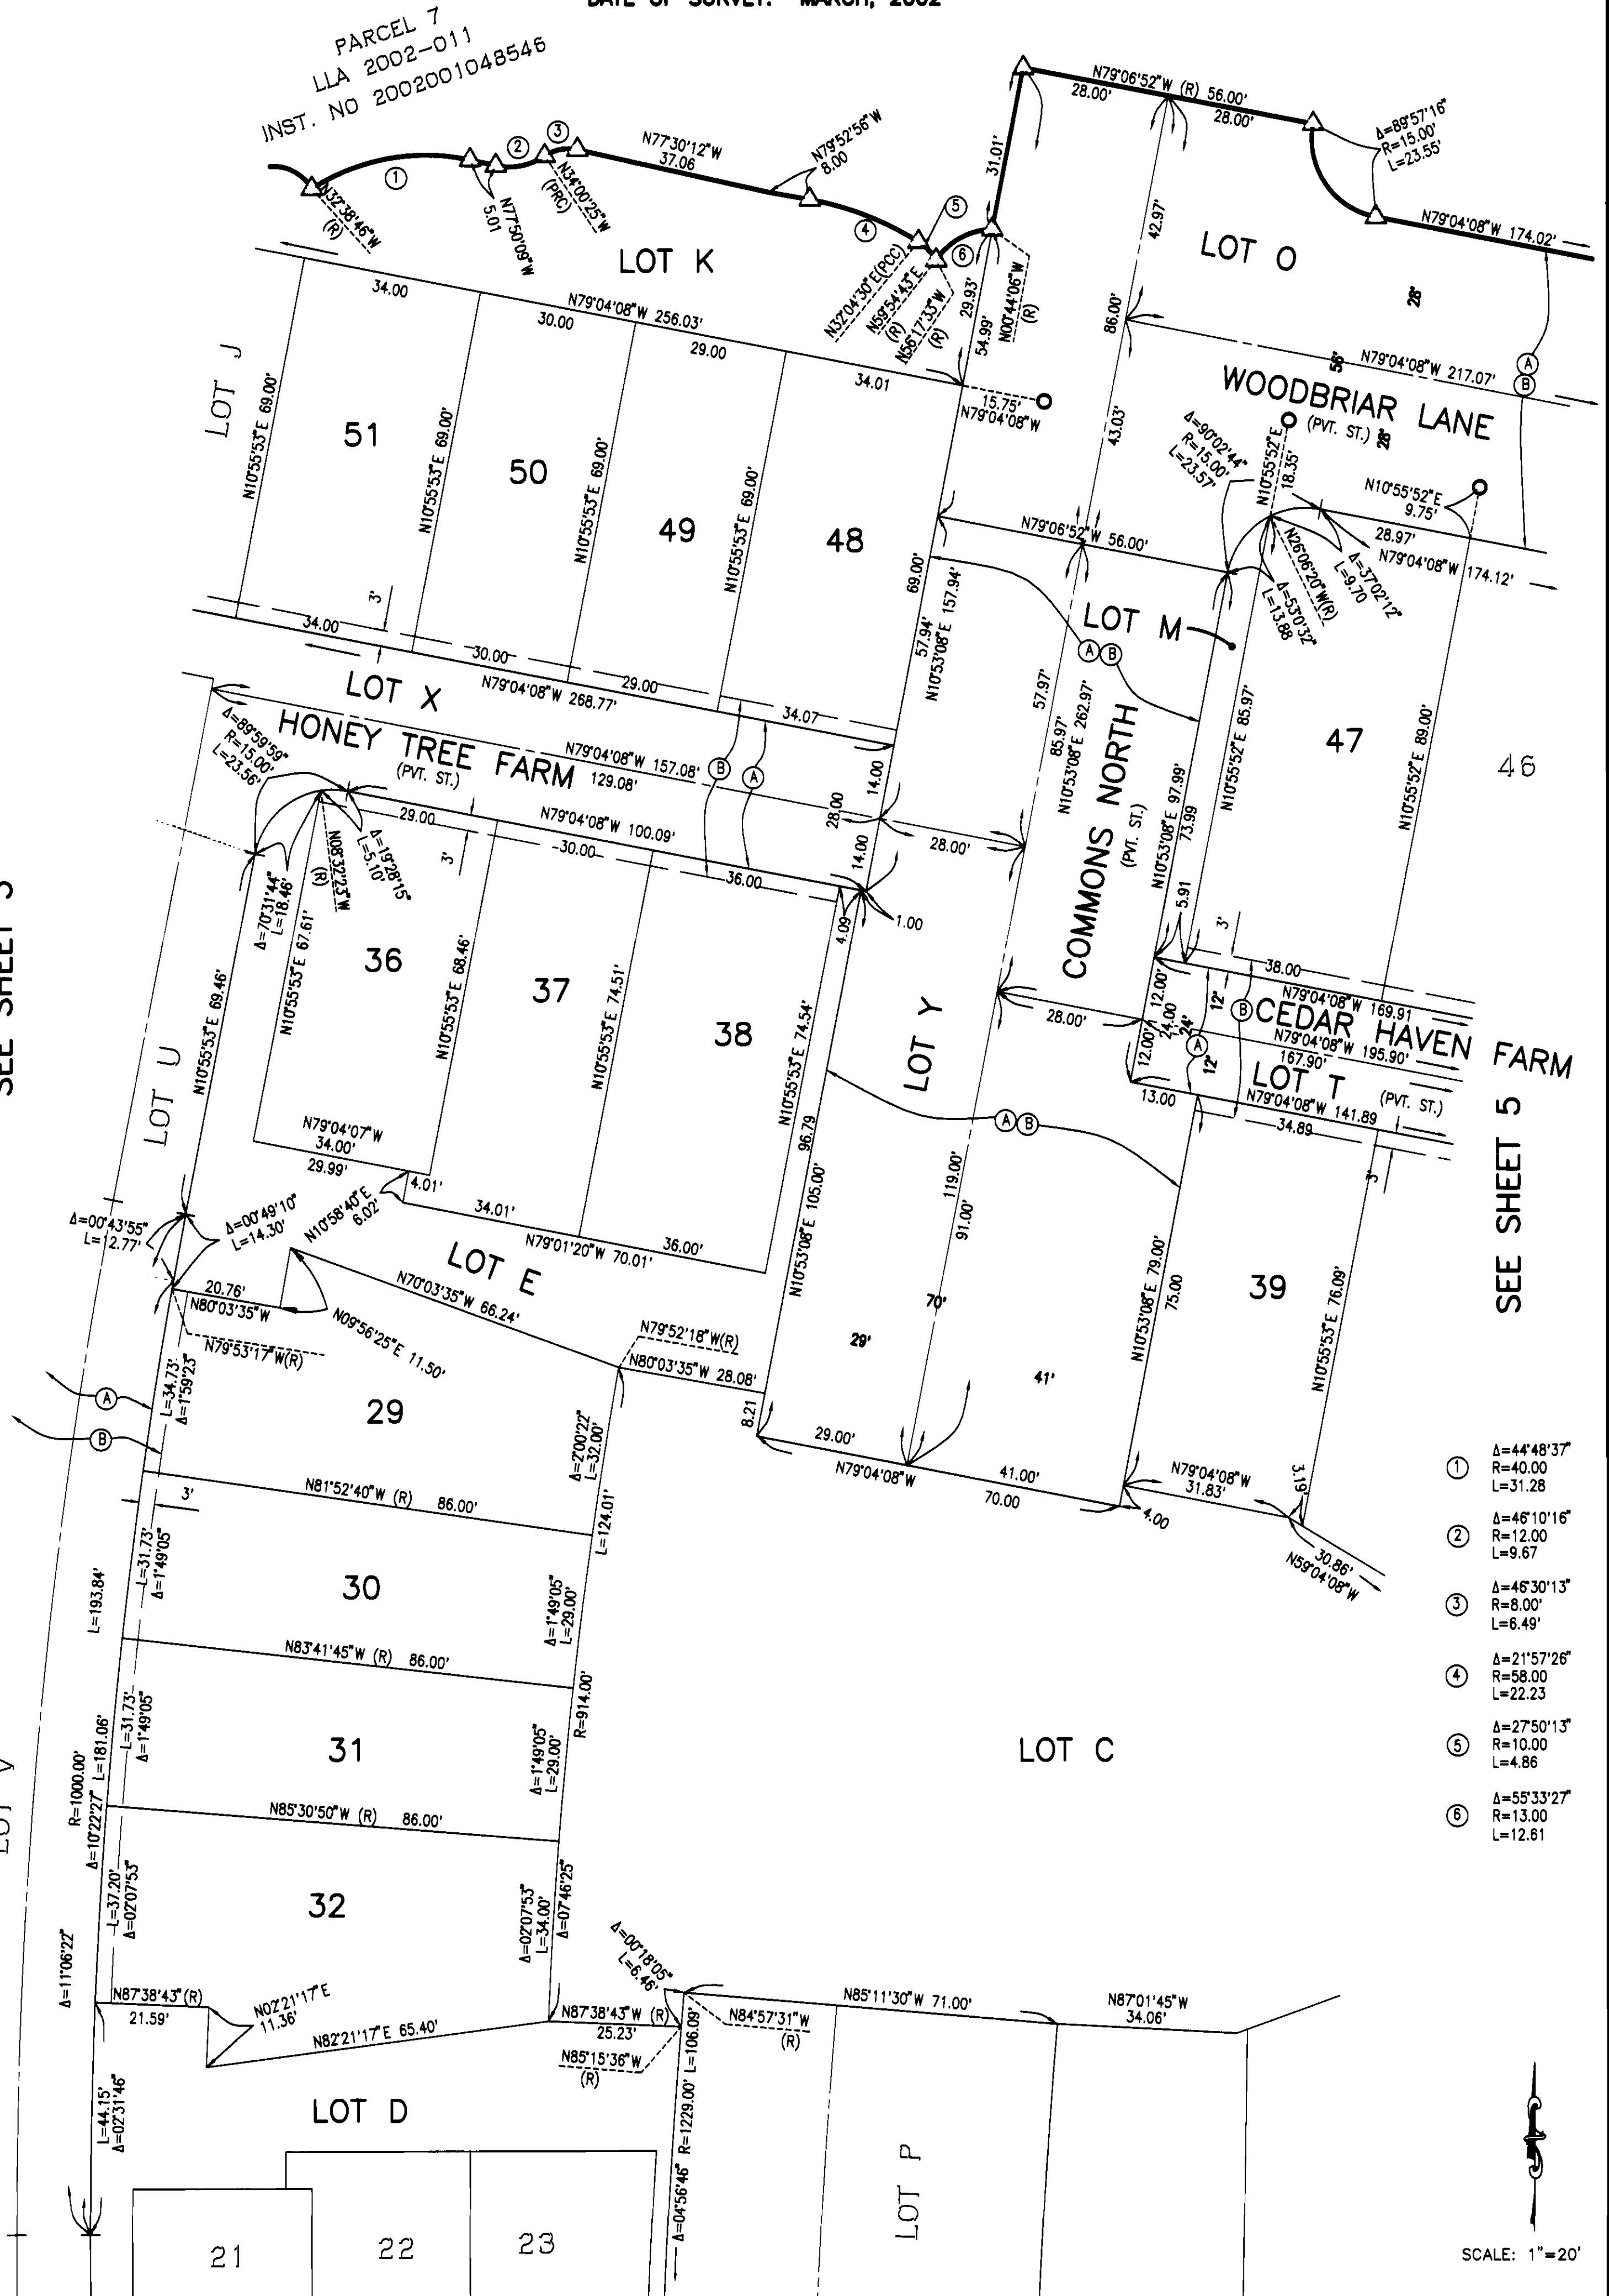

- ① $\Delta=44^{\circ}48'37''$
 $R=40.00$
 $L=31.28$
- ② $\Delta=46^{\circ}10'16''$
 $R=12.00$
 $L=9.67$
- ③ $\Delta=46^{\circ}30'13''$
 $R=8.00$
 $L=6.49$
- ④ $\Delta=21^{\circ}57'26''$
 $R=58.00$
 $L=22.23$
- ⑤ $\Delta=27^{\circ}50'13''$
 $R=10.00$
 $L=4.86$
- ⑥ $\Delta=55^{\circ}33'27''$
 $R=13.00$
 $L=12.61$

SCALE: 1"=20'

SEE SHEET 6

SHEET 5 OF 7 SHEETS

FINAL UNIT OF VESTING TENTATIVE
TRACT MAP NO. 16248
TOTAL LOTS: NUMBERED LOTS 1-55
AND LETTERED LOTS A-Y INCLUSIVE
TOTAL ACREAGE: 6.963 AC.
DATE OF SURVEY: MARCH, 2002

TRACT MAP NO. 16248


IN THE UNINCORPORATED TERRITORY OF THE COUNTY OF ORANGE,
STATE OF CALIFORNIA

ADAMS - STREETER CIVIL ENGINEERING, INC. JAN A. ADAMS, R.C.E. 21687
DATE OF SURVEY: MARCH, 2002

① $\Delta=90^{\circ}00'00''$
 $R=3.00'$
 $L=4.71'$



SCALE: 1"=20'

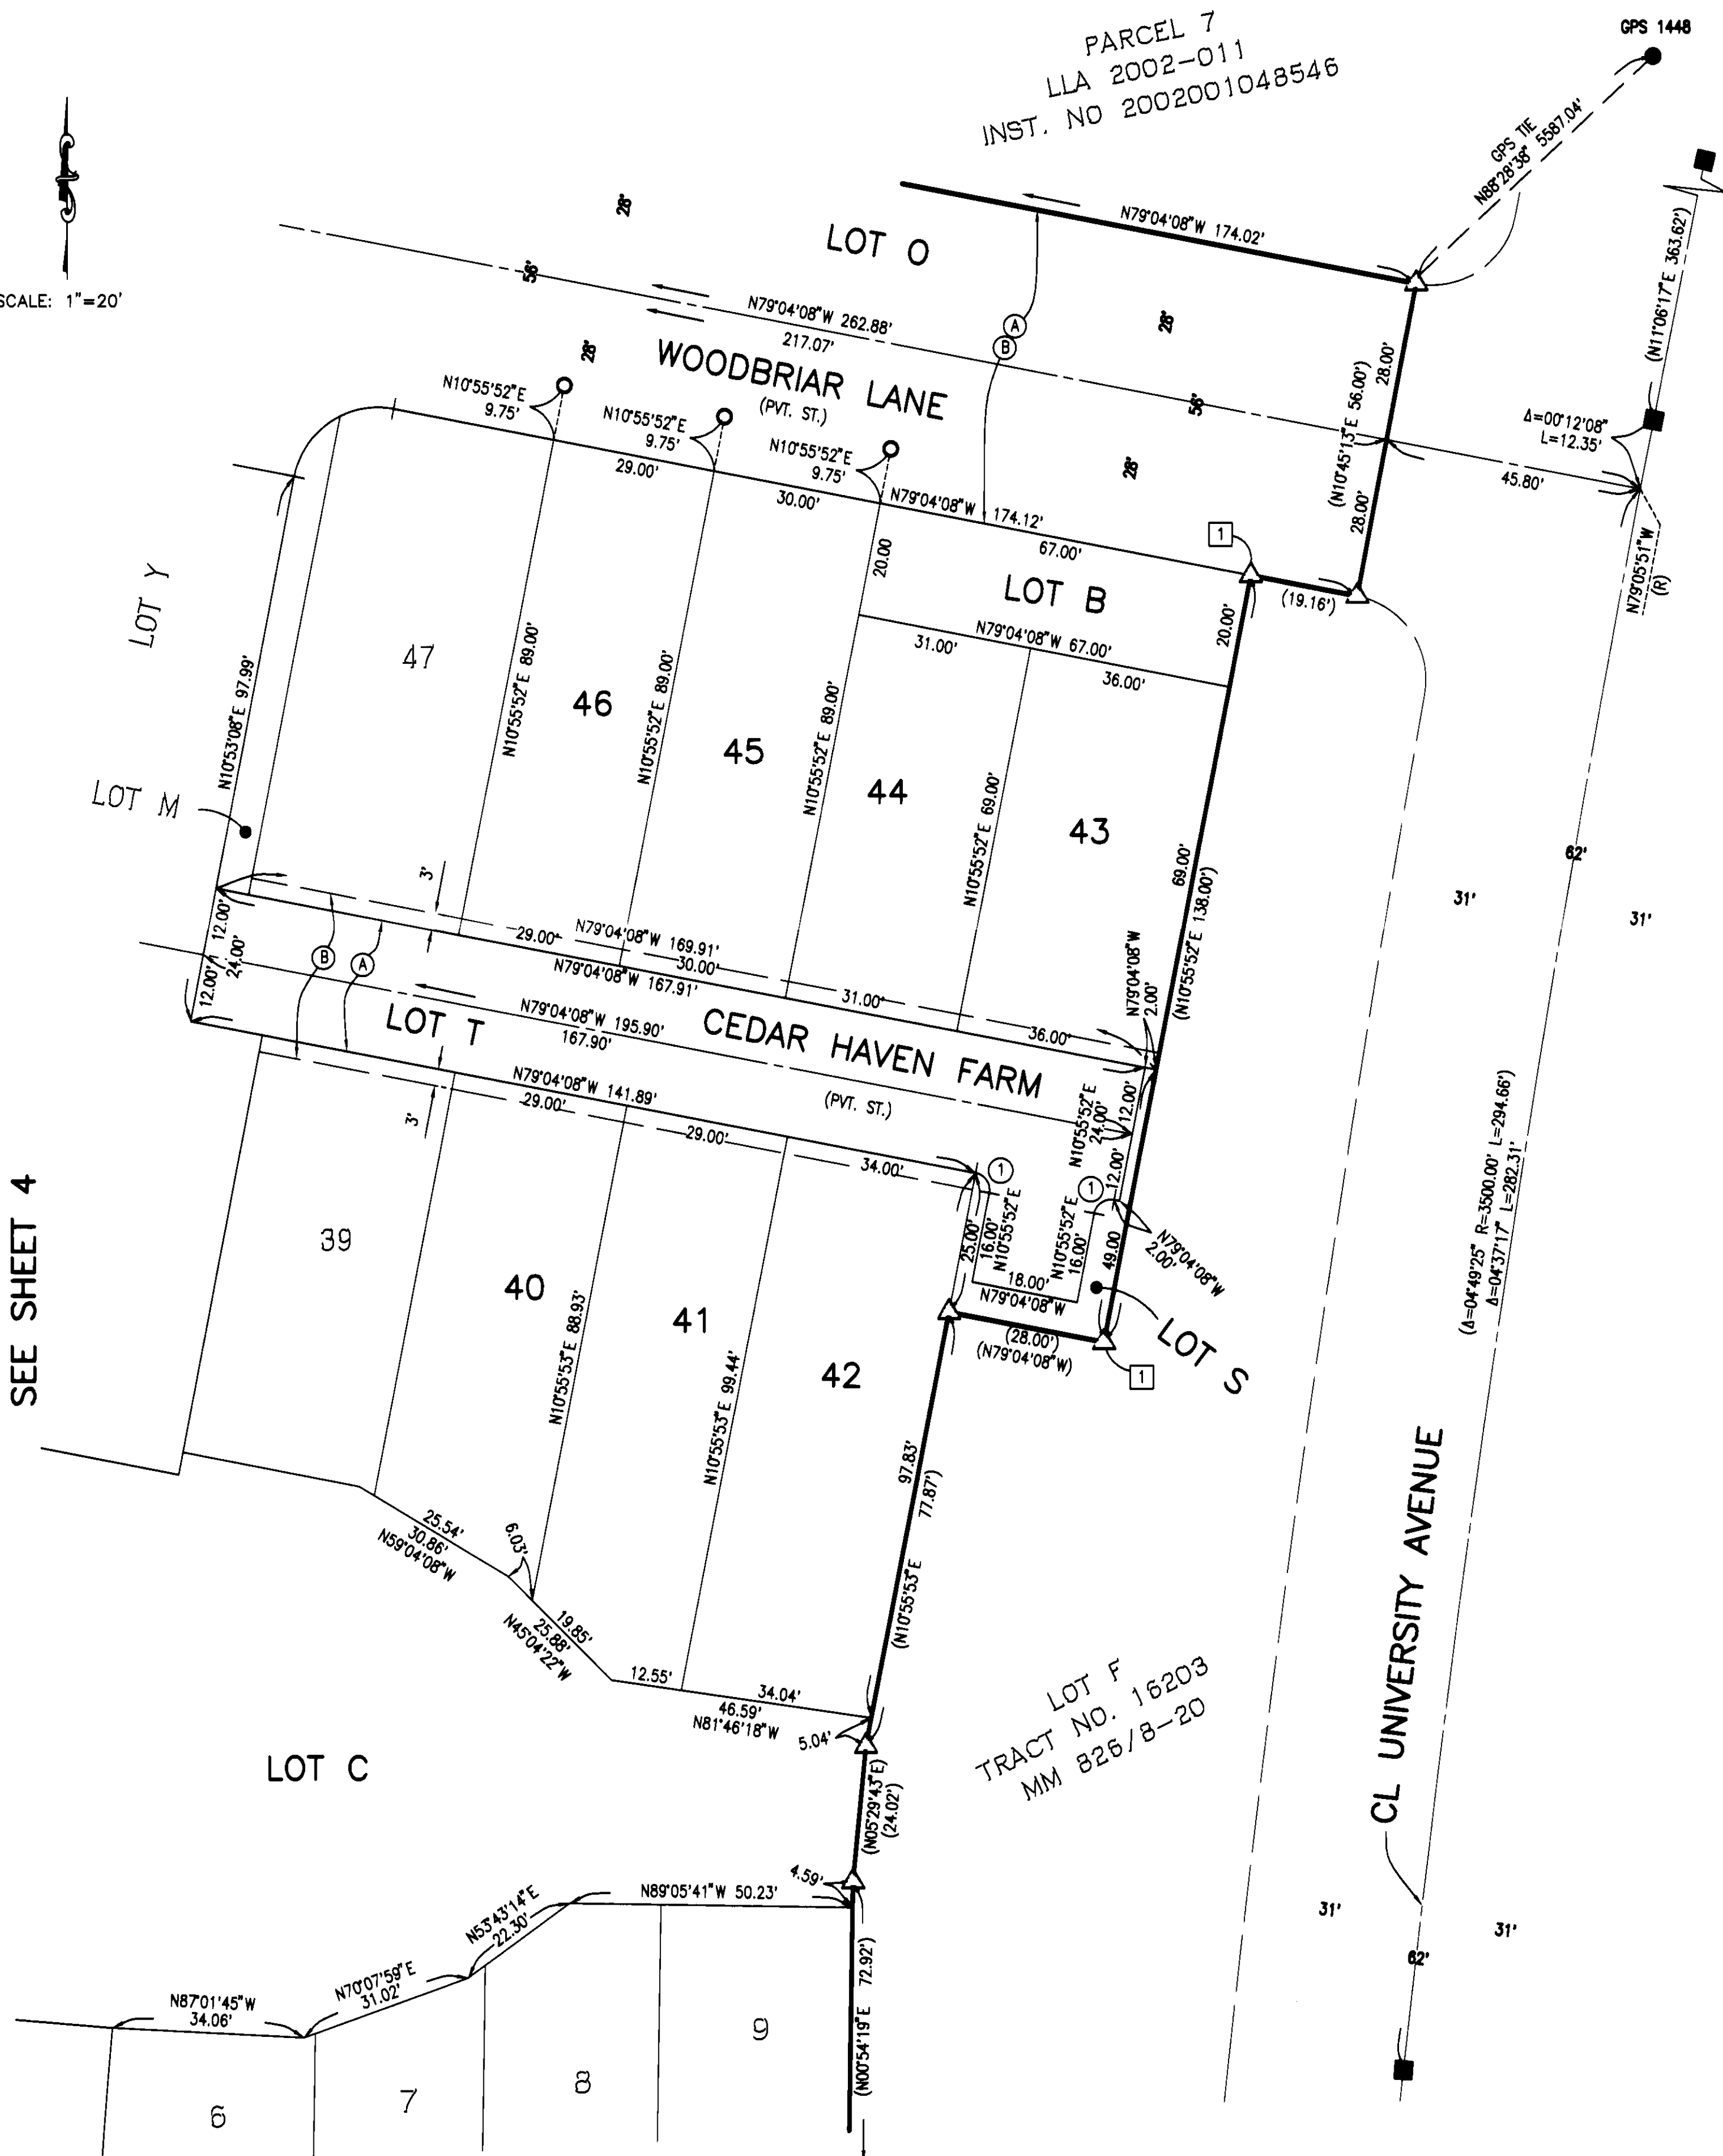

SEE SHEET 4

SEE SHEET 7

SHEET 6 OF 7 SHEETS


FINAL UNIT OF VESTING TENTATIVE
TRACT MAP NO. 16248
TOTAL LOTS: NUMBERED LOTS 1-55
AND LETTERED LOTS A-Y INCLUSIVE
TOTAL ACREAGE: 6.963 AC.
DATE OF SURVEY: MARCH, 2002

TRACT MAP NO. 16248

IN THE UNINCORPORATED TERRITORY OF THE COUNTY OF ORANGE,
STATE OF CALIFORNIA

ADAMS - STREETER CIVIL ENGINEERING, INC. JAN A. ADAMS, R.C.E. 21687
DATE OF SURVEY: MARCH, 2002

SCALE: 1"=20'

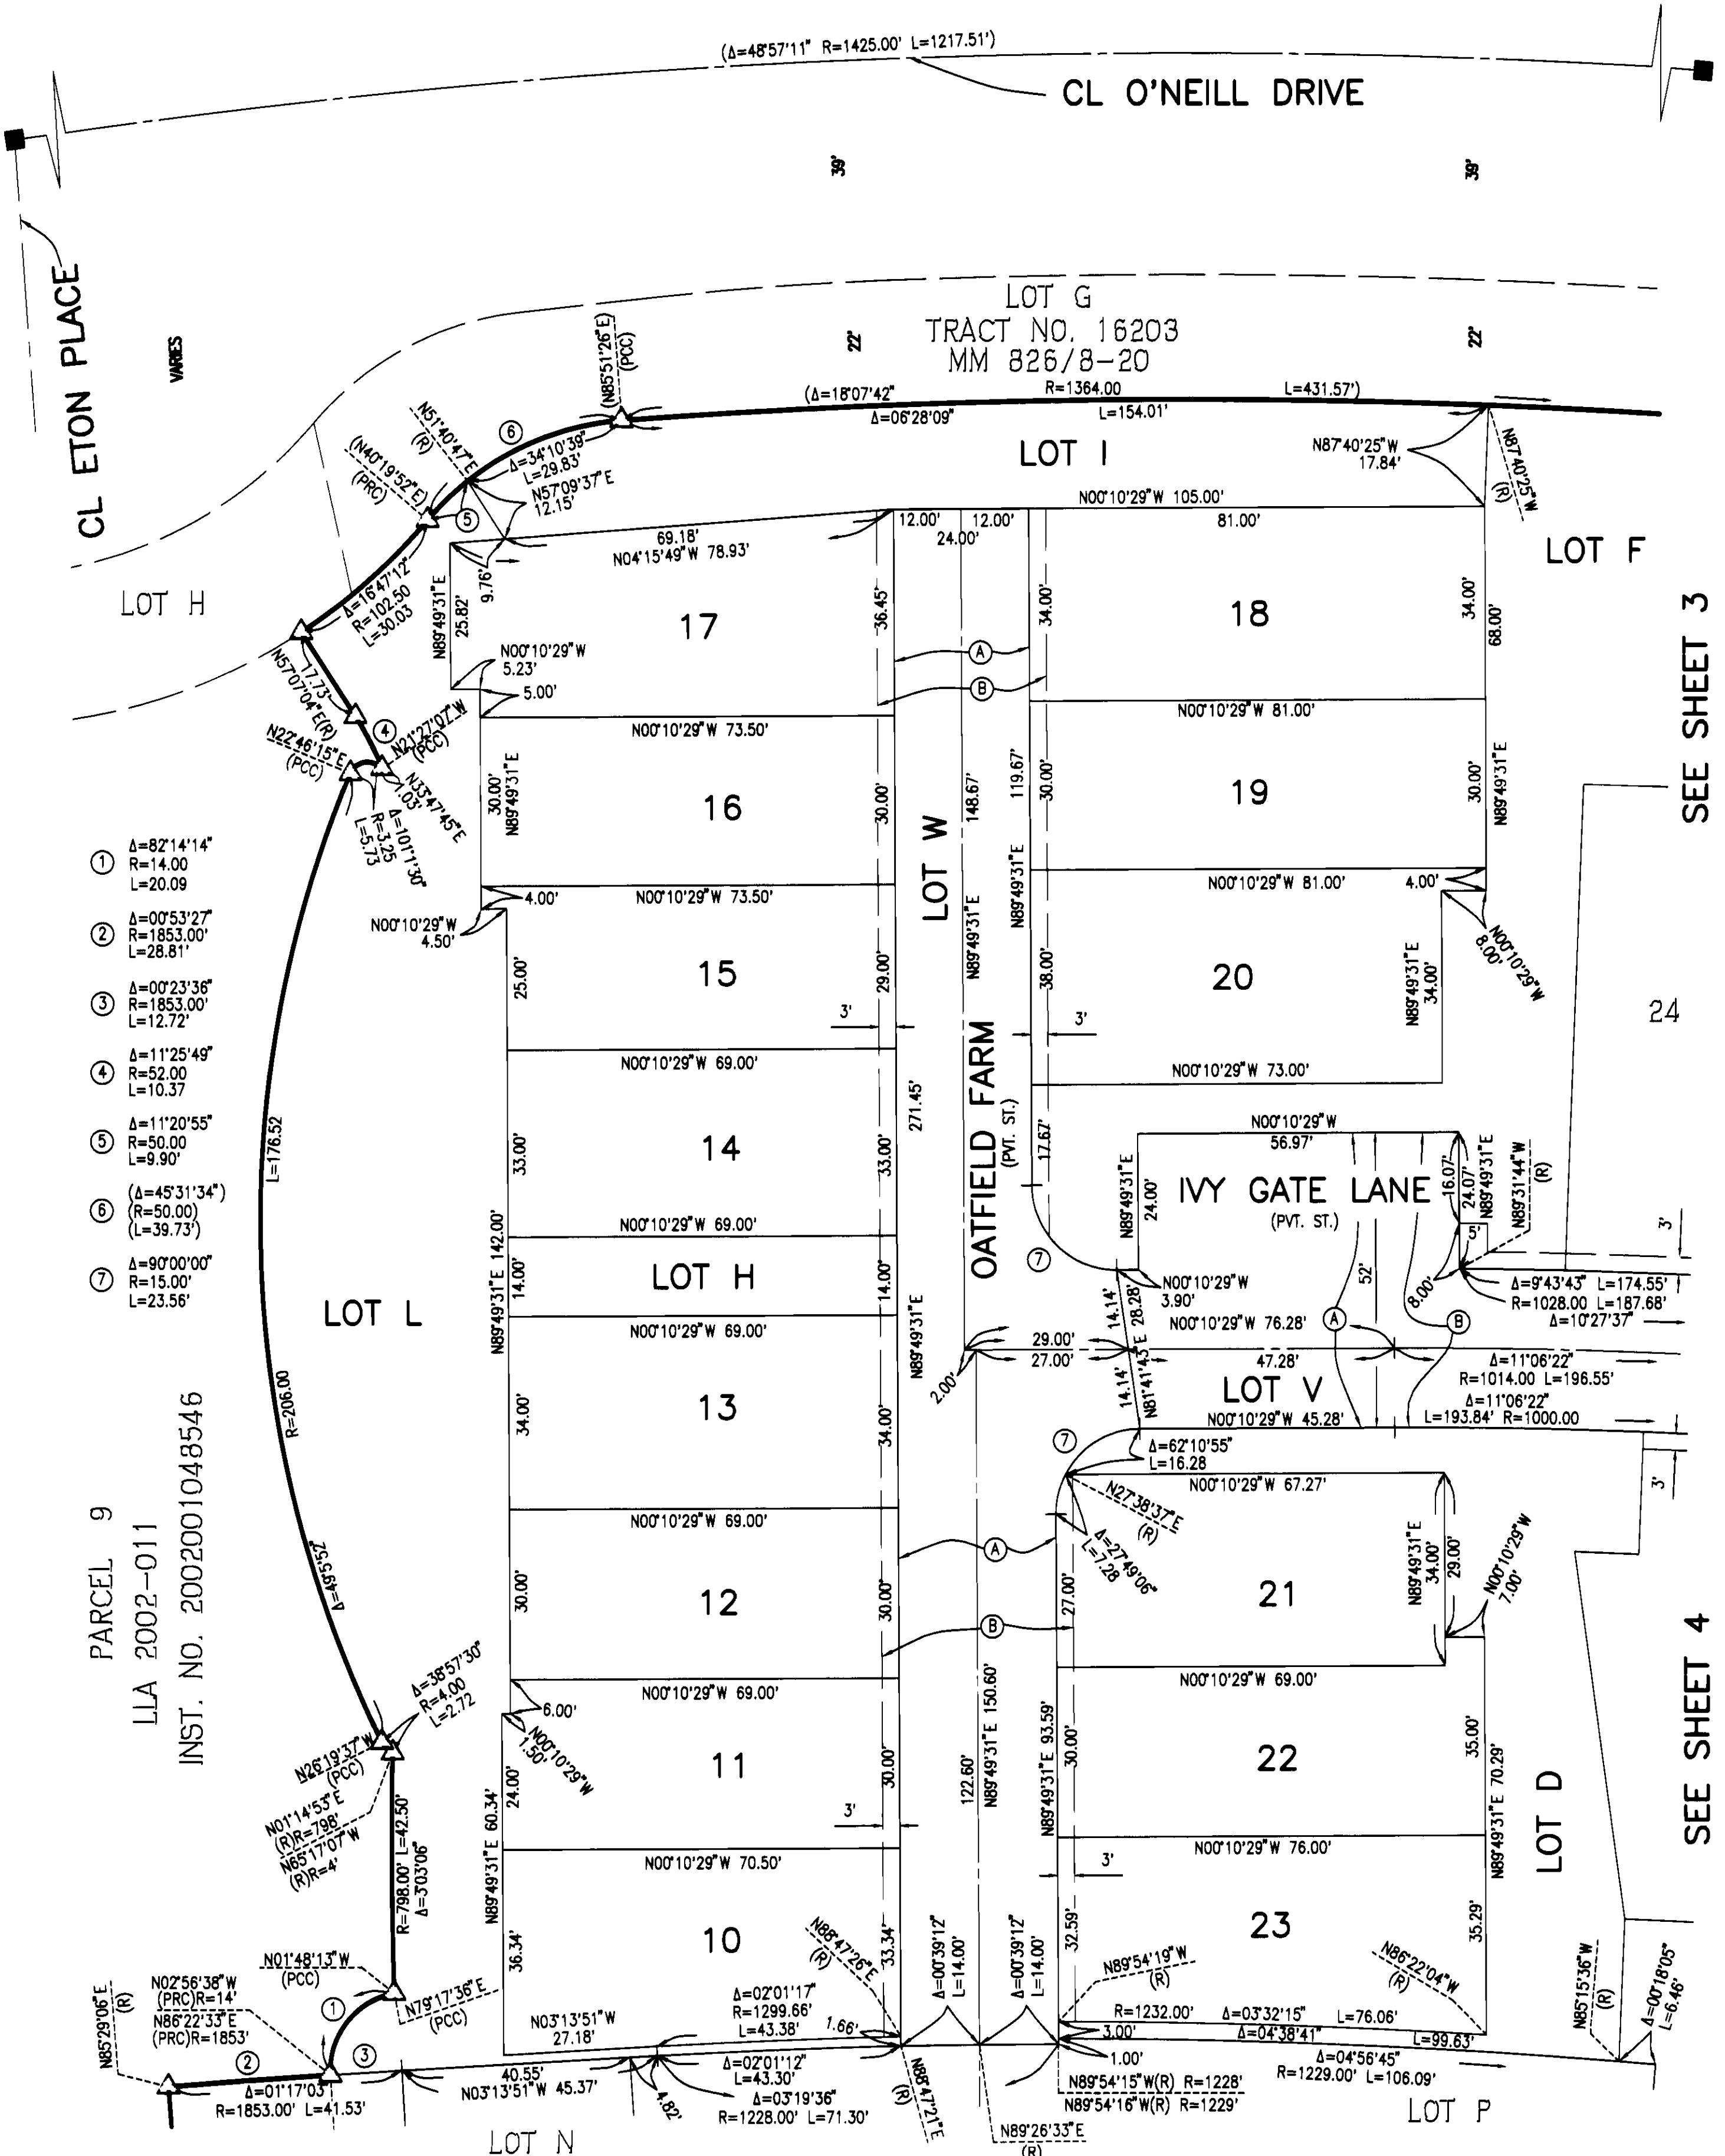

SHEET 7 OF 7 SHEETS

FINAL UNIT OF VESTING TENTATIVE
TRACT MAP NO. 16248
TOTAL LOTS: NUMBERED LOTS 1-55
AND LETTERED LOTS A-Y INCLUSIVE
TOTAL ACREAGE: 6.963 AC.
DATE OF SURVEY: MARCH, 2002

TRACT MAP NO. 16248


IN THE UNINCORPORATED TERRITORY OF THE COUNTY OF ORANGE,
STATE OF CALIFORNIA

ADAMS - STREETER CIVIL ENGINEERING, INC. JAN A. ADAMS, R.C.E. 21687
DATE OF SURVEY: MARCH, 2002

① $\Delta=90^{\circ}00'00''$
 $R=3.00$
 $L=4.71'$

SCALE: 1"=20'

SEE SHEET 6

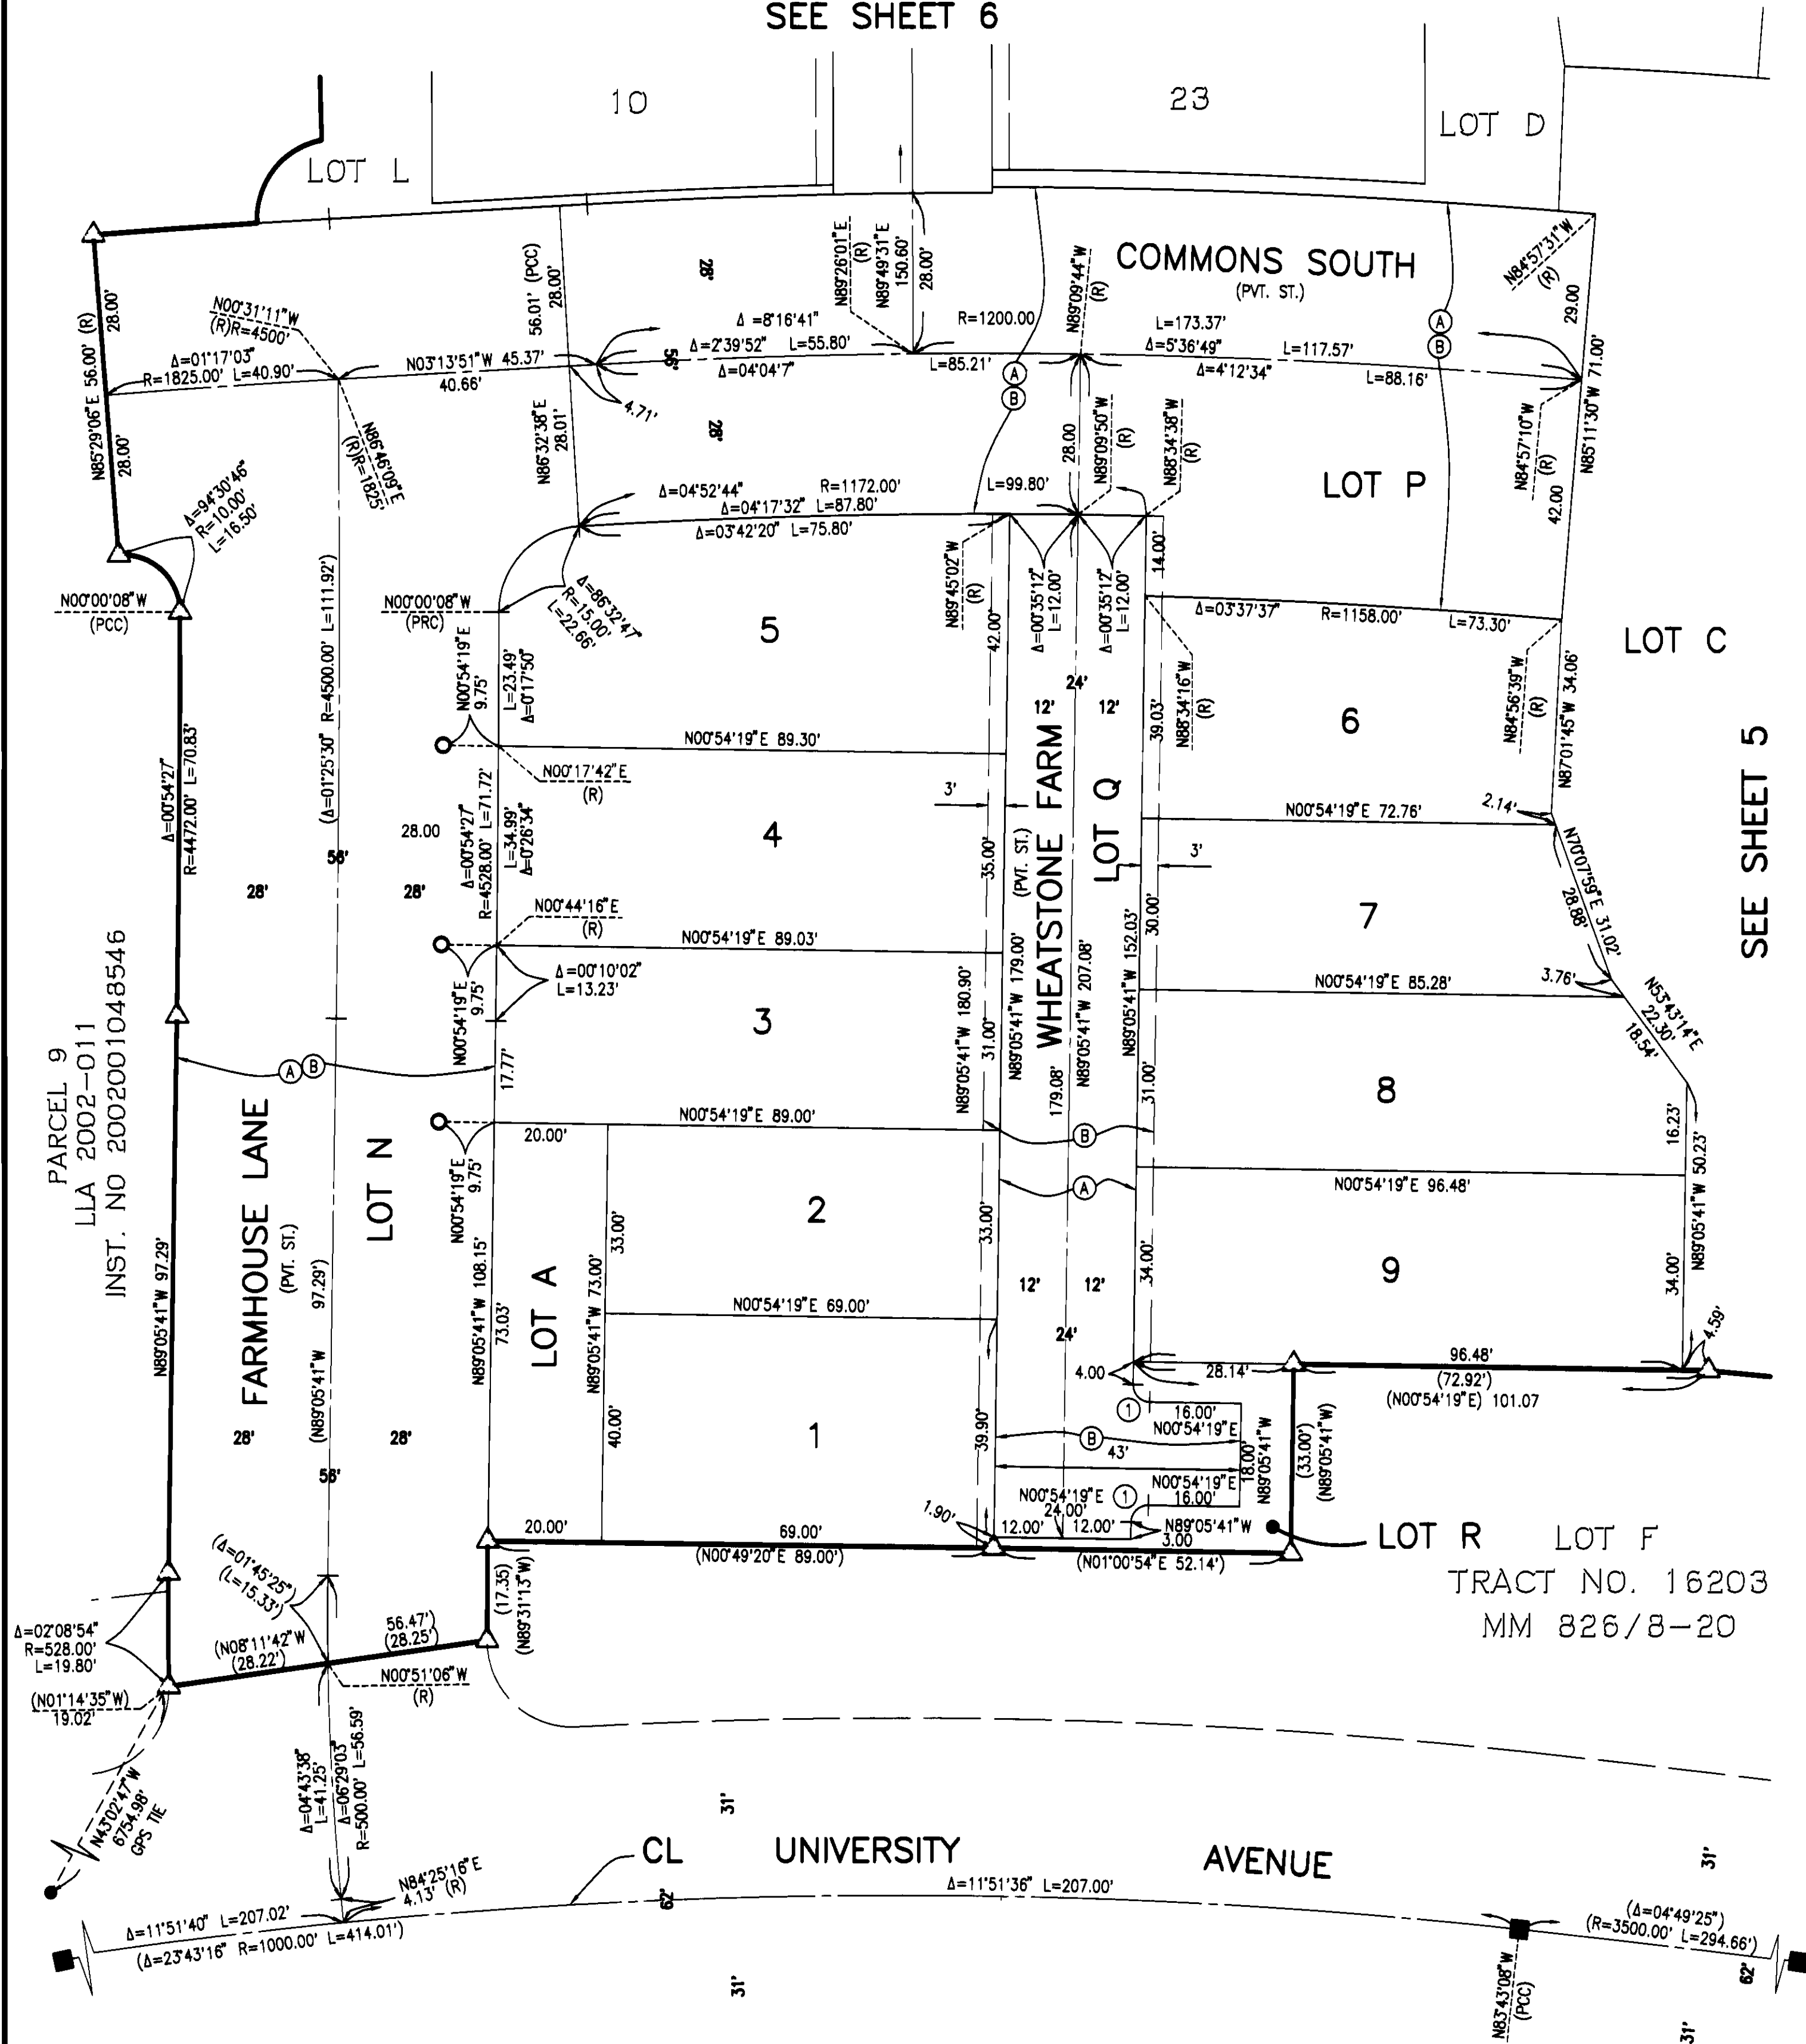

SEE SHEET 5